



ตามนโยบายของ
หม่อมราชวงศ์สุขุมพันธุ์ บริพัตร
ผู้ว่าราชการกรุงเทพมหานคร
โดย สำนักการโยธา



แบบบ้านยืม... เพื่อประชาชน

100 แบบบ้านมาตรฐาน...
สวย ดี โดนใจ...
พร้อมปลูกสร้างได้ทันที

ห้ามพลาด!!! โอกาส...
ยืมรับ... บ้านใหม่
แบบ **บ้านสวย
เลือกได้**
ใน “โครงการแบบบ้านยืม...เพื่อประชาชน”

แบบ 100 แบบบ้าน
มาตรฐาน...
สวย ดี โดนใจ
พร้อมปลูก
สร้างได้ทันที
มีให้เลือก
หลากหลาย
ตอบสนอง
ทุกไลฟ์สไตล์คนเมือง

สราญรมย์ 2

โดยความอนุเคราะห์แบบจาก
บริษัท แลนด์ โธม (ประเทศไทย) จำกัด

รายการประกอบแบบก่อสร้าง TYPE "S"



รายการประกอบแบบทั่วไป

- โครงสร้างบ้านพักอาศัยโดยทั่วไปเป็นคอนกรีตเสริมเหล็กหล่อในที่ ตั้งแต่วางราก ; เสา , คาน , พื้นชั้นล่าง - บน เป็นพื้น - สำเร็จรูป บางส่วนหล่อในที่ ขนาด และ รายละเอียด ตามแบบวิศวกรรม
- เสาเข็มบ้าน 2 ชั้น ใช้คอนกรีตอัดแรง รูปตัว I - 18 X 18 ซม. ยาว 16 ม. กรณีบ้านเกิน 2 ชั้น จะใช้เสาเข็มตาม - การคำนวณของวิศวกร
- หลังคา โครงหลังคาเหล็กรูปพรรณ ทาสีกันสนิม TOA2 ชั้น พร้อมฉนวนฉนวนกันความร้อน 1 ชั้น มุงด้วยกระเบื้อง CPAC MONIER สีมาตรฐานบริษัท หรือ เทียบเท่า
- ผนังทั่วไปใช้อลูมิเนียม จากปูนเรียบ ทาสี ยกเว้นผนังโชว์ ทำผิวพิเศษตามระบุในแบบ
- ฝ้าเพดานภายใน แผ่นยิปซัมบอร์ด ทนไฟ 9 มม. จากปูนเรียบ ทาสี ความสูงจากพื้นถึงฝ้า 2.60 เมตร
- ภายนอกกระเบื้องแผ่นเรียบ ทนไฟ 4 มม. , ห้องน้ำแผ่นยิปซัมบอร์ด ทนไฟ 9 มม. วางบนโครงคร่าว T - BAR
- บันไดโครงสร้างไม้ดีด ลูกตั้งบันได , ลูกนอนบันไดไม้ดีด เสา , ราวบันได , ลูกกรงบันไดไม้ดีด
- สีที่ใช้ SUPERCOAT ผลิตของ ICI หรือ เทียบเท่า
- การป้องกันปลวก ใช้ระบบดินทอกที่บริเวณคานชั้นล่างทั้งหมด และทากันยุงกับปลวกบนเนื้อโครงคร่าวด้วยที่เปื้อน

รายการประกอบแบบการเปลี่ยนแปลงเพิ่มเติม

• หมายเหตุ : งานโครงหลังคา ปรองรับกระเบื้องใช้แป้นไม้ความหนา 0.7 ซม.

* ไม่มีรายการเปลี่ยนแปลง

สัญลักษณ์ประกอบแบบสถาปัตย์

สัญลักษณ์	ความหมาย
N	ทิศเหนือ
	1 , 2 , 3 , 4 ชื่อรูปลูกันกำหนดจากแปลน
A	A หมายถึง ชื่อรูปลูกัน
A	A หมายถึง ชื่อแบบขยาย
A	A หมายถึง ชื่อรูปลูกัน
A	A หมายถึง แนวการระบายศูนย์กลาง
+0000 , -0000	+0000 มีค่ามากได้ไม่เกินตัวเลขที่กำหนด , -0000 มีค่าน้อยได้ไม่เกินตัวเลขที่กำหนด
B	B หมายถึง ระยะความยาวจากศูนย์กลางถึงศูนย์กลาง
B	B หมายถึง ระยะความยาวจากริมถึงริม
A	A หมายถึง ระยะความยาวจากศูนย์กลางถึงผนังริมนอก
A	A หมายถึง ระยะความยาวจากศูนย์กลางถึงผนังริมใน
①	1 หมายถึง รั้วประตู
①	1 หมายถึง รั้วหน้าต่าง
△	1 หมายถึง หมายเลขผนัง
	ผนังอิฐครึ่งแผ่น จากปูน
	ผนังอิฐครึ่งแผ่น จากปูน
	ผนังอิฐมวลเบา จากปูน
GB	ผนังอิฐบล็อกแก้ว ตามแบบระบุ
	ผนังเบรคโครงไม้ดีด กรุฉนวนตามแบบระบุ
	ดิน
	คอนกรีต
	ทรายอัดแน่น
	หินกบ
	ปูนฉาบเรียบ
	จากปูนชะร่อง
	จากปูนเรียบ

บ้าน SMILE HOME
V.1 [11/2/45]

สัญญาฉบับที่ 2


ได้รับความอนุเคราะห์แบบ
จาก
บริษัท แลนด์ โฮม
(ประเทศไทย) จำกัด



โครงการ
แบบบ้านยืมเพื่อประชาชน

ตามนโยบาย
ม.ร.ว. สุขุมพันธุ์ บริพัตร
ผู้ว่าราชการกรุงเทพมหานคร


โดยสำนักงานโยธา
กรุงเทพมหานคร

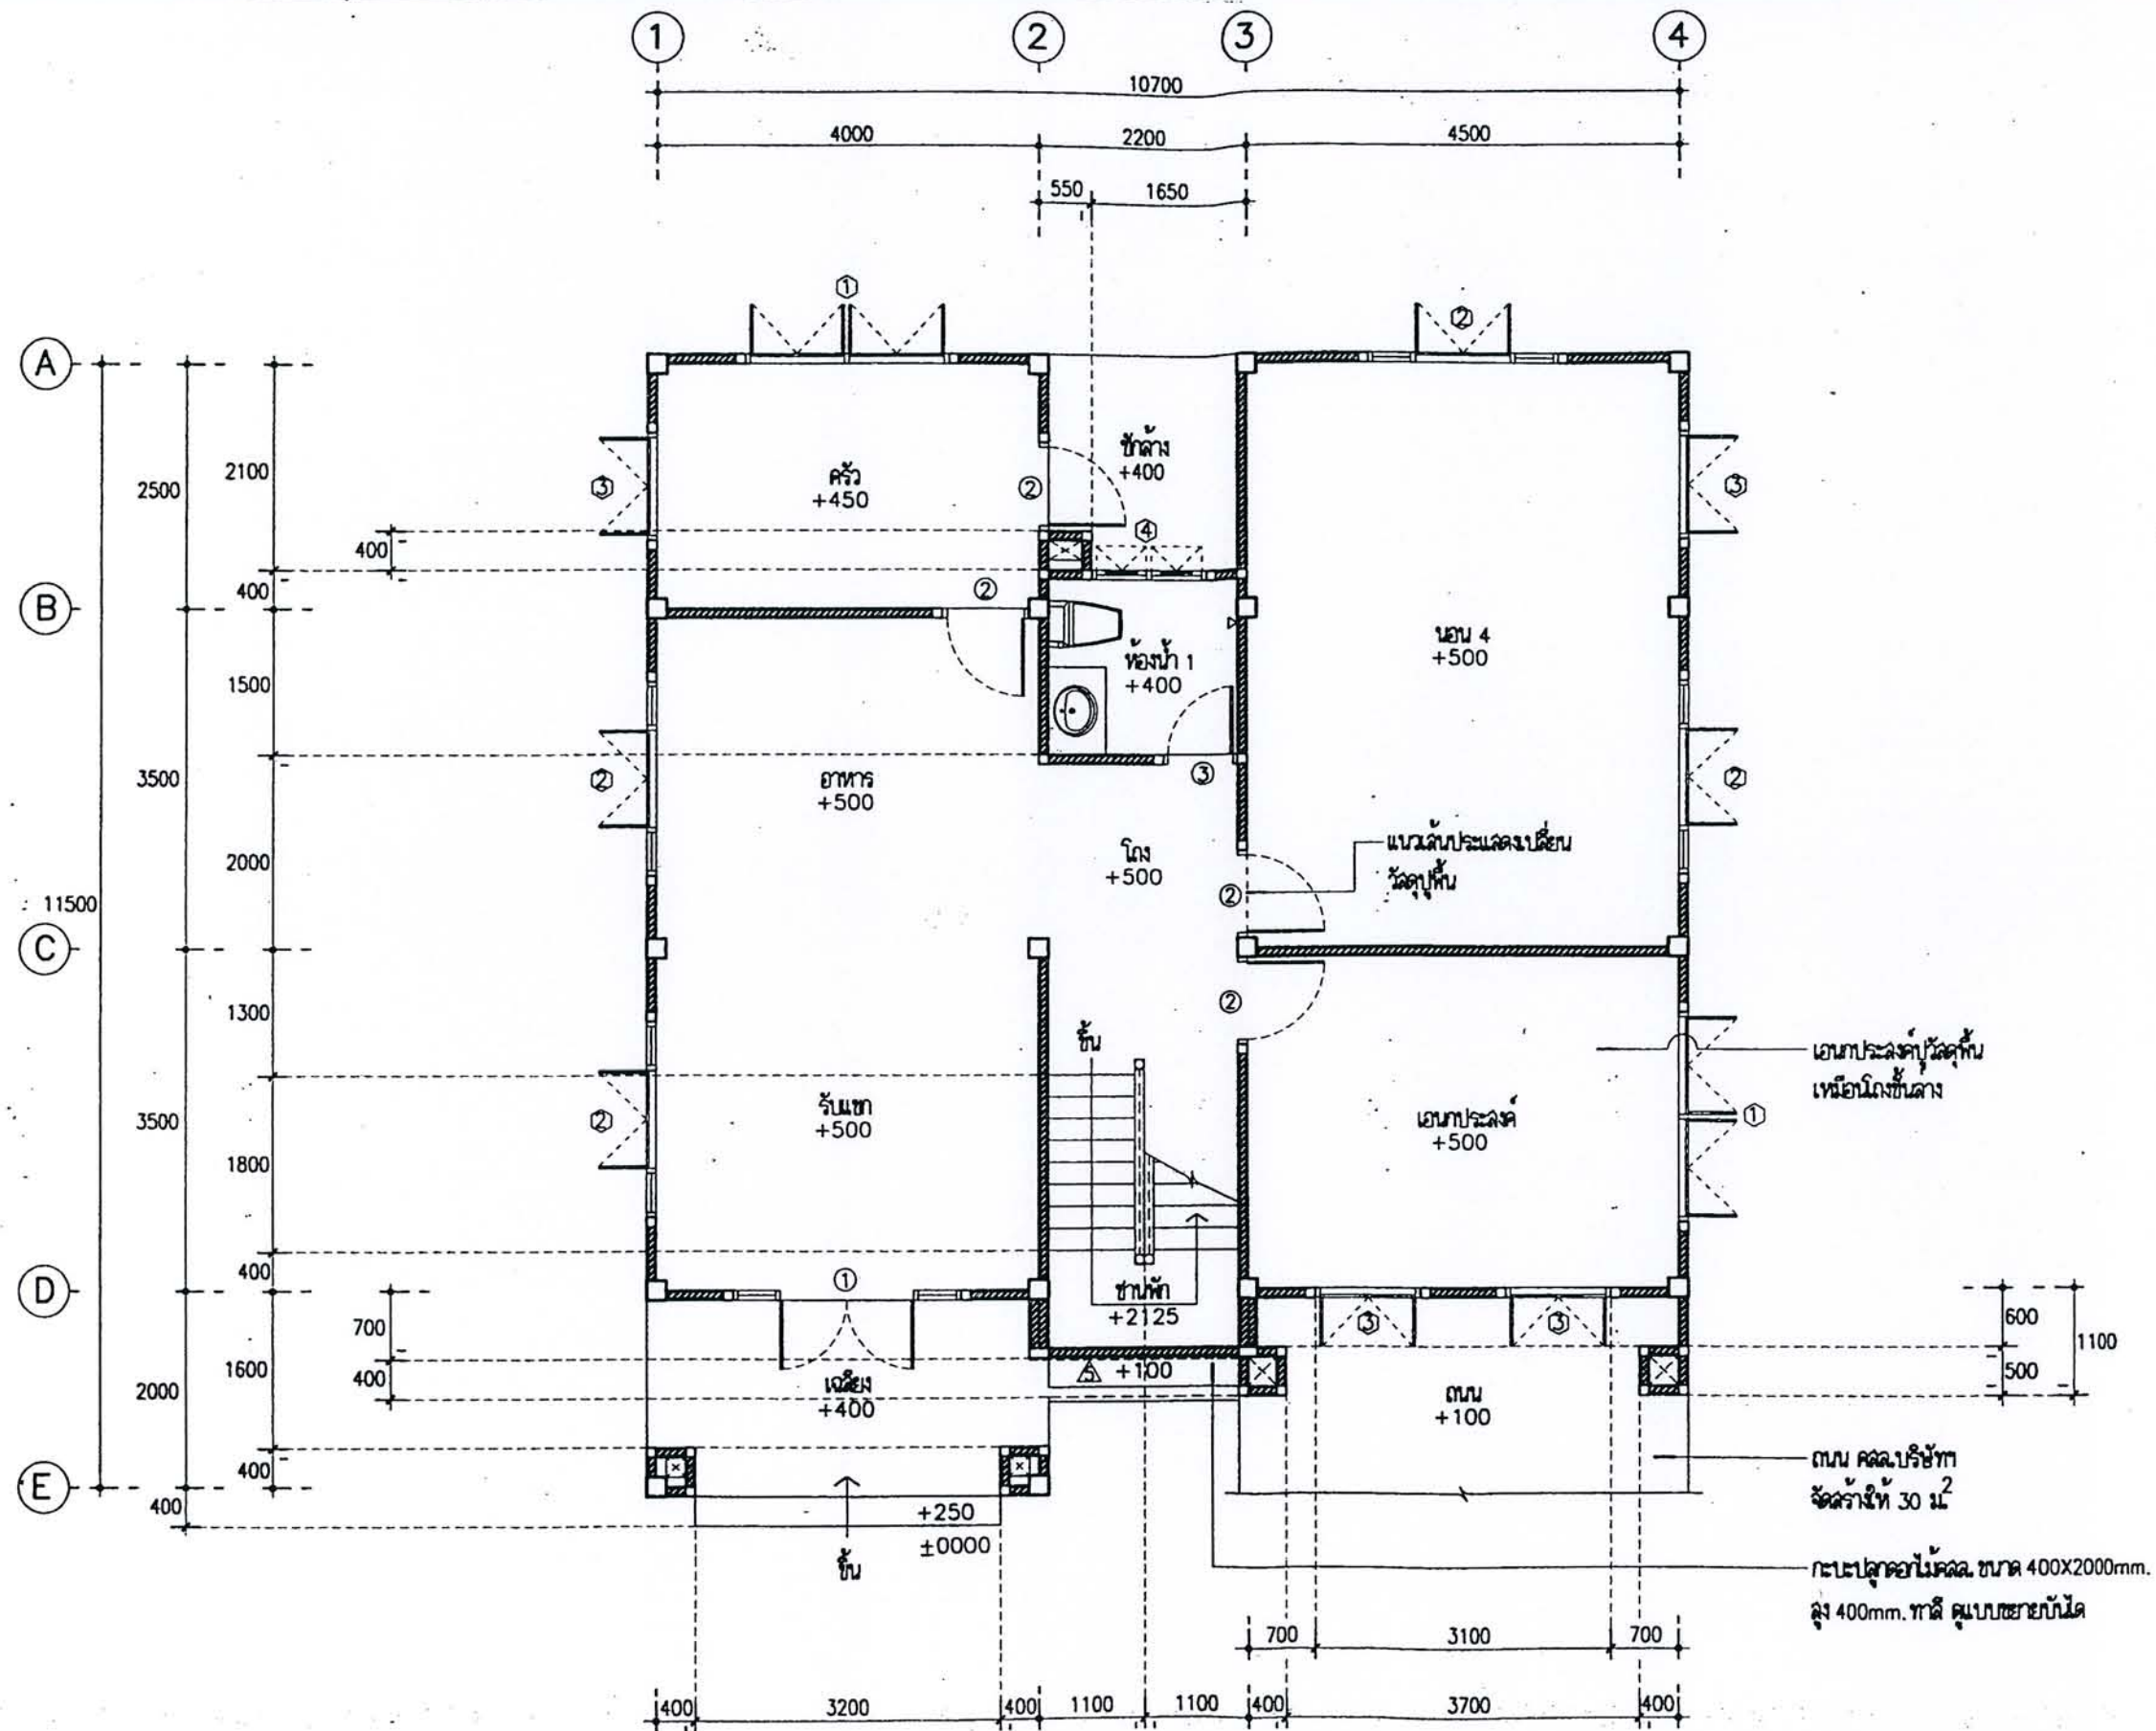

แปลนพื้นที่ชั้นล่าง

มาตราส่วน

1 : 75

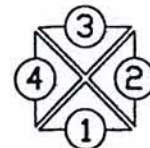

* หมายเหตุ : ช่องประตูบานประตูไม้ทาสีเหลือง
งานระบบเครื่องใช้ไฟฟ้า ติดตั้งให้เรียบร้อย
เพื่อกับทาสีบริเวณพื้นชั้นล่าง

ได้รับความอนุเคราะห์แบบ
จาก
บริษัท แลนด์ โยม -
(ประเทศไทย) จำกัด




โครงการ
แบบบ้านยืมเพื่อประชาชน

ตามนโยบาย
ม.ร.ว. สุขุมพันธุ์ บริพัตร
ผู้ว่าราชการกรุงเทพมหานคร

โดยสำนักงานโยธา
กรุงเทพมหานคร


ได้รับความอนุเคราะห์แบบ
จาก
บริษัท แลนด์ โสม
(ประเทศไทย) จำกัด

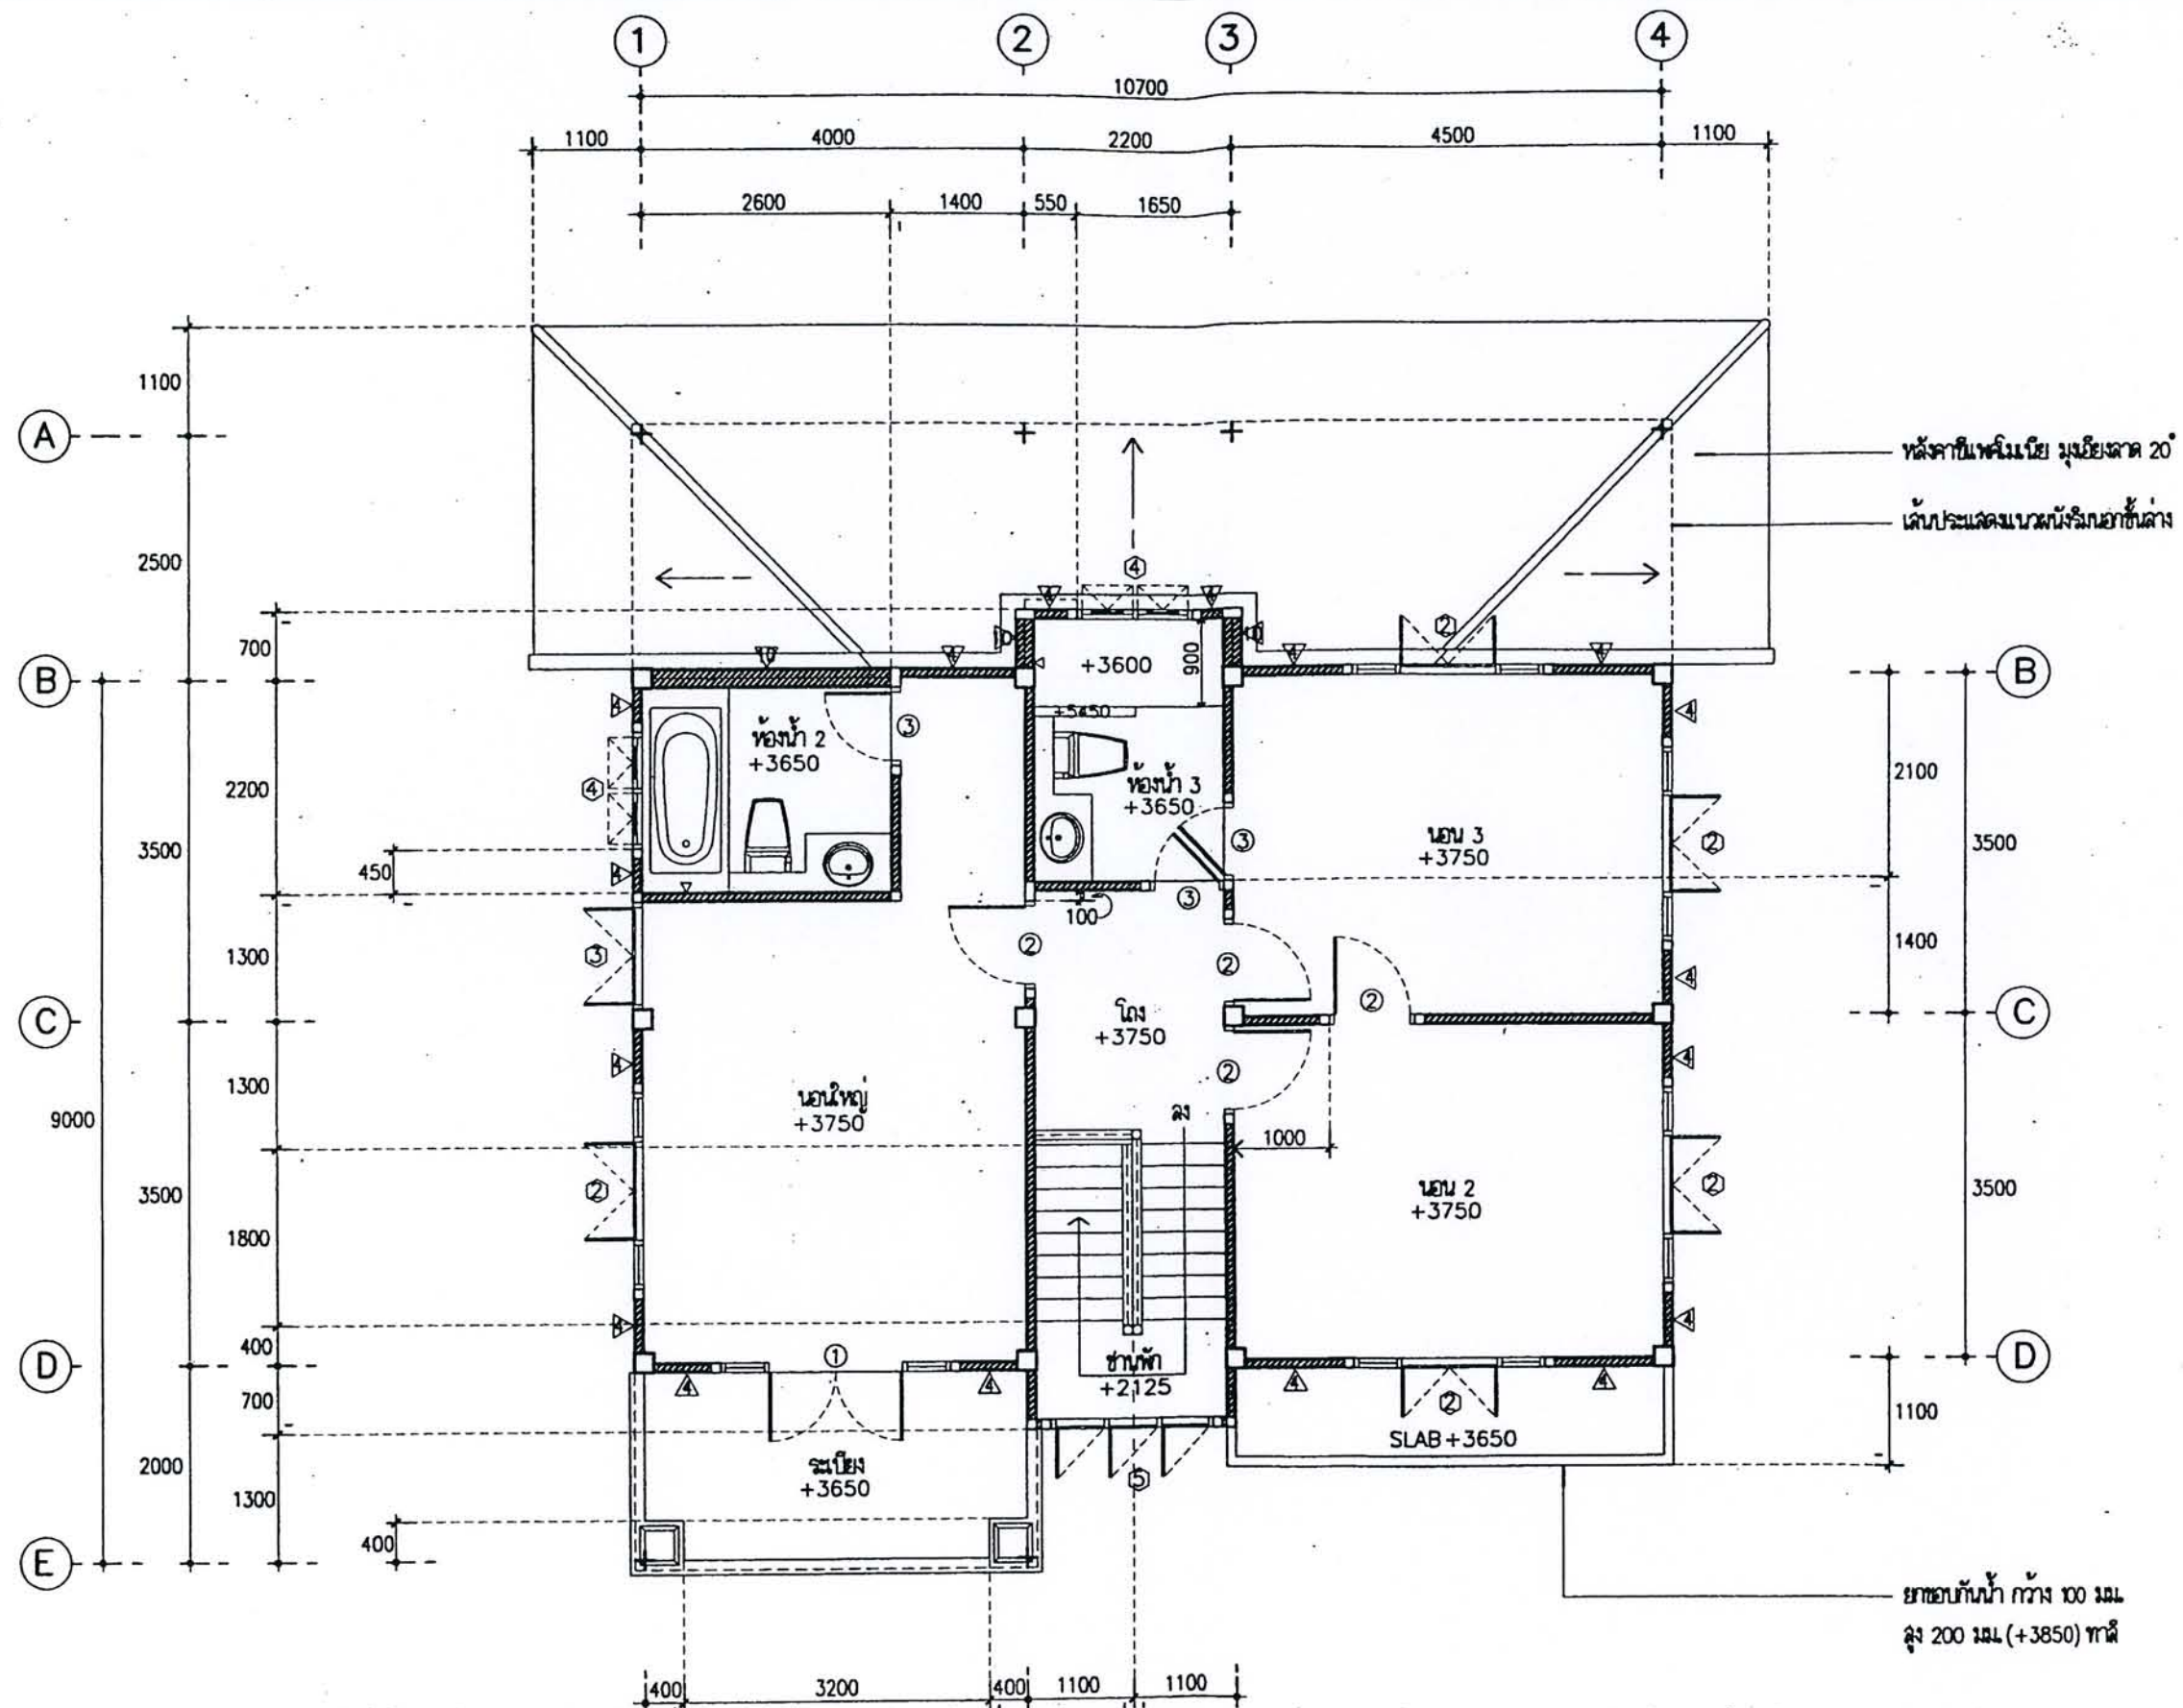

แปลนพื้นที่ขึ้นบน

มาตราส่วน

1 : 75

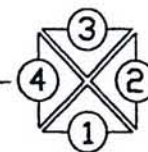




โครงการ
แบบบ้านยืมเพื่อประชาชน

ตามนโยบาย
ม.ร.ว. สุขุมพันธุ์ บริพัตร
ผู้ว่าราชการกรุงเทพมหานคร

โดยสำนักงานโยธา
กรุงเทพมหานคร

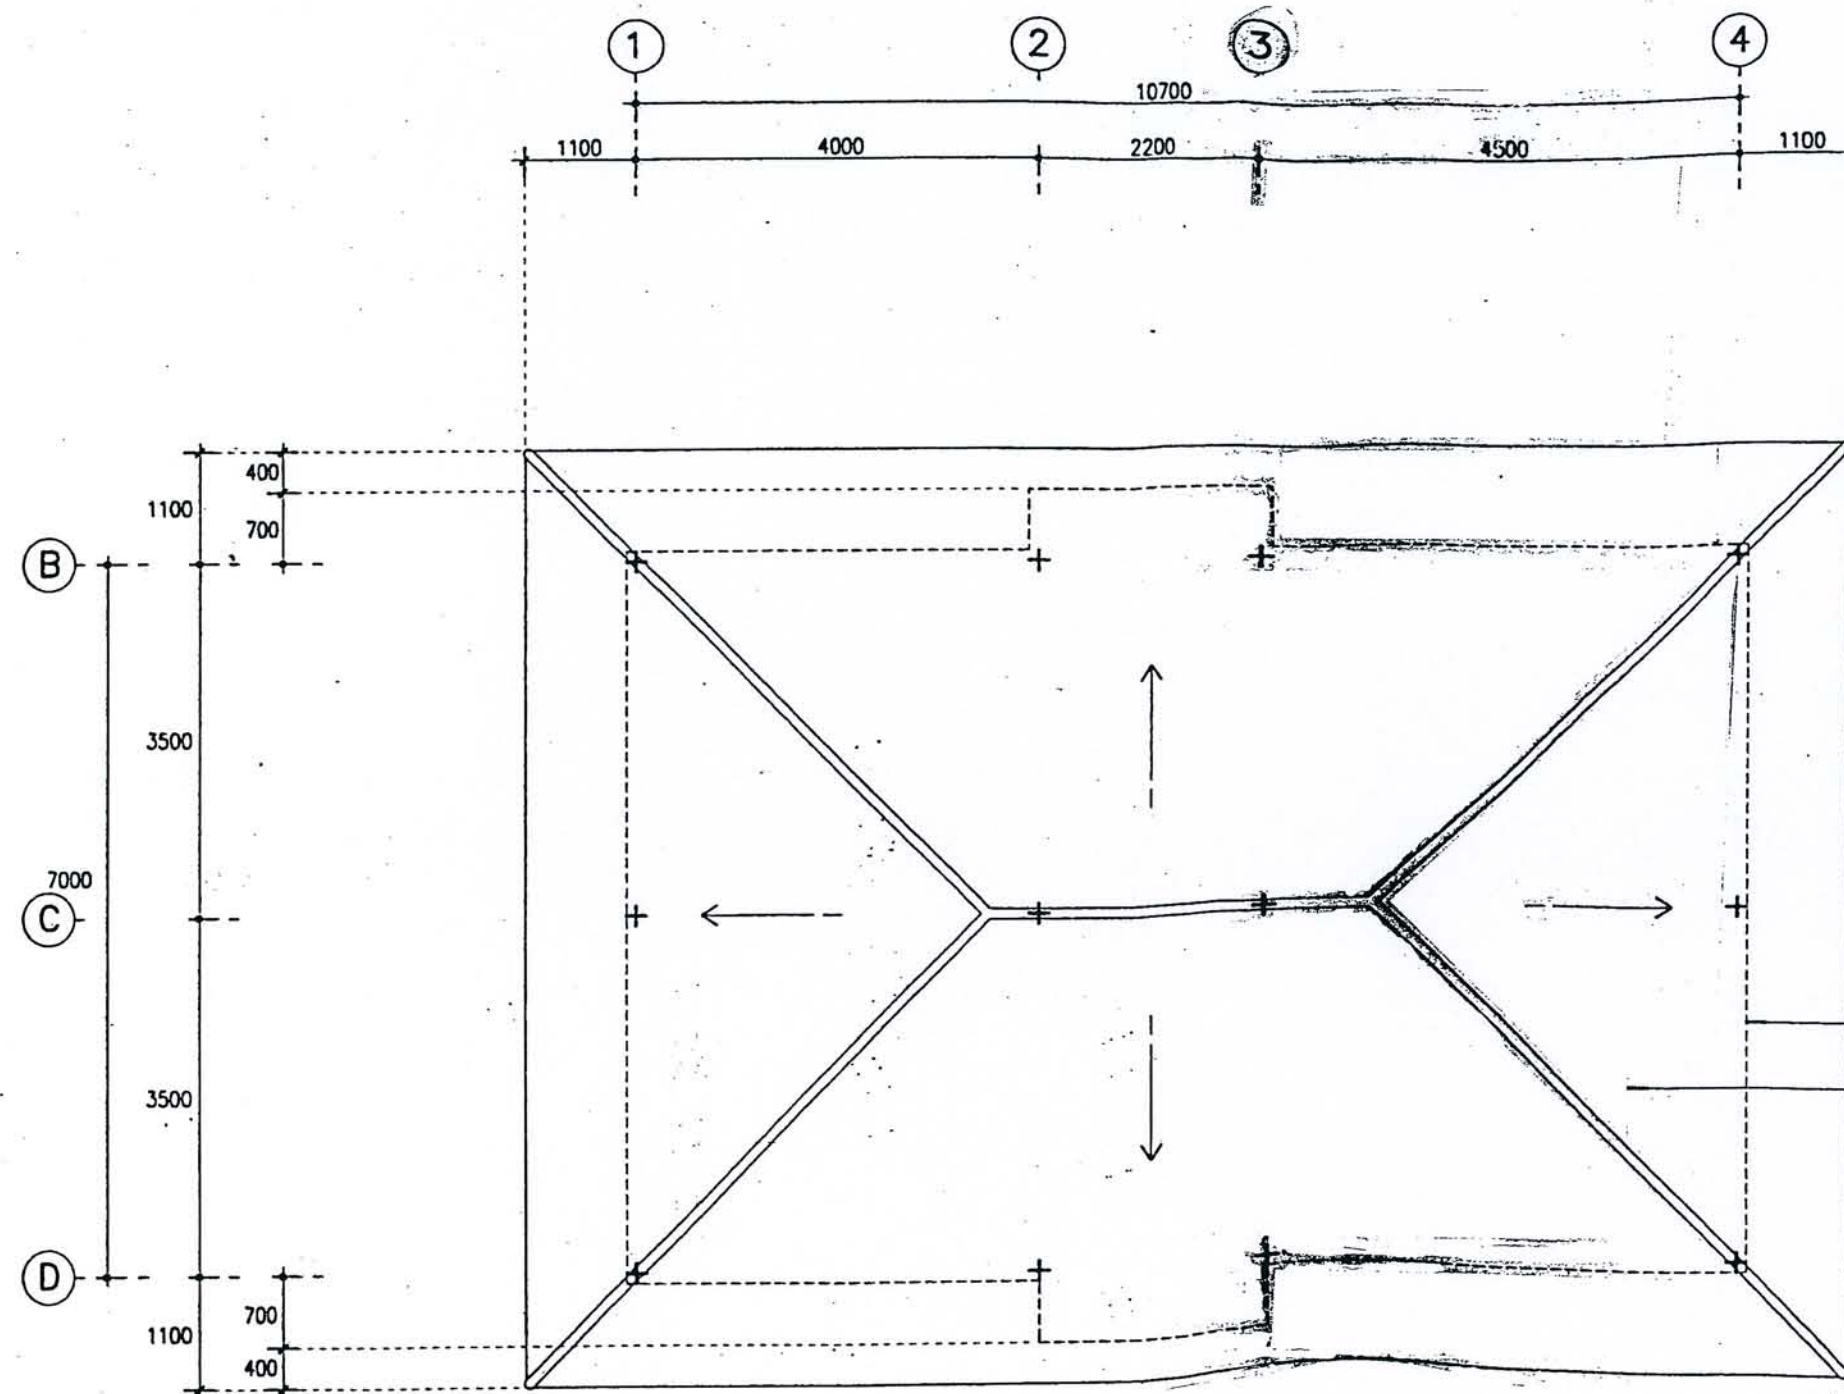

เส้นประแสดงแนวรั้วเดิม
หลังคาเป็นโพรมิเอ มุมลาด 30°

แปลนหลังคา
มาตราส่วน 1:75




ได้รับความอนุเคราะห์แบบ
จาก
บริษัท แลนด์ โฮม
(ประเทศไทย) จำกัด



โครงการ
แบบบ้านยืมเพื่อประชาชน

ตามนโยบาย
ม.ร.ว. สุขุมพันธุ์ บริพัตร
ผู้ว่าราชการกรุงเทพมหานคร

โดยสำนักงานโยธา
กรุงเทพมหานคร

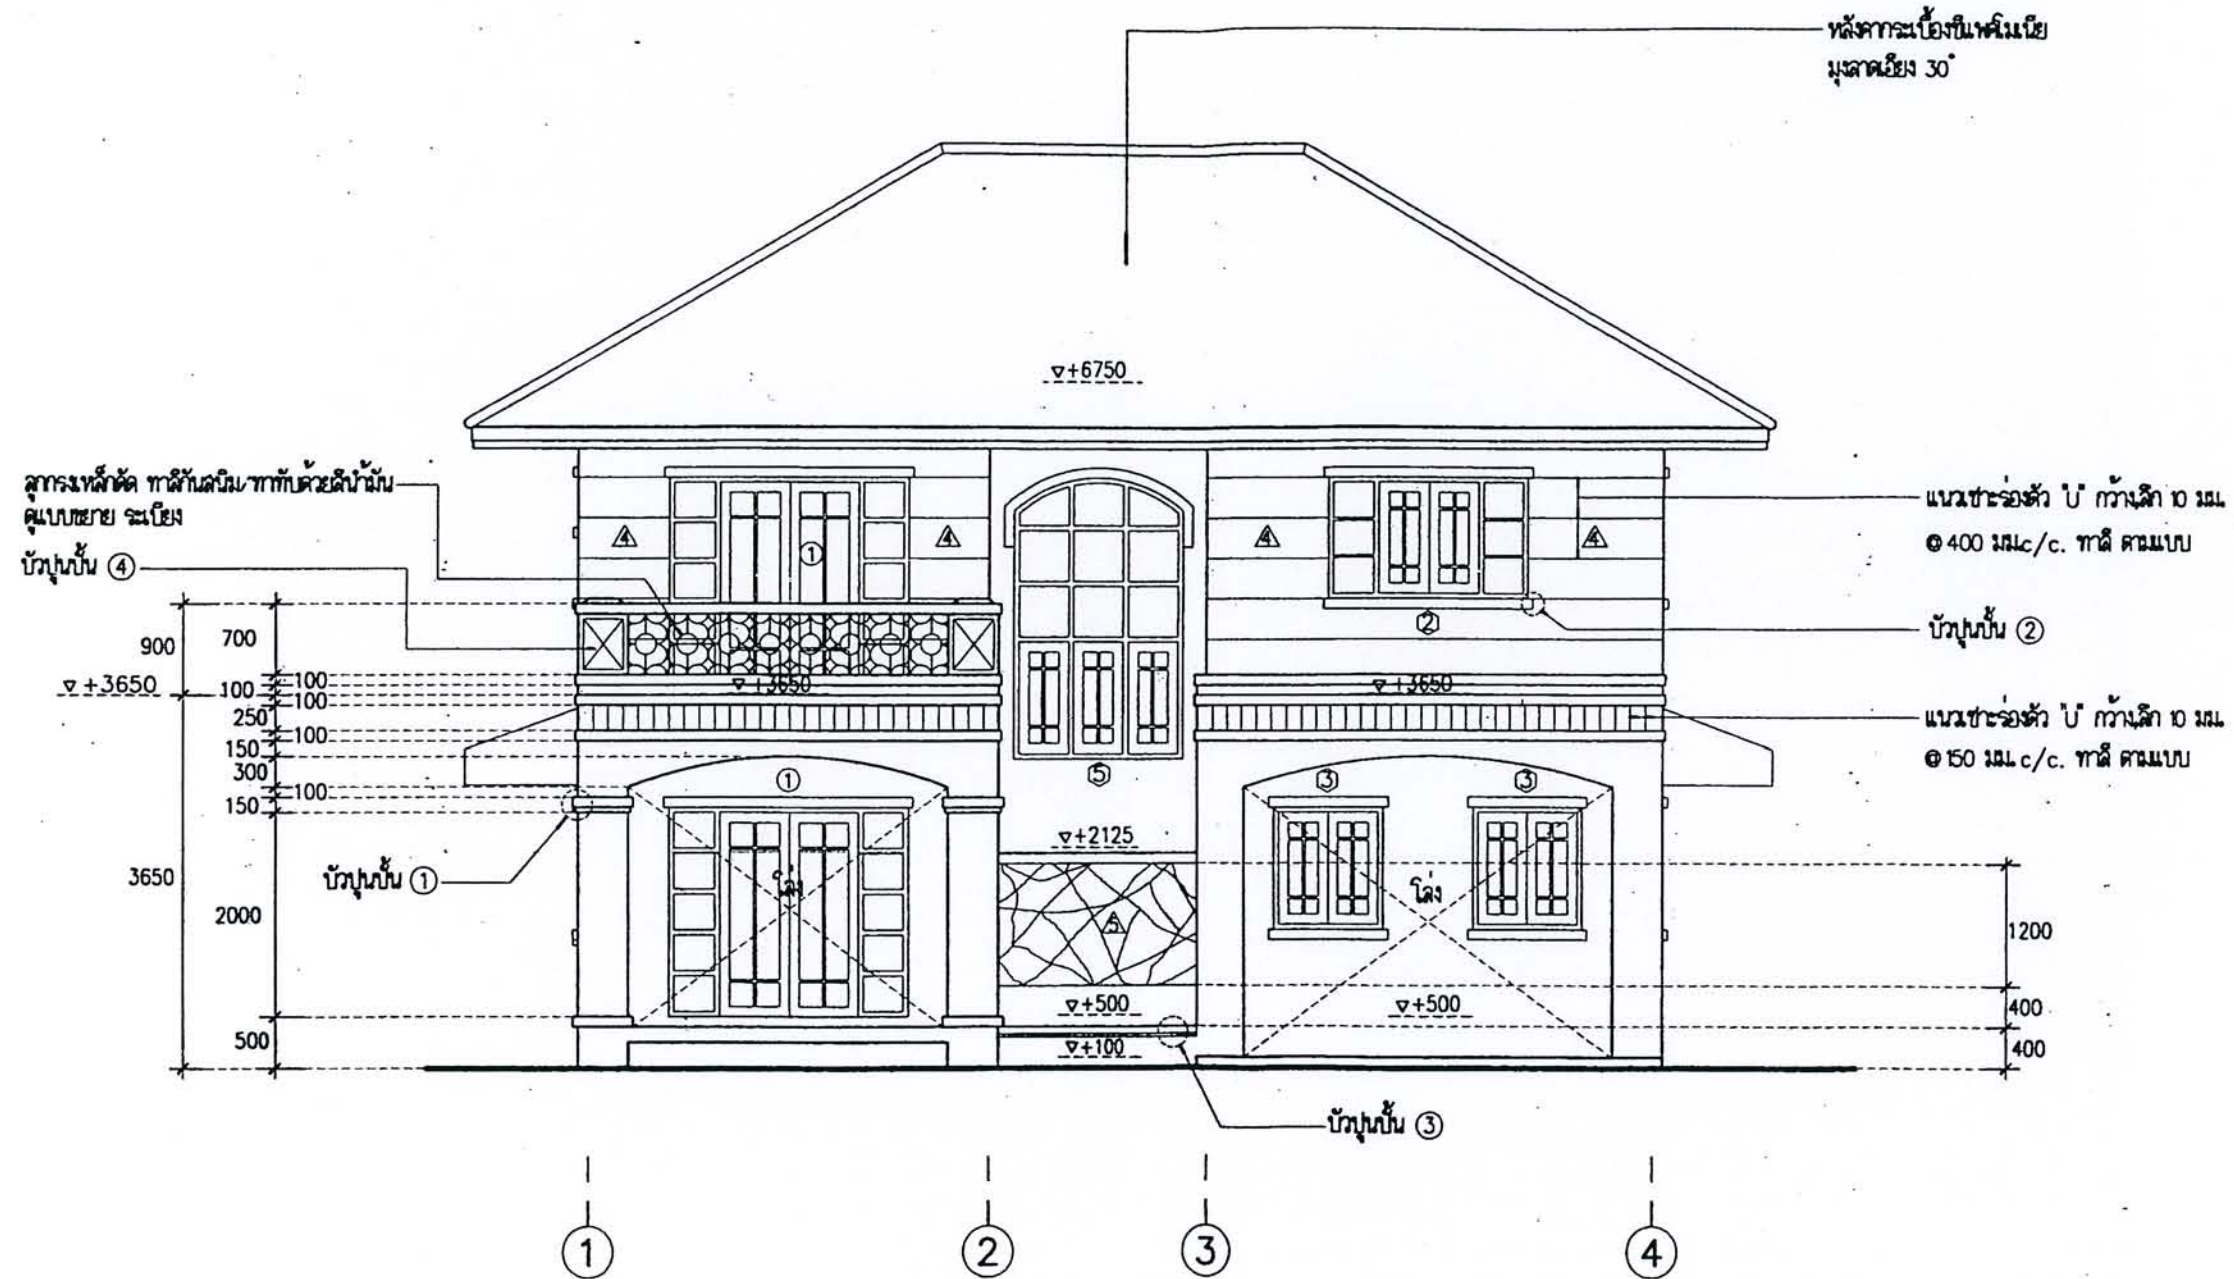

รูปด้าน
หน้า
มาตราส่วน 1 : 75


ได้รับความอนุเคราะห์แบบ
จาก
บริษัท แลนด์ โสม
(ประเทศไทย) จำกัด



โครงการ
แบบบ้านยืมเพื่อประชาชน

ตามนโยบาย
ม.ร.ว. สุขุมพันธุ์ บริพัตร
ผู้ว่าราชการกรุงเทพมหานคร

โดยสำนักงานโยธา
กรุงเทพมหานคร

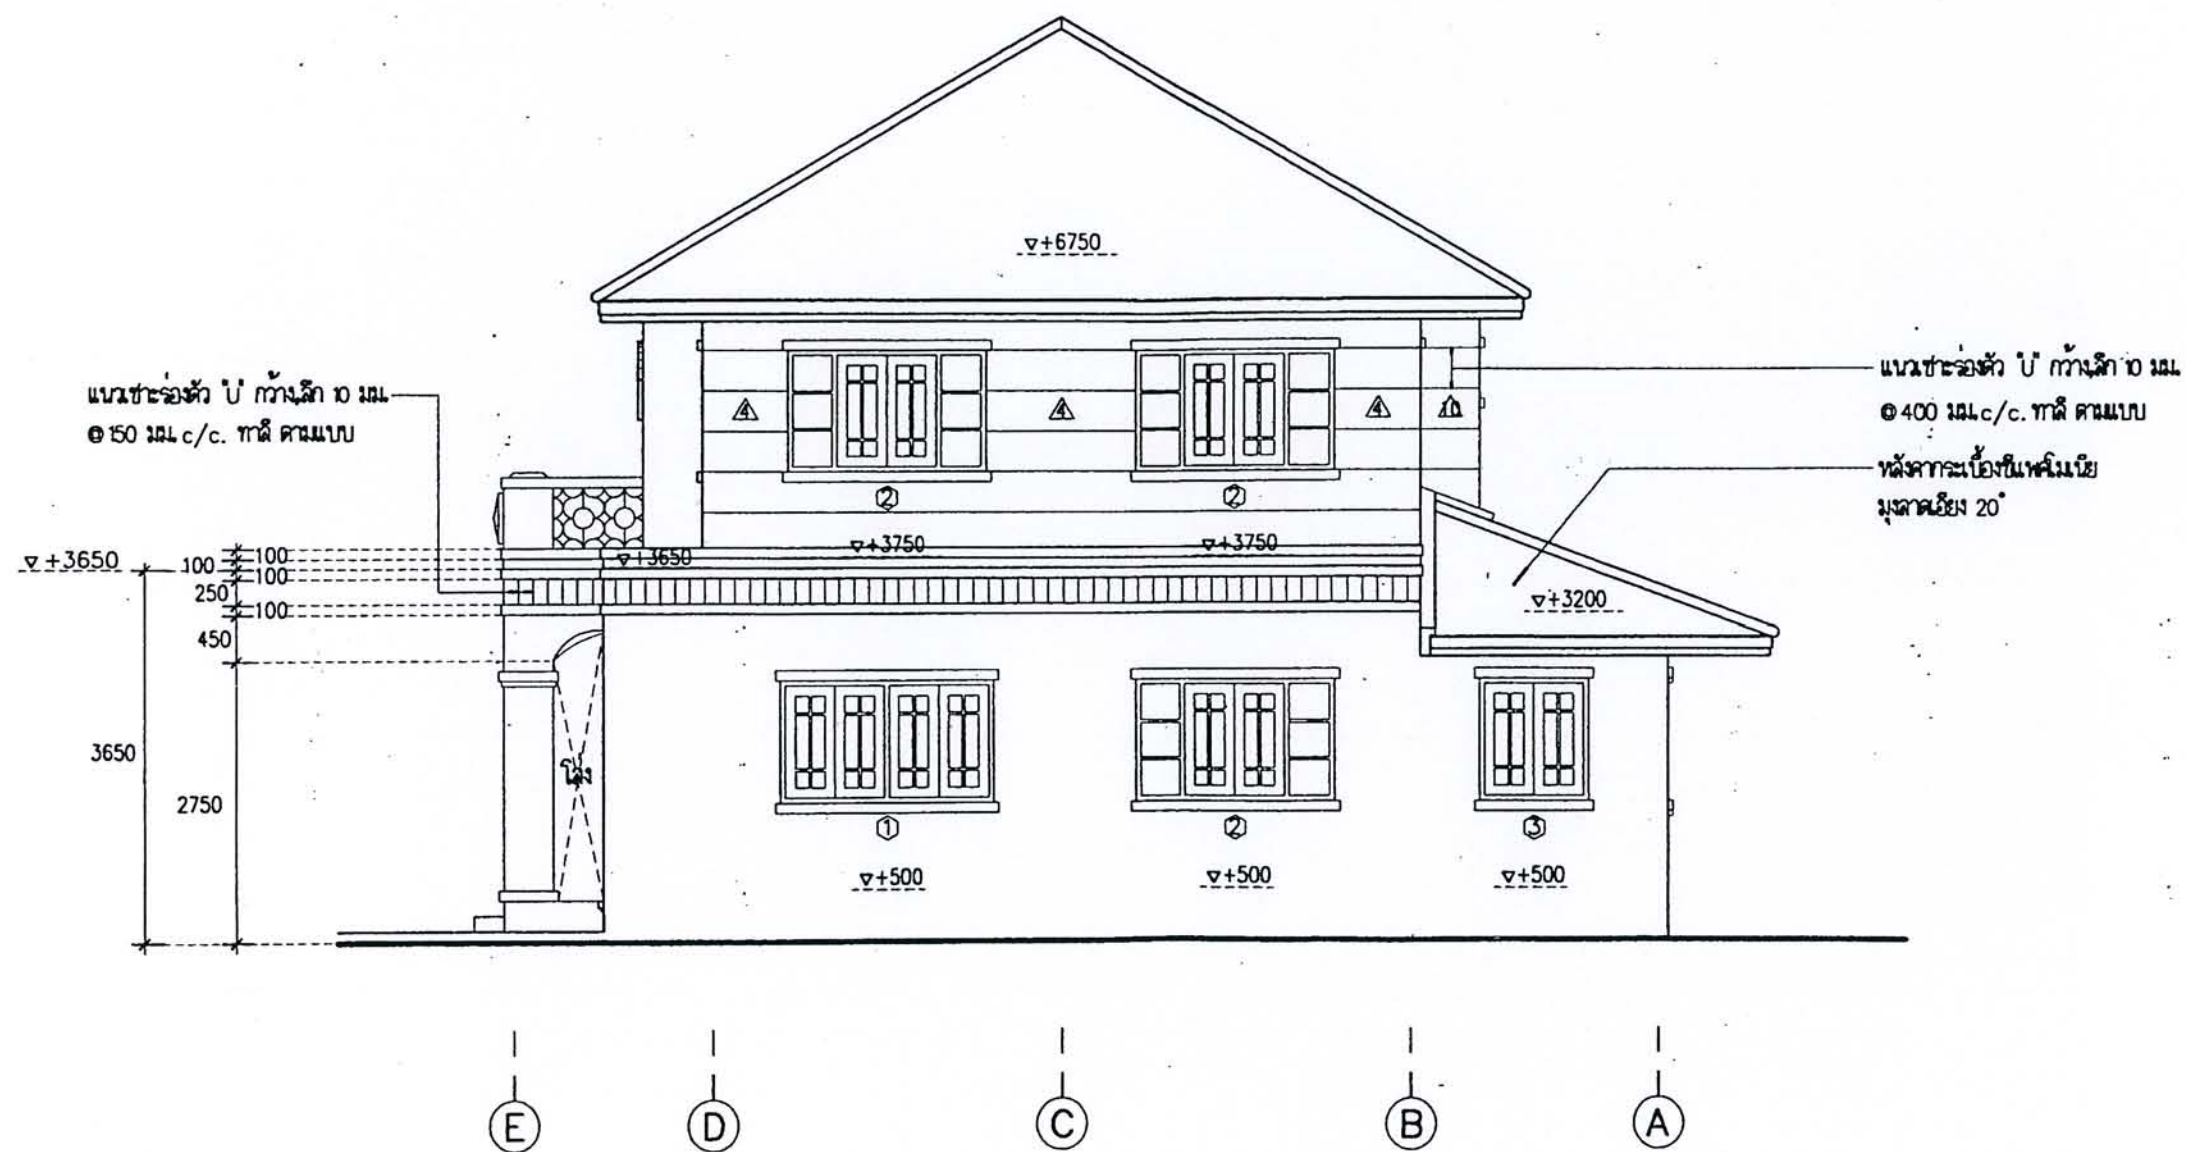

รูปด้าน ๒
มาตรฐาน
1 : 75


ได้รับความอนุเคราะห์แบบ
จาก
บริษัท แลนด์ โยม
(ประเทศไทย) จำกัด



โครงการ
แบบบ้านยืมเพื่อประชาชน

ตามนโยบาย
ม.ร.ว. สุขุมพันธุ์ บริพัตร
ผู้ว่าราชการกรุงเทพมหานคร

โดยสำนักการโยธา
กรุงเทพมหานคร

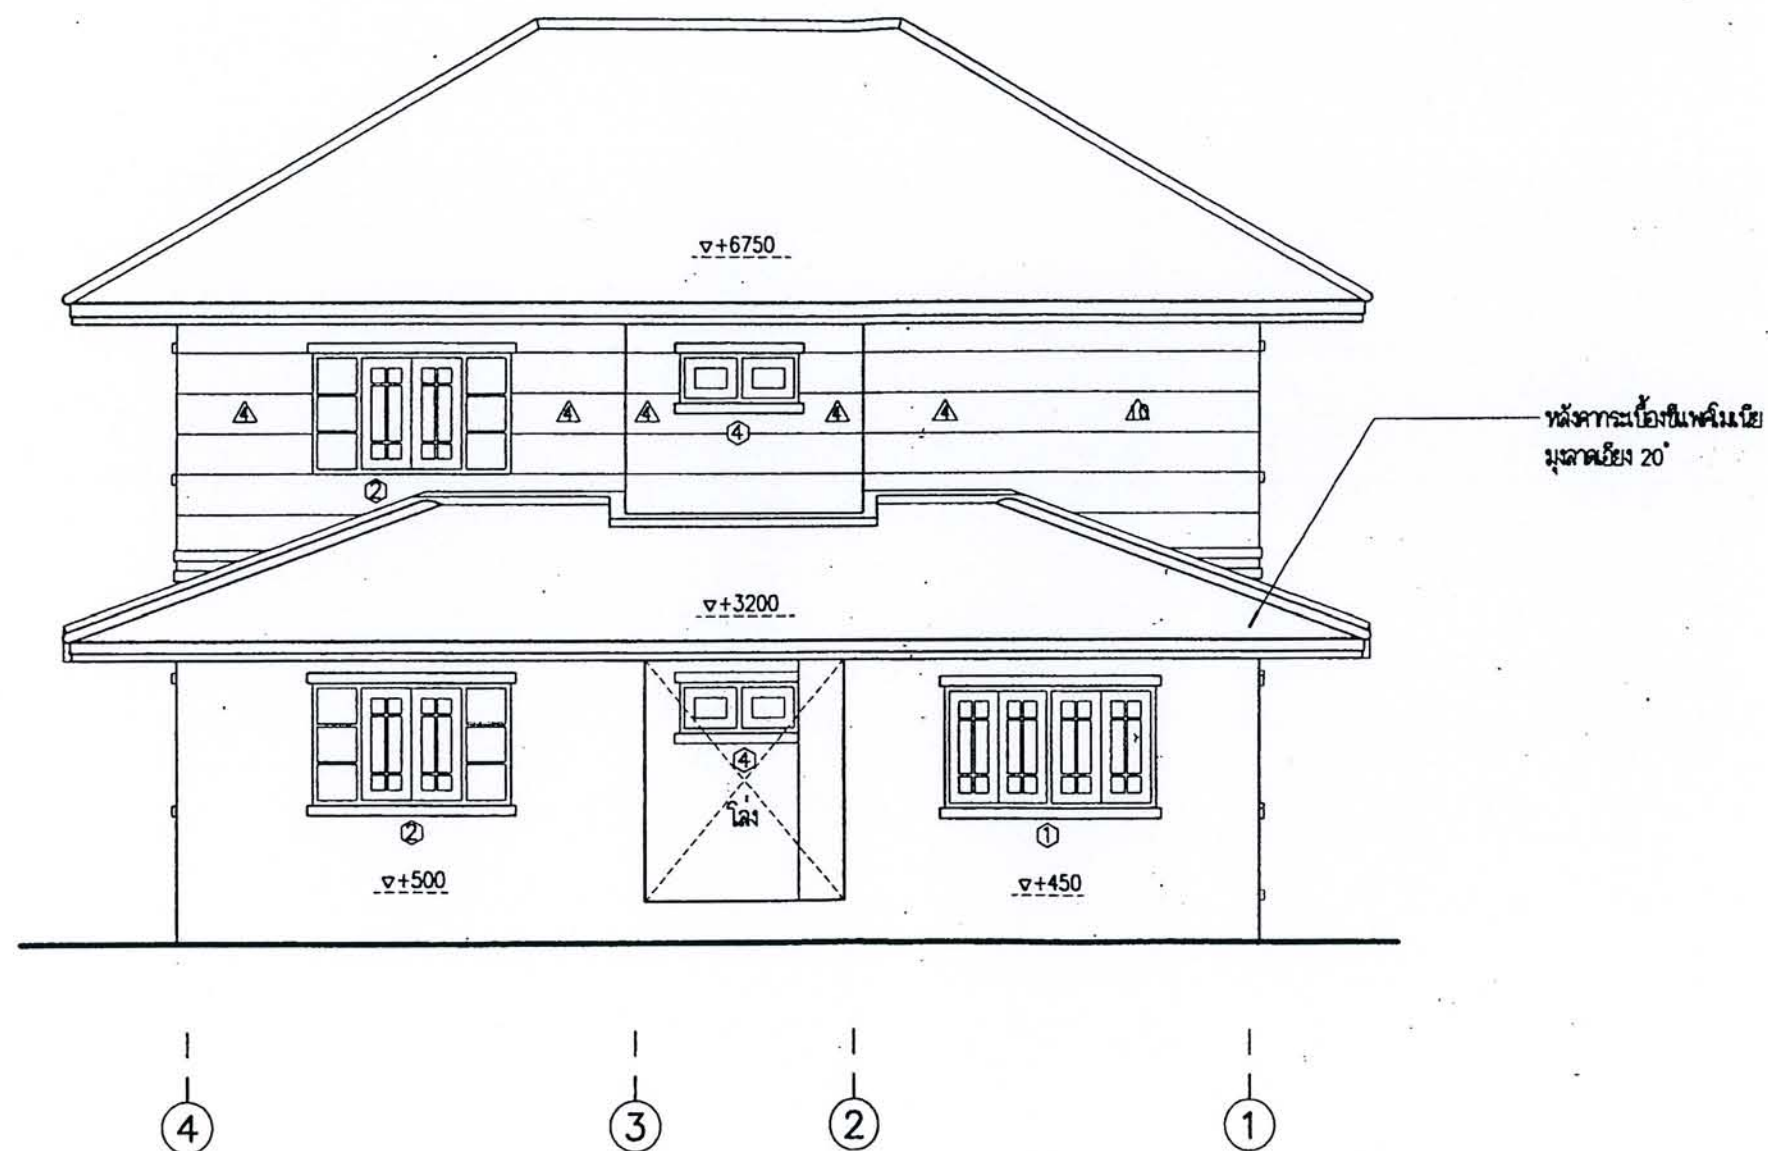

รูปด้าน
มาตรฐาน
1 : 75


ได้รับความอนุเคราะห์แบบ
จาก
บริษัท แลนด์ โฮม
(ประเทศไทย) จำกัด



โครงการ
แบบบ้านยืมเพื่อประชาชน

ตามนโยบาย
ม.ร.ว. สุขุมพันธุ์ บริพัตร
ผู้ว่าราชการกรุงเทพมหานคร

โดยสำนักงานโยธา
กรุงเทพมหานคร

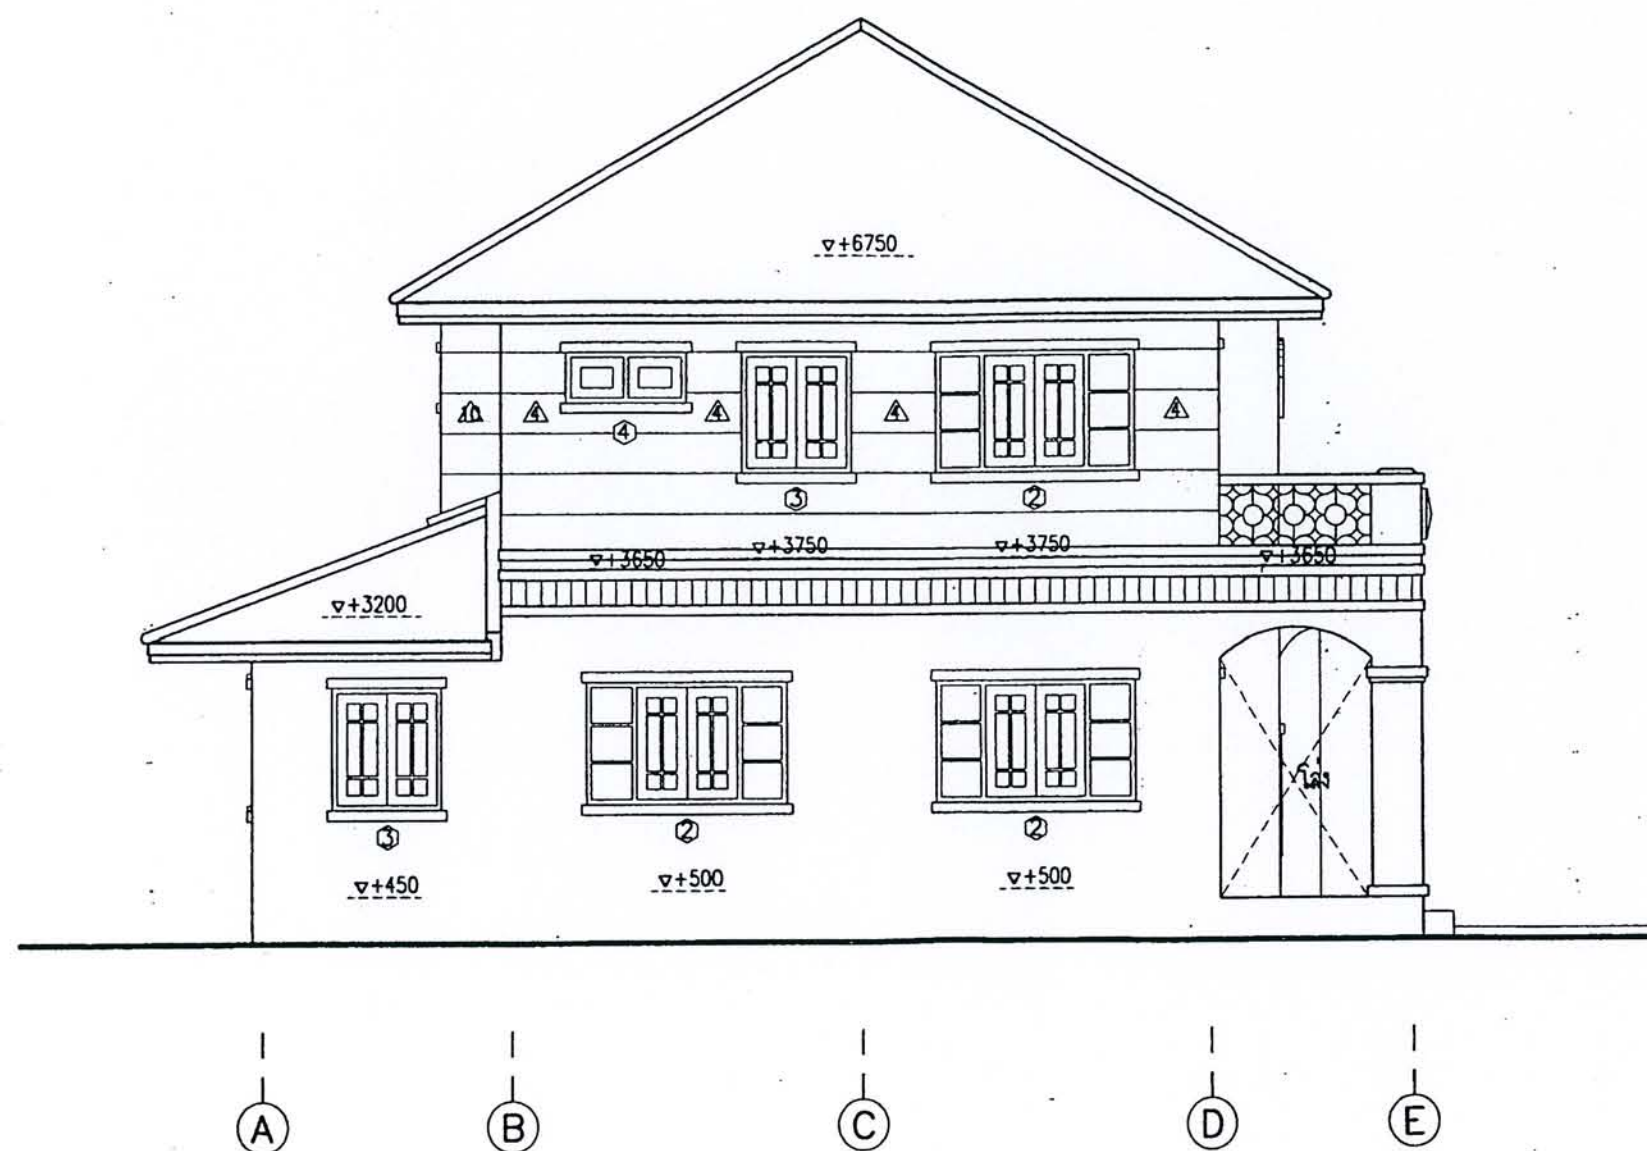

รูปด้าน
มาตราส่วน 1 : 75

ได้รับความอนุเคราะห์แบบ
จาก
บริษัท แลนด์ โยม
(ประเทศไทย) จำกัด

สัญลักษณ์ประกอบแบบ "S"



โครงการ
แบบบ้านยิ้มเพื่อประชาชน

ตามนโยบาย
ม.ร.ว. สุขุมพันธุ์ บริพัตร
ผู้ว่าราชการกรุงเทพมหานคร

โดยสำนักงานโยธา
กรุงเทพมหานคร

ได้รับความอนุเคราะห์แบบ
จาก
บริษัท แลนด์ โสม
(ประเทศไทย) จำกัด

รายการไฟฟ้า

สัญลักษณ์	ความหมาย	ขนาด - ยี่ห้อ - รุ่น
	แผงควบคุมไฟฟ้า	Square-D ขนาด 15 Amp. แบบกล่องเหล็กพร้อม circuit Breaker 7 ชุด
	โคมไฟฟ้า	ครอบแก้วกลม Ø 14" ผิวปูนหล่อดูลือลื่น 32 W. แบบกลมแสงสีขาว
	โคมไฟฟ้า	ครอบแก้วกลม Ø 8" หลอดทั้งหลอด 60 W. แสงสีเหลือง
	หลอดฟลูออโรลูเมน	รางหลอดฟลูออโรลูเมน ครอบหลอดเล็ก ขนาด 1 X 20 W. แสงสีขาว
	หลอดฟลูออโรลูเมน	รางหลอดฟลูออโรลูเมน ครอบหลอดเล็ก ขนาด 1 X 40 W. แสงสีขาว
	ไฟ โคมแขวนเพดาน	โคมไฟแก้วผิวปูน Ø 12" หลอดธรรมดา 60 W.
	ไฟตั้งโต๊ะ	โคมไฟหลอด 60 W. พกหิ้ว
	สวิทช์ไฟฟ้า	Single way ชนิดมีเงินนํ้าของ NATIONAL (ช่องแท้) ติดตั้งสูงจากพื้น 1200 มม.
	สวิทช์ไฟฟ้า 2 ทาง	Two way ชนิดมีเงินนํ้าของ NATIONAL (ช่องแท้) ติดตั้งสูงจากพื้น 1200 มม.
	ปลั๊กไฟ , เต้าเสียบ	ปลั๊กไฟแบบเรียบชนิดมีเงินนํ้าแบบ 2 เต้าเสียบต่อ 1 ชุด พร้อมสายดินตาม-
		การไฟฟ้า ติดตั้งสูงจากพื้น 200 มม. ของ NATIONAL (ช่องแท้) ติดห่างจากผนัง
		100 มม.
	ปลั๊กไฟ , เต้าเสียบ	ปลั๊กไฟแบบเรียบชนิดมีเงินนํ้าแบบ 2 เต้าเสียบต่อ 1 ชุด พร้อมสายดินตาม-
		การไฟฟ้า ติดตั้งสูงจากพื้น 1000 มม. ของ NATIONAL (ช่องแท้) ติดห่างจากผนัง
		100 มม.
	ปลั๊กสายอากาศ TV.	ใช้สายอากาศ TV.RG-6 โดยเดินสายไปยังห้องนอนที่ติดตั้งแล้วที่ปลายปลั๊กไว้ 1 ม.
	โทรทัศน์	เดินสายตามมาตรฐานไฟฟ้า โดยเดินสายไปยังห้องนอนที่ติดตั้งแล้วที่ปลายปลั๊กไว้ 1 ม.
	สวิทช์แอร์	ตามท่วงตามแบบ
	แสดงการเดินสายไฟแบบ-	สายไฟใช้สาย PVC. ของ YAZAKI หรือ BANGKOK CABLE
	เดินลอย	เดินลอยยึดด้วยสายรัดเข็มขัดระยะห่าง 100 มม. โดย
		- สายไฟสำหรับ สวิทช์ไฟ ที่ใช้ใช้ ขนาด 1.0 มม. ²
		- สายไฟสำหรับ ปลั๊กไฟ ที่ใช้ใช้ ขนาด 2.5 มม. ² (แบบมีสายดิน)
		- สายไฟสำหรับ แอร์ ที่ใช้ใช้ ขนาด 10.0 มม. ²
		- สายไฟสำหรับ เครื่องทำน้ำร้อน ที่ใช้ใช้ ขนาด 10.0 มม. ²
		- สำหรับสายเมนใช้สาย PVC. ของ YAZAKI หรือ BANGKOK CABLE
		ขนาด 16.00 มม. ² ต่อห่างจากชายคาน้ำฝน 16000 มม.

- หมายเหตุ :
- ให้เดินสายดินตามระเบียบของการไฟฟ้าอย่างถูกต้อง
 - ราคากำหนด 3,000,000 บาท ใช้ไฟ ขนาด 30 Amp. 2 สายของ Square-D พร้อมสายเมน
 - แบบดูเซอร์กิต 16 ช่อง
 - ราคากำหนด 5,000,000 บาท ใช้ไฟ ขนาด 50 Amp. 2 สายของ Square-D พร้อมสายเมน

รายการเปลี่ยนแปลงเพิ่มเติมไฟฟ้า

* ไม่มีรายการเปลี่ยนแปลง

บ้าน SMILE HOME
V.1 [11/2/45]

สัญลักษณ์ประกอบแบบ "S"



รายการสัญลักษณ์

สัญลักษณ์	ความหมาย	ขนาด และ จำนวนอุปกรณ์ที่ใช้
	ท่อ PVC	ท่อ PVC. Ø 4" ขึ้นคุณภาพ Class 8.5 ติดตั้งให้มีความลาดเอียง 1 : 200 ปลายท่อ-ให้ต่อแบบ 3 ทาง ตัว T
	ท่อน้ำทิ้ง	(ท่อเมน) ท่อ PVC. Ø 2" ขึ้นคุณภาพ Class 8.5 ติดตั้งให้มีความลาดเอียง 1 : 200 ให้ท่อน้ำทิ้งไหลได้สะดวก
	ท่อน้ำทิ้ง	(ต่อจากสัญลักษณ์) ท่อ PVC. Ø 1 1/2" ขึ้นคุณภาพ Class 8.5
	ท่อน้ำดี	(ท่อน้ำประปา) ท่อ PVC. Ø 1/2" ขึ้นคุณภาพ Class 13.5
	ท่อน้ำเย็น	(ท่อเมน) ท่อ PVC. Ø 3/4" ขึ้นคุณภาพ Class 13.5
	ท่อน้ำร้อน	ใช้ท่อเหล็กกล้าไร้สนิม Class B Ø 1/2"
	ท่อระบายอากาศ	ท่อ PVC Ø 1" ขึ้นคุณภาพ Class 8.5 ปลายท่อด้วยข้อต่อ 3 ทาง ตัว T ท่อระบายอากาศสูงจากพื้น 3500 มม. ยึดติดกับผนังหรือล้อยึดระยะห่าง 300 มม.
	ท่อระบายน้ำเสีย	ท่อขึ้นแบบโพลิเอทิลีน Ø 150 มม. ติดตั้งให้มีความลาดเอียง 1 : 200 ข้อต่อรับแรงทอนกับ-ข้อต่อให้ท่อยันเข้าในข้อต่ออย่างน้อย 50 มม.
	จุดระบายน้ำทิ้ง	ตำแหน่งที่จุดระบายน้ำทิ้งจะลงซึ่งต้องท่อเมนน้ำทิ้งมีแผ่นเหล็กตะแกรงชักล้น
	จุดระบายน้ำทิ้ง	ตำแหน่งจุดน้ำทิ้งจากชักโครก
	บ่อพัก	บ่อพักน้ำเสียสำเร็จรูป ขนาด 300X400X400 มม. พร้อมฝาปิดทึบระยะ 6.00 ม. ทุกช่วงพักเสีย
	จุดจ่ายน้ำประปา	จุดจ่ายน้ำดี (ประปา) ที่ต้องสูงให้ได้ตามแบบ
	บ่อกรอง	ใช้ระบบบำบัดน้ำเสีย ถึงบำบัดน้ำเสียสำเร็จรูป ของ AQUA-PAC หรือเทียบเท่า
	มิเตอร์น้ำ	ตามมาตรฐานของการประปา
	เครื่องปั๊มน้ำ	ตำแหน่งตามแบบ
	แนวลาดเอียง	ลาดเอียงตามแบบ

- หมายเหตุ :**
- ท่อ PVC. ที่ข้อต่อทุกจุดจะต้องทากาวก่อนต่อ เมื่อต่อท่อเสร็จเรียบร้อยแล้วน้ำจะซึมไม่รั่วซึม
 - ท่อน้ำดีจะต้องขุดดินให้ลึกพอที่จะฝังท่อเมนน้ำดีและบิรณรยต่อระหว่างท่อ PVC. เข้ากับข้อต่อเหล็กจะต้องพันทาก่อนต่อ เมื่อต่อท่อเสร็จเรียบร้อยแล้วน้ำจะซึมไม่รั่วซึม
 - ท่อประปา (น้ำร้อน) ที่ต่อกับสายอ่อนให้ใช้ข้อต่อกลึงทุกจุด
 - ท่อระบายน้ำและบ่อพักต้องจากตัวอาคาร ถึงบ่อพักอาคารละไม่เกิน 16.00 ม.

รายการประกอบแบบสัญลักษณ์ TYPE "S"

อ่างอาบน้ำ (ถัง)	CRISTINA (TEENA-D) CT-5013 C พร้อมเดินสายไฟฟ้า และ ท่อน้ำร้อนของเครื่องทำน้ำร้อน 1 ชุด (ไม่รวมเครื่องทำน้ำร้อน) ก๊อกผสมน้ำ JAZZ STD. A 7601 (AMERICAN STANDARD)
อ่างล้างหน้า	AMERICAN STANDARD รุ่น TF-476 ชนิดฝังคานเตอร์ , ก๊อกน้ำ JAZZ STD. A 7000 พร้อมอุปกรณ์ชักล้น
ก๊อกอาบน้ำ	ใช้แบบ BALL VALVE (หัวปั๊)
โถล้างนั่งราบ	AMERICAN STANDARD รุ่น TF-2310 (หัวปั๊) , ลายซาร์ HANG 5502 , รุ่น TF-2310 (คนใช้)
ฝักบัวสายอ่อน	JAZZ STD. A 7003 A (AMERICAN STANDARD)
ที่วางสบู่	AMERICAN STANDARD รุ่น TF-9000
ที่ใส่กระดาษชำระ	AMERICAN STANDARD รุ่น TF-9001
ราวนานชัก	AMERICAN STANDARD รุ่น TF-9085
กระจกเงา	กระจกเงาเรียบเรียบ ยึดด้วยหมุด
สีลู่วินท์	หัวปั๊แบบทาสี BEIGE ยาววันห้องน้ำคนใช้ ใช้สีขาว

รายการประกอบแบบสัญลักษณ์ กรณีมีการเปลี่ยนแปลงเพิ่มเติม

* ไม่มีรายการเปลี่ยนแปลง

รายการเปลี่ยนแปลงเพิ่มเติมสัญลักษณ์

* ไม่มีรายการเปลี่ยนแปลง

บ้าน SMILE HOME
V.1 [11/2/45]

ได้รับความอนุเคราะห์แบบ
จาก
บริษัท แลนด์ โฮม
(ประเทศไทย) จำกัด

ได้รับความอนุเคราะห์แบบ
จาก
บริษัท แลนด์ โฮม
(ประเทศไทย) จำกัด


ได้รับความอนุเคราะห์แบบ
จาก
บริษัท แลนด์ โสม
(ประเทศไทย) จำกัด



โครงการ
แบบบ้านยืมเพื่อประชาชน

ตามนโยบาย
ม.ร.ว. สุขุมพันธุ์ บริพัตร
ผู้ว่าราชการกรุงเทพมหานคร

โดยสำนักงานโยธา
กรุงเทพมหานคร

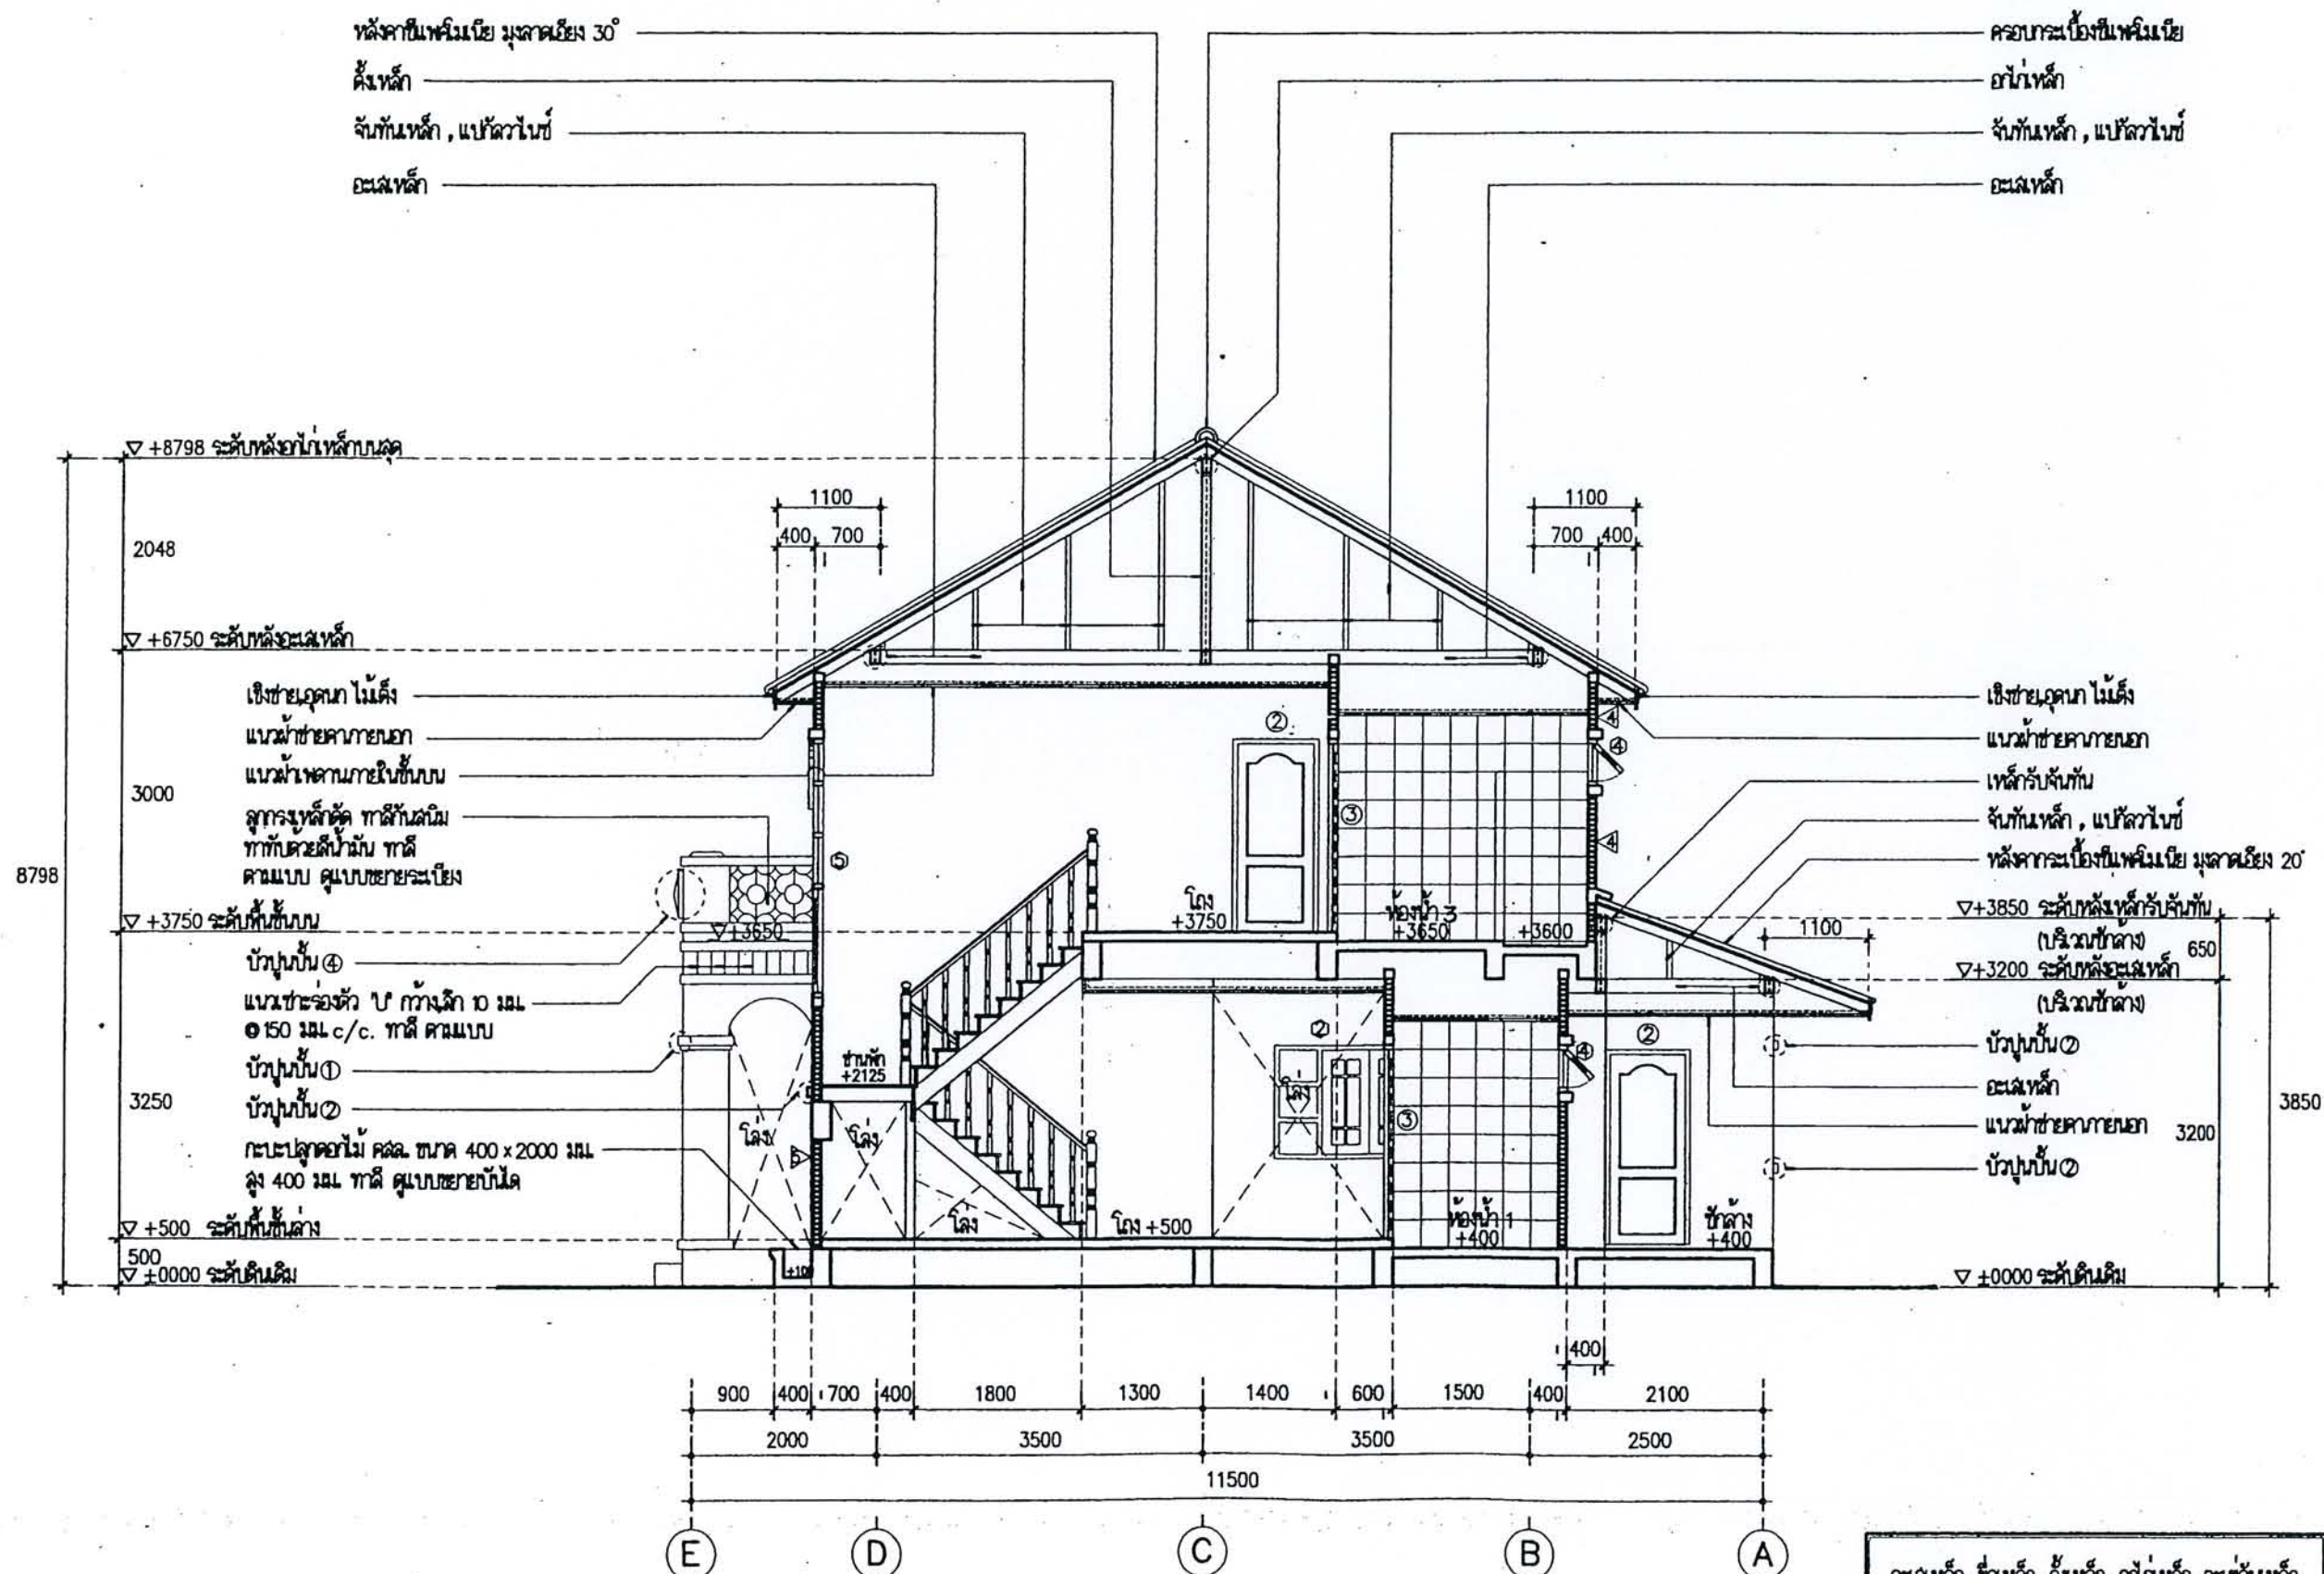


รูปตัด B-B


มาตราส่วน 1 : 75

อะไหล่หลังคา, ฝ้าหลังคา, ค้ำหลังคา, อน้ำหลังคา, อะไหล่หลังคา,
ค้ำหลังคา, จันทันหลังคา, แป้นคิ้วไม้, เชิงชายไม้ค้ำ,
อุดหน้าไม้ คสล. คูแบบขยายระยะยิง


ได้รับความอนุเคราะห์แบบ
จาก
บริษัท แลนด์ โสม
(ประเทศไทย) จำกัด

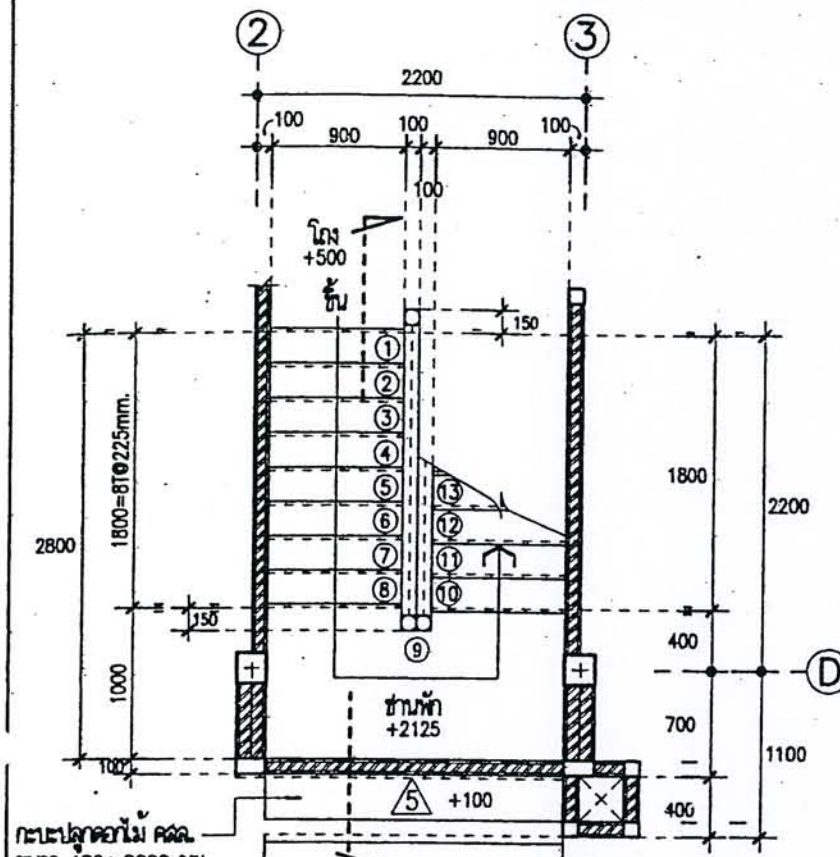

มาตรา ๖๖ 1:50

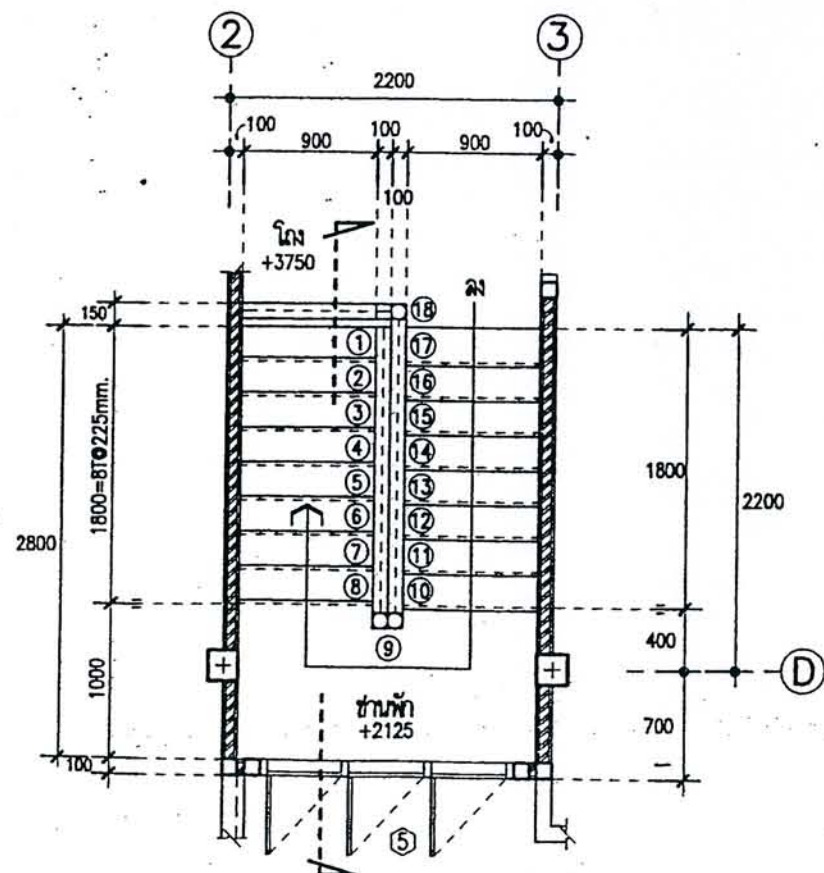

ภาคเช้า 1:50

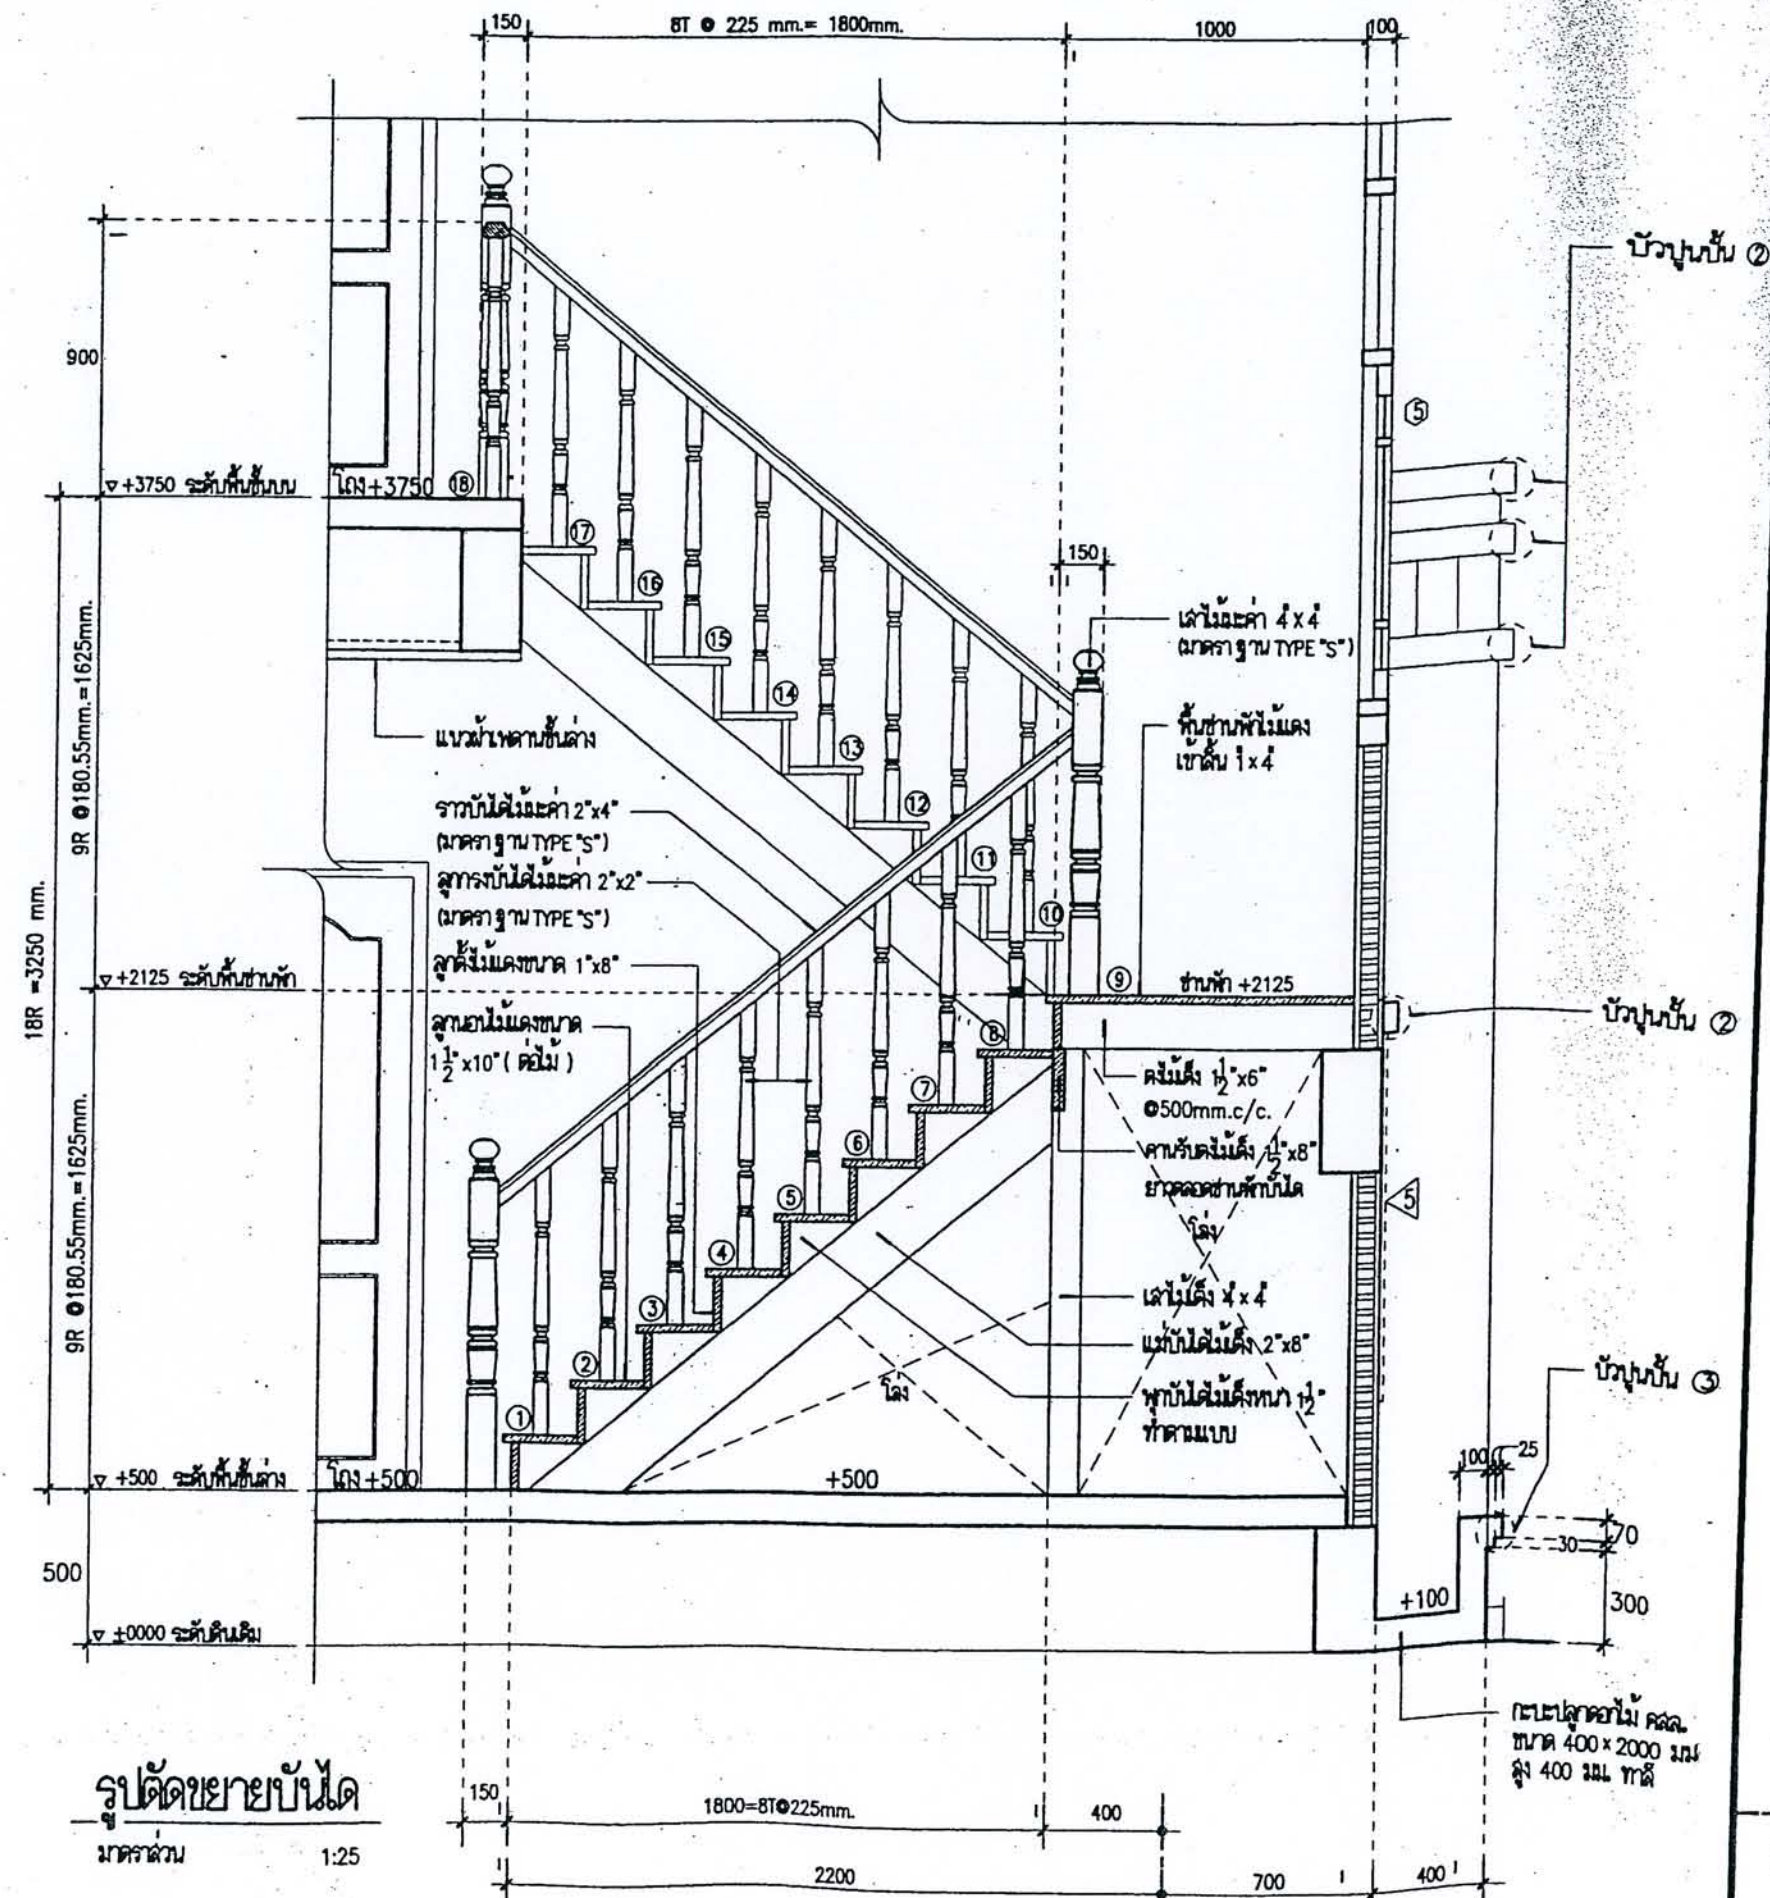






มาตราส่วน 1:25



โครงการ
แบบบ้านยืมเพื่อประชาชน

ตามนโยบาย
ม.ร.ว. สุขุมพันธุ์ บริพัตร
ผู้ว่าราชการกรุงเทพมหานคร

โดยสำนักงานโยธา
กรุงเทพมหานคร

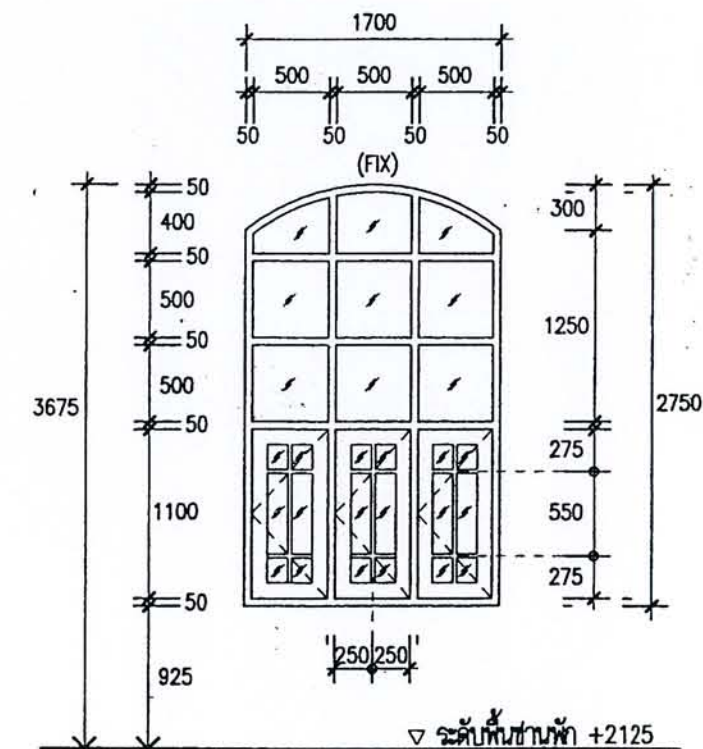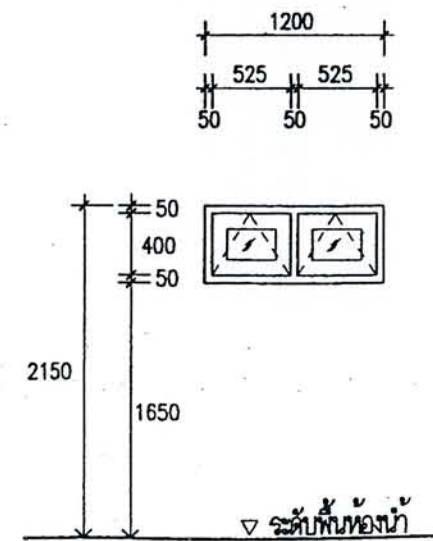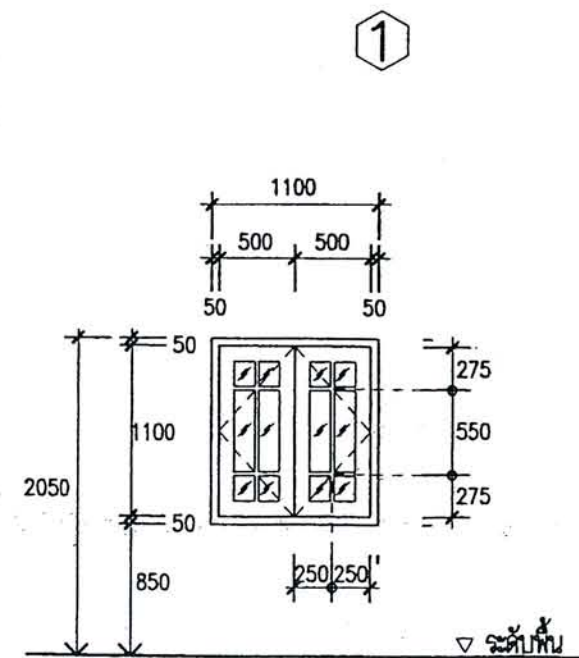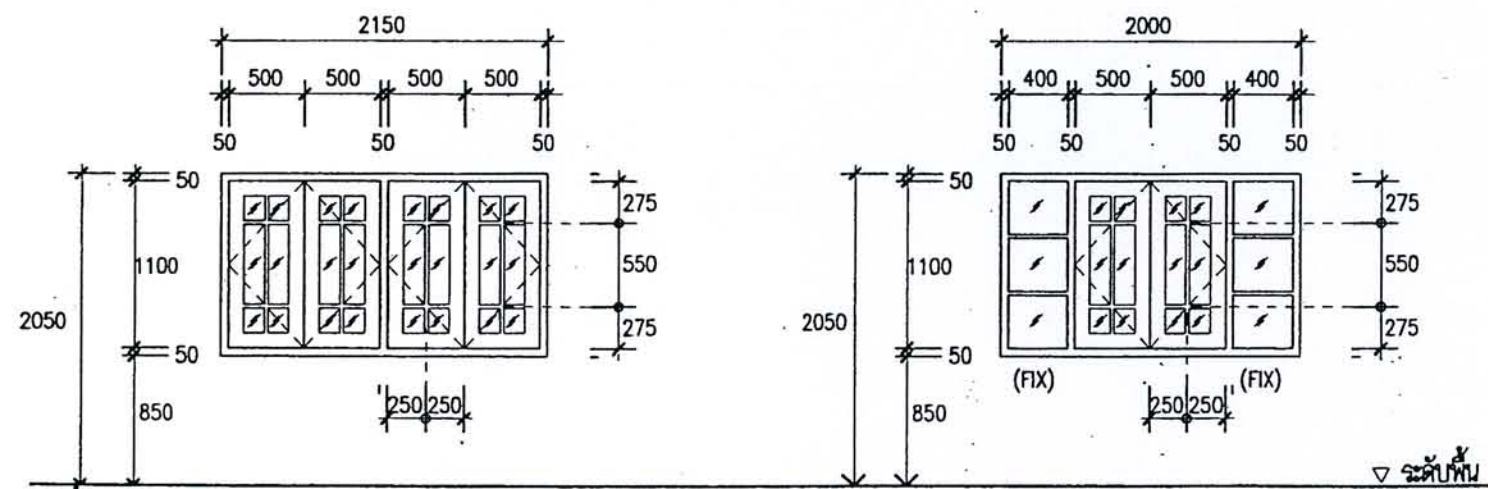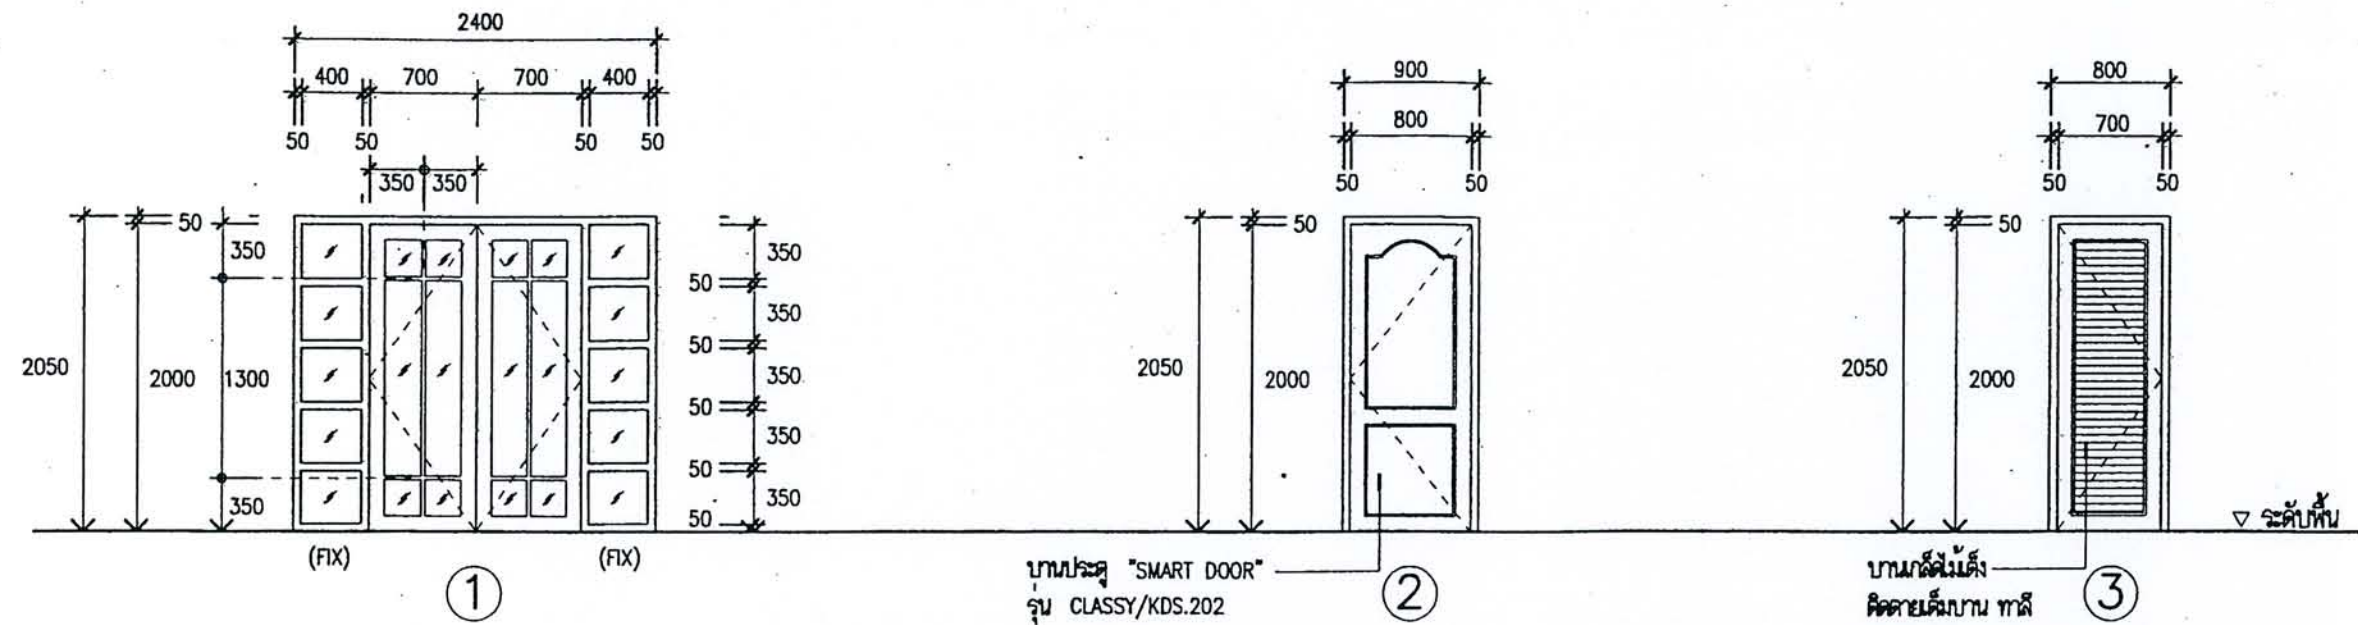

แบบขยายประตู - หน้าต่าง
มาตราส่วน 1 : 50


ได้รับความอนุเคราะห์แบบ
จาก
บริษัท แลนด์ โสภ
(ประเทศไทย) จำกัด



โครงการ
แบบบ้านยืมเพื่อประชาชน

ตามนโยบาย
ม.ร.ว. สุขุมพันธุ์ บริพัตร
ผู้ว่าราชการกรุงเทพมหานคร

โดยสำนักงานโยธา
กรุงเทพมหานคร

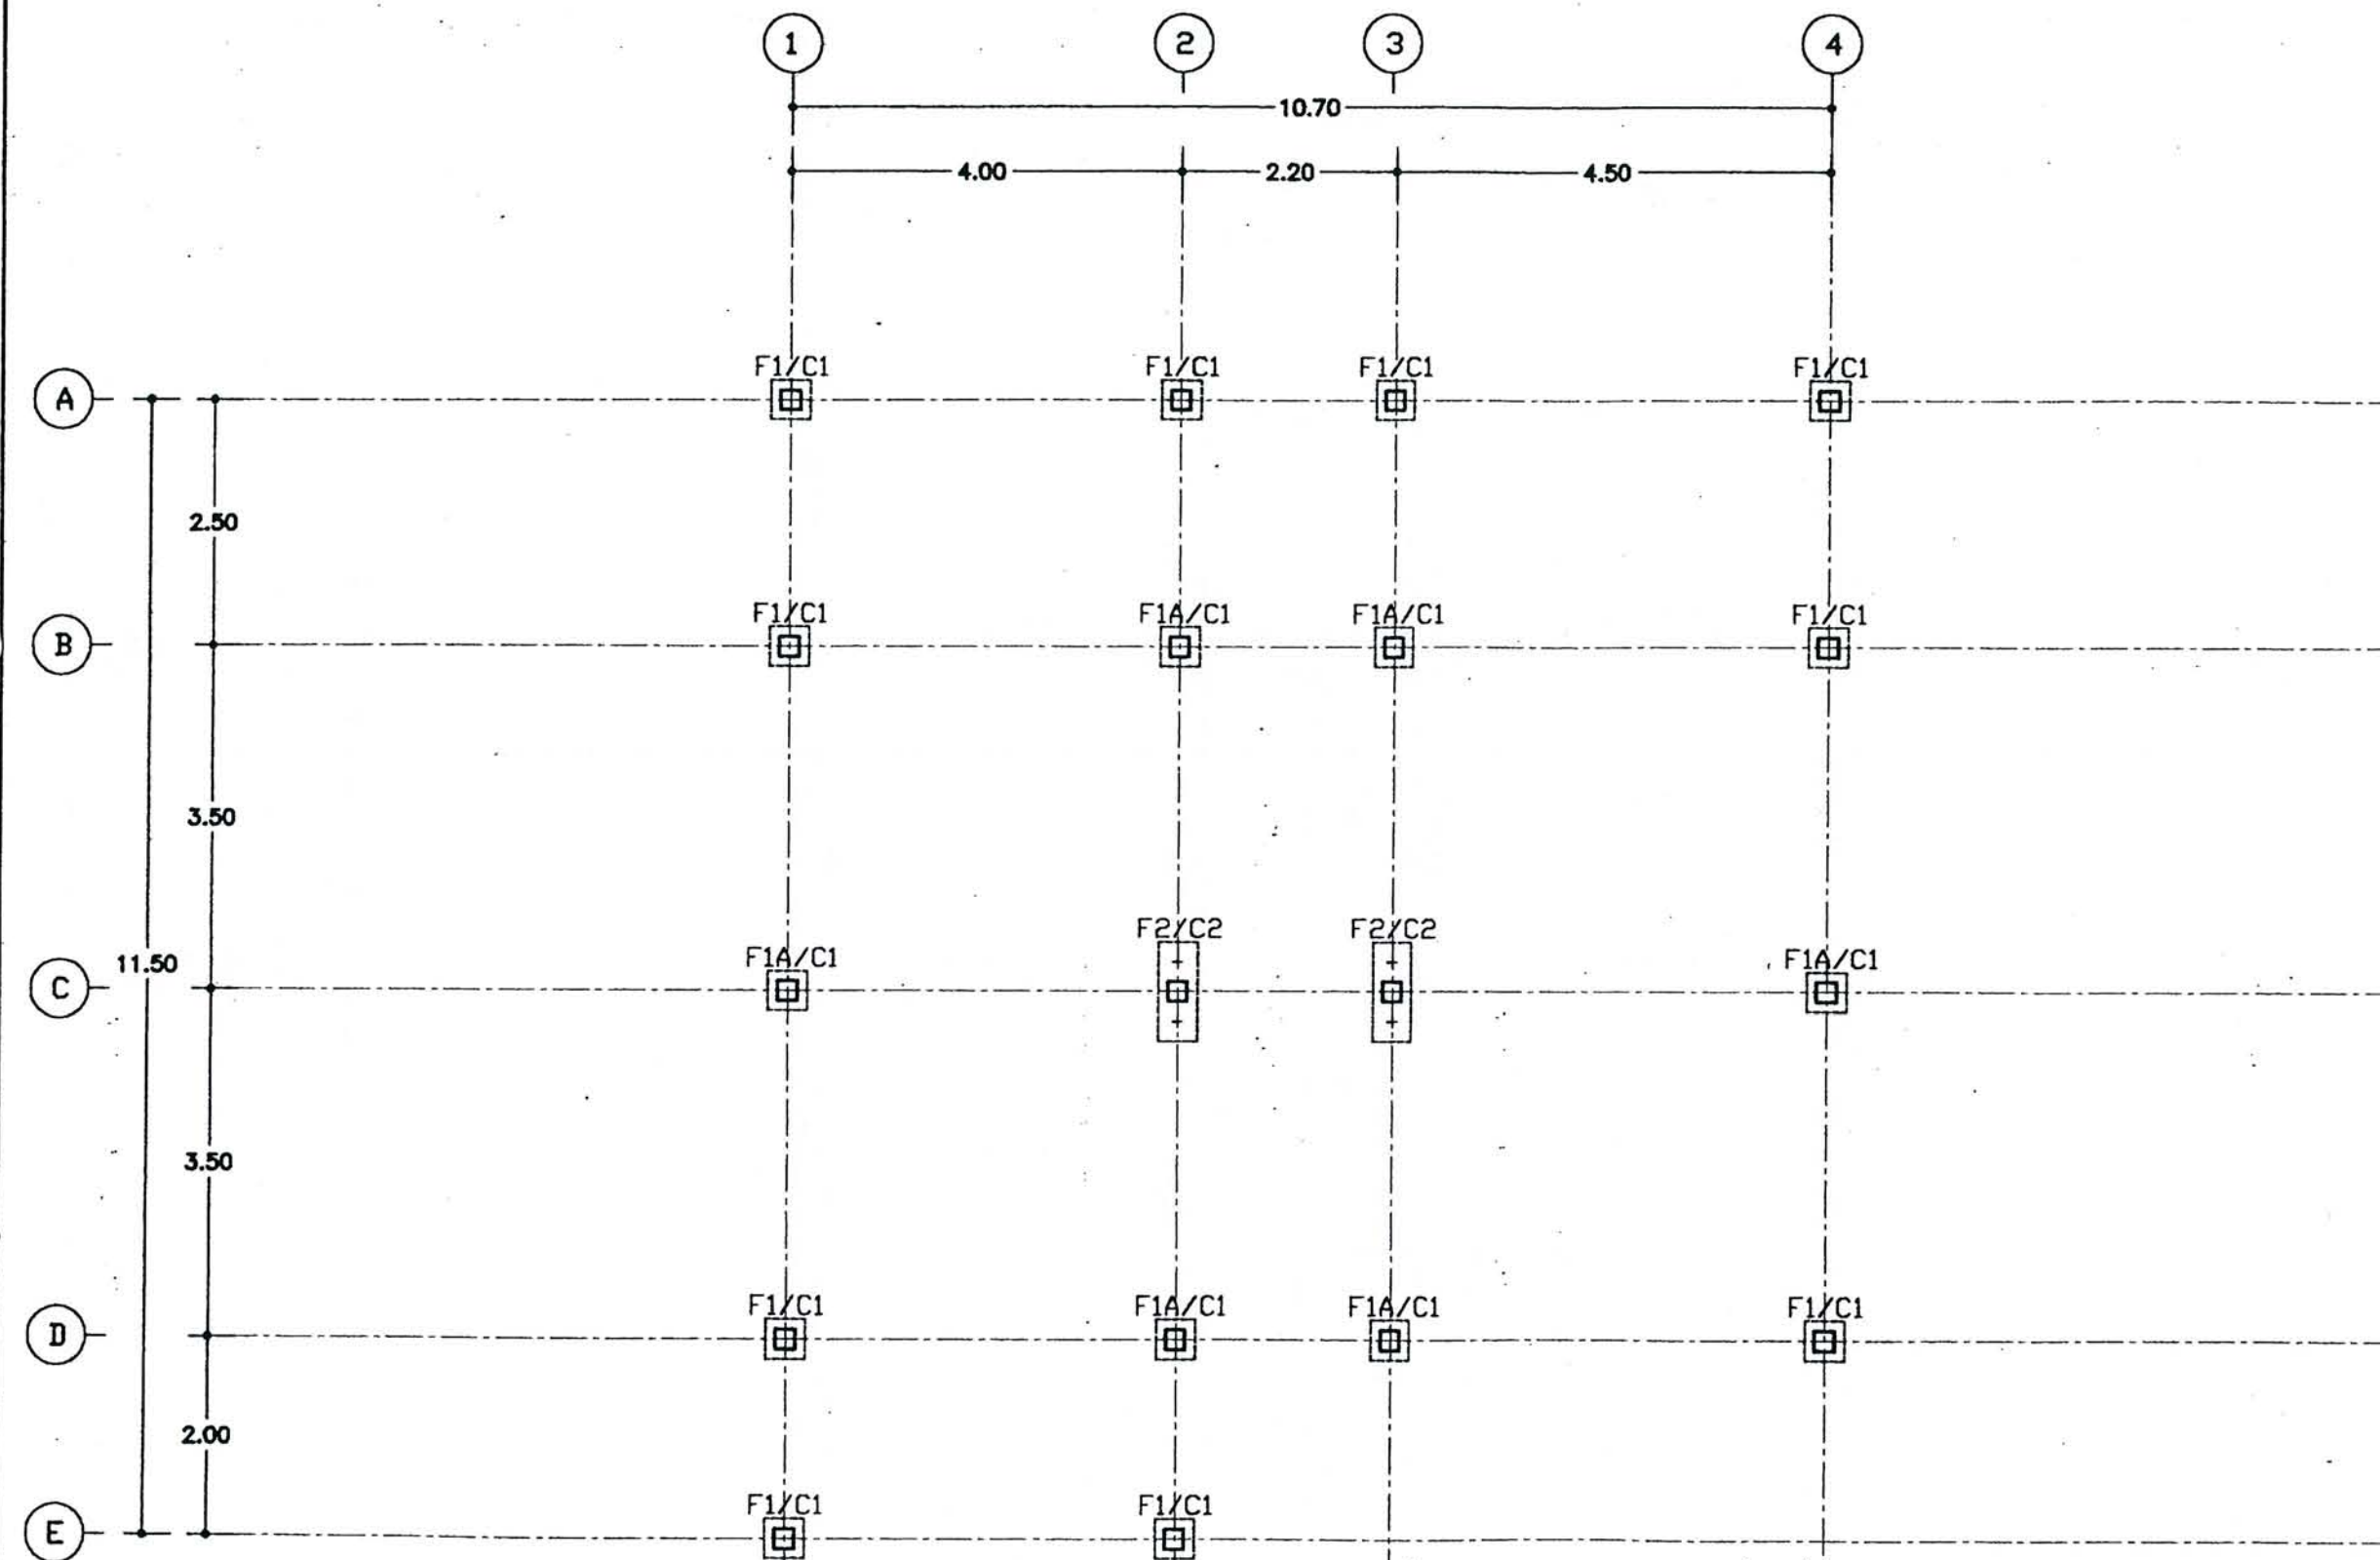

หมายเหตุ เข็ม I 0.18x0.18x16.00m. (2 ต้น ต่อปลอก) จำนวน = 14 ต้น

F1 = 10 หลุม = 10 ต้น

F2 = 2 หลุม = 4 ต้น

เข็ม I 0.22x0.22x16.00m. (2 ต้น ต่อปลอก) F1A = 6 หลุม = 6 ต้น

ผังโครงสร้างฐานราก
มาตราส่วน 1:75


ได้รับความอนุเคราะห์แบบ
จาก
บริษัท แลนด์ โฮม
(ประเทศไทย) จำกัด



โครงการ
แบบบ้านยืมเพื่อประชาชน

ตามนโยบาย
ม.ร.ว. สุขุมพันธุ์ บริพัตร
ผู้ว่าราชการกรุงเทพมหานคร

โดยสำนักงานโยธา
กรุงเทพมหานคร

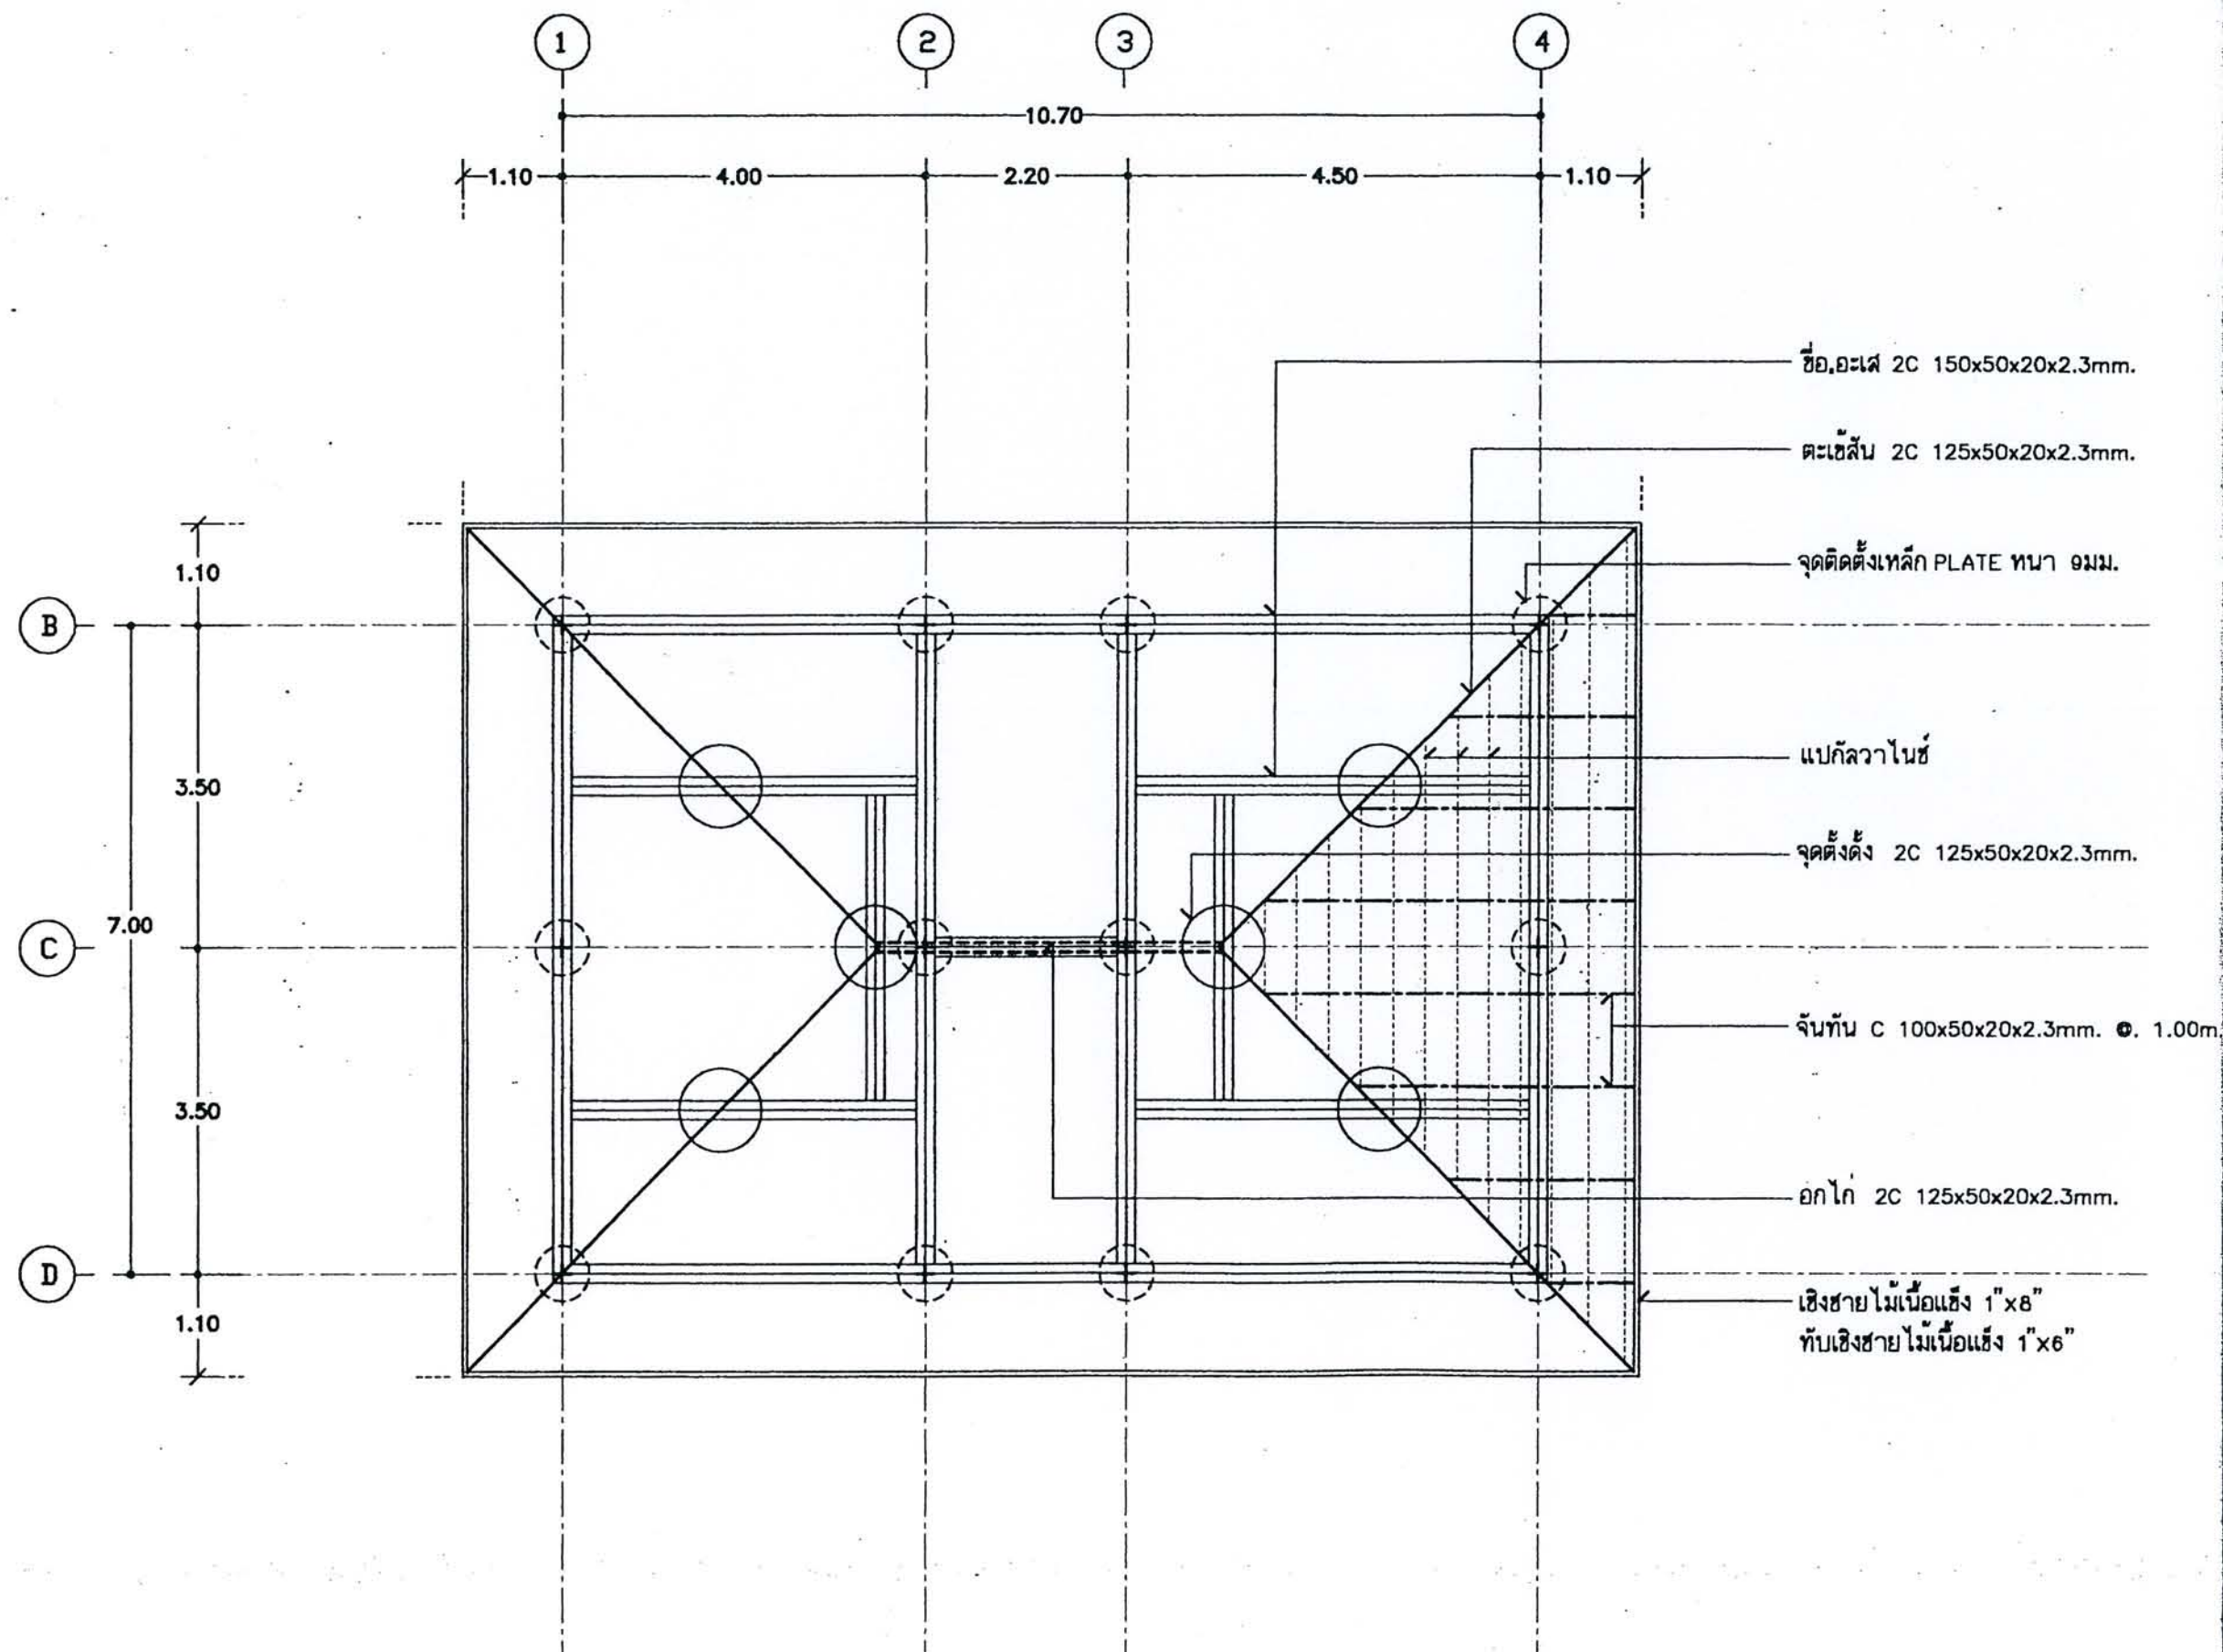

ผังโครงสร้างหลังคา

มาตราส่วน 1:75

ได้รับความอนุเคราะห์แบบ


จาก
บริษัท แลนด์ โสม
(ประเทศไทย) จำกัด




โครงการ
แบบบ้านยืมเพื่อประชาชน

ตามนโยบาย
ม.ร.ว. สุขุมพันธุ์ บริพัตร
ผู้ว่าราชการกรุงเทพมหานคร


โดยสำนักงานโยธา
กรุงเทพมหานคร

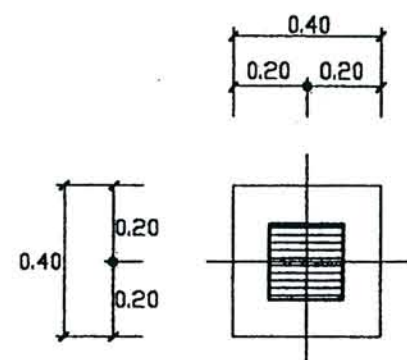


PLAN F1A

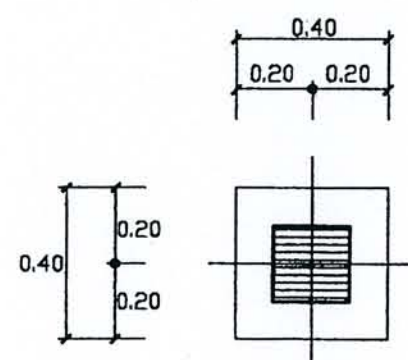


PLAN F1

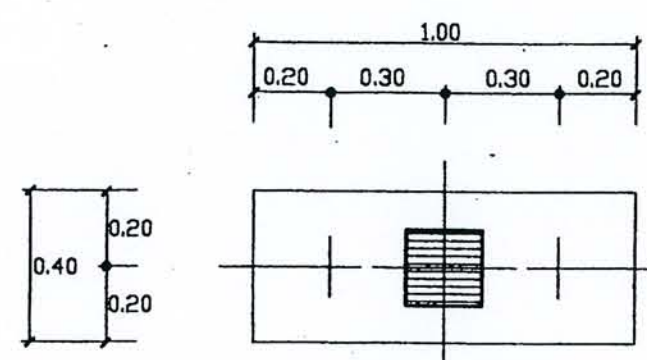


PLAN F2

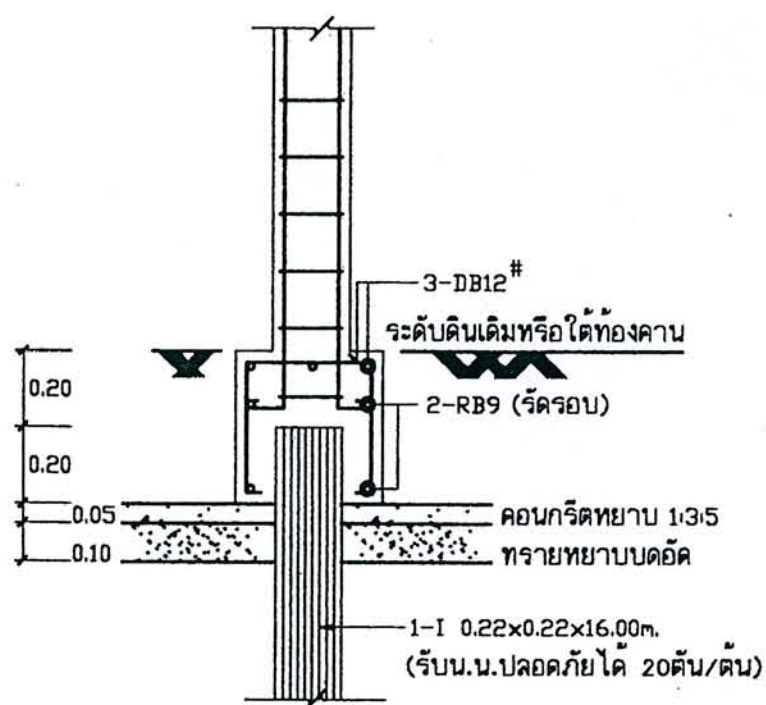

SECTION F1A 1:20

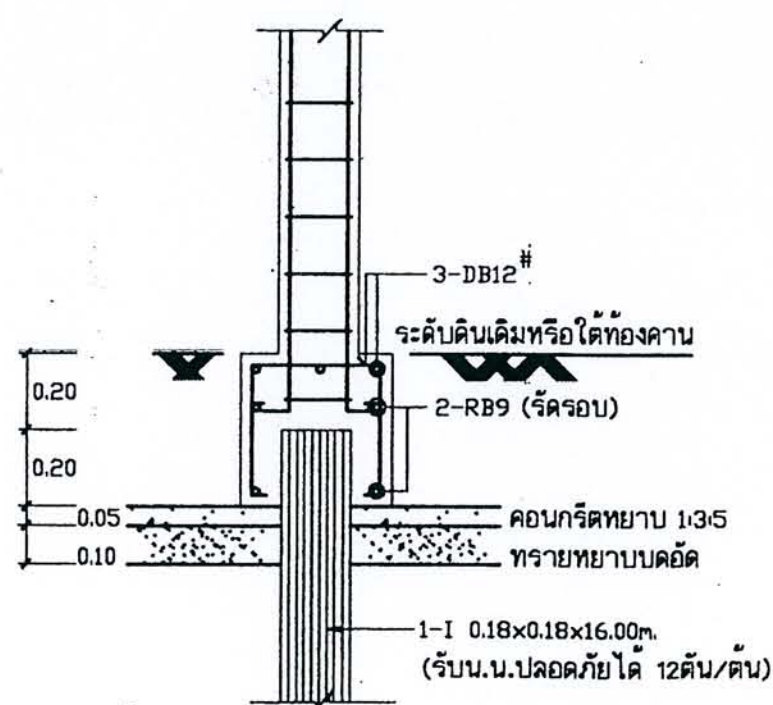

SECTION F1 1:20

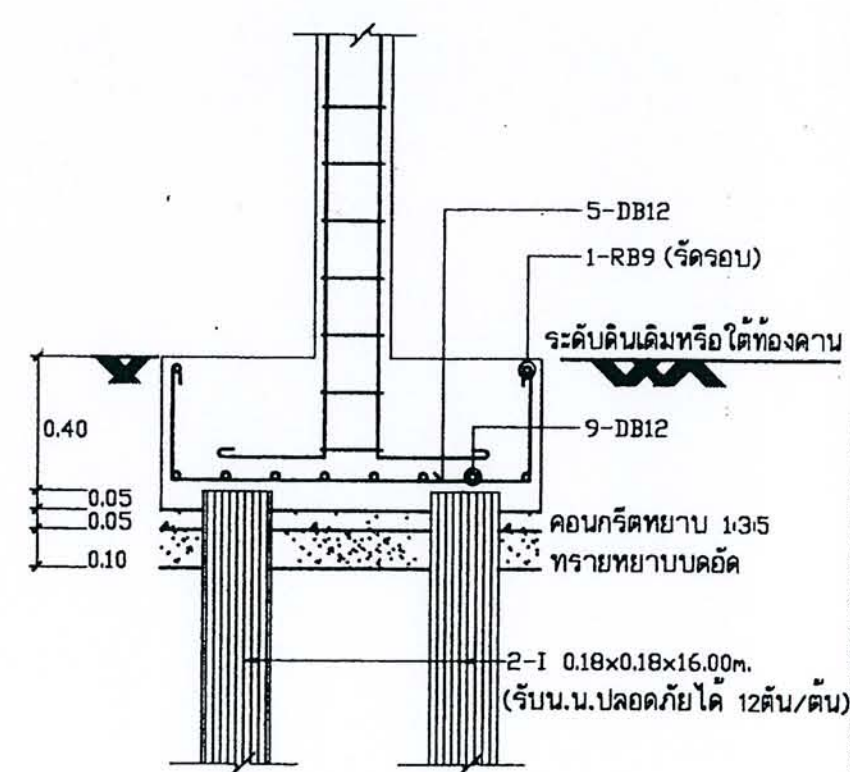

SECTION F2 1:20


ได้รับความอนุเคราะห์แบบ
จาก
บริษัท แลนด์ โสม
(ประเทศไทย) จำกัด




โครงการ
แบบบ้านยืมเพื่อประชาชน

ตามนโยบาย
ม.ร.ว. สุขุมพันธุ์ บริพัตร
ผู้ว่าราชการกรุงเทพมหานคร

โดยสำนักงานโยธา
กรุงเทพมหานคร

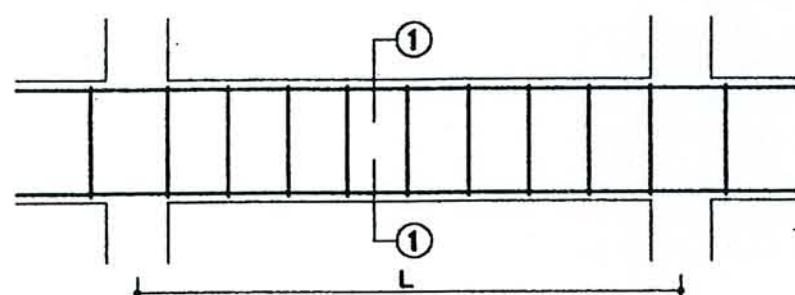


LONG SECTION

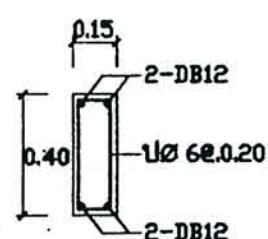


SECTION 1-1

B1

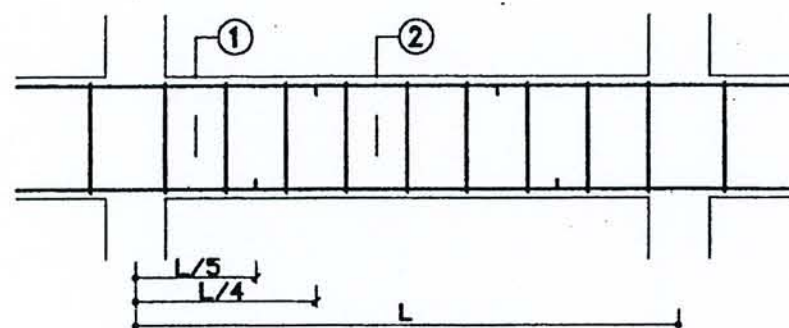


LONG SECTION

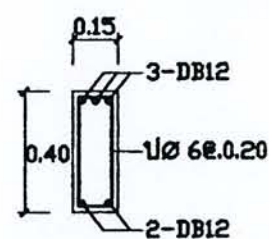


SECTION 1-1


B2

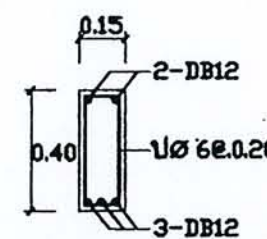

SECTION 2-2

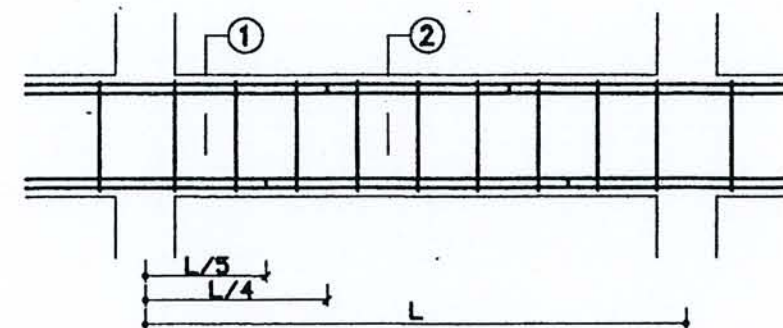


LONG SECTION

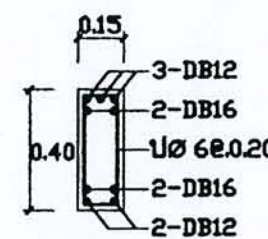


SECTION 1-1


B6

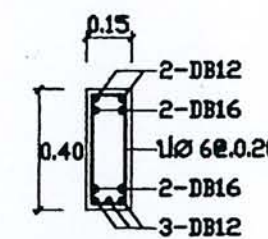

SECTION 2-2

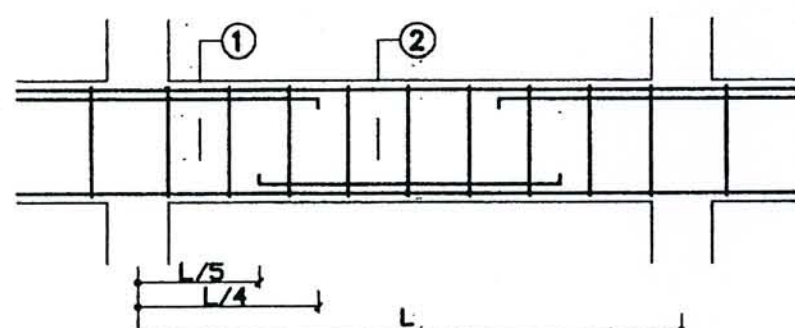


LONG SECTION

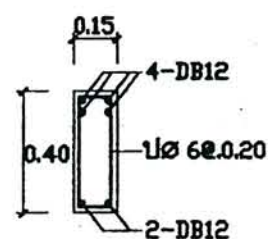


SECTION 1-1


B3

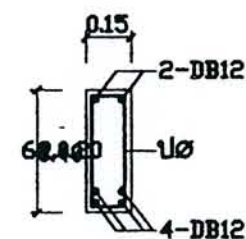

SECTION 2-2

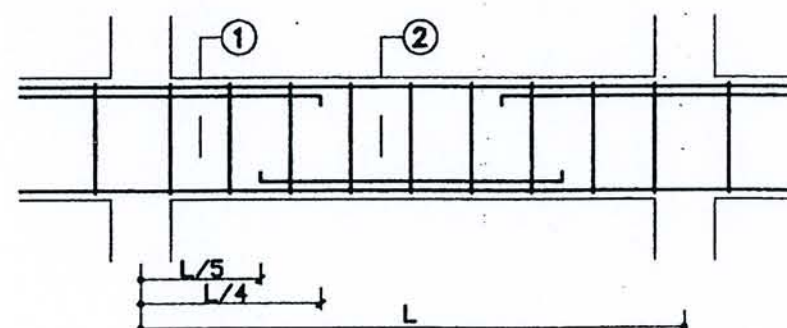


LONG SECTION

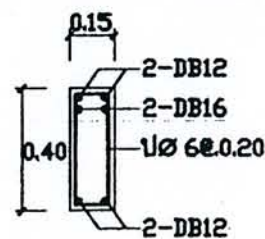


SECTION 1-1

B4

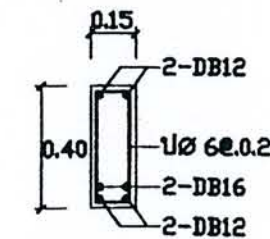

SECTION 2-2

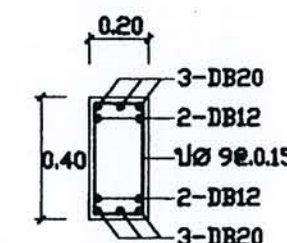

B10A

ได้รับความอนุเคราะห์แบบ
จาก
บริษัท แลนด์ โสม
(ประเทศไทย) จำกัด





โครงการ
แบบบ้านยืมเพื่อประชาชน

ตามนโยบาย
ม.ร.ว. สุขุมพันธุ์ บริพัตร
ผู้ว่าราชการกรุงเทพมหานคร


โดยสำนักงานโยธา
กรุงเทพมหานคร

ได้รับความอนุเคราะห์แบบ
จาก
บริษัท แลนด์ โสม
(ประเทศไทย) จำกัด

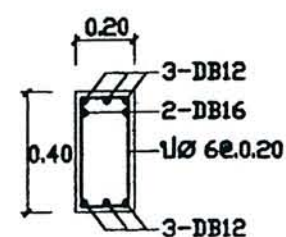
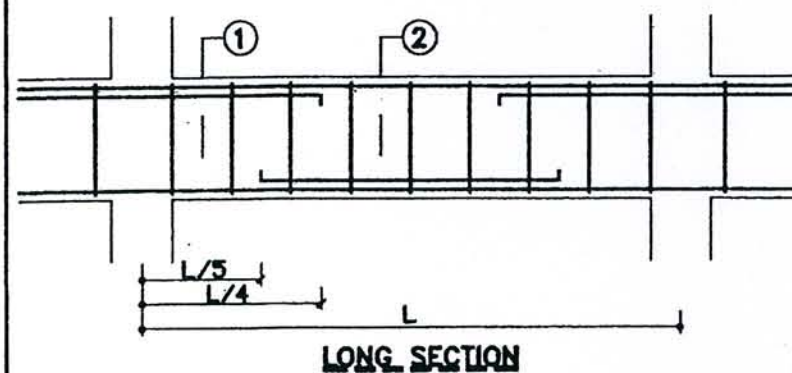


SECTION 1-1

(B5A)

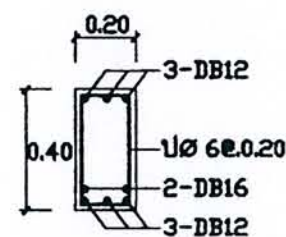


SECTION 2-2

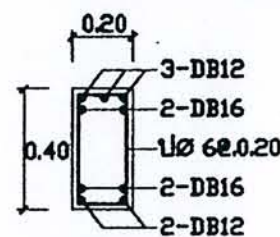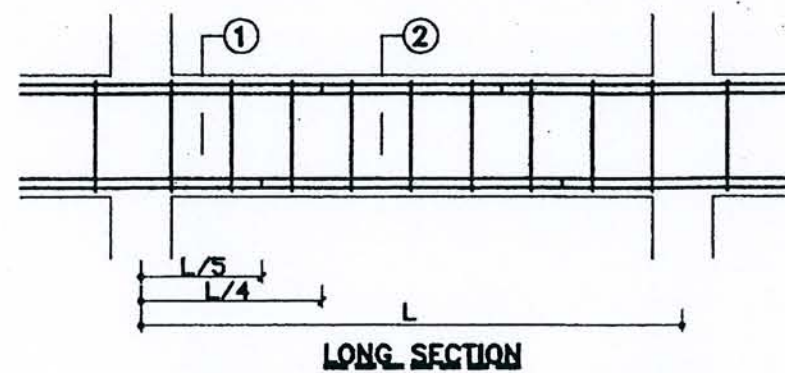


SECTION 1-1



(B6A)

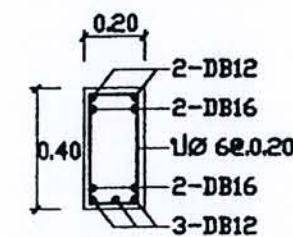

SECTION 2-2

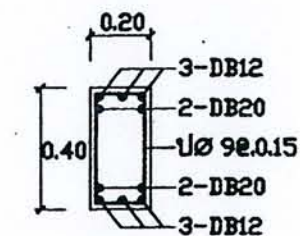


(B8A)

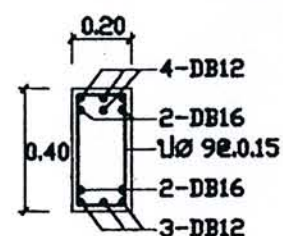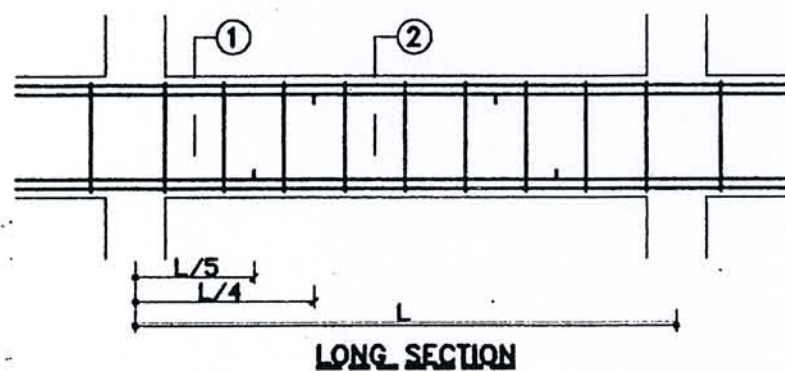


SECTION 1-1

(B7A)

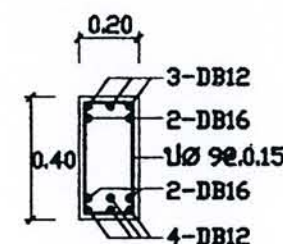


SECTION 2-2

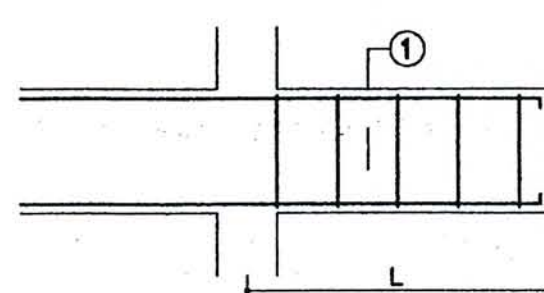


LONG SECTION

(B1')

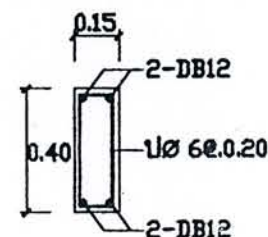


SECTION 1-1

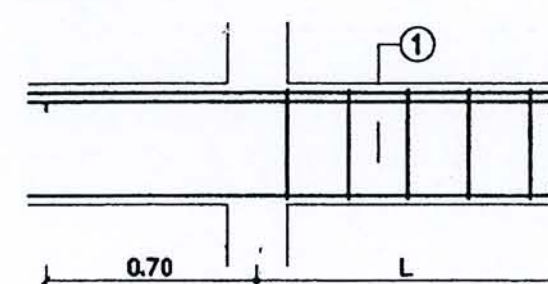


LONG SECTION

(B4')

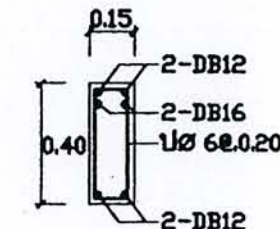


SECTION 1-1

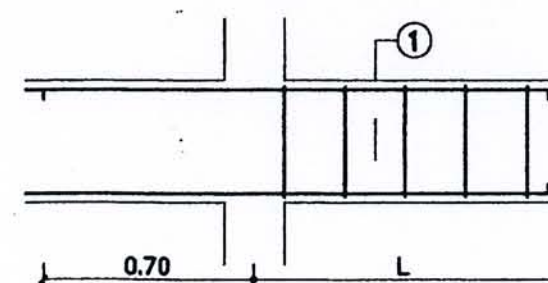


LONG SECTION

(B3')

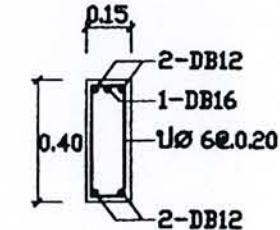


SECTION 1-1

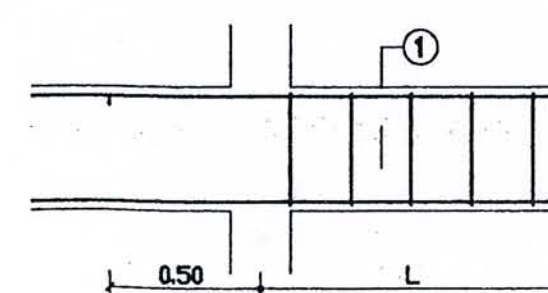

LONG SECTION

(B2')

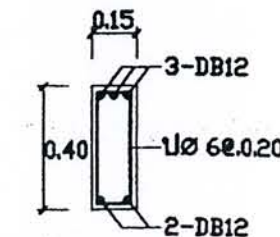


SECTION 1-1




โครงการ
แบบบ้านยืมเพื่อประชาชน

ตามนโยบาย
ม.ร.ว. สุขุมพันธุ์ บริพัตร
ผู้ว่าราชการกรุงเทพมหานคร


โดยสำนักการโยธา
กรุงเทพมหานคร

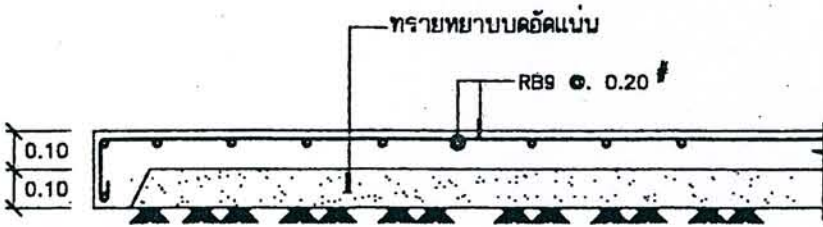


S0

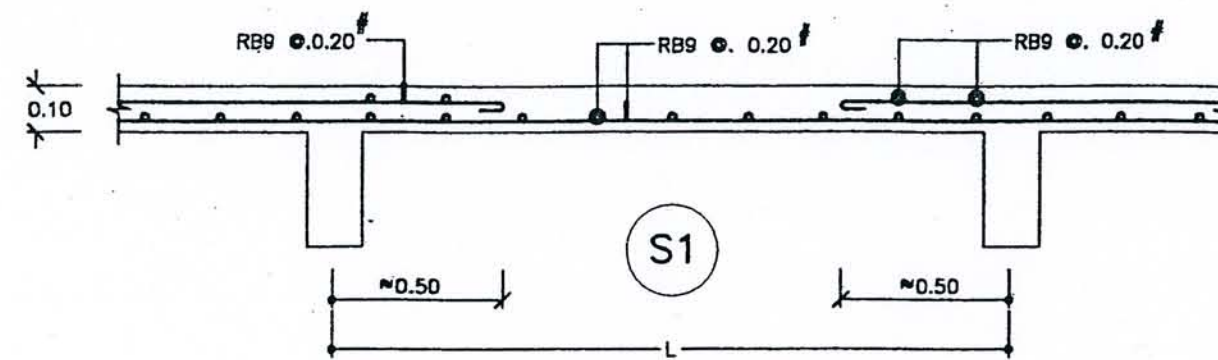


S1

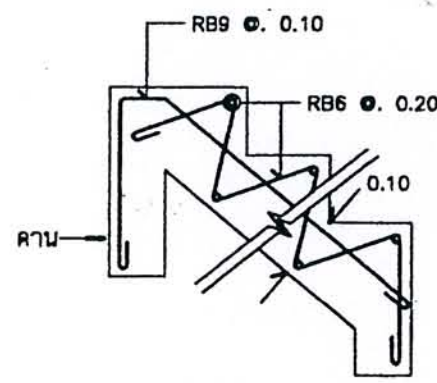


SECTION - 1
(ตามแบบโครงสร้างชั้นล่าง)

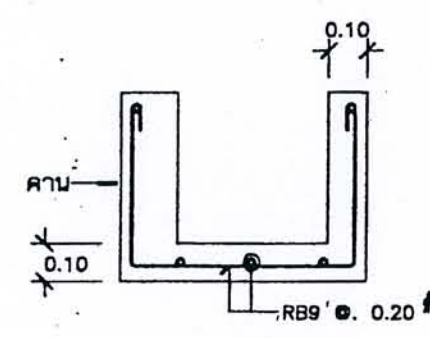


SECTION - 2
(ตามแบบโครงสร้างชั้นล่าง)

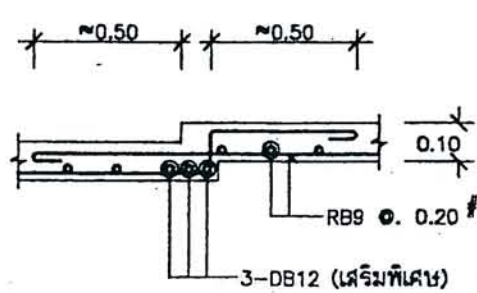

ขยายพื้นลดระดับ

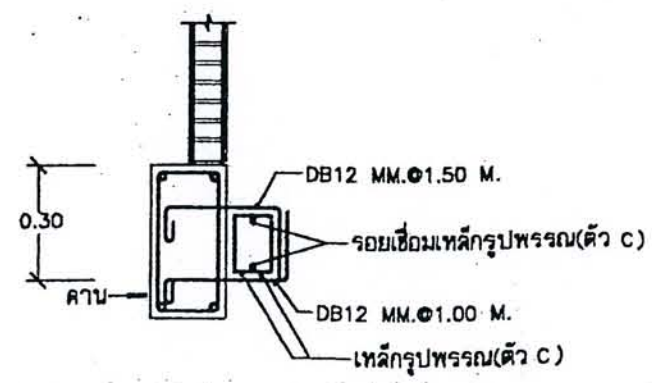

แบบขยายจุดที่มีหลังคารอบล่างติดผนัง

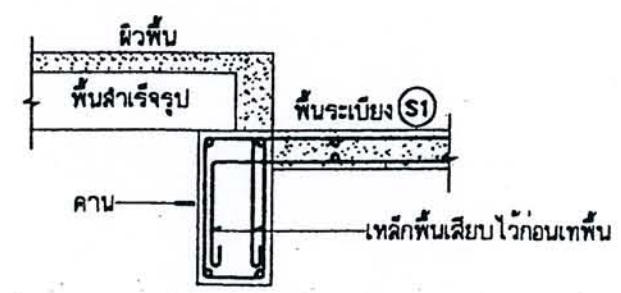

แบบขยายรอยต่อพื้นกับระเบียง

ได้รับความอนุเคราะห์แบบ
จาก
บริษัท แลนด์ โยม
(ประเทศไทย) จำกัด









โครงการ
แบบบ้านยืมเพื่อประชาชน


ตามนโยบาย
ม.ร.ว. สุขุมพันธุ์ บริพัตร
ผู้ว่าราชการกรุงเทพมหานคร

โดยสำนักงานโยธา
กรุงเทพมหานคร

ได้รับความอนุเคราะห์แบบ
จาก
บริษัท แลนด์ โยม
(ประเทศไทย) จำกัด

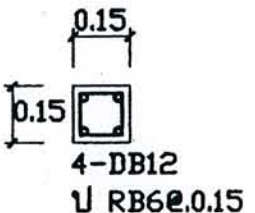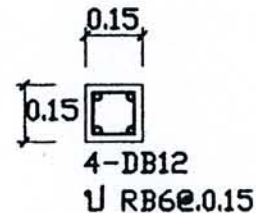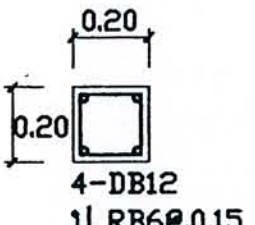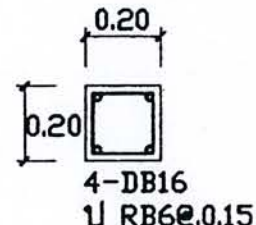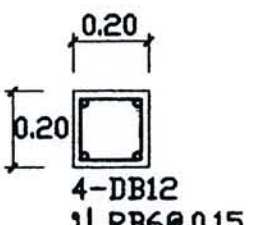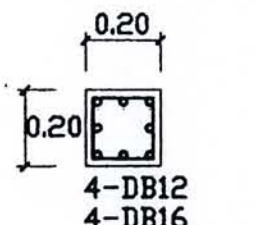FLOOR 2	 4-DB12 150 RB6@0.15	 4-DB12 150 RB6@0.15
FLOOR 1	 4-DB12 200 RB6@0.15	 4-DB16 200 RB6@0.15
FOOTING	 4-DB12 200 RB6@0.15	 4-DB12 4-DB16 200 RB6@0.15
	C1	C2

SECTION COLUMN 1:20

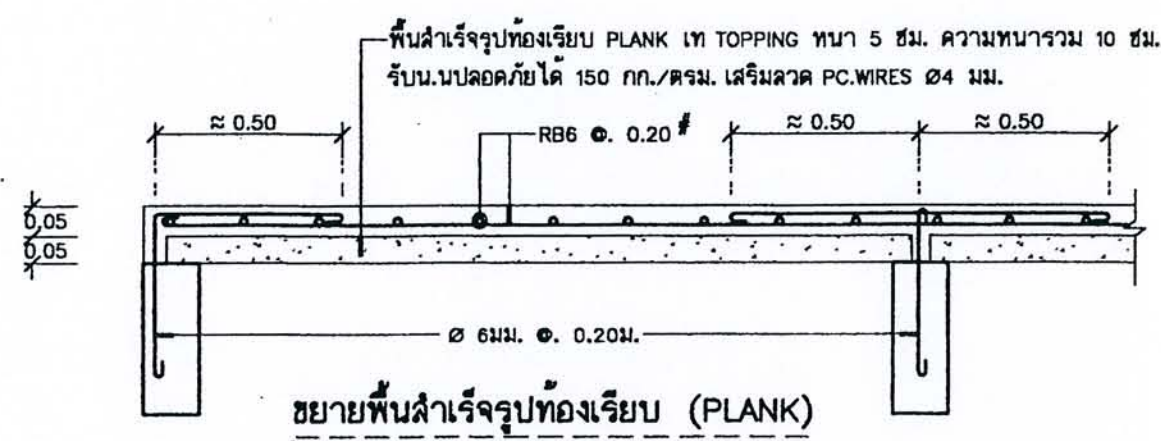

ตารางแสดงการรับน้ำหนักจร (LIVE LOAD)												
สำหรับพื้นสำเร็จรูปแบบทอเรียบ PLANK ขนาดหน้าตัด 0.05x0.35 ม.												
N \ S	2.80	3.00	3.20	3.40	3.60	3.80	4.00	4.20	4.40	4.60	4.80	5.00
4	504											
5		532	464	400	350	300						
6							318	274				
7									305	300		
8											300	250

- หมายเหตุ - มีค้ำยันชั่วคราว
- S = ระยะช่วงทอเรียบในถึงขอบในของคาน (CLEAR SPAN) หน่วยเป็นเมตร
- N = จำนวนลวดอัดแรง ขนาด Ø 4 มม.
- ตัวเลขในตารางแสดงความสามารถในการรับน้ำหนักจรทุกปลอดภัยหน่วยเป็น กก./ตารางเมตร




โครงการ
แบบบ้านยืมเพื่อประชาชน

ตามนโยบาย
ม.ร.ว. สุขุมพันธุ์ บริพัตร
ผู้ว่าราชการกรุงเทพมหานคร

โดยสำนักงานโยธา
กรุงเทพมหานคร

ได้รับความอนุเคราะห์แบบ
จาก
บริษัท แลนด์ โชม
(ประเทศไทย) จำกัด

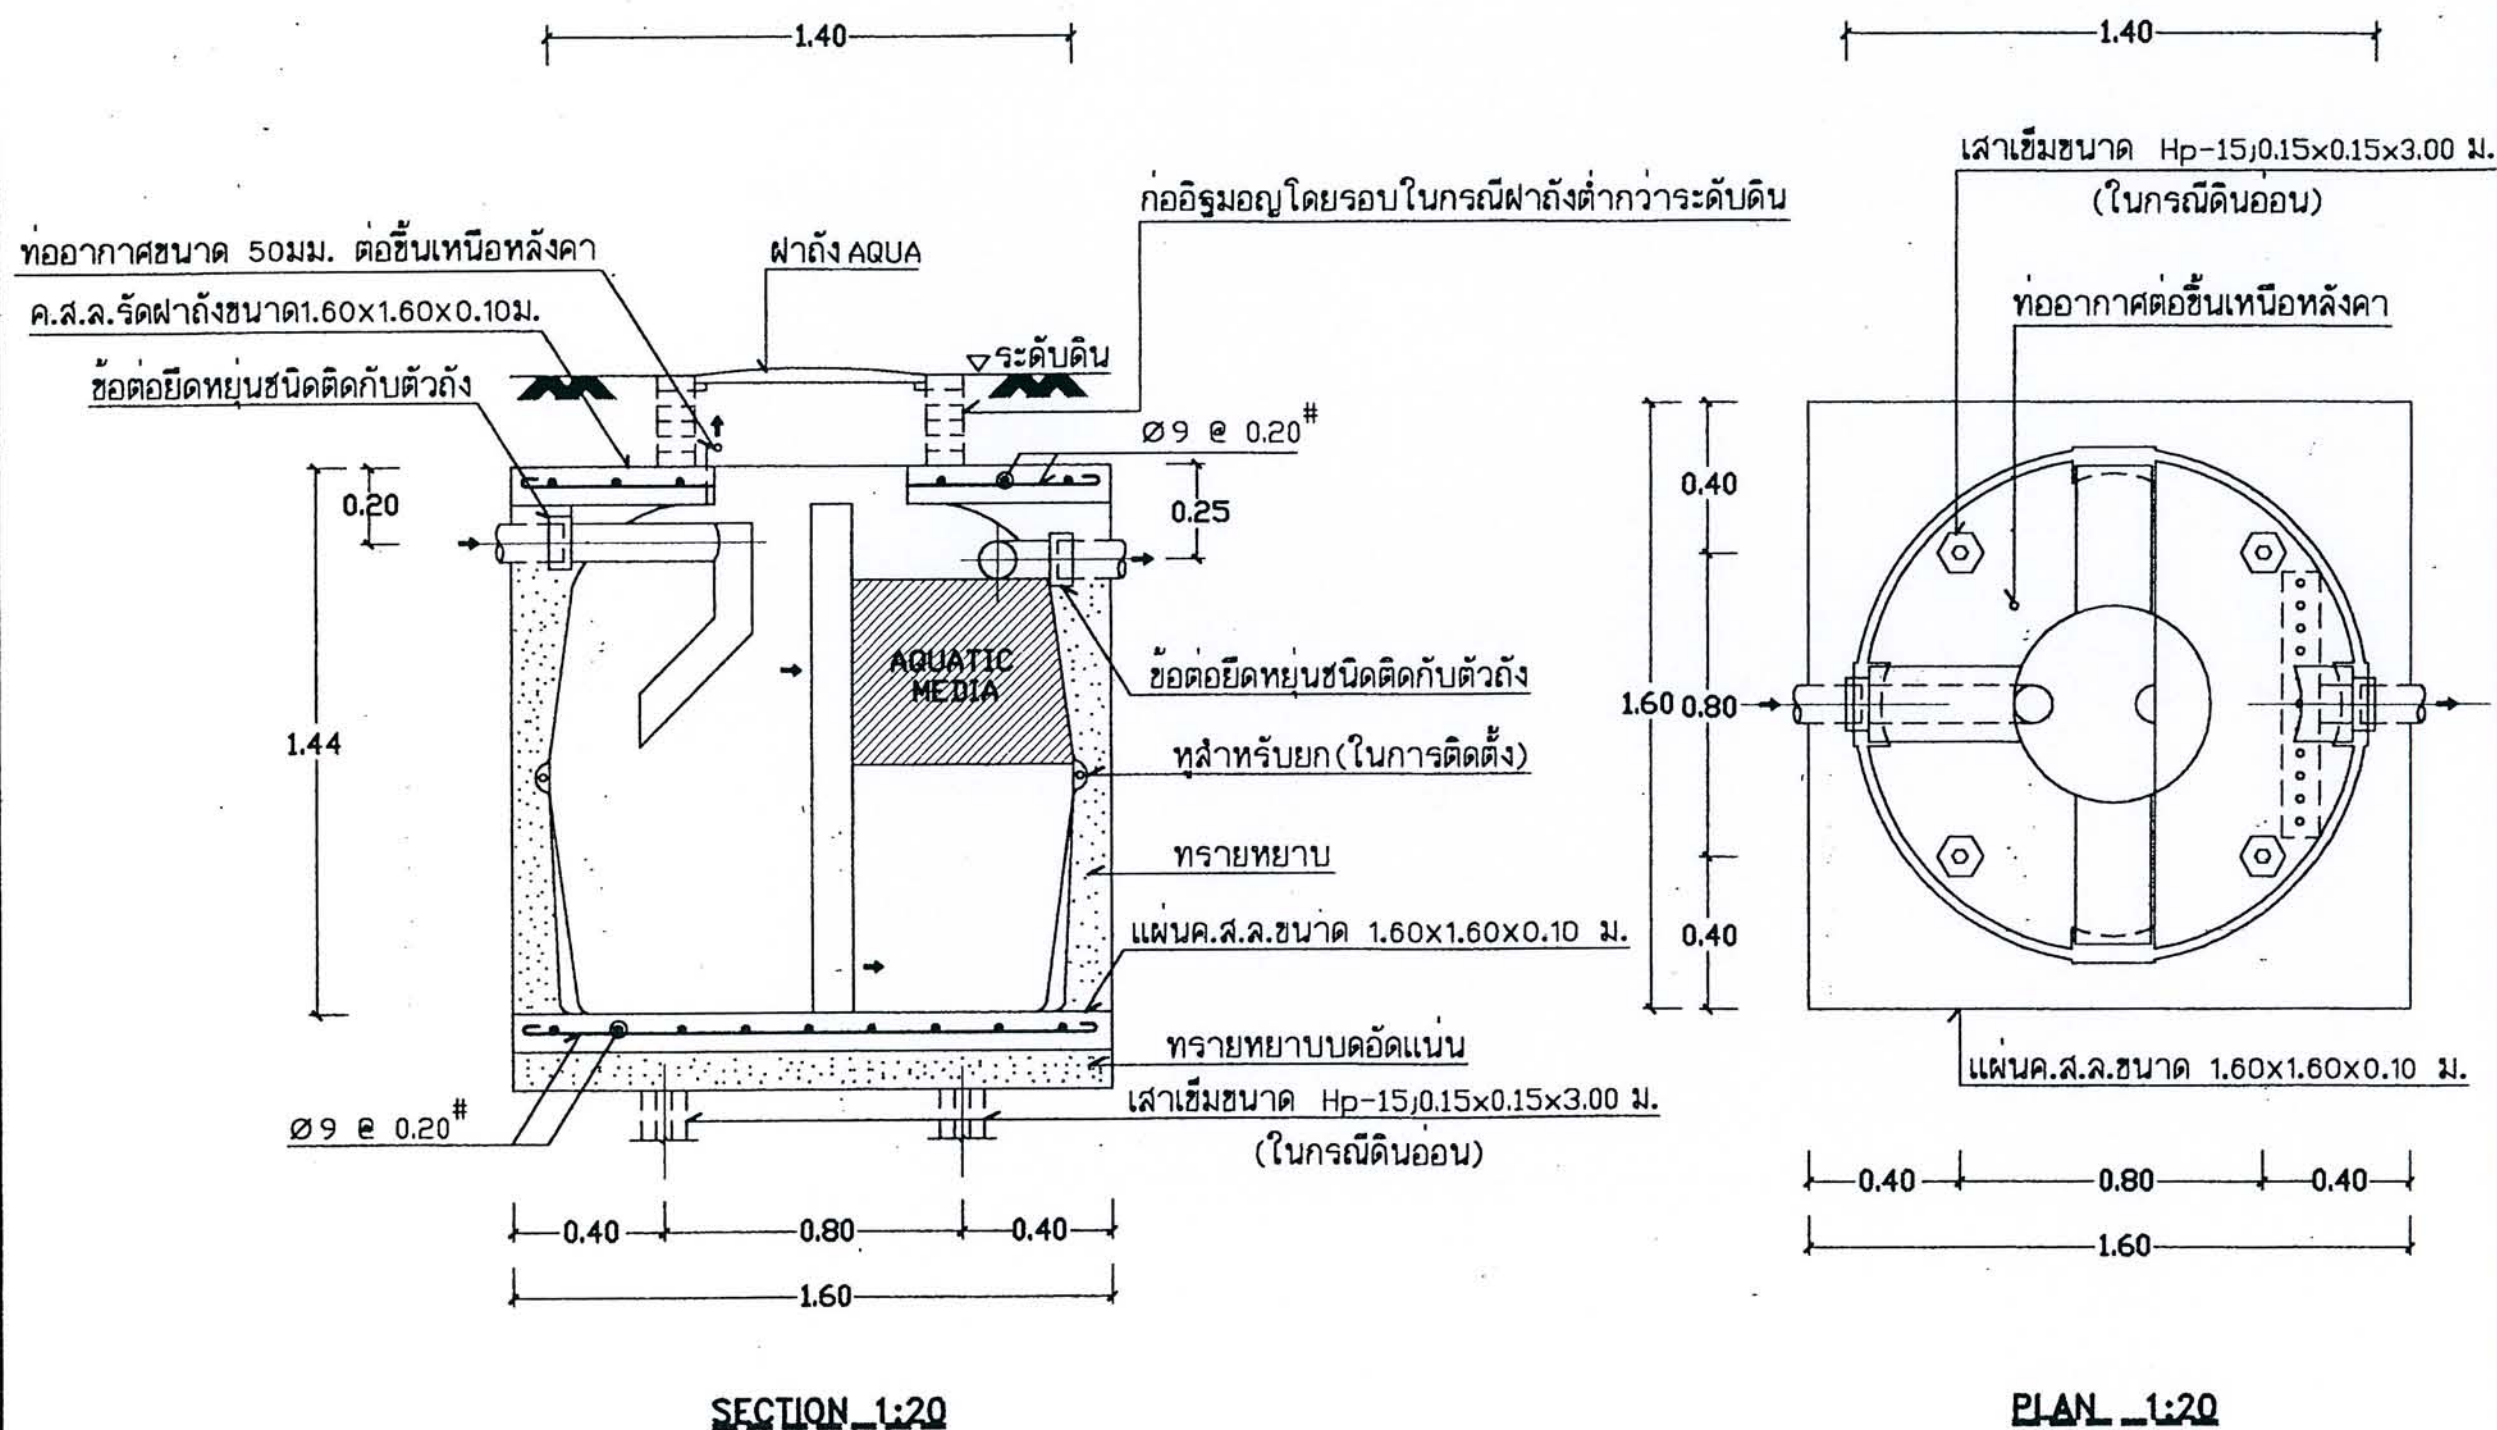

AQUA-PAC (AP-1600)