



ตามนโยบายของ
หม่อมราชวงศ์สุขุมพันธุ์ บริพัตร
ผู้ว่าราชการกรุงเทพมหานคร
โดย สำนักการโยธา



แบบบ้านยืม... เพื่อประชาชน

100 แบบบ้านมาตรฐาน...
สวย ดี โดนใจ...
พร้อมปลูกสร้างได้ทันที

ห้ามพลาด!!! โอกาส...
ยืมรับ... บ้านใหม่
แบบ **บ้านสวย
เลือกได้**
ใน “โครงการแบบบ้านยืม...เพื่อประชาชน”

แบบ 100 แบบบ้าน
มาตรฐาน...
สวย ดี โดนใจ
พร้อมปลูก
สร้างได้ทันที
มีให้เลือก
หลากหลาย
ตอบสนอง
ทุกไลฟ์สไตล์คนเมือง

สร้างจิต 2

โดยความอนุเคราะห์แบบจาก
บริษัท แลนด์ โฮม (ประเทศไทย) จำกัด

สัญญาลักษณะประกอบแบบสถาปัตยกรรม


- | สัญลักษณ์ | ความหมาย |
|---------------|--|
| N | ทิศเหนือ |
| | 1 , 2 , 3 , 4 ชื่อจุดบันทึกพบจากแปลน |
| | A หมายถึง ชื่อรูปถ่าย |
| | A หมายถึง ชื่อแบบขยาย |
| | A หมายถึง ชื่อรูปตัด |
| | A หมายถึง แบบเฉพาะจากศูนย์กลาง |
| +0000 , -0000 | +0000 มีค่ามากได้ไม่เกินตัวเลขที่กำหนด , -0000 มีค่าน้อยได้ไม่เกินตัวเลขที่กำหนด |
| | B หมายถึง ระยะการขยายจากศูนย์กลางถึงศูนย์กลาง |
| | B หมายถึง ระยะการขยายจากหัวถึงหัว |
| | A หมายถึง ระยะการขยายจากศูนย์กลางถึงหัวหรือหาง |
| | A หมายถึง ระยะการขยายจากศูนย์กลางถึงหัวหรือหาง |
| | 1 หมายถึง ทิศประตู่ |
| | 1 หมายถึง ทิศหน้าบ้าน |
| | 1 หมายถึง หมายเลขถนน |
| | ผนังก่ออิฐครึ่งแผ่น จากปูน |
| | ผนังก่ออิฐเต็มแผ่น จากปูน |
| | ผนังก่ออิฐมวลเบา จากปูน |
| | GB ผนังก่ออิฐฉาบผิว ตามแบบระบุ |
| | ผนังบริเวณคาน้ำดื่ม ก่อด้วยตามแบบระบุ |
| | ดิน |
| | คอนกรีต |
| | ทรายอัดแน่น |
| | หินกรวด |
| | ปูฉนวนกันความร้อน |
| | จากปูนขัดมัน |
| | จากปูนเรียบ |
- บ้าน SMILE HOME
V.1 [11/2/45]

•หมายเหตุ : ภาชนะบรรจุยา บรรจุปริมาณร้อยละ ๑๐๐ ใช้บรรจุยา ๐.7 เมล


* บริษัทฯ ทำถนนและทางเดินให้ 30 ม² สุกค้ากำหนดตหน้าหน่วยงาน
ตามใบ ป/ป. 2/10

नमस्कार २

ได้รับความอนุเคราะห์แบบ
จาก
บริษัท แลนด์ โสม
(ประเทศไทย) จำกัด

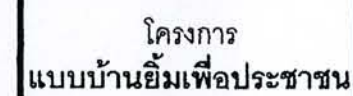

โดยสำนักงานโยธา
กรุงเทพมหานคร

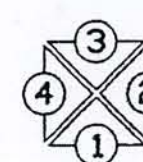

แปลนพื้นชั้นล่าง

มาตราส่วน 1 : 75

* หมายเหตุ: ชื่อที่อะระบบเลขที่บิดาทุกช่อง หลังฉันทนาระบบเลขชี้ให้ทศ. คณ. ปิดท้ายให้ฉันทน. เพื่อแยกทบกับฉันทน. ส่วน

ได้รับความอนุเคราะห์แบบ
จาก
บริษัท แลนด์ โฮม
(ประเทศไทย) จำกัด




โครงการ
แบบบ้านยืมเพื่อประชาชน

ตามนโยบาย
ม.ร.ว. สุขุมพันธุ์ บริพัตร
ผู้ว่าราชการกรุงเทพมหานคร

โดยสำนักงานโยธา
กรุงเทพมหานคร

ได้รับความอนุเคราะห์แบบ
จาก
บริษัท แลนด์ ไฮเน
(ประเทศไทย) จำกัด

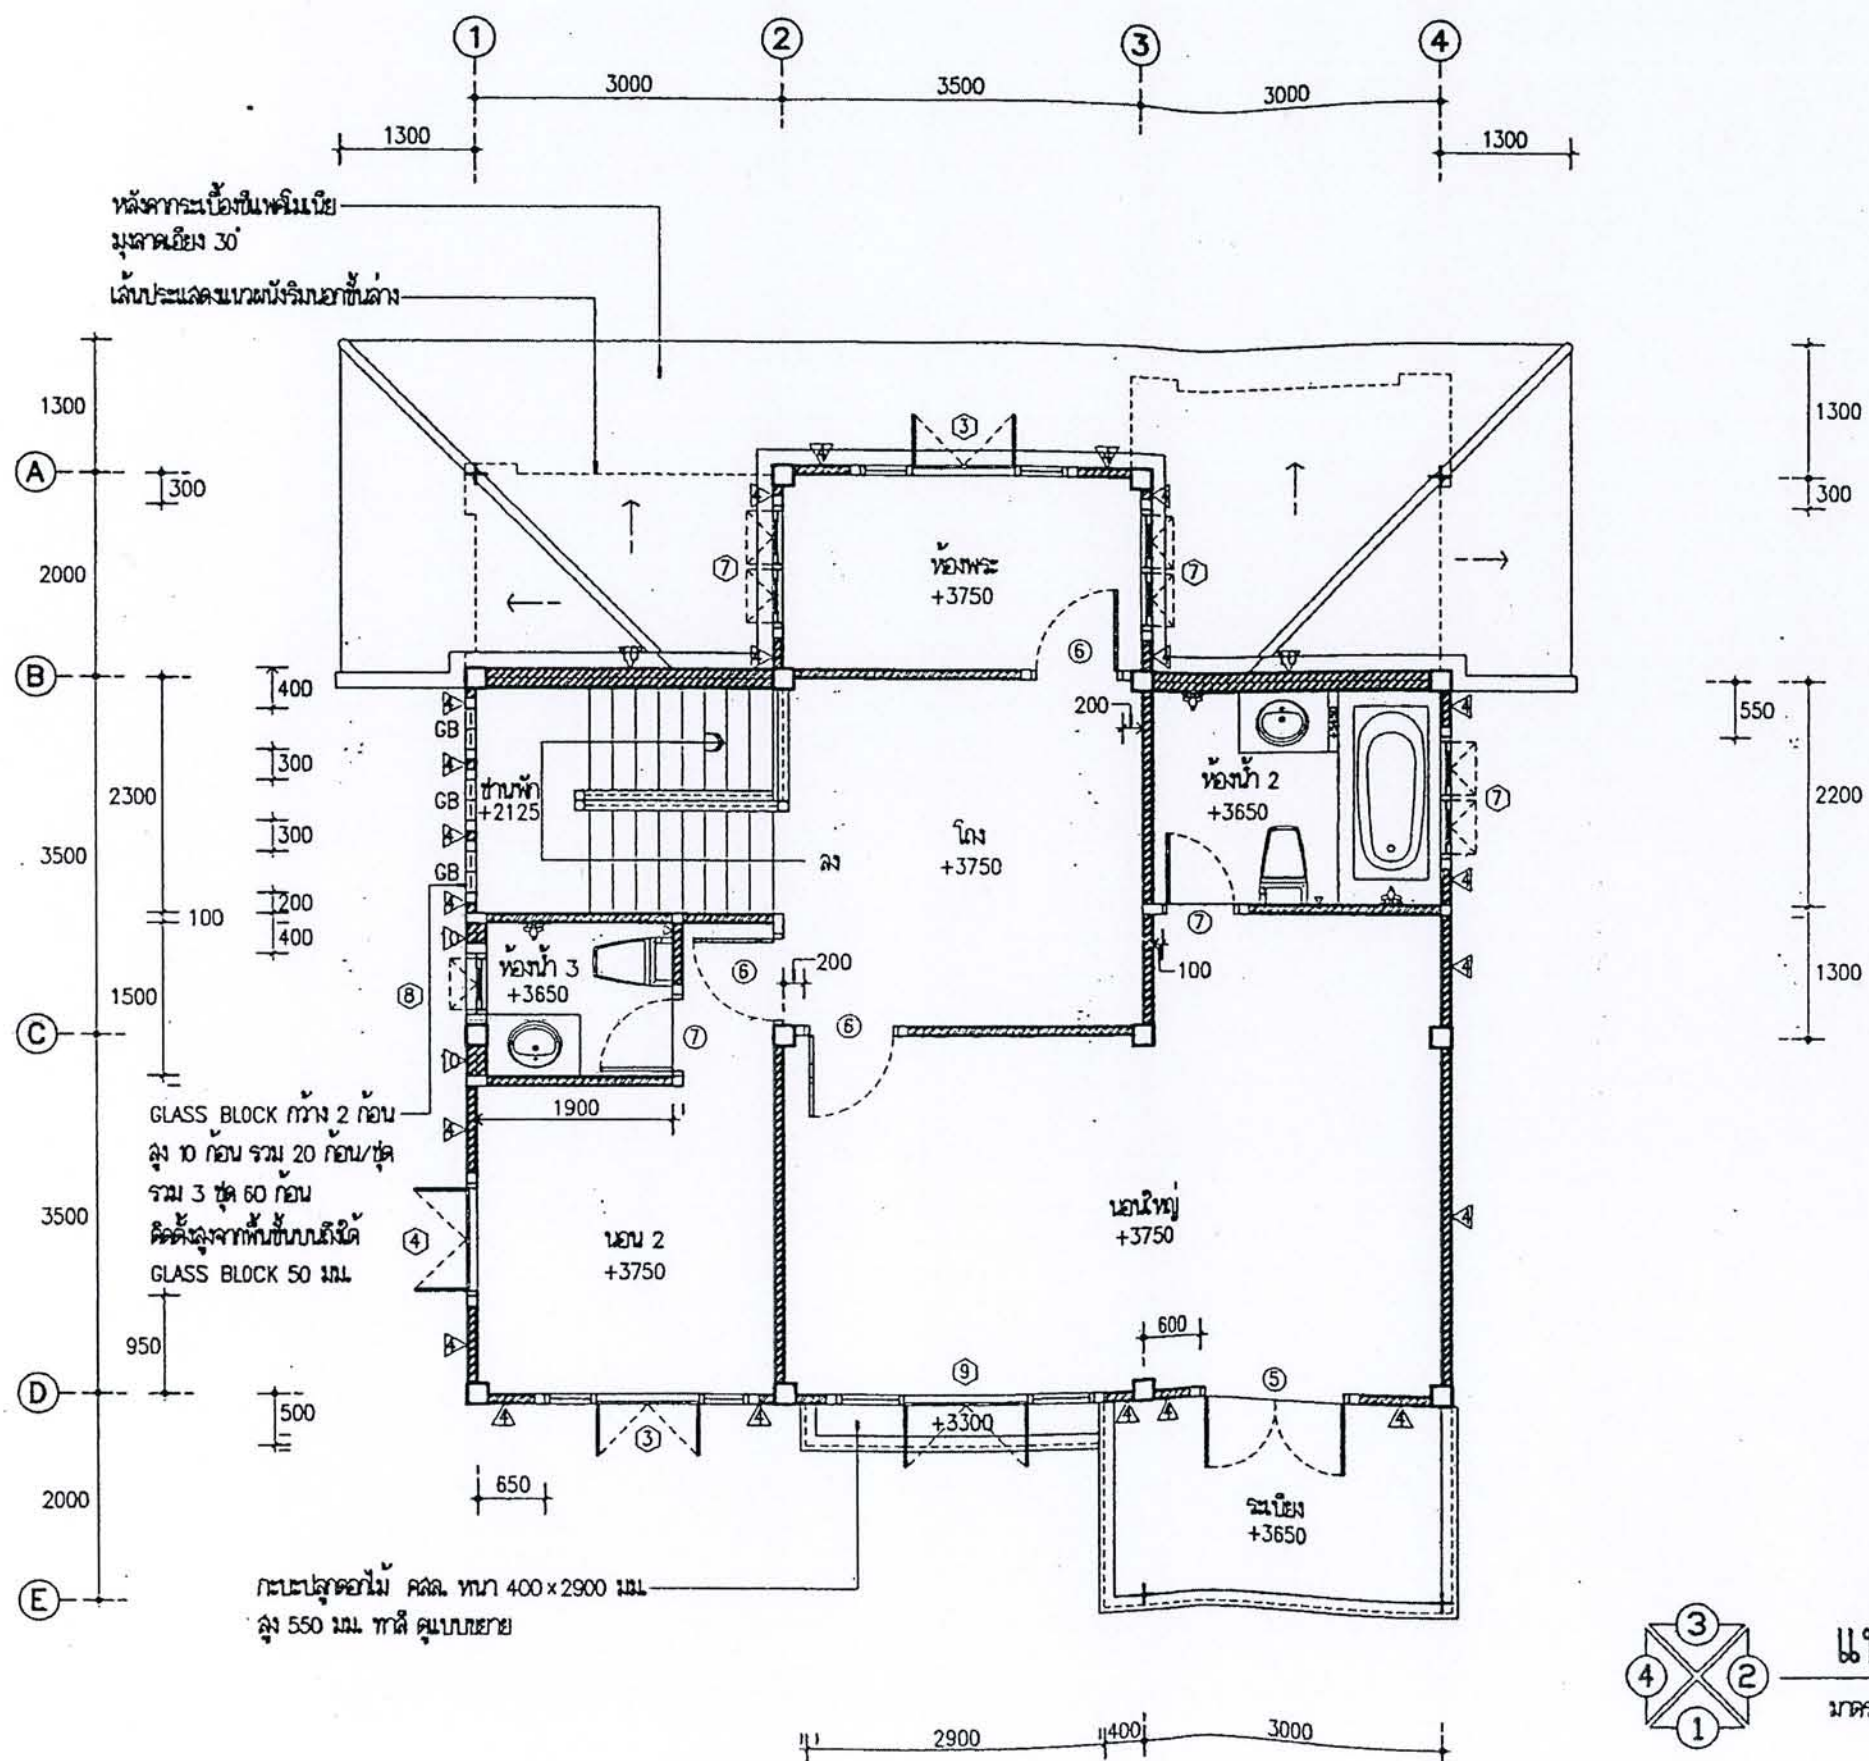





โครงการ
แบบบ้านอิมเพื่อประชาชน

ตามนโยบาย
ม.ร.ว. สุขุมพันธุ์ บริพัตร
ผู้ว่าราชการกรุงเทพมหานคร

โดยสำนักงานโยธา
กรุงเทพมหานคร

ได้รับความอนุเคราะห์แบบ
จาก
บริษัท แลนด์ โสม
(ประเทศไทย) จำกัด

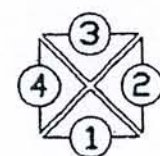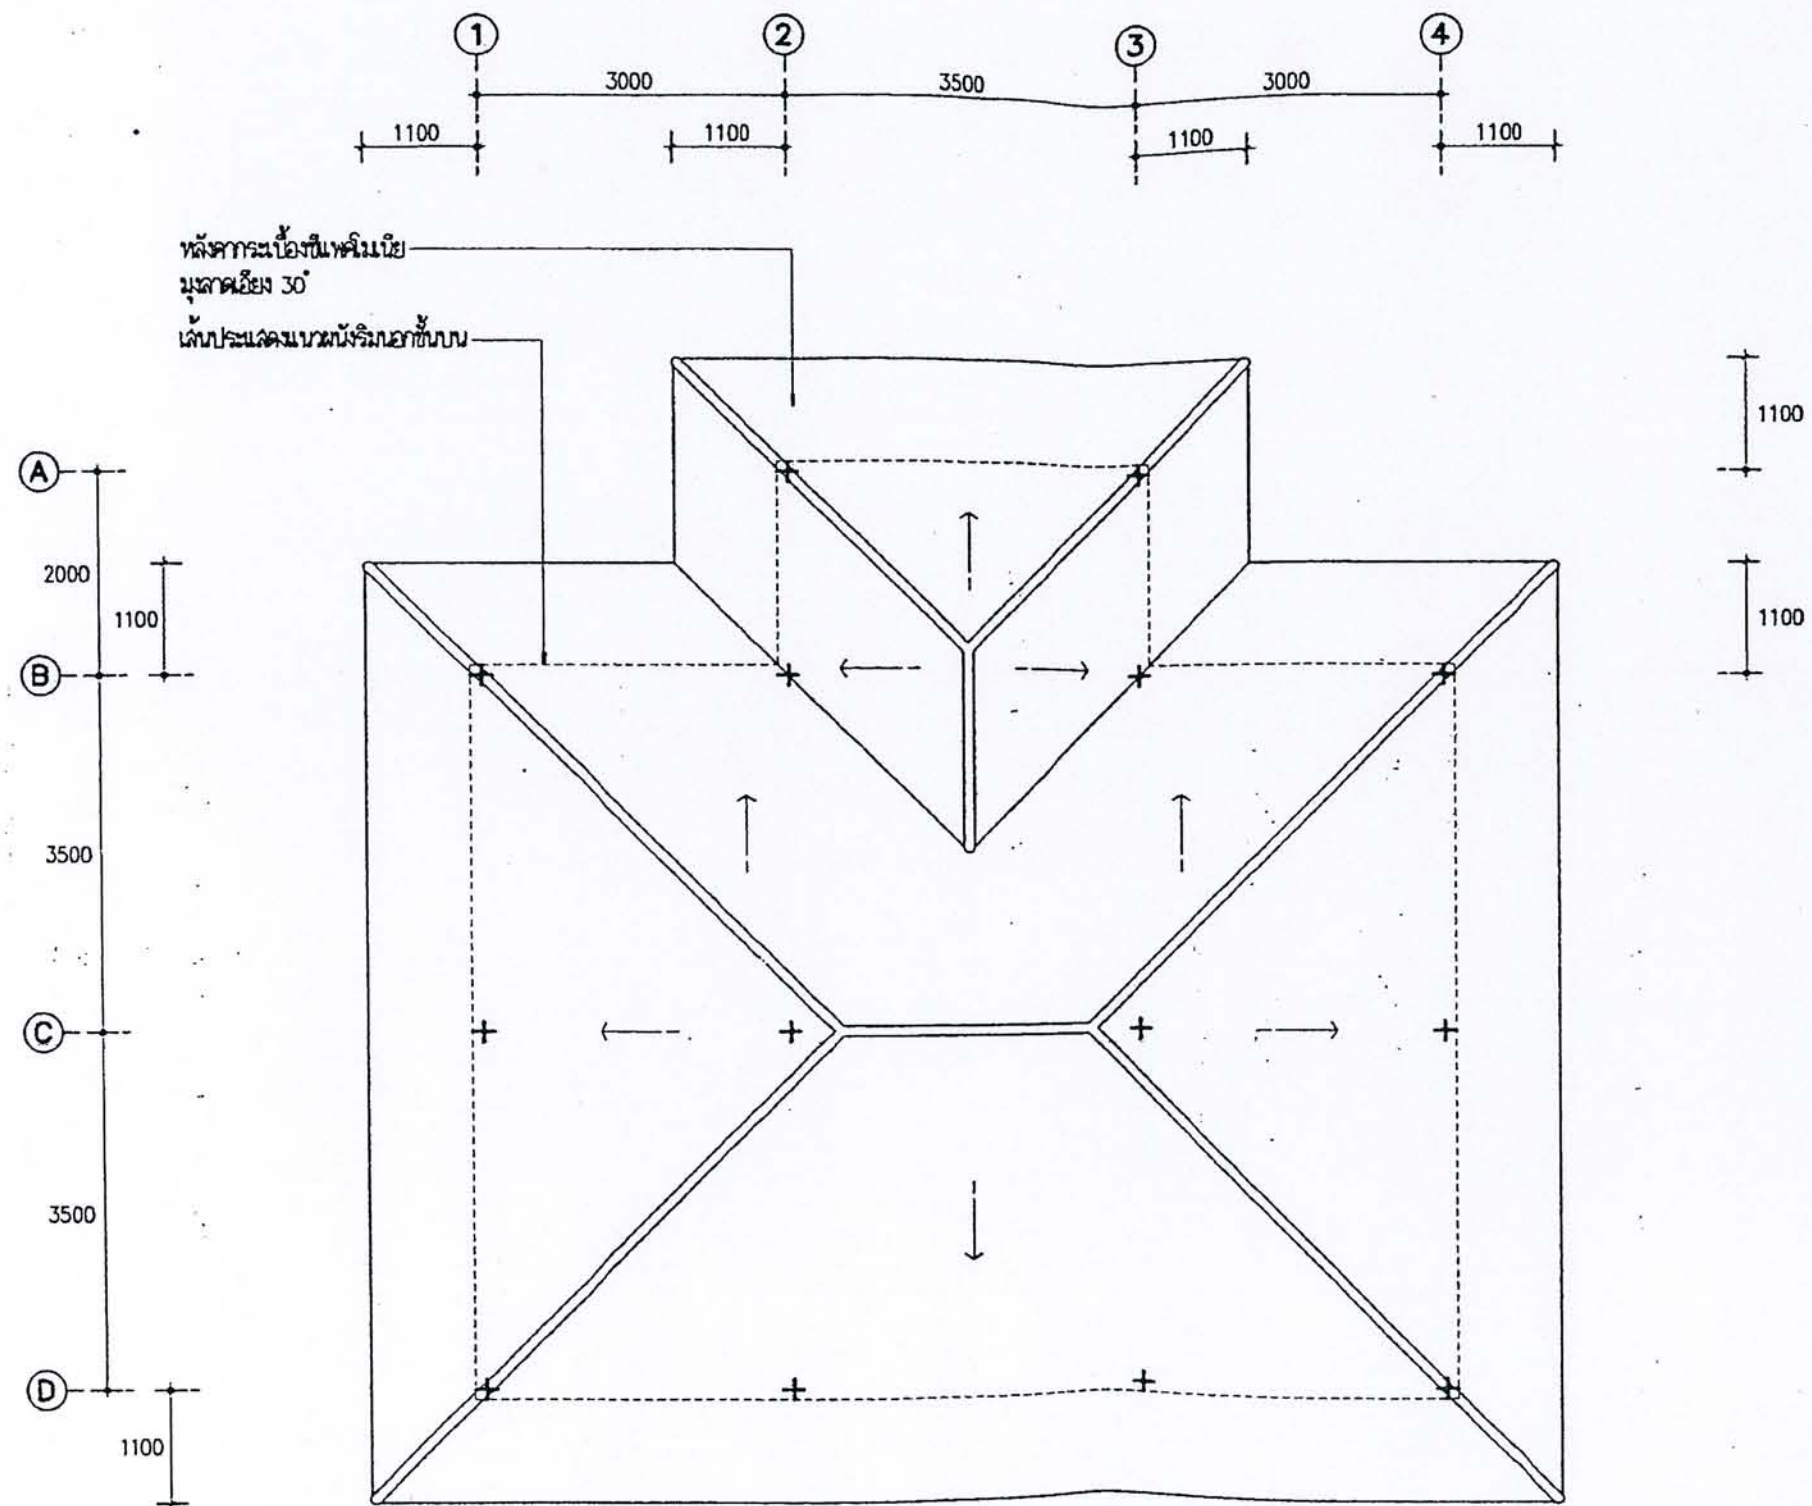

แปลนหลังคา


มาตราส่วน 1 : 75



โครงการ
แบบบ้านยืมเพื่อประชาชน

ตามนโยบาย
ม.ร.ว. สุขุมพันธุ์ บริพัตร
ผู้ว่าราชการกรุงเทพมหานคร

โดยสำนักงานการโยธา
กรุงเทพมหานคร

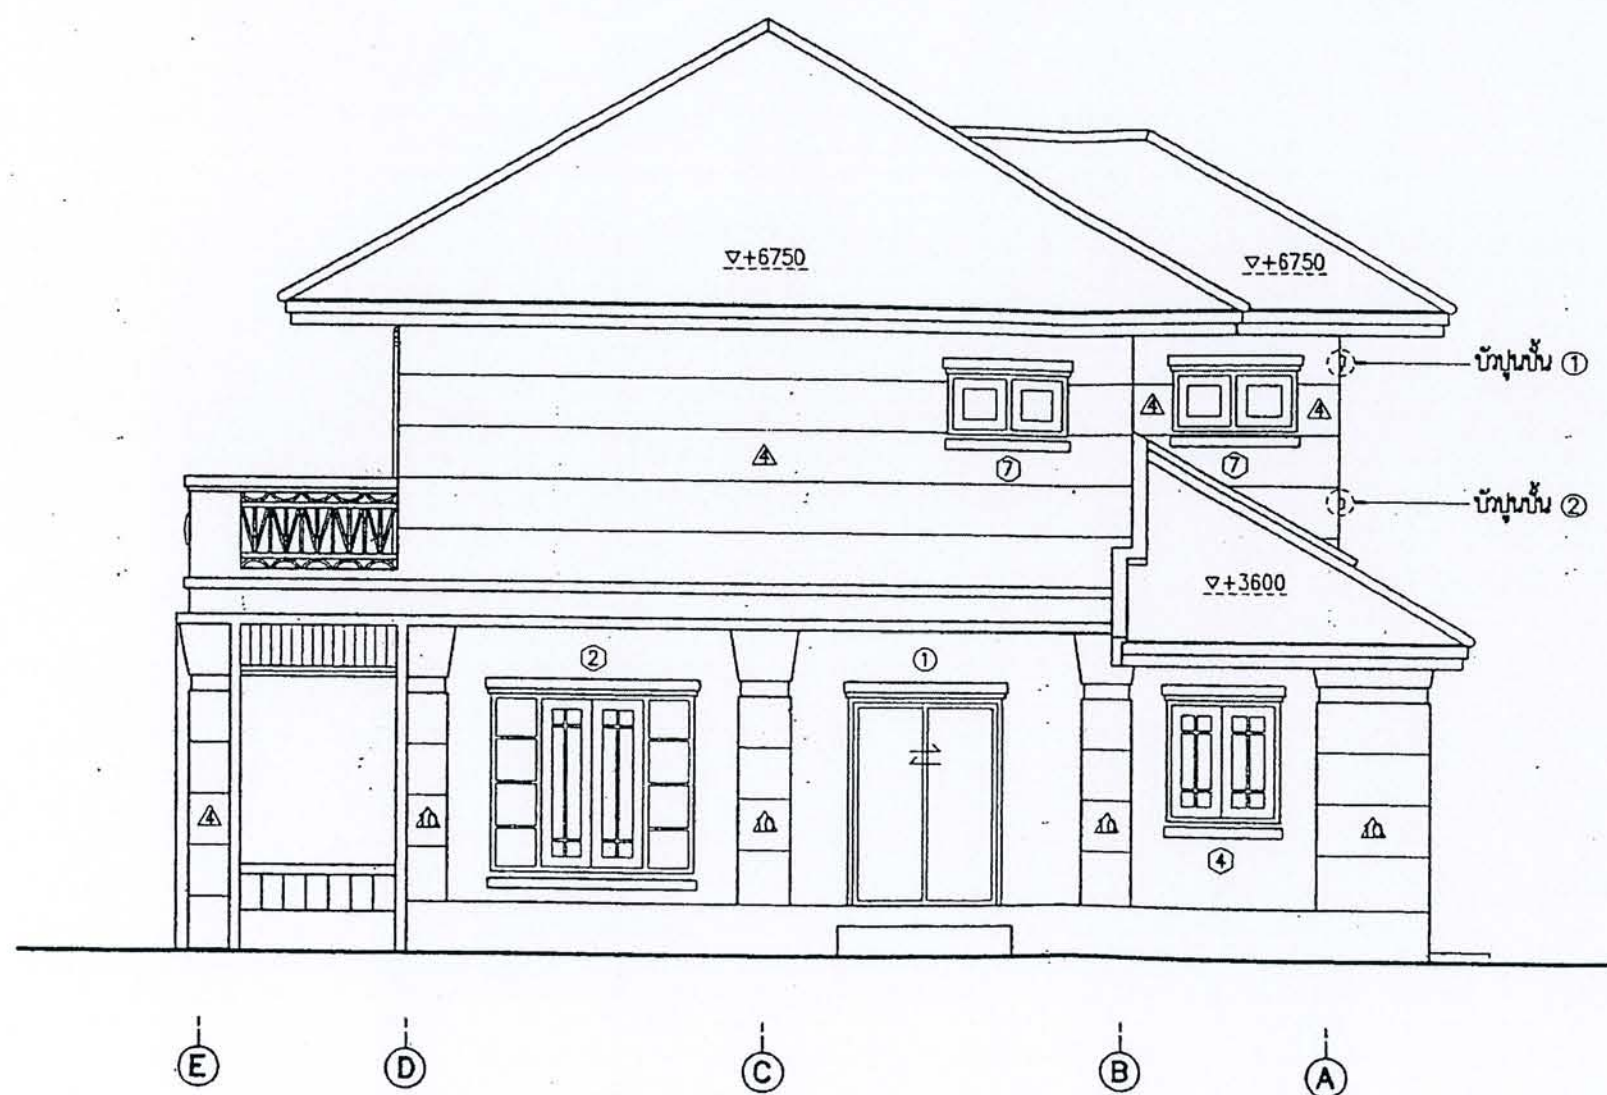

รูปด้าน
มาตรฐาน
1 : 75


ได้รับความอนุเคราะห์แบบ
จาก
บริษัท แลนด์ โสม
(ประเทศไทย) จำกัด



โครงการ
แบบบ้านยืมเพื่อประชาชน

ตามนโยบาย
ม.ร.ว. สุขุมพันธุ์ บริพัตร
ผู้ว่าราชการกรุงเทพมหานคร

โดยสำนักงานโยธา
กรุงเทพมหานคร

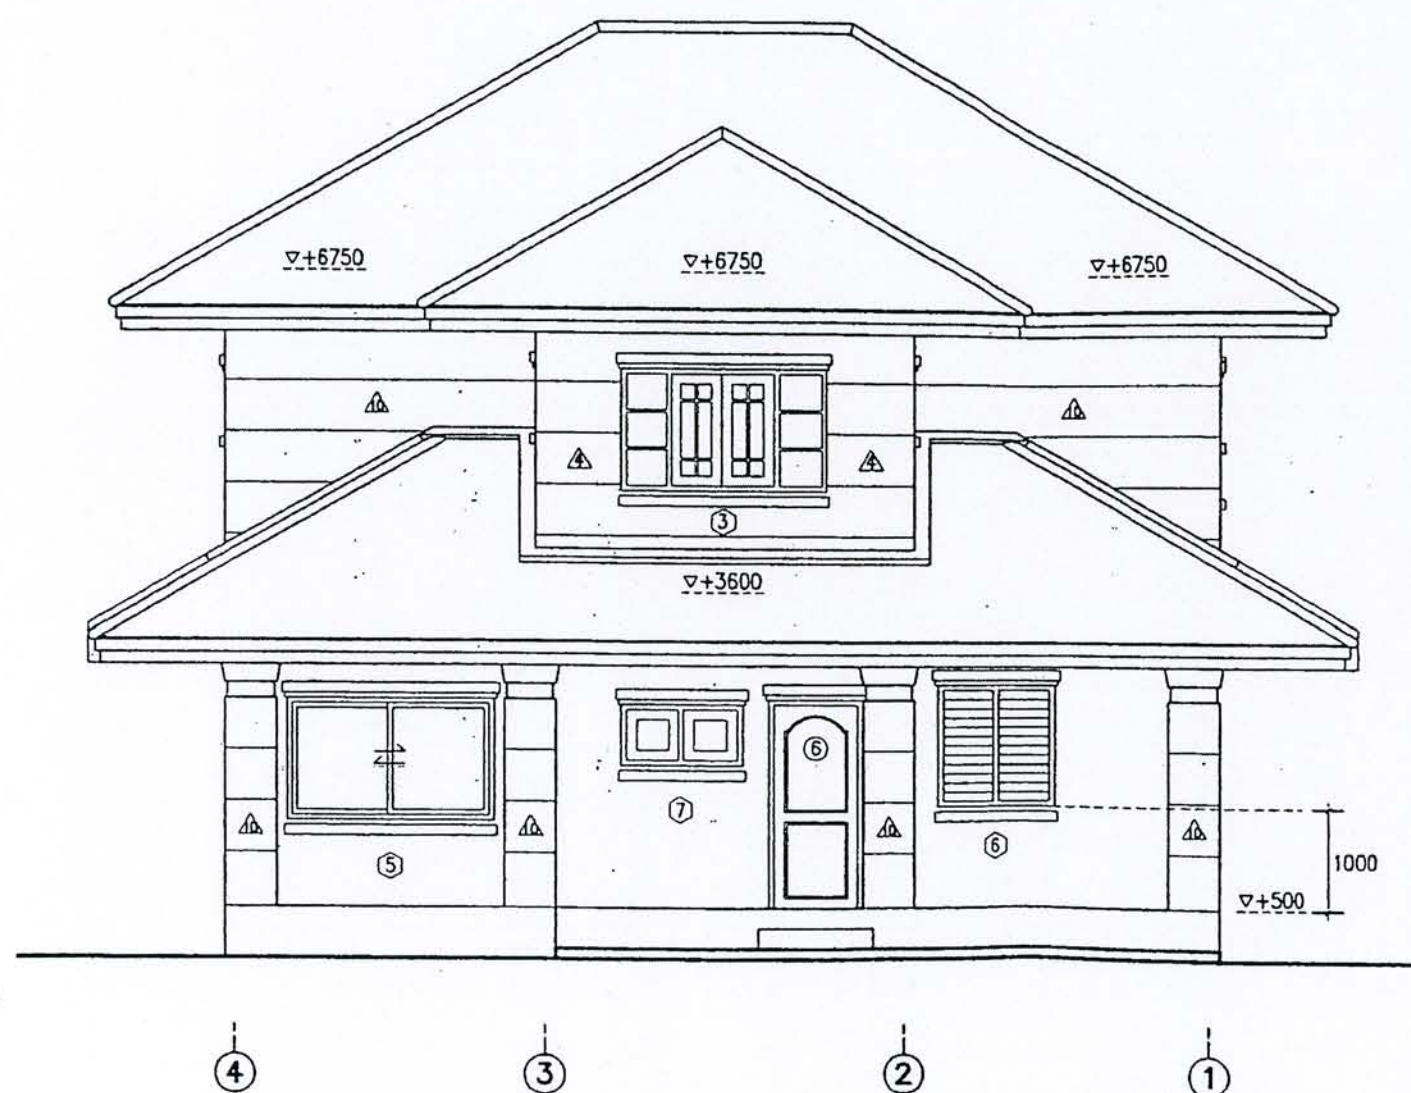

รูปด้าน
หน้า
ขนาด
1 : 75


ได้รับความอนุเคราะห์แบบ
จาก
บริษัท แลนด์ โฮม
(ประเทศไทย) จำกัด



โครงการ
แบบบ้านยืมเพื่อประชาชน

ตามนโยบาย
ม.ร.ว. สุขุมพันธุ์ บริพัตร
ผู้ว่าราชการกรุงเทพมหานคร

โดยสำนักงานโยธา
กรุงเทพมหานคร

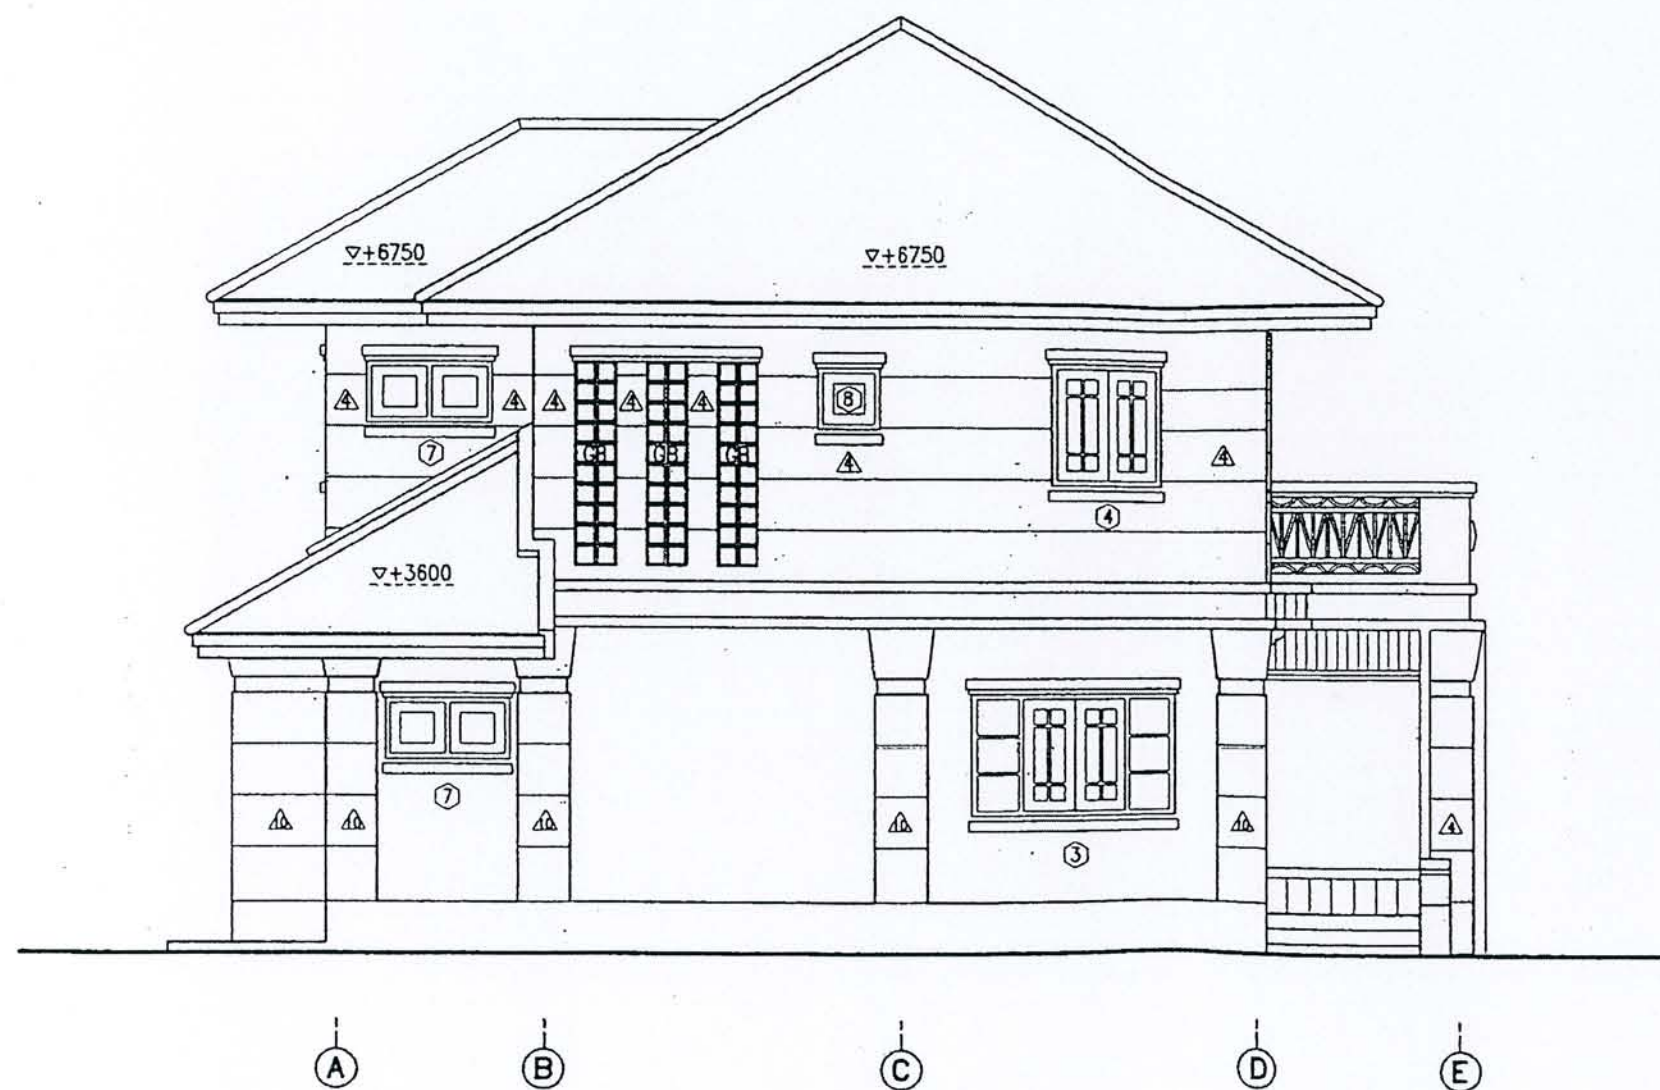

รูปด้าน
มาตราส่วน 1 : 75


ได้รับความอนุเคราะห์แบบ
จาก
บริษัท แลนด์ โฮม
(ประเทศไทย) จำกัด




โครงการ
แบบบ้านอิมเพื่อประชาชน

ตามนโยบาย
ม.ร.ว. สุขุมพันธุ์ บริพัตร
ผู้ว่าราชการกรุงเทพมหานคร

โดยสำนักการโยธา
กรุงเทพมหานคร

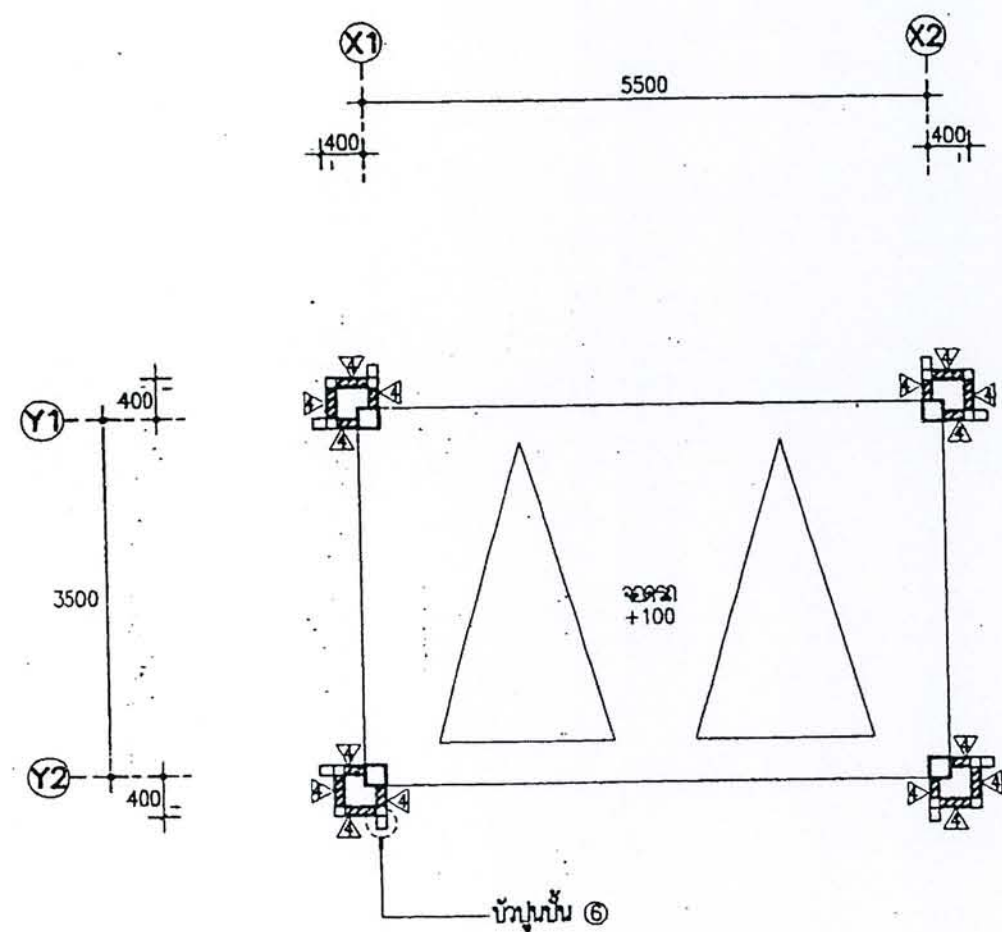

แปลนพื้น
มาตราส่วน 1 : 75

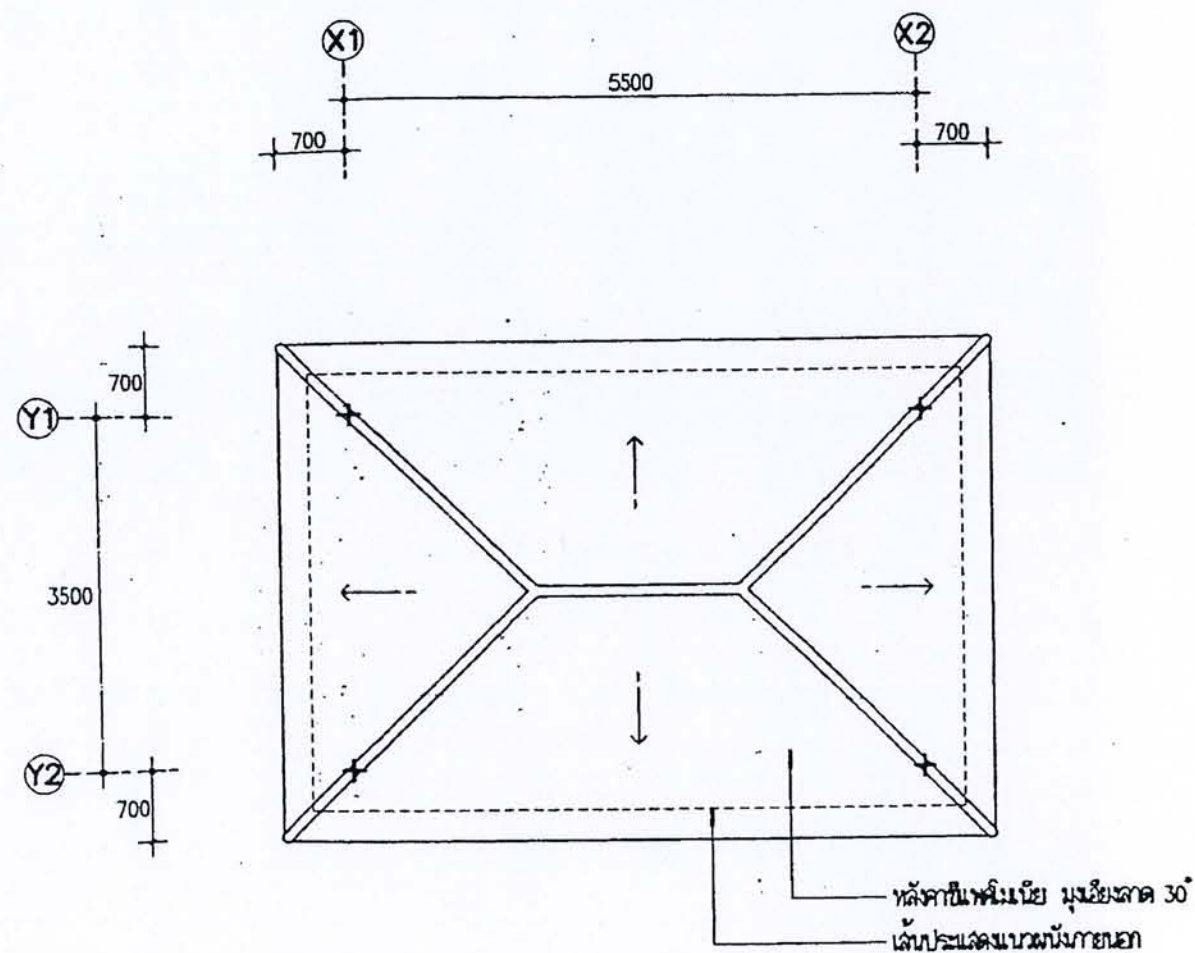

แปลนหลังคา
มาตราส่วน 1 : 75



ได้รับความอนุเคราะห์แบบ
จาก
บริษัท แลนด์ โสม
(ประเทศไทย) จำกัด







โครงการ
แบบบ้านยืมเพื่อประชาชน

ตามนโยบาย
ม.ร.ว. สุขุมพันธุ์ บริพัตร
ผู้ว่าราชการกรุงเทพมหานคร

โดยสำนักงานโยธา
กรุงเทพมหานคร

ได้รับความอนุเคราะห์แบบ
จาก
บริษัท แลนด์ โฮม
(ประเทศไทย) จำกัด

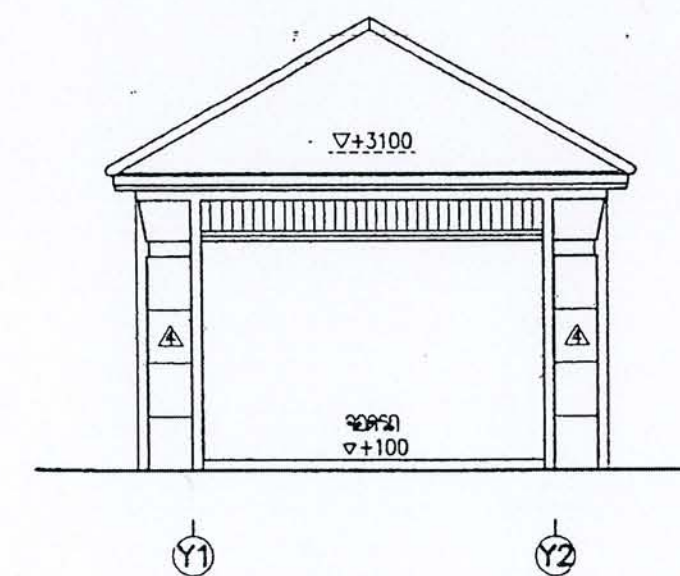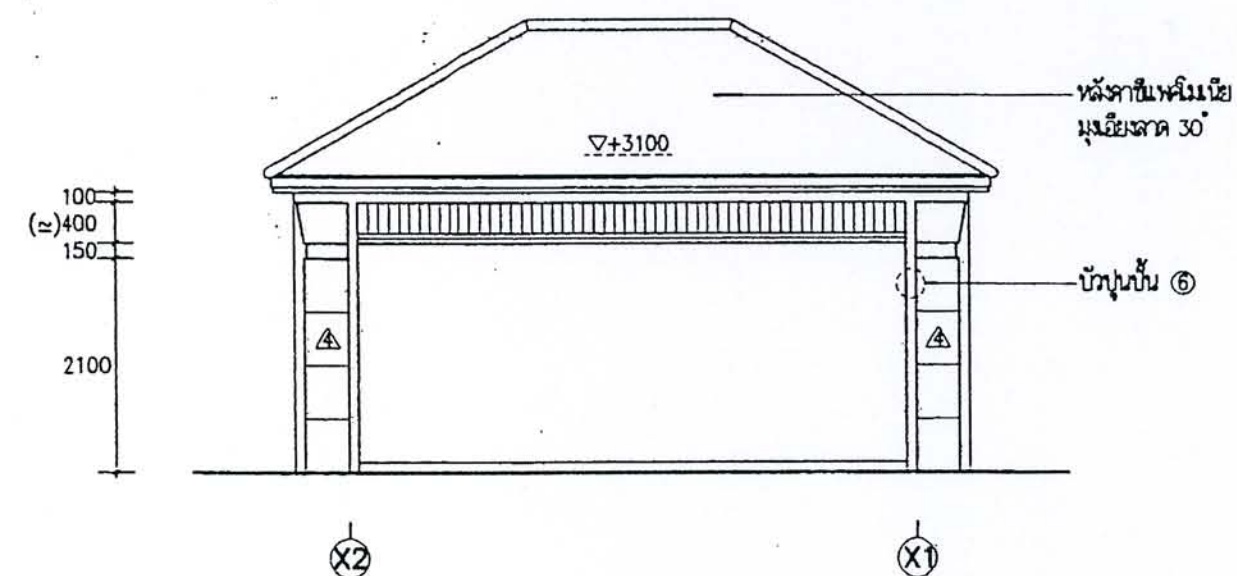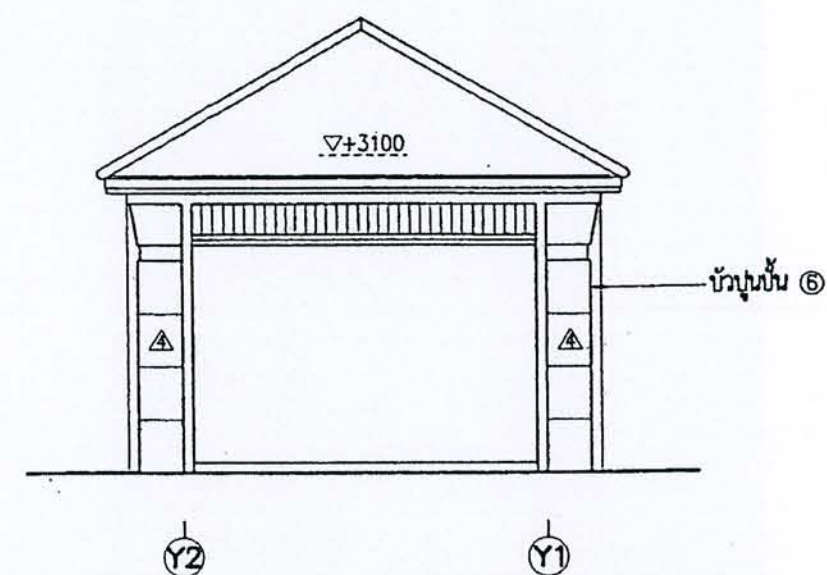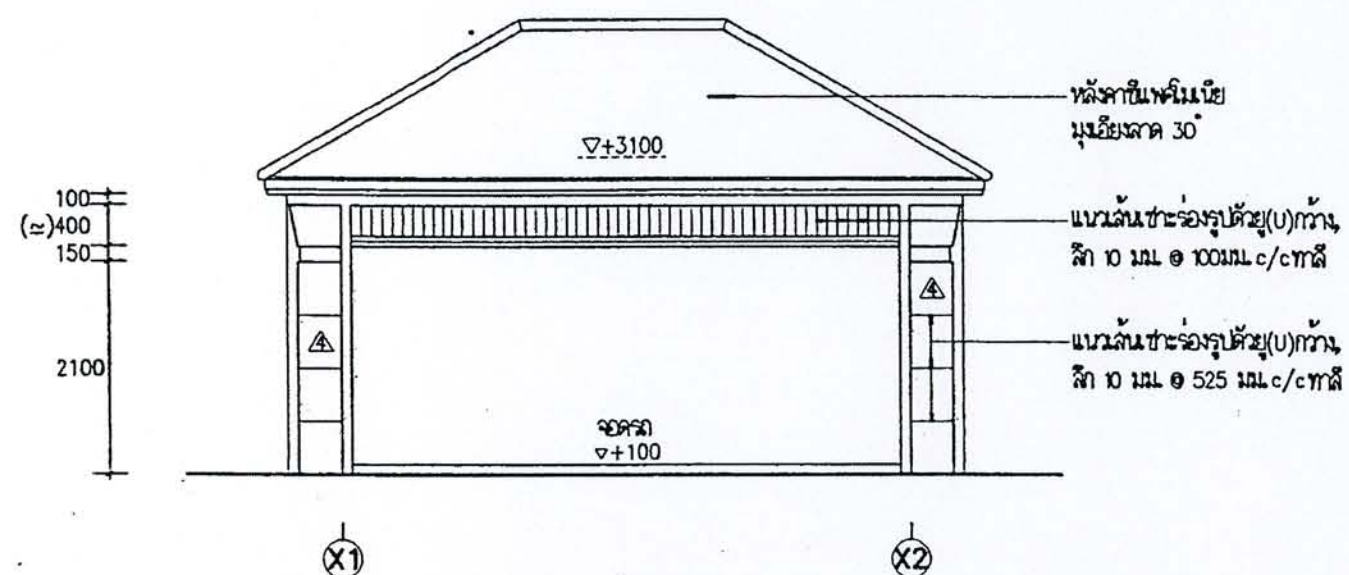

สัญญาลักษณะประกอบแบบ "ร"



รายการไฟฟ้า

สัญลักษณ์	ความหมาย	ขนาด - ยี่ห้อ - รุ่น
	แผงควบคุมไฟฟ้า	Square-D ขนาด 15 Amp. แบบกล่องเหล็กพร้อม circuit Breaker 7 ชุด
	โคมไฟฟ้า	ครอบแก้วกลม ๑ 14" ผิวทึบหลอดฟลูออโรเรสเซนต์ 32 W. แบบกลมแสงสีขาว
	โคมไฟฟ้า	ครอบแก้วกลม ๑ 8" หลอดทั้งหลอด 60 W. แสงสีขาว
	หลอดฟลูออโรเรสเซนต์	รางหลอดฟลูออโรเรสเซนต์ ครอบพลาสติก ขนาด 1 X 20 W. แสงสีขาว
	หลอดฟลูออโรเรสเซนต์	รางหลอดฟลูออโรเรสเซนต์ ครอบพลาสติก ขนาด 1 X 40 W. แสงสีขาว
	ไฟโคมแบบเพดาน	โคมไฟแก้วผิวทึบ ๑ 12" หลอดธรรมดา 60 W.
	ไฟตั้งโต๊ะ	ไฟตั้งโต๊ะ 60 W. พน.เหลี่ยม
	สวิทช์ไฟฟ้า	Single way ชนิดฉีฉนวนของ NATIONAL (ซองท) ติดตั้งสูงจากพื้น 1200 มม.
	สวิทช์ไฟฟ้า 2 ทาง	Two way ชนิดฉีฉนวนของ NATIONAL (ซองท) ติดตั้งสูงจากพื้น 1200 มม.
	ปลั๊กไฟ, เต้าเสียบ	ปลั๊กไฟแบบเรียบชนิดฉีฉนวนแบบ 2 เต้าเสียบต่อ 1 ชุด พร้อมสายดินตาม- การไฟฟ้า ติดตั้งสูงจากพื้น 200 มม. ของ NATIONAL (ซองท) ติดตั้งห่างจากขอบ 100 มม.
	ปลั๊กไฟ, เต้าเสียบ	ปลั๊กไฟแบบเรียบชนิดฉีฉนวนแบบ 2 เต้าเสียบต่อ 1 ชุด พร้อมสายดินตาม- การไฟฟ้า ติดตั้งสูงจากพื้น 1000 มม. ของ NATIONAL (ซองท) ติดตั้งห่างจากขอบ 100 มม.
	ปลั๊กสายอากาศ TV.	ใช้สายอากาศ TV.RG-6 โดยเดินสายไปยังท่อน้ำทองเหลืองที่ติดตั้งไว้ 1 ม.
	โทรทัศน์	เดินสายตามมาตรฐานไฟฟ้า โดยเดินสายไปยังสายเคเบิลที่บ้านแล้วเปลี่ยนปลั๊ก 1 ม.
	สวิทช์แอร์	ตำแหน่งตามแบบ
	แสดงการเดินสายไฟแบบ-	สายไฟใช้สาย PVC. ของ YAZAKI หรือ BANGKOK CABLE
	เดินลอย	เดินลอยยึดด้วยสายรัดเข็มขัดระยะห่าง 100 มม. โดย
		- สายไฟสำหรับ สวิทช์ไฟ ที่ไม่ใช้ ขนาด 1.0 มม. ²
		- สายไฟสำหรับ ปลั๊กไฟ ที่ไม่ใช้ ขนาด 2.5 มม. ² (แบบมีสายดิน)
		- สายไฟสำหรับ แอร์ ที่ไม่ใช้ ขนาด 10.0 มม. ²
		- สายไฟสำหรับ เครื่องทำน้ำร้อน ที่ไม่ใช้ ขนาด 10.0 มม. ²
		- สำหรับสายเมนใช้สาย PVC. ของ YAZAKI หรือ BANGKOK CABLE
		ขนาด 16.00 มม. ² ต่อห่างจากชายคาน้ำฝน 16000 มม.

- หมายเหตุ :
- ให้เดินสายดินตามระเบียบของการไฟฟ้าอย่างถูกต้อง
 - ราคากำหนด 3,000,000 บาท ใ้ไฟ ขนาด 30 Amp. 2 สาย ของ Square-D พร้อมสายเมน
ต้นแบบชุดรีด 16 ช่อง
 - ราคากำหนด 5,000,000 บาท ใ้ไฟ ขนาด 50 Amp. 2 สาย ของ Square-D พร้อมสายเมน

รายการเปลี่ยนแปลงเพิ่มเติมไฟฟ้า

* ไม่มีรายการเปลี่ยนแปลง

โครงการ
แบบบ้านยิ้มเพื่อประชาชน

ตามนโยบาย
ม.ร.ว. สุขุมพันธุ์ บริพัตร
ผู้ว่าราชการกรุงเทพมหานคร

โดยสำนักงานโยธา
กรุงเทพมหานคร

บ้าน SMILE HOME
V.1 [11/2/45]

ได้รับความอนุเคราะห์แบบ
จาก
บริษัท แลนด์ โสม
(ประเทศไทย) จำกัด

สัญลักษณ์ประกอบแบบ "S"

รายการสัญลักษณ์

สัญลักษณ์	ความหมาย	ขนาด และ จำนวนอุปกรณ์ที่ใช้
	ท่อรวม	ท่อ PVC. Ø 4" ขึ้นคุณภาพ Class 8.5 ติดตั้งให้มีความลาดเอียง 1 : 200 ปลายท่อ- ให้ท่อแบบ 3 ทาง ตัว T
	ท่อน้ำทิ้ง	(ท่อนม) ท่อ PVC. Ø 2" ขึ้นคุณภาพ Class 8.5 ติดตั้งให้มีความลาดเอียง 1 : 200 ให้ท่อน้ำทิ้งให้เสถียร
	ท่อน้ำทิ้ง	(ต่อจากสัญลักษณ์) ท่อ PVC. Ø 1 1/2" ขึ้นคุณภาพ Class 8.5
	ท่อน้ำดี	(ท่อน้ำประปา) ท่อ PVC. Ø 1/2" ขึ้นคุณภาพ Class 13.5
	ท่อน้ำเย็น	(ท่อนม) ท่อ PVC. Ø 3/4" ขึ้นคุณภาพ Class 13.5
	ท่อน้ำร้อน	ใช้ท่อเหล็กอบสังกะสี Class B Ø 1/2"
	ท่อระบายอากาศ	ท่อ PVC Ø 1" ขึ้นคุณภาพ Class 8.5 ปลายท่อด้วยข้อต่อ 3 ทาง ตัว T ท่อระบายอากาศสูงจากพื้น 3500 มม. ยึดติดกับผนังหรือเสาด้วยระยะห่าง 300 มม.
	ท่อระบายน้ำเสีย	ท่อซีเมนต์ใยหิน Ø 150 มม. ติดตั้งให้มีความลาดเอียง 1 : 200 ข้อต่อบริเวณท่อกับ- บ่อพักให้ท่อน้ำเข้าในบ่อพักอย่างน้อย 50 มม.
	จุดระบายน้ำทิ้ง	ตำแหน่งที่จุดระบายน้ำทิ้งจะลงซึ่งต้องลงท่อน้ำทิ้งมีแผ่นเหล็กตะแกรงดักสิ่ง
	จุดระบายน้ำทิ้ง	ตำแหน่งจุดน้ำทิ้งจากชักโครก
	บ่อพัก	บ่อพักน้ำเสียสำเร็จรูป ขนาด 300X400X400 มม. พร้อมฝาปิดทึบ 6.00 ม. ทุกช่วงพักเสีย
	จุดจ่ายน้ำประปา	จุดจ่ายน้ำดี (ประปา) ซึ่งต้องสูงให้ได้ตามแบบ
	บ่อน้ำ	ใช้ระบบน้ำบาดาลเสีย ถึงบ่อน้ำบาดาลสำเร็จรูป ของ AQUA-PAC หรือเทียบเท่า
	มิเตอร์น้ำ	ตามมาตรฐานของการประปา
	เครื่องปั๊มน้ำ	ตำแหน่งตามแบบ
	แนวลาดเอียง	ลาดเอียงตามแบบ

- หมายเหตุ :
1. ท่อ PVC. ที่ข้อต่อทุกจุดจะต้องทากาวก่อนต่อ เมื่อต่อท่อเสร็จเรียบร้อยแล้วให้รีบรัดขึ้น
 2. ท่อน้ำดีจะต้องมีสัญลักษณ์ที่ข้อต่อผ่านของเหล็กทุกจุดและบริเวณรอยต่อระหว่างท่อ PVC.
เข้ากับข้อต่อเหล็กจะต้องพันท่อน้ำดี เมื่อต่อท่อเสร็จเรียบร้อยแล้วให้รีบรัดขึ้น
 3. ท่อประปา (น้ำร้อน) ที่ต่อกับสายอ่อนให้ใช้ข้อต่อทุกจุด
 4. ท่อระบายน้ำและบ่อพักต้องจากตัวอาคาร ถึงบ่อพักสาธารณะไม่เกิน 16.00 ม.


รายการประกอบแบบสัญลักษณ์ TYPE "S"

อ่างอาบน้ำ (ถักม)	CRISTINA (TEENA-D) CT-5013 C พร้อมเดินสายไฟฟ้า และ ท่อน้ำร้อนของเครื่องทำน้ำร้อน 1 ชุด (ไม่รวมเครื่องทำน้ำร้อน) ก๊อปปี้ JAZZ STD. A 7601 (AMERICAN STANDARD)
อ่างล้างหน้า	AMERICAN STANDARD รุ่น TF-476 ซีเนตติ้งคานด์อร์ , ก๊อปปี้ JAZZ STD. A 7000 พร้อมอุปกรณ์ติดตั้ง
ก๊อกฉนวน	ใช้แบบ BALL VALVE (ทักม)
โถชักโครก	AMERICAN STANDARD รุ่น TF-2310 (ทักม) , สายชำระ HANG 5502 , รุ่น TF-2310 (คนี)
ฝักบัวสายอ่อน	JAZZ STD. A 7003 A (AMERICAN STANDARD)
ที่วางสบู่	AMERICAN STANDARD รุ่น TF-9000
ที่ใส่กระดาษชำระ	AMERICAN STANDARD รุ่น TF-9001
ราชมทวน	AMERICAN STANDARD รุ่น TF-9085
กระจกเงา	กระจกเงาเรียบ ยึดด้วยหมุด
สีผนัง	สีไม่เย็นทักม BEIGE ยกเว้นห้องน้ำคนใช้ ใช้สีขาว

รายการประกอบแบบสัญลักษณ์ กรณีมีการเปลี่ยนแปลงเพิ่มเติม

* ไม่มีรายการเปลี่ยนแปลง

รายการเปลี่ยนแปลงเพิ่มเติมสัญลักษณ์

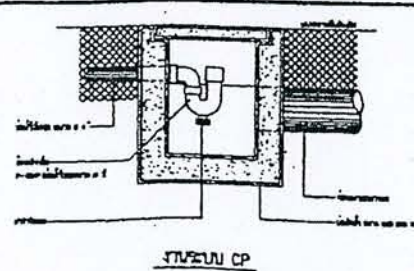

ท่อน้ำทิ้งที่เข้าตัวบ้านให้ซ่อนอยู่
บ่อพักสำเร็จรูป ดูแบบแยกต่างหาก

* ไม่มีรายการเปลี่ยนแปลง

บ้าน SMILE HOME
V.1 [11/2/45]



โครงการ
แบบบ้านยืมเพื่อประชาชน

ตามนโยบาย
ม.ร.ว. สุขุมพันธุ์ บริพัตร
ผู้ว่าราชการกรุงเทพมหานคร

โดยสำนักงานโยธา
กรุงเทพมหานคร

ได้รับความอนุเคราะห์แบบ
จาก
บริษัท แลนด์ โฮม
(ประเทศไทย) จำกัด




โครงการ
แบบบ้านยืมเพื่อประชาชน

ตามนโยบาย
ม.ร.ว. สุขุมพันธุ์ บริพัตร
ผู้ว่าราชการกรุงเทพมหานคร

โดยสำนักการโยธา
กรุงเทพมหานคร

ได้รับความอนุเคราะห์แบบ
จาก
บริษัท แลนด์ โสณ
(ประเทศไทย) จำกัด

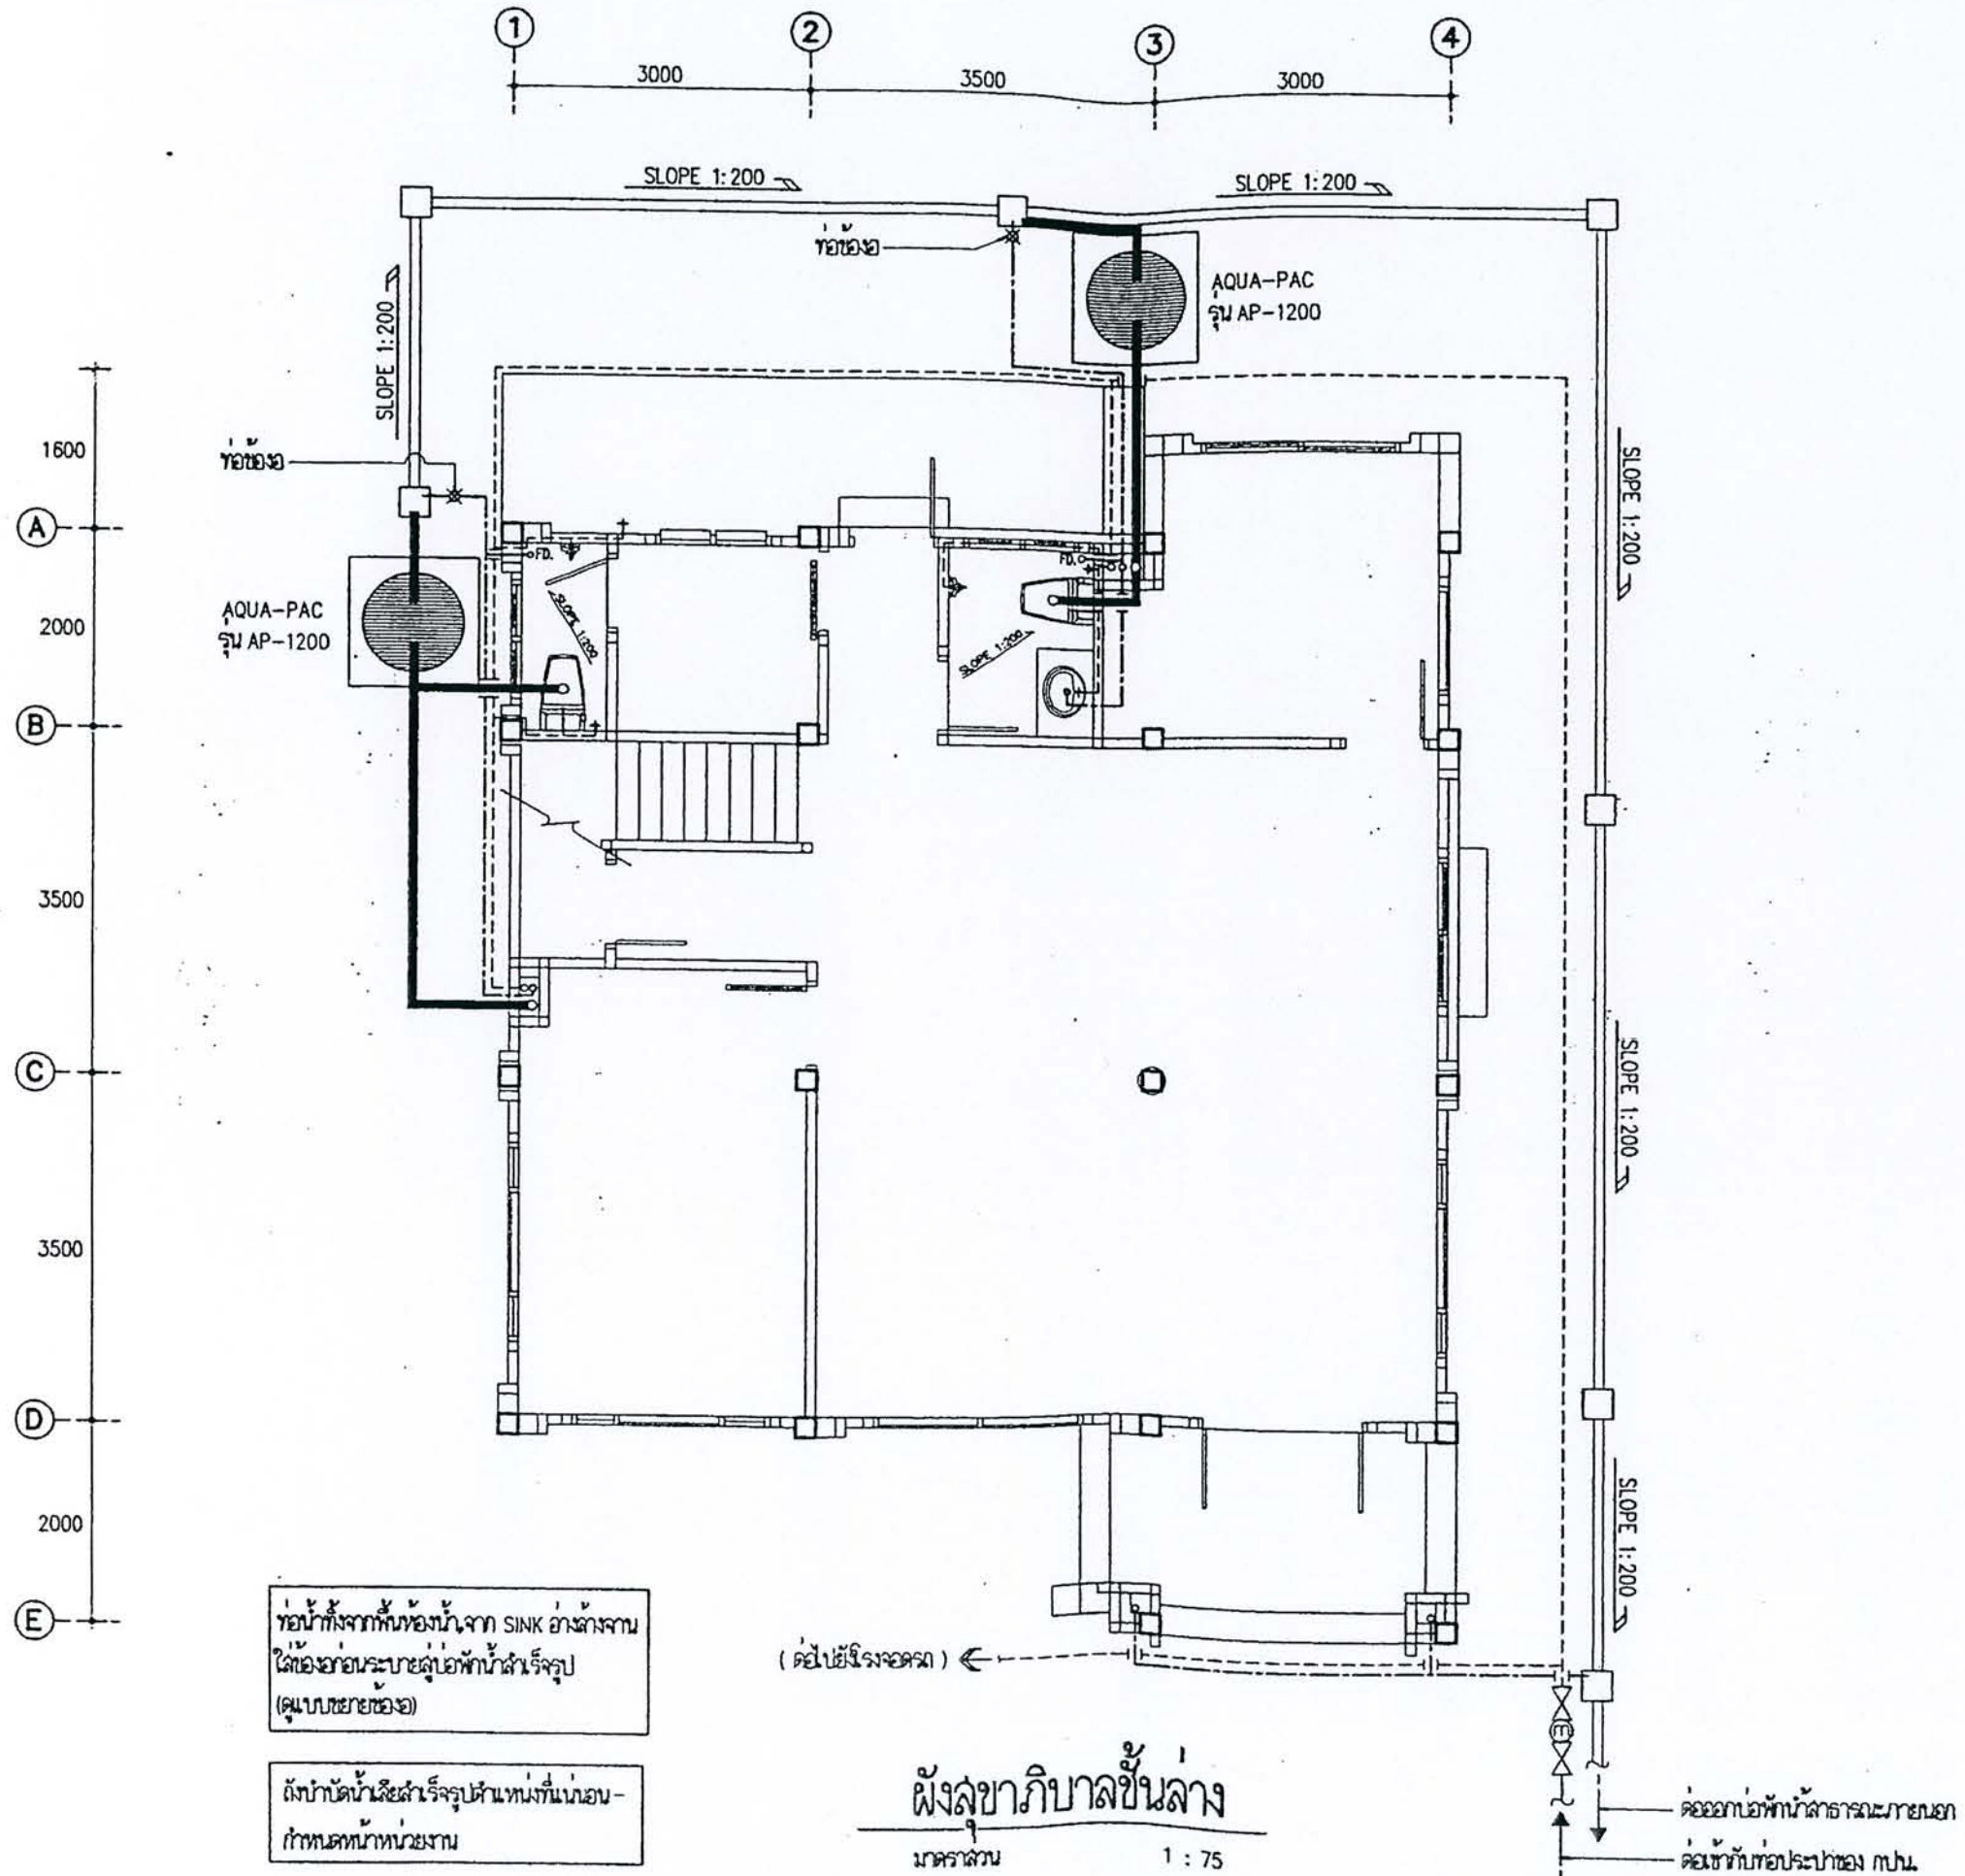




โครงการ
แบบบ้านยืมเพื่อประชาชน

ตามนโยบาย
ม.ร.ว. สุขุมพันธุ์ บริพัตร
ผู้ว่าราชการกรุงเทพมหานคร

โดยสำนักการโยธา
กรุงเทพมหานคร

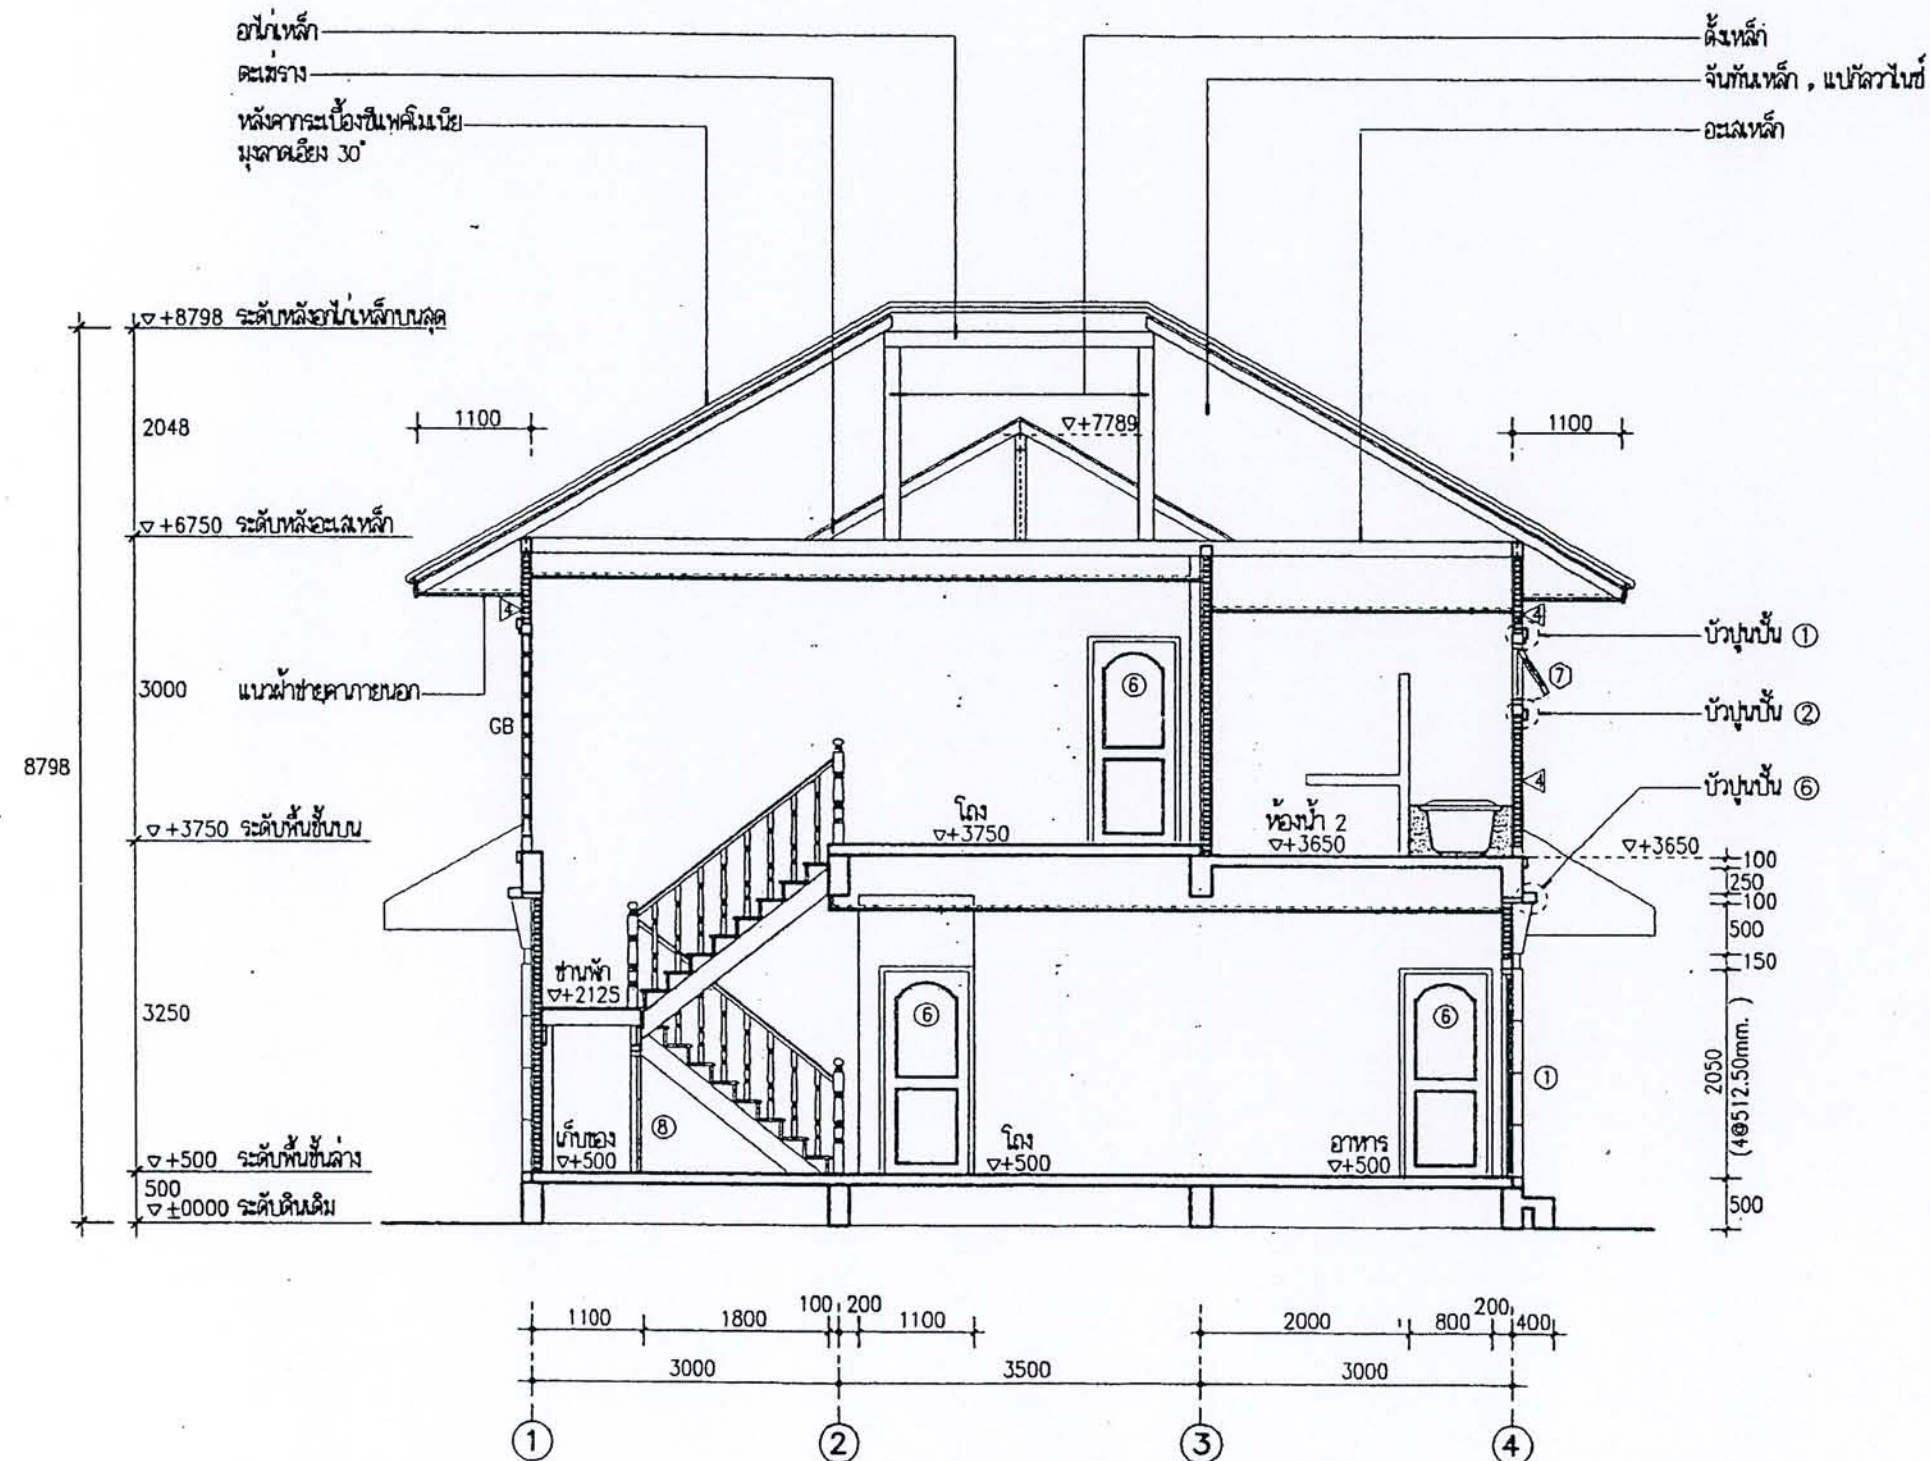

รูปตัด A-A
มาตราส่วน 1 : 75


ได้รับความอนุเคราะห์แบบ
จาก
บริษัท แลนด์ โฮม
(ประเทศไทย) จำกัด



โครงการ
แบบบ้านยืมเพื่อประชาชน

ตามนโยบาย
ม.ร.ว. สุขุมพันธุ์ บริพัตร
ผู้ว่าราชการกรุงเทพมหานคร

โดยสำนักงานโยธา
กรุงเทพมหานคร

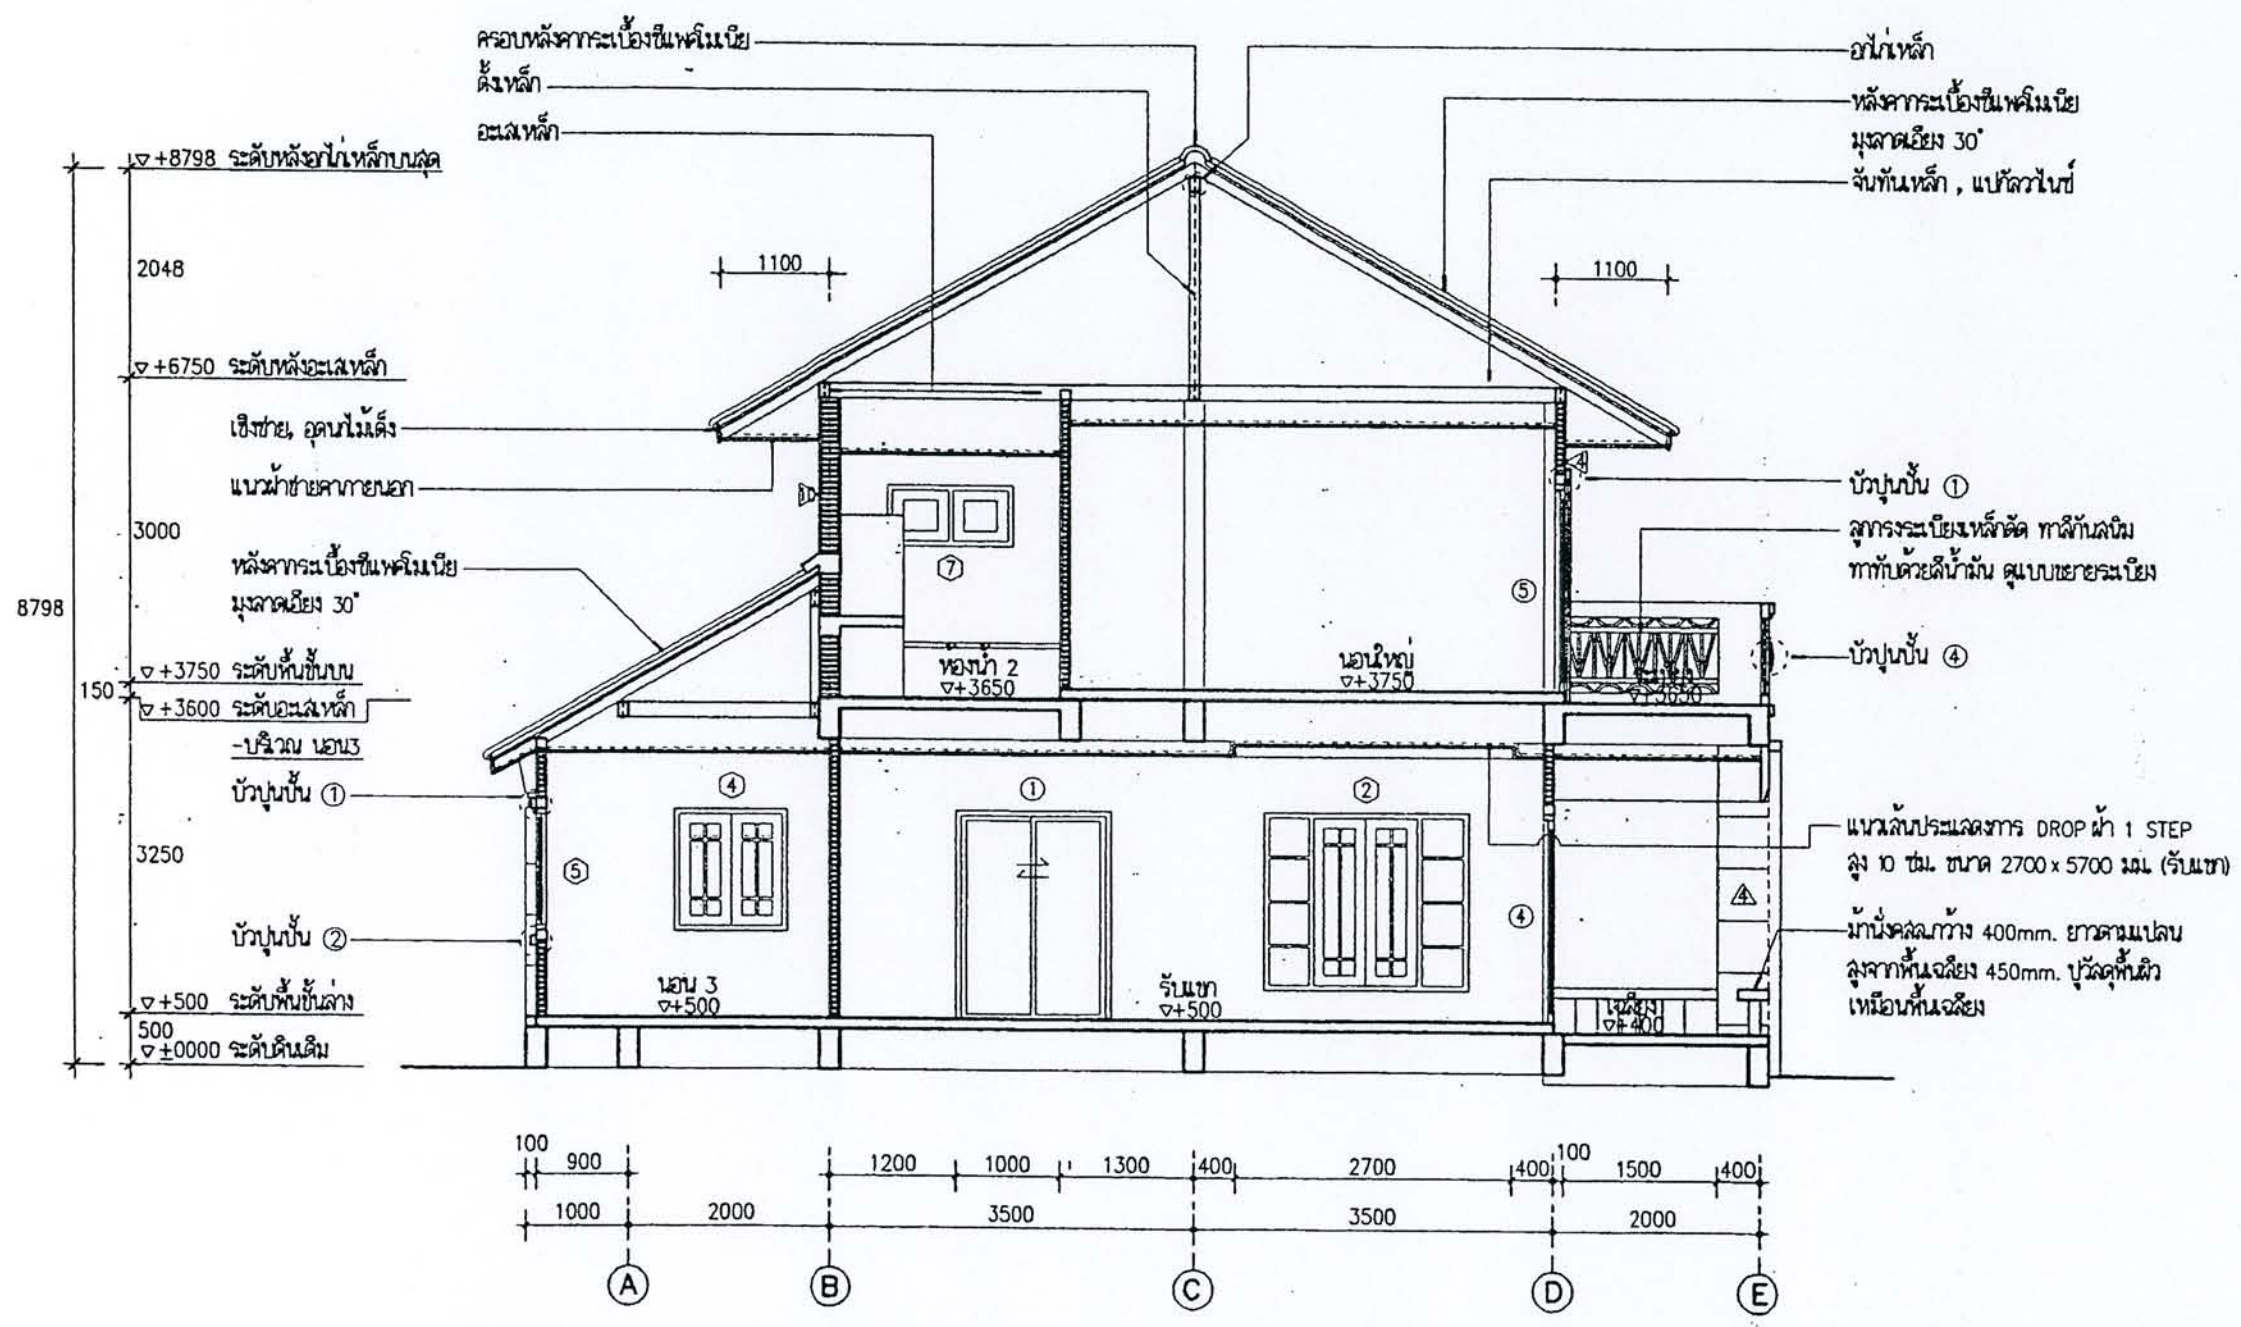

รูปตัด B-B
มาตราส่วน 1 : 75



ได้รับความอนุเคราะห์แบบ
จาก
บริษัท แลนด์ โชม
(ประเทศไทย) จำกัด




โครงการ
แบบบ้านยืมเพื่อประชาชน

ตามนโยบาย
ม.ร.ว. สุขุมพันธุ์ บริพัตร
ผู้ว่าราชการกรุงเทพมหานคร

โดยสำนักงานโยธา
กรุงเทพมหานคร

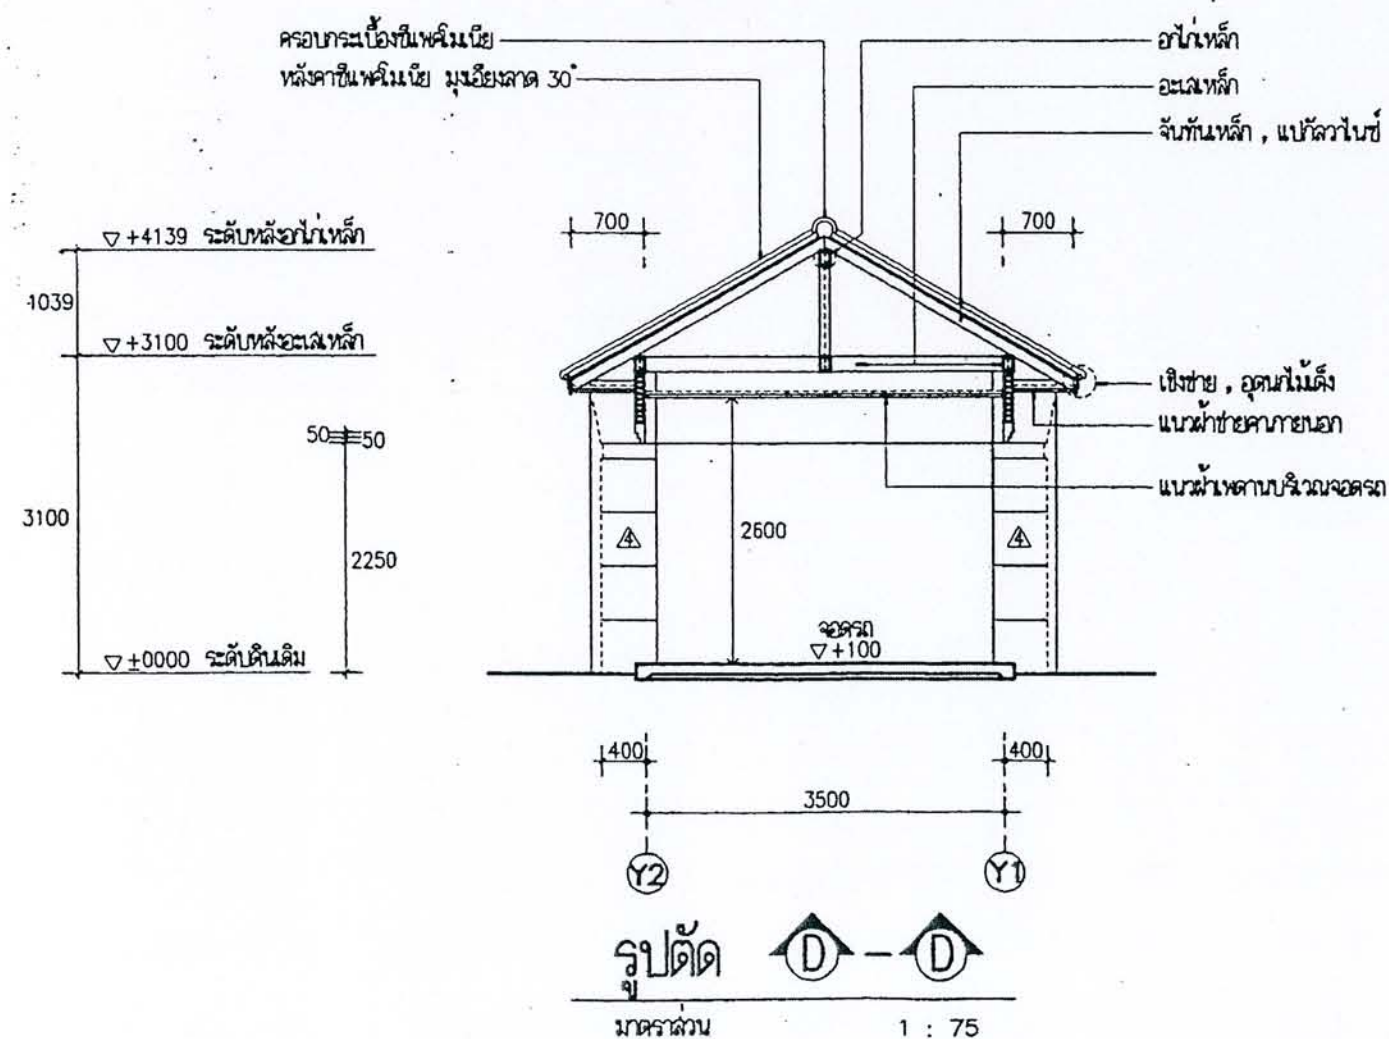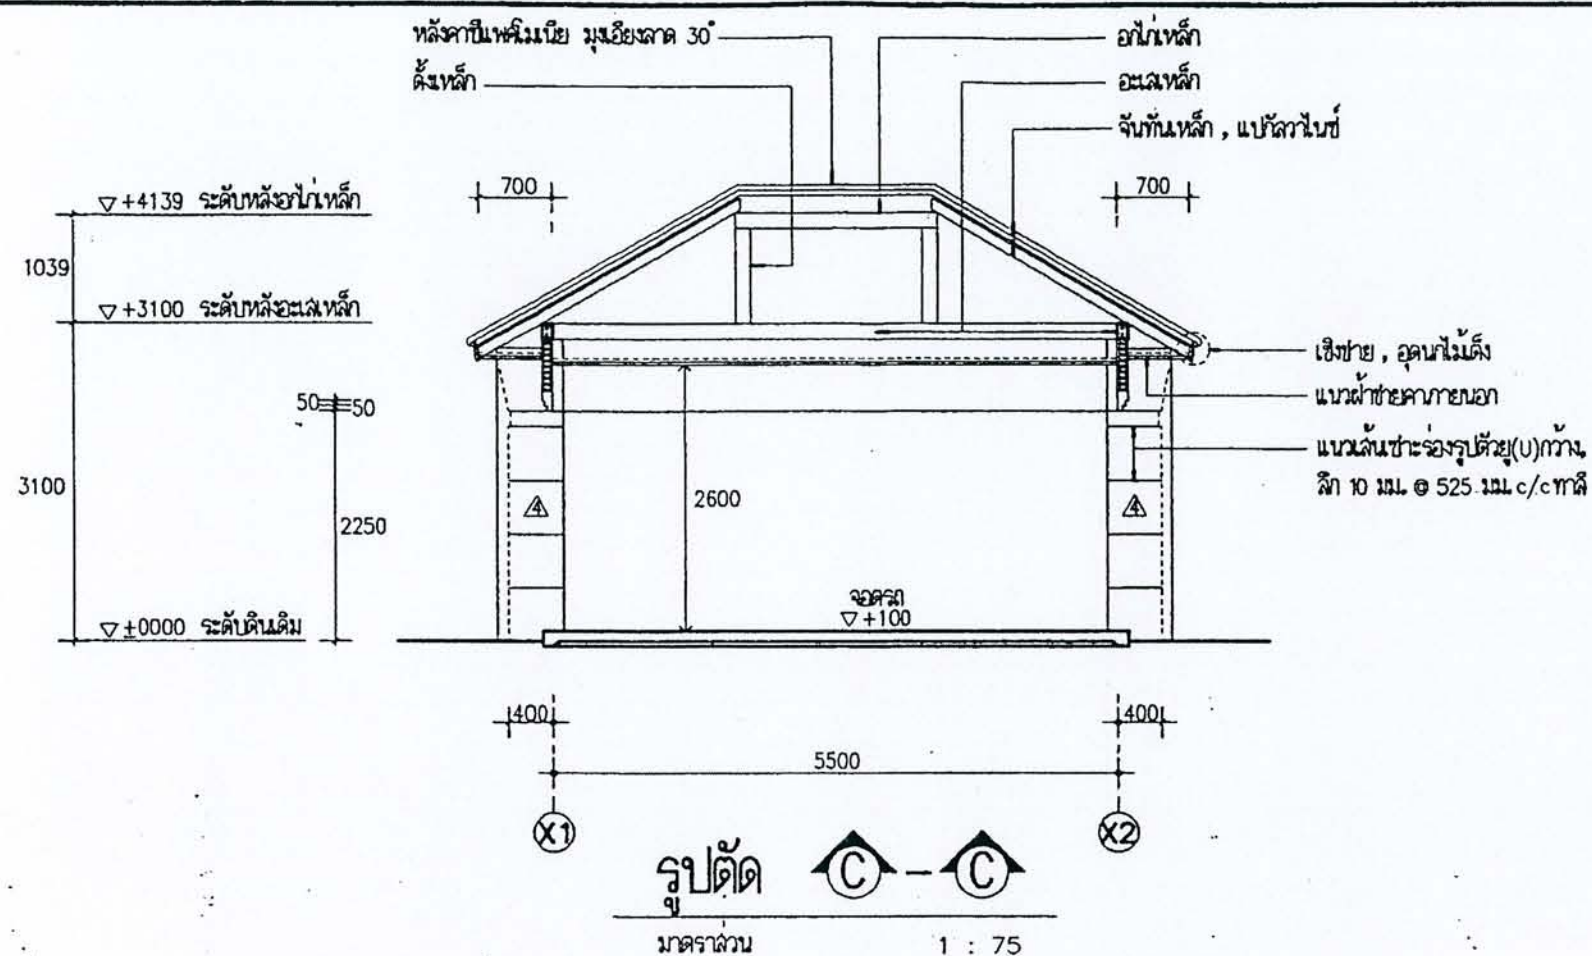


ได้รับความอนุเคราะห์แบบ
จาก
บริษัท แลนด์ โสภ
(ประเทศไทย) จำกัด

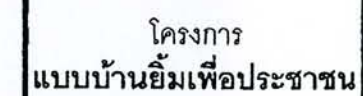

โดยสำนักงานโยธา
กรุงเทพมหานคร


ได้รับความอนุเคราะห์แบบ
จาก
บริษัท แลนด์ โยม
(ประเทศไทย) จำกัด

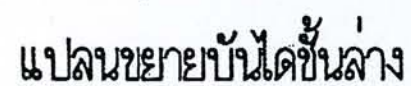

มาตรฐาน 1:50



มาตราส่วน 1:50

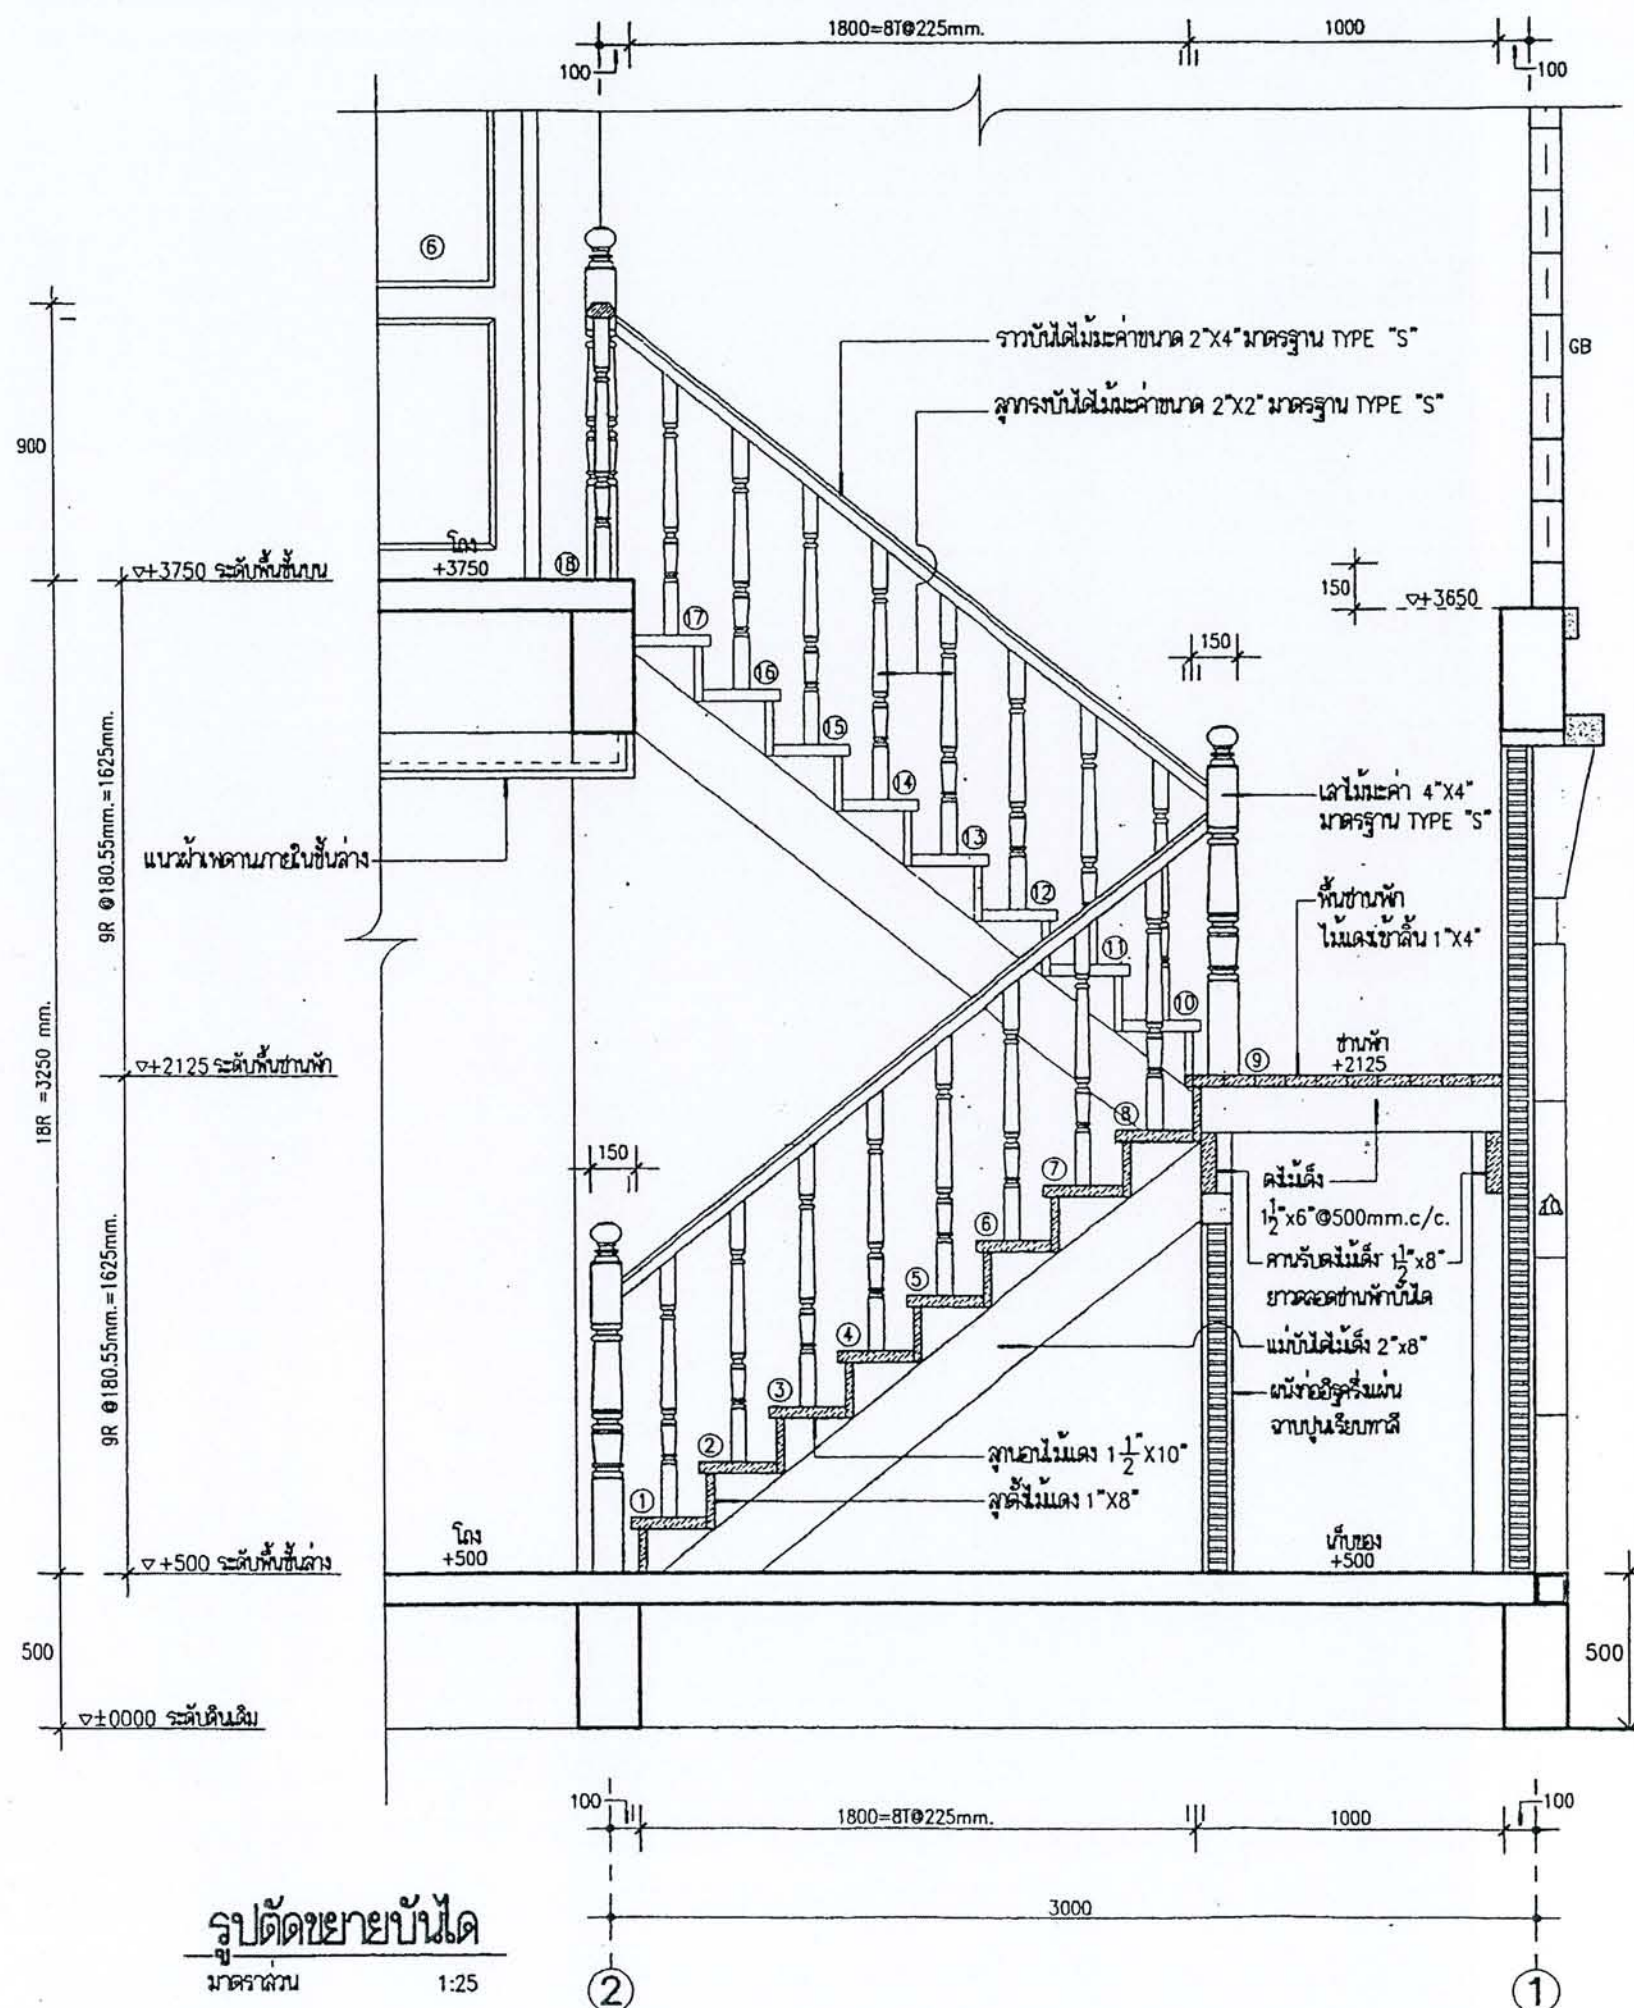

รูปตัดขยายบ้านไค



มาตราส่วน 1:25



โครงการ
แบบบ้านยืมเพื่อประชาชน

ตามนโยบาย
ม.ร.ว. สุขุมพันธุ์ บริพัตร
ผู้ว่าราชการกรุงเทพมหานคร

โดยสำนักงานโยธา
กรุงเทพมหานคร

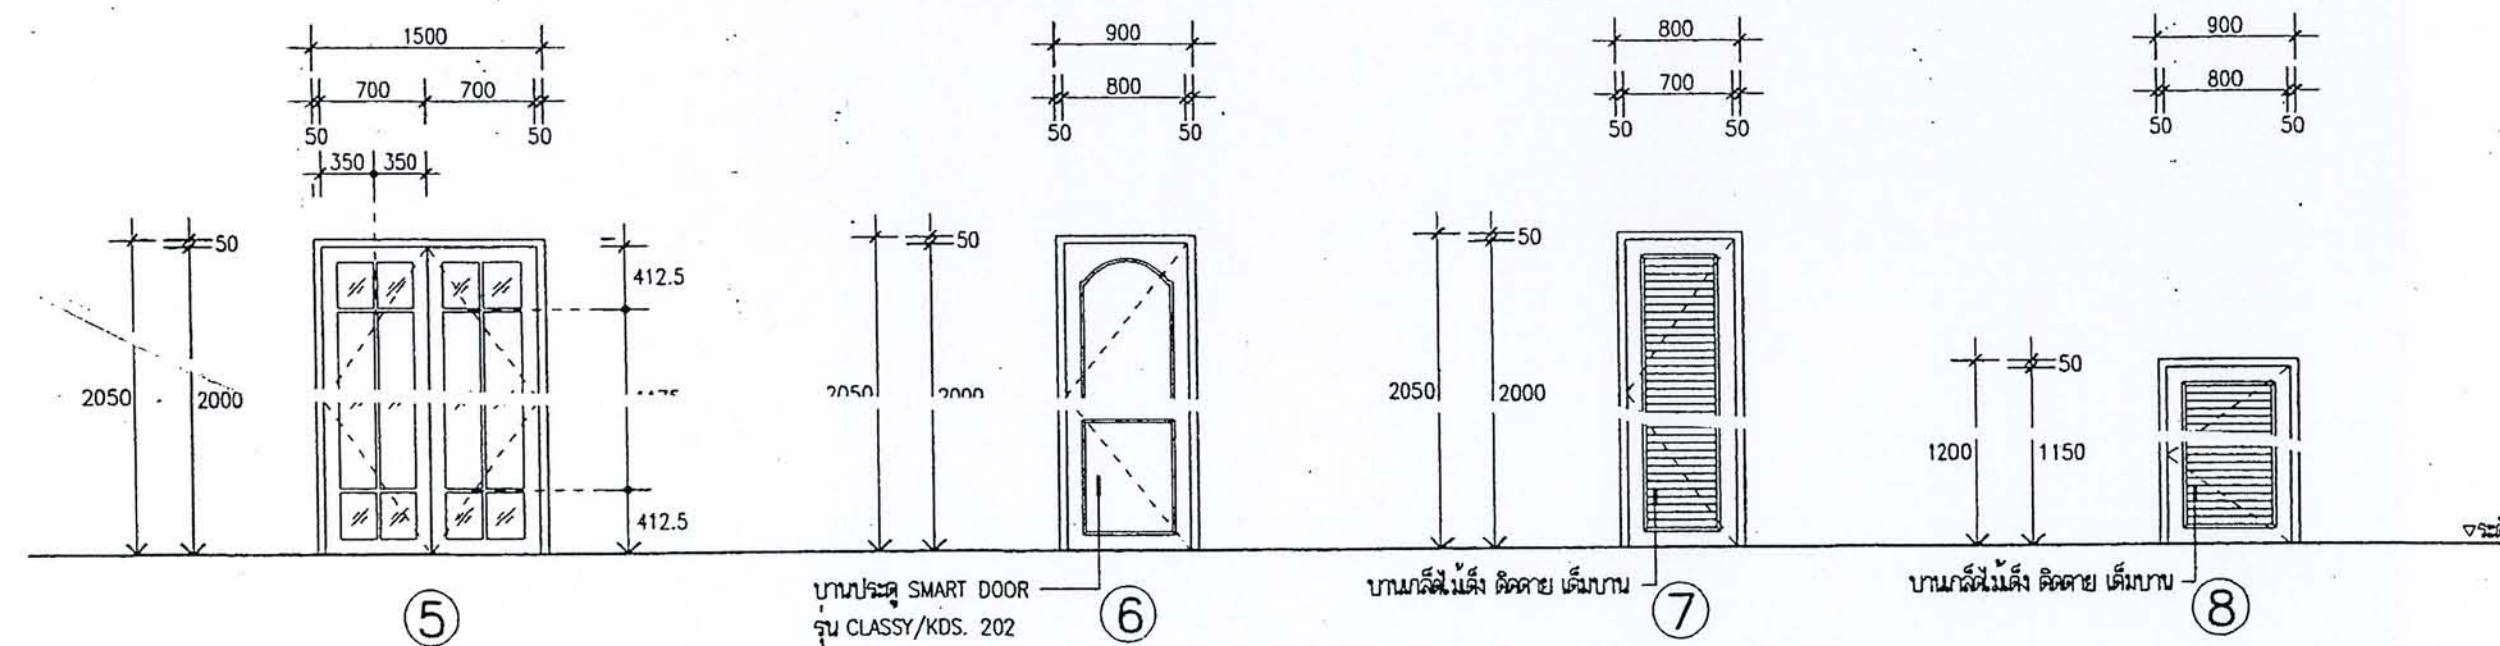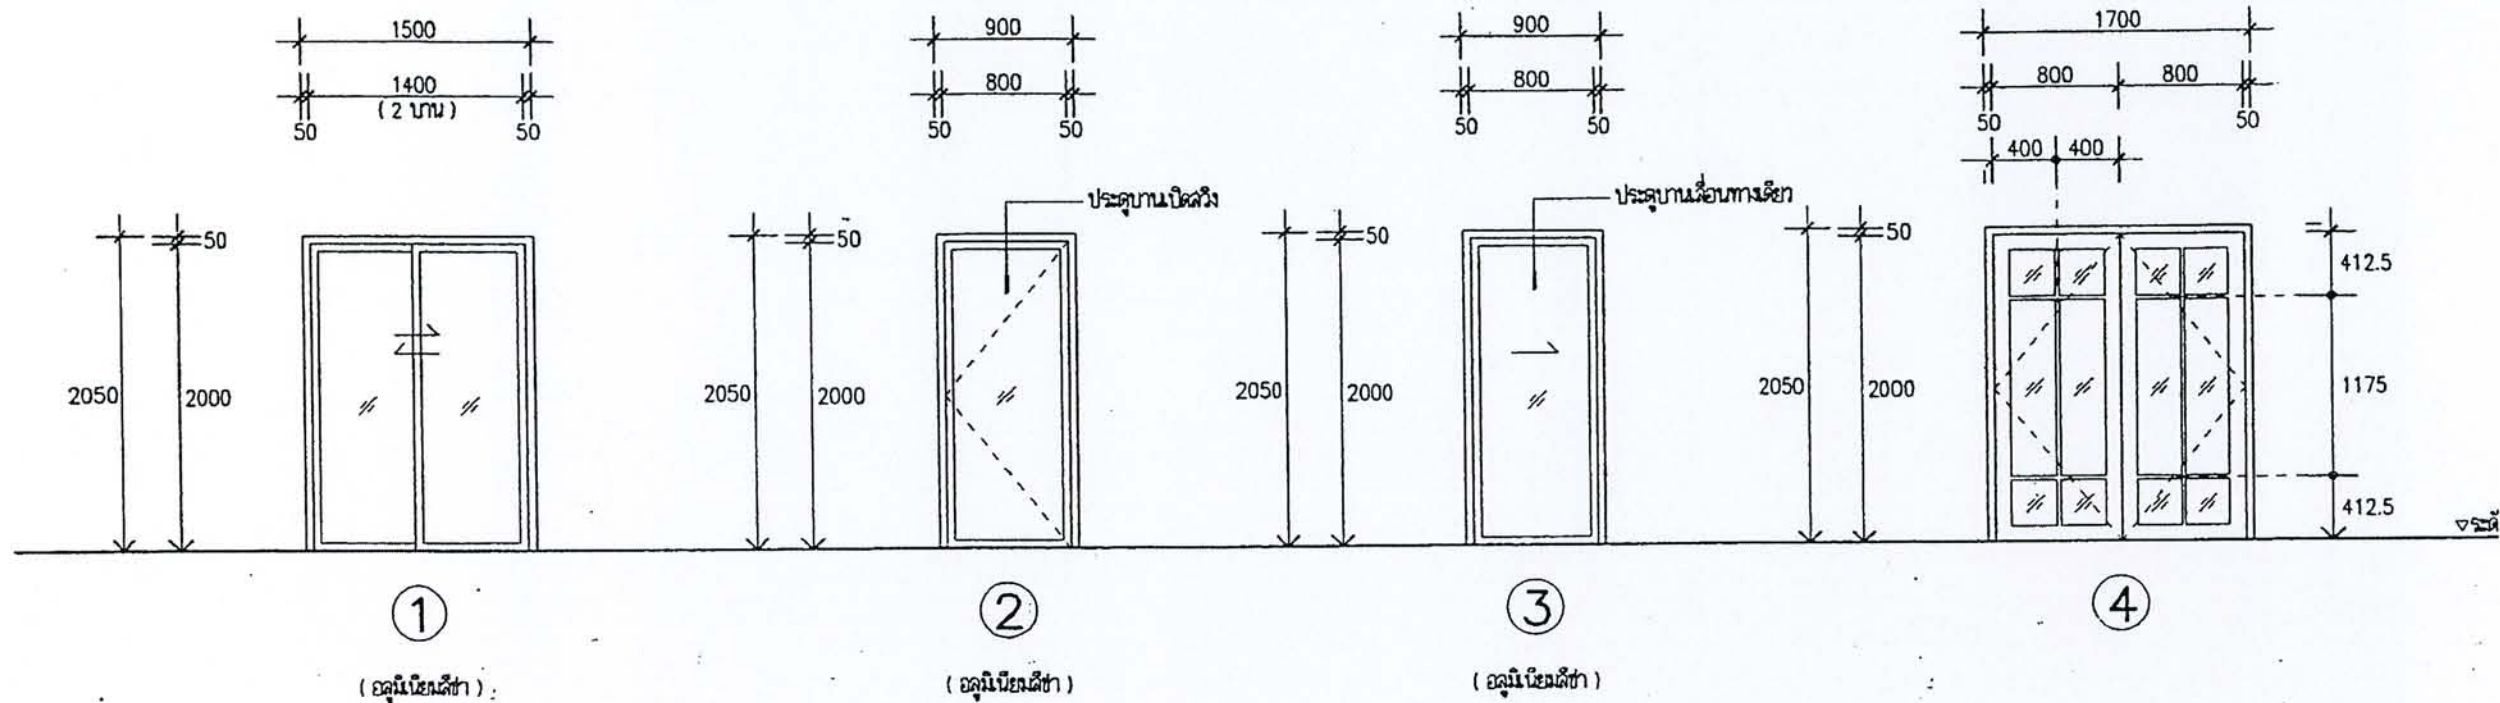

แบบขยายประตู

มาตรฐาน 1:50


ได้รับความอนุเคราะห์แบบ
จาก
บริษัท แลนด์ โยบ
(ประเทศไทย) จำกัด



ตามนโยบาย
ม.ร.ว. สุขุมพันธุ์ บริพัตร
ผู้ว่าราชการกรุงเทพมหานคร

โดยสำนักงานโยธา
กรุงเทพมหานคร

ได้รับความอนุเคราะห์แบบ
จาก
บริษัท แลนด์ โสม
(ประเทศไทย) จำกัด

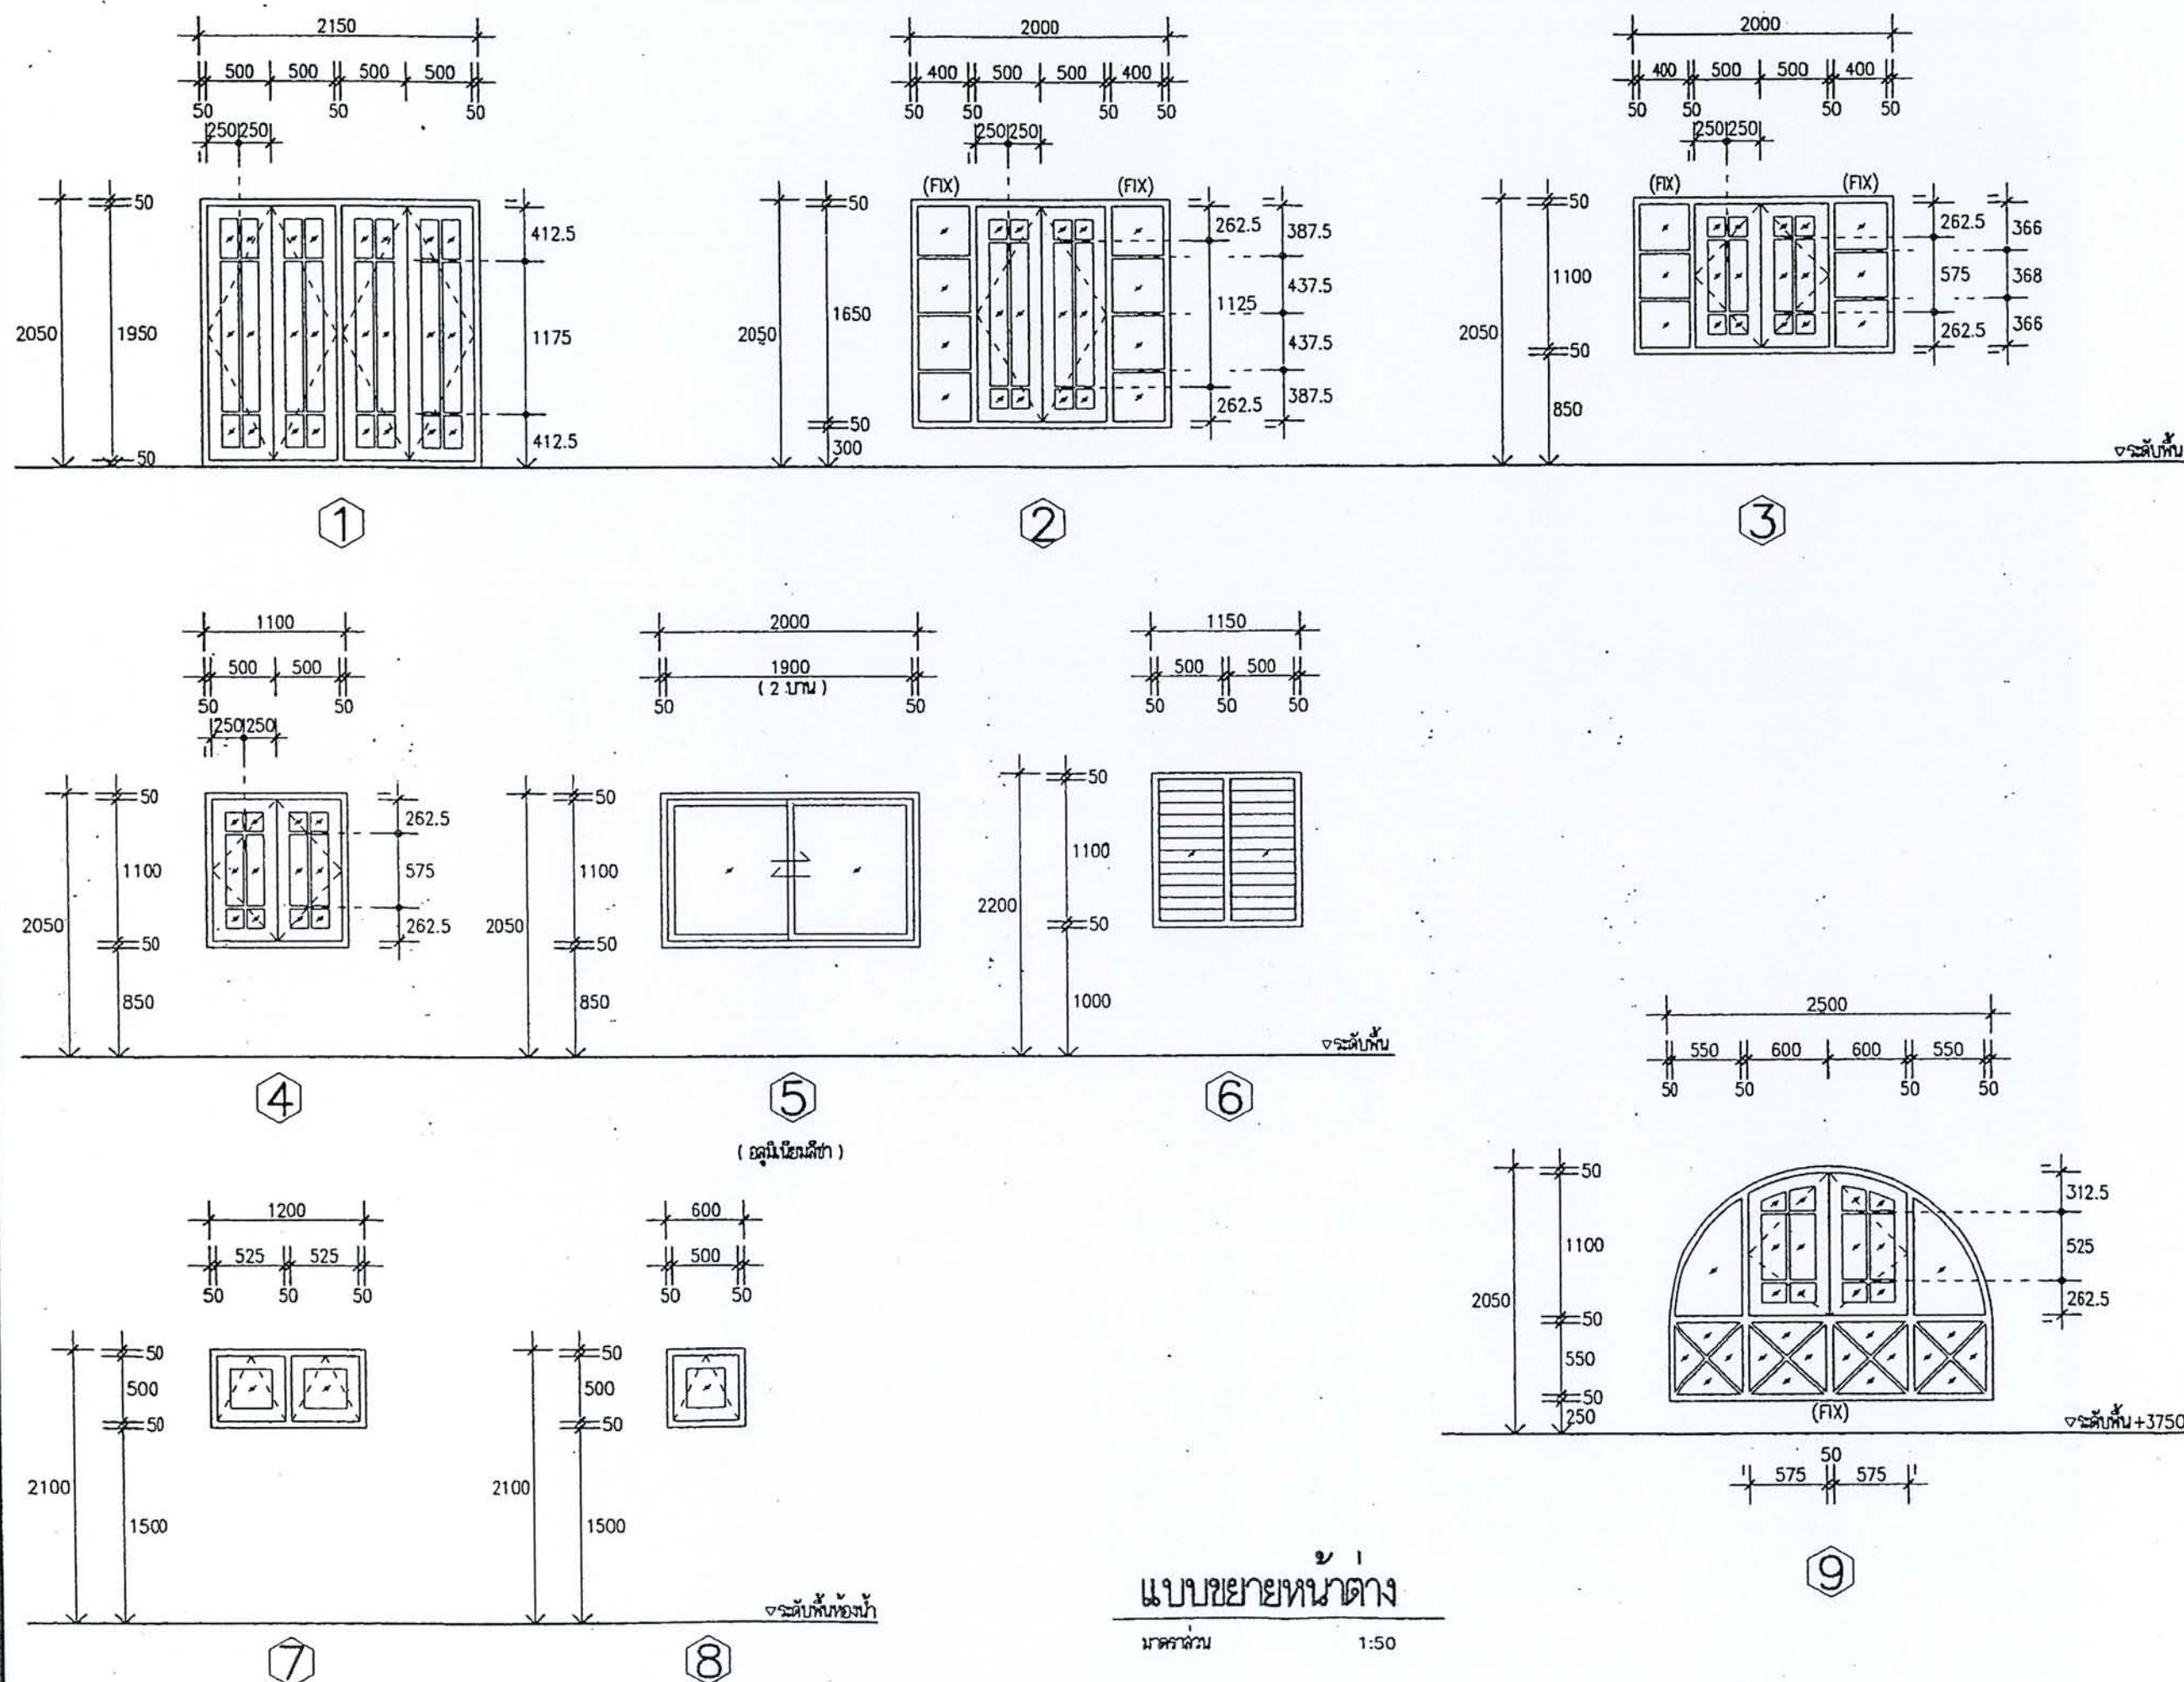





โครงการ
แบบบ้านยืมเพื่อประชาชน

ตามนโยบาย
ม.ร.ว. สุขุมพันธุ์ บริพัตร
ผู้ว่าราชการกรุงเทพมหานคร

โดยสำนักงานการโยธา
กรุงเทพมหานคร

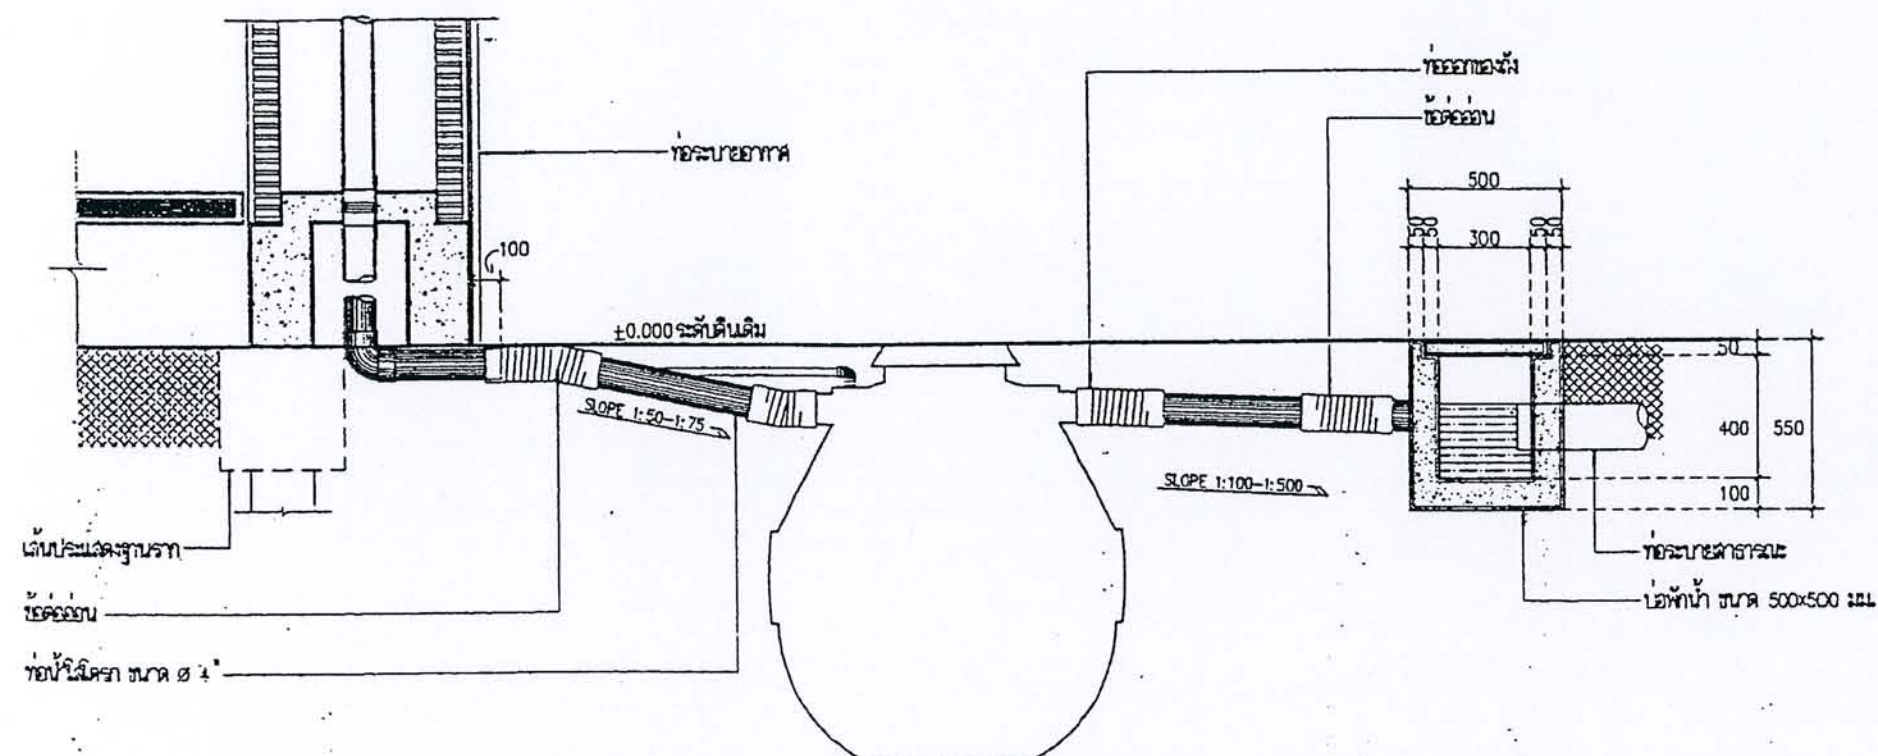

แบบขยายการวางท่อและตั้งระดับถึงบำบัดสำเร็จรูป
มาตราส่วน 1 : 25

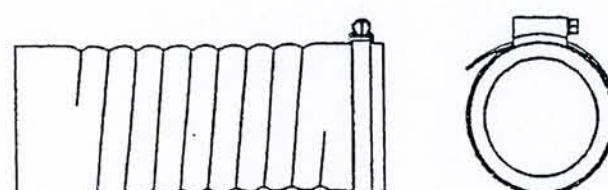

ถังตกตะกอน


ได้รับความอนุเคราะห์แบบ
จาก
บริษัท แลนด์ โสม
(ประเทศไทย) จำกัด



โครงการ
แบบบ้านยืมเพื่อประชาชน

ตามนโยบาย
ม.ร.ว. สุขุมพันธุ์ บริพัตร
ผู้ว่าราชการกรุงเทพมหานคร

โดยสำนักงานโยธา
กรุงเทพมหานคร

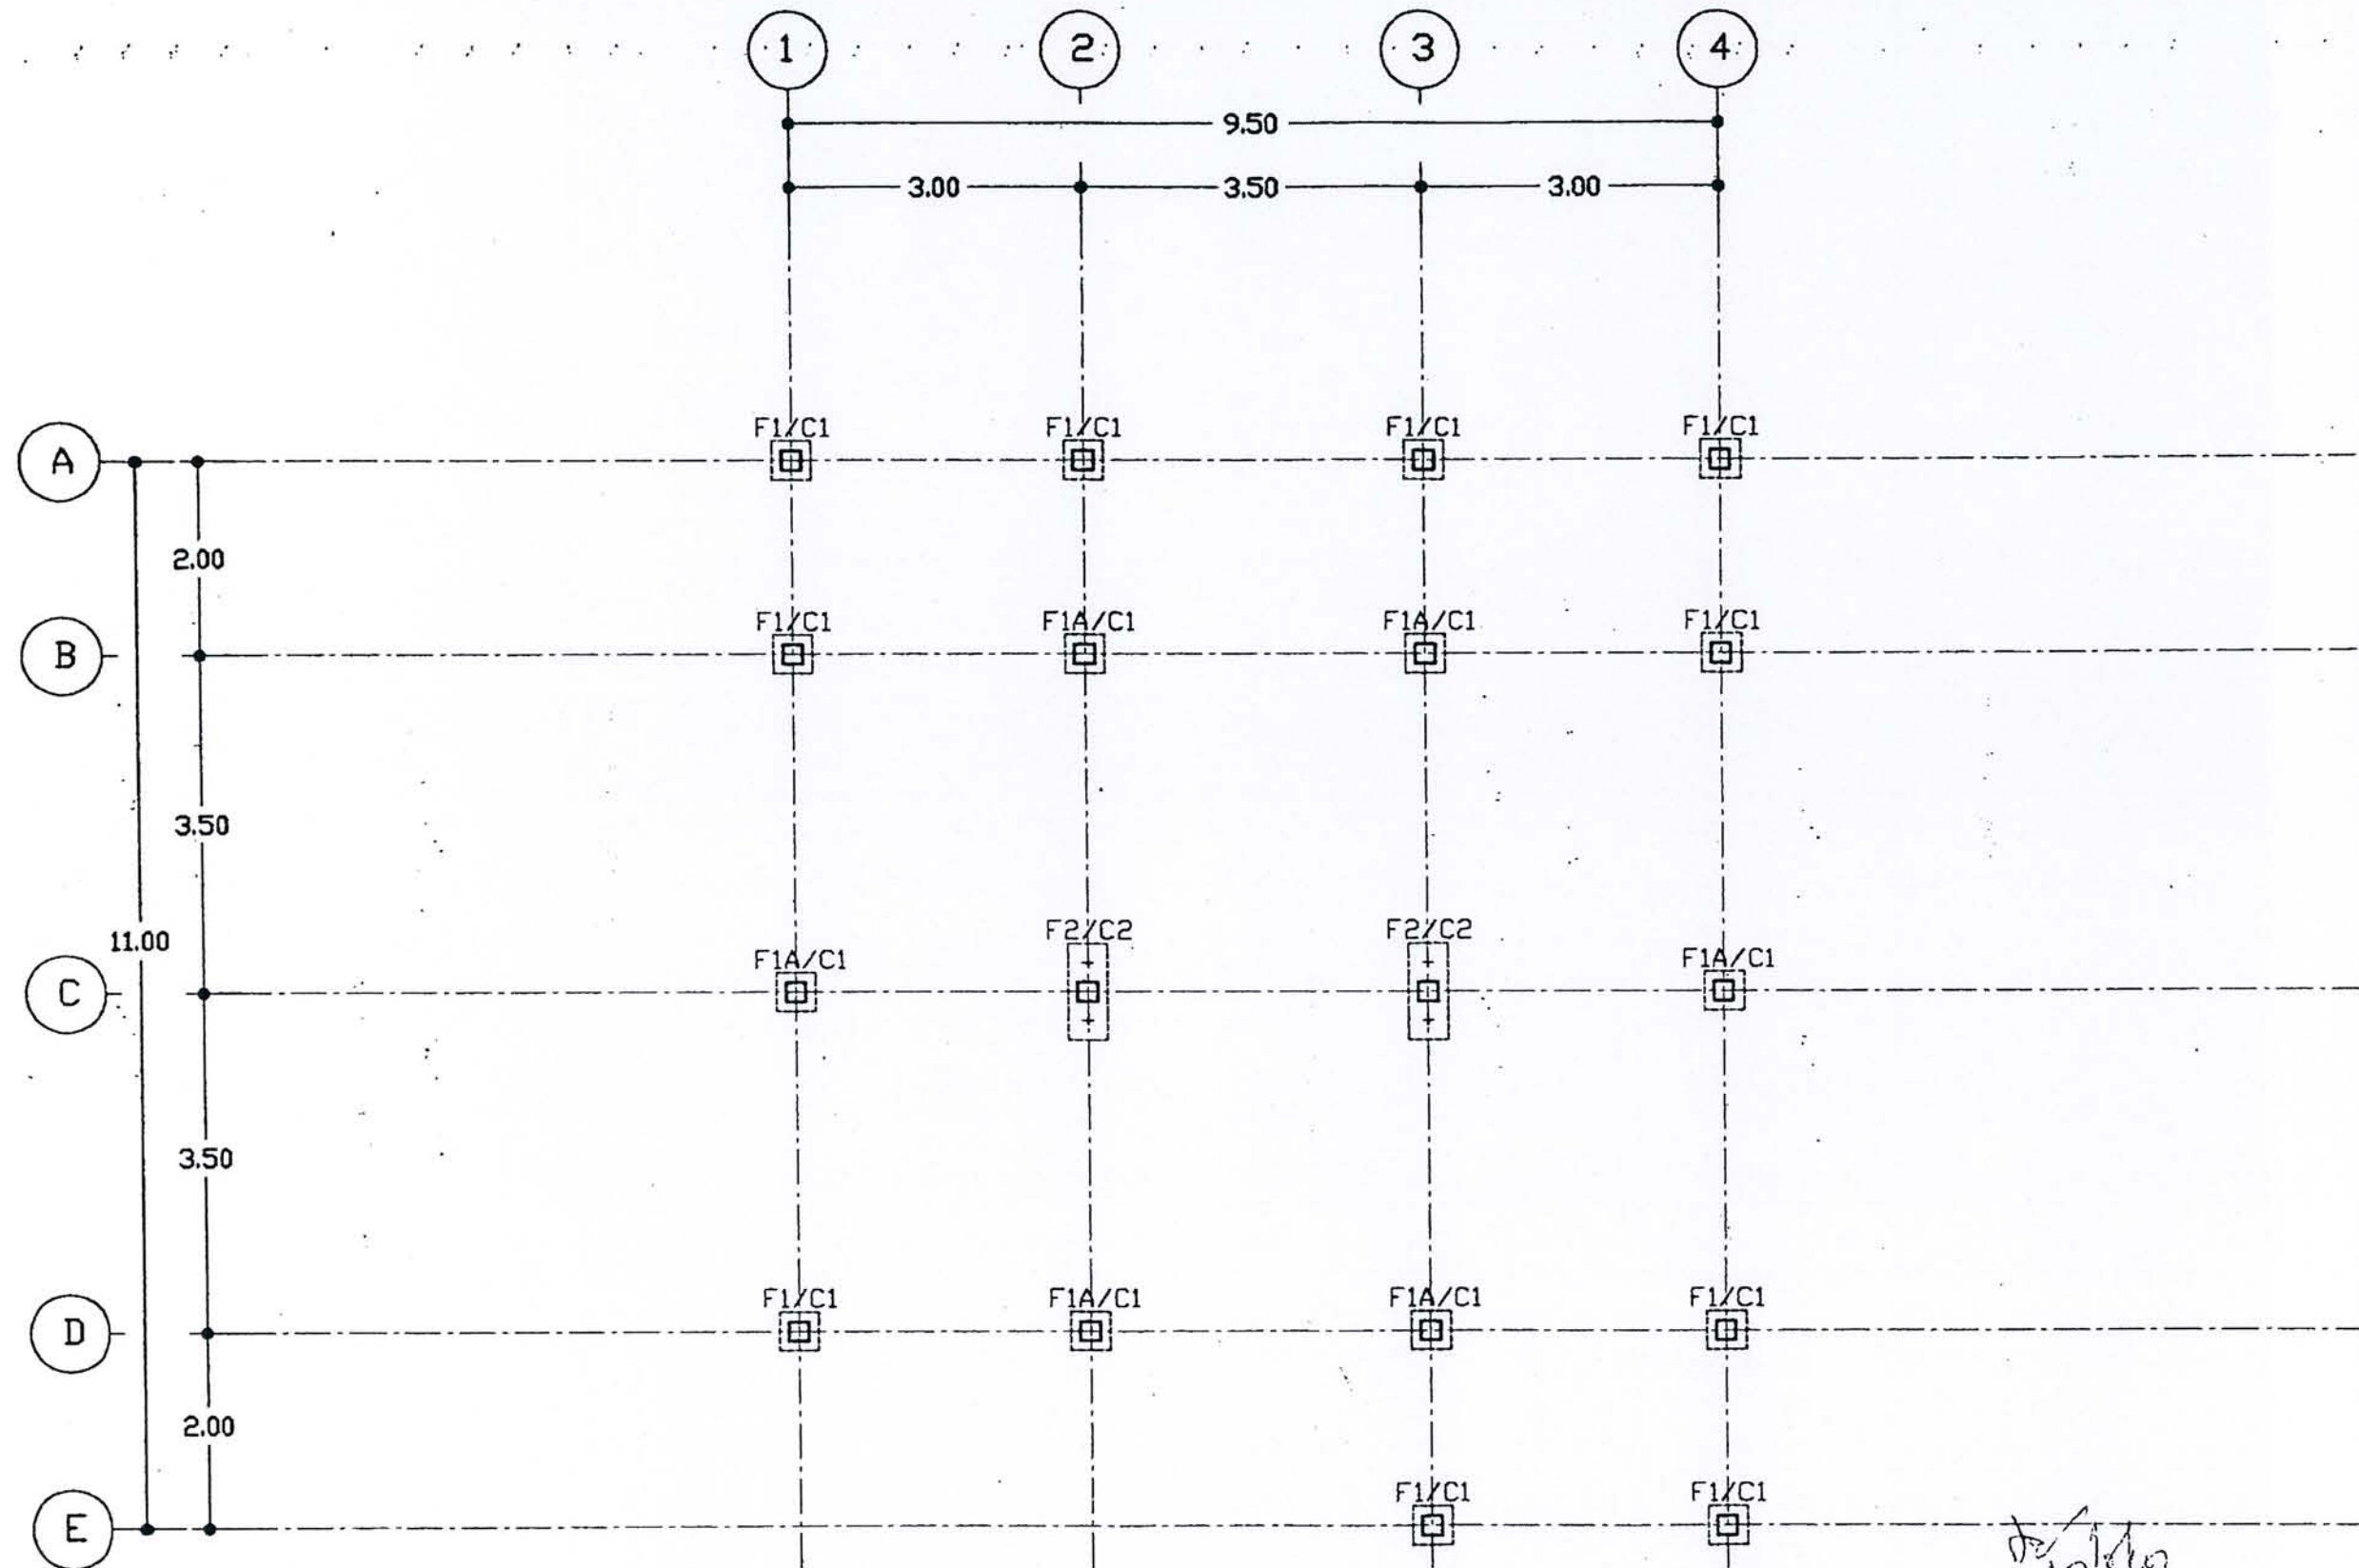

หมายเหตุ เข็ม I 0.18x0.18x16.00m. (2 ต้น ต่อปลอก) จำนวน 14 ต้น
F1 = 10 หลุม = 10 ต้น
F2 = 2 หลุม = 4 ต้น
เข็ม I 0.22x0.22x16.00m. (2 ต้น ต่อปลอก) F1A = 6 หลุม = 6 ต้น

ผังโครงสร้างฐานราก
มาตราส่วน 1:75

ได้รับความอนุเคราะห์แบบ
จาก
บริษัท แลนด์ โฮม
(ประเทศไทย) จำกัด

สำนักการโยธา กรุงเทพมหานคร




โครงการ
แบบบ้านยืมเพื่อประชาชน

ตามนโยบาย
ม.ร.ว. สุขุมพันธุ์ บริพัตร
ผู้ว่าราชการกรุงเทพมหานคร

โดยสำนักงานโยธา
กรุงเทพมหานคร

ได้รับความอนุเคราะห์แบบ
จาก
บริษัท แลนด์ โยม
(ประเทศไทย) จำกัด

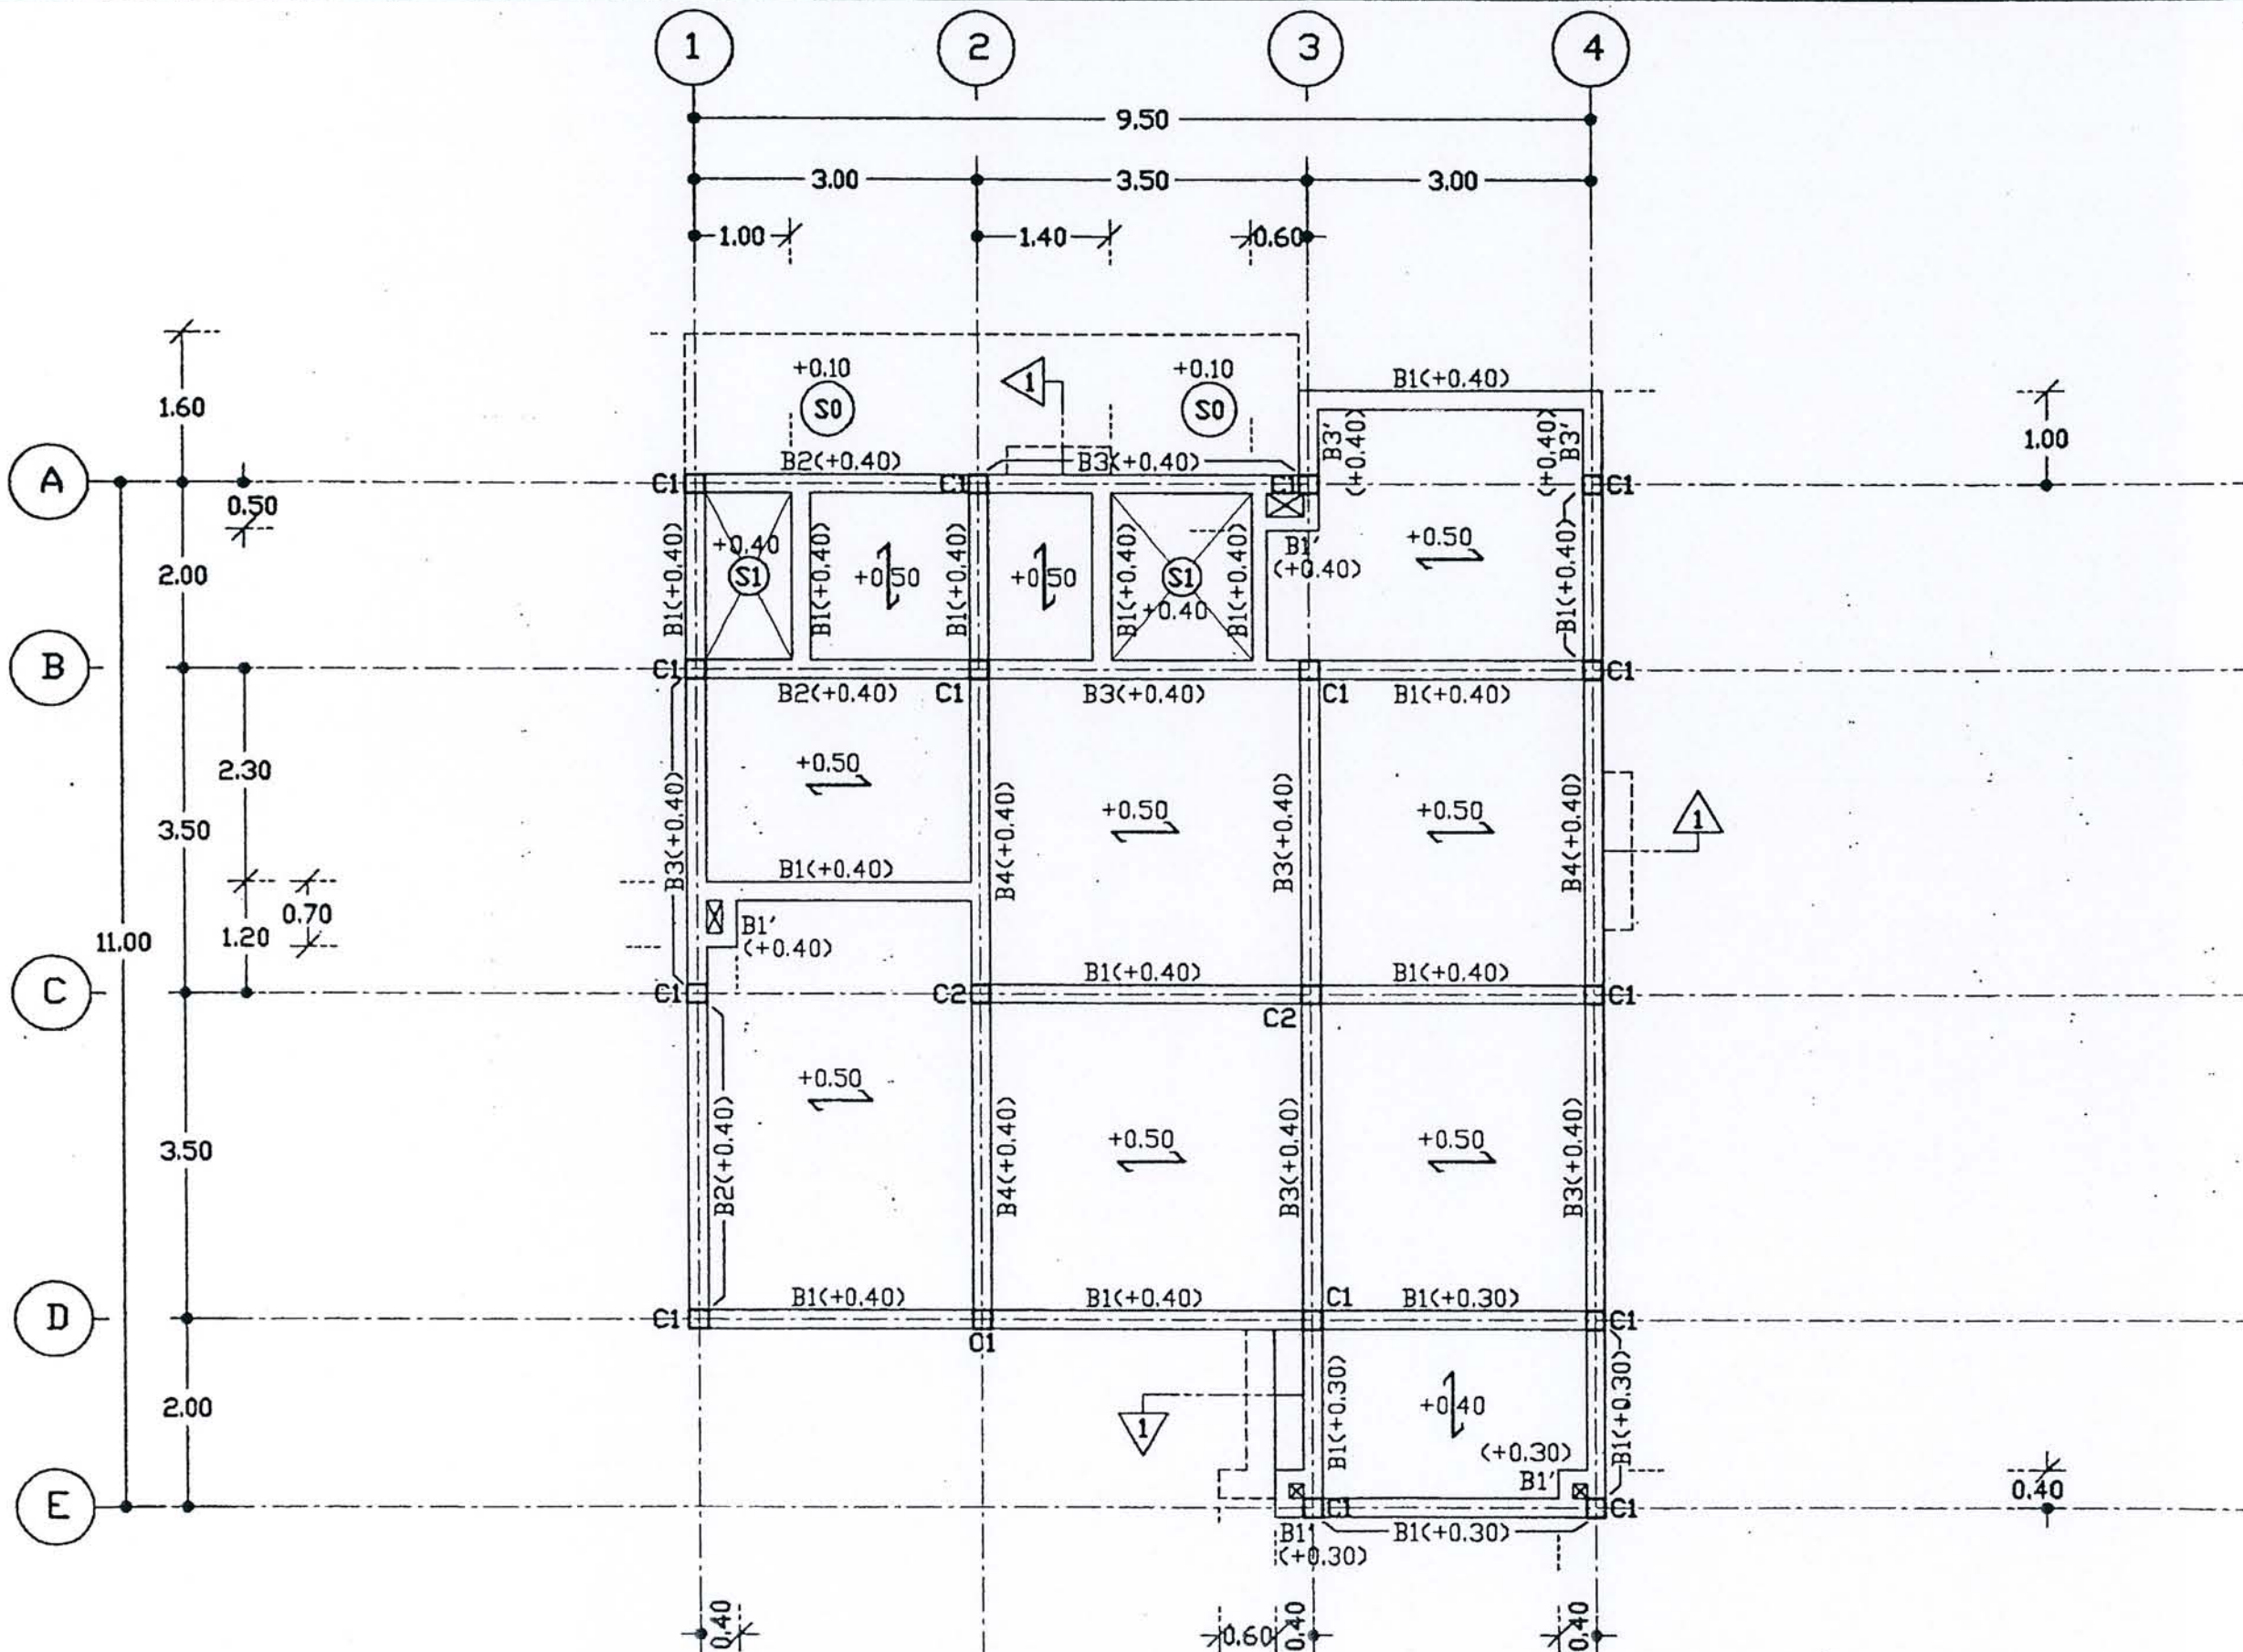

หมายเหตุ - แสดงทิศทางการวางพื้นสำเร็จรูป PLANK
- ระยะแนวคานทั้งหมดก่อนวางให้ทำการเช็คกับแปลนสถาปัตย์ด้วยทุกครั้งเพื่อป้องกันความผิดพลาด
หรือปรึกษากับผู้ควบคุมงานของทางบริษัทก่อน
- ผังสลิปที่ทอตามผังสถาปัตย์ด้วย

ผังโครงสร้างชั้นล่าง
มาตราส่วน 1:75

CND CONSULTING




โครงการ
แบบบ้านยืมเพื่อประชาชน

ตามนโยบาย
ม.ร.ว. สุขุมพันธุ์ บริพัตร
ผู้ว่าราชการกรุงเทพมหานคร

โดยสำนักงานโยธา
กรุงเทพมหานคร

ได้รับความอนุเคราะห์แบบ
จาก
บริษัท แลนด์ โฮม
ประเทศไทย จำกัด

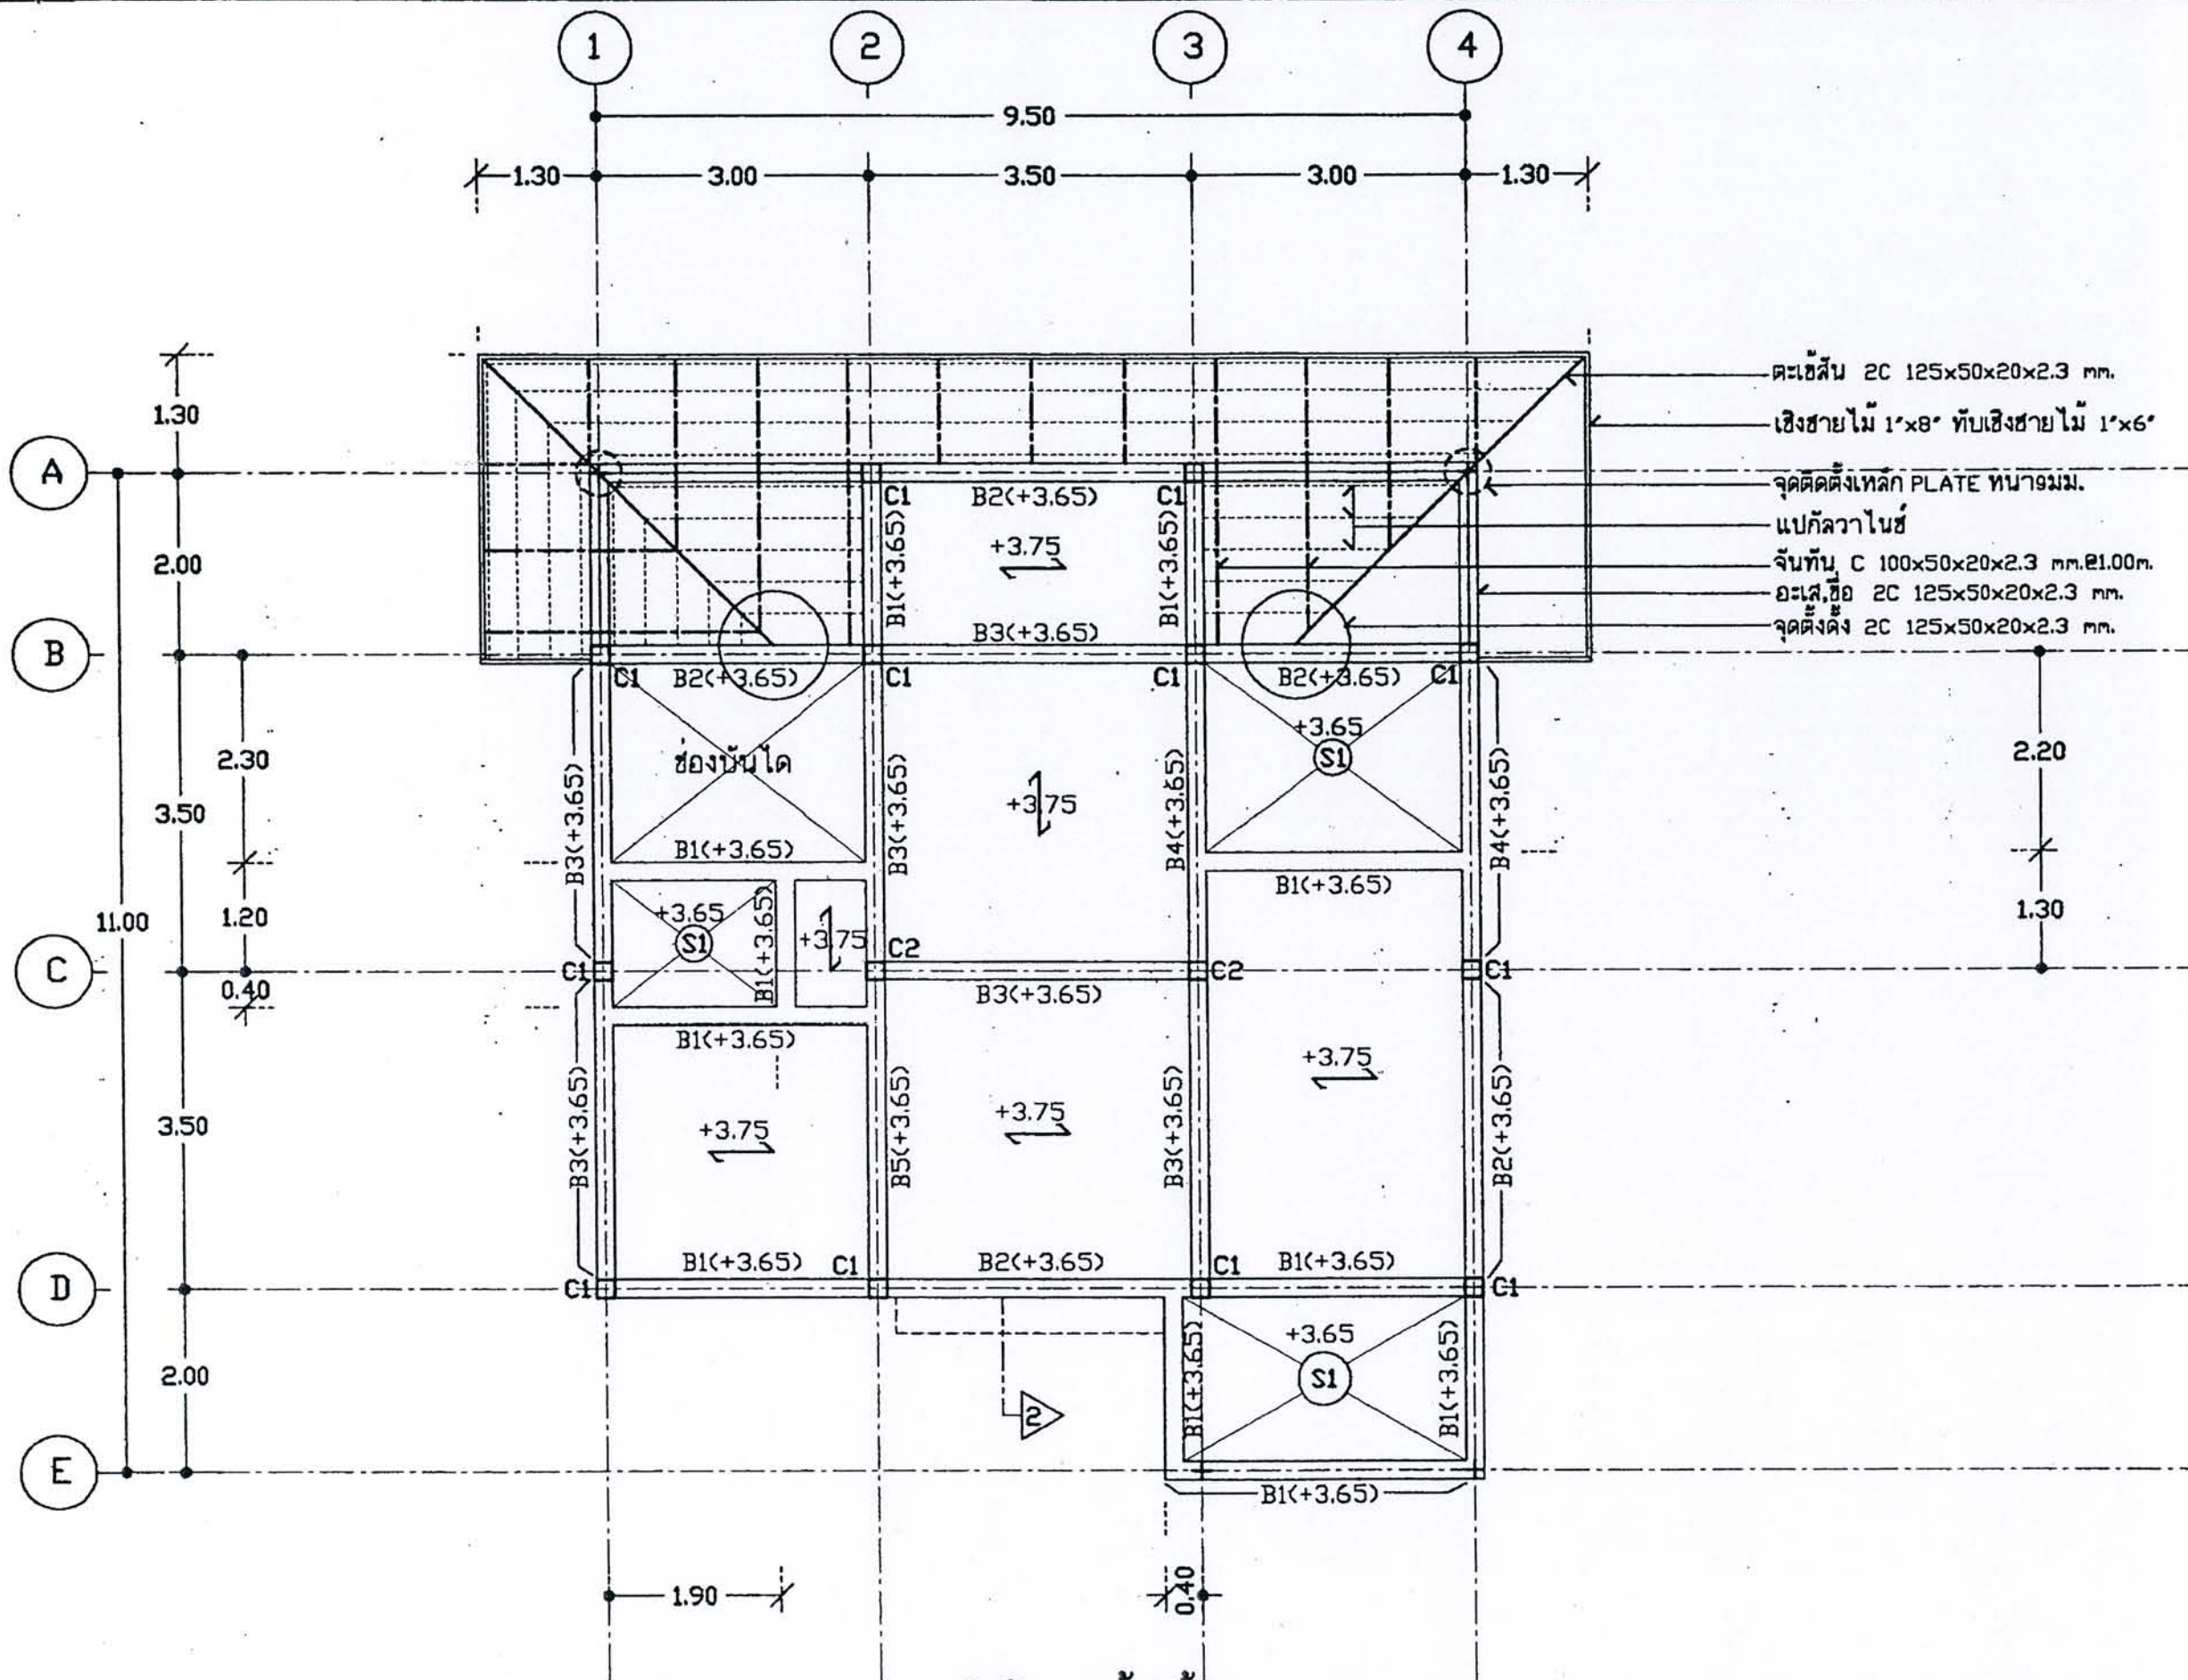

ผังโครงสร้างชั้นบน
มาตราส่วน 1:75

- ตะเข้ดิน 2C 125x50x20x2.3 มม.
- เชิงชายไม้ 1'x8' ทับเชิงชายไม้ 1'x6'
- จุดติดตั้งเหล็ก PLATE ทน 9 มม.
- แบ็กกลวไนซ์
- จันทัน C 100x50x20x2.3 มม. @ 1.00 ม.
- อะไหล่, ข้อ 2C 125x50x20x2.3 มม.
- จุดติดตั้ง 2C 125x50x20x2.3 มม.

FOR CONSTRUCTION




โครงการ
แบบบ้านยืมเพื่อประชาชน

ตามนโยบาย
ม.ร.ว. สุขุมพันธุ์ บริพัตร
ผู้ว่าราชการกรุงเทพมหานคร

โดยสำนักงานโยธา
กรุงเทพมหานคร

ได้รับความอนุเคราะห์แบบ
จาก
บริษัท แลนด์ ไชย
(ประเทศไทย) จำกัด

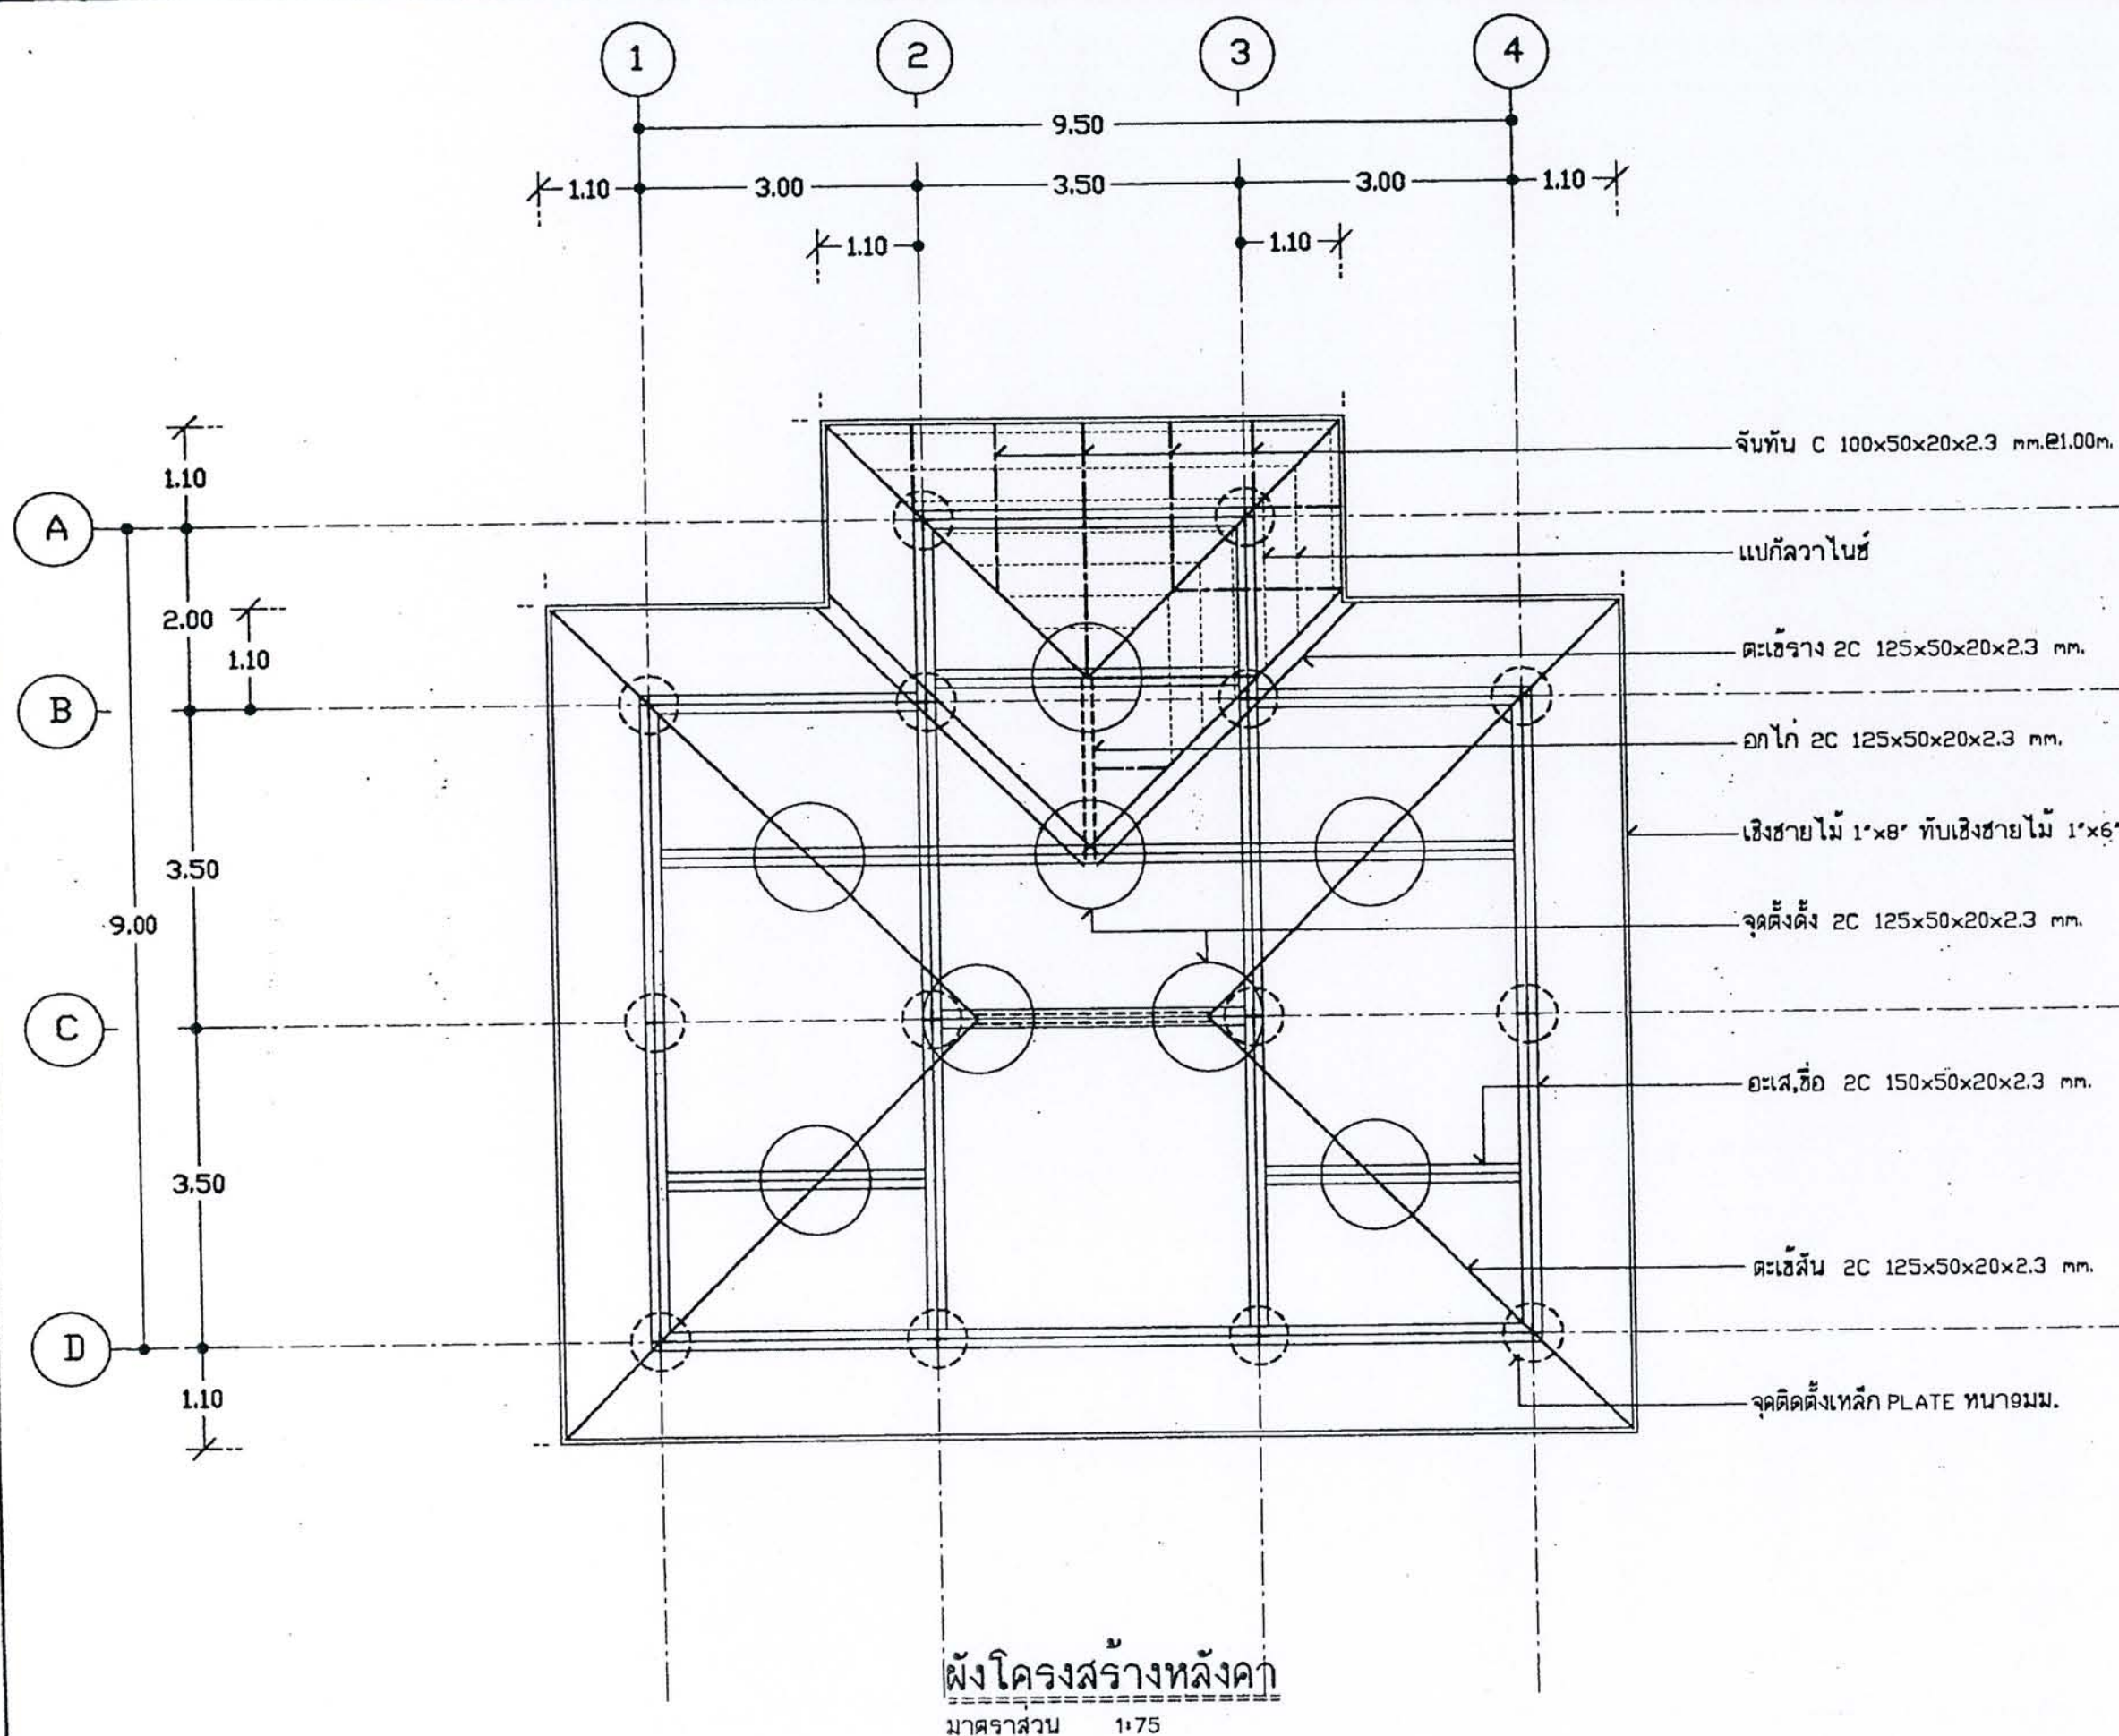


FOR CONSULT



โครงการ
แบบบ้านอิมเพื่อประชาชน

ตามนโยบาย
ม.ร.ว. สุขุมพันธุ์ บริพัตร
ผู้ว่าราชการกรุงเทพมหานคร

โดยสำนักการโยธา
กรุงเทพมหานคร

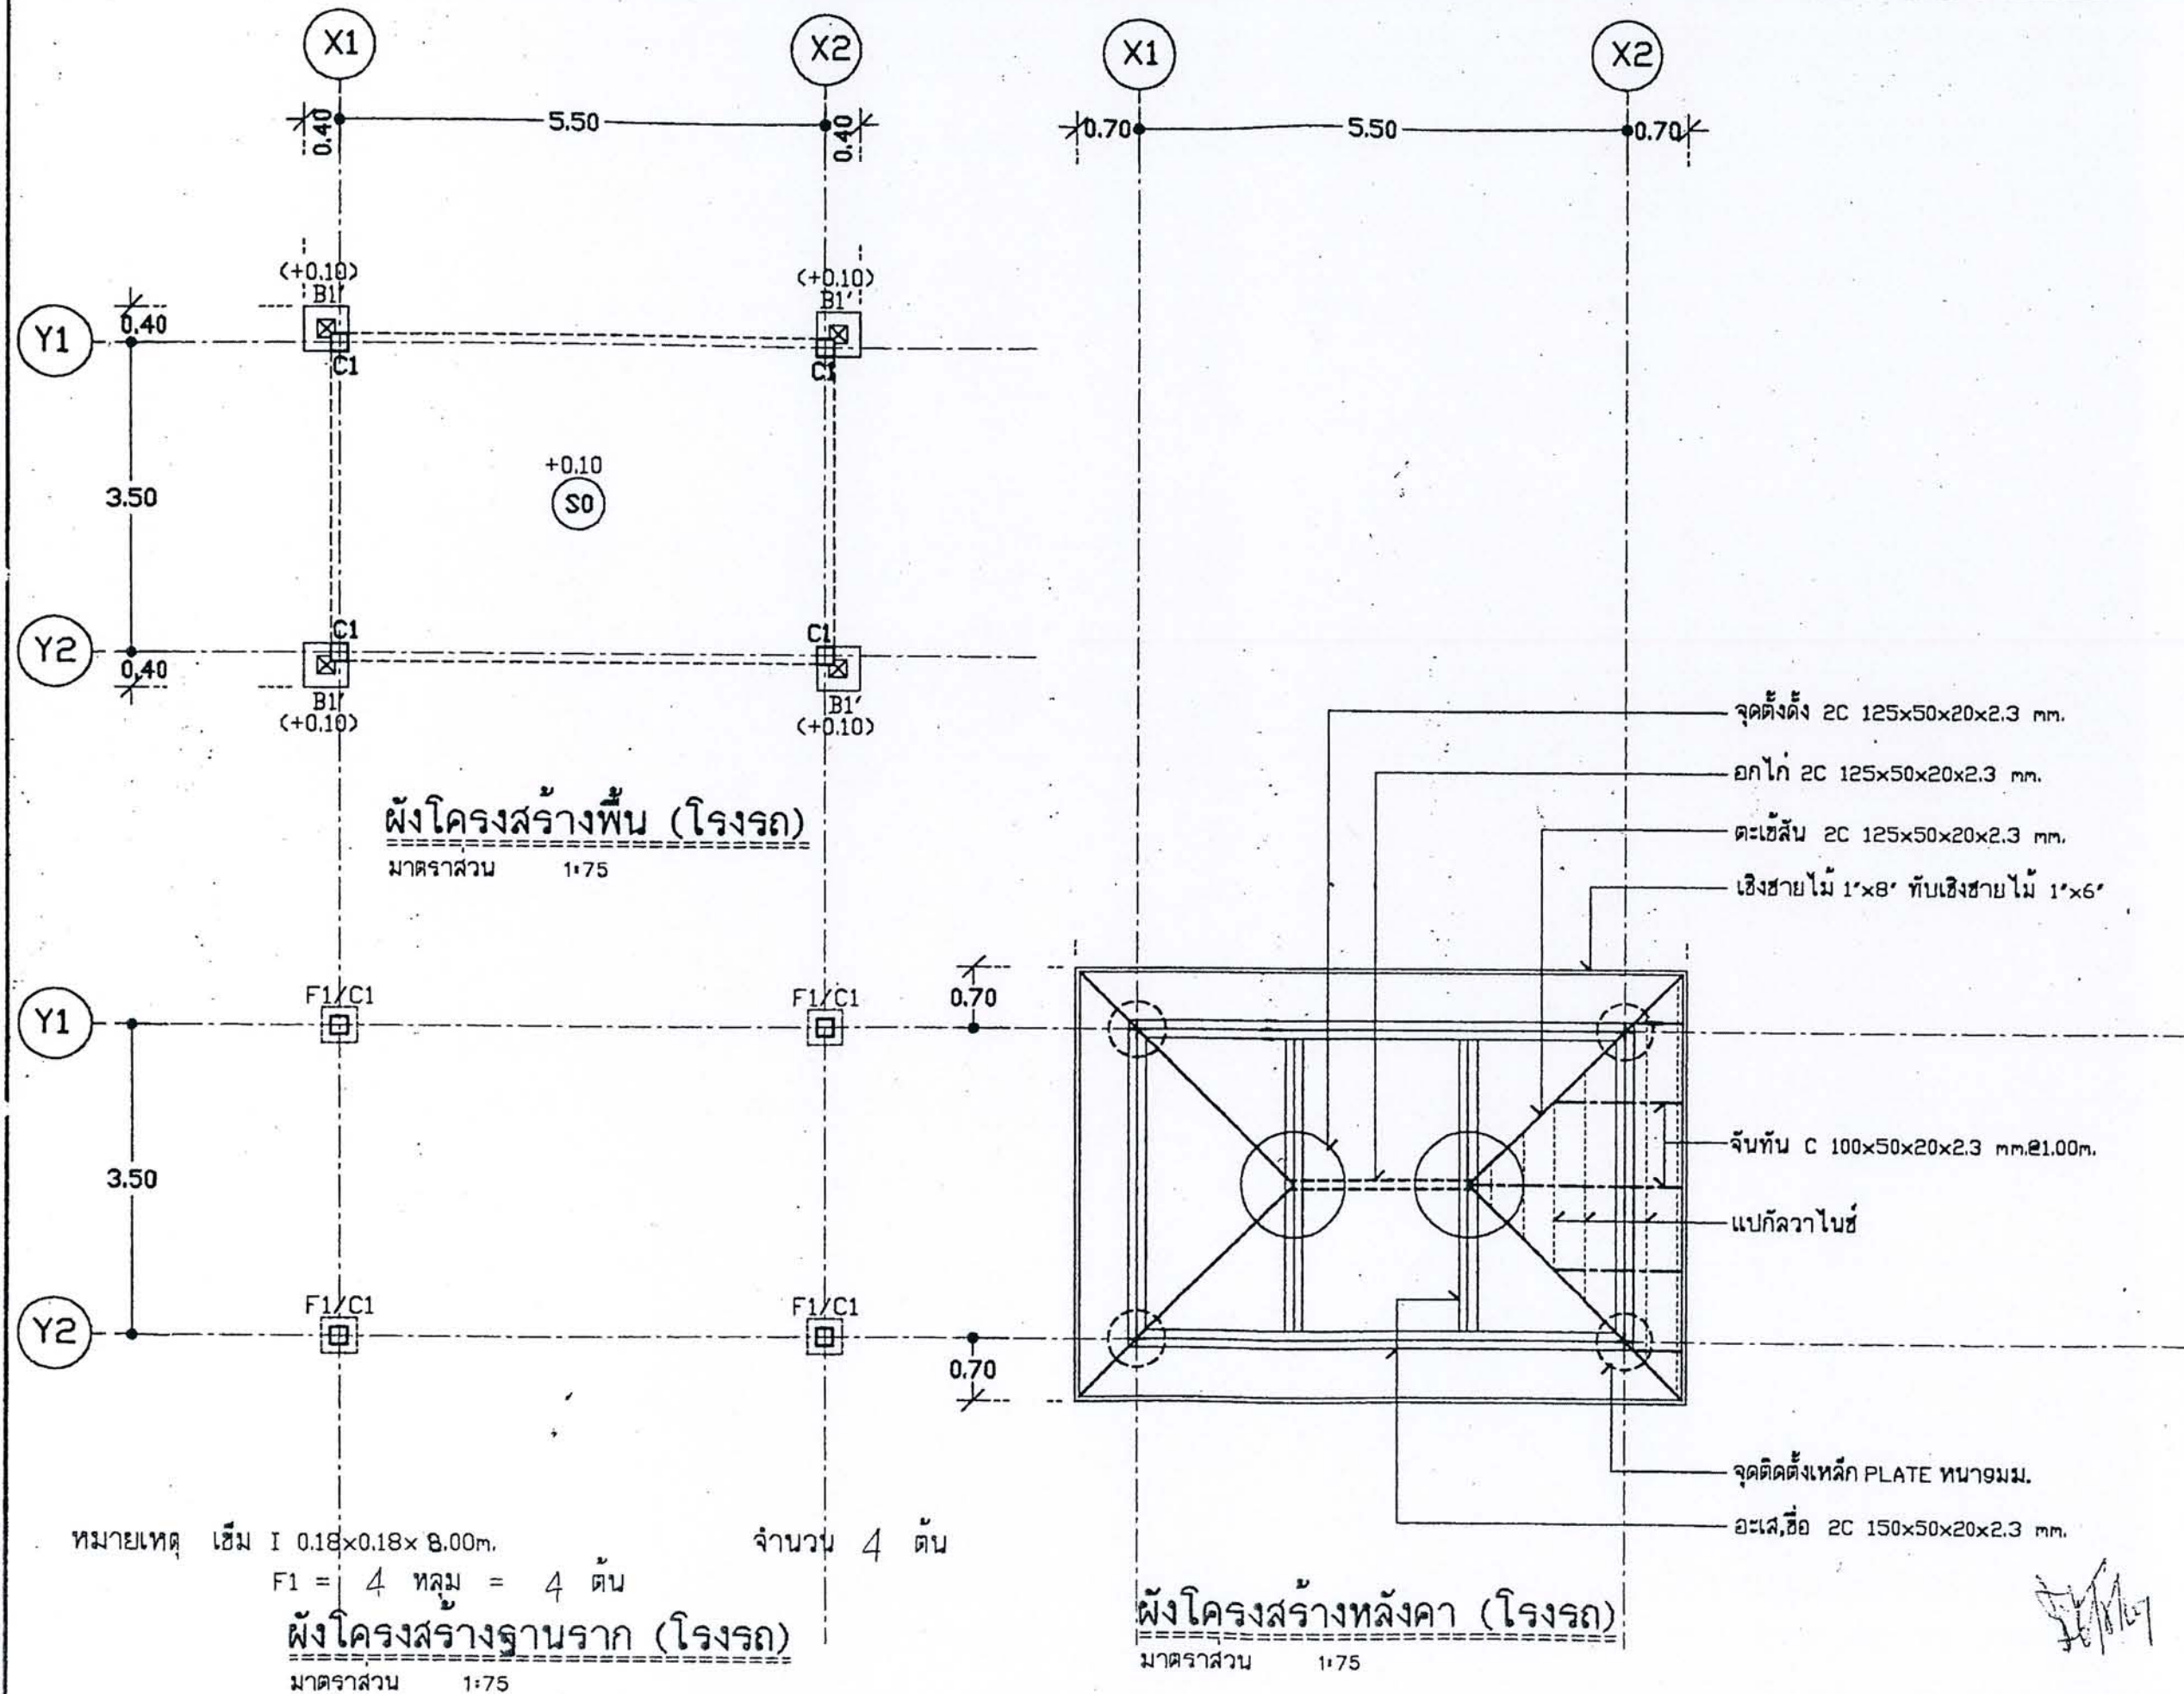

FOR CONSTRUCTION


ได้รับความอนุเคราะห์แบบ
จาก
บริษัท แลนด์ ไสม
(ประเทศไทย) จำกัด




โครงการ
แบบบ้านยิมเพื่อประชาชน

ตามนโยบาย
ม.ร.ว. สุขุมพันธุ์ บริพัตร
ผู้ว่าราชการกรุงเทพมหานคร


โดยสำนักการโยธา
กรุงเทพมหานคร

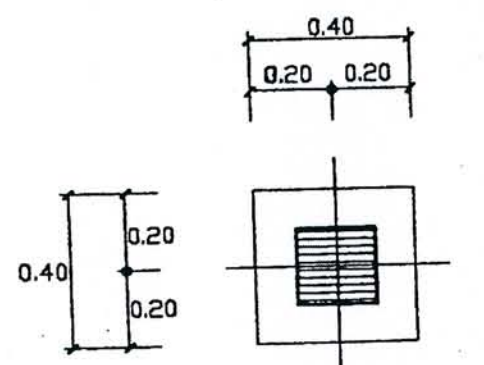


PLAN F1A

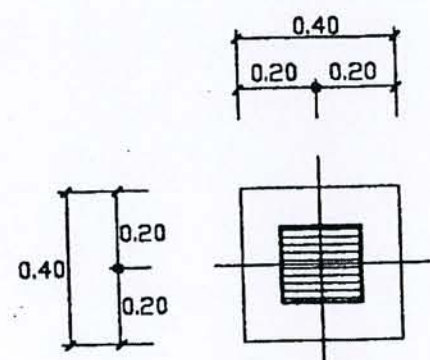


PLAN F1

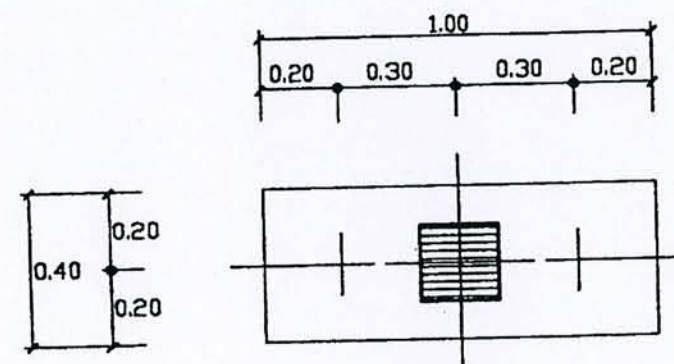


PLAN F2

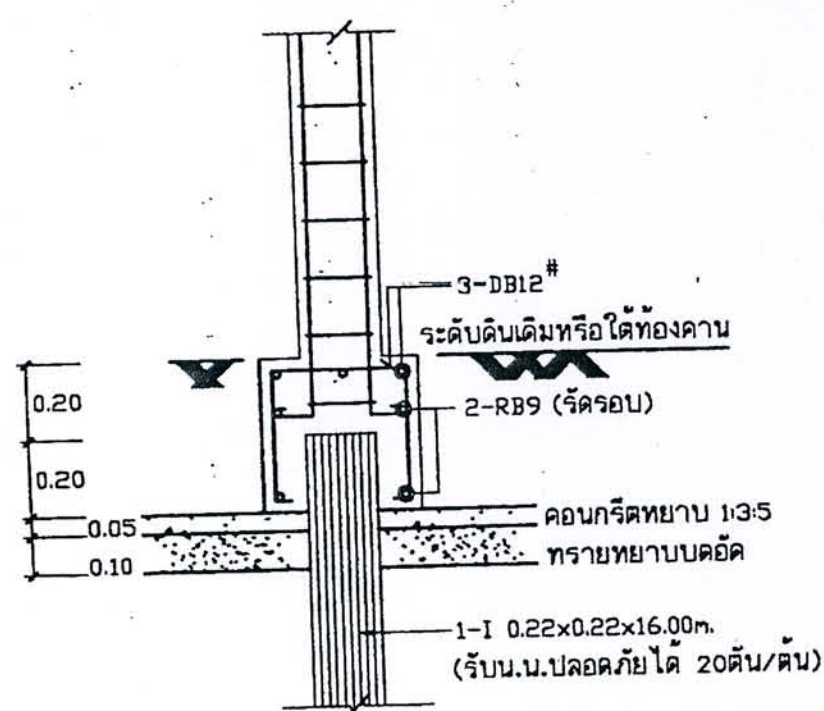

SECTION F1A 1:20

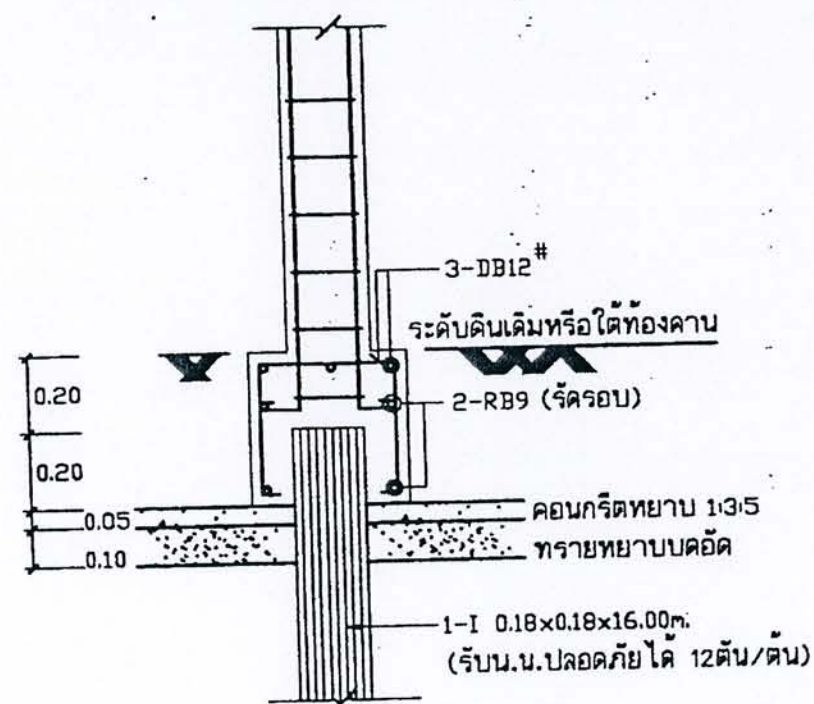

SECTION F1 1:20

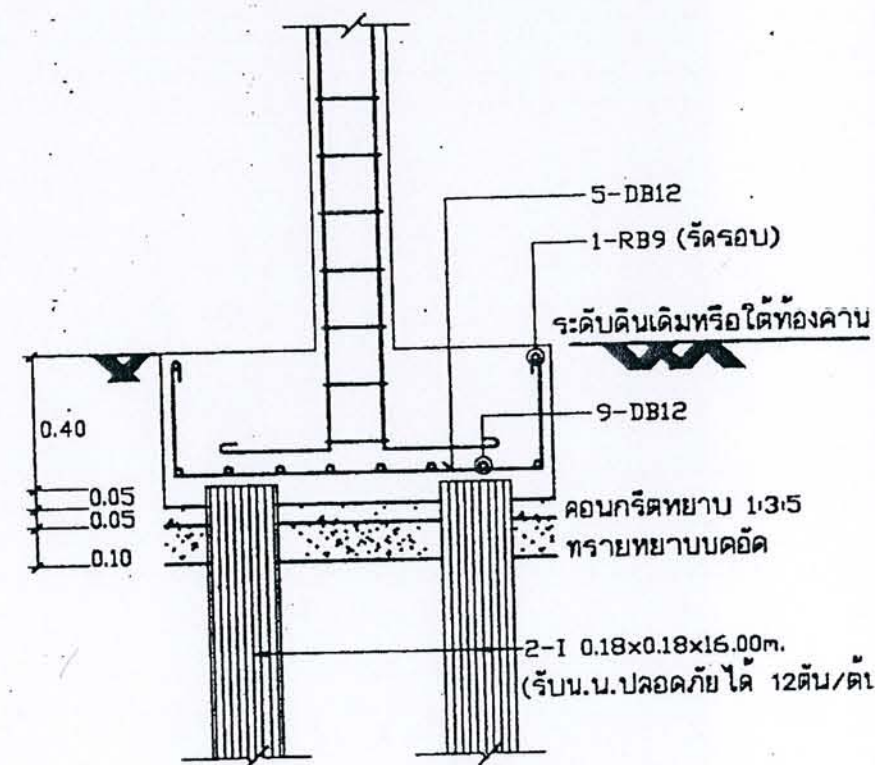

SECTION F2 1:20

ได้รับความอนุเคราะห์แบบ
จาก
บริษัท แลนด์ โฮม
(ประเทศไทย) จำกัด


FOR CONSTRUCTION




โครงการ
แบบบ้านยืมเพื่อประชาชน

ตามนโยบาย
ม.ร.ว. สุขุมพันธุ์ บริพัตร
ผู้ว่าราชการกรุงเทพมหานคร


โดยสำนักงานโยธา
กรุงเทพมหานคร

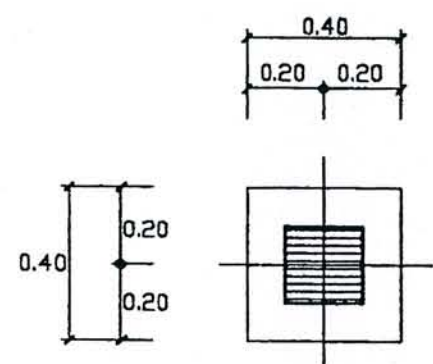


PLAN F1A

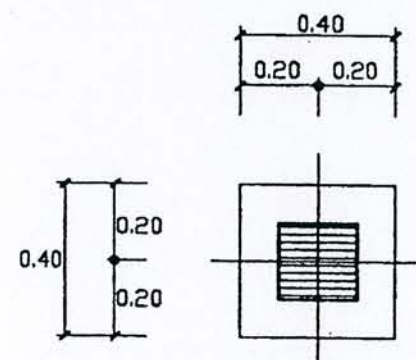


PLAN F1

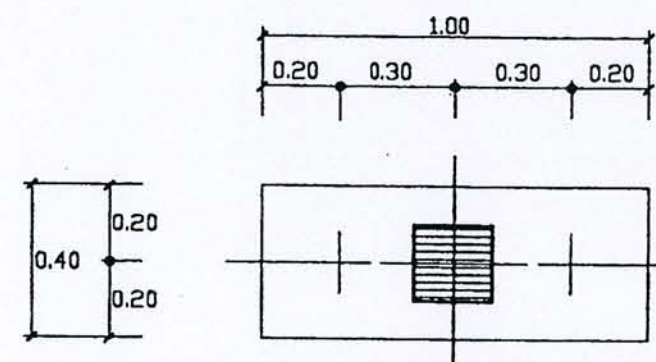


PLAN F2

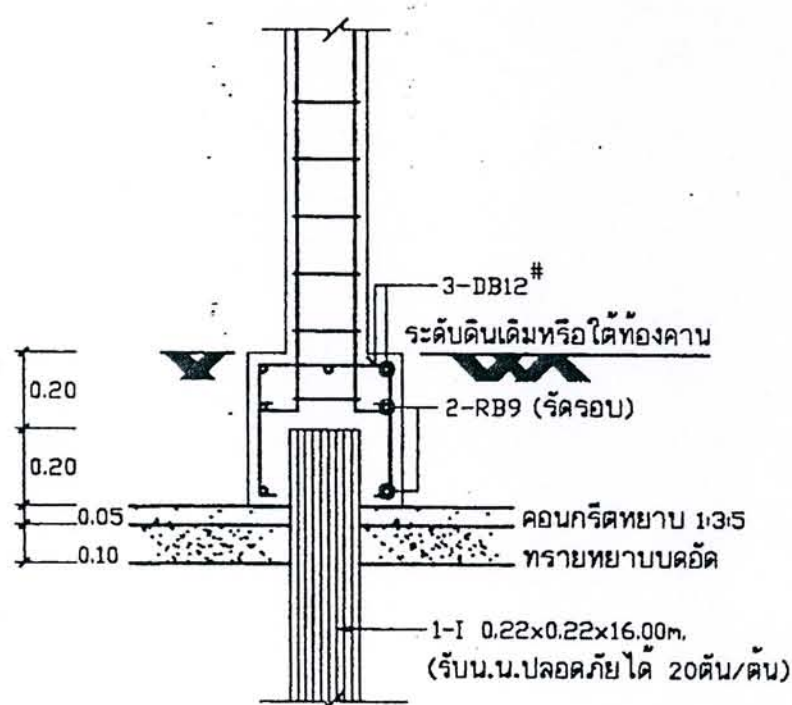

SECTION F1A 1:20

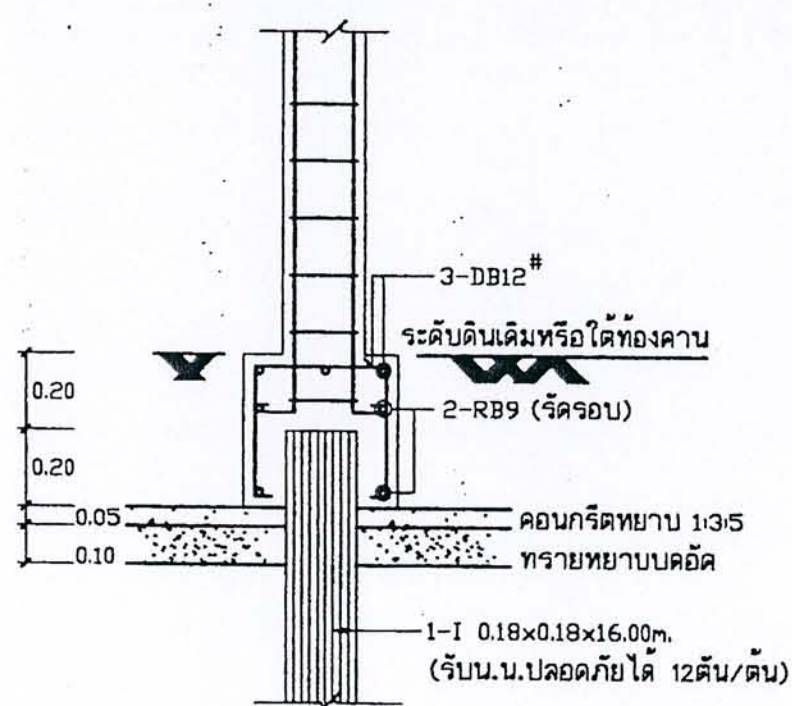

SECTION F1 1:20

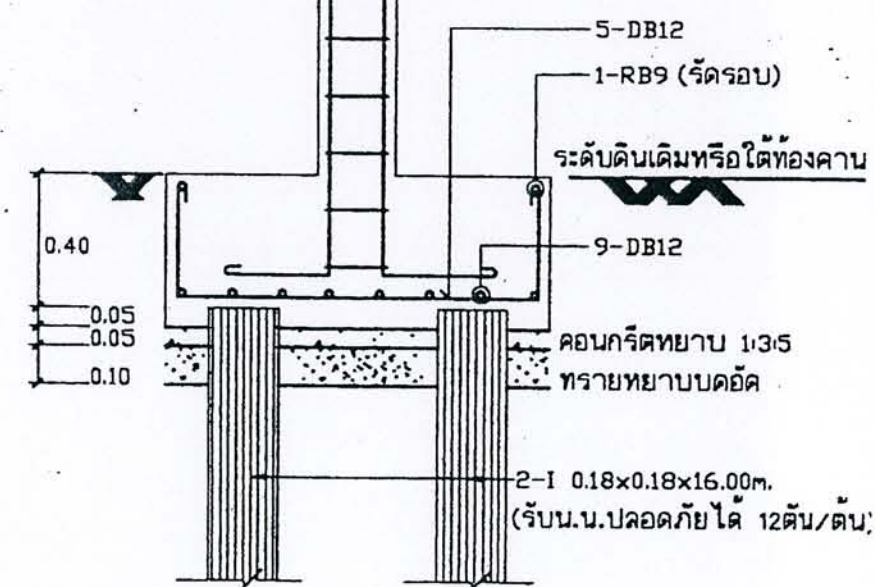

SECTION F2 1:20







ได้รับความอนุเคราะห์แบบ
จาก
บริษัท แลนด์ ไชบ
(ประเทศไทย) จำกัด




โครงการ
แบบบ้านยืมเพื่อประชาชน

ตามนโยบาย
ม.ร.ว. สุขุมพันธุ์ บริพัตร
ผู้ว่าราชการกรุงเทพมหานคร

โดยสำนักการโยธา
กรุงเทพมหานคร

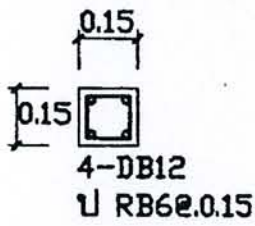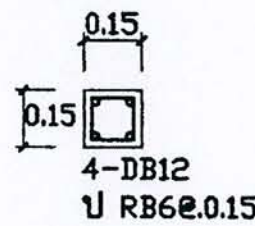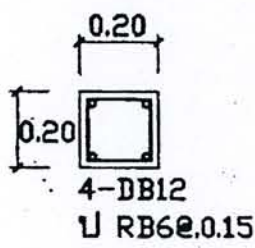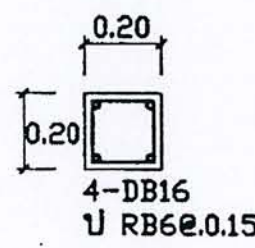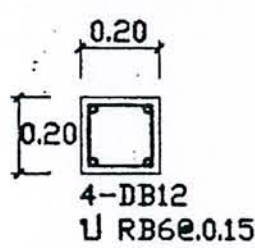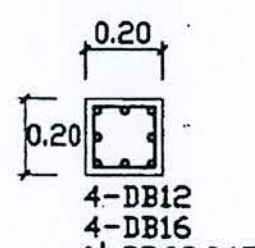FLOOR 2		
FLOOR 1		
FOOTING		
	C1	C2

SECTION COLUMN 1:20

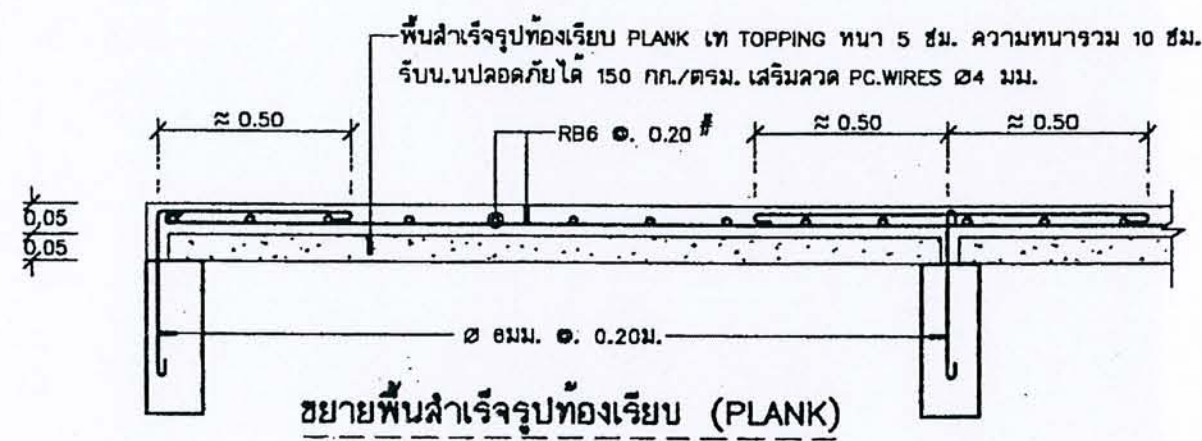

ตารางแสดงการรับน้ำหนักจร (LIVE LOAD)												
สำหรับพื้นสำเร็จรูปแบบทอเรียบ PLANK ขนาดหน้าตัด 0.05x0.35 ม.												
N \ S	2.80	3.00	3.20	3.40	3.60	3.80	4.00	4.20	4.40	4.60	4.80	5.00
4	504											
5		532	464	400	350	300						
6							318	274				
7									305	300		
8											300	250

- หมายเหตุ - มีค้ำยันชั่วคราว
- S = ระยะช่วงพาดวัดขอบในถึงขอบในของคาน (CLEAR SPAN) หน่วยเป็นเมตร
- N = จำนวนลวดค้ำยัน ขนาด ๔ มม.
- ตัวเลขในตารางแสดงความสามารถในการรับน้ำหนักจรทุกปลอดภัยหน่วยเป็น กก./ตารางเมตร


ได้รับความอนุเคราะห์แบบ
จาก
บริษัท แลนด์ โสม
(ประเทศไทย) จำกัด




โครงการ
แบบบ้านยืมเพื่อประชาชน

ตามนโยบาย
ม.ร.ว. สุขุมพันธุ์ บริพัตร
ผู้ว่าราชการกรุงเทพมหานคร


โดยสำนักการโยธา
กรุงเทพมหานคร

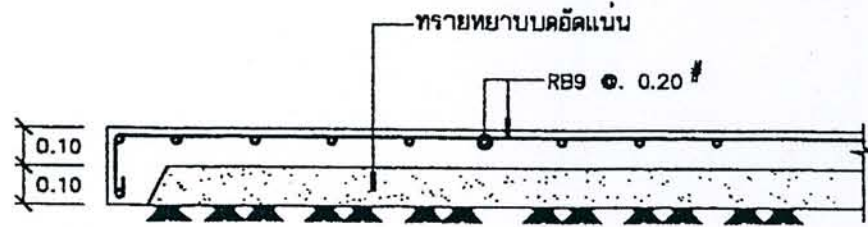


S0

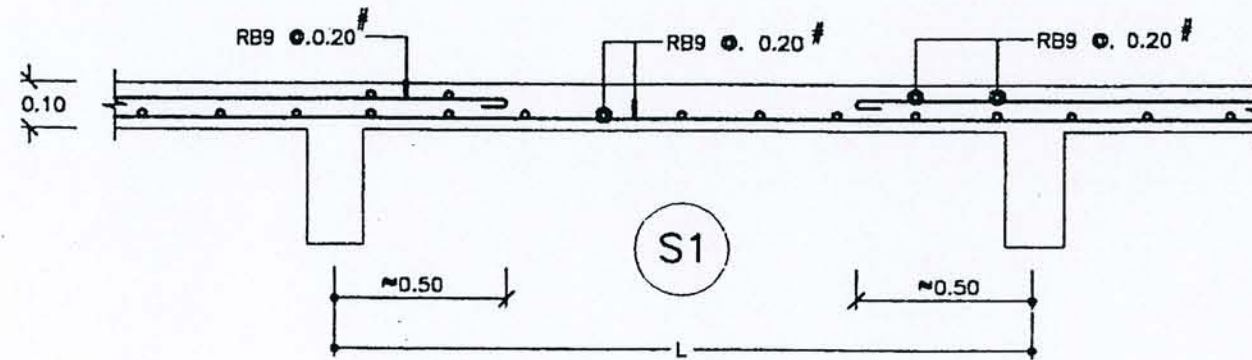


S1

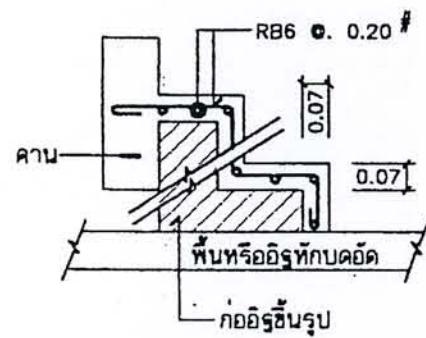


SECTION - 1
(ตามแบบโครงสร้างชั้นล่าง)

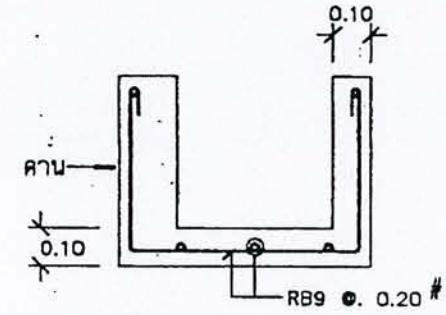

SECTION - 2
(ตามแบบโครงสร้าง)

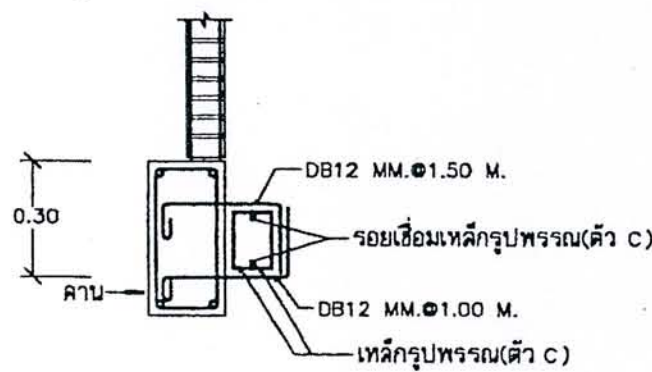

แบบขยายจุดที่มีหลังคาครอบกลางติดผนัง

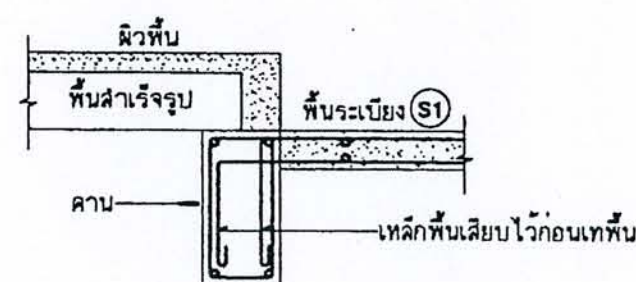

แบบขยายรอยต่อพื้นกับกระเบื้อง

ได้รับความอนุเคราะห์แบบ
จาก
บริษัท แลนด์ โสม
(ประเทศไทย) จำกัด




โครงการ
แบบบ้านยืมเพื่อประชาชน


ตามนโยบาย
ม.ร.ว. สุขุมพันธุ์ บริพัตร
ผู้ว่าราชการกรุงเทพมหานคร

โดยสำนักงานโยธา
กรุงเทพมหานคร

ได้รับความอนุเคราะห์แบบ
จาก
บริษัท แลนด์ โสม
(ประเทศไทย) จำกัด

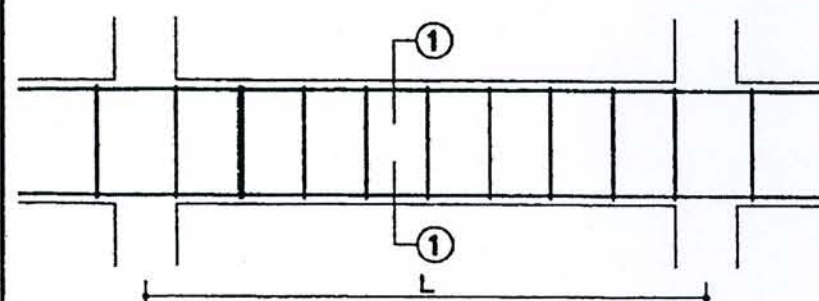


LONG SECTION

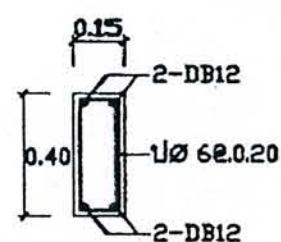


SECTION 1-1

B1

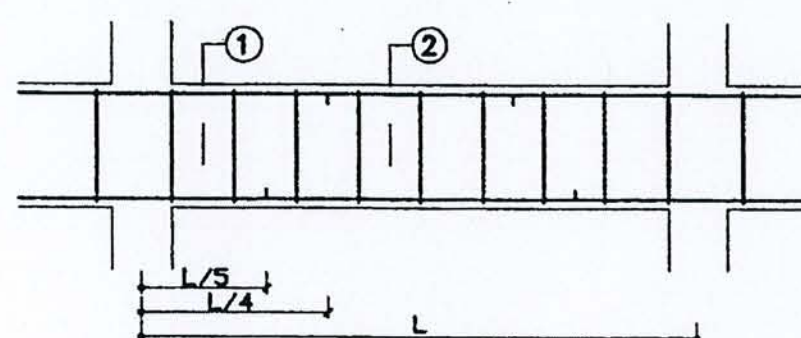


LONG SECTION

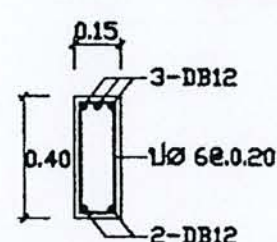


SECTION 1-1


B2

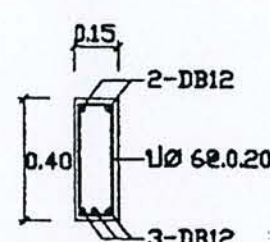

SECTION 2-2

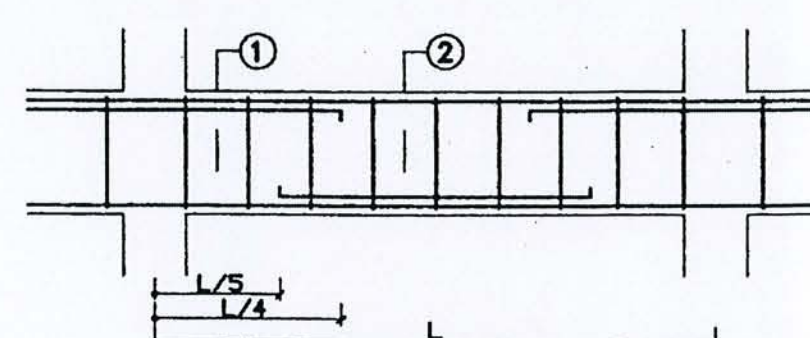


LONG SECTION

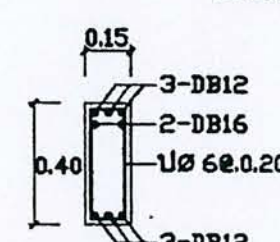


SECTION 1-1


B5

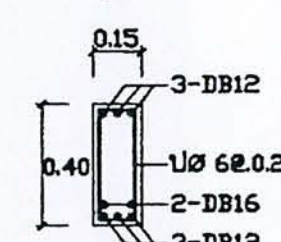

SECTION 2-2

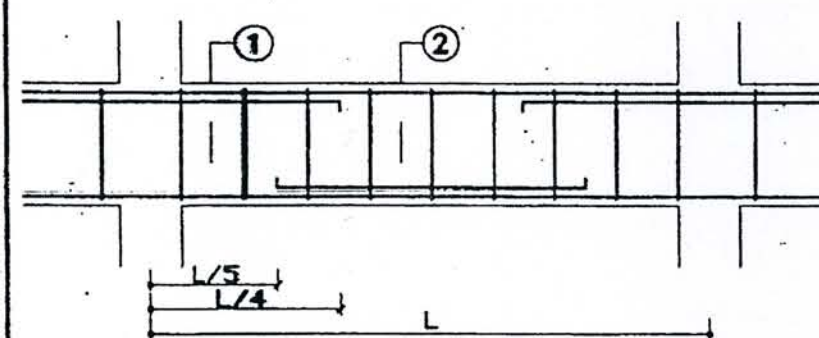


LONG SECTION

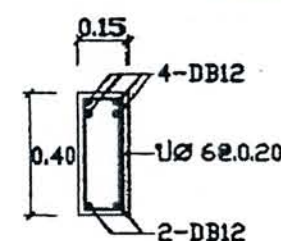


SECTION 1-1


B3

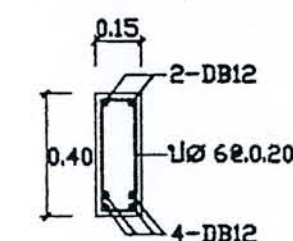

SECTION 2-2

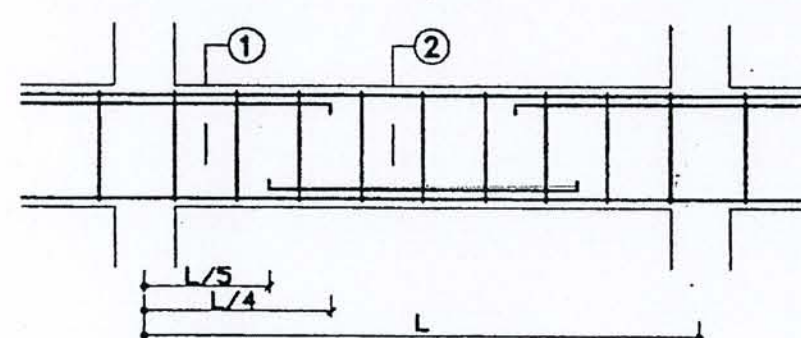


LONG SECTION

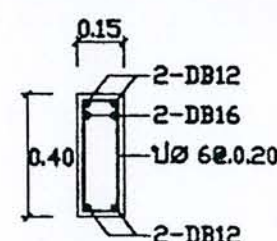


SECTION 1-1

B4

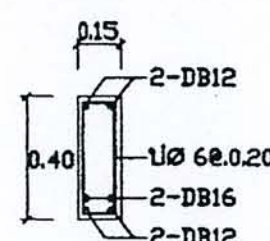


SECTION 2-2

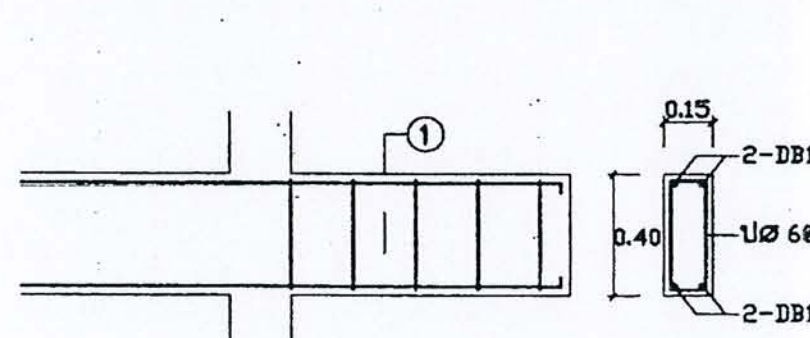


LONG SECTION

B1'

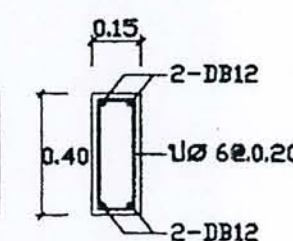


SECTION 1-1

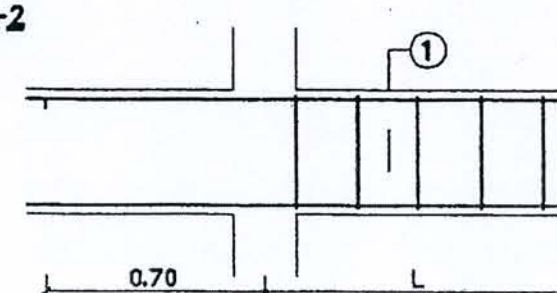

LONG SECTION

B3'

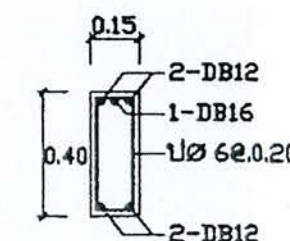

SECTION 1-1





โครงการ
แบบบ้านยืมเพื่อประชาชน

ตามนโยบาย
ม.ร.ว. สุขุมพันธุ์ บริพัตร
ผู้ว่าราชการกรุงเทพมหานคร

โดยสำนักงานโยธา
กรุงเทพมหานคร

ได้รับความอนุเคราะห์แบบ
จาก
บริษัท แลนด์ โสแมท
(ประเทศไทย) จำกัด

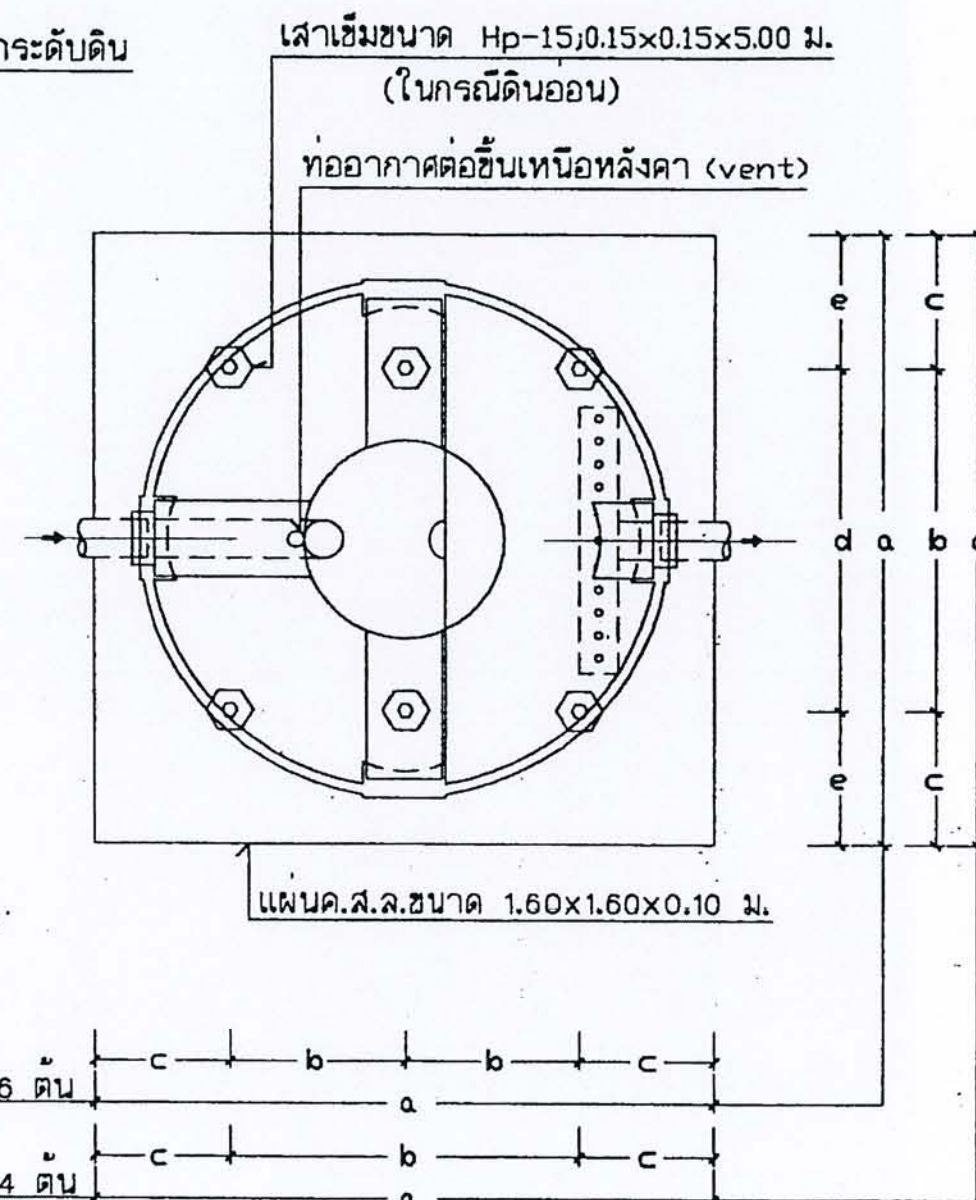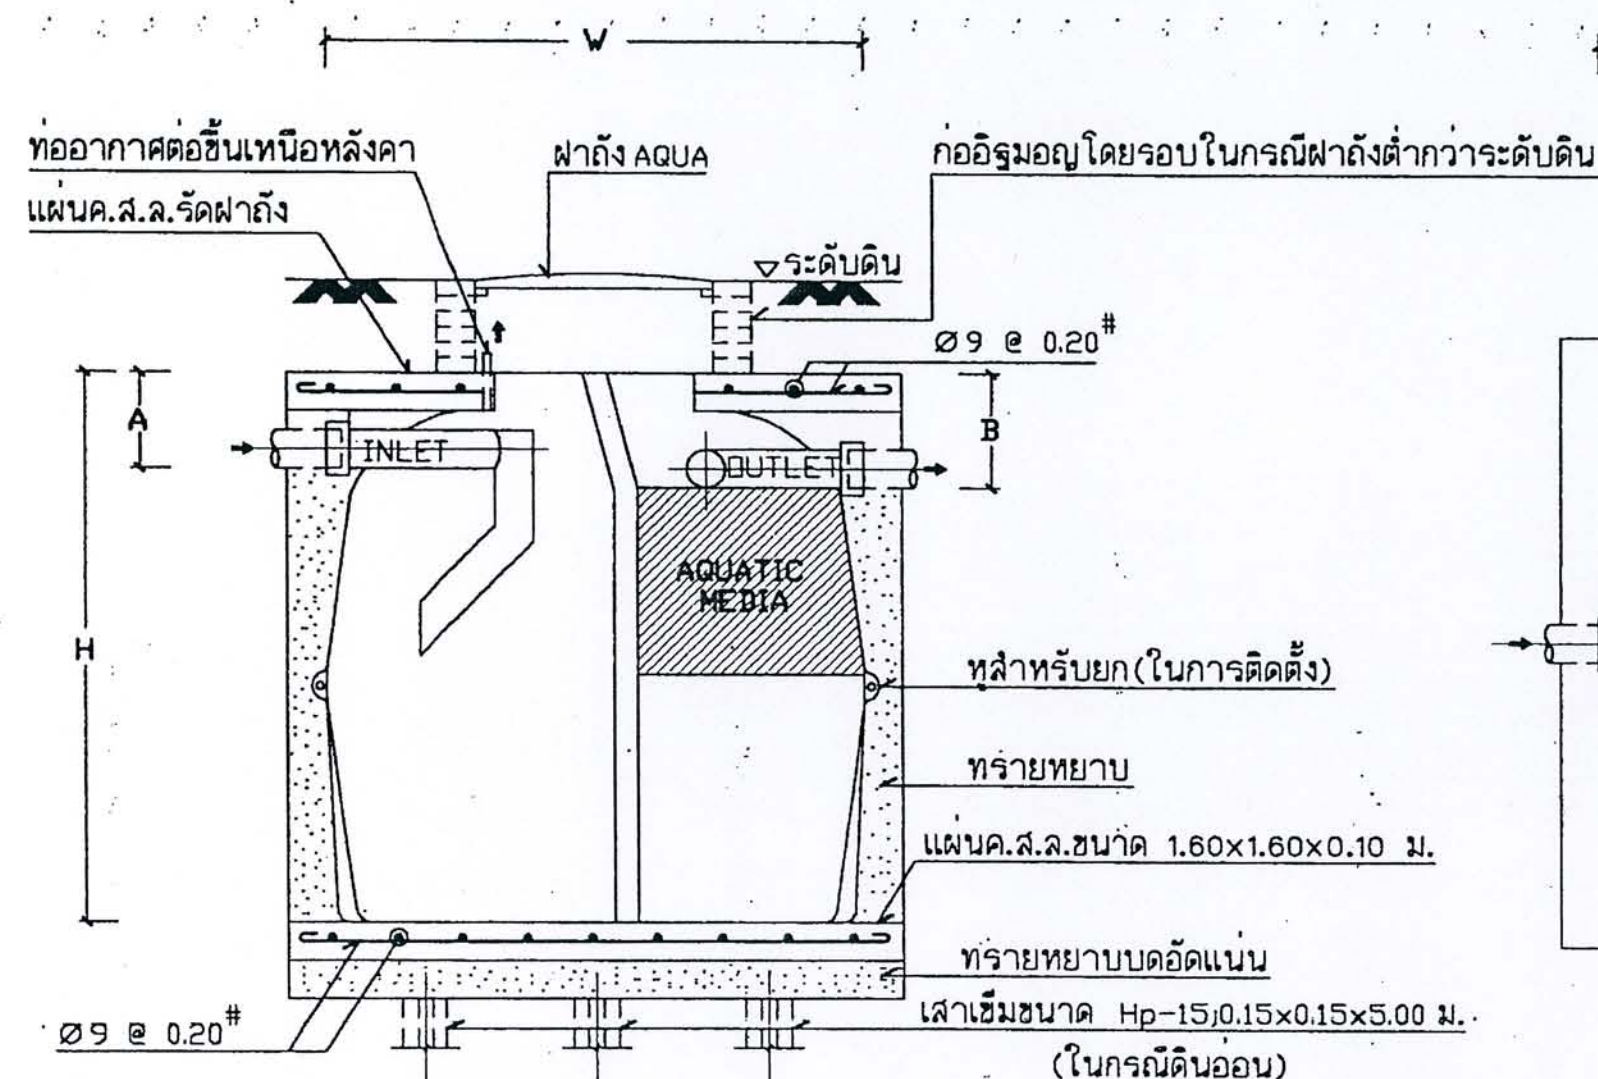

SECTION 1:20

PLAN 1:20

ตาราง แสดงขนาดของถังรวม (ส่วนกระโหลก+ส่วนกรอง) ในรุ่นต่างๆ (มม.)

MODEL	H	W	A	B	INLET	OUTLET	VENT	a	b	c	d	e
AP-1200	1700	1200	250	300	100	100	50	1400	700	350	-	-
AP-1800	1590	1450	250	300	100	100	50	1650	850	400	-	-
AP-2000	1750	1500	250	300	100	100	50	1700	850	425	-	-
AP-3000	1900	1700	250	300	100	100	50	1900	700	250	900	500
AP-4000	1930	1890	250	300	100	100	50	2090	750	295	1090	500
AP-6000	2300	1970	250	300	100	100	50	2170	750	335	1010	580
AP-5000	2350	2100	300	350	150	150	50	2300	750	400	1200	550

หมายเหตุ การใช้เส้าเข็มกับขนาดถัง
ถังรุ่น 1200 ถึงรุ่น 2000 ใช้เส้าเข็มจำนวน 4 ต้น
ถังรุ่น 3000 ถึงรุ่น 6000 ใช้เส้าเข็มจำนวน 6 ต้น

AQUA-PAC