



ตามนโยบายของ
หม่อมราชวงศ์สุขุมพันธุ์ บริพัตร
ผู้ว่าราชการกรุงเทพมหานคร
โดย สำนักการโยธา



ห้ามพลาด!!! โอกาส...
ยืมรับ... บ้านใหม่
แบบ **บ้านสวย**
เลือกได้
ใน “โครงการแบบบ้านยืม...เพื่อประชาชน”

แบบบ้านยืม... เพื่อประชาชน

100 แบบบ้านมาตรฐาน...
สวย ดี โดนใจ...
พร้อมปลูกสร้างได้ทันที

แบบ 100 แบบบ้าน
มาตรฐาน...
สวย ดี โดนใจ
พร้อมปลูก
สร้างได้ทันที
มีให้เลือก
หลากหลาย
ตอบสนอง
ทุกไลฟ์สไตล์คนเมือง

งามพิศ 2

โดยความอนุเคราะห์แบบจาก
บริษัท แลนด์ โธม (ประเทศไทย) จำกัด

รายการประกอบแบบก่อสร้าง TYPE "S"



รายการประกอบแบบทั่วไป

- โครงสร้างบ้านพักอาศัยโดยทั่วไปเป็นคอนกรีตเสริมเหล็กหล่อในที่ ตั้งแต่วางราก ; เสา , คาน , พื้นชั้นล่าง - บน เป็นพื้น - สำเร็จรูป บางส่วนหล่อในที่ ขนาด และ รายละเอียด ตามแบบวิศวกรรม
- เสาเข็มบ้าน 2 ชั้น ใช้คอนกรีตอัดแรง รูปตัว I - 18 X 18 ซม. ยาว 16 ม. กรณีบ้าน 2 ชั้น จะใช้เสาเข็มตาม - การคำนวณของวิศวกร
- หลังคา โครงหลังคาหลักรูปพรรณ ทาสีกันสนิม TOA 2 ชั้น พร้อมฉนวนฉนวนกันความร้อน 1 ชั้น มุงด้วยกระเบื้อง CPAC MONIER สีส้มตราฐานบริษัท หรือ เทียนฟ้า
- ผนังที่ไม่ก่ออิฐฉาบปูน ทาสี ยาวกันสนิม ทาสีผิวพิเศษตามระบอบ
- ฝ้าเพดานภายใน แผ่นยิปซัมบอร์ดหนา 9 มม. ฉาบเรียบ ทาสี ความสูงจากพื้นถึงฝ้า 2.60 เมตร
- ภายนอกกระเบื้องแผ่นเรียบ หนา 4 มม. , ห้องน้ำแผ่นยิปซัมบอร์ด หนา 9 มม. วางบนโครงคร่าว T - BAR
- บันไดโครงสร้างไม้ตั้ง ลูกตั้งบันได , ลูกนอนบันไดไม้แดง เสา , ราวบันได , ลูกกรงบันไดไม้ระแนง
- ลิ้นชักใช้สี SUPERCOAT ผลงานของ ICI หรือ เทียนฟ้า
- การป้องกันปลวก ใช้ระบบดินทอกที่บริเวณคานชั้นล่างทั้งหมด และทากายากันปลวกบนเนื้อโครงคร่าวส่วนที่เป็นไม้

รายการประกอบแบบการเปลี่ยนแปลงเพิ่มเติม

*หมายเหตุ : งานโครงหลังคา ปรองรับกระเบื้องใช้แป้นไม้ความหนา 0.7 ซม.

*.ไม่มีรายการเปลี่ยนแปลง

สัญลักษณ์ประกอบแบบสถาปัตย์

สัญลักษณ์	ความหมาย
N	ทิศเหนือ
	1, 2, 3, 4 ชื่อรูปด้านกำหนดจากแปลน
	A หมายถึง ชื่อรูปด้าน
	A หมายถึง ชื่อแบบขยาย
	A หมายถึง ชื่อรูปตัด
	A หมายถึง แนวการระดมจากศูนย์กลาง
+0000 , -0000	+0000 มีค่ามากได้ไม่เกินตัวเลขที่กำหนด , -0000 มีค่าน้อยได้ไม่เกินตัวเลขที่กำหนด
	B หมายถึง ระยะความยาวจากศูนย์กลางถึงศูนย์กลาง
	B หมายถึง ระยะความยาวจากริมถึงริม
	A หมายถึง ระยะความยาวจากศูนย์กลางถึงผนังริมนอก
	A หมายถึง ระยะความยาวจากศูนย์กลางถึงผนังริมใน
	1 หมายถึง รั้วประตู
	1 หมายถึง รั้วหน้าต่าง
	1 หมายถึง หมายเลขผนัง
	ผนังก่ออิฐครึ่งแผ่น ฉาบปูน
	ผนังก่ออิฐเต็มแผ่น ฉาบปูน
	ผนังก่ออิฐมวลเบา ฉาบปูน
	ผนังก่ออิฐบล็อกแก้ว ตามแบบระบุ
	ผนังแบบโครงคร่าวไม้ตั้ง กรุฉนวนตามแบบระบุ
	ดิน
	คอนกรีต
	ทรายอัดแน่น
	หินกาบ
	ปูนฉาบเรียบ
	จากปูนชำระรอง
	จากปูนเรียบ


บ้าน SMILE HOME
V.1 [11/2/45]

ง/ส/ก/ส/ 2

ได้รับความอนุเคราะห์แบบ
จาก
บริษัท แลนด์ โยม
(ประเทศไทย) จำกัด

A
B
C
D
E

คอกอกนอกหน้า

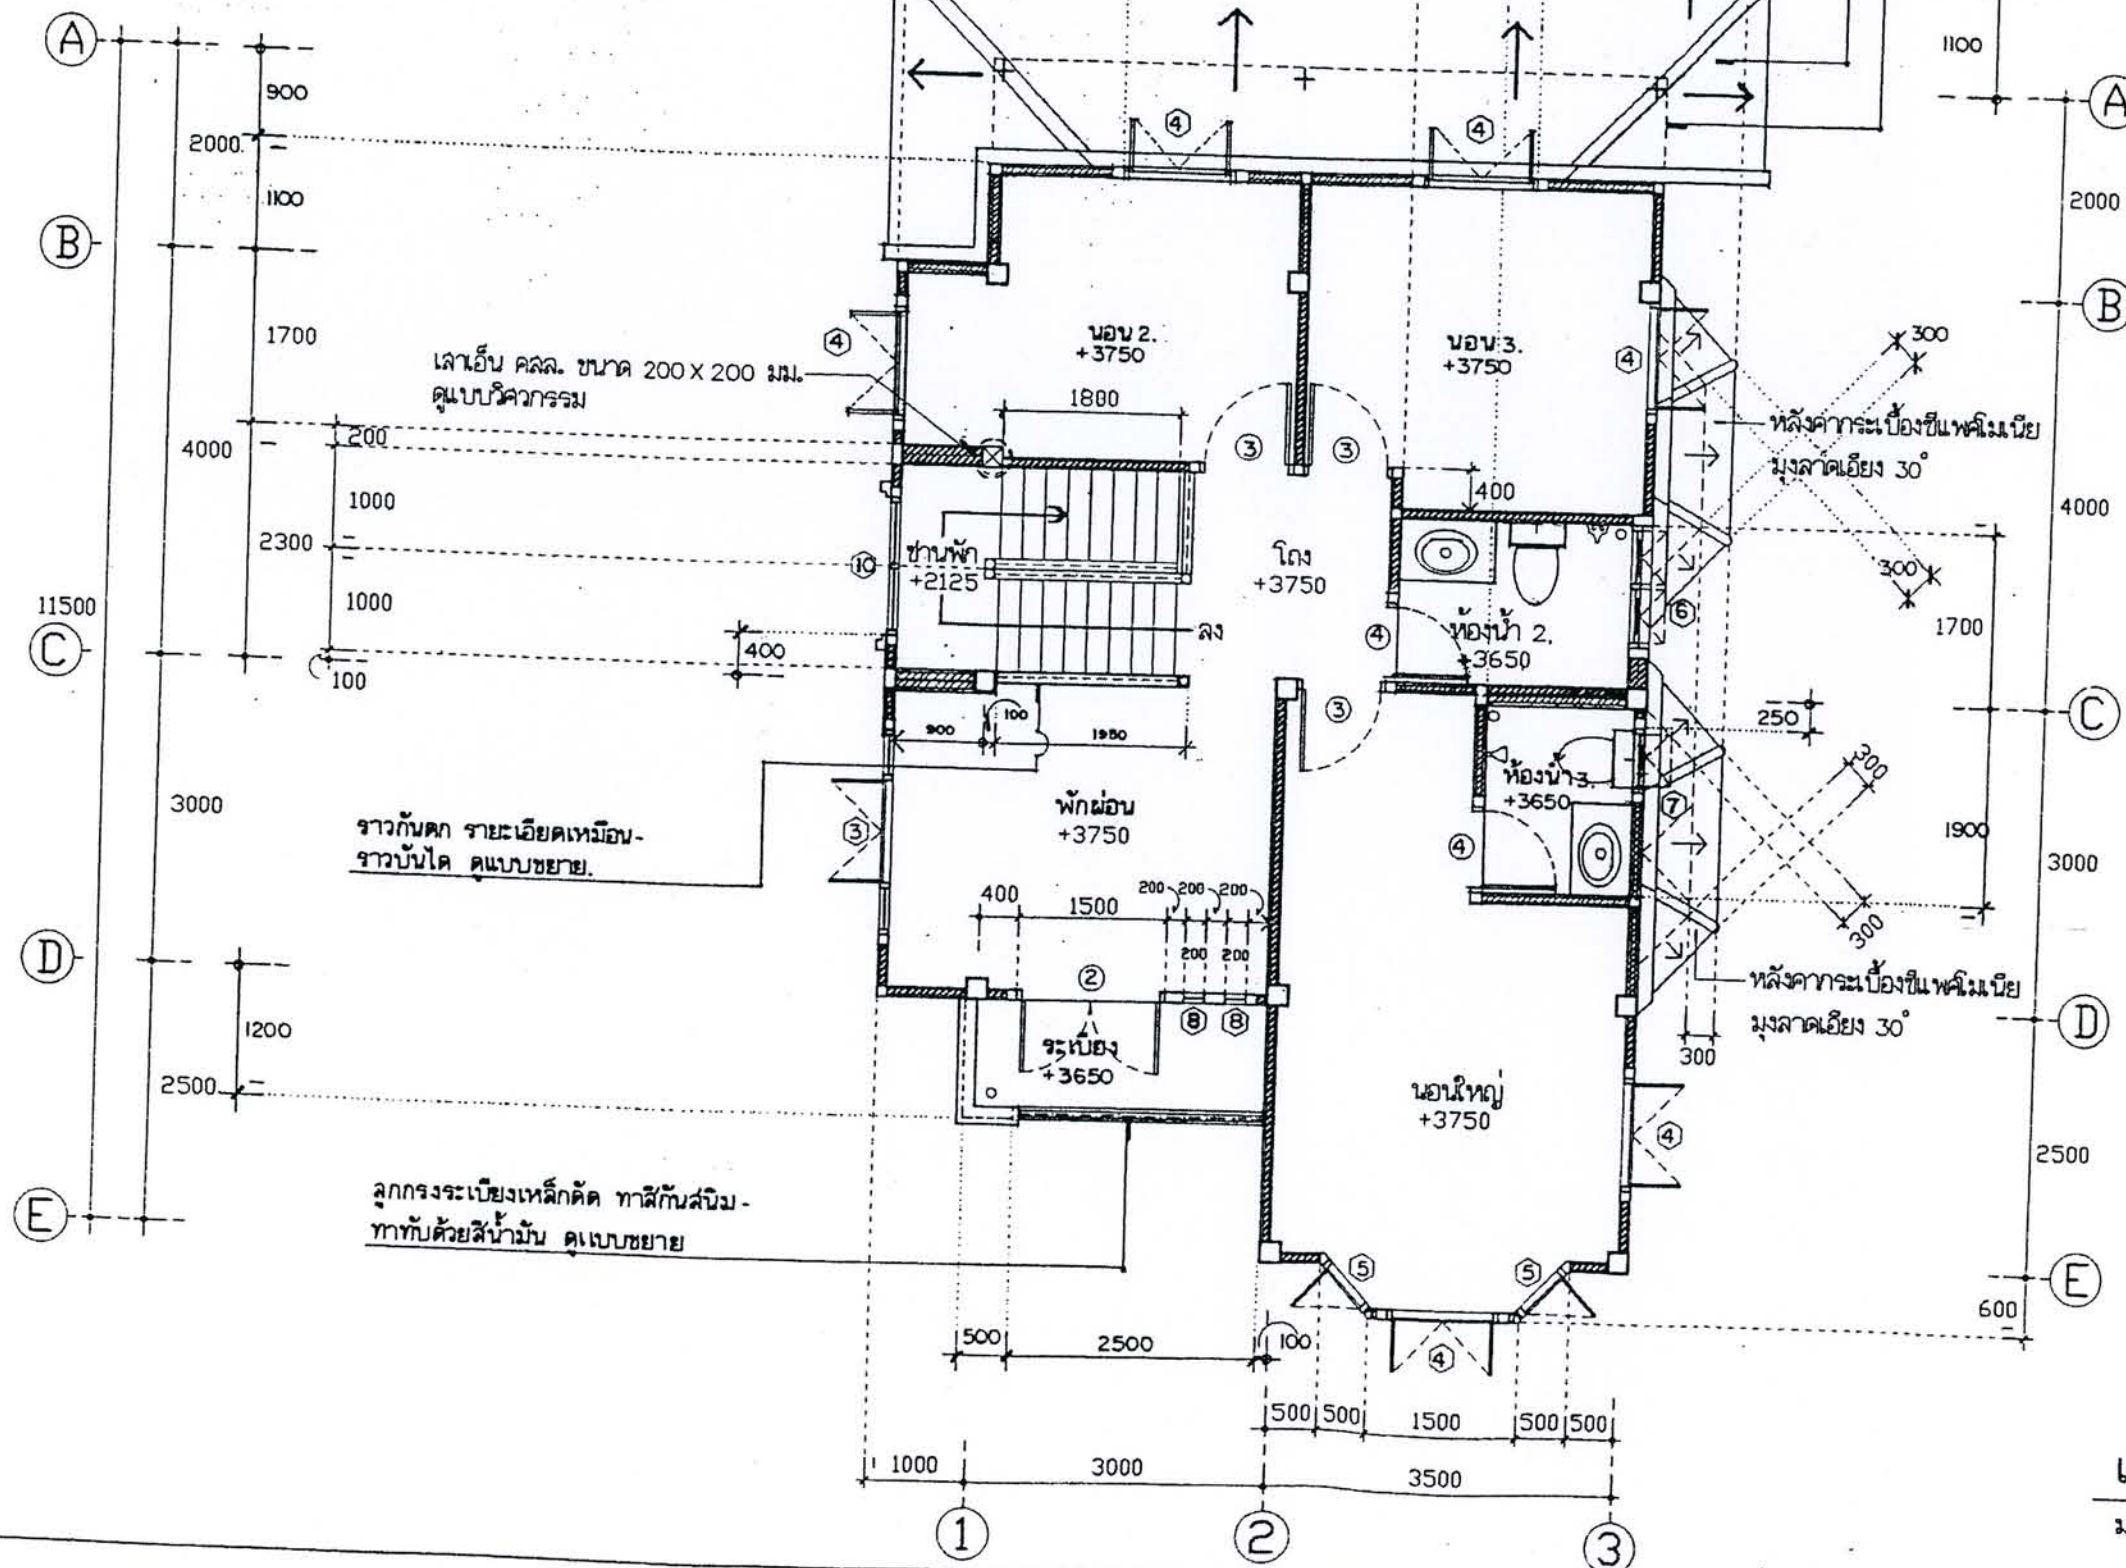

แปลนพื้นที่บน
มาตราส่วน 1 : 75

แบบบ้าน
ม.ร.ว.
ผู้ว่าราชการ
โดย
ก.

ได้รับ
ปรี




โครงการ
แบบบ้านยืมเพื่อประชาชน

ตามนโยบาย
ม.ร.ว. สุขุมพันธุ์ บริพัตร
ผู้ว่าราชการกรุงเทพมหานคร

โดยสำนักงานโยธา
กรุงเทพมหานคร

ได้รับความอนุเคราะห์แบบ
จาก
บริษัท แลนด์ โสม
(ประเทศไทย) จำกัด

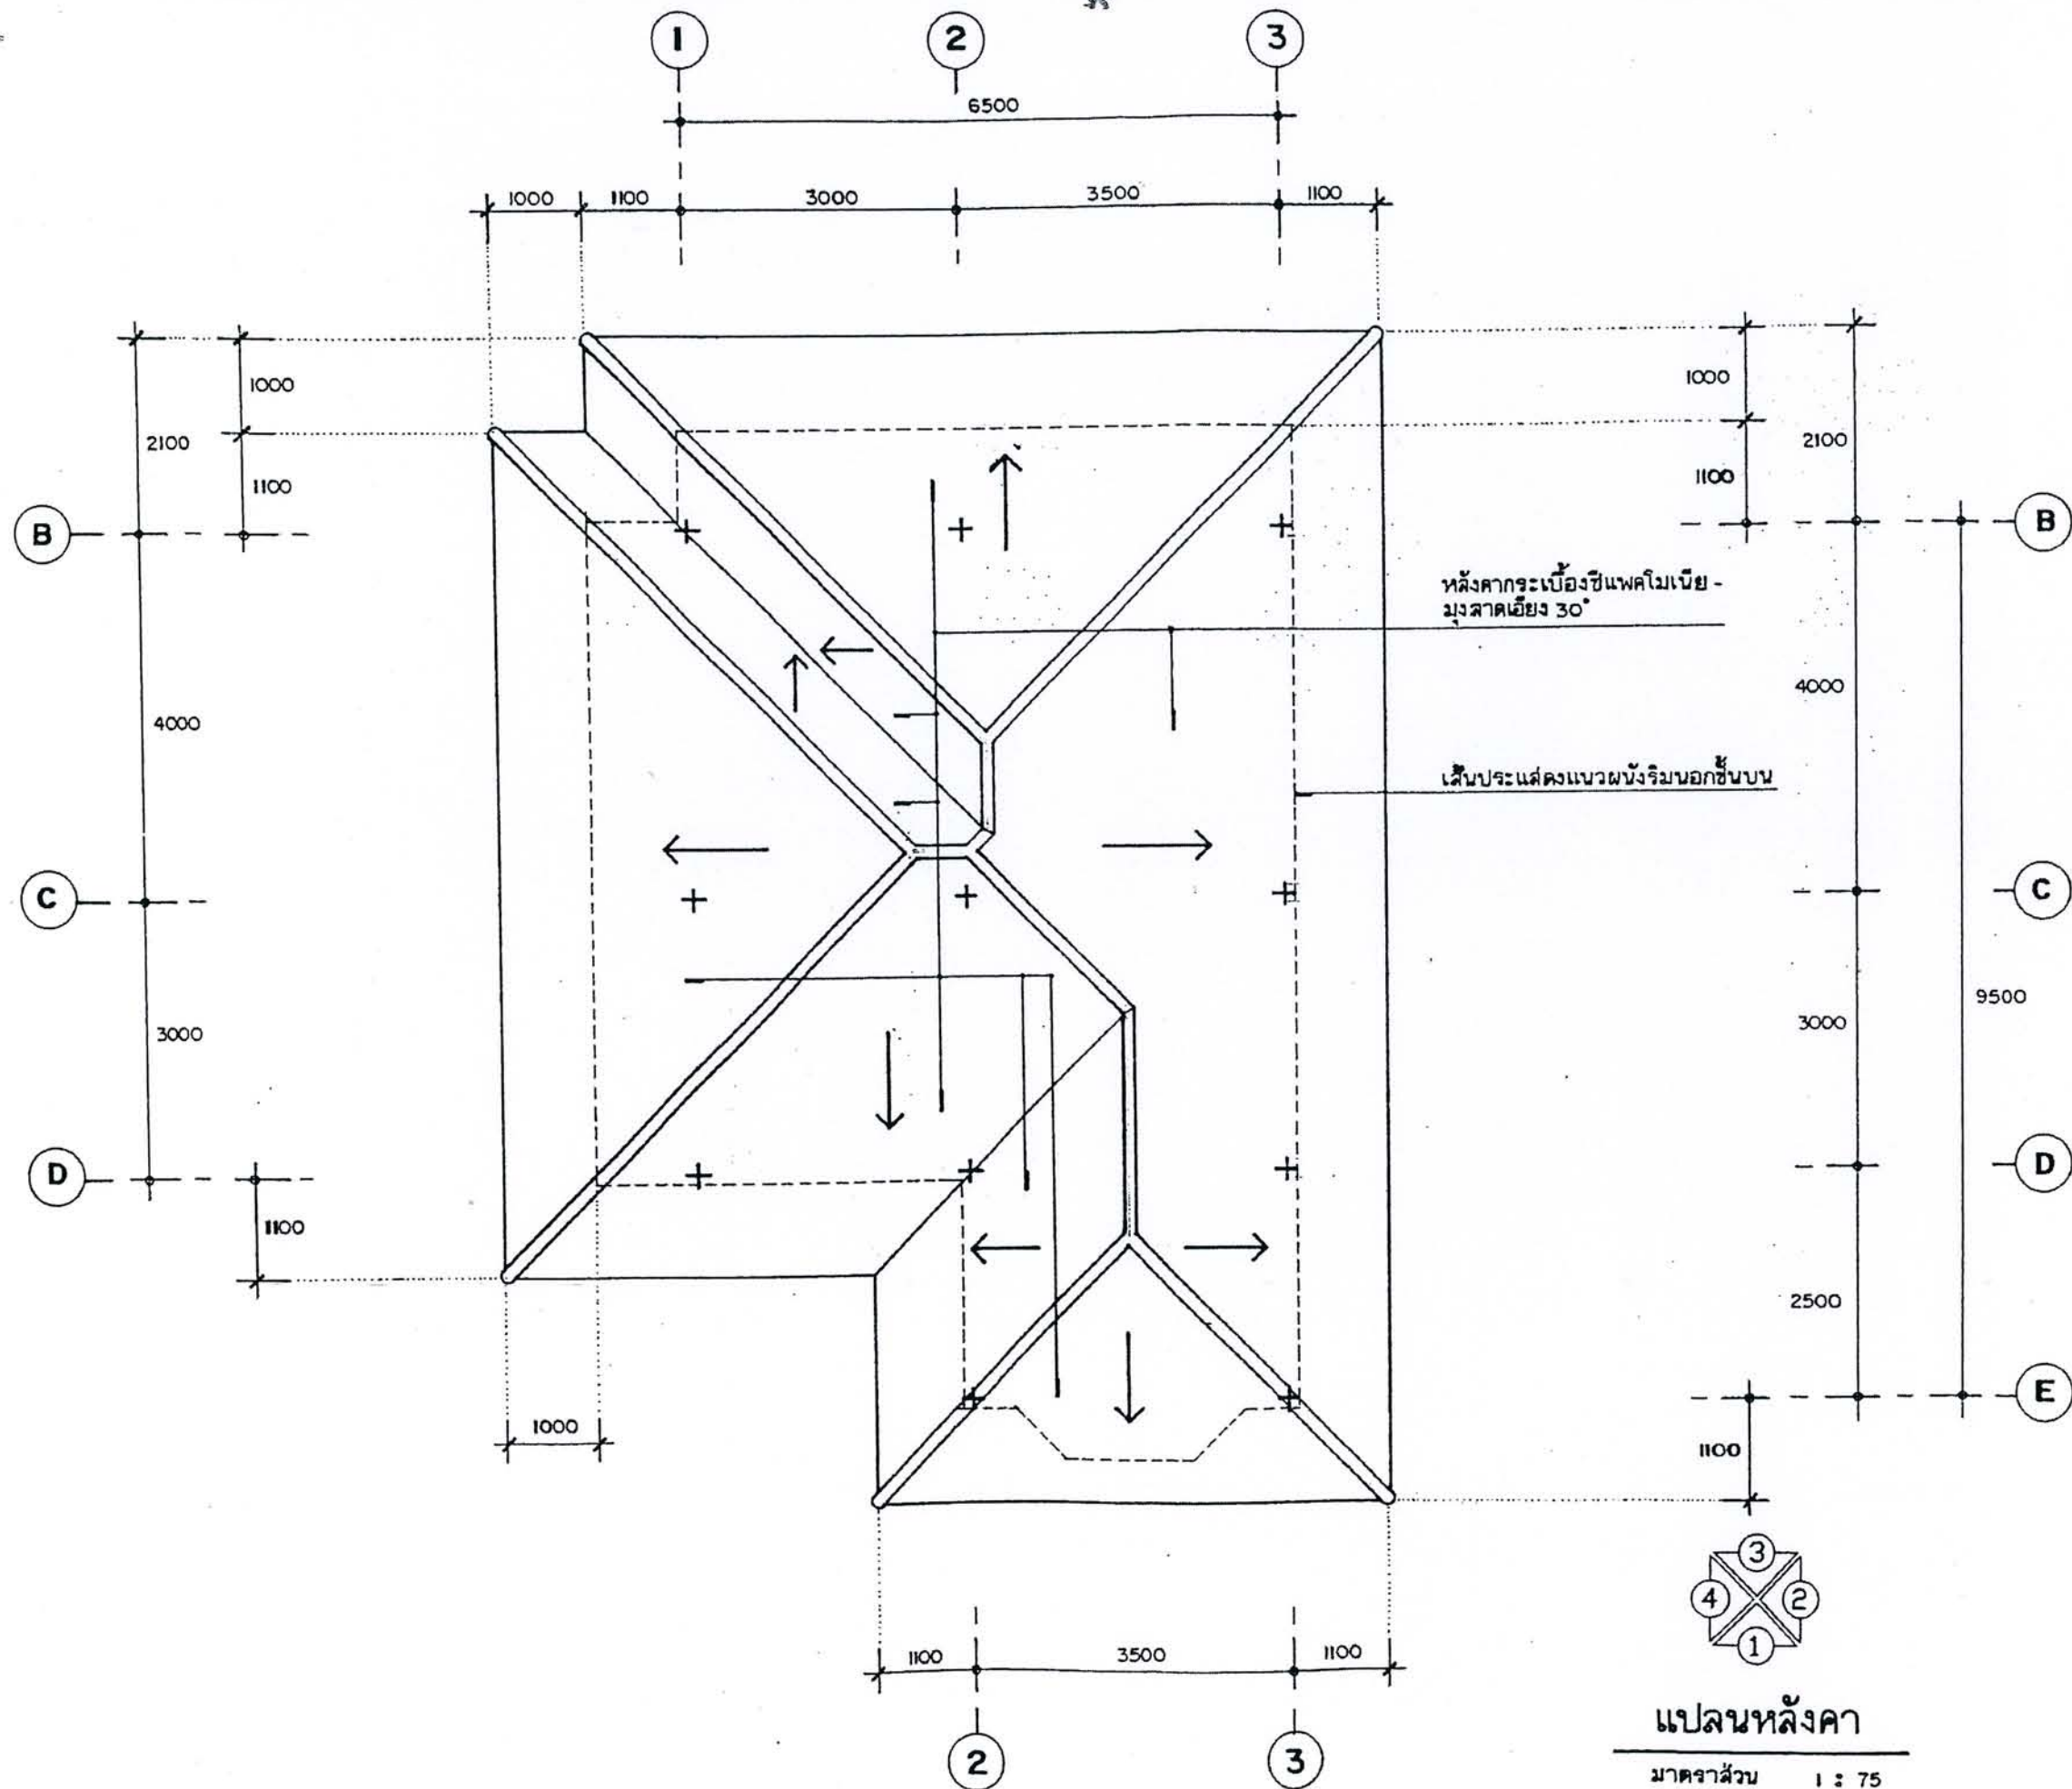




โครงการ
แบบบ้านยืมเพื่อประชาชน

ตามนโยบาย
ม.ร.ว. สุขุมพันธุ์ บริพัตร
ผู้ว่าราชการกรุงเทพมหานคร

โดยสำนักงานโยธา
กรุงเทพมหานคร

ได้รับความอนุเคราะห์แบบ
จาก
บริษัท แคนดี้ โฮม
(ประเทศไทย) จำกัด

หลังคากระเบื้องซีเมนต์โมเนีย มุงลาดเอียง 30°

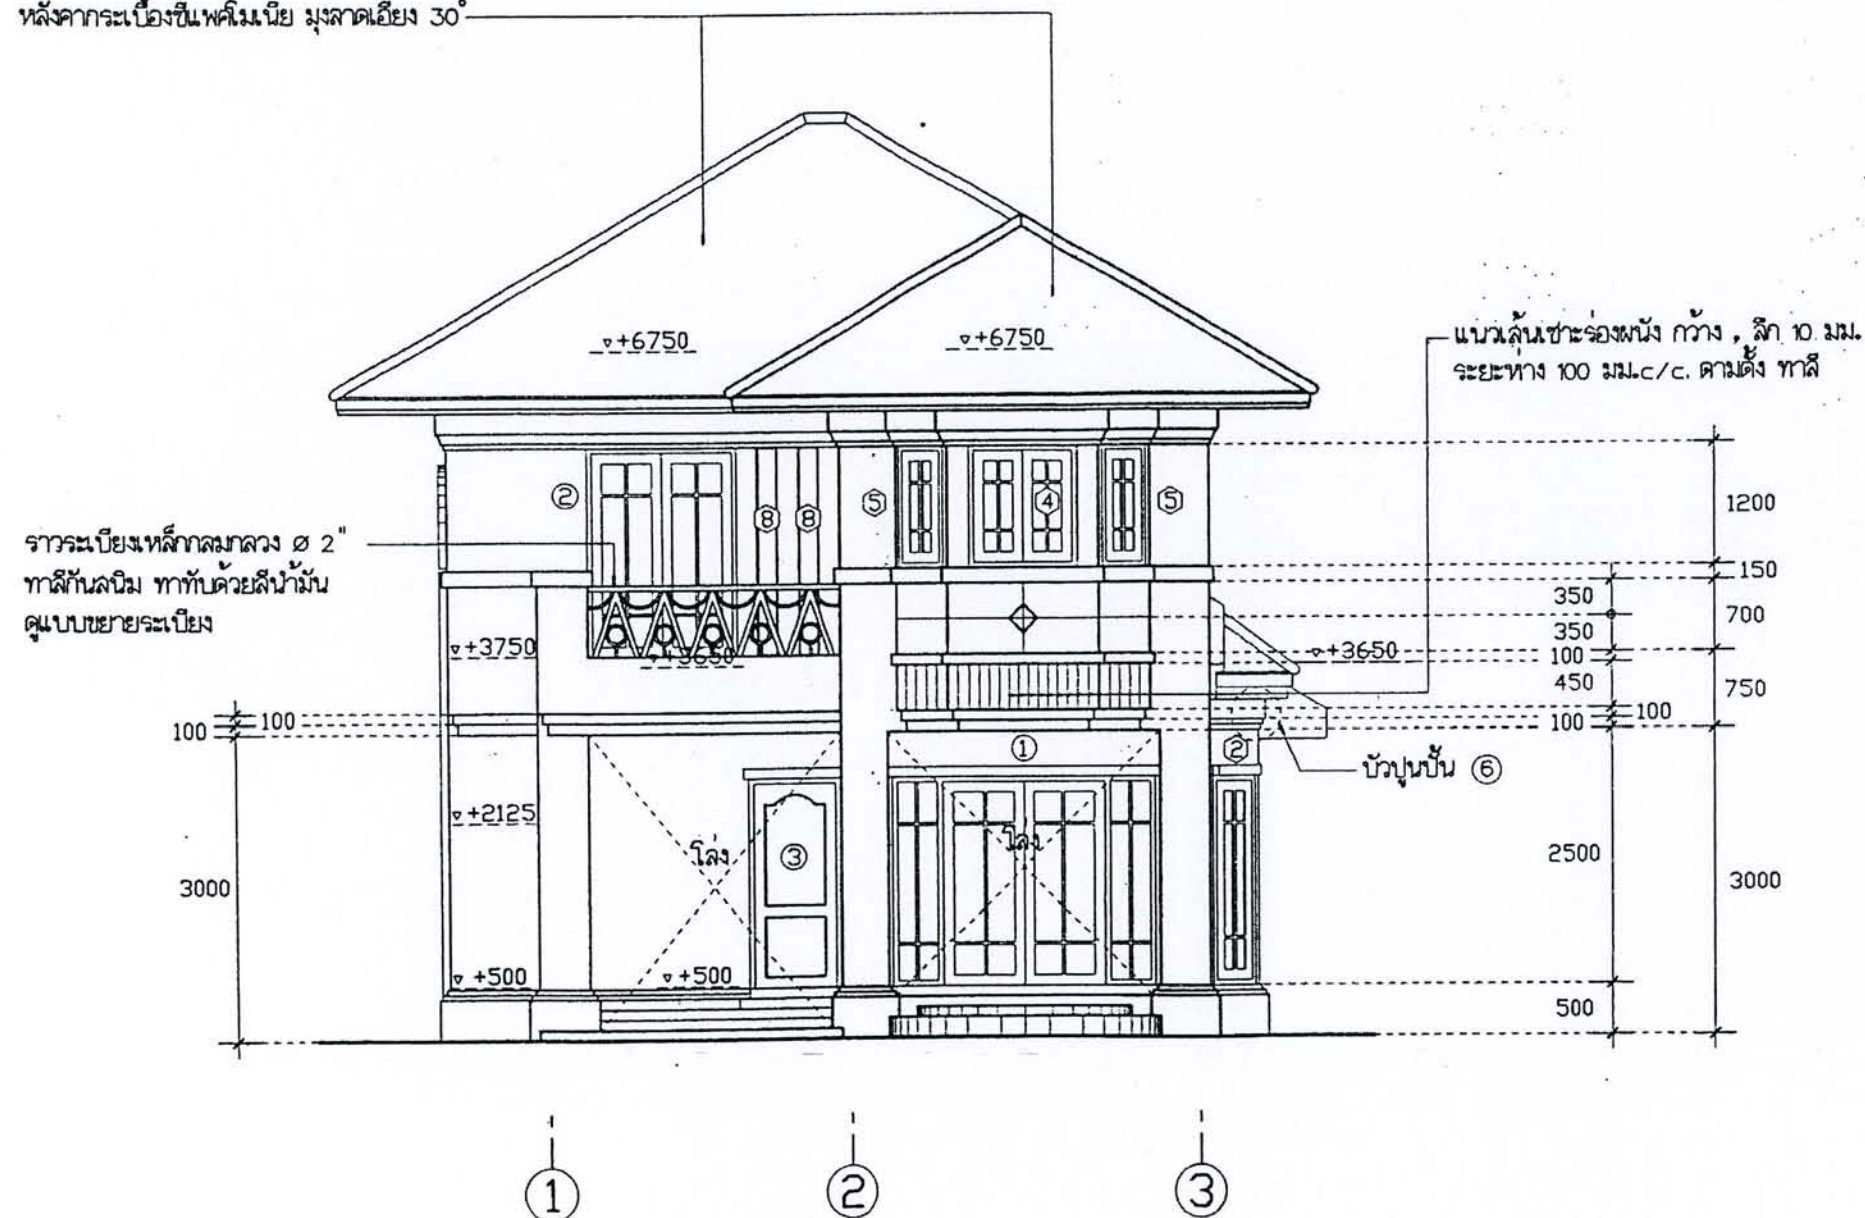


รูปด้าน ①
มาตราส่วน 1 : 75



โครงการ
แบบบ้านยืมเพื่อประชาชน

ตามนโยบาย
ม.ร.ว. สุขุมพันธุ์ บริพัตร
ผู้ว่าราชการกรุงเทพมหานคร

โดยสำนักการโยธา
กรุงเทพมหานคร

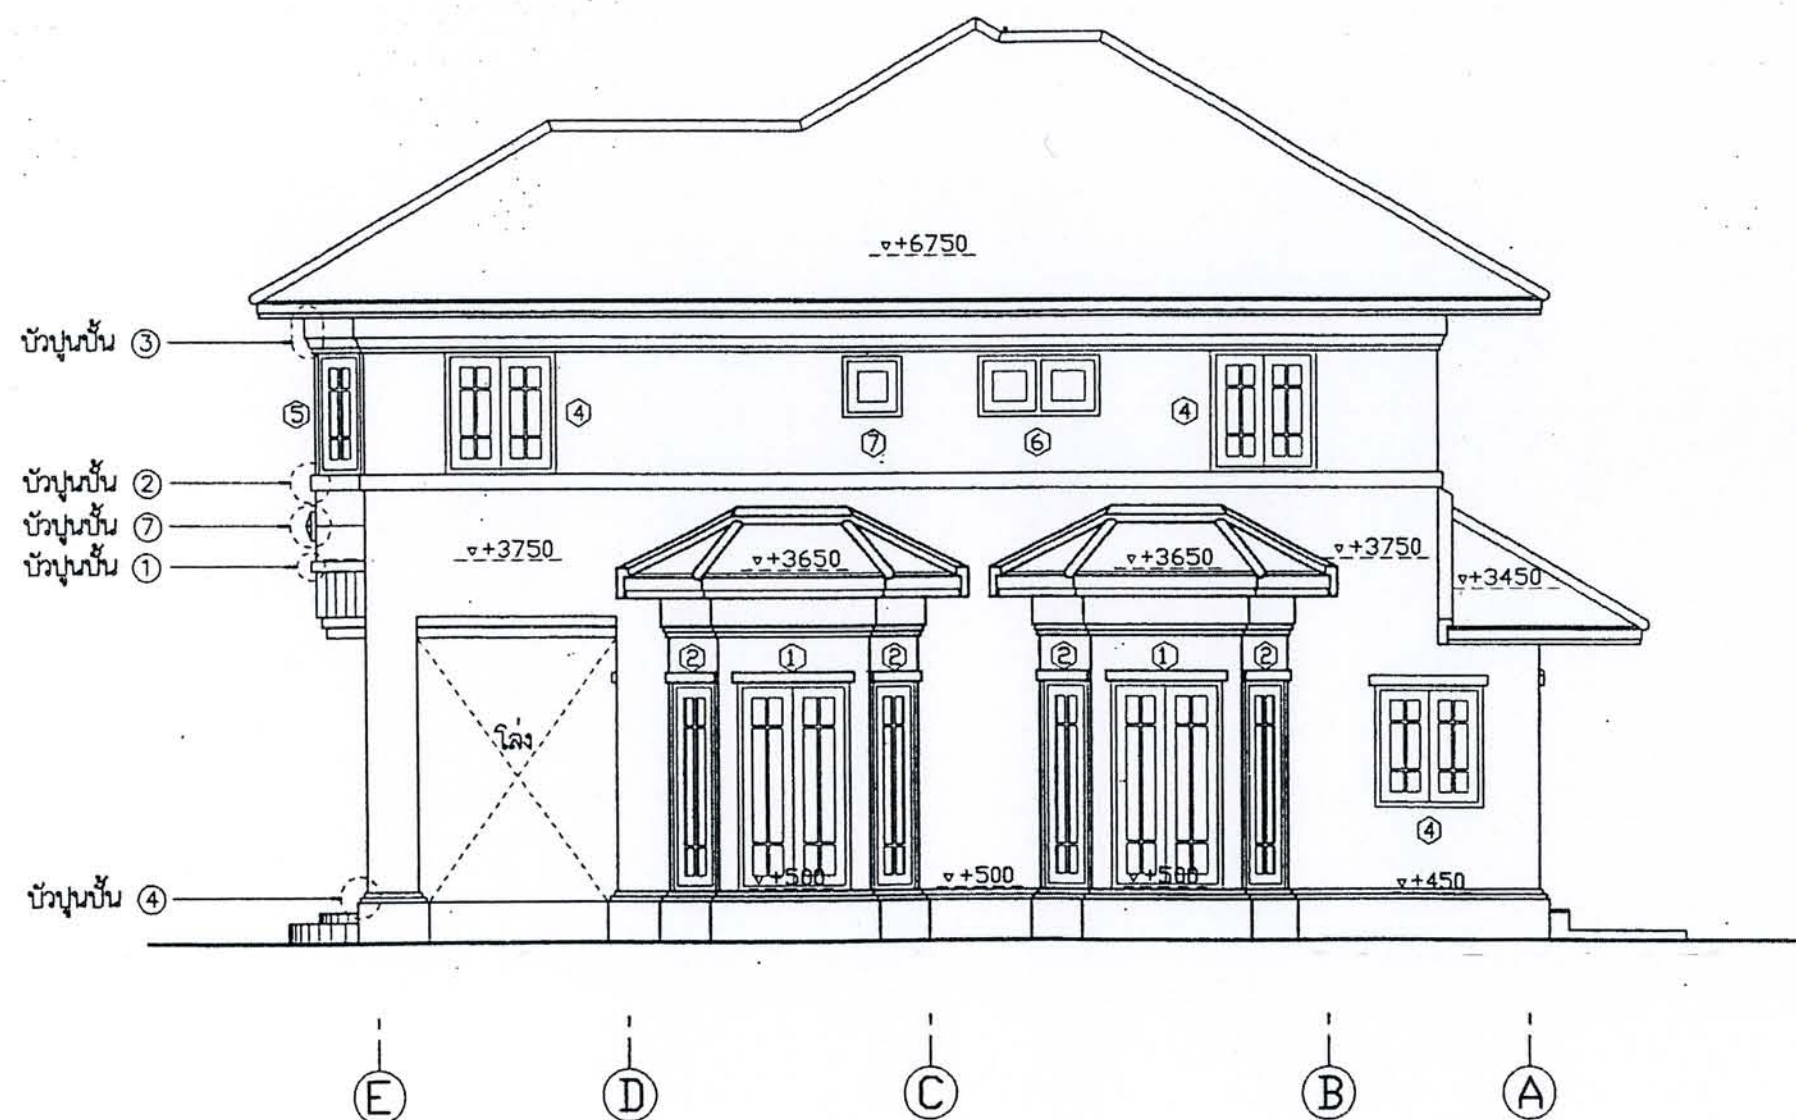

รูปด้าน ②
มาตราส่วน 1 : 75


ได้รับความอนุเคราะห์แบบ
จาก
บริษัท แลนด์ โธม
(ประเทศไทย) จำกัด



โครงการ
แบบบ้านยืมเพื่อประชาชน

ตามนโยบาย
ม.ร.ว. สุขุมพันธุ์ บริพัตร
ผู้ว่าราชการกรุงเทพมหานคร

โดยสำนักงานโยธา
กรุงเทพมหานคร

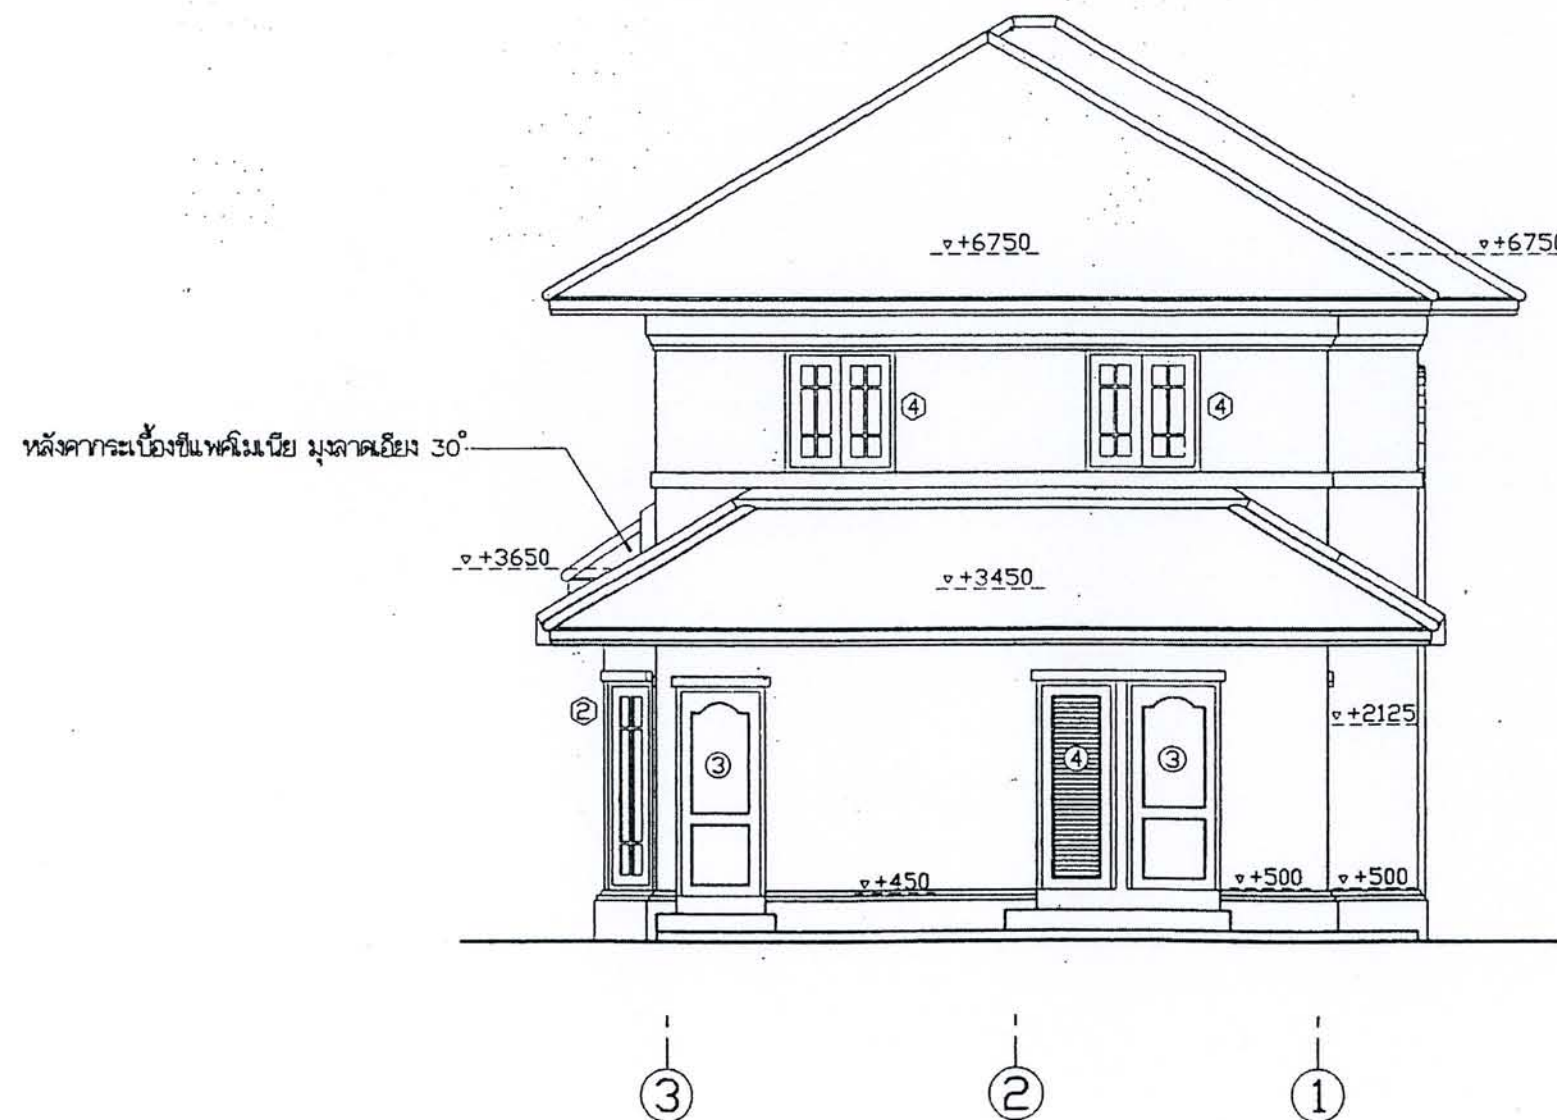

รูปด้าน ③
มาตราส่วน 1 : 75


ได้รับความอนุเคราะห์แบบ
จาก
บริษัท แลนด์ โฮม
(ประเทศไทย) จำกัด



โครงการ
แบบบ้านยืมเพื่อประชาชน

ตามนโยบาย
ม.ร.ว. สุขุมพันธุ์ บริพัตร
ผู้ว่าราชการกรุงเทพมหานคร

โดยสำนักการโยธา
กรุงเทพมหานคร

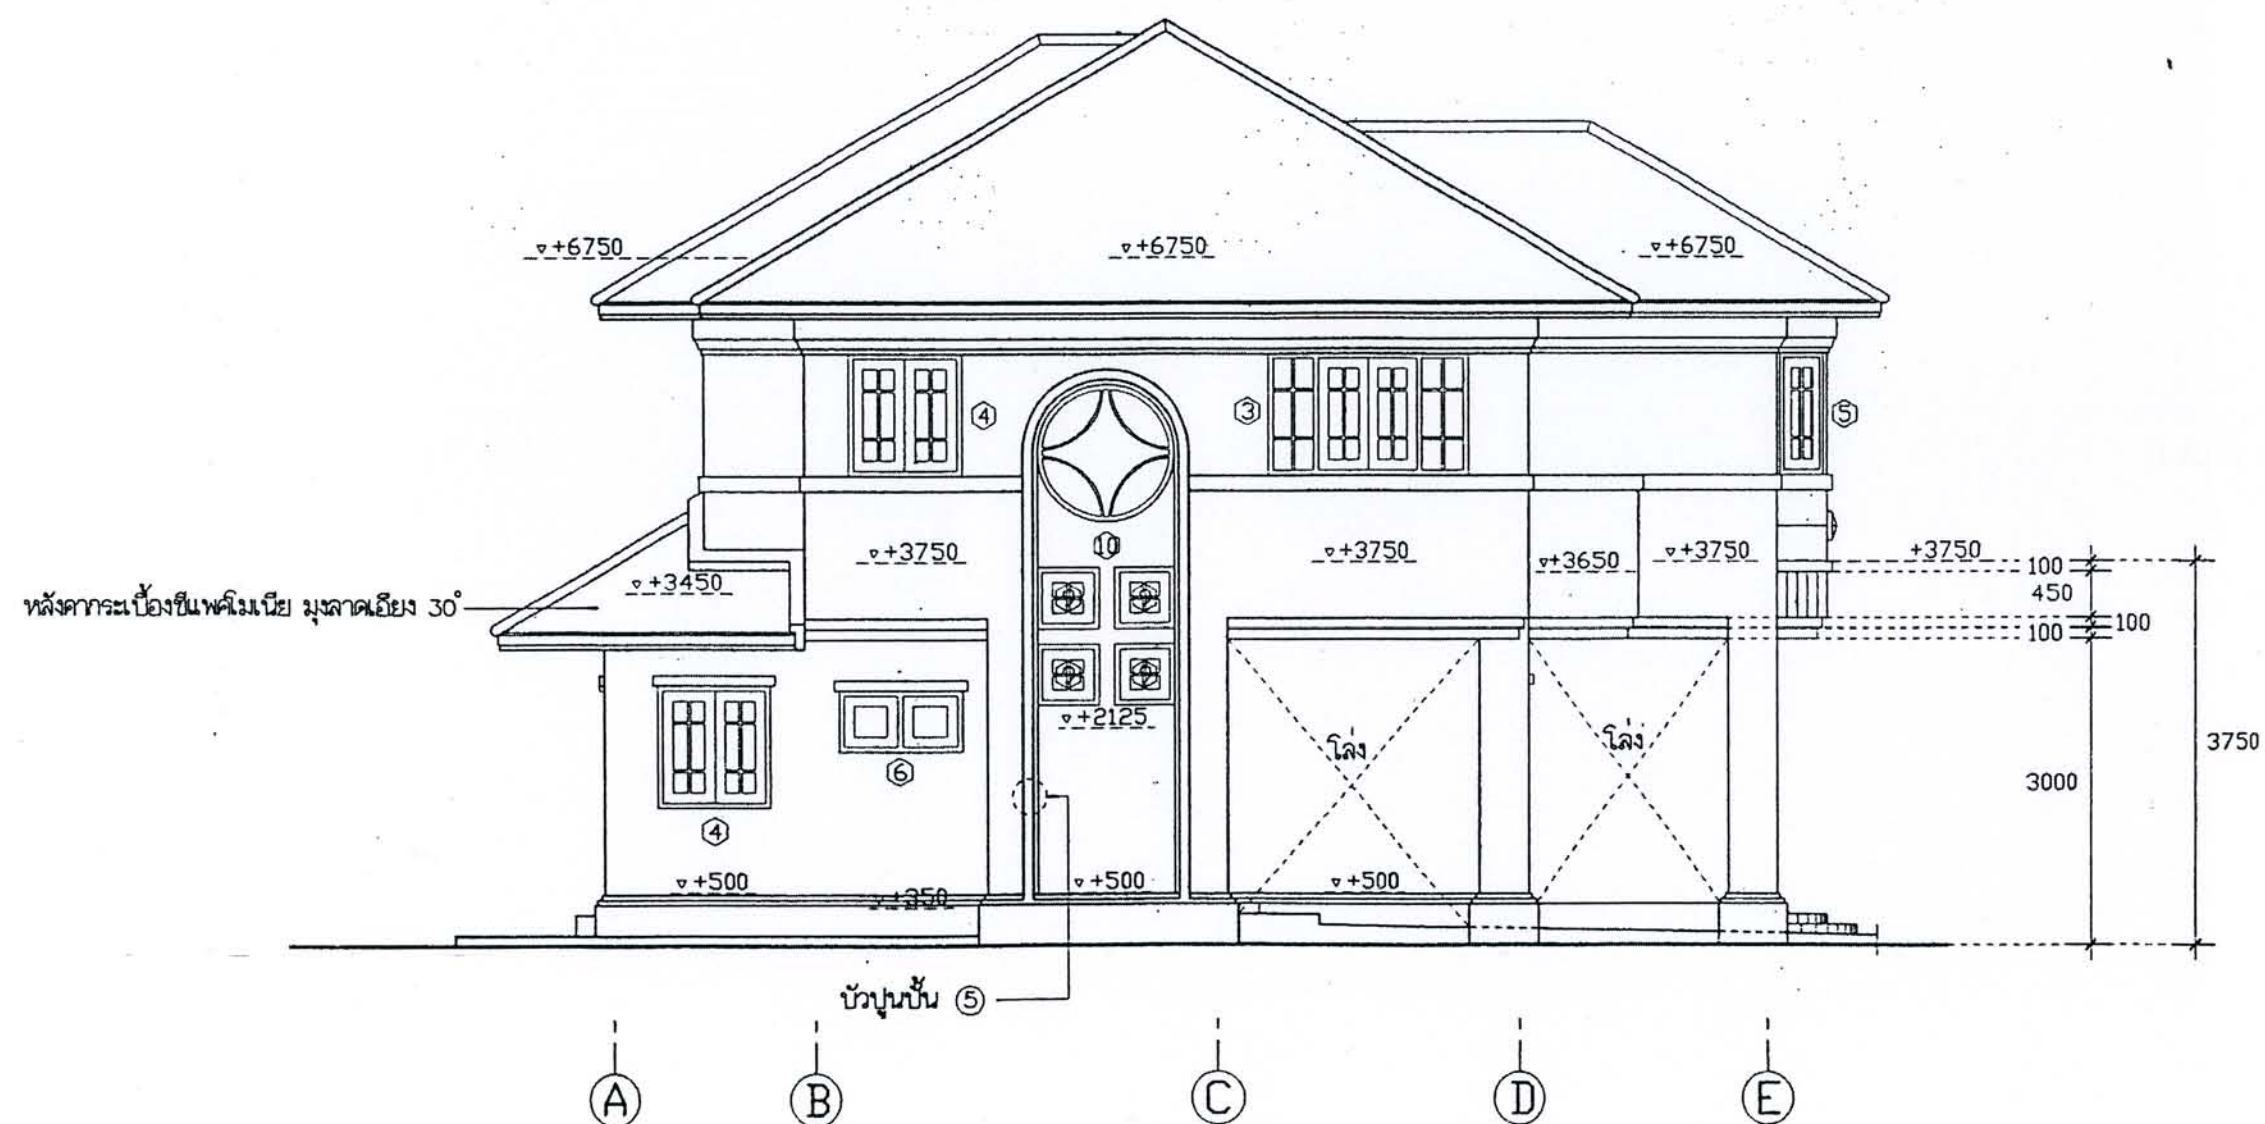

รูปด้าน 4
มาตราส่วน 1 : 75

ได้รับความอนุเคราะห์แบบ
จาก
บริษัท แคนดี้ โฮม
(ประเทศไทย) จำกัด

สัญลักษณ์ประกอบแบบ "S"



รายการไฟฟ้า

สัญลักษณ์	ความหมาย	ขนาด - ยี่ห้อ - รุ่น
	แผงควบคุมไฟฟ้า	Square-D ขนาด 15 Amp. แบบกล่องเหล็กพร้อม circuit Breaker 7 ชุด
	โคมไฟฟ้า	ครอบแก้วกลม ๑๔" ตัวขึ้นหลอดฟลูออโรเรสเซนต์ 32 W. แบบกลมแสงสีขาว
	โคมไฟฟ้า	ครอบแก้วกลม ๑๘" หลอดฟลูออโรเรสเซนต์ 60 W. แสงสีเหลือง
	หลอดฟลูออโรเรสเซนต์	รางหลอดฟลูออโรเรสเซนต์ ครอบพลาสติก ขนาด 1 X 20 W. แสงสีขาว
	หลอดฟลูออโรเรสเซนต์	รางหลอดฟลูออโรเรสเซนต์ ครอบพลาสติก ขนาด 1 X 40 W. แสงสีขาว
	ไฟโคมแขวนเพดาน	โคมไฟแก้วผิวขึ้น ๑๒" หลอดธรรมดา 60 W.
	ไฟกิ่งติดผนัง	โคมไฟกิ่งหลอด 60 W. พลาสติก
	สวิทช์ไฟฟ้า	Single way ชนิดฝังในผนังของ NATIONAL (ชองแท) ติดตั้งสูงจากพื้น 1200 มม.
	สวิทช์ไฟฟ้า 2 ทาง	Two way ชนิดฝังในผนังของ NATIONAL (ชองแท) ติดตั้งสูงจากพื้น 1200 มม.
	ปลั๊กไฟ, เต้าเสียบ	ปลั๊กไฟแบบเรียบชนิดฝังในผนังแบบ 2 เต้าเสียบต่อ 1 ชุด พร้อมสายดินตาม- การไฟฟ้า ติดตั้งสูงจากพื้น 200 มม. ของ NATIONAL (ชองแท) ติดห่างจากผนัง 100 มม.
	ปลั๊กไฟ, เต้าเสียบ	ปลั๊กไฟแบบเรียบชนิดฝังในผนังแบบ 2 เต้าเสียบต่อ 1 ชุด พร้อมสายดินตาม- การไฟฟ้า ติดตั้งสูงจากพื้น 1000 มม. ของ NATIONAL (ชองแท) ติดห่างจากผนัง 100 มม.
	ปลั๊กสายอากาศ TV.	ใช้สายอากาศ TV.RG-6 โดยเดินสายไปยังห้องนอนที่ติดตั้งแล้วที่ปลายปลั๊กไว้ 1 ม.
	โทรทัศน์	เดินสายตามมาตรฐานไฟฟ้า โดยเดินสายไปยังห้องนอนที่ติดตั้งแล้วที่ปลายปลั๊กไว้ 1 ม.
	สวิทช์แอร์	ตำแหน่งตามแบบ
	แสดงการเดินสายไฟแบบ-	สายไฟใช้สาย PVC. ของ YAZAKI หรือ BANGKOK CABLE
	เดินลอย	เดินลอยยึดด้วยสายรัดเข็มขัดระยะห่าง 100 มม. โดย
		- สายไฟสำหรับ สวิทช์ไฟ ที่ใช้ไฟ ขนาด 1.0 มม ²
		- สายไฟสำหรับ ปลั๊กไฟ ที่ใช้ไฟ ขนาด 2.5 มม ² (แบบมีสายดิน)
		- สายไฟสำหรับ แอร์ ที่ใช้ไฟ ขนาด 10.0 มม ²
		- สายไฟสำหรับ เครื่องทำน้ำร้อน ที่ใช้ไฟ ขนาด 10.0 มม ²
		- สำหรับสายเมนใช้สาย PVC. ของ YAZAKI หรือ BANGKOK CABLE
		ขนาด 16.00 มม ² ต่อห่างจากชายคาน้ำฝน 16000 มม.

รายการเปลี่ยนแปลงเพิ่มเติมไฟฟ้า

* ไม่มีรายการเปลี่ยนแปลง

- หมายเหตุ :
- ให้เดินสายดินตามมาตรฐานของการไฟฟ้าอย่างถูกต้อง
 - ราคากำหนด 3,000,000 บาท ใช้ไฟ ขนาด 30 Amp. 2 สายของ Square-D พร้อมสายเมน
ตู้เบสตู้เซอร์กิต 16 ช่อง
 - ราคากำหนด 5,000,000 บาท ใช้ไฟ ขนาด 50 Amp. 2 สายของ Square-D พร้อมสายเมน

บ้าน SMILE HOME
V.1 [11/2/45]

ได้รับความอนุเคราะห์แบบ
จาก
บริษัท แลนด์ โฮม
(ประเทศไทย) จำกัด

สัญลักษณ์ประกอบแบบ "S"



โครงการ
แบบบ้านยิ้มเพื่อประชาชน

ตามนโยบาย
ม.ร.ว. สุขุมพันธุ์ บริพัตร
ผู้ว่าราชการกรุงเทพมหานคร

โดยสำนักการโยธา
กรุงเทพมหานคร

ได้รับความอนุเคราะห์แบบ
จาก
บริษัท แลนด์ โสม
(ประเทศไทย) จำกัด

รายการลูขากิบาล

สัญลักษณ์	ความหมาย	ขนาด และ จำนวนอุปกรณ์ที่ใช้
	ท่อ PVC	ท่อ PVC. Ø 4" ขึ้นคุณภาพ Class 8.5 ติดตั้งให้มีความลาดเอียง 1 : 200 ปลายท่อ- ให้ท่อแบบ 3 ทาง ตัว T
	ท่อน้ำทิ้ง	(ท่อเมน) ท่อ PVC. Ø 2" ขึ้นคุณภาพ Class 8.5 ติดตั้งให้มีความลาดเอียง 1 : 200 ให้ท่อน้ำทิ้งมีผลัดสะดวก
	ท่อน้ำทิ้ง	(ต่อจากลูขากิบาล) ท่อ PVC. Ø 1 1/2" ขึ้นคุณภาพ Class 8.5
	ท่อน้ำดี	(ท่อน้ำประปา) ท่อ PVC. Ø 1/2" ขึ้นคุณภาพ Class 13.5
	ท่อน้ำเย็น	(ท่อเมน) ท่อ PVC. Ø 3/4" ขึ้นคุณภาพ Class 13.5
	ท่อน้ำร้อน	ให้ท่อเหล็กอานลึงระลึ Class B Ø 1/2"
	ท่อระบายอากาศ	ท่อ PVC Ø 1" ขึ้นคุณภาพ Class 8.5 ปลายท่อต่อด้วยข้อต่อ 3 ทาง ตัว T ท่อระบายอากาศสูงจากพื้น 3500 มม. ยึดติดกับผนังหรือลาคยัดระยะห่าง 300 มม.
	ท่อระบายน้ำเสีย	ท่อโม่คยัดหิน Ø 150 มม. ติดตั้งให้มีความลาดเอียง 1 : 200 ข้อต่อบริเวณท่อกับ- บ่อพักให้ท่อยื่นเข้าไปบ่อพักอย่างน้อย 50 มม.
	จุดระบายน้ำทิ้ง	ตำแหน่งที่จุดระบายน้ำทิ้งจะลงข้อต่อลงท่อเมนน้ำทิ้งมีแผ่นเหล็กอะกรดักล้น
	จุดระบายน้ำล้น	ตำแหน่งจุดน้ำทิ้งจากชักโครก
	บ่อพัก	บ่อพักน้ำเสียสำเร็จรูป ขนาด 300X400X400 มม. พร้อมฝาปิดทุกระยะ 6.00 ม. ทุกช่วงพักเสีย
	จุดจ่ายน้ำประปา	จุดจ่ายน้ำดี (ประปา) ซึ่งต้องสูงให้ได้ตามแบบ
	บ่อกรอง	ใช้ระบบบำบัดน้ำเสีย ถึงบำบัดน้ำเสียสำเร็จรูป ของ AQUA-PAC หรือเทียบเท่า
	มิเตอร์น้ำ	ตามมาตรฐานของการประปา
	เครื่องปั้มน้ำ	ตำแหน่งตามแบบ
	แนวลาดเอียง	ลาดเอียงตามแบบ

- หมายเหตุ :
- ท่อ PVC. ที่ข้อต่อทุกจุดจะต้องทากาวก่อนต่อ เมื่อต่อท่อเสร็จเรียบร้อยแล้วจะต้องไม่รื้อขึ้น
 - ท่อน้ำดีจะต้องขุดขั้วดินที่จะต่อท่อผ่านช่องเหล็กท่อกุดและบริเวณรอยต่อระหว่างท่อ PVC.
เข้ากับช่องเหล็กจะต้องพันท่อก่อนต่อ เมื่อต่อท่อเสร็จเรียบร้อยแล้วจะต้องไม่รื้อขึ้น
 - ท่อประปา (น้ำร้อน) ที่ต่อกับลาคยัดให้ใช้ปากวาล์วทุกจุด
 - ท่อระบายน้ำและบ่อพักต้องจากตัวอาคาร ถึงบ่อพักอาคารมีไม่เกิน 16.00 ม.


รายการประกอบแบบลูขากิบาล TYPE "S"

อ่างอาบน้ำ (ถ้ามมี)	CRISTINA (TEENA-D) CT-5013 C พร้อมเดินลาคยัดไฟฟ้า และ ท่อน้ำร้อนของเครื่องทำน้ำร้อน 1 ชุด (ไม่รวมเครื่องทำน้ำร้อน) ก๊อกลมหน้า JAZZ STD. A 7601 (AMERICAN STANDARD)
อ่างล้างหน้า	AMERICAN STANDARD รุ่น TF-476 ชนิดฝังคาน์เตอร์ , ก๊อกลมหน้า JAZZ STD. A 7000 หรือลูขากิบาลดักล้น
ก๊อกลม	ใช้แบบ BALL VALVE (ทั่วป)
โถล้างน้ราบ	AMERICAN STANDARD รุ่น TF-2310 (ทั่วป) , ลาคยัดระ HANG 5502 . รุ่น TF-2310 (คนใช้)
ฝักบัวลาคยัด	JAZZ STD. A 7003 A (AMERICAN STANDARD)
ที่วางลูป	AMERICAN STANDARD รุ่น TF-9000
ที่ใส่กระดาษชำระ	AMERICAN STANDARD รุ่น TF-9001
ราวนวนลาค	AMERICAN STANDARD รุ่น TF-9085
กระจก	กระจกเบยอญีรป ยัดด้วยลาค
ลาคยัด	ทั่วปเบยอญีรป BEIGE ยกเว้นห้องน้คานใช้ ใช้ลาค

รายการประกอบแบบลูขากิบาล กรณีมีการเปลี่ยนแปลงเพิ่มเติม

* ไม่มีรายการเปลี่ยนแปลง

รายการเปลี่ยนแปลงเพิ่มเติมลูขากิบาล

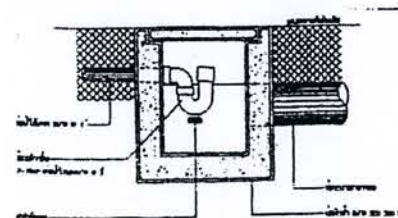

แบบขยัดดักล้นกับเมน

ท่อน้ำทิ้งที่ใช้ดักน้ำในข้อขยัด
บ่อพักสำเร็จรูป คูแบบขยัดขยัด

* ไม่มีรายการเปลี่ยนแปลง


บ้าน SMILE HOME
V.1 [11/2/45]




โครงการ
แบบบ้านยืมเพื่อประชาชน

ตามนโยบาย
ม.ร.ว. สุขุมพันธุ์ บริพัตร
ผู้ว่าราชการกรุงเทพมหานคร

โดยสำนักการโยธา
กรุงเทพมหานคร

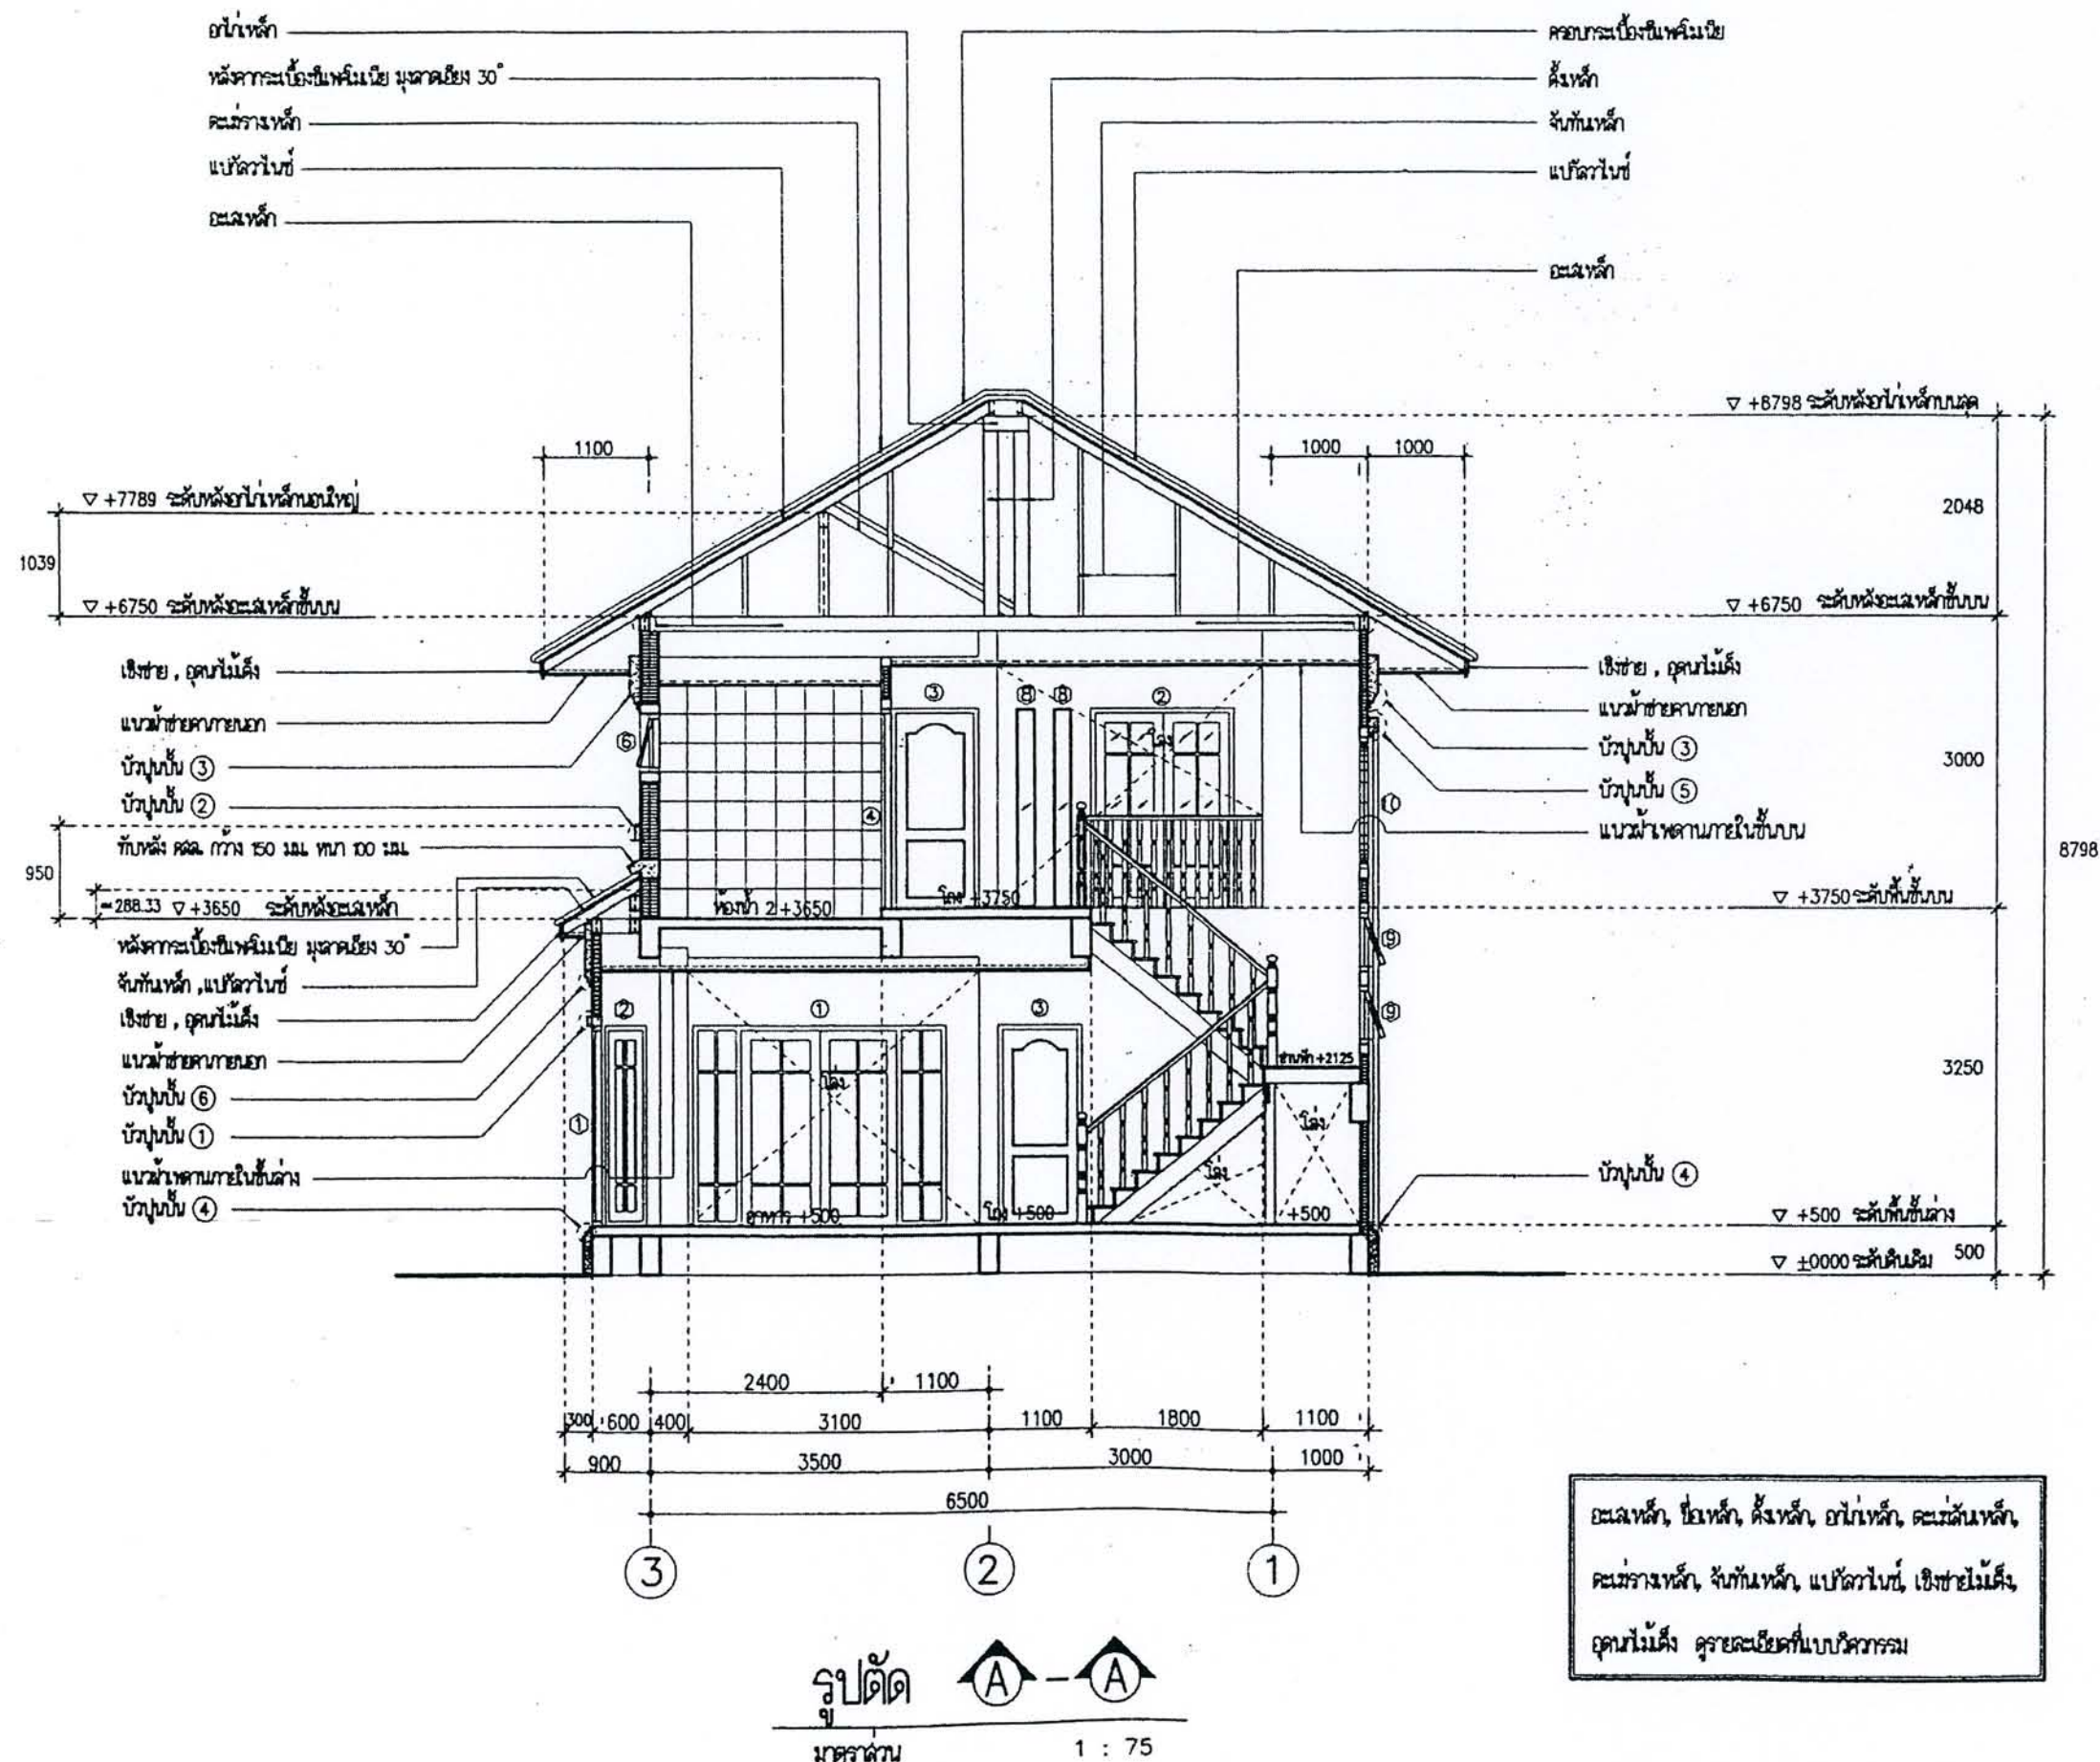


ได้รับความอนุเคราะห์แบบ
จาก
บริษัท แลนด์ โฮม
(ประเทศไทย) จำกัด

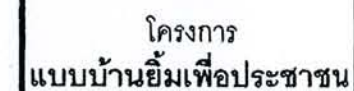

โดยสำนักงานโยธา
กรุงเทพมหานคร

ได้รับความอนุเคราะห์แบบ
จาก
บริษัท แลนด์ โฮม
(ประเทศไทย) จำกัด

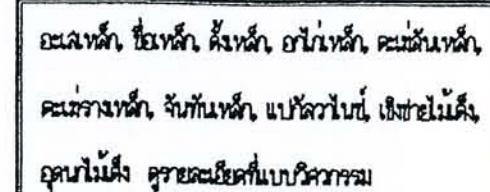






โครงการ
แบบบ้านยืมเพื่อประชาชน

ตามนโยบาย
ม.ร.ว. สุขุมพันธุ์ บริพัตร
ผู้ว่าราชการกรุงเทพมหานคร

โดยสำนักงานโยธา
กรุงเทพมหานคร

ได้รับความอนุเคราะห์แบบ
จาก
บริษัท แลนด์ โยม
(ประเทศไทย) จำกัด

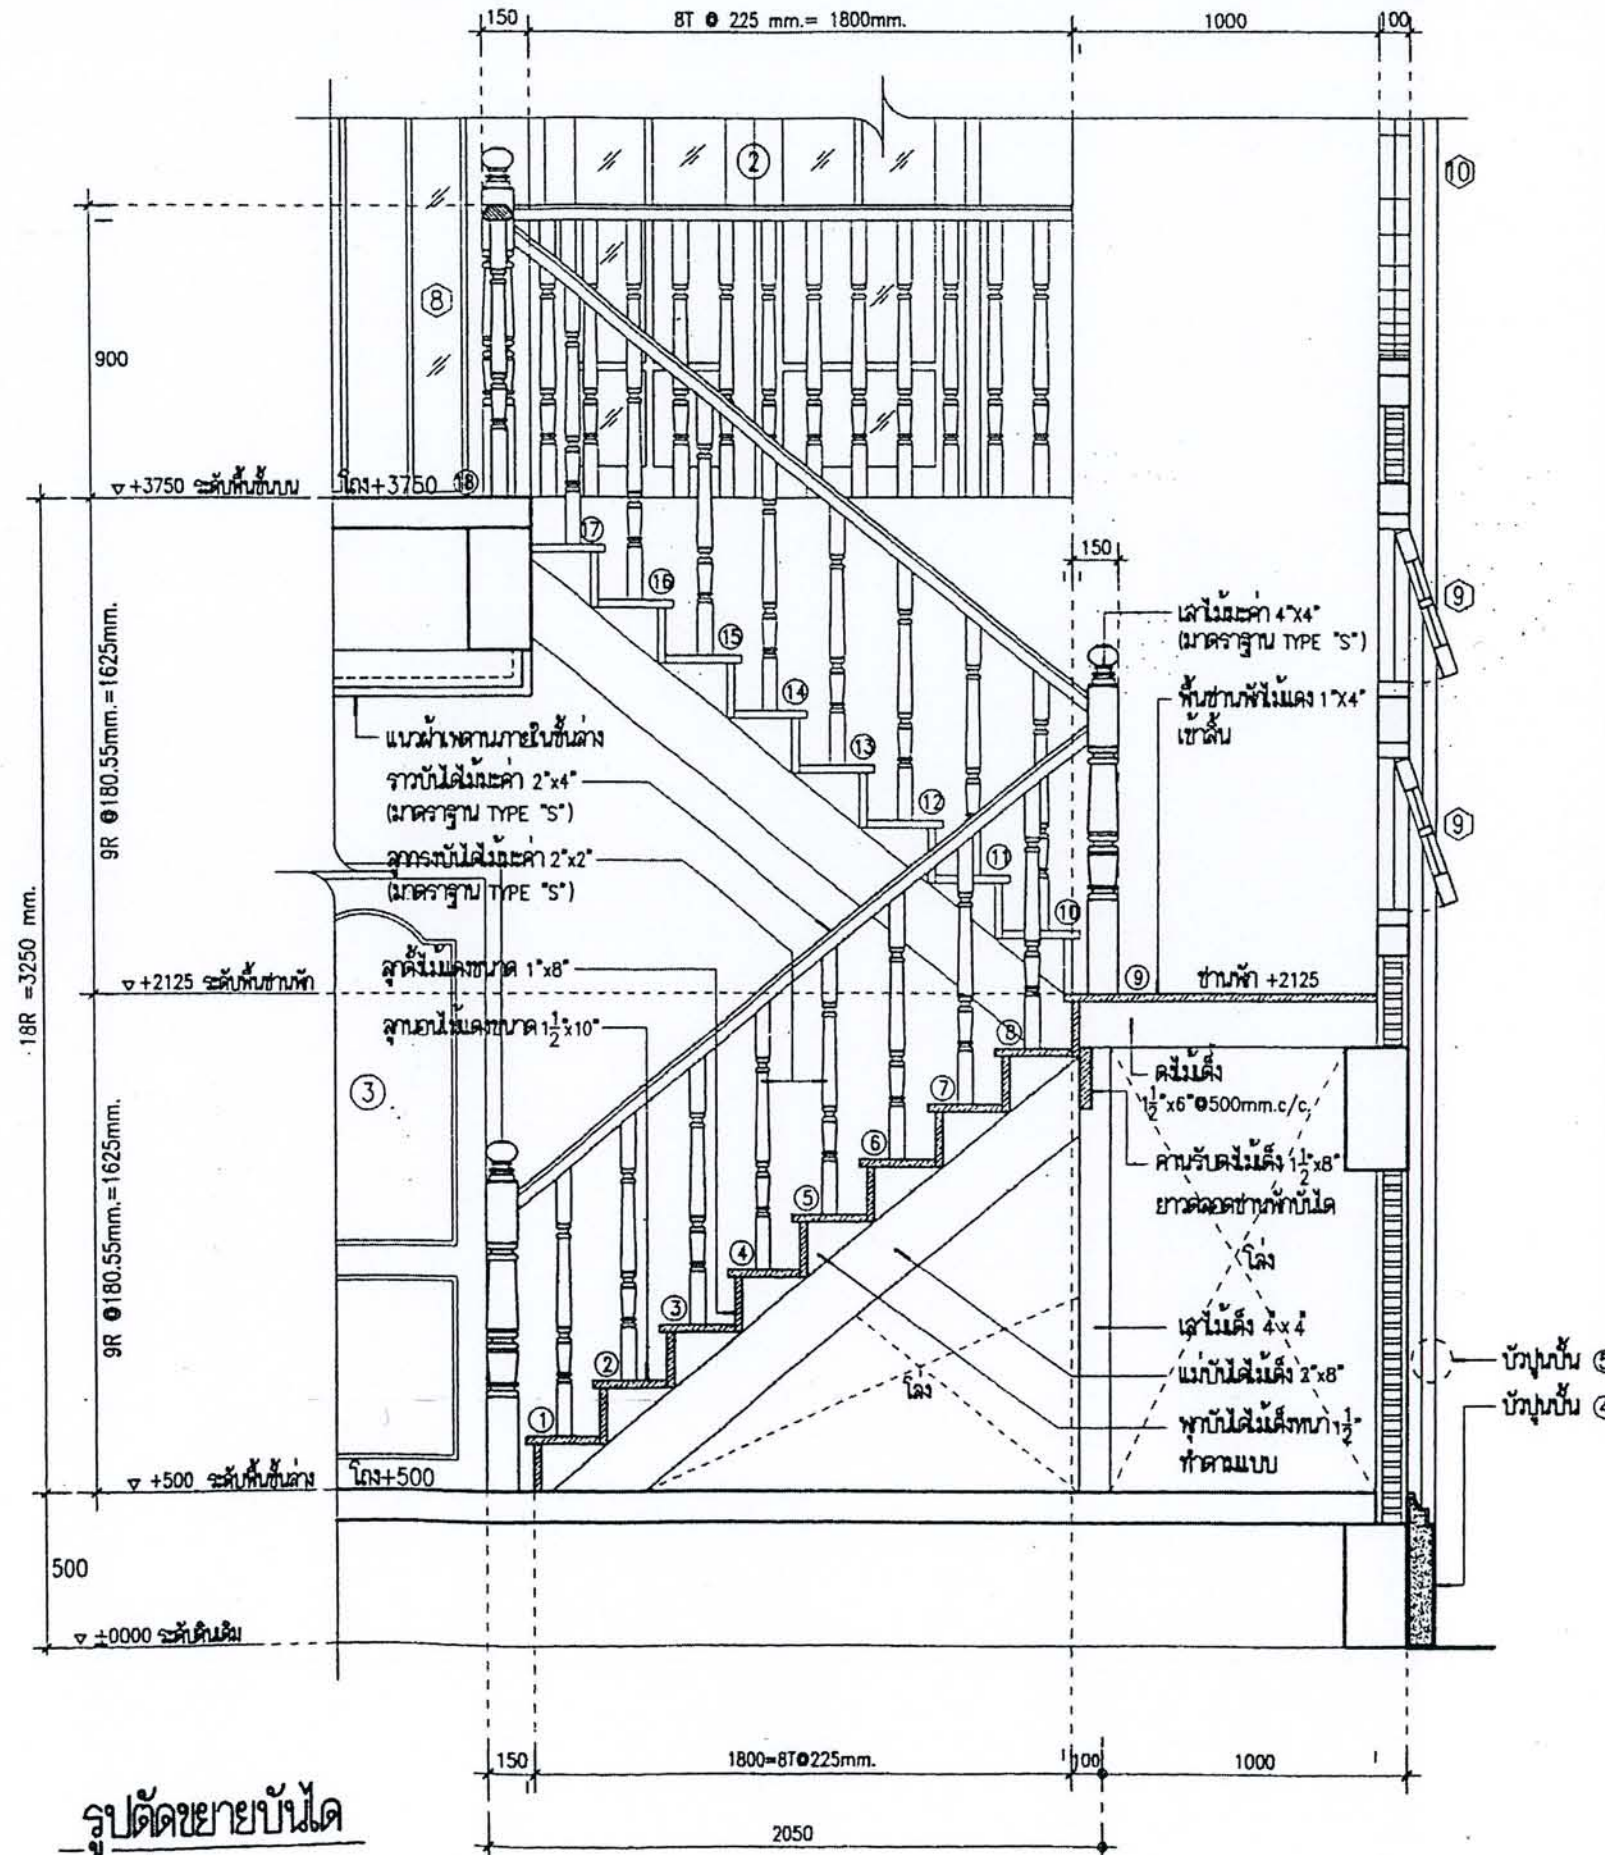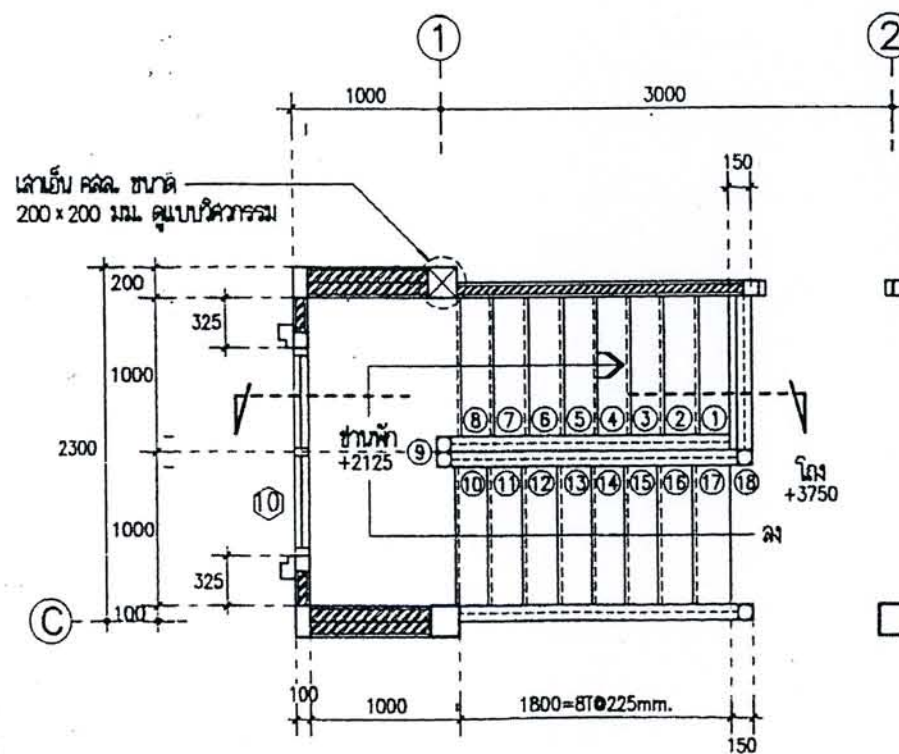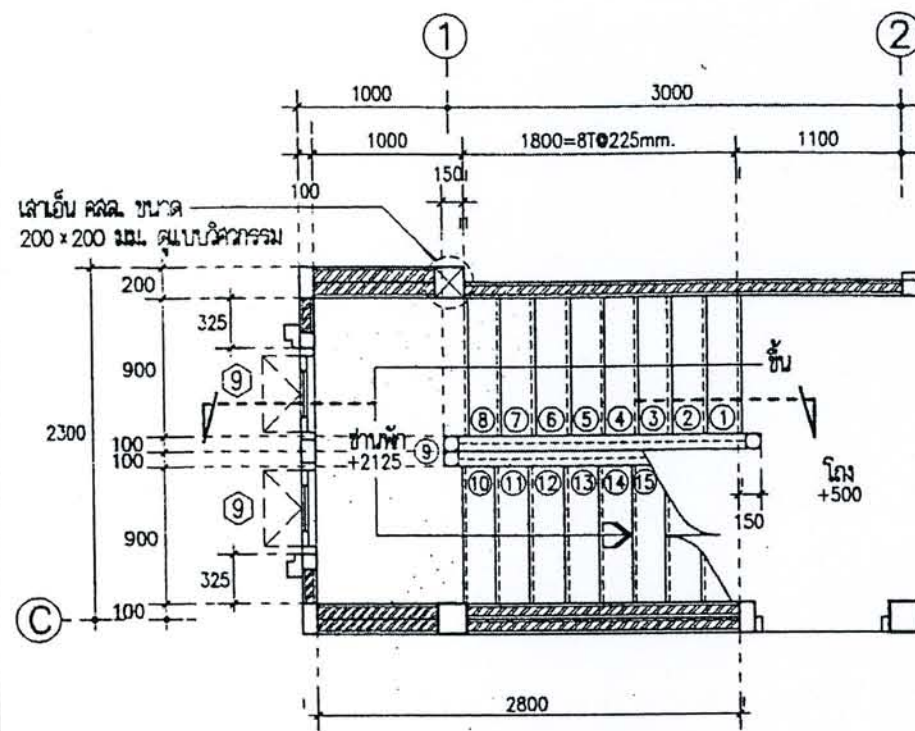





โครงการ
แบบบ้านยืมเพื่อประชาชน

ตามนโยบาย
ม.ร.ว. สุขุมพันธุ์ บริพัตร
ผู้ว่าราชการกรุงเทพมหานคร


โดยสำนักงานโยธา
กรุงเทพมหานคร

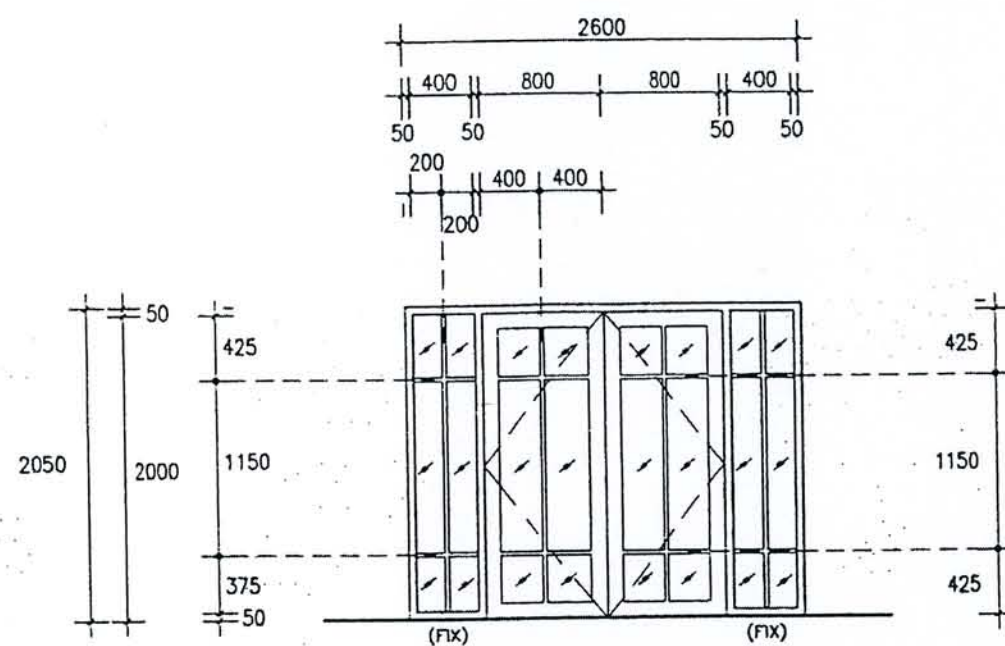


①

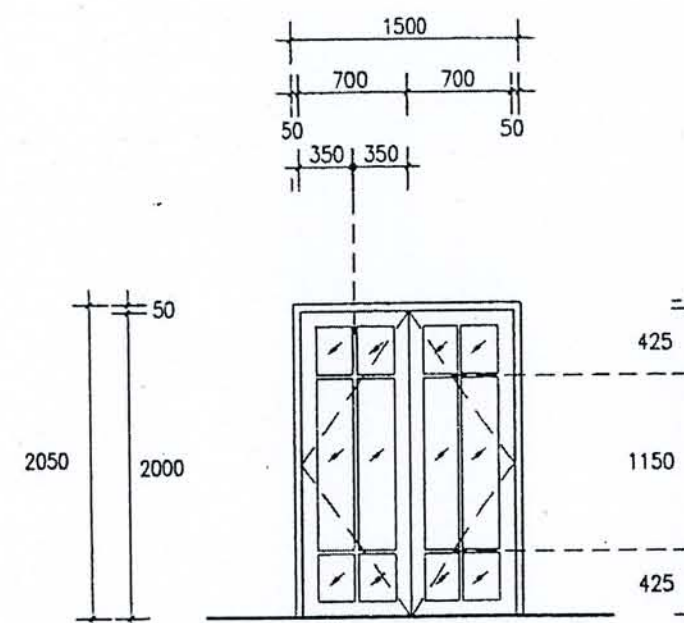

②

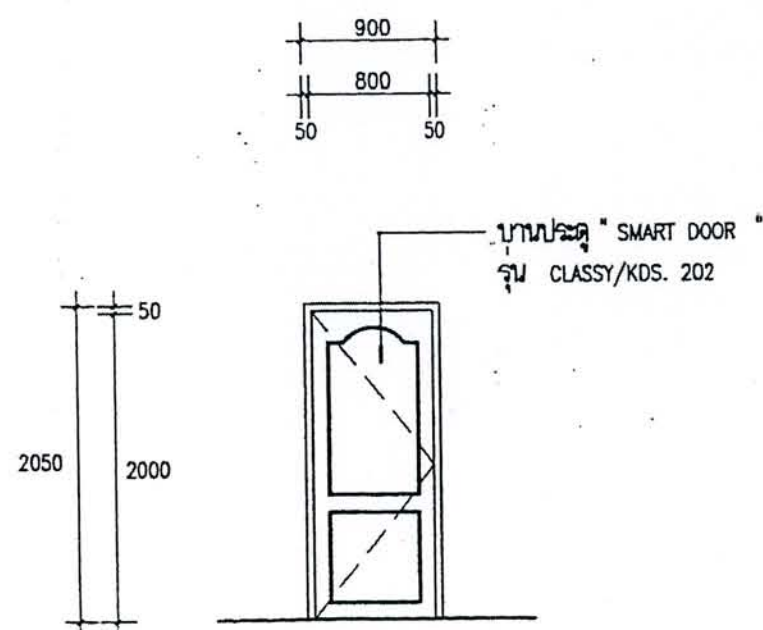

③

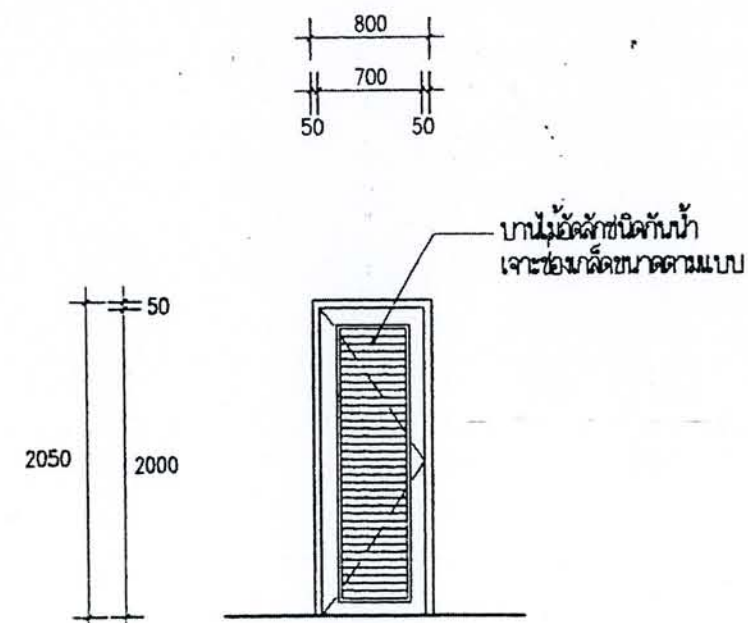

④

แบบขยายประตู

มาตรฐาน 1 : 50



ได้รับความอนุเคราะห์แบบ
จาก
บริษัท แลนด์ โฮม
(ประเทศไทย) จำกัด



โครงการ
แบบบ้านยืมเพื่อประชาชน

ตามนโยบาย
ม.ร.ว. สุขุมพันธุ์ บริพัตร
ผู้ว่าราชการกรุงเทพมหานคร

โดยสำนักงานโยธา
กรุงเทพมหานคร

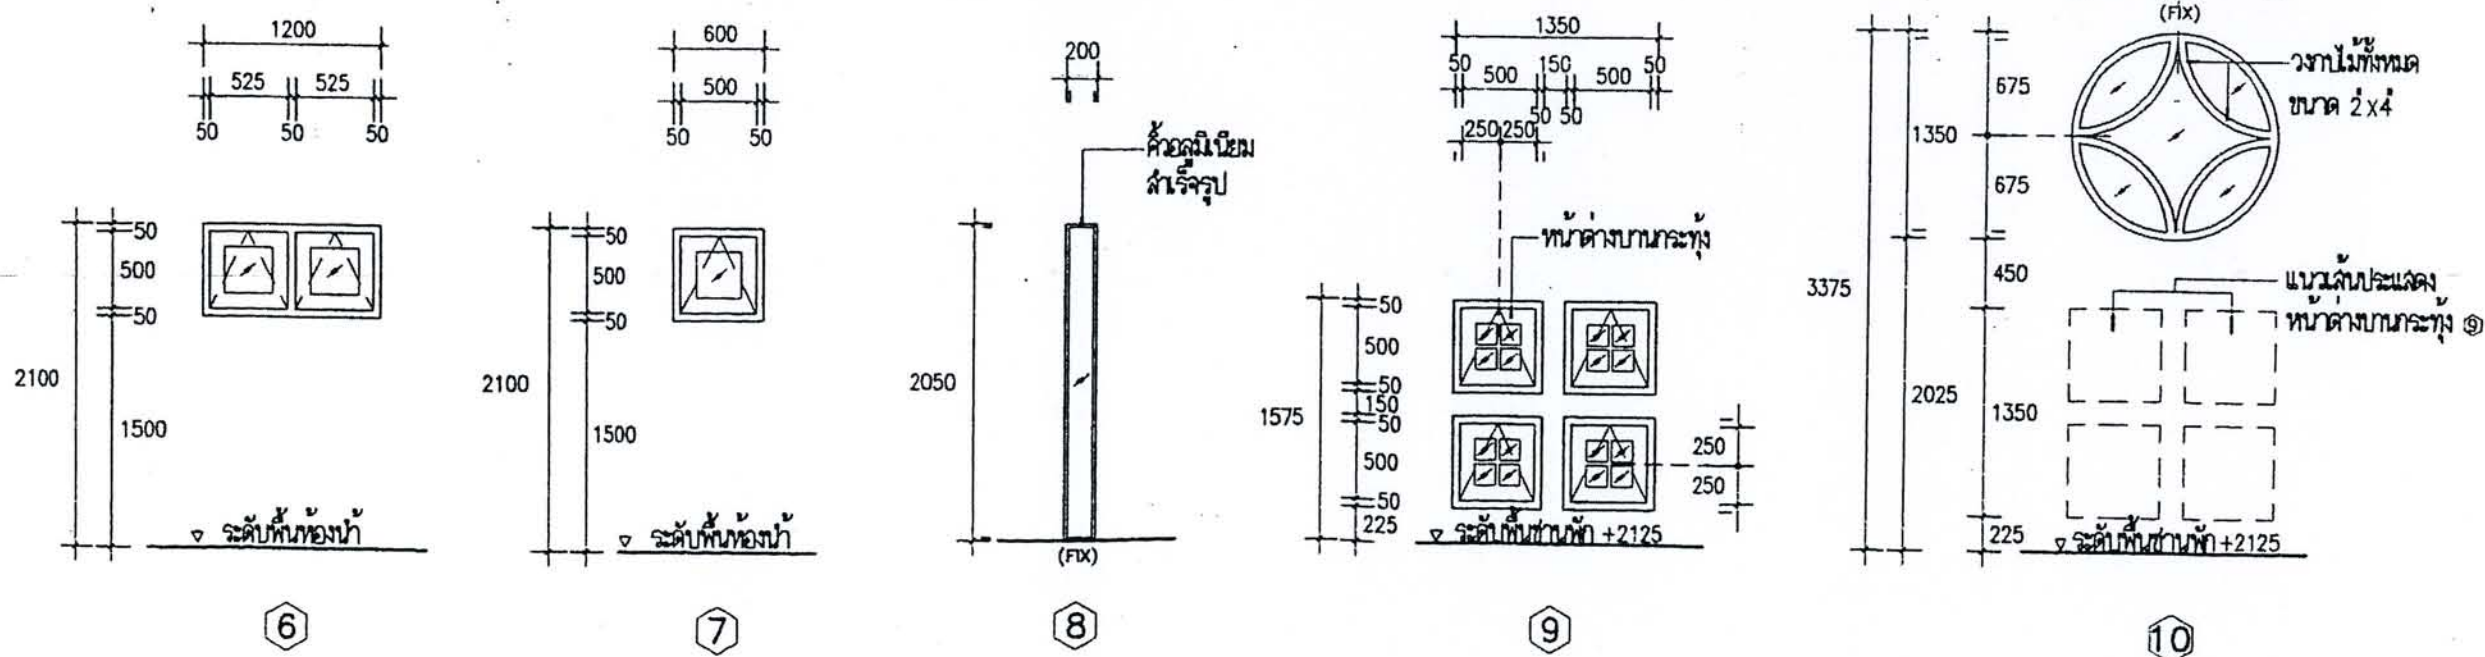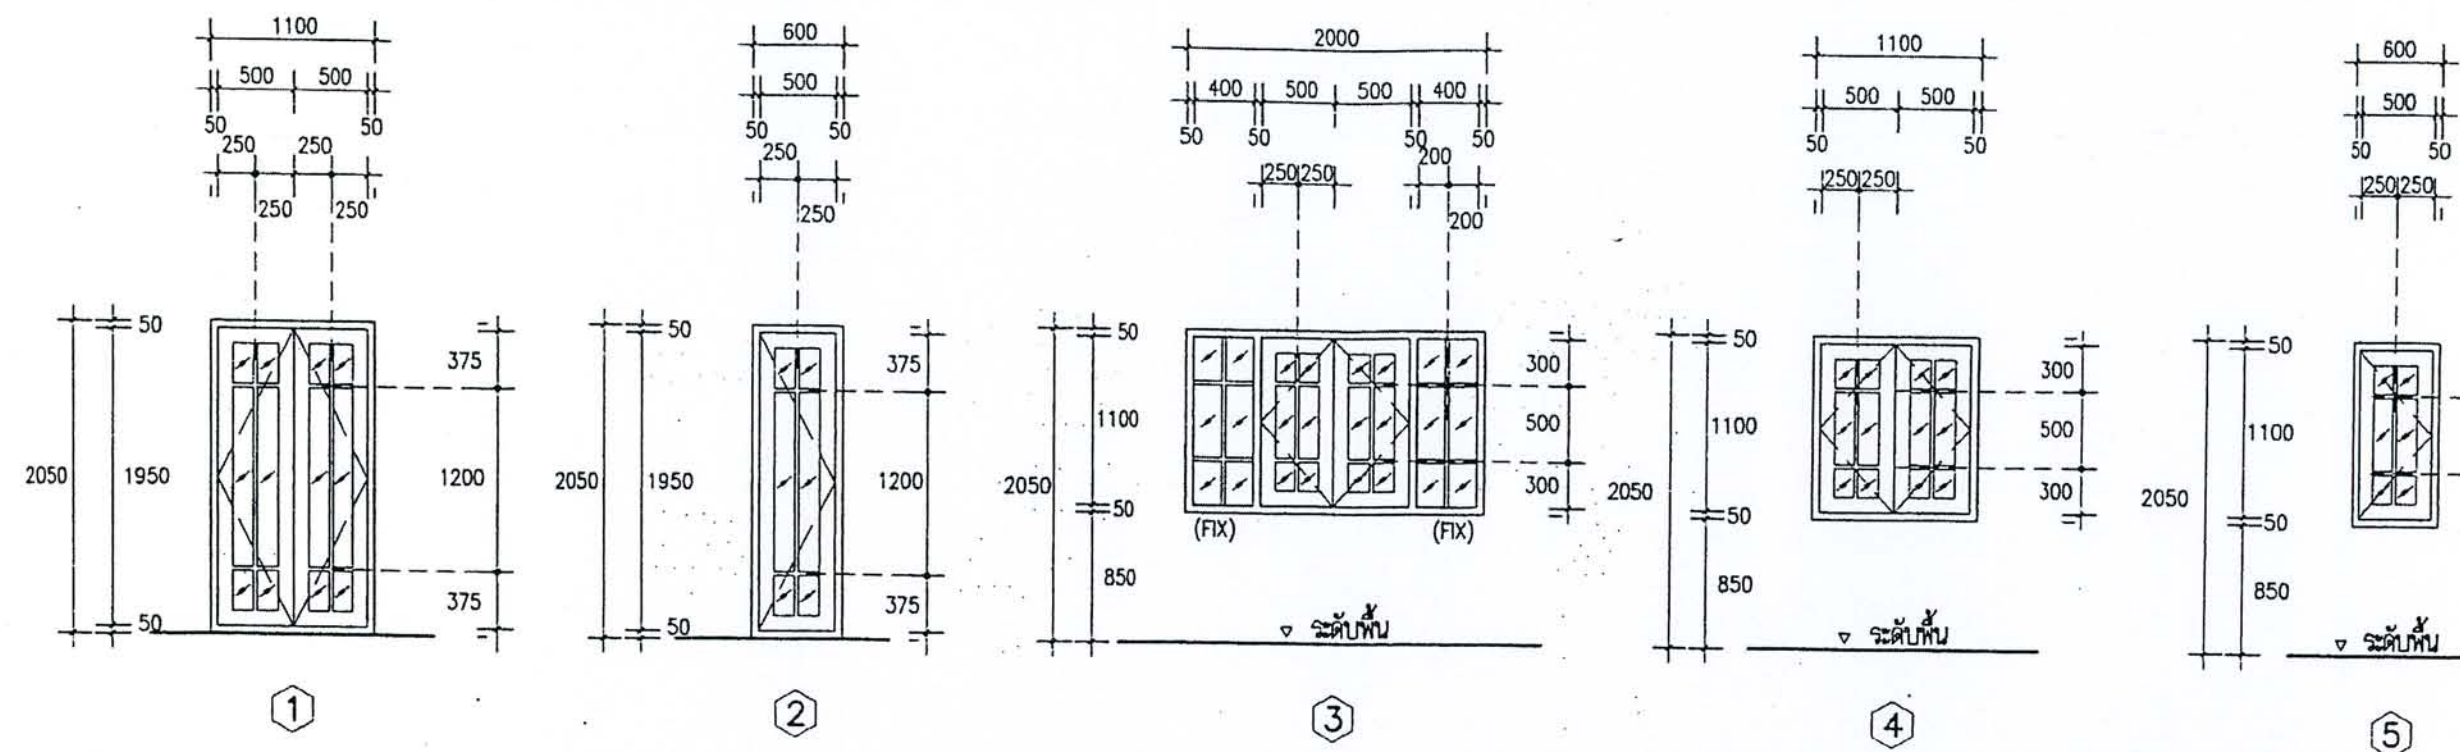

แบบขยายหน้าต่าง
มาตราส่วน 1 : 50


ได้รับความอนุเคราะห์แบบ
จาก
บริษัท แลนด์ โฮม
(ประเทศไทย) จำกัด



โครงการ
แบบบ้านยืมเพื่อประชาชน

ตามนโยบาย
ม.ร.ว. สุขุมพันธุ์ บริพัตร
ผู้ว่าราชการกรุงเทพมหานคร

โดยสำนักงานโยธา
กรุงเทพมหานคร

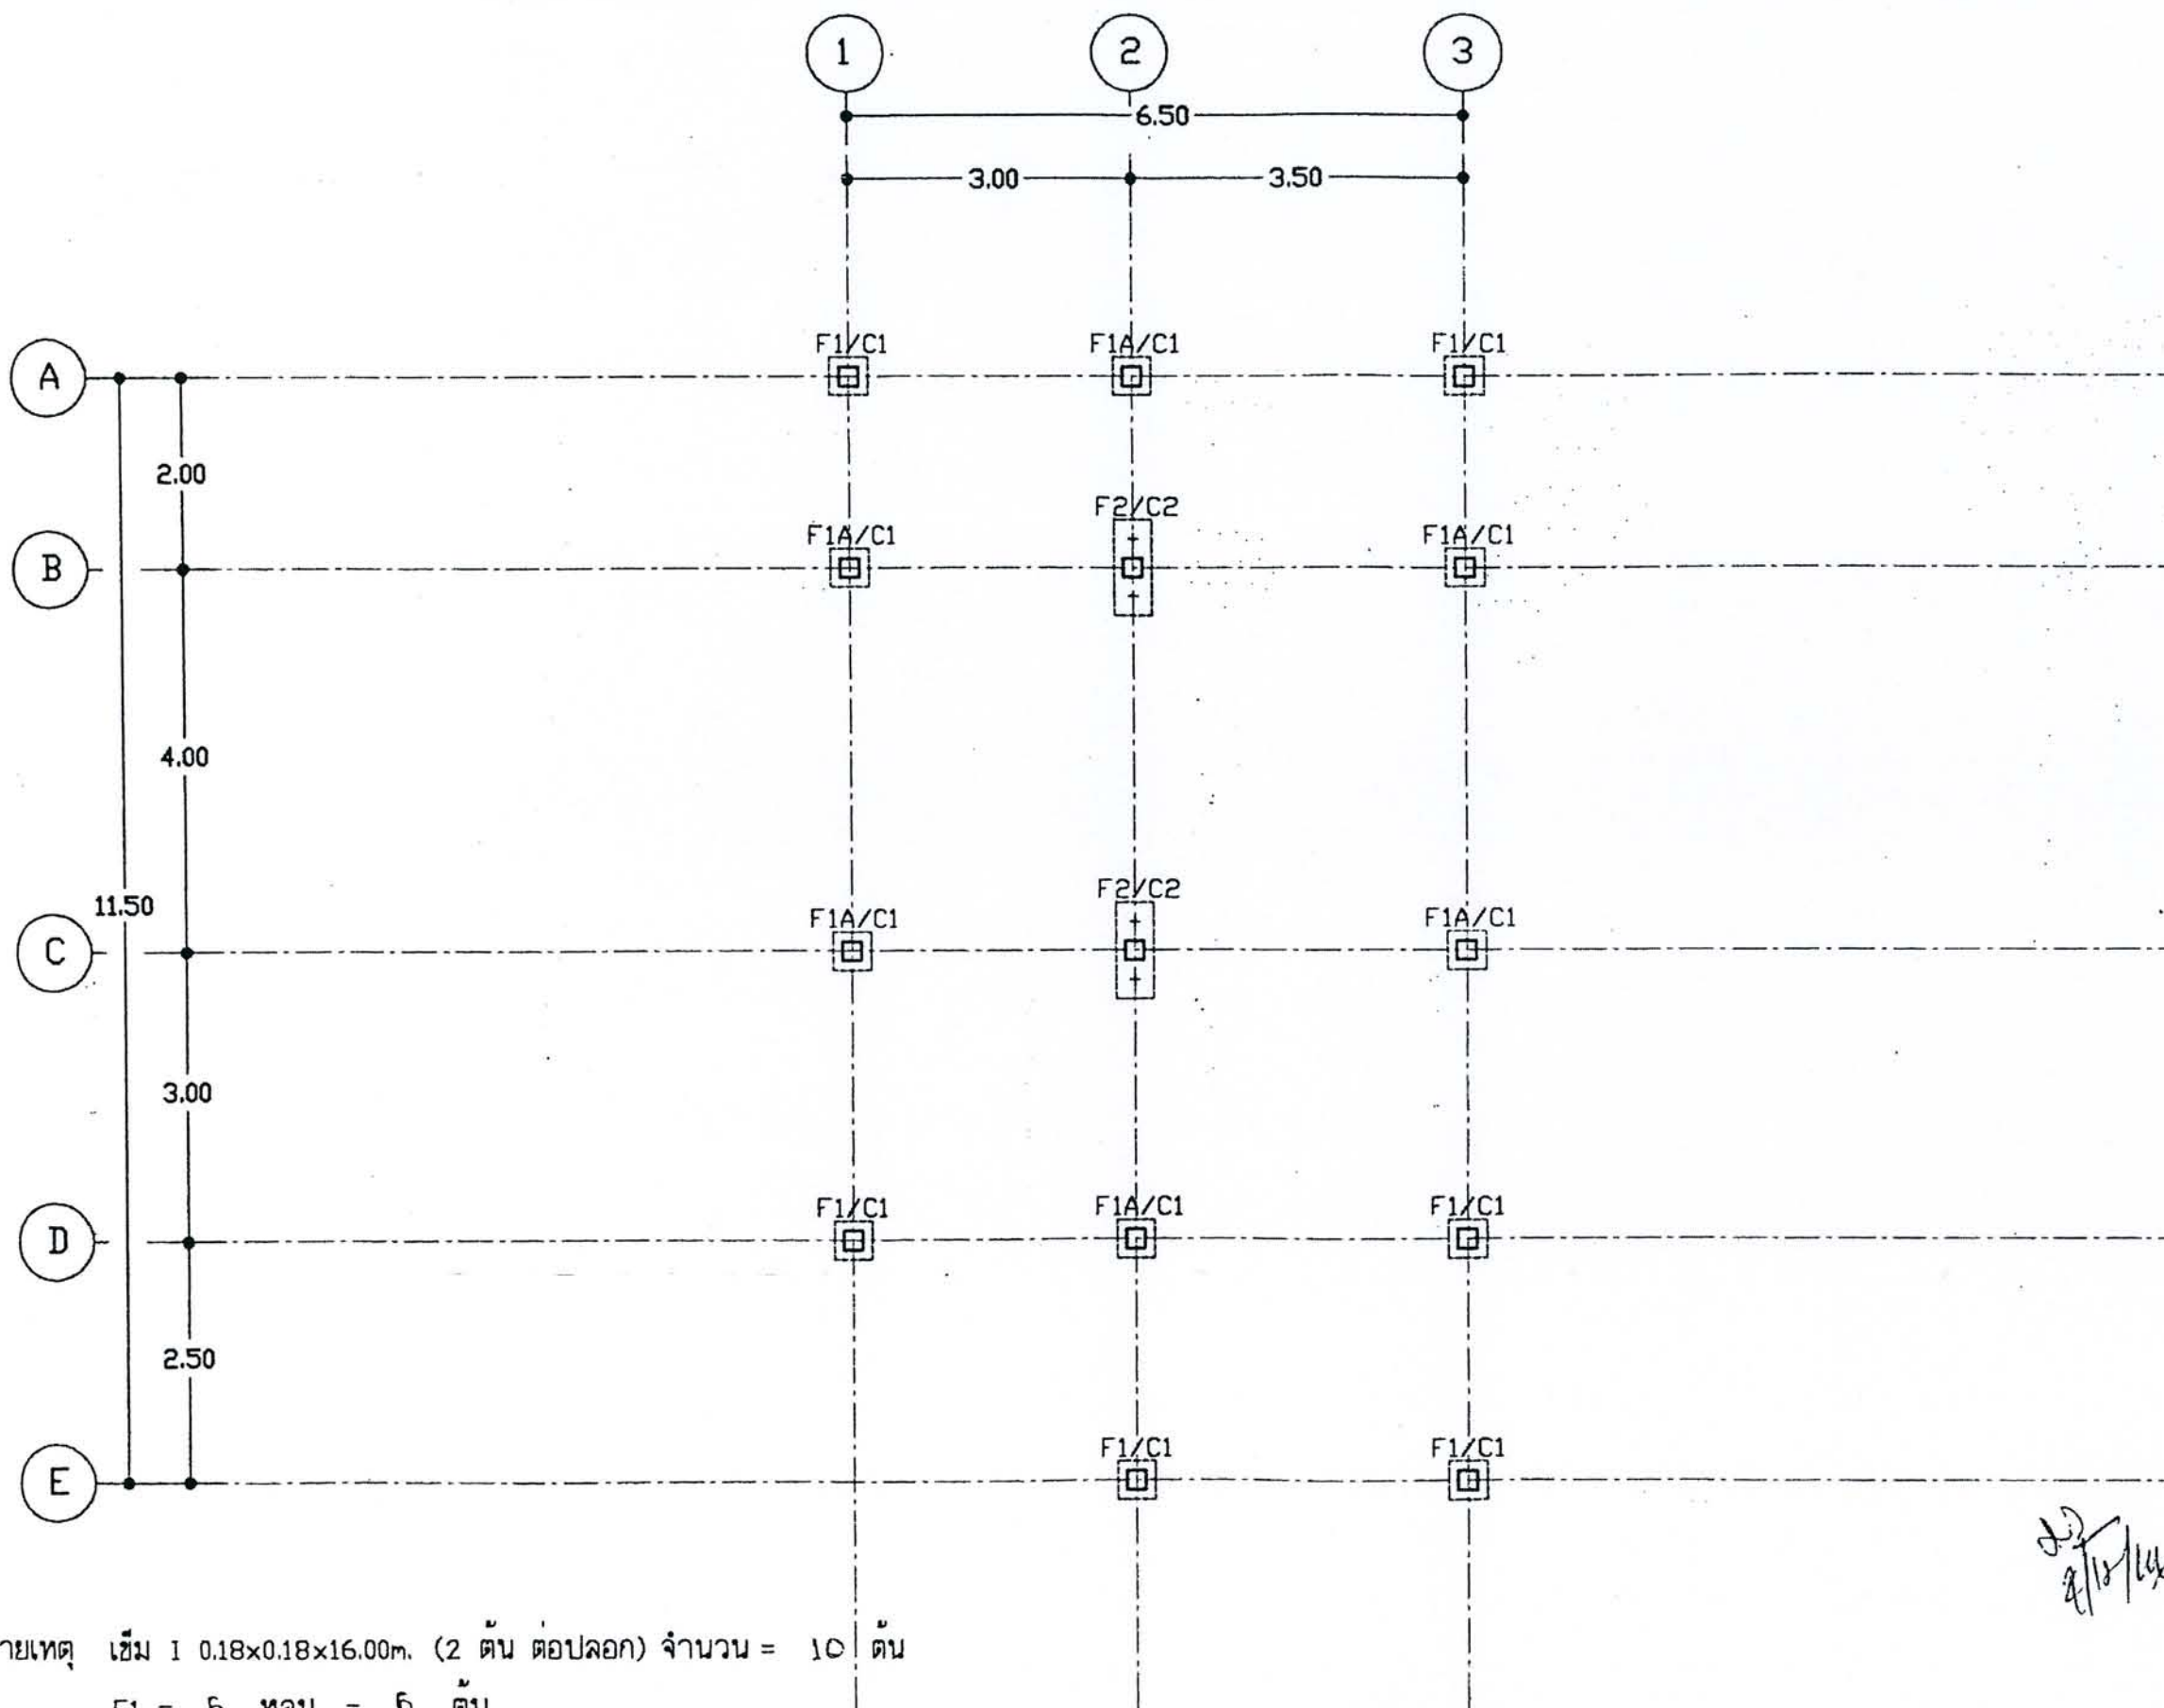

หมายเหตุ เข็ม I 0.18x0.18x16.00m. (2 ต้น ต่อปลอก) จำนวน = 10 ต้น

F1 = 6 หลุม = 6 ต้น


F2 = 2 หลุม = 4 ต้น

เข็ม I 0.22x0.22x16.00m. (2 ต้น ต่อปลอก) F1A = 6 หลุม = 6 ต้น

ผังโครงสร้างฐานราก
มาตราส่วน 1:75

run 2011/11/11


ได้รับความอนุเคราะห์แบบ
จาก
บริษัท แลนด์ โสม
(ประเทศไทย) จำกัด

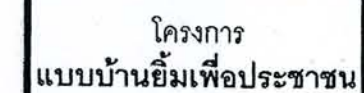

ตามนโยบาย
ม.ร.ว. สุขุมพันธุ์ บริพัตร
ผู้ว่าราชการกรุงเทพมหานคร

โดยสำนักงานนโยบาย
กรุงเทพมหานคร

ได้รับความอนุเคราะห์แบบ
จาก
บริษัท แลนด์ โฮม
(ประเทศไทย) จำกัด

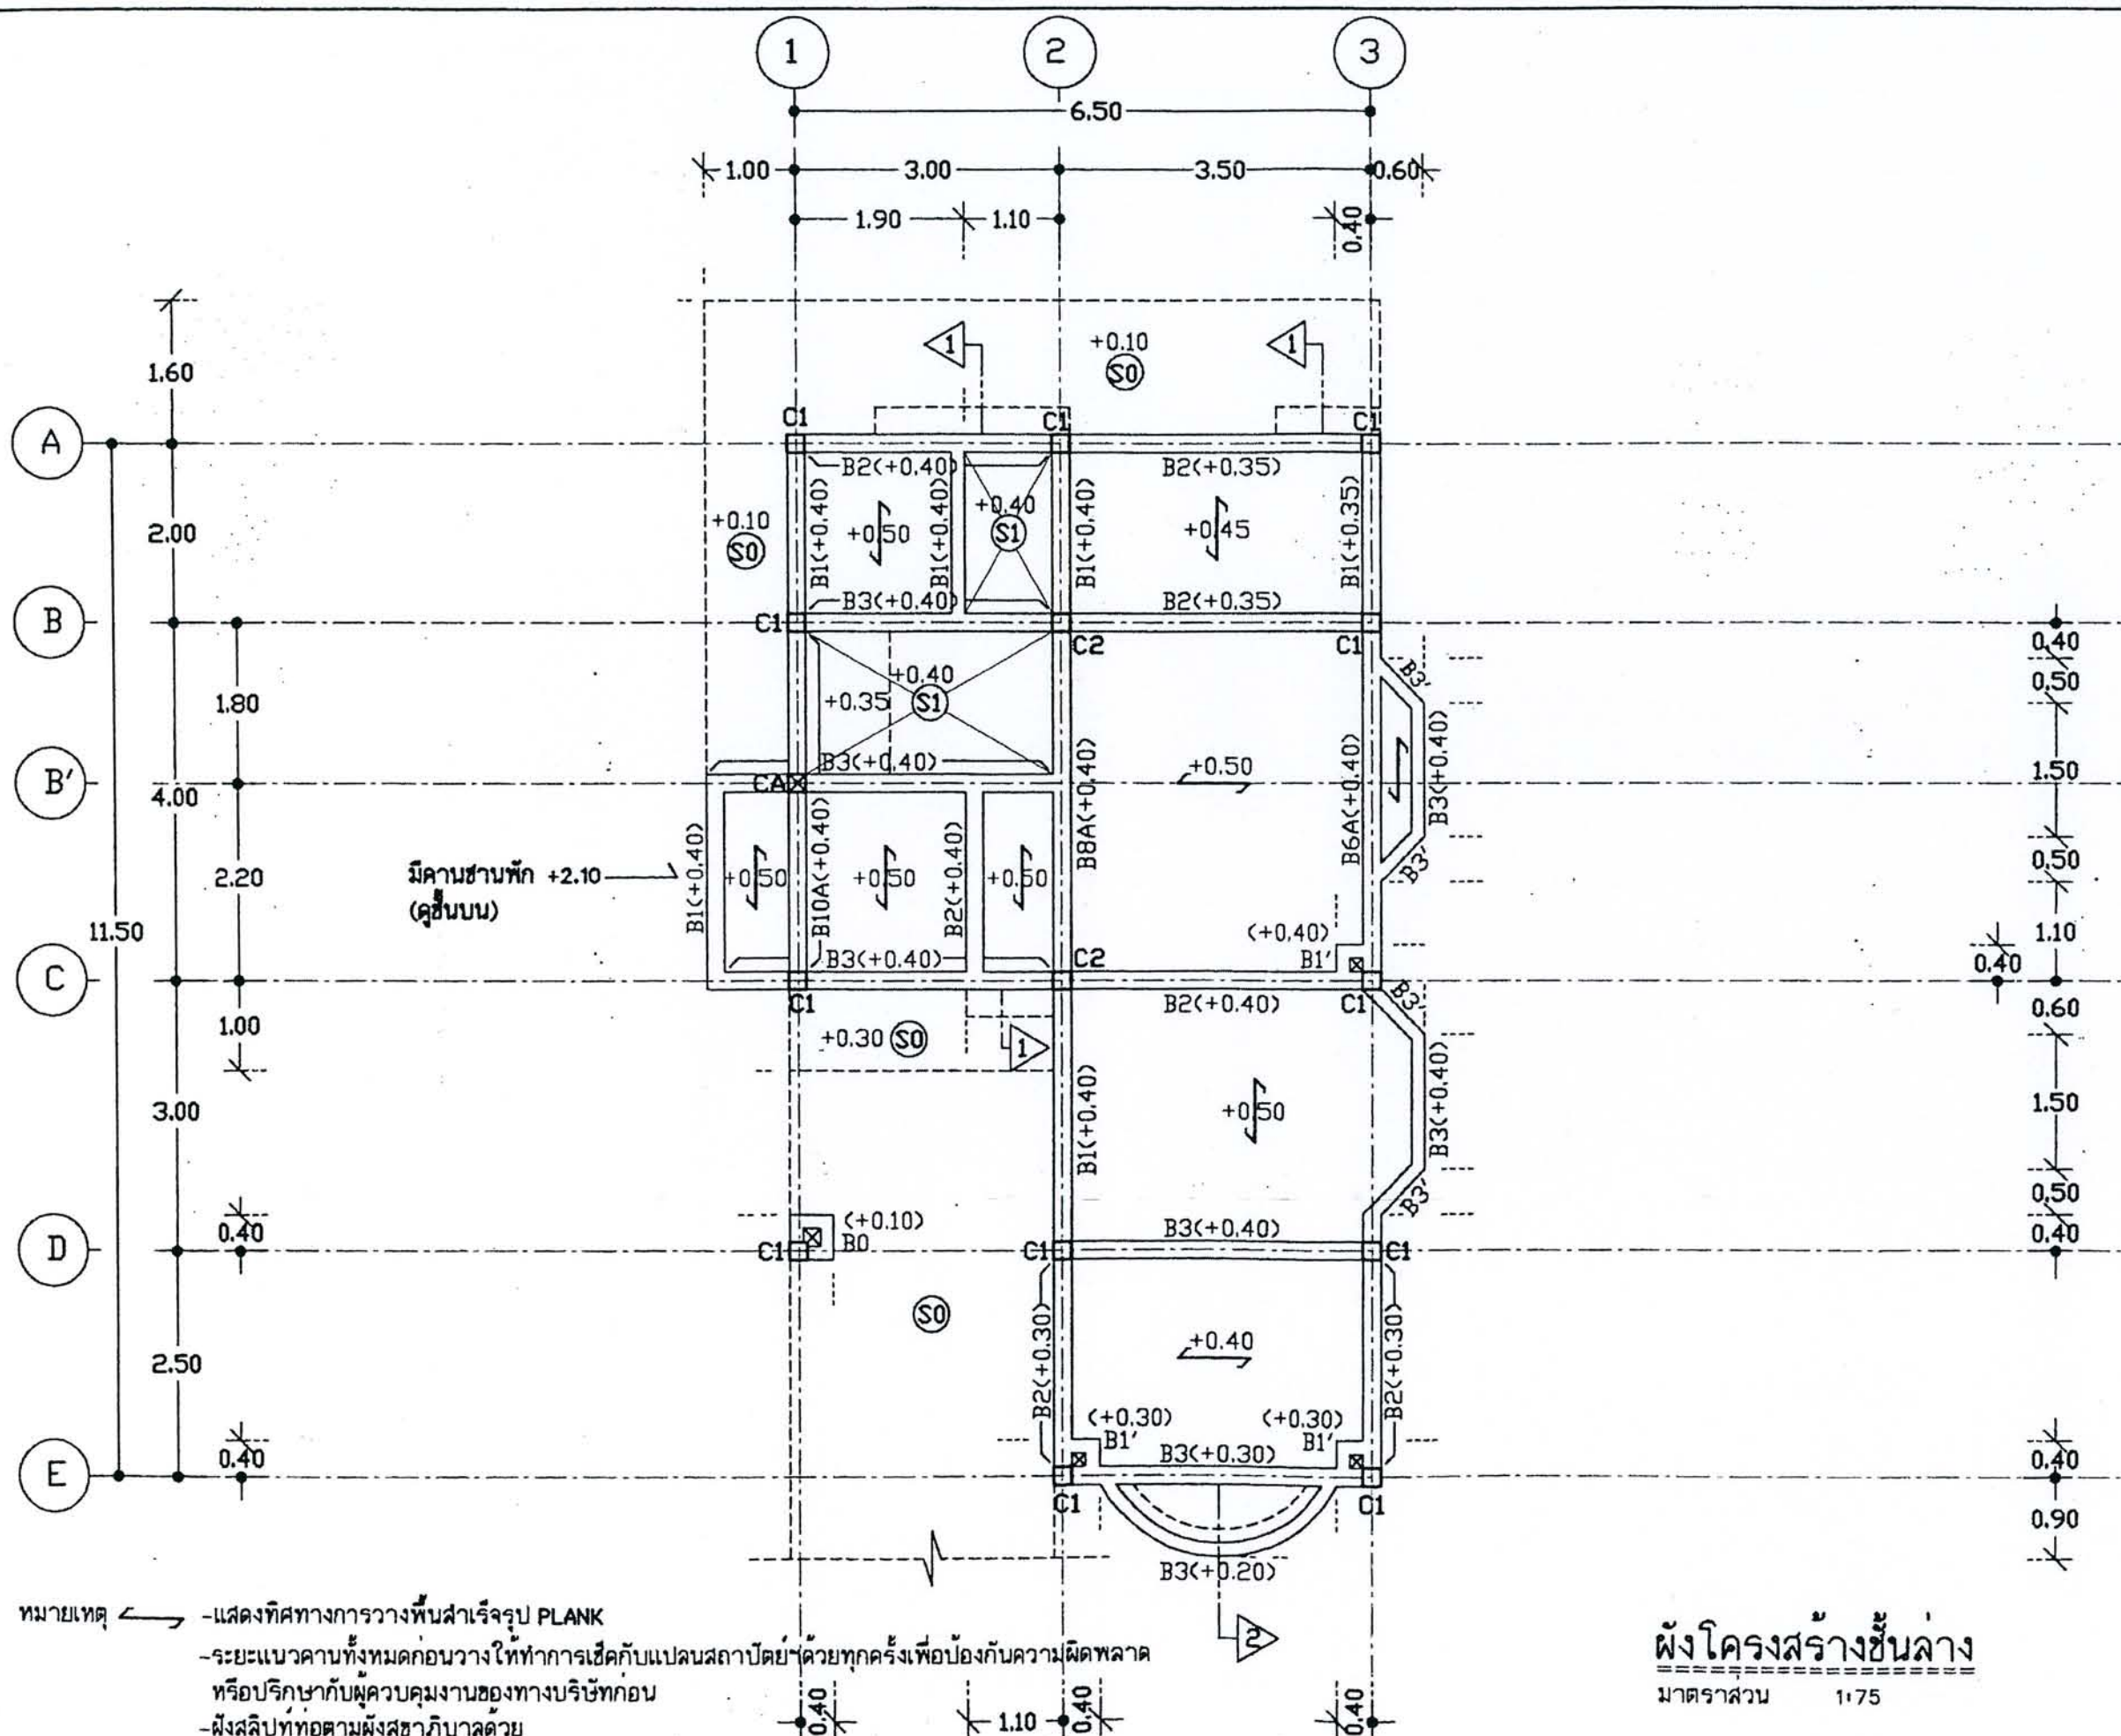

หมายเหตุ $\leftarrow$ -แสดงทิศทางการวางพื้นสำเร็จรูป PLANK
 -ระยะแนวคานทั้งหมดก่อนวางให้ทำการเช็ดกับแปลนสถาปัตย์ด้วยทุกครั้งเพื่อป้องกันความผิดพลาด
 หรือปรึกษากับผู้ควบคุมงานของทางบริษัทก่อน
 -ฝังสลีปทอทตามผังสุขาภิบาลด้วย
 ☒ -เสา CA เสริมพิเศษบนคาน

ผังโครงสร้างชั้นล่าง
มาตราส่วน 1:75




โครงการ
แบบบ้านยืมเพื่อประชาชน

ตามนโยบาย
ม.ร.ว. สุขุมพันธุ์ บริพัตร
ผู้ว่าราชการกรุงเทพมหานคร

โดยสำนักการโยธา
กรุงเทพมหานคร

ได้รับความอนุเคราะห์แบบ
จาก
บริษัท แลนด์ โสม
(ประเทศไทย) จำกัด

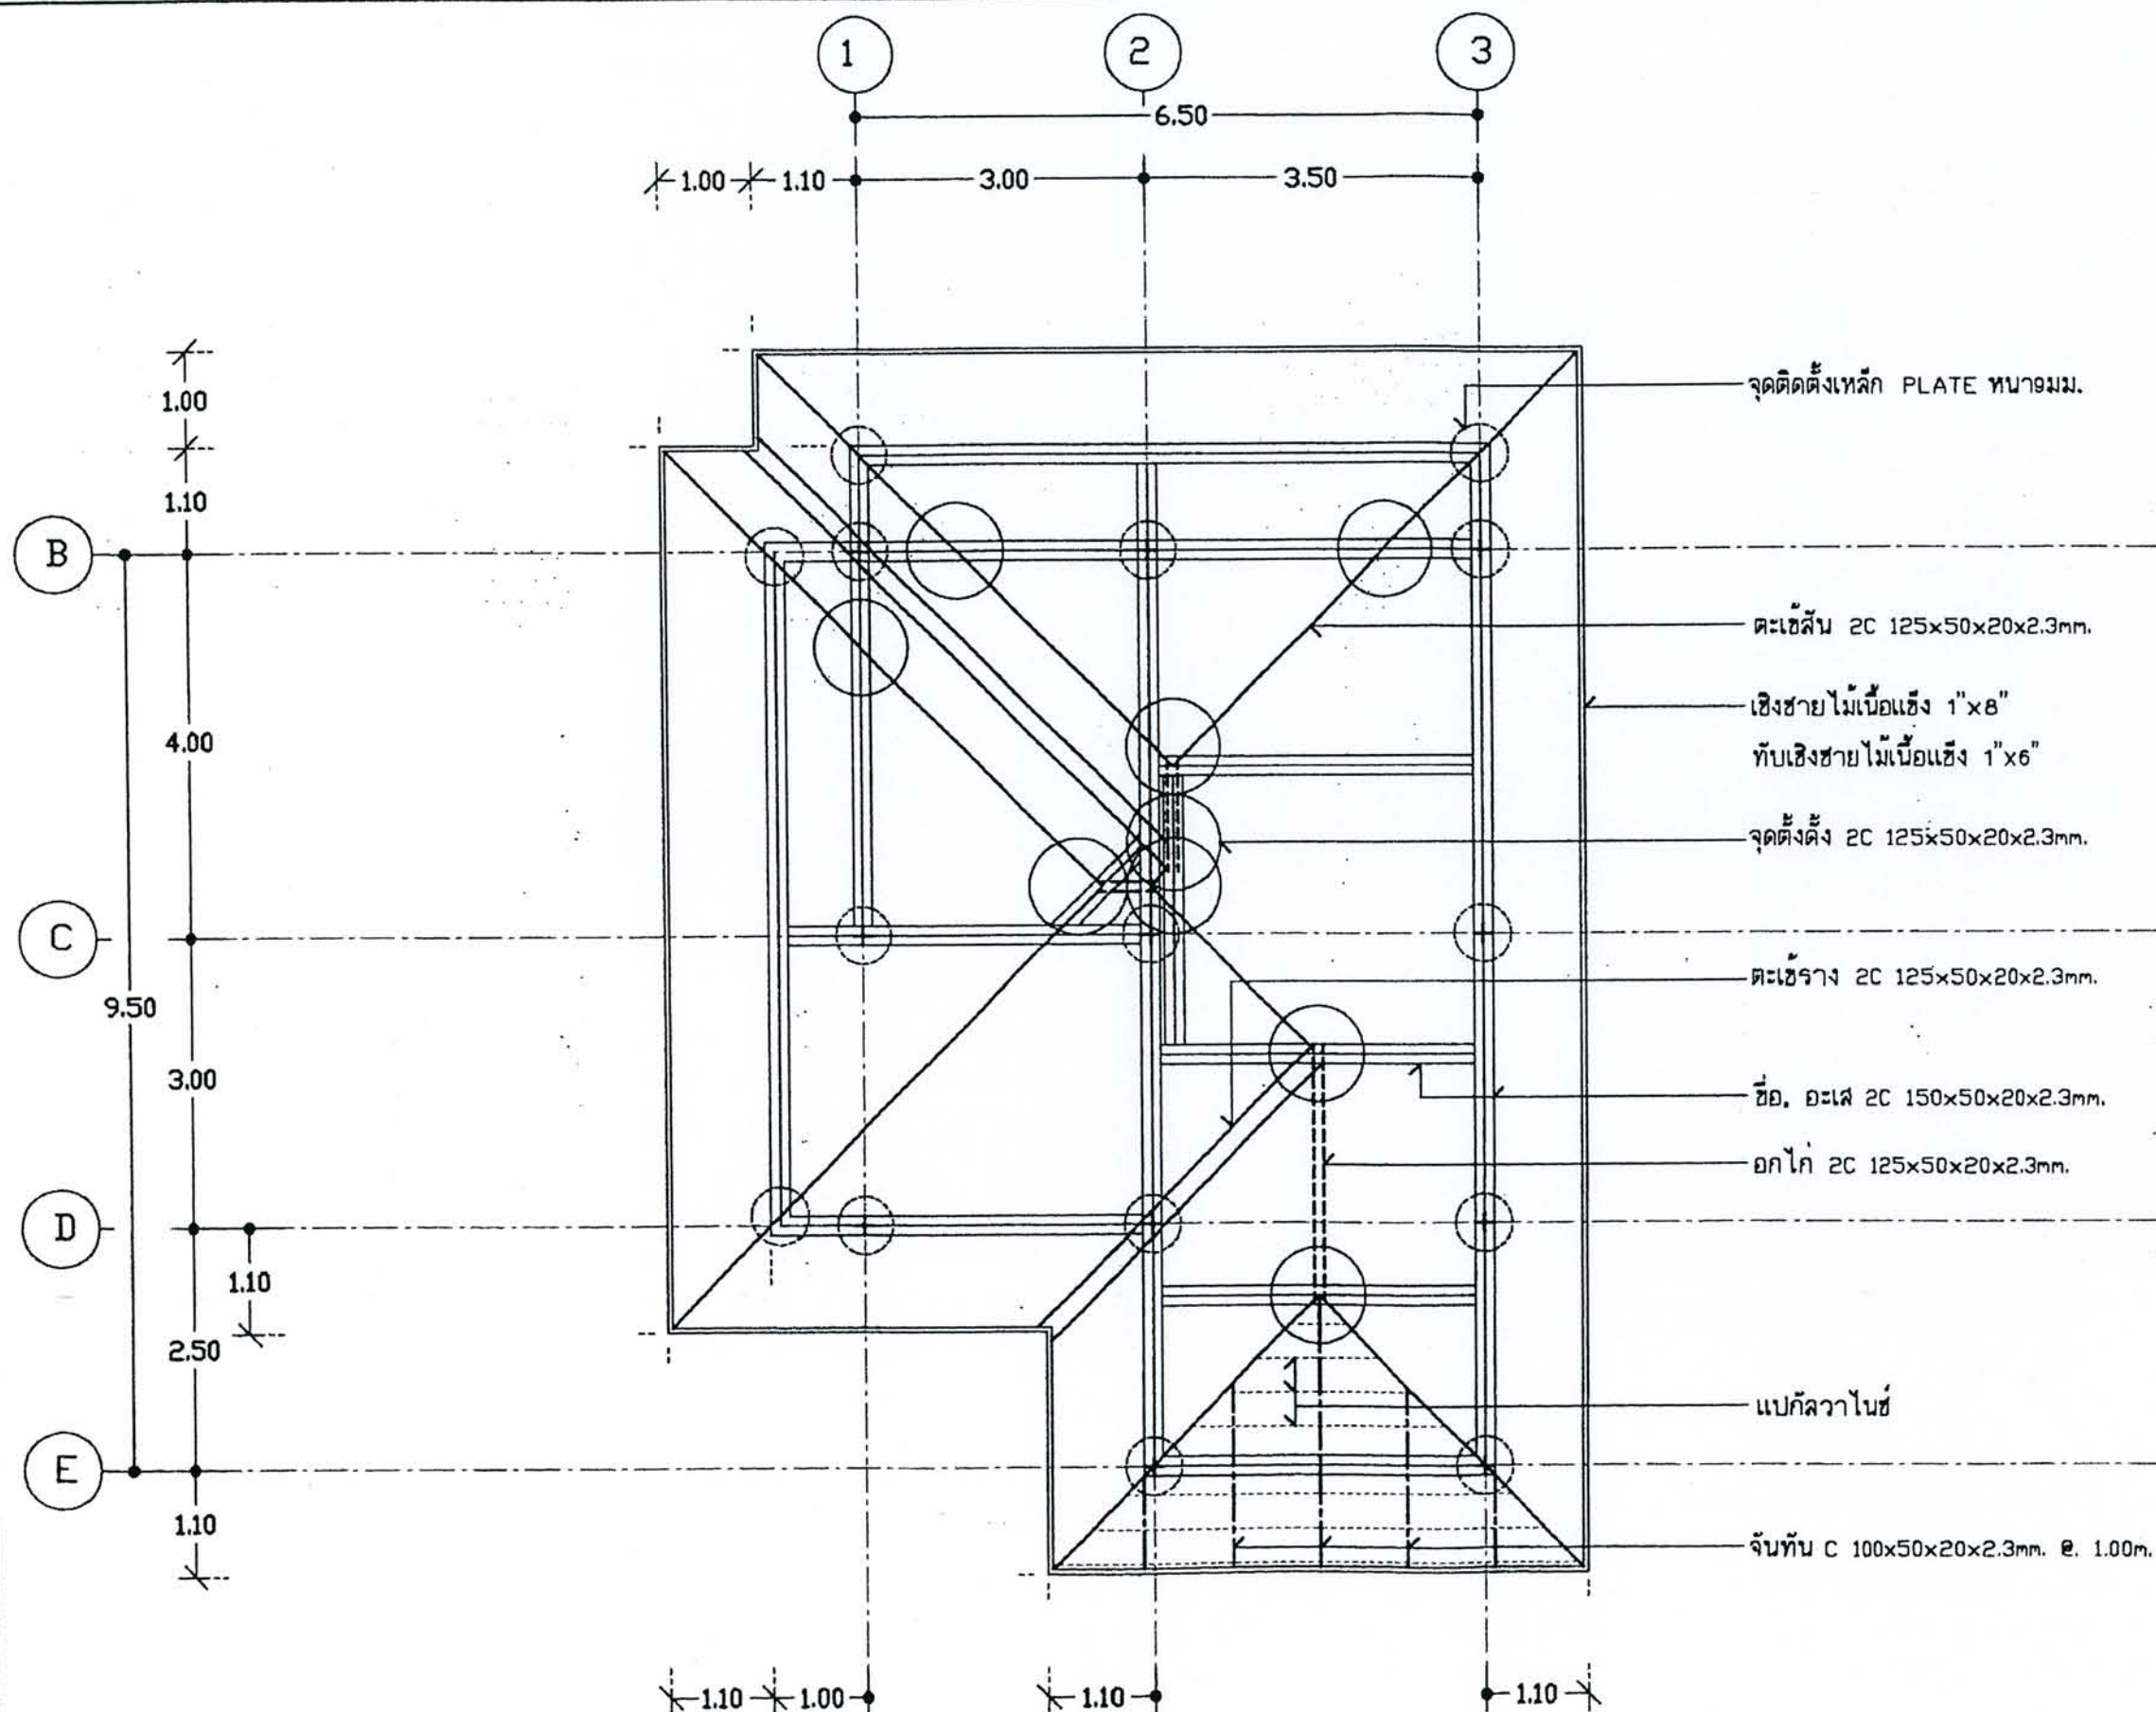

ผังโครงสร้างหลังคา
มาตราส่วน 1:75


FOR CONSTRUCTION




โครงการ
แบบบ้านยืมเพื่อประชาชน

ตามนโยบาย
ม.ร.ว. สุขุมพันธุ์ บริพัตร
ผู้ว่าราชการกรุงเทพมหานคร


โดยสำนักงานโยธา
กรุงเทพมหานคร

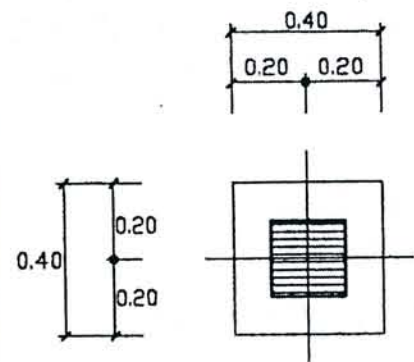


PLAN F1A

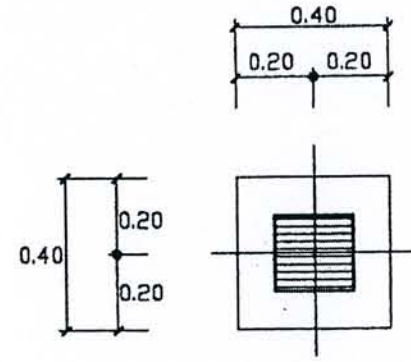


PLAN F1

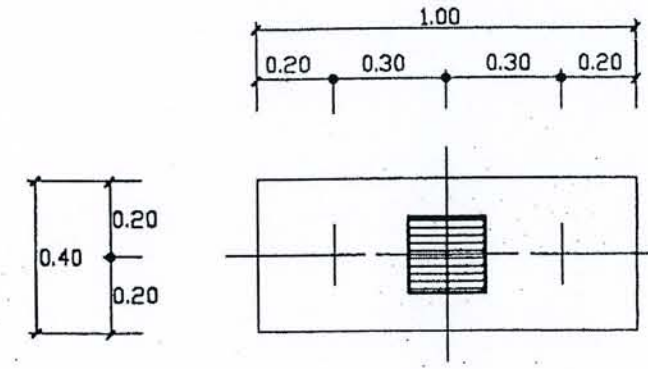


PLAN F2

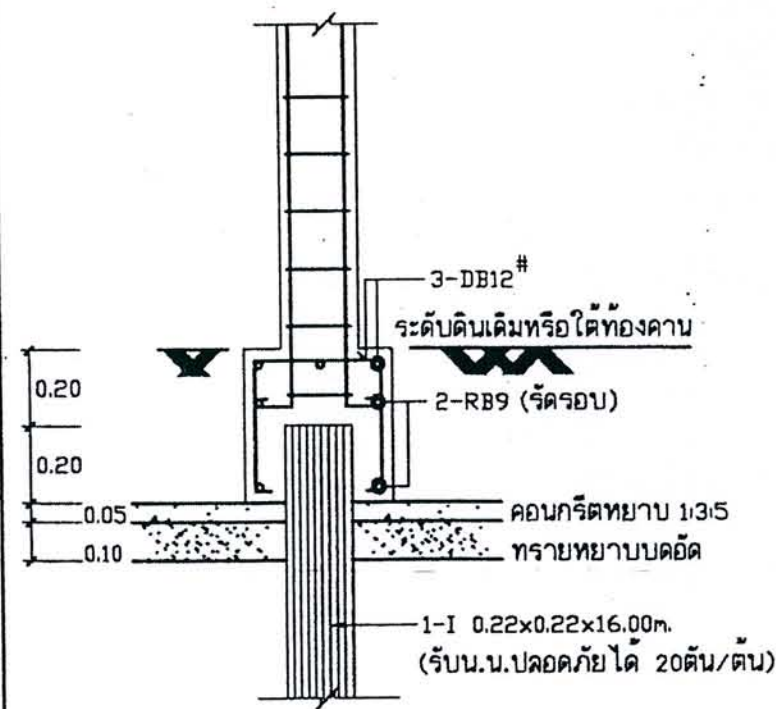

SECTION F1A 1:20

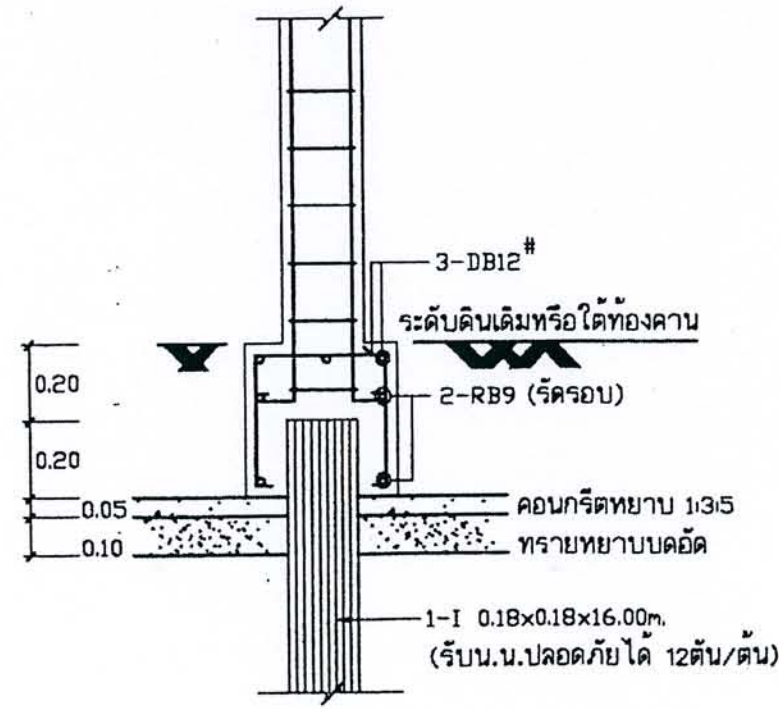

SECTION F1 1:20

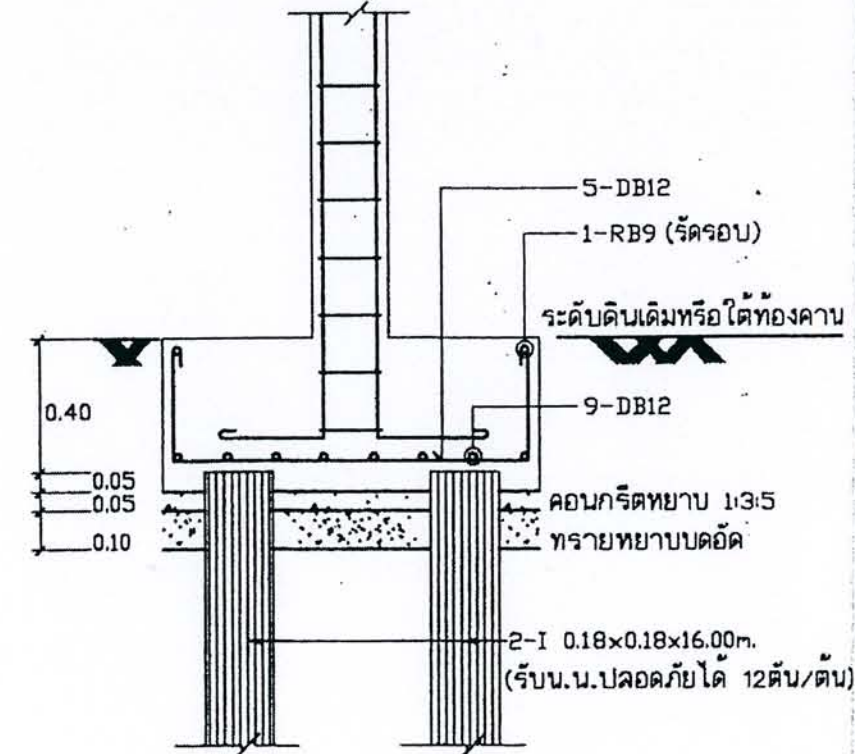

SECTION F2 1:20

ได้รับความอนุเคราะห์แบบ
จาก
บริษัท แลนด์ โสม
(ประเทศไทย) จำกัด




โครงการ
แบบบ้านยืมเพื่อประชาชน

ตามนโยบาย
ม.ร.ว. สุขุมพันธุ์ บริพัตร
ผู้ว่าราชการกรุงเทพมหานคร

โดยสำนักงานโยธา
กรุงเทพมหานคร

FLOOR 2	 4-DB12 150 RB6@0.15	 4-DB12 150 RB6@0.15	 4-DB12 150 RB6@0.15
FLOOR 1	 4-DB12 200 RB6@0.15	 4-DB16 200 RB6@0.15	 4-DB12 150 RB6@0.15
FOOTING	 4-DB12 200 RB6@0.15	 4-DB12 200 RB6@0.15	
	C1	C2	CA

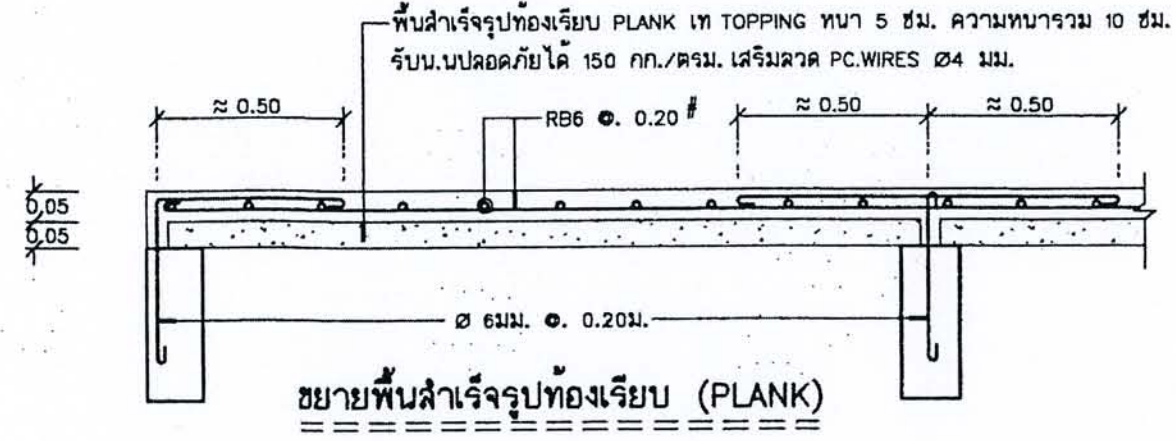

ตารางแสดงการรับน้ำหนักจร (LIVE LOAD)													
สำหรับพื้นสำเร็จรูปแบบท้องเรียบ PLANK ขนาดหน้าตัด 0.05x0.35 ม.													
N \ S	2.80	3.00	3.20	3.40	3.60	3.80	4.00	4.20	4.40	4.60	4.80	5.00	
4	504												
5		532	464	400	350	300							
6							318	274					
7									305	300			
8											300	250	

หมายเหตุ - มีค้ำยันชั่วคราว
- S = ระยะช่วงพาดวัดขอบในถึงขอบในของคาน (CLEAR SPAN) หน่วยเป็นเมตร
- N = จำนวนลวดยึดแรง ขนาด Ø 4 มม.
- ตัวเลขในตารางแสดงความสามารถในการรับน้ำหนักจรทุกพลอยหน่วยเป็น กก./ตารางเมตร


SECTION COLUMN 1:20




โครงการ
แบบบ้านยืมเพื่อประชาชน

ตามนโยบาย
ม.ร.ว. สุขุมพันธุ์ บริพัตร
ผู้ว่าราชการกรุงเทพมหานคร

โดยสำนักงานโยธา
กรุงเทพมหานคร

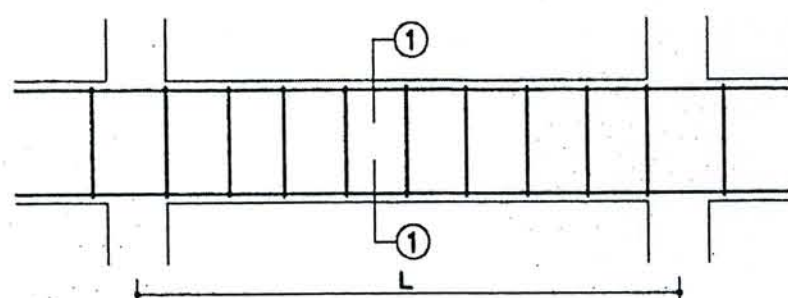


LONG SECTION

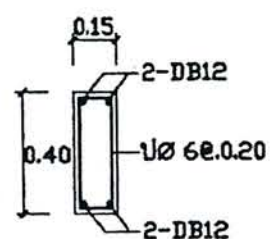


SECTION 1-1

B1

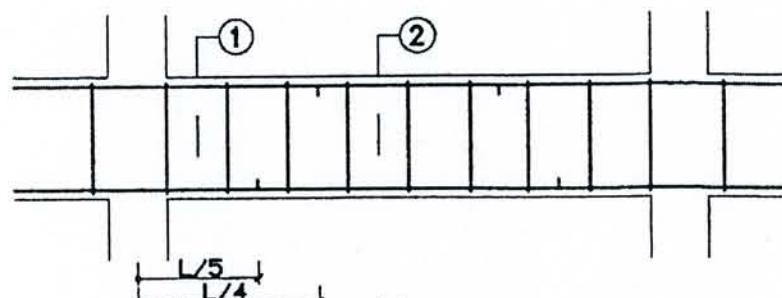


LONG SECTION

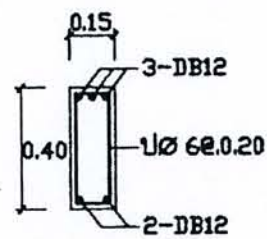


SECTION 1-1

B2

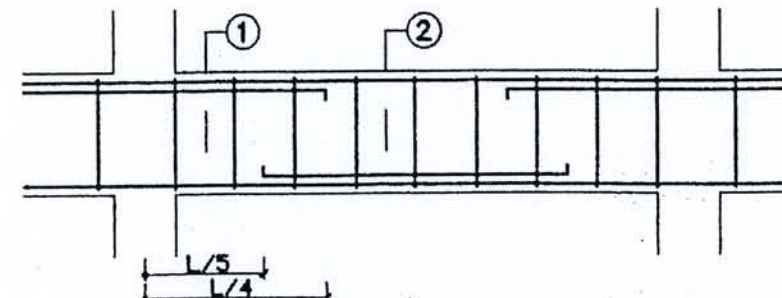


LONG SECTION

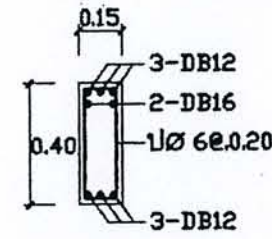


SECTION 1-1


B5

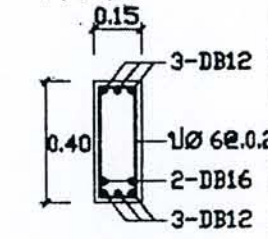

SECTION 2-2

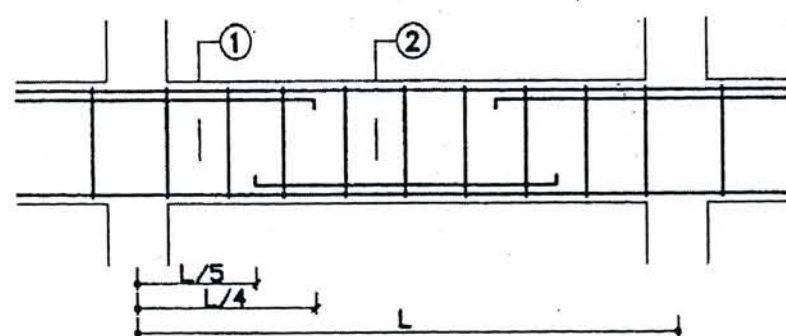


LONG SECTION

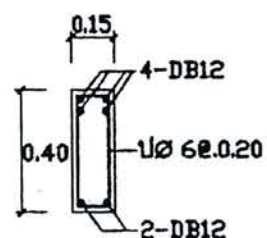


SECTION 1-1


B3

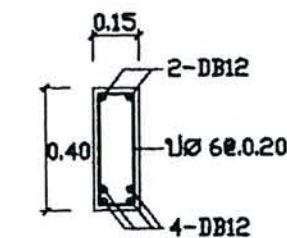

SECTION 2-2

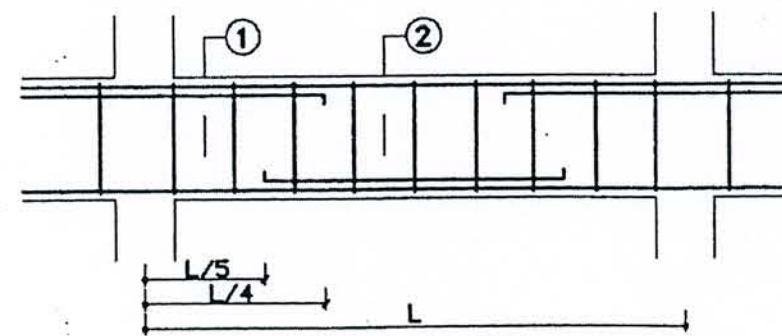


LONG SECTION

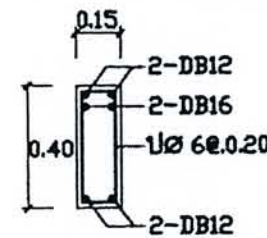


SECTION 1-1


B4

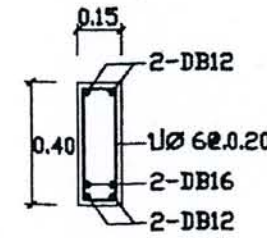

SECTION 2-2

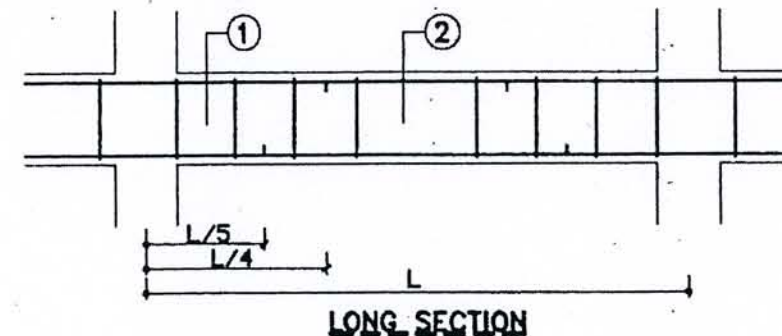


LONG SECTION

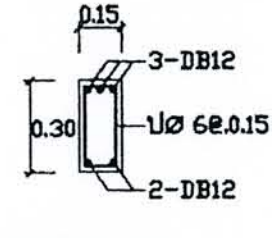

SECTION 1-1



RB2

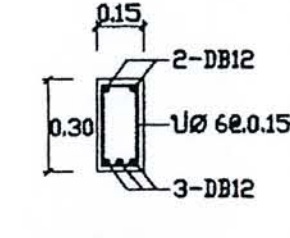




SECTION 2-2

ได้รับความอนุเคราะห์แบบ
จาก
บริษัท แลนด์ โชม
(ประเทศไทย) จำกัด



FOR CONSTRUCTION

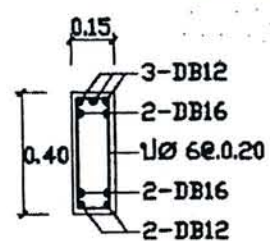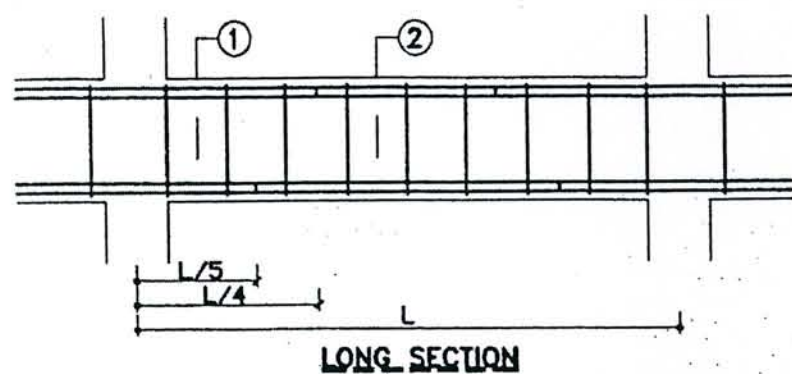



B6

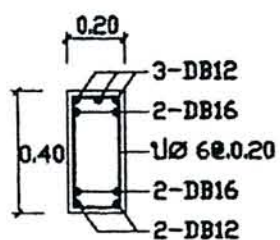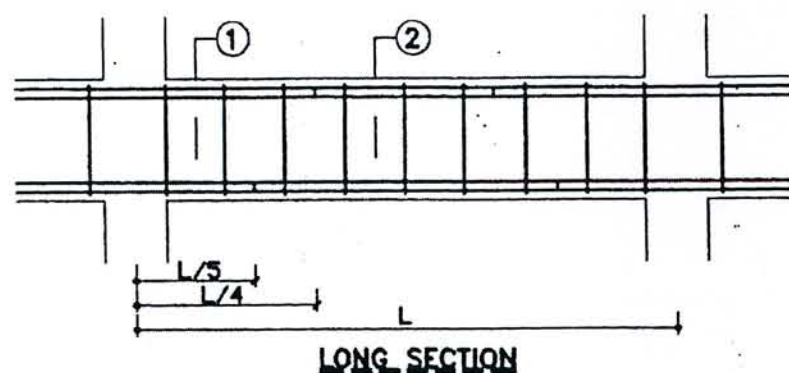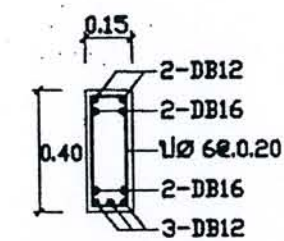



B6A

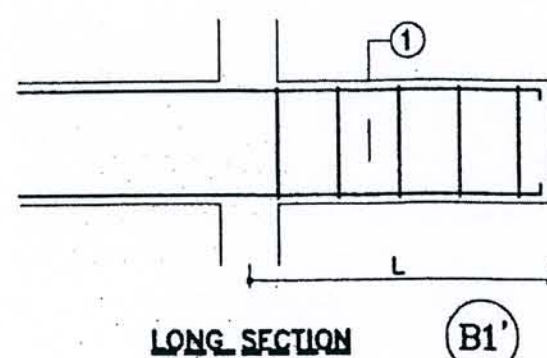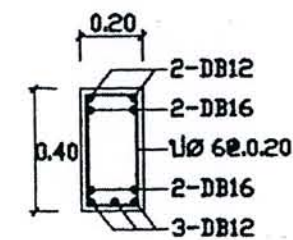



B1'

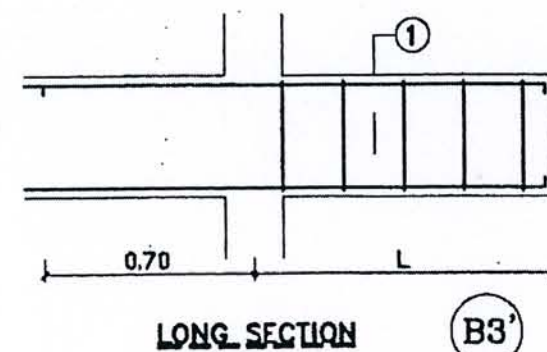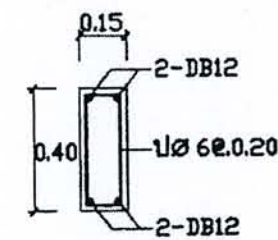


B3'

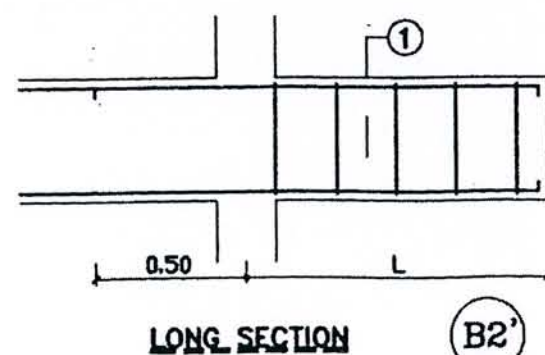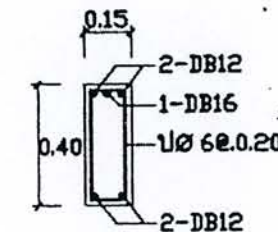


B2'

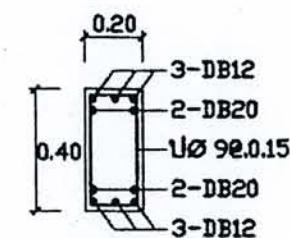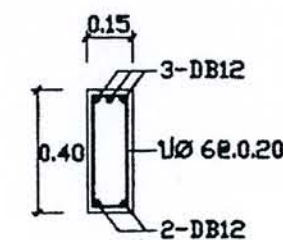

B8A

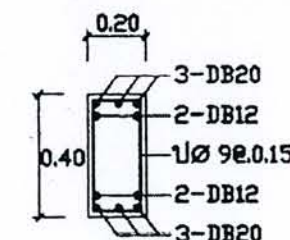

B10A

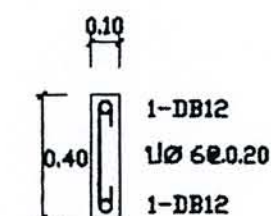

B0



โครงการ
แบบบ้านยืมเพื่อประชาชน

ตามนโยบาย
ม.ร.ว. สุขุมพันธุ์ บริพัตร
ผู้ว่าราชการกรุงเทพมหานคร

โดยสำนักการโยธา
กรุงเทพมหานคร

ได้รับความอนุเคราะห์แบบ
จาก
บริษัท แลนด์ โฮม
(ประเทศไทย) จำกัด


FOR CONSTRUCTION




โครงการ
แบบบ้านยืมเพื่อประชาชน

ตามนโยบาย
ม.ร.ว. สุขุมพันธุ์ บริพัตร
ผู้ว่าราชการกรุงเทพมหานคร


โดยสำนักการโยธา
กรุงเทพมหานคร

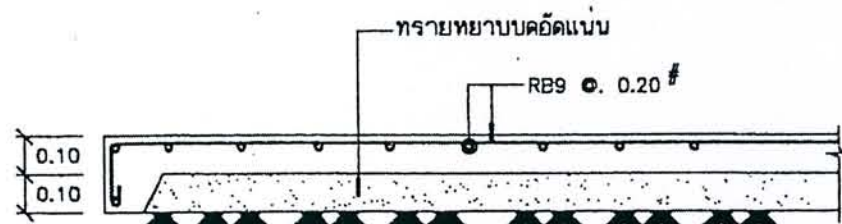


S0

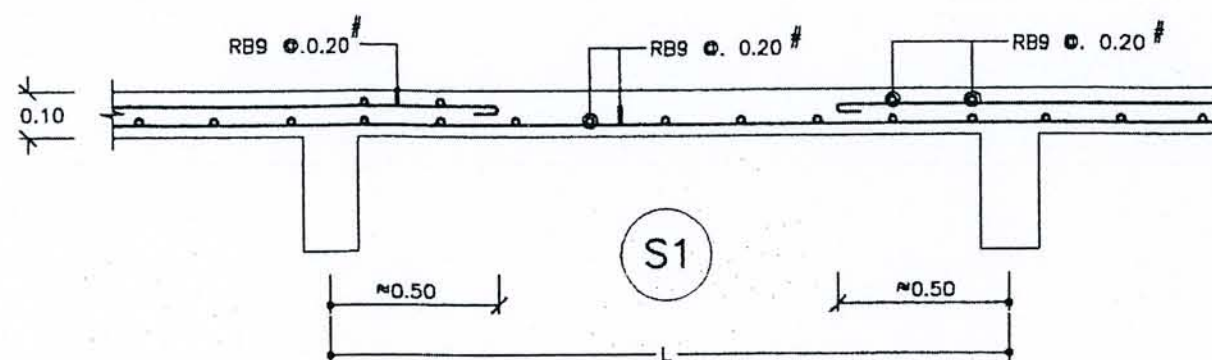


S1

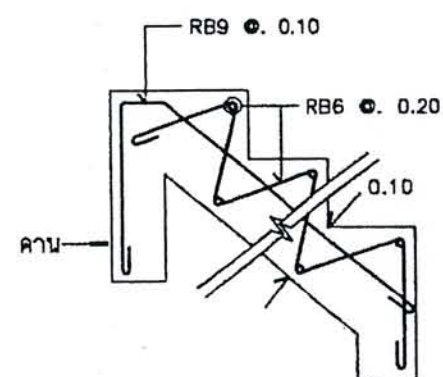


SECTION - 1
(ตามแบบโครงสร้างชั้นล่าง)

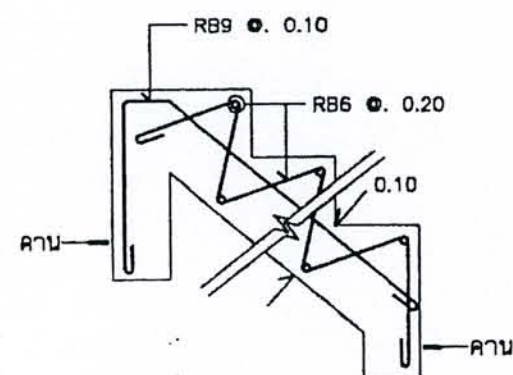


SECTION - 2
(ตามแบบโครงสร้างชั้นล่าง)

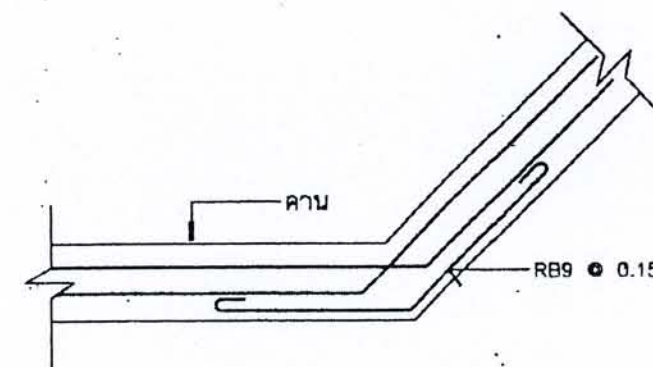


(แสดงการเดินเหล็กคานช่วงมุม)

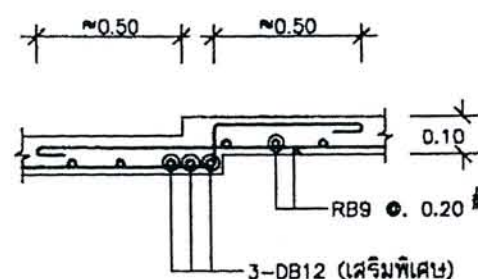

ขยายพื้นลดระดับ

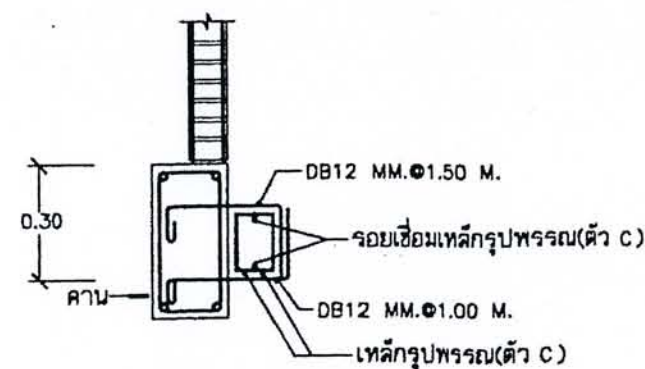


แบบขยายจุดที่มีหลังคาครอบวางติดผนัง

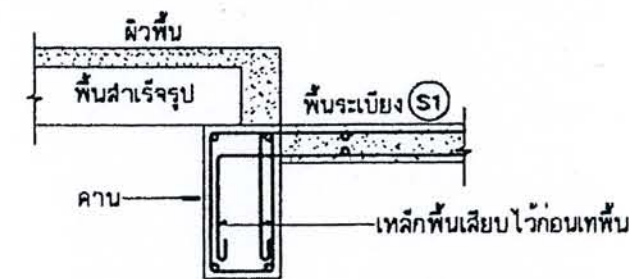


แบบขยายรอยต่อพื้นที่กับระเบียง

ได้รับความอนุเคราะห์แบบ
จาก
บริษัท แลนด์ โฮม
(ประเทศไทย) จำกัด

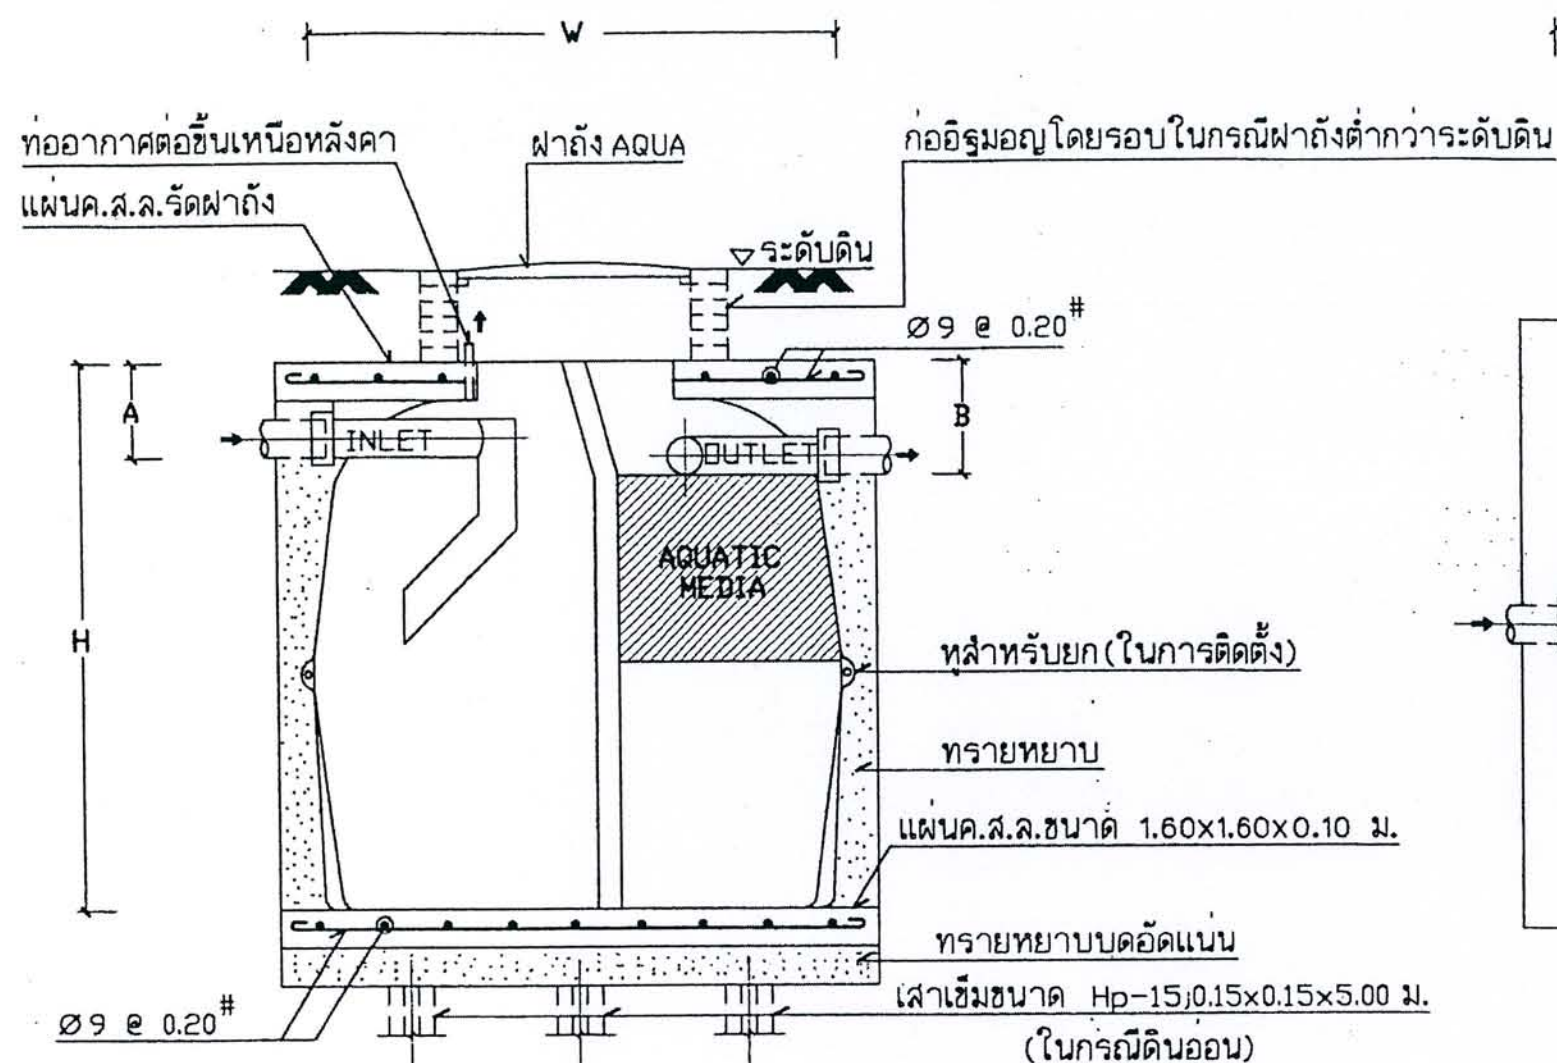

SECTION 1:20

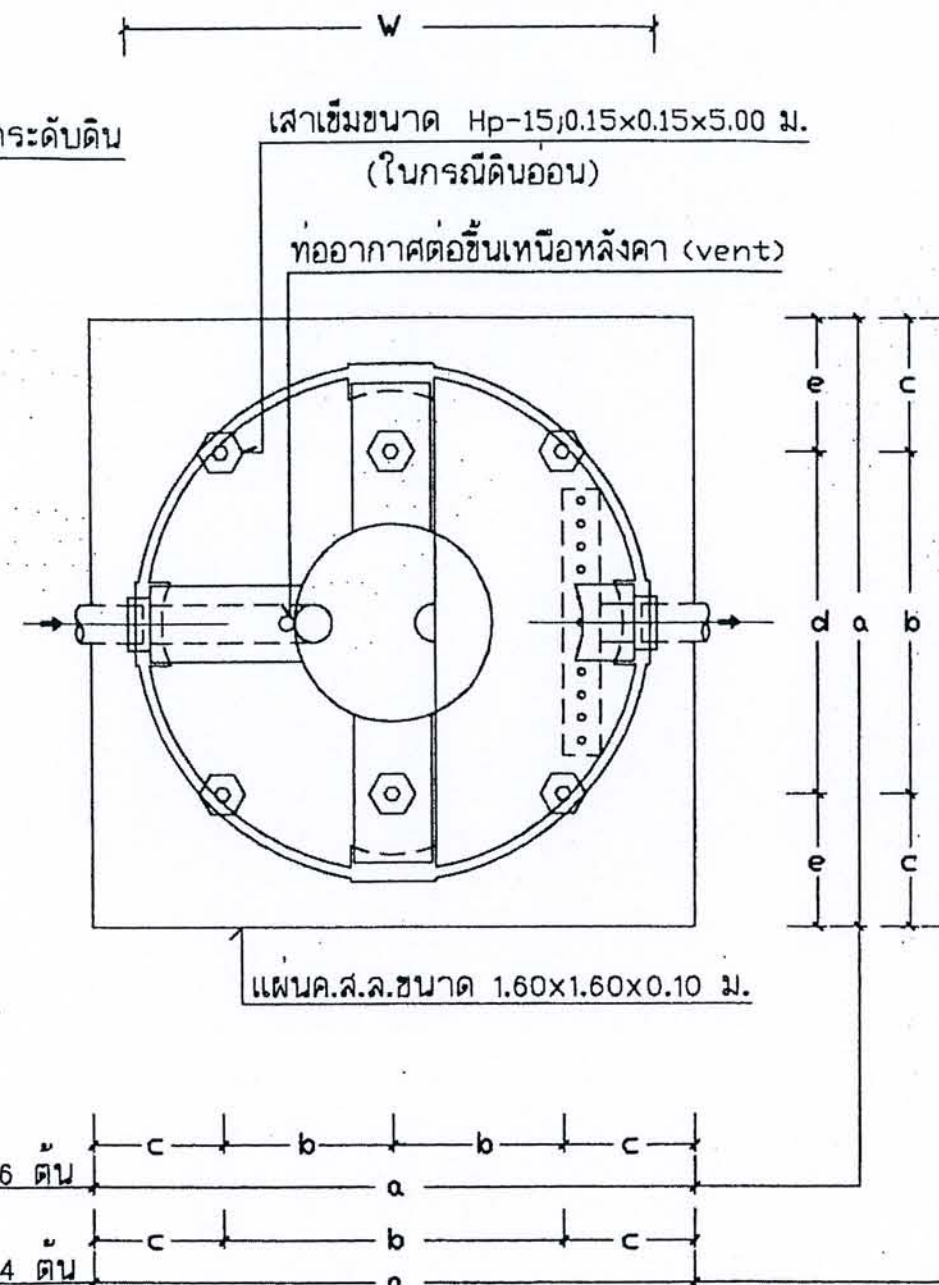

PLAN 1:20

ตาราง แสดงขนาดของถังรวม (ส่วนกระโหลก+ส่วนกรอง) ในรุ่นต่างๆ (มม.)

MODEL	H	W	A	B	INLET	OUTLET	VENT	a	b	c	d	e
AP-1200	1700	1200	250	300	100	100	50	1400	700	350	-	-
AP-1800	1590	1450	250	300	100	100	50	1650	850	400	-	-
AP-2000	1750	1500	250	300	100	100	50	1700	850	425	-	-
AP-3000	1900	1700	250	300	100	100	50	1900	700	250	900	500
AP-4000	1930	1890	250	300	100	100	50	2090	750	295	1090	500
AP-6000	2300	1970	250	300	100	100	50	2170	750	335	1010	580
AP-5000	2350	2100	300	350	150	150	50	2300	750	400	1200	550

หมายเหตุ การใช้เส้าเข็มกับขนาดถัง
ถึงรุ่น 1200 ถึงรุ่น 2000 ใช้เส้าเข็มจำนวน 4 ต้น
ถึงรุ่น 3000 ถึงรุ่น 6000 ใช้เส้าเข็มจำนวน 6 ต้น

AQUA-PAC



โครงการ
แบบบ้านยืมเพื่อประชาชน

ตามนโยบาย
ม.ร.ว. สุขุมพันธุ์ บริพัตร
ผู้ว่าราชการกรุงเทพมหานคร

โดยสำนักงานโยธา
กรุงเทพมหานคร

ได้รับความอนุเคราะห์แบบ
จาก
บริษัท แลนด์ โชม
(ประเทศไทย) จำกัด

FOR CONSTRUCTION