



ตามนโยบายของ
หม่อมราชวงศ์สุขุมพันธุ์ บริพัตร
ผู้ว่าราชการกรุงเทพมหานคร
โดย สำนักการโยธา



แบบบ้านยืม... เพื่อประชาชน

100 แบบบ้านมาตรฐาน...
สวย ดี โดนใจ...
พร้อมปลูกสร้างได้ทันที



ห้ามพลาด!!! โอกาส...
ยืมรับ... บ้านใหม่

พบ **บ้านสวย**

เลือกได้

ใน “โครงการแบบบ้านยืม...เพื่อประชาชน”

พบ 100 แบบบ้าน

มาตรฐาน...

สวย ดี โดนใจ

พร้อมปลูก

สร้างได้ทันที

มีให้เลือก

หลากหลาย

ตอบสนอง

ทุกไลฟ์สไตล์คนเมือง

ดูเงินดูทอง




สำนักการโยธา กรุงเทพมหานคร

[illegible]

รายการสัญลักษณ์ผนังและผิวผนัง	
①	ผนังทั่วไป ผนังก่ออิฐก่อสกรูสามัญหรือคอนกรีตมวลเบา หรืออื่นๆ ฉาบเรียบ ทาสี
②	ผนังห้องน้ำ ผนังก่ออิฐก่อสกรูสามัญหรือคอนกรีตมวลเบา หรืออื่นๆ ปูกระเบื้องเซรามิค ชนิดปูผนัง ขนาด A
หมายเหตุ - ชนิดของผนัง และรายละเอียดในการตกแต่งผิวผนัง เจ้าของงานเป็นผู้ตัดสินใจ โดยผู้รับจ้างจัดหาวัสดุวัสดุ และปรึกษาเจ้าของงาน ก่อนดำเนินการ - ไม่ผู้รับจ้างติดตั้งบัวพื้น ไม่สังเคราะห์ ไม่มี Asbestos พร้อมทาสี	
รายการสัญลักษณ์พื้น	
①	ท-1 พื้นคอนกรีต ปูทับด้วยกระเบื้องเซรามิค ชนิดปูพื้น ขนาด A
②	ท-2 พื้นคอนกรีต ปูทับด้วยปาร์เก้ไม้ หรือพื้นไม้สังเคราะห์
หมายเหตุ - ชนิดของพื้น และรายละเอียดในการตกแต่งผิวพื้น เจ้าของงานเป็นผู้ตัดสินใจ โดยผู้รับจ้างจัดหาวัสดุวัสดุ และปรึกษาเจ้าของงาน ก่อนดำเนินการ - ไม่ผู้รับจ้างติดตั้งบัวพื้น ไม่สังเคราะห์ ไม่มี Asbestos พร้อมทาสี	
รายการสัญลักษณ์ฝ้าเพดาน	
①	ฝ้าเพดานไฟเบอร์ซีเมนต์ หน้าไม้น้อยกว่า ๐.๘มม ชนิดขอบลาด ฉาบรอยต่อเรียบ ทาสี
②	ฝ้าเพดานไฟเบอร์ซีเมนต์ หน้าไม้น้อยกว่า ๐.๘มม ชนิดขอบลาด ทนชื้น ฉาบรอยต่อเรียบ ทาสี
หมายเหตุ - เจ้าของ SERVICE แบบต้นร่างรูป บริเวณฝ้าเพดาน ขึ้นบนที่ติดกับหลังคา ขนาด 0.60x0.60 ม. ต้นบนหน้าของกันชนหน้างาน - ไม่ติดตั้งฉนวนกันความร้อน บนฝ้าเพดานห้องชั้นบน หรือใต้โครงสร้าง - ไม่ผู้รับจ้างติดตั้งบัวฝ้าเพดาน ไม่สังเคราะห์ ไม่มี Asbestos พร้อมทาสี	

မေလ ၁၈ ရက်



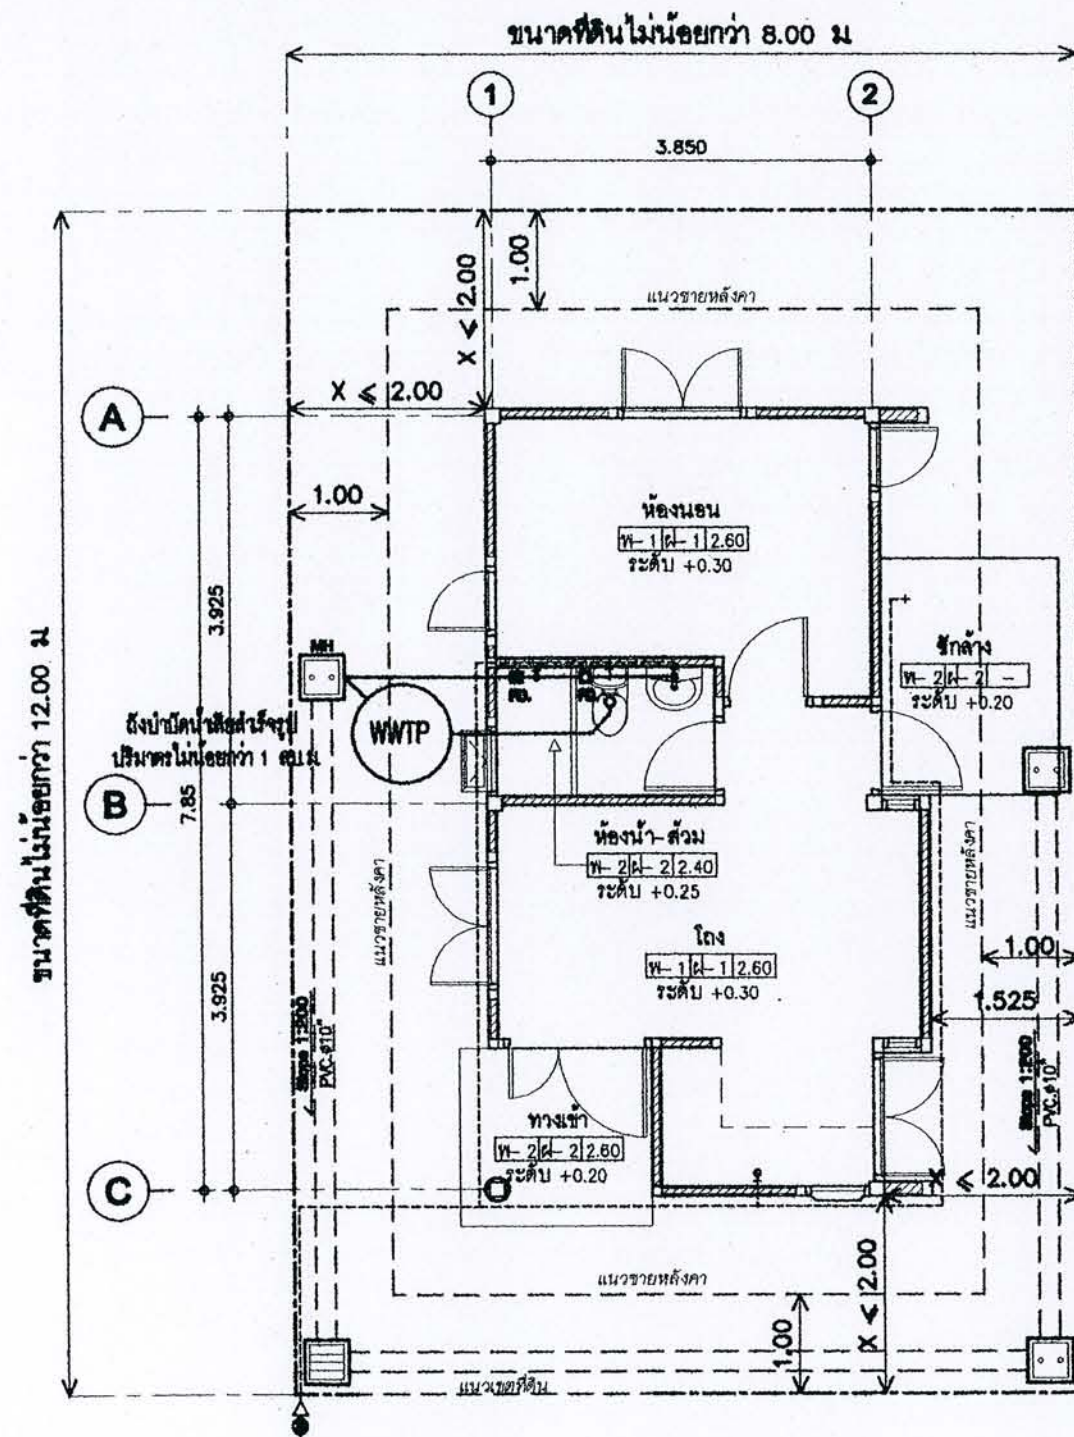

ผังบริเวณ

มาตราส่วน 1:75

พื้นที่ใช้สอยในอาคาร ประมาณ 30.75 ตร.ม

บนโฉนดที่ดินเลขที่

----- ท่อระบายน้ำดินขนาด 10.20 ม

□ บ่อพักน้ำรูป ขนาด 0.40 x 0.40 ทุกระยะ
ไม่เกิน 6.00 ม ความยาวไม่เกิน 18.00 ม
จากจุดเชื่อมท่อระบายน้ำ

□ บ่อพักขยะ



สำนักงานโยธา
กรุงเทพมหานคร

โครงการ
แบบบ้านชั้นเดียวประชาชน

ตามนโยบาย

ม.ร.ว.สุขุมพันธุ์ บริพัตร ผู้ว่าฯกทม.
นายพรเทพ เศรษฐินกุล รองผู้ว่าฯกทม.
นายธีระชน มโนชัยพิบูลย์ รองผู้ว่าฯกทม.
นายพงษ์ศักดิ์ แสนลิ้นดี ปลัดฯกทม.

ผู้อำนวยการสำนักงานโยธา

นายชุมพล สำนกาศ

รองผู้อำนวยการสำนักงานโยธา

นายศักดิ์ เศรษฐินกุล

ผู้อำนวยการสำนักงานออกแบบ

นายสุรศักดิ์ แสนลิ้นดี

หัวหน้ากลุ่มงานสถาปัตยกรรม

นายสุวิทย์ บุญปักษ์

หัวหน้ากลุ่มงานวิศวกรรม

นายธีระยุทธ คงสวัสดิ์เสถียร

สถาปนิก

นางสาวสุมนมาลย์ กาญจนะ

วิศวกรโครงสร้าง

นายวิวัฒน์ บริรักษ์

วิศวกรไฟฟ้า

นายวิฑิตพงษ์ จิระเสนา

วิศวกรสุขาภิบาล

นางสาวมณฑิรา สมพงษ์

วิศวกรเครื่องกล

นายช่างเขียนแบบ

นายณัฐพงศ์ ณรงค์บุญชู

แบบ
021 บ้านฉุกเฉินฉุกเฉิน

เจ้าของ

สถานที่

แบบแสดง

ผังบริเวณ

มาตราส่วน 1:75

FILE : เลขที่

วันที่ 2553 A-02 02

คัดลอกแบบ

รวมแผ่น 11

รายการแนบ



สำนักงานโยธา
กรุงเทพมหานคร

โครงการ
แบบบ้านขึ้นเพื่อประชาชน

ตามนโยบาย

ม.ร.ว.สุขุมพันธุ์ บริพัตร ผู้ว่าฯกทม.
นายพรเทพ เศรษฐินร้อย ร่องูวาทกน
นายธีระชน มโนวิจิตร ร่องูวาทกน
นายพงษ์ศักดิ์ แสนสุนด์ ปดิธากน

ผู้อำนวยการสำนักงานโยธา
นายสุรพล สันภาพ
รองผู้อำนวยการสำนักงานโยธา
นายทวีศักดิ์ เดชประพันธ์
ผู้อำนวยการสำนักงานออกแบบ
นายจตุรงค์ สมเทียม
หัวหน้ากลุ่มงานสถาปัตยกรรม
นายสันติสุข บุญยิกษ
หัวหน้ากลุ่มงานวิศวกรรม
นายธีระยุทธ คงสวัสดิ์ไชย

สถาปนิก
นางสาวสุมนมวณีย์ กาญจนะ
วิศวกรโครงสร้าง
นายวันโอ บัณฑิต
วิศวกรไฟฟ้า
นายจิตติพงษ์ จิระนคร
วิศวกรสุขาภิบาล
นางสาวณณศิรา สมหอม
วิศวกรเครื่องกล

นายช่างเขียนแบบ
นายณัฐพงศ์ ณรงค์บุญชูทรัพย์

แบบ
021 บ้านฉุกเฉินอุทก

เจ้าของ

สถานที่

แบบแสดง

ผังพื้น และผังหลังคา

มาตราส่วน 1:75


FILE : เลขที่ 03


วันที่ 2553

คิดออกแบบ

รวมหน้า 11

รายการแก้ไขแบบ

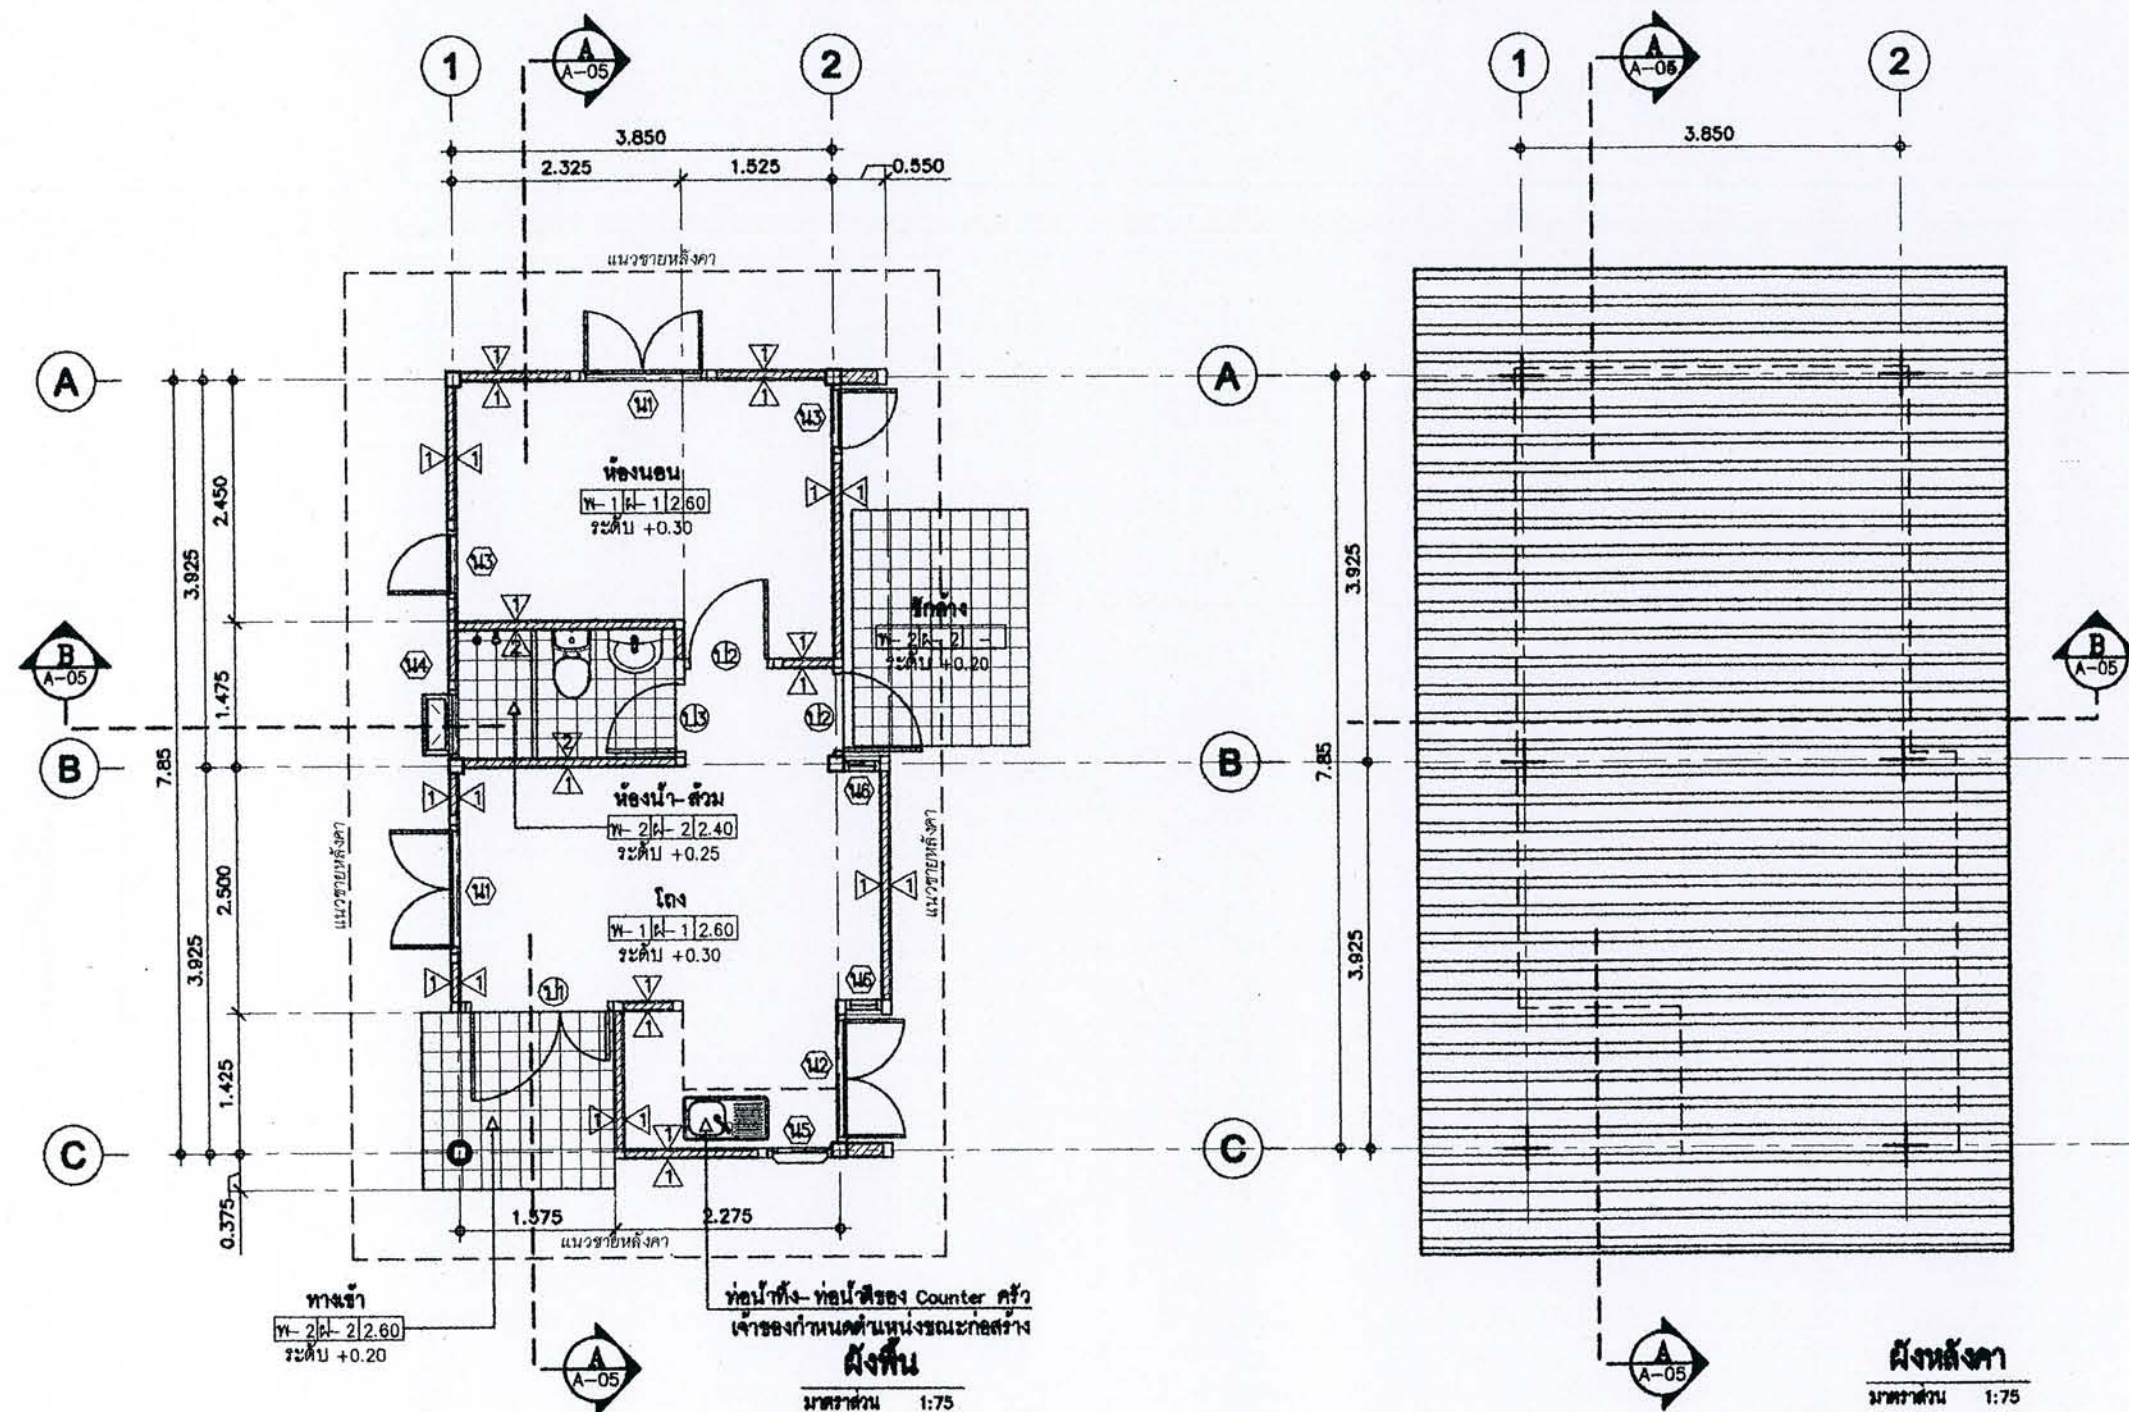

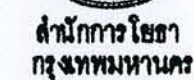

ตามนโยบาย

ม.๒.๒ สุขุมพันธุ์ บริษัท	ผู้ว่าฯกทม.
นายพทพ. เศรษฐบุตร	รองผู้ว่าฯกทม.
นายธีระชน มโนวิจิตร	รองผู้ว่าฯกทม.
นายพงษ์ศักดิ์ เตมียา	ปลัดฯกทม.


ตลาดหุ้น
--

นายทรงสิทธิ์ รุ่งนฤมิตร

[illegible]

สถานที่	
---------	--

	11
--	----

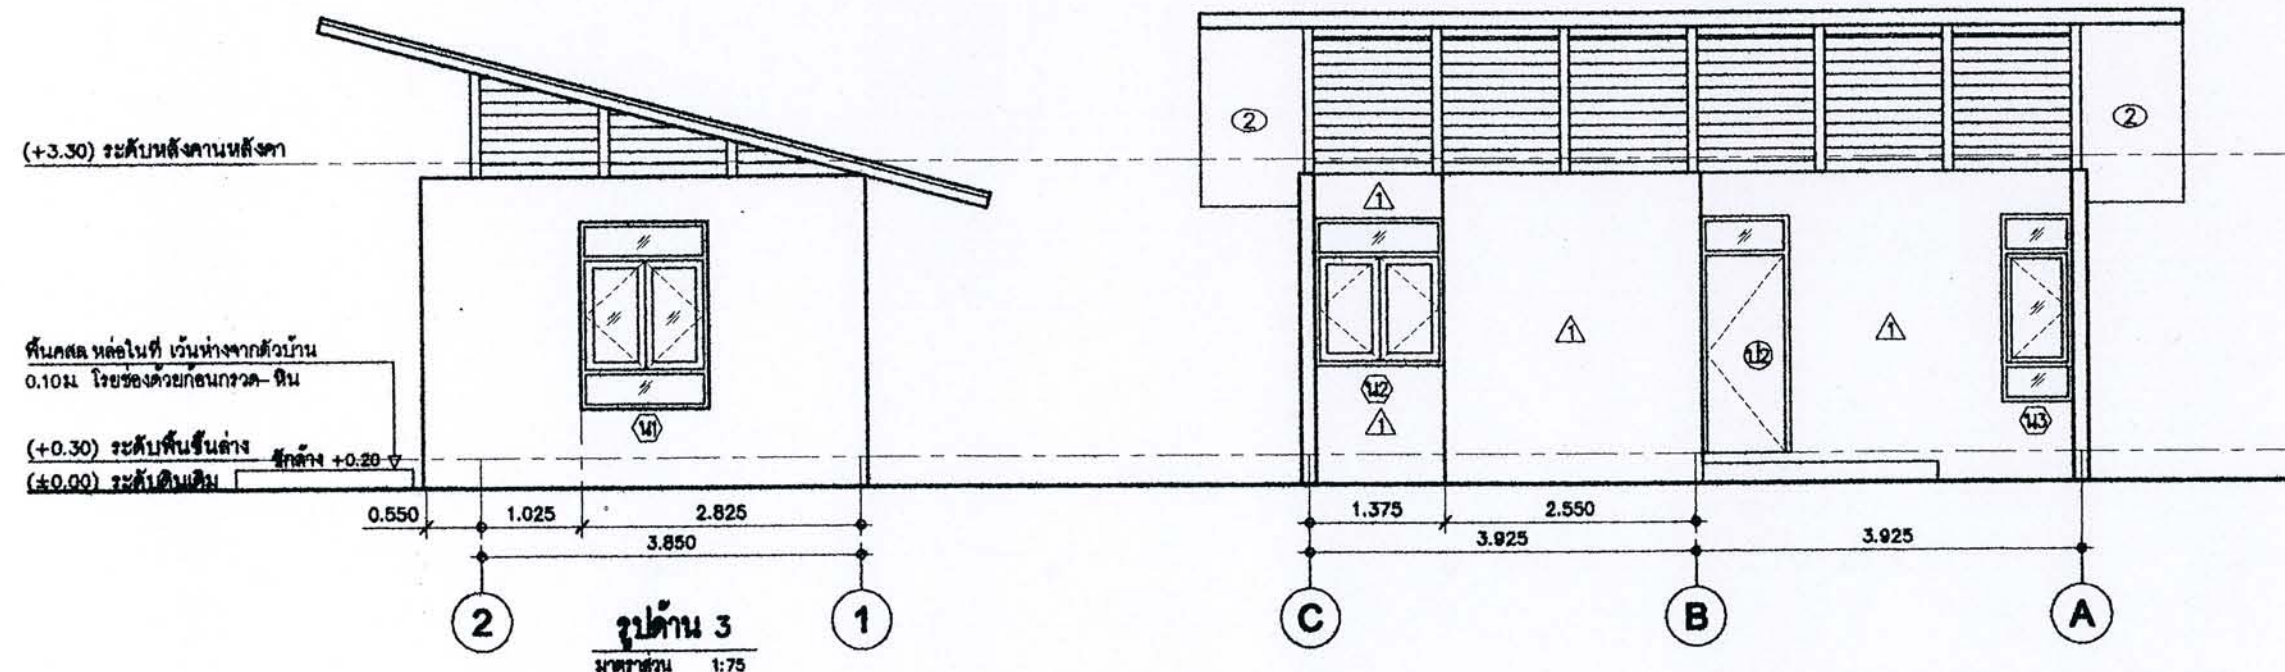



สำนักงานโยธา
กรุงเทพมหานคร

โครงการ
แบบบ้านยี่สิบเอ็ดประชาชน

ตามนโยบาย

นางจุฬารัตน์ ตรีวิทย์ หัวหน้า
นายพลท พะทะบุตร รองหัวหน้า
นายธีระชัย มโนวิทย์กุล รองหัวหน้า
นายพงษ์ศักดิ์ แสนสำนึก ปลัดกอง

ผู้อำนวยการสำนักงานโยธา
นายชุมพล สันกาล
รองผู้อำนวยการสำนักงานโยธา
นายวิวัฒน์ เติบประพันธ์
ผู้อำนวยการสำนักงานออกแบบ
นายสุวิทย์ สันติ
หัวหน้ากลุ่มงานสถาปัตยกรรม
นายสุวิทย์ บุญฤทธิ์
หัวหน้ากลุ่มงานวิศวกรรม
นายธีระยุทธ คงศรีชัย

สถาปนิก
นางสาวจุฬารัตน์ ตรีวิทย์
วิศวกรโครงสร้าง
นายวิวัฒน์ เติบประพันธ์
วิศวกรไฟฟ้า
นายวิวัฒน์ เติบประพันธ์
วิศวกรสุขาภิบาล
นางสาวณัฏฐา สอนทอง
วิศวกรเครื่องกล

นายช่างเขียนแบบ
นายณัฏฐา ธีระวิทย์กุล

แบบ
021 บ้านฉุกเฉินอุทกภัย

เจ้าของ

สถานที่

แบบแสดง
รูปตัด A-A, B-B
และผังพื้นขยายห้องน้ำ

มาตราส่วน 1:50



FILE : วันที่ 15 พฤษภาคม 2553

ครั้งที่ A-05 05


คิดค่าปรับแบบ

รวม 11

รายการแก้ไขแบบ

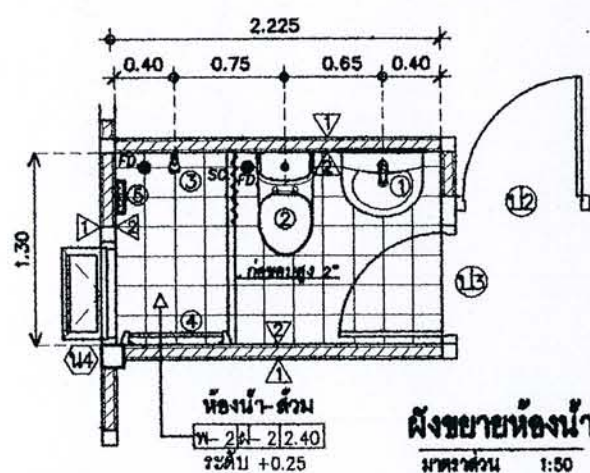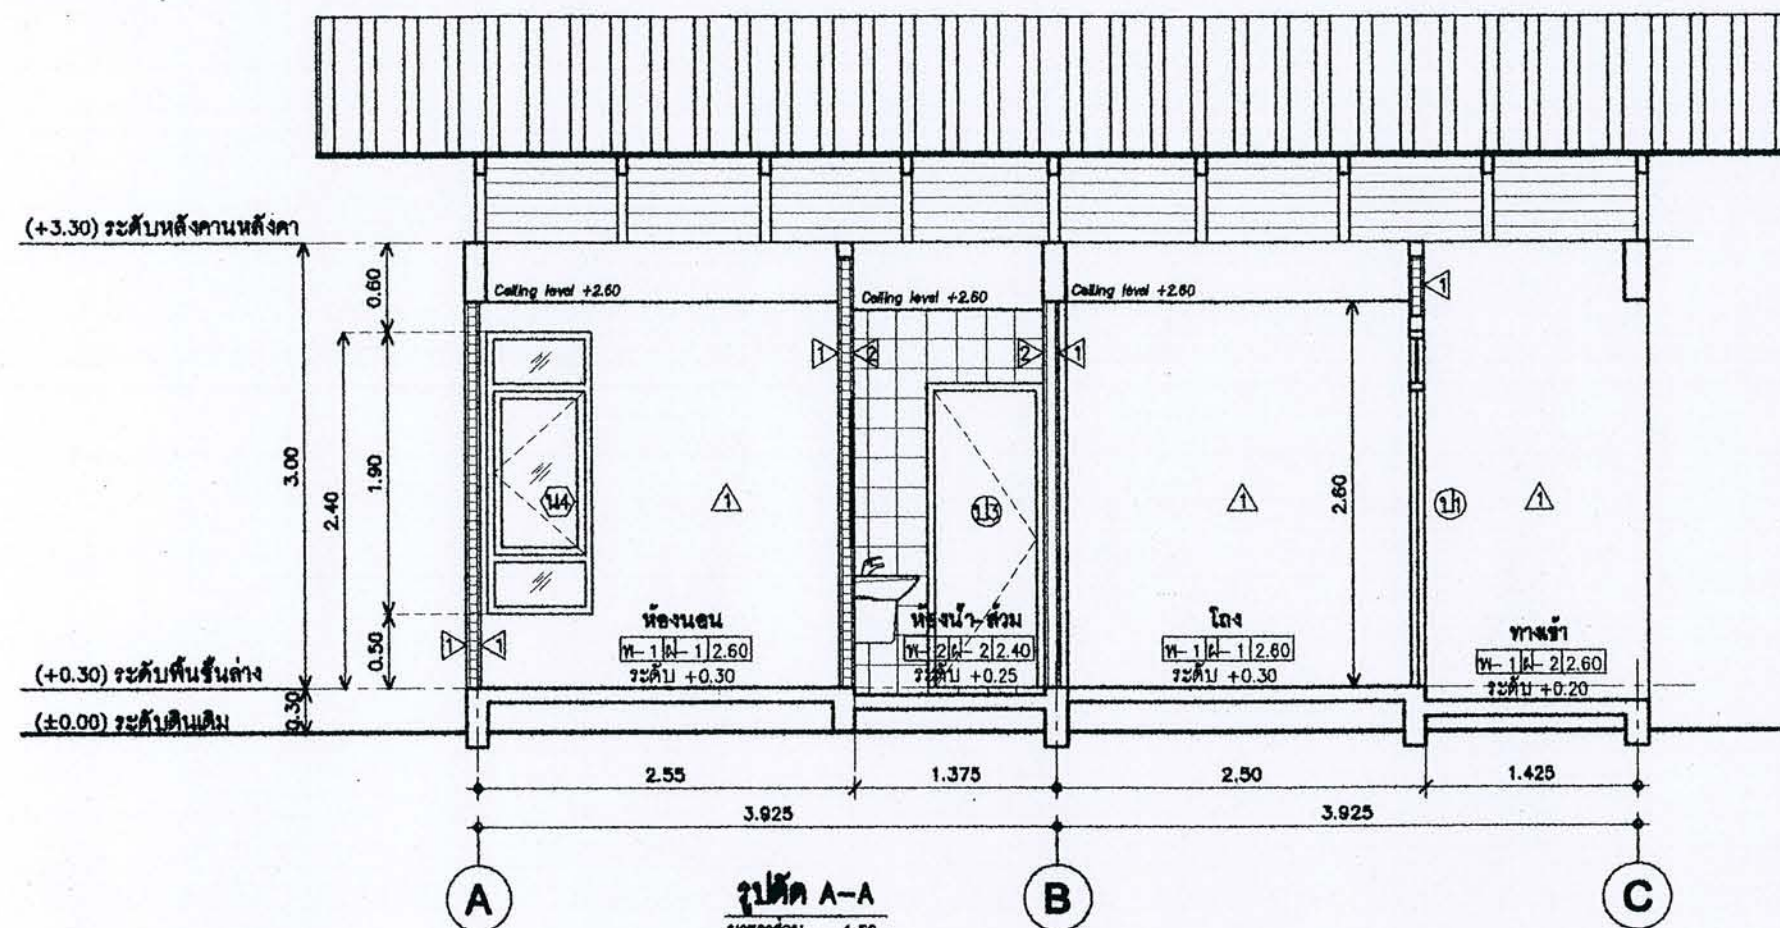

สัญลักษณ์	รายการ
①	อ่างล้างหน้าชนิดแขวนผนัง พร้อมก๊อกน้ำ ด้านบน ติดตั้งกระจกเงา สูงจากพื้น 1.00ม.
②	ชักโครกแบบนั่งราบ พร้อมอุปกรณ์ครบชุด
③	ฝักบัวสายอ่อนอย่างดี ด้านล่างติดตั้งก๊อกน้ำล้างพื้น
④	ราวแขวนผ้า
⑤	ที่วางสบู่
SC.	ม่านอาบน้ำ พร้อมราวแขวนชนิดปรับระดับได้
FD.	รูระบายน้ำทิ้งแบบดัด
หมายเหตุ	ยึด รื้อ, ถู, เจาะของกำหนดภายหลัง

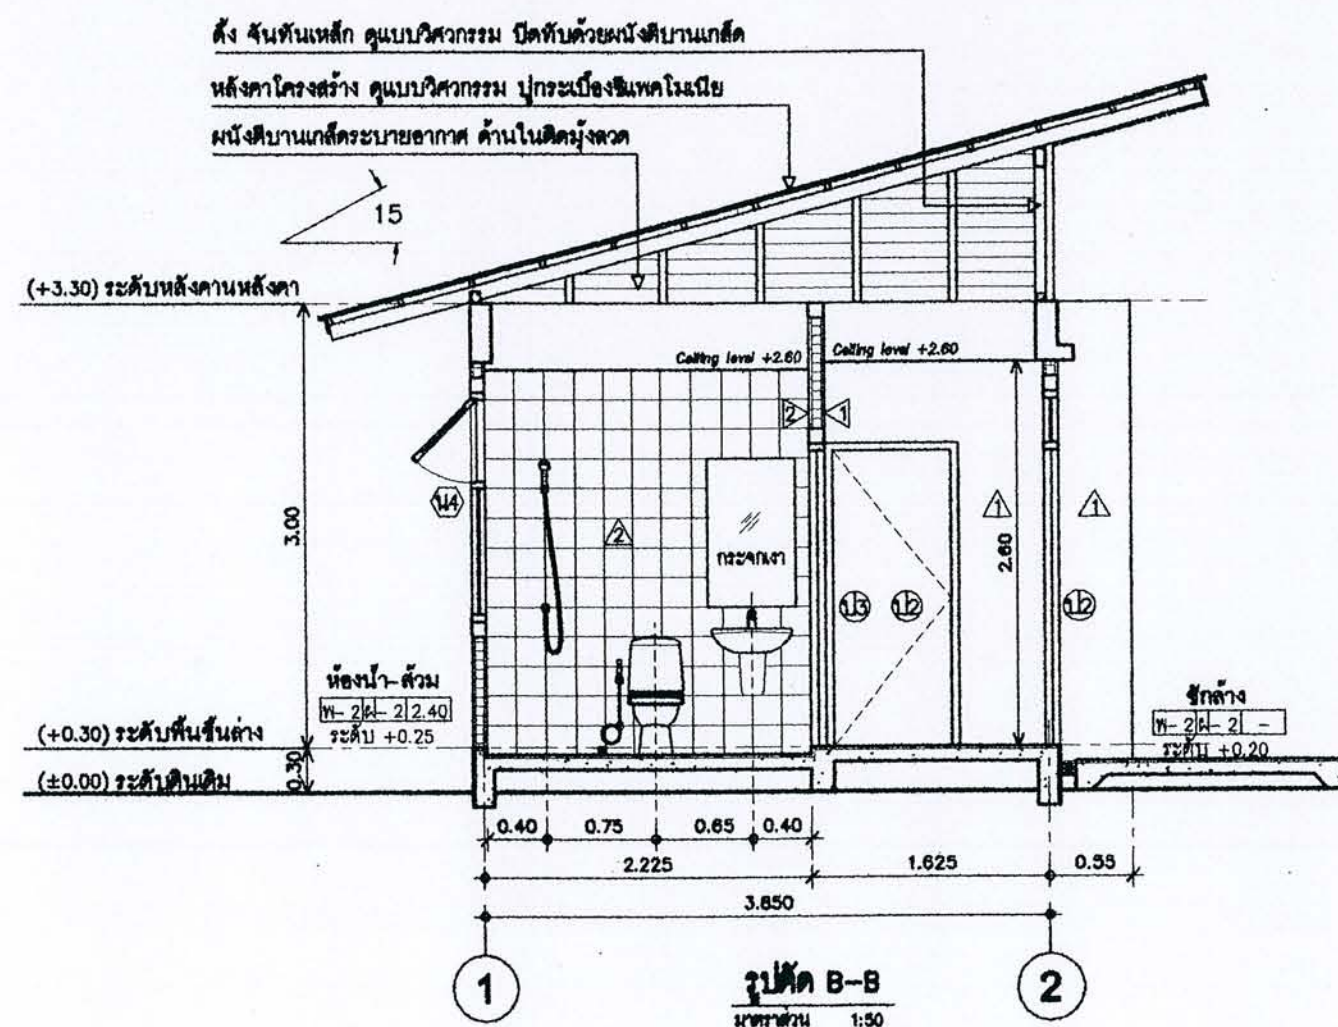

ตั้ง จันทันเหล็ก คูณบานวิศวกรรม ปิดทับด้วยผนังบานเกล็ด
หลังคาโครงสร้าง คูณบานวิศวกรรม ปูกระเบื้องหินขัดโมเนีย
ผนังบานเกล็ดระบายอากาศ ด้านในติดมุ้งลวด



สำนักงานโยธา
กรุงเทพมหานคร

โครงการ
แบบบ้านขึ้นเพื่อประชาชน

ตามนโยบาย

น.ร. ๒๕๖๓ พันธุ์ บริพัตร ผู้ว่าราชการ
นายพรเทพ เกษมทรัพย์ รองผู้ว่าราชการ
นายธีระชน มโนมณีบุญ รองผู้ว่าราชการ
นายพงศ์ศักดิ์ เกษมสันต์ ปลัดกรุงเทพมหานคร

ผู้อำนวยการสำนักงานโยธา
นายสมศักดิ์ สำนักทด
รองผู้อำนวยการสำนักงานโยธา
นายศักดิ์สิทธิ์ นิตยประพันธ์
ผู้อำนวยการสำนักงานออกแบบ
นายสุรศักดิ์ สมเยี่ยม
หัวหน้ากลุ่มงานสถาปัตยกรรม
นายสันติสุข บุญมีเกียรติ
หัวหน้ากลุ่มงานวิศวกรรม
นายธีระยุทธ คงสวัสดิ์เสถียร

สถาปนิก
นางสาวสุมนะมาศ กาญจนะ
วิศวกรโครงสร้าง
นายวิวัฒน์ โนน ธีระโพธิ์
วิศวกรไฟฟ้า
นายศักดิ์พงษ์ จิระธนากร
วิศวกรสุขาภิบาล
นางสาวณณศิรา สดกหอม
วิศวกรเครื่องกล
นายธนากร เรืองงาม
นายณัฐพงศ์ ณรงค์บุญชูทรัพย์


แบบ
021 บ้านดงเงินดงทอง

คำร้อง
สถานที่


แบบแสดง
แบบขยายประตู-หน้าต่าง

มาตราส่วน 1:50
FILE :
วันที่ ๒๕๖๓ ๒๕๖๓ A-06 06
ชื่อสถาปนิก/ช่างเขียน
รวมแผ่น 11


รายการแก้ไขแบบ

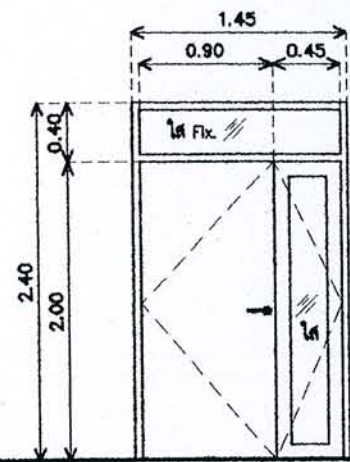

๑๑

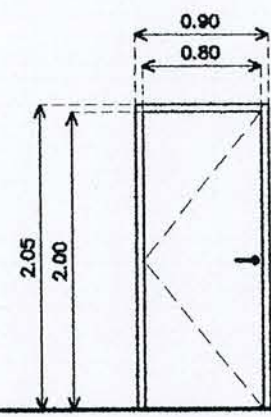

๑๒

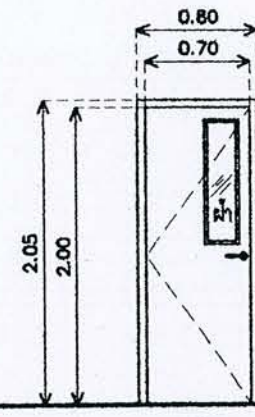


๑๓


ลักษณะบาน	ประตูบานเปิดคู่ ด้านบนช่องแสงกระจกติดตาย (ประตูทางเข้า)
วงกบ	ไม้เนื้อแข็ง ขนาด 2"x4"
กรอบบาน	บานไม้จริงสำเร็จรูป หรือเจ้าของกำหนดขณะก่อสร้าง
ลูกฟัก	กระจกโฟลด์ได หรือกระจกใสติดตาย หน้า 6 มม. (เจ้าของกำหนดขณะก่อสร้าง)
อุปกรณ์	พร้อมมือจับและอุปกรณ์ครบชุด กำหนดให้ติดตั้งบานพับมาตรฐาน 3 ตัว/บาน

ลักษณะบาน	ประตูบานเปิดเดี่ยว (ประตูทั่วไป)
วงกบ	ไม้เนื้อแข็ง ขนาด 2"x4"
กรอบบาน	บานไม้จริงสำเร็จรูป ทาสี หรือเจ้าของกำหนดขณะก่อสร้าง
ลูกฟัก	
อุปกรณ์	พร้อมมือจับและอุปกรณ์ครบชุด กำหนดให้ติดตั้งบานพับมาตรฐาน 3 ตัว/บาน


ลักษณะบาน	ประตูบานเปิดเดี่ยว (ประตูห้องน้ำ)
วงกบ	ไม้เนื้อแข็ง ขนาด 2"x4"
กรอบบาน	บานไม้จริงสำเร็จรูป ทาสี หรือเจ้าของกำหนดขณะก่อสร้าง
ลูกฟัก	กระจกฝ้า หรือกระจกใสติดตาย หน้า 6 มม. (เจ้าของกำหนดขณะก่อสร้าง)
อุปกรณ์	พร้อมมือจับและอุปกรณ์ครบชุด กำหนดให้ติดตั้งบานพับมาตรฐาน 3 ตัว/บาน

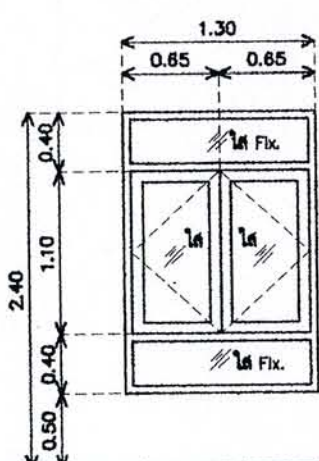


๑๑

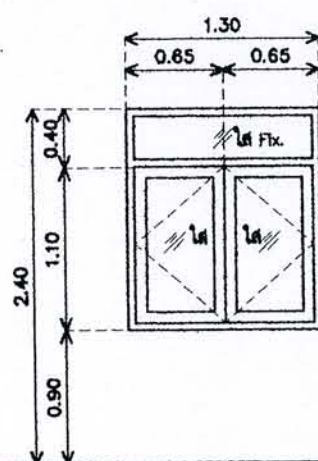


๑๒

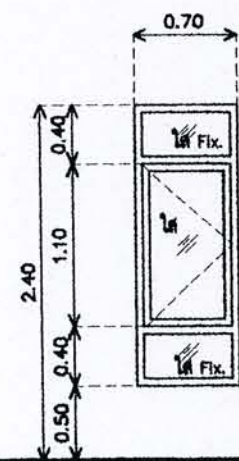


๑๓

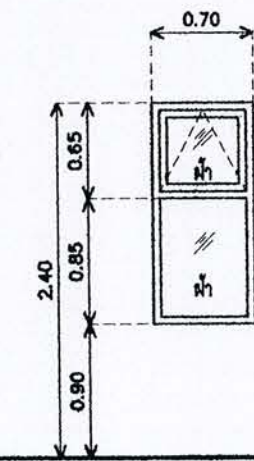

๑๔

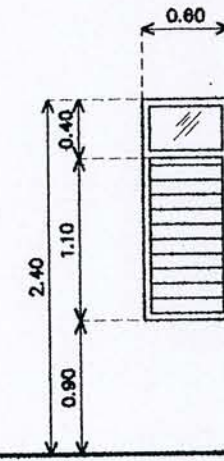

๑๕

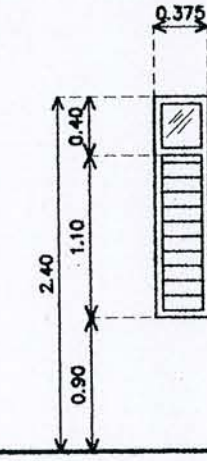

๑๖

ลักษณะบาน	หน้าต่างบานเปิดคู่ ช่องแสงกระจกติดตาย
วงกบ	ไม้เนื้อแข็ง หรืออลูมิเนียม ขนาด 2"x4" (เจ้าของกำหนดขณะก่อสร้าง)
กรอบบาน	ไม้จริงสำเร็จรูป หรืออลูมิเนียม (เจ้าของกำหนดขณะก่อสร้าง)
ลูกฟัก	กระจกโฟลด์ได หรือกระจกใสติดตาย หน้า 6 มม. (เจ้าของกำหนดขณะก่อสร้าง)
อุปกรณ์	พร้อมมือจับและอุปกรณ์ครบชุด

ลักษณะบาน	๑๓ = หน้าต่างบานเปิดเดี่ยว ช่องแสงกระจกติดตาย
วงกบ	ไม้เนื้อแข็ง หรืออลูมิเนียม ขนาด 2"x4" (เจ้าของกำหนดขณะก่อสร้าง)
กรอบบาน	ไม้จริงสำเร็จรูป หรืออลูมิเนียม (เจ้าของกำหนดขณะก่อสร้าง)
ลูกฟัก	กระจกโฟลด์ได หรือกระจกใสติดตาย หน้า 6 มม. (เจ้าของกำหนดขณะก่อสร้าง)
อุปกรณ์	พร้อมมือจับและอุปกรณ์ครบชุด

ลักษณะบาน	หน้าต่างบานเปิดคู่ ด้านบนช่องแสงกระจกติดตาย
วงกบ	ไม้เนื้อแข็ง หรืออลูมิเนียม ขนาด 2"x4" (เจ้าของกำหนดขณะก่อสร้าง)
กรอบบาน	ไม้จริงสำเร็จรูป หรืออลูมิเนียม (เจ้าของกำหนดขณะก่อสร้าง)
ลูกฟัก	๑๕ = กระจกโฟลด์ได หรือกระจกใสติดตาย หน้า 6 มม. (เจ้าของกำหนดขณะก่อสร้าง)
อุปกรณ์	๑๖ = กระจกฝ้า หรือกระจกใสติดตาย หน้า 6 มม. (เจ้าของกำหนด)

รายการประกอบแบบด้านวิศวกรรมโยธา

1. ซีเมนต์

- 1.1 ส่วนของโครงสร้างคอนกรีตเสริมเหล็กทั้งหมดต้องใช้ PORTLAND CEMENT ประเภทที่ 1 ที่มีคุณสมบัติตามมาตรฐานผลิตภัณฑ์อุตสาหกรรมเท่านั้น
- 1.2 ถ้าไม่ได้ระบุเป็นอย่างอื่น คอนกรีต 1 ลบ.ม. ต้องมีส่วนผสมของซีเมนต์ไม่น้อยกว่า 320 กก.

2. คอนกรีต

- 2.1 คอนกรีตที่ใช้กับโครงสร้างอาคารได้แก่ ฐานราก, เสา, คาน, พื้น, คอนกรีตทับหน้าพื้นสำเร็จรูป, ผนัง ค.ส.ล. ฯลฯ ต้องมีกำลังอัดประลัยไม่น้อยกว่า 210 กก./ตร.ซม. เมื่ออายุ 28 วัน โดยทดสอบจากแท่งคอนกรีตตัวอย่างทรงกระบอก Ø 150 x 300 มม.
- 2.2 ADMIXTURES ที่ใช้ต้องมีคุณสมบัติตาม ASTM หรือ BS

3. งานเหล็ก

- 3.1 คุณสมบัติของเหล็กเส้นเสริมคอนกรีต มีดังนี้

ขนาดเหล็กเส้น มม.	สัญลักษณ์	มาตรฐาน	หมายเหตุ
RB 6 , RB 9	SR - 24	มอก. 20-2527	
DB 12 ขึ้นไป	SD - 30	มอก. 24-2536	

- 3.2 เหล็กรูปพรรณ , เหล็กกลวงสำหรับก่อสร้าง

- 3.2.1 เหล็กรูปพรรณที่จะใช้ต้องมีคุณสมบัติตาม มอก. 1227-2537, มอก.1228 -2537 หรือ JIS เหล็กกลวงที่ใช้ต้องมีคุณสมบัติตาม มอก. 107-2533 หรือ JIS และเหล็กรูปพรรณเชื่อมประกอบจะต้องมีคุณสมบัติตาม มอก. 1303-2538
- 3.2.2 เหล็กรูปพรรณทั้งหมดต้องเป็นของใหม่ ไม่เคยใช้งานมาก่อน ตรวจสอบเป็นรอย ไม่มีการดัดบิด ไม่มีการดัดหน้า ไม่มีการดัดหน้า ไม่เปื้อนสี หรือน้ำมัน
- 3.2.3 การต่อเหล็กรูปพรรณ ถ้าไม่จำเป็นจริงๆ แล้วห้ามต่อ ในกรณีที่มีการต่อเหล็ก รอยต่อของเหล็กต้องมีการกำหนดตำแหน่งการต่อเหล็กที่ไม่มีการต่อ การต่อให้ตรงตามข้อกำหนด และการต่อให้เป็นไปตามมาตรฐาน AISC
- 3.2.4 การประกอบเหล็กโครงสร้าง ให้ดำเนินการตามมาตรฐาน AISC หรือตามมาตรฐานสำหรับอาคารเหล็กรูปพรรณของ วสท. ที่ 1015-40
- 3.2.5 ผู้รับจ้างจะต้องทำ คำนวณ ชิดโครง ให้เพียงพอเพื่อยึดโครงสร้างให้แน่นหนาอยู่ในแนวและตำแหน่งที่ต้องการ
- 3.2.6 องค์อาคารที่วางทาบหรือเชื่อมจะต้องวางให้แนบสนิทเต็มหน้า
- 3.2.7 การเชื่อมต้องทั้งหมดให้ใช้วิธีเชื่อมด้วยไฟฟ้าการ (Electric arc welding) โดยตลอดผิวหน้าที่จะมีการเชื่อมให้เป็นไปตามมาตรฐาน AWS ขนาดของรอยเชื่อมต้องไม่น้อยกว่าความหนาของแผ่นเหล็ก
- 3.2.8 ถ้าไม่ได้กำหนดเป็นอย่างอื่นรอยต่อระหว่างชิ้นส่วนเหล็กต่างๆ ให้ใช้วิธี เชื่อมตะเข็บตลอดแนว
- 3.2.9 ผิวหน้าที่จะทำการเชื่อม ต้องสะอาดปราศจากสนิมคราบน้ำมัน สนิมกรัน ไขมัน สี หรือสิ่งแปลกปลอมอื่นใด
- 3.2.10 รอยเชื่อมต้องปฏิบัติตาม มอก. หรือ AWS หรือ AISC
- 3.2.11 ให้ทาสีกันสนิมไม่น้อยกว่า 2 ชั้น คุณภาพเทียบเท่า RUST-OLEAM, JOTAN, SIKKENS


4. ระบบกันซึม

- 4.1 รายละเอียดและคุณสมบัติ

ส่วนของอาคาร	ชนิดและผลิตภัณฑ์	ผลิตภัณฑ์คุณภาพเทียบเท่า
พื้นห้องน้ำ , กันสาด ค.ส.ล.	น้ำยาเคมีแบบกันซึมชนิดทา	BRUSHBOND ของ FOSROC
รางน้ำ ค.ส.ล. หลังคา ค.ส.ล.		LANKO 225 P-? DAVCO

5. ท่อไปและการเตรียมงาน

- 5.1 รายการประกอบแบบอื่นใดที่ไม่ได้กำหนดไว้ให้ถือปฏิบัติตาม " บทกำหนดทั่วไปสำหรับการก่อสร้างอาคารคอนกรีตเสริมเหล็ก " ของ วสท. เป็นเกณฑ์
- 5.2 แบบรายการเหล่านี้ เป็นแบบรายการที่ใช้เป็นแนวทางในการก่อสร้างเท่านั้น หากมีความจำเป็นต้องเพิ่มเติมรายละเอียดเพื่อให้เกิดความมั่นคงแข็งแรงหรือความกลมหาดินมากยิ่งขึ้น หรือหากแบบขัดแย้ง แสดงรายละเอียดไม่ครบถ้วน วิศวกรฝ่ายวิศวกรรมจะเป็นผู้กำหนดให้ หรืออาจผู้รับจ้างดำเนินการออกแบบในส่วนนั้นๆ โดยอาศัยหลักวิชาช่างในขณะก่อสร้างจะต้องมีวิศวกร ไม่ต่ำกว่าสามัญวิศวกรลงนามรับรอง และต้องเสนอต่อฝ่ายวิศวกรรมอาคารเห็นชอบก่อน โดยถือเป็นส่วนหนึ่งของแบบรายการนี้ และไม่ถือว่ามีการก่อสร้างผิดไปจากแบบรายการก่อสร้างแต่อย่างใด แต่ทั้งนี้ เนื่องงานต้องไม่ลดน้อยกว่าเดิมและผู้รับจ้างจะต้องไม่คิดค่าใช้จ่ายเพิ่ม

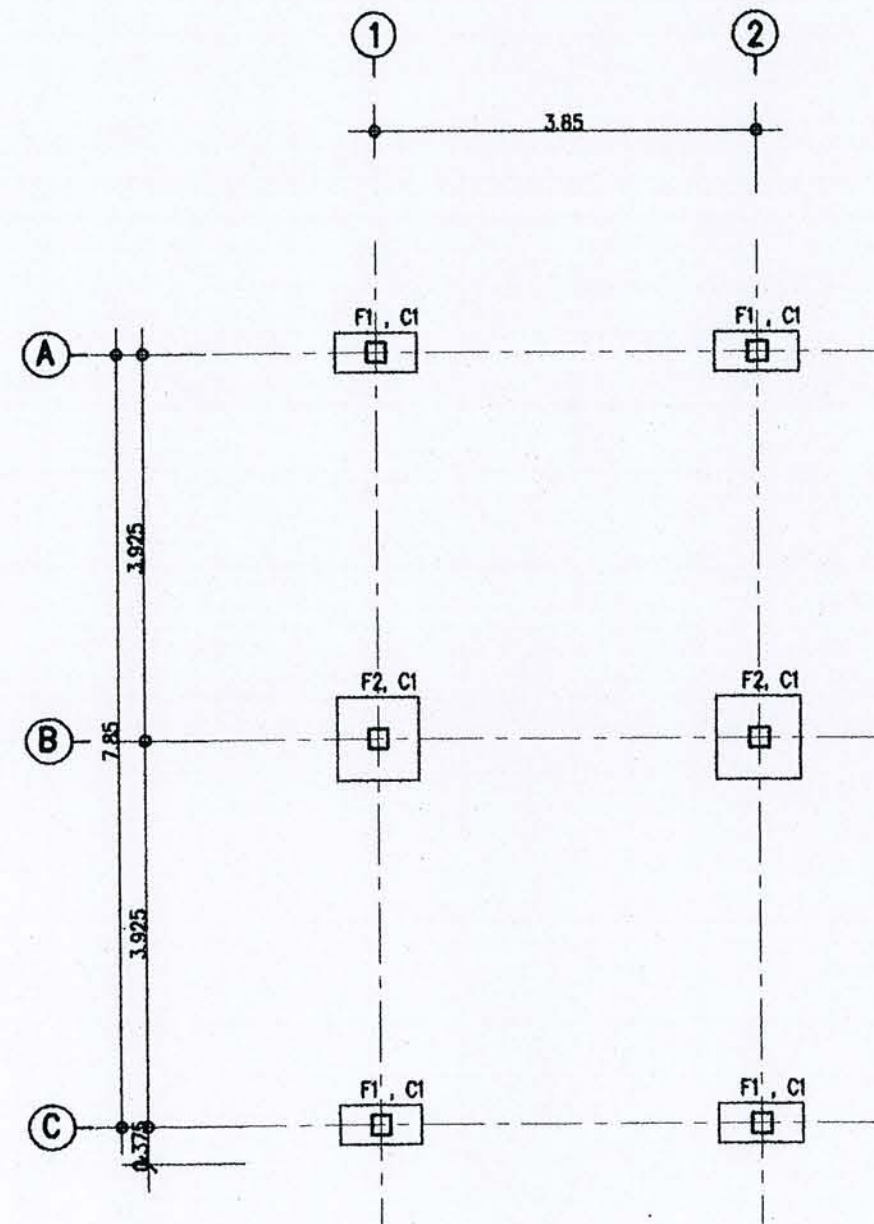

แปลนเสาเข็มและฐานราก
มาตราส่วน 1 : 75



สำนักงานโยธา
กรุงเทพมหานคร

โครงการ
แบบบ้านขึ้นเพื่อประชาชน

ตามนโยบาย
น.ร.สุจินต์ บริดัยชเรศน์ รัฐมนตรี
กระทรวงมหาดไทย รองผู้ว่าราชการ
นายกรัฐมนตรี นายสุวิทย์ คุณกิตติ
นายพงษ์ศักดิ์ แสนสมันต์ ปลัด
กระทรวงมหาดไทย

ผู้อำนวยการสำนักงานโยธา
นายสุจินต์ บริดัยชเรศน์
รองผู้อำนวยการสำนักงานโยธา
นายสุวิทย์ คุณกิตติ
ผู้อำนวยการสำนักงานออกแบบ
นายสุจินต์ บริดัยชเรศน์
หัวหน้ากลุ่มงานสถาปัตยกรรม
นายสุจินต์ บริดัยชเรศน์
หัวหน้ากลุ่มงานวิศวกรรม
นายสุจินต์ บริดัยชเรศน์
นายสุจินต์ บริดัยชเรศน์

สถาปนิก
นางสาวสุจินต์ บริดัยชเรศน์
วิศวกรโครงสร้าง
นายสุจินต์ บริดัยชเรศน์
วิศวกรไฟฟ้า
นายสุจินต์ บริดัยชเรศน์
วิศวกรสุขาภิบาล
นางสาวสุจินต์ บริดัยชเรศน์
วิศวกรเครื่องกล
นายสุจินต์ บริดัยชเรศน์
นางสาวสุจินต์ บริดัยชเรศน์
นางสาวสุจินต์ บริดัยชเรศน์

แบบ
021 บ้านฉุกเฉินฉุกเฉิน
เจ้าของ
สถานที่

แบบแสดง
รายการประกอบแบบโยธา
แปลนเสาเข็มและฐานราก
มาตราส่วน 1: 75
FILE : S-01 07
วันที่ 2553
โดย 11

รายการแบบ



สำนักงานโยธา
กรุงเทพมหานคร

โครงการ
แบบบ้านขึ้นเพื่อประชาชน

ตามนโยบาย

น.ร.สุจินต์ พันธุ์ เกษิต วิศวกร
นายแพทย์ นายแพทย์ รอดูจาก
นายธีระชน มโนวิบูลย์ รอดูจาก
นายพงศ์ศักดิ์ แสนรัตน์ ปัสสาวะ

ผู้อำนวยการสำนักงานโยธา

นายจุมพล สันกาล

รองผู้อำนวยการสำนักงานโยธา

นายวิจิตร วัฒนพันธ์

ผู้อำนวยการสำนักงานออกแบบ

นายจุมพล สันกาล

หัวหน้ากลุ่มงานสถาปัตยกรรม

นายสันติสุข บุญปักษ์

หัวหน้ากลุ่มงานวิศวกรรม

นายธีระยุทธ คงสวัสดิ์

สถาปนิก

นางสาวสุนนมาลย์ กาญจนะ

วิศวกรโครงสร้าง

นายวันโน นริศโพธิ์

วิศวกรไฟฟ้า

นายวิศิษฐ์ จิตตภาพ

วิศวกรสุขาภิบาล

นางสาวณัฏฐา สดก

วิศวกรเครื่องกล

นายช่างเขียนแบบ

นางปณณัฐ ประจวบกิจ

แบบ
021 บ้านฉุกเฉินฉุกเฉิน

พื้นที่

สถานที่

แบบแสดง

แปลนโครงสร้างชั้นล่าง

แปลนคานและโครงหลังคา


มาตราส่วน 1:75

FILE : S-02 08

วันที่ 25/05/2553


ครั้งที่ 11

รายการแก้ไขแบบ

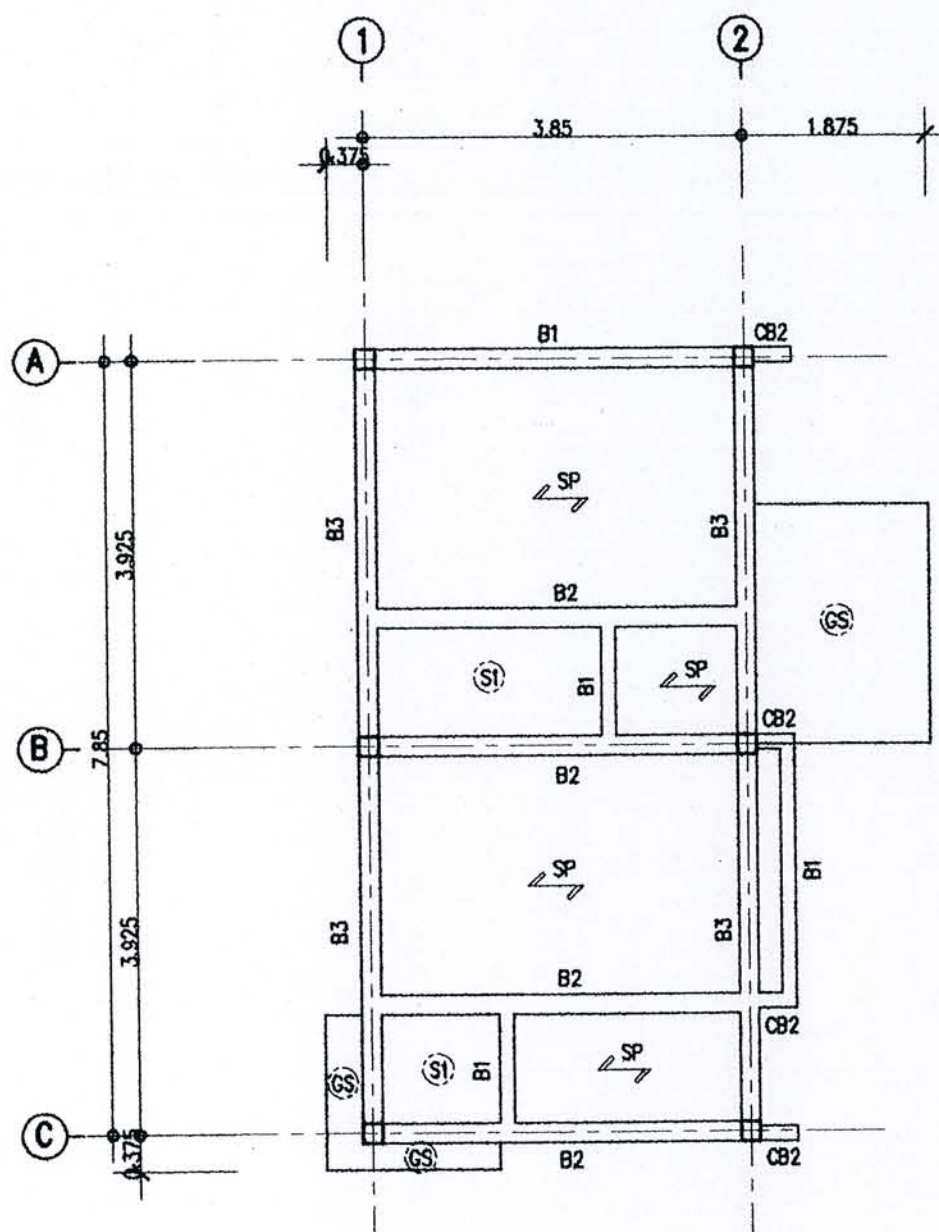

แปลนโครงสร้างชั้นล่าง

มาตราส่วน 1 : 75

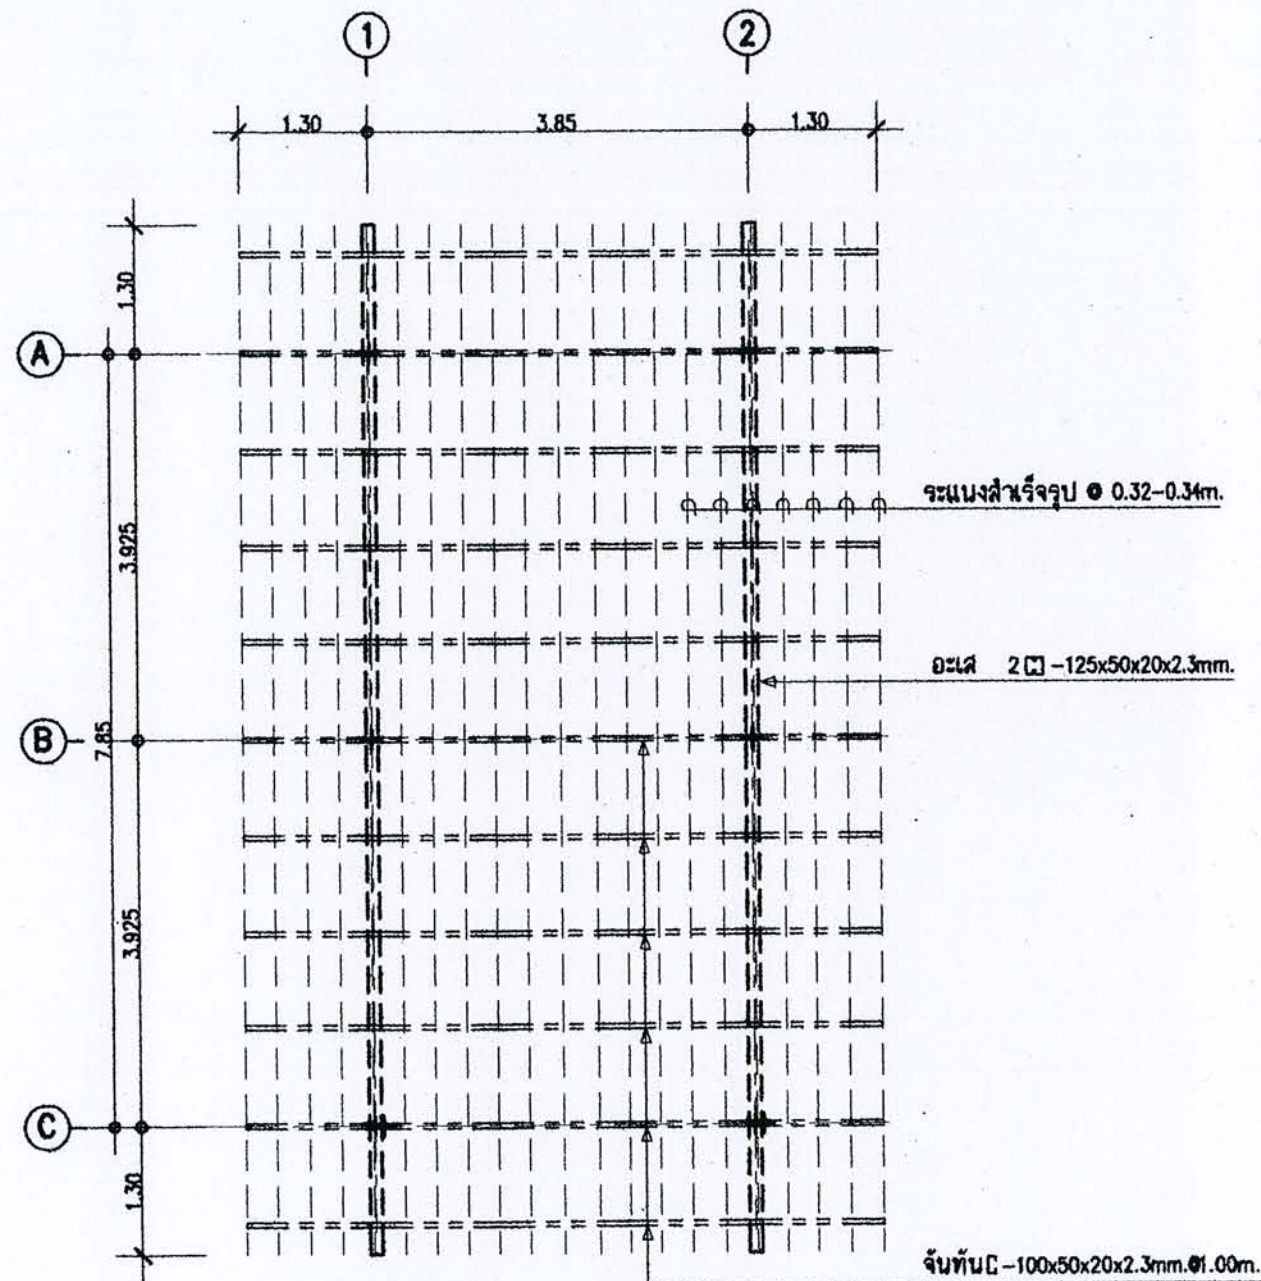

แปลนคานและโครงหลังคา

มาตราส่วน 1 : 75



สำนักงาน
กรุงเทพมหานคร

โครงการ
แบบบ้านชั้นเดียวประชาชน

ตามนโยบาย

ม.ร.ว.สุขุมพันธุ์ บริพัตร ผู้ว่าฯกทม.
นายทรงยศ เศรษฐ์ รักษาราชการ
นายธีระชน มโนชัยพิบูลย์ รักษาราชการ
นายพงศ์ศักดิ์ เสงี่ยมศักดิ์ ปลัดฯกทม.

ผู้อำนวยการสำนักงานโยธา

นายสมศักดิ์ สันติสุข

รองผู้อำนวยการสำนักงานโยธา

นายทวีศักดิ์ เติมประพันธ์

ผู้อำนวยการสำนักงานออกแบบ

นายสุรศักดิ์ สันติสุข

หัวหน้ากลุ่มงานสถาปัตยกรรม

นายสันติสุข บุญปักษ์

หัวหน้ากลุ่มงานวิศวกรรม

นายธีระยุทธ คงสวัสดิ์

สถาปนิก

นางสาวสุนนมาศ กาญจนะ

วิศวกรโครงสร้าง

นายวิวัฒน์ บัณฑิตไพฑูริย์

วิศวกรไฟฟ้า

นายวิศิษฐ์ จิระเดชาร

วิศวกรสุขาภิบาล

นางสาวณิชา สมทอง

วิศวกรเครื่องกล

นายช่างเขียนแบบ

นางปณณพร ประจวบกิจ

แบบ
021 บ้านฉุกเฉินอุทกภัย

เจ้าของ

สถานที่

สถานที่

แบบแสดง

แบบขยายวิศวกรรมโครงสร้าง

มาตราส่วน 1:25

FILE : วันที่ 2553

วันที่ 2553 S-03 09

วันที่ 2553 S-03 09

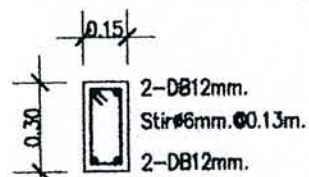

DETAIL B1

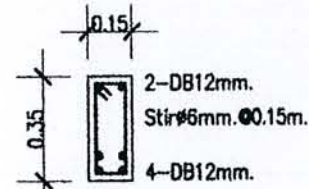


DETAIL B2

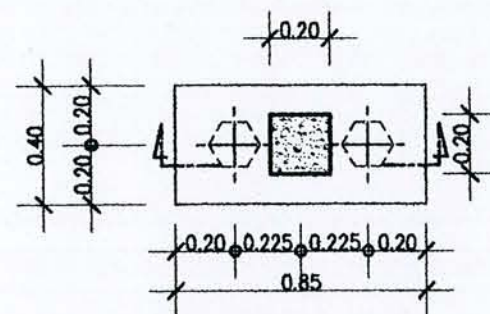


แบบขยาย F1

มาตราส่วน 1 : 25

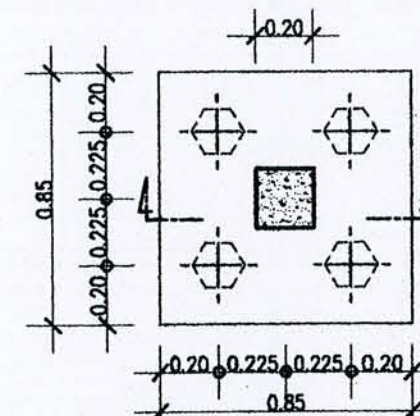


แบบขยาย F2


มาตราส่วน 1 : 25

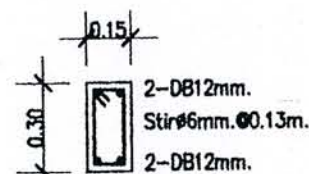


DETAIL CB2

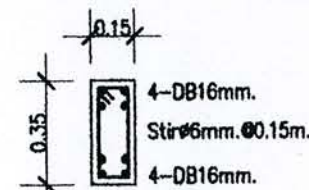

DETAIL B3

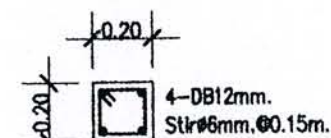


C1 ฐานราก - ทิ้งค่า

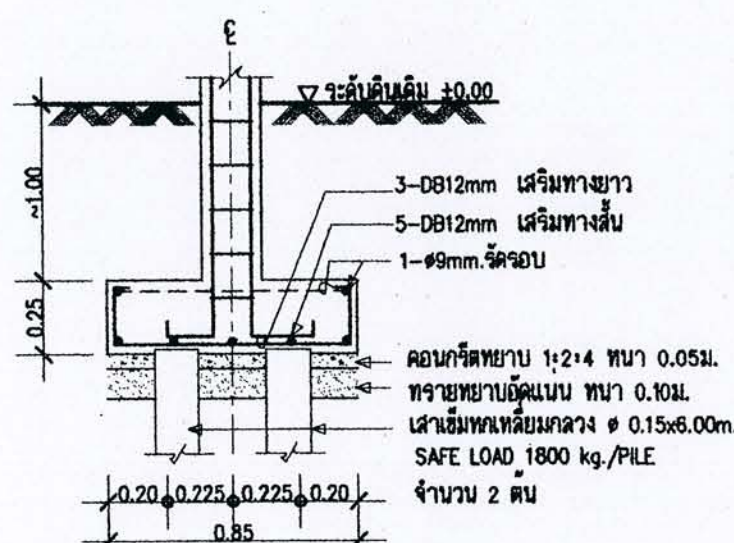


รูปตัด F1

มาตราส่วน 1 : 100

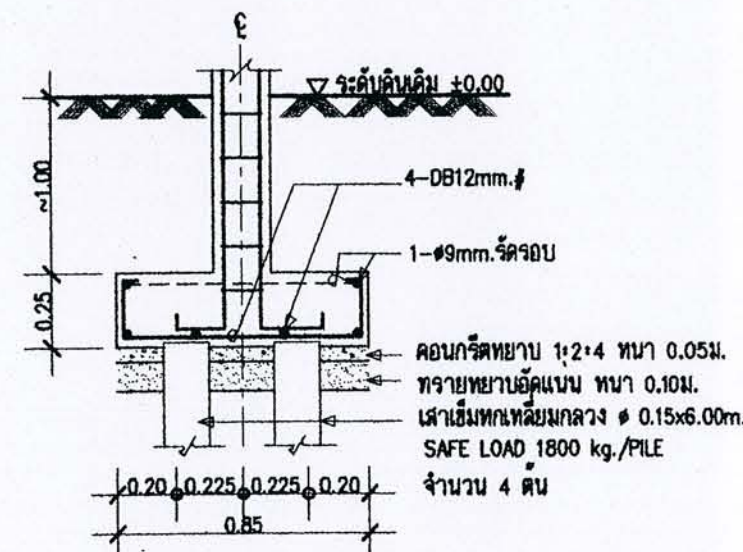


รูปตัด F2


มาตราส่วน 1 : 25

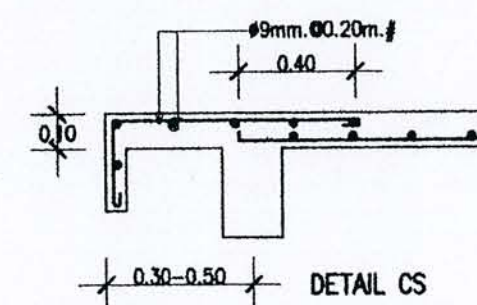





DETAIL CS

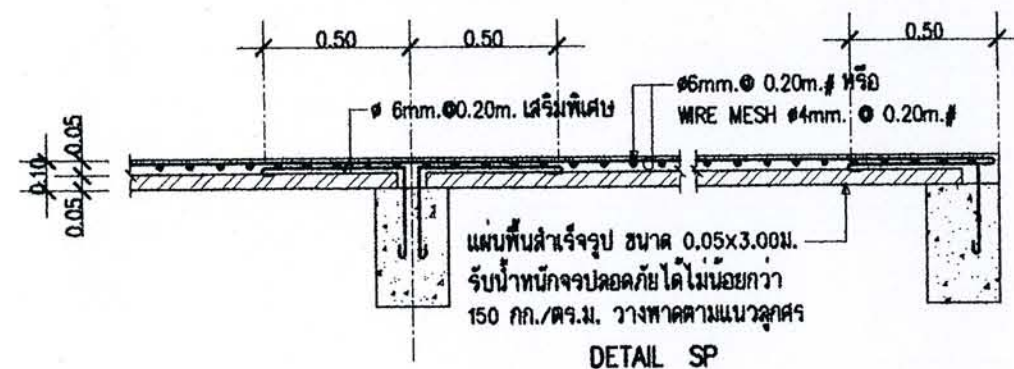


DETAIL SP

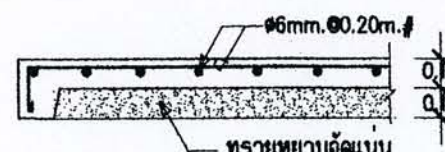


DETAIL GS

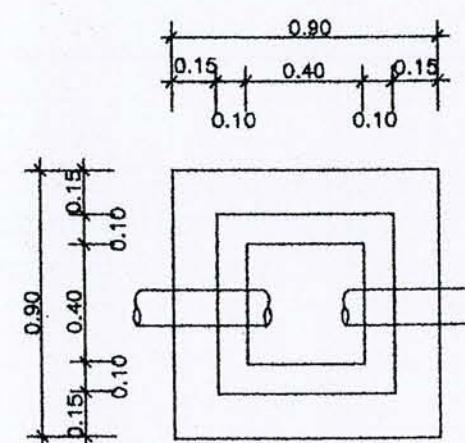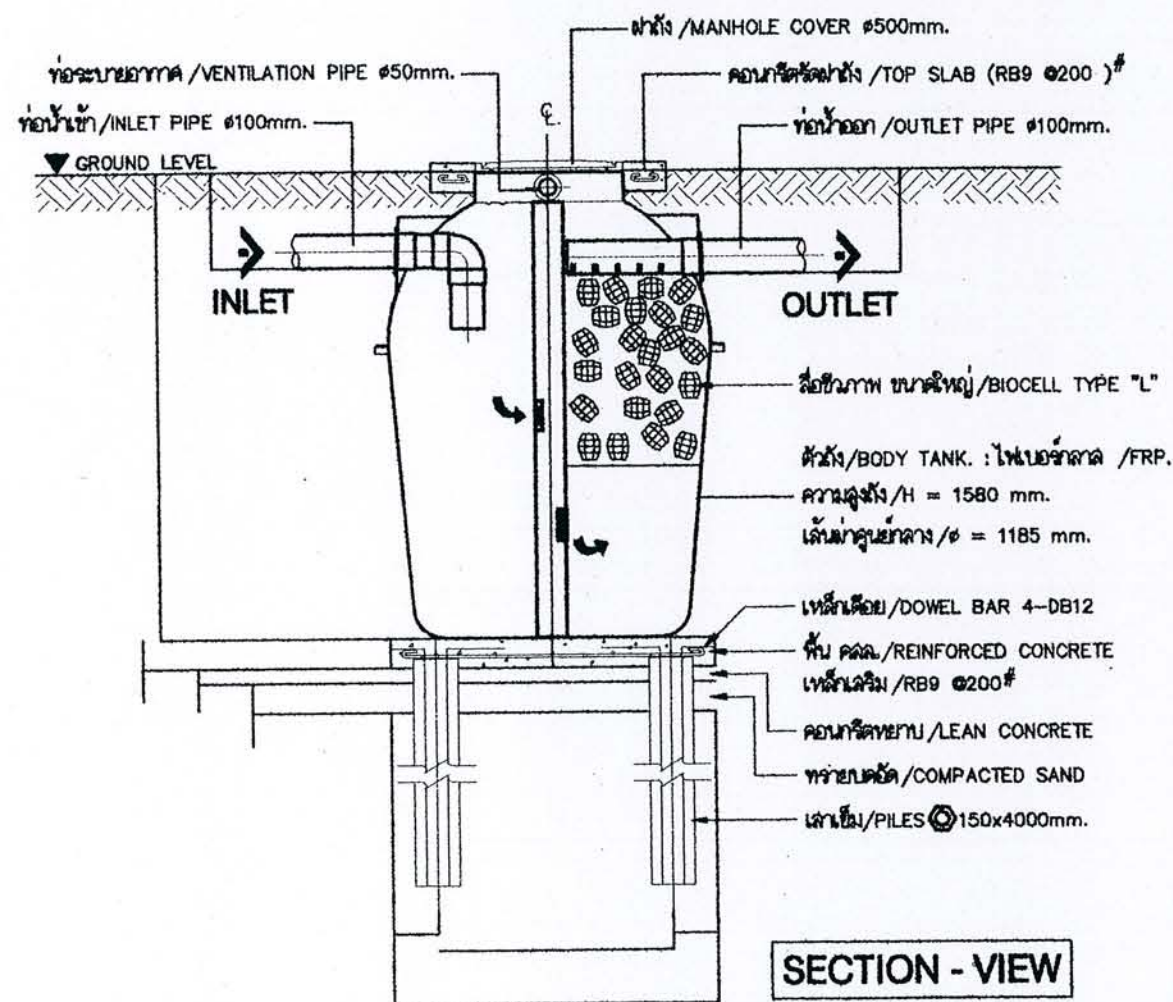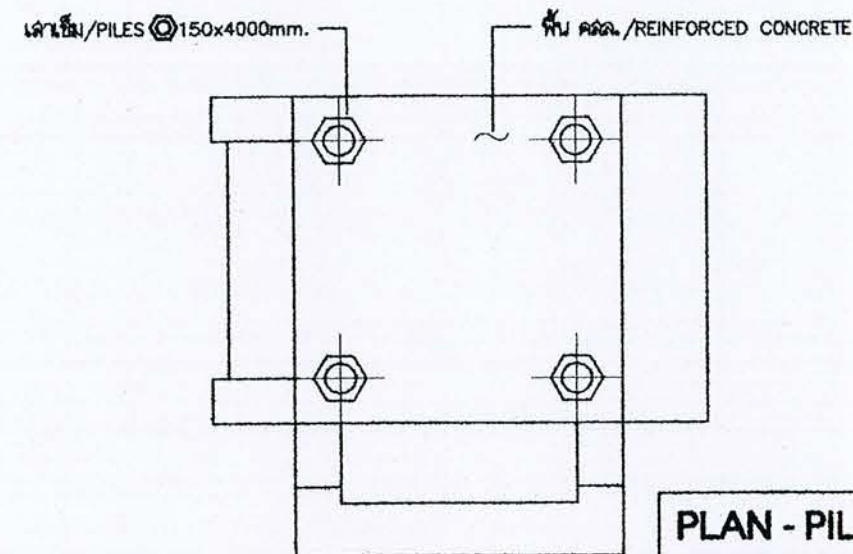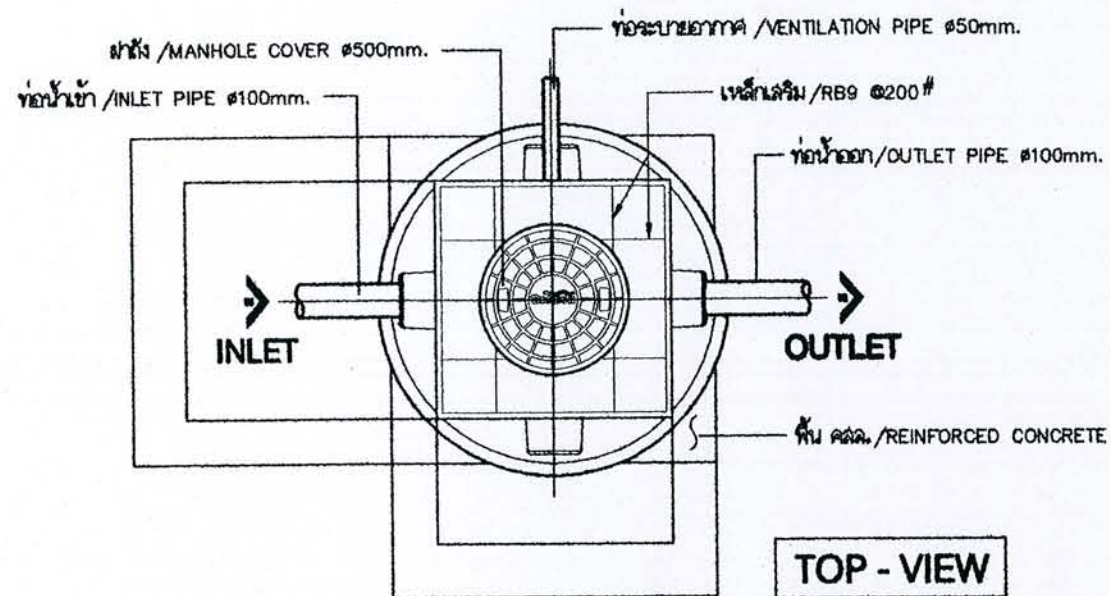


แปลนขยายบ่อพัก

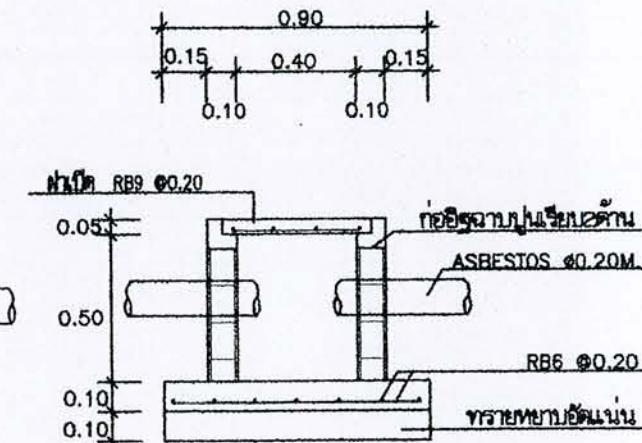

รูปตัดขยายบ่อพัก

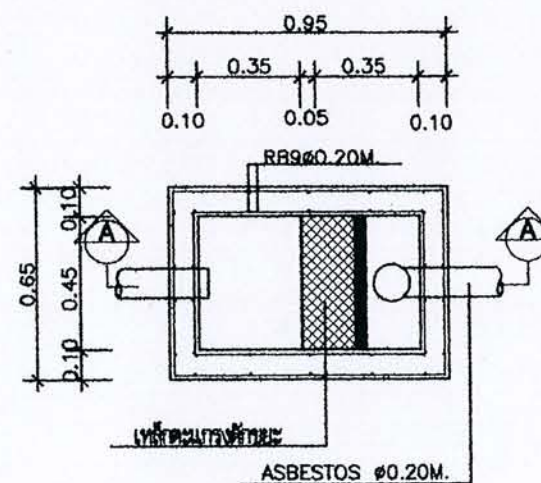

แปลนขยายบ่อดักขยะ

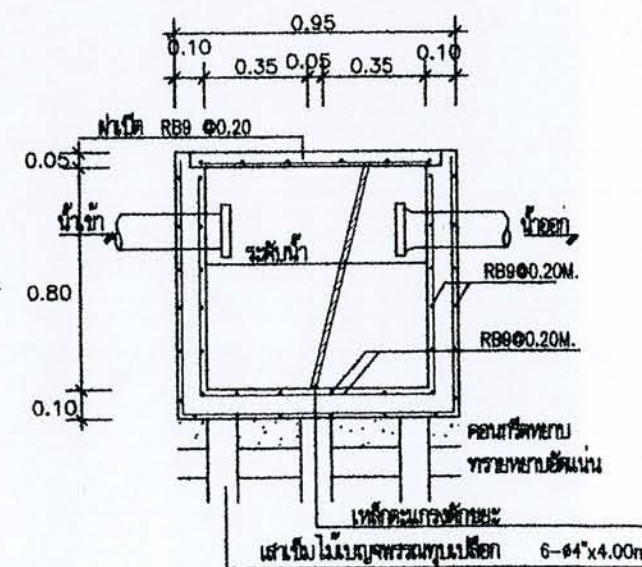

รูปตัดขยายบ่อดักขยะ

REMARK

PILING AND FOUNDATION DESIGN, SHALL BE DETERMINED OR OMITTED BASED ON ACTUAL SOIL BEARING CAPACITY BY CONSULTING WITH CIVIL ENGINEER.

การออกแบบและฐานรากให้ยึดตามผลการการรับน้ำหนักของดินที่หน้างาน ภายใต้การควบคุมและให้คำปรึกษาโดยวิศวกรโครงสร้าง



สำนักงานนโยบาย
และแผนทรัพยากรธรรมชาติและสิ่งแวดล้อม

โครงการ
แบบบ้านขี้เฒ่าเพื่อประชาชน

ตามนโยบาย

ม.ร.ว.สุขุมพันธุ์ บริพัตร ผู้ว่าราชการ
กรุงเทพมหานคร เศรษฐกิจพอเพียง
นายธีระวัฒน์ ชื่นชูชัยกิจ รองผู้ว่าราชการ
กรุงเทพมหานคร นายธีระวัฒน์ ชื่นชูชัยกิจ
นายธีระวัฒน์ ชื่นชูชัยกิจ

ผู้อำนวยการสำนักงานนโยบาย

นายสุเมธ ชื่นชูชัยกิจ

รองผู้อำนวยการสำนักงานนโยบาย

นายสุเมธ ชื่นชูชัยกิจ

ผู้อำนวยการสำนักงานนโยบาย

นายสุเมธ ชื่นชูชัยกิจ

ผู้อำนวยการสำนักงานนโยบาย

