



บ้านครอบครัวไทยเป็นสุข ๑

รายการแบบสถาปัตยกรรม (A)	รายการแบบโครงสร้าง (S)	รายการสัญลักษณ์ประกอบแบบ		
A-01 สารบัญแบบ,สัญลักษณ์ประกอบแบบ A-02 รายการประกอบแบบ A-03 ผังบริเวณ A-04 แปลนพื้น ,แปลนหลังคา A-05 รูปด้าน 1,2,3,4 A-06 รูปตัด A,B ,แบบขยายหลังคา A-07 แบบขยายห้องน้ำ ,แบบขยายประตู-หน้าต่าง	S-01 แปลนฐานราก เสา คานและพื้น ,แปลน โครงหลังคา S-02 แบบขยายการเสริมเหล็ก ฐานราก,คาน ,คาน และพื้น			
		① ใช้กำหนดหมายเลขประตู ในแบบเพื่ออ้างอิงถึง ② ใช้กำหนดหมายเลขหน้าต่าง ในแบบเพื่ออ้างอิงถึง 	โครงการแบบอาคารเพื่อประชาชน ครอบครัวไทยเป็นสุข แบบ บ้านครอบครัวไทยเป็นสุข 1	
	รายการแบบวิศวกรรมไฟฟ้า(E) E-01 สัญลักษณ์,รายละเอียด,DIAGRAM ,แปลน ไฟฟ้าแสงสว่าง		รายการแบบวิศวกรรมสุขาภิบาล(SN) SN-01 แปลนสุขาภิบาล ,สัญลักษณ์ ,แบบขยายห้องน้ำ	รายการแบบวิศวกรรมสุขาภิบาล(SN)
			รายการแบบวิศวกรรมสุขาภิบาล(SN) 	
			รายการแบบวิศวกรรมสุขาภิบาล(SN) 	
1. วัตถุประสงค์

กรมโยธาธิการและผังเมืองมีความประสงค์ทำการออกแบบอาคารเพื่อประชาชนตามดำริของ
พจนานายกรัฐมนตรี และเป็นไปตามนโยบายรัฐบาลเพื่อบริการประชาชน โดยไม่คิดค่าบริการ
ออกแบบใดๆทั้งสิ้น

2. รายละเอียดประกอบแบบ

2.1 การวางผังและระดับ

ผู้รับจ้างจะต้องทำการวางผังระดับมาตรฐานให้ถูกต้องเรียบร้อยตามกฎหมายควบคุมอาคาร
ก่อนดำเนินการต่อไป

2.2 งานฐานรากและโครงสร้าง ค.ส.ล.

ตามที่ได้กำหนดไว้ในแบบและรายการวิศวกรรมโครงสร้าง ส่วนรายละเอียดอื่นๆ ให้ดำเนินการ
ตามมาตรฐานงานก่อสร้าง มยธ.101-มยธ.106

2.3 งานสถาปัตยกรรม

ก. งานพื้น

- พื้น ค.ส.ล. ทำผิวขัดมันเรียบ หรือผิวขัดหยาบ
ใช้ปูนซีเมนต์ตามมาตรฐาน เลขที่ มอก.15 เล่มที่ 1-2532
- พื้น ค.ส.ล. ปูกระเบื้องเคลือบผิวด้าน ขนาด 8"x8" หรือ 12"x12" ตามแบบระบุ
ใช้กระเบื้องเซรามิกผิวเคลือบด้าน ตามมาตรฐาน มอก. 37-2529 นํ้ายากันซึม ใช้ของ
ที่ผลิตในประเทศ
- พื้น ค.ส.ล. ปูไม้เนื้อแข็ง 1"x4" สีเข้มน้ำ
ใช้ไม้เนื้อแข็ง เช่น ไม้มะค่า ไม้แดง หรือไม้เต็ง 1"x4" อบเข้าเส้นยึดสนิท ขัดให้เรียบ
แล้วเคลือบด้วยนํ้ายาเคลือบเงาไม้ บัวเชิงผนังใช้บัวไม้ขนาด 3/4"x4"

หมายเหตุ การเตรียมผิวพื้นและการปูกระเบื้องให้ทำตามมาตรฐานวิชาชีพช่างที่ดี

ข. งานผนัง

- ผนังทั่วไปก่ออิฐฉาบปูนครึ่งแผ่น อิฐต้องเป็นอิฐที่แกร่ง เสาสุกเสมอ ไม่บิดเบี้ยว
ต้องพรมนํ้าให้ชุ่มก่อนก่อ
- การก่อชนคาน เสา หรือเอ็น ค.ส.ล. ต้องเสียบเหล็ก 6 มม. ทุกระยะไม่เกิน 40 ซม.
โดยยื่นออกมา 25 ซม. และฝังในเสา คาน 10 ซม.
- การก่อชนกันเป็นมุม การก่อวงช่อสำหรับประตูหน้าต่าง และทุกระยะเกิน 2 ม. ตาม
ความยาวของผนังหรือทุกระยะเกิน 3 ม. ให้ทำเอ็น หรือทับหลัง ค.ส.ล. หน้าทำผนัง
กว้าง 15 ซม. เสียบเหล็ก 2 RB 6 มม. @ 0.20 ม.

ค. งานฝ้า

- ฝ้าเพดานแผ่นยิปซัมบอร์ดหนา 9 มม. ชนิดมีแผ่นอลูมิเนียมฟอยล์ ชนิดธรรมดา ชนิดกัน
ความชื้น ผลิตในประเทศตามมาตรฐาน มอก. เลขที่ 219-2524 ยานวรอยต่อด้วย
พลาสติกยิปซัม โครงโครงเหล็กชุบสังกะสี @ 0.40x1.00 หรือ 1.20 ม.
- ฝ้าชายคไม้เนื้อแข็ง 1/2"x2" เว้นร่อง 0.5 ซม. โครงโครงไม้เนื้อแข็ง 1 1/2"x3"
@ 0.60 ม. มอบฝ้าไม้เนื้อแข็ง 3/4"x2" ภายในบุตาข่ายกันแมลง

ง. งานหลังคา

- โครงหลังคา ตามที่ได้กำหนดไว้ในแบบและรายการวิศวกรรมโครงสร้าง
- วัสดุหลังคา กระเบื้องคอนกรีต ที่ผลิตภายในประเทศ

จ. งานประตู-หน้าต่าง และอุปกรณ์

- รายละเอียดตามระบุในแบบขยายประตู-หน้าต่าง และอุปกรณ์
- ติดตั้งมุ้งลวดในช่อง กรอบบานอลูมิเนียมสีดํา

ฉ. งานท่อนํ้า-ส้วม และสุขภัณฑ์

- รายละเอียดตามระบุในแบบขยายท่อนํ้า-ส้วม สุขภัณฑ์ และอุปกรณ์ประกอบ
- การเดินท่อนํ้าประปา-ท่อนํ้าทิ้ง-ท่อนํ้าส้วม ให้เป็นไปตามงานวิศวกรรมสุขาภิบาล

ช. งานสี

- งานทาสีภายนอก สีทาผนังปูนใช้สีอะครีลิก 100%
สีทาภายนอกเหล็กและไม้ ใช้สีน้ำมันตาม มอก. 327-2538
- งานทาสีภายใน สีทาผนังปูนใช้สีน้ำตาม มอก. 272-2531

หมายเหตุ วัสดุต่างๆดังกล่าวข้างต้น สามารถเปลี่ยนแปลงได้ตามความเหมาะสมและวัตถุประสงค์
ของผู้ว่าจ้าง

2.4 งานวิศวกรรมสุขาภิบาล

ให้ติดตั้งตามแบบวิศวกรรมสุขาภิบาลและมาตรฐานการประปาฯ

2.4 งานวิศวกรรมไฟฟ้า

ให้ติดตั้งตามแบบวิศวกรรมไฟฟ้าและมาตรฐานการไฟฟ้าฯ



โครงการแบบอาคารเพื่อประชาชน

ครอบครัวไทยเป็นสุข

แบบ

บ้านครอบครัวไทยเป็นสุข 1

สำนักสถาปัตยกรรม

ผู้ควบคุมการก่อสร้าง

สถาปัตย์กรรม

สถาปัตย์กรรม

นายธนวรรณ์ ชลวิวัฒน์ สถาปัตย์

สถาปัตย์

สถาปัตย์

สำนักวิศวกรรมโครงสร้างและงานระบบ

ผู้ควบคุมการก่อสร้าง

วิศวกรรม

วิศวกรรม

โครงสร้าง

โครงสร้าง

วิศวกรรมไฟฟ้า

วิศวกรรม

และเครื่องกล

และเครื่องกล

วิศวกรรม

วิศวกรรม

สุขาภิบาล

สุขาภิบาล

ปี 2561

ปี 2561

อนุมัติ

อนุมัติ

(นายสว่าง ศรีสุคนธ์)

อธิบดีกรมโยธาธิการและผังเมือง

แสดงแบบ

รายการประกอบแบบ

มาตรฐาน

วัน/เดือน/ปี 21 พ.ย. 2546

เลขที่แบบ ม.บ.462119

แผ่นที่


A-02

จำนวนแผ่น



7

หมายเหตุ แบบที่แสดงอยู่นี้ได้รับการยืมส่วน เพื่อใช้แสดงผลทางหน้าจอเท่านั้น สำหรับแบบที่ใช้ขออนุญาตก่อสร้าง ให้ถ่ายสำเนาจากหนังสือแบบบ้าน

หมายเหตุ แบบที่แสดงอยู่นี้ได้รับการย่อส่วน เพื่อใช้แสดงผลทางหน้าจอเท่านั้น สำหรับแบบที่ใช้ขออนุญาตก่อสร้าง ให้ถ่ายสำเนาจากหนังสือแบบบ้าน

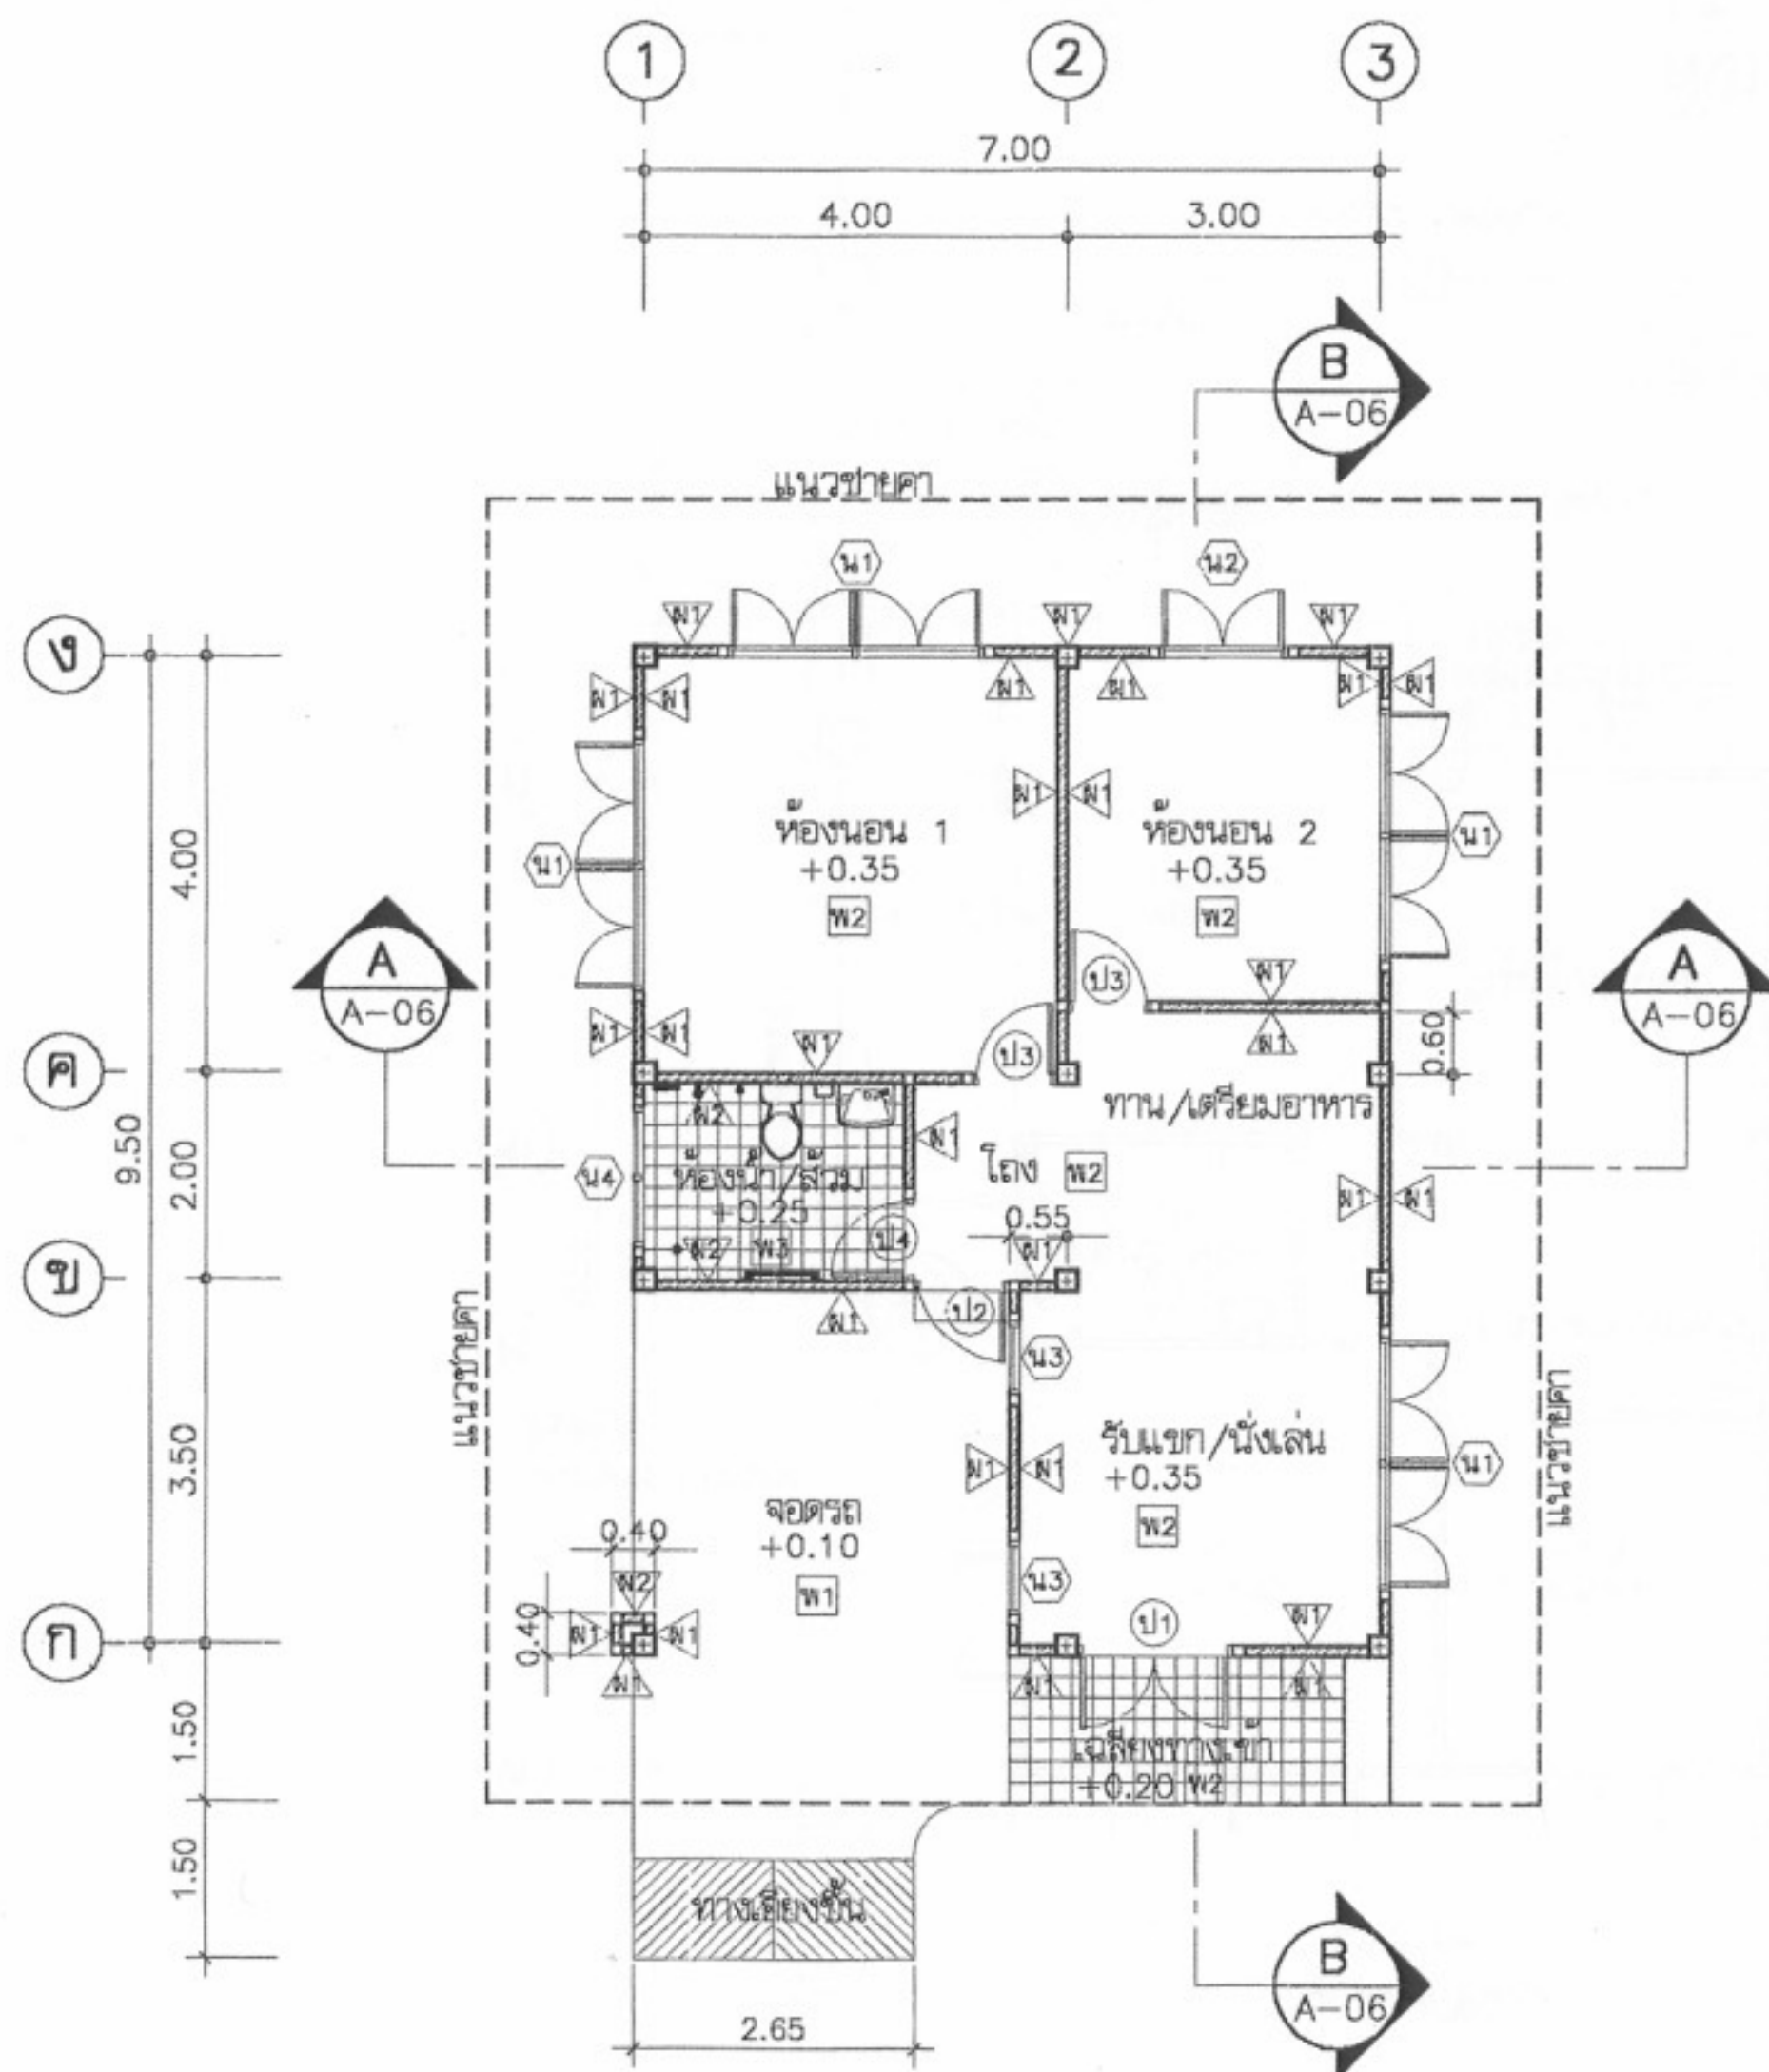


แปลนพื้นที่ 1
มาตราส่วน 1:100

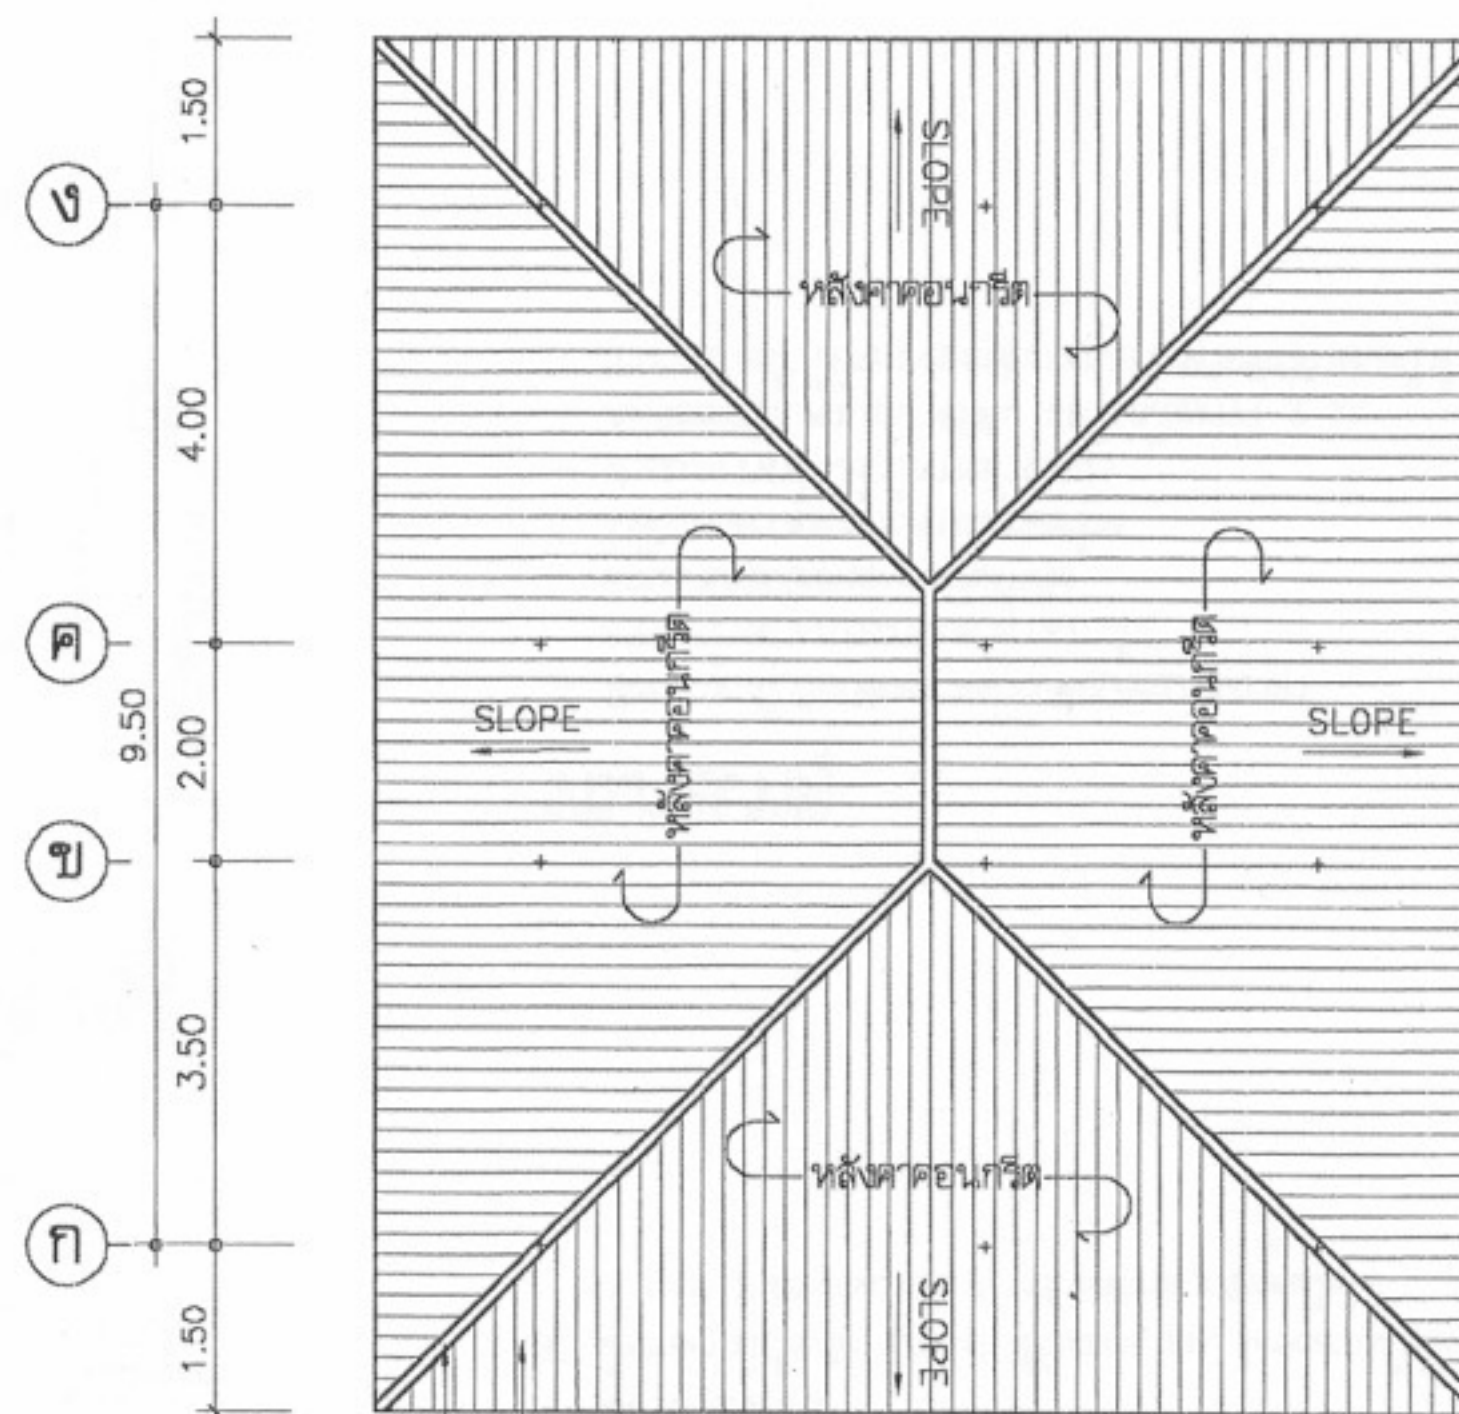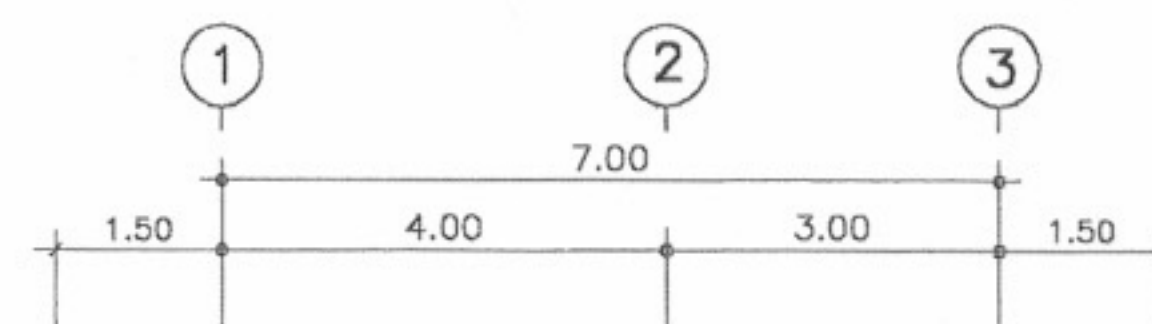

หลังคากระเบื้องคอนกรีต
ครอบหลังคากระเบื้องคอนกรีต
ติดด้วยใบหลังคา

แปลนหลังคา
มาตราส่วน 1:100

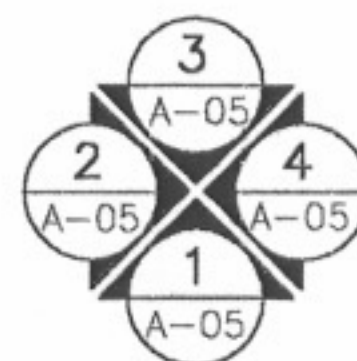

โครงการแบบอาคารเพื่อประชาชน

ครอบครัวไทยเป็นสุข

แบบ

บ้านครอบครัวไทยเป็นสุข 1

สำนักสถาปัตยกรรม

ผู้ดำเนินการหลัก

สถาปนิก

สถาปนิก

นายสมรรณ ชลวิวัฒน์สถาปนิก

สถาปนิก

สถาปนิก

สำนักวิศวกรรมโครงสร้างและงานระบบ

ผู้ดำเนินการหลัก

วิศวกร

วิศวกร

โครงสร้าง

วิศวกร

วิศวกรรมไฟฟ้า

วิศวกร

และเครื่องกล

วิศวกร

วิศวกรรม

วิศวกร

สุขาภิบาล

วิศวกร

อนุมัติ

(นายสว่าง ศรีสกุล)

อธิบดีกรมโยธาธิการและผังเมือง

แสดงแบบ

แปลน

มาตราส่วน 1:100

วัน/เดือน/ปี 21 พ.ย. 2546

เลขที่แบบ ม.บ.462119


แผ่นที่

A-04


จำนวนแผ่น

7


หมายเหตุ แบบที่แสดงอยู่นี้ได้รับการยืมส่วน เพื่อใช้แสดงผลทางหน้าจอเท่านั้น สำหรับแบบที่ใช้ขออนุญาตก่อสร้าง ให้ถ่ายสำเนาจากหนังสือแบบบ้าน

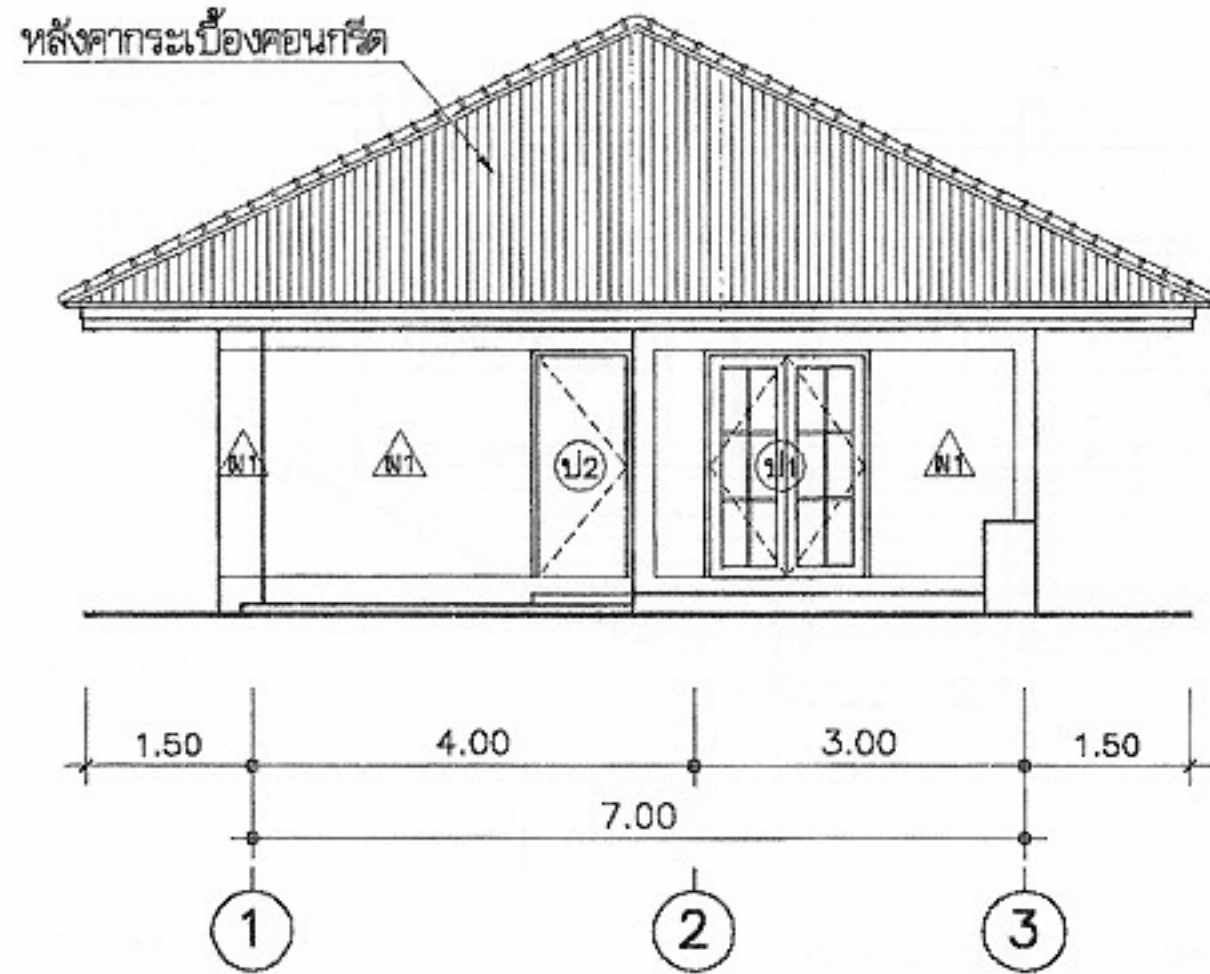


รูปด้าน 1
มาตราส่วน 1:100

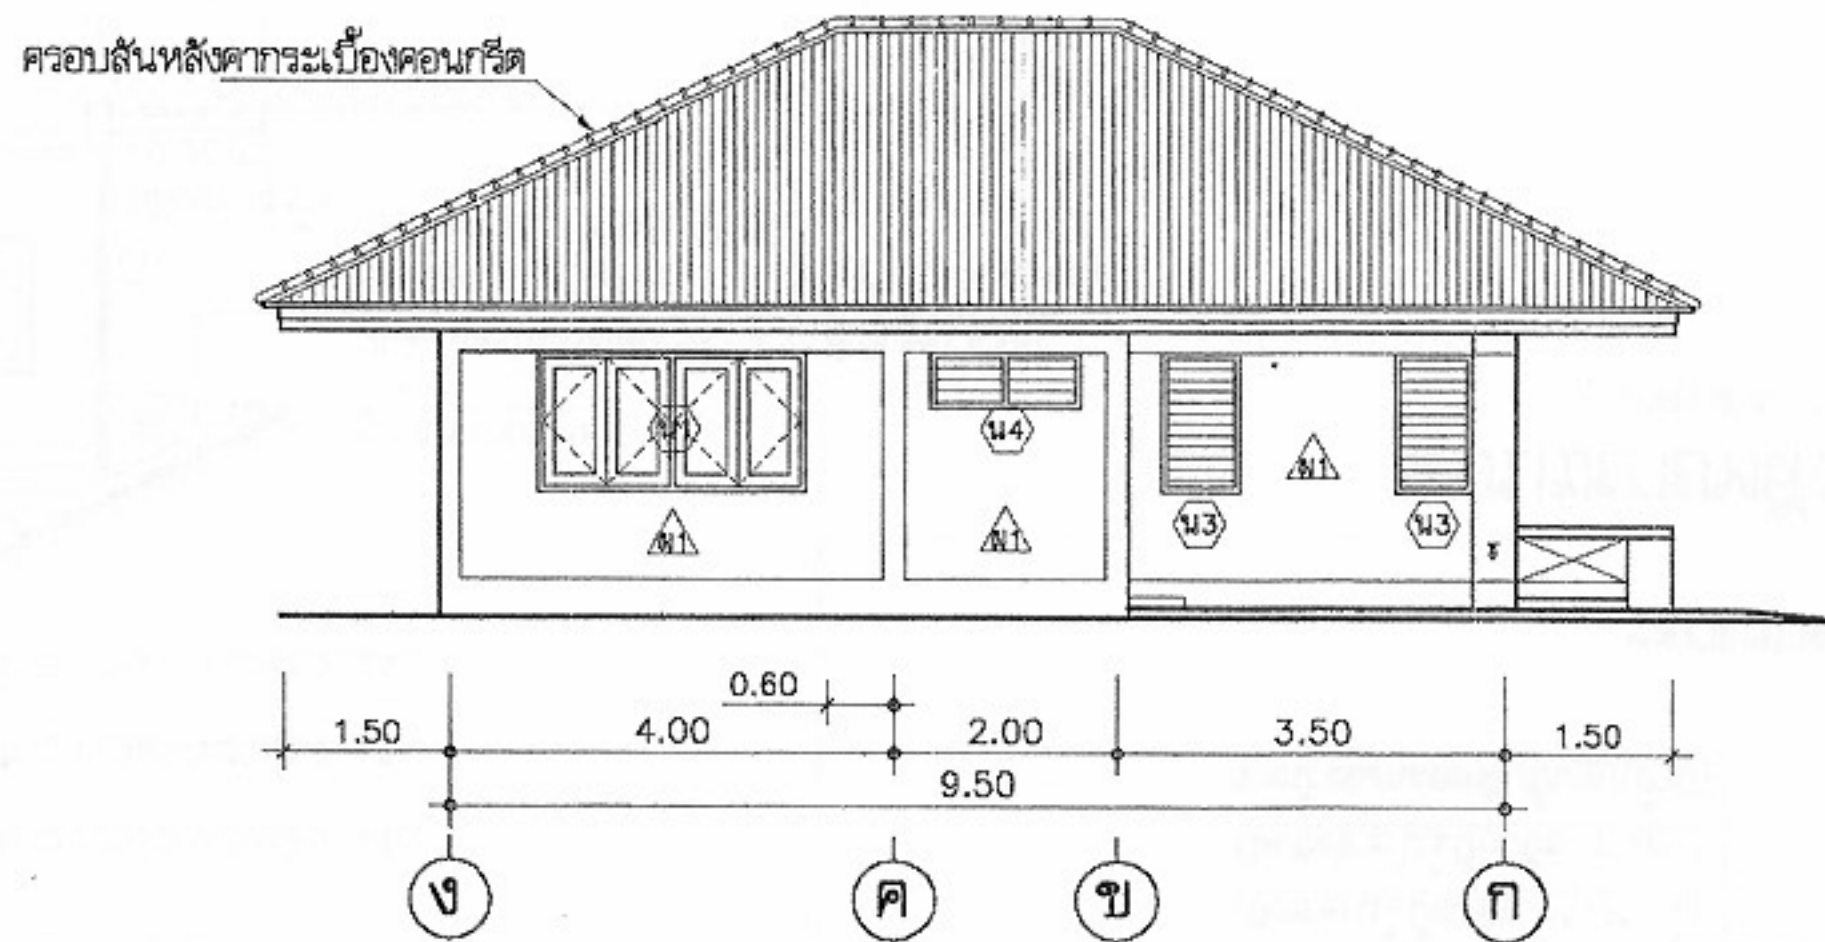

รูปด้าน 2
มาตราส่วน 1:100

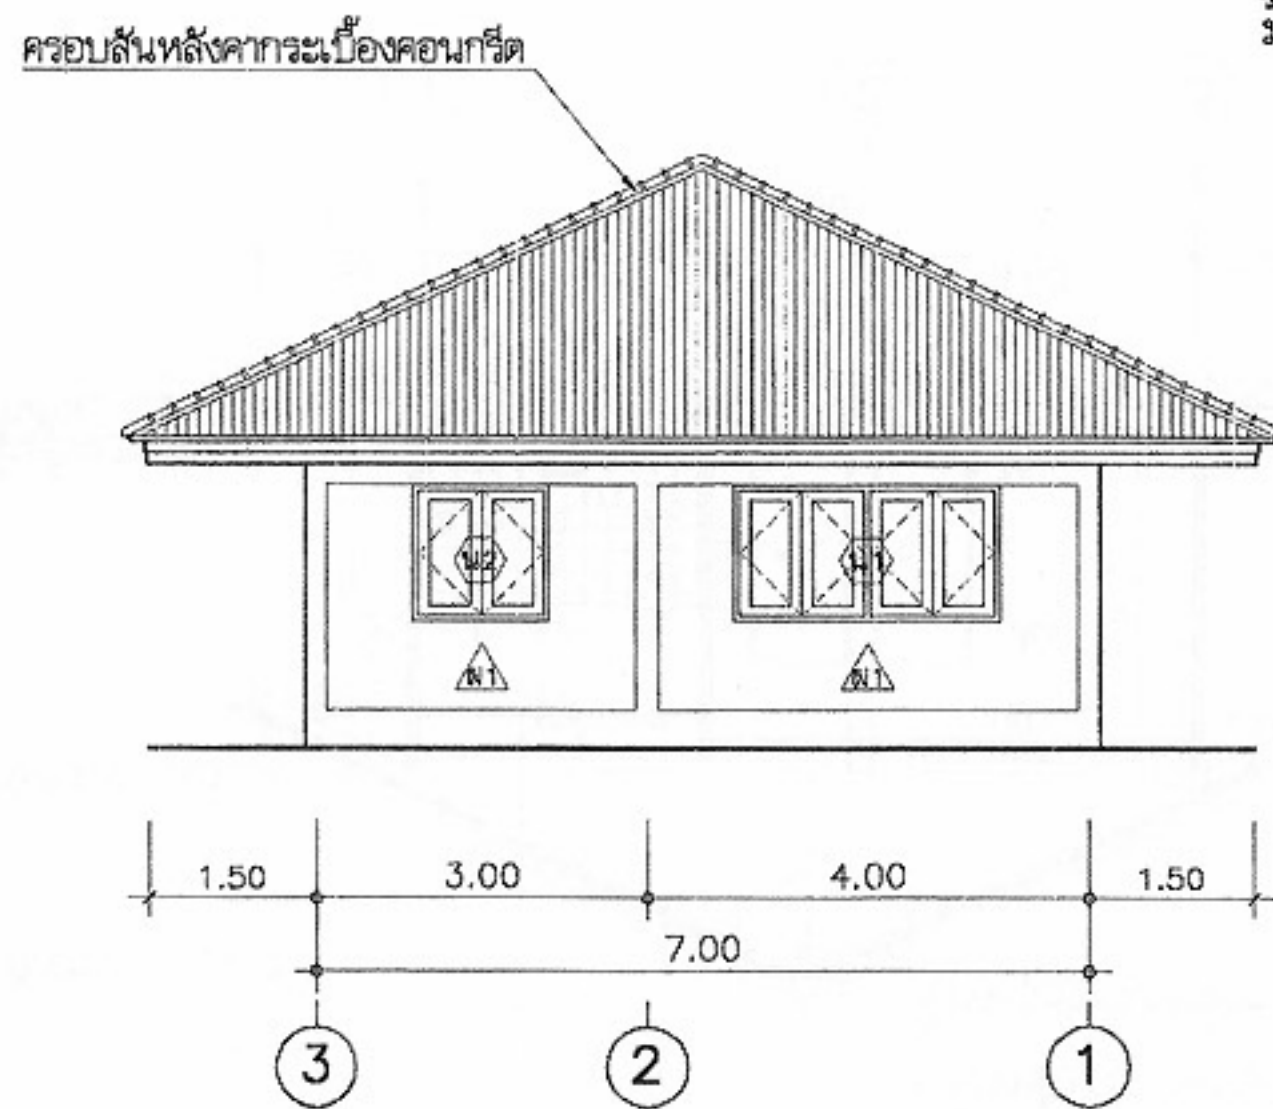

รูปด้าน 3
มาตราส่วน 1:100

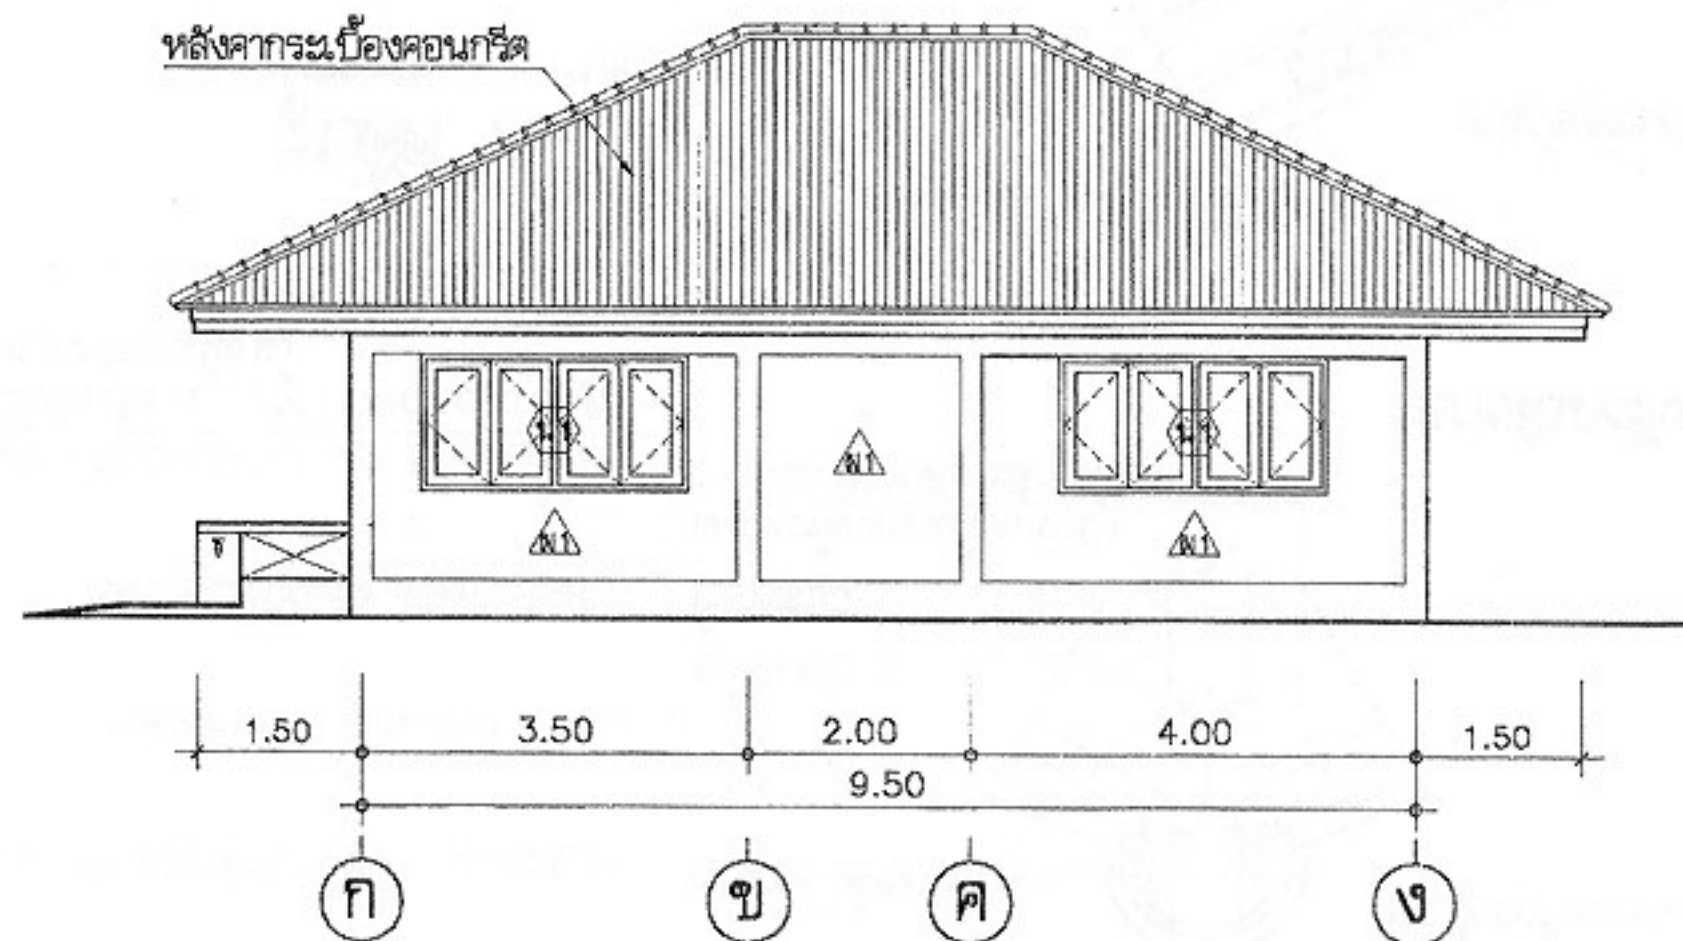

รูปด้าน 4
มาตราส่วน 1:100



โครงการแบบอาคารเพื่อประชาชน
ครอบครัวไทยเป็นสุข

แบบ

บ้านครอบครัวไทยเป็นสุข 1

สำนักสถาปัตยกรรม

สถาปนิก

ผู้อำนวยการสำนัก

นายสมรรถ ชลวดีวัฒน์ สถาปนิก

สถาปนิก

สถาปนิก

สำนักวิศวกรรมโครงสร้างและงานระบบ

วิศวกรรม

โครงสร้าง

วิศวกรรมไฟฟ้า

และเครื่องกล

วิศวกรรม

สุขาภิบาล

อนุมัติ

(นายสว่าง ศรีสุกัน)
อธิบดีกรมโยธาธิการและผังเมือง

แสดงแบบ

รูปด้าน 1,2,3,4

มาตราส่วน 1:100

วัน/เดือน/ปี 21 พ.ย. 2546

เลขที่แบบ ม.บ.462119





แผ่นที่

A-05

จำนวนแผ่น

7

หมายเหตุ แบบที่แสดงอยู่นี้ได้รับการยืมส่วน เพื่อใช้แสดงผลทางหน้าจอเท่านั้น สำหรับแบบที่ใช้ขออนุญาตก่อสร้าง ให้ถ่ายสำเนาจากหนังสือแบบบ้าน

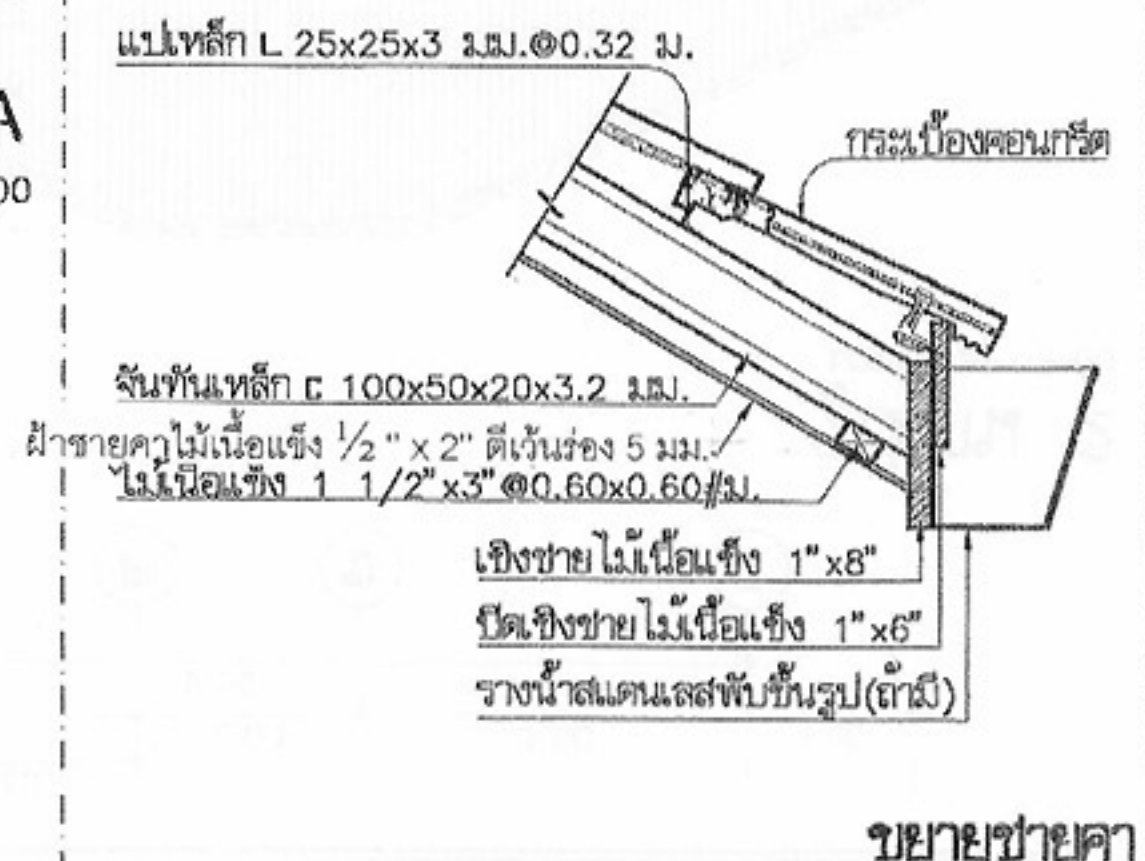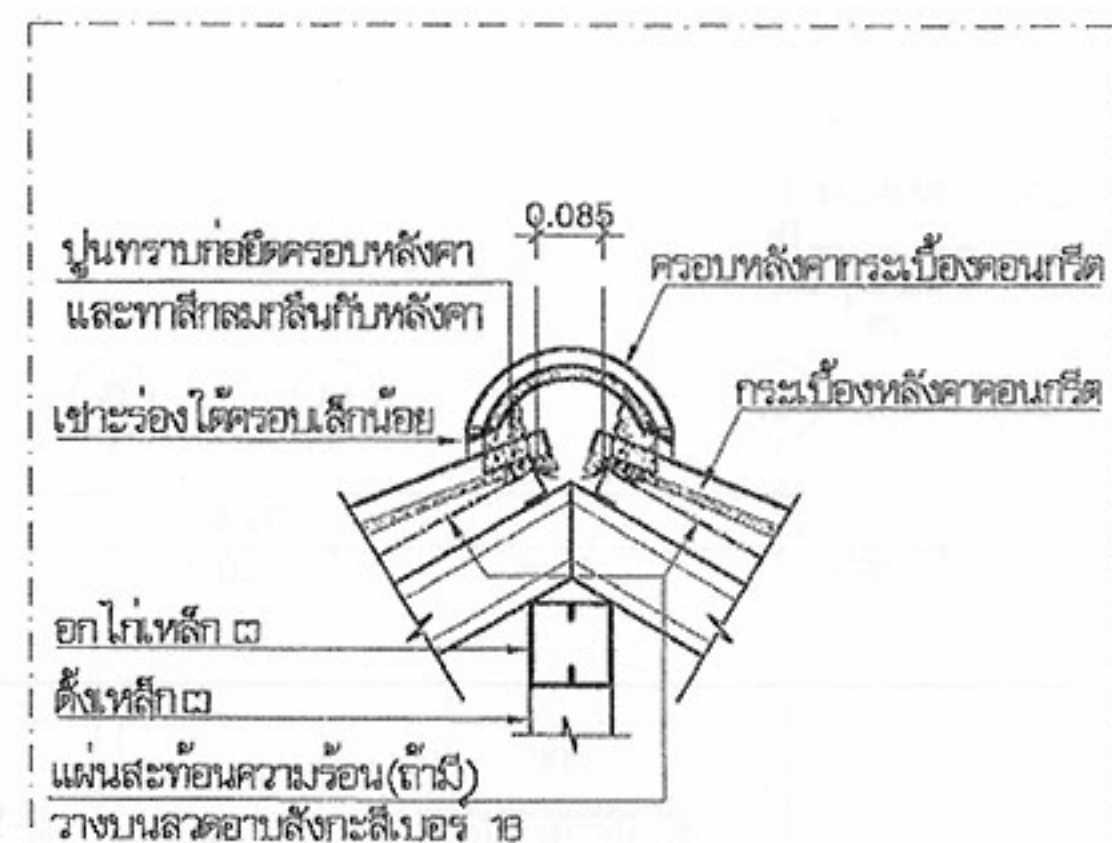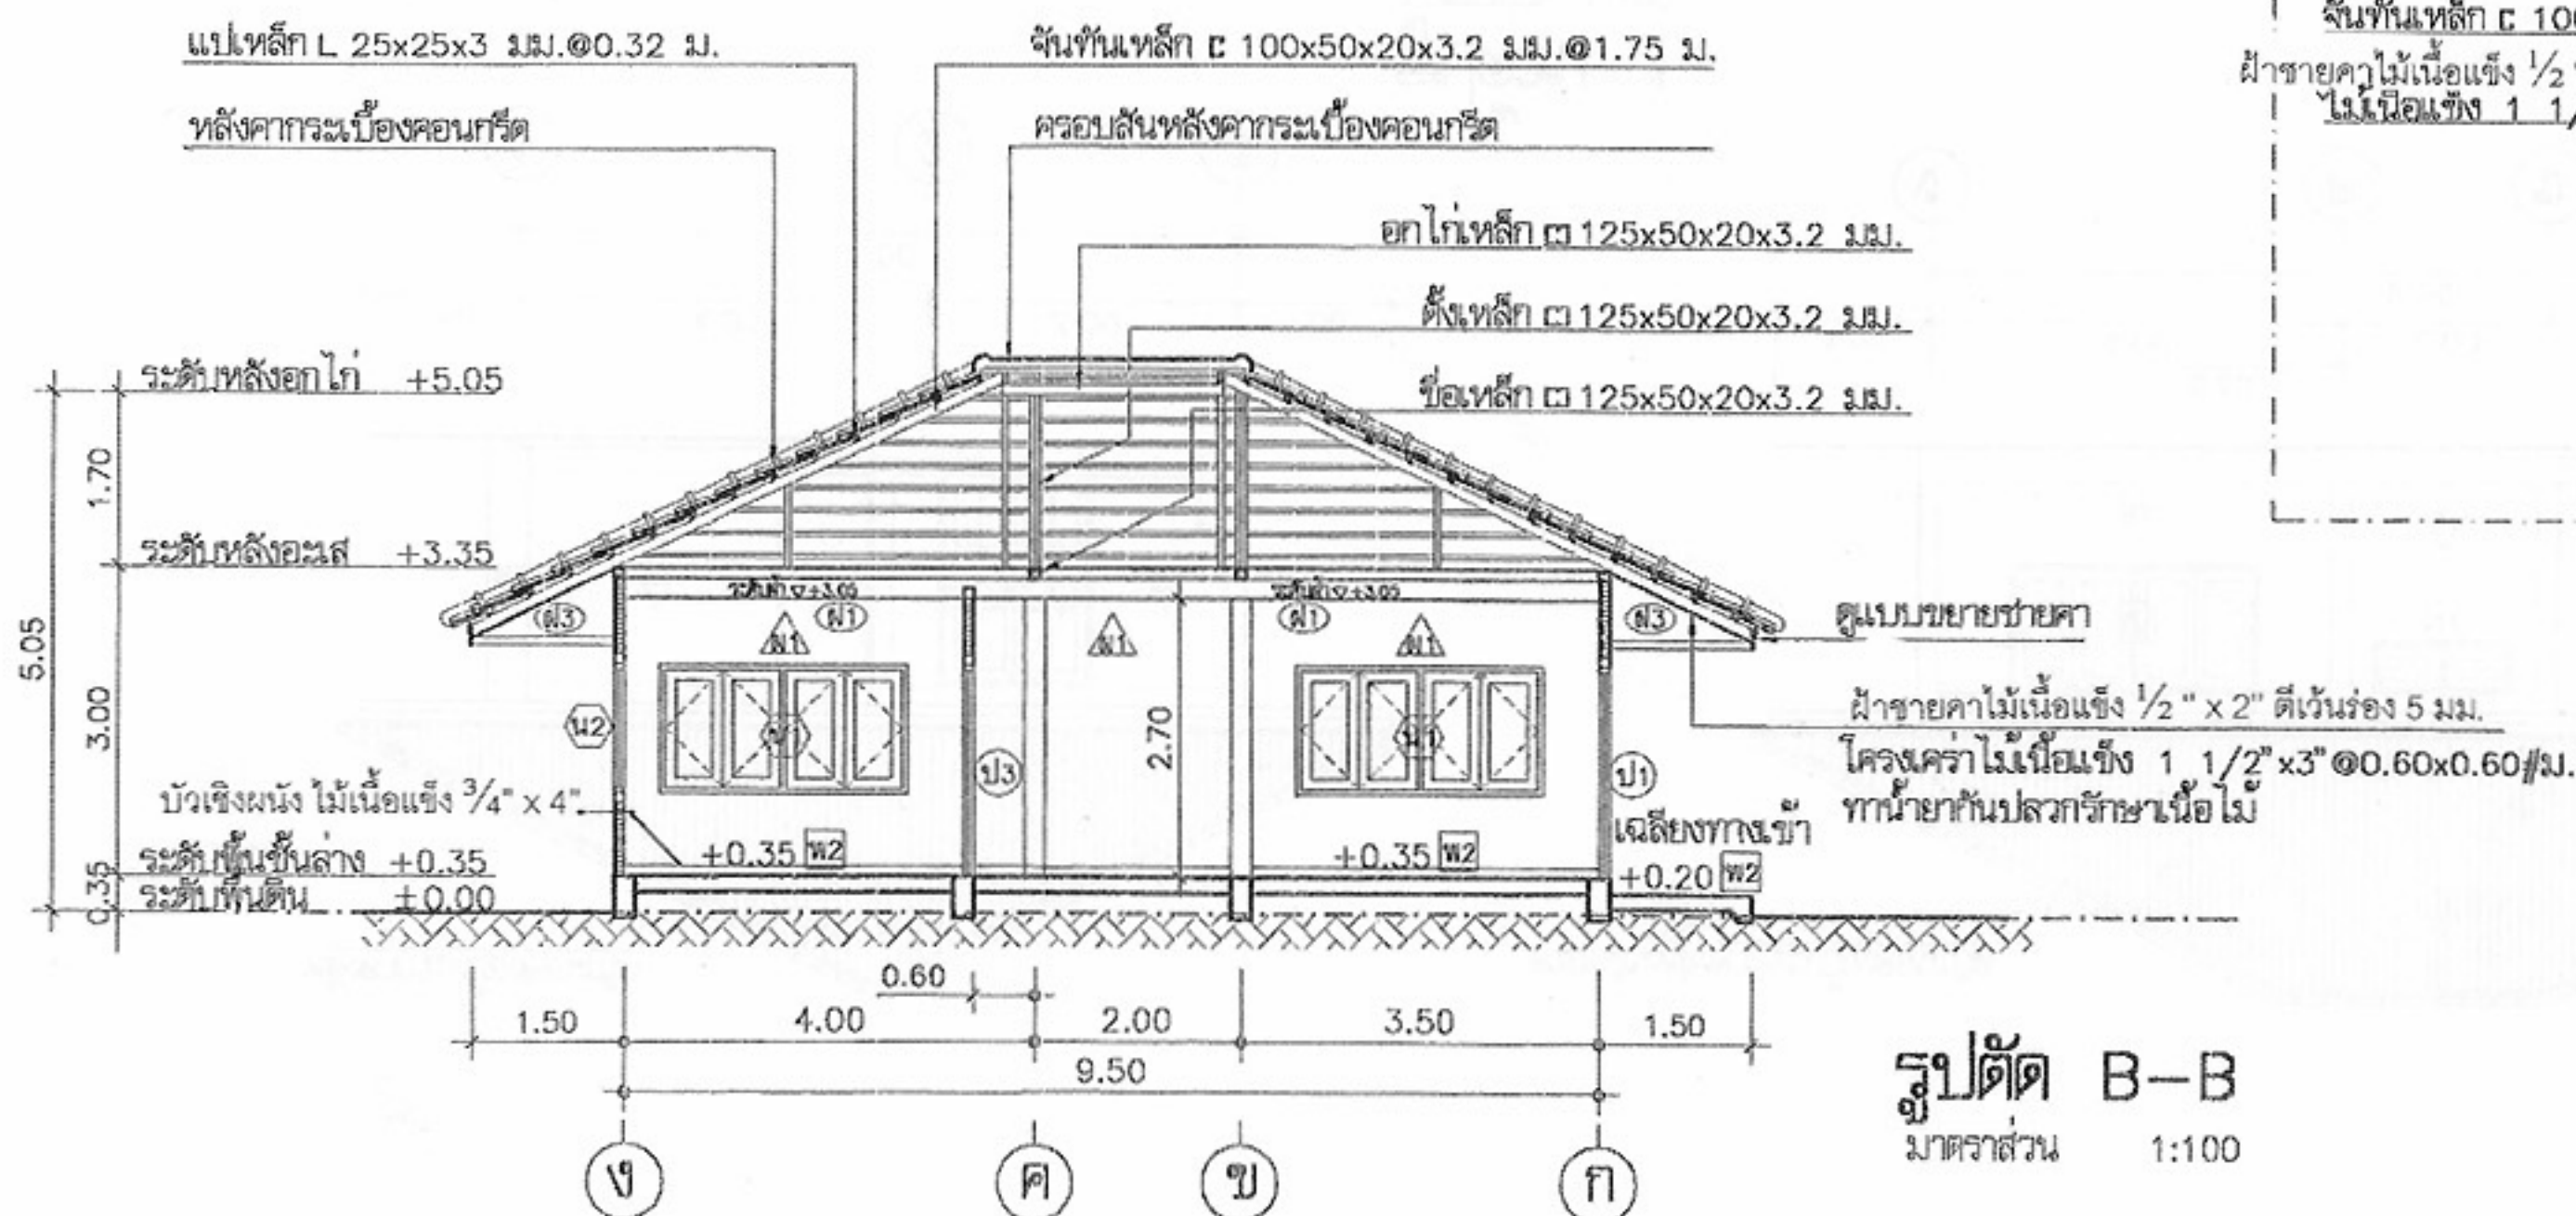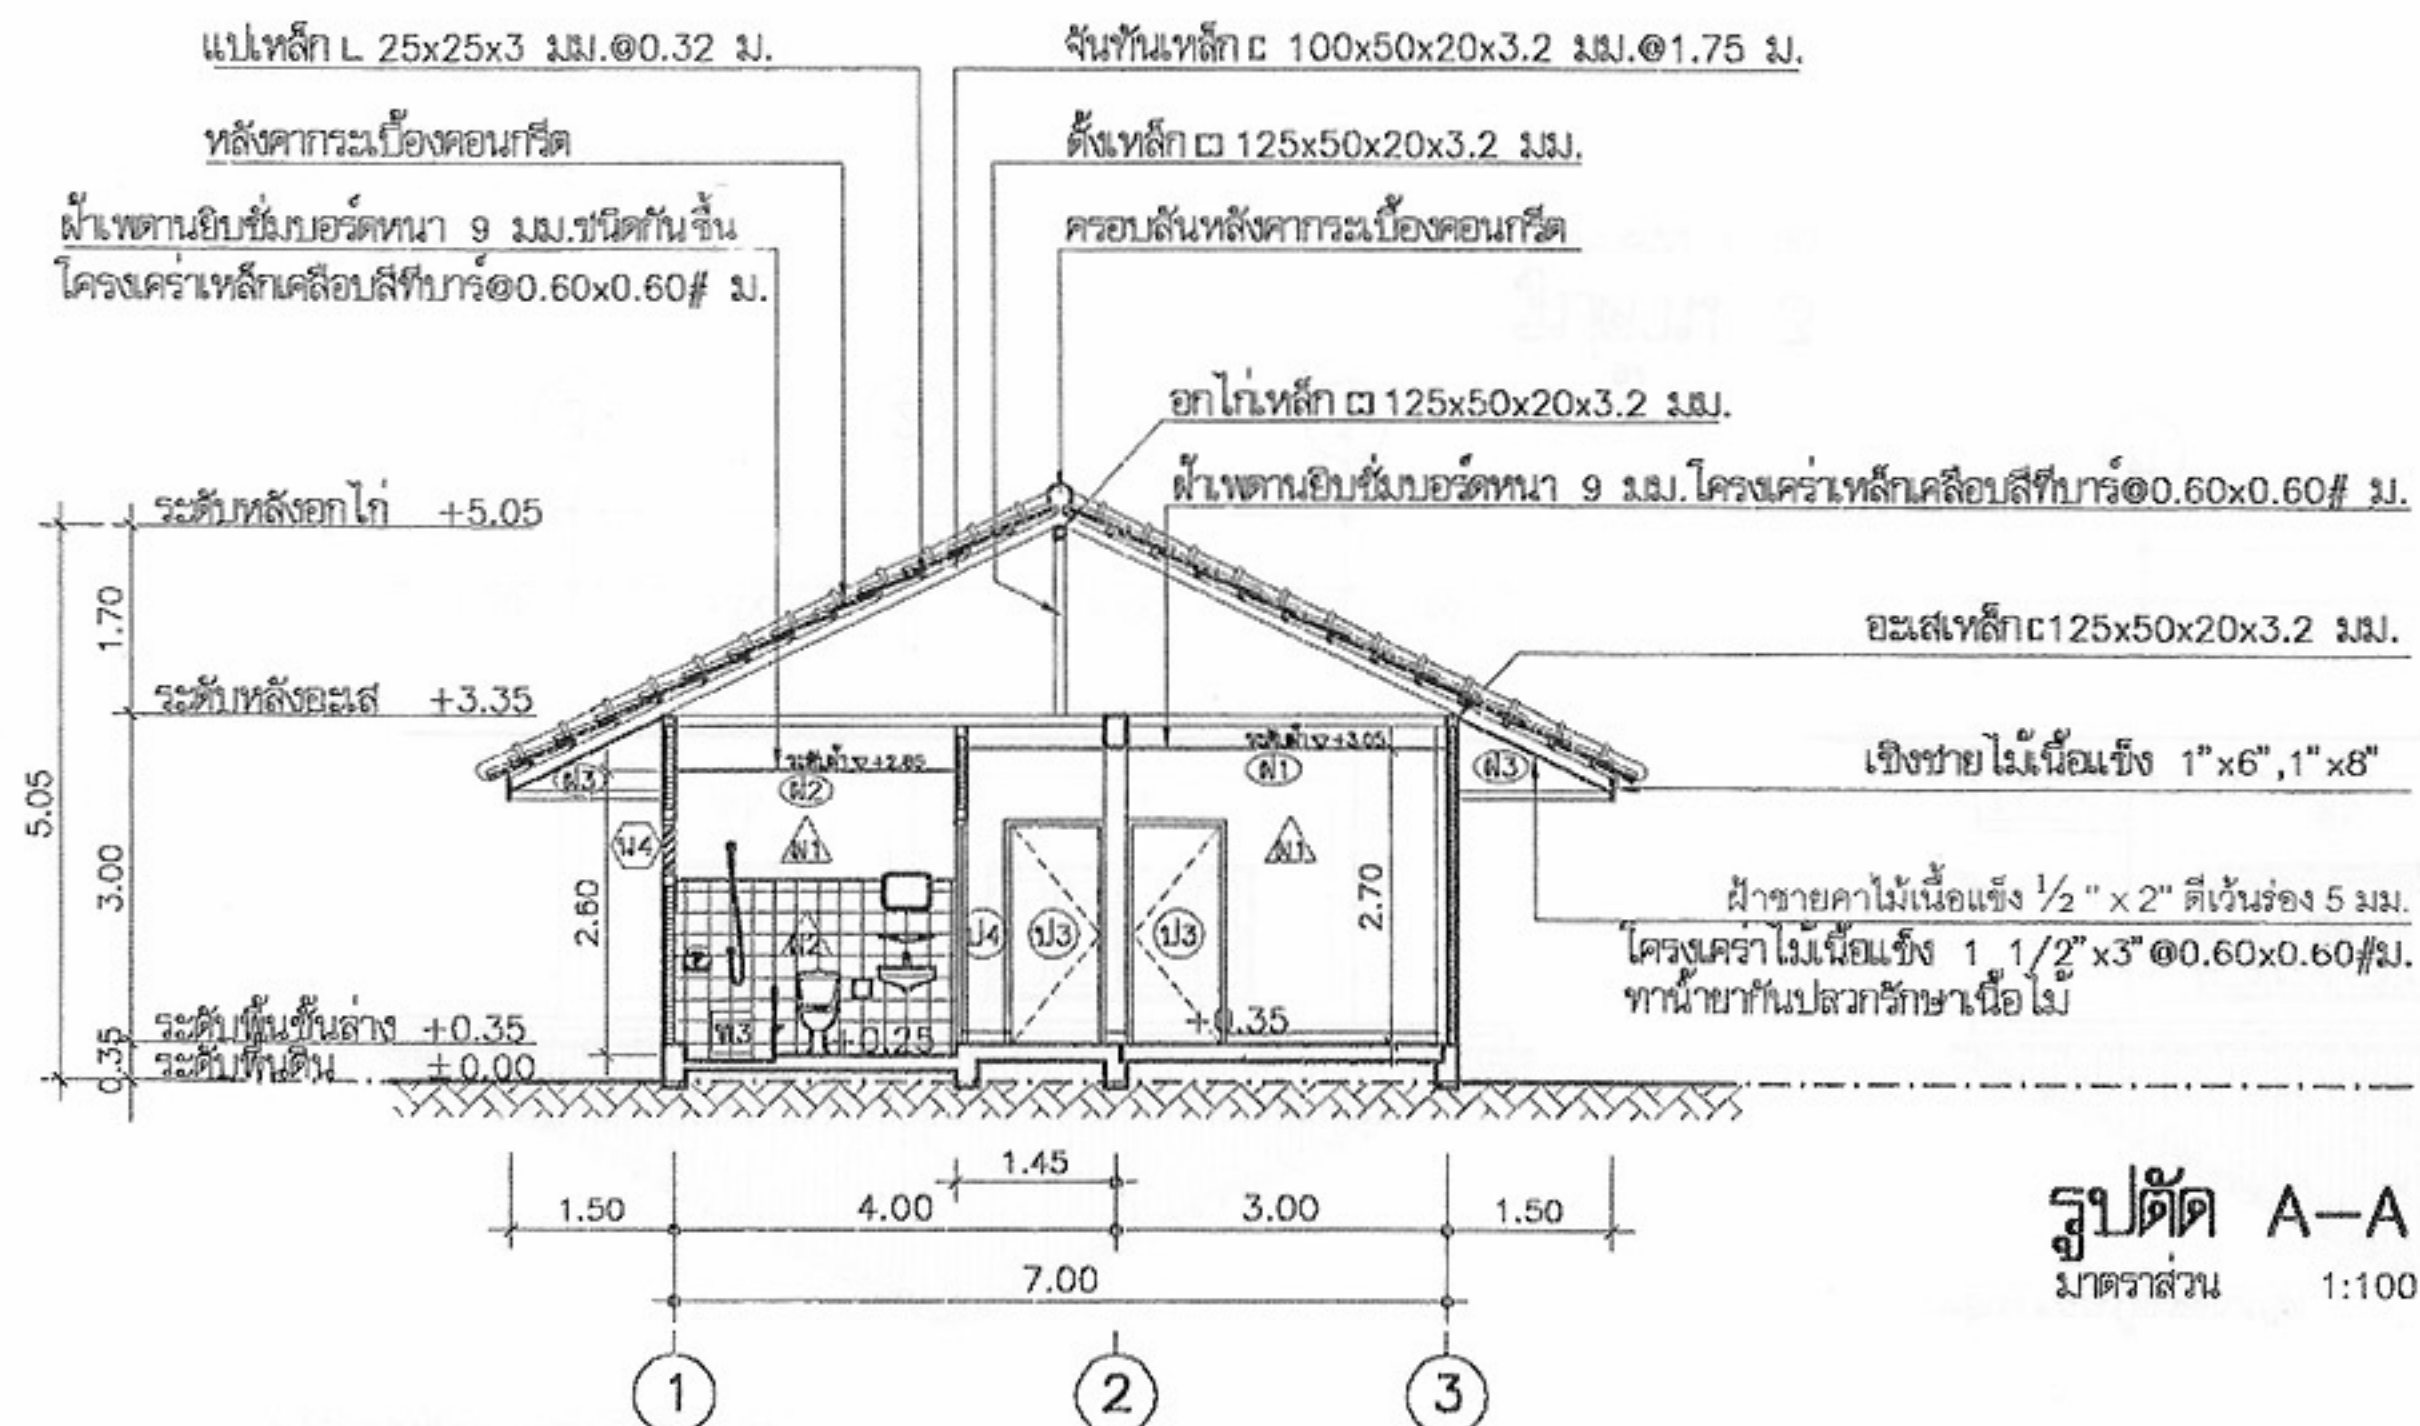

แบบขยายหลังคา
มาตราส่วน 1:10



โครงการแบบอาคารเพื่อประชาชน
ครอบครัวไทยเป็นสุข

แบบ
บ้านครอบครัวไทยเป็นสุข 1


สำนักสถาปัตย์กรรม
สถาปัตย์กรรม
นายสมรรถ ชาญวิทย์ สถาปัตย์
สถาปัตย์
สถาปัตย์

สำนักวิศวกรรมโครงสร้างและงานระบบ
วิศวกร
โครงสร้าง
วิศวกรไฟฟ้า
และเครื่องกล
วิศวกร
สุขาภิบาล

อนุมัติ
(นายสว่าง ศิริสุนทร)
อธิบดีกรมโยธาธิการและผังเมือง


แสดงแบบ
รูปตัดแบบขยายหลังคา

มาตราส่วน 1:100
วัน/เดือน/ปี 21 พ.ย. 2546
เลขที่แบบ ม.บ.462119
แผ่นที่ A-06 จำนวนแผ่น 7

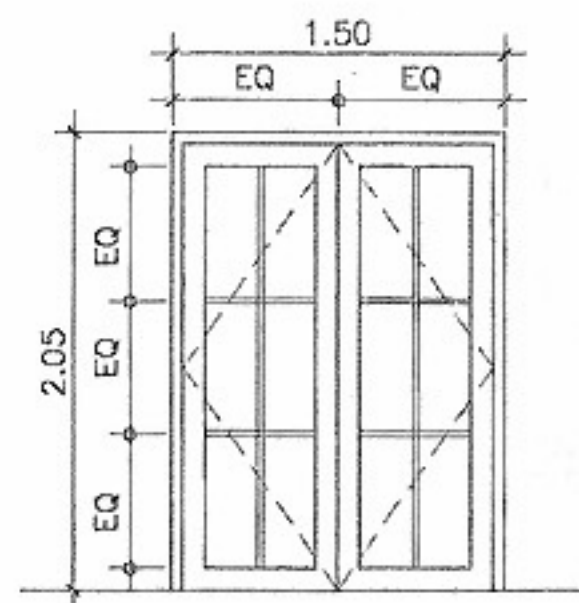


ป1

วงกบไม้เนื้อแข็ง 2" x 4"
กรอบบาน ไม้สัก 1 1/2" x 4"
ลูกฟักกระจกใส

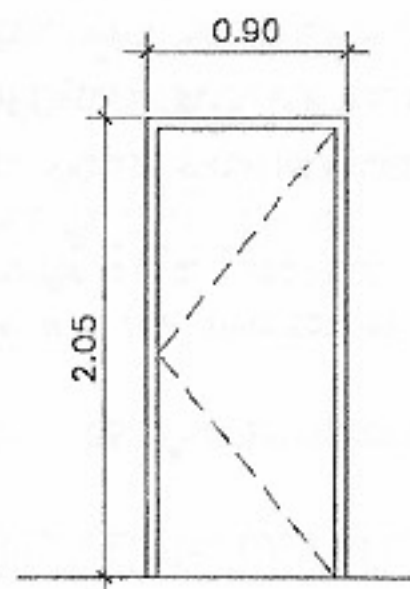


ป2

วงกบไม้เนื้อแข็ง 2" x 4"
บาน ไม้ยูคาลิปตัสชนิดกันน้ำ
ชนิดใช้ภายนอก

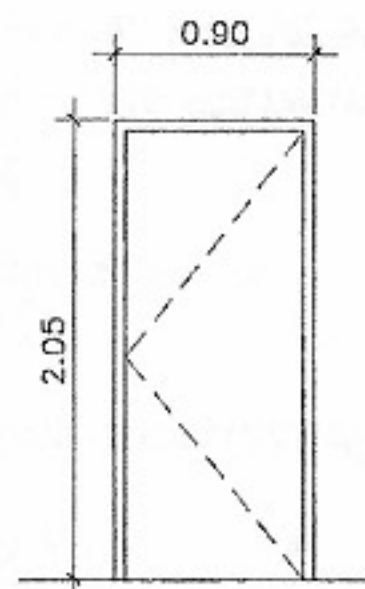


ป3

วงกบไม้เนื้อแข็ง 2" x 4"
บาน ไม้ยูคาลิปตัส

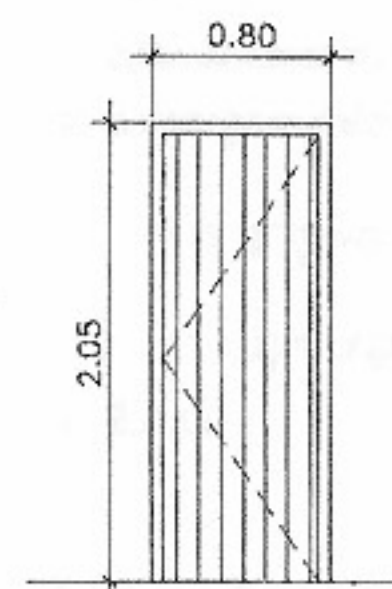


ป4

วงกบPVC
บานประตูPVC

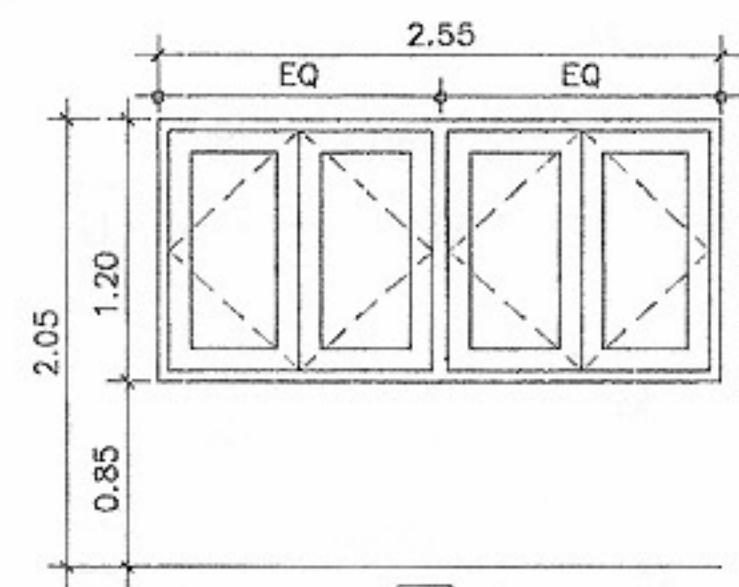


น1

วงกบอลูมิเนียม
กรอบบานอลูมิเนียม
ลูกฟักกระจกใส

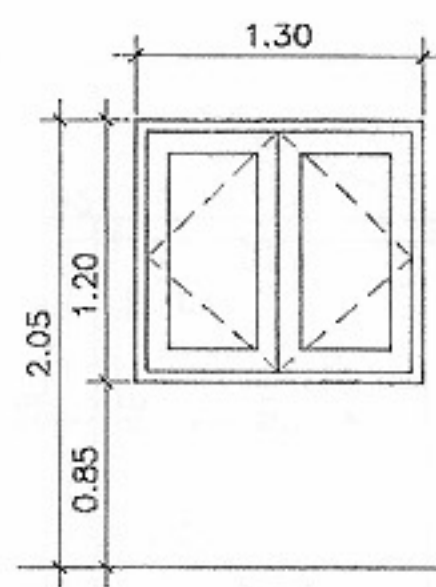


น2

วงกบอลูมิเนียม
กรอบบานอลูมิเนียม
ลูกฟักกระจกใส

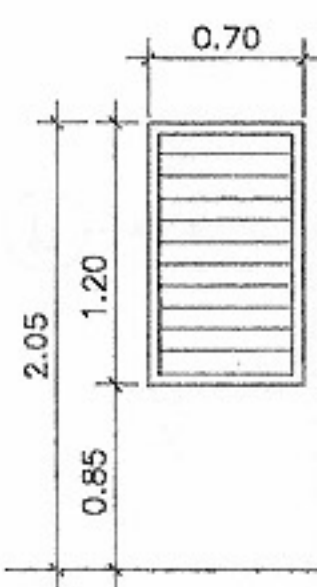


น3

วงกบอลูมิเนียม
เกล็ดกระจกใสปรับมุมได้

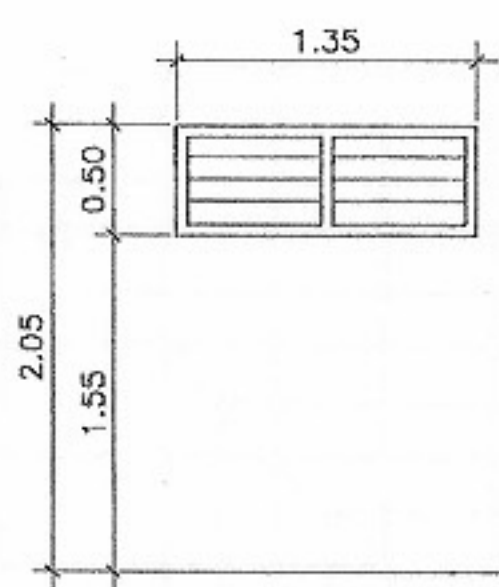


น4

วงกบอลูมิเนียม
เกล็ดกระจกฝ้าปรับมุมได้

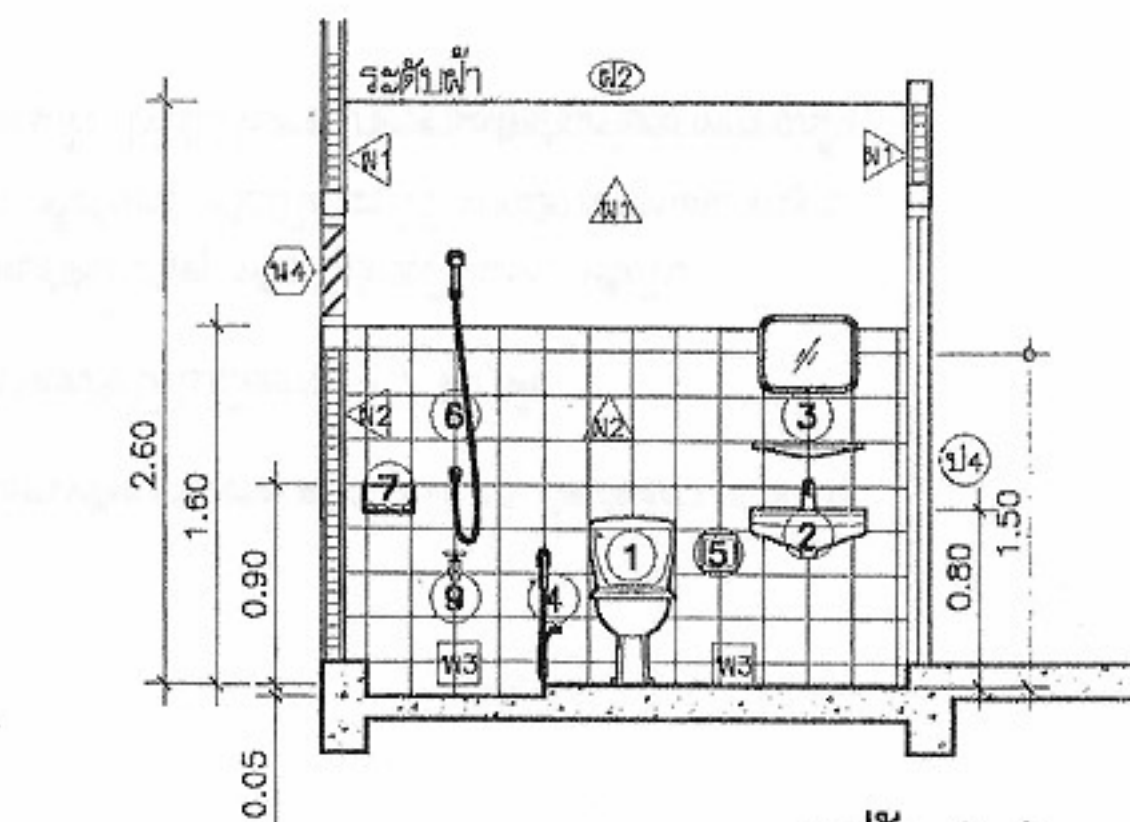

รูปตัด A-A

มาตราส่วน 1:50

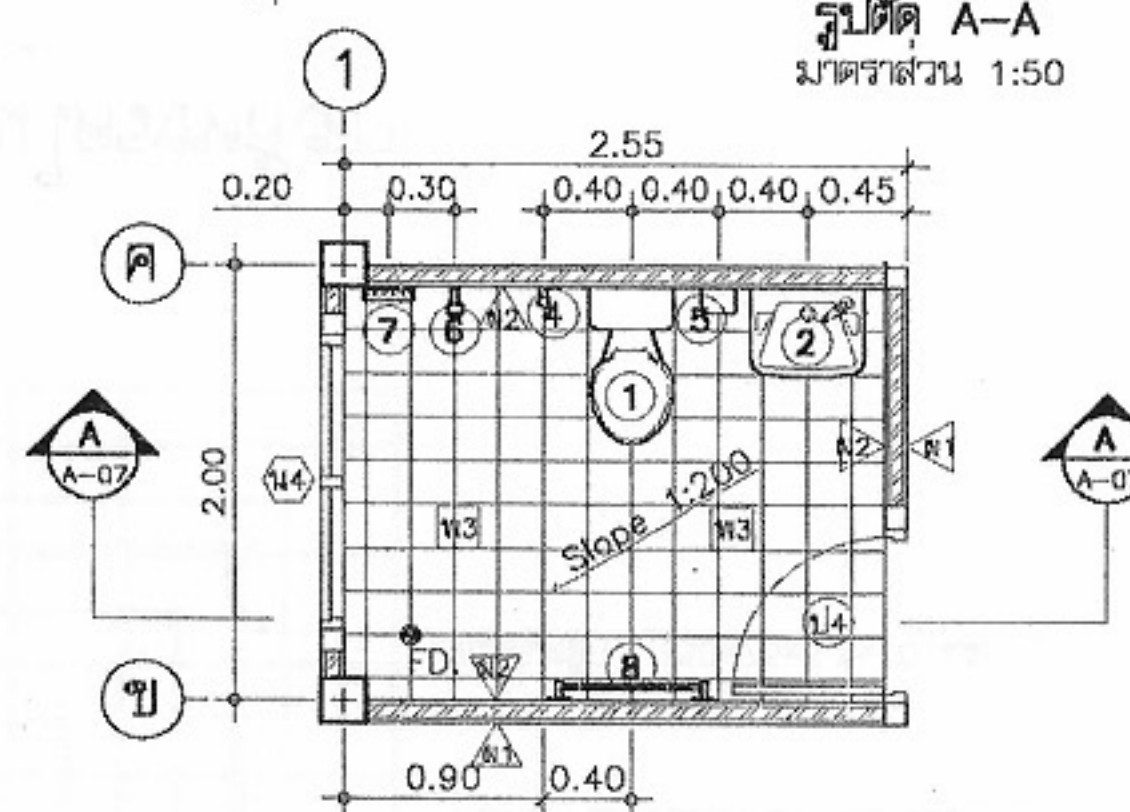

แบบขยายห้องน้ำ

มาตราส่วน 1:50

รายการประกอบแบบห้องน้ำ

1	โถส้วมนั่งราบมีฐานแบบฟลัชพร้อมหม้อน้ำ รุ่นTF-100FP
2	อ่างล้างหน้าชนิดแขวนผนัง
3	กระจกเงาพร้อมทั้งวางของพลาสติก
4	สายชำระ
5	กล่องใส่กระดาษชำระ
6	ฝักบัวอาบน้ำสายอ่อนพร้อมวาล์วเปิด-ปิด
7	กล่องใส่สบู่
8	ราวแขวนผ้าพลาสติก
9	ก๊อกน้ำรูปโครเมียม
หมายเหตุ: สุขภัณฑ์ใช้ของอเมริกันแบรนด์คาร์ต, คอตโต้, เกซัด, ซีอีเอ็มตา	



โครงการแบบอาคารเพื่อประชาชน

ครอบครัวไทยเป็นสุข

แบบ

บ้านครอบครัวไทยเป็นสุข 1

สำนักสถาปัตยกรรม

สถาปนิก

นายธนวรรณ์ ชลวิวัฒน์ สถาปนิก

สถาปนิก

สถาปนิก

สถาปนิก

สถาปนิก

สถาปนิก

สำนักวิศวกรรมโครงสร้างและงานระบบ

วิศวกร

วิศวกร

รายการประกอบแบบ ประตู หน้าต่าง

- 1 บานพับ บานพับ ใช้ STAINLESS 3"x4"x25 มม. แหวนลูกบิด
- 2 มือจับ ใช้ชนิดกันบิดเป็นโลหะชุบโครเมียม
- 3 กุญแจลูกบิด ใช้ชนิดทรงกลมเป็นโลหะชุบโครเมียม สลักติดประตูทุกบาน
- 4 กลอน สลักบาน (MORTISE LOCK) สำหรับบานเปิดคู่
- 5 ปุ่มยางกันชน ติดประตูทุกบาน
- 6 ที่ยึดประตู เป็นโลหะชุบโครเมียมชนิดลูกบิดเปลี่ยน ติดประตูทุกบาน
- 7 กระจกใส/ฝ้า กระจกหนา 6 มม.


หมายเหตุ

- ไม้วงกบสำหรับประตู-หน้าต่าง ใช้ไม้เนื้อแข็งตามบัญชี มยธ. ขนาดวงกบที่ไม่ได้ระบุไว้ในแบบให้ใช้ขนาด 2"x4" ทั้งหมด
- วงกบอลูมิเนียมใช้ สี NATURAL ANODIZER 1 3/4"x4" หนา 2 มม. กรอบบานอลูมิเนียมใช้ สี NATURAL ANODIZER 1"x4" หนา 2.3 มม.
- ประตู PVC สำเร็จรูปใช้ ทรายข้างชนิดอย่างหนา อุปกรณ์ครบชุด หรือเทียบเท่า

หมายเหตุ แบบที่แสดงอยู่นี้ได้รับการย่อส่วน เพื่อใช้แสดงผลทางหน้าจอเท่านั้น สำหรับแบบที่ใช้ขออนุญาตก่อสร้าง ให้ถ่ายสำเนาจากหนังสือแบบบ้าน

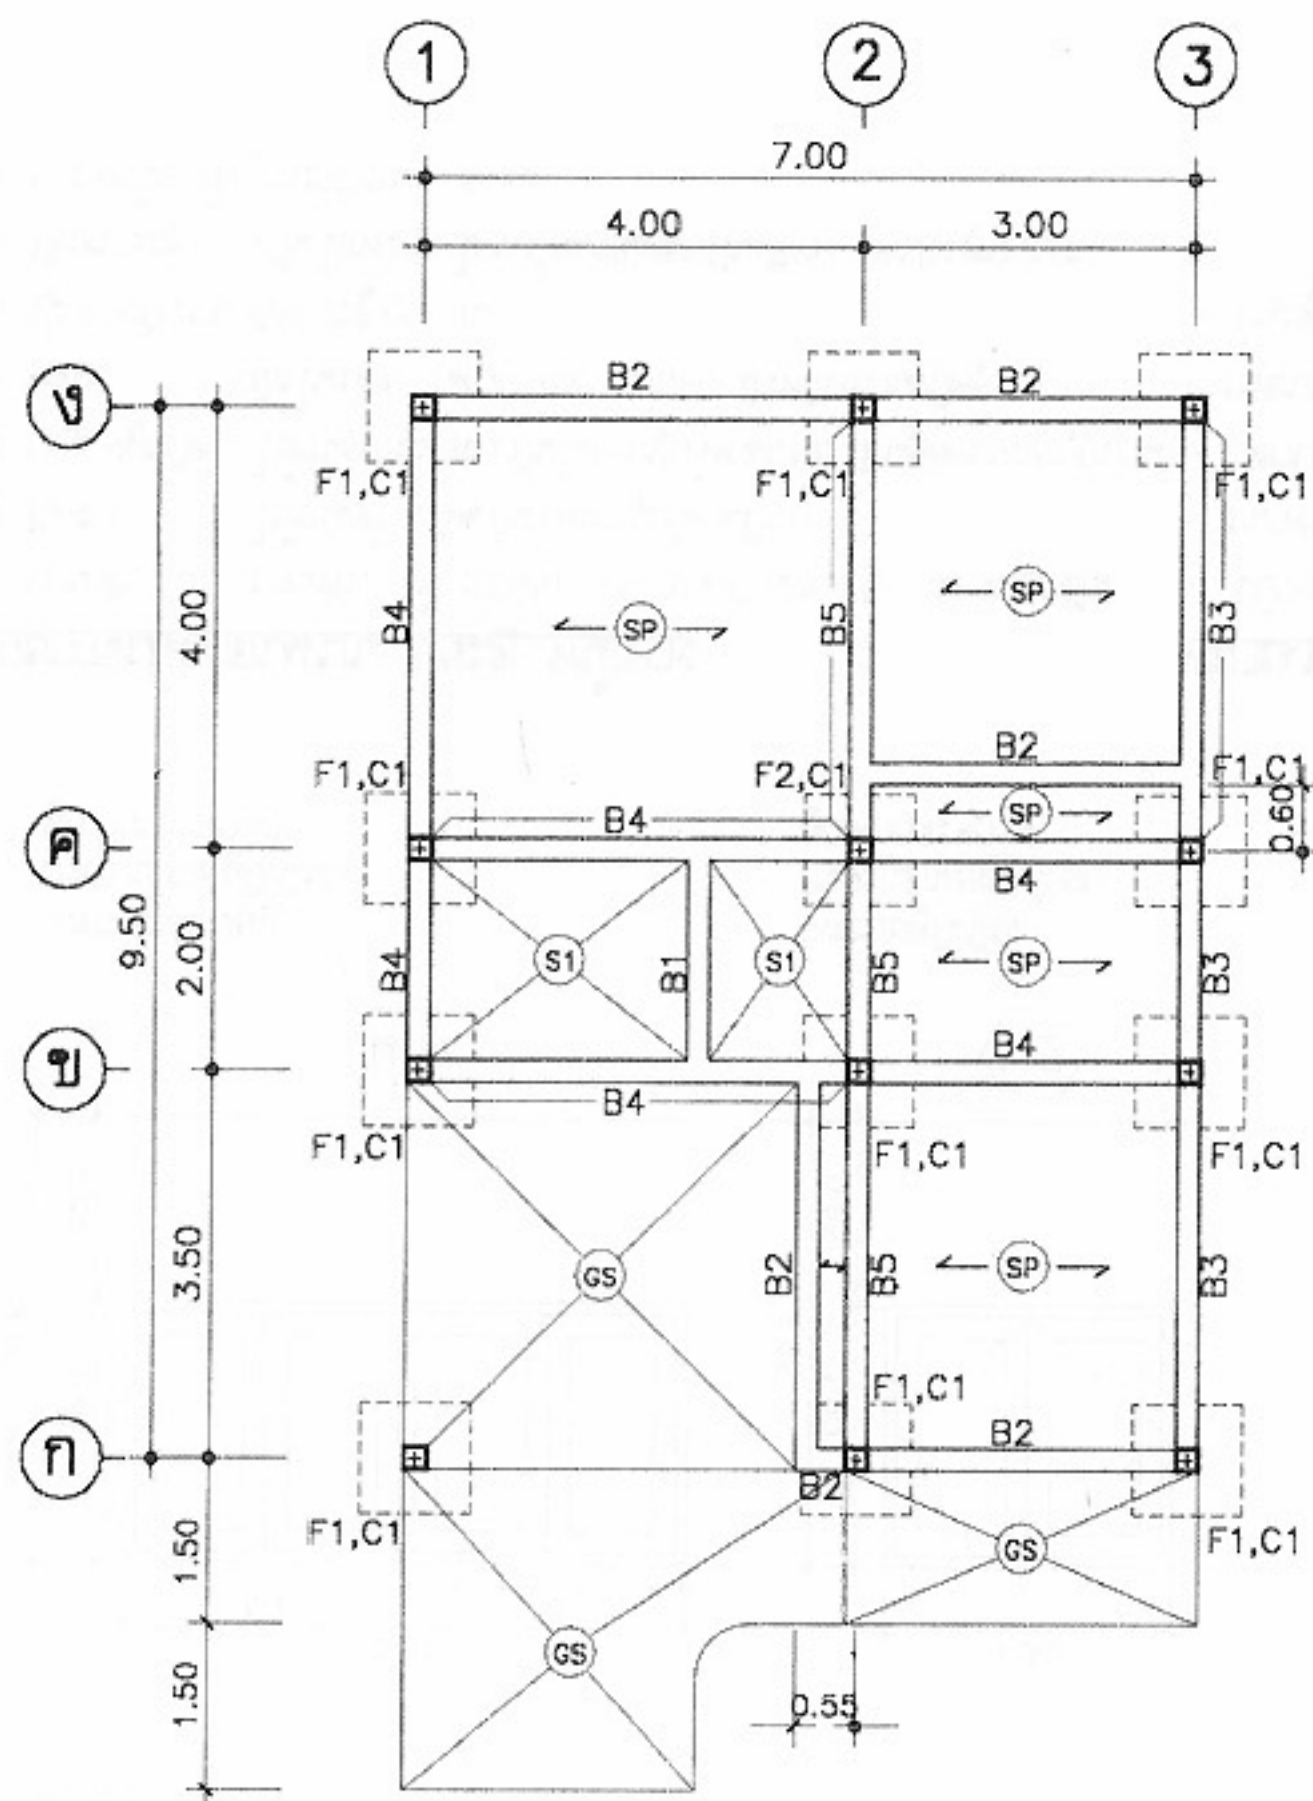

แปลนฐานราก, เสาคานและพื้น
มาตรฐาน
1:100

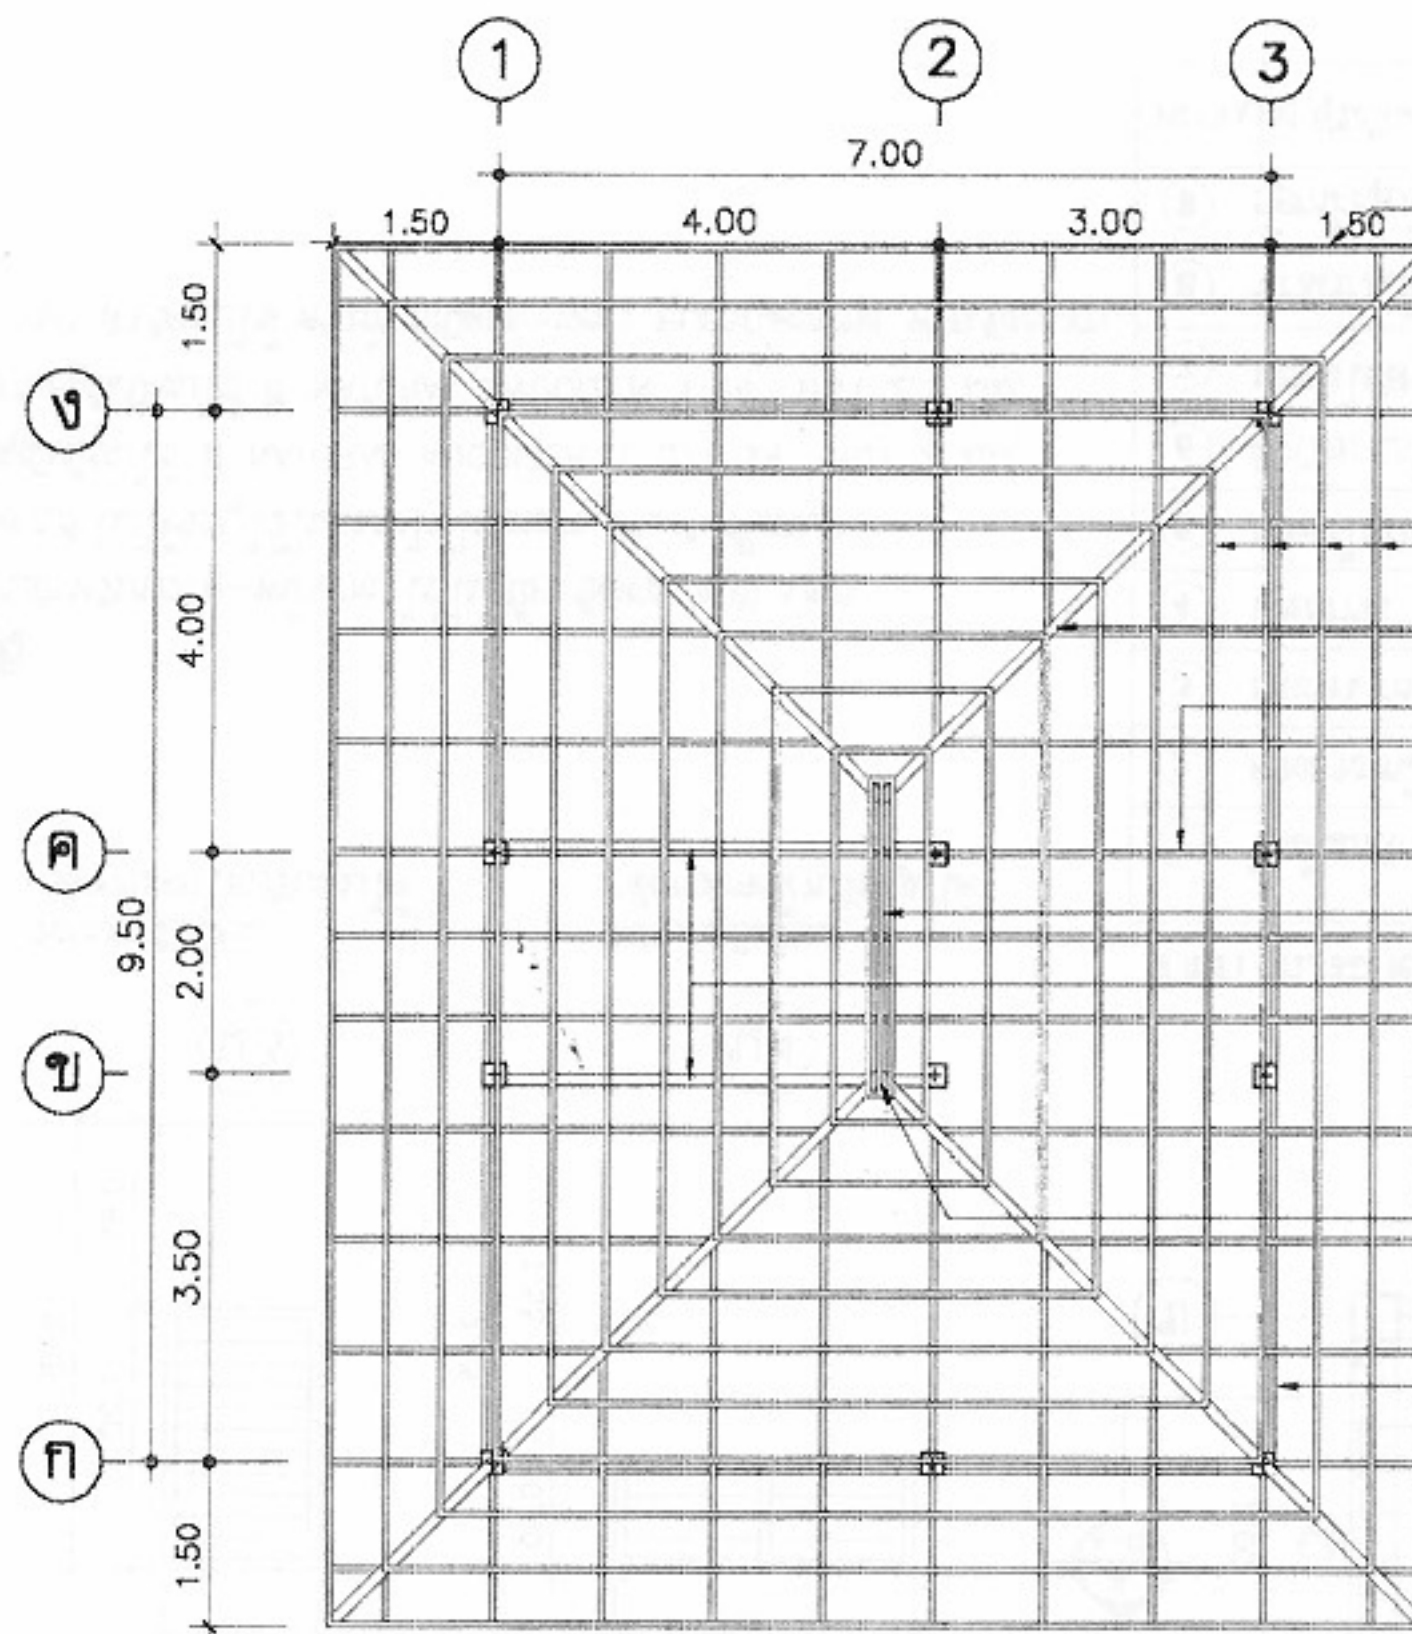

แปลนโครงหลังคา
มาตรฐาน
1:100

เพิงชายปิดปลายจันทัน $\square 125 \times 50 \times 20 \times 3.2$ มม.
ระแนงเหล็ก L $25 \times 25 \times 3$ มม. @ 0.32 ม.
ตะแคงเหล็ก $\square 100 \times 50 \times 5 \times 7.5$ มม.
จันทันเหล็ก $\square 100 \times 50 \times 20 \times 2.3$ มม. @ 1.00 ม.
อกไก่เหล็ก $\square 125 \times 50 \times 20 \times 3.2$ มม.
ข้อเหล็ก $\square 150 \times 75 \times 6.5 \times 10$ มม.
ดิ่งเหล็ก $\square 125 \times 50 \times 20 \times 3.2$ มม.
อะเสเหล็ก $\square 150 \times 75 \times 6.5 \times 10$ มม.

รายการประกอบแบบโครงสร้าง

ให้ใช้ มยอ. 101-106 เป็นรายการประกอบแบบและมีรายการเฉพาะแบบดังนี้

- คอนกรีตให้ใช้ ค.1 ($f'c$ ทรงแท่งบด = 150 ksc)
- เหล็กเสริมคอนกรีต $\phi 6$ มม. และ $\phi 9$ มม. ให้ใช้เหล็กเสริมกลม SR-24 ขนาด $\phi 12$ มม. ขึ้นไปใช้ SP-30
- เหล็กรูปพรรณ ที่นำมาใช้จะต้องมีคุณสมบัติดังต่อไปนี้
 - ใช้เหล็กที่มีคุณสมบัติเป็นไปตามมาตรฐาน ASTM - A36 หรือเทียบเท่า
 - การต่อเชื่อมให้ทำการเชื่อมด้วยไฟฟ้า (arc welding) โดยรอบทุกจุด
 - เหล็กที่นำมาใช้จะต้องปราศจากสนิมขุม ไม่มีดองหรือเสียรูป
 - ให้ทาสีกันสนิมประเภท lead oxide อย่างน้อย 2 ชั้น

4. ฐานราก

- เป็นเสาเข็มเหล็กเหลี่ยมกลวงขนาด 0.15×0.15 มีความยาว 6.00 ม.
- รับน้ำหนักปลอดภัยได้ไม่น้อยกว่า 1.7 ตัน/ตัน

- รายละเอียดหรือคุณสมบัติของวัสดุ หรือ อุปกรณ์ในแบบ หรือในรายการประกอบแบบ ทั้งที่ระบุ หรือมิได้ระบุไว้ หากมีการกำหนดมาตรฐานผลิตภัณฑ์อุตสาหกรรมแล้ว ให้เป็นไปตามมาตรฐานผลิตภัณฑ์อุตสาหกรรมนั้น



โครงการแบบอาคารเพื่อประชาชน
ครอบครัวไทยเป็นสุข

แบบ

บ้านครอบครัวไทยเป็นสุข 1

สำนักสถาปัตย์กรรม

สถาปัตย์กรรม

สถาปัตย์กรรม

นายสมรรถนะ สวัสดิวิวัฒน์ สถาปัตย์

สถาปัตย์

สถาปัตย์

สำนักวิศวกรรมโครงสร้างและงานระบบ

วิศวกรรม

โครงสร้าง

วิศวกรรมไฟฟ้า

และเครื่องกล

วิศวกรรม

สุขาภิบาล

อนุมัติ

นายสว่าง ศรีสกุล

(นายสว่าง ศรีสกุล)

อธิบดีกรมโยธาธิการและผังเมือง

แสดงแบบ

แปลนโครงสร้าง

มาตรฐาน 1:100

วัน/เดือน/ปี 21 พ.ย. 2546


เลขที่แบบ ม.บ.462119

แผ่นที่


S-01

จำนวนแผ่น


2

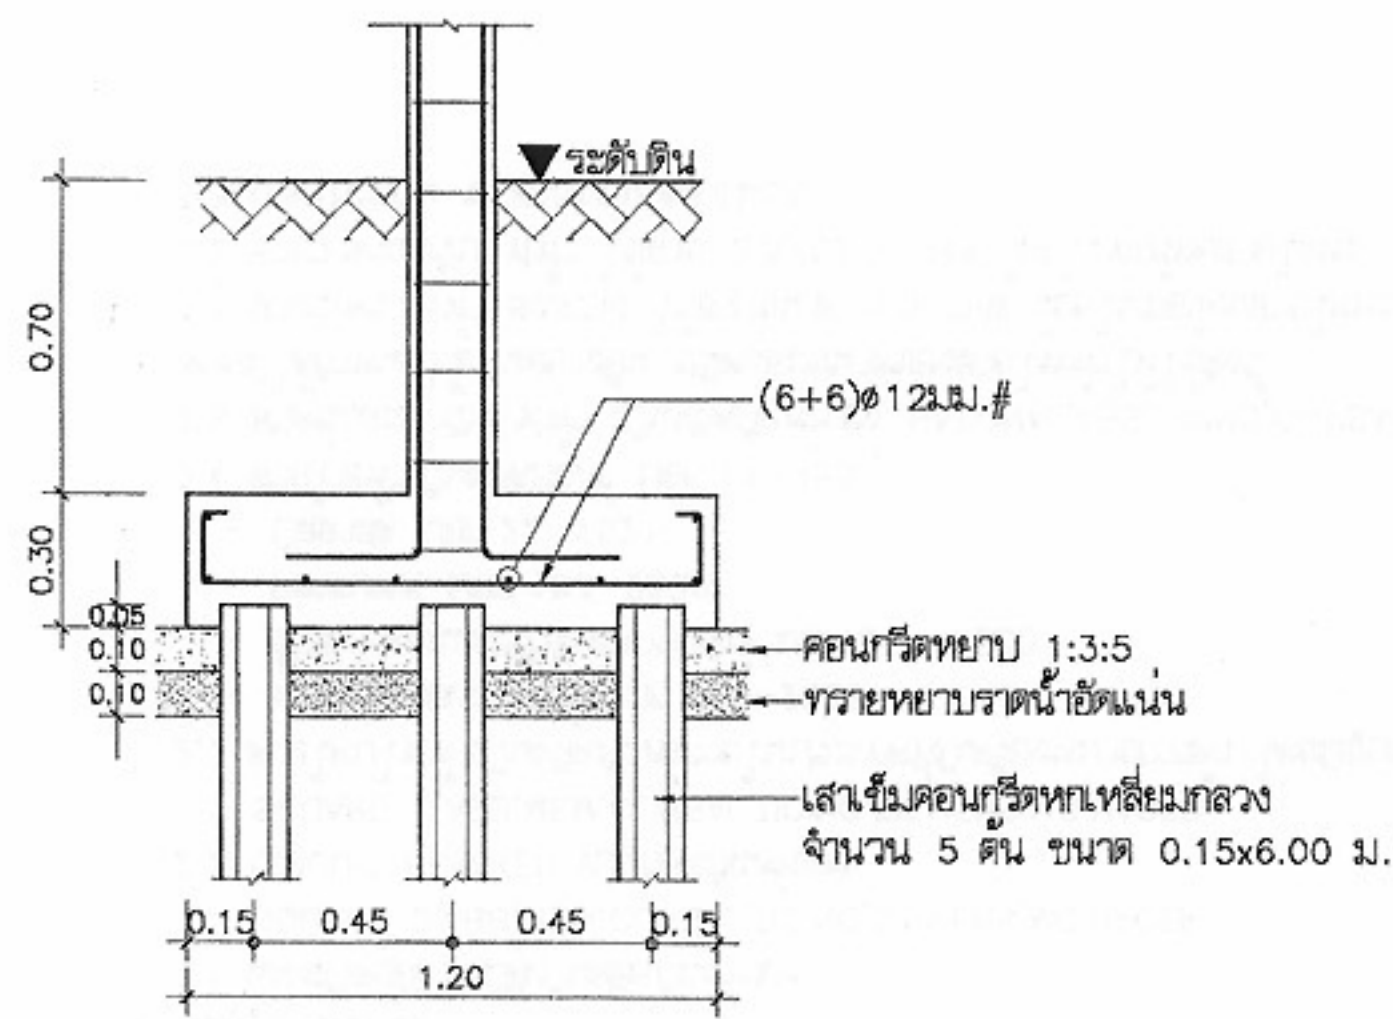


รูปตัด ฐานราก F-2

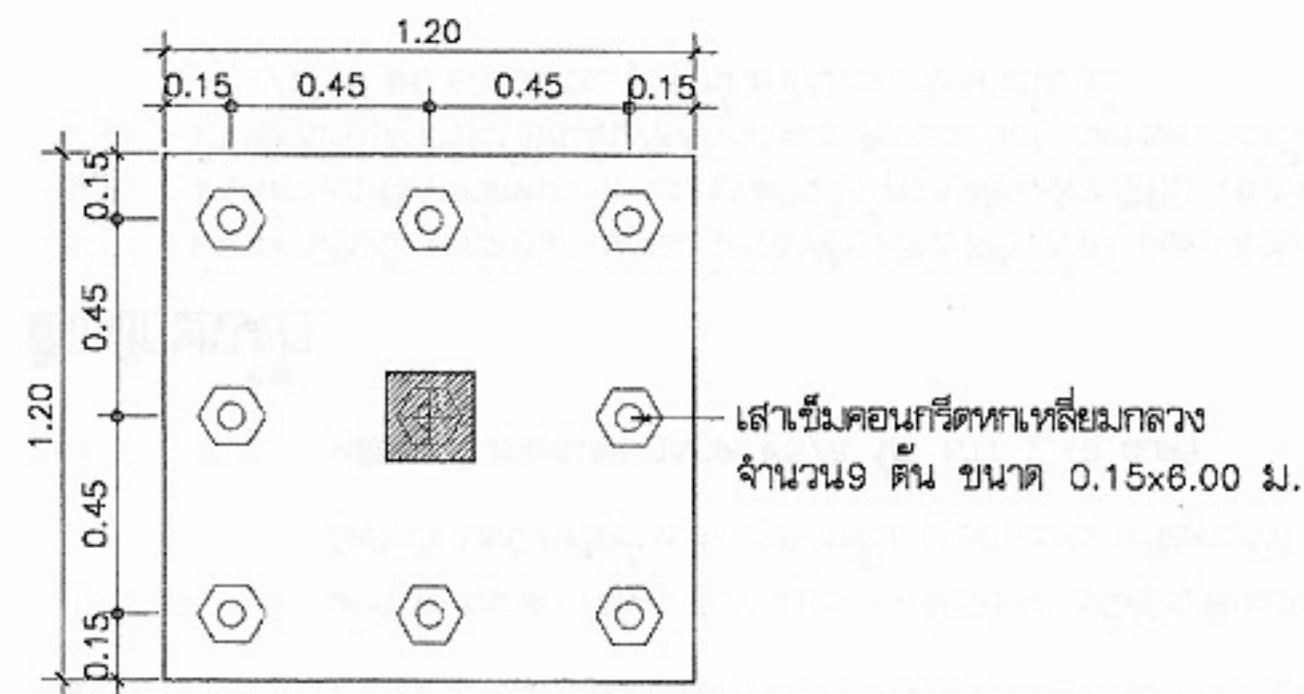






แปลน ฐานราก F-2

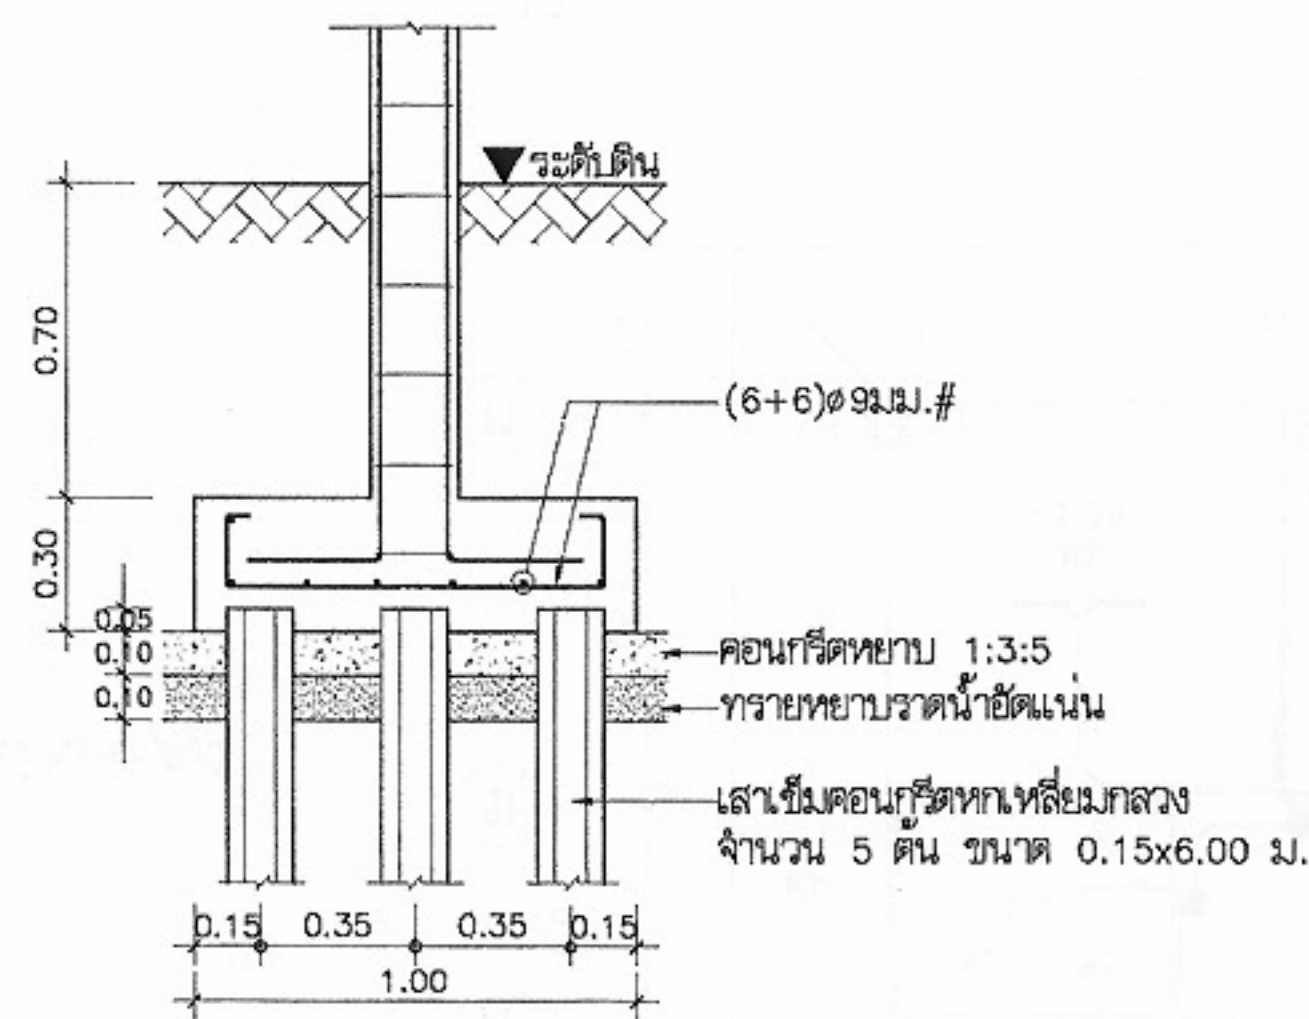



รูปตัด ฐานราก F-1

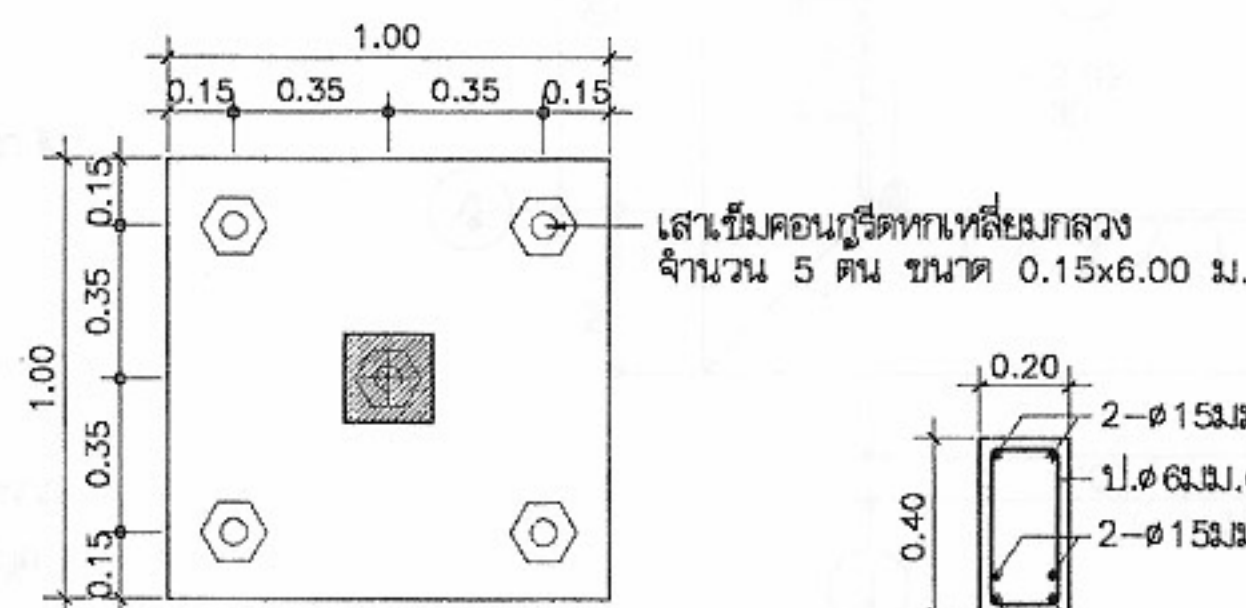

แปลน ฐานราก F-1

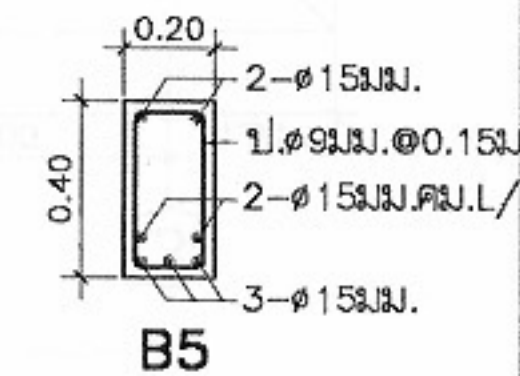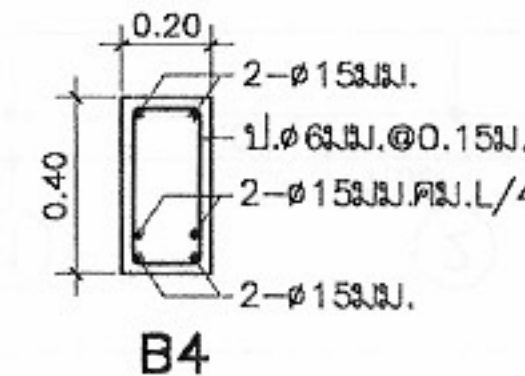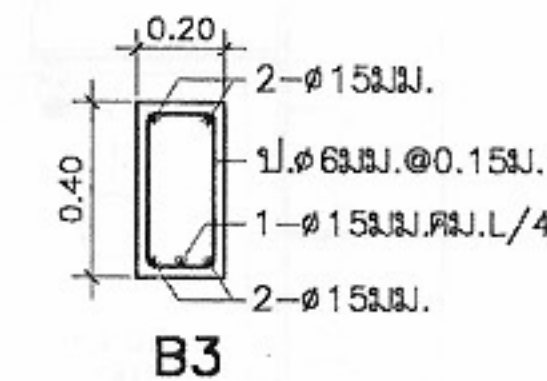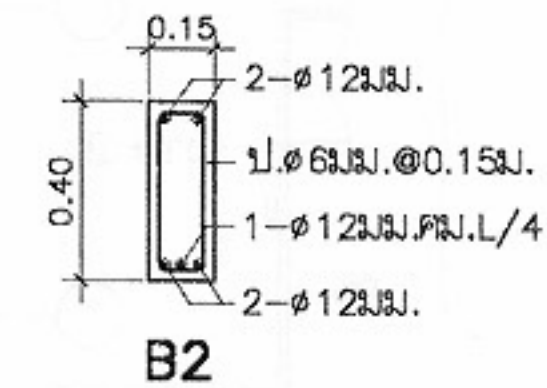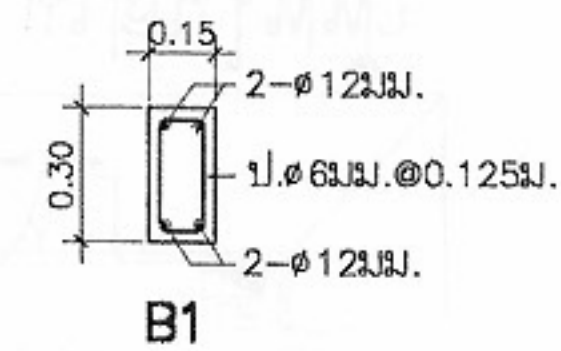

ระดับชั้น	เสา C1 มาตรฐาน 1:25
ระดับพื้นที่ 1 รับโครงสร้างคาน	4 $\phi 12$ mm. 1 $\phi 6$ mm @ 0.15 m.
ระดับเสาต่อมอ.ฐานราก รับพื้นที่ 1	4 $\phi 12$ mm. 1 $\phi 6$ mm @ 0.15 m.

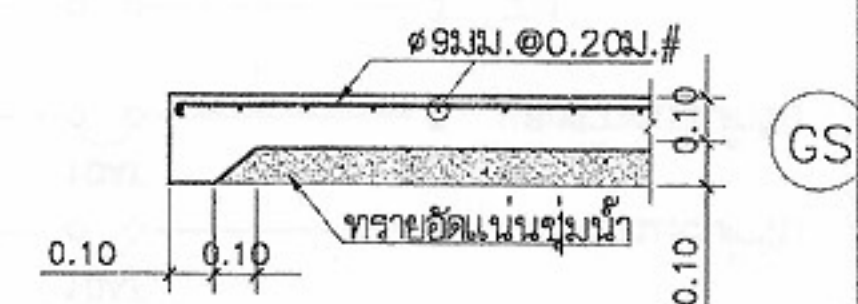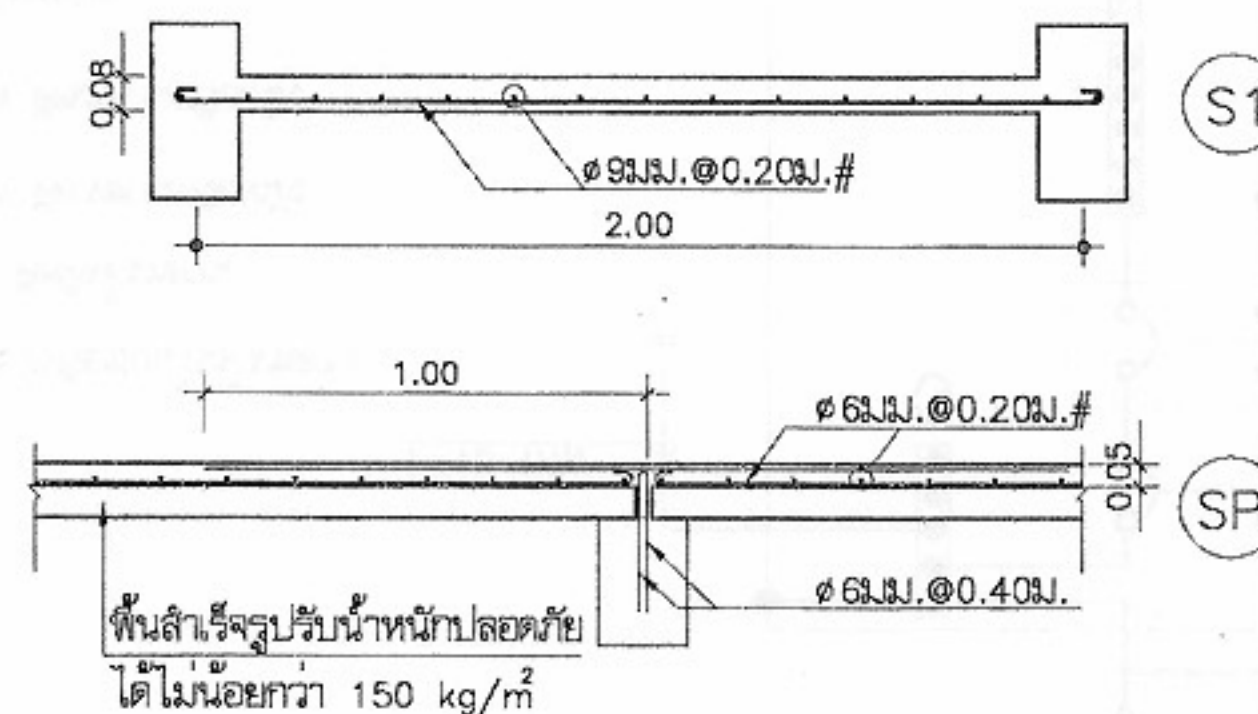

แบบขยายเสา,คาน,พื้น
มาตรฐาน 1:25



โครงการแบบอาคารเพื่อประชาชน
ครอบครัวไทยเป็นสุข

แบบ
บ้านครอบครัวไทยเป็นสุข 1

สำนักสถาปัตย์กรรม
ผู้ดำเนินการหลัก

สถาปัตย์กรรม
นายธนวรรณ ขอลุมวิวัฒน์ สถาปนิก
สถาปนิก
สถาปนิก

สำนักวิศวกรรมโครงสร้างและงานระบบ
ผู้ดำเนินการหลัก

วิศวกรรม	วิศวกร
โครงสร้าง	วิศวกร
วิศวกรรมไฟฟ้า	วิศวกร
และเครื่องกล	วิศวกร
วิศวกรรม	วิศวกร
สุขาภิบาล	วิศวกร

อนุมัติ
(นายสว่าง ศรีสุกัน)
อธิบดีกรมโยธาธิการและผังเมือง

แสดงแบบ
แบบขยายฐานราก,เสา,คาน,พื้น

มาตรฐาน	1:25
วัน/เดือน/ปี	21 พ.ย. 2546
เลขที่แบบ	ม.บ.462119
แผ่นที่	จำนวนแผ่น
S-02	2

สัญลักษณ์ไฟฟ้า



	CIRCUIT BREAKER
	แผงสวิตช์อัตโนมัติ(LP) ติดผนัง
	สายไฟฟ้าเดินร้อยในท่อร้อยสายโลหะ ผังผนังคอนกรีต และ/หรือซ่อนในฝ้าเพดาน
	ดวงโคม DOWNLIGHT หลอด INCANDESCENT 1-60 W ติดฝ้าเพดาน
	ดวงโคมฟลูออเรสเซนต์ กล่องเหล็กเปื้อนยอย หลอด 1-18 W ติดเพดานหรือผนัง
	ดวงโคมฟลูออเรสเซนต์ กล่องเหล็กเปื้อนยอย หลอด 1-36 W ติดเพดานหรือผนัง
	ดวงโคมฟลูออเรสเซนต์ ครอบแก้วกลม หลอด 1-32 W ติดเพดาน
	สวิตช์เดี่ยว ขนาด 16A-250V ติดตั้งเรียบผนังหรือข้างเสาสูง 1.30 ม.
	สวิตช์สามทาง ขนาด 16A-250V ติดตั้งเรียบผนังหรือข้างเสาสูง 1.30 ม.
	เต้ารับคู่ ขนาด 16A-250V แบบ UNIVERSAL ชนิดมีขาติ้นและม่านนิรภัย ติดตั้งเรียบผนังหรือข้างเสา สูงจากพื้น 0.50 เมตร หรือตามที่กำหนดในแบบ
	หลักสายดินทองแดง ขนาด ๑5/8 นิ้ว ยาว 2.40 เมตร

สัญลักษณ์ฝ้า

- (ผ1) ฝ้าเพดานยิบซีบอร์ดหนา 9 มม. โครงเหล็กเคลือบสีที่บาร์ ๑0.60x0.60ม.#
 (ผ2) ฝ้าเพดานยิบซีบอร์ดหนา 9 มม. ชนิดกันน้ำ โครงเหล็กเคลือบสีที่บาร์ ๑0.60x0.60ม.#
 (ผ3) ฝ้าเพดานขยาคกระเบื้องแผ่นเรียบหนา 4 มม. ติดตาม SLOPE โครงเคราไม้เนื้อแข็ง 1 1/2" x 3" ๑0.60x0.60ม.# ทากายาภิบาลกรรณ.เนื้อไม้

รายละเอียด

- ในการติดตั้ง ผู้รับจ้างต้องปฏิบัติตามกฎระเบียบข้อบังคับของการไฟฟ้า
- วัสดุอุปกรณ์ที่ใช้
 - แผงสวิตช์อัตโนมัติเป็นผลิตภัณฑ์ของ SQUARE D, ABB, MEM, CLIPSAL, TICINO, SIEMENS, MG, HAGER
 - CIRCUIT BREAKER เป็นผลิตภัณฑ์ของ SQUARE D, ABB, MEM, CLIPSAL, TICINO, SIEMENS, MG, HAGER
 - ดวงโคมไฟฟ้าเป็นผลิตภัณฑ์ภายในประเทศที่มีเครื่องหมายการค้า โดยมีอุปกรณ์ประกอบดังนี้
 - หลอดฟลูออเรสเซนต์ มอก. 236-2533
 - ขั้วรับหลอดและขั้วรับสตาปเตอร์ มอก. 344-2530
 - สตาปเตอร์ มอก. 183-2528
 - บัลลาสต์ มอก. 23-2521
 - สายไฟฟ้าเป็นผลิตภัณฑ์ มอก. 11-2531
 - สวิตช์และเต้ารับไฟฟ้า เป็นผลิตภัณฑ์ของ NATIONAL, ABB, TICINO, CLIPSAL
- หากมิได้กำหนดไว้เป็นอย่างอื่น ชนิดและขนาดของสายไฟฟ้าให้ใช้ดังนี้
 - สายวงจรไฟฟ้าแสงสว่าง ใช้สายขนาด 2.5 THW ร้อยในท่อร้อยสายโลหะ
 - สายวงจรเต้ารับไฟฟ้า ใช้สาย 2.5/G2.5 THW ร้อยในท่อร้อยสายโลหะ
 - สายประธาน ชนิดและขนาดตามแบบ

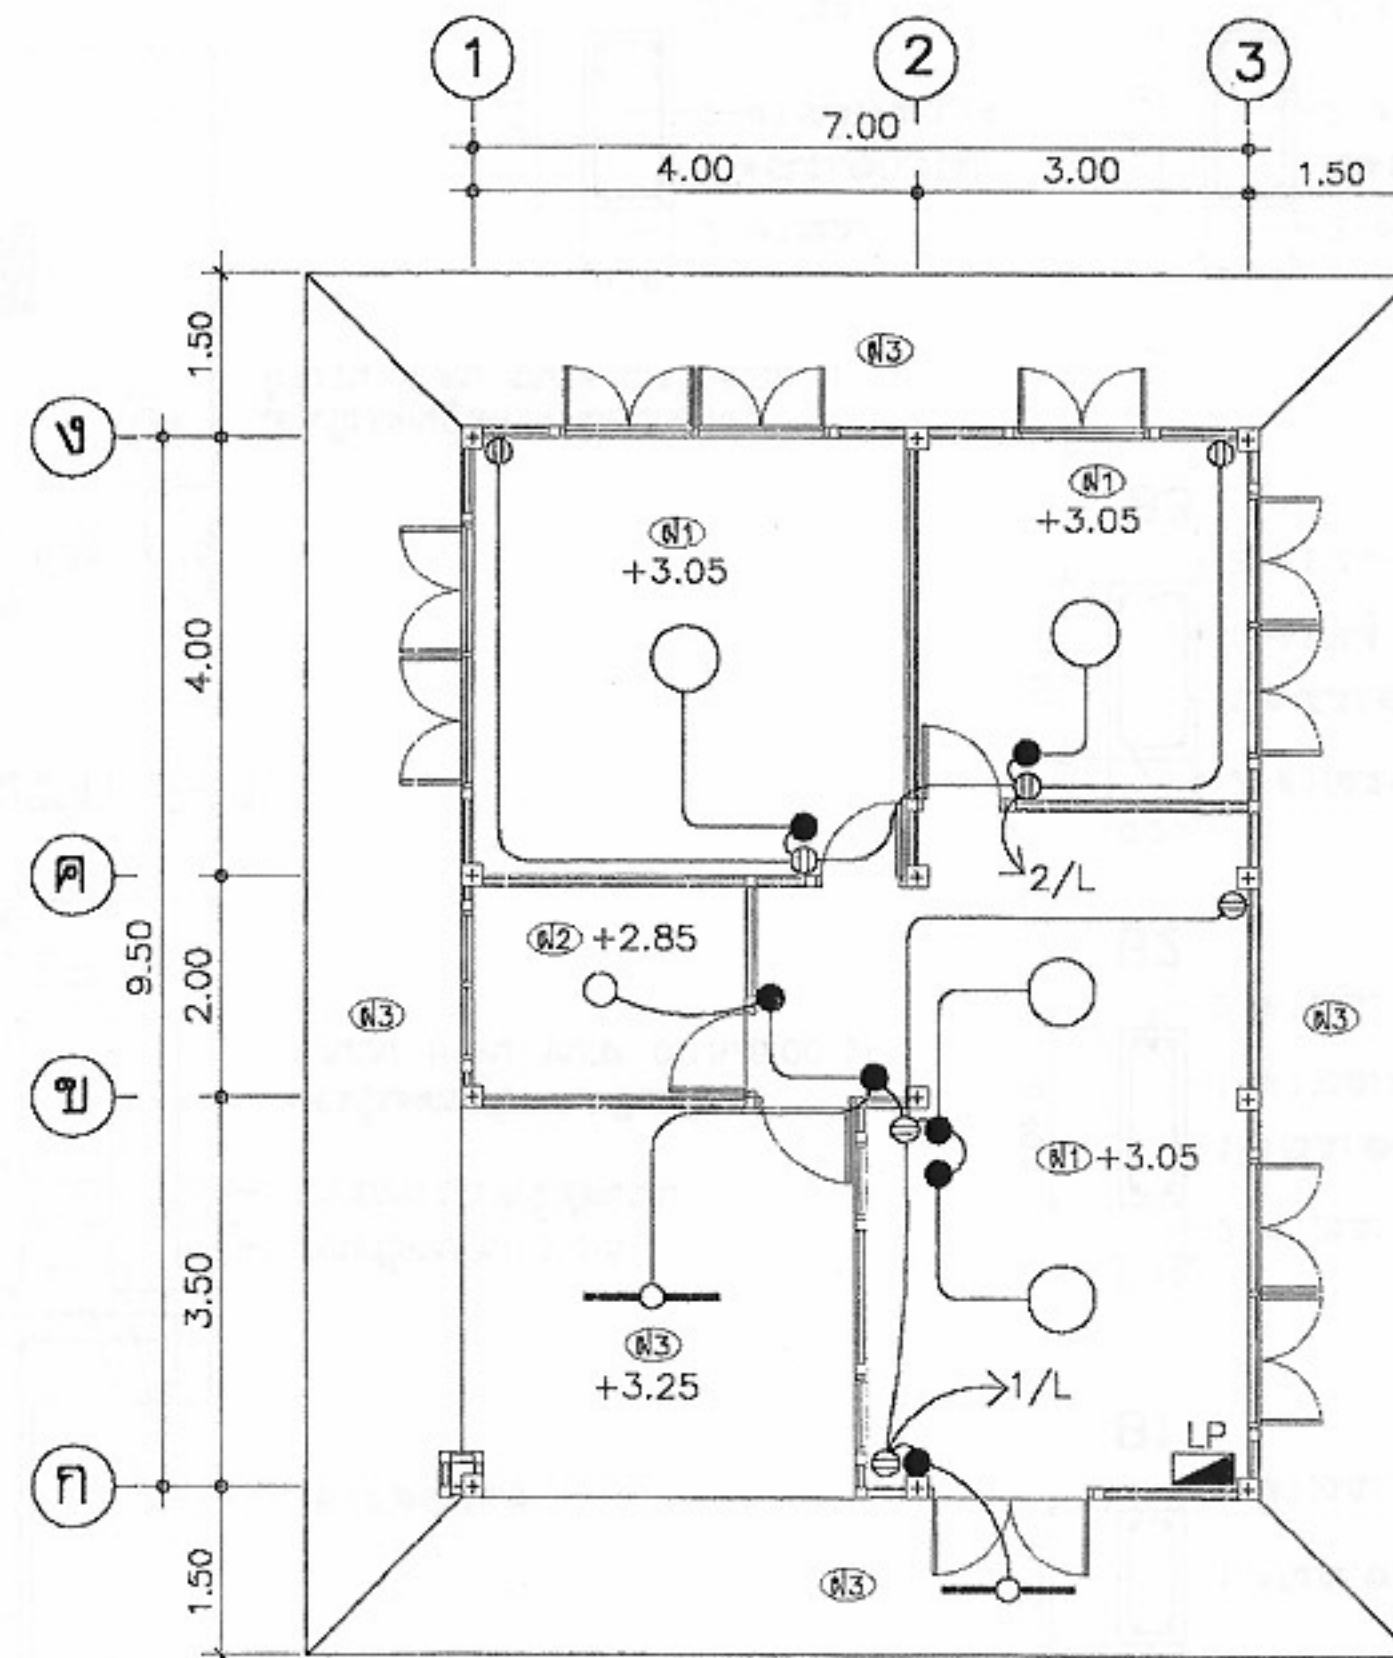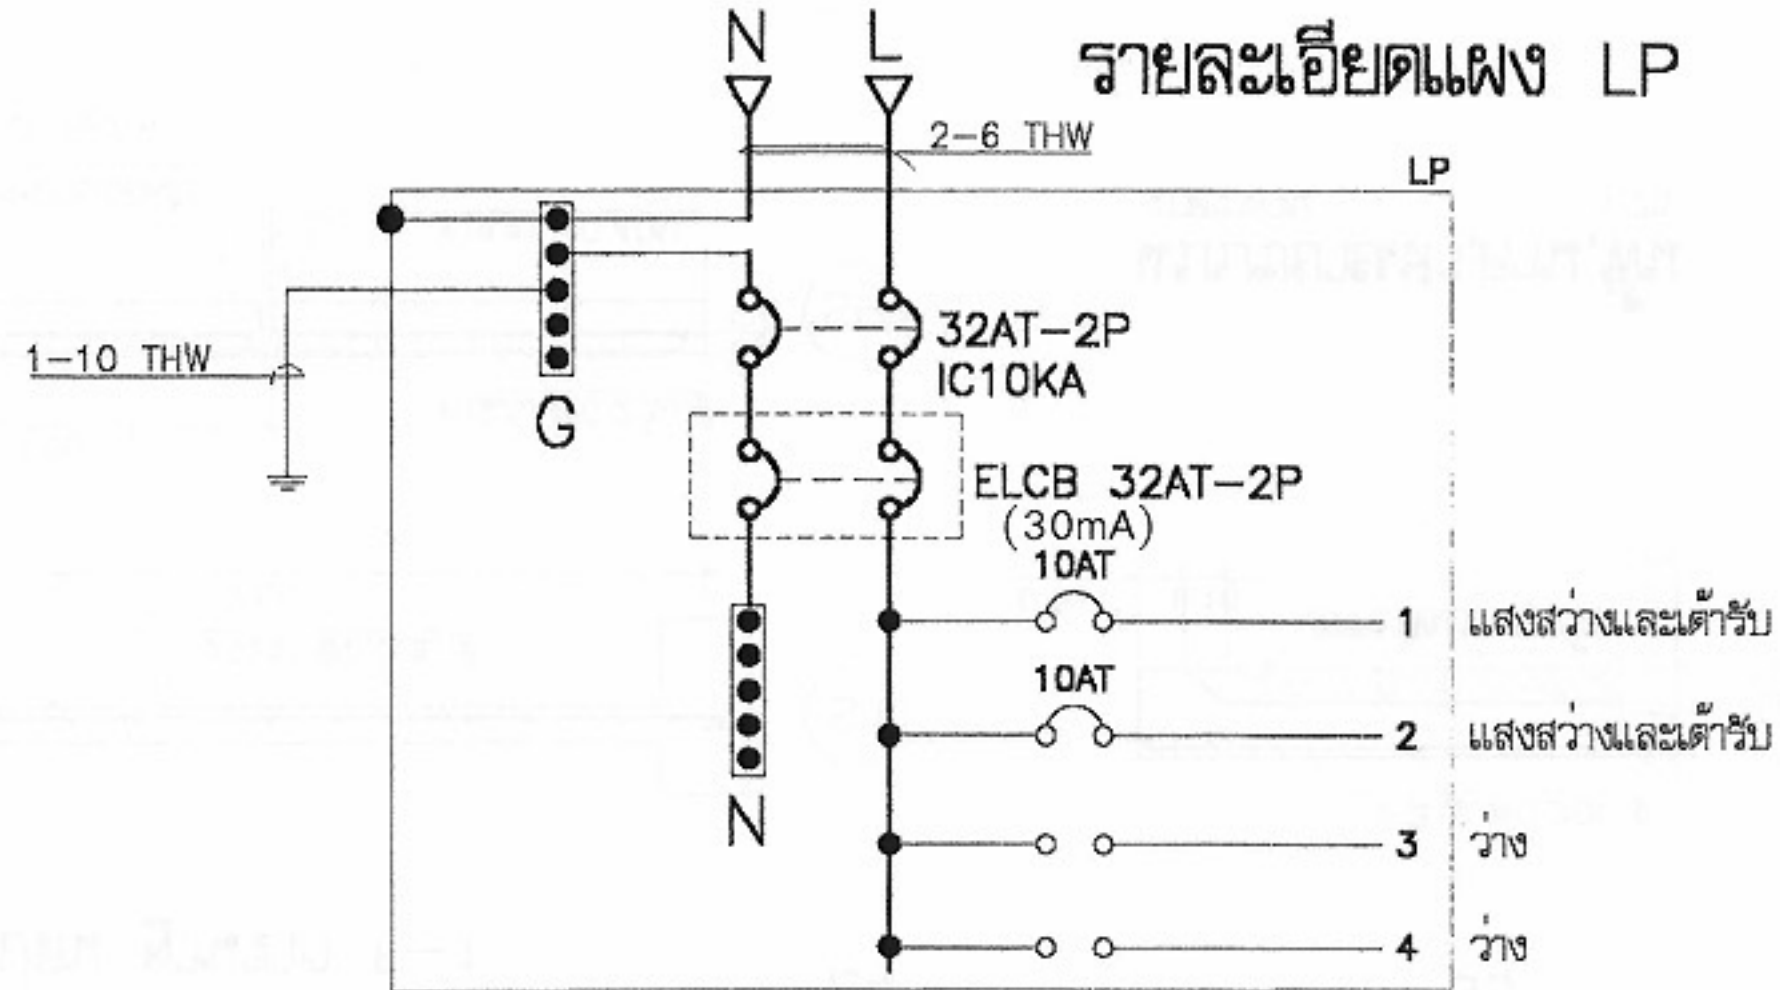

แปลนไฟฟ้า

มาตราส่วน 1:100



โครงการแบบอาคารเพื่อประชาชน
ครอบครัวไทยเป็นสุข

แบบ
บ้านครอบครัวไทยเป็นสุข 1

สำนักสถาปัตยกรรม
ผู้ควบคุมการปฏิบัติงาน

สถาปัตยกรรม
นายธนวรรธน์ ชลวิวัฒน์

สถาปัตยกรรม
นายธนวรรธน์ ชลวิวัฒน์

สำนักวิศวกรรมโครงสร้างและงานระบบ
ผู้ควบคุมการปฏิบัติงาน

วิศวกรรม
โครงสร้าง

วิศวกรรมไฟฟ้า
และเครื่องกล

วิศวกรรม
สุขาภิบาล

อนุมัติ
(นายสว่าง ศรีสุกัน)
อธิบดีกรมโยธาธิการและผังเมือง

แสดงแบบ
แปลนไฟฟ้า

มาตราส่วน 1:100

วัน/เดือน/ปี 21 พ.ย. 2546

เลขที่แบบ ม.บ.462119

แผ่นที่ E-01 จำนวนแผ่น 1

หมายเหตุ แบบที่แสดงอยู่นี้ได้รับการยืมส่วน เพื่อใช้แสดงผลทางหน้าจอเท่านั้น สำหรับแบบที่ใช้ขออนุญาตก่อสร้าง ให้ถ่ายสำเนาจากหนังสือแบบบ้าน

