



ตามนโยบายของ
หม่อมราชวงศ์สุขุมพันธุ์ บริพัตร
ผู้ว่าราชการกรุงเทพมหานคร
โดย สำนักการโยธา



แบบบ้านยืม... เพื่อประชาชน

100 แบบบ้านมาตรฐาน...
สวย ดี โดนใจ...
พร้อมปลูกสร้างได้ทันที

ห้ามพลาด!!! โอกาส...
ยืมรับ... บ้านใหม่
แบบ **บ้านสวย**
เลือกได้
ใน “โครงการแบบบ้านยืม...เพื่อประชาชน”

แบบ 100 แบบบ้าน
มาตรฐาน...
สวย ดี โดนใจ
พร้อมปลูก
สร้างได้ทันที
มีให้เลือก
หลากหลาย
ตอบสนอง
ทุกไลฟ์สไตล์คนเมือง

งามพิศ

ด้วยความอนุเคราะห์แบบจาก
บริษัท แลนด์ โฮม (ประเทศไทย) จำกัด

รายการประกอบแบบก่อสร้าง TYPE "S"

รายการประกอบแบบทั่วไป

- โครงสร้างบ้านพักอาศัยโดยทั่วไปเป็นคอนกรีตเสริมเหล็กหล่อในที่ ตั้งแต่ฐานราก ; เสา , คาน , พื้นชั้นล่าง - บน เป็นพื้น - สำเร็จรูป บางส่วนหล่อในที่ ขนาด และ รายละเอียด ตามแบบวิศวกรรม
- เสาเข็มบ้าน 2 ชั้น ใช้คอนกรีตอัดแรง  กรณีสถานที่ 2 ชั้น จะใช้เสาเข็มตาม - การคำนวณของวิศวกร
- หลังคา โครงหลังคาเหล็กรูปพรรณ ทาสีกันสนิม TOA 2 ชั้น พร้อมฉนวนฉนวนกันความร้อน 1 ชั้น มุงด้วยกระเบื้อง CPAC MONIER สลักตราฐานบริษัท หรือ เทียนดำ
- ผนังทั่วไปใช้อิฐมวลเบา จากปูนเรียบ ทาสี ยาววันฉวีขาว ทำผิวพิเศษตามระบุในแบบ
- ฝ้าเพดานภายใน แผ่นยิปซัมบอร์ดหนา 9 มม. จากปูนเรียบ ทาสี ความสูงจากพื้นถึงฝ้า 2.60 เมตร
- ภายนอกกระเบื้องแผ่นเรียบ หนา 4 มม. , ห้องน้ำแผ่นยิปซัมบอร์ด หนา 9 มม. วางบนโครงคร่าว T - BAR
- บันไดโครงสร้างไม้จริง สลักบันได , ลูกนอนบันไดไม้จริง เสา , ราวบันได , ลูกกรงบันไดไม้จริง
- สีที่ใช้ใช้ SUPERCOAT ผลของ ICI หรือ เทียนดำ
- การป้องกันปลวก ใช้ระบบดินท่อน้ำบริเวณฐานชั้นล่างทั้งหมด และทาน้ำยากันปลวกบนเนื้อโครงสร้างด้วย



รายการประกอบแบบการเปลี่ยนแปลงเพิ่มเติม

•หมายเหตุ : งานโครงสร้าง ประกอบรับกระเบื้องใช้ปูนปลาสเตอร์ ความหนา 0.7 มม.

* บ้านหลังนี้ใช้เข็มเสา ขนาด ϕ 35 ซม. ลึก 21 ม. ทั้งหมด - ตามใบ ป/ป 1/7.

* แคมชดคร่าวสำเร็จรูปของ MODERNFORM มูลค่า 91,000 บาท โดยลูกค้าจะได้รับ GIFT VOUCHER ชดคร่าว MODERNFORM - หลังสัปดาห์ที่ 5 เรียบร้อยแล้ว ตามใบ ป/ป 3/1.

สัญลักษณ์ประกอบแบบสถาปัตย์

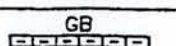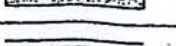สัญลักษณ์	ความหมาย
N 	ทิศเหนือ
	1, 2, 3, 4 ชื่อรูปด้านกำหนดจากแปลน
A 	A หมายถึง ชื่อรูปด้าน
	A หมายถึง ชื่อแบบขยาย
A - A 	A หมายถึง ชื่อรูปตัด
A 	A หมายถึง แนวการระบายจากศูนย์กลาง
+0000 , -0000	+0000 มีค่ามากได้ไม่เกินตัวเลขที่กำหนด , -0000 มีค่าน้อยได้ไม่เกินตัวเลขที่กำหนด
B 	B หมายถึง ระยะความยาวจากศูนย์กลางถึงศูนย์กลาง
B 	B หมายถึง ระยะความยาวจากริมถึงริม
A 	A หมายถึง ระยะความยาวจากศูนย์กลางถึงผนังริมนอก
A 	A หมายถึง ระยะความยาวจากศูนย์กลางถึงผนังริมใน
①	1 หมายถึง รหัสประตู
①	1 หมายถึง รหัสหน้าต่าง
①	1 หมายถึง หมายเลขผนัง
	ผนังอิฐครึ่งแผ่น จากปูน
	ผนังอิฐครึ่งแผ่น จากปูน
	ผนังอิฐมวลเบา จากปูน
GB 	ผนังอิฐรูปสี่เหลี่ยม ตามแบบระบุ
	ผนังแบบโครงคร่าวไม้จริง กรุด้วยตามแบบระบุ
	ดิน
	คอนกรีต
	ทรายอัดแน่น
	หินกาบ
	ปูนฉาบเรียบ
	จากปูนชะร่อง
	จากปูนเรียบ

บ้าน SMILE HOME
V.1 [11/2/45]




โครงการ
แบบบ้านยืมเพื่อประชาชน

ตามนโยบาย
ม.ร.ว. สุขุมพันธุ์ บริพัตร
ผู้ว่าราชการกรุงเทพมหานคร

โดยสำนักงานโยธา
กรุงเทพมหานคร

งามพิศ

ได้รับความอนุเคราะห์แบบ
จาก
บริษัท แลนด์ โฮม
(ประเทศไทย) จำกัด

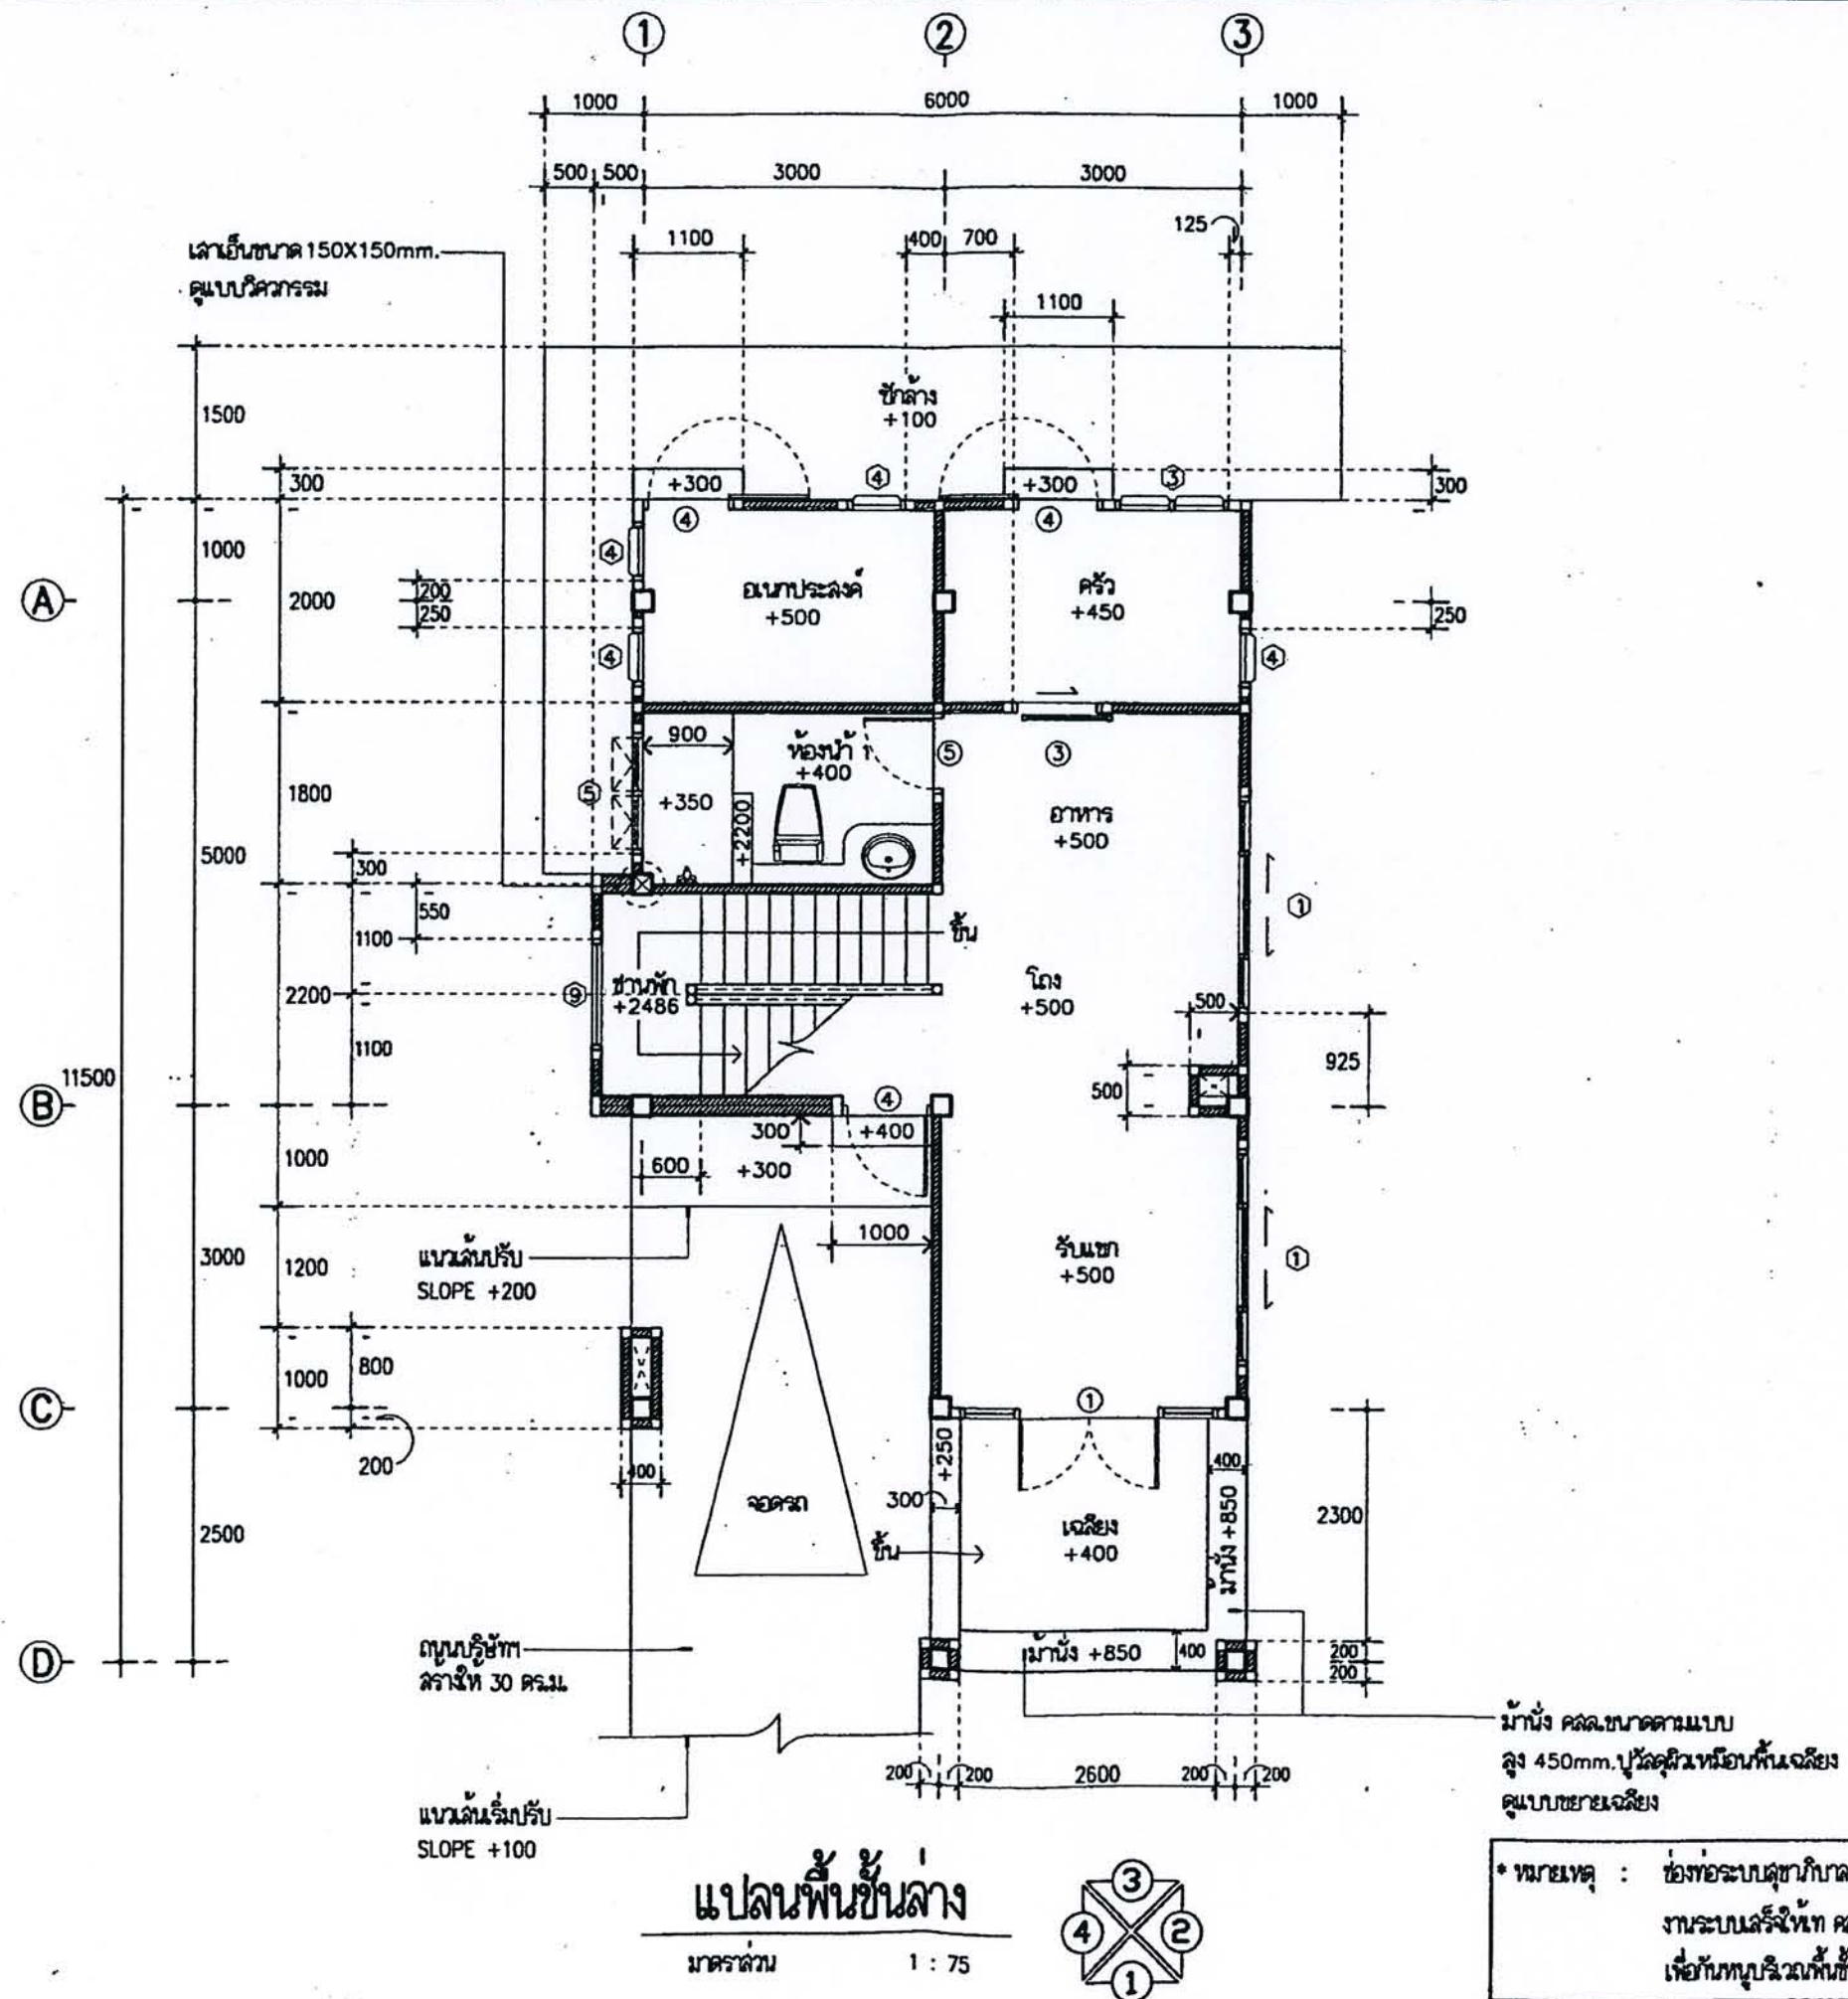




โครงการ
แบบบ้านอิมเพื่อประชาชน

ตามนโยบาย
ม.ร.ว. สุขุมพันธุ์ บริพัตร
ผู้ว่าราชการกรุงเทพมหานคร

โดยสำนักงานโยธา
กรุงเทพมหานคร

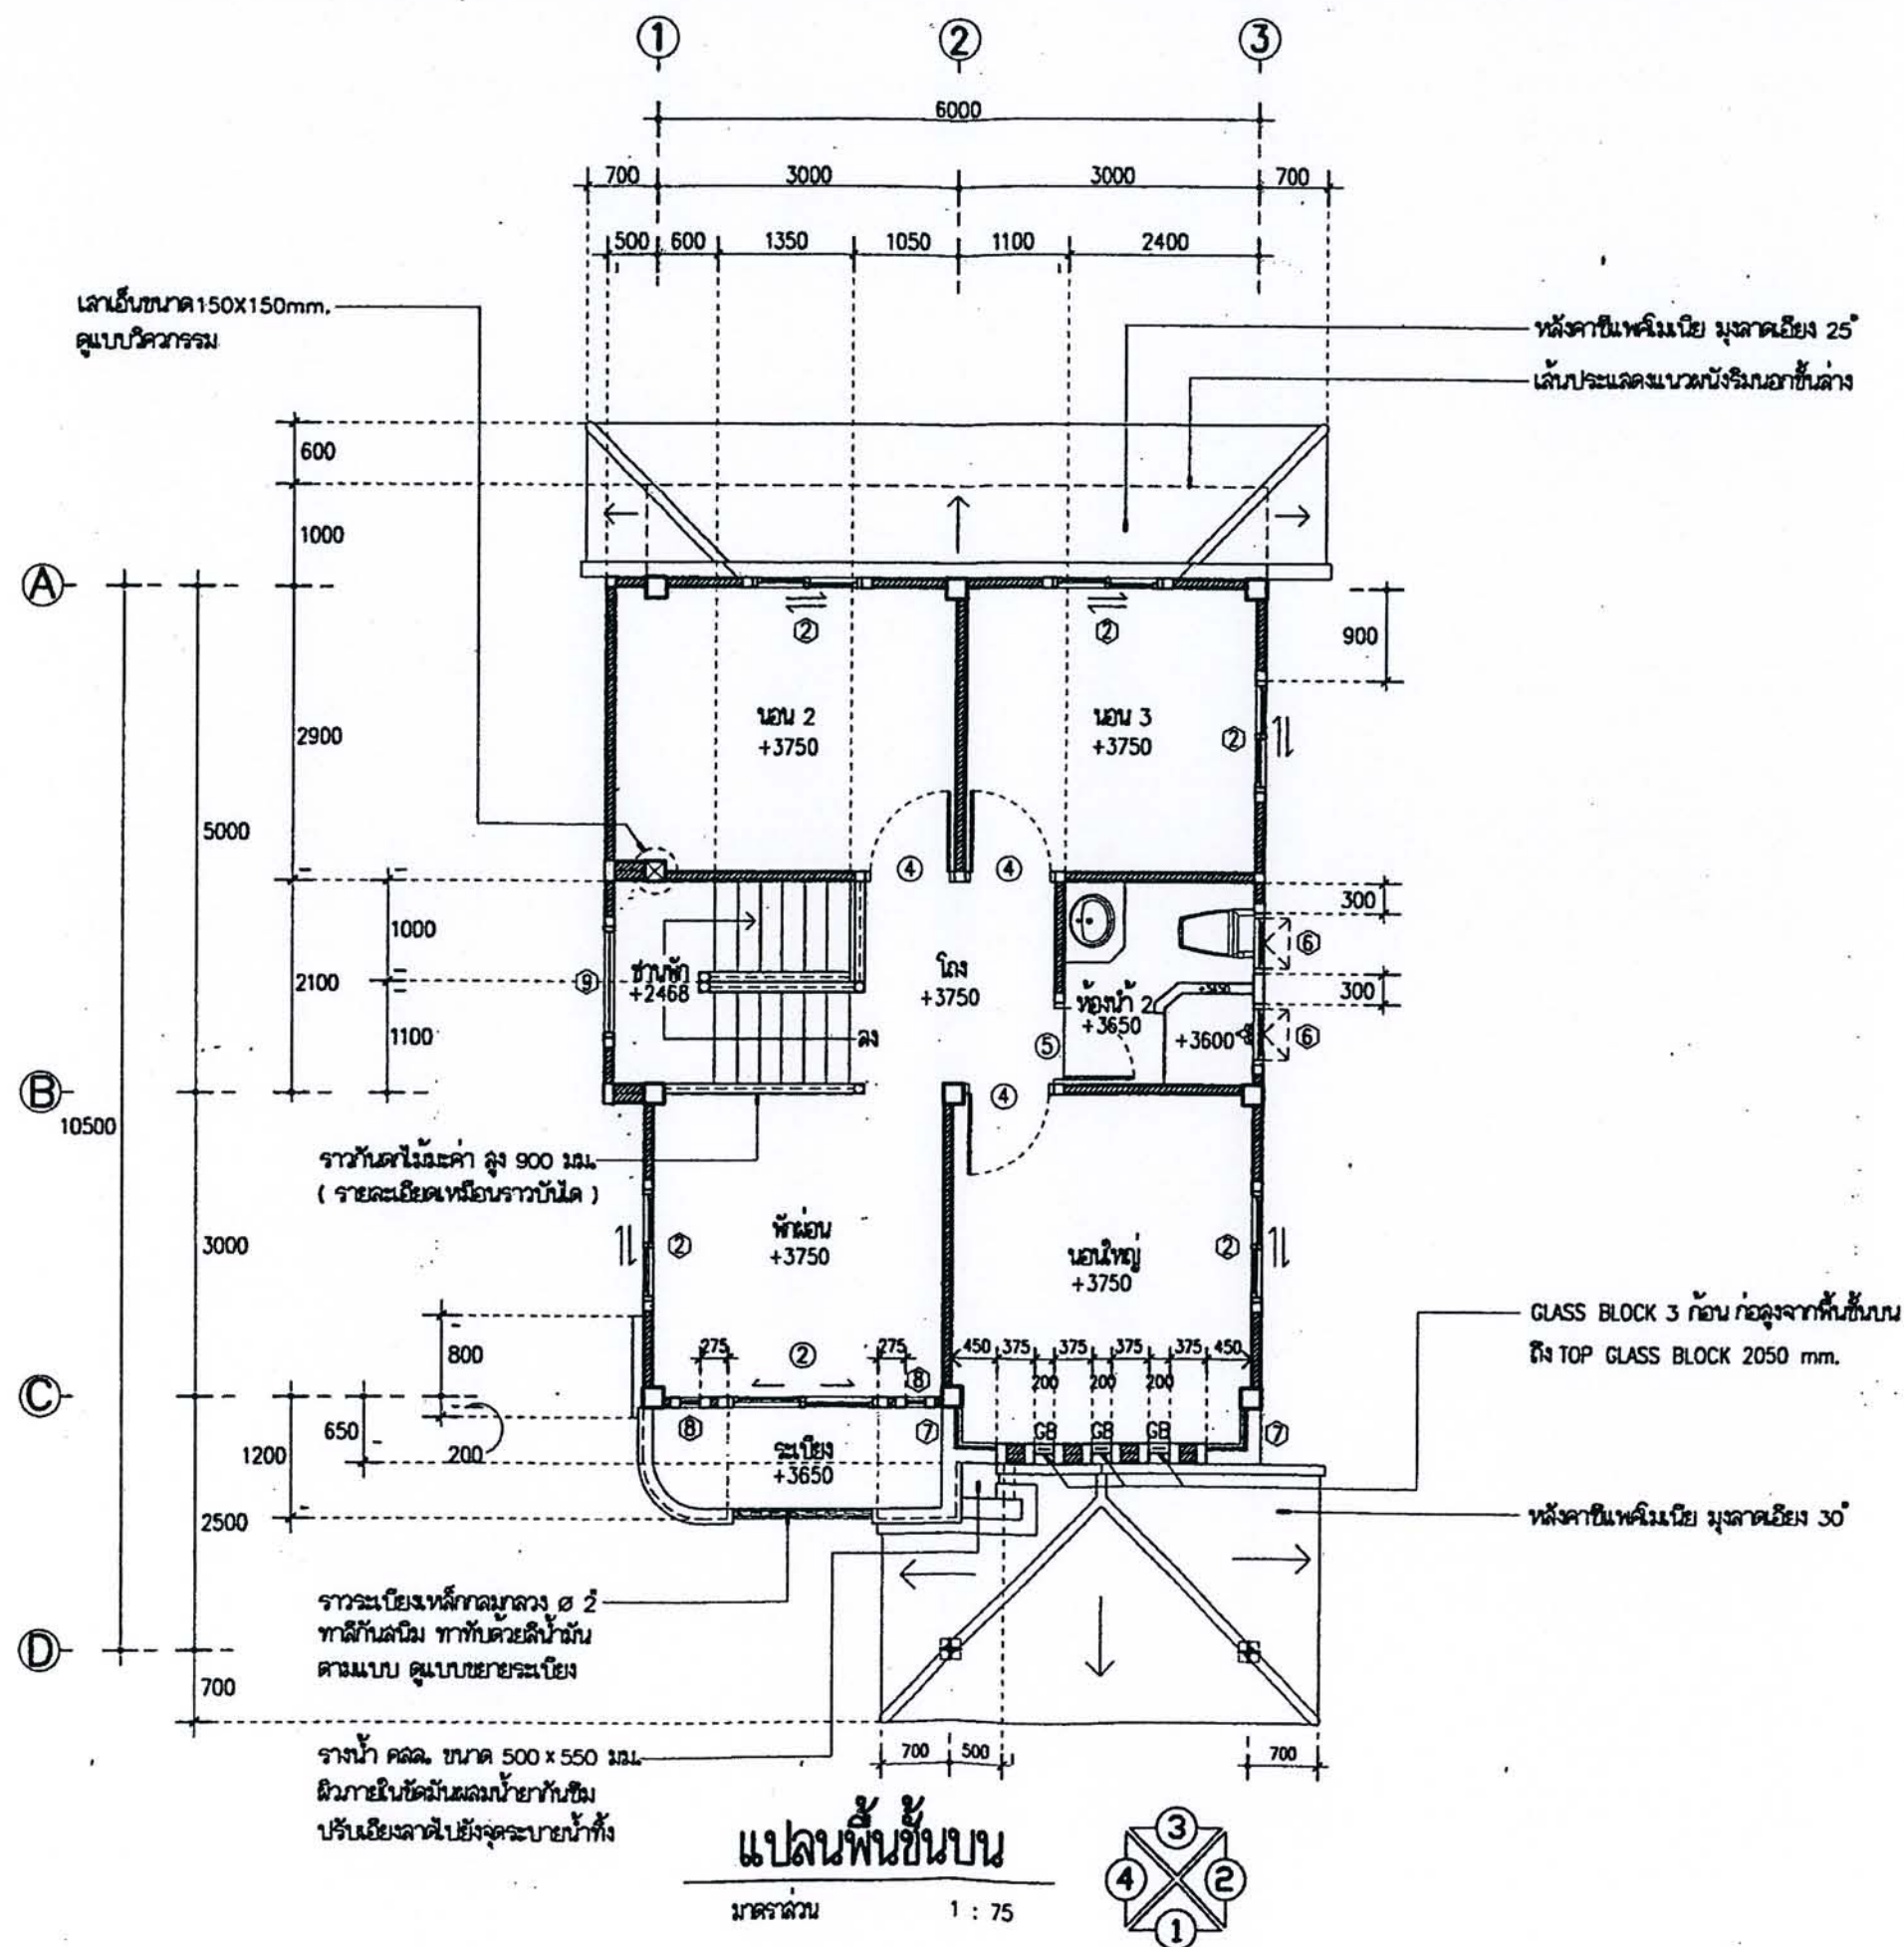


ได้รับความอนุเคราะห์แบบ
จาก
บริษัท แลนด์ โสม
(ประเทศไทย) จำกัด



โครงการ
แบบบ้านยืมเพื่อประชาชน

ตามนโยบาย
ม.ร.ว. สุขุมพันธุ์ บริพัตร
ผู้ว่าราชการกรุงเทพมหานคร

โดยสำนักการโยธา
กรุงเทพมหานคร

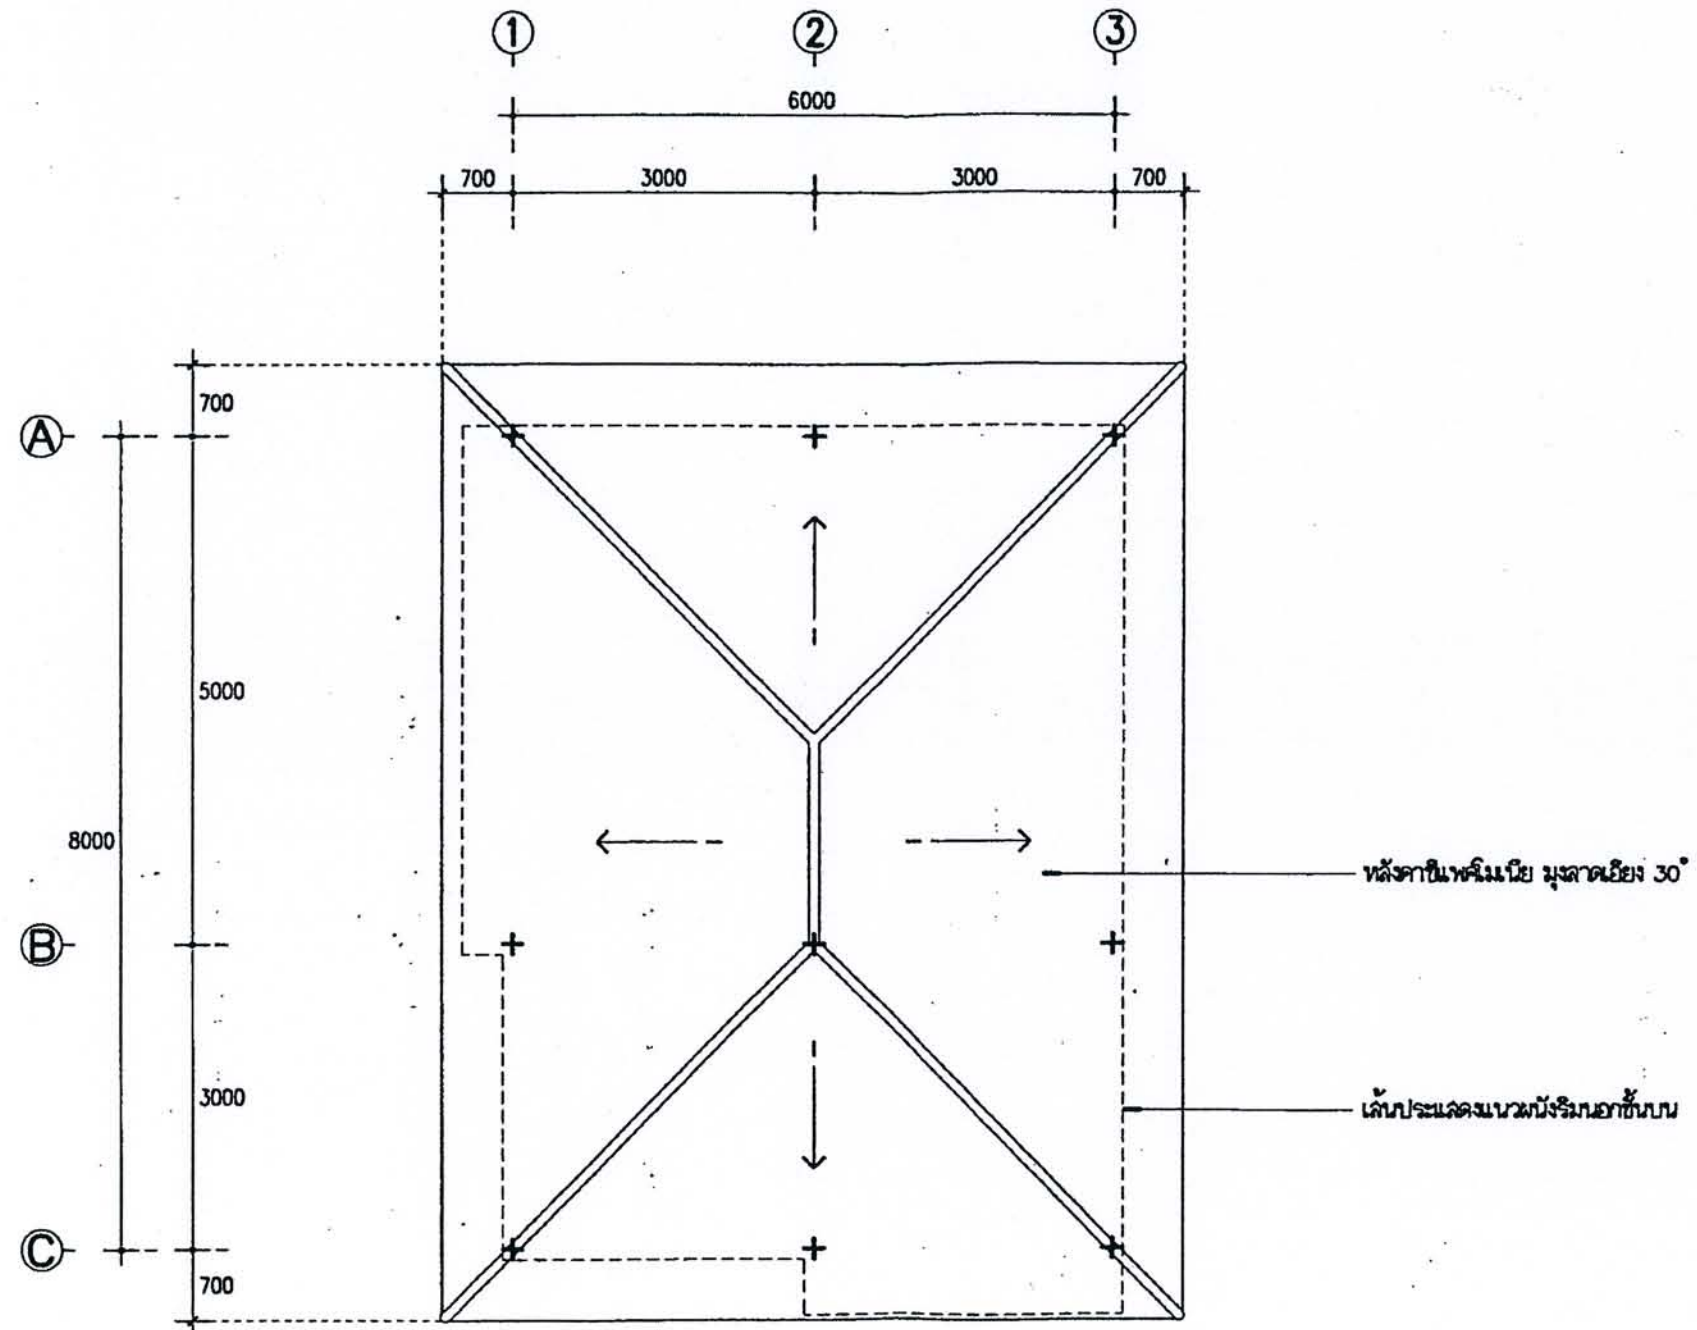

แปลนหลังคา

มาตราส่วน 1 : 75




ได้รับความอนุเคราะห์แบบ
จาก
บริษัท แลนด์ โยม
(ประเทศไทย) จำกัด



โครงการ
แบบบ้านยืมเพื่อประชาชน

ตามนโยบาย
ม.ร.ว. สุขุมพันธุ์ บริพัตร
ผู้ว่าราชการกรุงเทพมหานคร

โดยสำนักการโยธา
กรุงเทพมหานคร

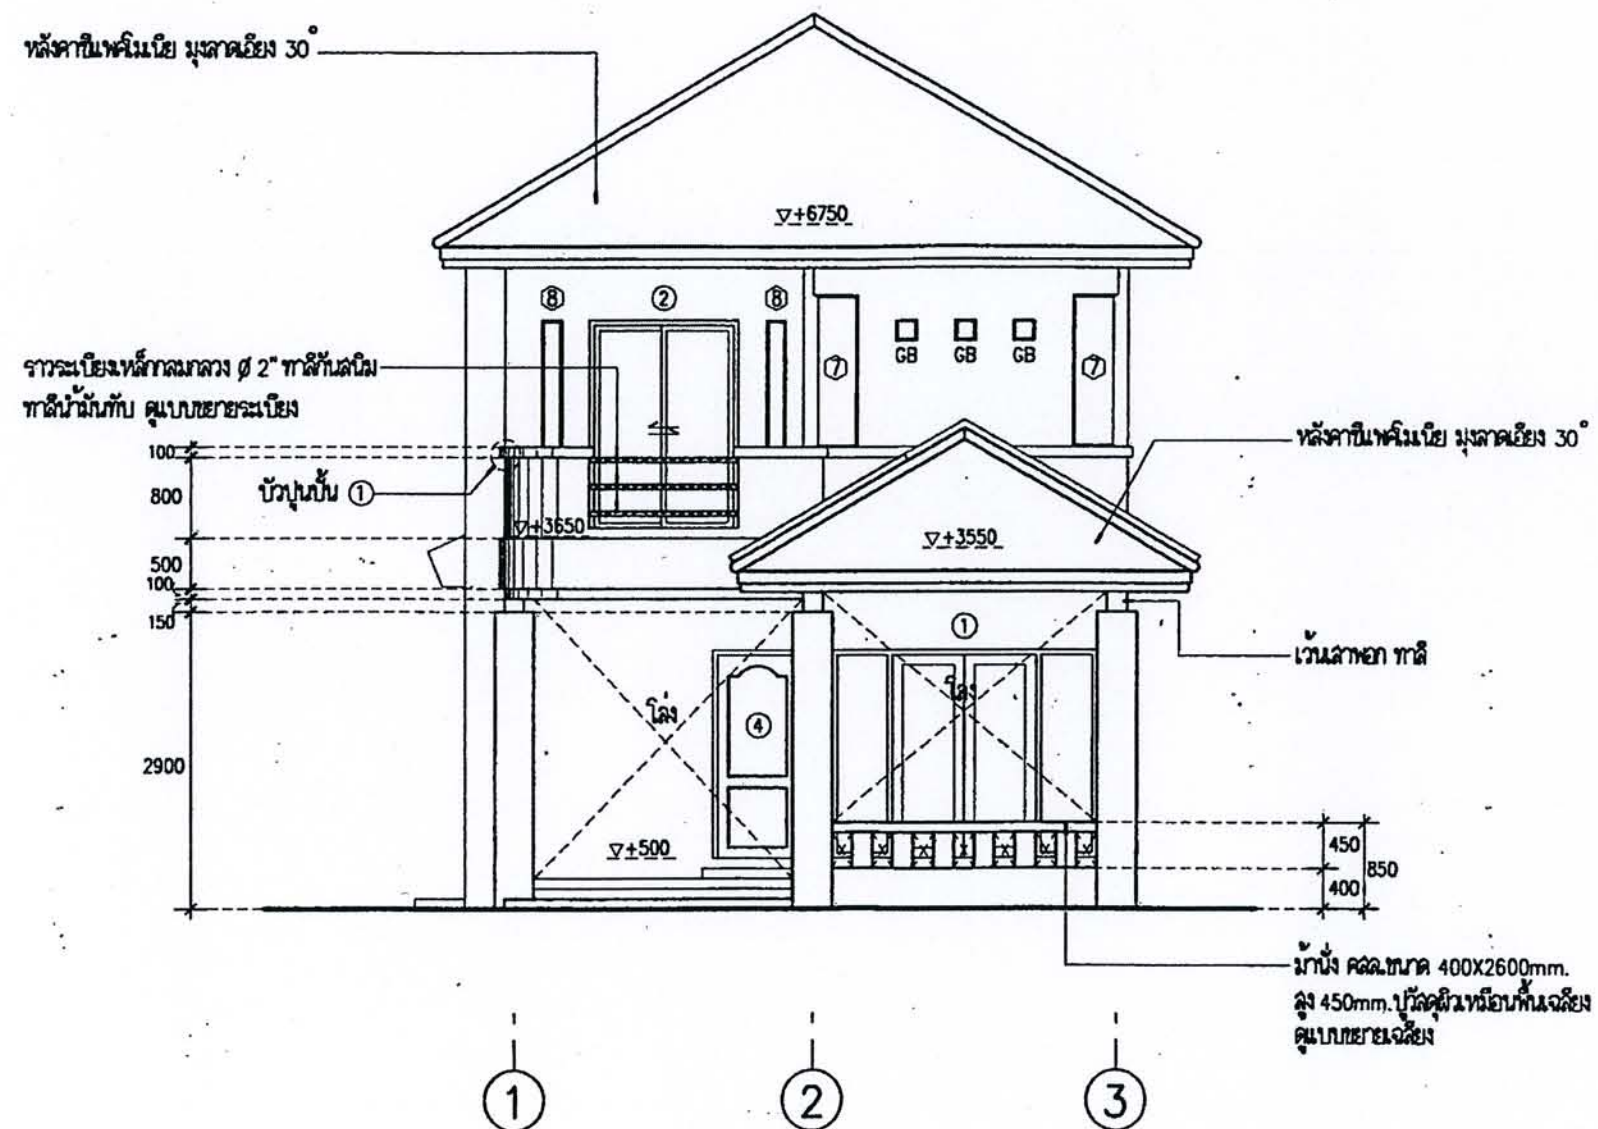

รูปด้าน
มาตราส่วน 1:75


ได้รับความอนุเคราะห์แบบ
จาก
บริษัท แลนด์ โสม
(ประเทศไทย) จำกัด



โครงการ
แบบบ้านยืมเพื่อประชาชน

ตามนโยบาย
ม.ร.ว. สุขุมพันธุ์ บริพัตร
ผู้ว่าราชการกรุงเทพมหานคร

โดยสำนักงานโยธา
กรุงเทพมหานคร

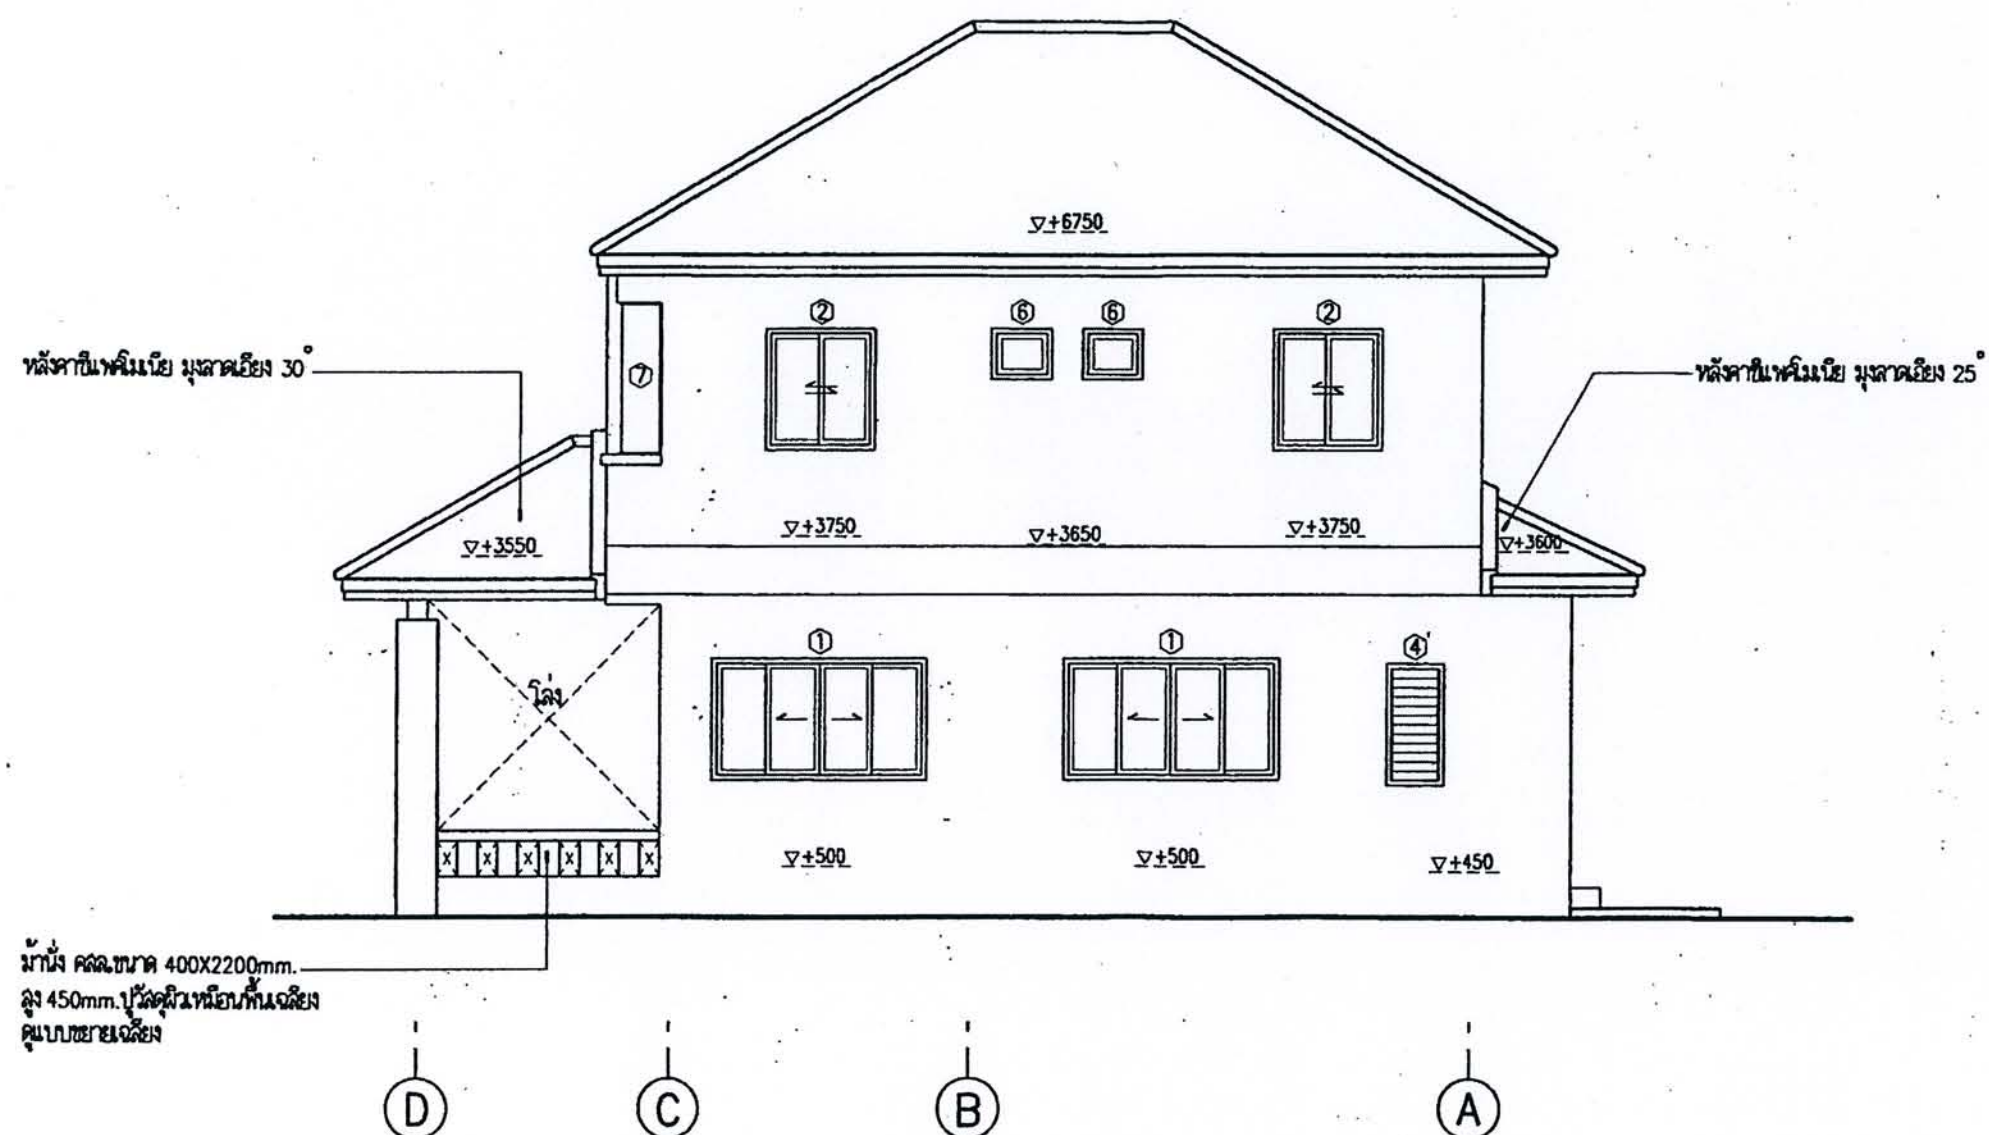

รูปด้าน
มาตราส่วน 1:75


ได้รับความอนุเคราะห์แบบ
จาก
บริษัท แลนด์ โสม
(ประเทศไทย) จำกัด



โครงการ
แบบบ้านยืมเพื่อประชาชน

ตามนโยบาย
ม.ร.ว. สุขุมพันธุ์ บริพัตร
ผู้ว่าราชการกรุงเทพมหานคร

โดยสำนักงานโยธา
กรุงเทพมหานคร

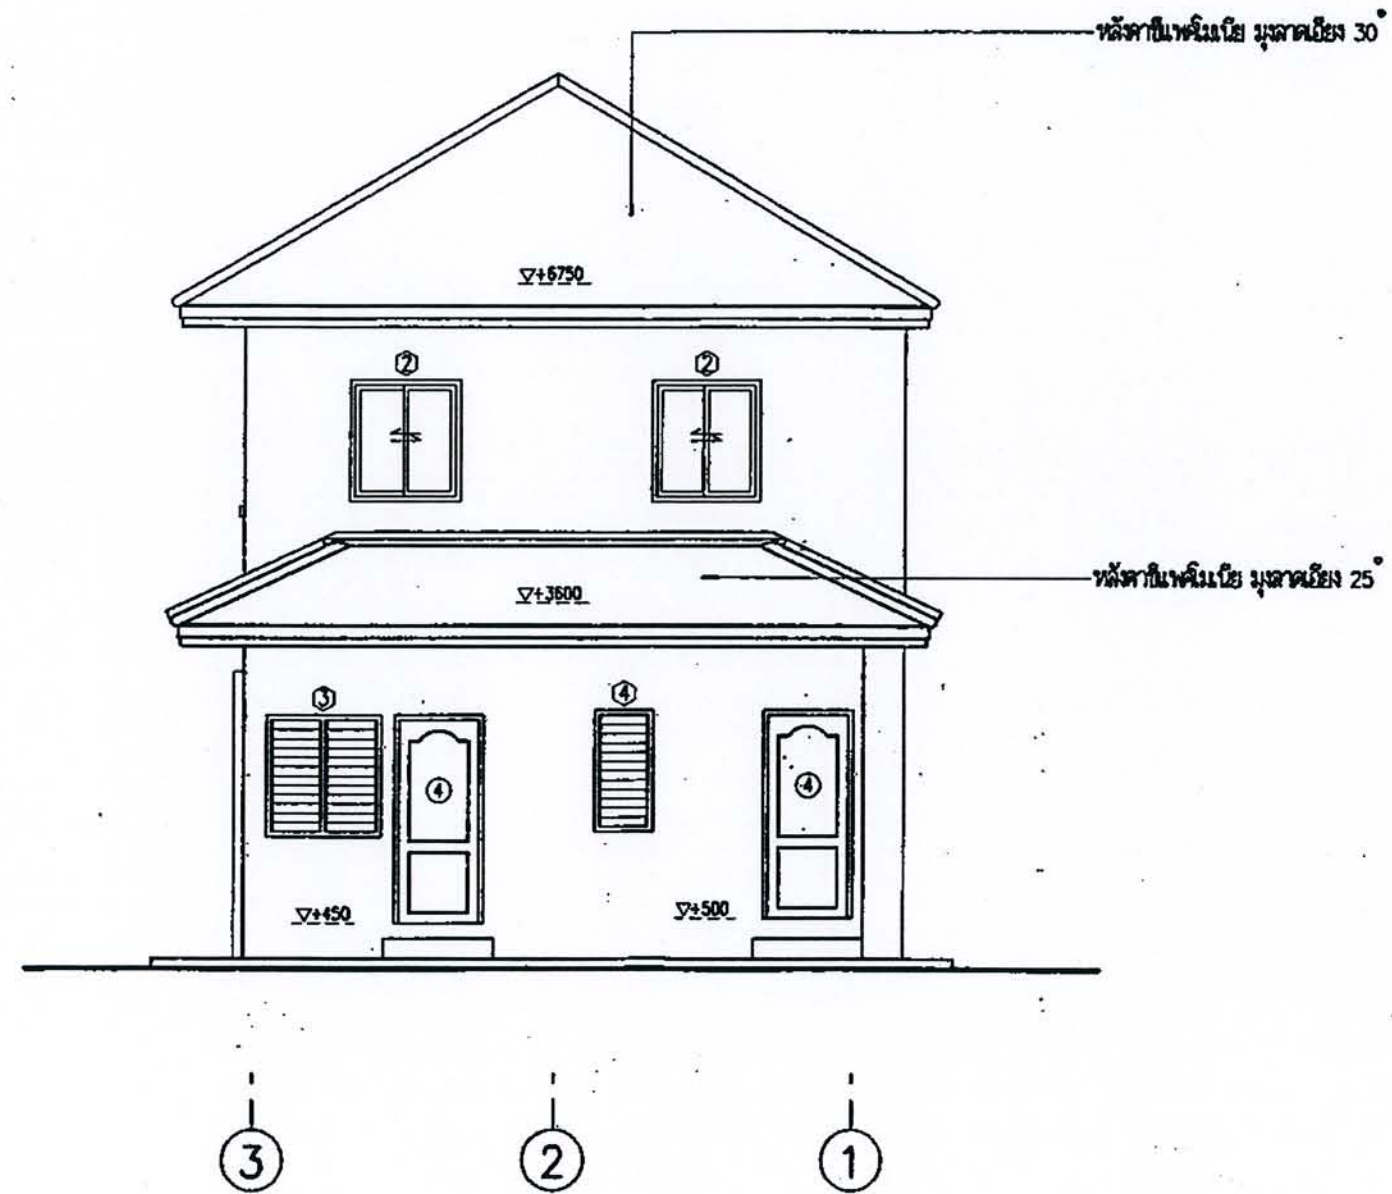

รูปด้าน
มาตราส่วน 1:75


ได้รับความอนุเคราะห์แบบ
จาก
บริษัท แลนด์ โยธ
(ประเทศไทย) จำกัด



โครงการ
แบบบ้านยืมเพื่อประชาชน

ตามนโยบาย
ม.ร.ว. สุขุมพันธุ์ บริพัตร
ผู้ว่าราชการกรุงเทพมหานคร

โดยสำนักงานโยธา
กรุงเทพมหานคร

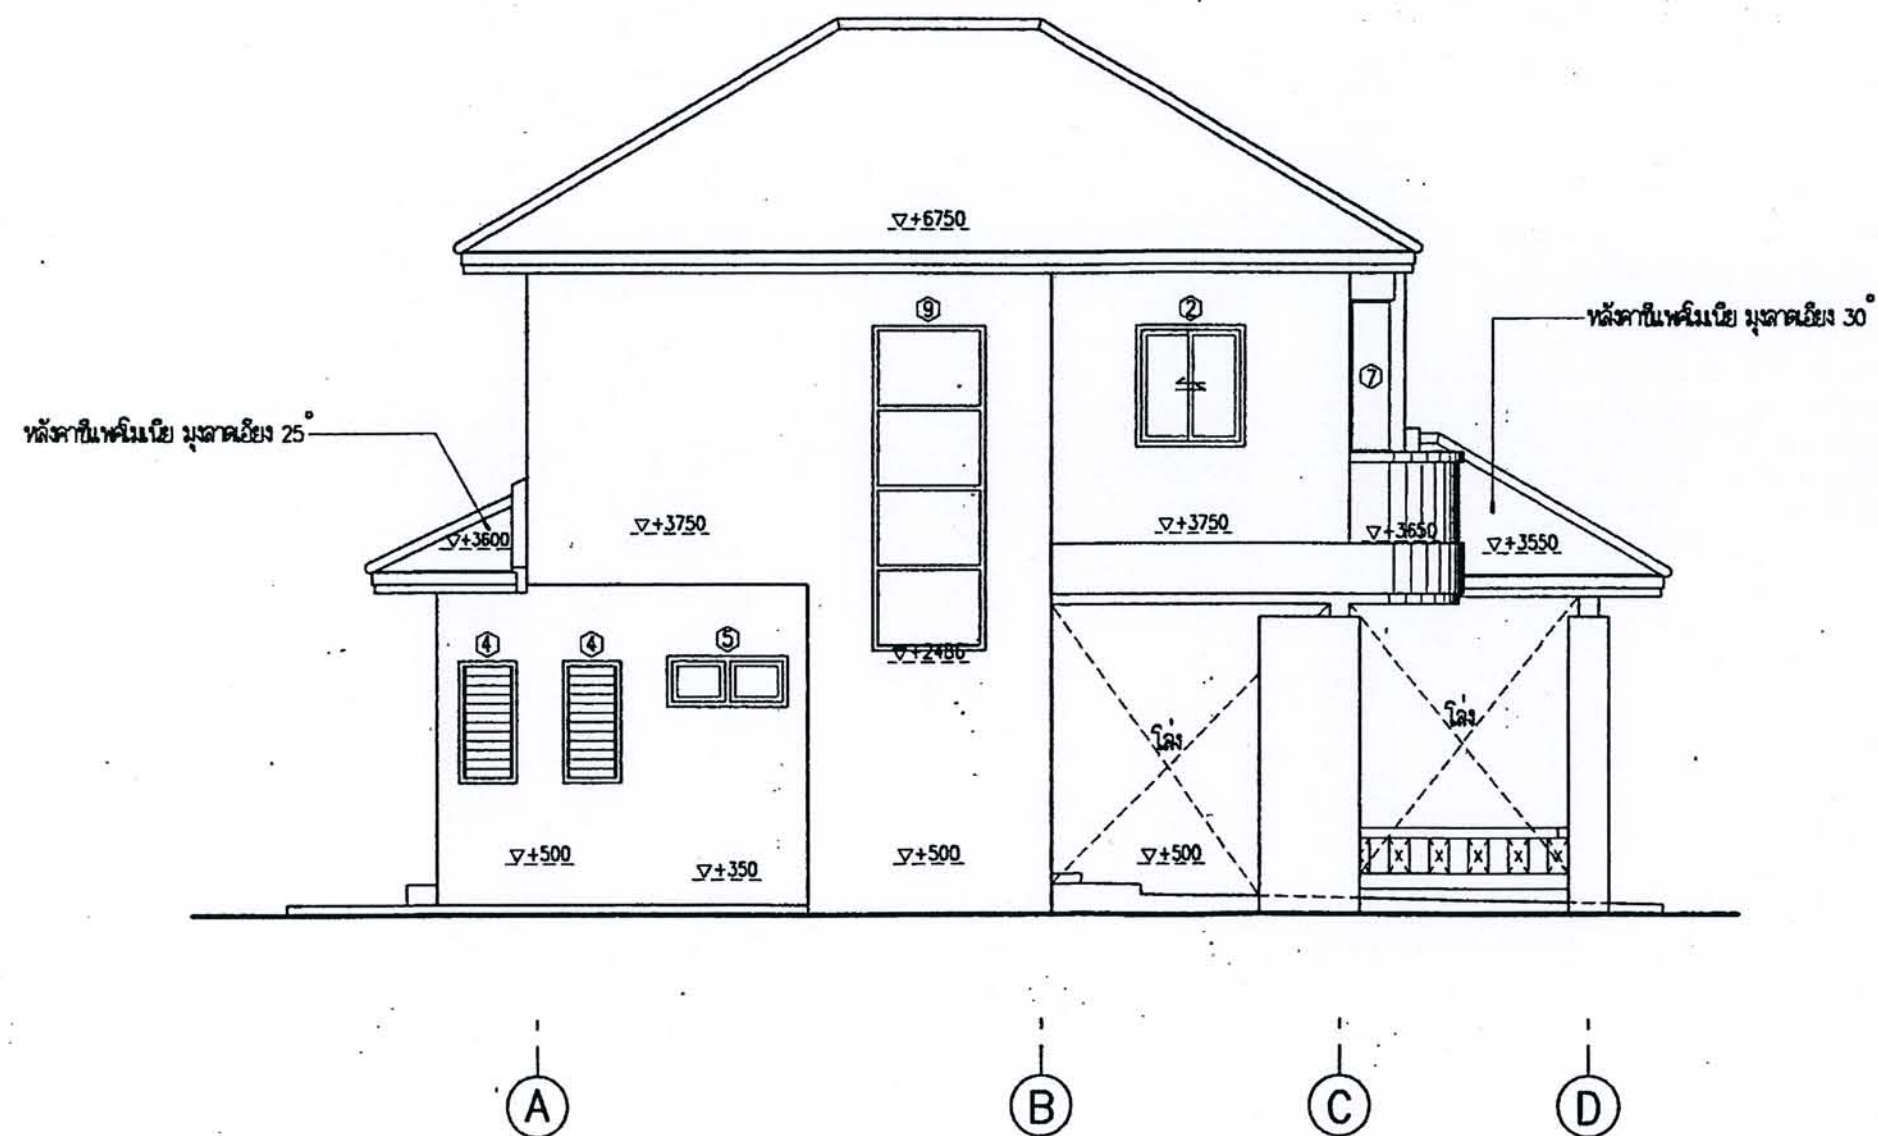


รูปด้าน
มาตราส่วน 1:75

ได้รับความอนุเคราะห์แบบ
จาก
บริษัท แลนด์ โฮม
(ประเทศไทย) จำกัด




ตามนโยบาย
ม.ร.ว. สุขุมพันธุ์ บริพัตร
ผู้ว่าราชการกรุงเทพมหานคร

โดยสำนักงานการโยธา
กรุงเทพมหานคร

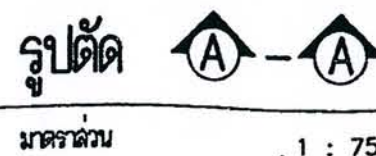

อะเนห์ล้า, ซือเทห์ล้า, คังเทห์ล้า, ยอโกเทห์ล้า, คเมงันเทห์ล้า,
คเมงาเทห์ล้า, จันกันเทห์ล้า, แป้วลวไนย์,
ครายคเมยอด้แปบวิคกรรม

ได้รับความอนุเคราะห์แบบ
จาก
บริษัท แลนด์ โสม
(ประเทศไทย) จำกัด

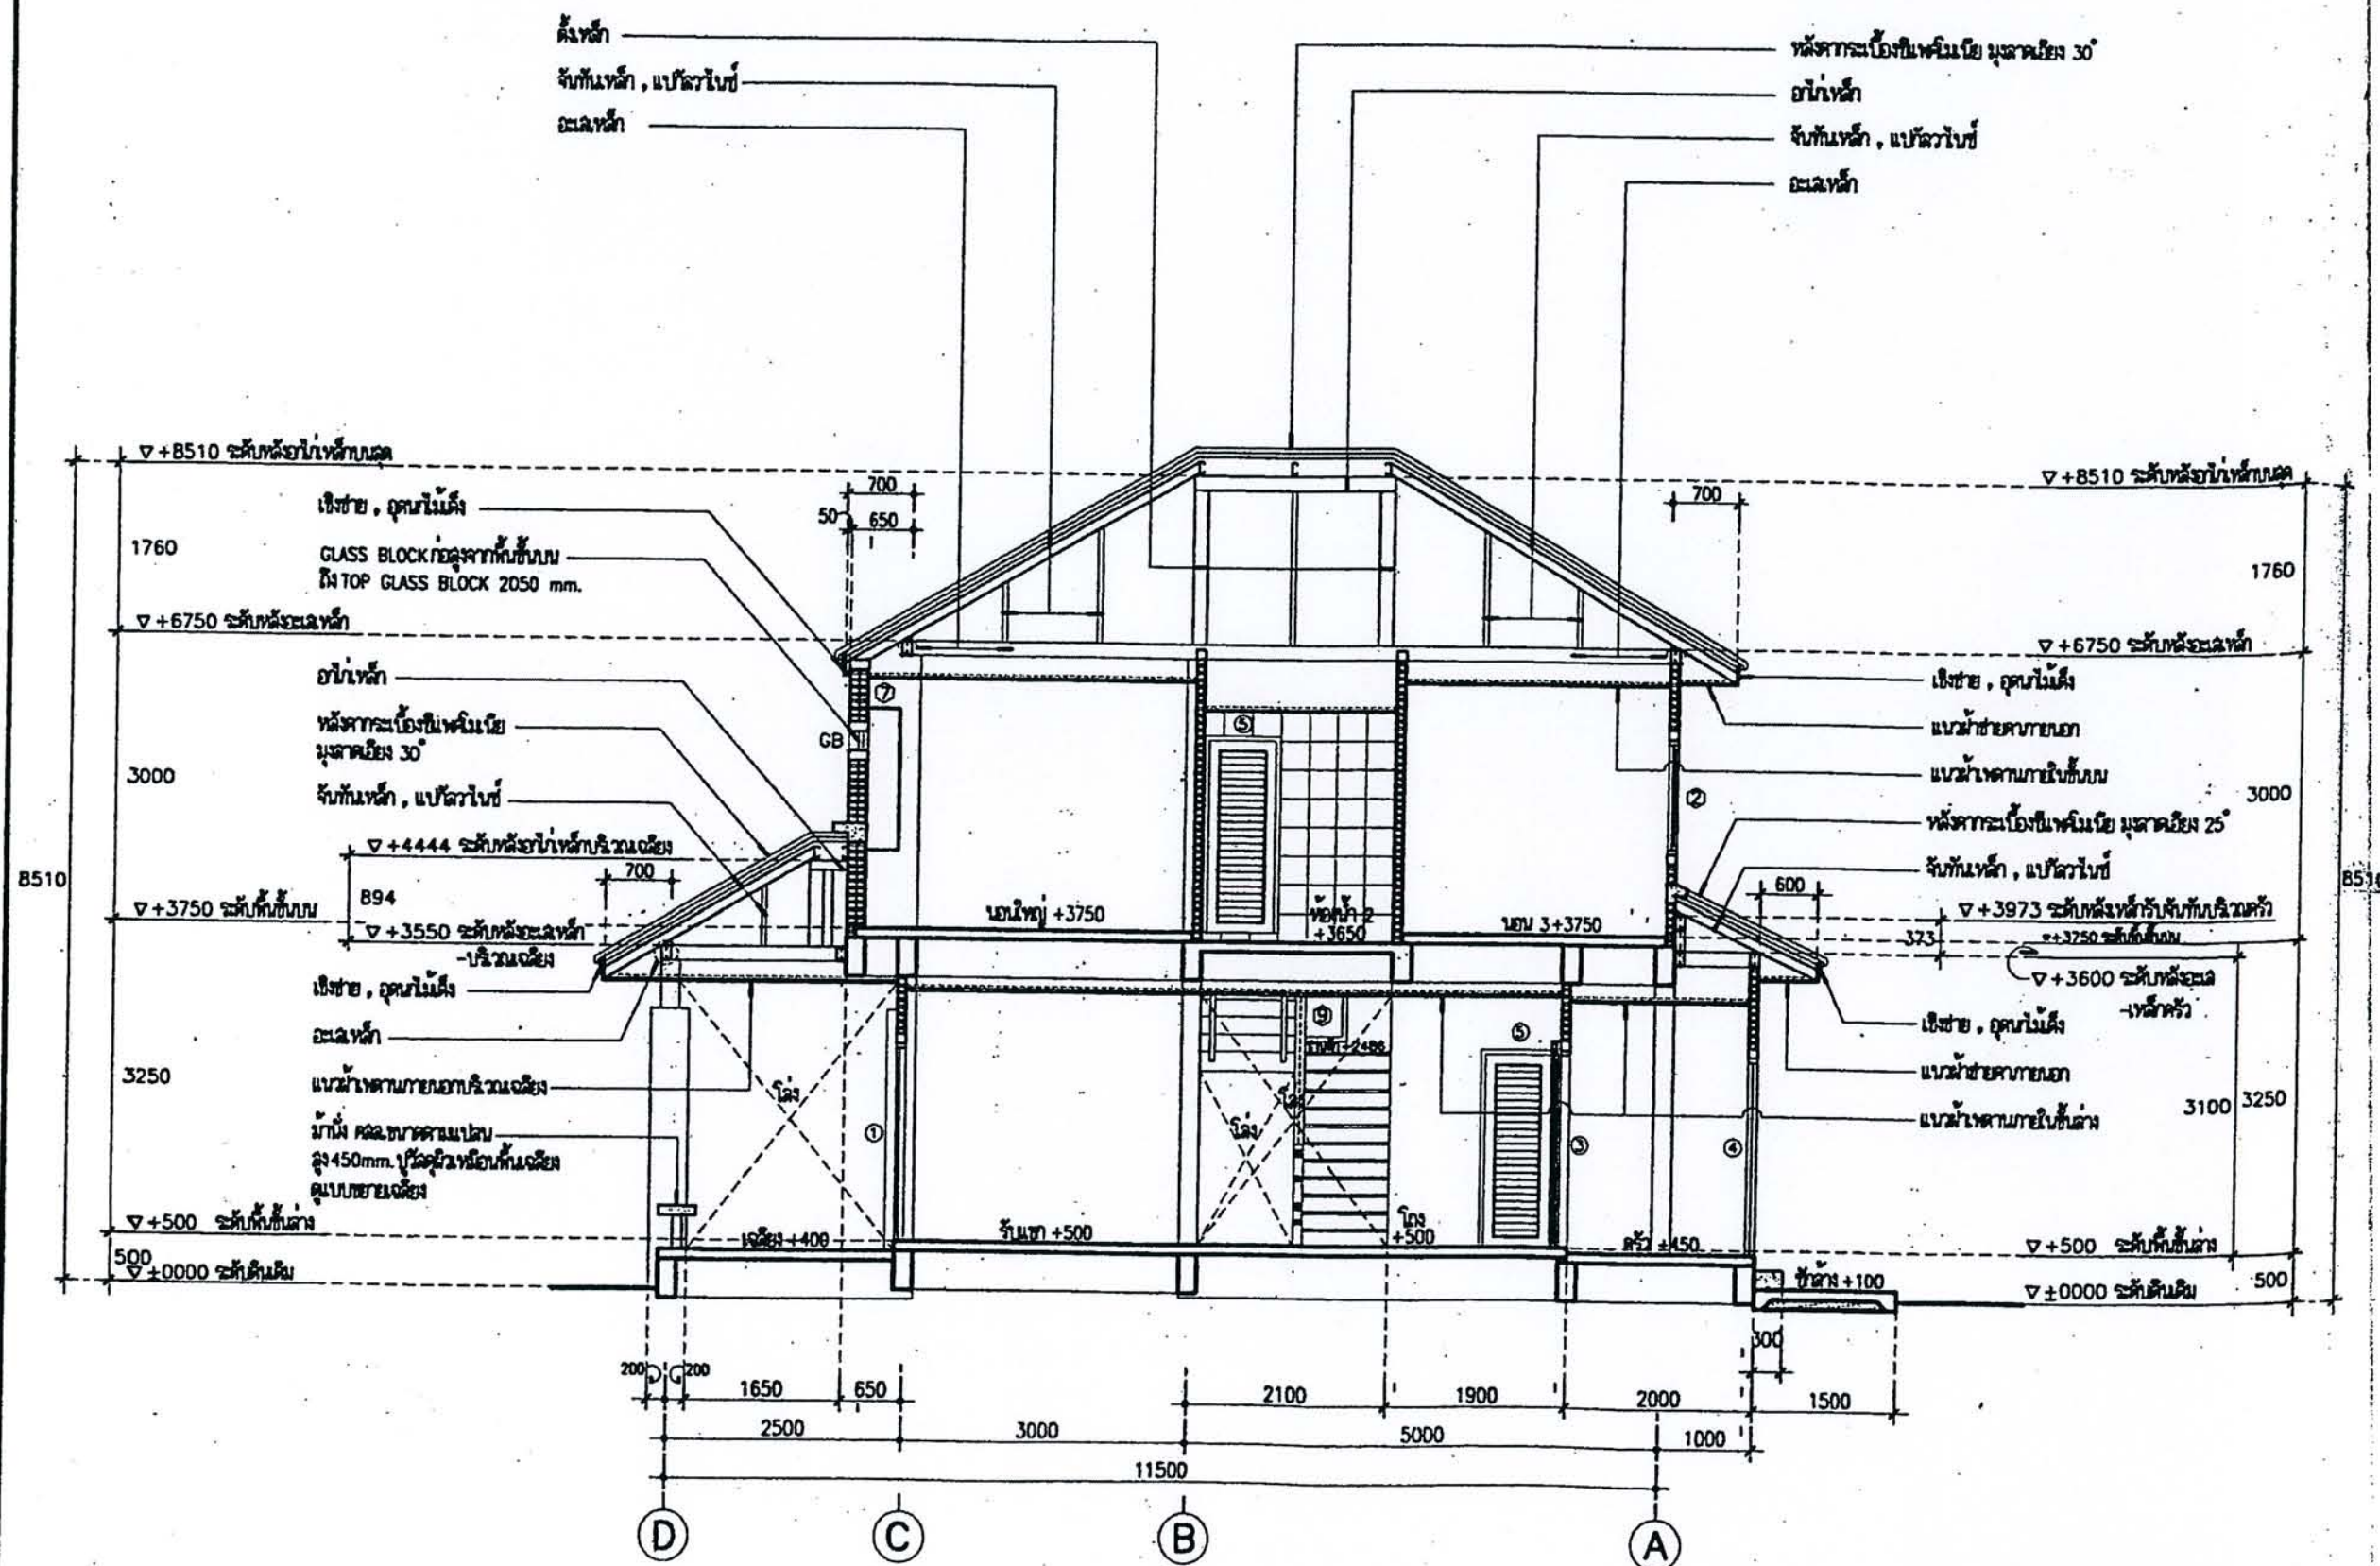

รูปตัด



มาตุราฐาน

1 : 75

อะเลหฺลัน, ช็อหฺลัน, คังหฺลัน, ยักบ์หฺลัน, อะมัลหฺลัน,
อะมฺรฺฮฺลัน, จับกัหฺลัน, แภคฺทฺวีนัน,
ศุรฺยอะมฺยฺยฺดัก์แภบิหฺวกรรม




โครงการ
แบบบ้านยืมเพื่อประชาชน


ตามนโยบาย
ม.ร.ว. สุขุมพันธุ์ บริพัตร
ผู้ว่าราชการกรุงเทพมหานคร

โดยสำนักงานโยธา
กรุงเทพมหานคร


ได้รับความอนุเคราะห์แบบ
จาก
บริษัท แลนด์ โฮม
(ประเทศไทย) จำกัด

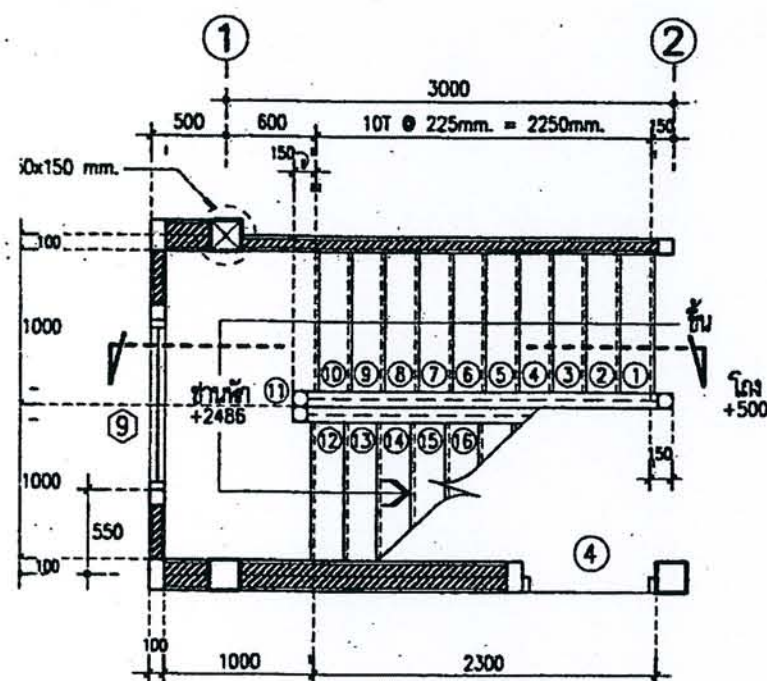

แปลนขยายบันไดชั้นล่าง
มาตรฐาน 1:50

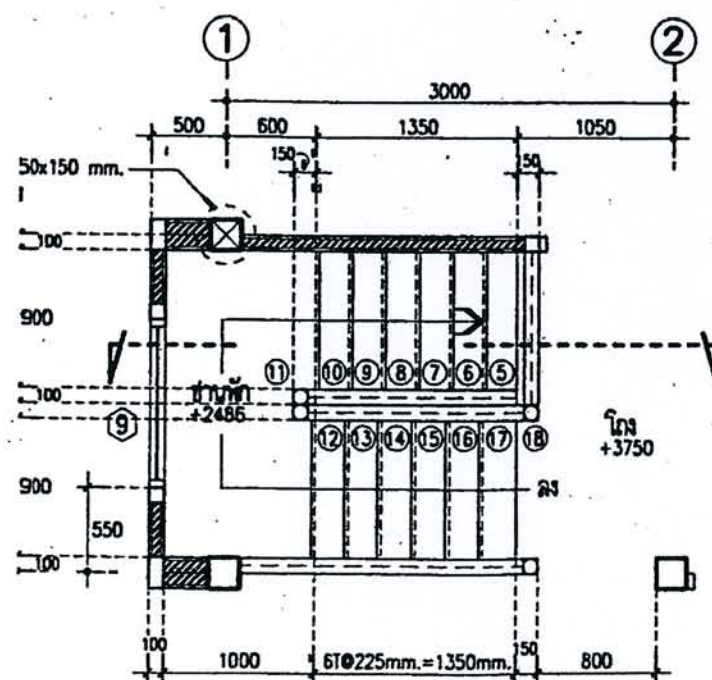

แปลนขยายบันไดชั้นบน
มาตรฐาน 1:50

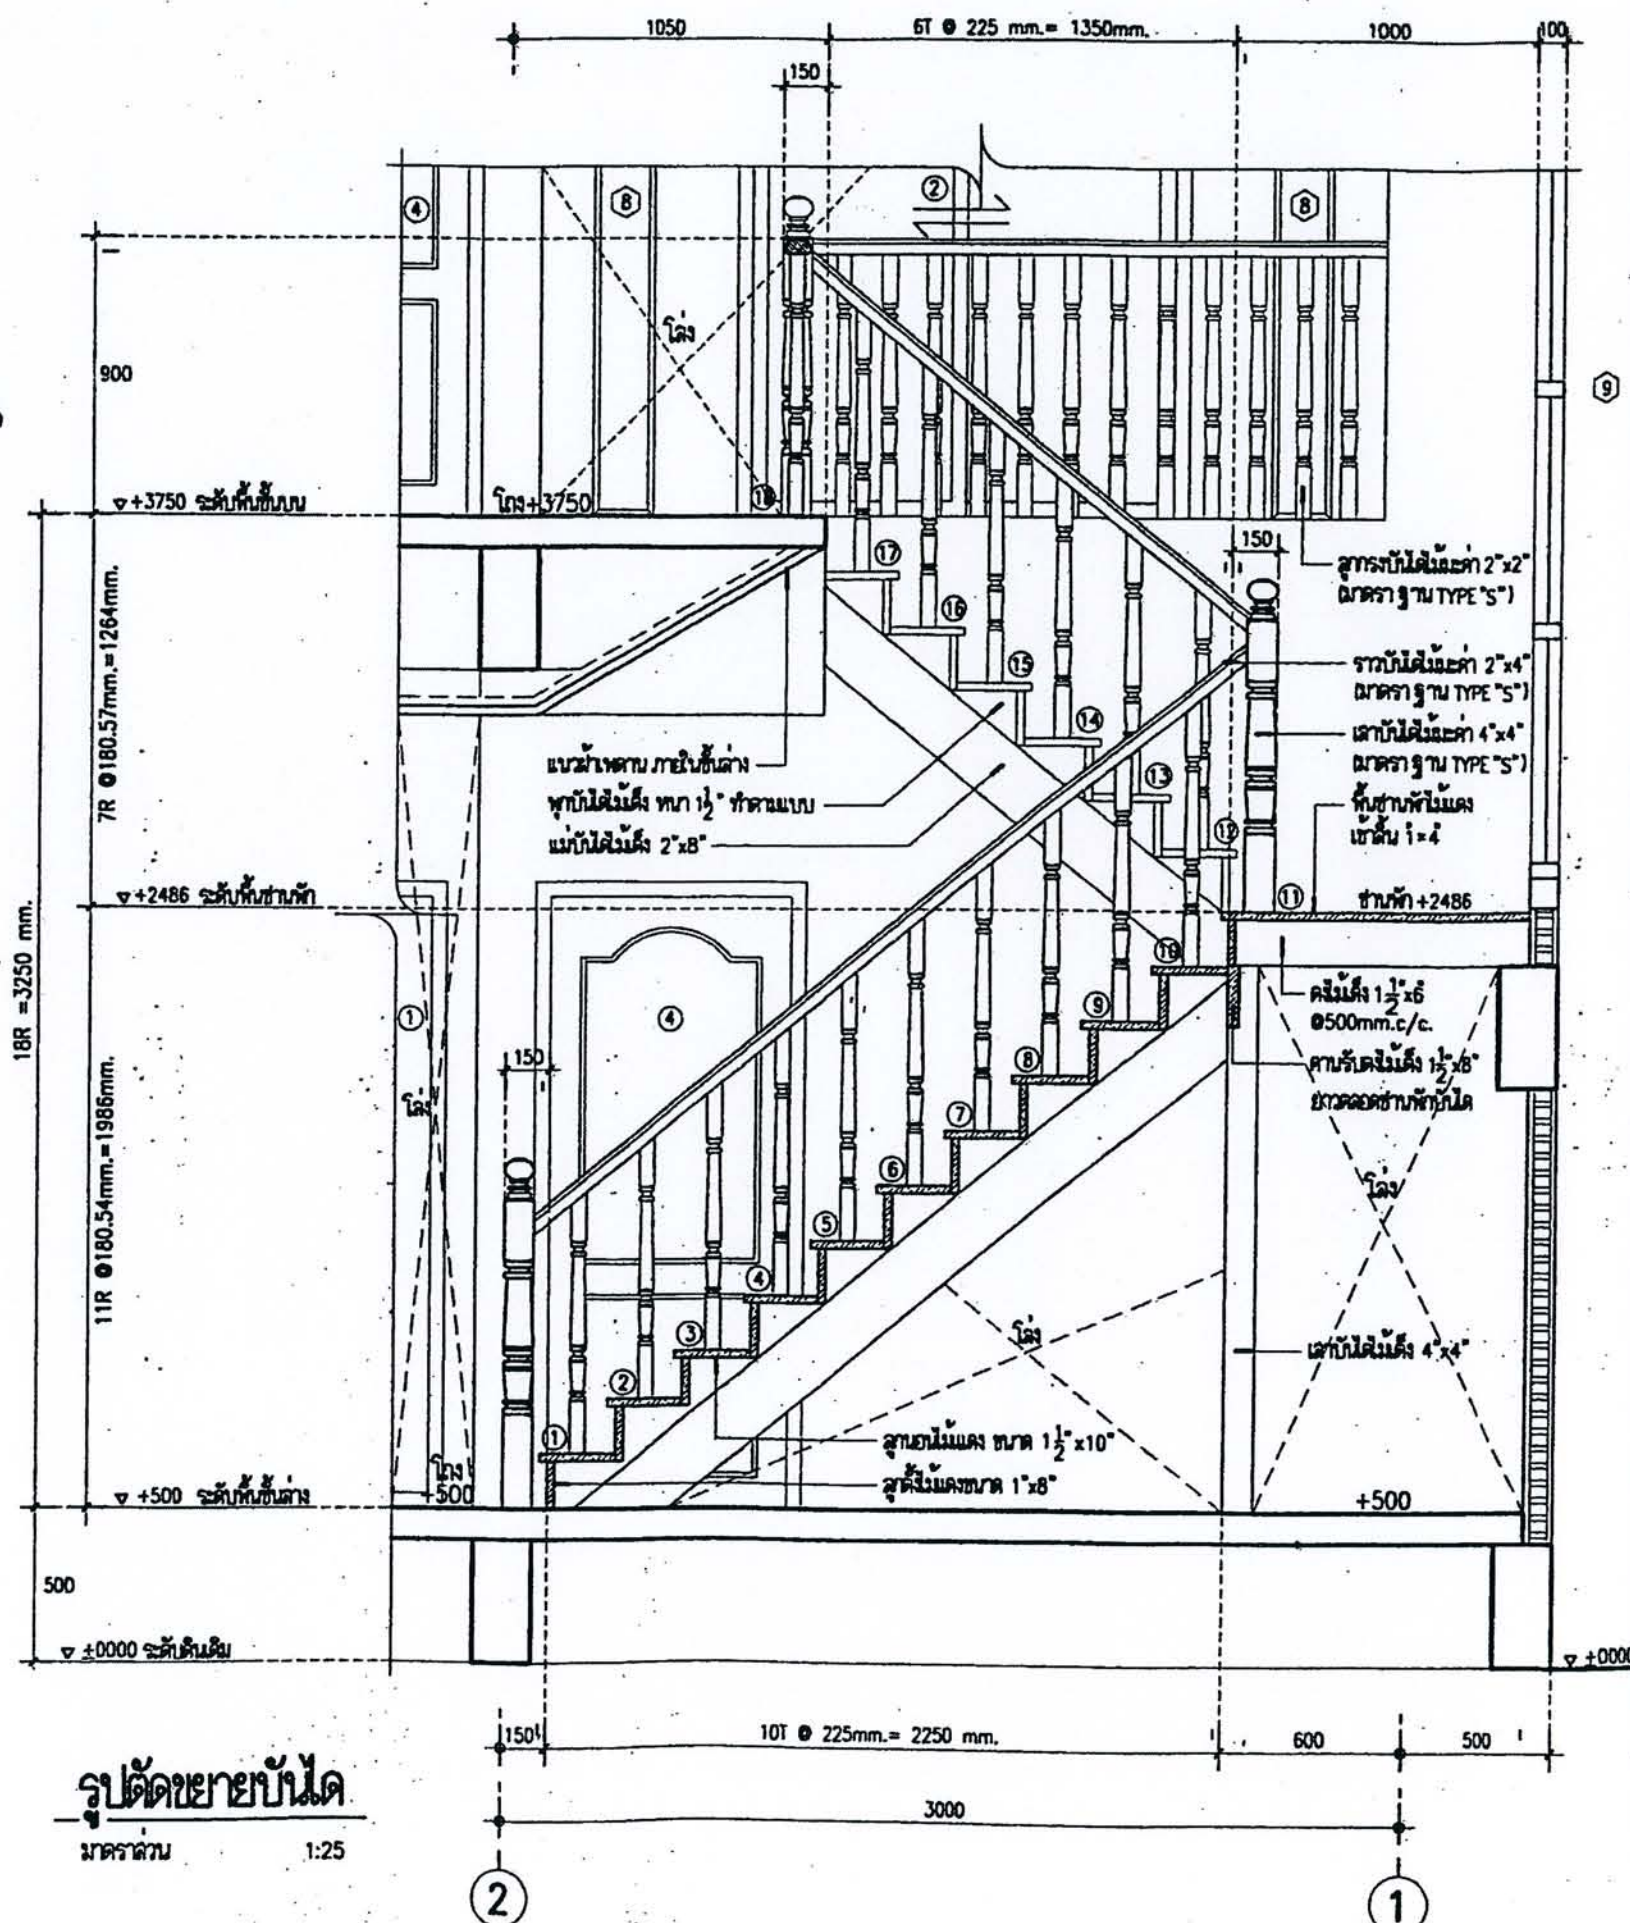

รูปตัดขยายบันได
มาตรฐาน 1:25







โครงการ
แบบบ้านยืมเพื่อประชาชน

ตามนโยบาย
ม.ร.ว. สุขุมพันธุ์ บริพัตร
ผู้ว่าราชการกรุงเทพมหานคร

โดยสำนักการโยธา
กรุงเทพมหานคร

ได้รับความอนุเคราะห์แบบ
จาก
บริษัท แลนด์ โธม
(ประเทศไทย) จำกัด

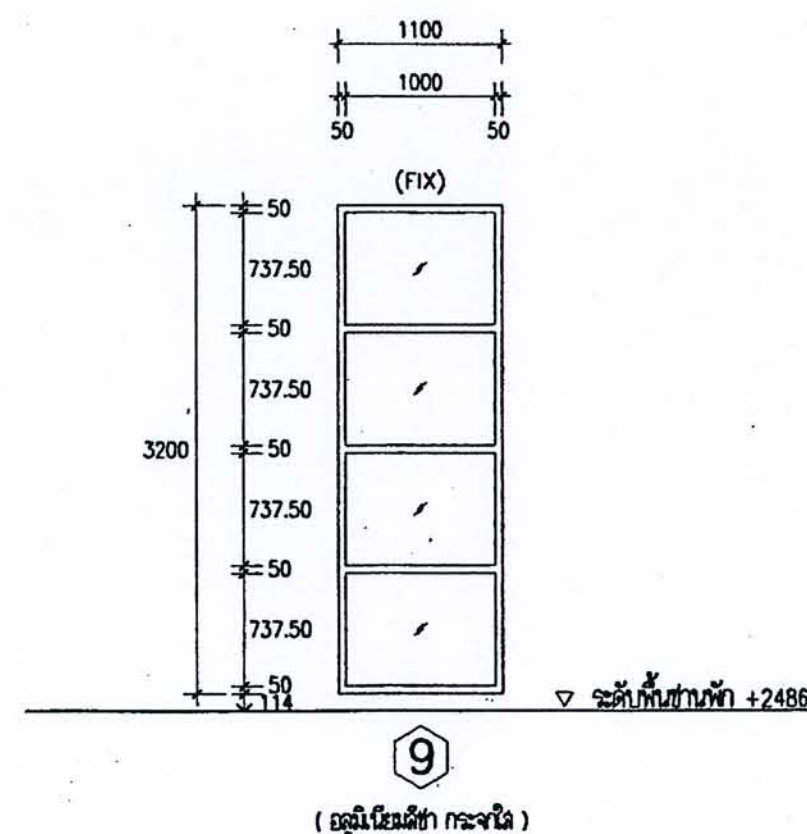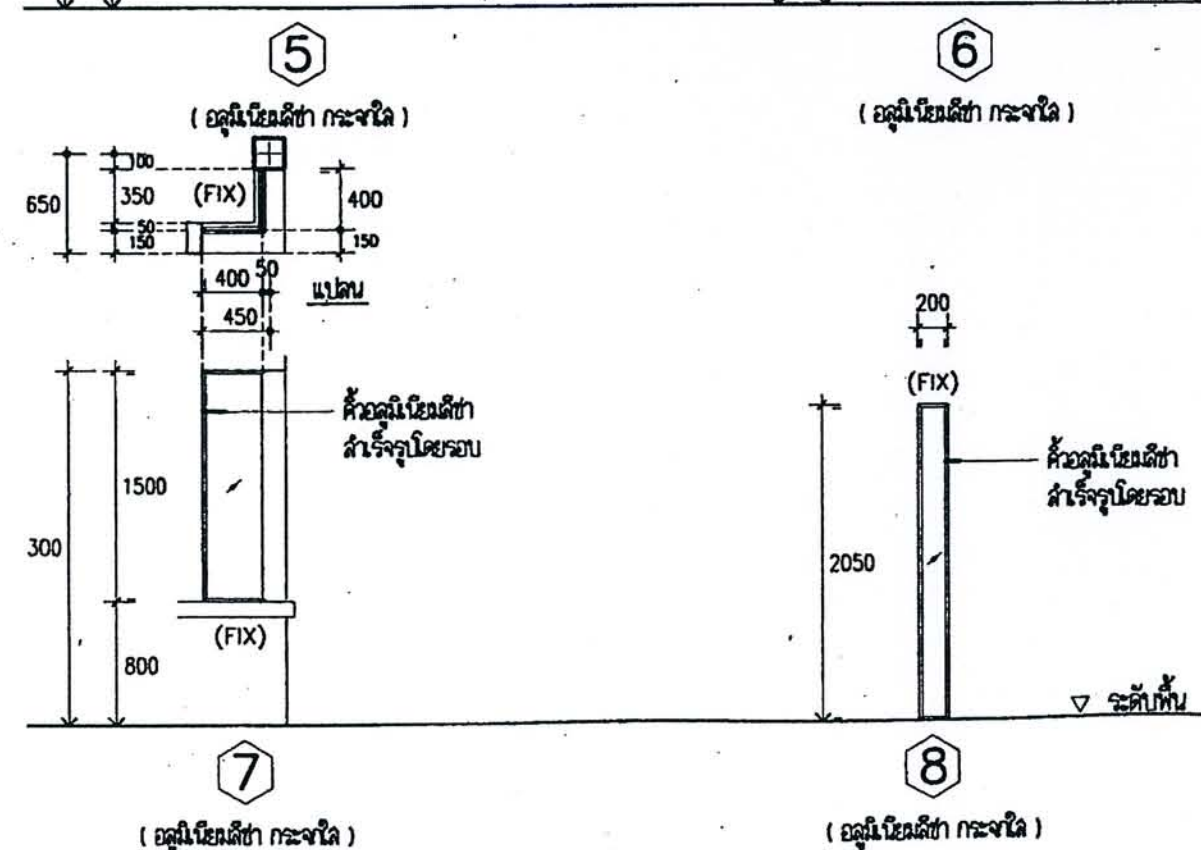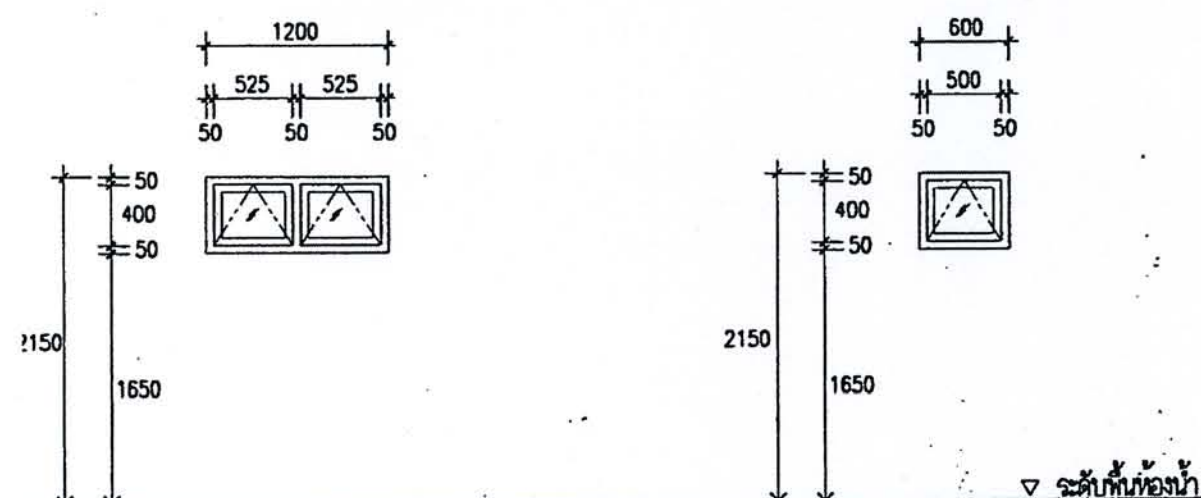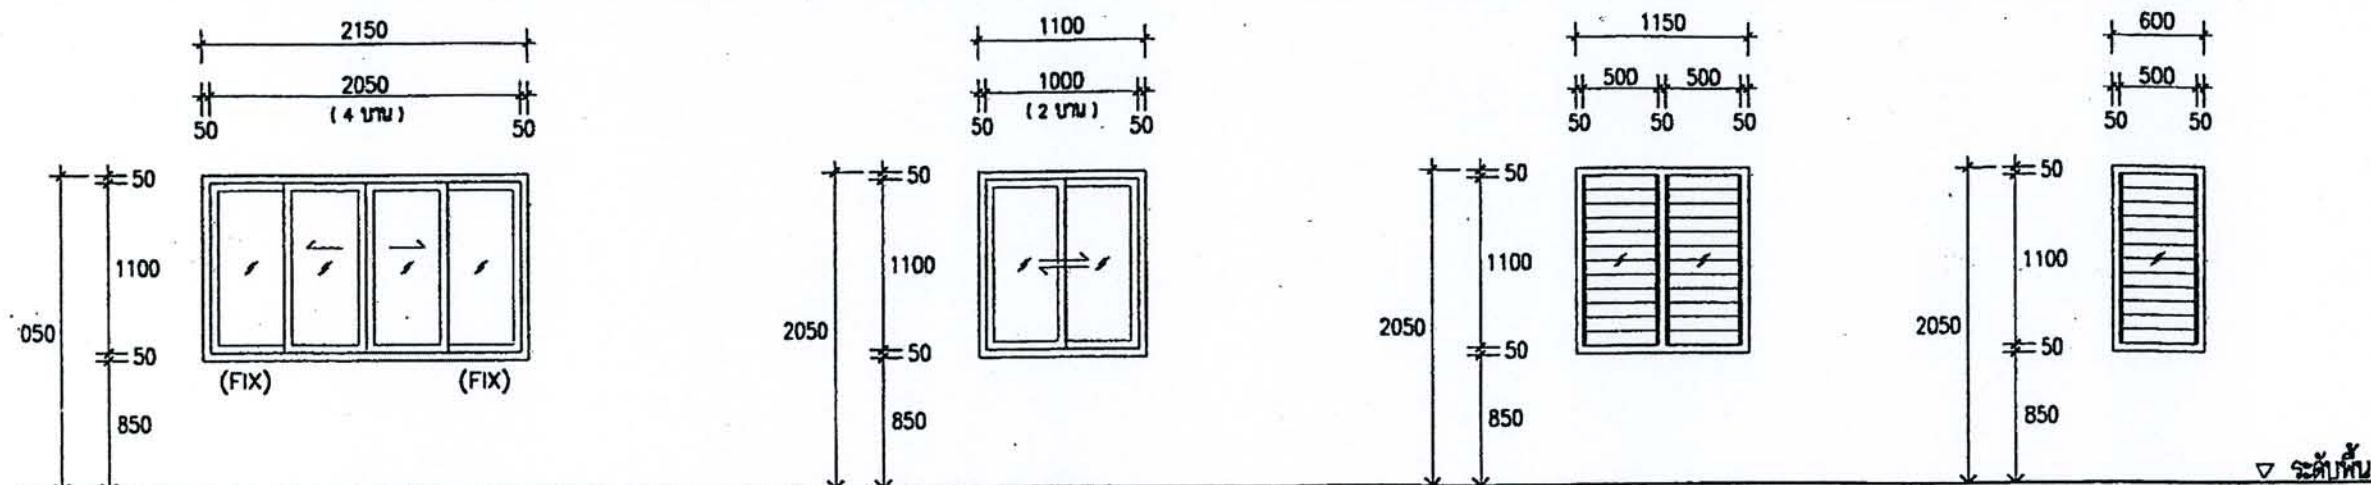

แบบขยายหน้าต่าง

มาตราส่วน 1 : 50




โครงการ
แบบบ้านยืมเพื่อประชาชน

ตามนโยบาย
ม.ร.ว. สุขุมพันธุ์ บริพัตร
ผู้ว่าราชการกรุงเทพมหานคร

โดยสำนักงานโยธา
กรุงเทพมหานคร

ได้รับความอนุเคราะห์แบบ
จาก
บริษัท แลนด์ ไชย
(ประเทศไทย) จำกัด

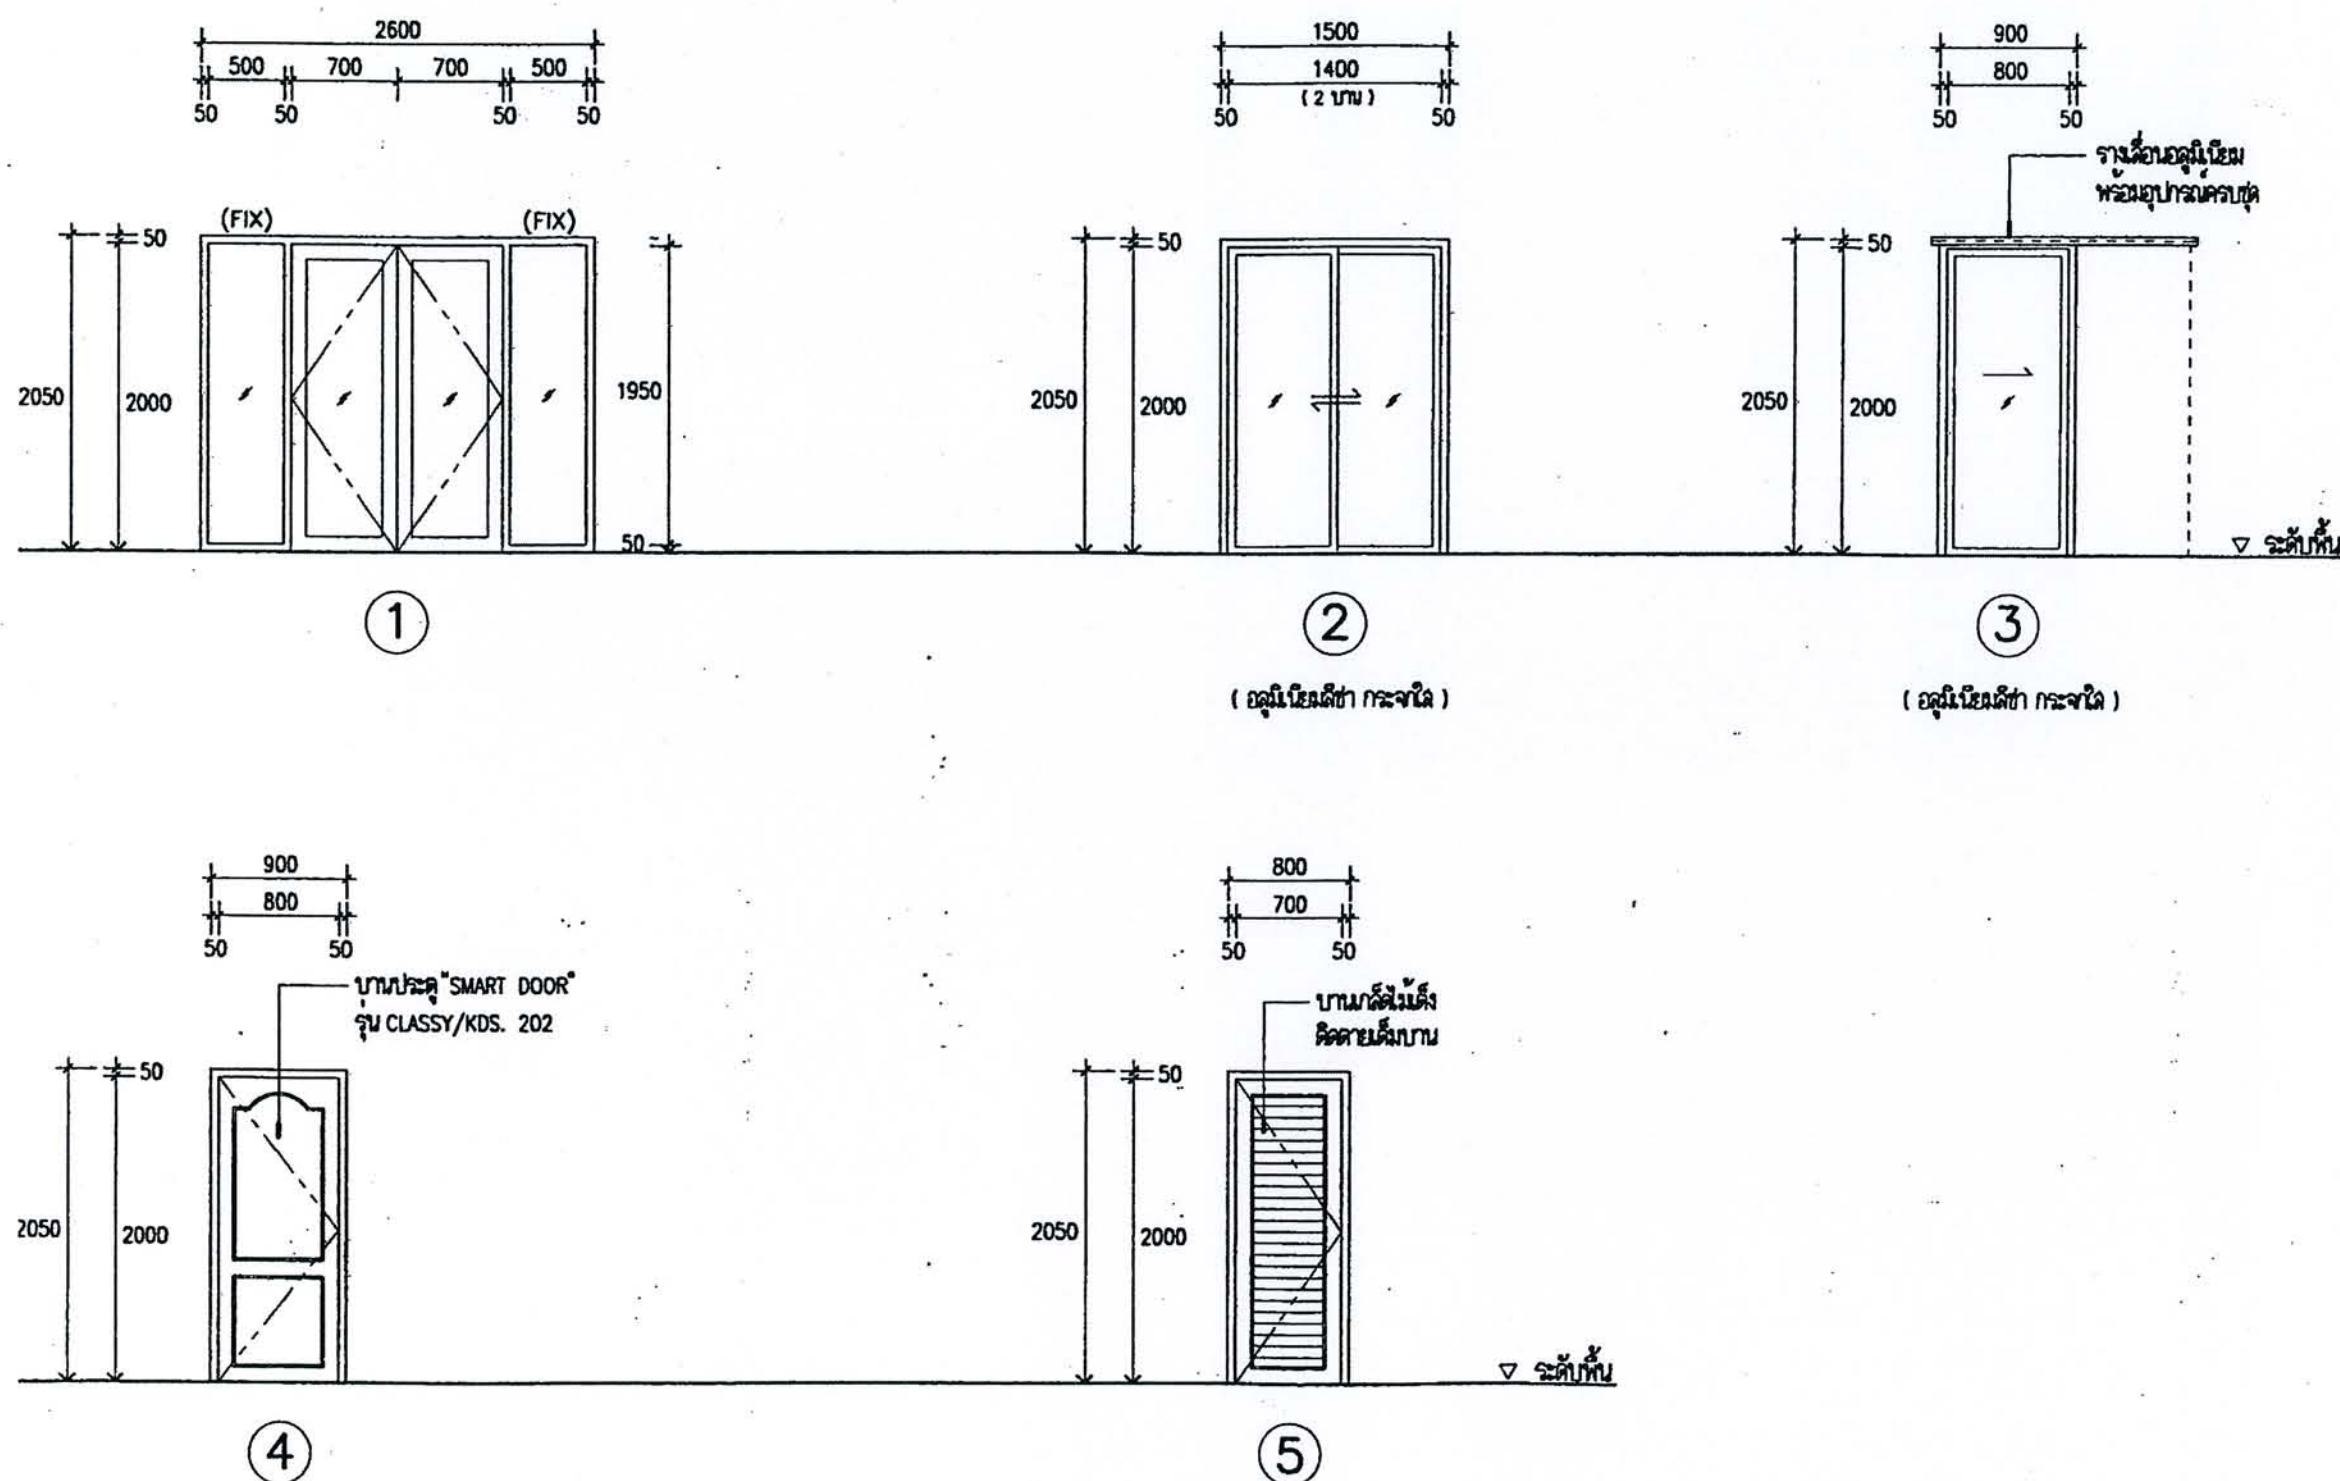

แบบขยายประตู
มาตราส่วน 1 : 50




โครงการ
แบบบ้านยืมเพื่อประชาชน

ตามนโยบาย
ม.ร.ว. สุขุมพันธุ์ บริพัตร
ผู้ว่าราชการกรุงเทพมหานคร

โดยสำนักงานโยธา
กรุงเทพมหานคร


ได้รับความอนุเคราะห์แบบ
จาก
บริษัท แลนด์ โสม
ประเทศไทย จำกัด

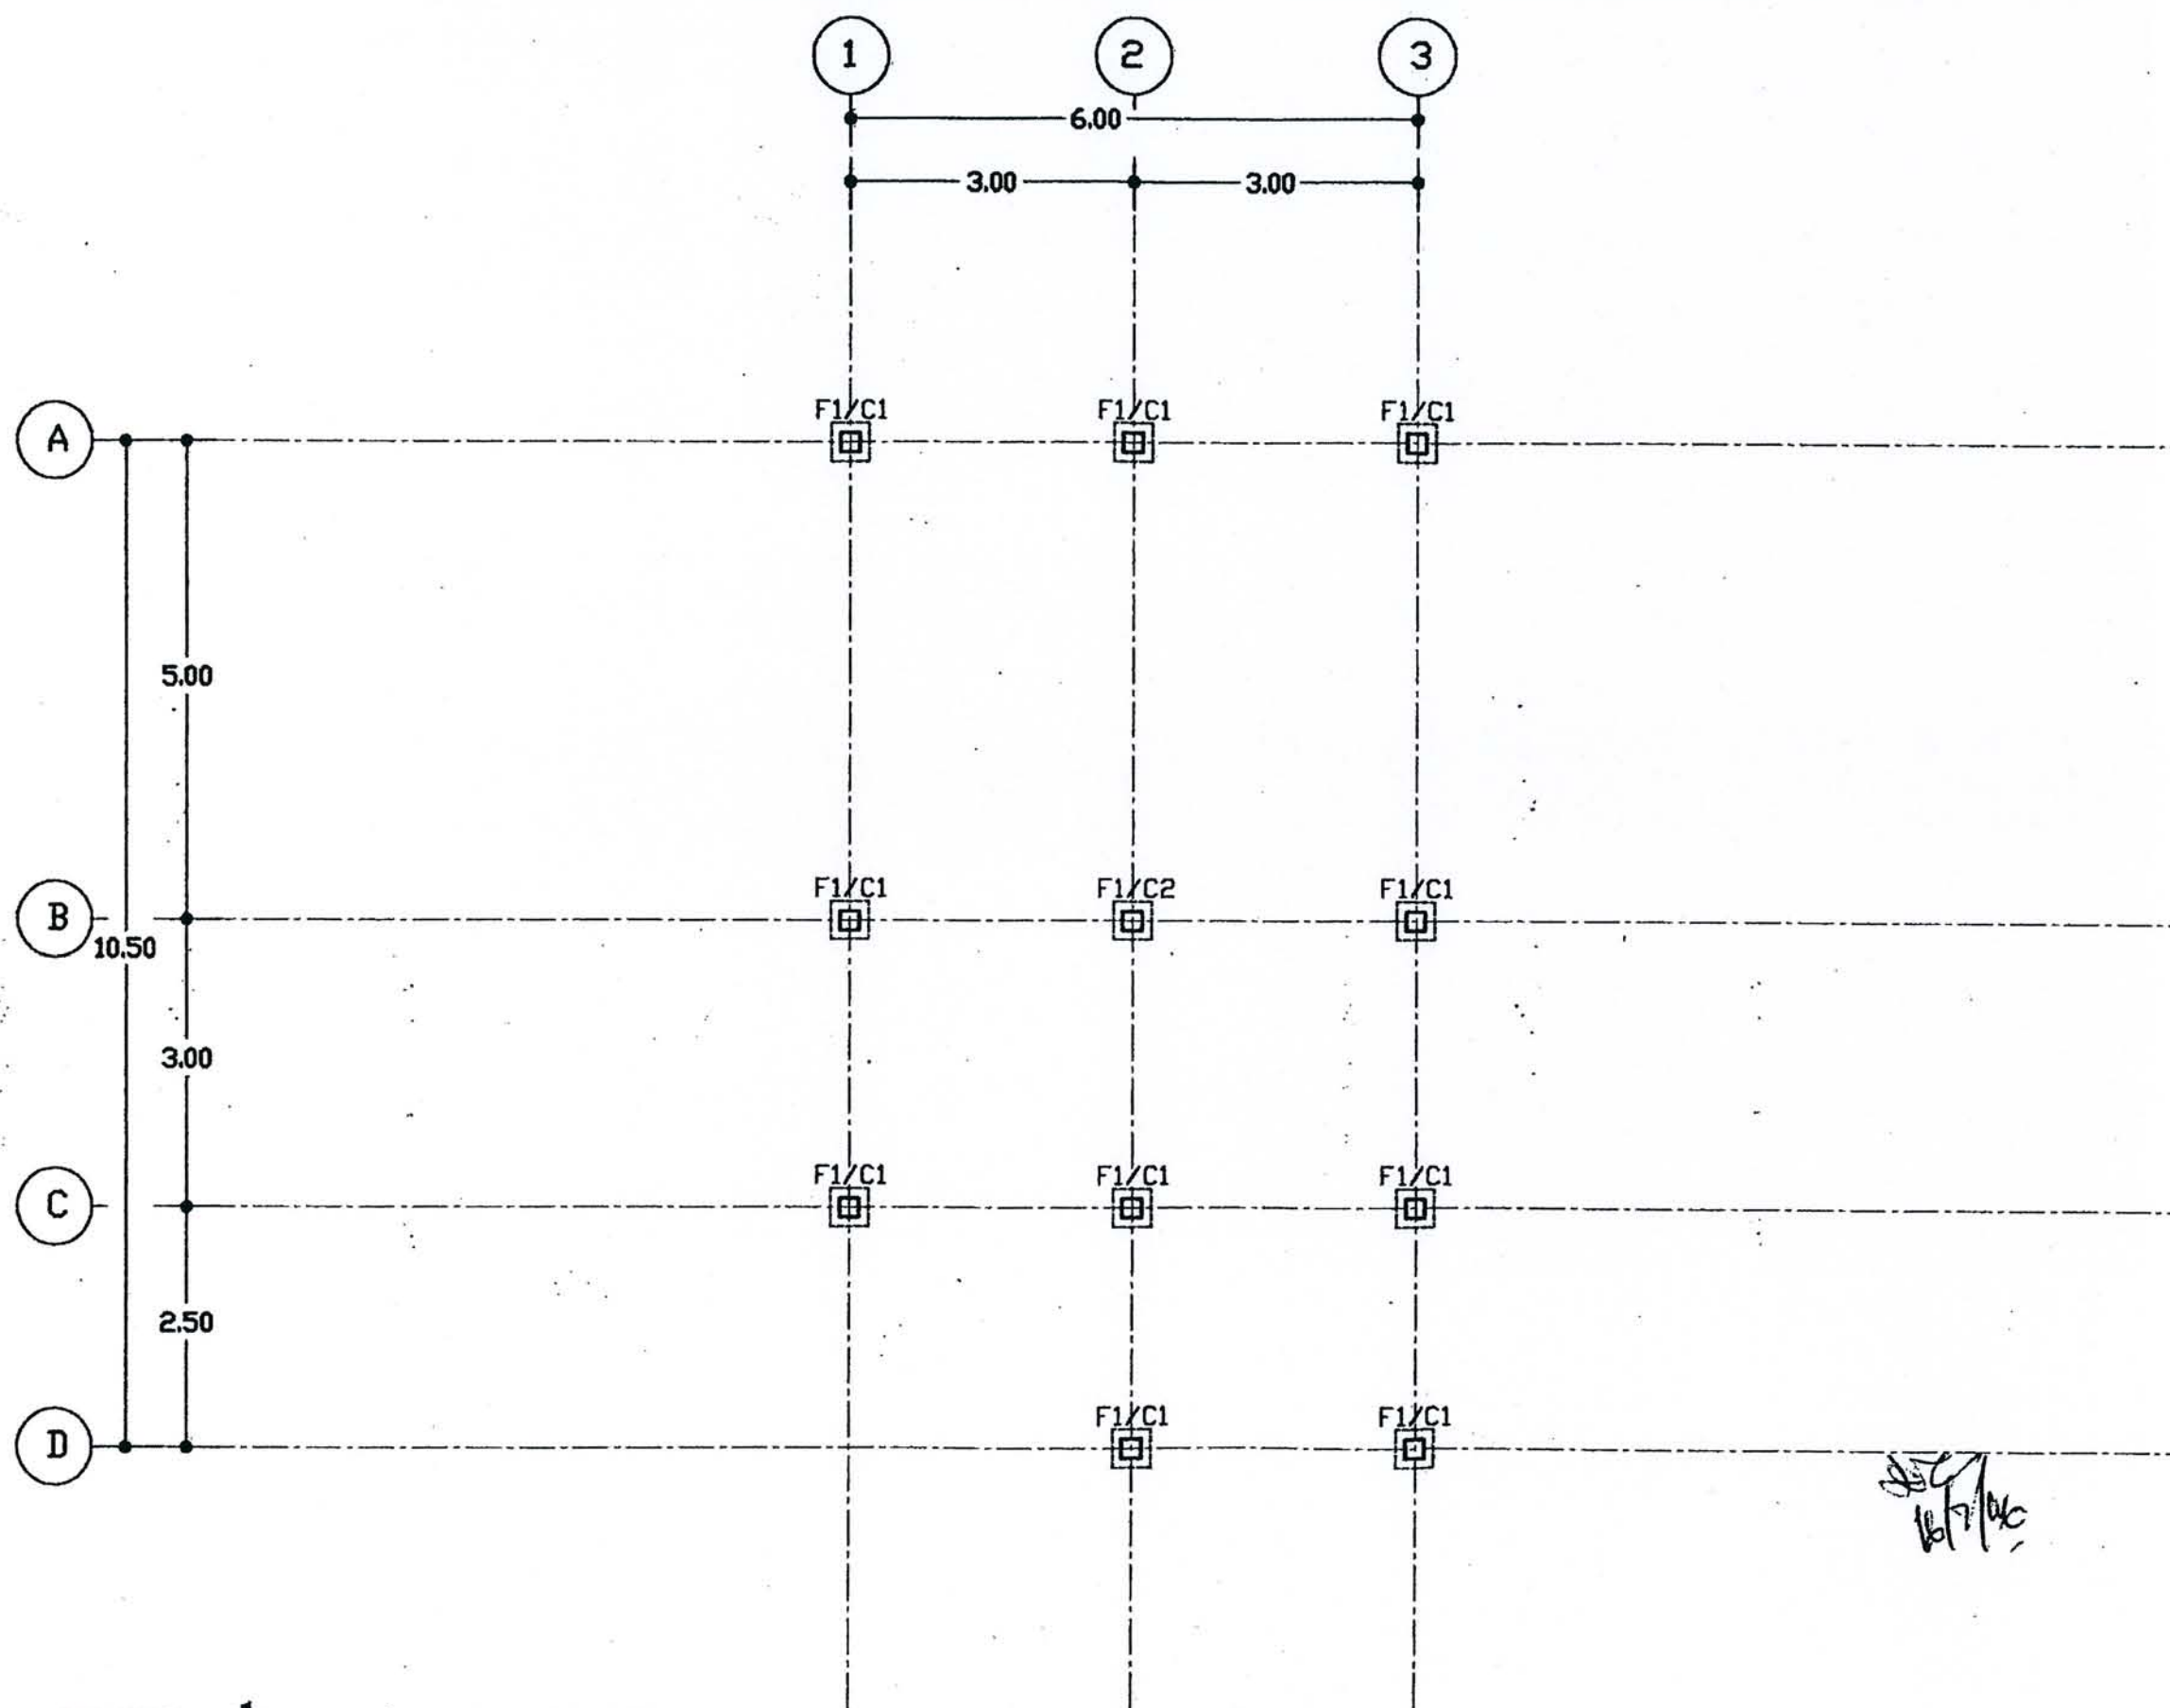

หมายเหตุ- เข็ม เจาะ คสล. Ø0.35 ยาว 21ม.


F1 = || ทลุม= || ต้น

ผังโครงสร้างฐานราก
มาตรฐาน 1:75

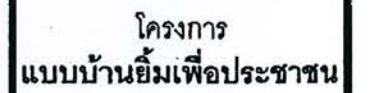

โดยสำนักงานโยธา
กรุงเทพมหานคร

ได้รับความอนุเคราะห์แบบ
จาก
บริษัท แลนด์ โสม
(ประเทศไทย) จำกัด

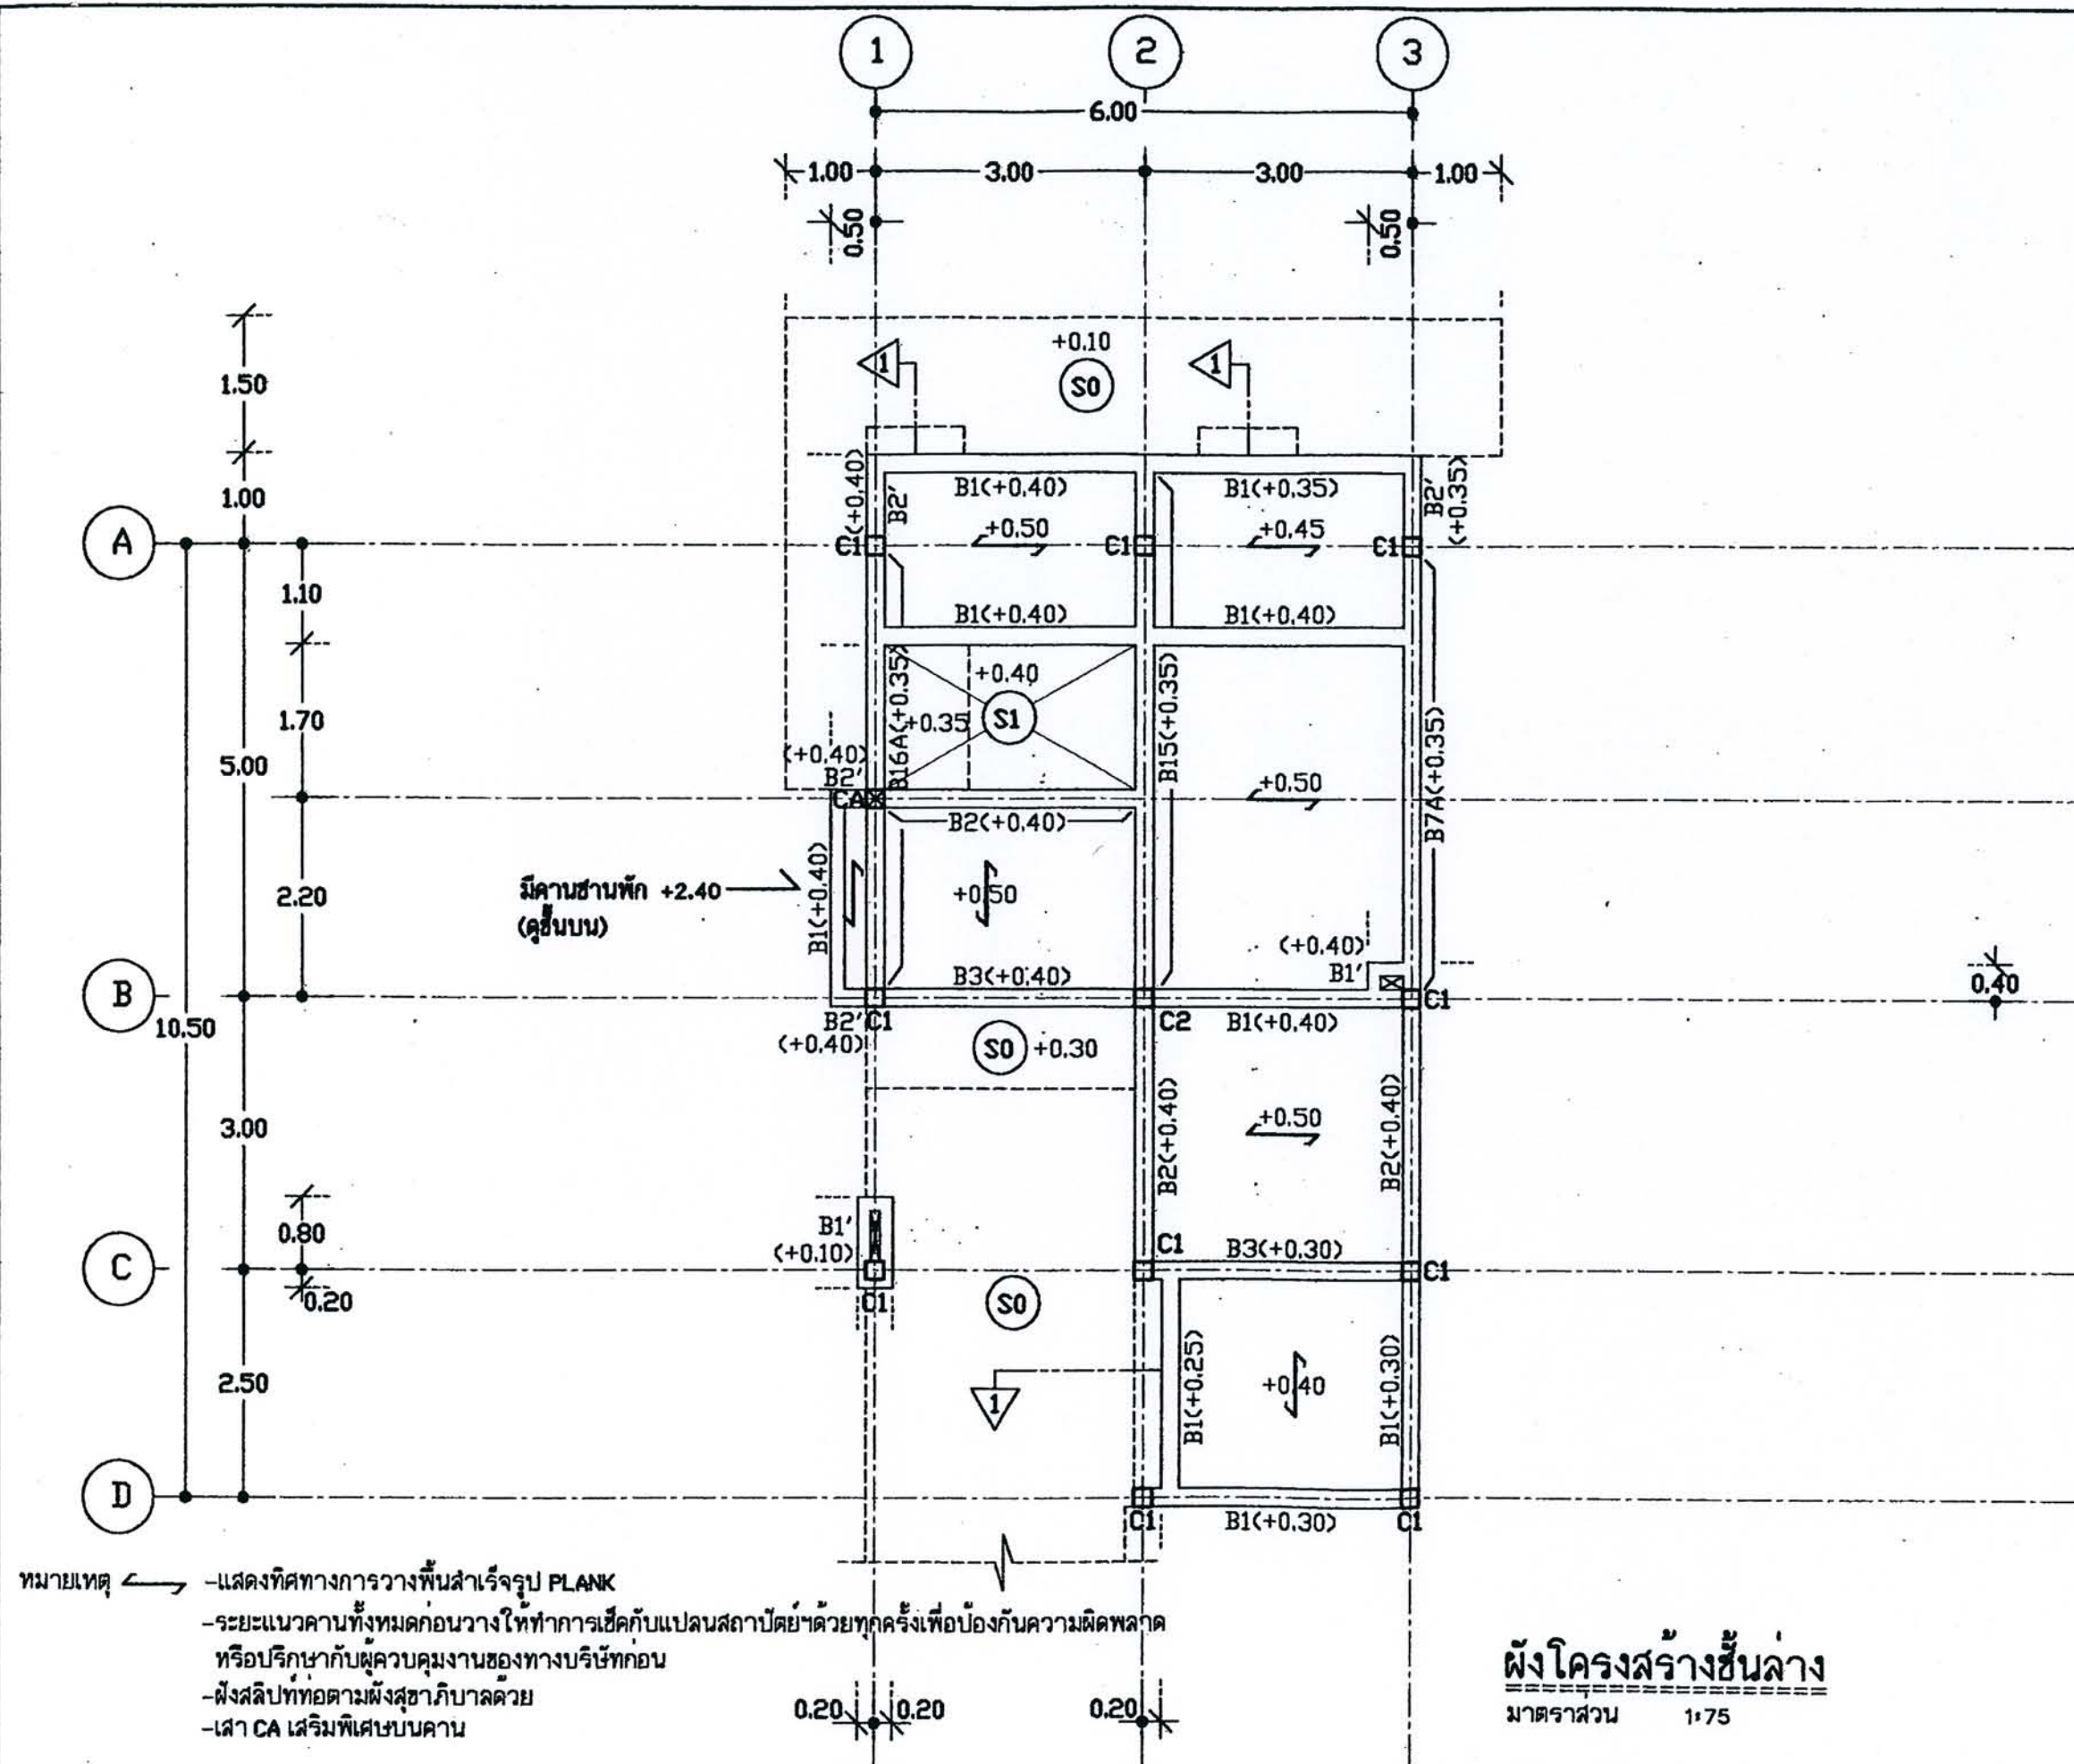




ตามนโยบาย
ม.ร.ว. สุขุมพันธุ์ บริพัตร
ผู้ว่าราชการกรุงเทพมหานคร

โดยสำนักการโยธา
กรุงเทพมหานคร

ได้รับความอนุเคราะห์แบบ
จาก
บริษัท แลนด์ ไโฮม
(ประเทศไทย) จำกัด

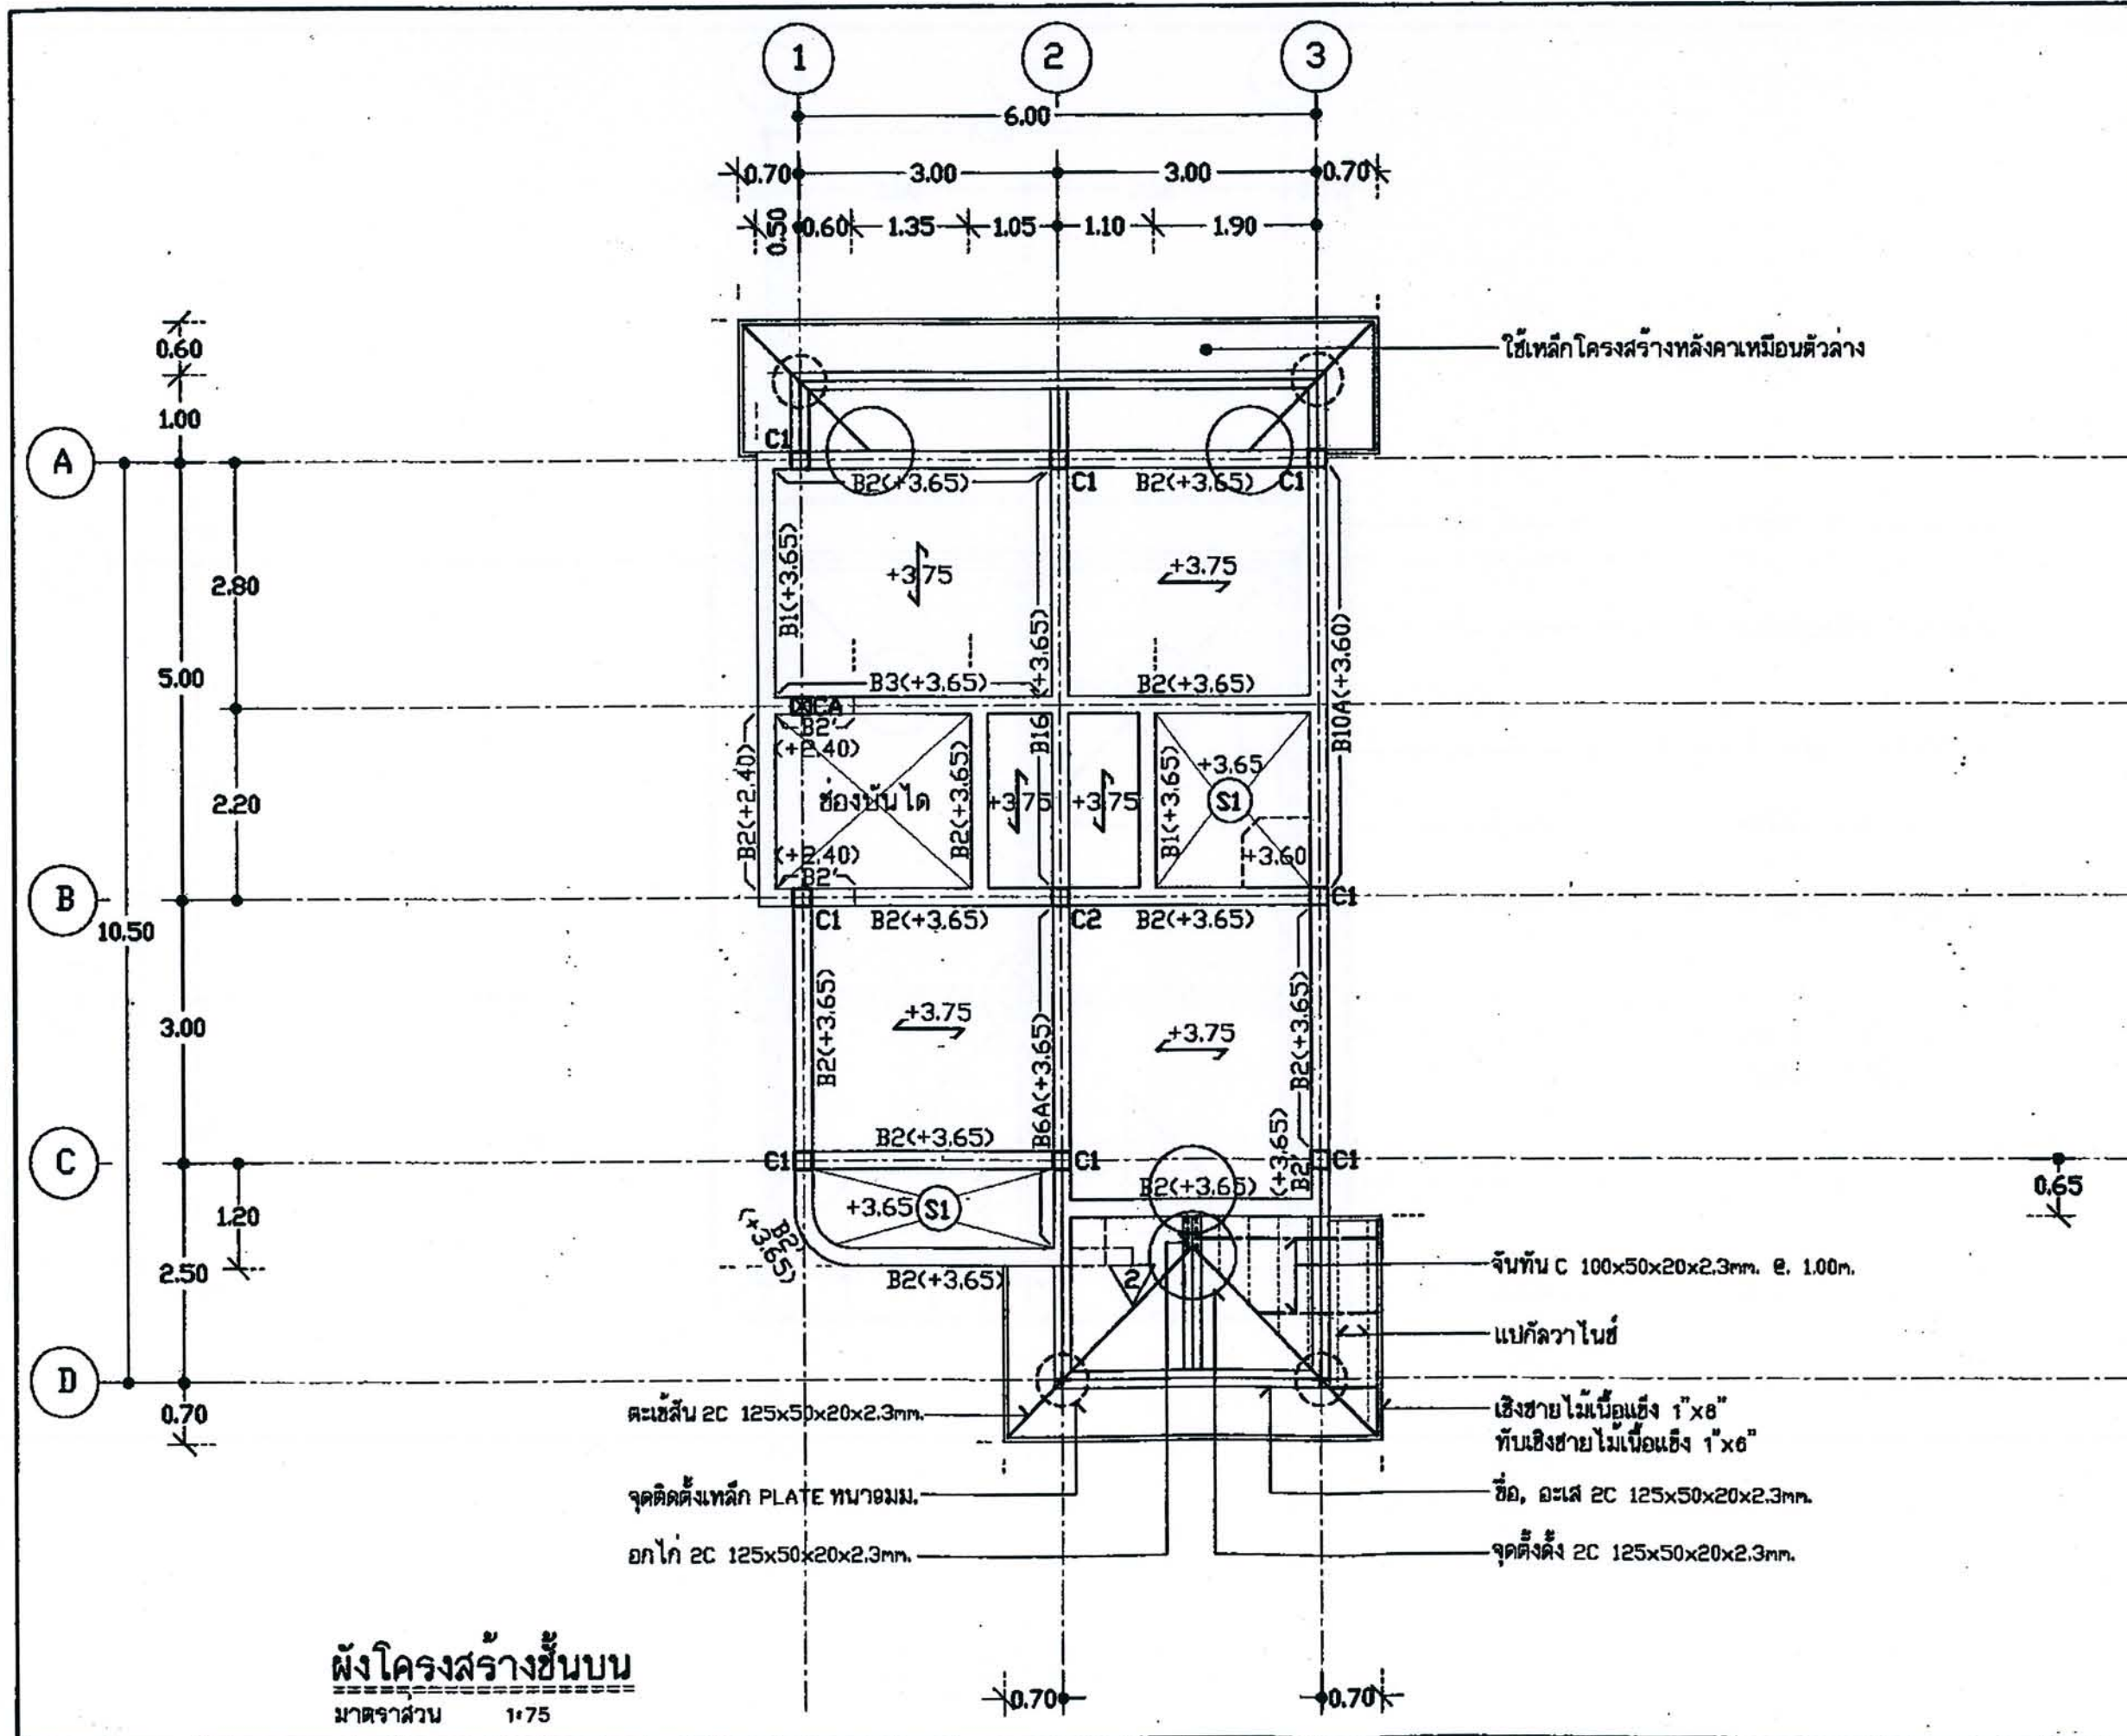





โครงการ
แบบบ้านยืมเพื่อประชาชน

ตามนโยบาย
ม.ร.ว. สุขุมพันธุ์ บริพัตร
ผู้ว่าราชการกรุงเทพมหานคร

โดยสำนักการโยธา
กรุงเทพมหานคร

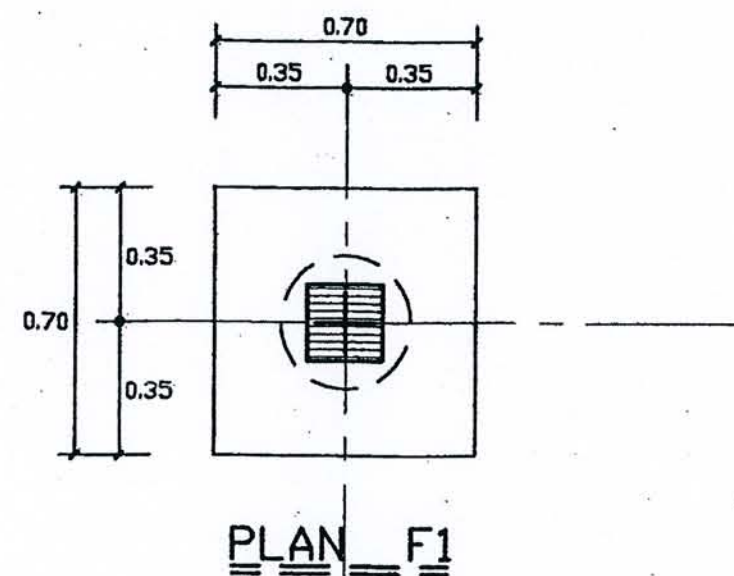

PLAN F1

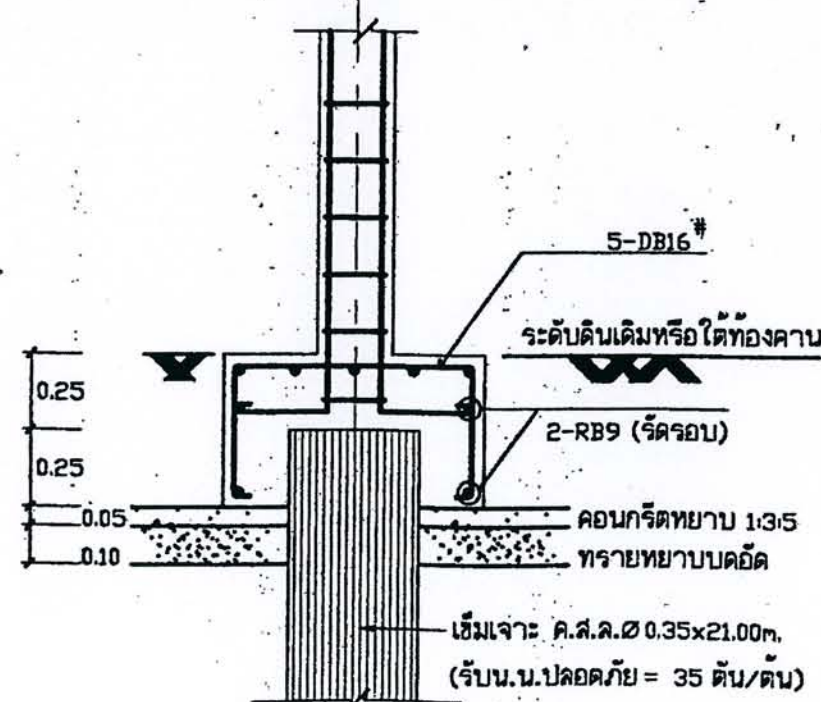

SECTION F1 1:20

ได้รับความอนุเคราะห์แบบ
จาก
บริษัท แลนด์ โฮม
(ประเทศไทย) จำกัด




โครงการ
แบบบ้านยืมเพื่อประชาชน

ตามนโยบาย
ม.ร.ว. สุขุมพันธุ์ บริพัตร
ผู้ว่าราชการกรุงเทพมหานคร

โดยสำนักงานโยธา
กรุงเทพมหานคร

FLOOR 2	 4-DB12 150 RB6@0.15	 4-DB12 150 RB6@0.15	 4-DB12 150 RB6@0.15
FLOOR 1	 4-DB12 200 RB6@0.15	 4-DB16 200 RB6@0.15	 4-DB12 150 RB6@0.15
FOOTING	 4-DB12 200 RB6@0.15	 4-DB12 200 RB6@0.15	
	C1	C2	CA

SECTION COLUMN 1:20

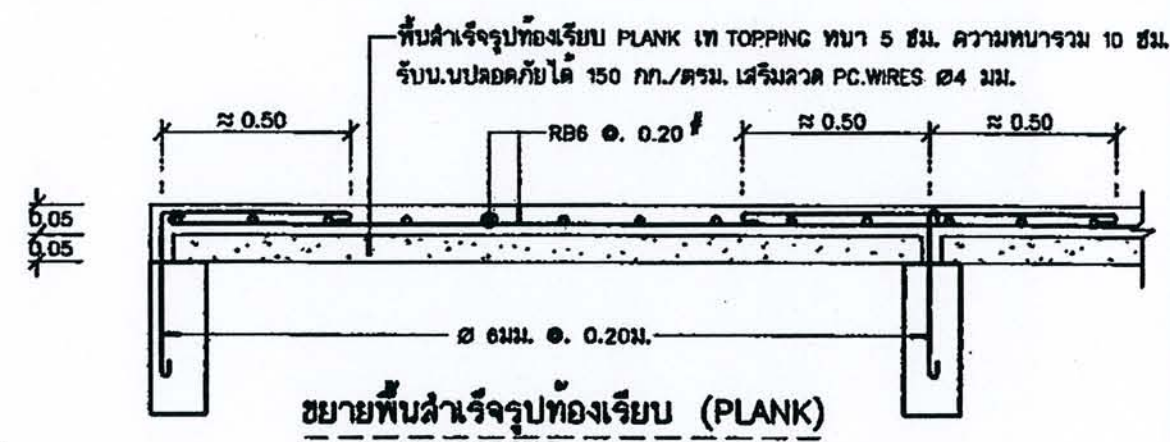

ตารางแสดงการรับน้ำหนักจร (LIVE LOAD)												
สำหรับพื้นสำเร็จรูปแบบทอเรียบ PLANK ขนาดหน้าตัด 0.05x0.36 ม.												
N \ S	2.80	3.00	3.20	3.40	3.60	3.80	4.00	4.20	4.40	4.60	4.80	5.00
4	504											
5		532	464	400	350	300						
6							318	274				
7									305	300		
8											300	250

- หมายเหตุ - มีค้ำยันชั่วคราว
 - S = ระยะช่วงพาดวัดขอบในถึงขอบในของคาน (CLEAR SPAN) หน่วยเป็นเมตร
 - N = จำนวนลวดค้ำแรง ขนาด Ø 4 มม.
 - ตัวเลขในตารางแสดงความสามารถในการรับน้ำหนักจรทุกปลอดภัยหน่วยเป็น กก./ตารางเมตร

ได้รับความอนุเคราะห์แบบ
จาก
บริษัท แลนด์ โสม
(ประเทศไทย) จำกัด




โครงการ
แบบบ้านยืมเพื่อประชาชน


ตามนโยบาย
ม.ร.ว. สุขุมพันธุ์ บริพัตร
ผู้ว่าราชการกรุงเทพมหานคร

โดยสำนักงานโยธา
กรุงเทพมหานคร

ได้รับความอนุเคราะห์แบบ
จาก
บริษัท แลนด์ โสแม
(ประเทศไทย) จำกัด

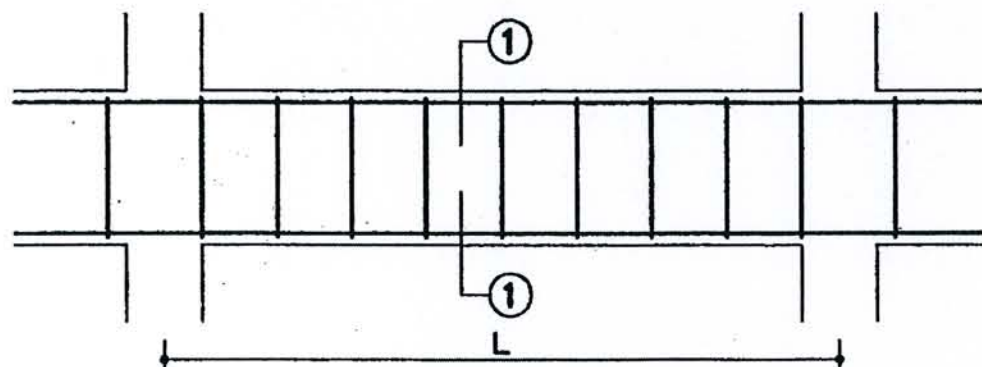


LONG SECTION

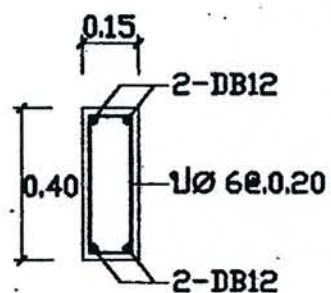


SECTION 1-1

B1

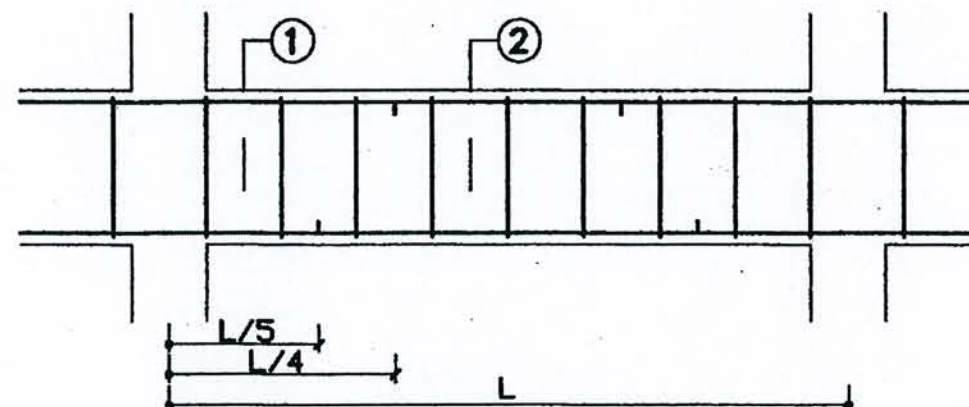


LONG SECTION

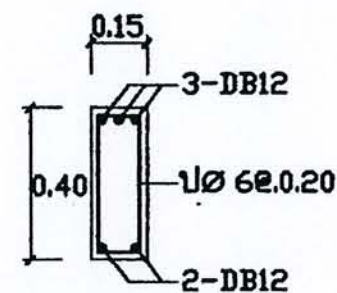


SECTION 1-1


B2

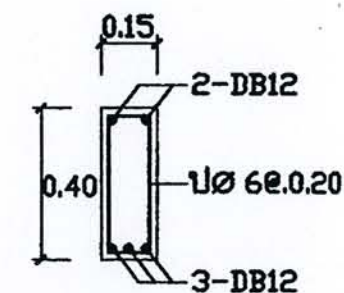

SECTION 2-2

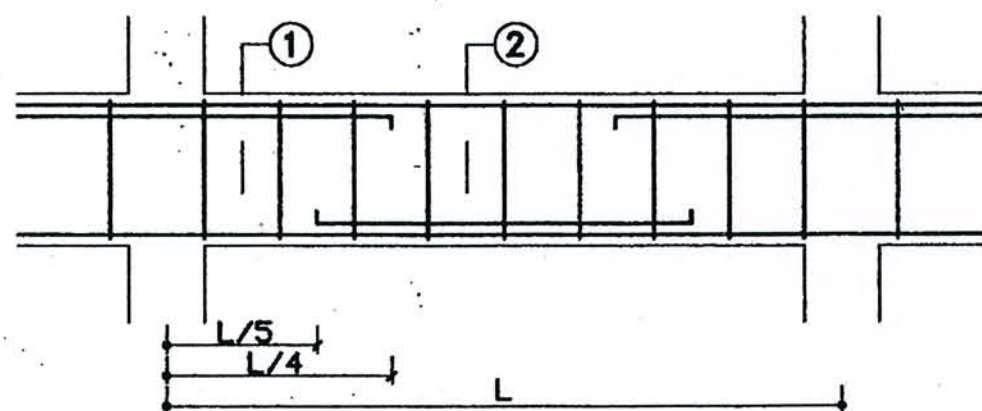


LONG SECTION

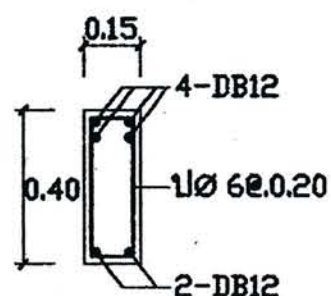


SECTION 1-1

B3

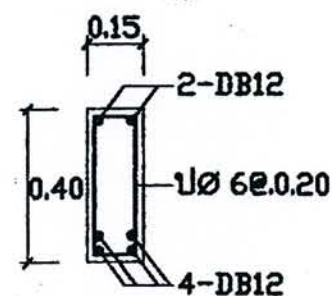


SECTION 2-2

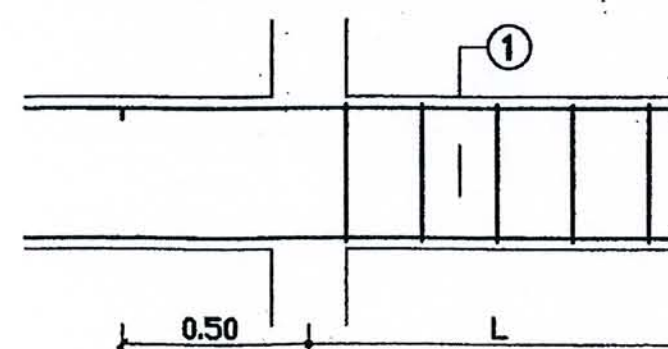

LONG SECTION

B2'

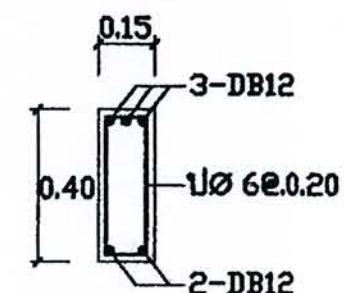

SECTION 1-1





โครงการ
แบบบ้านยืมเพื่อประชาชน




ตามนโยบาย
ม.ร.ว. สุขุมพันธุ์ บริพัตร
ผู้ว่าราชการกรุงเทพมหานคร

โดยสำนักการโยธา
กรุงเทพมหานคร







ได้รับความอนุเคราะห์แบบ
จาก
บริษัท แลนด์ โยม
(ประเทศไทย) จำกัด

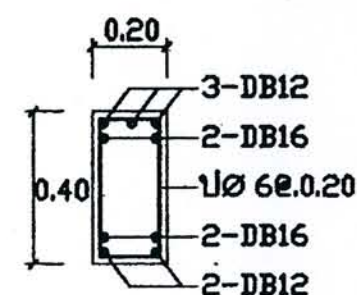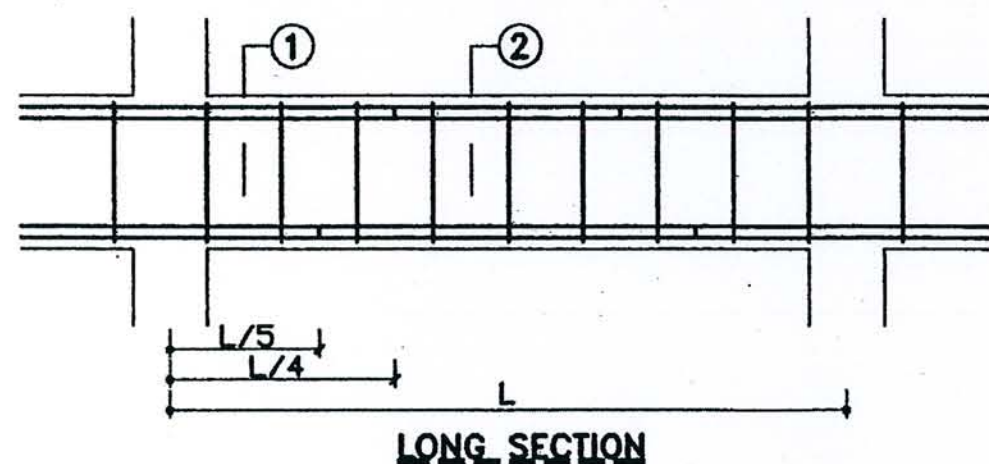


B6A

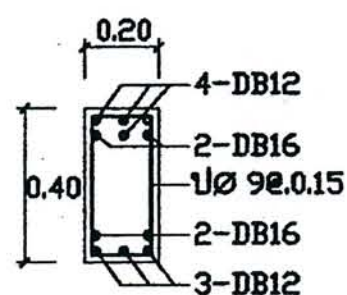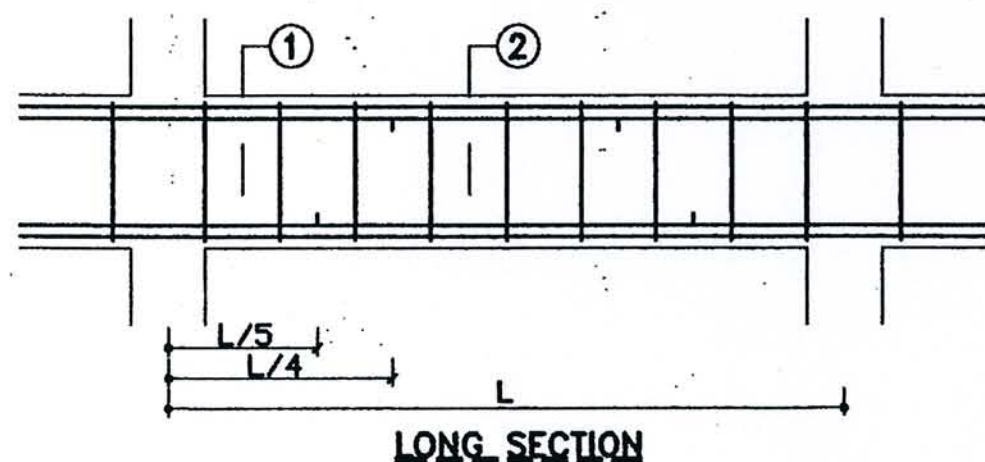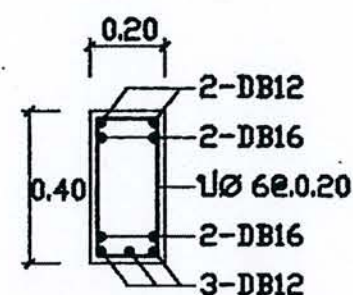

B7A

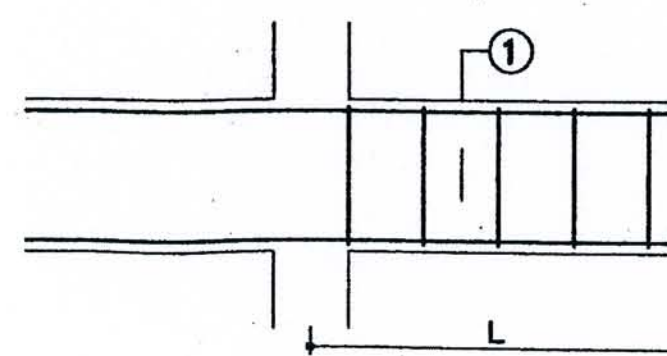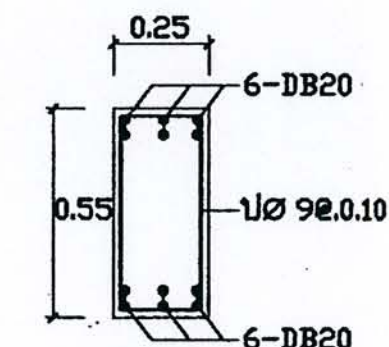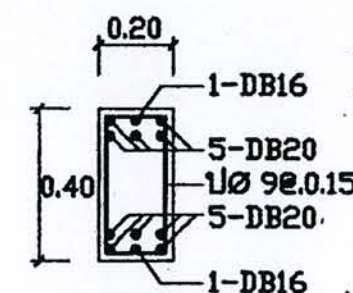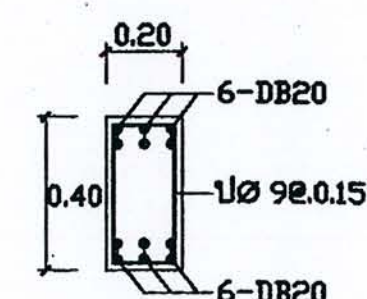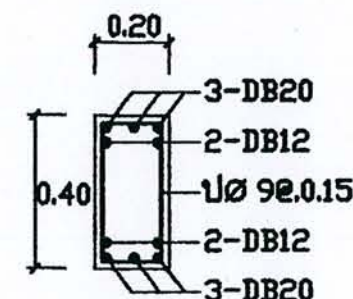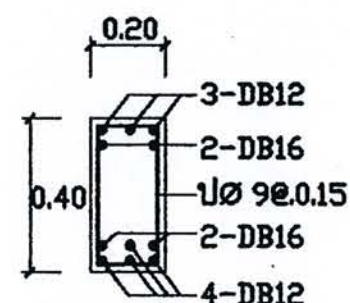

B1'


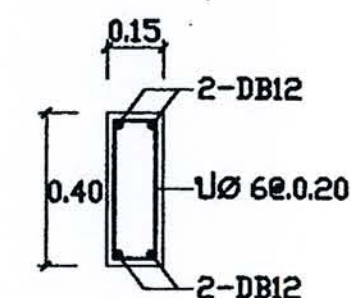





โครงการ
แบบบ้านยืมเพื่อประชาชน

ตามนโยบาย
ม.ร.ว. สุขุมพันธุ์ บริพัตร
ผู้ว่าราชการกรุงเทพมหานคร


โดยสำนักการโยธา
กรุงเทพมหานคร

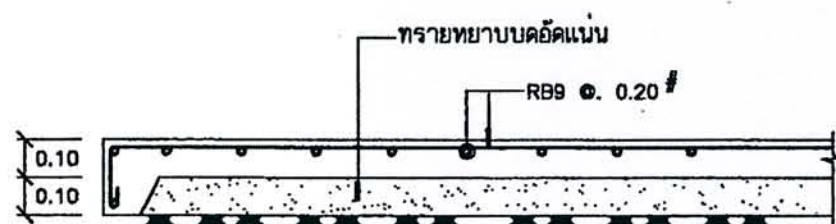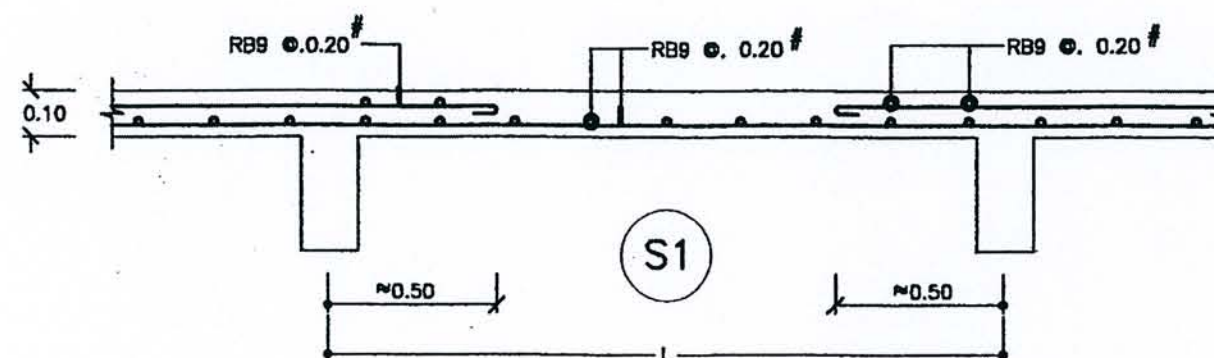


S0

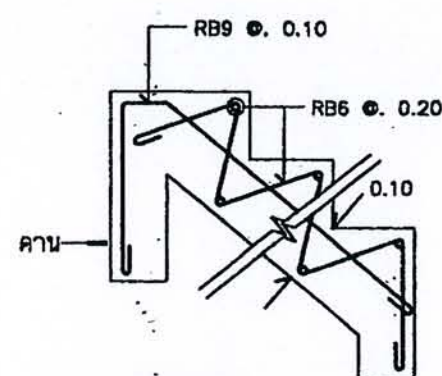


SECTION - 1 -
(ตามแบบโครงสร้างชั้นล่าง)

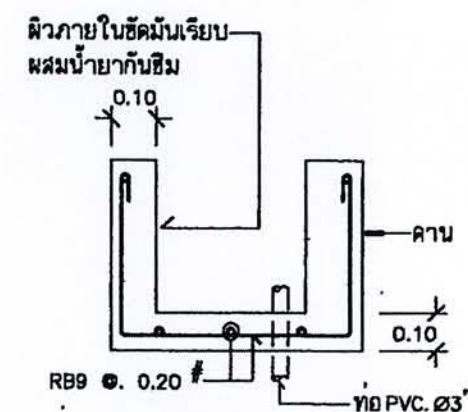


SECTION - 2 -
(ตามแบบโครงสร้างชั้นบน)

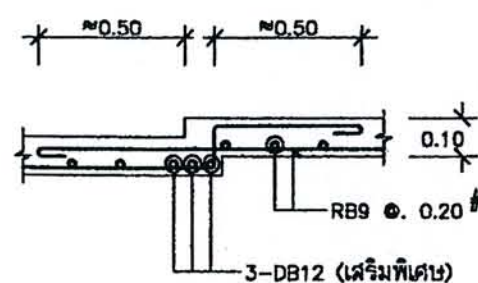

ขยายพื้นลดระดับ

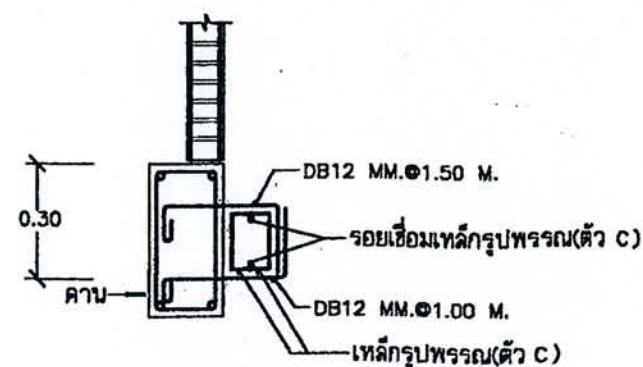

แบบขยายจุดที่มีหลังคาครอบล่างติดผนัง

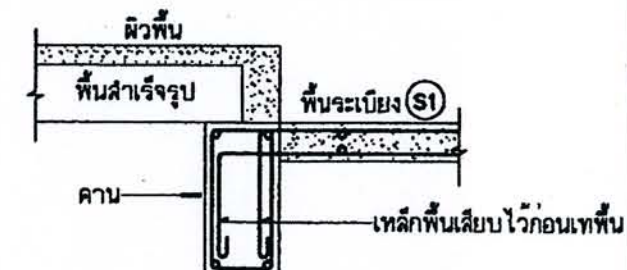

แบบขยายรอยต่อพื้นกับระเบียง

ได้รับความอนุเคราะห์แบบ
จาก
บริษัท แลนด์ โสม
(ประเทศไทย) จำกัด

สัญลักษณ์ประกอบแบบ "S"



โครงการ
แบบบ้านยืมเพื่อประชาชน

ตามนโยบาย
ม.ร.ว. สุขุมพันธุ์ บริพัตร
ผู้ว่าราชการกรุงเทพมหานคร

โดยสำนักงานโยธา
กรุงเทพมหานคร

รายการไฟฟ้า

สัญลักษณ์	ความหมาย	ขนาด - ยี่ห้อ - รุ่น
	แผงควบคุมไฟฟ้า	Square-D ขนาด 15 Amp. แบบกล่องเหล็กพร้อม circuit Breaker 7 ชุด
	โคมไฟฟ้า	ครอบแก้วกลม ๑๔" ผิวบุหลอดฟลูออโรสเซนต์ 32 W. แบบกลมแสงสีขาว
	โคมไฟฟ้า	ครอบแก้วกลม ๑๘" หลอดทั้งหลอด 60 W. แสงสีเหลือง
	หลอดฟลูออโรสเซนต์	รางหลอดฟลูออโรสเซนต์ ครอบพลาสติก ขนาด 1 X 20 W. แสงสีขาว
	หลอดฟลูออโรสเซนต์	รางหลอดฟลูออโรสเซนต์ ครอบพลาสติก ขนาด 1 X 40 W. แสงสีขาว
	ไฟโคมแขวนหลอด	โคมไฟแก้วผิวเรียบ ๑๒" หลอดธรรมดา 60 W.
	ไฟตั้งโต๊ะ	ไฟตั้งโต๊ะ 60 W. พานเหล็ก
	สวิทช์ไฟฟ้า	Single way ชนิดฝังในผนังของ NATIONAL (ของแท้) ติดตั้งสูงจากพื้น 1200 มม.
	สวิทช์ไฟฟ้า 2 ทาง	Two way ชนิดฝังในผนังของ NATIONAL (ของแท้) ติดตั้งสูงจากพื้น 1200 มม.
	ปลั๊กไฟ, เต้าเสียบ	ปลั๊กไฟแบบเรียบชนิดฝังในผนังแบบ 2 เต้าเสียบต่อ 1 ชุด พร้อมสายดินตาม- การไฟฟ้า ติดตั้งสูงจากพื้น 200 มม. ของ NATIONAL (ของแท้) ติดห่างจากผนัง 100 มม.
	ปลั๊กไฟ, เต้าเสียบ	ปลั๊กไฟแบบเรียบชนิดฝังในผนังแบบ 2 เต้าเสียบต่อ 1 ชุด พร้อมสายดินตาม- การไฟฟ้า ติดตั้งสูงจากพื้น 1000 มม. ของ NATIONAL (ของแท้) ติดห่างจากผนัง 100 มม.
	ปลั๊กสายอากาศ TV.	ใช้สายอากาศ TV.RG-6 โดยเดินสายไปยังห้องน้ำขึ้นบนแล้วจึงสายปลั๊กไว้ 1 ม.
	โทรศัพท์	เดินสายตามมาตรฐานไฟฟ้า โดยเดินสายไฟไปยังสายเคเบิลที่ขึ้นบนแล้วจึงสายปลั๊กไว้ 1 ม.
	สวิทช์แอร์	ตำแหน่งตามแบบ
	แสดงการเดินสายไฟแบบ-	สายไฟใช้สาย PVC. ของ YAZAKI หรือ BANGKOK CABLE
	เดินลอย	เดินลอยยึดด้วยสายรัดเข็มขัดระยะห่าง 100 มม. โดย
		- สายไฟสำหรับ สวิทช์ไฟ ที่มิใช่ ขนาด 1.0 มม. ²
		- สายไฟสำหรับ ปลั๊กไฟ ที่มิใช่ ขนาด 2.5 มม. ² (แบบมีสายดิน)
		- สายไฟสำหรับ แอร์ ที่มิใช่ ขนาด 10.0 มม. ²
		- สายไฟสำหรับ เครื่องทำน้ำร้อน ที่มิใช่ ขนาด 10.0 มม. ²
		- สำหรับสายเมนใช้สาย PVC. ของ YAZAKI หรือ BANGKOK CABLE
		ขนาด 16.00 มม. ² ต่อห่างจากชายคาน้ำฝน 16000 มม.

รายการเปลี่ยนแปลงเพิ่มเติมไฟฟ้า

* ไม่มีรายการเปลี่ยนแปลง

- หมายเหตุ :
- ให้เดินสายดินตามกฎระเบียบของการไฟฟ้าอย่างถูกต้อง
 - ราคากำหนด 3,000,000 บาท ใช้ไฟ ขนาด 30 Amp. 2 สายของ Square-D พร้อมสายเมน
 - ดูแบบลูกเซอร์กิต 16 ช่อง
 - ราคากำหนด 5,000,000 บาท ใช้ไฟ ขนาด 50 Amp. 2 สายของ Square-D พร้อมสายเมน

บ้าน SMILE HOME
V.1 [11/2/45]

ได้รับความอนุเคราะห์แบบ
จาก
บริษัท แลนด์ โสม
(ประเทศไทย) จำกัด

สัญลักษณ์ประกอบแบบ "S"

รายการสุขาภิบาล

สัญลักษณ์	ความหมาย	ขนาด และ จำนวนอุปกรณ์ที่ใช้
	ท่อรวม	ท่อ PVC. Ø 4" ขึ้นคุณภาพ Class 8.5 ติดตั้งให้มีความลาดเอียง 1 : 200 ปลายท่อ-ให้ต่อแบบ 3 ทาง ตัว T
	ท่อน้ำทิ้ง	(ท่อเมน) ท่อ PVC. Ø 2" ขึ้นคุณภาพ Class 8.5 ติดตั้งให้มีความลาดเอียง 1 : 200 ให้ท่อน้ำทิ้งไหลได้สะดวก
	ท่อน้ำทิ้ง	(ต่อจากสุขภัณฑ์) ท่อ PVC. Ø 1 1/2" ขึ้นคุณภาพ Class 8.5
	ท่อน้ำดี	(ท่อน้ำประปา) ท่อ PVC. Ø 1/2" ขึ้นคุณภาพ Class 13.5
	ท่อน้ำเย็น	(ท่อเมน) ท่อ PVC. Ø 3/4" ขึ้นคุณภาพ Class 13.5
	ท่อน้ำร้อน	ใช้ท่อเหล็กอาบสังกะสี Class B Ø 1/2"
	ท่อระบายอากาศ	ท่อ PVC Ø 1" ขึ้นคุณภาพ Class 8.5 ปลายท่อด้วยข้อต่อ 3 ทาง ตัว T ท่อระบายอากาศสูงจากพื้น 3500 มม. ยึดติดกับผนังหรือฝ้าเพดานระยะห่าง 300 มม.
	ท่อระบายน้ำเสีย	ท่อซีเมนต์ใยหิน Ø 150 มม. ติดตั้งให้มีความลาดเอียง 1 : 200 ข้อต่อบริเวณท่อน้ำ-บ่อพักให้ท่อน้ำขึ้นในบ่อพักอย่างน้อย 50 มม.
	จุดระบายน้ำทิ้ง	ตำแหน่งที่จุดระบายน้ำทิ้งจะลงซึ่งต้องท่อน้ำทิ้งมีแนวหน้าหลังและผนังติดกัน
	จุดระบายน้ำทิ้ง	ตำแหน่งจุดน้ำทิ้งจากชักโครก
	บ่อพัก	บ่อพักน้ำเสียสำเร็จรูป ขนาด 300X400X400 มม. หรือขนาดที่กระยะ 6.00 ม. ทุกช่วงพักเดียว
	จุดจ่ายน้ำประปา	จุดจ่ายน้ำดี (ประปา) ซึ่งต้องสูงให้ตามแบบ
	บ่อกรอง	ใช้ระบบบำบัดน้ำเสีย ถึงบำบัดน้ำเสียสำเร็จรูป ของ AQUA-PAC หรือเทียบเท่า
	มิเตอร์น้ำ	ตามมาตรฐานของการประปา
	เครื่องปั๊มน้ำ	ตำแหน่งตามแบบ
	แนวลาดเอียง	ลาดเอียงตามแบบ

- หมายเหตุ :
1. ท่อ PVC. ที่ข้อต่อทุกจุดจะต้องทากาวก่อนต่อ เมื่อต่อท่อเสร็จเรียบร้อยแล้วน้ำจะต้องไม่รั่วซึม
 2. ท่อน้ำดีจะต้องมีลักษณะต้องขมวดข้อต่อเหล็กทุกจุดและบริเวณรอยต่อระหว่างท่อ PVC. เข้ากับข้อต่อเหล็กจะต้องพันท่อน้ำดีก่อน เมื่อต่อท่อเสร็จเรียบร้อยแล้วน้ำจะต้องไม่รั่วซึม
 3. ท่อประปา (น้ำร้อน) ที่ต่อกับสายอ่อนให้ใช้โอกาวล้างทุกจุด
 4. ท่อระบายน้ำและบ่อพักต่อจากตัวอาคาร ถึงบ่อพักสาธารณะไม่เกิน 16.00 ม.

รายการประกอบแบบสุขภัณฑ์ TYPE S

อ่างอาบน้ำ (ถัง)	CRISTINA (TEENA-D) CT-5013 C พร้อมเดินสายฟ้าฟ้า และ ท่อร้อยของเครื่องทำน้ำร้อน 1 ชุด (ไม่รวมเครื่องทำน้ำร้อน) ก๊อกผสมน้ำ JAZZ STD. A 7601 (AMERICAN STANDARD)
อ่างล้างหน้า	AMERICAN STANDARD รุ่น TF-476 ชนิดฝังคานเตอร์ , ก๊อกน้ำ JAZZ STD. A 7000 หรืออุปกรณ์ที่เทียบ
ก๊อกอาบน้ำ	ใช้แบบ BALL VALVE (ที่เปิด)
โถ้วมนั่งราบ	AMERICAN STANDARD รุ่น TF-2310 (ที่เปิด) , ลายชำระ HANG 5502 รุ่น TF-2310 (คนใช้)
ฝักบัวสายอ่อน	JAZZ STD. A 7003 A (AMERICAN STANDARD)
ที่วางสบู่	AMERICAN STANDARD รุ่น TF-9000
ที่ใส่กระดาษชำระ	AMERICAN STANDARD รุ่น TF-9001
ราวนวนชัก	AMERICAN STANDARD รุ่น TF-9085
กระจกเงา	กระจกเงาเรียบเรียบ ยึดด้วยกาว
สีสุขภัณฑ์	ที่เน้นสีแบบที่ BEIGE ยกเว้นห้องน้ำคนใช้ ให้สีขาว

รายการประกอบแบบสุขภัณฑ์ กรณีมีการเปลี่ยนแปลงเพิ่มเติม

* ไม่มีรายการเปลี่ยนแปลง

รายการเปลี่ยนแปลงเพิ่มเติมสุขาภิบาล

* ไม่มีรายการเปลี่ยนแปลง

บ้าน SMILE HOME
V.1 [11/2/45]



โครงการ
แบบบ้านยืมเพื่อประชาชน

ตามนโยบาย
ม.ร.ว. สุขุมพันธุ์ บริพัตร
ผู้ว่าราชการกรุงเทพมหานคร

โดยสำนักงานโยธา
กรุงเทพมหานคร


ได้รับความอนุเคราะห์แบบ
จาก
บริษัท แดนดี โฮม
(ประเทศไทย) จำกัด



โครงการ
แบบบ้านยืมเพื่อประชาชน

ตามนโยบาย
ม.ร.ว. สุขุมพันธุ์ บริพัตร
ผู้ว่าราชการกรุงเทพมหานคร

โดยสำนักงานโยธา
กรุงเทพมหานคร

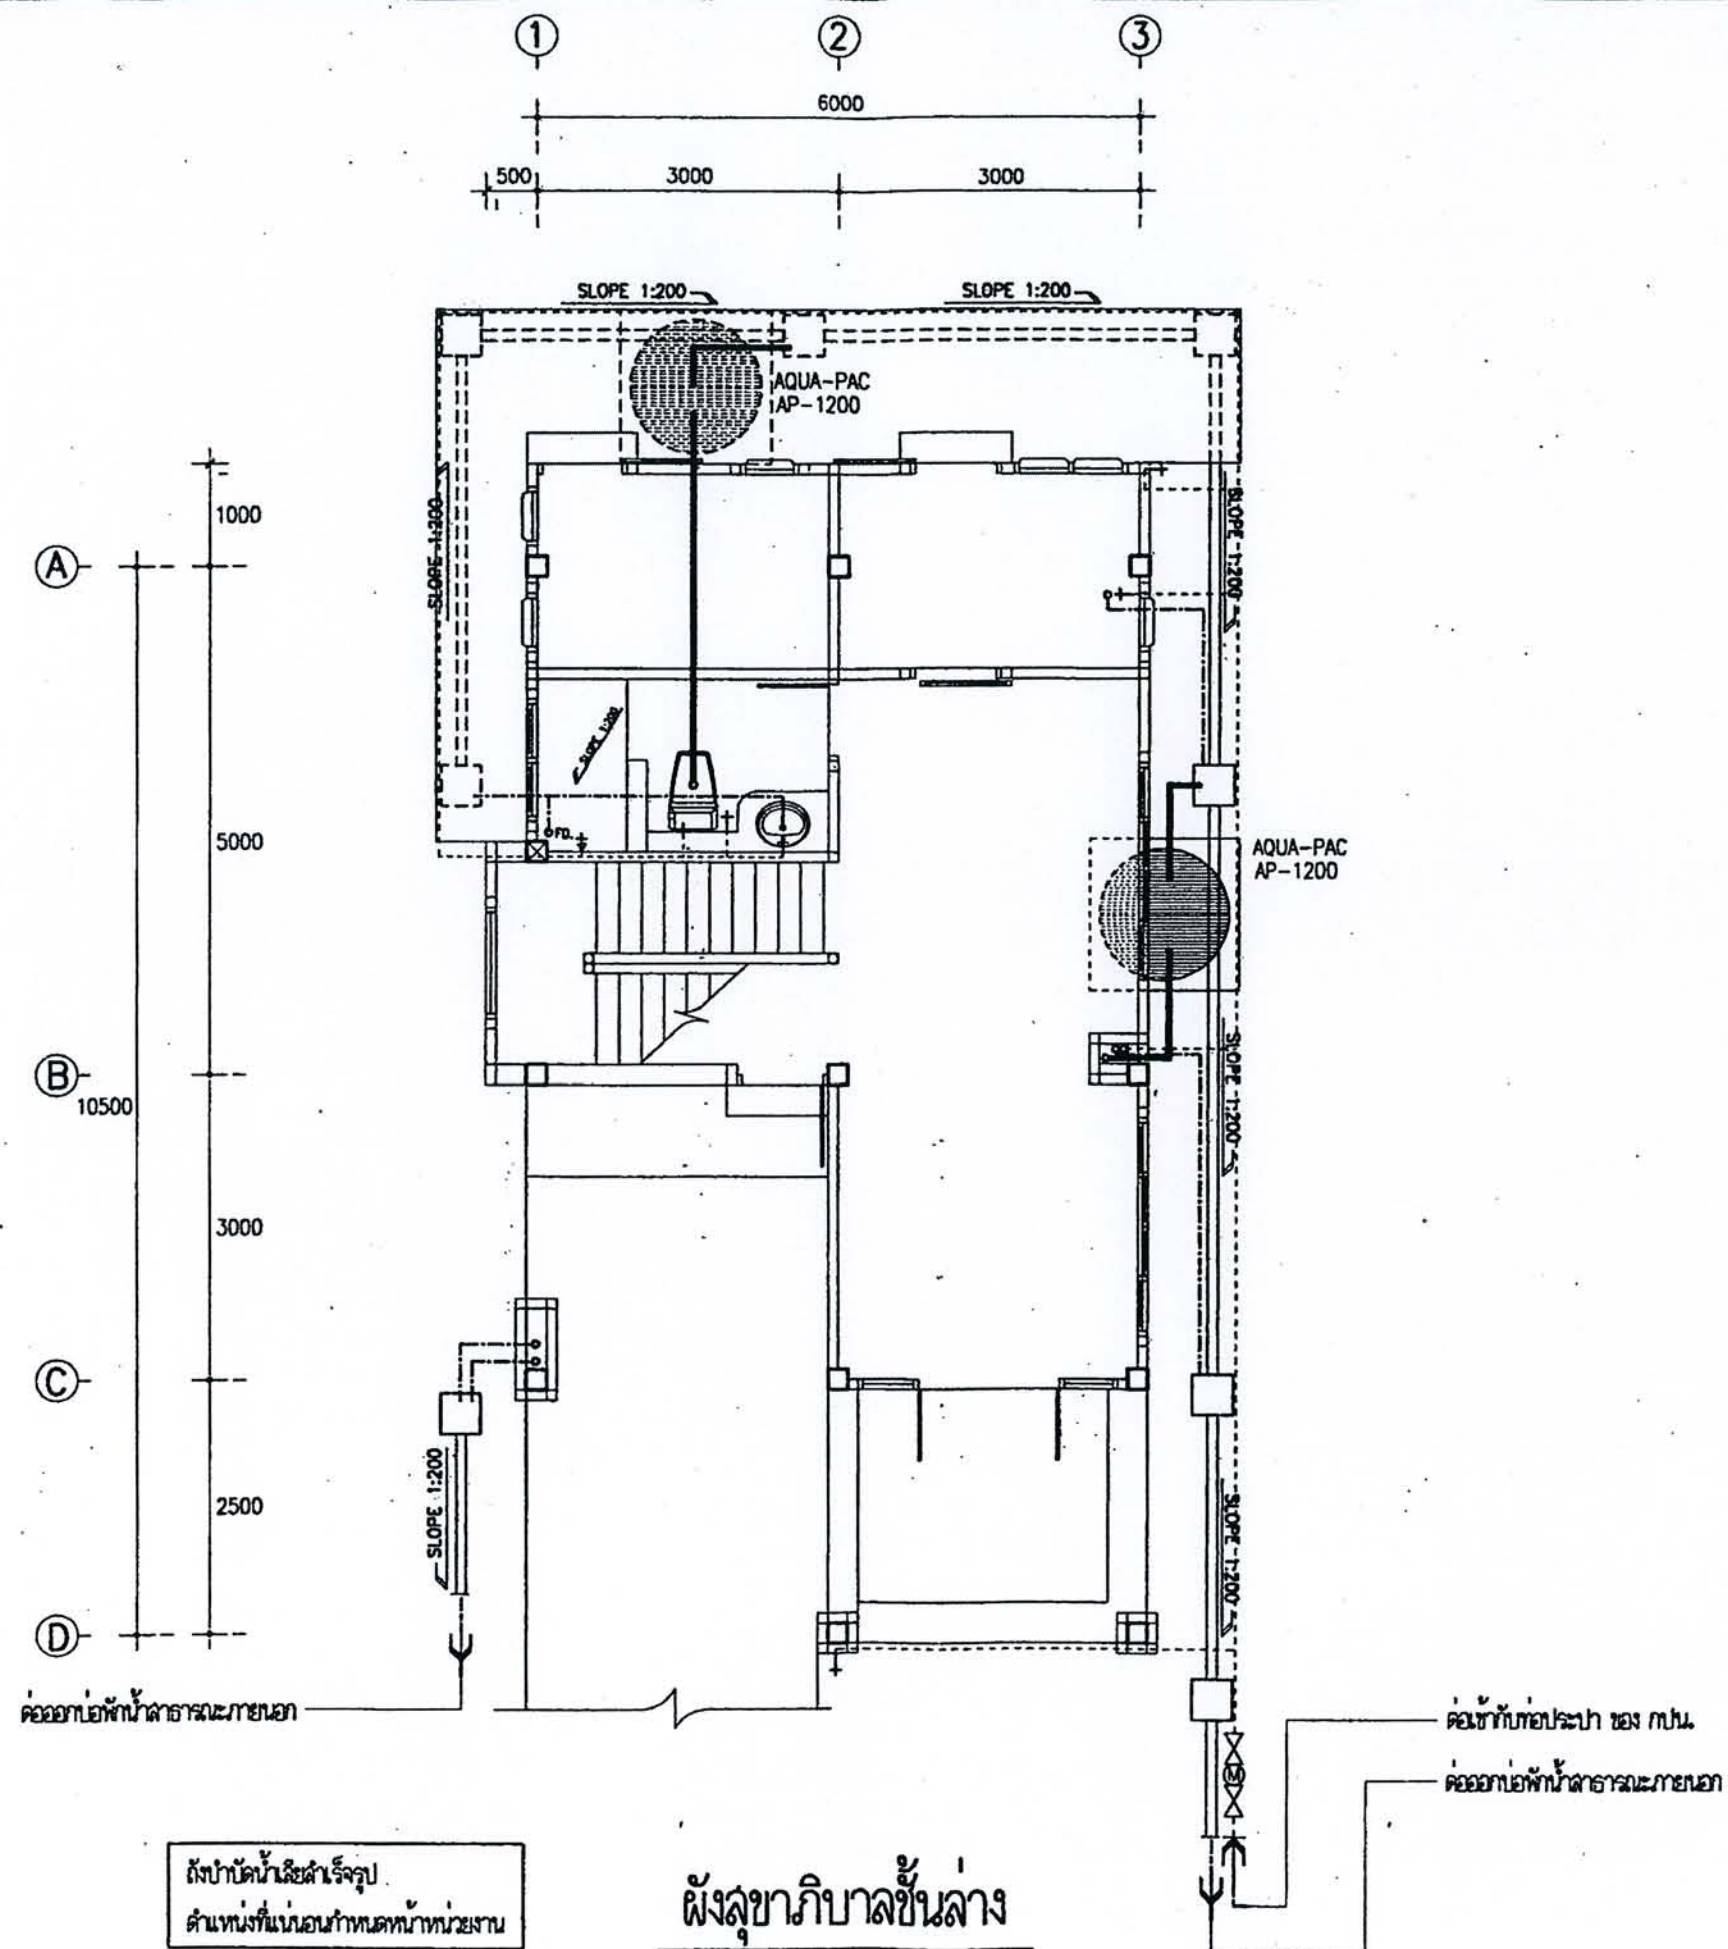

ได้รับความอนุเคราะห์แบบ
จาก
บริษัท แลนด์ โสม
(ประเทศไทย) จำกัด




โครงการ
แบบบ้านยืมเพื่อประชาชน


ตามนโยบาย
ม.ร.ว. สุขุมพันธุ์ บริพัตร
ผู้ว่าราชการกรุงเทพมหานคร

โดยสำนักงานโยธา
กรุงเทพมหานคร

ได้รับความอนุเคราะห์แบบ
จาก
บริษัท แลนด์ โสม
(ประเทศไทย) จำกัด

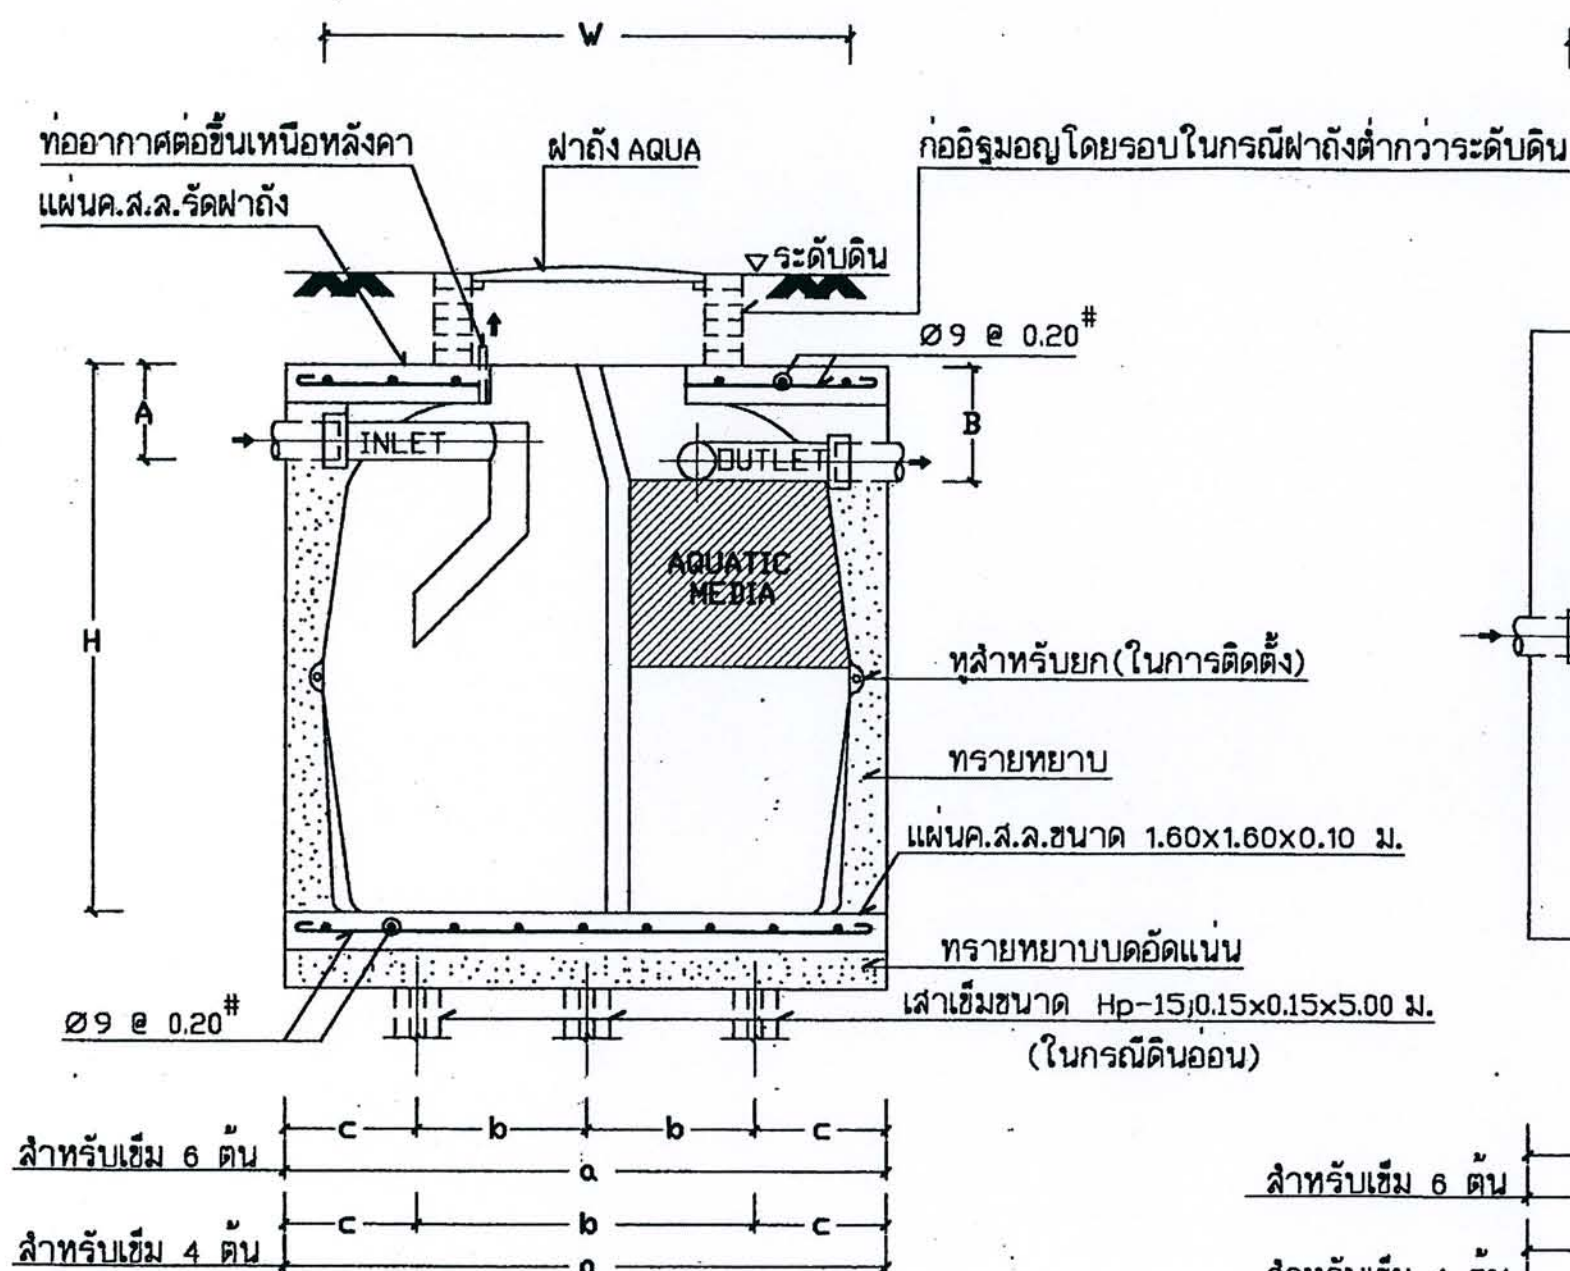

SECTION 1:20

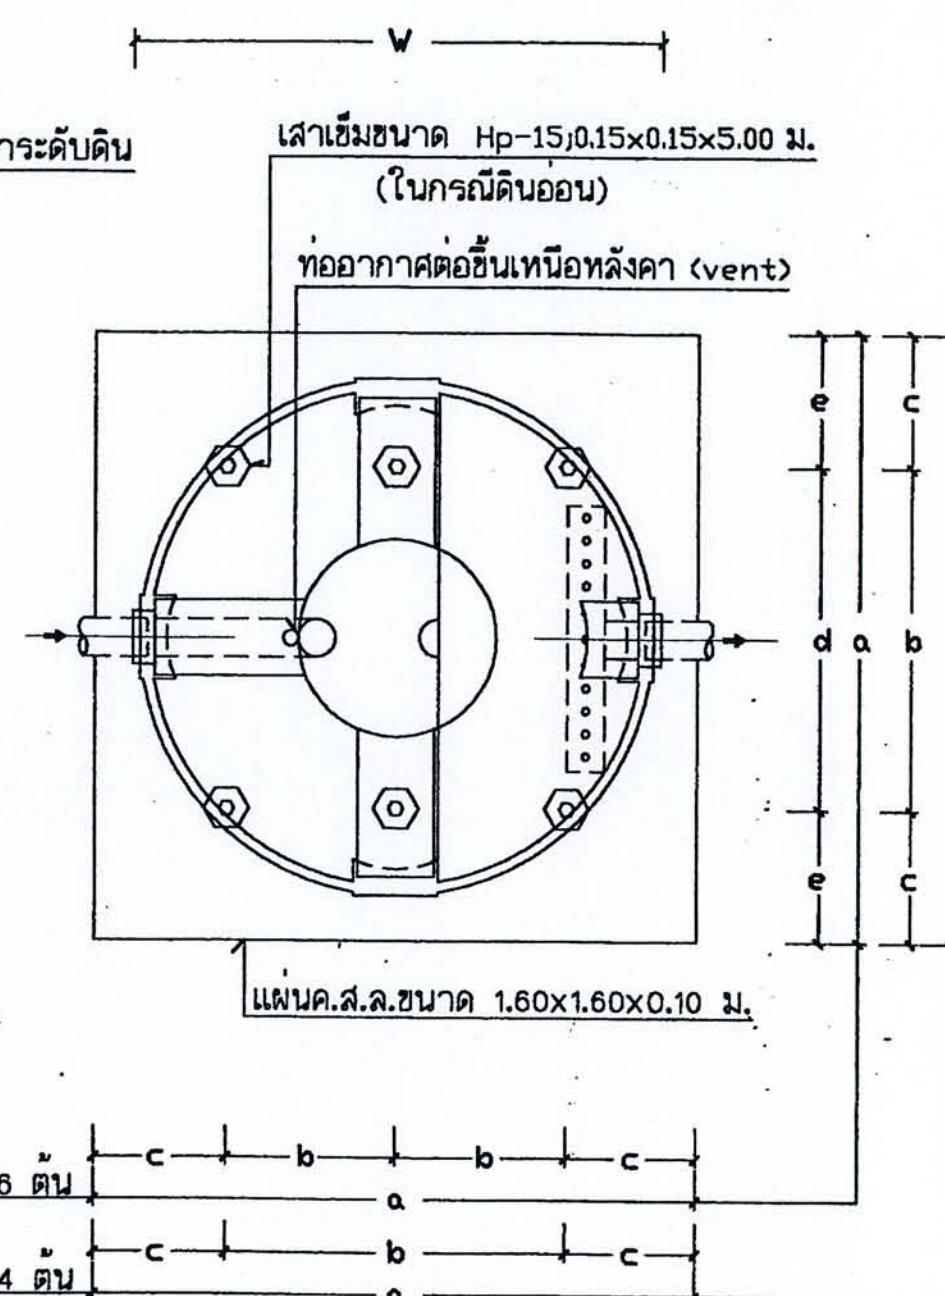

PLAN 1:20

ตาราง แสดงขนาดของถังรวม (ส่วนเกราะ+ส่วนกรอง) ในรุ่นต่างๆ (มม.)

MODEL	H	W	A	B	INLET	OUTLET	VENT	a	b	c	d	e
AP-1200	1700	1200	250	300	100	100	50	1400	700	350	-	-
AP-1800	1590	1450	250	300	100	100	50	1650	850	400	-	-
AP-2000	1750	1500	250	300	100	100	50	1700	850	425	-	-
AP-3000	1900	1700	250	300	100	100	50	1900	700	250	900	500
AP-4000	1930	1890	250	300	100	100	50	2090	750	295	1090	500
AP-6000	2300	1970	250	300	100	100	50	2170	750	335	1010	580
AP-5000	2350	2100	300	350	150	150	50	2300	750	400	1200	550

หมายเหตุ การใช้เสาเข็มกับขนาดถัง
ถังรุ่น 1200 ถึงรุ่น 2000 ใช้เสาเข็มจำนวน 4 ต้น
ถังรุ่น 3000 ถึงรุ่น 6000 ใช้เสาเข็มจำนวน 6 ต้น

AQUA-PAC