



ตามนโยบายของ
หม่อมราชวงศ์สุขุมพันธุ์ บริพัตร
ผู้ว่าราชการกรุงเทพมหานคร
โดย สำนักการโยธา



แบบบ้านยืม... เพื่อประชาชน

100 แบบบ้านมาตรฐาน...
สวย ดี โดนใจ...
พร้อมปลูกสร้างได้ทันที



ห้ามพลาด!!! โอกาส...
ยืมรับ... บ้านใหม่

แบบบ้านสวย
เลือกได้

ใน “โครงการแบบบ้านยืม...เพื่อประชาชน”

แบบ 100 แบบบ้าน
มาตรฐาน...

สวย ดี โดนใจ
พร้อมปลูก

สร้างได้ทันที
มีให้เลือก

หลากหลาย
ตอบสนอง
ทุกไลฟ์สไตล์คนเมือง

ซีดเอ็ม



โดยความอนุเคราะห์แบบจาก
บริษัท แลนด์ โธม (ประเทศไทย) จำกัด

รายการประกอบแบบก่อสร้าง TYPE "S"



รายการประกอบแบบทั่วไป

- โครงสร้างบ้านพักอาศัยโดยทั่วไปเป็นคอนกรีตเสริมเหล็กหล่อในที่ ตั้งแต่ฐานราก ; เสา , คาน , พื้นชั้นล่าง - บน เป็นพื้น - สำเร็จรูป บางส่วนหล่อในที่ ขนาด และ รายละเอียด ตามแบบวิศวกรรม
- เสาเข็มบ้าน 2 ชั้น ใช้คอนกรีตอัดแรง รูปตัว I - ~~22 x 22 ซม. ยาว 18 ม.~~ กรณีบ้าน 2 ชั้น จะใช้เสาเข็มตาม - การคำนวณของวิศวกร
- หลังคา โครงหลังคาหลังรูปทรง ทดกั้นลอน TOA2 ชั้น พร้อมเคลือบผิวพิเศษอีก 1 ชั้น มุงด้วยกระเบื้อง CPAC MONIER สีมาตรฐานบริษัท หรือ เทียนดำ
- ผนังทั่วไปก่ออิฐฉาบปูน ทาสี ยางวันฉวีขาว ทำผิวพิเศษตามระบุในแบบ
- ฝ้าเพดานภายใน ฝ้าฉาบเรียบทาสี ทน 9 มม. ฉาบเรียบ ทาสี ความสูงจากพื้นถึงฝ้า 2.60 เมตร
- ภายนอกกระเบื้องแผ่นเรียบ ทน 4 มม. , ห้องน้ำฝ้าฉาบเรียบทาสี ทน 9 มม. วางบนโครงคร่าว T - BAR
- บันไดโครงสร้างไม้ดีด ลูกตั้งบันได , ลูกนอนบันไดไม้ดีด เสา , ราวบันได , ลูกกรงบันไดไม้ดีด
- ลิ้นชักใช้ SUPERCOAT ผลิตของ ICI หรือ เทียนดำ
- การป้องกันปลวก ใช้ระบบดินทาก่อนบริเวณคานชั้นล่างทั้งหมด และทากันปลวกบนเนื้อโครงสร้างด้วยไม้

รายการประกอบแบบการเปลี่ยนแปลงเพิ่มเติม

* บ้านหลังนี้ใช้เข็ม I-22x22 ซม. ยาว 18 ม. ทั้งหมด ตามใบ - ป/ป 4/3

สัญลักษณ์ประกอบแบบสถาปัตย์

สัญลักษณ์	ความหมาย
N	ทิศเหนือ
	1, 2, 3, 4 ชื่อรูปด้านกำหนดจากแปลน
	A หมายถึง ชื่อรูปด้าน
	A หมายถึง ชื่อแบบขยาย
	A หมายถึง ชื่อรูปตัด
	A หมายถึง แนวจากระยะจากศูนย์กลาง
+0000 , -0000	+0000 มีค่าเท่ากับระดับที่กำหนด , -0000 มีค่าต่ำกว่าระดับที่กำหนด
	B หมายถึง ระยะความยาวจากศูนย์กลางถึงศูนย์กลาง
	B หมายถึง ระยะความยาวจากริมถึงริม
	A หมายถึง ระยะความยาวจากศูนย์กลางถึงผนังริมนอก
	A หมายถึง ระยะความยาวจากศูนย์กลางถึงผนังริมใน
	1 หมายถึง รหัสประตู
	1 หมายถึง รหัสหน้าต่าง
	1 หมายถึง หมายเลขผนัง
	ผนังก่ออิฐครึ่งแผ่น ฉาบปูน
	ผนังก่ออิฐเต็มแผ่น ฉาบปูน
	ผนังก่ออิฐมวลเบา ฉาบปูน
	ผนังก่ออิฐฉาบปูน ตามแบบระบุ
	ผนังแบบโครงคร่าวไม้ดีด กรวดตามแบบระบุ
	ดิน
	คอนกรีต
	ทรายอัดแน่น
	หินกาบ
	ปูนฉาบเรียบ
	ฉาบปูนขัดรอง
	ฉาบปูนเรียบ

บ้าน SMILE HOME
V.1 [11/2/45]


โครงการ
แบบบ้านยิ้มเพื่อประชาชน

ตามนโยบาย
ม.ร.ว. สุขุมพันธุ์ บริพัตร
ผู้ว่าราชการกรุงเทพมหานคร

โดยสำนักงานโยธา
กรุงเทพมหานคร


วัดชัย

ได้รับความอนุเคราะห์แบบ
จาก
บริษัท แลนด์ โฮม
(ประเทศไทย) จำกัด

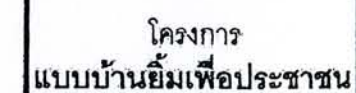

โดยสำนักงานโยธา
กรุงเทพมหานคร

ได้รับความอนุเคราะห์แบบ
จาก
บริษัท แลนด์ ไทม
(ประเทศไทย) จำกัด

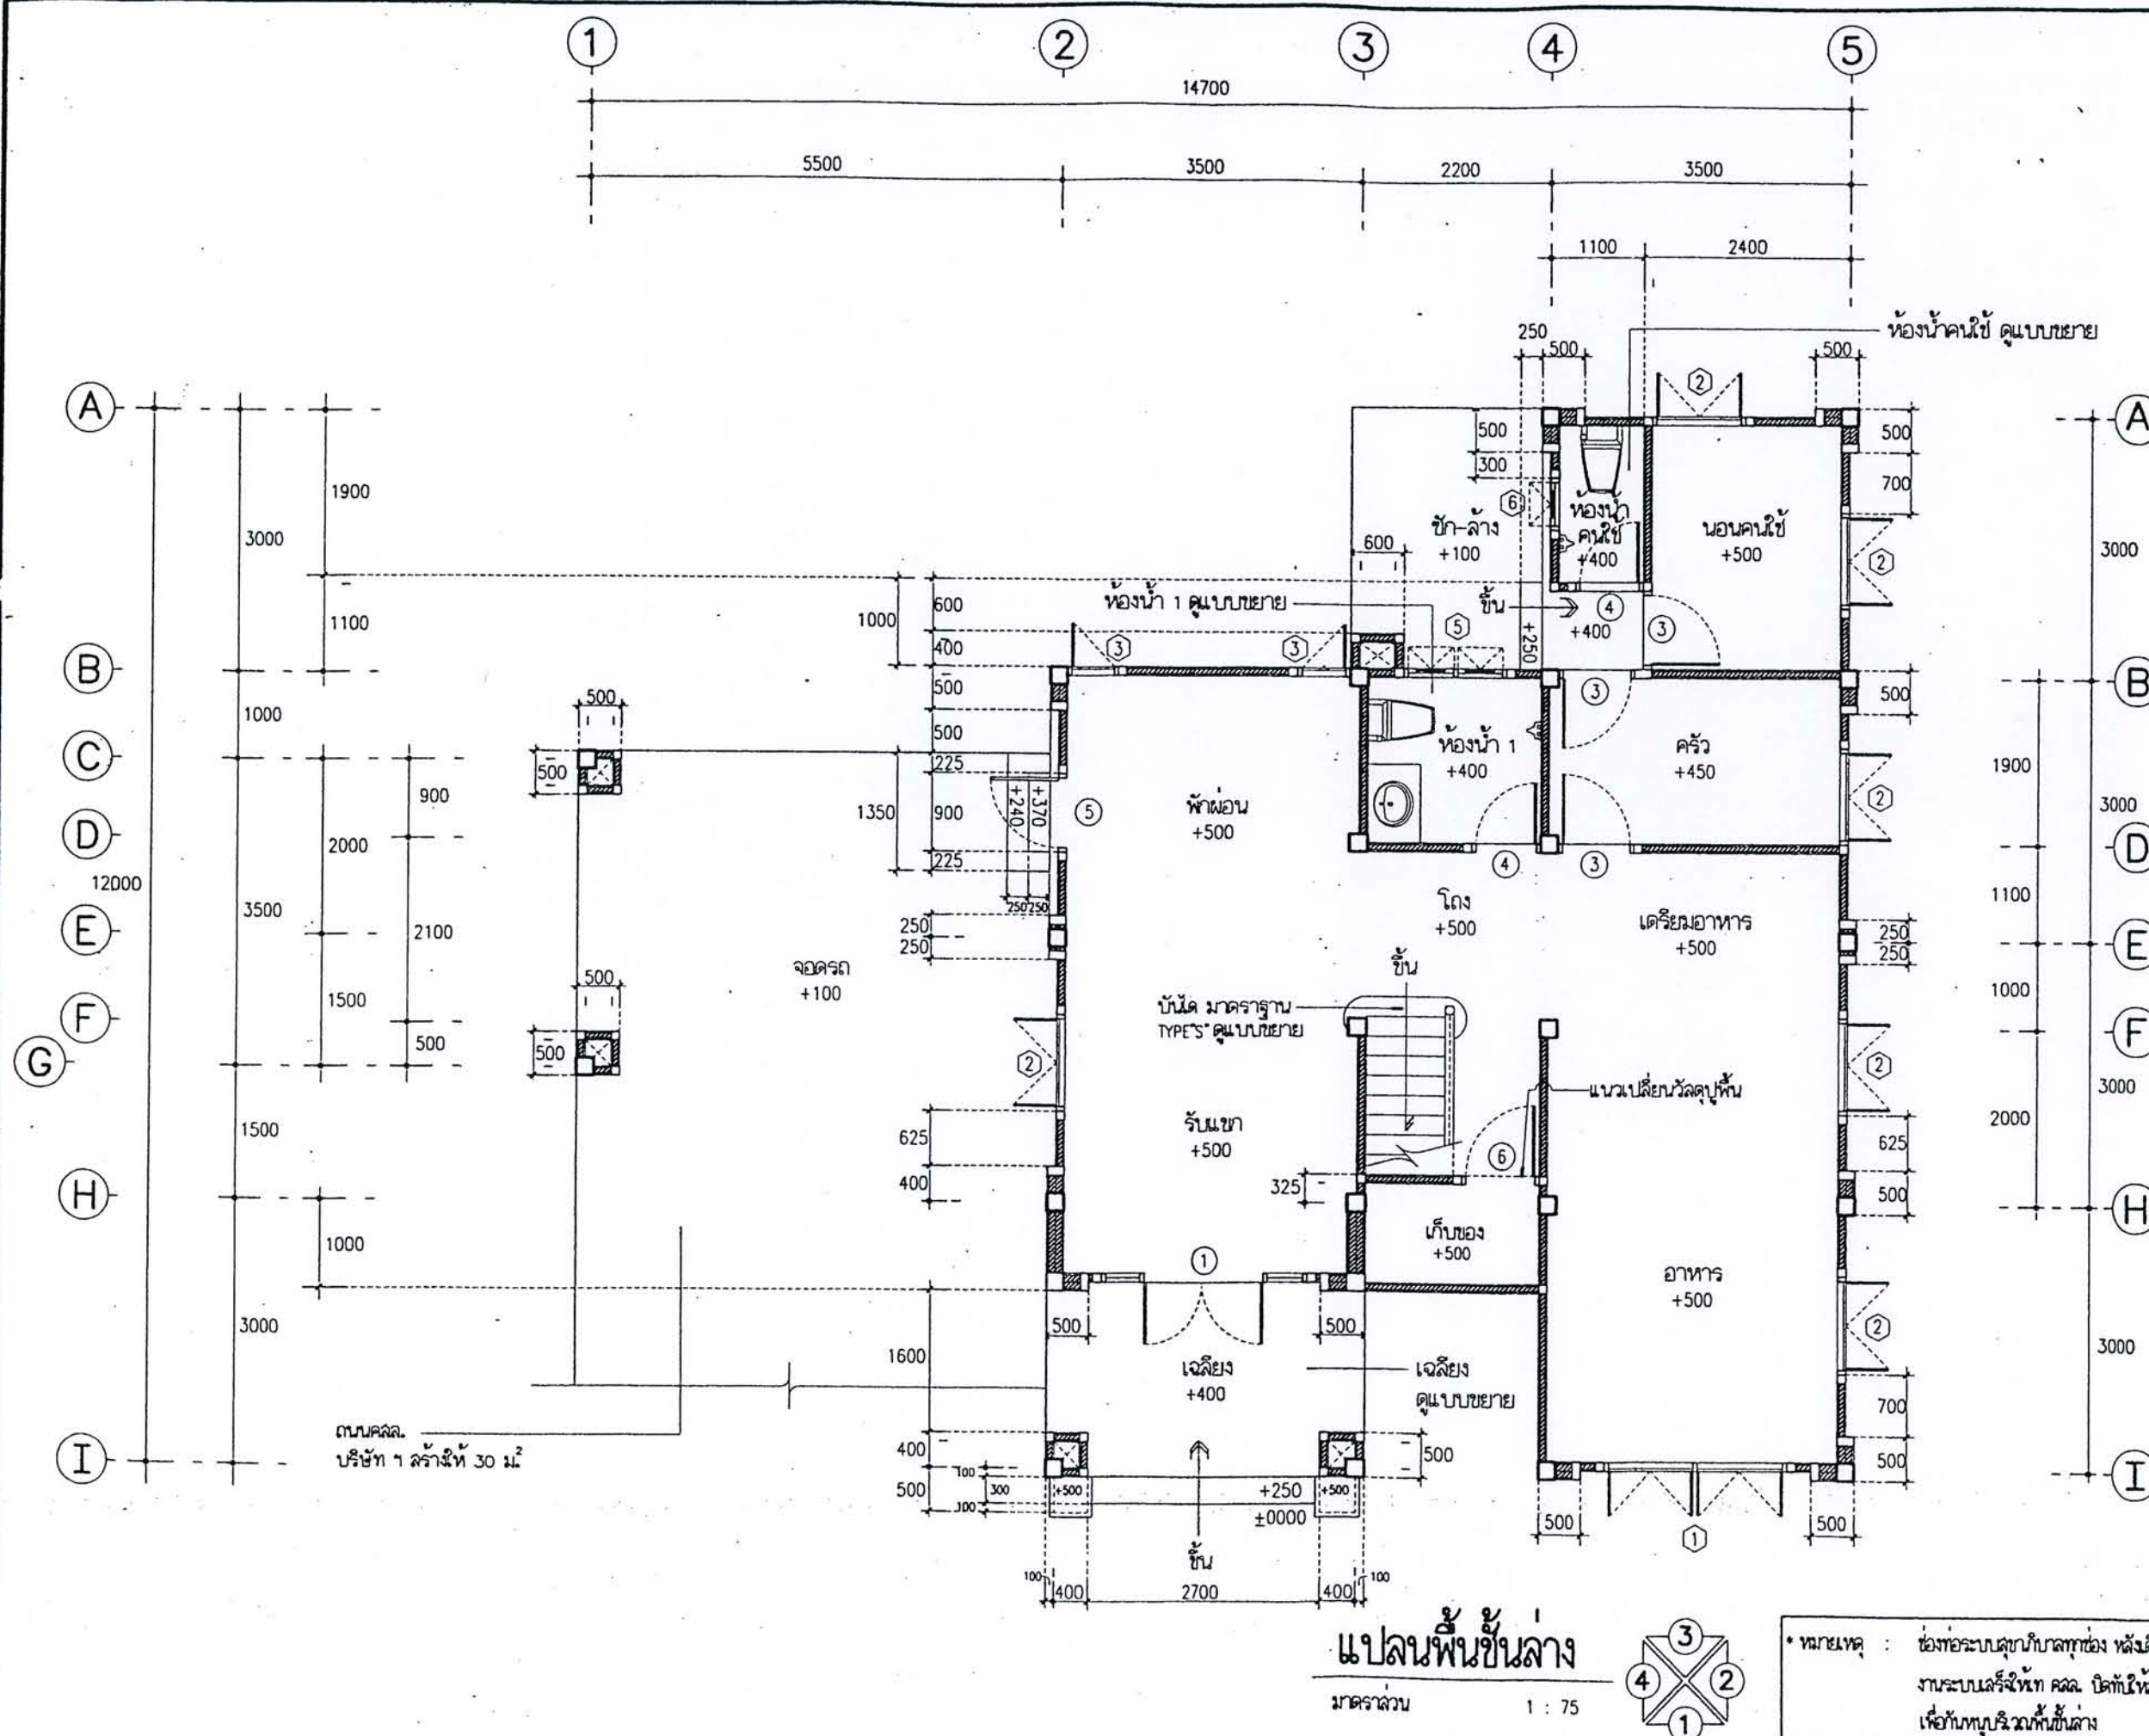




โครงการ
แบบบ้านยืมเพื่อประชาชน


ตามนโยบาย
ม.ร.ว. สุขุมพันธุ์ บริพัตร
ผู้ว่าราชการกรุงเทพมหานคร

โดยสำนักงานโยธา
กรุงเทพมหานคร

ได้รับความอนุเคราะห์แบบ
จาก
บริษัท แลนด์ โฮม
(ประเทศไทย) จำกัด

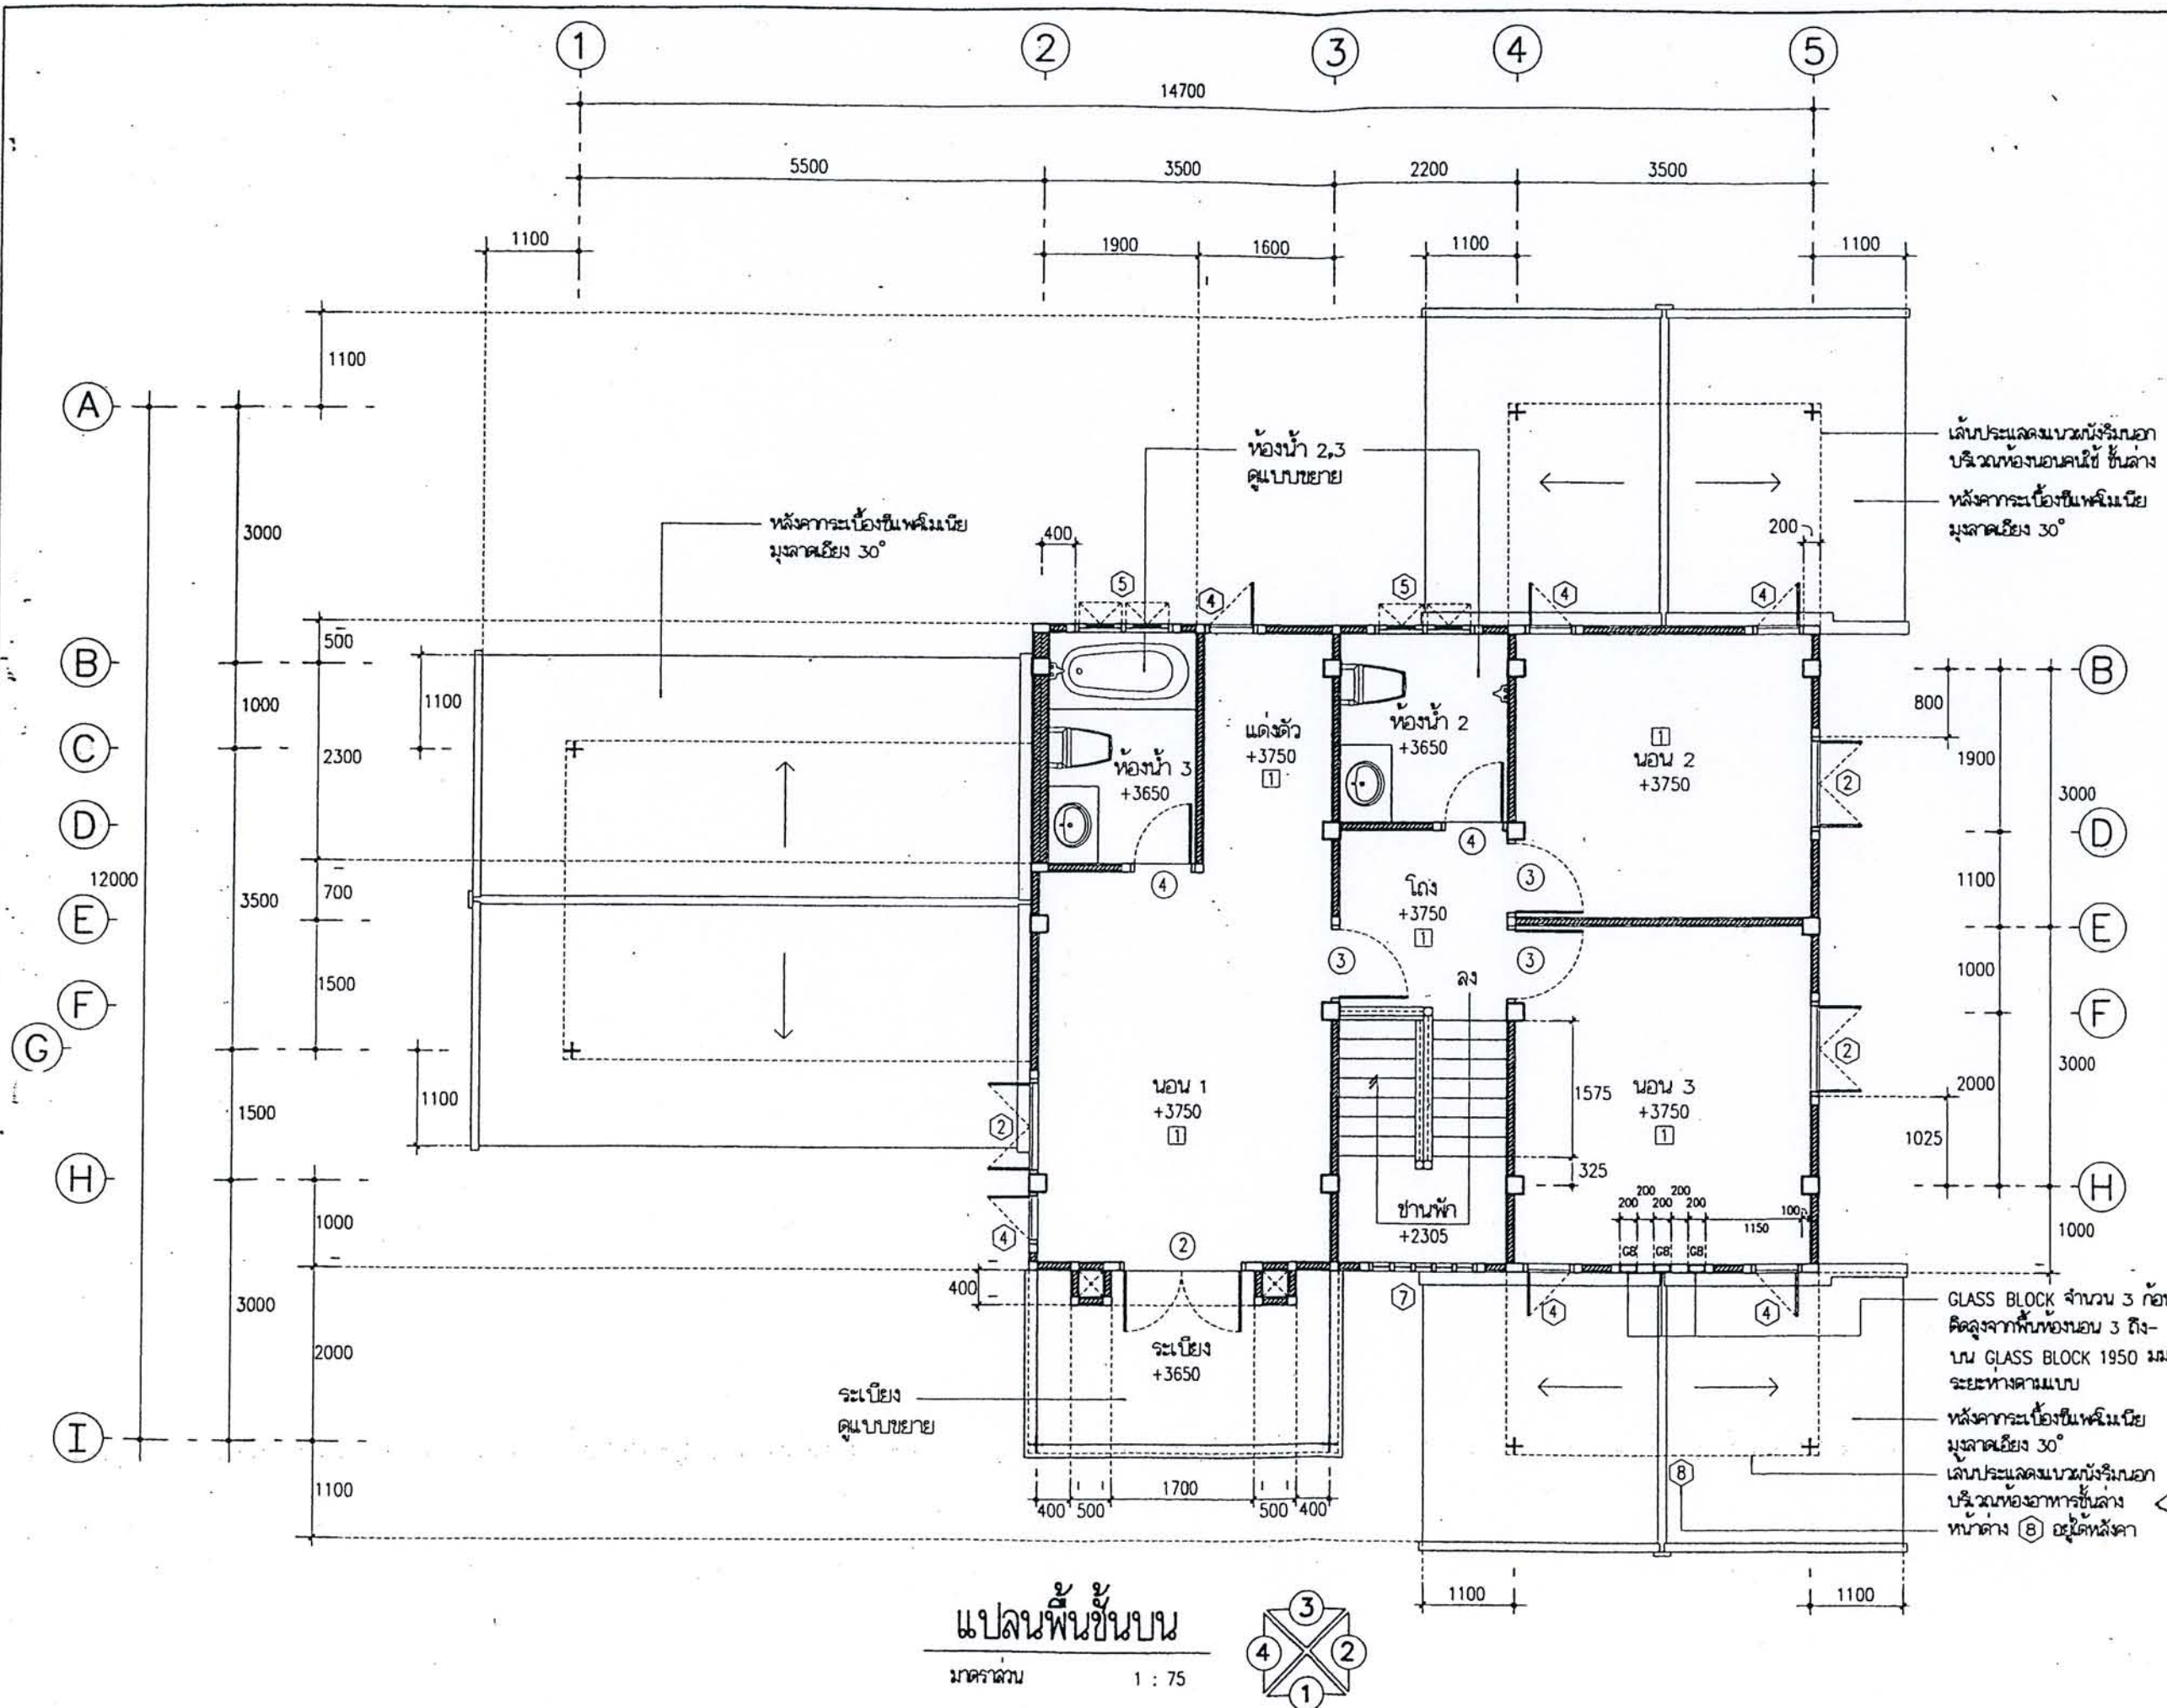

แปลนพื้นที่บน
มาตราส่วน 1 : 75

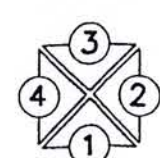




โครงการ
แบบบ้านยืมเพื่อประชาชน


ตามนโยบาย
ม.ร.ว. สุขุมพันธุ์ บริพัตร
ผู้ว่าราชการกรุงเทพมหานคร

โดยสำนักการโยธา
กรุงเทพมหานคร

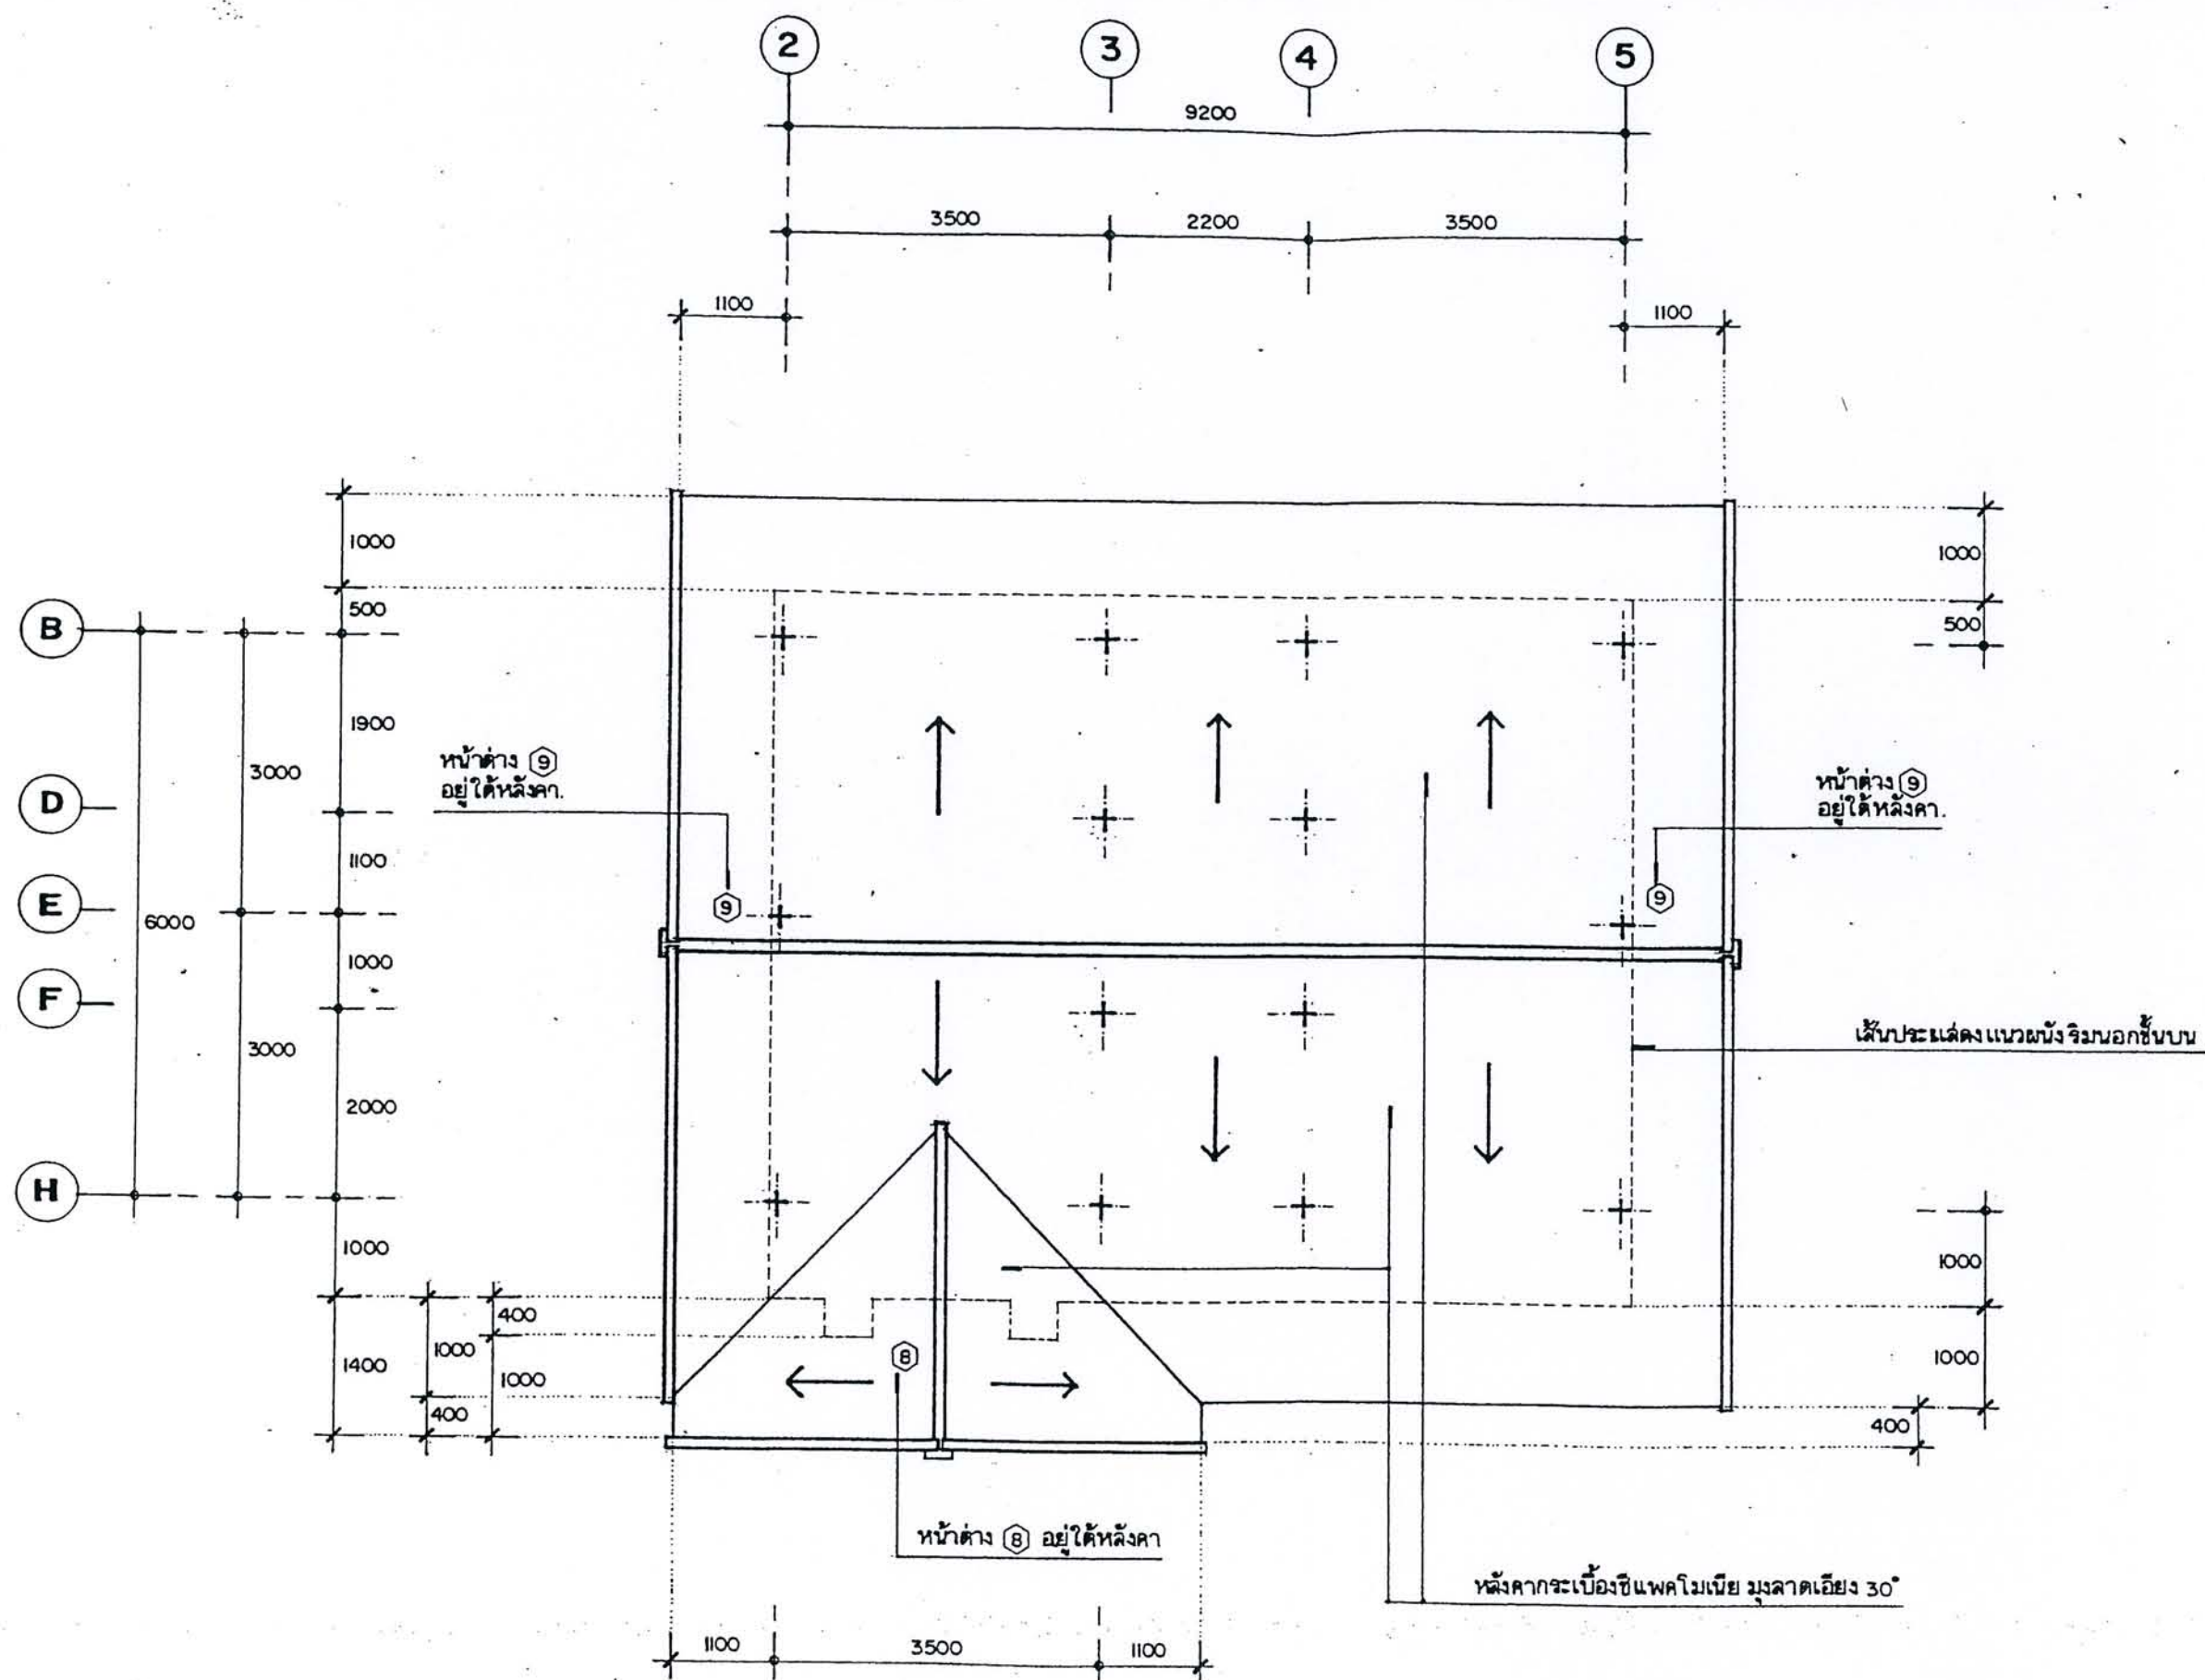


แปลนหลังคา

มาตราส่วน 1 : 75

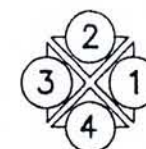

ได้รับความอนุเคราะห์แบบ
จาก
บริษัท แลนด์ โฮม
(ประเทศไทย) จำกัด

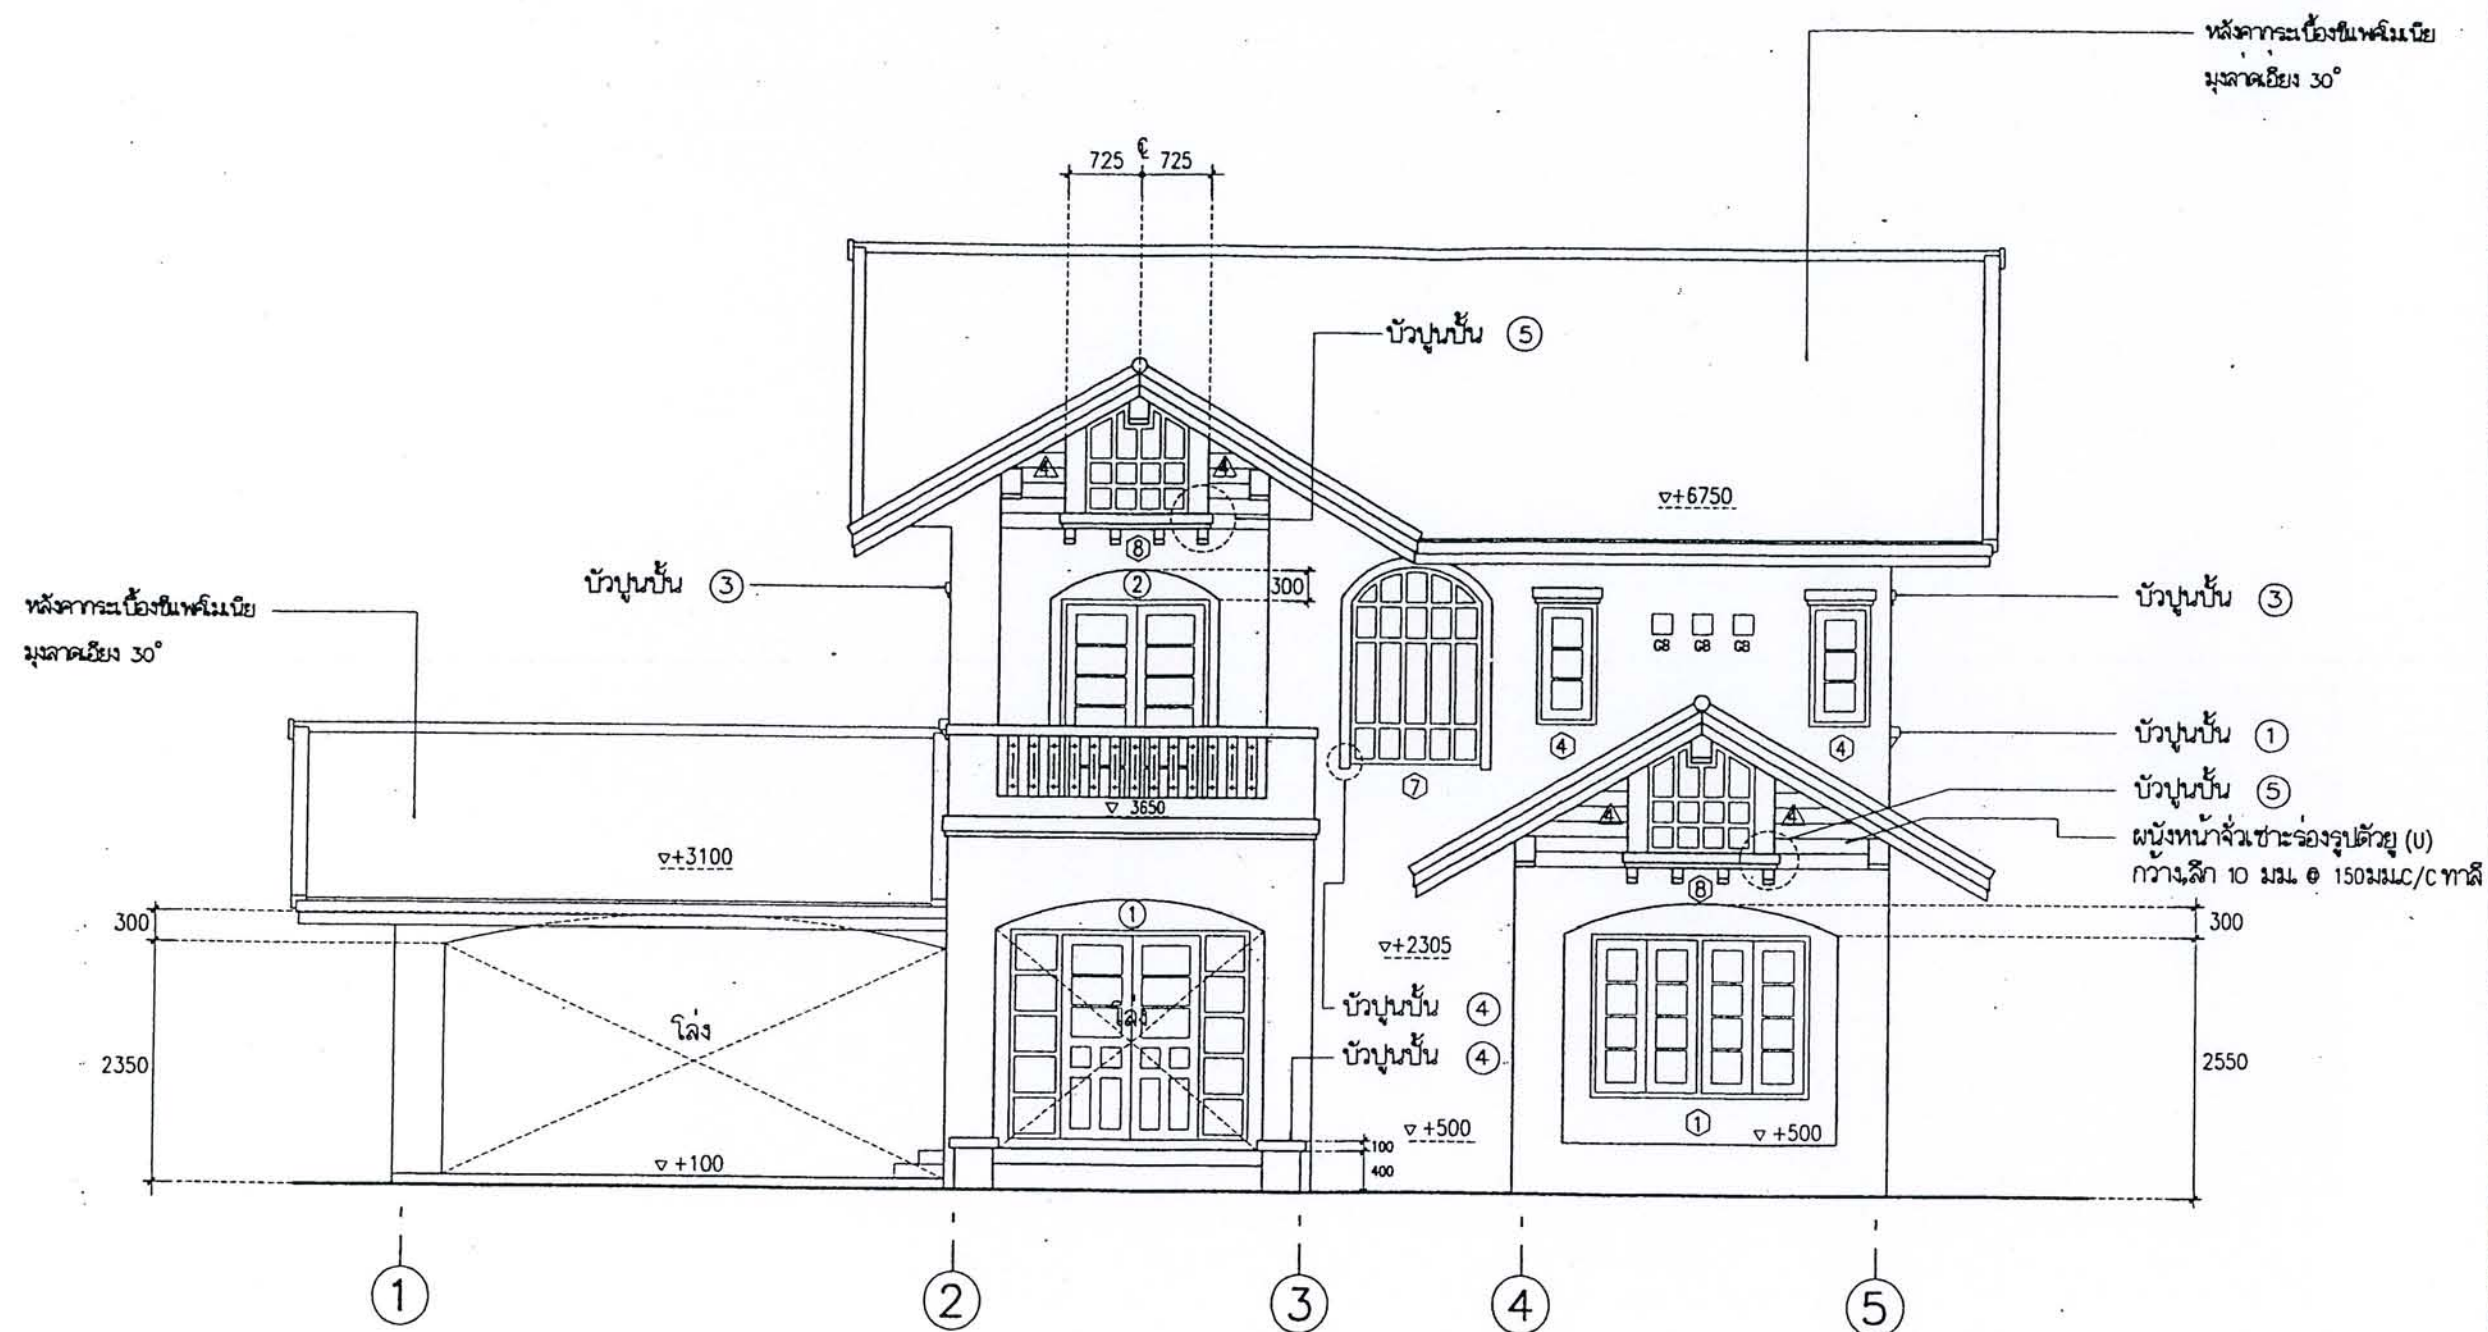


รูปด้าน 
มาตราส่วน 1 : 75



โครงการ
แบบบ้านยืมเพื่อประชาชน

ตามนโยบาย
ม.ร.ว. สุขุมพันธุ์ บริพัตร
ผู้ว่าราชการกรุงเทพมหานคร

โดยสำนักงานโยธา
กรุงเทพมหานคร

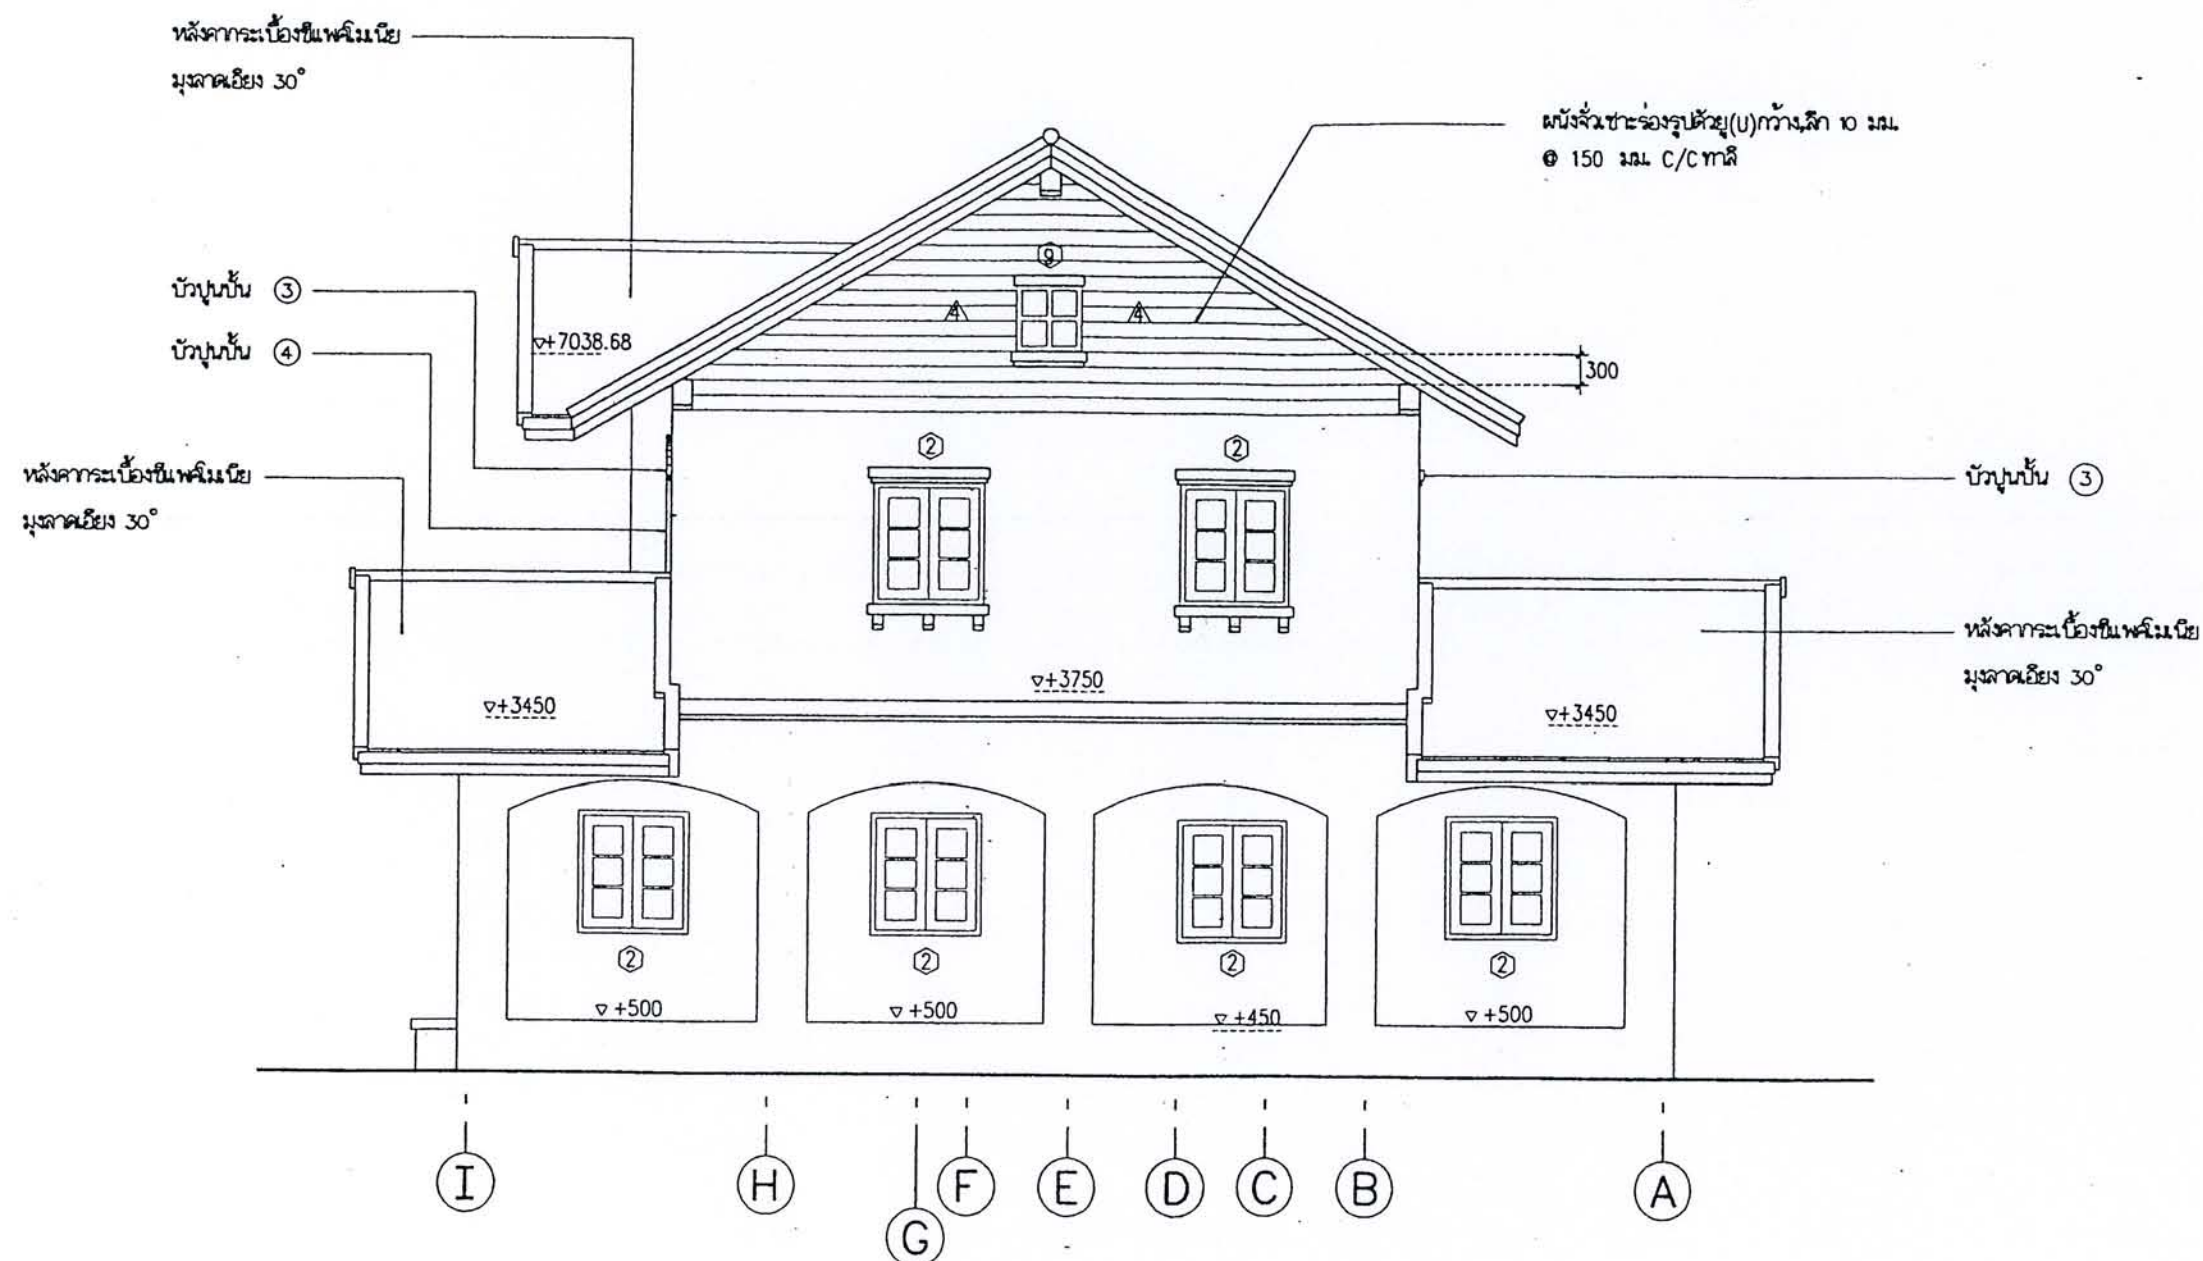

รูปด้าน ②
มาตราส่วน 1 : 75


ได้รับความอนุเคราะห์แบบ
จาก
บริษัท แลนด์ โชม
(ประเทศไทย) จำกัด



โครงการ
แบบบ้านยิมเพื่อประชาชน

ตามนโยบาย
ม.ร.ว. สุขุมพันธุ์ บริพัตร
ผู้ว่าราชการกรุงเทพมหานคร

โดยสำนักงานโยธา
กรุงเทพมหานคร

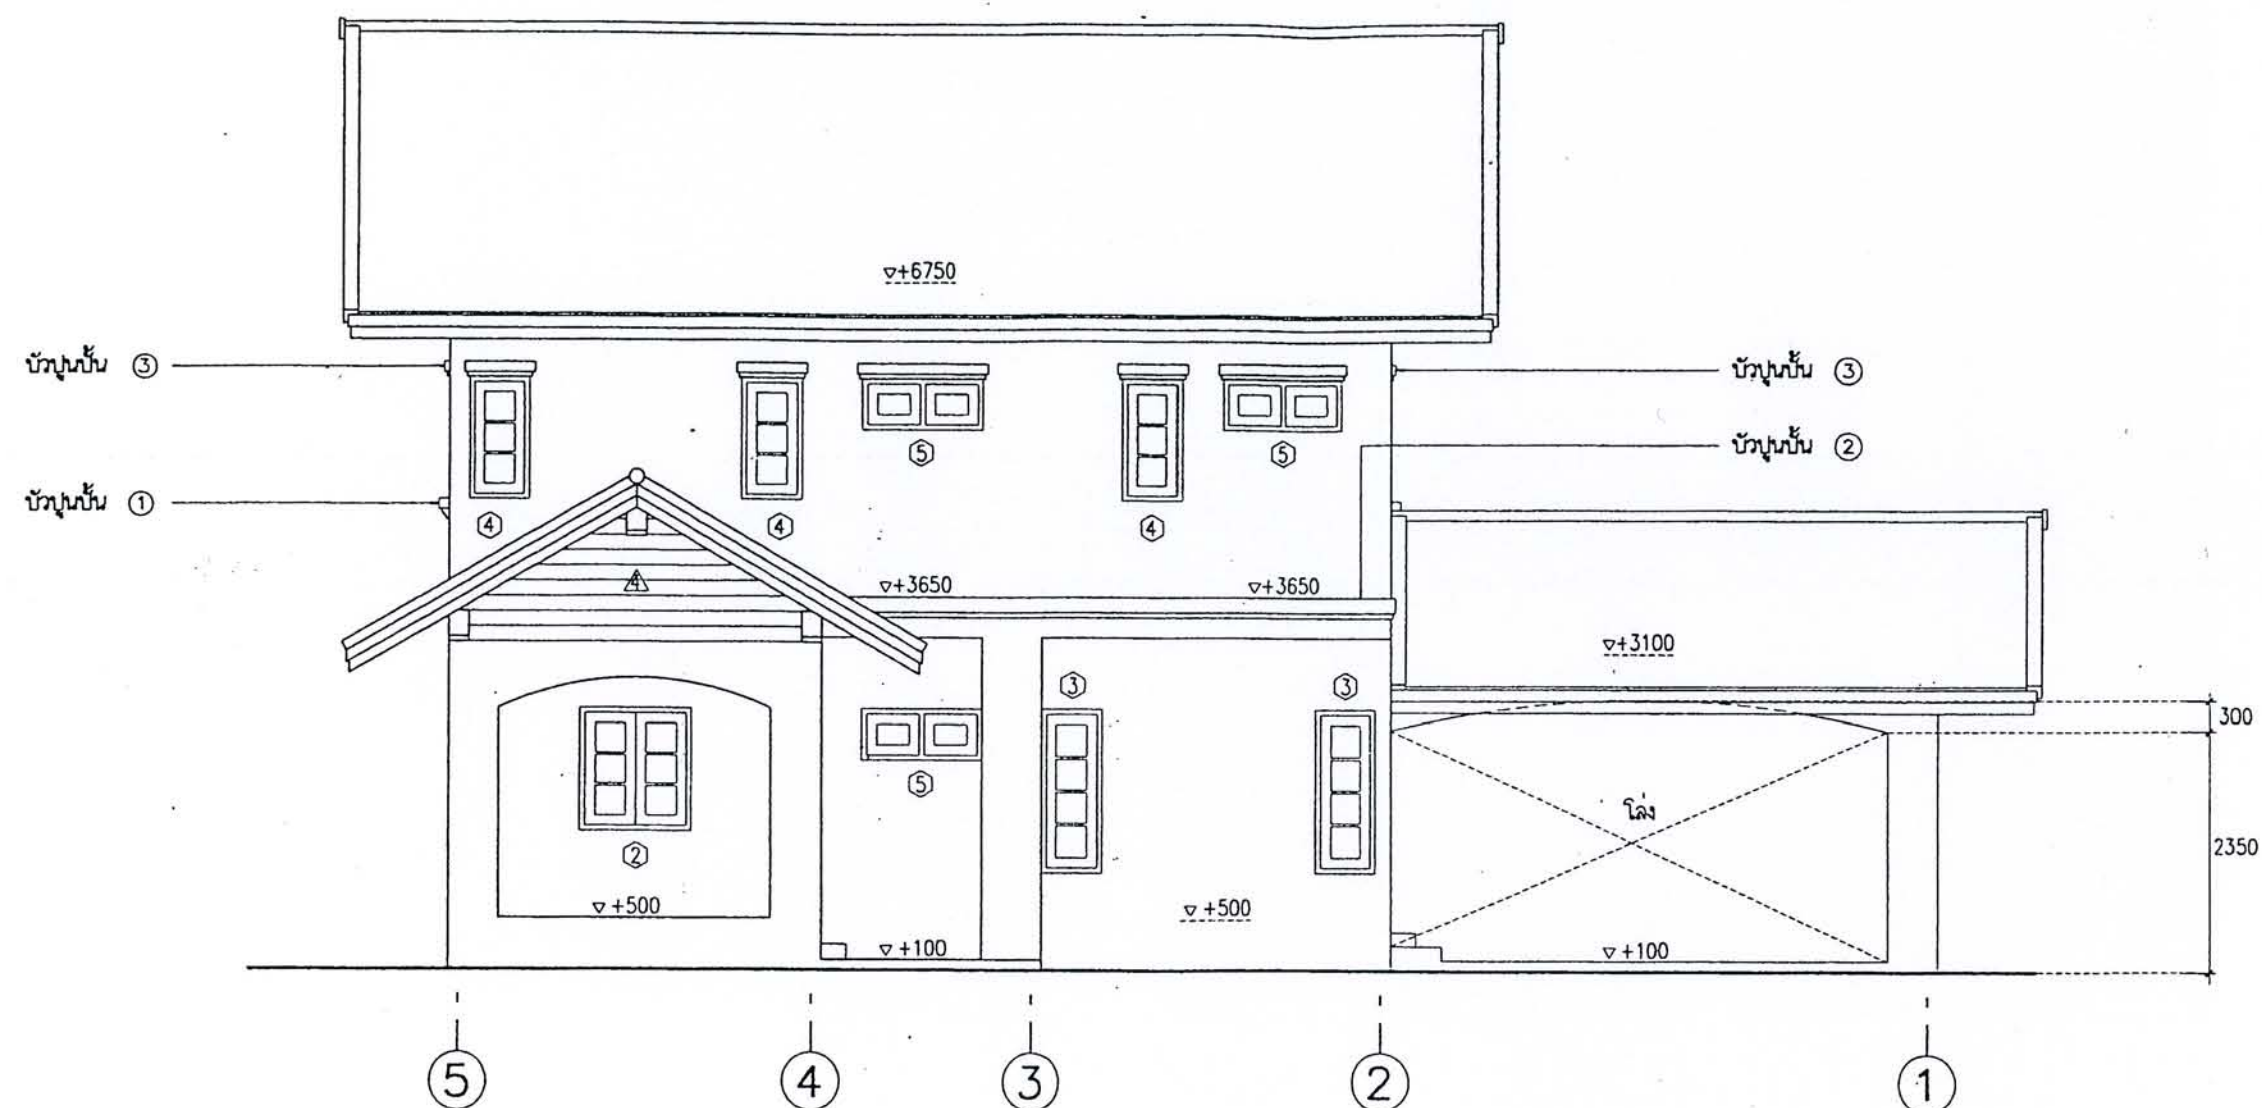

รูปด้าน 3
มาตราส่วน 1 : 75


ได้รับความอนุเคราะห์แบบ
จาก
บริษัท แลนด์ โสม
(ประเทศไทย) จำกัด



โครงการ
แบบบ้านยืมเพื่อประชาชน

ตามนโยบาย
ม.ร.ว. สุขุมพันธุ์ บริพัตร
ผู้ว่าราชการกรุงเทพมหานคร

โดยสำนักการโยธา
กรุงเทพมหานคร

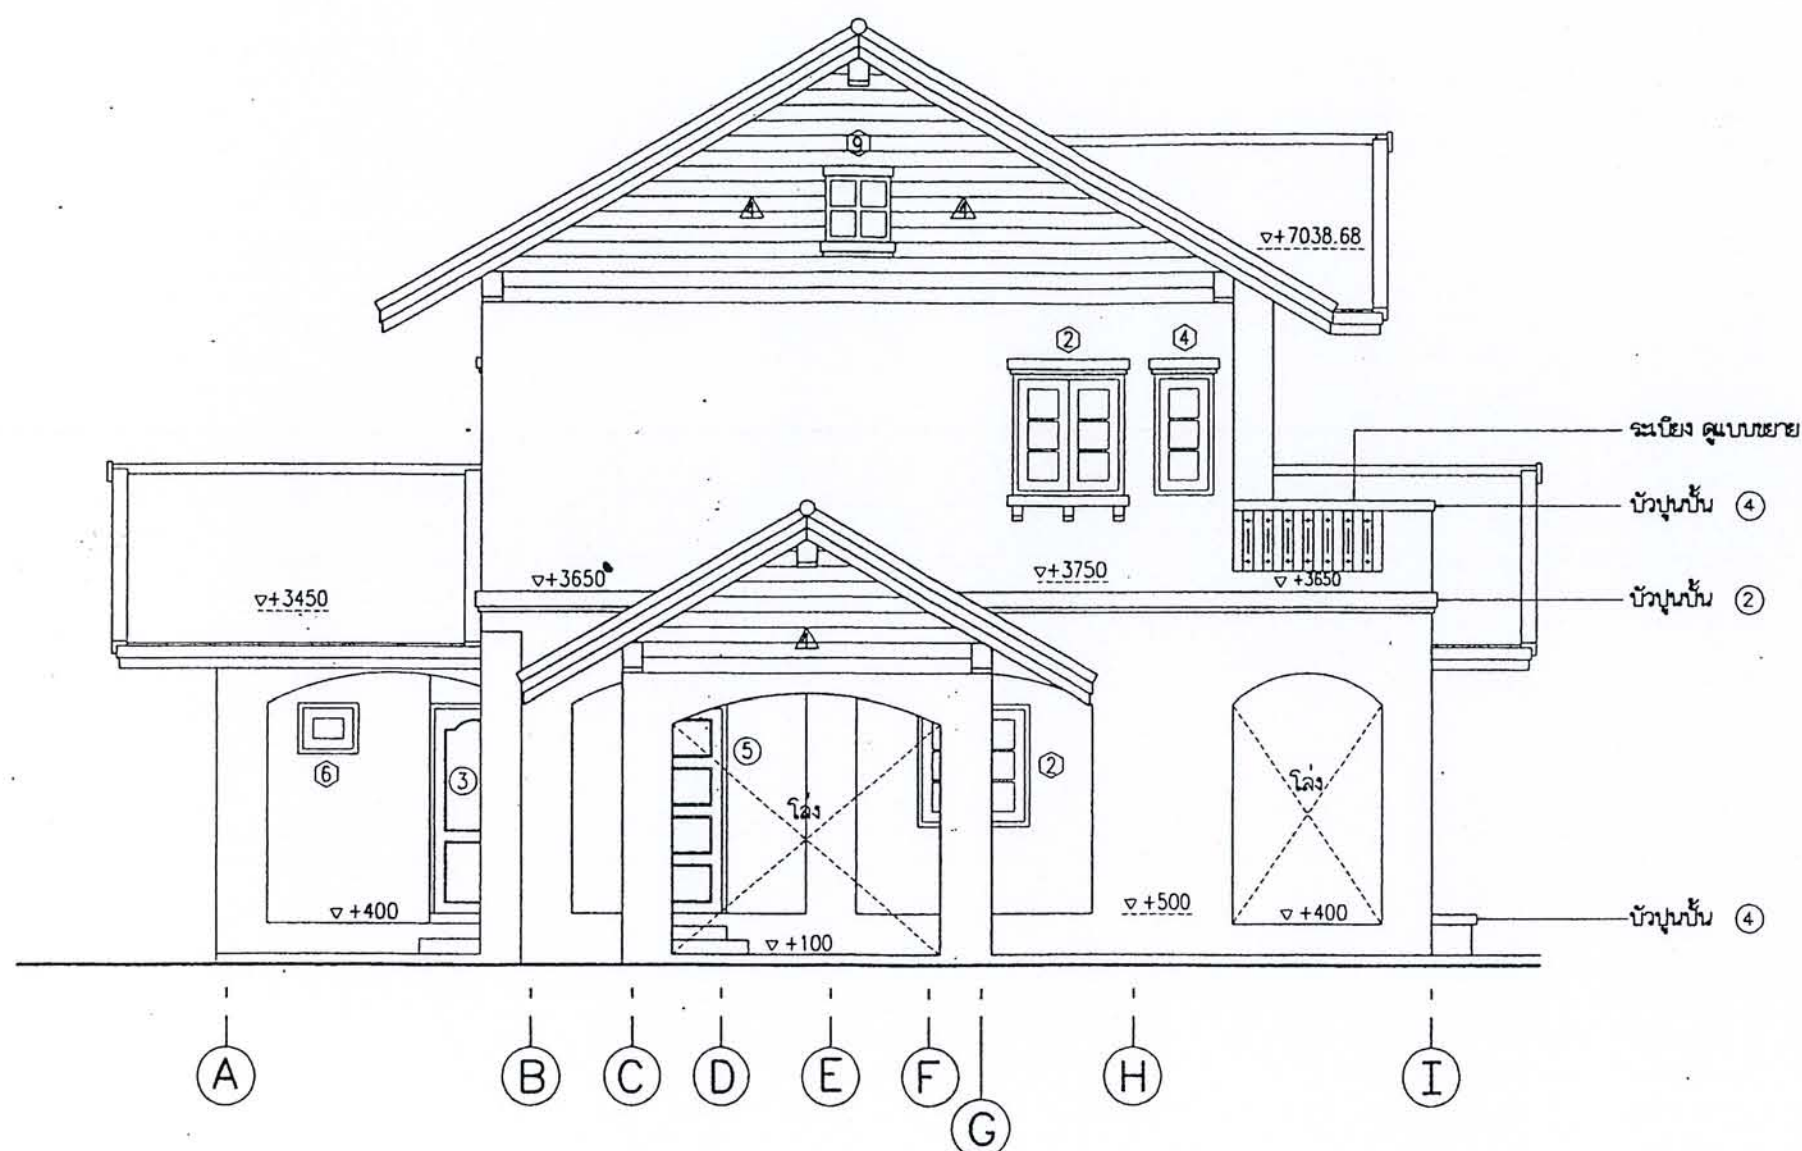

รูปด้าน
มาตราส่วน 1 : 75

ได้รับความอนุเคราะห์แบบ
จาก
บริษัท แลนด์ โสม
(ประเทศไทย) จำกัด

สัญลักษณ์ประกอบแบบ "S"



รายการไฟฟ้า

สัญลักษณ์	ความหมาย	ขนาด - ยี่ห้อ - รุ่น
	แผงควบคุมไฟฟ้า	Square-D ขนาด 15 A แบบควบคุมด้วยมือ
	โคมไฟฟ้า	ครอบแก้วกลม Ø 14" ผิวทึบหลอดฟลูออโรเรสเซนต์ 32 W. แบบกลมแสงสีขาว
	โคมไฟฟ้า	ครอบแก้วกลม Ø 8" หลอดทั้งหลอด 60 W. แสงสีเหลือง
	หลอดฟลูออโรเรสเซนต์	รางหลอดฟลูออโรเรสเซนต์ ครอบพลาสติก ขนาด 1 X 20 W. แสงสีขาว
	หลอดฟลูออโรเรสเซนต์	รางหลอดฟลูออโรเรสเซนต์ ครอบพลาสติก ขนาด 1 X 40 W. แสงสีขาว
	ไฟโคมแบบพาดาน	โคมไฟแก้วผิวทึบ Ø 12" หลอดธรรมดา 60 W.
	ไฟกิ่งติดผนัง	ไฟกิ่งหลอด 60 W. พานเหลี่ยม
	สวิทช์ไฟฟ้า	Single way ชนิดฝังในผนังของ NATIONAL (ชองเก้) ติดตั้งสูงจากพื้น 1200 มม.
	สวิทช์ไฟฟ้า 2 ทาง	Two way ชนิดฝังในผนังของ NATIONAL (ชองเก้) ติดตั้งสูงจากพื้น 1200 มม.
	ปลั๊กไฟ, เต้าเสียบ	ปลั๊กไฟแบบเรียบชนิดฝังในผนังแบบ 2 เต้าเสียบต่อ 1 ชุด พร้อมสายดินตาม- การไฟฟ้า ติดตั้งสูงจากพื้น 200 มม. ของ NATIONAL (ชองเก้) ติดห่างจากผนัง 100 มม.
	ปลั๊กไฟ, เต้าเสียบ	ปลั๊กไฟแบบเรียบชนิดฝังในผนังแบบ 2 เต้าเสียบต่อ 1 ชุด พร้อมสายดินตาม- การไฟฟ้า ติดตั้งสูงจากพื้น 1000 มม. ของ NATIONAL (ชองเก้) ติดห่างจากผนัง 100 มม.
	ปลั๊กสายอากาศ TV.	ใช้สายอากาศ TV. C-5 โดยเดินสายไปยังหม้อน้ำห้องน้ำขึ้นบนแล้วห้อยปลั๊กไว้ 1 ม.
	โทรศัพท์	เดินสายตามมาตรฐานไฟฟ้า โดยเดินสายไปยังสายเคเบิลหน้าบ้านแล้วห้อยปลั๊กไว้ 1 ม.
	สวิทช์แอร์	ตามแบบฉบับ
	แสดงการเดินสายไฟแบบ-	สายไฟใช้สาย PVC. ของ YAZAKI หรือ BANGKOK CABLE
	เดินลอย	เดินลอยยึดด้วยสายรัดเข็มขัดระยะห่าง 100 มม. โดย - สายไฟสำหรับ สวิทช์ไฟ ที่มิใช่ใช้ ขนาด 1.0 มม. ² - สายไฟสำหรับ ปลั๊กไฟ ที่มิใช่ใช้ ขนาด 2.5 มม. ² (แบบมีสายดิน) - สายไฟสำหรับ แอร์ ที่มิใช่ใช้ ขนาด 10.0 มม. ² - สายไฟสำหรับ เครื่องทำน้ำร้อน ที่มิใช่ใช้ ขนาด 10.0 มม. ² - สำหรับสายเมนใช้สาย PVC. ของ YAZAKI หรือ BANGKOK CABLE- ขนาด 16.00 มม. ² ต่อห่างจากชายค้ำไม่เกิน 16000 มม.
หมายเหตุ :		- ให้เดินสายดินตามกฎระเบียบของการไฟฟ้าอย่างถูกต้อง
		- ราคากำหนด 3,000,000 บาท ใช้ไฟ ขนาด 30 Amp. 2 สายของ Square-D พร้อมสายเมน แบบลูกเซอร์กิต 18 ช่อง
		- ราคากำหนด 5,000,000 บาท ใช้ไฟ ขนาด 50 Amp. 2 สายของ Square-D พร้อมสายเมน

รายการเปลี่ยนแปลงเพิ่มเติมไฟฟ้า

* บ้านเลขที่ 111 ใช้ไฟฟ้าขนาด 30 Amp. 2 สายของ Square-D พร้อม-
สายเมน แบบลูกเซอร์กิต 18 ช่อง ตามใบปลิว 4/2

โครงการ
แบบบ้านยืมเพื่อประชาชน

ตามนโยบาย
ม.ร.ว. สุขุมพันธุ์ บริพัตร
ผู้ว่าราชการกรุงเทพมหานคร

โดยสำนักงานโยธา
กรุงเทพมหานคร

บ้าน SMILE HOME
V.1 [11/2/45]

ได้รับความอนุเคราะห์แบบ
จาก
บริษัท แลนด์ โสม
(ประเทศไทย) จำกัด

สัญลักษณ์ประกอบแบบ "S"



โครงการ
แบบบ้านยิ้มเพื่อประชาชน

ตามนโยบาย
ม.ร.ว. สุขุมพันธุ์ บริพัตร
ผู้ว่าราชการกรุงเทพมหานคร

โดยสำนักงานโยธา
กรุงเทพมหานคร

ได้รับความอนุเคราะห์แบบ
จาก
บริษัท แลนด์ โสม
(ประเทศไทย) จำกัด

รายการสัญลักษณ์

สัญลักษณ์	ความหมาย	ขนาด และ จำนวนอุปกรณ์ที่ใช้
	ท่อรวม	ท่อ PVC. Ø 4" ขึ้นคุณภาพ Class 8.5 ติดตั้งให้มีความลาดเอียง 1 : 200 ปลายท่อ-
		ให้ท่อแบบ 3 ทาง ตัว T
	ท่อน้ำทิ้ง	(ท่อเมน) ท่อ PVC. Ø 2" ขึ้นคุณภาพ Class 8.5 ติดตั้งให้มีความลาดเอียง 1 : 200
		ให้ท่อน้ำทิ้งให้ลึกลง
	ท่อน้ำทิ้ง	(ต่อจากสัญลักษณ์) ท่อ PVC. Ø 1 1/2" ขึ้นคุณภาพ Class 8.5
	ท่อน้ำดี	(ท่อประปา) ท่อ PVC. Ø 1/2" ขึ้นคุณภาพ Class 13.5
	ท่อน้ำเย็น	(ท่อเมน) ท่อ PVC. Ø 3/4" ขึ้นคุณภาพ Class 13.5
	ท่อน้ำร้อน	ใช้ท่อเหล็กอาบสังกะสี Class B Ø 1/2"
	ท่อระบายอากาศ	ท่อ PVC Ø 1" ขึ้นคุณภาพ Class 8.5 ปลายท่อด้วยข้อต่อ 3 ทาง ตัว T
		ท่อระบายอากาศสูงจากพื้น 3500 มม. ยึดติดกับผนังหรือล้อยึดระยะห่าง 300 มม.
	ท่อระบายน้ำเสีย	ท่อซีเมนต์ใยหิน Ø 150 มม. ติดตั้งให้มีความลาดเอียง 1 : 200 ข้อต่อบริเวณท่อกับ-
		บ่อพักให้ท่อน้ำเข้าในบ่อพักอย่างน้อย 50 มม.
	จุดระบายน้ำทิ้ง	ตำแหน่งที่จุดระบายน้ำทิ้งจะลงซึ่งต้องลงท่อเมนน้ำทิ้งมีแผ่นเหล็กตะแกรงจกพื้น
	จุดระบายน้ำทิ้ง	ตำแหน่งจุดน้ำทิ้งจากชักโครก
	บ่อพัก	บ่อพักน้ำเสียสำเร็จรูป ขนาด 300X400X400 มม. พร้อมฝาปิดทึบระยะ 6.00 ม.
		ทุกช่วงพักเดียว
	จุดจ่ายน้ำประปา	จุดจ่ายน้ำดี (ประปา) ซึ่งต้องสูงให้ได้ตามแบบ
	บ่อกรอง	ใช้ระบบบำบัดน้ำเสีย ดักบำบัดน้ำเสียสำเร็จรูป ของ AQUA-PAC รุ่น AP-1600 หรือเทียบเท่า
	มิเตอร์น้ำ	ตามมาตรฐานของการประปา
	เครื่องปั๊มน้ำ	ตำแหน่งตามแบบ
	แนวลาดเอียง	ลาดเอียงตามแบบ

- หมายเหตุ :
1. ท่อ PVC. ที่ข้อต่อทุกจุดจะต้องทากาวก่อนต่อ เมื่อต่อท่อเสร็จเรียบร้อยแล้วให้รอให้แห้ง
 2. ท่อน้ำดีจะต้องมีสัญลักษณ์ที่แสดงตำแหน่งของเหล็กทุกจุดและบริเวณรอยต่อระหว่างท่อ PVC. เข้ากับข้องอเหล็กจะต้องพันทากาวก่อนต่อ เมื่อต่อท่อเสร็จเรียบร้อยแล้วให้รอให้แห้ง
 3. ท่อประปา (น้ำร้อน) ที่ต่อกับสายอ่อนให้ใช้กาวลาเท็กซ์ทุกจุด
 4. ท่อระบายน้ำและบ่อพักต้องจากตัวอาคาร ถึงบ่อพักสาธารณะไม่น้อยกว่า 16.00 ม.

รายการประกอบแบบสัญลักษณ์ TYPE "S"

อ่างอาบน้ำ (ถัง)	CRISTINA (TEENA-D) CT-5013 C พร้อมเดินสายไฟฟ้า และ ท่อน้ำร้อนของเครื่องทำน้ำร้อน 1 ชุด (ไม่รวมเครื่องทำน้ำร้อน) ก๊อกผสมน้ำ JAZZ STD. A 7601 (AMERICAN STANDARD)
อ่างล้างหน้า	AMERICAN STANDARD รุ่น TF-476 ชนิดฝังคาน์เตอร์ , ก๊อกน้ำ JAZZ STD. A 7000 พร้อมอุปกรณ์ติดตั้ง
ก๊อกอาบน้ำ	ใช้แบบ BALL VALVE (ที่เปิด)
โถล้างนั่งราบบ	AMERICAN STANDARD รุ่น TF-2310 (ที่เปิด) , ลายฮาร์ส HANG 5502 , รุ่น TF-2310 (คนใช้)
ฝักบัวสายอ่อน	JAZZ STD. A 7003 A (AMERICAN STANDARD)
ที่วางสบู่	AMERICAN STANDARD รุ่น TF-9000
ที่ใส่กระดาษชำระ	AMERICAN STANDARD รุ่น TF-9001
ราวน้ำหนัก	AMERICAN STANDARD รุ่น TF-9085
กระจกเงา	กระจกเบveled กระจกใส ยึดด้วยกาว
สีอุปกรณ์	ที่ปิดเปิดแบบ BEIGE ยกเว้นห้องน้ำคนใช้ ใช้สีขาว

รายการประกอบแบบสัญลักษณ์ กรณีมีการเปลี่ยนแปลงเพิ่มเติม

* ไม่มีรายการเปลี่ยนแปลง

รายการเปลี่ยนแปลงเพิ่มเติมสัญลักษณ์

* ไม่มีรายการเปลี่ยนแปลง

บ้าน SMILE HOME
V.1 [11/2/45]




โครงการ
แบบบ้านยิมเพื่อประชาชน

ตามนโยบาย
ม.ร.ว. สุขุมพันธุ์ บริพัตร
ผู้ว่าราชการกรุงเทพมหานคร

โดยสำนักการโยธา
กรุงเทพมหานคร

ได้รับความอนุเคราะห์แบบ
จาก
บริษัท แลนด์ โฮม
(ประเทศไทย) จำกัด

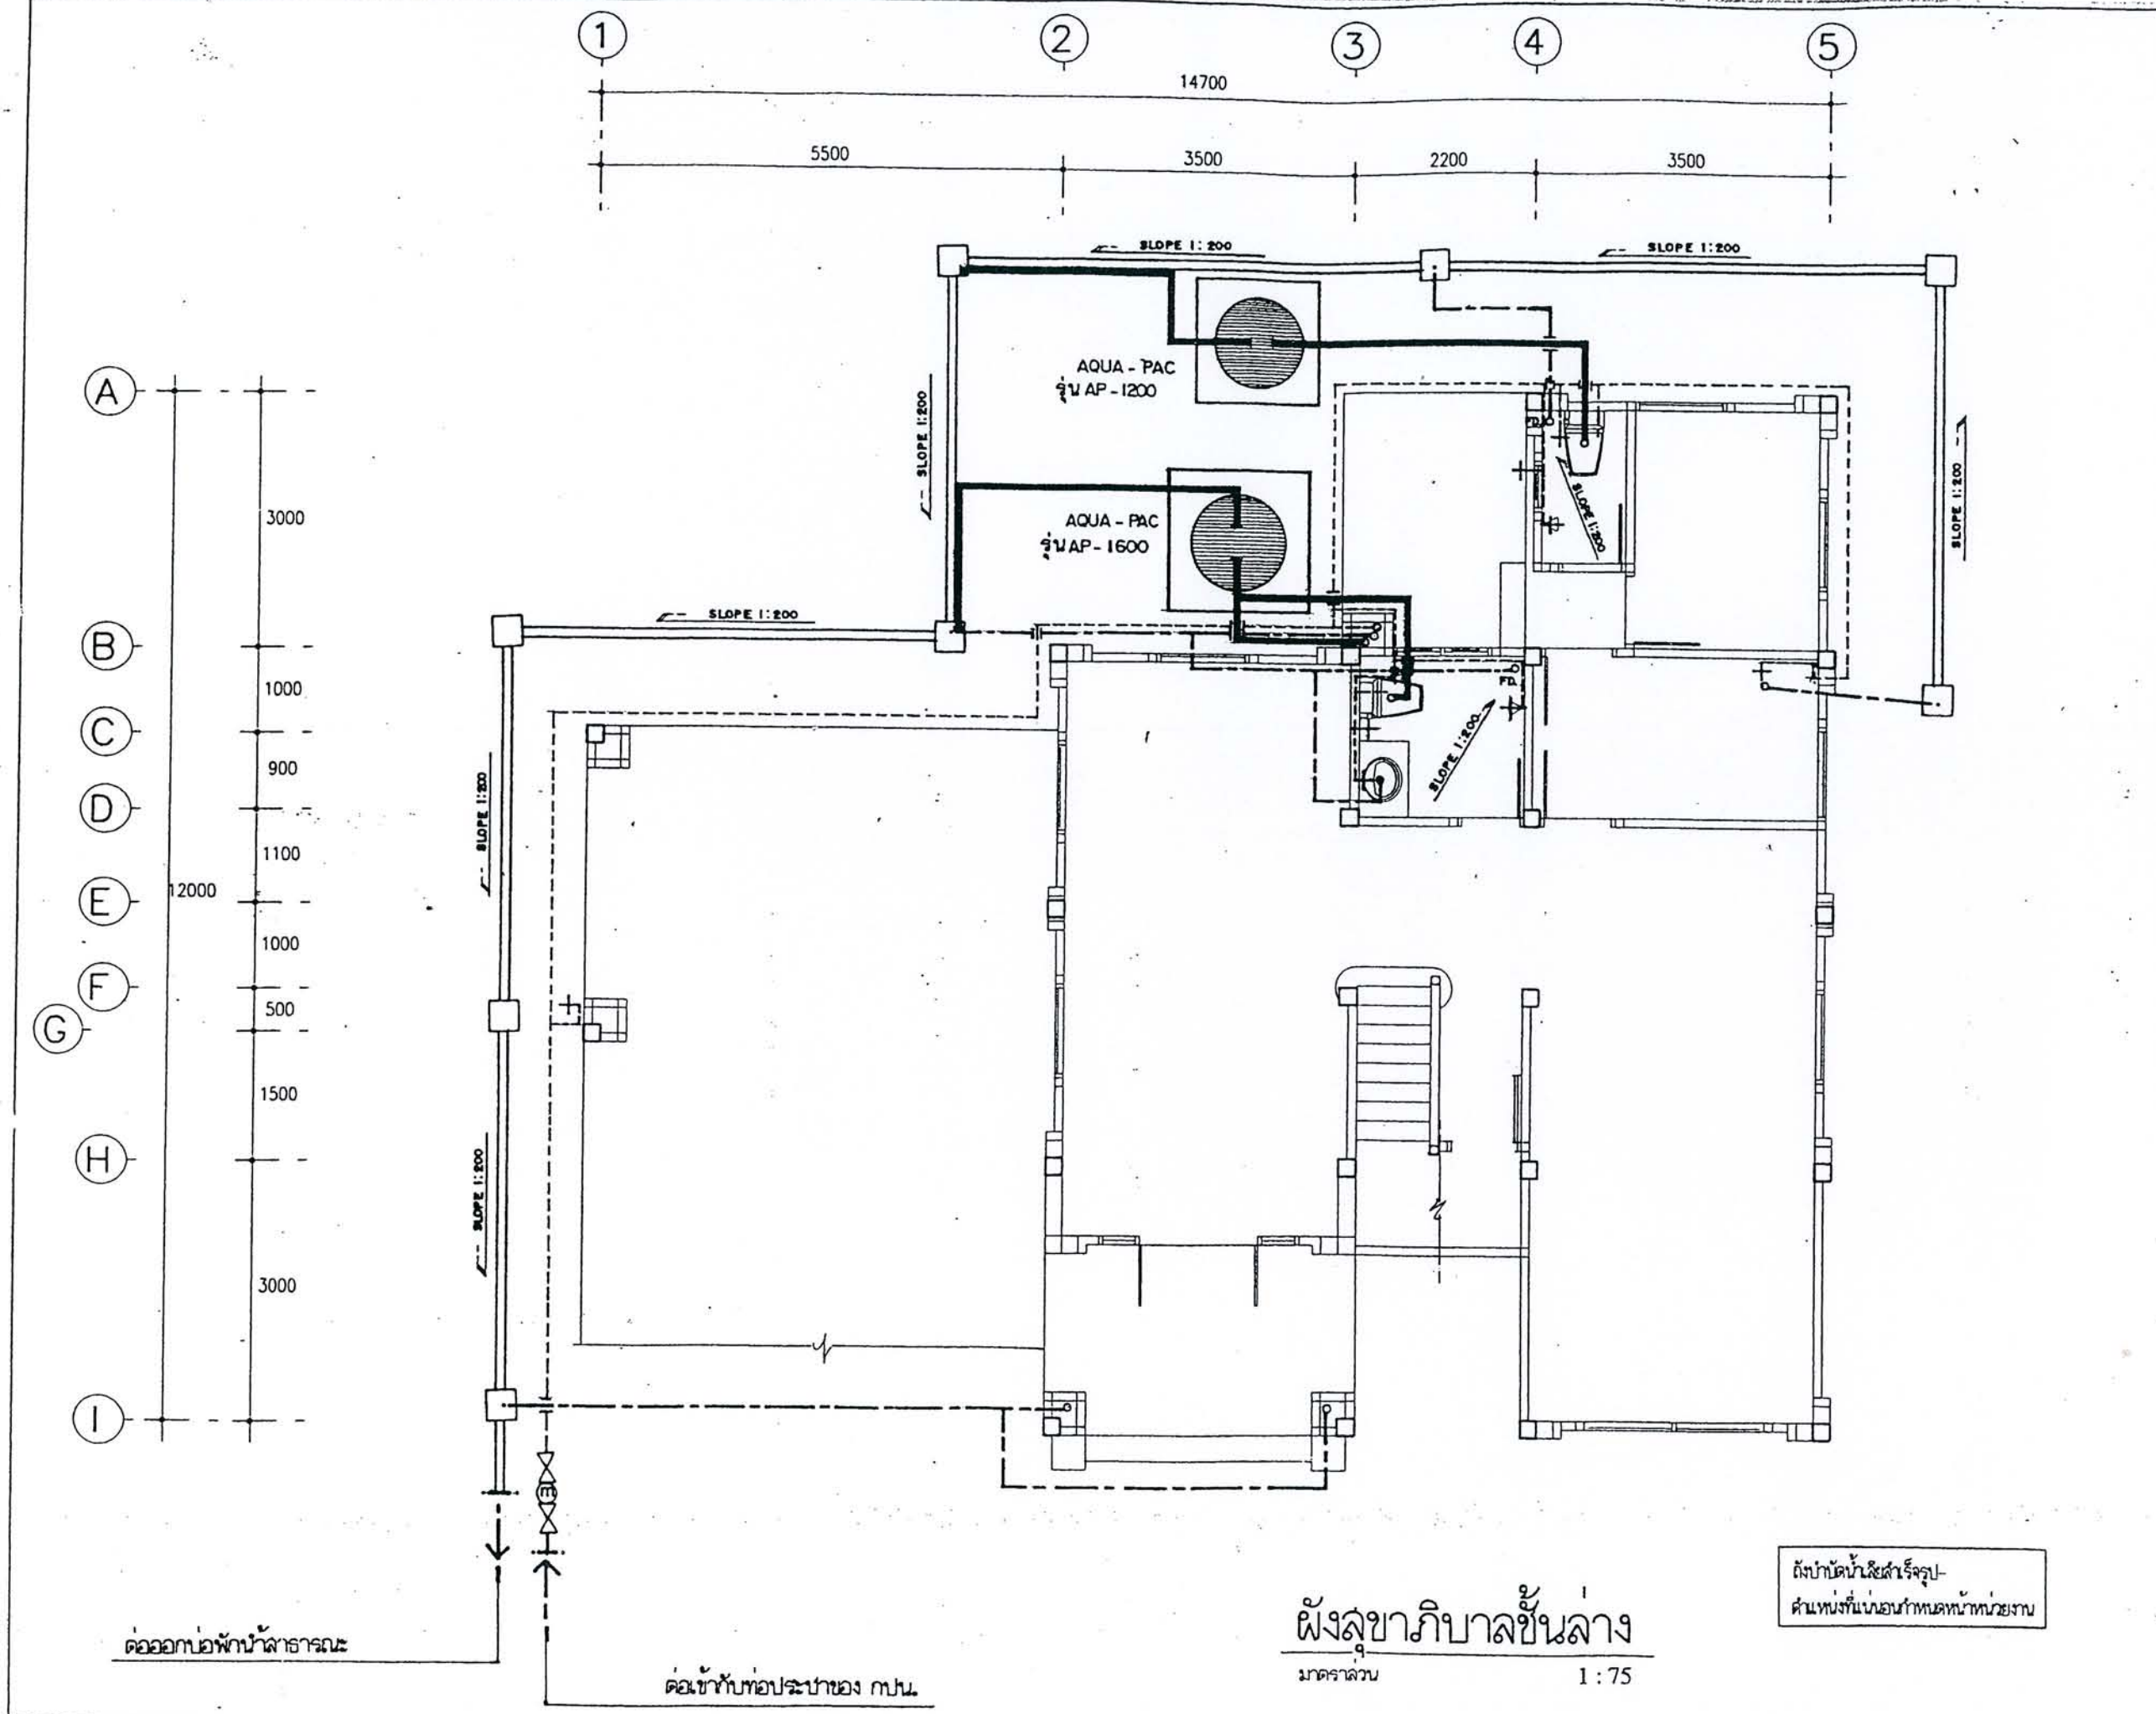

ต่อออกนอกพื้นที่สาธารณะ

ต่อเข้ากับท่อประปาของ กปน.

ผังสถาปัตยกรรมชั้นล่าง
มาตราส่วน 1 : 75

ถังบำบัดน้ำเสียรูป-
ผ่านทั้งที่แน่นอนกำหนดหน้าหน่วยงาน




โครงการ
แบบบ้านยืมเพื่อประชาชน

ตามนโยบาย
ม.ร.ว. สุขุมพันธุ์ บริพัตร
ผู้ว่าราชการกรุงเทพมหานคร

โดยสำนักงานโยธา
กรุงเทพมหานคร

ได้รับความอนุเคราะห์แบบ
จาก
บริษัท แลนด์ โสม
(ประเทศไทย) จำกัด

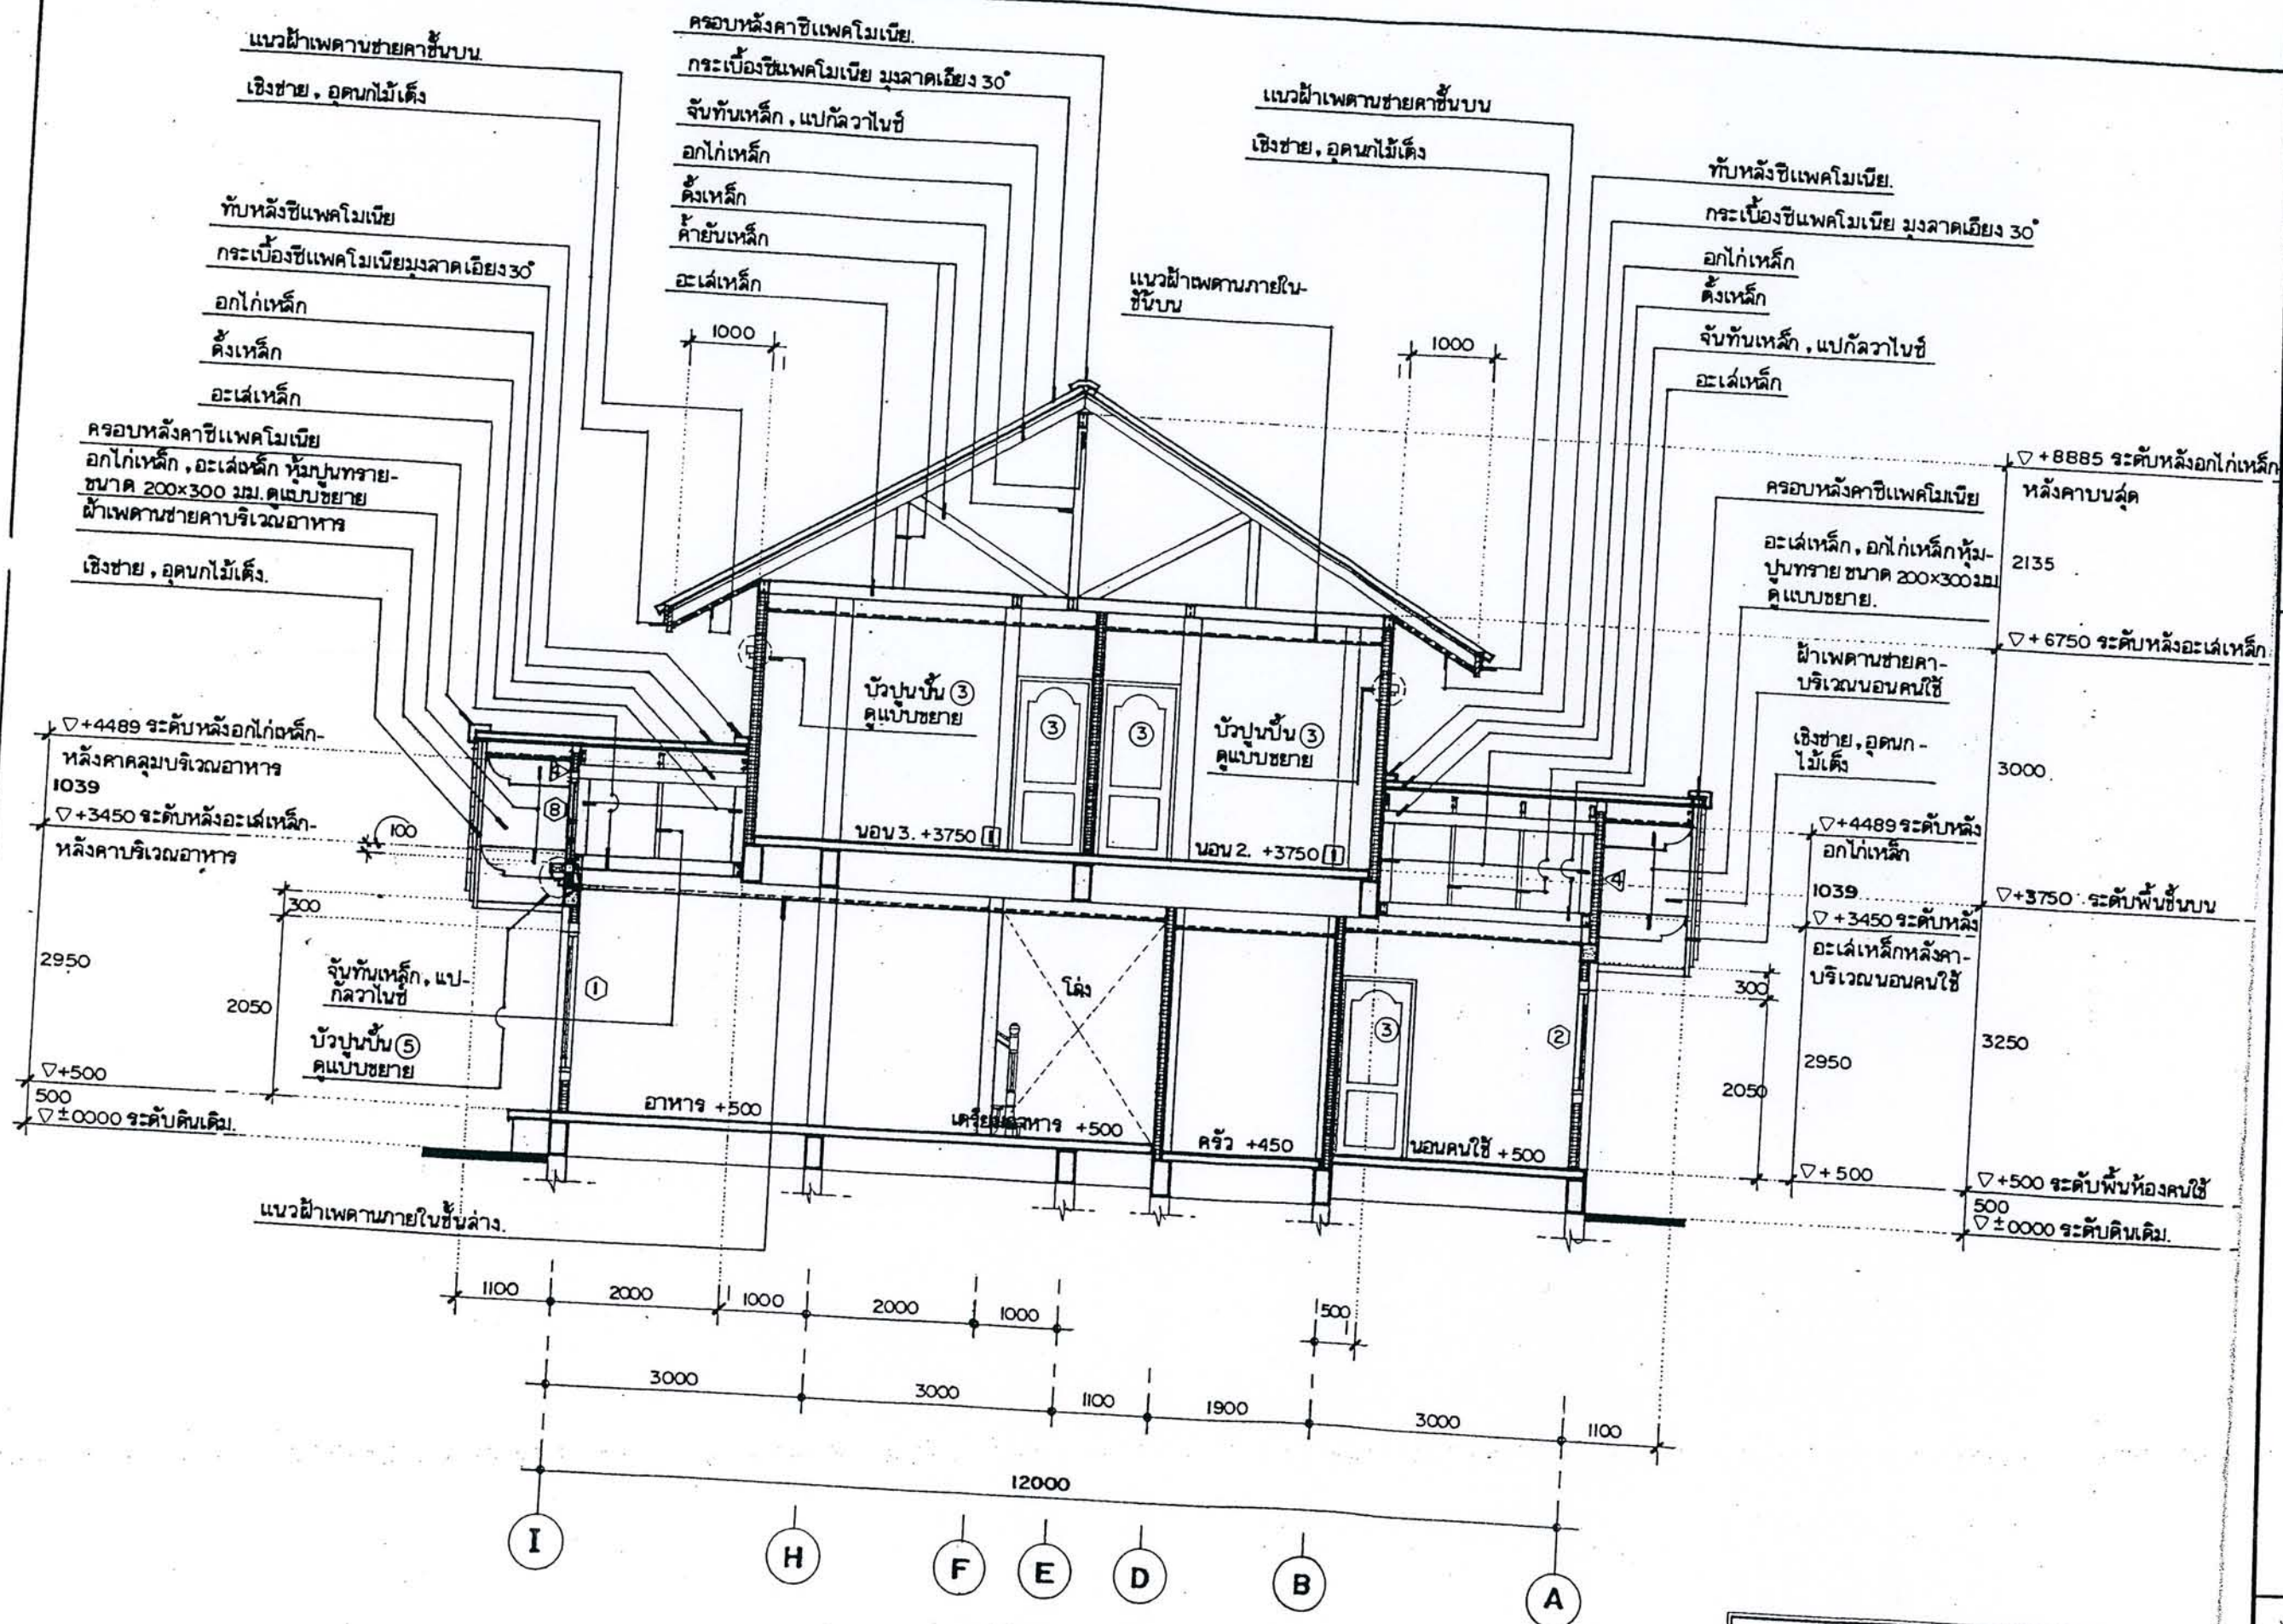

รูปตัด A-A

มาตราส่วน

1 : 75

อะไหล่เหล็ก, ช่อเหล็ก, คั้งเหล็ก, อกไก่เหล็ก, อะไหล่เหล็ก
ตะแกรงเหล็ก, จันทันเหล็ก, ค้ำยันเหล็ก, ระแนงเหล็ก,
เชิงชายไม้เต็ง, อดนกไม้เต็ง คูแบบขยายวิศวกรรม




โครงการ
แบบบ้านยืมเพื่อประชาชน

ตามนโยบาย
ม.ร.ว. สุขุมพันธุ์ บริพัตร
ผู้ว่าราชการกรุงเทพมหานคร


โดยสำนักงานโยธา
กรุงเทพมหานคร

ได้รับความอนุเคราะห์แบบ
จาก
บริษัท แลนด์ โสม
(ประเทศไทย) จำกัด

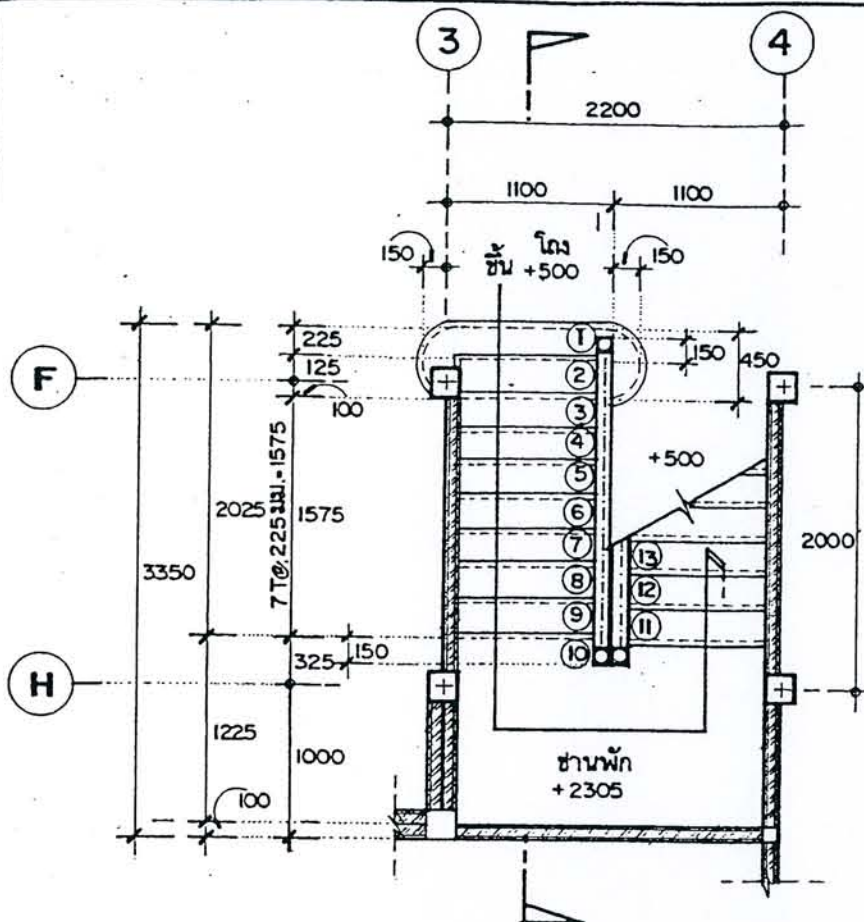


แปลนขยายบันไดชั้นล่าง

มาตราส่วน 1 : 50

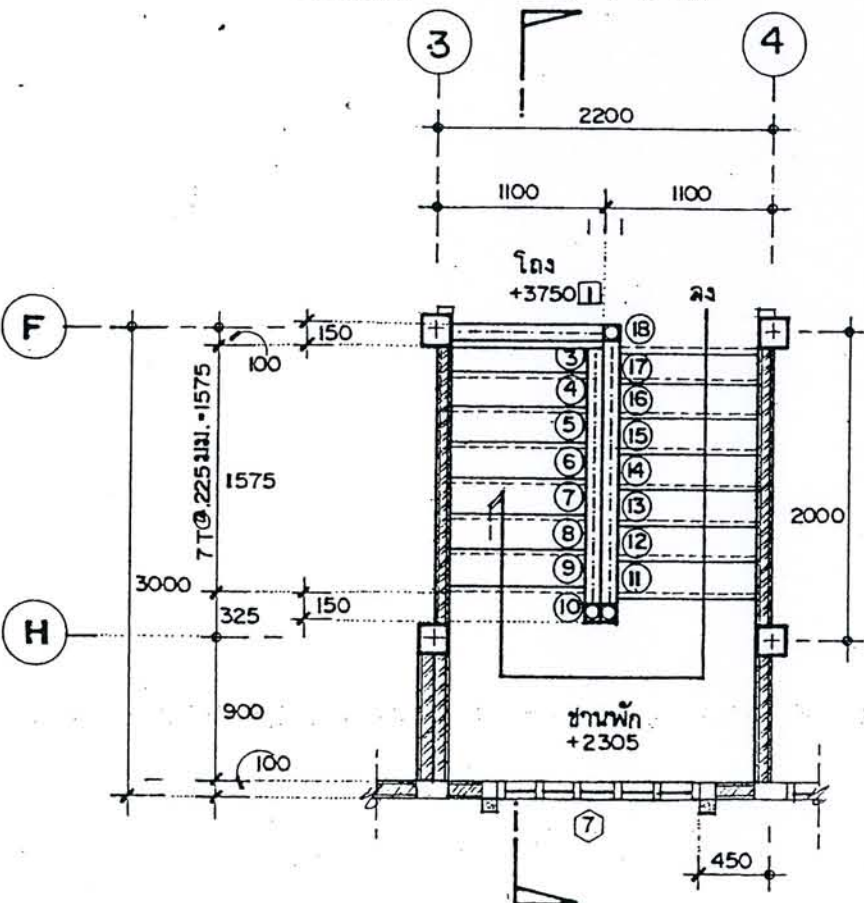

แปลนขยายบันไดชั้นบน

มาตราส่วน 1 : 50

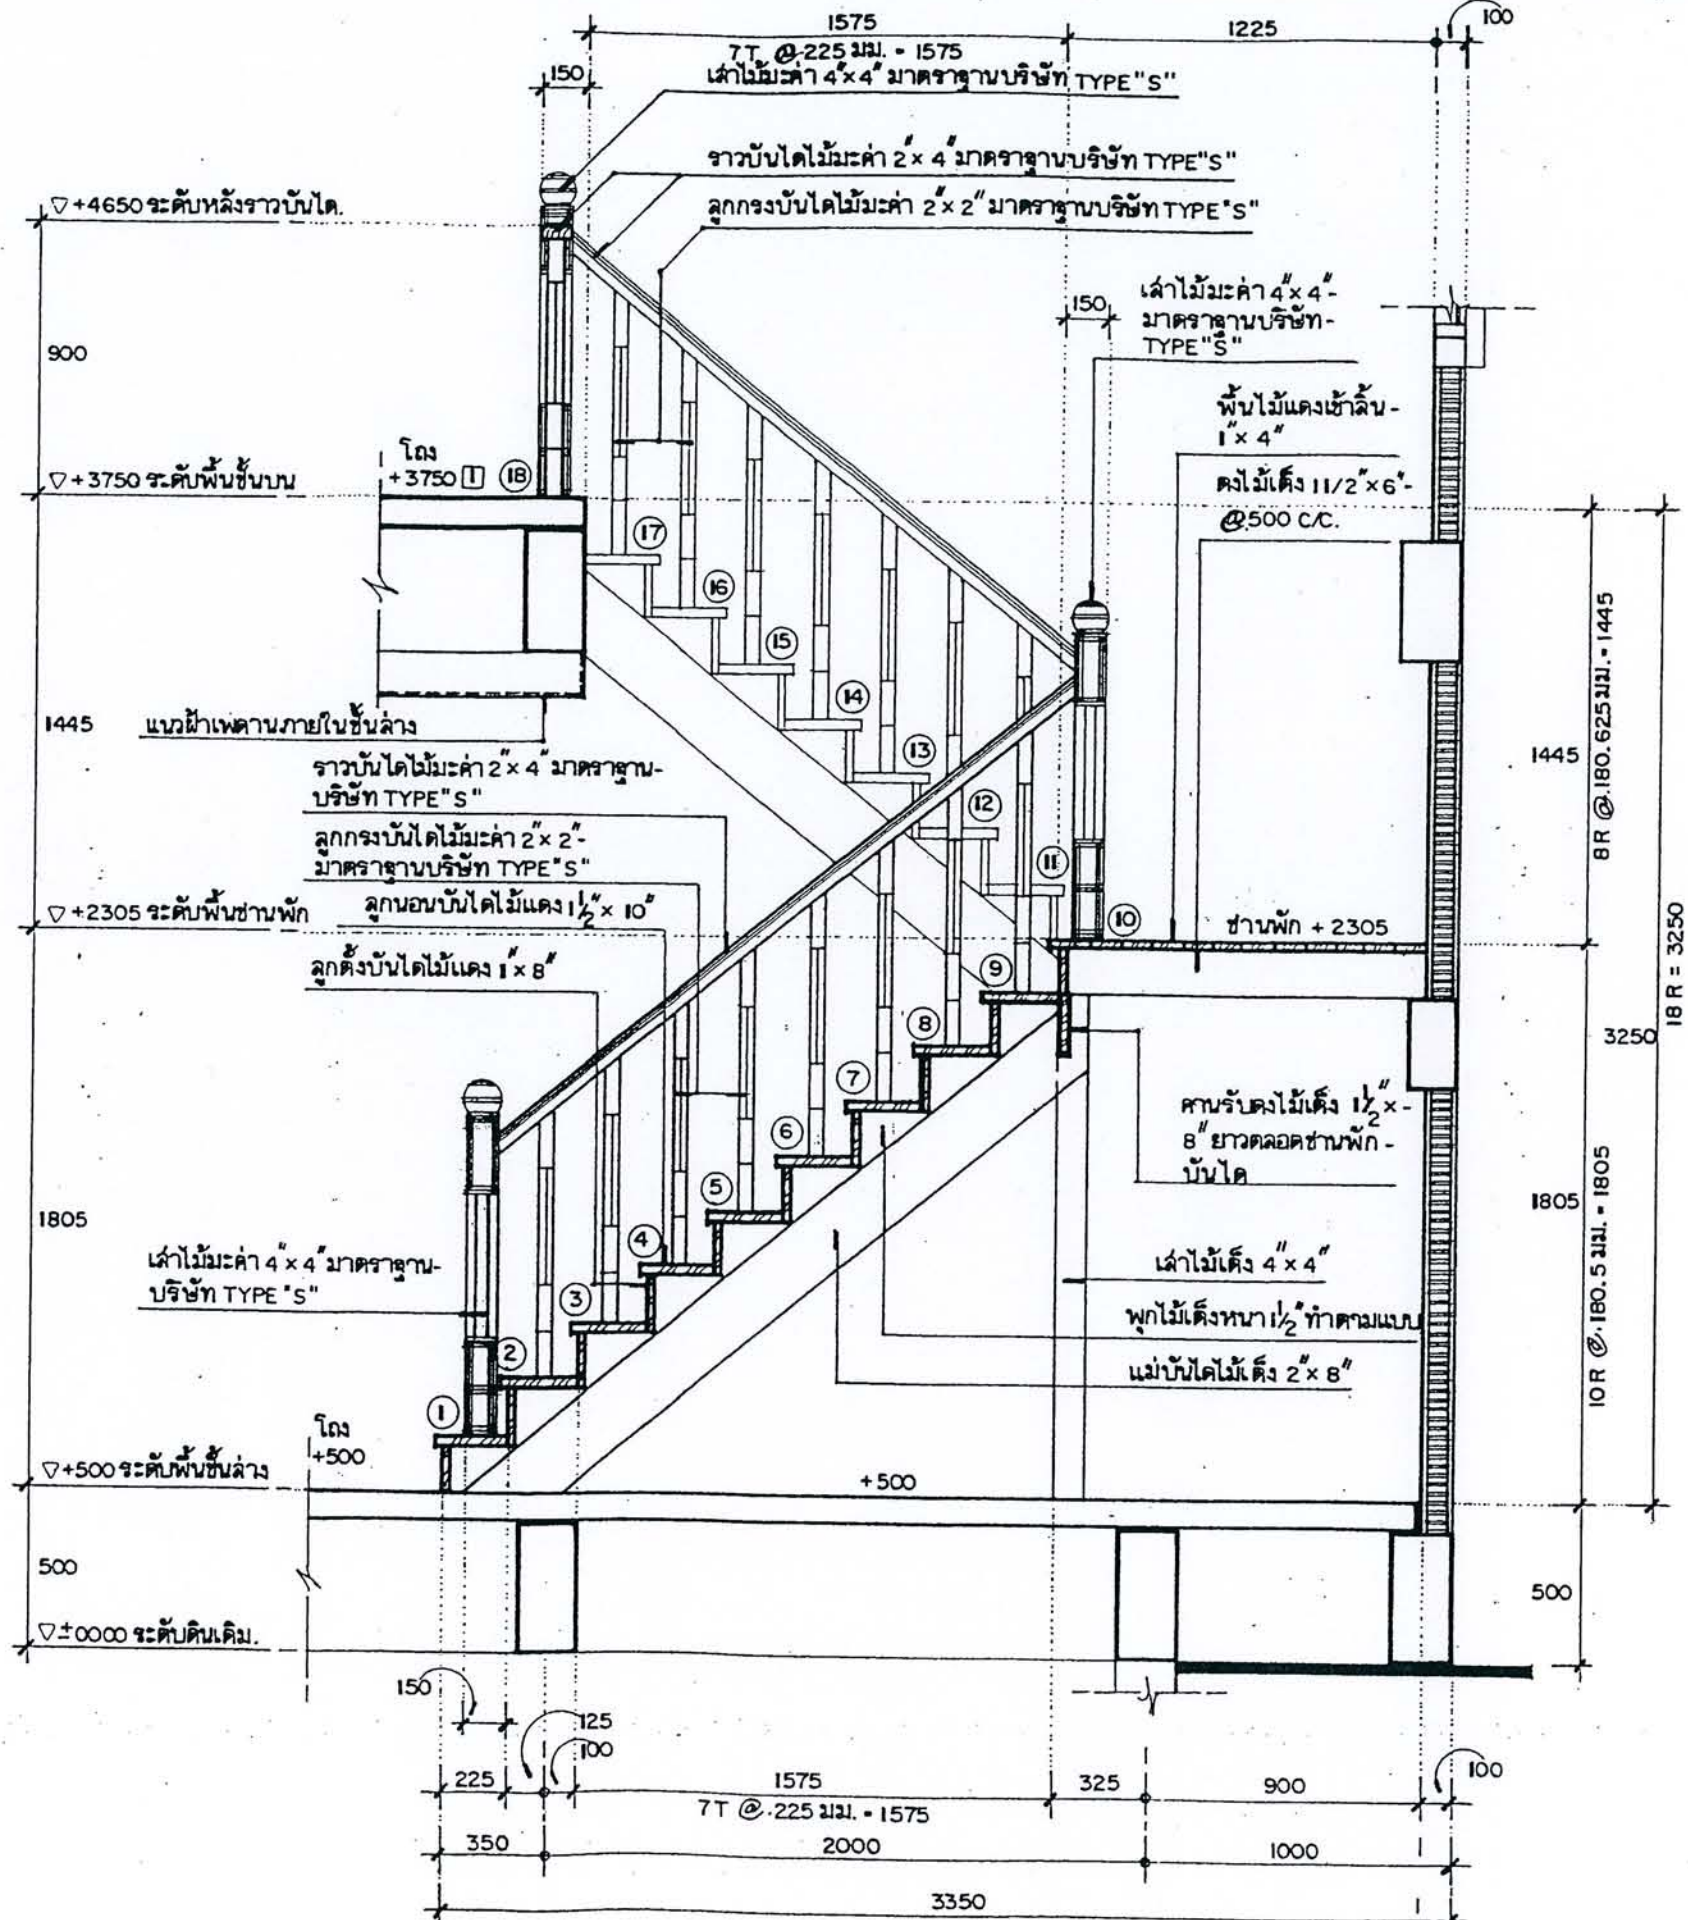

รูปตัดขยายบันได

มาตราส่วน 1 : 25



โดยสำนักการโยธา
กรุงเทพมหานคร



มาตราล่วน

1 : 50

ได้รับความอนุเคราะห์แบบ
จาก
บริษัท แลนด์ โสม
(ประเทศไทย) จำกัด




โครงการ
แบบบ้านยืมเพื่อประชาชน

ตามนโยบาย
ม.ร.ว. สุขุมพันธุ์ บริพัตร
ผู้ว่าราชการกรุงเทพมหานคร

โดยสำนักงานโยธา
กรุงเทพมหานคร

ได้รับความอนุเคราะห์แบบ
จาก
บริษัท แลนด์ โสม
(ประเทศไทย) จำกัด

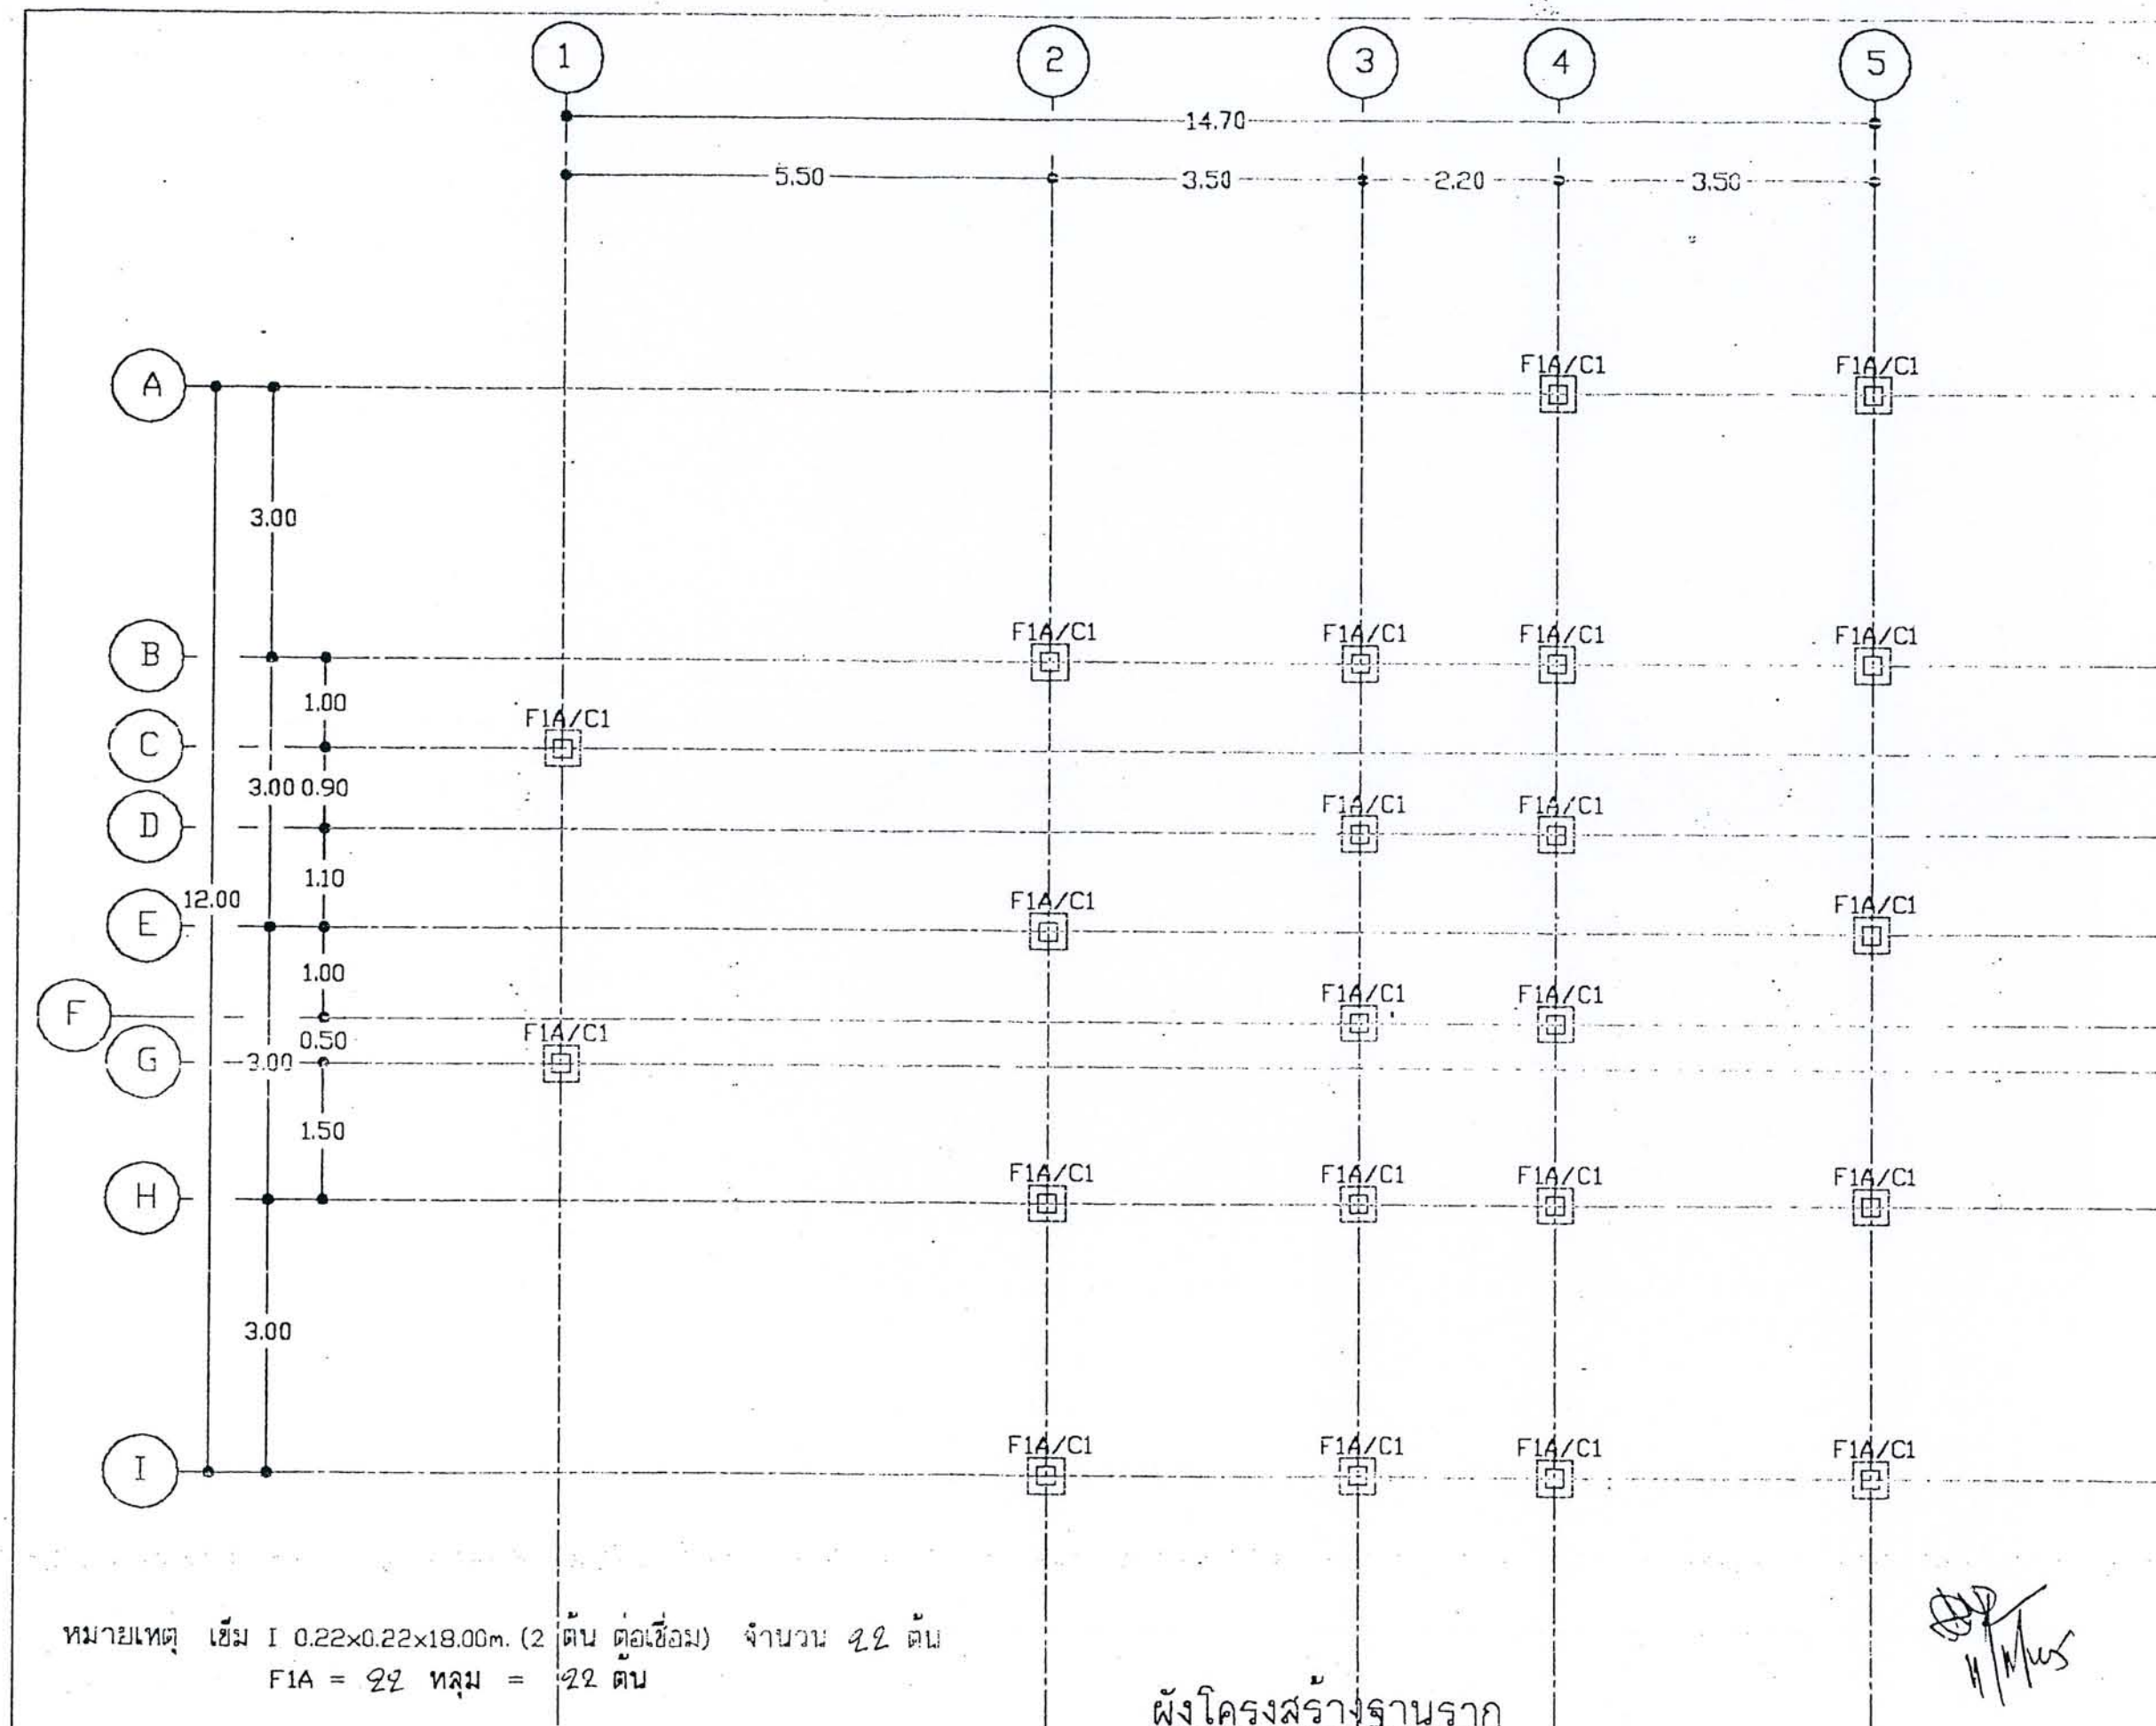

Handwritten signature and date: 11/11/55


ผังโครงสร้างฐานราก
มาตราส่วน 1:75



โครงการ
แบบบ้านยืมเพื่อประชาชน

ตามนโยบาย
ม.ร.ว. สุขุมพันธุ์ บริพัตร
ผู้ว่าราชการกรุงเทพมหานคร

โดยสำนักการโยธา
กรุงเทพมหานคร

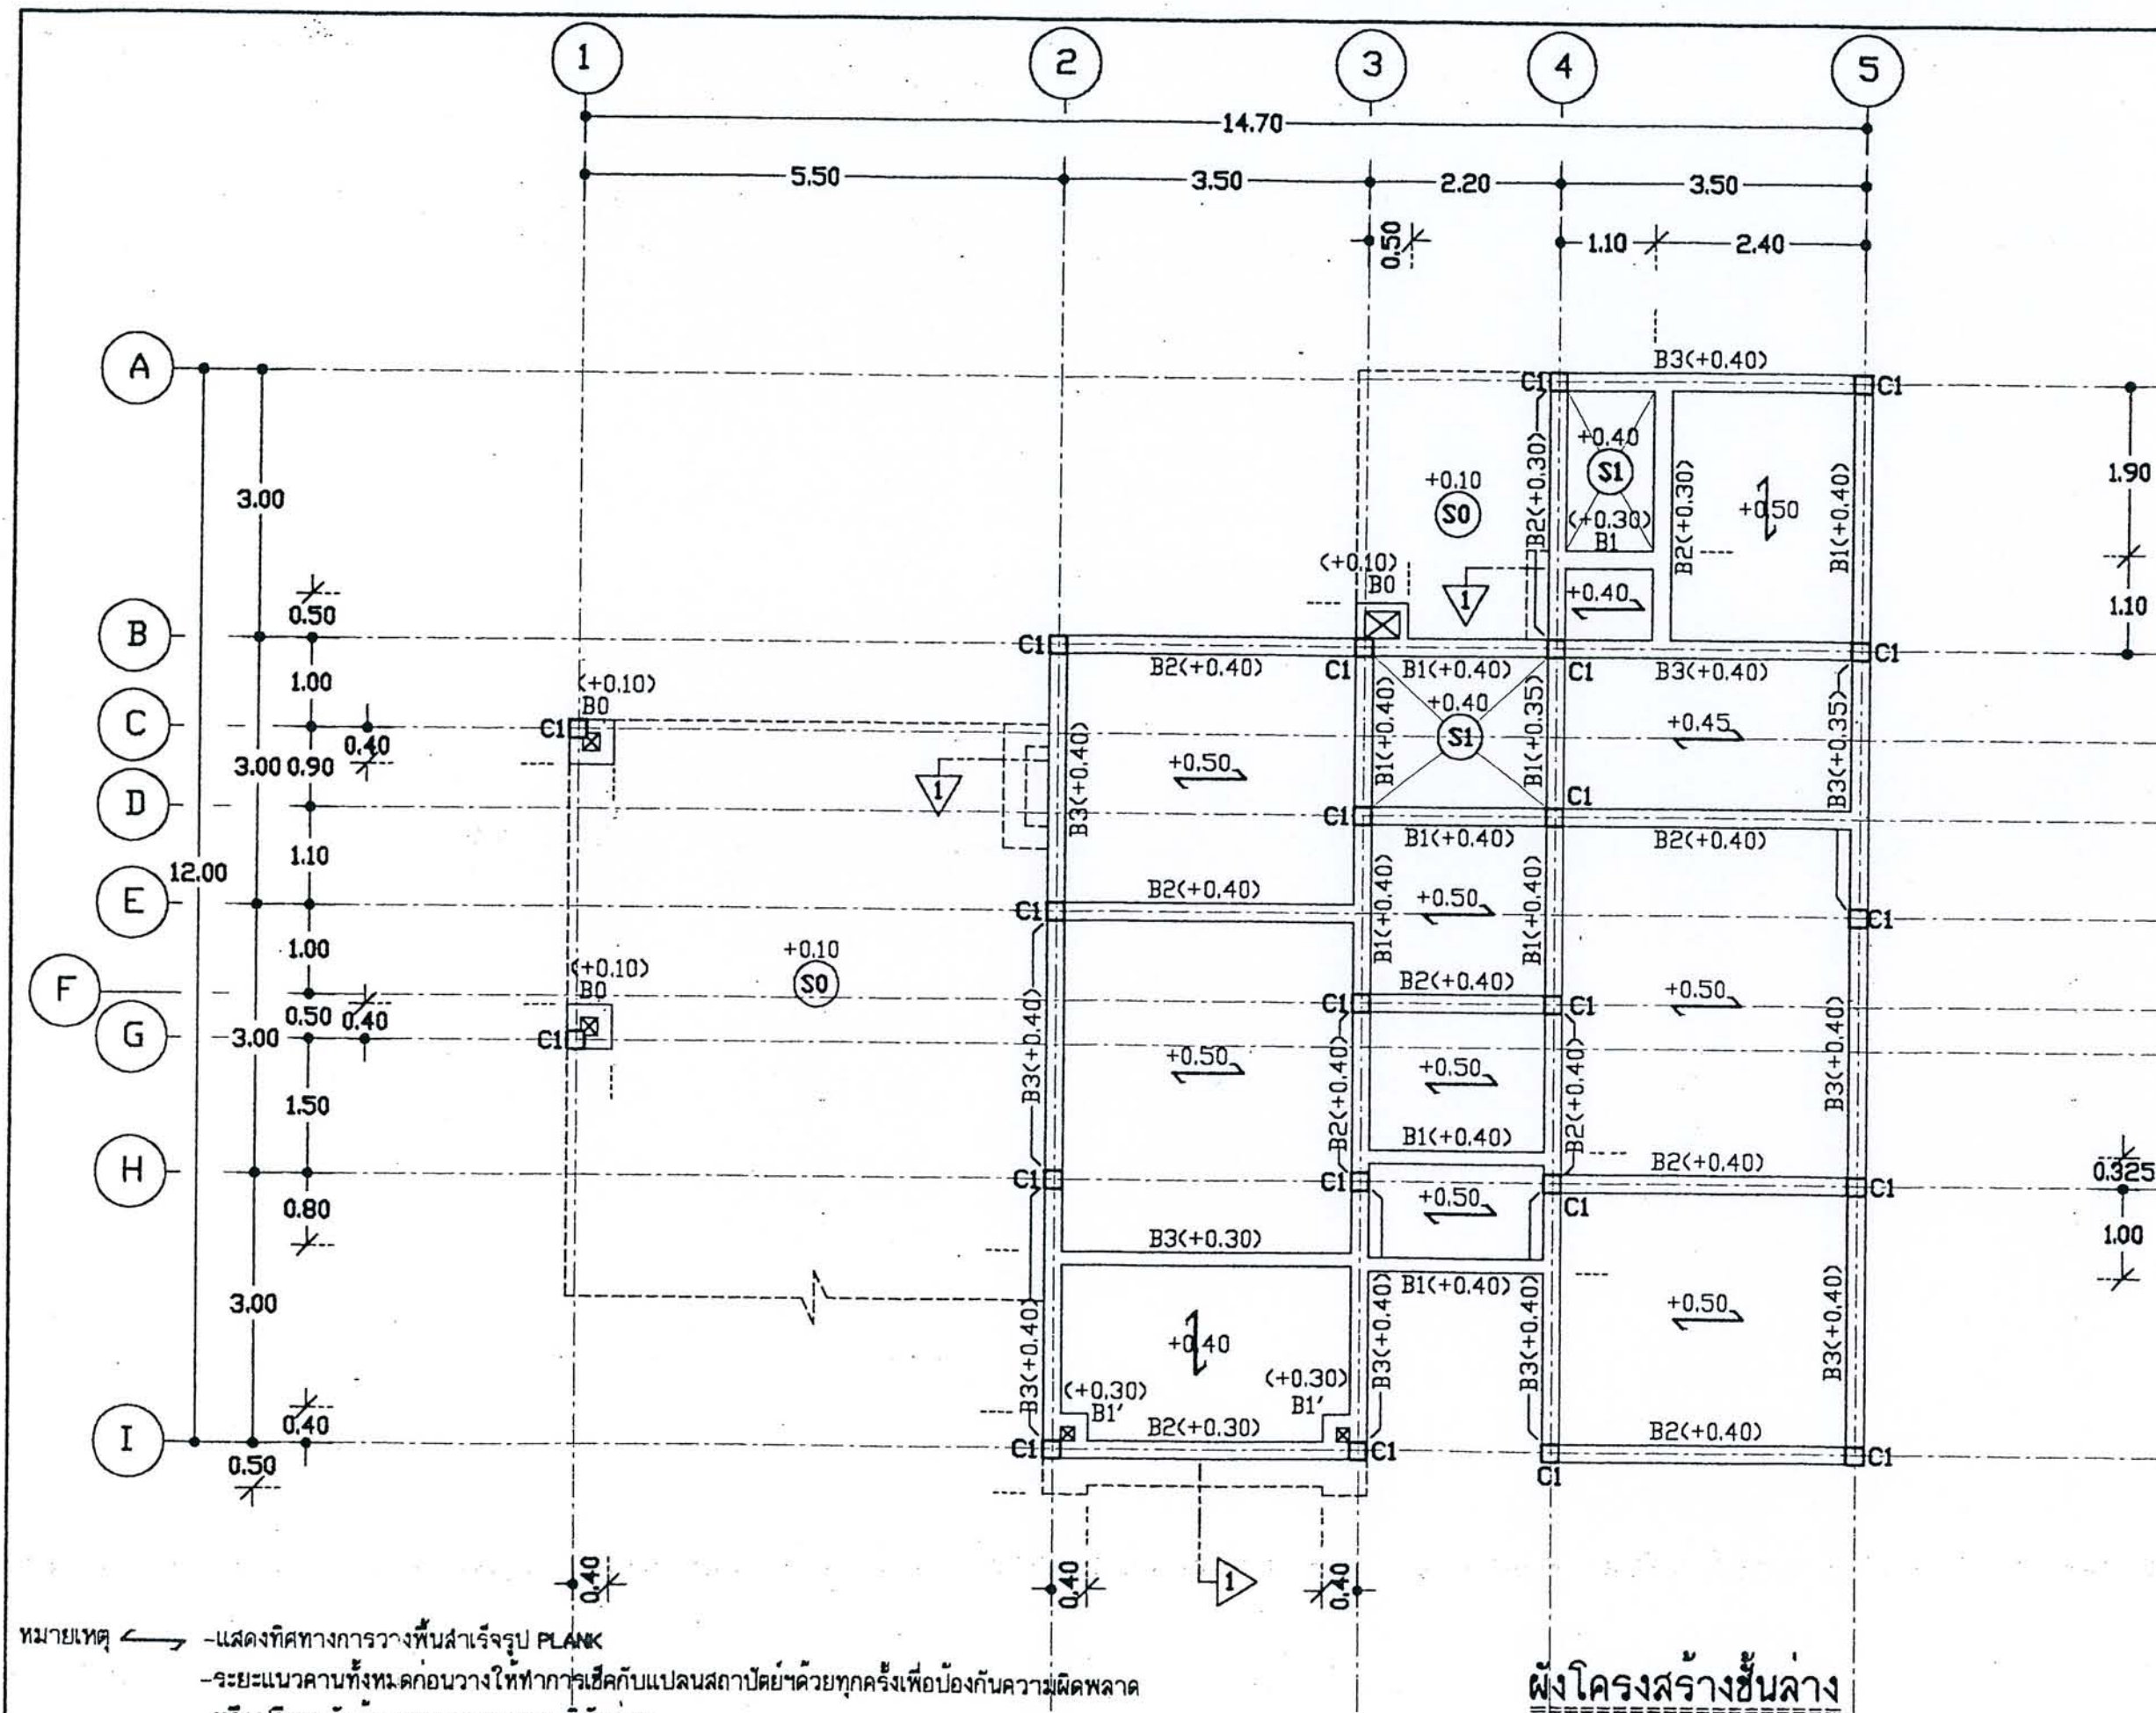

หมายเหตุ ← -แสดงทิศทางการวางพื้นสำเร็จรูป PLANK
-ระยะแนวคานทั้งหมดก่อนวางให้ทำการเช็คกับแปลนสถาปัตย์ด้วยทุกครั้งเพื่อป้องกันความผิดพลาด
หรือปรึกษากับผู้ควบคุมงานของทางบริษัทก่อน
-ผังสลีปที่ต่อตามผังสุขาภิบาลด้วย

ผังโครงสร้างชั้นล่าง
มาตราส่วน 1:75

ได้รับความอนุเคราะห์แบบ
จาก
บริษัท แลนด์ ไชย
(ประเทศไทย) จำกัด




โครงการ
แบบบ้านยืมเพื่อประชาชน

ตามนโยบาย
ม.ร.ว. สุขุมพันธุ์ บริพัตร
ผู้ว่าราชการกรุงเทพมหานคร

โดยสำนักงานโยธา
กรุงเทพมหานคร

ได้รับความอนุเคราะห์แบบ
จาก
บริษัท แลนด์ โยม
(ประเทศไทย) จำกัด

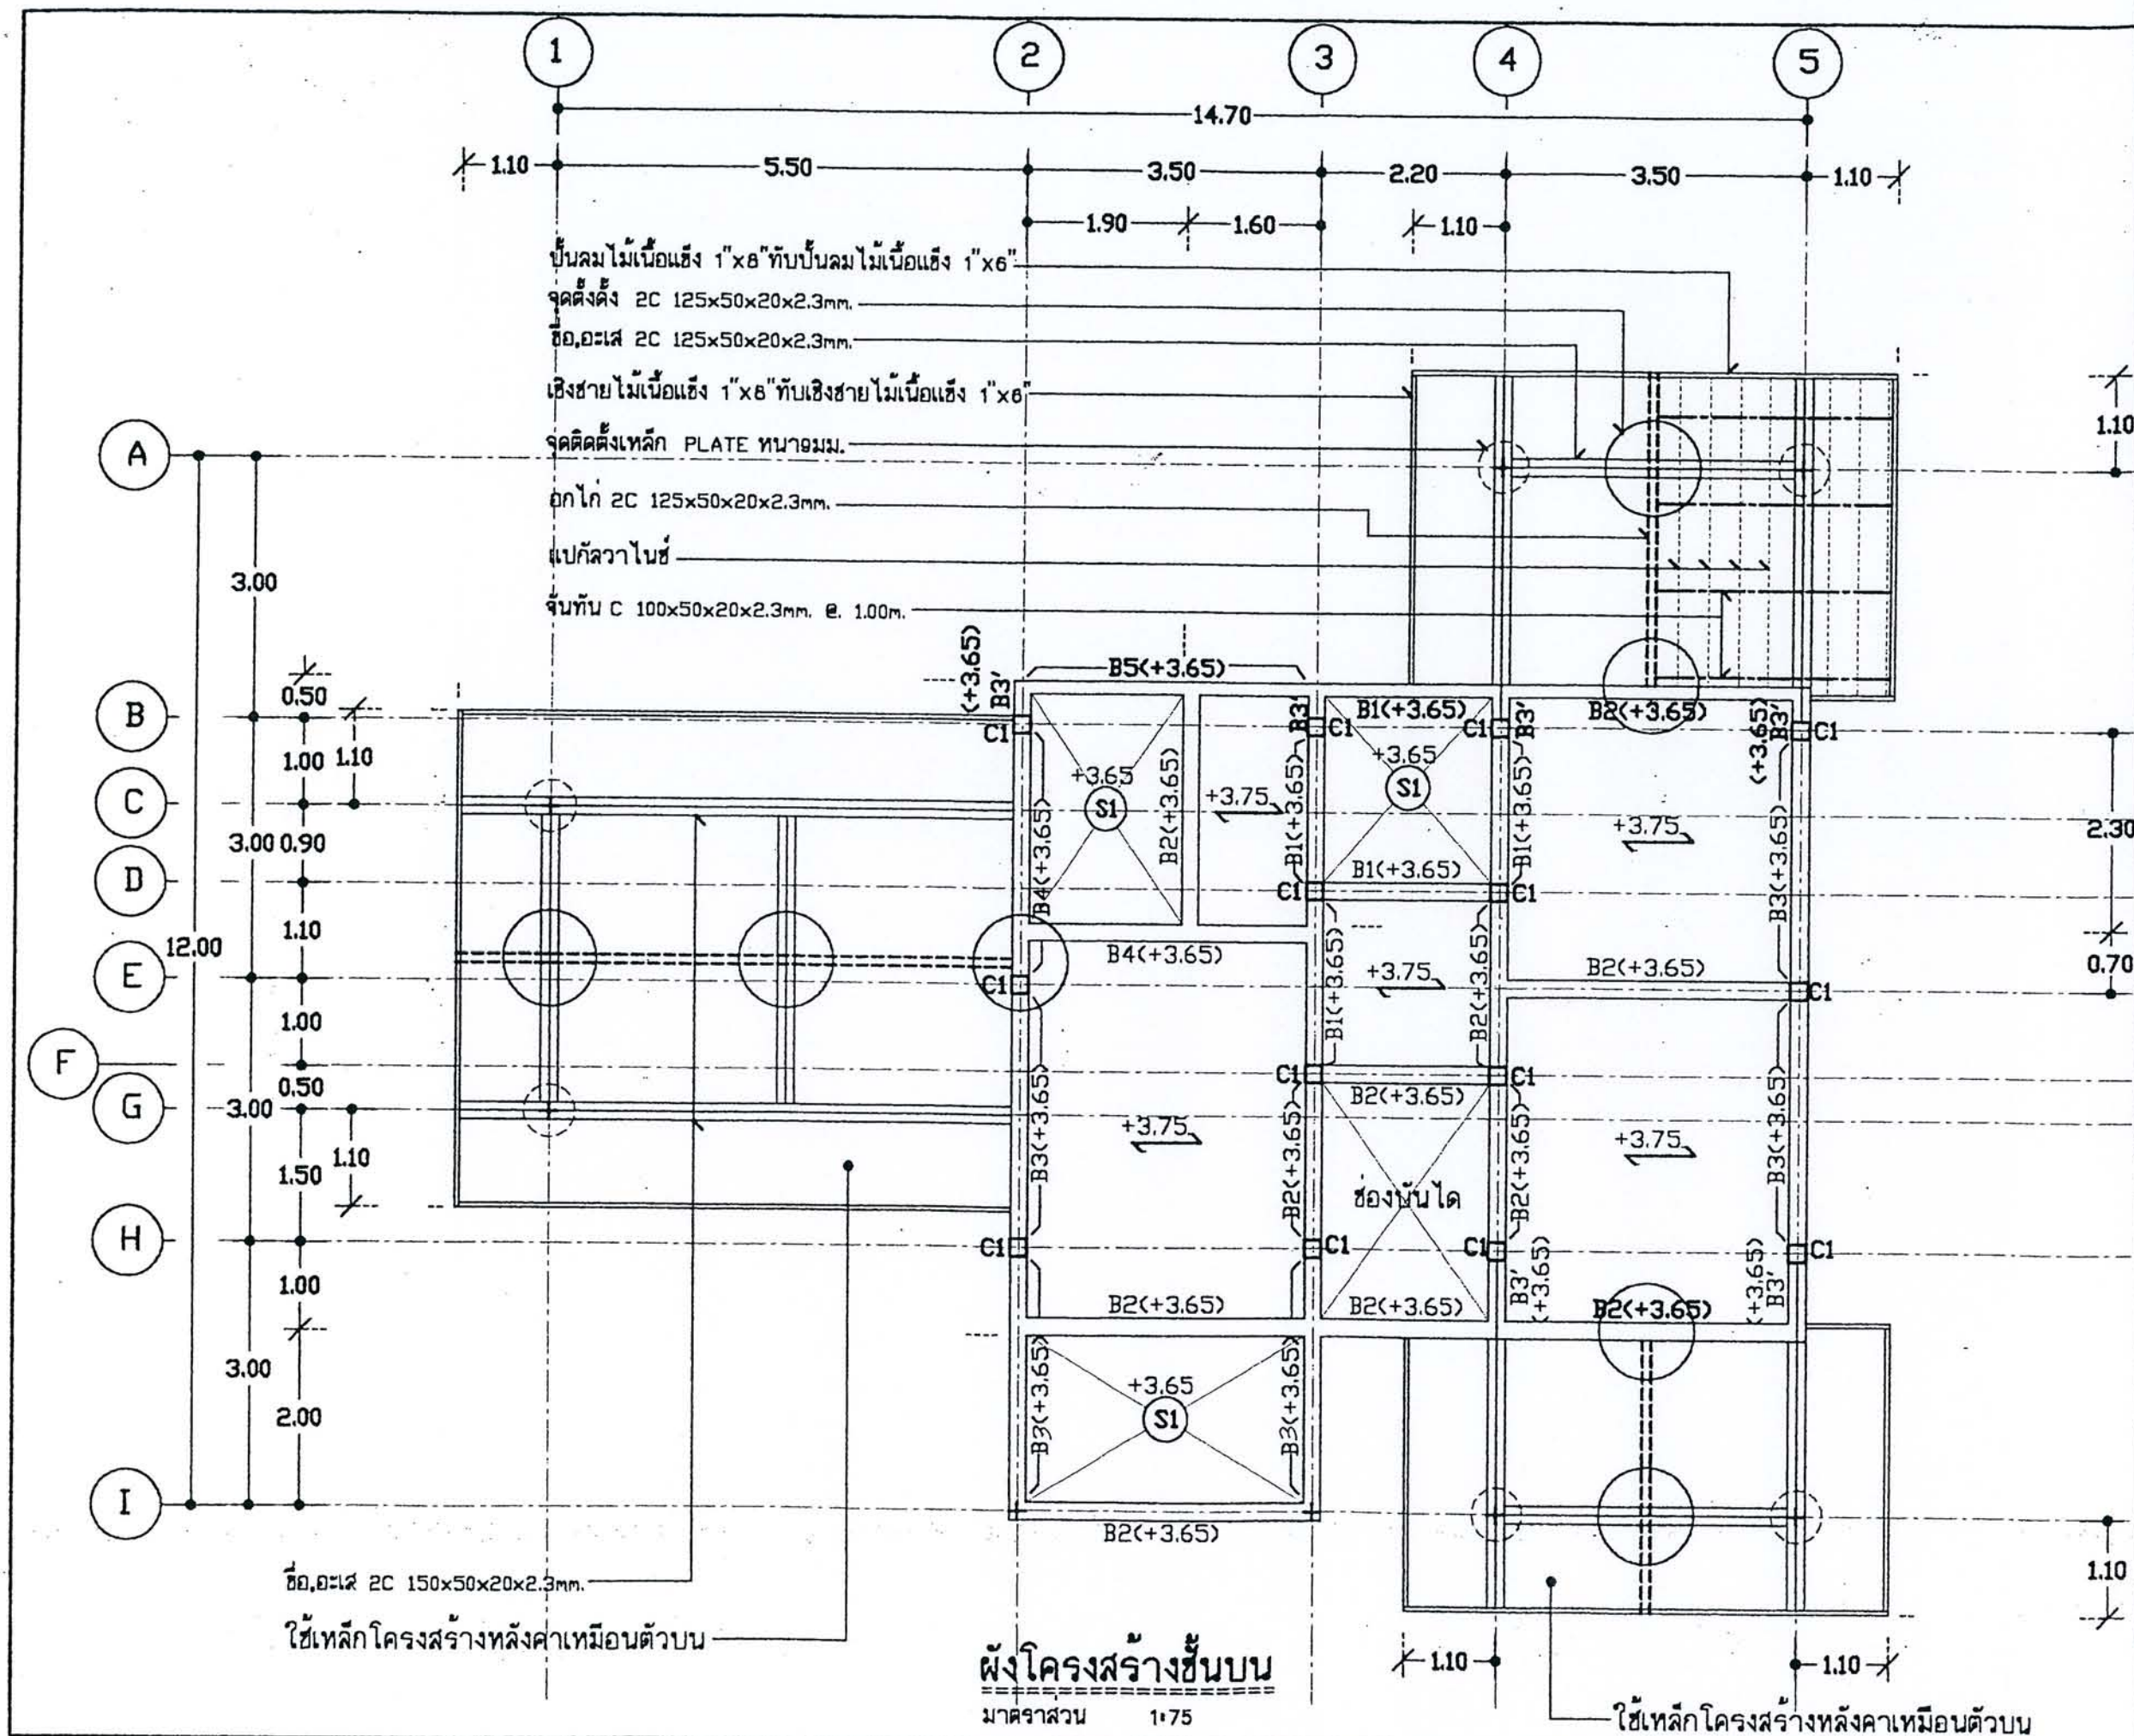




โครงการ
แบบบ้านยืมเพื่อประชาชน

ตามนโยบาย
ม.ร.ว. สุขุมพันธุ์ บริพัตร
ผู้ว่าราชการกรุงเทพมหานคร

โดยสำนักการโยธา
กรุงเทพมหานคร

ได้รับความอนุเคราะห์แบบ
จาก
บริษัท แลนด์ โฮม
(ประเทศไทย) จำกัด



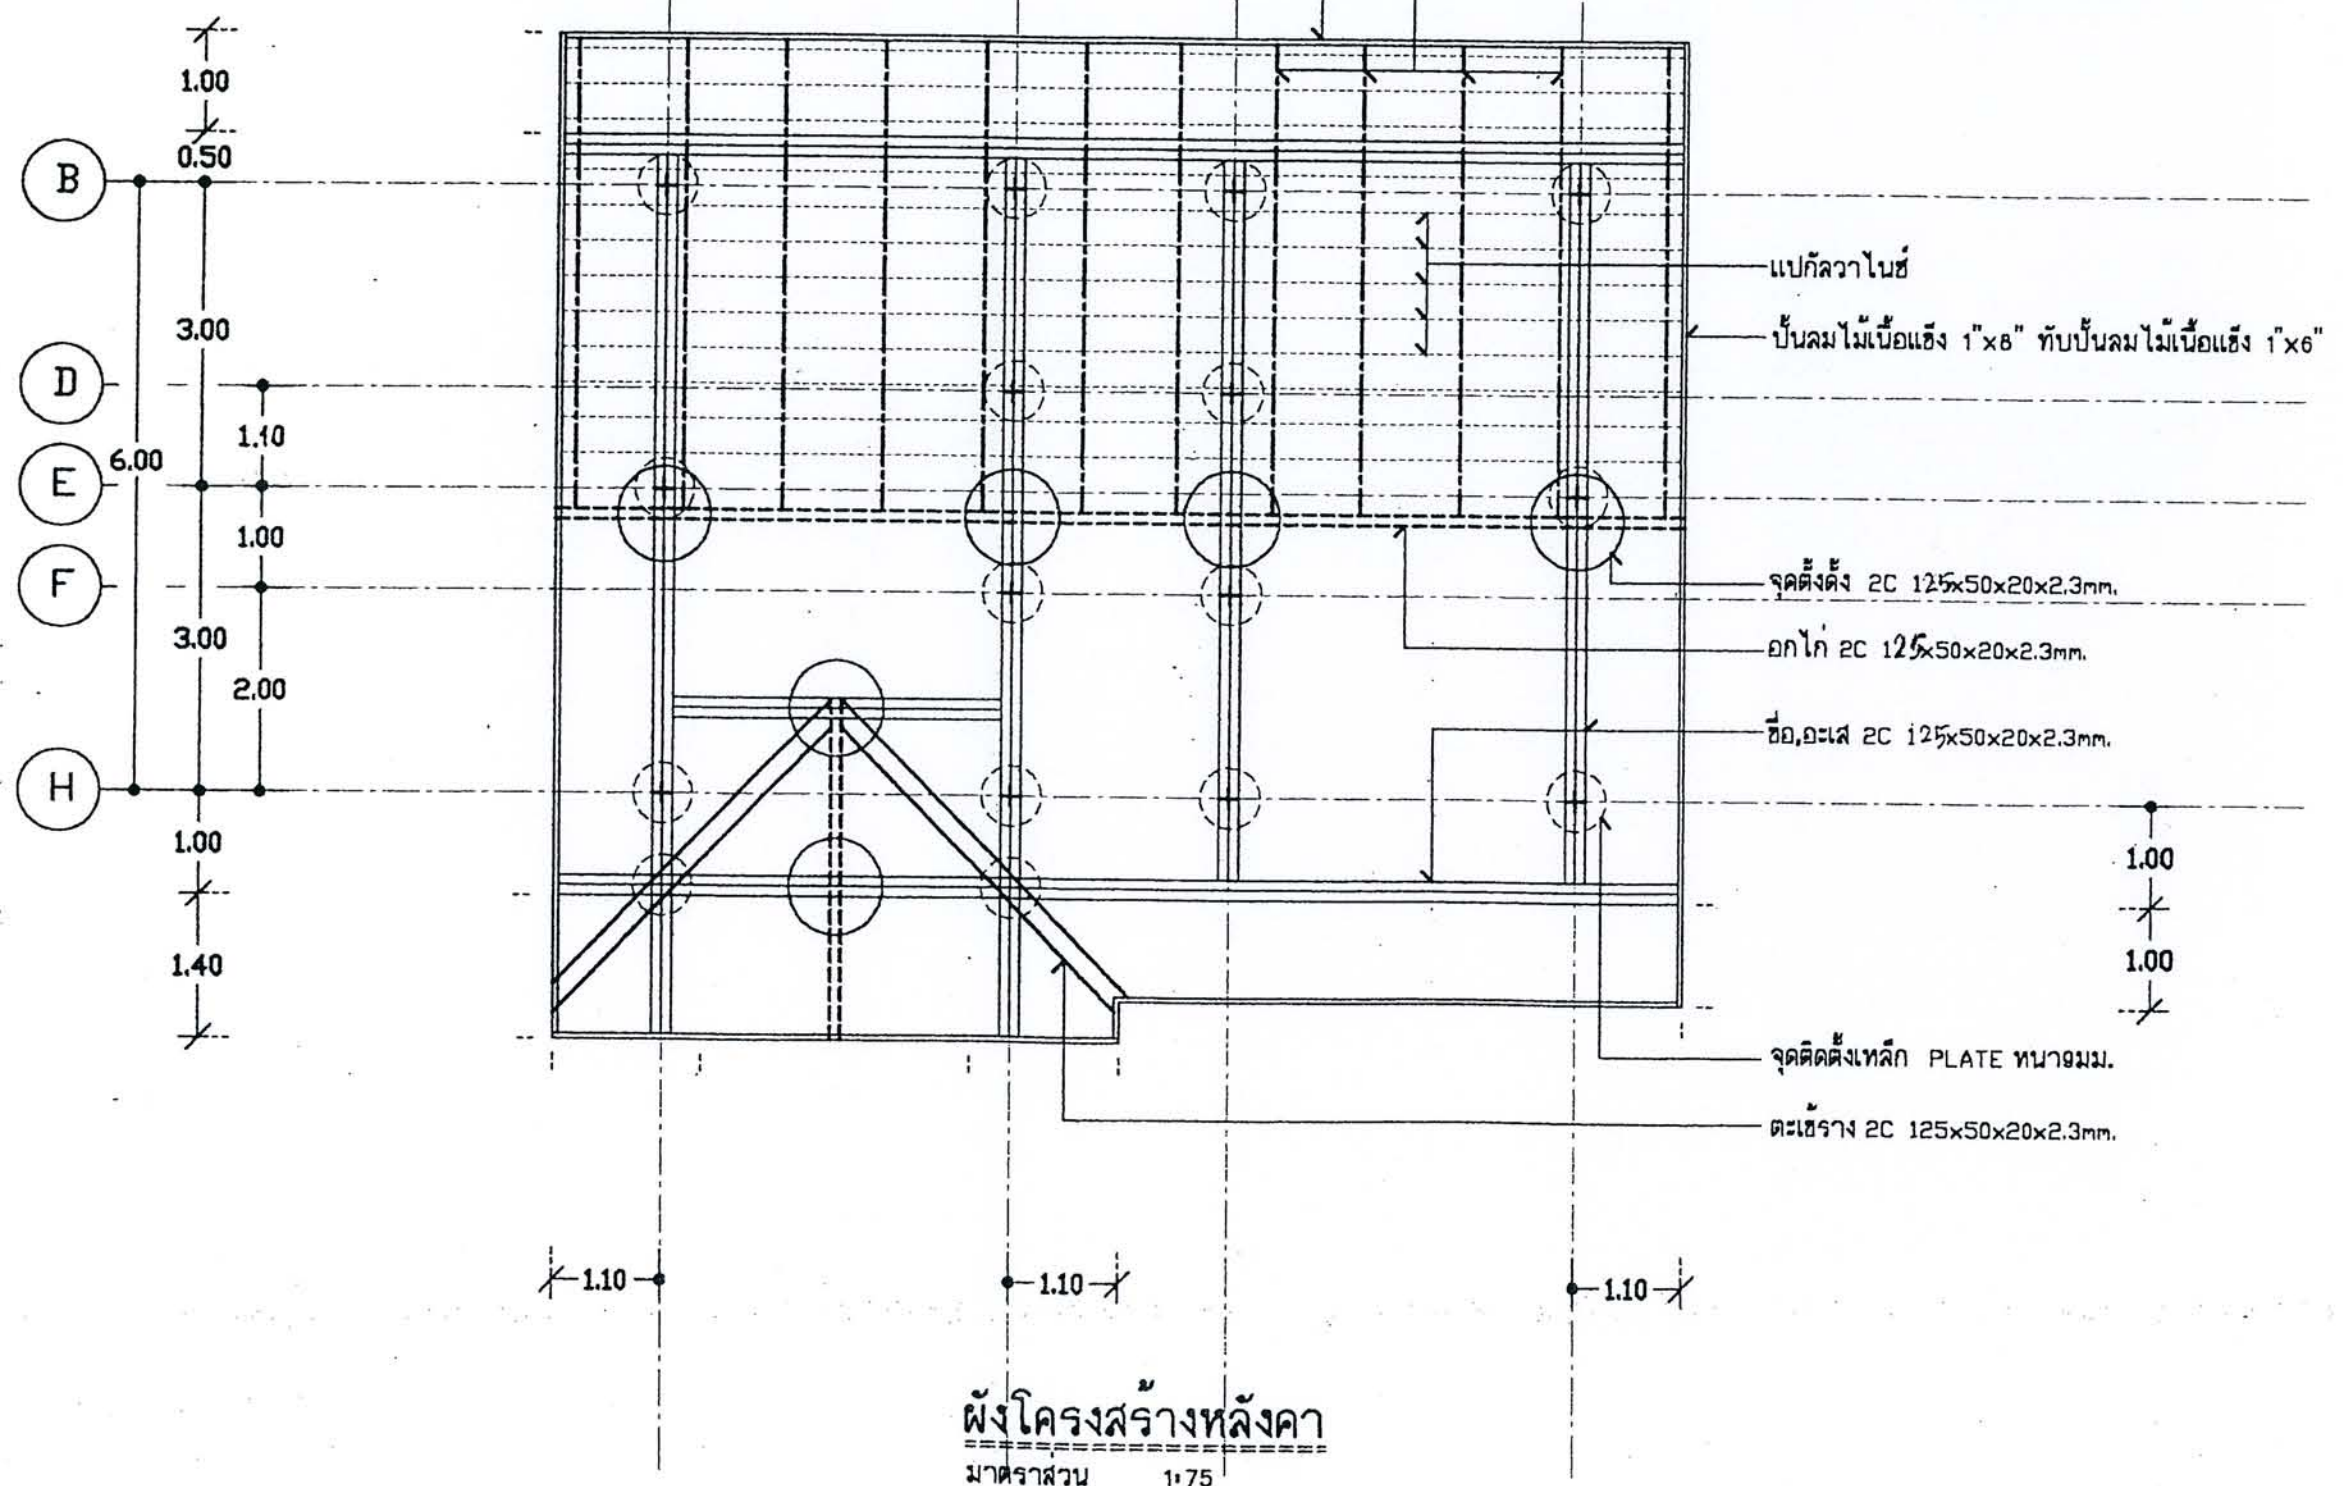





โครงการ
แบบบ้านยืมเพื่อประชาชน

ตามนโยบาย
ม.ร.ว. สุขุมพันธุ์ บริพัตร
ผู้ว่าราชการกรุงเทพมหานคร


โดยสำนักงานโยธา
กรุงเทพมหานคร

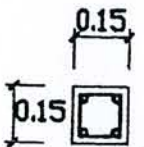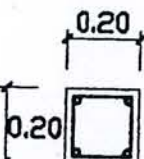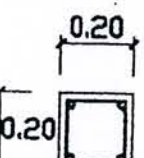FLOOR 2	 0.15 0.15 4-DB12 1 RB6@0.15
FLOOR 1	 0.20 0.20 4-DB12 1 RB6@0.15
FOOTING	 0.20 0.20 4-DB12 1 RB6@0.15
	C1

SECTION COLUMN 1:20

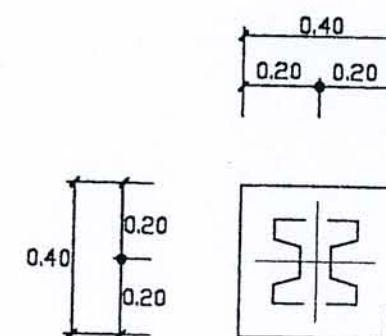

PLAN F1A

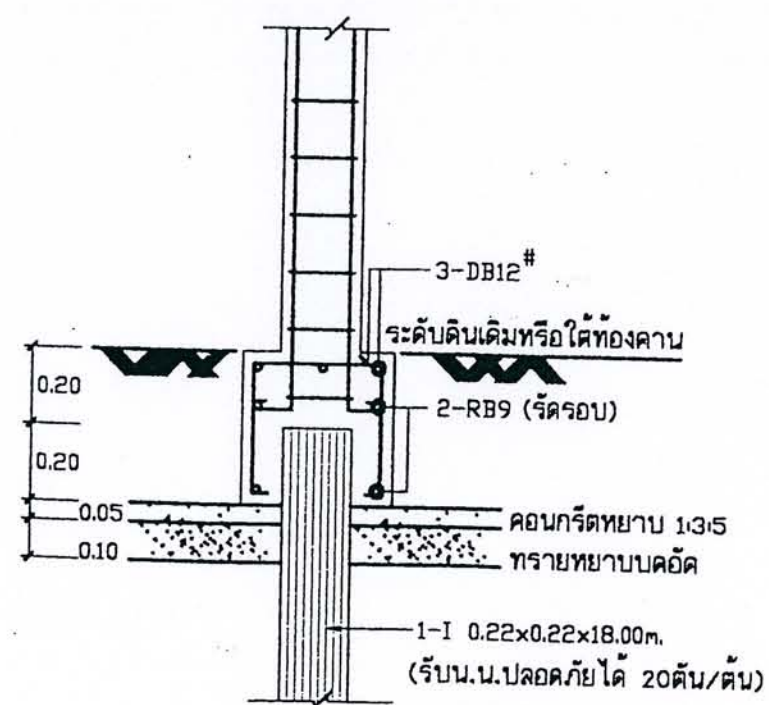

SECTION F1A 1:20

ได้รับความอนุเคราะห์แบบ
จาก
บริษัท แลนด์ โฮม
(ประเทศไทย) จำกัด




โครงการ
แบบบ้านยืมเพื่อประชาชน


ตามนโยบาย
ม.ร.ว. สุขุมพันธุ์ บริพัตร
ผู้ว่าราชการกรุงเทพมหานคร

โดยสำนักงานโยธา
กรุงเทพมหานคร

ได้รับความอนุเคราะห์แบบ
จาก
บริษัท แลนด์ ไบ
(ประเทศไทย) จำกัด

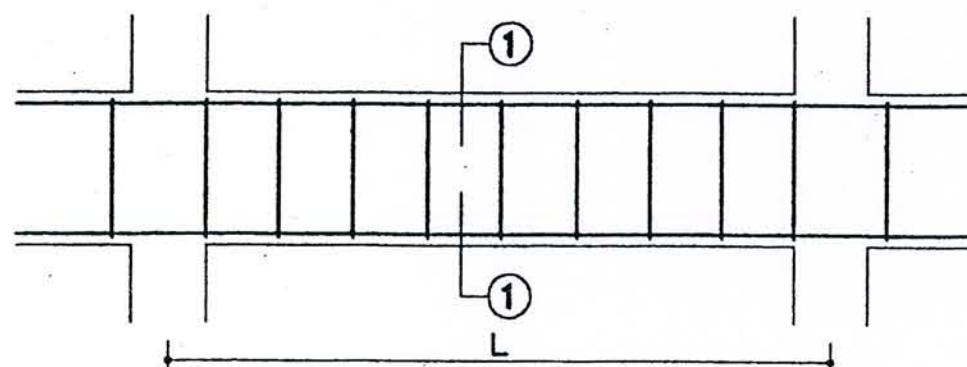


LONG SECTION

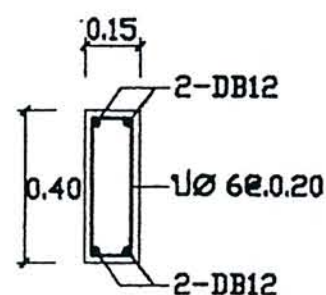


SECTION 1-1

B1

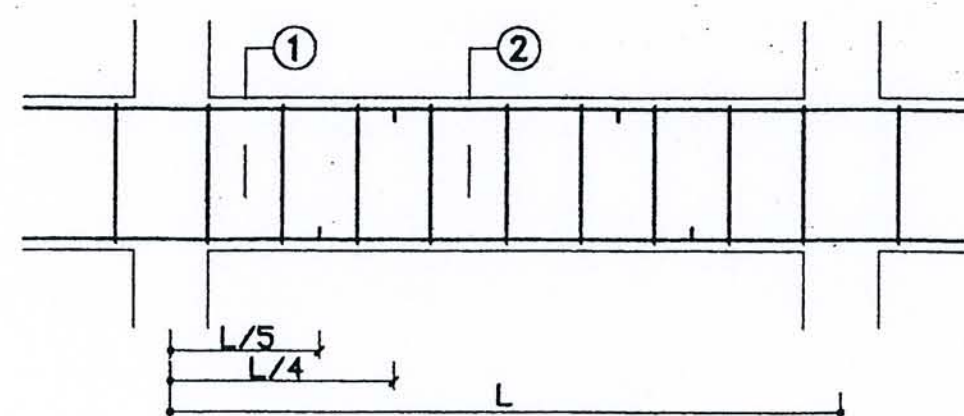


LONG SECTION

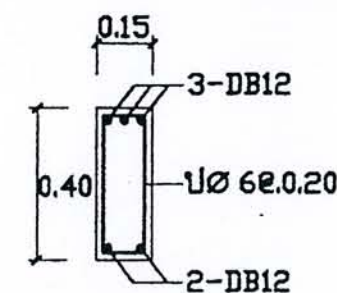


SECTION 1-1


B2

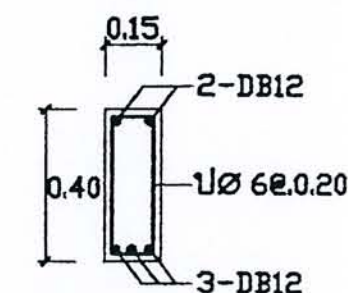

SECTION 2-2

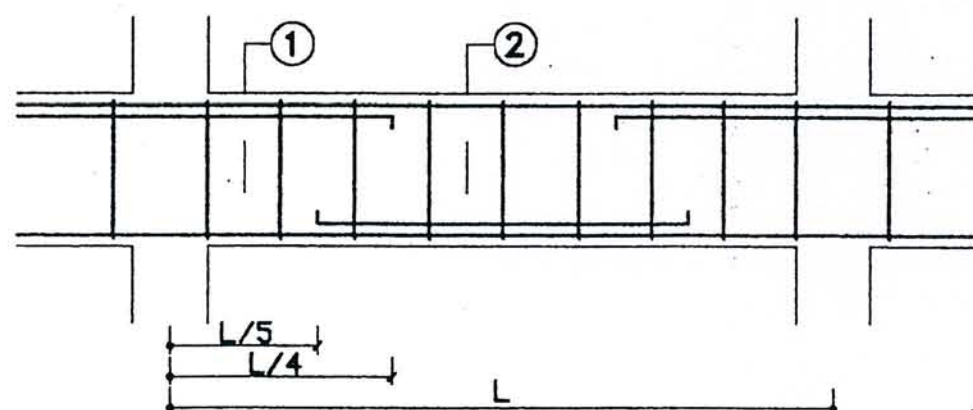


LONG SECTION

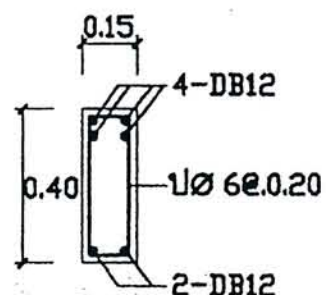


SECTION 1-1


B3

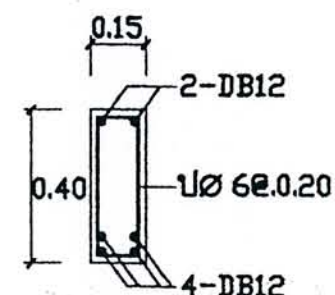

SECTION 2-2

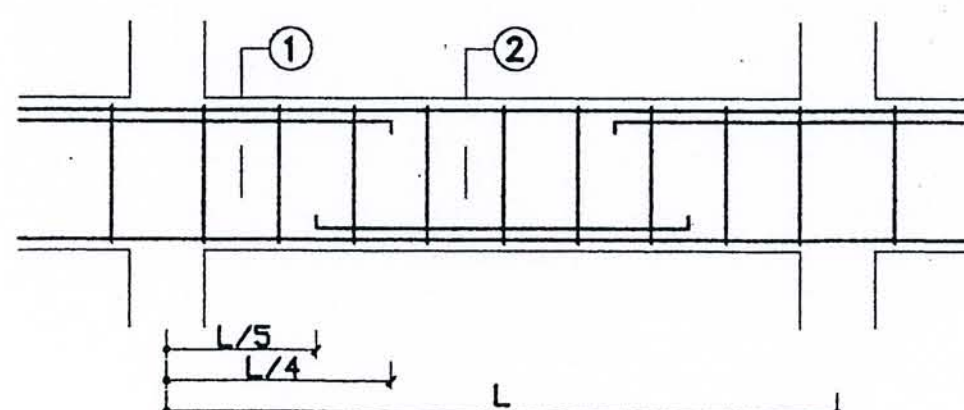


LONG SECTION

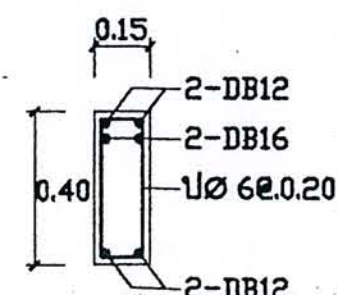

SECTION 1-1

B4

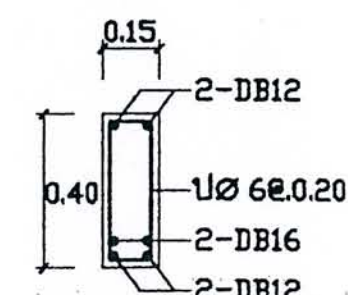



SECTION 2-2



โครงการ
แบบบ้านยืมเพื่อประชาชน


ตามนโยบาย
ม.ร.ว. สุขุมพันธุ์ บริพัตร
ผู้ว่าราชการกรุงเทพมหานคร

โดยสำนักงานโยธา
กรุงเทพมหานคร

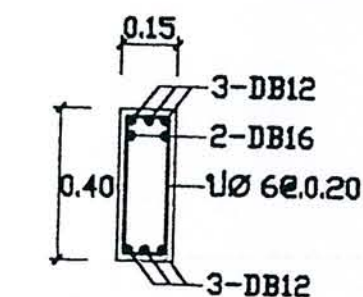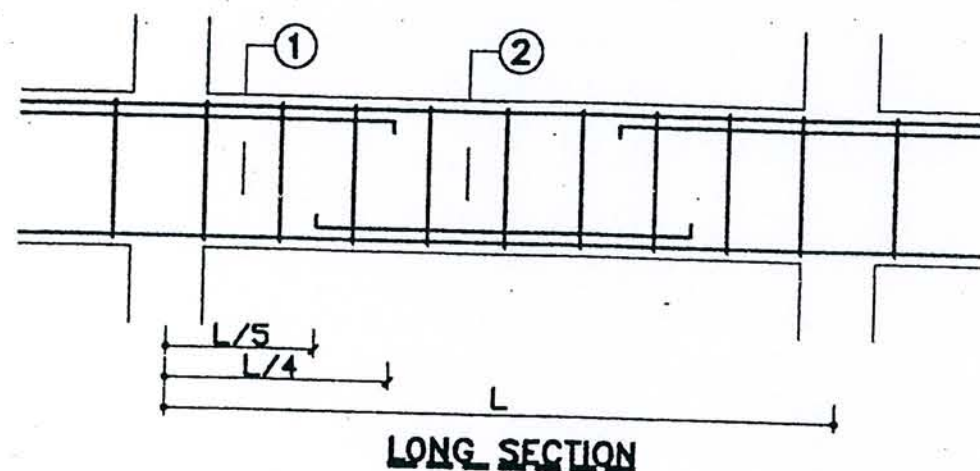


SECTION 1-1


B5

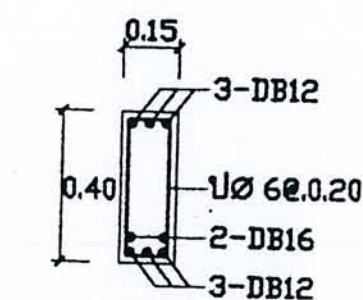

SECTION 2-2

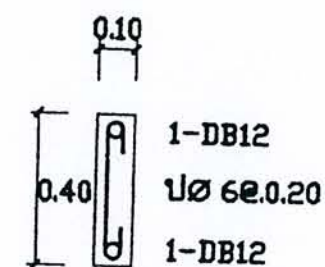


B0

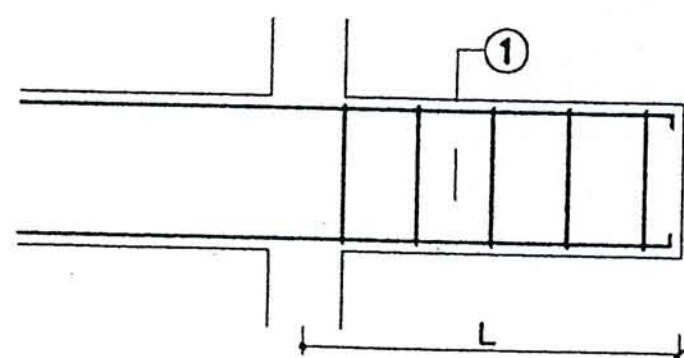


LONG SECTION

B1'

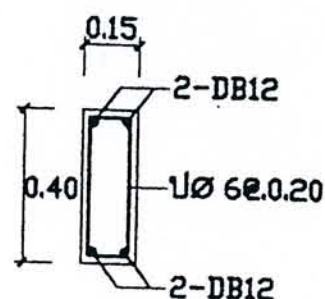


SECTION 1-1

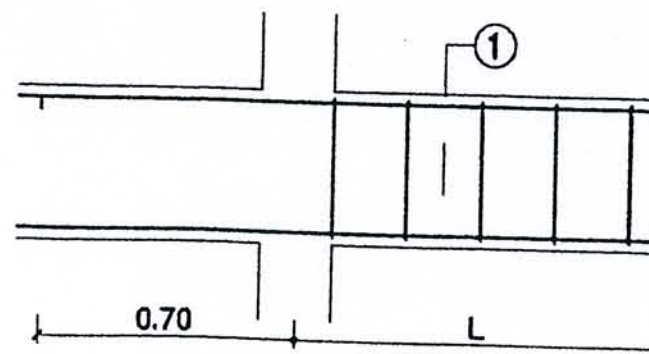

LONG SECTION

B3'

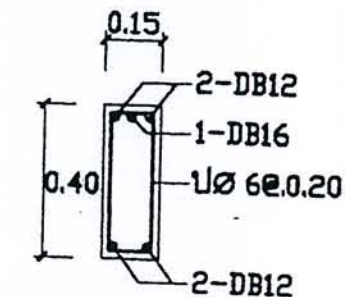

SECTION 1-1

ได้รับความอนุเคราะห์แบบ
จาก
บริษัท แลนด์ โสม
(ประเทศไทย) จำกัด



FOR INFORMATION





โครงการ
แบบบ้านยืมเพื่อประชาชน

ตามนโยบาย
ม.ร.ว. สุขุมพันธุ์ บริพัตร
ผู้ว่าราชการกรุงเทพมหานคร


โดยสำนักงานโยธา
กรุงเทพมหานคร

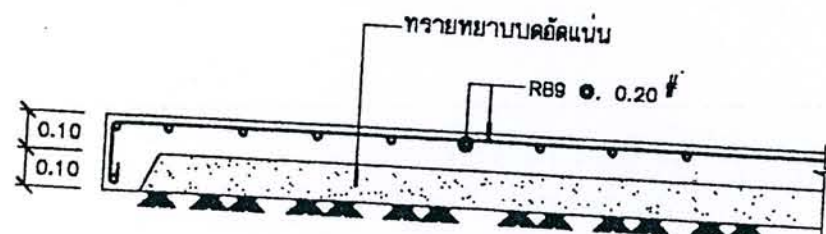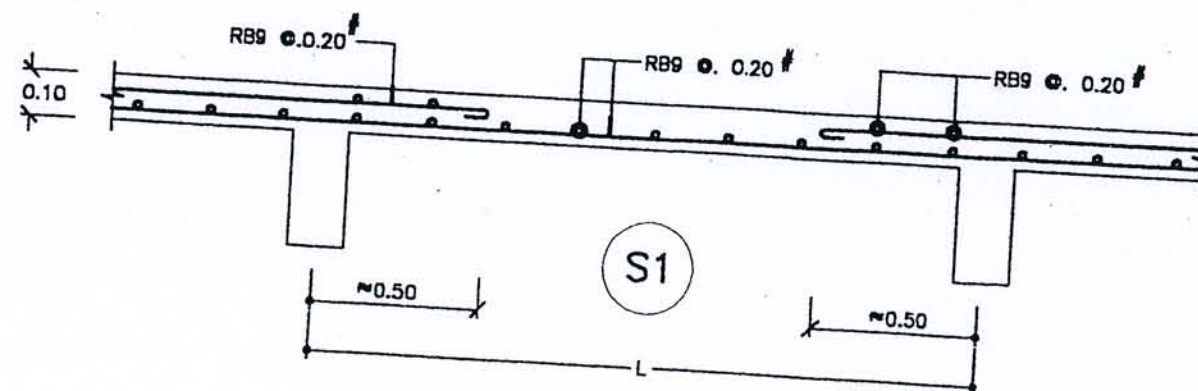

S0

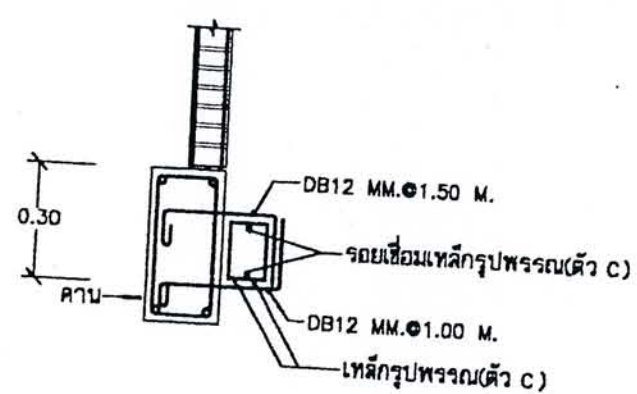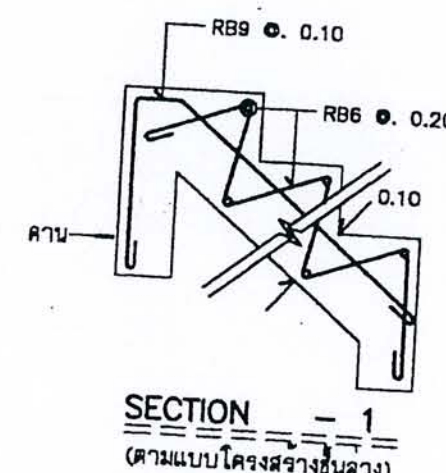

แบบขยายจุดที่มีหลังคาครอบบังแดดผนัง

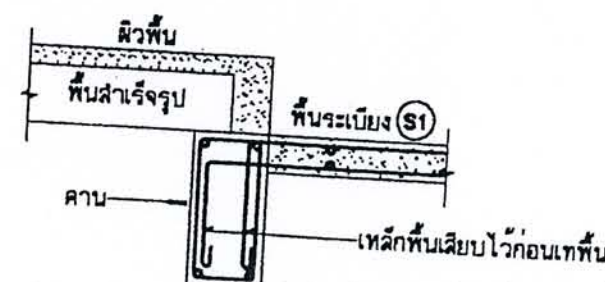

แบบขยายรอยต่อพื้นกับระเบียง

ได้รับความอนุเคราะห์แบบ
จาก
บริษัท แลนด์ โฮม
(ประเทศไทย) จำกัด




โครงการ
แบบบ้านยืมเพื่อประชาชน

ตามนโยบาย
ม.ร.ว. สุขุมพันธุ์ บริพัตร
ผู้ว่าราชการกรุงเทพมหานคร

โดยสำนักงานโยธา
กรุงเทพมหานคร

ได้รับความอนุเคราะห์แบบ
จาก
บริษัท แลนด์ โสม
(ประเทศไทย) จำกัด

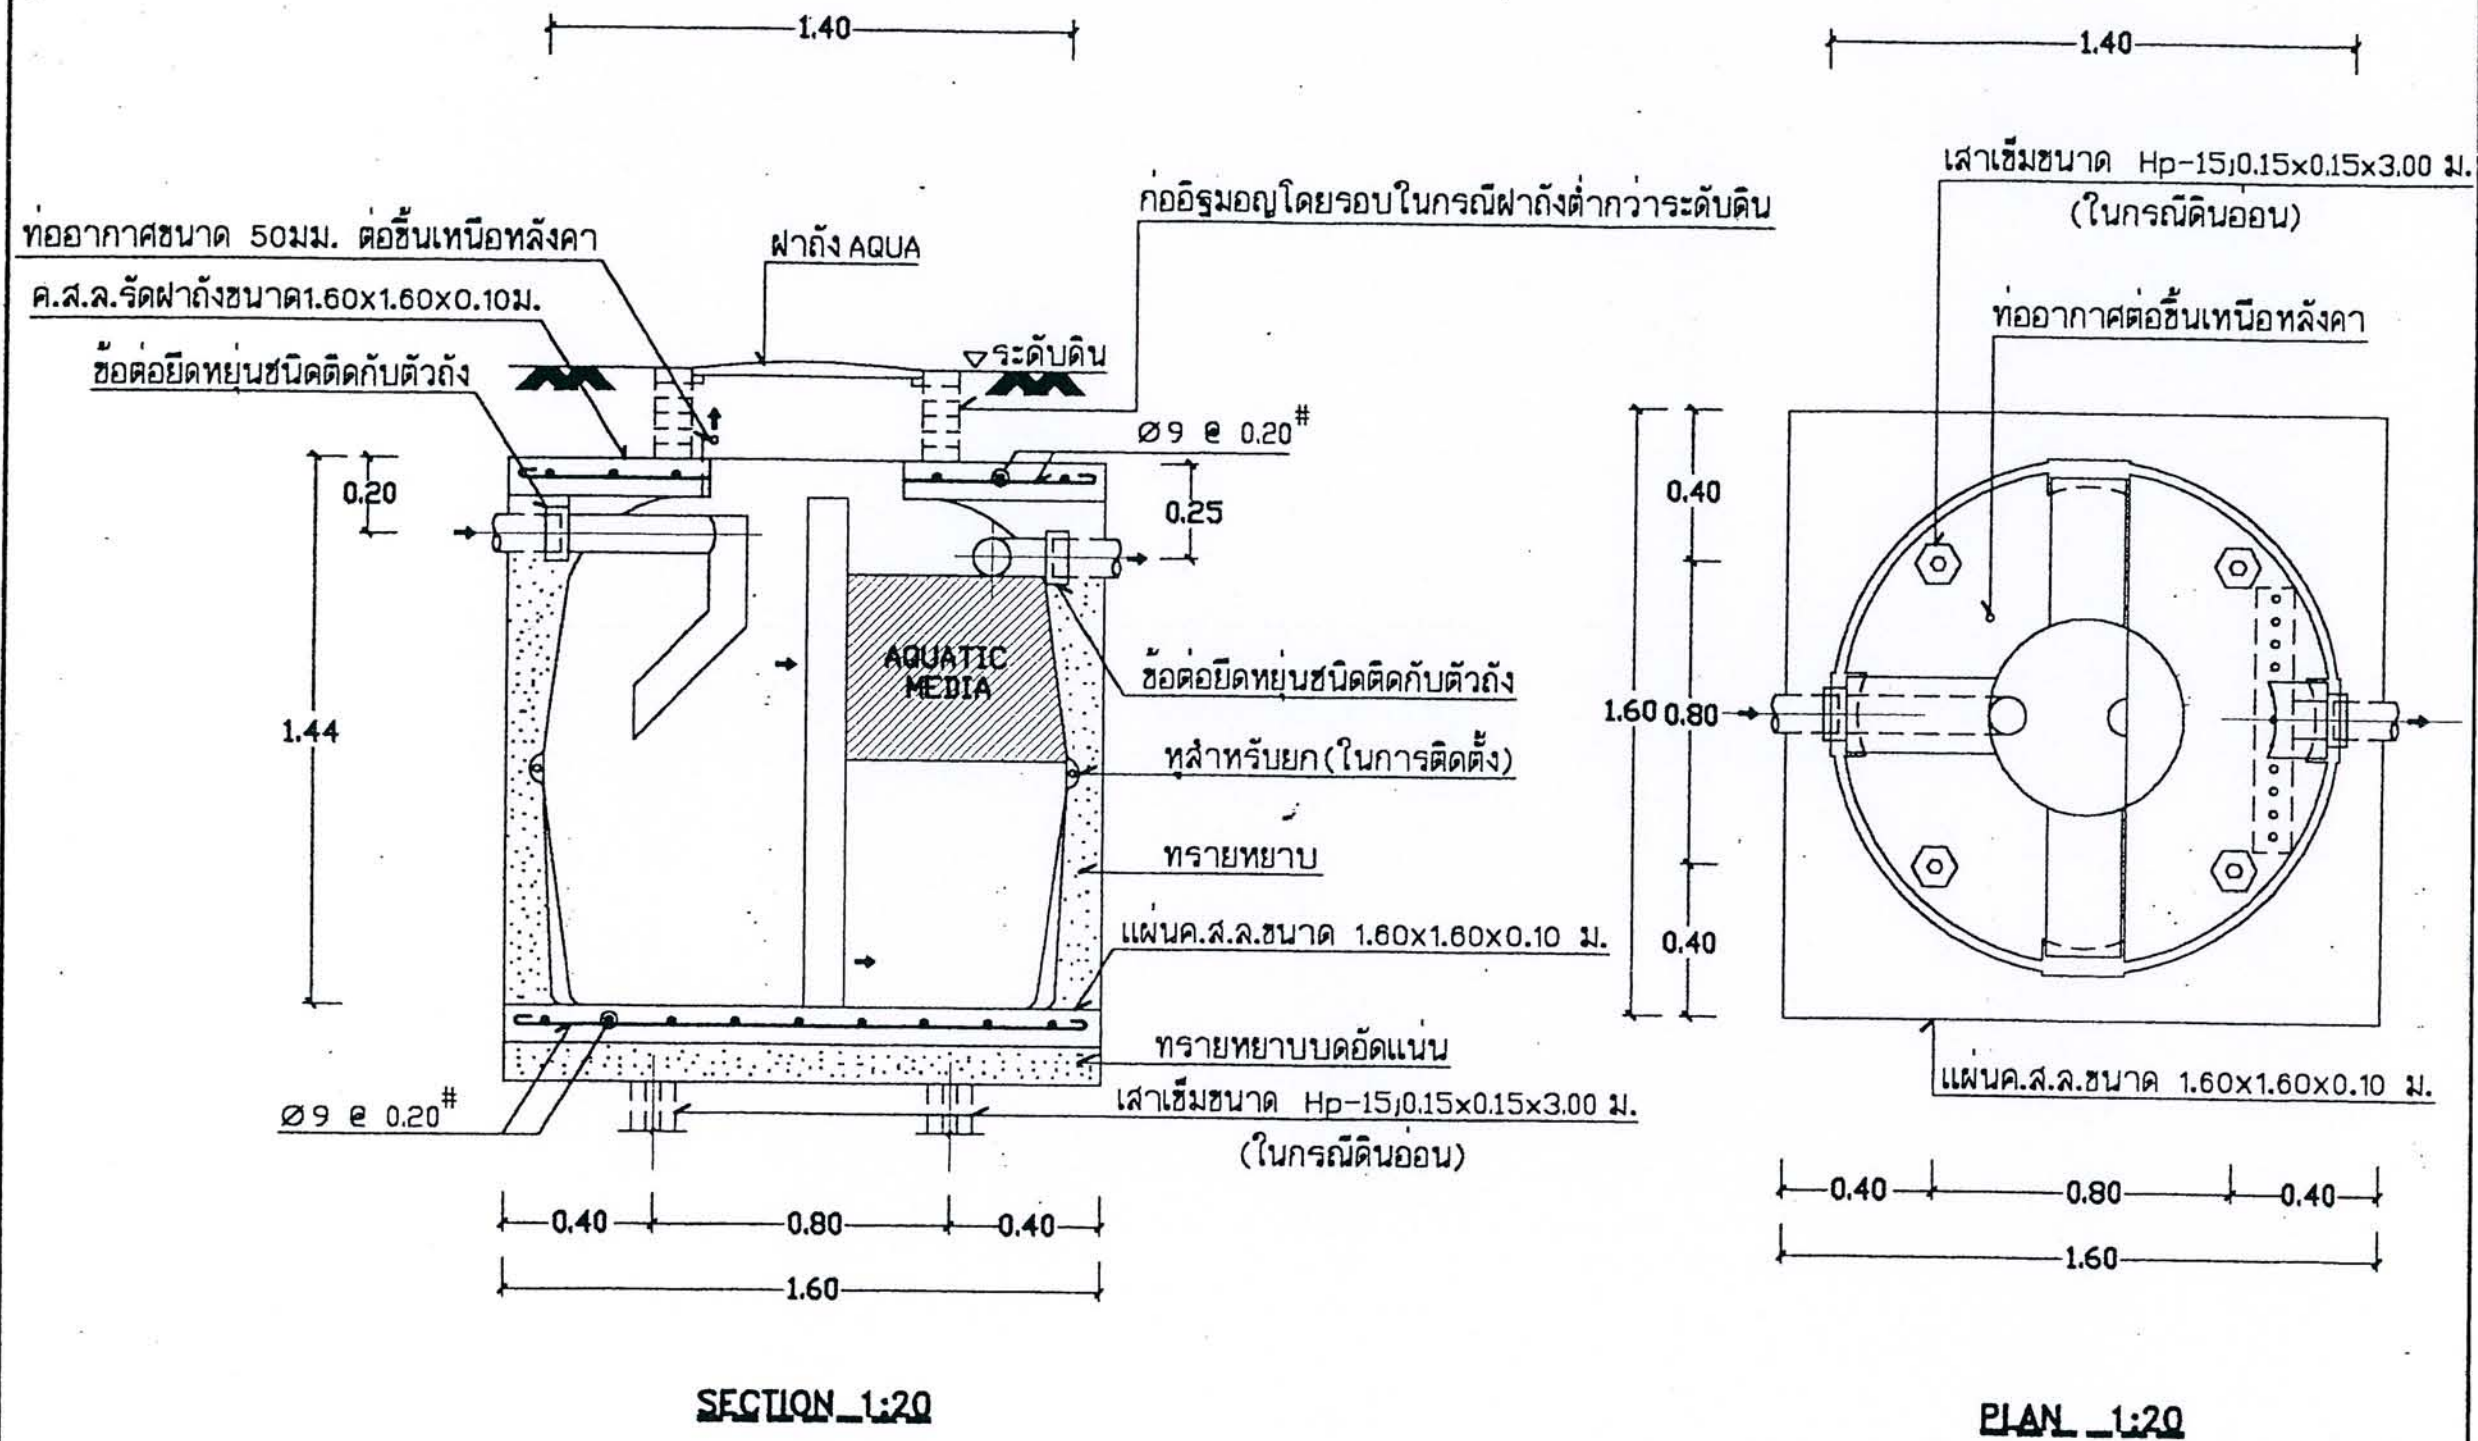

AQUA-PAC(AP-1600)