



ตามนโยบายของ
หม่อมราชวงศ์สุขุมพันธุ์ บริพัตร
ผู้ว่าราชการกรุงเทพมหานคร
โดย สำนักการโยธา



แบบบ้านยืม... เพื่อประชาชน

100 แบบบ้านมาตรฐาน...
สวย ดี โดนใจ...
พร้อมปลูกสร้างได้ทันที

ห้ามพลาด!!! โอกาส...
ยืมรับ... บ้านใหม่
พบ **บ้านสวย
เลือกได้**
ใน “โครงการแบบบ้านยืม...เพื่อประชาชน”

พบ 100 แบบบ้าน
มาตรฐาน...
สวย ดี โดนใจ
พร้อมปลูก
สร้างได้ทันที
ชี้ให้เห็นเลือก
หลากหลาย
ตอบสนอง
ทุกไลฟ์สไตล์คนเมือง

กัลปพฤกษ์ 
สำนักการโยธา กรุงเทพมหานคร

สารบัญแบบสถาปัตยกรรม		
เลขที่	รายการ	
1	A-01	สารบัญแบบ และสัญลักษณ์ประกอบแบบ
2	A-02	รายการประกอบแบบ และแผนที่ตั้ง
3	A-03	ผังบริเวณ
4	A-04	ผังพื้นที่อาคาร
5	A-05	ผังพื้นที่ที่ 2
6	A-06	ผังพื้นที่ที่ 3
7	A-07	ผังผังคา
8	A-08	รูปด้าน 1
9	A-09	รูปด้าน 2
10	A-10	รูปด้าน 3
11	A-11	รูปด้าน 4
12	A-12	รูปตัด A-A
13	A-13	รูปตัด B-B
14	A-14	แบบรายละเอียดบันได
15	A-15	แบบขยายรูปตัดบันได
16	A-16	แบบรายละเอียดน้ำ
17	A-17	แบบรายละเอียดทาง
18	A-18	แบบรายละเอียดทาง
19	A-19	แบบรายละเอียด
แบบวิศวกรรมโครงสร้าง		
20	S-01	รายการประกอบแบบ และผังฐานราก
21	S-02	ผังโครงสร้างชั้นล่าง และผังโครงสร้างชั้น 2
22	S-03	ผังโครงสร้างหลังคา
23	S-04	แบบขยายโครงสร้าง 1
24	S-05	แบบขยายโครงสร้าง 2
แบบวิศวกรรมไฟฟ้า		
25	E-01	รายการและสัญลักษณ์ระบบไฟฟ้า
26	E-02	แปลนไฟฟ้าแสงสว่าง และแปลนเต้ารับไฟฟ้า โพรทัศน์ ชั้น 1
27	E-03	แปลนไฟฟ้าแสงสว่าง และแปลนเต้ารับไฟฟ้า โพรทัศน์ ชั้น 2
28	E-04	แปลนไฟฟ้าแสงสว่าง และแปลนเต้ารับไฟฟ้า โพรทัศน์ ชั้น 3
แบบวิศวกรรมสุขาภิบาล		
29	SN-01	ผังสุขาภิบาลชั้นล่าง
30	SN-02	ผังสุขาภิบาลชั้นที่ 2
31	SN-03	ผังสุขาภิบาลชั้นที่ 3
32	SN-04	ผังสุขาภิบาลหลังคา

ตารางรายการวัสดุ	
สัญลักษณ์	ความหมาย
รายการวัสดุพื้น	
F-1	พื้น ค.ส.ล. ผิวหน้าคอนกรีตขัดหยาบ
F-2	พื้น ค.ส.ล. ผิวหน้าถูกระเบียงขรามีค ชนิดกันลื่นขนาด 0.40x0.40 ม.
F-3	พื้น ค.ส.ล. ผิวหน้าถูกระเบียงขรามีค ชนิดกันลื่นขนาด 0.60x0.60 ม.
F-4	พื้น ค.ส.ล. ผสมน้ำยากันซึม ผิวหน้าถูกระเบียงขรามีค ชนิดกันลื่นขนาด 0.40x0.40 ม.
F-5	พื้น ค.ส.ล. ผสมน้ำยากันซึม ผิวหน้าถูกระเบียงขรามีค ชนิดกันลื่นขนาด 0.30x0.30 ม.
F-6	พื้น ค.ส.ล. ผิวหน้าถูกระเบียงขรามีค ทาสีอะครีลิค
F-7	พื้น ค.ส.ล. ผสมน้ำยากันซึม ผิวหน้าถูกระเบียงขรามีค ชนิดกันลื่นขนาด 0.30x0.30 ม.
รายการวัสดุผนัง	
1	ผนังก่ออิฐฉาบปูน หรือส่วน ค.ส.ล. ทำผิวฉาบเรียบ ทาสีน้ำสำหรับทาภายนอก สีครีม
2	ผนังก่ออิฐฉาบปูน หรือส่วน ค.ส.ล. ทำผิวฉาบเรียบ ทาสีน้ำสำหรับทาภายนอก สีครีมเข้ม หรือ น้ำตาลอ่อน
3	ผนังก่ออิฐฉาบปูน หรือส่วน ค.ส.ล. ทำผิวฉาบเรียบ เศษร่องตามแบบ ทาสีน้ำสำหรับทาภายนอก
4	ผนังก่ออิฐฉาบปูน หรือส่วน ค.ส.ล. ทำผิวฉาบเรียบ ทาสีน้ำสำหรับทาภายนอก ด้านบนติดตะแกรงถี่ 3 แถว
5	ผนังก่ออิฐฉาบปูน หรือส่วน ค.ส.ล. ทำผิวฉาบเรียบ ทาสีน้ำอะครีลิค 100% สำหรับทาภายใน
6	ผนังก่ออิฐฉาบปูน หรือส่วน ค.ส.ล. ถูกระเบียงขรามีค ขนาด 0.30x0.30 ม. สี.
รายการวัสดุมานะ	
C-1	แผ่นดาน GYP BOAREL 9 มม. ธรรมดา ฉาบรอยต่อเรียบ โครงสร้างหลักรูปสี่เหลี่ยม
	ระยะโครง 120 x 240 ซม. ทาสีน้ำอะครีลิค 100 %
C-2	แผ่นดาน GYP BOAREL 9 มม. ทนชื้น ฉาบรอยต่อเรียบ โครงสร้างหลักรูปสี่เหลี่ยม
	ระยะโครง 40 x 120 ซม. ทาสีน้ำอะครีลิค 100 %
C-3	แผ่นดานท้องพื้นโครงสร้าง ค.ส.ล. ทาสีน้ำอะครีลิค 100 % สีขาว
หมายเหตุ	
- งานเหล็กทั่วไปให้ทาสีกันสนิม 2 ครั้ง แล้วทาสีด้วยสีน้ำมันอีก 2 ครั้ง	



สำนักงานโยธา
กรุงเทพมหานคร

โครงการ
แบบบ้านชั้นเดียวประชาชน

ตามนโยบาย
ม.ร.ว.สุขุมพันธุ์ บริพัตร ผู้ว่าฯกทม.
นายพรเทพ เศรษฐิน นายช่างเทคนิค
นายธีระชน มโนวิมล นายช่างเทคนิค
นายพงษ์ศักดิ์ แสนจันทร์ ปลัดกทม.

ผู้อำนวยการสำนักงานโยธา
นายชุมพล อัมมพันธ์
รองผู้อำนวยการสำนักงานโยธา
นายทวีศักดิ์ นิลประพันธ์
ผู้อำนวยการสำนักงานออกแบบ
นายสุรพงศ์ สมบูรณ์
หัวหน้ากลุ่มงานสถาปัตยกรรม
นายสุวิทย์ บุญมี
หัวหน้ากลุ่มงานวิศวกรรม
นายธีระยุทธ คงสวัสดิ์

สถาปนิก
นางสาวสุมนมาลย์ กาญจนะ
วิศวกรโครงสร้าง
นายศุภสิทธิ์ นิลประพันธ์
วิศวกรไฟฟ้า
นายศุภสิทธิ์ นิลประพันธ์
วิศวกรสุขาภิบาล
นางสาวณิชา สมทอง
วิศวกรเครื่องกล

นายช่างเขียนแบบ
นายณัฐพงศ์ ณรงค์บุญชู

แบบ
028 บ้านกัลปพฤกษ์

ที่ตั้ง
สถานที่

แบบร่าง
สารบัญแบบ
สัญลักษณ์แบบ
มาตราส่วน No Scale

FILE : เลขที่ 01
วันที่ 2553
คัดลอกแบบ
32

รายการแก้ไขแบบ

รายการประกอบแบบงานก่อสร้าง

1. วัสดุประสงค์

กรุงเทพมหานคร มีความประสงค์ที่จะทำการออกแบบบ้านพักอาศัย "โครงการหมู่บ้านชั้นเพื่อประชาชน" แบบบ้านที่ 028 ซึ่งอยู่บริเวณถนนสุขุมวิท โดยที่กรุงเทพมหานครได้จัดค่าใช้จ่ายโดย ทั้งสิ้น

2. รายละเอียดประกอบแบบรายการ

2.1 การวัดพื้นที่

หากขนาดหรือรูปร่างที่ดินแตกต่างจากที่ระบุไว้ ควรทำการตรวจสอบและพิจารณาปรับผังบริเวณ ให้ตรงกับข้อกำหนดต่างๆ ที่เกี่ยวข้องกับการก่อสร้างอาคาร แต่โดยทั่วไปแล้ว หากที่ดินที่ขุดถมหรือถมดินนั้น มีขนาดใหญ่มากกว่าที่ระบุในผังบริเวณ ย่อมมีโอกาสที่จะเกิดการปฏิบัติงานกฎหมายและสิ่งแวดล้อมที่ดีขึ้น

ผู้รับจ้างจะต้องทำการวัดพื้นที่วางระดับมาตรฐานให้ถูกต้องตามที่ปรากฏในผังบริเวณ ก่อนที่จะดำเนินการต่อไป ระดับ ± 0.00 ให้ถือตามระดับถนนด้านหน้าหรือถนนสาธารณะ ทางเข้าของที่ดิน ส่วนการลดระดับหรือเปลี่ยนแปลงระดับภายในอาคาร ให้ยึดถือระดับเมื่อถมดินเรียบร้อยแล้ว ตามที่ระบุในแบบสถาปัตยกรรมเป็นหลัก

2.2 งานโครงสร้าง

รายละเอียดตามแบบวิศวกรรมโครงสร้าง โดยแบบโครงสร้างที่ปรากฏในแบบฉบับนี้ เป็นการออกแบบเพื่อให้สำหรับก่อสร้างในเขตกรุงเทพมหานครทั่วไป กรณีที่ไม่ได้ก่อสร้างบนพื้นที่ที่มีลักษณะพิเศษ เช่น เขตบางขุนเทียน เขตทุ่งครุ หรือพื้นที่ต่างจังหวัด จะต้องมีการพิจารณาการออกแบบโครงสร้างฐานรากใหม่ เพื่อให้ได้ SAFE LOAD ตามวิศวกรรมกำหนด

2.3 งานสถาปัตยกรรม

2.3.1 งานผนังอาคารทั้งหมด ให้ใช้ผนังอิฐก่อครึ่งซึก หรือคอนกรีตมวลเบา หรืออื่นๆ (เจ้าของกำหนด) การก่อผนังภายใน ให้ก่อด้วยอิฐก่อครึ่งซึกขึ้นบน โดยผนังทั่วไป ให้ตามแบบสถาปัตย์ ทาสี ส่วนผนังห้องน้ำ ให้ตามแบบกระเบื้องเคลือบ ชนิดปูผนังลายและขนาด (เจ้าของกำหนด)

2.3.2 งานพื้น พื้นอาคารเป็น คสล. ตามแบบสถาปัตย์วิศวกรรมโครงสร้าง ในกรณีที่เป็นพื้นคสล. ในกรณีที่เป็นพื้นคสล. หลังปูพื้นด้วยทราย เป็นแบบ ส่วนการตกแต่งผิวพื้น ให้เป็นไปตามลักษณะแบบสถาปัตยกรรม ที่งานนี้ให้รวมงานปูพื้น จะต้องทำทุกส่วนที่พื้นนั้นไปรวม ให้ใช้ปูนพื้นไม่สีทราย ไม่มีส่วนผสมของ Asbestos

2.3.3 งานฝ้าเพดาน เป็นโครงค้ำเหล็กชุบสังกะสี ปูด้วยแผ่นไฟเบอร์ซีเมนต์ หนาไม่น้อยกว่า 8 มม. (ในท้องถิ่นที่ชื้นหรือฝนชุก) ฉาบเรียบ ทาสี ครอบด้วยโครงค้ำเหล็กตามมาตรฐานบริษัทผู้ผลิต ให้ยึดตั้งบนผนังความชื้น บนฝ้าเพดานห้องขึ้นบน หรือใต้โครงหลังคา

2.3.4 งานประตู-หน้าต่าง ช่องแสง และกระจก รูปแบบให้เป็นไปตามแบบสถาปัตย์ หรือเจ้าของกำหนด

- งานประตูบานเปิด ให้ใช้บานไม้เนื้อแข็ง ขนาด 2"x4" บานประตูบานเปิด ทั่ว
- งานหน้าต่าง ให้ใช้บานไม้เนื้อแข็ง หรือใช้บานอลูมิเนียมชุบสังกะสีชนิด 6063-T5 หรือ 505-T5
- ลูกบิดประตูบานเปิด ให้ใช้ลูกบิดที่ทำด้วยเหล็กชุบสังกะสี หนาไม่น้อยกว่า 8 มม. (เจ้าของกำหนด) ส่วนกระจกบานเปิด ต้องทำจากกระจกใสใสทึบกัน
- ให้ติดตั้งมุ้งลวดไฟเบอร์ กรอบอลูมิเนียม ทุกบาน

2.3.5 งานห้องน้ำ-ตัว และสุขภัณฑ์ รูปแบบให้เป็นไปตามแบบสถาปัตย์ หรือเจ้าของกำหนด โดยที่ผู้รับจ้าง จะต้องประสานงาน ระบายน้ำเพื่อทำการติดตั้งสุขภัณฑ์ อุปกรณ์ประกอบห้องน้ำและอื่นๆ ผู้รับจ้างต้องตรวจสอบขนาด ตำแหน่ง และระดับของงานท่อต่างๆ ให้ตรงกับรุ่นและยี่ห้อที่ผู้รับจ้างกำหนด พื้นห้องน้ำ-ตัว ต้องเป็นคสล.ผสมน้ำยากันซึม ทาสีด้วยน้ำยากันซึม ก่อนปูกระเบื้องเคลือบ

2.3.6 งานทาสี โดยทั่วไป ผู้รับจ้างต้องทำการเตรียมผิววัสดุทุกส่วนที่จะทาสีให้เรียบก่อน จึงจะทาสีได้

- ส่วนที่เป็นปูน ชิมมิด ให้ทาสีรองพื้นปูนใหม่ 1 เที่ยว ก่อนทาสีจริงกับหน้าอย่างน้อย 2 เที่ยว ทั้งนี้ ผิวปูนฉาบ ฝ้าเพดาน ให้ทาสีด้วยสี ACRYLIC 100% ที่เงา หรือเจ้าของกำหนด
- ส่วนที่เป็นไม้จะต้องอุดไม้และขัดผิวด้วยกระดาษทรายละเอียด ทาสีรองพื้นไม้ 1 เที่ยว ก่อนทาสีจริงกับหน้าอย่างน้อย 2 เที่ยว
- ส่วนที่เป็นเหล็ก หากมีสนิม ให้ขัดสนิมออกให้มากที่สุด รวมทั้งทำความสะอาดรอยเชื่อม ทาสีรองพื้นกันสนิม 1 เที่ยว ก่อนทาสีจริง (สีน้ำมัน) กับหน้าอย่างน้อย 2 เที่ยว

2.3.7 งานหลังคา โครงสร้างหลังคา ตามแบบวิศวกรรมโครงสร้าง ในกรณีที่เป็นหลังคากระเบื้อง ให้ใช้กระเบื้องซีเมนต์ใยหิน การติดตั้งให้เป็นไปตามกรรมวิธีของบริษัทผู้ผลิตอย่างเคร่งครัด ในกรณีที่เป็นหลังคา หรือกันสาดคสล. ให้ผสมน้ำยากันซึมในโครงสร้าง และทำระแนงกันซึม สำหรับหลังคา หรือกันสาด สำหรับกันสาด

2.3.8 งานบันได บันไดคอนกรีตเสริมเหล็ก โครงสร้างตามแบบวิศวกรรมโครงสร้าง ฉาบเรียบ ทาสี พื้นบันไดและราวกันกั้น ให้ปูด้วยแผ่นไม้จริง เป็นไม้เนื้อแข็ง หนา 1" ขนาดเท่าลูกนอน โดยยื่นจากขอบลูกกั้น 1"

2.3.9 งานอื่นๆ

- งานค้ำยัน ไม้ท่อนในงานก่อสร้างนี้ ยกเว้นเจ้าของงานตกลงเป็นงานเพิ่มเติมเป็นรายการอื่น
- กรณีที่ผู้รับจ้างรับติดตั้งระบบสายสัญญาณและระบบไฟฟ้า เพื่อรองรับการติดตั้งอุปกรณ์
- การเดินท่อ PVC Class 13.5 เพื่อใส่พัดลมดูด มอด แสง รวมอยู่ในงานก่อสร้างนี้

2.4 งานระบบสุขาภิบาล ผู้รับจ้างต้องตรวจสอบระบบสุขาภิบาล ตามแบบ หรือติดตั้งสุขภัณฑ์ บ่อน้ำอัดน้ำเสีย และอื่นๆที่ระบุในแบบ กรณีที่ต้องเดินท่อผ่านคาน พื้น หรือโครงสร้าง จะต้องจัดเตรียม SLEEVE ให้เรียบร้อย

2.5 งานระบบไฟฟ้า ผู้รับจ้างต้องติดตั้งและเดินสายระบบไฟฟ้า ระบบแสงสว่าง ตามแบบรายการประกอบแบบทางไฟฟ้า และตามมาตรฐานการไฟฟ้า กรณีที่ต้องเดินท่อผ่านคาน พื้น หรือโครงสร้าง จะต้องจัดเตรียม SLEEVE ให้เรียบร้อย

3. ข้อกำหนดเฉพาะงาน

การดำเนินการก่อสร้าง

- 1 การก่อสร้างให้เป็นไปตามแบบ และรายการประกอบแบบ ผู้รับจ้างจะต้องเตรียม วัสดุ อุปกรณ์ เครื่องมือ เครื่องจักร ช่างฝีมือดี และแรงงานที่เหมาะสม ให้เพียงพอ และพร้อมเพื่อปฏิบัติงานก่อสร้างให้ดำเนินงานไปด้วยความรวดเร็ว เียบร้อยและมีประสิทธิภาพและได้งานที่ถูกต้องสมบูรณ์ตามแบบและรายการก่อสร้างทุกประการ โดยมีผลงานที่ปรากฏด้วย
- 2 แบบ และรายการก่อสร้าง หากมีข้อขัดแย้งกันให้ยึดถือแบบสถาปัตย์วิศวกรรมโครงสร้างเป็นหลัก หรือถ้าแบบสถาปัตย์วิศวกรรมโครงสร้างและรายการก่อสร้างขัดแย้งกัน ให้ยึดถือแบบสถาปัตย์วิศวกรรมโครงสร้างเป็นหลัก แต่เพื่อความเรียบร้อยของงานก่อสร้าง ให้ยึดถือรายการก่อสร้างเป็นหลัก ผู้รับจ้างจะต้องดำเนินการแก้ไขข้อขัดแย้งที่ปรากฏในแบบสถาปัตย์วิศวกรรมโครงสร้างให้ถูกต้องก่อนดำเนินการก่อสร้าง
- 3 ผู้รับจ้างต้องปฏิบัติตามแบบ และ/หรือ รายการก่อสร้าง หรือมีข้อขัดแย้งกันรายการก่อสร้างขัดแย้งกัน ให้ยึดถือแบบสถาปัตย์วิศวกรรมโครงสร้างเป็นหลัก แต่ถ้าแบบสถาปัตย์วิศวกรรมโครงสร้างและรายการก่อสร้างขัดแย้งกัน ให้ยึดถือแบบสถาปัตย์วิศวกรรมโครงสร้างเป็นหลัก แต่ถ้าแบบสถาปัตย์วิศวกรรมโครงสร้างและรายการก่อสร้างขัดแย้งกัน ให้ยึดถือแบบสถาปัตย์วิศวกรรมโครงสร้างเป็นหลัก
- 4 ผู้รับจ้างต้องจัดทำบัญชีรายการวัสดุอุปกรณ์ที่ใช้ในการก่อสร้างให้ครบถ้วนและถูกต้องตามที่กำหนดในแบบสถาปัตย์วิศวกรรมโครงสร้าง และรายการก่อสร้าง และต้องเป็นบัญชีรายการวัสดุอุปกรณ์ที่ใช้ในการก่อสร้างที่ไม่ใช่รายการวัสดุอุปกรณ์ที่ใช้ในการก่อสร้างที่ไม่ใช่รายการวัสดุอุปกรณ์ที่ใช้ในการก่อสร้าง

มาตรการป้องกันเหตุฉุกเฉินด้านความปลอดภัยทางเคมี

- ปฏิบัติตามหลักเกณฑ์ วิธีการ ตามประกาศกระทรวงมหาดไทย ฉบับที่ 8 พ.ศ. 2534 โดยต้อง
- จัดให้มีรั้วหรือกำแพงสูงไม่น้อยกว่า 2.00 ม. ทั่วบริเวณเขตอันตราย
 - จัดให้มีป้ายเตือนภัย โดยข้อความและเครื่องหมายต้องชัดเจนเกี่ยวกับอันตรายของอาคาร สถานที่ก่อสร้าง
 - จัดให้มีช่องระบายอากาศสำหรับทั้งของ และป้องกันผู้ปฏิบัติงานจากอันตราย
 - การทำงาน ต้องสวมหน้ากากป้องกันพิษ หรืออุปกรณ์ป้องกันภัยอันตรายอย่างอื่นที่ไม่ได้กำหนดไว้
 - การก่อสร้างต้องมีการป้องกันอันตรายจากไฟฟ้าแรงสูง
 - การก่อสร้างต้องมีการป้องกันอันตรายจากอัคคีภัย
 - ไม่ทำการก่อสร้างในช่วงที่มีฝนตกและแสงสว่างไม่เพียงพอตั้งแต่เวลา 22.00 - 06.00 น.
 - พนักงานต้องเป็นชาวไทย 1 ของภาคกลางหรือภาคอื่น (2528) นอกตามความ พ.ร.บ. ความปลอดภัย พ.ศ. 2522 ฉบับที่ 30 มีผลบังคับ 2523
 - ตามประกาศกระทรวงมหาดไทย เรื่อง ความปลอดภัยในการทำงานก่อสร้างด้วยมือ
 - ให้มีใบ มาตรการ หรือข้อมูลด้านความปลอดภัยกับลูกจ้างทุกคน ที่มีความสูงไม่น้อยกว่า 14.00 ม. หรือ 2 ใน 3 ของความสูง
 - ให้มีใบ มาตรการ หรือข้อมูลด้านความปลอดภัยกับลูกจ้างทุกคน ที่มีความสูงไม่น้อยกว่า 14.00 ม. หรือ 2 ใน 3 ของความสูง

แผนที่ที่ส่งเข้า



สำนักงานโยธา
กรุงเทพมหานคร

โครงการ
แบบบ้านชั้นเพื่อประชาชน

ตามนโยบาย

นางจุฬารัตน์ นิลรัตน์ ผู้อำนวยการ
นายพรเทพ เศรษฐกิจ รองผู้อำนวยการ
นายธีรวัฒน์ นิลรัตน์ รองผู้อำนวยการ
นายพงศ์ศักดิ์ นิลรัตน์ ปลัด

ผู้อำนวยการสำนักงานโยธา
นายจุฬารัตน์ นิลรัตน์
รองผู้อำนวยการสำนักงานโยธา
นายพรเทพ เศรษฐกิจ
นายธีรวัฒน์ นิลรัตน์
นายพงศ์ศักดิ์ นิลรัตน์

สถานีย่อย
นางสาวสุมนพร นิลรัตน์
วิศวกรโครงสร้าง
นายพรเทพ เศรษฐกิจ
วิศวกรไฟฟ้า
นายธีรวัฒน์ นิลรัตน์
วิศวกรสุขาภิบาล
นางสาวสุมนพร นิลรัตน์
วิศวกรเครื่องกล

นายจุฬารัตน์ นิลรัตน์
นายพงศ์ศักดิ์ นิลรัตน์

แบบ
028 บ้านกึ่งปลูก

เจ้าของ

สถานที่

แบบแสดง
รายการประกอบแบบ
และแผนที่ส่งเข้า

มาตราส่วน No Scale

FILE : วันที่ 02

วันที่ 02

วันที่ 02

วันที่ 02

วันที่ 02

วันที่ 02

วันที่ 02

วันที่ 02



สำนักงานโยธา
กรุงเทพมหานคร

โครงการ
แบบบ้านชั้นเดียวประชาชน

ตามนโยบาย

ม.ร.ว.สุขุมพันธุ์ บริพัตร ผู้ว่าฯกทม.
นายพรเทพ เศรษฐินทุเรศ รองผู้ว่าฯกทม.
นายธีระชน มโนวิมลนุกุลย์ รองผู้ว่าฯกทม.
นายพงศ์ศักดิ์ สุขะพันธ์ ปลัดฯกทม.

ผู้อำนวยการสำนักงานโยธา
นายชุมพล อำนวยกุล
รองผู้อำนวยการสำนักงานโยธา
นายวิฑิต วัฒนประพันธ์
ผู้อำนวยการสำนักงานออกแบบ
นายชุตัญดา แสนเยี่ยม
ผู้อำนวยการงานสถาปัตยกรรม
นายสันติสุข บุญมีเกษ
ผู้อำนวยการงานวิศวกรรม
นายธีระยุทธ คงทรัพย์เจริญ

สถาปนิก
นางสาวสุนนมาลย์ กาญจนะ
วิศวกรโครงสร้าง
นายจิรสิงห์ วัฒนชัย
วิศวกรไฟฟ้า
นายกิตติพงษ์ จิระเศกกร
วิศวกรสุขาภิบาล
นางสาวณนชิตา สมพจน์
วิศวกรเครื่องกล

นายช่างเขียนแบบ
นายณัฐพงศ์ ณรงค์บุญชูสุข

แบบ
028 บ้านกัลปพฤกษ์

เจ้าของ

สถานที่

แบบแสดง
ผังบริเวณ

มาตราส่วน 1:75


FILE : เลขที่

วันที่ 25/04/2553 A-03 03

ชุดแบบบ้านประชาชน

รวมแผ่น 32

รายการแนบ

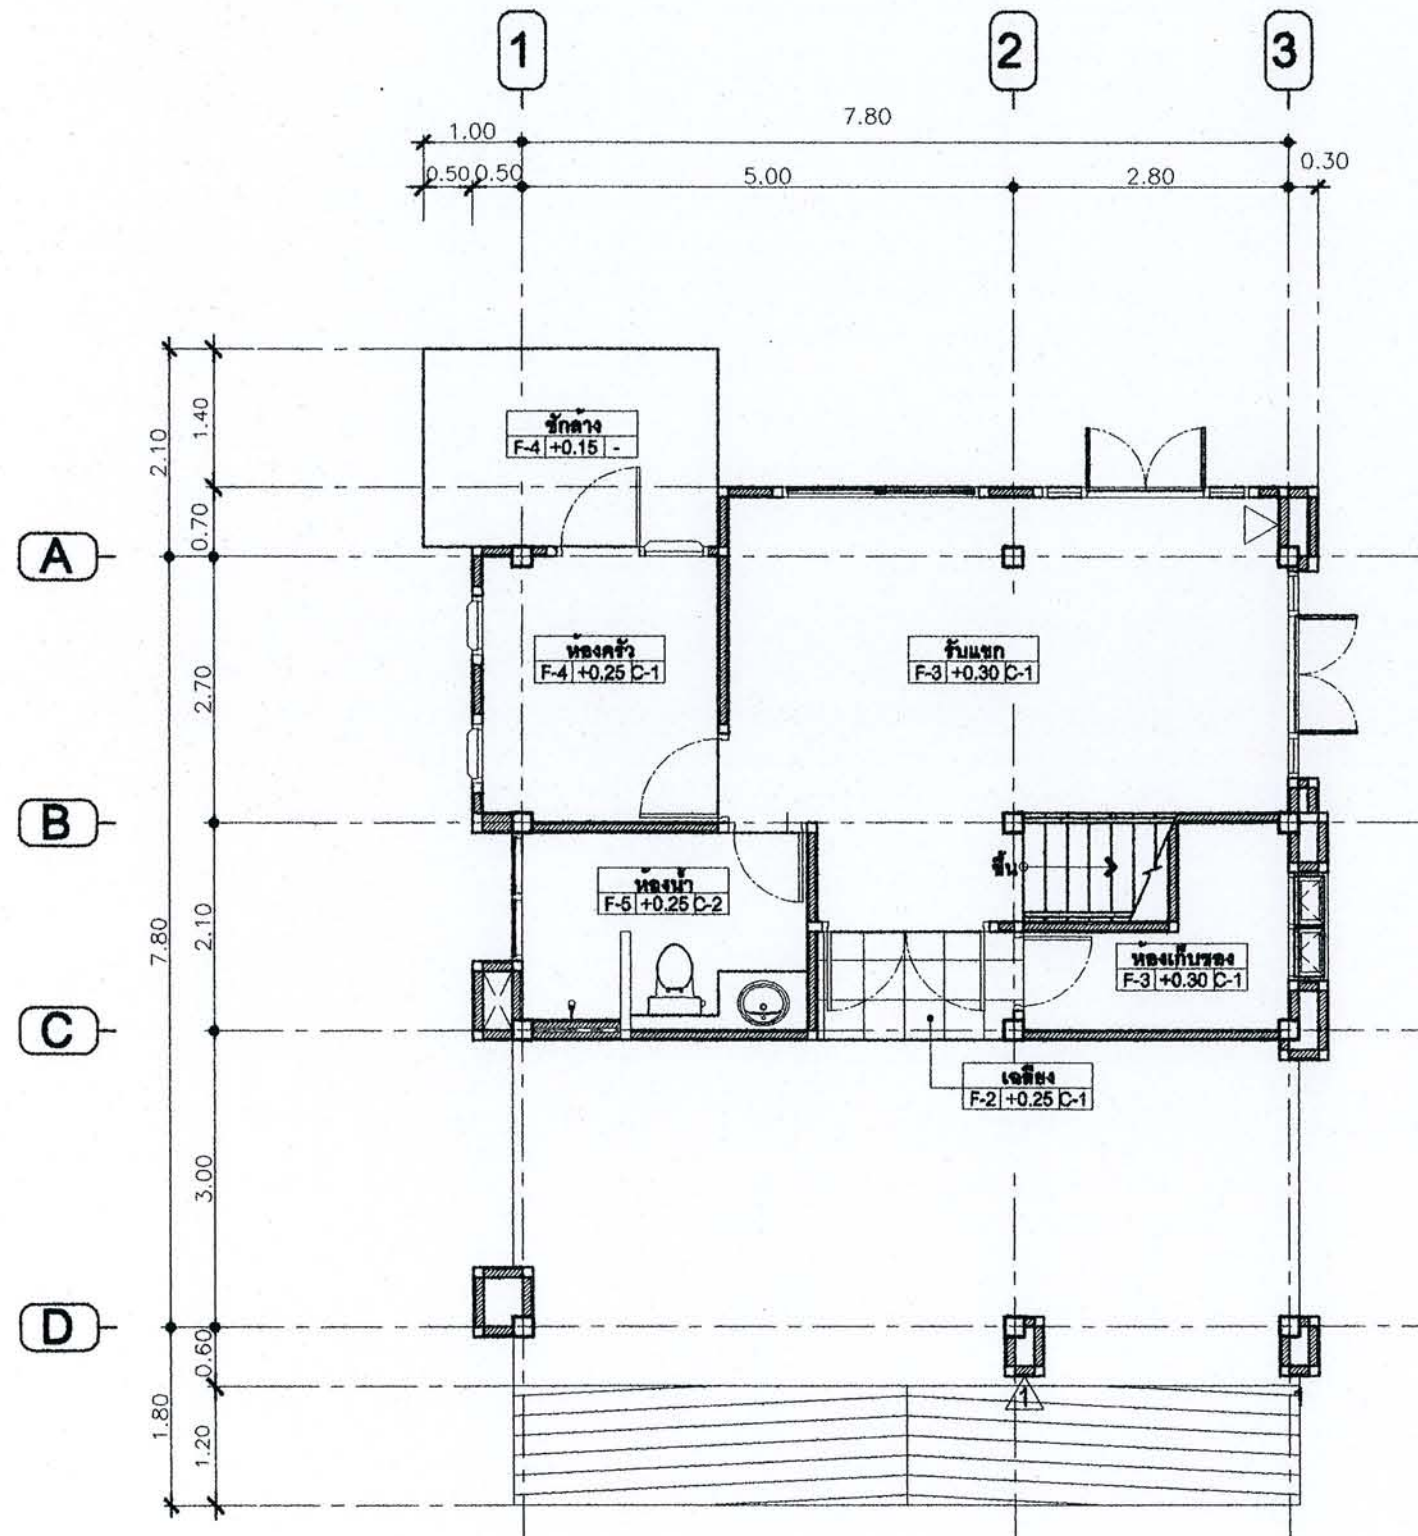



สำนักงานโยธา
กรุงเทพมหานคร

โครงการ
แบบบ้านขึ้นเพื่อประชาชน

ตามนโยบาย

ม.ร.ว.สุขุมพันธุ์ บริพัตร ผู้ว่าฯกทม.
นายทศพร หะริกุลชัย รองผู้ว่าฯกทม.
นายธีระชน มโนวิมลนุกุล รองผู้ว่าฯกทม.
นายพงศ์ศักดิ์ เทพรักษ์ ปลัดฯกทม.

ผู้อำนวยการสำนักงานโยธา
นายสุเมธ สันติสุข
รองผู้อำนวยการสำนักงานโยธา
นายทศพร หะริกุลชัย
ผู้อำนวยการสำนักงานออกแบบ
นายสุเมธ สันติสุข
หัวหน้ากลุ่มงานสถาปัตยกรรม
นายสุเมธ สันติสุข
หัวหน้ากลุ่มงานวิศวกรรม
นายธีระชน มโนวิมลนุกุล

สถาปนิก
นางสาวสุนันทา กาญจนะ
วิศวกรโครงสร้าง
นายสุเมธ สันติสุข
วิศวกรไฟฟ้า
นายทศพร หะริกุลชัย
วิศวกรสุขาภิบาล
นางสาวสุนันทา กาญจนะ
วิศวกรเครื่องกล

นายช่างเขียนแบบ
นายสุเมธ สันติสุข

แบบ
028 บ้านกิตติพิทักษ์

ค่าของ

สถานที่

แบบแสดง
ผังพื้นที่ขั้วล่าง

มาตราส่วน 1:75


FILE : เลขที่ 04

วันที่ 2553

ค.ศ. 2553

32

รายการแก้ไขแบบ

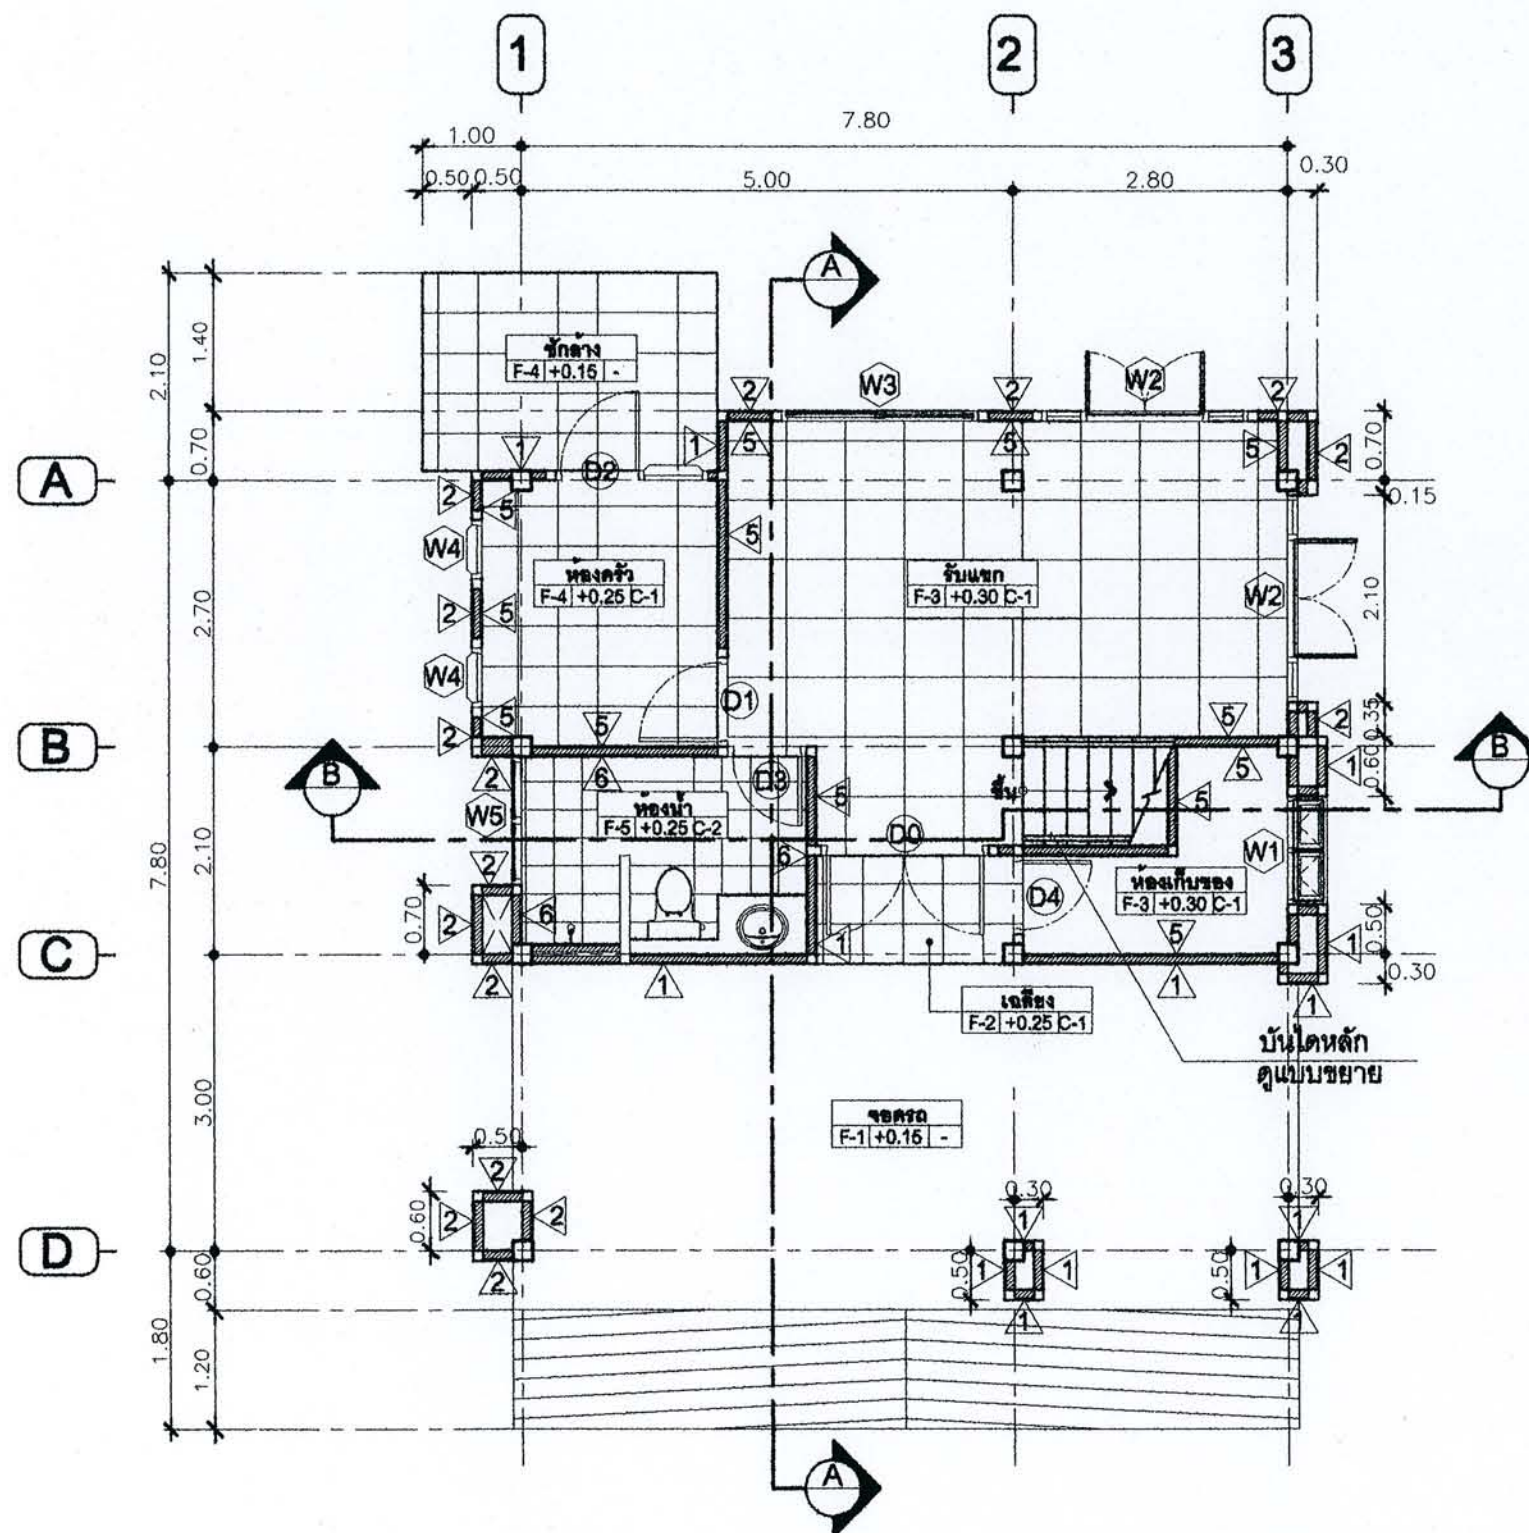

สำนักงานโยธา
กรุงเทพมหานคร

ผังพื้นที่ขั้วล่าง

1:75



สำนักงานโยธา
กรุงเทพมหานคร

โครงการ
แบบบ้านขึ้นเพื่อประชาชน

ตามนโยบาย

ม.ร.ว.สุขุมพันธุ์ บริพัตร ผู้ว่าฯกทม.
นายพรเทพ เศรษฐิน้อย รองผู้ว่าฯกทม.
นายธีระชน มโนวิมลนิตย์ รองผู้ว่าฯกทม.
นายพงษ์ศักดิ์ เศรษฐินันต์ ปลัดฯกทม.

ผู้อำนวยการสำนักงานโยธา
นายชุมพล สันภาพ
รองผู้อำนวยการสำนักงานโยธา
นายทวิศักดิ์ เศรษฐินันต์
ผู้อำนวยการสำนักงานออกแบบ
นายจตุรงค์ สมนิคม
หัวหน้ากลุ่มงานสถาปัตยกรรม
นายสันติชัย บุญปักษ์
หัวหน้ากลุ่มงานวิศวกรรม
นายธีระยุทธ คงศรีเดโช

สถาปนิก
นางสาวดวงนภดา กาญจนะ
วิศวกรโครงสร้าง
นายศิริพงษ์ จินตนิย
วิศวกรไฟฟ้า
นายกิตติพงษ์ จิระเดชาร
วิศวกรสุขาภิบาล
นางสาวมณีนีรา สมนิคม
วิศวกรเครื่องกล

นายช่างเขียนแบบ
นายณัฐพงศ์ ณรงค์บุญชูสุทธิ

แบบ
028 บ้านกัลปพฤกษ์

เจ้าของ

สถานที่

แบบแสดง
ผังพื้นที่ 2

มาตราส่วน 1:75


FILE : เลขที่ 05

วันที่ 25/05/2563

คัดลอกไปใช้แบบ

จำนวน 32

รายการแก้ไขแบบ

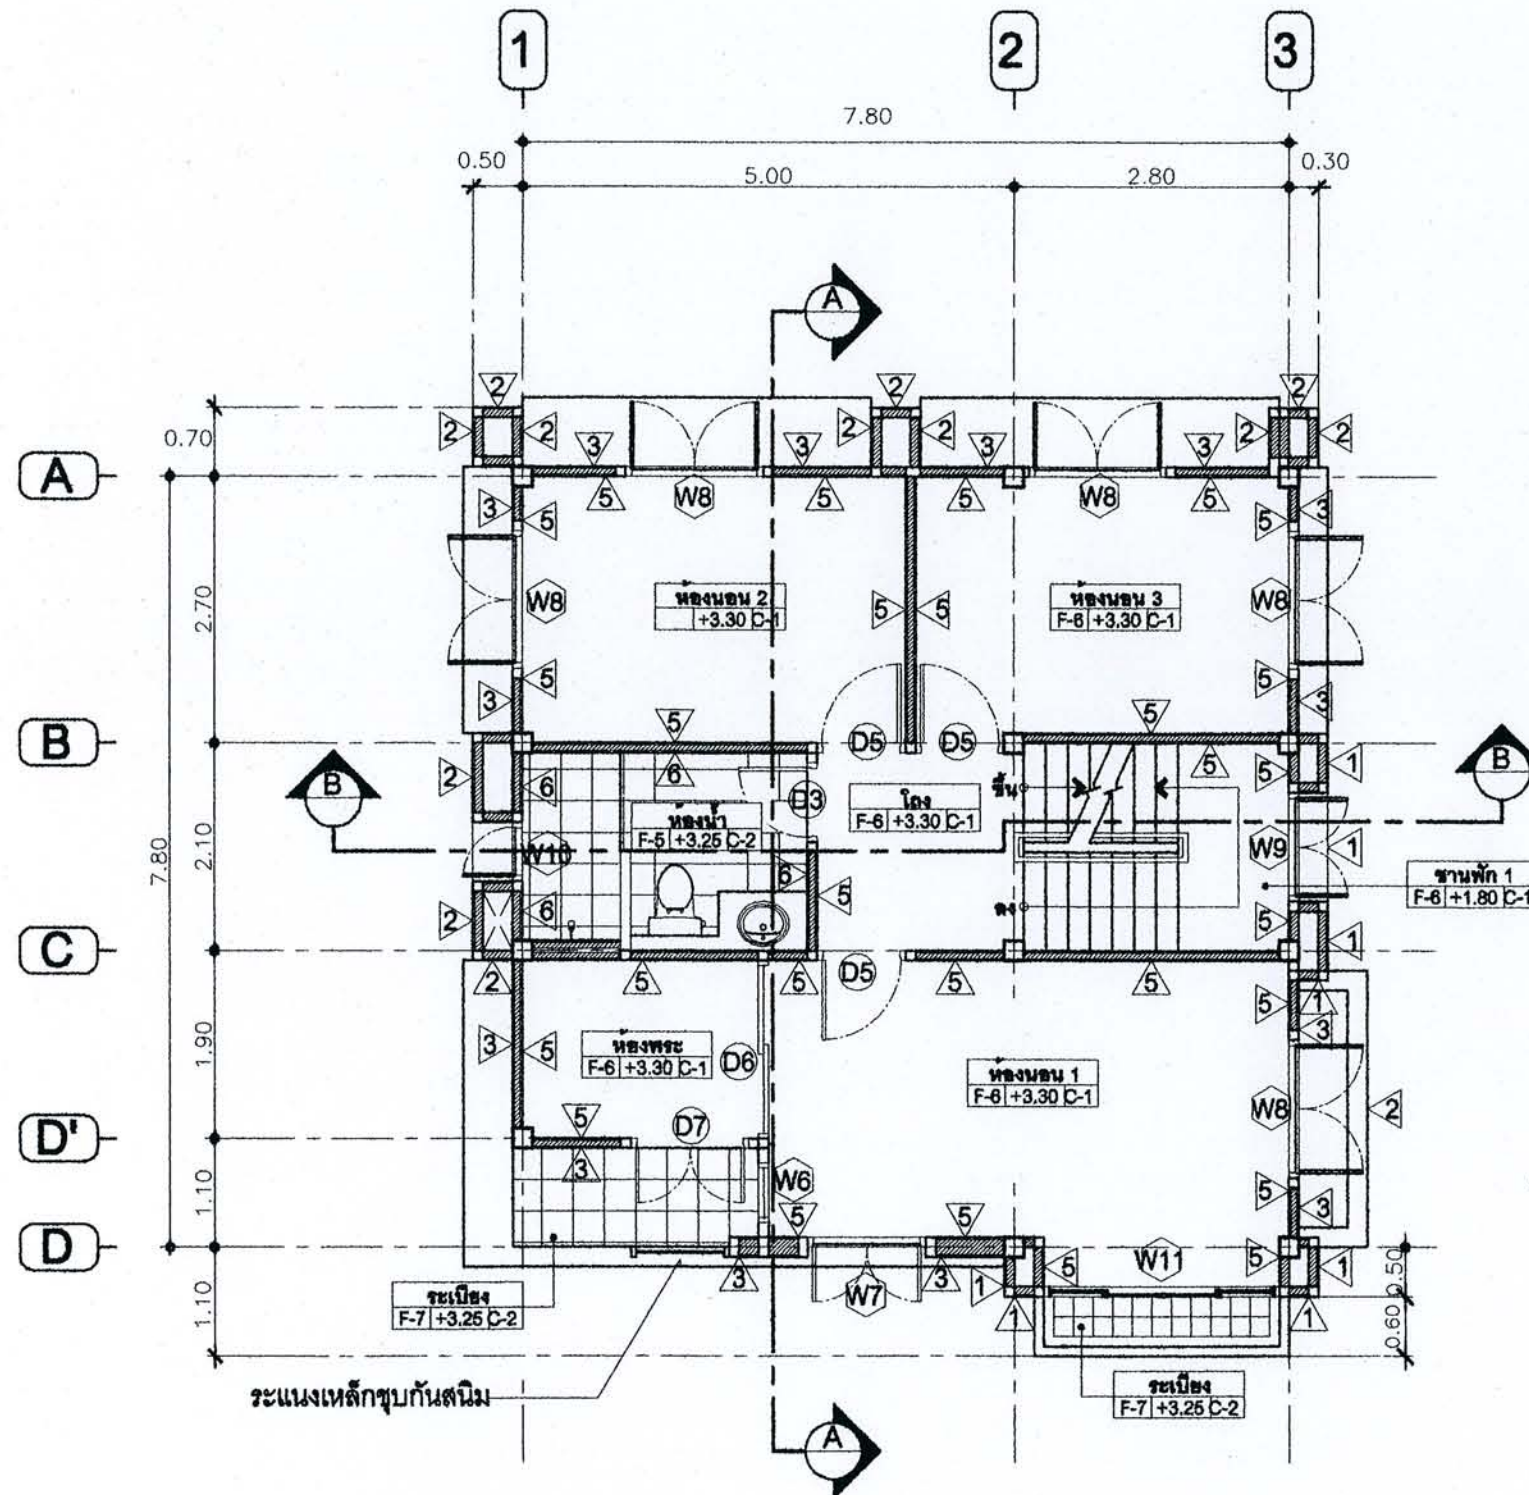

สัญลักษณ์ของรูปบ้าน

ผังพื้นที่ 2

มาตราส่วน

1:75



สำนักงาน
กรุงเทพมหานคร

โครงการ
แบบบ้านใช้เพื่อประชาชน

ตามนโยบาย

น.ร.สุจินต์ บริดลย์ ผู้อำนวยการ
นายแพทย์ เศรษฐ์ รอดูจาก
นายธีระชน มโนชัยกุล รองผู้อำนวยการ
นายพงษ์ศักดิ์ แสนจันทร์ ปลัด

ผู้อำนวยการสำนักงาน
นายจุมพล สันกาล
รองผู้อำนวยการสำนักงาน
นายวิฑิต เตชะประพันธ์
ผู้อำนวยการสำนักงาน
นายจุมพล สันกาล
หัวหน้ากลุ่มงานสถาปัตยกรรม
นายสินธุ์ บุญภิรักษ์
หัวหน้ากลุ่มงานวิศวกรรม
นายธีระยุทธ คงทรัพย์

สถาปนิก
นางสาวสุนทรภรณ์ กาญจนะ
วิศวกรโครงสร้าง
นายธีระชัย หินพิชัย
วิศวกรไฟฟ้า
นายคณิศร จิระเดช
วิศวกรสุขาภิบาล
นางสาวณัฏฐา สมน้อม
วิศวกรเครื่องกล

นายช่างเขียนแบบ
นายณัฐพงศ์ ณรงค์บุญชู

แบบ
028 บ้านกิตติพิทักษ์

หน้าของ

สถานที่

แบบแสดง
ผังพื้นที่ 3

มาตราส่วน 1:75

FILE : เลขที่


วันที่ 2553 A-06 06

ชนิดของแบบ

รวม

32


รายการแก้ไขแบบ

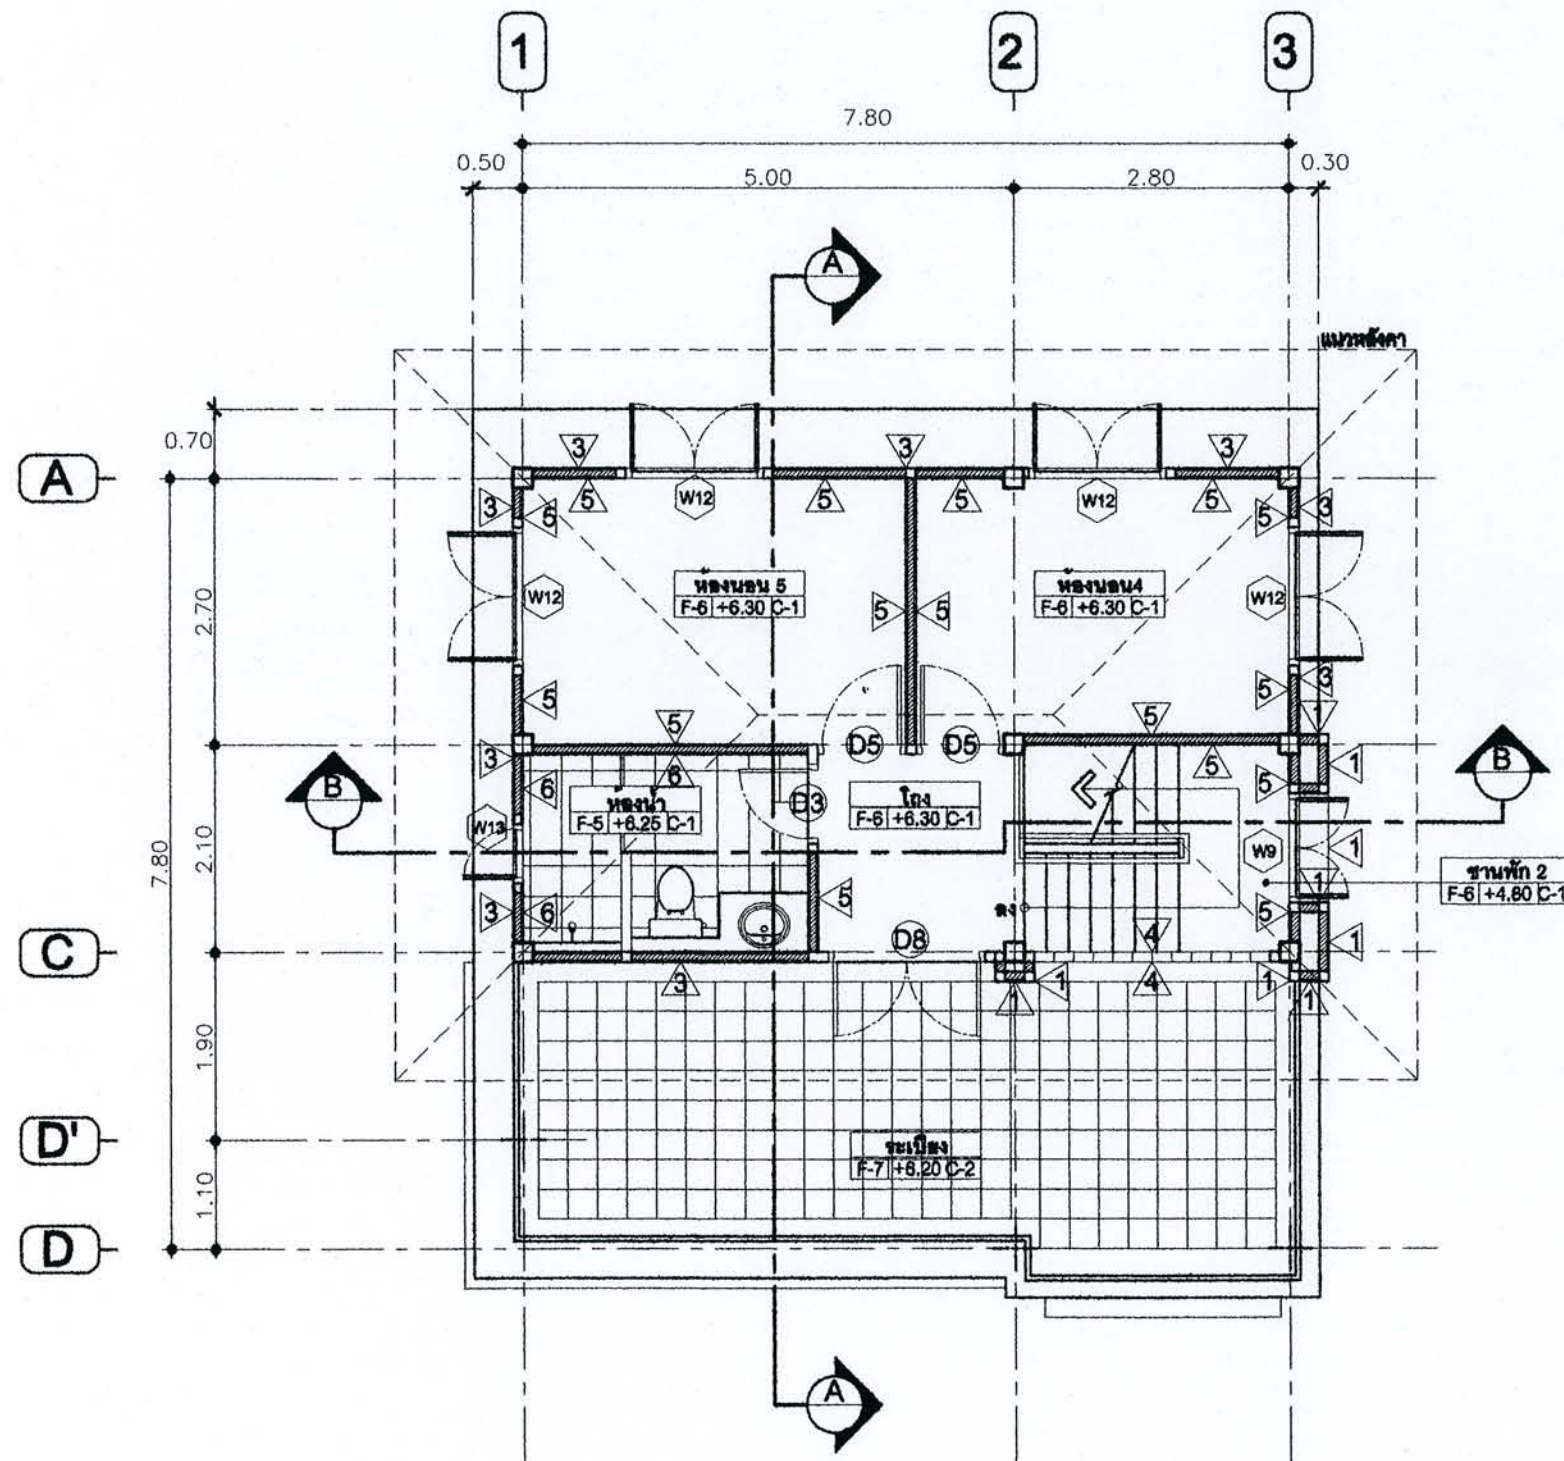

สัญลักษณ์เบื้องต้น

ผังพื้นที่ 3

มาตราส่วน 1:75

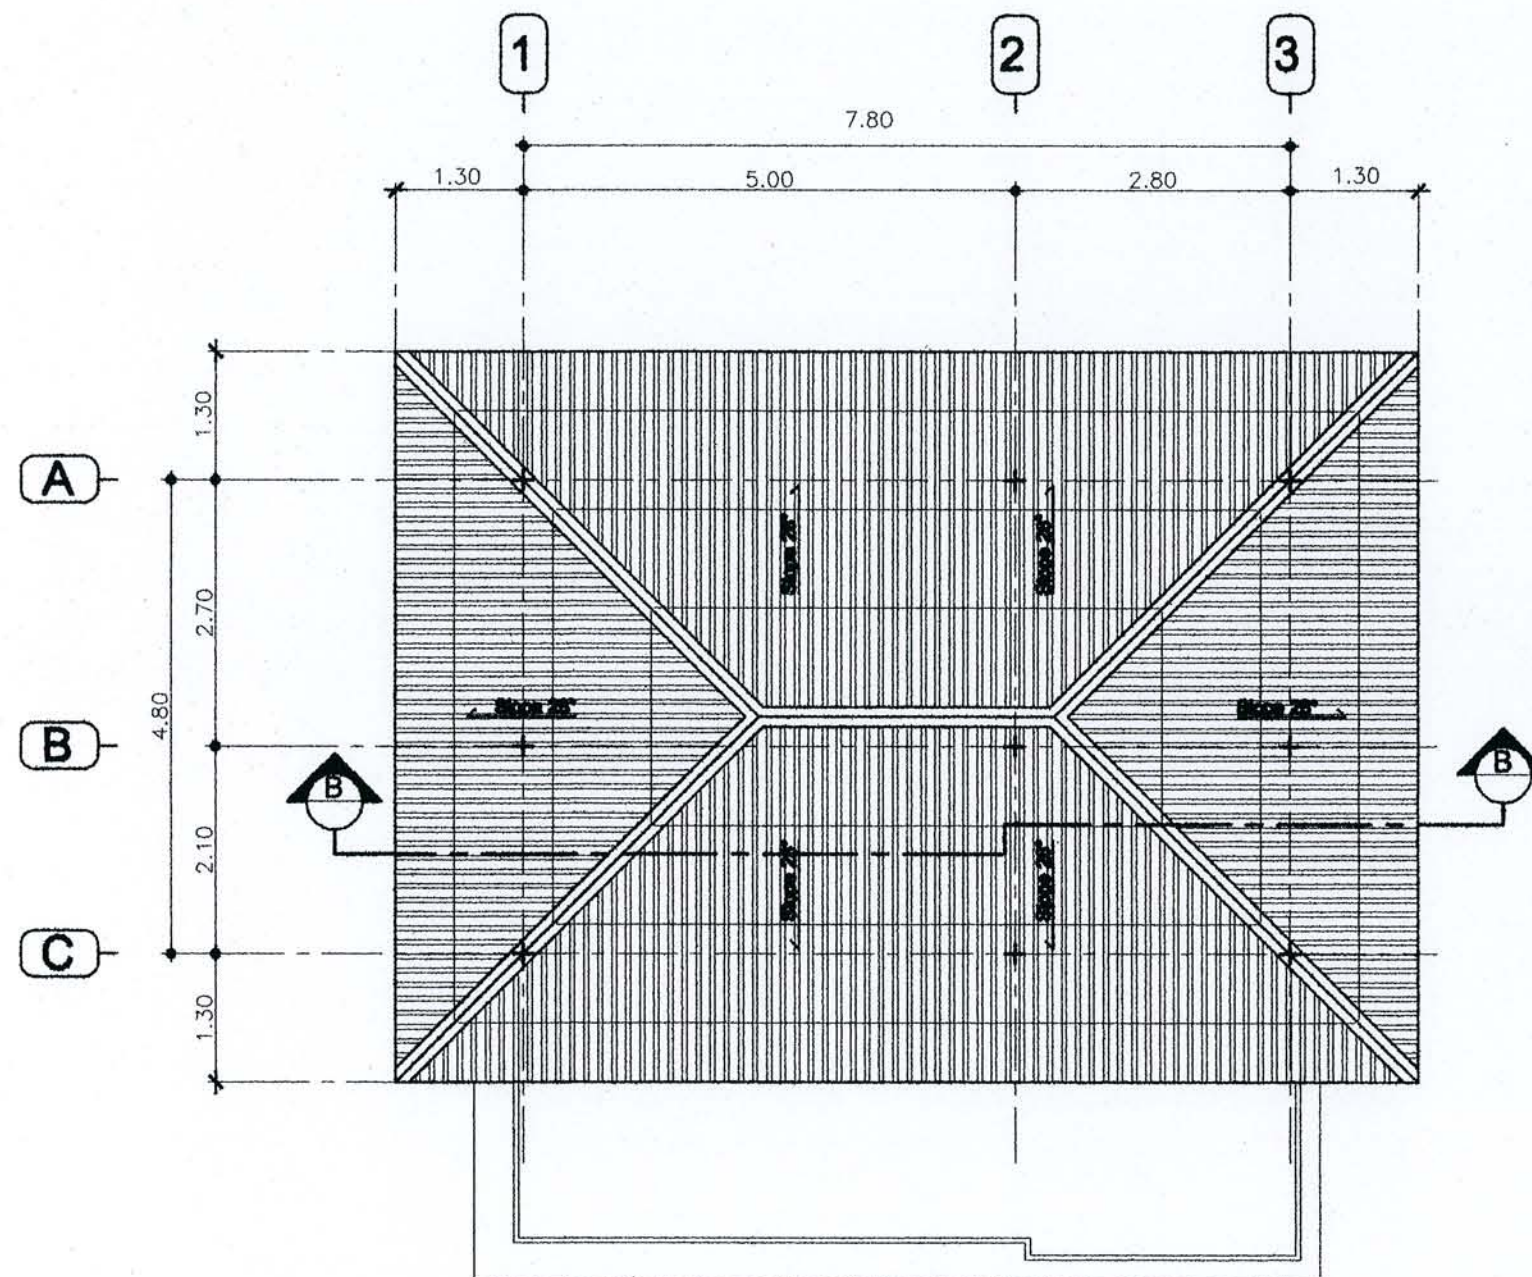

เอกสารนี้เป็นเอกสารของบริษัท



ผังหลังคา

มาตราส่วน 1:75



สำนักงานโยธา
กรุงเทพมหานคร

โครงการ
แบบบ้านชั้นเดียวประชาชน

ตามนโยบาย

น.ร.สุจินต์ ปิณฑะ ผู้ว่าฯกทม.
นายแพทย์ ประทีป ปิณฑะ รองผู้ว่าฯกทม.
นายธีระชน มโนวิมล ปิณฑะ รองผู้ว่าฯกทม.
นายพงศ์พิบูลย์ เสน่ห์สันต์ ปลัดฯกทม.

ผู้อำนวยการสำนักงานโยธา
นายจุมพล สันกาลาด
รองผู้อำนวยการสำนักงานโยธา
นายวิศักดิ์ เติมประพันธ์
ผู้อำนวยการสำนักงานออกแบบ
นายชัชวาลย์ สอนิคม
หัวหน้ากลุ่มงานสถาปัตยกรรม
นายสินธุ์ชัย บุญภิรักษ์
หัวหน้ากลุ่มงานวิศวกรรม
นายธีระยุทธ คงสวัสดิ์โยธา

สถาปนิก
นางสาวสุมนมัตย์ กาญจนะ
วิศวกรโครงสร้าง
นายจิรพันธ์ ชินชัย
วิศวกรไฟฟ้า
นายกิตติพงษ์ จิระนคร
วิศวกรสุขาภิบาล
นางสาวกมลจิรา สมพยอม
วิศวกรเครื่องกล

นายช่างเขียนแบบ
นายณัฐพงศ์ ณรงค์บุญชูทรัพย์

แบบ
028 บ้านกัลปพฤกษ์

เจ้าของ

สถานที่

แบบแสดง
ผังหลังคา

มาตราส่วน 1:75

FILE : เลขที่

วันที่ 25/05/2563 A-07 07

คิดค่า เป็นใบเสนอราคา

รวมค่า

32

รายการแก้ไขแบบ



สำนักงานโยธา
กรุงเทพมหานคร

โครงการ
แบบบ้านขึ้นเพื่อประชาชน

ตามนโยบาย

ม.ว.สุจินต์ บริหาร บัณฑิต
นายพรเทพ เศรษฐกิจ รองผู้ว่าฯ
นายธีรวัฒน์ นนทบุรี รองผู้ว่าฯ
นายพงศ์ศักดิ์ แสนสุว ปลัดฯ

ผู้อำนวยการสำนักงานโยธา
นายชุมพล สว่างกุล
รองผู้อำนวยการสำนักงานโยธา
นายวิศักดิ์ เดชประพันธ์
ผู้อำนวยการสำนักงานออกแบบ
นายสุรศักดิ์ สอนิยม
หัวหน้ากลุ่มงานสถาปัตยกรรม
นายพิษณุ บุญมี
หัวหน้ากลุ่มงานวิศวกรรม
นายธีรยุทธ คงสวัสดิ์

สถาปนิก
นางสาวสุเมธมาศ กาญจนะ
วิศวกรโครงสร้าง
นายจิรศักดิ์ พิมพ์ชัย
วิศวกรไฟฟ้า
นายกิตติพงษ์ จิระเศกการ
วิศวกรสุขาภิบาล
นางสาวณัฏฐา สอนิยม
วิศวกรเครื่องกล

นายช่างเขียนแบบ
นายณัฐพงศ์ ณรงค์บุญชู

แบบ
028 บ้านกัลปพฤกษ์

เจ้าของ


สถานที่

แบบแสดง
รูปด้าน 1

มาตราส่วน 1:75

FILE :
วันที่ 2553
คิดค้นปรับปรุงแบบ
เลขที่ A-08
แผ่นที่ 08
รวมแผ่น 32

รายการแก้ไขแบบ

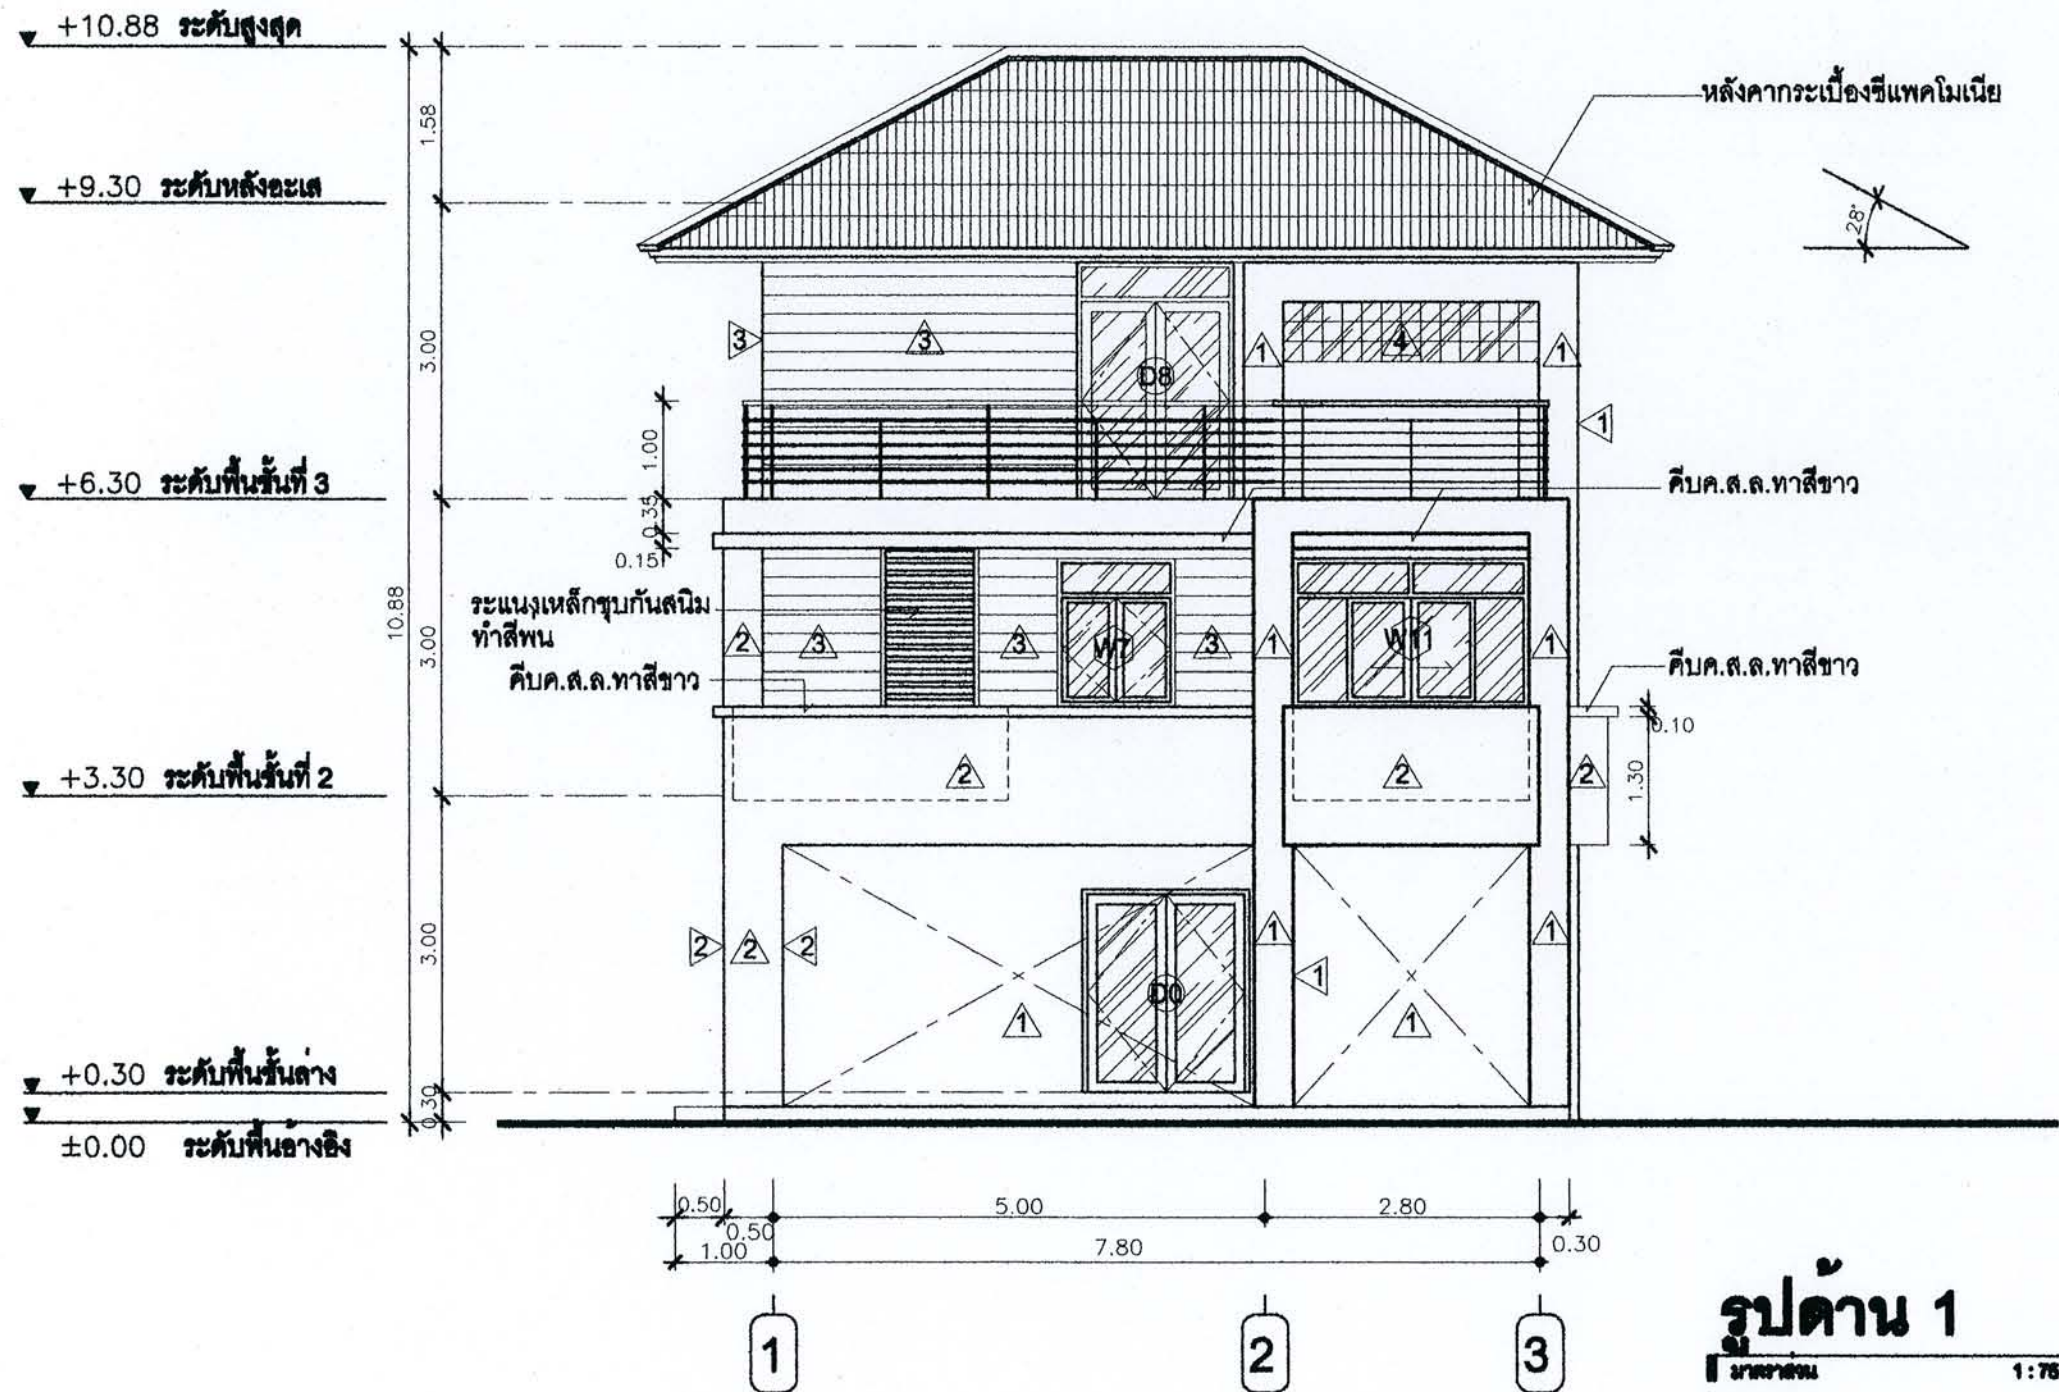

รูปด้าน 1

มาตราส่วน 1:75



สำนักงานโยธา
กรุงเทพมหานคร

โครงการ
แบบบ้านชั้นเดียวประชาชน

ตามนโยบาย

ม.ร.ว.สุขุมพันธุ์ บริพัตร ผู้ว่าฯ กทม.
นายชัชชาติ สิทธิพันธุ์ รองผู้ว่าฯ กทม.
นายธีรวัฒน์ นิลน้อย รองผู้ว่าฯ กทม.
นายพงษ์ศักดิ์ เตมียาภรณ์ ปลัดฯ กทม.

ผู้อำนวยการสำนักงานโยธา
นายจุมพล สันกาลาด
รองผู้อำนวยการสำนักงานโยธา
นายวิศักดิ์ เติมประพันธ์
ผู้อำนวยการสำนักงานออกแบบ
นายจตุรงค์ สันติชน
หัวหน้ากลุ่มงานสถาปัตยกรรม
นายสันติชัย บุญภิรักษ์
หัวหน้ากลุ่มงานวิศวกรรม
นายธีรวัฒน์ คณสรณ์ไชย

สถาปนิก
นางสาวสุมนมาลย์ กาญจนะ
วิศวกรโครงสร้าง
นายจิรศักดิ์ หินตติย์
วิศวกรไฟฟ้า
นายวิฑิตพงษ์ จิระเดชาก
วิศวกรสุขาภิบาล
นางสาวณณศิรา สมพยอม
วิศวกรเครื่องกล

นายจำเริญแบบ
นายณัฐพงศ์ ณรงค์บุญชูทรัพย์

แบบ
028 บ้านกัลปพฤกษ์

คำขอ


สถานที่

แบบแสดง
รูปด้าน 2

มาตราส่วน 1:75

FILE :	เลขที่	แผนที่
วันที่ 15 มิถุนายน 2553	A-09	09
ชนิดของบ้าน	รวมแผ่น	32

รายการแก้ไขแบบ

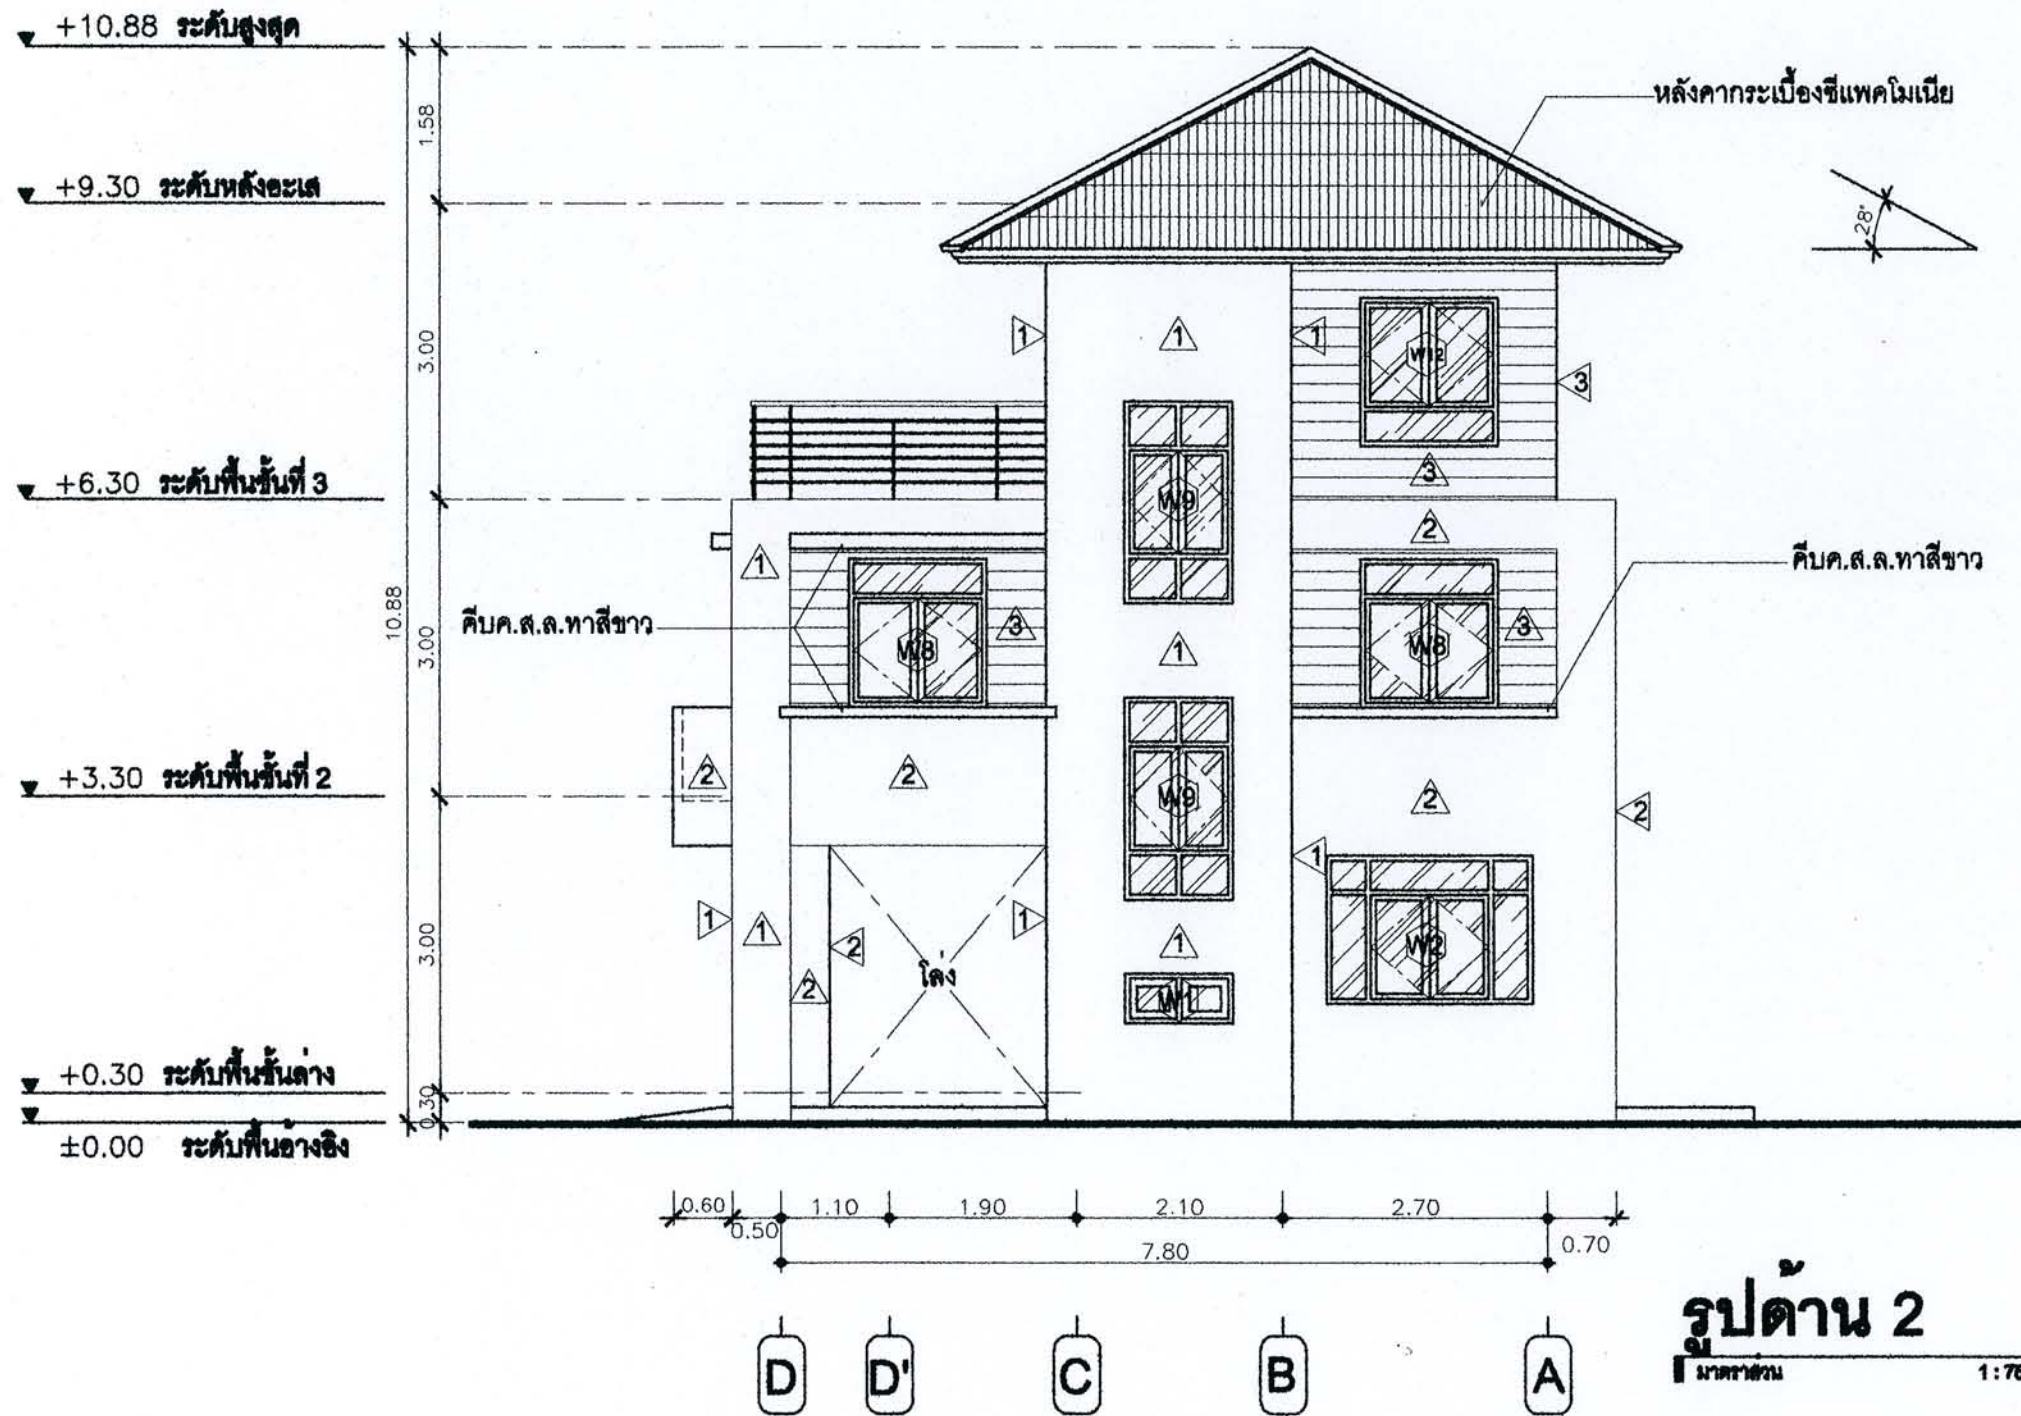



สำนักงานโยธา
กรุงเทพมหานคร

โครงการ
แบบบ้านขึ้นเพื่อประชาชน

ตามนโยบาย

น.ร.สุเมธพันธ์ บัณฑิต ผู้ว่าฯกทม.
นายแพทย์ เศรษฐกิจ รองผู้ว่าฯกทม.
นายธีระชน นิมะสินธุ์ รองผู้ว่าฯกทม.
นายพงศ์ศักดิ์ แสนสุทนต์ ปลัดฯกทม.

ผู้อำนวยการสำนักงานโยธา
นายชุมพล สันภาพ
รองผู้อำนวยการสำนักงานโยธา
นายศักดิ์ เกตุประพันธ์
ผู้อำนวยการสำนักงานออกแบบ
นายสุรศักดิ์ สันติธรรม
หัวหน้ากลุ่มงานสถาปัตยกรรม
นายสันติชัย บุญภิรักษ์
หัวหน้ากลุ่มงานวิศวกรรม
นายธีระยุทธ คงศรีชัย

สถาปนิก
นางสาวสุเมธมณีย์ กาญจนะ
วิศวกร โครงสร้าง
นายศิริพงษ์ ชินสิทธิ์
วิศวกร ไฟฟ้า
นายศักดิ์พงษ์ จิระเดชากร
วิศวกร สุขาภิบาล
นางสาวณณชิตา สมนอน
วิศวกร เครื่องกล

นายช่างเขียนแบบ
นายณัฐพงศ์ นวรัตน์สุทนต์

แบบ
028 บ้านกัลปพฤกษ์


เจ้าของ
สถานที่

แบบแสดง
รูปบ้าน 3

มาตราส่วน 1:75

FILE : เลขที่ 10
วันที่ 10
ปี 2553
ชุดแบบ 32

รายการแก้ไขแบบ

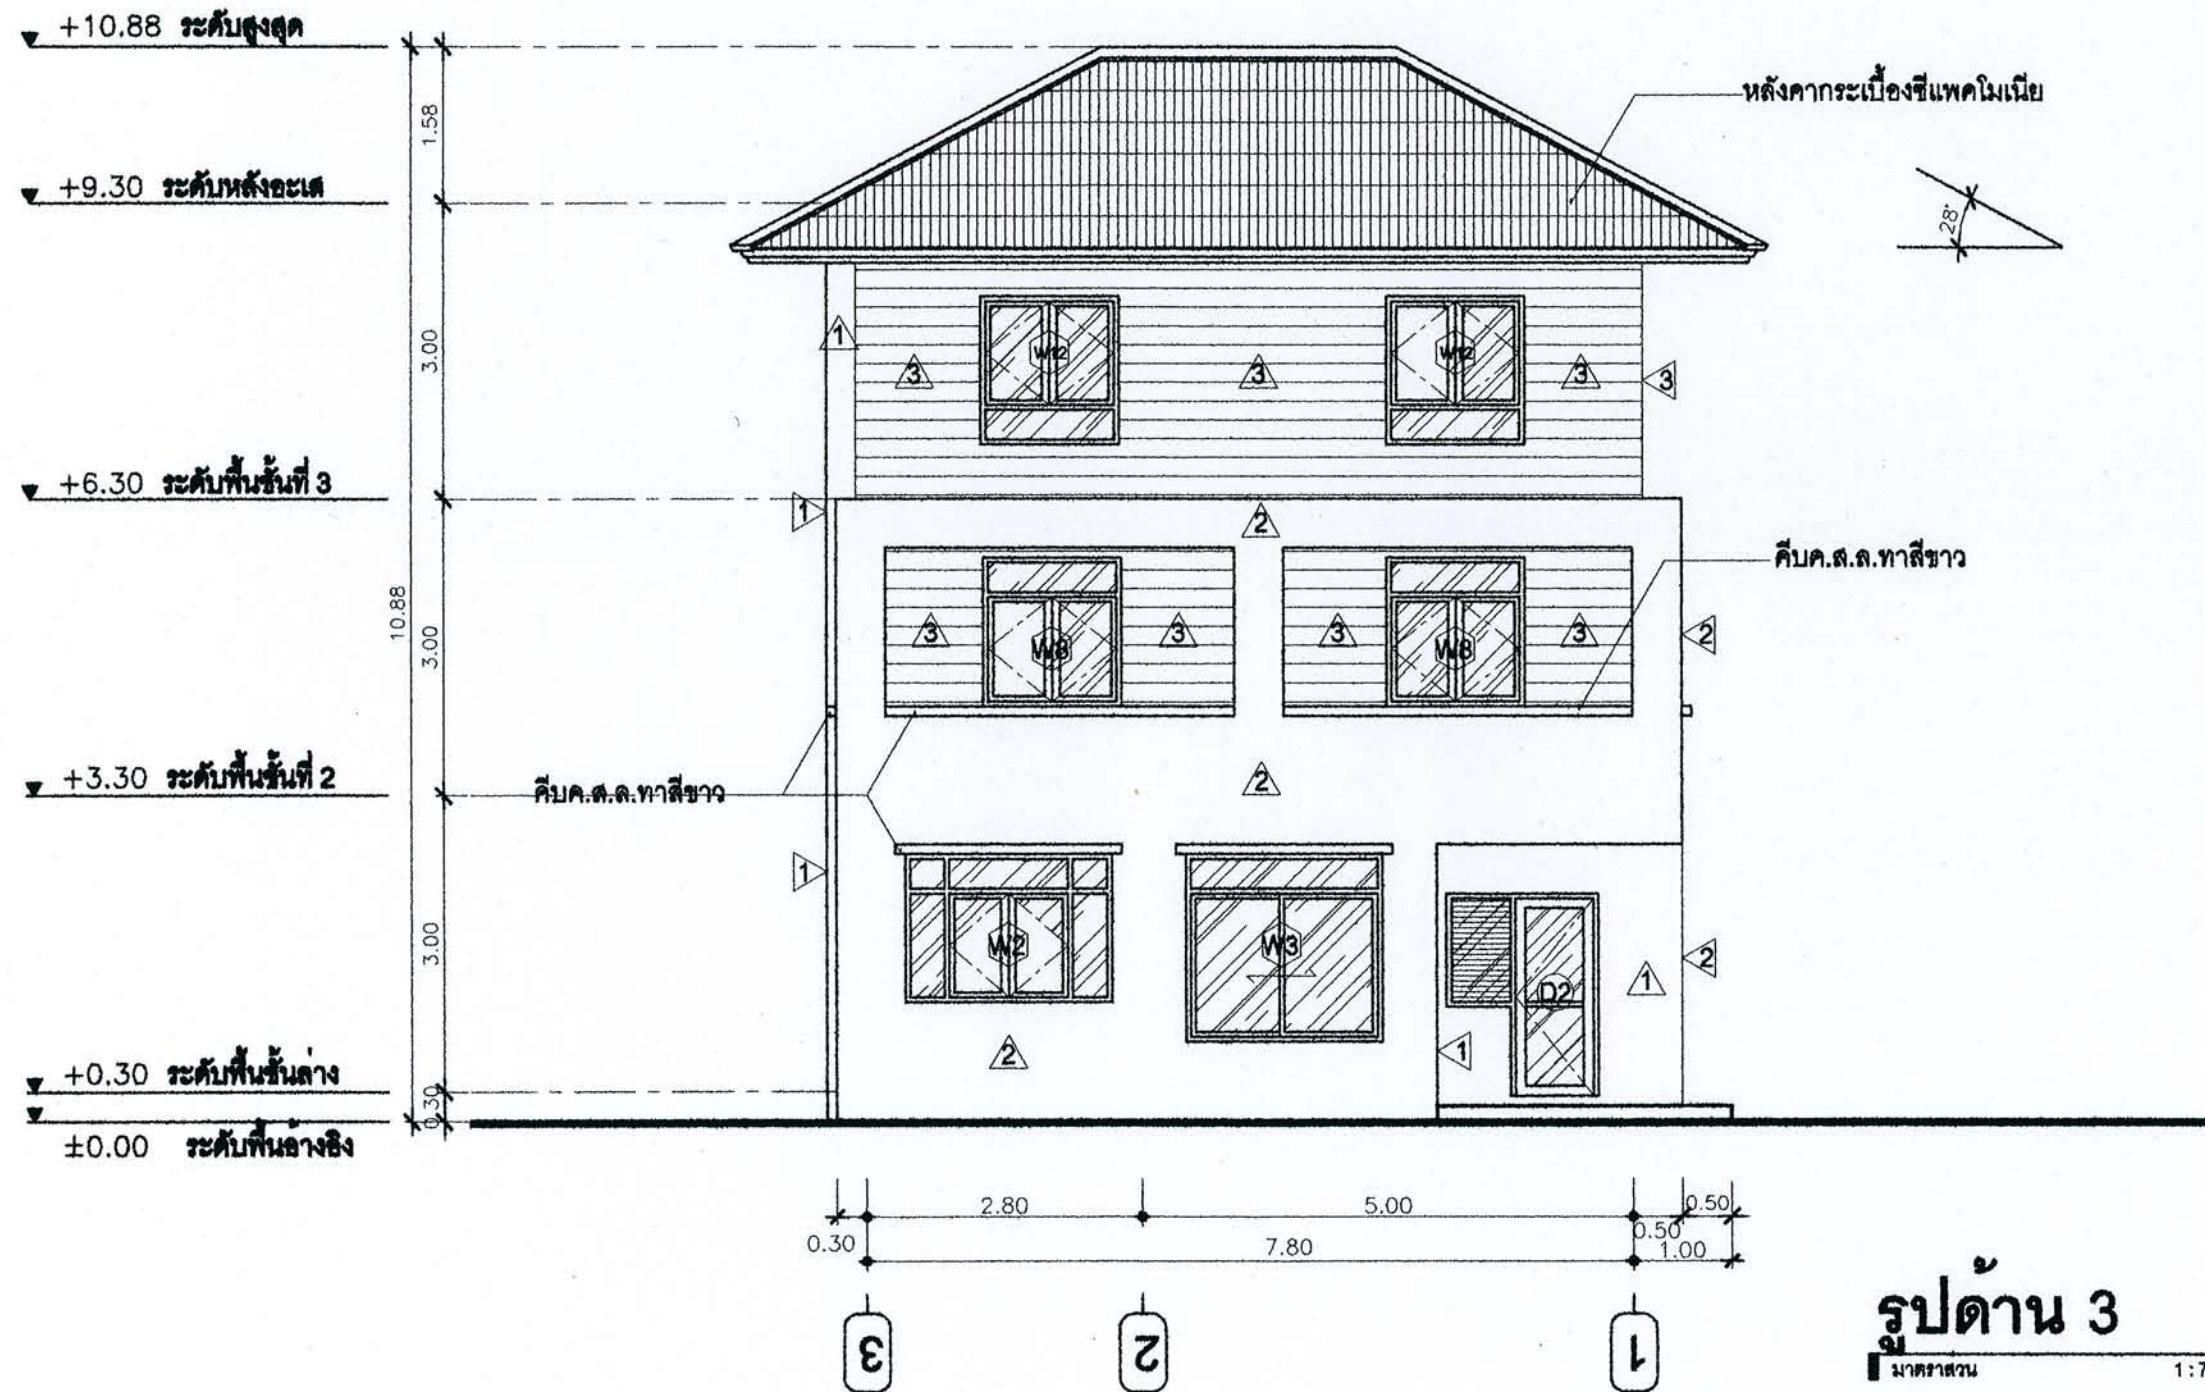

รูปด้าน 3

มาตราส่วน

1:75



สำนักงานโยธา
กรุงเทพมหานคร

โครงการ
แบบบ้านยังชีพประชาชน

ตามนโยบาย

น.ร.สุเมสันต์ ปรีดิศร ผู้ว่าฯกทม.
นายแพทย์ เสงี่ยมพงษ์ รองผู้ว่าฯกทม.
นายธีระชน มโนชัยปณัฏธ์ รองผู้ว่าฯกทม.
นายพงษ์ศักดิ์ เตมียาภรณ์ ปลัดฯกทม.

ผู้อำนวยการสำนักงานโยธา
นายจุมพล ตันภาพ
รองผู้อำนวยการสำนักงานโยธา
นายวิศักดิ์ เตชะประพันธ์
ผู้อำนวยการสำนักงานออกแบบ
นายจรูญ สมนิยม
หัวหน้ากลุ่มงานสถาปัตยกรรม
นายสินธุ์ บุญปักษ์
หัวหน้ากลุ่มงานวิศวกรรม
นายธีระยุทธ คงสวัสดิ์ไชย

สถาปนิก
นางสาวรุ่งนภมณี กาญจน
วิศวกรโครงสร้าง
นายศิริพงษ์ พิมพ์ชัย
วิศวกรไฟฟ้า
นายกิตติพงษ์ จิระเดชาก
วิศวกรสุขาภิบาล
นางสาวณณชิตา สมภอม
วิศวกรเครื่องกล

นายช่างเขียนแบบ
นายณัฐพงศ์ ณรงค์บุญชูทรัพย์

แบบ
028 บ้านกิลปพฤกษ์

เจ้าของ

สถานที่

แบบแสดง
รูปบ้าน 4


มาตราส่วน 1:75

FILE : เลขที่ 11

วันที่ 2553 11

คัดลอกเป็นรูปแบบ รวมหน้า 32

รายการแก้ไขแบบ

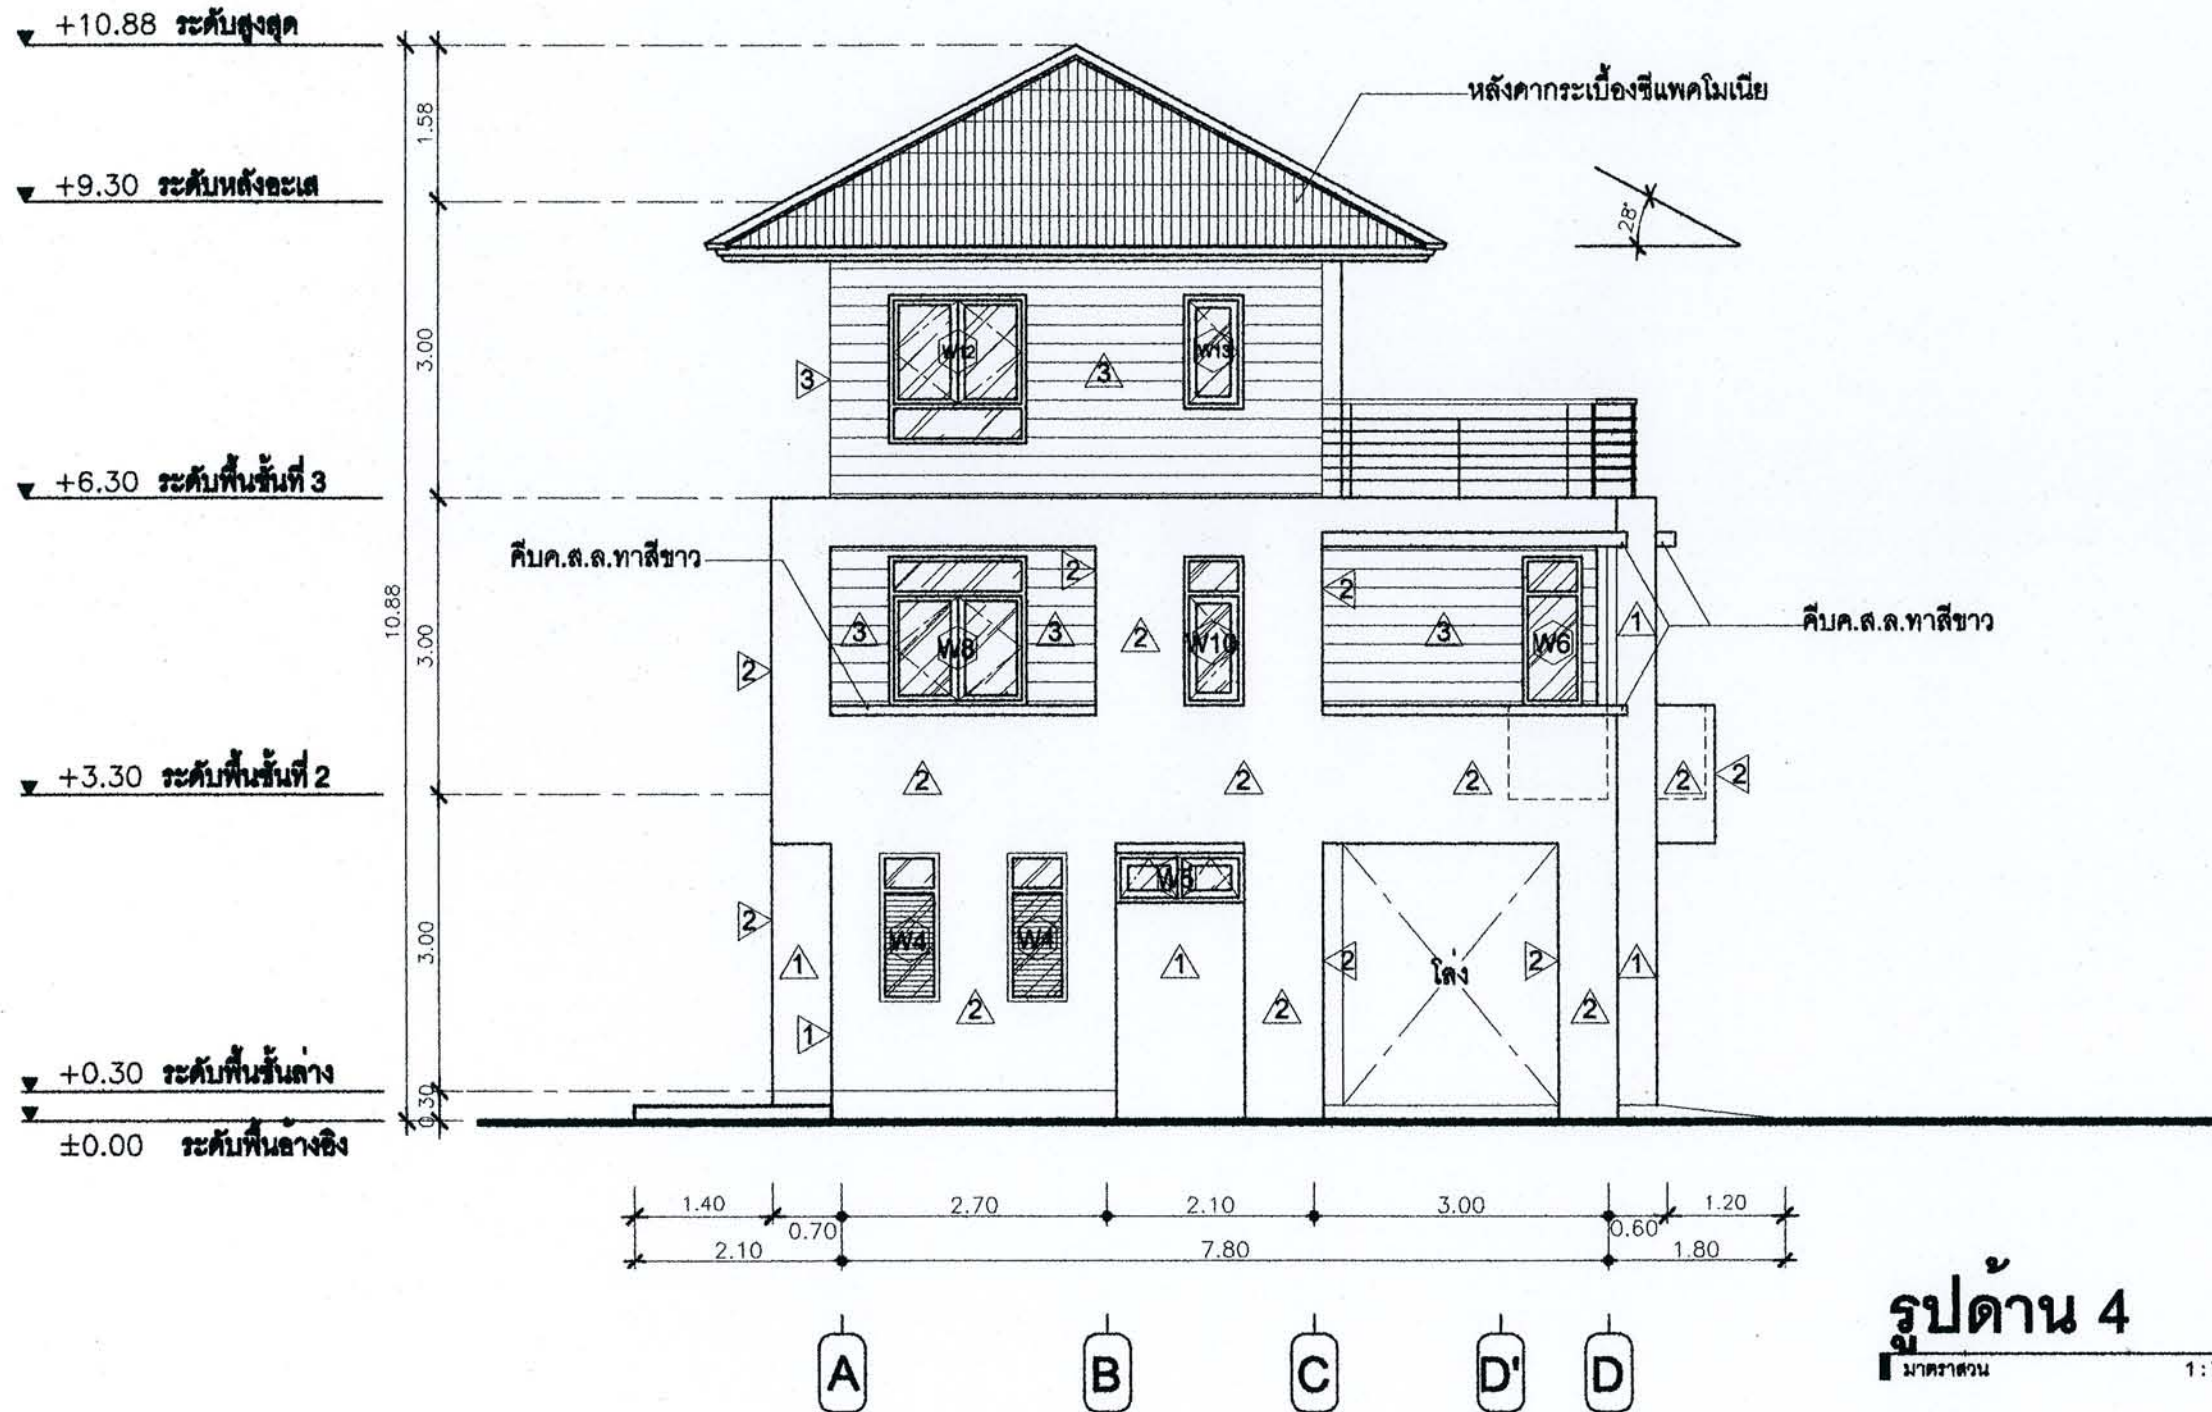

รูปด้าน 4

มาตราส่วน 1:75



สำนักงานโยธา
กรุงเทพมหานคร

โครงการ
แบบบ้านยืมเพื่อประชาชน

ตามนโยบาย

นางจุฬารัตน์ ธีรภัทร ผู้อำนวยการ
นายแพทย์ ประทีป ธีระโกศล รองผู้อำนวยการ
นายธีระชน มโนชัยพิบูลย์ รองผู้อำนวยการ
นายพงศ์ศักดิ์ เตมียาดี ปลัดสำนัก

ผู้อำนวยการสำนักงานโยธา
นายบุญทนต์ ตันภักดี
รองผู้อำนวยการสำนักงานโยธา
นายศักดิ์สิทธิ์ เตมียาดี
ผู้อำนวยการสำนักงานออกแบบ
นายสุวิทย์ สมชัย
หัวหน้ากลุ่มงานสถาปัตยกรรม
นายสุวิทย์ บุญภิรักษ์
หัวหน้ากลุ่มงานวิศวกรรม
นายธีระยุทธ คงทรัพย์โยธา

สถาปนิก
นางสาวสุนทรภรณ์ กาญจน
วิศวกรโครงสร้าง
นายศิริพิชัย ชินชัย
วิศวกรไฟฟ้า
นายวิฑิตพงษ์ จิระนคร
วิศวกรสุขาภิบาล
นางสาวกมลทิศา สมพยอม
วิศวกรเครื่องกล

นายช่างเขียนแบบ
นายณัฐพงศ์ ณรงค์บุญชู

แบบ
028 บ้านกัลปพฤกษ์

เจ้าของ


สถานที่

แบบแสดง
รูปตัด A - A

มาตราส่วน 1:75

FILE :
วันที่ 25/04/2563
ชุดแบบ 1/1
แผ่นที่ 12
รวม 32

รายการแก้ไขแบบ

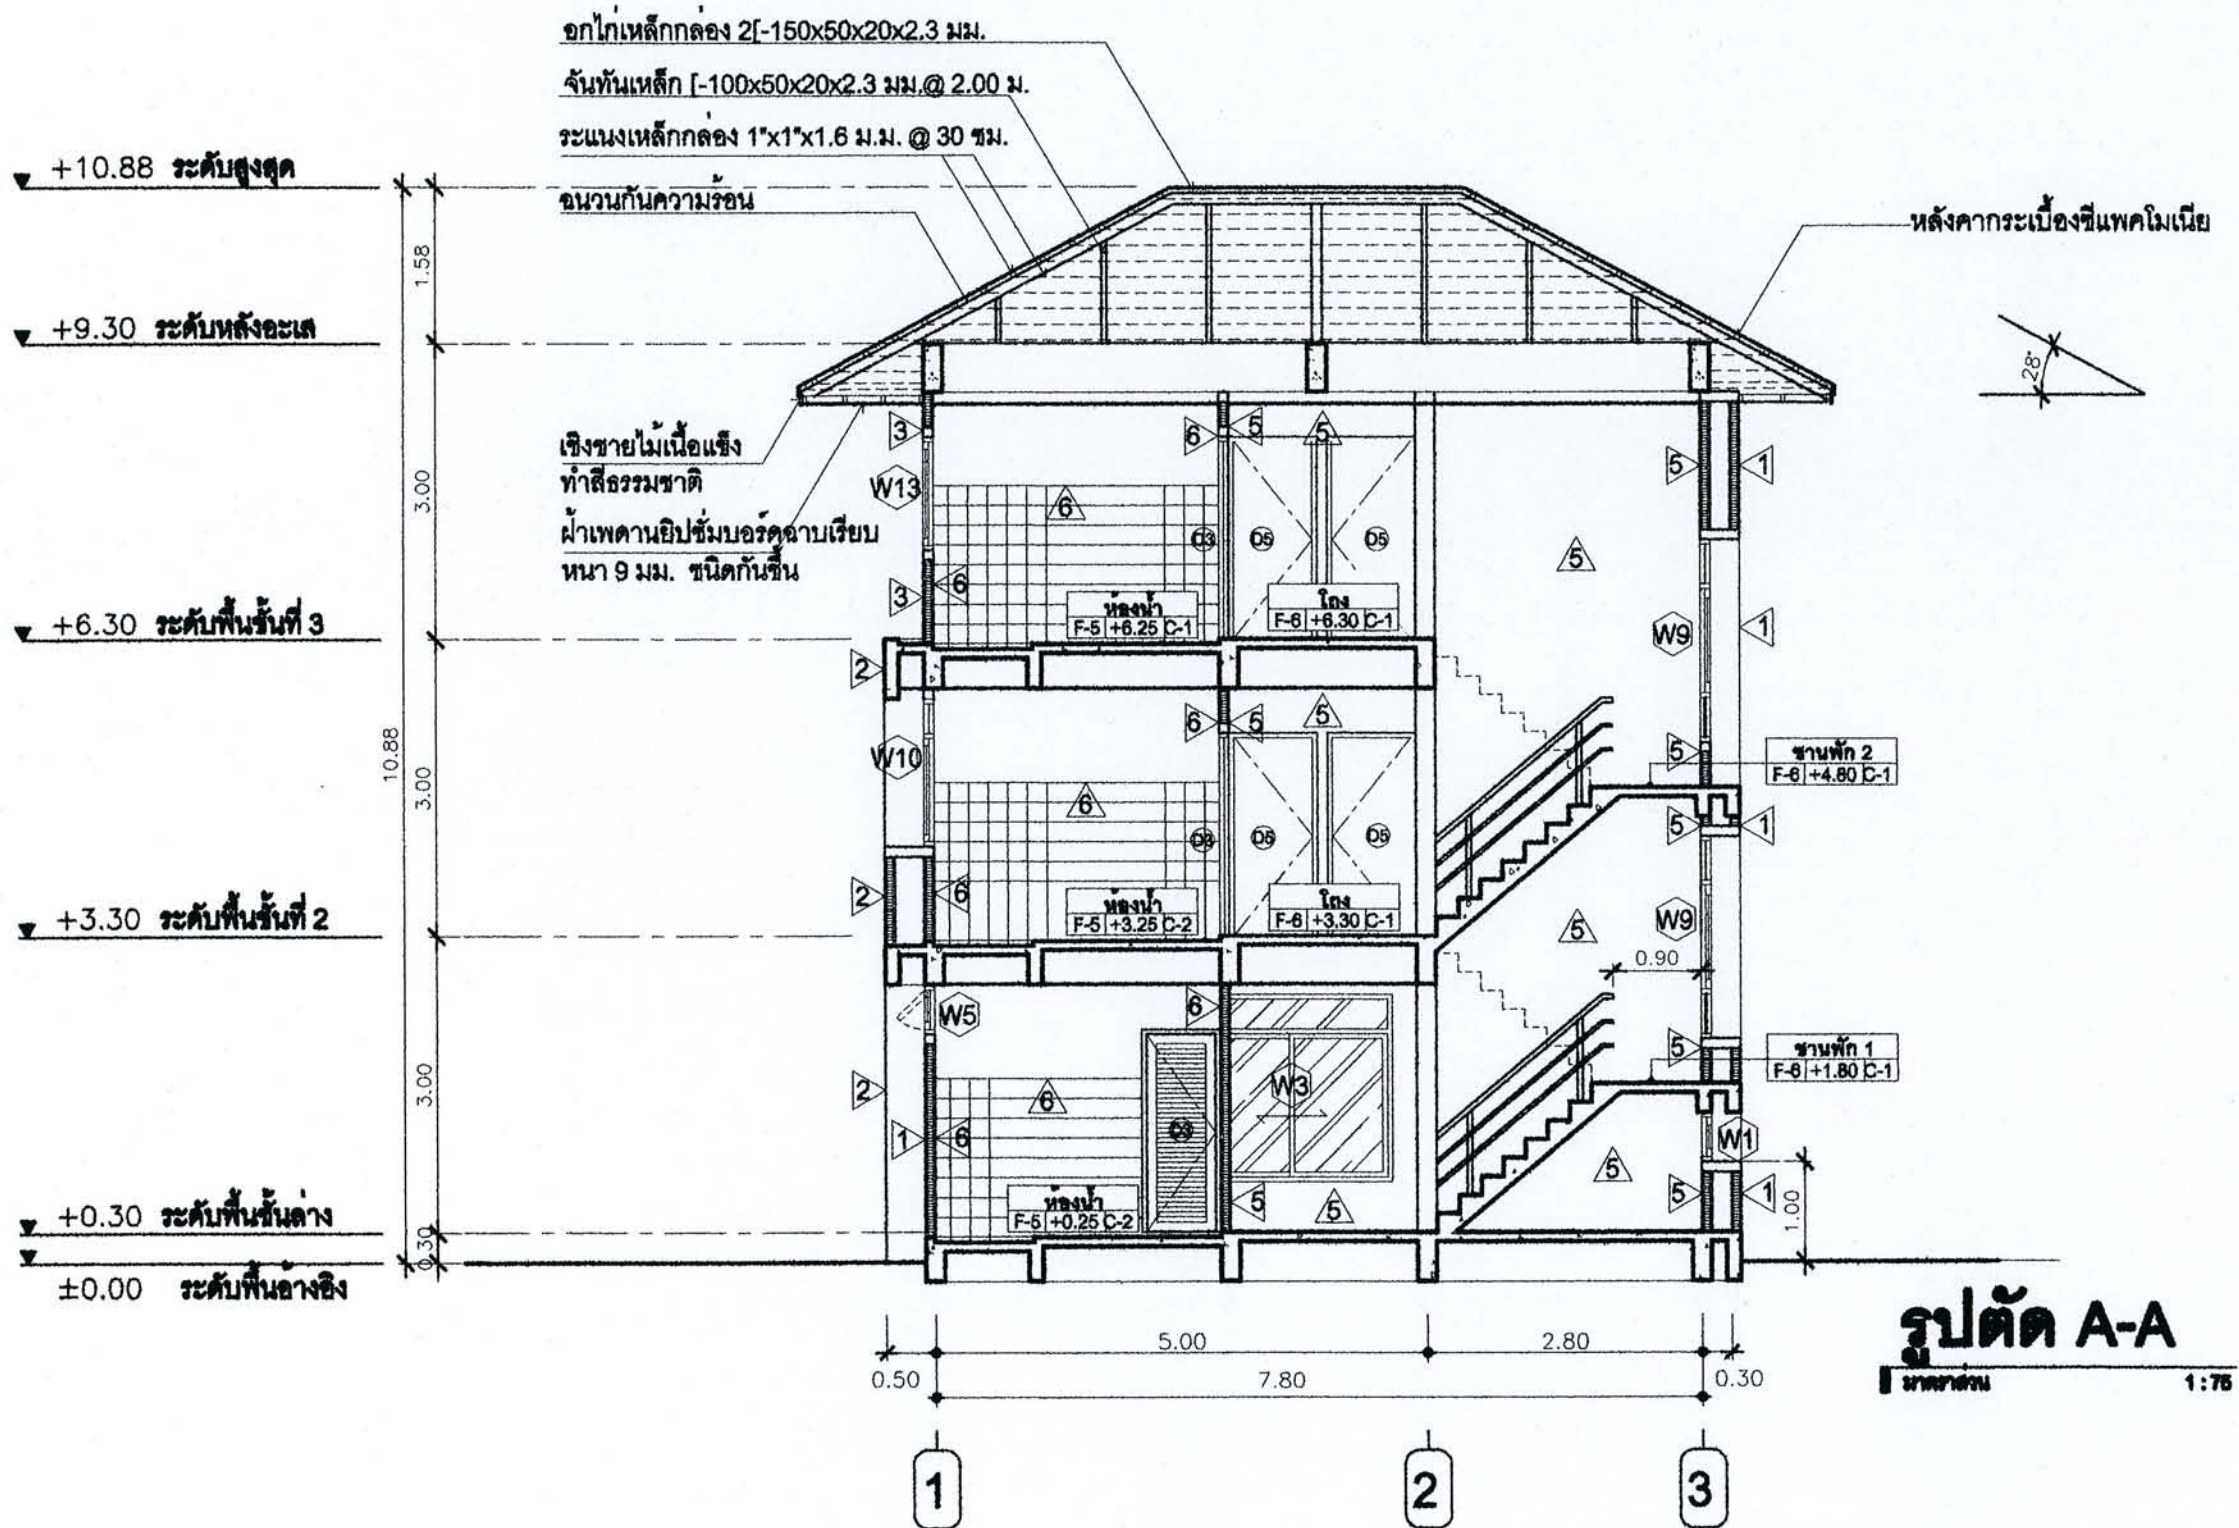



สำนักงานโยธา
กรุงเทพมหานคร

โครงการ
แบบบ้านขึ้นเพื่อประชาชน

ตามนโยบาย

น.ร.สุจินต์ ปิณฑะ ผู้ว่าฯกทม.
นายพรเทพ เศรษฐ์ รอ.ผู้ว่าฯกทม.
นายธีระชน มโนวิมลรัตน์ รอ.ผู้ว่าฯกทม.
นายพงษ์ศักดิ์ แสนรัตน์ ปลัดฯกทม.

ผู้อำนวยการสำนักงานโยธา
นายจุฑามาศ สันภาพ
รองผู้อำนวยการสำนักงานโยธา
นายวิศักดิ์ เป็ดโพธิ์
ผู้อำนวยการสำนักงานออกแบบ
นายจตุรงค์ สมชัย
หัวหน้ากลุ่มงานสถาปัตยกรรม
นายสันติชัย บุญปักษ์
หัวหน้ากลุ่มงานวิศวกรรม
นายธีระยุทธ คงสวัสดิ์

สถาปนิก
นางสาวสุนทรภรณ์ กาญจนะ
วิศวกรโครงสร้าง
นายธีรสิทธิ์ ชินชัย
วิศวกรไฟฟ้า
นายศักดิ์พงษ์ จิระนคร
วิศวกรสุขาภิบาล
นางสาวมนสิศา สมพงษ์
วิศวกรเครื่องกล

นายช่างเขียนแบบ
นายณัฐพงศ์ ณรงค์บุญสุทธิ์

แบบ
028 บ้านกิลปพฤกษ์


เจ้าของ
สถานที่

แบบแสดง
รูปตัด B - B

มาตราส่วน 1:75

FILE : เลขที่ 13
วันที่ 2553
ชนิดเอกสาร 32

รายการแก้ไขแบบ

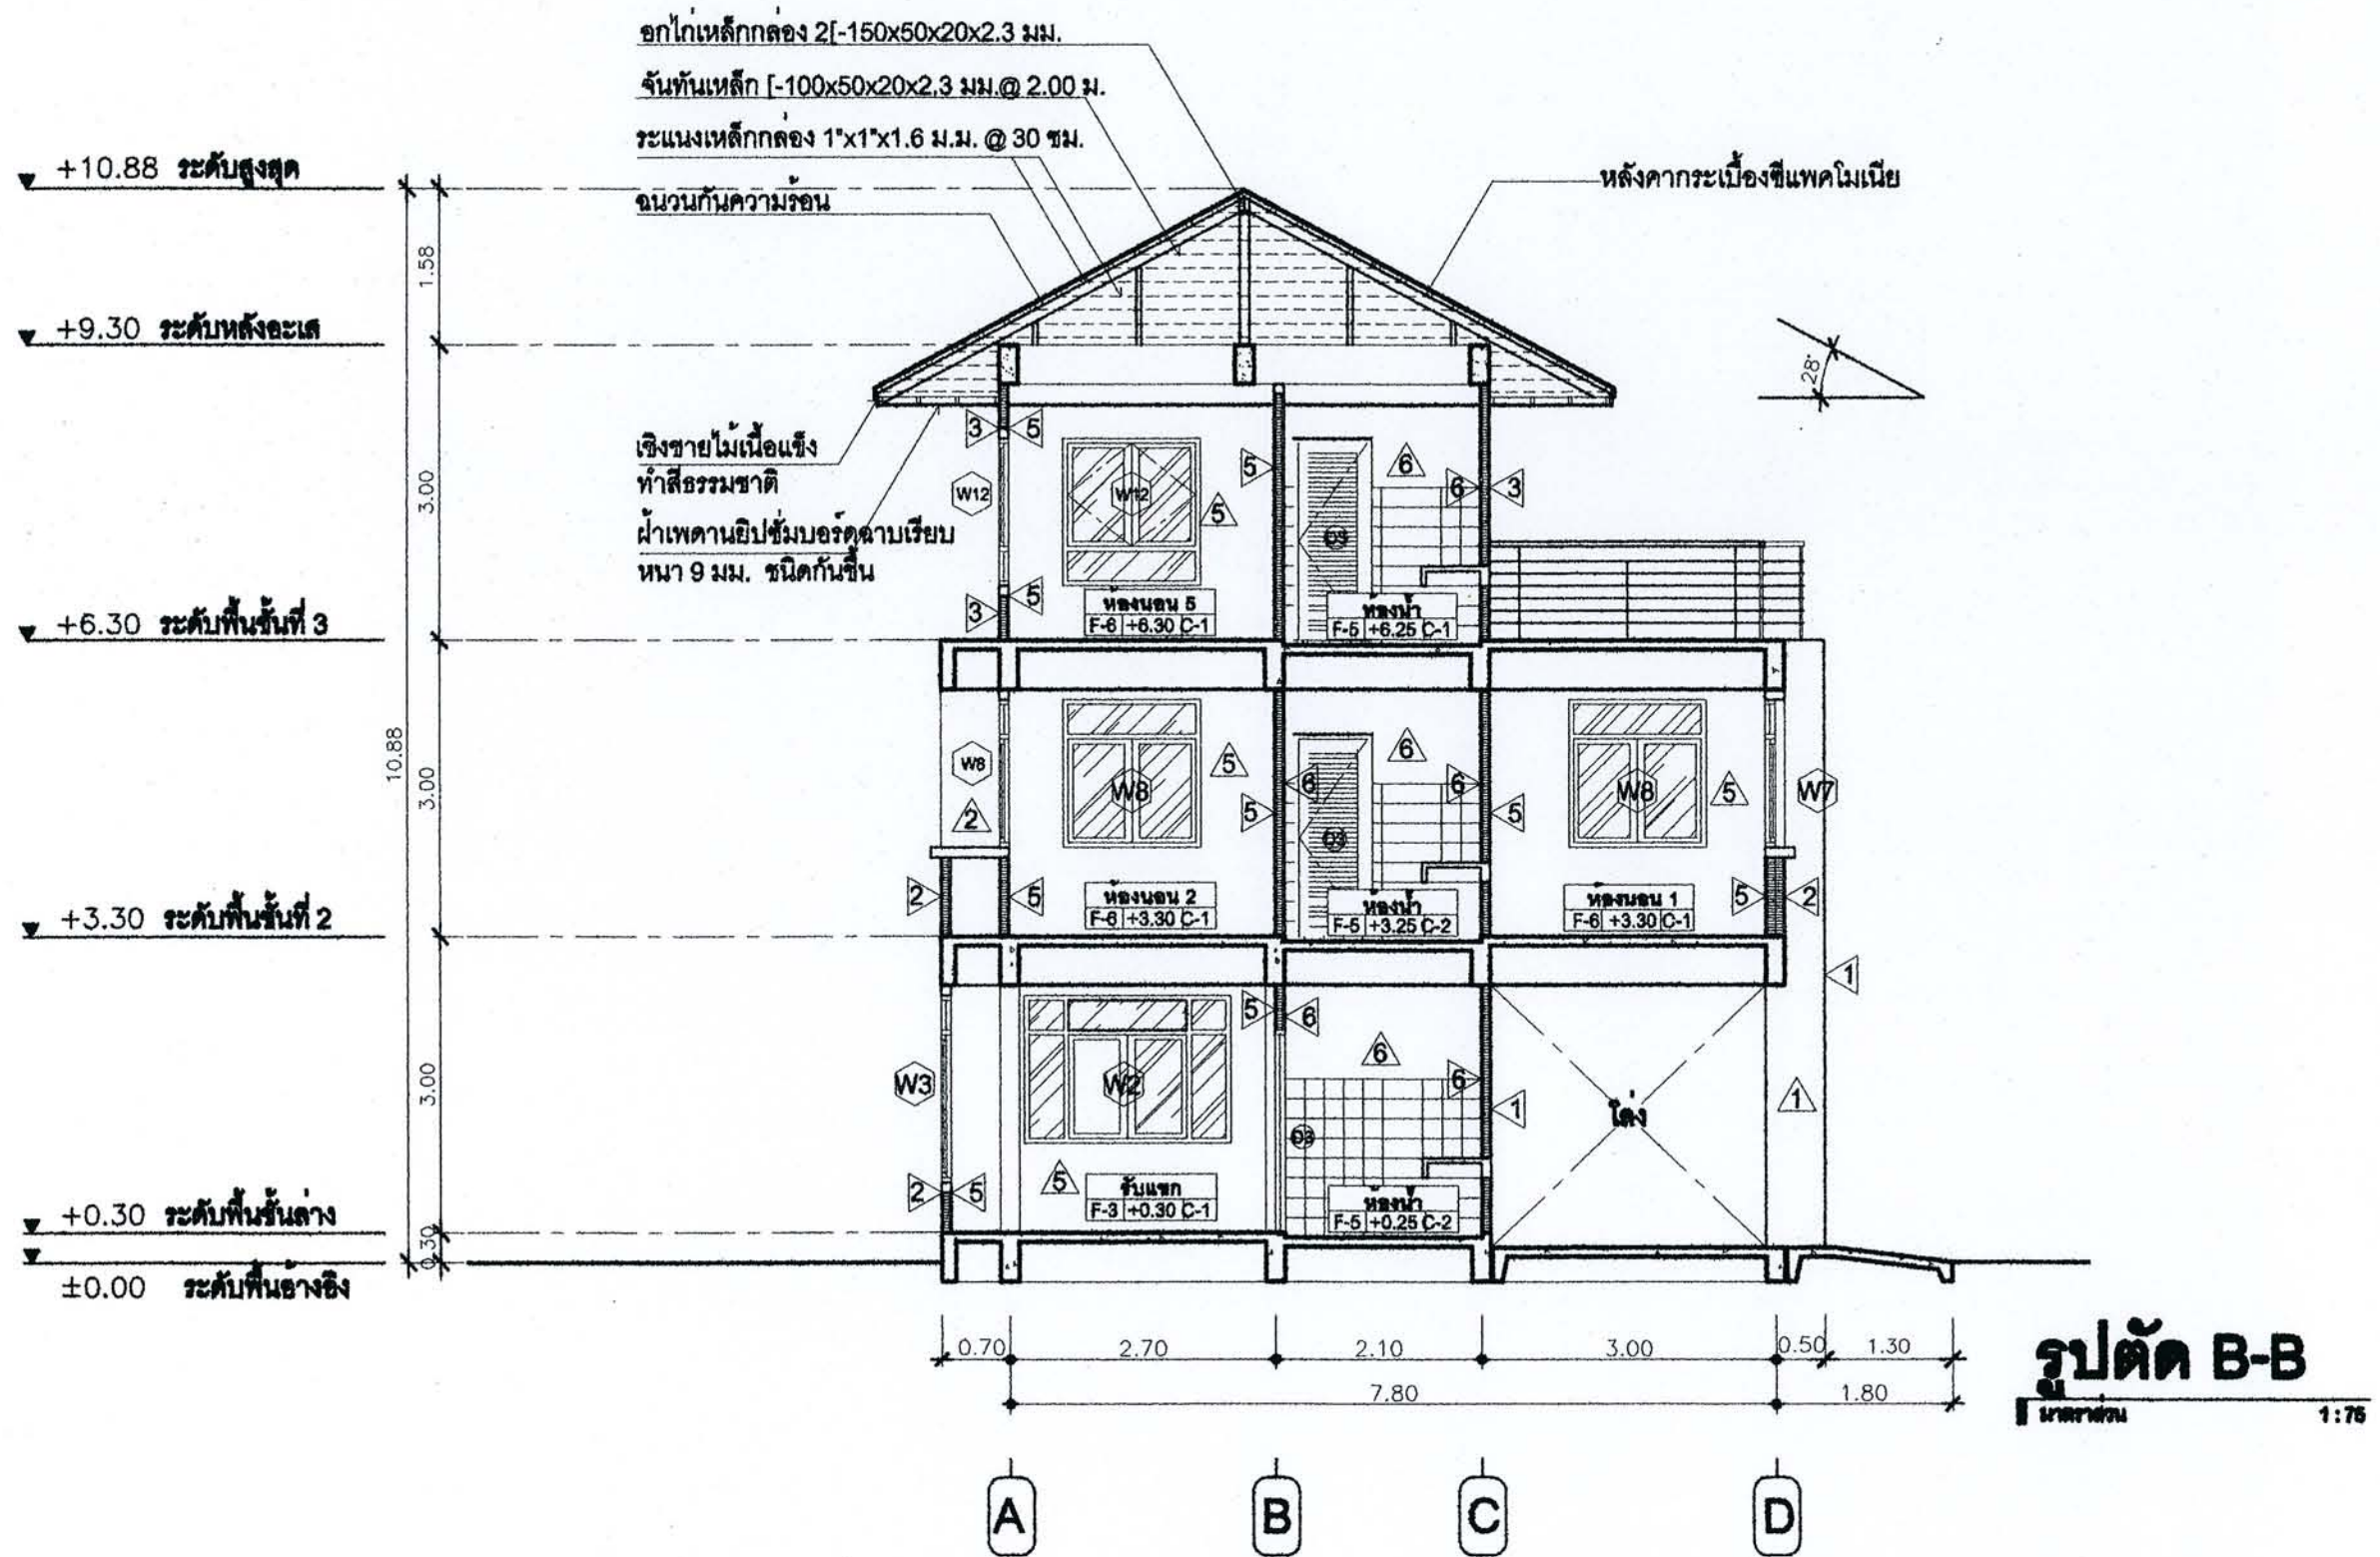



สำนักงานโยธา
กรุงเทพมหานคร

โครงการ
แบบบ้านขี้เหล็กประชาชน

ตามนโยบาย
ม.ร.ว.สุขุมพันธุ์ บริพัตร ผู้ว่าฯ กทม.
นายพรเทพ เศรษฐินทุเรศ รองผู้ว่าฯ กทม.
นายธีระวัฒน์ มโนลิตะกุล รองผู้ว่าฯ กทม.
นายพงศ์ศักดิ์ แสนสุทนต์ ปลัดฯ กทม.

ผู้อำนวยการสำนักงานโยธา
นายจุมพล สันภาพ
รองผู้อำนวยการสำนักงานโยธา
นายวิศักดิ์ เศรษฐินทุเรศ
ผู้อำนวยการสำนักงานออกแบบ
นายจตุรงค์ สันติธรรม
หัวหน้ากลุ่มงานสถาปัตยกรรม
นายสันติชัย บุญภิรักษ์
หัวหน้ากลุ่มงานวิศวกรรม
นายธีระยุทธ คงสวัสดิ์เสถียร

สถาปนิก
นางสาวสุมนมาลย์ กาญจนะ
วิศวกรโครงสร้าง
นายจิรศักดิ์ พิมพ์ชัย
วิศวกรไฟฟ้า
นายกิตติพงษ์ จิระเดชากร
วิศวกรสุขาภิบาล
นางสาวกมลทิศา สมพงษ์
วิศวกรเครื่องกล

นายช่างเขียนแบบ
นายณัฐพงศ์ ณรงค์บุญชูพิทักษ์

แบบ
028 บ้านกัลปพฤกษ์

เจ้าของ


สถานที่

แบบแสดง
แบบขยายผังบันได

มาตราส่วน 1:50

FILE :	เลขที่	แผ่นที่
วันที่ อนุมัติ 2553	A-14	14
คัดลอกไปทำแบบ	รวมแผ่น	32

รายการแนบ

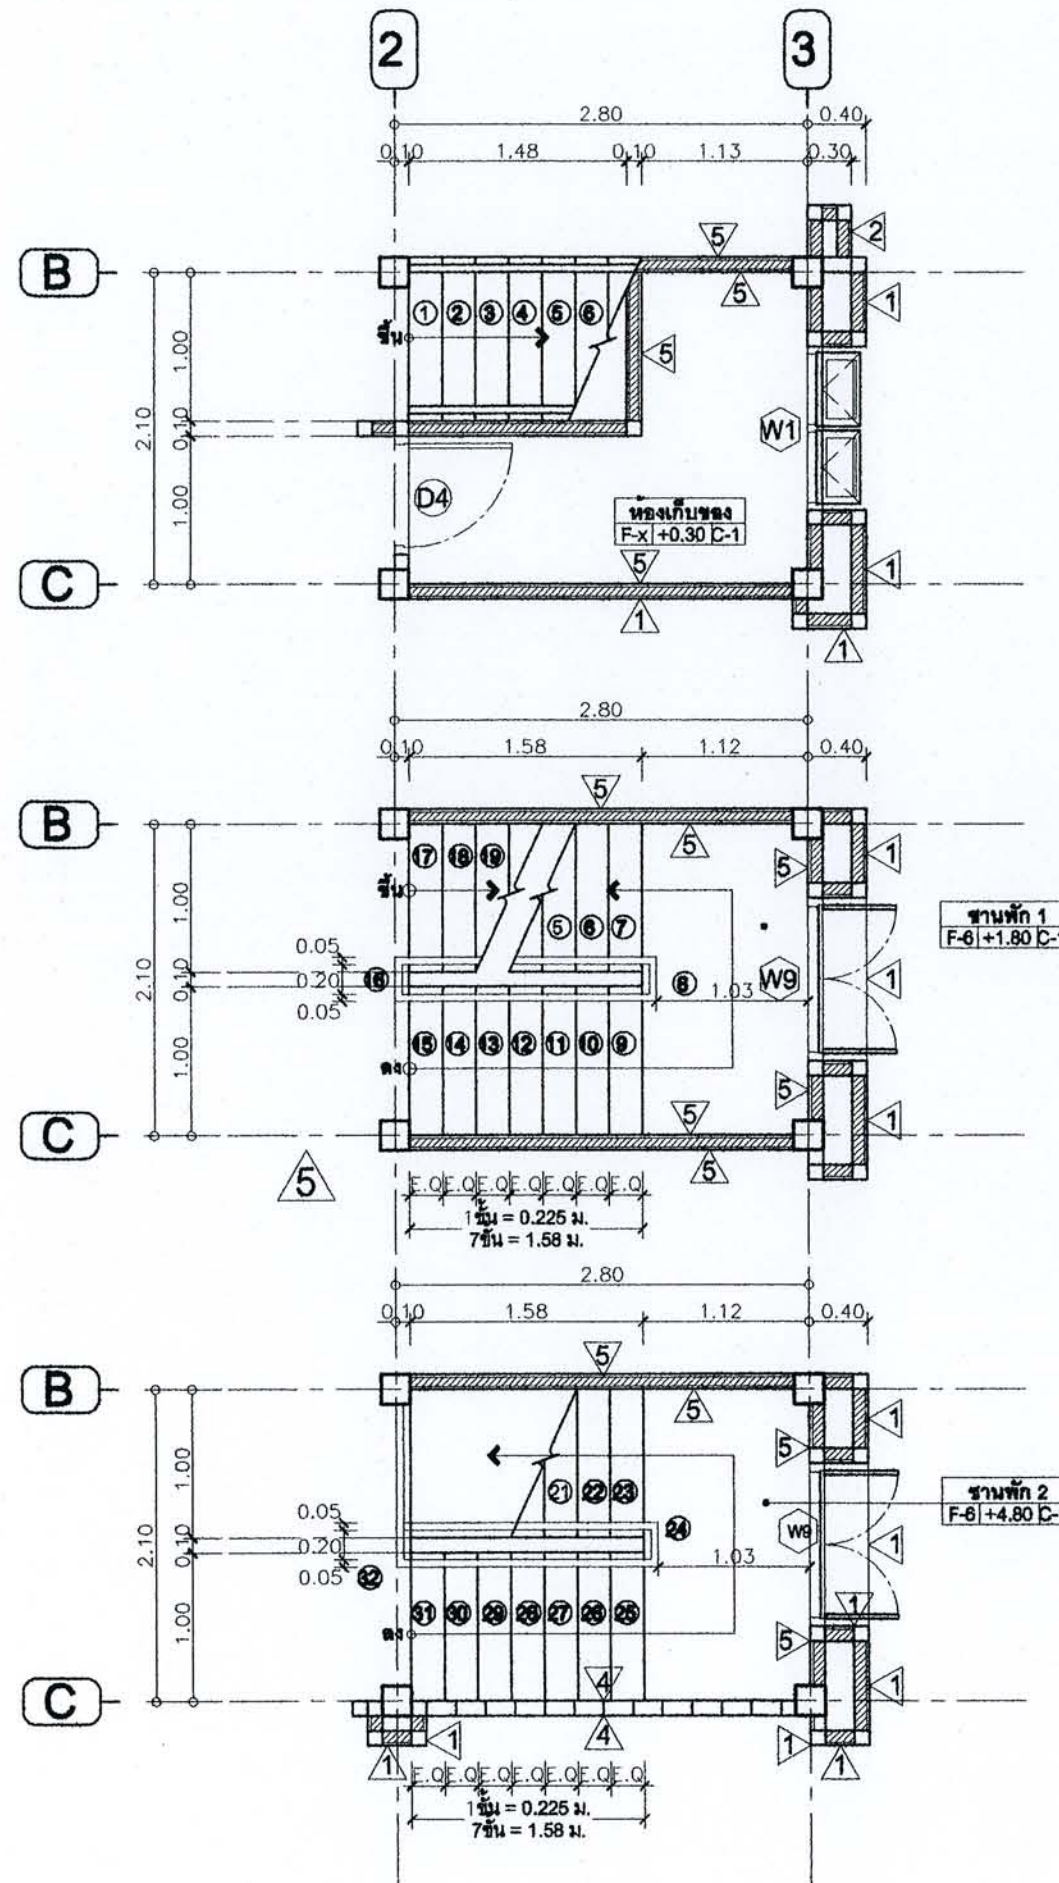

ผังบันไดชั้นล่าง
มาตราส่วน 1:50

ผังบันไดชั้นสอง
มาตราส่วน 1:50

ผังบันไดชั้นสาม
มาตราส่วน 1:50

▼ +10.88 ระดับสูงสุด

▼ +9.30 ระดับหลังอะเส

▼ +6.30 ระดับพื้นชั้นที่ 3


▼ +4.80 ระดับชานพัก 2

▼ +3.30 ระดับพื้นชั้นที่ 2

▼ +1.80 ระดับชานพัก 1

▼ +0.30 ระดับพื้นชั้นล่าง

▼ ±0.00 ระดับพื้นอ้างอิง

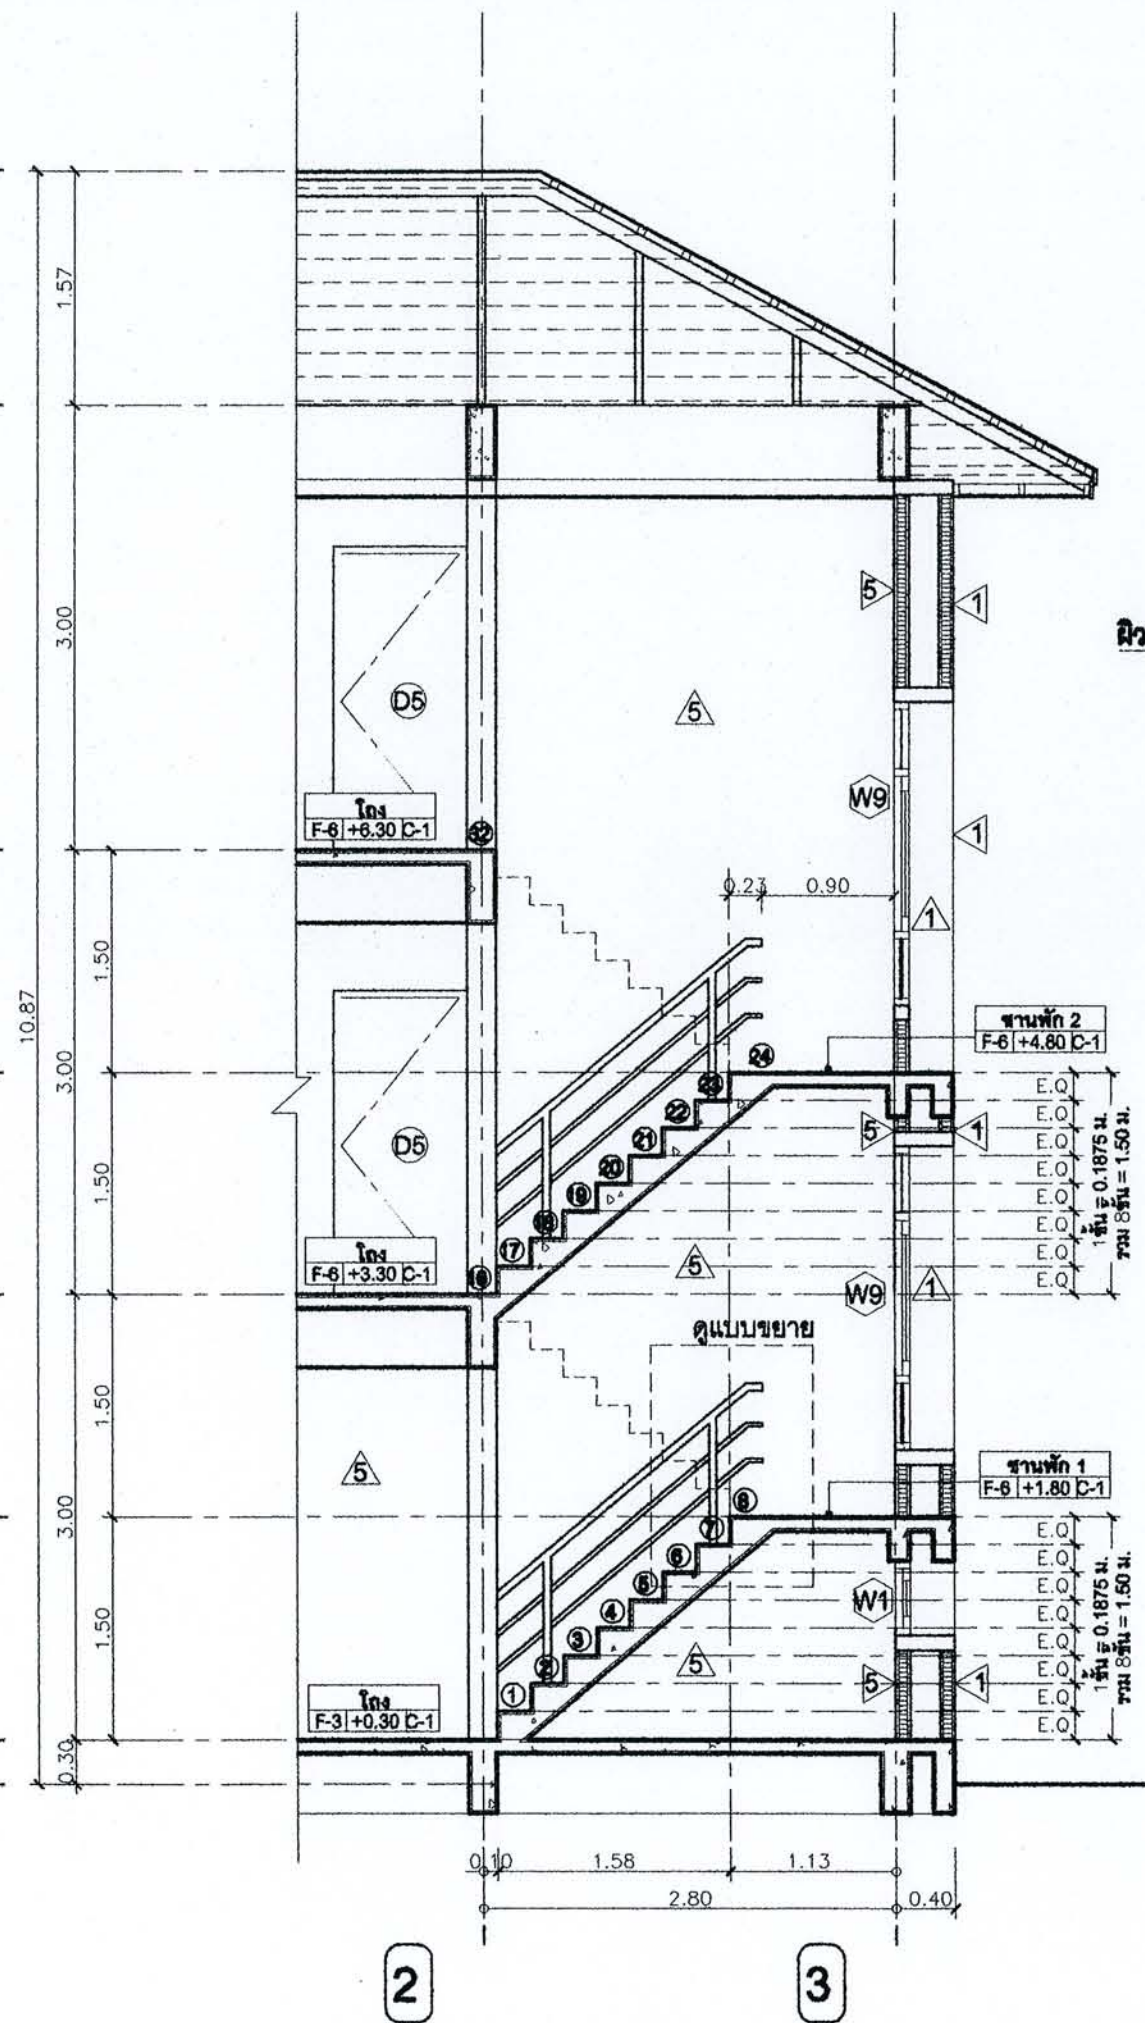

ราวจับเหล็กขนาด 2"x2" ทำสีพ่น

เหล็ก Ø 1" ทำสีพ่น

ฉนวนกันน้ำโดกรูไม้ปาเก้

แบบขยายราวบันได

มาตราส่วน

1:25

รูปตัดบันได

มาตราส่วน

1:50



สำนักงานโยธา
กรุงเทพมหานคร

โครงการ
แบบบ้านยี่สิบเอ็ดประชาชน

ตามนโยบาย

นางสาวสุนันท์ ธีรพิตร ผู้ว่าฯ กทม.
นายพรเทพ เศรษฐ์ไพฑูริย์ รองผู้ว่าฯ กทม.
นายธีรวัชร นนธิ์ชัยไพฑูริย์ รองผู้ว่าฯ กทม.
นายพงศ์ศักดิ์ สุขสันต์ ปลัดฯ กทม.

ผู้อำนวยการสำนักงานโยธา
นายจุมพล ชื่นภักดิ์
รองผู้อำนวยการสำนักงานโยธา
นายวิศักดิ์ เลิศประพันธ์
ผู้อำนวยการสำนักงานออกแบบ
นายชวรงค์ สอนเนียม
หัวหน้ากลุ่มงานสถาปัตยกรรม
นายสินธุ์ชัย บุญนิกร
หัวหน้ากลุ่มงานวิศวกรรม
นายธีรยุทธ คงสวัสดิ์ชัย

สถาปนิก
นางสาวสุนันท์ ธีรพิตร
วิศวกรโครงสร้าง
นายธีรวัชร นนธิ์ชัยไพฑูริย์
วิศวกรไฟฟ้า
นายวิศักดิ์ เลิศประพันธ์
วิศวกรสุขาภิบาล
นางสาวกนกชรีรา สอนเนียม
วิศวกรเครื่องกล

นายช่างเขียนแบบ
นายณัฐพงศ์ ณรงค์บุญชูชาติ

แบบ
028 บ้านกัลปพฤกษ์

เจ้าของ
สถานที่

แบบแสดง
แบบขยายรูปตัดบันได

มาตราส่วน 1:50

FILE :
วันที่ 15 พฤษภาคม 2553
ชื่อสถาปนิก
รวมแผ่น 32

รายการแก้ไขแบบ



สำนักงานโยธา
กรุงเทพมหานคร

โครงการ
แบบบ้านขี้เหล็กประชาชน

ตามนโยบาย

น.ร.สุมนพันธ์ เอธิศ ผู้ว่าฯกทม.
นายแพทย์ ประทีปเดช รองผู้ว่าฯกทม.
นายธีระชน นิ่มนัยพิสัย รองผู้ว่าฯกทม.
นายพงษ์ศักดิ์ แสนรัตน์ ปลัดฯกทม.

ผู้อำนวยการสำนักงานโยธา
นายจุมพล สันภาพ
รองผู้อำนวยการสำนักงานโยธา
นายวิศักดิ์ เติบระพันธ์
ผู้อำนวยการสำนักงานออกแบบ
นายจรูญ สันติธรรม
หัวหน้ากลุ่มงานสถาปัตยกรรม
นายสินธุ์ชัย บุญภิรักษ์
หัวหน้ากลุ่มงานวิศวกรรม
นายธีระยุทธ คงสวัสดิ์ชัย

สถาปนิก
นางสาวสุมนมวาศย์ กาญจนะ
วิศวกรโครงสร้าง
นายศิริพิชัย ชินนิตย
วิศวกรไฟฟ้า
นายกิตติพงษ์ จิระดาการ
วิศวกรสุขาภิบาล
นางสาวมณิชา สงทอง
วิศวกรเครื่องกล

นายชาญชัยแบบ
นายณัฐพงศ์ ณรงค์บุญสุทธิ์

แบบ
028 บ้านกิลปพฤกษ์

เจ้าของ
สถานที่


แบบแสดง
แบบขยายห้องน้ำ

มาตราส่วน 1:50


FILE : เลขที่ 16
วันที่ 25/3/2553
คดีเลขที่ 16
รวมแผ่น 32

รายการแก้ไขแบบ

สัญลักษณ์	รายการประกอบแบบห้องน้ำ
1	อ่างล้างหน้าแบบฝังเคาน์เตอร์ พร้อมมกอกน้ำ
2	กระจกเงาสำเร็จรูป
3	โถ้วมแบบชักโครกยี่ห้อ
4	สายฉีดชำระแบบสายอ่อน
5	ที่ใส่กระดาษชำระ
6	ฝักบัวอาบน้ำ
7	FD. แบบดักกลิ่น

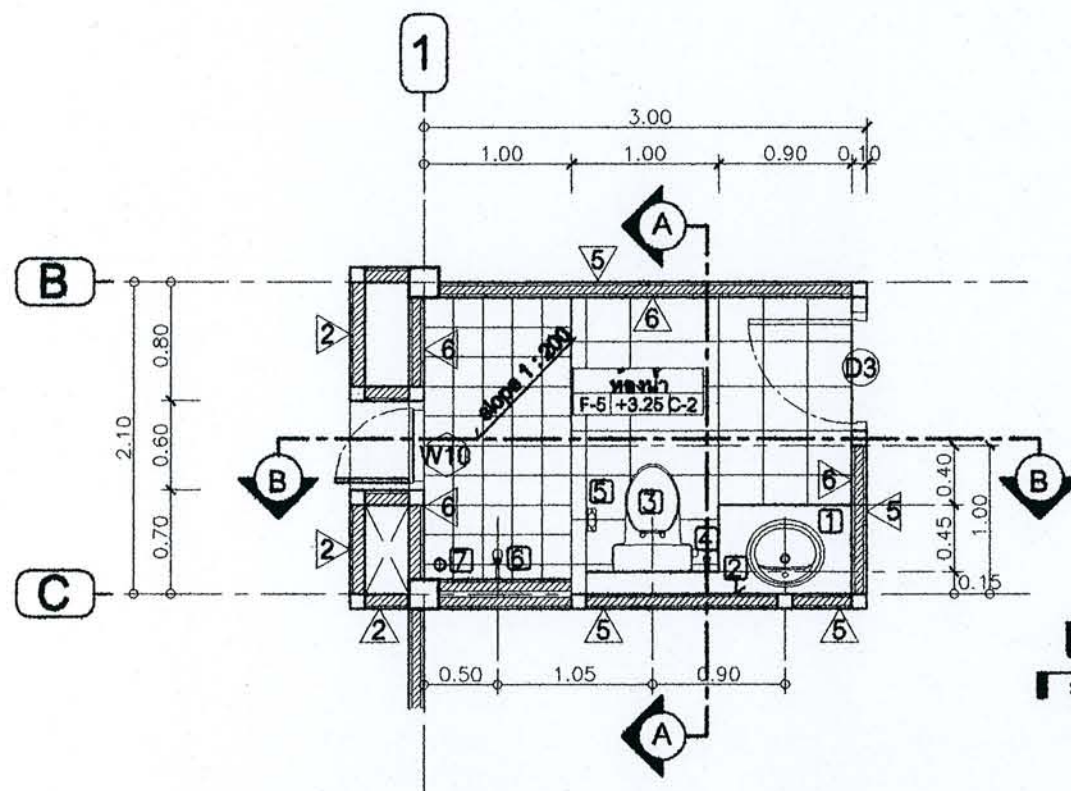


แบบขยายผนัง
มาตราส่วน 1:50

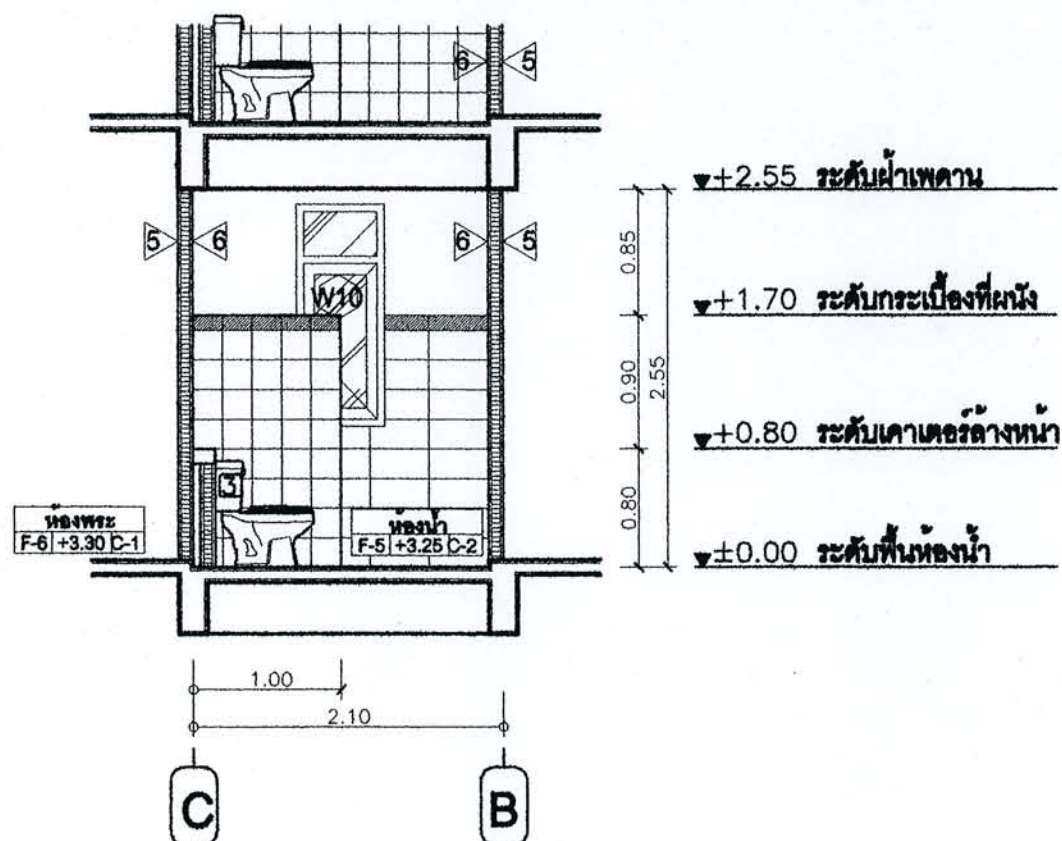

รูปตัด A-A

มาตราส่วน 1:50

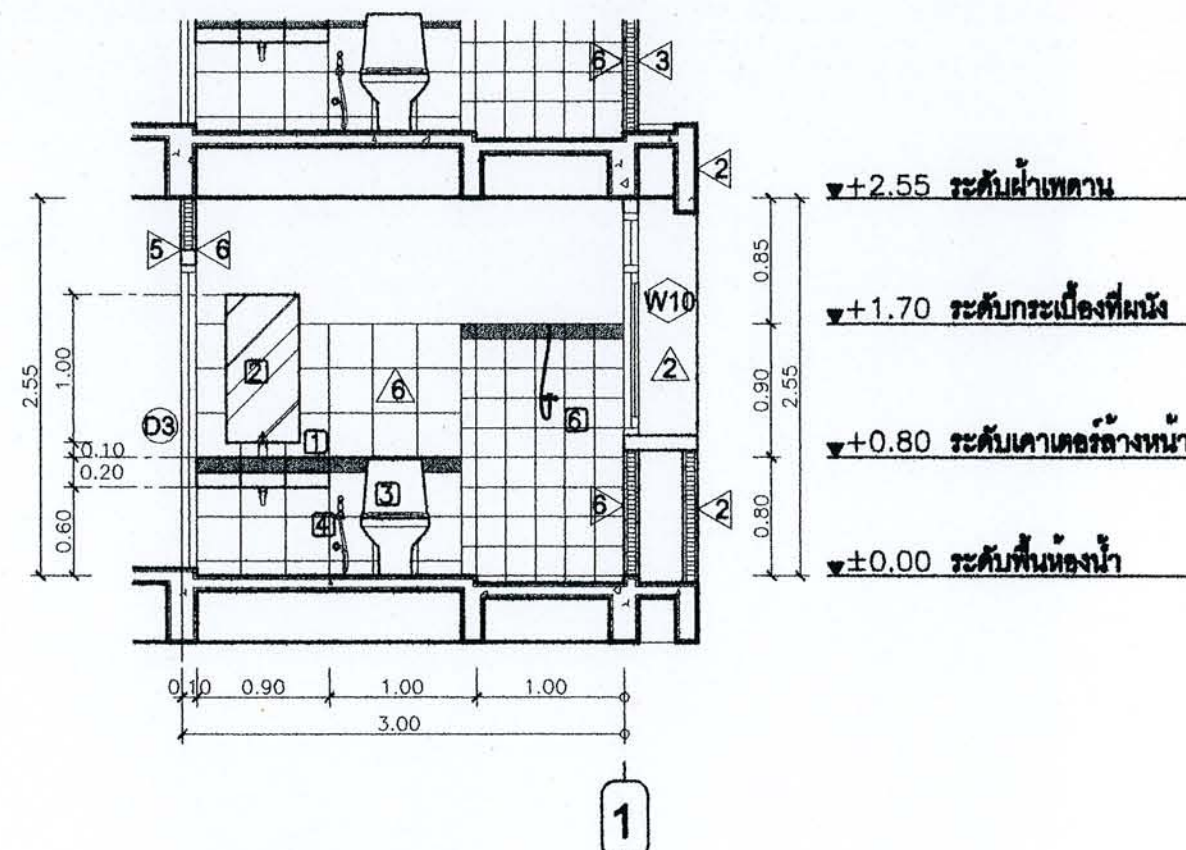

รูปตัด B-B

มาตราส่วน 1:50



สำนักงาน
กรุงเทพมหานคร

โครงการ
แบบบ้านยี่สิบสี่ประชาชน

ตามนโยบาย

น.ส.สุมนทิพย์ ปิณฑะ ผู้ว่าฯกทม.
นายพรเทพ เศรษฐกิจ รองผู้ว่าฯกทม.
นายธีระชัย มโนชัยนันท์ รองผู้ว่าฯกทม.
นายพงศ์ศักดิ์ แสนสุทนต์ ปลัดฯกทม.

ผู้อำนวยการสำนักงาน
นายสุเมธ สว่างใส
รองผู้อำนวยการสำนักงาน
นายวิวัฒน์ นิตยประพันธ์
ผู้อำนวยการสำนักงาน
นายสุวิทย์ นิตยประพันธ์
หัวหน้ากลุ่มงานสถาปัตยกรรม
นายสุวิทย์ นิตยประพันธ์
หัวหน้ากลุ่มงานวิศวกรรม
นายธีระชัย มโนชัยนันท์
นายธีระชัย มโนชัยนันท์

สถาปนิก
นางสาวสุเมธ นิตยประพันธ์
วิศวกรโครงสร้าง
นายวิวัฒน์ นิตยประพันธ์
วิศวกรไฟฟ้า
นายวิวัฒน์ นิตยประพันธ์
วิศวกรสุขาภิบาล
นางสาวสุเมธ นิตยประพันธ์
นางสาวสุเมธ นิตยประพันธ์
วิศวกรเครื่องกล

นายช่างเขียนแบบ
นายวิวัฒน์ นิตยประพันธ์

แบบ
028 บ้านกึ่งอพยพ

เจ้าของ

สถานที่

แบบแสดง
แบบขยายหน้าต่าง 1

มาตราส่วน 1:50

FILE : เลขที่ 17

วันที่ 17

วันที่ 17

วันที่ 17






วันที่ 17

วันที่ 17

วันที่ 17

วันที่ 17

สัญลักษณ์	W1	W2	W3	W4
ชนิดบาน	-หน้าต่างบานกระทุ้ง	-หน้าต่างบานเปิดคู่	-หน้าต่างบานเลื่อน	-หน้าต่างบานเกล็ดกระดาก
วงกบ	-อลูมิเนียม ขนาด 2"x4" สีธรรมชาติ	-อลูมิเนียม ขนาด 2"x4" สีธรรมชาติ	-อลูมิเนียม ขนาด 2"x4" สีธรรมชาติ	-อลูมิเนียม ขนาด 2"x4" สีธรรมชาติ
กรอบบาน	-อลูมิเนียม สีธรรมชาติ	-อลูมิเนียม สีธรรมชาติ	-อลูมิเนียม สีธรรมชาติ	-
ลูกพับ, ช่องแสง	-กระดากโลหะหนา 2 หุน	-กระดากโลหะหนา 2 หุน	-กระดากโลหะหนา 2 หุน	-บานเกล็ดกระดากโลหะหนา 2 หุน
อุปกรณ์ติดตั้ง	-มือจับ, ตัวล็อก	-มือจับ, ตัวล็อก	-ตัวล็อก, รางเลื่อน	-อุปกรณ์บานเกล็ดกระดาก
สัญลักษณ์	W5	W6	W7	W8
ชนิดบาน	-หน้าต่างบานกระทุ้ง	-ช่องแสงกระดากโลหะ ปิดตาย	-หน้าต่างบานเปิดคู่	-หน้าต่างบานเปิดคู่
วงกบ	-อลูมิเนียม ขนาด 2"x4" สีธรรมชาติ	-อลูมิเนียม ขนาด 2"x4" สีธรรมชาติ	-อลูมิเนียม ขนาด 2"x4" สีธรรมชาติ	-อลูมิเนียม ขนาด 2"x4" สีธรรมชาติ
กรอบบาน	-อลูมิเนียม สีธรรมชาติ		-อลูมิเนียม สีธรรมชาติ	-อลูมิเนียม สีธรรมชาติ
ลูกพับ, ช่องแสง	-กระดากโลหะหนา 2 หุน	-กระดากโลหะหนา 2 หุน	-กระดากโลหะหนา 2 หุน	-กระดากโลหะหนา 2 หุน
อุปกรณ์ติดตั้ง	-มือจับ, ตัวล็อก		-มือจับ, ตัวล็อก	-มือจับ, ตัวล็อก

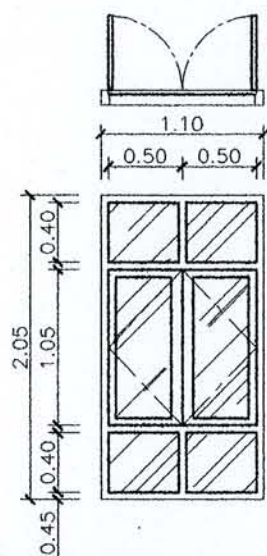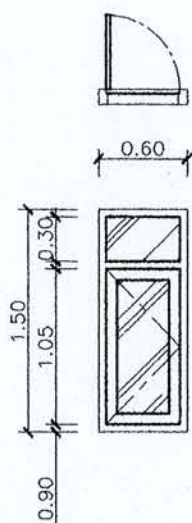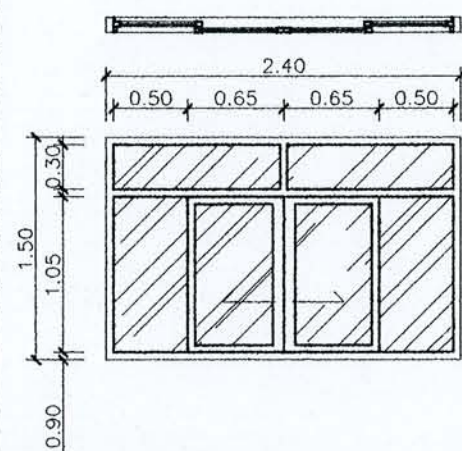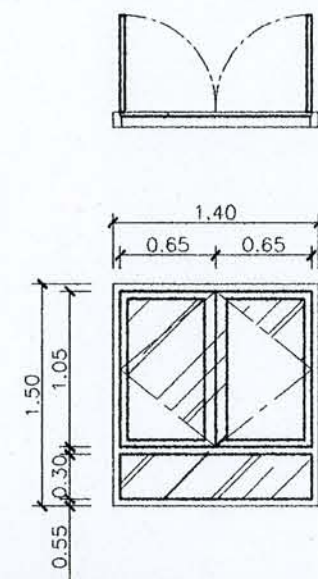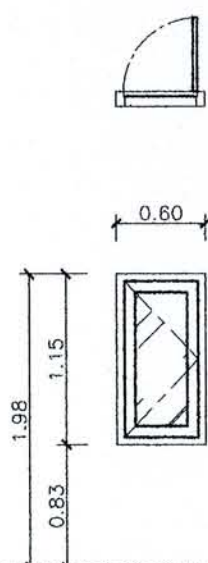สัญลักษณ์	W9	W10	W11	W12
				
ชนิดบาน	-หน้าต่างบานเปิดคู่	-หน้าต่างบานเปิดเดี่ยว	-หน้าต่างบานเลื่อน	-หน้าต่างบานเปิดคู่
วงกบ	-อลูมิเนียม ขนาด 2"x4" สีธรรมชาติ	-อลูมิเนียม ขนาด 2"x4" สีธรรมชาติ	-อลูมิเนียม ขนาด 2"x4" สีธรรมชาติ	-อลูมิเนียม ขนาด 2"x4" สีธรรมชาติ
กรอบบาน	-อลูมิเนียม สีธรรมชาติ	-อลูมิเนียม สีธรรมชาติ	-อลูมิเนียม สีธรรมชาติ	-อลูมิเนียม สีธรรมชาติ
ลูกพับ, ช่องแสง	-กระจกใสหนา 2 หุน	-กระจกใสหนา 2 หุน	-กระจกใสหนา 2 หุน	-กระจกใสหนา 2 หุน
อุปกรณ์ติดตั้ง	-มือจับ , ตัวล็อก	-มือจับ , ตัวล็อก	-ตัวล็อก, รางเลื่อน	-มือจับ , ตัวล็อก
สัญลักษณ์	W13			
				
ชนิดบาน	-หน้าต่างบานเปิดเดี่ยว			
วงกบ	-อลูมิเนียม ขนาด 2"x4" สีธรรมชาติ			
กรอบบาน	-อลูมิเนียม สีธรรมชาติ			
ลูกพับ, ช่องแสง	-กระจกใสหนา 2 หุน			
อุปกรณ์ติดตั้ง	-มือจับ , ตัวล็อก			



สำนักงานโยธา
กรุงเทพมหานคร

โครงการ
แบบบ้านชั้นเดียวประชาชน

ตามนโยบาย

ม.ร.ว.สุขุมพันธุ์ บริพัตร ผู้ว่าฯกทม.
นายแพทย์ เสรฐภไพฑูรย์ รองผู้ว่าฯกทม.
นายธีระวัฒน์ นิลนิริศ รองผู้ว่าฯกทม.
นายพงษ์ศักดิ์ แสนจันทร์ ปลัดฯกทม.

ผู้อำนวยการสำนักงานโยธา

นายชุมพล คำภักดิ์

รองผู้อำนวยการสำนักงานโยธา

นายวิวัฒน์ เตชะประสิทธิ์

ผู้อำนวยการสำนักงานออกแบบ

นายชัชวาลย์ สอนเนียม

หัวหน้ากลุ่มงานสถาปัตยกรรม

นายสันติชัย บุญอักษร

หัวหน้ากลุ่มงานวิศวกรรม

นายธีระยุทธ คงสวัสดิ์เกียรติ

สถาปนิก

นางสาวสุมนมาลย์ กาญจนะ

วิศวกรโครงสร้าง

นายจิรสิทธิ์ พิมพ์ชัย

วิศวกรไฟฟ้า

นายวิวัฒน์ ธีระเดชาก

วิศวกรสุขาภิบาล

นางสาวกมลทิศา สมหม

วิศวกรเครื่องกล

นายช่างเขียนแบบ

นายณัฐพงศ์ ณรงค์บุญชูทรัพย์

แบบ

028 บ้านกัลปพฤกษ์

เจ้าของ

สถานที่

แบบแสดง

แบบขยายหน้าต่าง 2

มาตราส่วน 1:50

FILE :

วันที่ 25 มิถุนายน 2553

คัดลอกไปทำแบบ

รวมหน้า

32

รายการแก้ไขแบบ



สำนักงานคณะกรรมการ
การศึกษาแห่งชาติ

โครงการ
แบบบ้านขึ้นเพื่อประชาชน

ตามนโยบาย

น.ร.สุจินต์ บริหาร บัณฑิต
นายแพทย์ ประทีป จรุงพิค
นายธีระชัย มโนทัศน์ บัณฑิต
นายแพทย์ศิริชัย เตมียาภรณ์ บัณฑิต

ผู้อำนวยการสำนักงาน
นายสุจินต์ บริหาร บัณฑิต
รองผู้อำนวยการสำนักงาน
นายธีระชัย มโนทัศน์ บัณฑิต
ผู้อำนวยการสำนักงาน
นายแพทย์ศิริชัย เตมียาภรณ์ บัณฑิต
นายแพทย์ศิริชัย เตมียาภรณ์ บัณฑิต
นายแพทย์ศิริชัย เตมียาภรณ์ บัณฑิต

สถาปนิก
นางสาวสุจินต์ บริหาร บัณฑิต
วิศวกร
นายธีระชัย มโนทัศน์ บัณฑิต
วิศวกรไฟฟ้า
นายแพทย์ศิริชัย เตมียาภรณ์ บัณฑิต
วิศวกรสุขาภิบาล
นายแพทย์ศิริชัย เตมียาภรณ์ บัณฑิต
นางสาวสุจินต์ บริหาร บัณฑิต
วิศวกรเครื่องกล

นายแพทย์ศิริชัย เตมียาภรณ์ บัณฑิต
นายแพทย์ศิริชัย เตมียาภรณ์ บัณฑิต

แบบ
028 บ้านกัลปพฤกษ์

เจ้าของ
สถานที่

แบบแสดง
แบบขยายประตู

มาตราส่วน 1:50

FILE : เลขที่ 19

วันที่ 2553 19

คัดลอกเป็นรูปแบบ รวม 32

รายการแก้ไขแบบ

สัญลักษณ์	D0	D1	D2	D3
ชนิดบาน	-ประตูบานเปิดคู่	-ประตูบานเปิดเดี่ยว	-ประตูบานเปิดเดี่ยว	-ประตูบานเปิดเดี่ยว
วงกบ	-อลูมิเนียม ขนาด 2"x4" สีธรรมชาติ	-อลูมิเนียม ขนาด 2"x4" สีธรรมชาติ	-อลูมิเนียม ขนาด 2"x4" สีธรรมชาติ	-พีวีซีสำเร็จรูป สี...
กรอบบาน	-อลูมิเนียม สีธรรมชาติ	-อลูมิเนียม สีธรรมชาติ	-อลูมิเนียม สีธรรมชาติ	-พีวีซีสำเร็จรูป สี...
ลูกพับ, ช่องแสง	-กระจกใสหนา 2 หุน	-กระจกใสหนา 2 หุน	-กระจกใสหนา 2 หุน	-พีวีซีสำเร็จรูป สี...
อุปกรณ์ติดตั้ง	-มือจับ , ตัวล็อก	-มือจับ , ตัวล็อก	-มือจับ , ตัวล็อก	-ลูกบิด
สัญลักษณ์	D5	D6	D7	D8
ชนิดบาน	-ประตูบานเปิดเดี่ยว	-ประตูบานเลื่อน	-ประตูบานเปิดคู่	-ประตูบานเปิดคู่
วงกบ	-ไม้เนื้อแข็ง ขนาด 2"x4" ทาสีน้ำมัน	-ไม้เนื้อแข็ง ขนาด 2"x4" ทาสีน้ำมัน	-อลูมิเนียม ขนาด 2"x4" สีธรรมชาติ	-อลูมิเนียม ขนาด 2"x4" สีธรรมชาติ
กรอบบาน	-โครงไม้เนื้อแข็ง ทุ่นไม้ขัดอย่างทาสีน้ำมัน	-โครงไม้เนื้อแข็ง ทุ่นไม้ขัดอย่างทาสีน้ำมัน	-อลูมิเนียม สีธรรมชาติ	-อลูมิเนียม สีธรรมชาติ
ลูกพับ, ช่องแสง			-กระจกใสหนา 2 หุน	-กระจกใสหนา 2 หุน
อุปกรณ์ติดตั้ง	-มือจับ , ตัวล็อก	-มือจับ , ตัวล็อก	-มือจับ , ตัวล็อก	-มือจับ , ตัวล็อก

รายการประกอบแบบคำนวณวิศวกรรมโยธา

1. ซีเมนต์

- 1.1 ส่วนของโครงสร้างคอนกรีตเสริมเหล็กทั้งหมดต้องใช้ PORTLAND CEMENT ประเภทที่ 1 ที่มีคุณสมบัติตามมาตรฐานผลิตภัณฑ์อุตสาหกรรมเท่านั้น
- 1.2 ถ้าไม่ได้ระบุเป็นอย่างอื่น คอนกรีต 1 ลบ.ม. ต้องมีส่วนผสมของซีเมนต์ไม่น้อยกว่า 320 กก.

2. คอนกรีต

- 2.1 คอนกรีตที่ใช้กับโครงสร้างอาคารได้แก่ ฐานราก, เสา, คาน, พื้น, คอนกรีตทับหน้าพื้นสำเร็จรูป, พัง ค.ส.ล. ฯลฯ ต้องมีกำลังอัดเฉลี่ยไม่น้อยกว่า 210 กก./ตร.ซม. เมื่ออายุ 28 วัน โดยทดสอบจากแท่งคอนกรีตตัวอย่างทรงกระบอก Ø 150 x 300 มม.

- 2.2 ADMIXTURES ที่ใช้ต้องมีคุณสมบัติตาม ASTM หรือ BS

3. งานเหล็ก

- 3.1 คุณสมบัติของเหล็กเส้นเสริมคอนกรีต มีดังนี้

ขนาดเหล็กเสริม มม.	สัญลักษณ์	มาตรฐาน	หมายเหตุ
RB 6 , RB 9	SR - 24	มอก. 20-2527	
DB 12 ขึ้นไป	SD - 30	มอก. 24-2536	

- 3.2 เหล็กรูปพรรณ , เหล็กกลวงสำหรับก่อสร้าง

- 3.2.1 เหล็กรูปพรรณที่จะใช้ต้องมีคุณสมบัติตาม มอก. 1227-2537, มอก.1228-2537 หรือ JS เหล็กกลวงที่ใช้ต้องมีคุณสมบัติตาม มอก. 107-2533 หรือ JS และเหล็กรูปพรรณเชื่อมประกอบจะต้องมีคุณสมบัติตาม มอก. 1303-2538
- 3.2.2 เหล็กรูปพรรณทั้งหมดต้องเป็นของใหม่ ไม่เคยใช้งานมาก่อน ตรงไม่บิดเบี้ยว ไม่มียอดตำหนิไม่มีสนิมกร่อน ไม่เปื้อนสี หรือน้ำมัน
- 3.2.3 การต่อเหล็กรูปพรรณ ถ้าไม่จำเป็นจริง ๆ แล้วห้ามต่อ ในกรณีที่มีการต่อเหล็ก รอยต่อของเหล็กต้องมี กำลังมากกว่าหรือเท่ากับเหล็กที่ไม่มีรอยต่อ การต่อให้ตรงจุดเดียวกัน และการต่อให้เป็นไปตามมาตรฐาน AISC
- 3.2.4 การประกอบและการติดตั้ง ให้ดำเนินการตามมาตรฐาน AISC หรือตามมาตรฐานสำหรับอาคารเหล็กรูปพรรณของ วสท. ที่ 1015-40
- 3.2.5 ผู้รับจ้างจะต้องทำ ค่ายัน ยึดโครง ให้เพียงพอเพื่อยึดโครงสร้างให้แน่นหนาอยู่ในแนวและตำแหน่งที่ต้องการ
- 3.2.6 องค์อาคารที่วางทาบหรือเชื่อมจะต้องวางให้แนบสนิทเต็มหน้า
- 3.2.7 การเชื่อมต้องทั้งหมดให้ใช้วิธีเชื่อมด้วยไฟฟ้าการ (Electric arc welding) โดยตลอดผิวหน้าที่ยังมีผลการเชื่อมให้เป็นไปตามมาตรฐาน AWS ขนาดของรอยเชื่อมต้องไม่น้อยกว่าความหนาของแผ่นเหล็ก
- 3.2.8 ถ้าไม่ได้กำหนดเป็นอย่างอื่นรอยต่อระหว่างชิ้นส่วนเหล็กต่างๆให้ใช้วิธี เชื่อมตะขบตลอดแนวชน
- 3.2.9 ผิวหน้าที่จะทำการเชื่อม ต้องสะอาดปราศจากสะเก็ดร่อน สนิมกร่อน ไขมัน สี หรือสิ่งแปลกปลอมอื่นใด
- 3.2.10 ตัวเชื่อมต้องมีคุณสมบัติตาม มอก. หรือ AWS หรือ AISC
- 3.2.11 ให้ทาสีกันสนิมไม่น้อยกว่า 2 ชั้น คุณภาพเทียบเท่า RUST-OLEAM, JOTAN, SIKKENS


4. ระบบกันซึม

- 4.1 รายละเอียดและคุณสมบัติ

ส่วนของอาคาร	ชนิดและผลิตภัณฑ์	ผลิตภัณฑ์คุณภาพเทียบเท่า
- พื้นห้องน้ำ , กันสาด ค.ส.ล.	น้ำยาเคมีแบบกันซึมชนิดทา	BRUSHBOND ของ FOSROC
รางน้ำ ค.ส.ล. ท่อระบาย ค.ส.ล.		LANKO 225 ?-? DAVCO

5. ทัวไปและการเตรียมงาน

- 5.1 รายการประกอบแบบอื่นใดที่ไม่ได้กำหนดไว้ให้ถือปฏิบัติตาม " บทกำหนดทั่วไปสำหรับกาสร้างอาคารคอนกรีตเสริมเหล็ก " ของ วสท. เป็นเกณฑ์
- 5.2 แบบรายการเหล่านี้ เป็นแบบรายการที่ใช้เป็นแนวทางในการก่อสร้างเท่านั้น หากมีความจำเป็นต้องเพิ่มเติมรายละเอียดเพื่อให้เกิดความมั่นคงแข็งแรงหรือความกลมกลืนมากยิ่งขึ้น หรือหากแบบมีข้อบกพร่อง แสดงรายละเอียดไม่ครบถ้วน วิศวกรฝ่ายวิศวกรรมจะเป็นผู้กำหนดให้ หรืออาจผู้รับจ้างดำเนินการออกแบบในส่วนนี้มา โดยอาศัยหลักวิชาช่างในขณะก่อสร้างจะต้องมีวิศวกรไม่ต่ำกว่าสามัญวิศวกรลงนามรับรอง และต้องเสนอต่อฝ่ายวิศวกรรมอาคารเห็นชอบก่อน โดยถือเป็นส่วนหนึ่งของแบบรายการนี้ และไม่ว่าการก่อสร้างนี้เกิดไปจากแบบรายการก่อสร้างแต่อย่างใด แต่ทั้งนี้ เนื่องจากต้องไม่ลดน้อยกว่าเดิมและผู้รับจ้างจะต้องไม่คิดค่าใช้จ่ายเพิ่ม

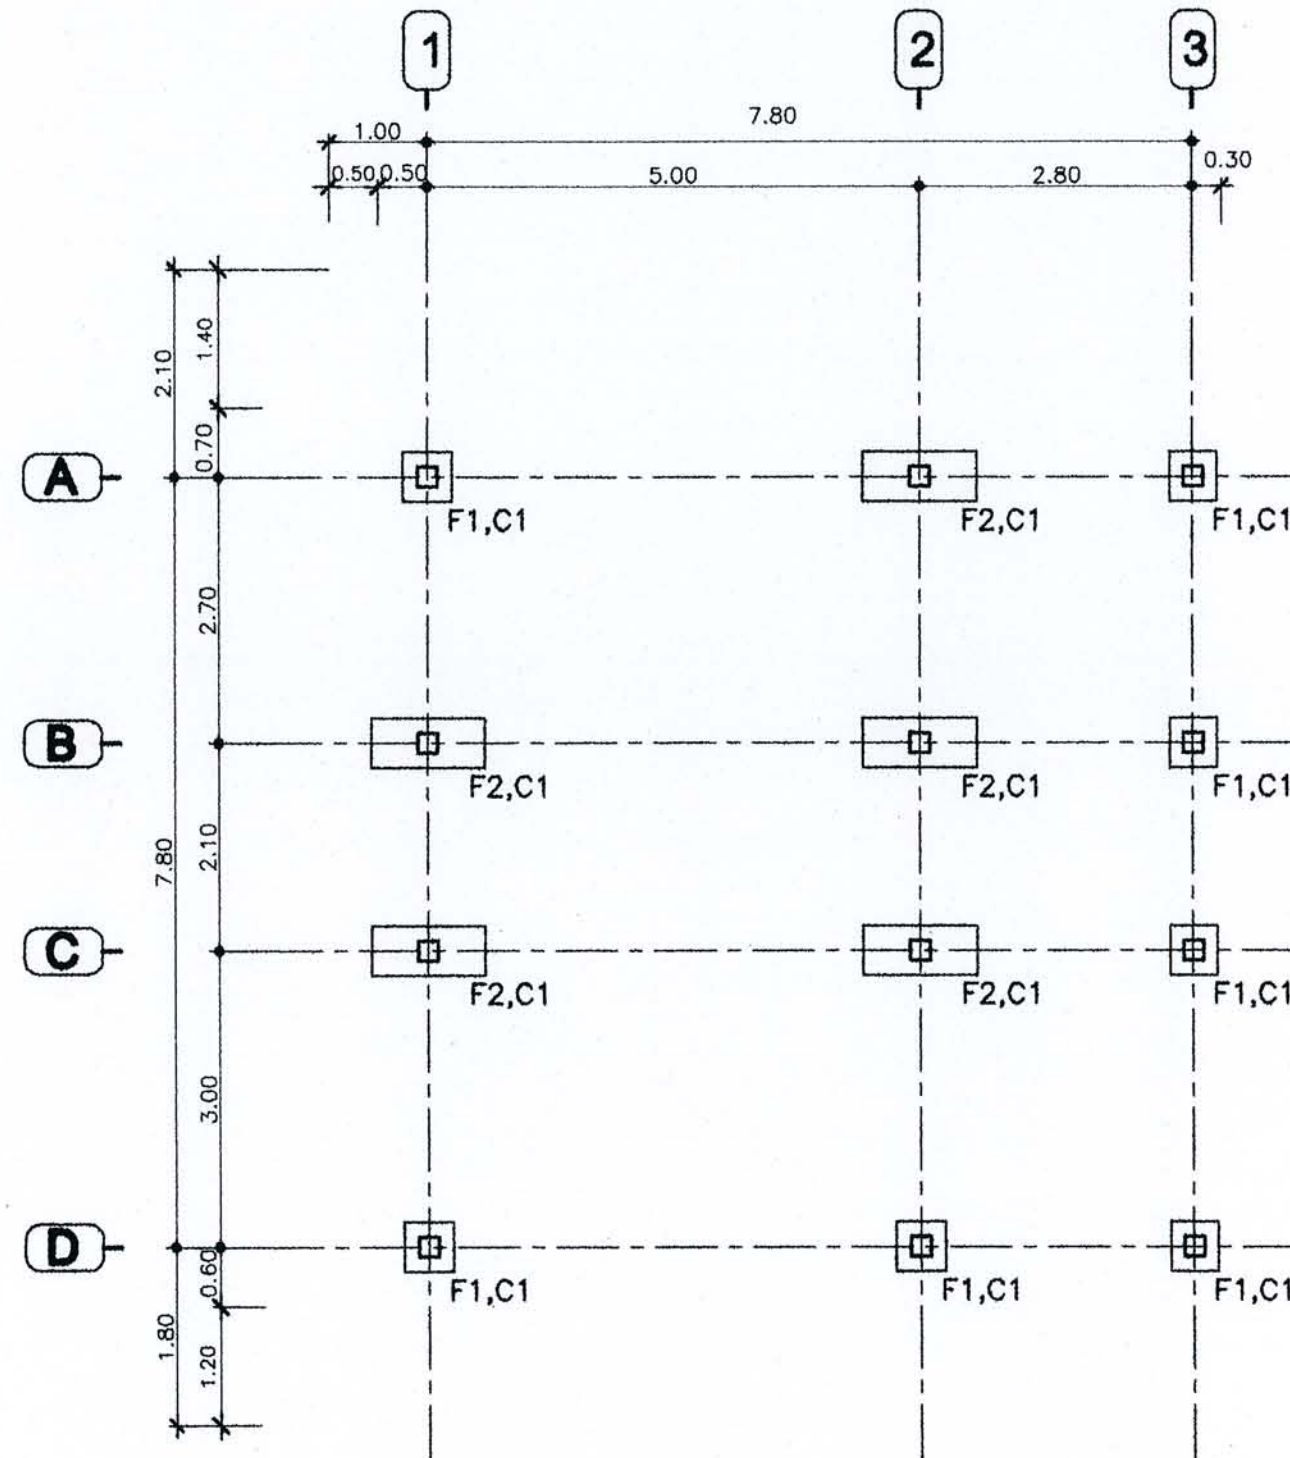

ผังฐานราก

มาตราส่วน 1:75



สำนักงานโยธา
กรุงเทพมหานคร

โครงการ
แบบบ้านชั้นเดียวประชาชน

ตามนโยบาย

น.ร.สุจินต์ บริดลย์ ผู้อำนวยการ
นายพรเทพ เศรษฐกิจ รองผู้อำนวยการ
นายธีระชน นิมิตต์ รองผู้อำนวยการ
นายพงษ์ศักดิ์ แสนดี ปลัดกอง

ผู้อำนวยการสำนักงานโยธา
นายอุดมพล ตันภาพ
รองผู้อำนวยการสำนักงานโยธา
นายวิศักดิ์ เกียรติพันธ์
ผู้อำนวยการสำนักงานออกแบบ
นายสุรศักดิ์ แสนงาม
หัวหน้ากลุ่มงานสถาปัตยกรรม
นายสันติชัย บุญอักษร
หัวหน้ากลุ่มงานวิศวกรรม
นายธีระยุทธ คงศรีเกียรติ

สถาปนิก
นางสาวสุนนมาลย์ กาญจนะ
วิศวกรโครงสร้าง
นายศิริพงษ์ จินตพันธ์
วิศวกรไฟฟ้า
นายวิฑิตพงษ์ จิระนาคกร
วิศวกรสุขาภิบาล
นางสาวณัชชา สมพยอม
วิศวกรเครื่องกล

นายช่างเขียนแบบ
นายสุทธ บวรณัน

แบบ
028 บ้านกัลปพฤกษ์

เจ้าของ

สถานที่

แบบแสดง
รายการประกอบแบบโยธา
ผังฐานราก

มาตราส่วน 1:75

FILE : S-01 วันที่ 20
วันที่ 2553
คัดลอกไปใช้ตามแบบ

รวมหน้า
32

รายการแก้ไขแบบ



สำนักงานโยธา
กรุงเทพมหานคร

โครงการ
แบบบ้านขึ้นเพื่อประชาชน

ตามนโยบาย
น.ร.สุจินต์ บริดลย์ ผู้อำนวยการ
นายแพทย์ เจริญพร รองผู้อำนวยการ
นายธีระชน นิมิตต์กุล รองผู้อำนวยการ
นายพงศ์ศักดิ์ แสนสุว ปลัดกรุงเทพมหานคร

ผู้อำนวยการสำนักงานโยธา
นายสมพงษ์ ตันภักดี
รองผู้อำนวยการสำนักงานโยธา
นายพิเชษฐ์ เตชะประสิทธิ์
ผู้อำนวยการสำนักงานออกแบบ
นายจตุรงค์ แสนชื่น
หัวหน้ากลุ่มงานสถาปัตยกรรม
นายสันติชัย บุญภิรักษ์
หัวหน้ากลุ่มงานวิศวกรรม
นายธีระยุทธ คงศรีชัย

สถาปนิก
นางสาวสมหมาย ภาณุเดช
วิศวกรโครงสร้าง
นายศิริพงษ์ พิเศษชัย
วิศวกรไฟฟ้า
นายศิริพงษ์ จริยะกลาง
วิศวกรสุขาภิบาล
นางสาวณิศา สัมพอม
วิศวกรเครื่องกล

นายช่างเขียนแบบ
นายสุทธ บวรณัน

แบบ
028 บ้านกัลปพฤกษ์

เจ้าของ

สถานที่

แบบแสดง

ผังโครงสร้างชั้นล่าง
และผังโครงสร้างชั้น 2


มาตราส่วน 1:75

FILE : เลขที่ 21


วันที่ 2553 S-02 21

คัดลอกปรับปรุงแบบ 32

รายการแก้ไขแบบ

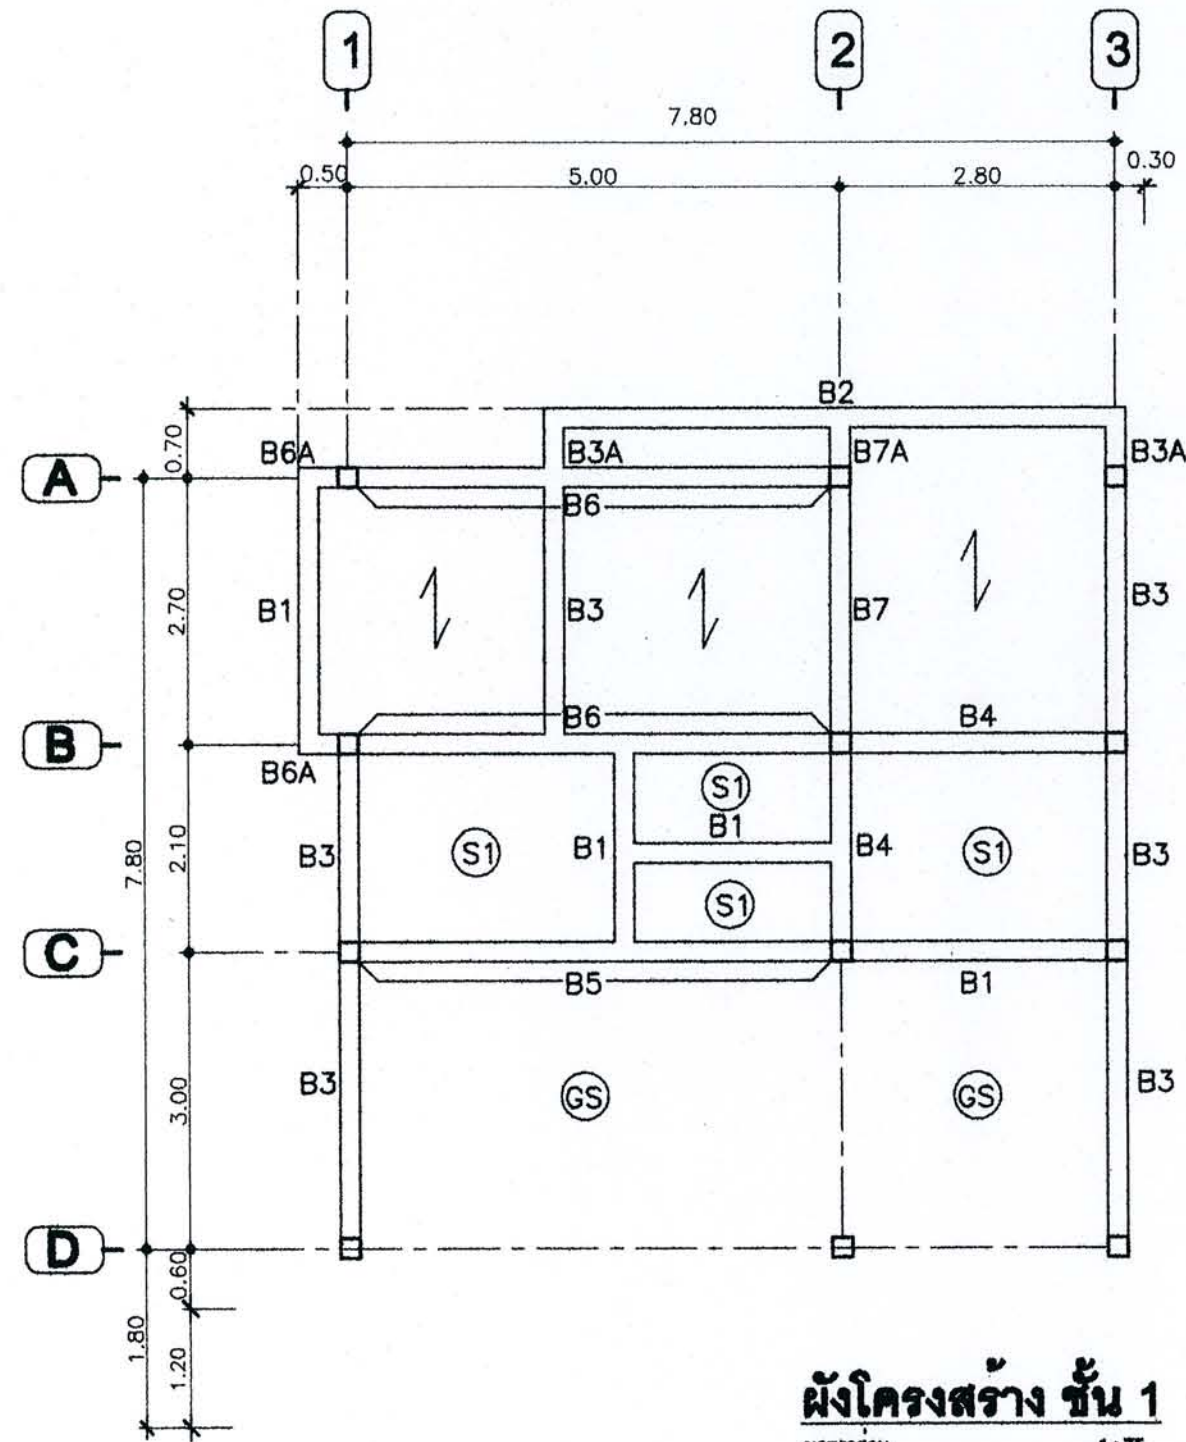

ผังโครงสร้าง ชั้น 1
มาตราส่วน 1:75

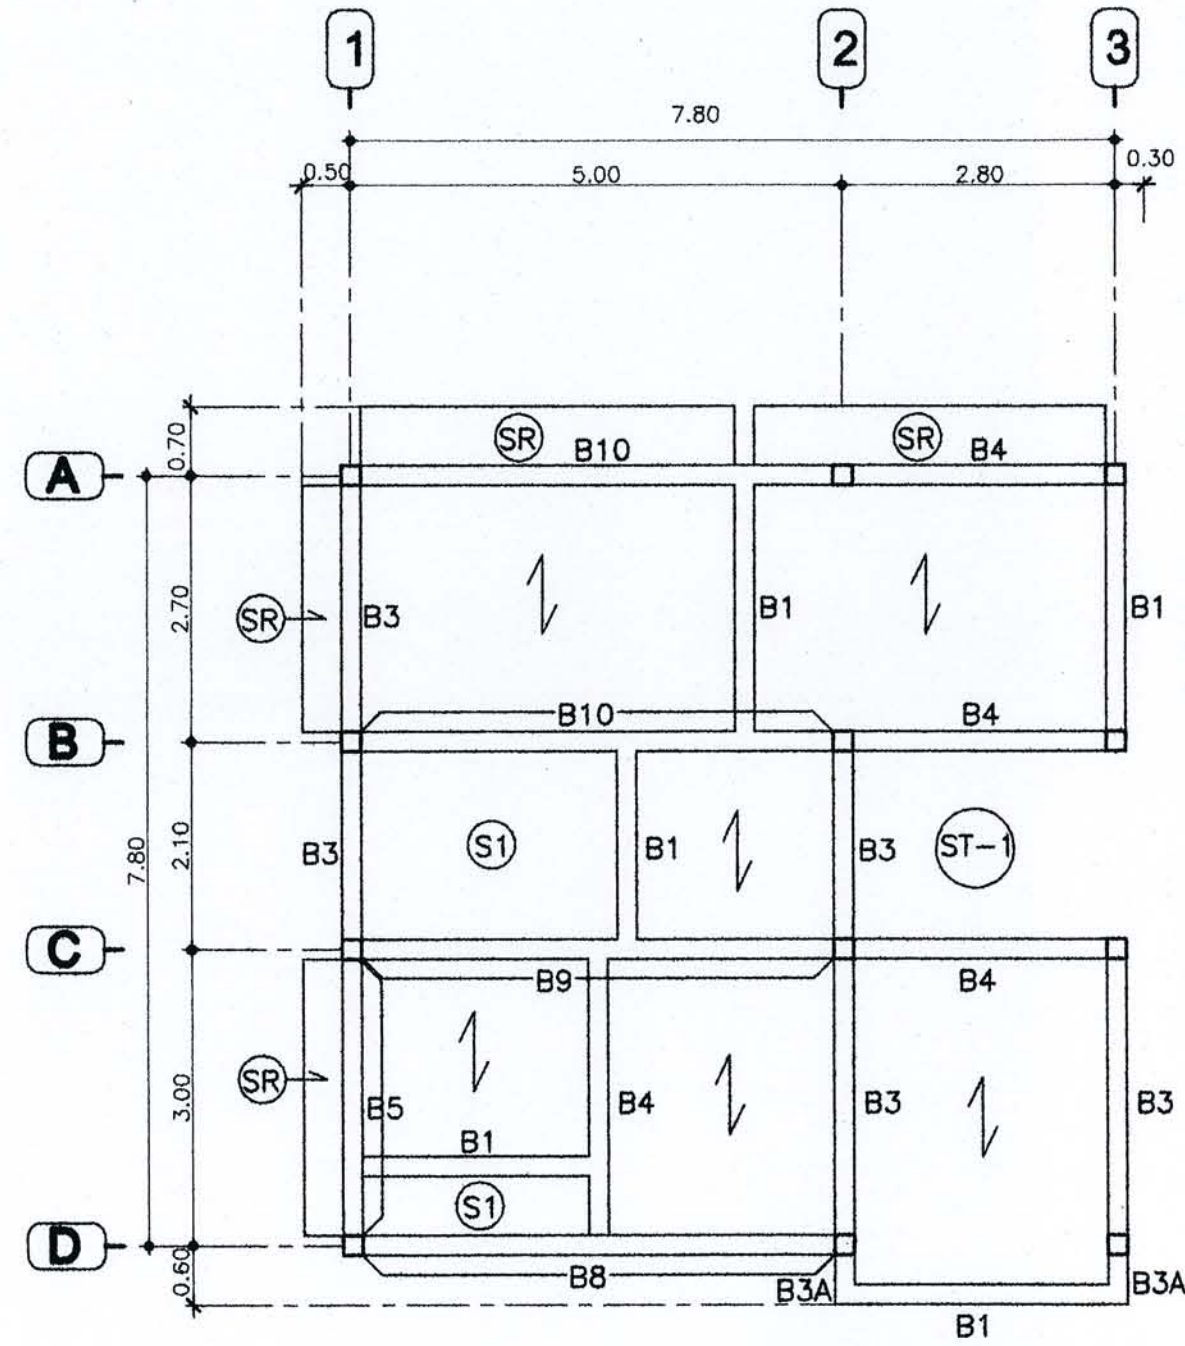

ผังโครงสร้าง ชั้น 2
มาตราส่วน 1:75



สำนักงานโยธา
กรุงเทพมหานคร

โครงการ
แบบบ้านขึ้นเพื่อประชาชน

ตามนโยบาย

น.ร.สุเมธพันธ์ บริพัตร ผู้ว่าฯกทม.
นายทศพร เศรษฐกิจ รองผู้ว่าฯกทม.
นายธีระชน นิ่มนาค รองผู้ว่าฯกทม.
นายพงษ์ศักดิ์ แสนลำดัย ปลัดฯกทม.

ผู้อำนวยการสำนักงานโยธา
นายชุมพล สว่าง
รองผู้อำนวยการสำนักงานโยธา
นายวิศักดิ์ เติบประพันธ์
ผู้อำนวยการสำนักงานออกแบบ
นายสุรศักดิ์ แสนเยี่ยม
หัวหน้ากลุ่มงานสถาปัตยกรรม
นายสันติชัย บุญวิเศษ
หัวหน้ากลุ่มงานวิศวกรรม
นายธีระยุทธ คงสวัสดิ์โยธา

สถาปนิก
นางสาวสุนทรมาศ กฤตชนะ
วิศวกรโครงสร้าง
นายศิริพงษ์ ชินสิทธิ์
วิศวกรไฟฟ้า
นายวิฑิตพงษ์ จิระเดชากร
วิศวกรสุขาภิบาล
นางสาวมนสิรา สมพงษ์
วิศวกรเครื่องกล

นายราชธิวัฒน์
นายสุทธ ปรอมสิน

แบบ
028 บ้านกึ่งปทุกษ


เจ้าของ
สถานที่

แบบแสดง
ผังโครงสร้างชั้น 3
ผังโครงสร้างคาน


มาตราส่วน 1:75

FILE :	วันที่	แผ่นที่
วันที่ 25/03/2553	S-03	22
คิดค่า เบื้องต้น	รวม	32

รายการแนบแบบ

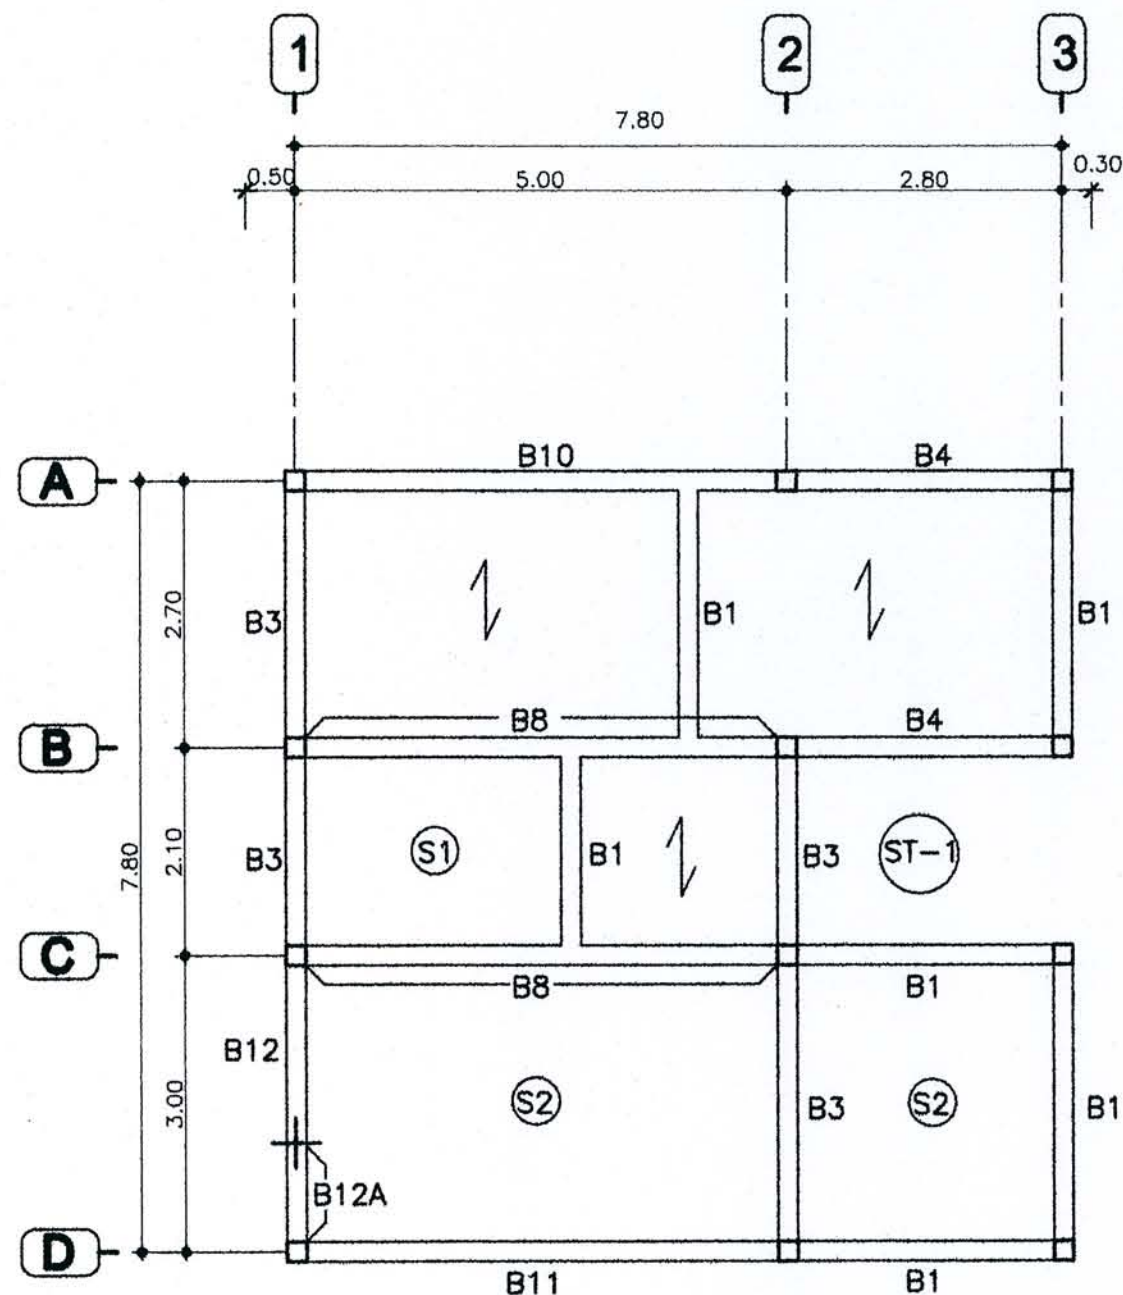

ผังโครงสร้าง ชั้น 3
มาตราส่วน 1:75

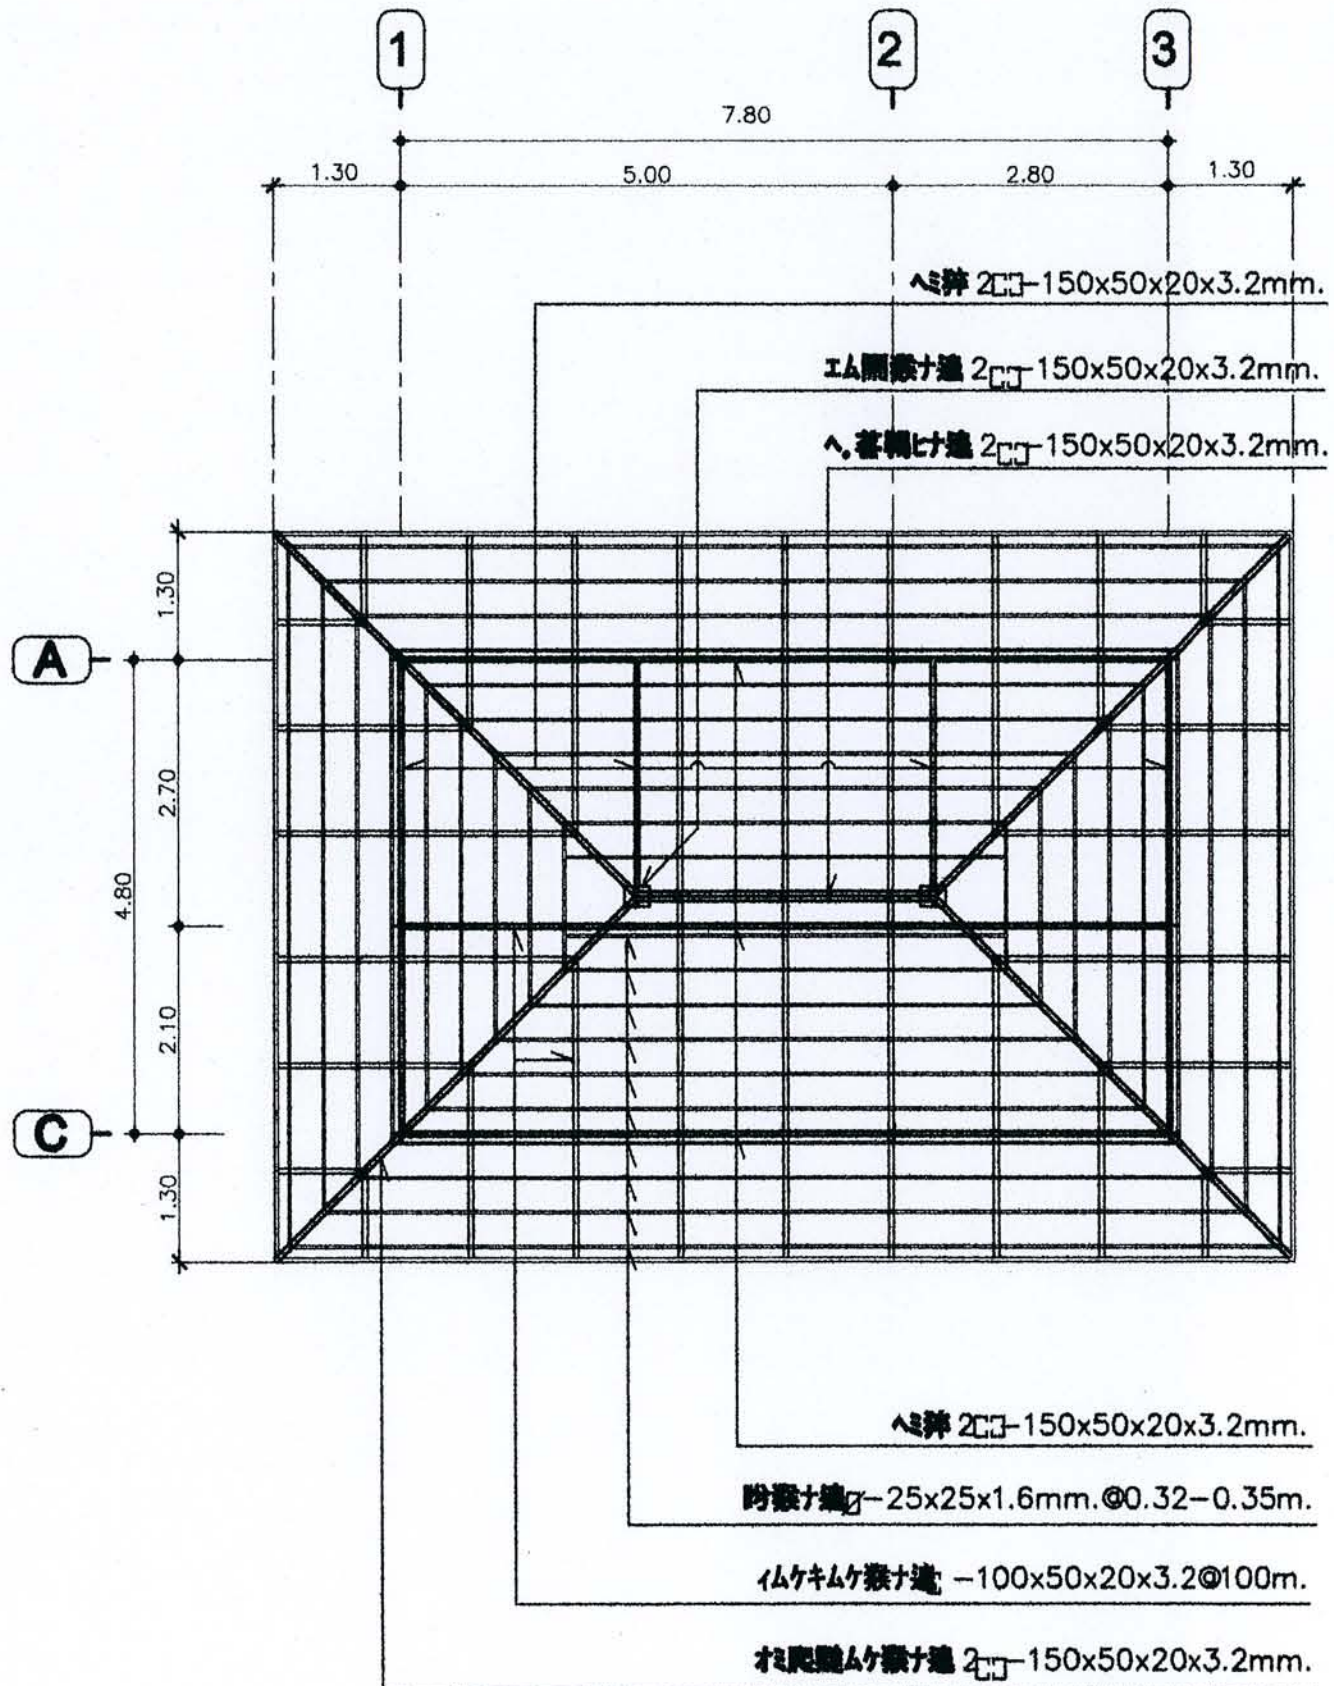

ผังโครงสร้างคาน
มาตราส่วน 1:75



สำนักงานโยธา
กรุงเทพมหานคร

โครงการ
แบบบ้านชั้นเดียวประชาชน

ตามนโยบาย

นางจุฬารัตน์ ตรีพิตร ผู้ว่ากรม
นายสมเทพ เศรษฐกิจ รองผู้ว่ากรม
นายธีระชน นิมิตพิบูลย์ รองผู้ว่ากรม
นายพงษ์ศักดิ์ เตมียาห์ ปลัดกรม

ผู้อำนวยการสำนักงานโยธา
นายสมเทพ เศรษฐกิจ
รองผู้อำนวยการสำนักงานโยธา
นายธีระชน นิมิตพิบูลย์
ผู้อำนวยการสำนักงานออกแบบ
นายสมเทพ เศรษฐกิจ
หัวหน้ากลุ่มงานสถาปัตยกรรม
นายธีระชน นิมิตพิบูลย์
หัวหน้ากลุ่มงานวิศวกรรม
นายธีระชน นิมิตพิบูลย์
นายธีระชน นิมิตพิบูลย์

สถาปนิก
นางสาวสมมาลย์ กาญจนะ
วิศวกรโครงสร้าง
นายธีระชน นิมิตพิบูลย์
วิศวกรไฟฟ้า
นายธีระชน นิมิตพิบูลย์
วิศวกรสุขาภิบาล
นายธีระชน นิมิตพิบูลย์
วิศวกรเครื่องกล
นายธีระชน นิมิตพิบูลย์

นายธีระชน นิมิตพิบูลย์
นายธีระชน นิมิตพิบูลย์

แบบ
028 บ้านกึ่งอพยพ

คำร้อง

สถานที่

แบบแปลน

แบบขยายโครงสร้าง 1

มาตราส่วน 1:75


FILE : S-04

วันที่ 25 ธันวาคม 2553

ผู้จัดทำ 23

ผู้ตรวจสอบ 32

รายการแก้ไข

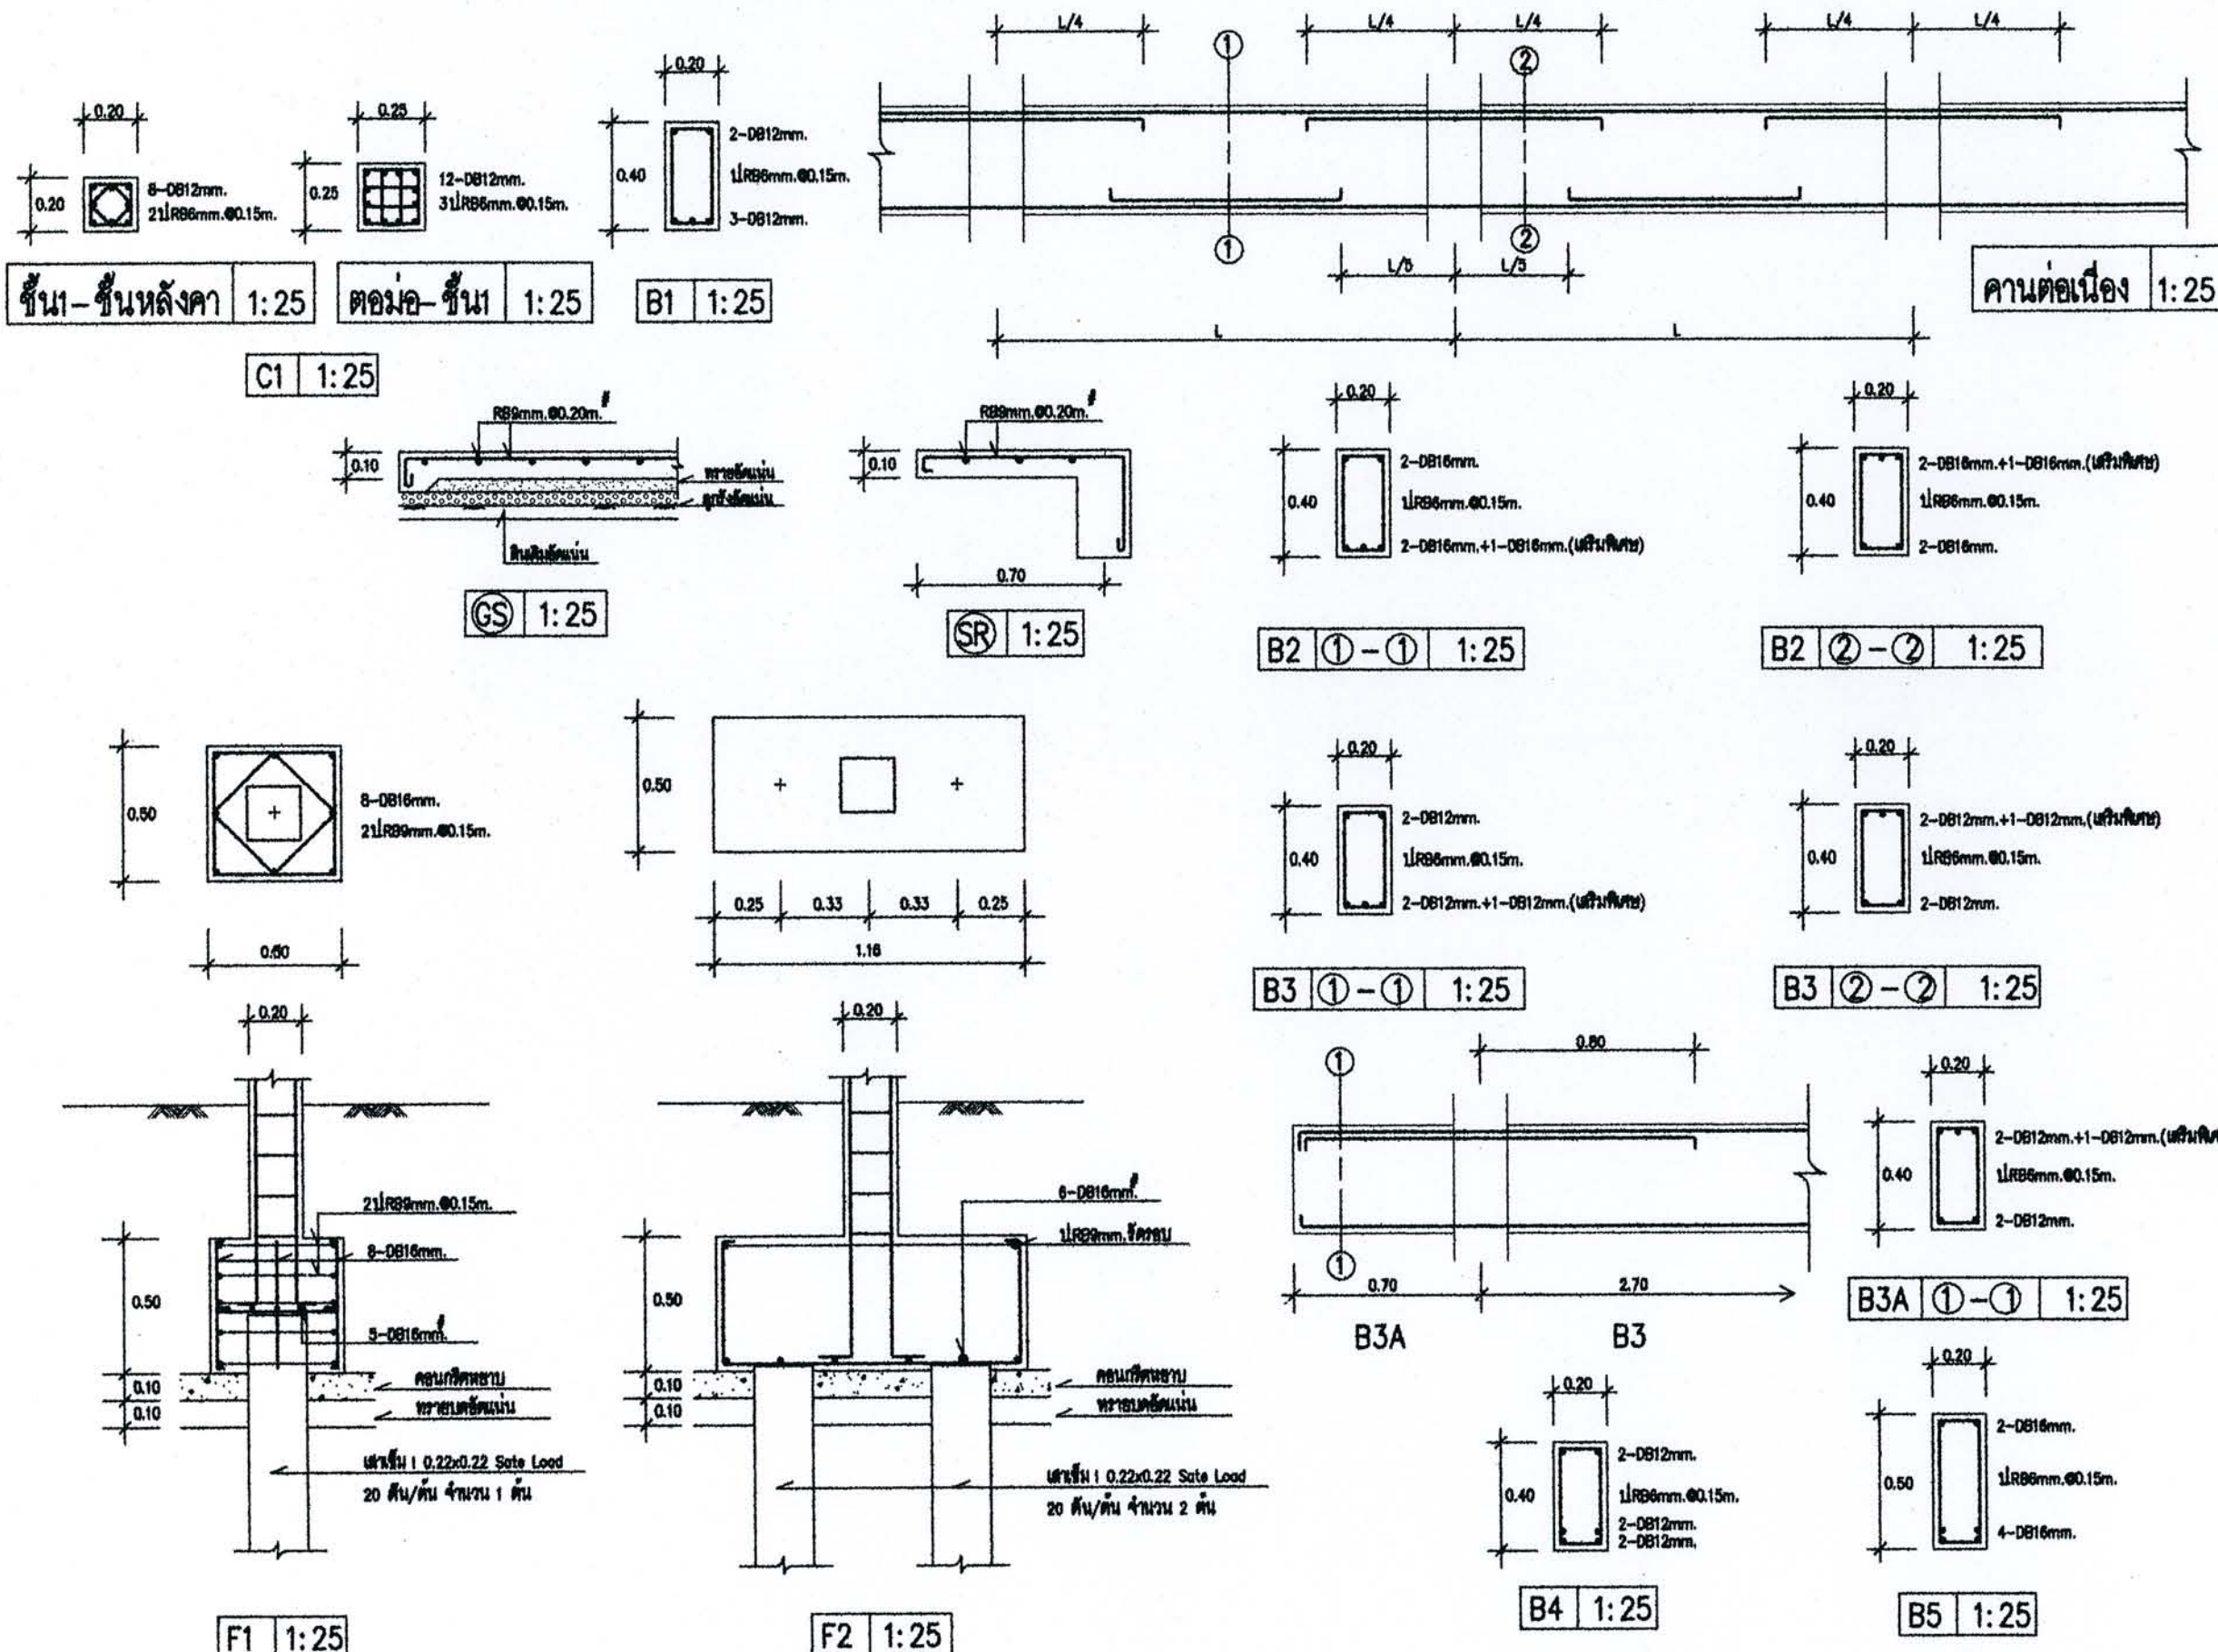



สำนักงานโยธา
กรุงเทพมหานคร

โครงการ
แบบบ้านขี้เฒ่าประชาชน

ตามนโยบาย

น.อ.สุรพงษ์ ปรีติวร ผู้ว่าฯ กทม.
นายแพทย์ เจริญพร รอดูวาทมน
นายธีระชน นิ่มน้อย รอดูวาทมน
นายพงษ์ศักดิ์ แสนลันต์ ปลัดฯ กทม.

ผู้อำนวยการสำนักงานโยธา

นายชุมพล สันภาพ

รองผู้อำนวยการสำนักงานโยธา

นายวิศักดิ์ เดชประพันธ์

ผู้อำนวยการสำนักงานออกแบบ

นายชวรงค์ สมเยี่ยม

หัวหน้ากลุ่มงานสถาปัตยกรรม

นายสินธุ์ชัย บุญวิทย์

หัวหน้ากลุ่มงานวิศวกรรม

นายธีระยุทธ คงศรีชัย

สถาปนิก

นางสาวสุนนมาลย์ กาญจนะ

วิศวกรโครงสร้าง

นายศิริพันธ์ ชิมสสัย

วิศวกรไฟฟ้า

นายศักดิ์พงษ์ จิระดาการ

วิศวกรสุขาภิบาล

นางสาวกมลทิรา สมทรง

วิศวกรเครื่องกล

นายช่างเขียนแบบ

นายสุทธ ปุณณแสน

แบบ
028 บ้านกึ่งปลูก

เจ้าของ

สถานที่

แบบแสดง
แบบขยายโครงสร้าง 2

มาตราส่วน 1:75


FILE : วันที่ 24

วันที่ 2553 S-05 24

คิดค้น ปรับปรุงแบบ รวมแผ่น


32

รายการแก้ไขแบบ

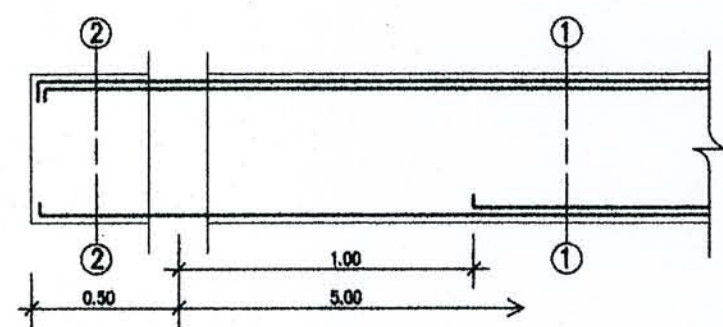


B6A

B6

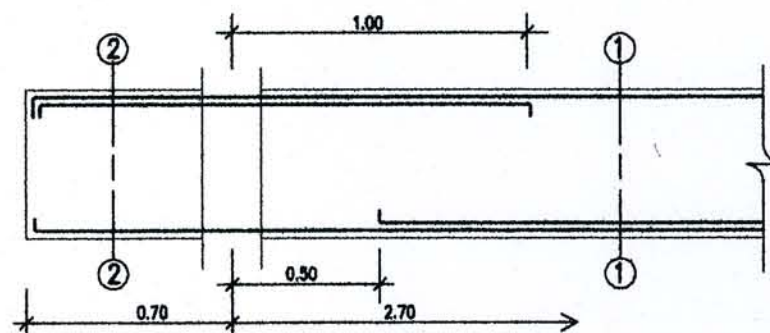


B7A


B7

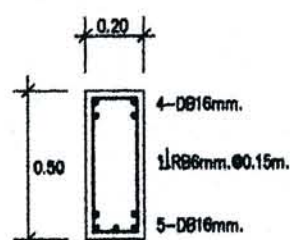


B8 1:25

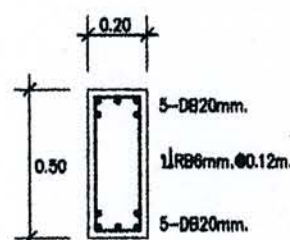


B9 1:25

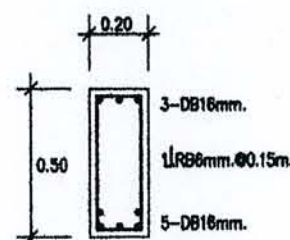

B10 1:25

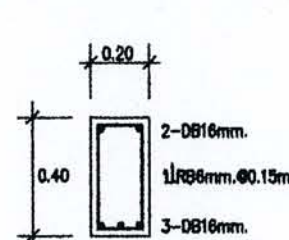


B11 1:25

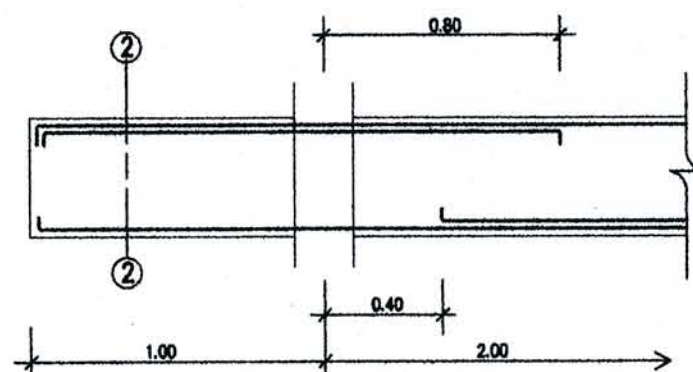


B12A


B12

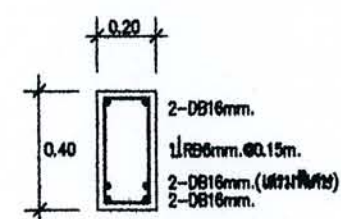


B12 ①-① 1:25

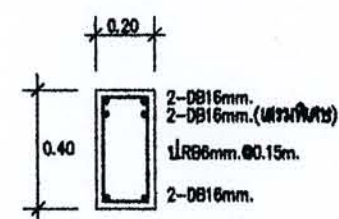


B12A ②-② 1:25

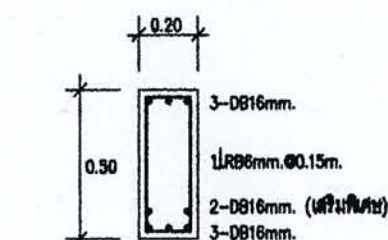


B6 ①-① 1:25

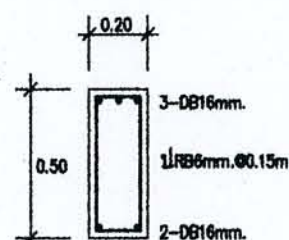


B6A ②-② 1:25

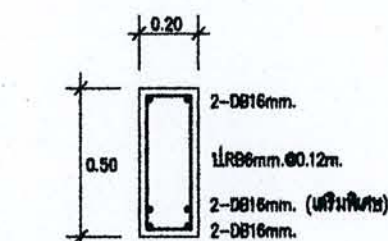


B7 ①-① 1:25

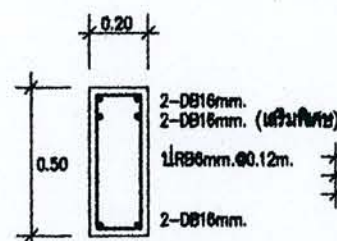

B7A ②-② 1:25

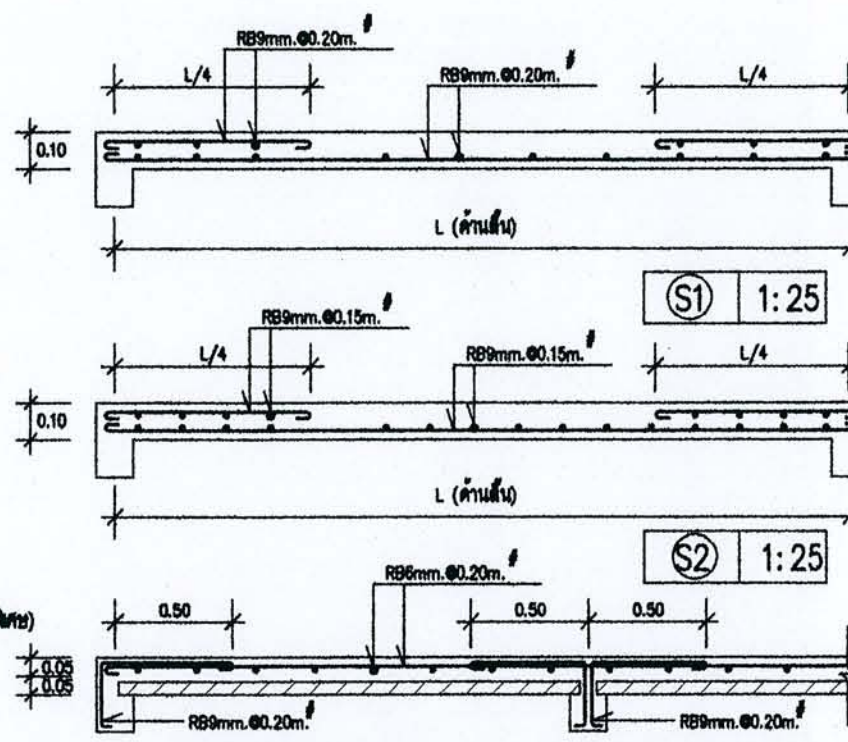

พื้นล่างฐานแบบหล่อเรียบสามารถรับน้ำหนัก
บรรทุกได้ไม่น้อยกว่า 150 kg/ก.ม.

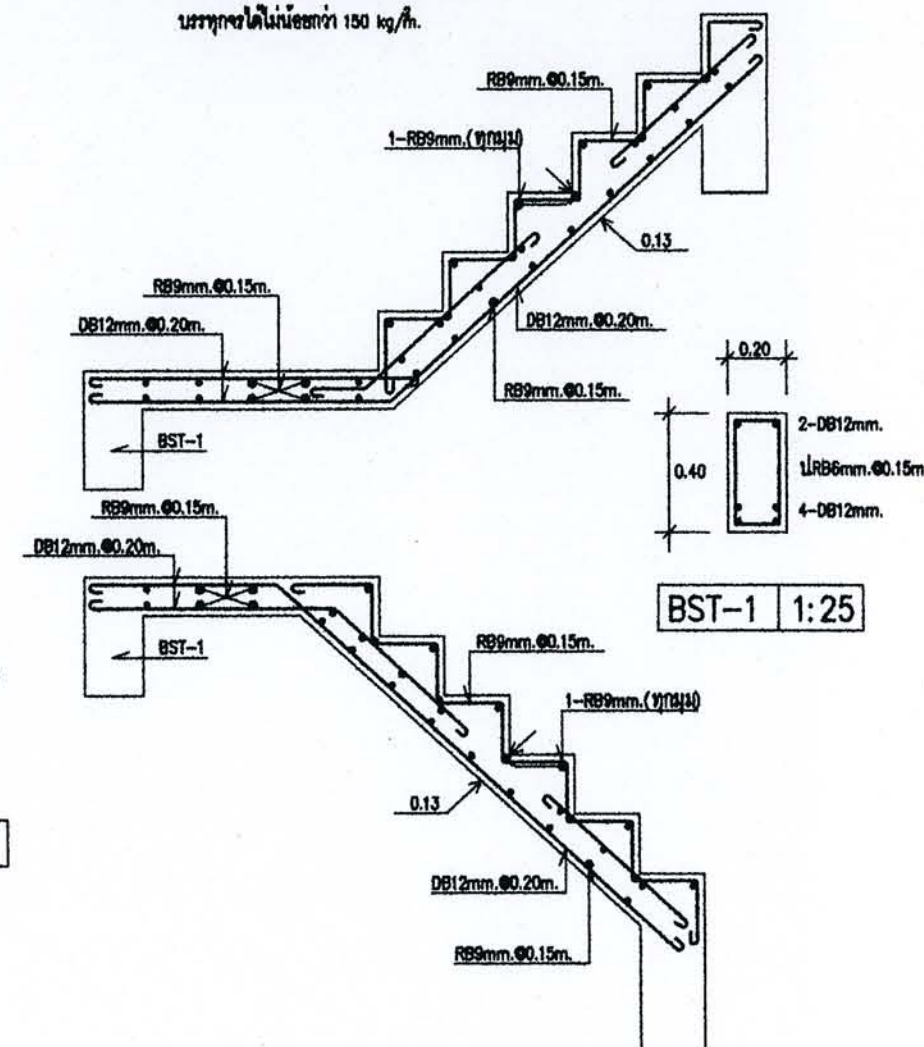

BST-1 1:25



สำนักงาน
กรุงเทพมหานคร

โครงการ
แบบบ้านชั้นเดียวประชาชน

ตามนโยบาย

น.ร. จุฬาลงกรณ์มหาวิทยาลัย
นายพรเทพ เศรษฐกิจ รองผู้อำนวยการ
นายธีระชน นิ่มนิตย์ รองผู้อำนวยการ
นายพงษ์ศักดิ์ แสนสิน ปัสดาภรณ์

ผู้อำนวยการสำนักงาน
นายชุมพล อัมภพ
รองผู้อำนวยการสำนักงาน
นายวิศักดิ์ เดชประพันธ์
ผู้อำนวยการสำนักงานออกแบบ
นายสุรพงศ์ แสนเยี่ยม
หัวหน้ากลุ่มงานสถาปัตยกรรม
นายสินธุ์ชัย บุญภิรักษ์
หัวหน้ากลุ่มงานวิศวกรรม
นายธีระยุทธ คงสวัสดิ์ไชย

สถาปนิก
นางสาวสุนนภาภรณ์ กาญจนะ
วิศวกรโครงสร้าง
นายศิริพงษ์ พิมพ์ใหญ่
วิศวกรไฟฟ้า
นายศักดิ์พงษ์ ชีระนคร
วิศวกรสุขาภิบาล
นางสาวณณชิตา สมพยอม
วิศวกรเครื่องกล

นายช่างเขียนแบบ
นายณัฐพงศ์ ณรงค์บุญชูพงศ์

แบบ
บ้านกึ่งอพยพ

เจ้าของ
สถานที่

แบบแสดง
แปลนไฟฟ้าแสงสว่าง และ
แปลนเดินไฟฟ้า โทรศัพท์ โทรทัศน์
โทรทัศน์ ชั้นล่าง

มาตราส่วน 1:75


FILE : เลขที่ 26

วันที่ 2553 E-02 26

ชนิดสถาปัตยกรรม

32


รายการแนบแบบ

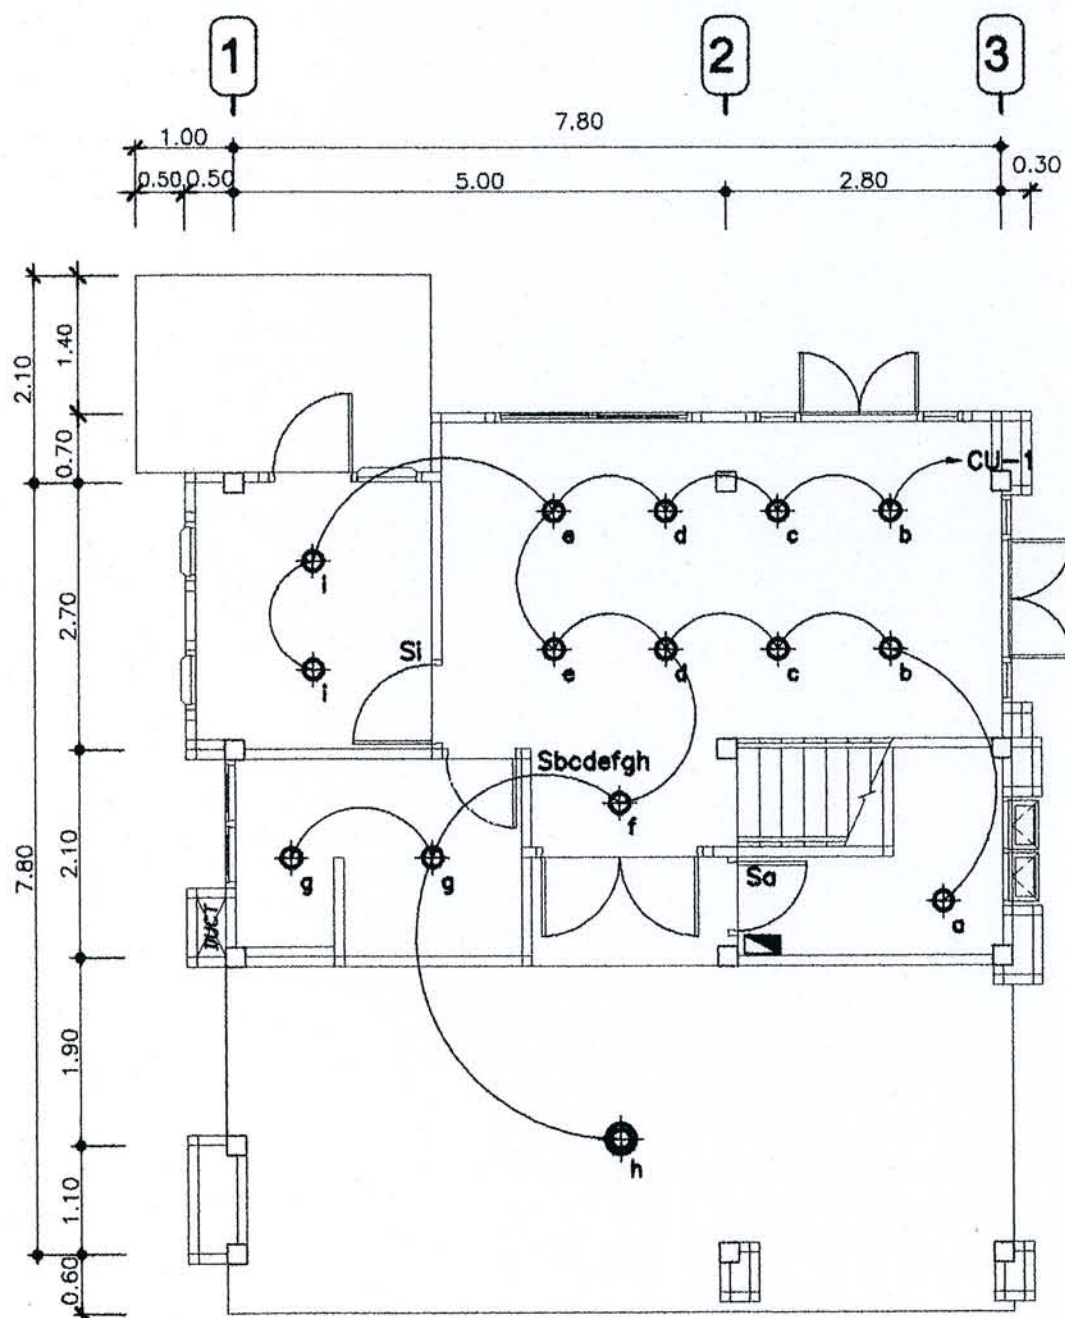

แปลนไฟฟ้าแสงสว่างชั้นล่าง

มาตราส่วน

1:75

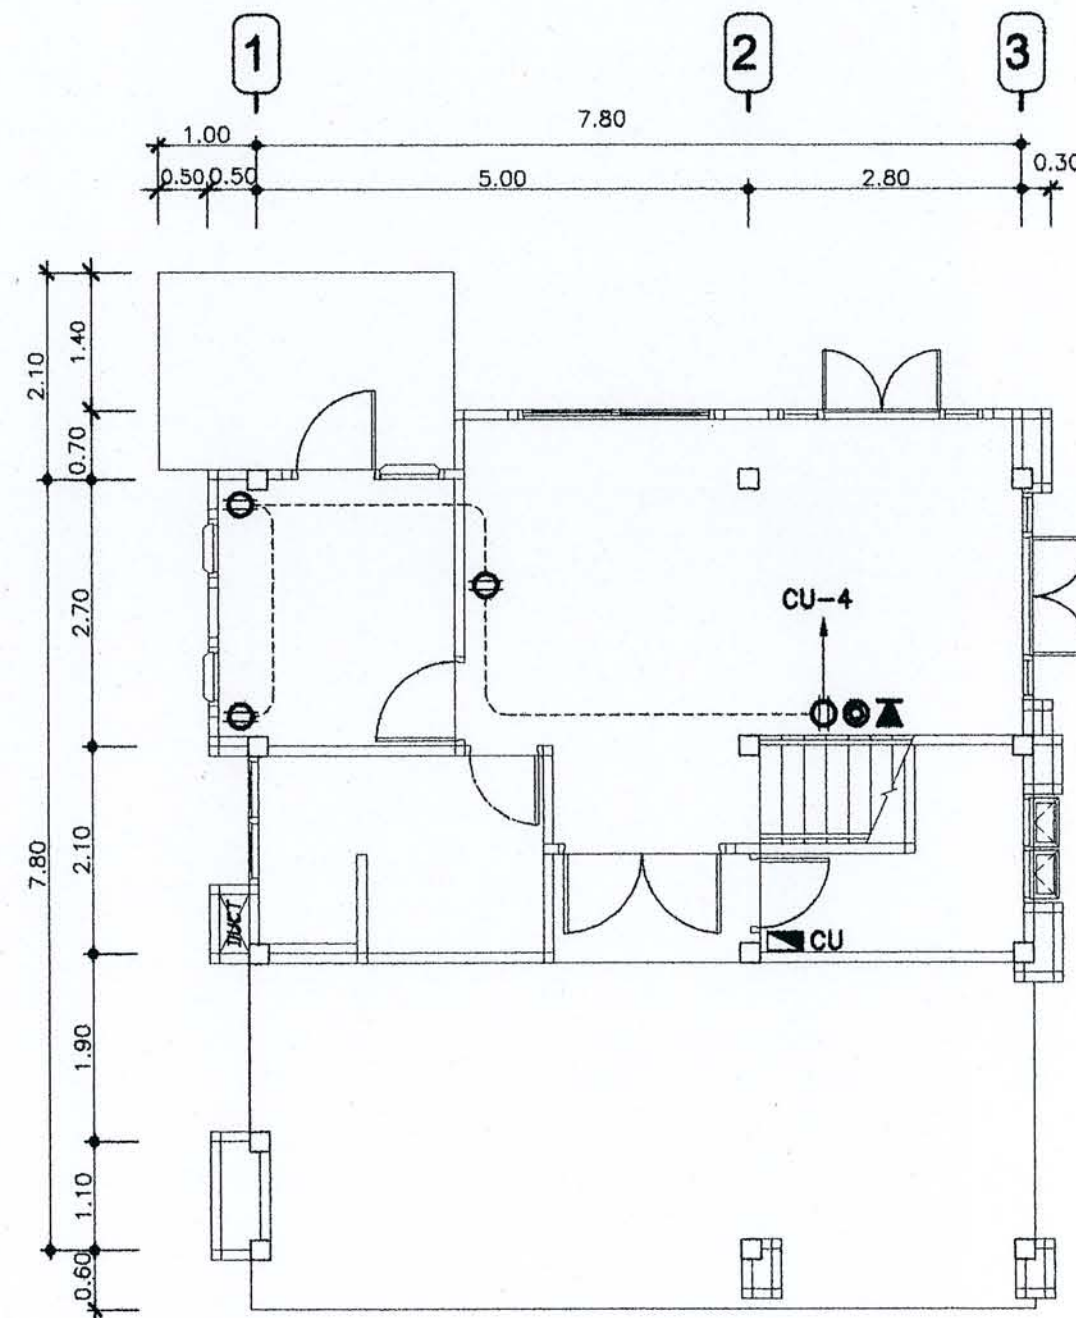

แปลนเดินไฟฟ้า โทรศัพท์ โทรทัศน์ ชั้นล่าง

มาตราส่วน

1:75



สำนักงาน
การประถมศึกษา
กรุงเทพมหานคร

โครงการ
แบบบ้านชั้นเดียวประชาชน

ตามนโยบาย

ม.ร.ว.สุขุมพันธุ์ บริพัตร ผู้ว่าฯ กทม.
นายพรเทพ เศรษฐ์ประสิทธิ์ รองผู้ว่าฯ กทม.
นายธีระชน มโนชัยพิสัย รองผู้ว่าฯ กทม.
นายพงษ์ศักดิ์ เตมียาห์ ปลัดฯ กทม.

ผู้อำนวยการสำนักงาน
นายจตุรนต์ ตันภักดี
รองผู้อำนวยการสำนักงาน
นายวิวัฒน์ เตชะประสิทธิ์
ผู้อำนวยการสำนักงานออกแบบ
นายจตุรนต์ ตันภักดี
หัวหน้ากลุ่มงานสถาปัตยกรรม
นายสันติชัย บุญภิรักษ์
หัวหน้ากลุ่มงานวิศวกรรม
นายธีระยุทธ คงสวัสดิ์ชัย

สถาปนิก
นางสาวสุนันทา กัญจนะ
วิศวกรโครงสร้าง
นายศิริชัย พิมพ์ไทย
วิศวกรไฟฟ้า
นายวิวัฒน์ จิตต์ธนากร
วิศวกรสุขาภิบาล
นางสาวกมลทิรา สมทอง
วิศวกรเครื่องกล

นายช่างเขียนแบบ
นายณัฐพงศ์ ณรงค์บุญชู

แบบ
บ้านกัลปพฤกษ์

เจ้าของ

สถานที่

แบบแสดง

แปลนไฟฟ้าแสงสว่าง และ
แปลนเดินไฟฟ้า โทรศัพท์
โทรศัพท์ ชั้นที่ 2

มาตราส่วน 1:75




FILE : เลขที่ 27

วันที่ 25 ธันวาคม 2553 E-03 27

ชื่อสถาปนิก/บริษัท

32


รายการแก้ไขแบบ

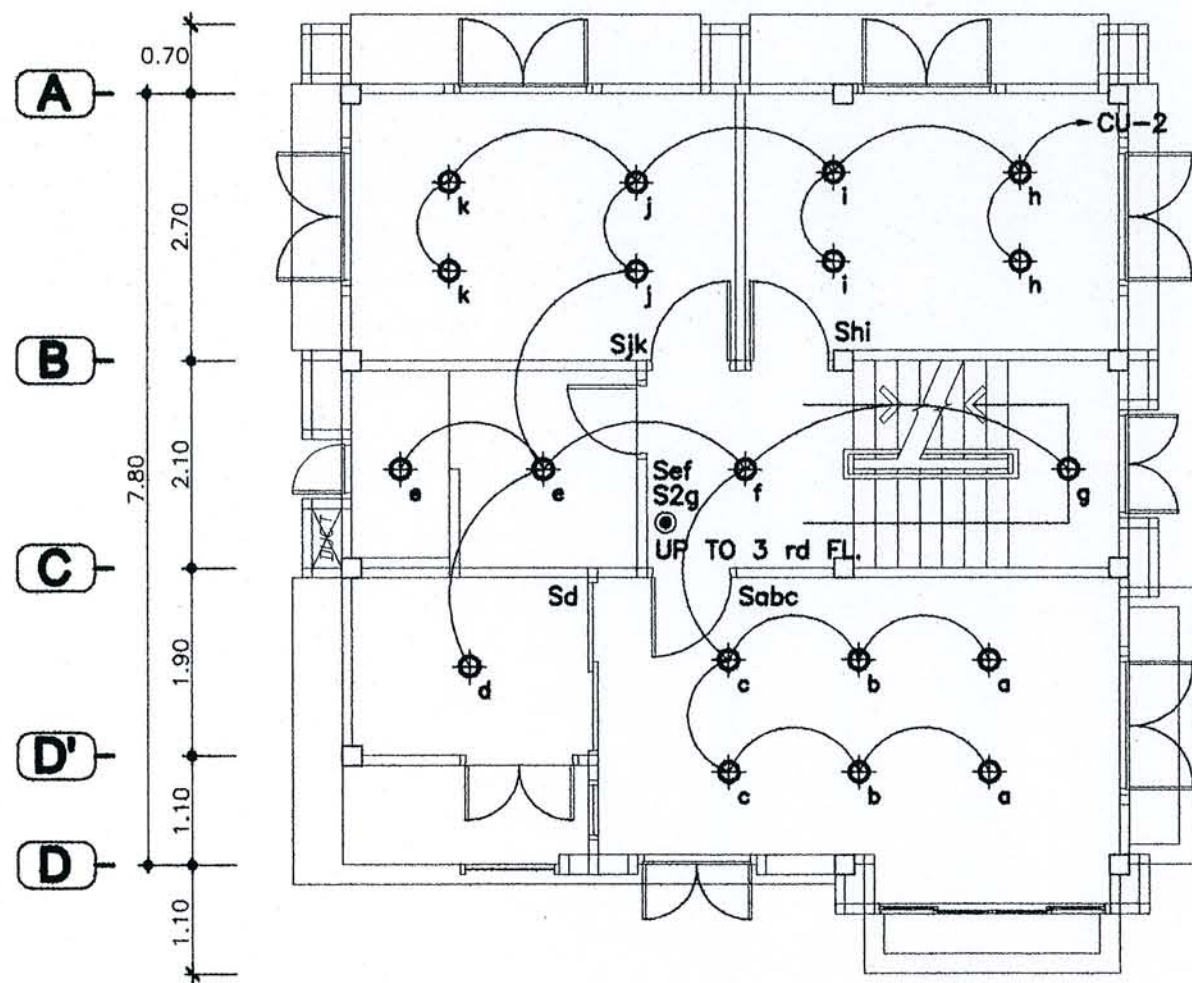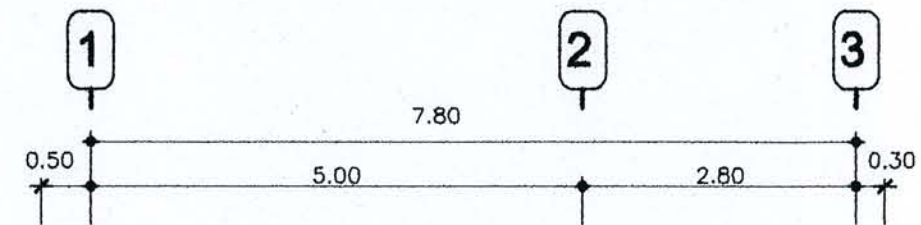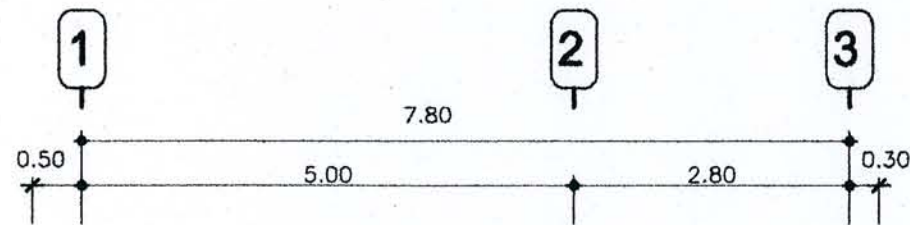

แปลนไฟฟ้าแสงสว่างชั้นที่ 2

มาตราส่วน

1:75

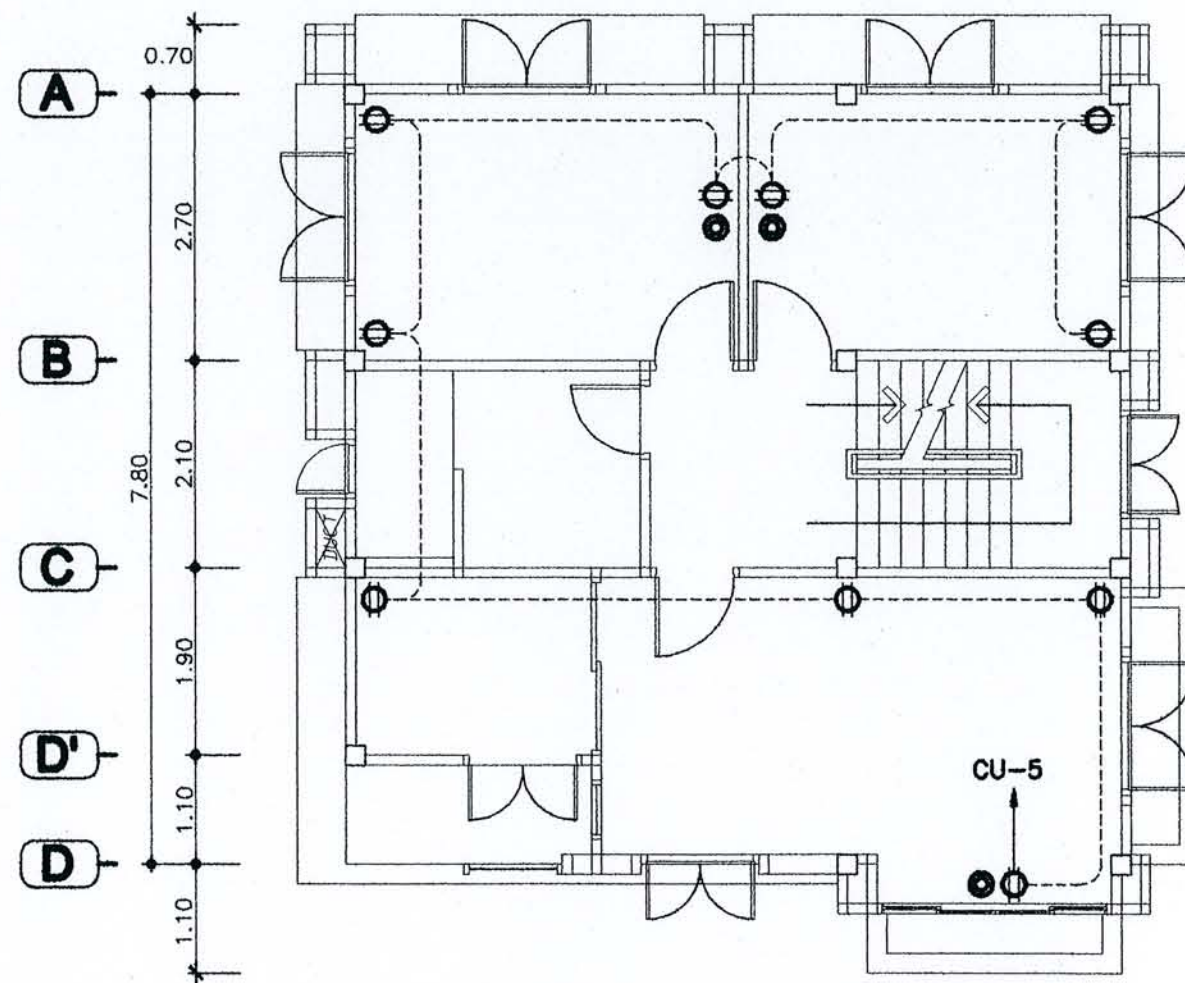

แปลนเดินไฟฟ้า โทรศัพท์ ชั้นที่ 2

มาตราส่วน

1:75



สำนักงาน
กรุงเทพมหานคร

โครงการ
แบบบ้านขึ้นเพื่อประชาชน

ตามนโยบาย
ม.ร.ว.สุขุมพันธุ์ บริพัตร ผู้ว่าฯ กทม.
นายพรหม พรหมน้อย รองผู้ว่าฯ กทม.
นายธีระชน นิมมิทธิ์ รองผู้ว่าฯ กทม.
นายพงศ์ภัฏ ปะนังค์ ปลัดฯ กทม.

ผู้อำนวยการสำนักงาน
นายชุมพล สำนาค
รองผู้อำนวยการสำนักงาน
นายพิทักษ์ เติมประพันธ์
ผู้อำนวยการสำนักงานออกแบบ
นายสุรศักดิ์ สันติธรรม
หัวหน้ากลุ่มงานสถาปัตยกรรม
นายสันติสุข บุญมี
หัวหน้ากลุ่มงานวิศวกรรม
นายธีระยุทธ คงสวัสดิ์

สถาปนิก
นางสาวสุเมธมาศ กาญจนะ
วิศวกรโครงสร้าง
นายศิริสิทธิ์ วัฒนชัย
วิศวกรไฟฟ้า
นายศักดิ์พงษ์ ชื่นระชากร
วิศวกรสุขาภิบาล
นางสาวรณิศา สอนทอง
วิศวกรเครื่องกล

นายช่างเขียนแบบ
นายณัฐพงศ์ ณรงค์บุญชู




แบบ
บ้านกัลปพฤกษ์
เจ้าของ
สถานที่

แบบแสดง
แปลนไฟฟ้าแสงสว่าง และ
แปลนเดินไฟฟ้า โทรศัพท์
โทรศัพท์ ชั้นที่ 3

มาตราส่วน 1:75

FILE :	เลขที่	แผ่นที่
วันที่ 10 ตุลาคม 2553	E-04	28
ชุดสถาปัตย์	รวมแผ่น	32


รายการแก้ไขแบบ

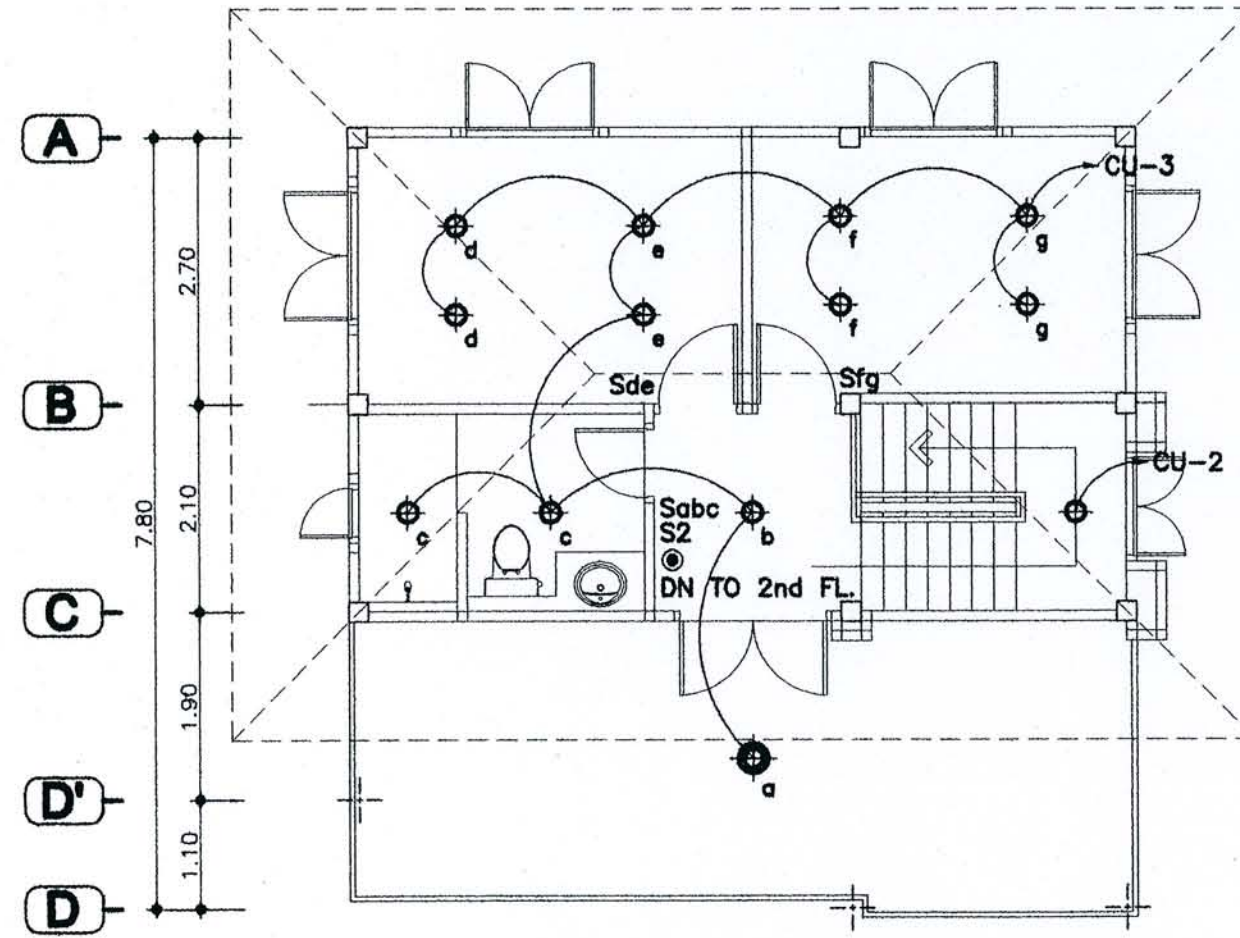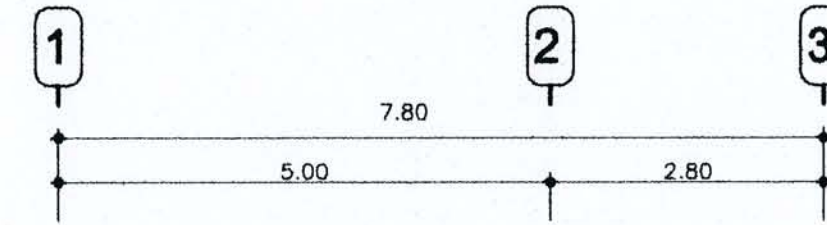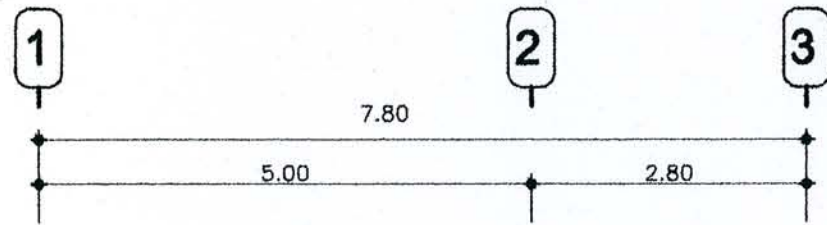

แปลนไฟฟ้าแสงสว่างชั้นที่ 3

มาตราส่วน

1:75

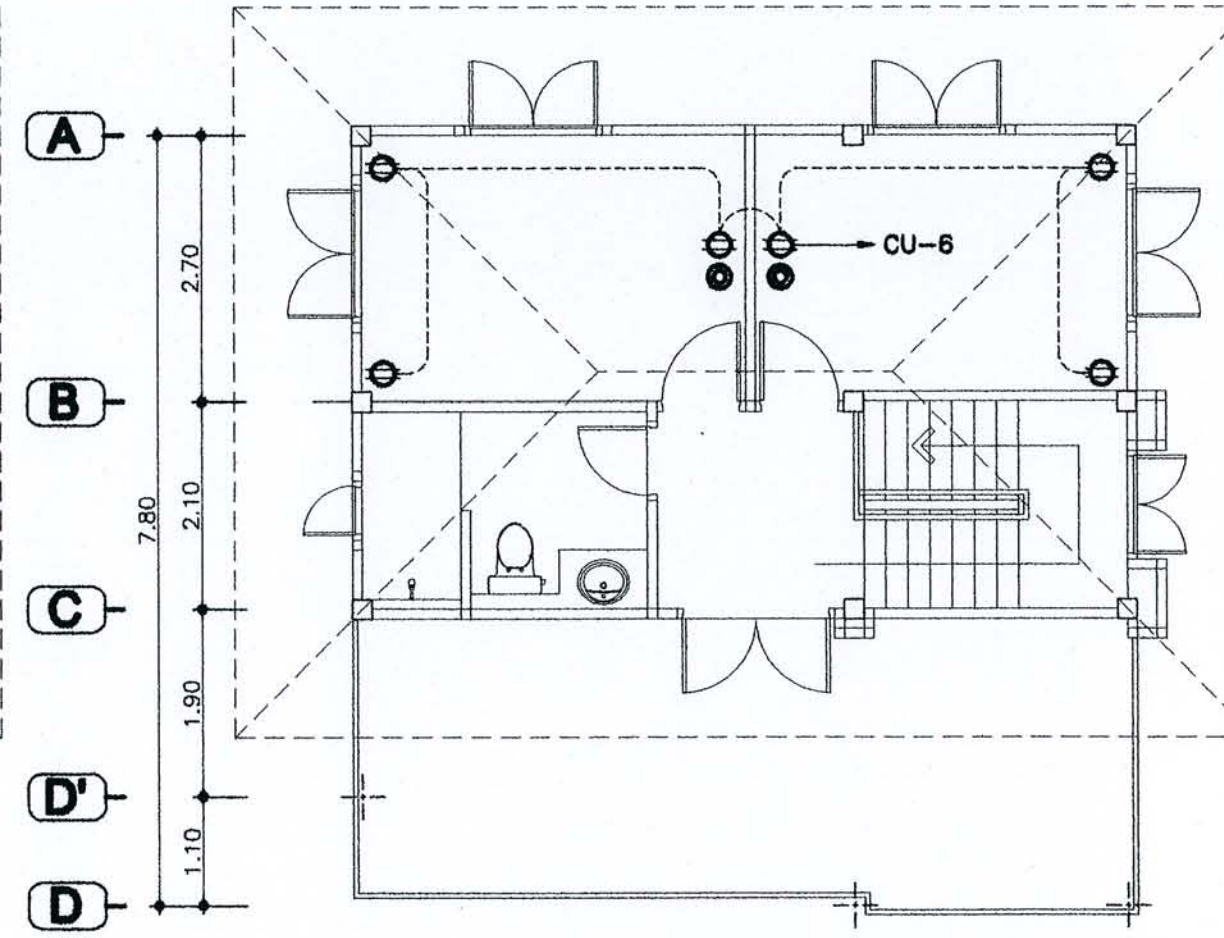

แปลนเดินไฟฟ้า โทรศัพท์ ชั้นที่ 3

มาตราส่วน

1:75



สำนักงานโยธา
กรุงเทพมหานคร

โครงการ
แบบบ้านขึ้นเพื่อประชาชน

ตามนโยบาย

นางจุฑามาศ บริพัตร ผู้ว่าฯ กทม.
นายพรเทพ เศรษฐ์ รักษาราชการ
นายธีระชน มโนชัยกุล รักษาราชการ
นายพงษ์ศักดิ์ แสนสิน ปลัด กทม.

ผู้ดำเนินการสำนักงานโยธา

นายจุฑามาศ บริพัตร
รองผู้อำนวยการสำนักงานโยธา
นายพริษฐ์ วัชรสินธุ์
ผู้อำนวยการสำนักงานออกแบบ
นายชัชวาลย์ แสนสิน
หัวหน้ากลุ่มงานสถาปัตยกรรม
นายสันติสุข บุญปัทม
หัวหน้ากลุ่มงานวิศวกรรม
นายธีระยุทธ คงสวัสดิ์

สถาปนิก

นางสาวสุนทรภรณ์ กาญจนะ
วิศวกรโครงสร้าง
นายศิริชัย ชินสินธุ์
วิศวกรไฟฟ้า
นายศิริพงษ์ จิระเดชาร
วิศวกรสุขาภิบาล
นางสาวณัฏฐา สอนทอง
วิศวกรเครื่องกล

นายชาญชัยแบบ
นายบุญชัย วงศ์วิญญู

แบบ
028 บ้านกิลปพฤกษ์

เจ้าของ

สถานที่

แบบแสดง

แปลนระบบท่อน้ำประปา และ
แปลนระบบสุขาภิบาลและท่อน้ำฝน

มาตราส่วน 1:75


FILE : เลขที่ 29

วันที่ 2553 SN-01

ผู้จัดทำ 32

รวมเล่ม


รายการแก้ไขแบบ

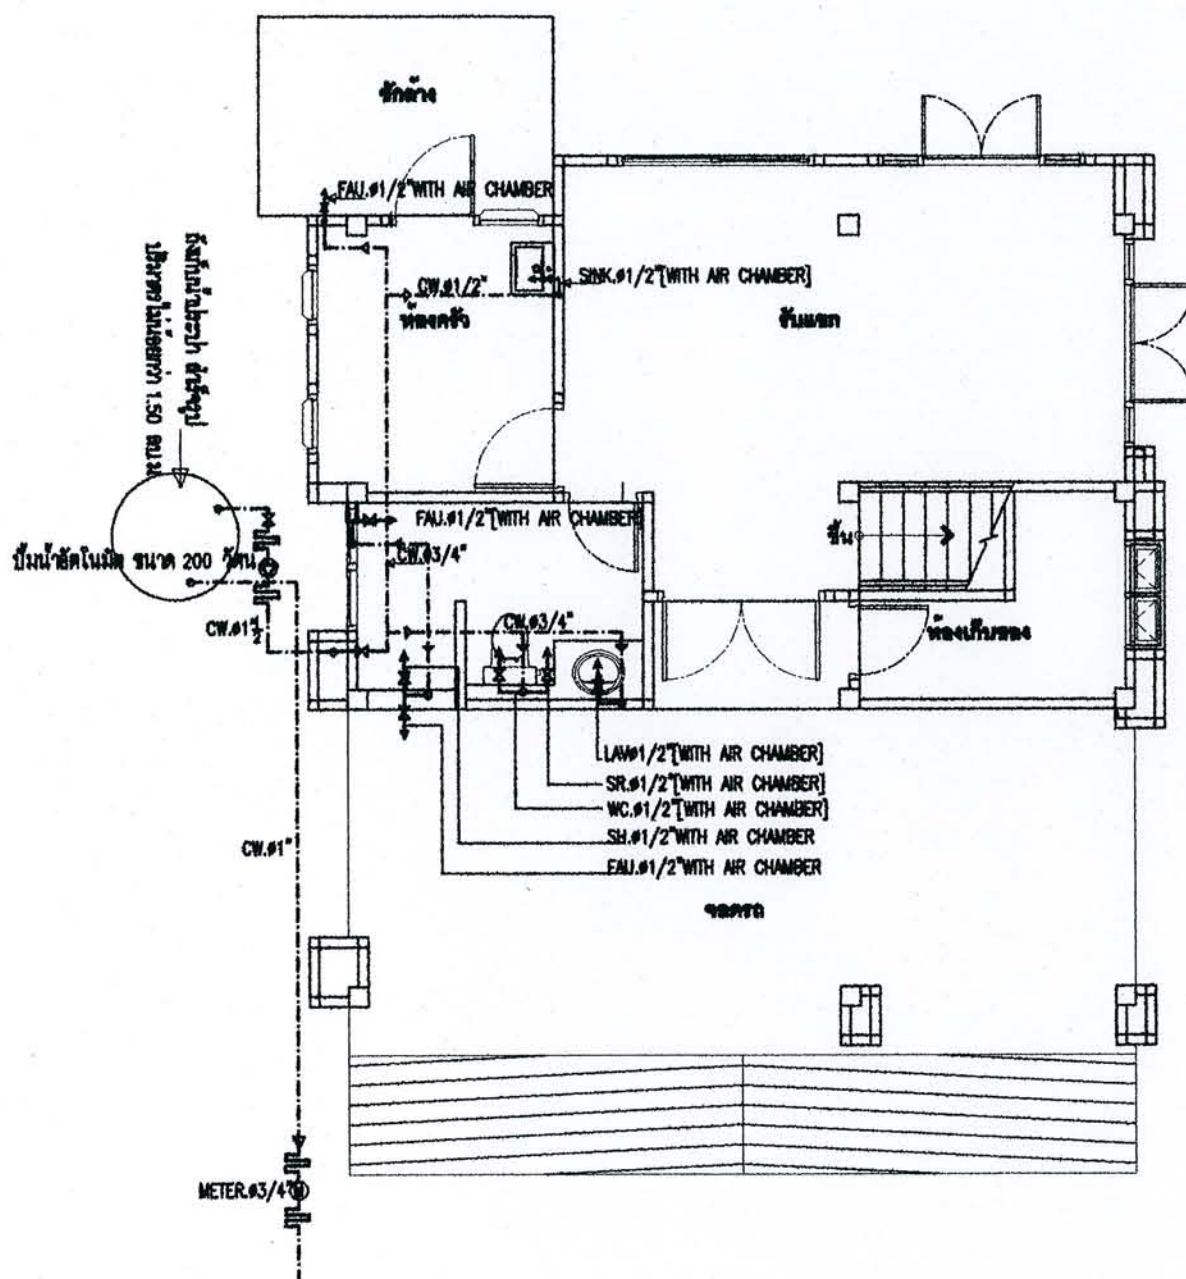

แปลนระบบท่อน้ำประปา ชั้นล่าง

มาตราส่วน

1:75

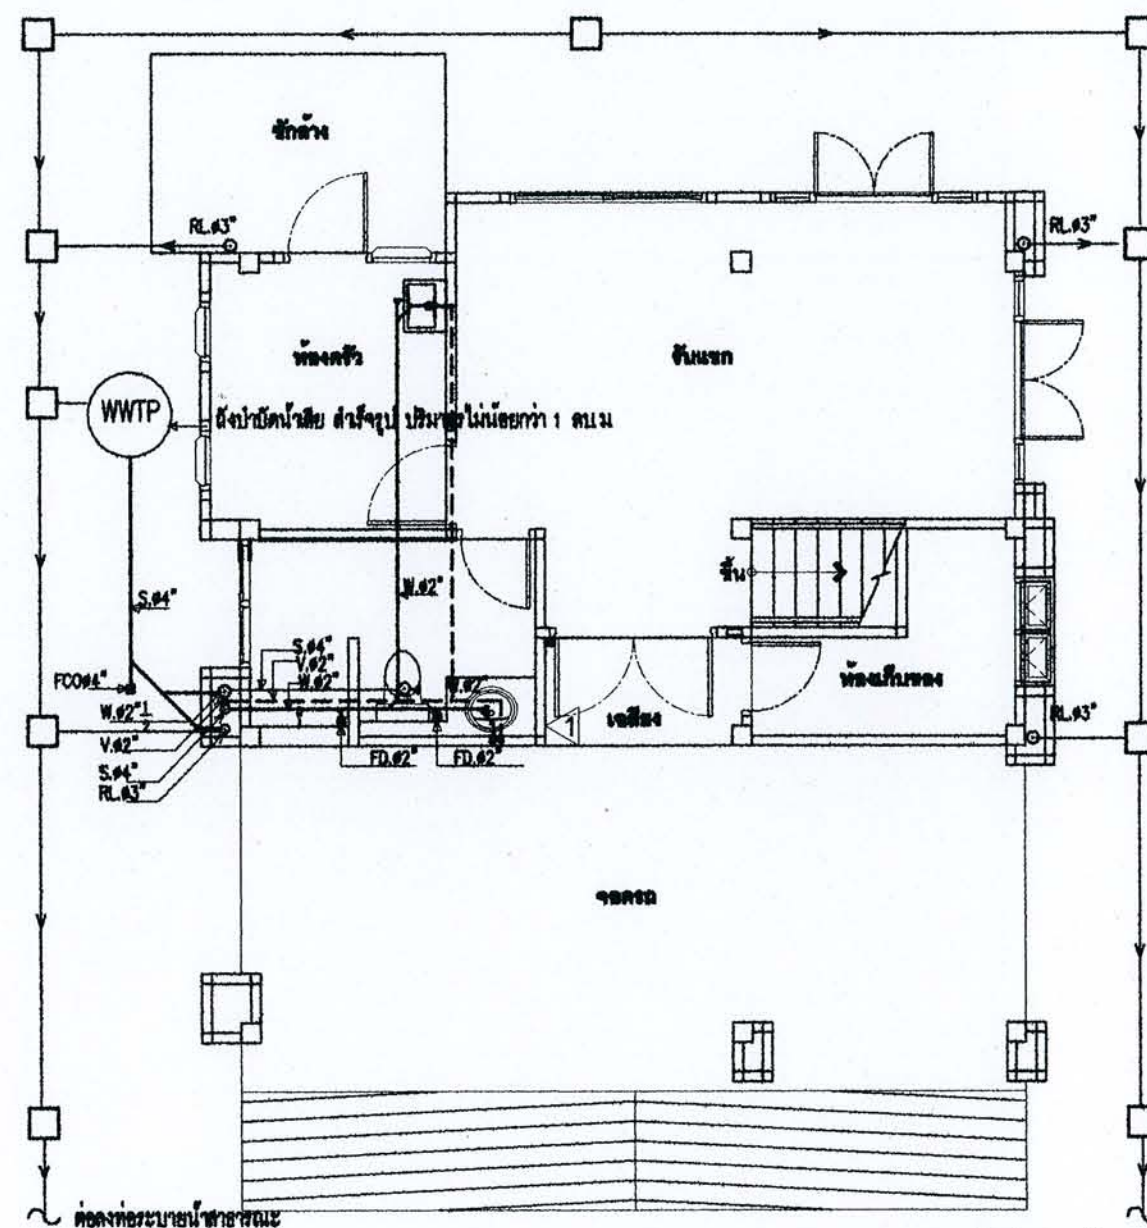

แปลนระบบสุขาภิบาลและท่อน้ำฝน ชั้นล่าง

มาตราส่วน

1:75

□ บ่อพักน้ำทิ้ง สล. ชนิดสี่เหลี่ยม
0.40 x 0.40 ม. พร้อมท่อน้ำ สล. ขนาด 0.20 ม.

VTR #2 ปลั๊กที่ระดับพื้นดินชั้น 3



สำนักงานโยธา
กรุงเทพมหานคร

โครงการ
แบบบ้านยี่สิบเอ็ดประชาชน

ตามนโยบาย

น.ร.สุเมธพันธ์ ศรีพิตร ผู้ว่าฯกทม.
นายแพทย์ เจริญพร รอดวิภาทมน
นายธีระชน นิ่มนัยศิริ รอดวิภาทมน
นายพงษ์ศักดิ์ แสนลิ้น ปัสลาภทมน

ผู้อำนวยการสำนักงานโยธา
นายชุมพล สำนกาศ
รองผู้อำนวยการสำนักงานโยธา
นายวิศักดิ์ เลิศประพันธ์
ผู้อำนวยการสำนักงานออกแบบ
นายสุรศักดิ์ แสนเยี่ยม
หัวหน้ากลุ่มงานสถาปัตยกรรม
นายสินธุ์ชัย บุญนิกร
หัวหน้ากลุ่มงานวิศวกรรม
นายธีระยุทธ คงทรัพย์เสถียร

สถาปนิก
นางสาวสุนนมาลย์ กาญจนะ
วิศวกรโครงสร้าง
นายจิรพันธ์ จันทิพย์
วิศวกรไฟฟ้า
นายวิศพงษ์ จิระธนากร
วิศวกรสุขาภิบาล
นางสาวณัฏฐา สมพยอม
วิศวกรเครื่องกล

นายช่างเขียนแบบ
นายบุญชัย วงษ์เจริญ

แบบ
028 บ้านกิตติพญักษ์

เจ้าของ

สถานที่

แบบแปลน
แปลนระบบท่อน้ำประปา และ
แปลนระบบสุขาภิบาลและท่อน้ำฝน ชั้น 2

มาตราส่วน 1:75


FILE : เลขที่

วันที่ 2553 SN-02 30

คิดค่าปรับแบบ

รวม 32


รายการแก้ไขแบบ

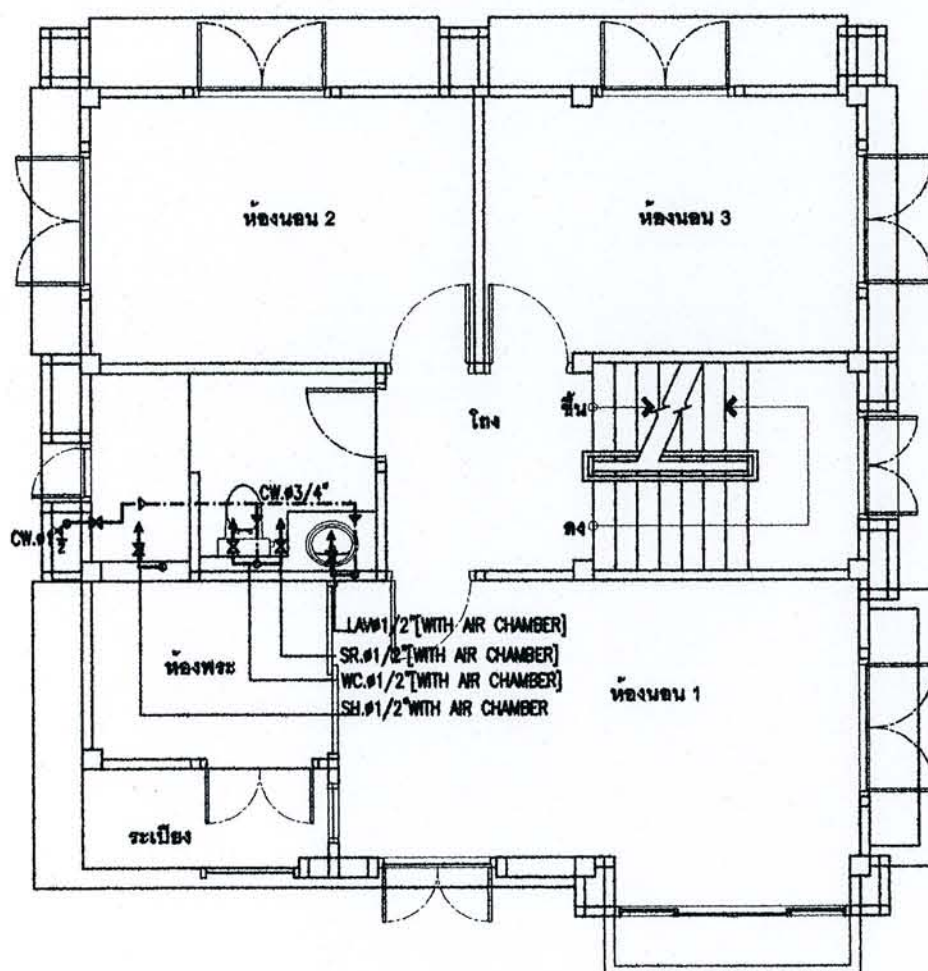

แปลนระบบท่อน้ำประปา ชั้น 2

มาตราส่วน

1:75

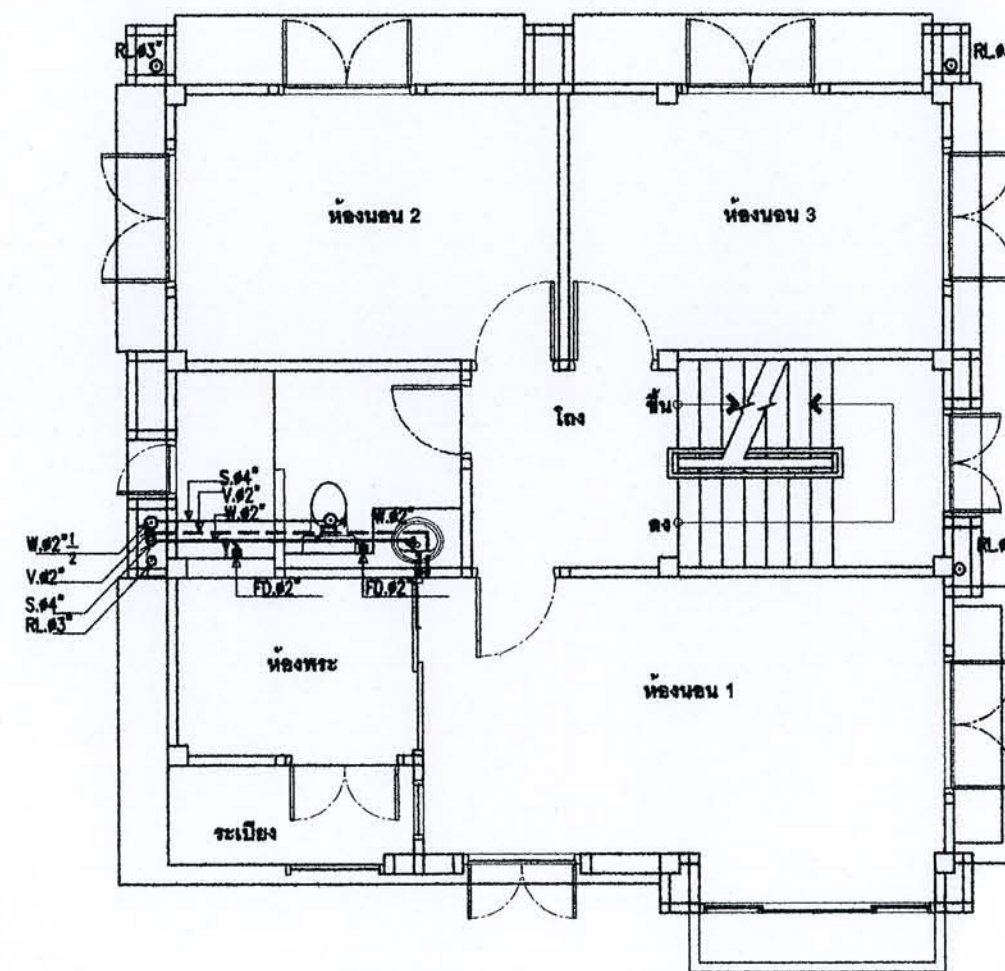

แปลนระบบสุขาภิบาลและท่อน้ำฝน ชั้น 2

มาตราส่วน

1:75



สำนักงานโยธา
กรุงเทพมหานคร

โครงการ
แบบบ้านยืมเพื่อประชาชน

ตามนโยบาย

ม.ร.ว.สุขุมพันธุ์ บริพัตร ผู้ว่าฯกทม.
นายแพทย์ เจริญพร รอดูวาทกน
นายธีระชัย มโนชัยบุตร รอดูวาทกน
นายพงษ์ศักดิ์ เตมียะกุล ปัสสยาภณ

ผู้อำนวยการสำนักงานโยธา
นายชุมพล ตันภักดี
รองผู้อำนวยการสำนักงานโยธา
นายวิฑิต ธีรประพันธ์
ผู้อำนวยการสำนักงานออกแบบ
นายสุวิทย์ ตันชัย
หัวหน้ากลุ่มงานสถาปัตยกรรม
นายสันติชัย บุญภิรักษ์
หัวหน้ากลุ่มงานวิศวกรรม
นายธีระยุทธ คงศิริเกียรติ

สถาปนิก
นางสาวสมนารถ กาญจนะ
วิศวกรโครงสร้าง
นายศิริพงษ์ วัฒนชัย
วิศวกรไฟฟ้า
นายวิฑิตพงษ์ ธีระเดชาก
วิศวกรสุขาภิบาล
นางสาวณิชา สมทอง
วิศวกรเครื่องกล

นายช่างเขียนแบบ
นายบุญชัย วงษ์พิญ

แบบ
028 บ้านกิลพฤกษ์

เจ้าของ


สถานที่

แบบแสดง
แปลนระบบท่อน้ำประปา และ
แปลนระบบสุขาภิบาลและท่อน้ำฝน ชั้น 3

ขนาดส่วน 1:75

FILE :	เลขที่	แผ่นที่
วันที่ 2553	SN-03	31
คัดลอกไปพิมพ์แบบ		รวมแผ่น
		32


รายการแก้ไขแบบ

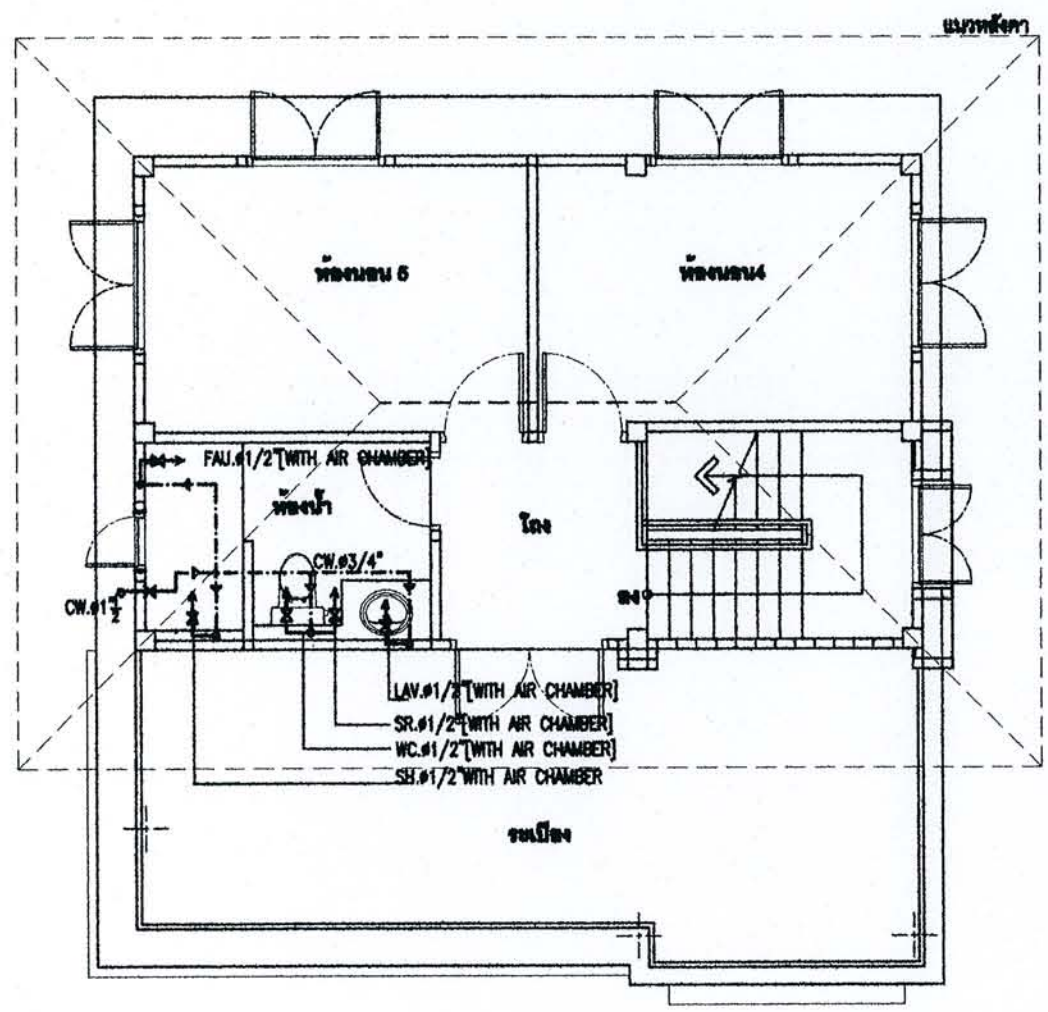

แปลนระบบท่อน้ำประปา ชั้น 3

ขนาดส่วน

1:75

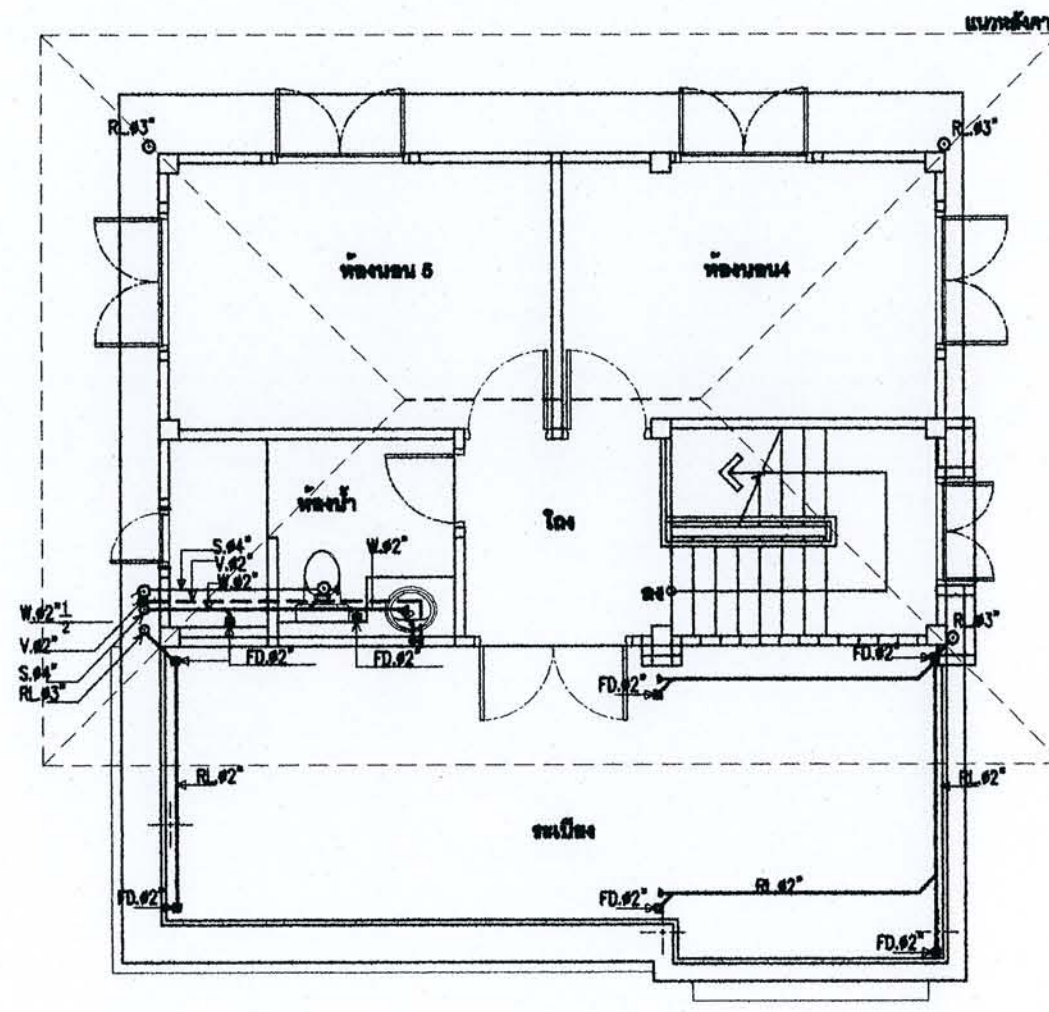

แปลนระบบสุขาภิบาลและท่อน้ำฝน ชั้น 3

ขนาดส่วน

1:75



สำนักงานโยธา
กรุงเทพมหานคร

โครงการ
แบบบ้านยี่สิบสี่ประชาชน

ตามนโยบาย

น.ร.สุจินต์ ปิณฑะ ผู้อำนวยการ
นายพรหม เทระไพฑูรย์ รองผู้อำนวยการ
นายธีระชน นโมโสมพิบูลย์ รองผู้อำนวยการ
นายพงษ์ศักดิ์ แสนลิ้นดี ปลัดเขต

ผู้อำนวยการสำนักงานโยธา
นายจุมพล คำภักดิ์
รองผู้อำนวยการสำนักงานโยธา
นายพินิจ เปียประพันธ์
ผู้อำนวยการสำนักงานออกแบบ
นายสุรศักดิ์ สันติธรรม
หัวหน้ากลุ่มงานสถาปัตยกรรม
นายสันติสุข บุญมีรักษ์
หัวหน้ากลุ่มงานวิศวกรรม
นายธีระยุทธ คงสวัสดิ์ชัย

สถาปนิก
นางสาวสุมนมดล กาญจนะ
วิศวกรโครงสร้าง
นายศิริสิทธิ์ วัฒนไชย
วิศวกรไฟฟ้า
นายกิตติพงษ์ จิระธนากร
วิศวกรสุขาภิบาล
นางสาวสมจิรา สมน้อม
วิศวกรเครื่องกล

นายช่างเขียนแบบ
นายบุญชัย วงษ์เจริญ

แบบ
028 บ้านกัลปพฤกษ์

เจ้าของ

สถานที่

แบบแสดง

แปลนระบบสุขาภิบาลและท่อน้ำฝน ชั้นหลังคา

มาตราส่วน 1:75


FILE : วันที่ 25/04/2553

วันที่ 25/04/2553

คัดลอกแบบไปใช้

รวมแผ่น 32

รายการแก้ไขแบบ

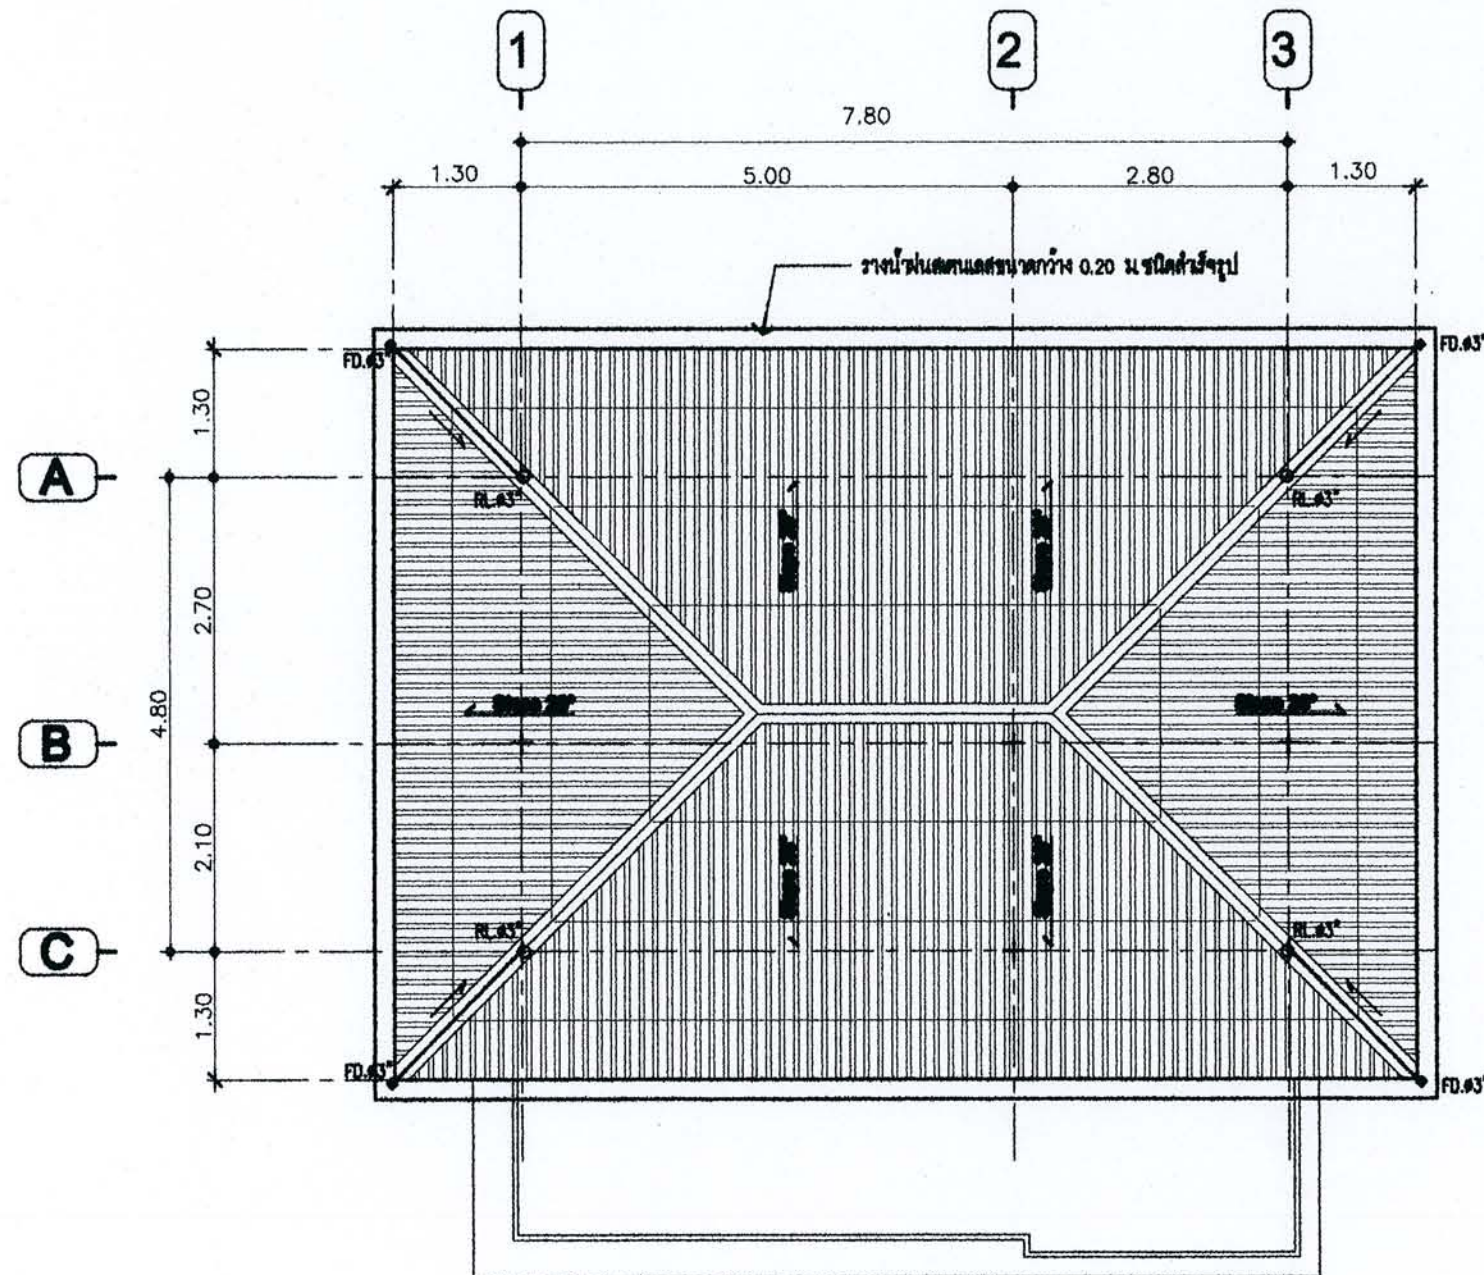

แปลนระบบสุขาภิบาลและท่อน้ำฝน ชั้นหลังคา

มาตราส่วน

1:75