



บ้านผู้ประสบภัย ๓

รายการแบบสถาปัตยกรรม (A)	รายการแบบโครงสร้าง (S)	รายการสัญลักษณ์ประกอบแบบ	 โครงการแบบอาคารเพื่อประชาชน ไทยช่วยไทย แบบ บ้านผู้ประสบภัย 3 ห้องสุขารวม สำนักสถาปัตยกรรม สถาปนิก สถาปนิก สถาปนิก สถาปนิก สำนักวิศวกรรมโครงสร้างและงานระบบ วิศวกร วิศวกร วิศวกรไฟฟ้าและเครื่องกล วิศวกร สุขาภิบาล อนุมัติ (นายสว่าง ศรีสุคนธ์) อธิบดีกรมโยธาธิการและผังเมือง แสดงแบบ สารบัญแบบ สัญลักษณ์ประกอบแบบ มาตราส่วน วัน/เดือน/ปี 21 พ.ย. 2546 เลขที่แบบ ม.บ.462099 แผ่นที่ จำนวนแผ่น
A-01 สารบัญแบบ,สัญลักษณ์ประกอบแบบ	S-01 แปลนฐานราก	1 ก แนวเวลา ระยะศูนย์กลางถึงศูนย์กลาง ระยะศูนย์กลางถึงริม ระยะจากริมถึงริม	
A-02 รายการประกอบแบบ	S-02 แปลน เสา คานและพื้น	① ใช้กำหนดหมายเลขประตู ในแบบเพื่ออ้างอิงถึง	
A-03 ผังบริเวณ	S-03 แปลน โครงหลังคา	① ใช้กำหนดหมายเลขหน้าต่าง ในแบบเพื่ออ้างอิงถึง	
A-04 แปลนพื้นที่อาคาร	S-04 แบบขยายการเสริมเหล็ก ฐานราก,ตอม่อ ,พื้น	1 A-NO. แบบขยายทั่วไป แผ่นที่ ที่อ้างอิงไปถึง	
A-05 แปลนหลังคา	S-05 แบบขยายการเสริมเหล็ก ฐานราก, คาน	N 3 A-NO. 2 A-NO. 4 A-NO. 1 A-NO. 1,2,3,4 ชื่อรูปด้าน แสดงทิศทางตามแนวข้อบอก A-NO. แผ่นที่ ที่อ้างอิงไปถึง A A-NO. A A-NO. ชื่อรูปตัดอาคาร แผ่นที่ ที่อ้างอิงไปถึง	
A-06 รูปด้าน 1,2,3,4	S-06 แบบขยาย โครงสร้าง	ผนังก่ออิฐครึ่งแผ่น ผนังกระฉก คอนกรีต กระฉก เหล็ก ดิน ไม้แต่งผิว SLOPE 1:100 แนวเอียงลาด	
A-07 รูปตัด 1,2 ,แบบขยายประตู-หน้าต่าง	S-07 แบบขยาย โครงหลังคา T1		
A-08 แปลนอาคารสุขา ,แบบหลังคา	S-08 แบบขยาย โครงหลังคา T2		
A-09 รูปด้าน 1,2			
A-10 รูปด้าน 3,4			
A-11 รูปตัด 1,2			
A-12 แบบขยายห้องน้ำ			
	รายการแบบวิศวกรรมไฟฟ้า(E)		
	E-01 สัญลักษณ์,รายละเอียด,DIAGRAM		
	E-02 แปลนไฟฟ้าแสงสว่าง		
	รายการแบบวิศวกรรมสุขาภิบาล(SN)		
	SN-01 แปลนสุขาภิบาล ,สัญลักษณ์		
	SN-02 แบบขยายบ่อเกรอะ		

หมายเหตุ แบบที่แสดงอยู่นี้ได้รับการย่อส่วน เพื่อใช้แสดงผลทางหน้าจอเท่านั้น สำหรับแบบที่ใช้ขออนุญาตก่อสร้าง ให้ถ่ายสำเนาจากหนังสือแบบบ้าน

รายการประกอบแบบอาคารบ้านไทยช่วยไทย บ้านผู้ประสบภัย

1. วัตถุประสงค์

กรมโยธาธิการและผังเมืองมีความประสงค์ทำการออกแบบอาคารเพื่อประชาชนตามดำริของ ฯพณฯนายกรัฐมนตรี และเป็นไปตามนโยบายรัฐบาลเพื่อบริการประชาชน โดยไม่คิดค่าบริการ ออกแบบใดๆทั้งสิ้น

2. รายละเอียดประกอบแบบ

2.1 การวางผังและระดับ

ผู้รับจ้างจะต้องทำการวางผังระดับมาตรฐานให้ถูกต้องเรียบร้อยตามกฎหมายควบคุมอาคาร ก่อนดำเนินการต่อไป

2.2 งานฐานรากและโครงสร้าง ค.ส.ล.

ตามที่ได้กำหนดไว้ในแบบและรายการวิศวกรรมโครงสร้าง ส่วนรายละเอียดอื่นๆ ให้ดำเนินการตามมาตรฐานงานก่อสร้าง มยธ.101-มยธ.106

2.3 งานสถาปัตยกรรม

ก. งานพื้น

- พื้น ค.ส.ล. ทำผิวขัดมันเรียบ หรือผิวขัดหยาบ ใช้ปูนซีเมนต์ตามมาตรฐาน เลขที่ มอก.15 เล่มที่ 1-2532
- พื้น ค.ส.ล. ปูกระเบื้องเคลือบผิวด้าน ขนาด 8"x8" ใช้กระเบื้องเซรามิกผิวเคลือบด้าน ตามมาตรฐาน มอก. 37-2529 น้ำยากันซึม ไซ้ของ ที่ผลิตในประเทศ
- พื้นรีวบอร์ดหนา 20 มม. วางบนดงเหล็ก ตามแบบโครงสร้าง

หมายเหตุ การเตรียมผิวพื้นและการปูกระเบื้องให้ทำตามมาตรฐานวิชาชีพช่างที่ดี

ข. งานผนัง

- ผนังทั่วไปก่ออิฐฉาบปูนหรือผนังอิฐก่อเป็นอิฐที่แกร่ง เสาสูงเสมอ ไม่บิดเบี้ยว ต้องพรมน้ำให้ชุ่มก่อนก่อ
- การก่อชนคาน เสา หรือเอ็น ค.ส.ล. ต้องเสียบเหล็ก 6 มม. ทูกระยะไม่เกิน 40 ซม. โดยยื่นออกมา 25 ซม. และฝังในเสา คาน 10 ซม.
- การก่อชนกันเป็นมุม การก่อเว้นช่องสำหรับตีประตูหน้าต่าง และทุกระยะเกิน 2 ม. ตามความยาวของผนังหรือทุกระยะเกิน 3 ม. ให้ทำเอ็น หรือทับหลัง ค.ส.ล. หนาเท่ากับผนัง กว้าง 15 ซม. เสียบเหล็ก 2 RB 6 มม. @ 0.20 ม.
- ผนังไม้เนื้อแข็ง หรือฝาไม้สำเร็จรูป หรือผนังไม้อัดยางบนโครงคร่าวไม้เนื้อแข็ง 1 1/2"x3" @ 0.60 ม. ทา้ำยากันปลวก
- ผนังรีวบอร์ดหนา 8 มม. โครงคร่าวเหล็ก @ 0.60 ม.

ค. งานฝ้า

- ฝ้าเพดานกระเบื้องแผ่นเรียบหนา 4 มม. โครงคร่าวไม้เนื้อแข็ง 1 1/2"x3" @ 0.60 ม. ทา้ำยากันปลวก

ง. งานหลังคา

- โครงหลังคา ตามที่ได้กำหนดไว้ในแบบและรายการวิศวกรรมโครงสร้าง
- วัสดุหลังคา กระเบื้องลูกฟูกลอนเล็ก สีซีเมนต์ ที่ผลิตภายในประเทศ

จ. งานประตู-หน้าต่าง และอุปกรณ์

- รายละเอียดตามระบุในแบบขยายประตู-หน้าต่าง และอุปกรณ์

ฉ. งานห้องน้ำ-ส้วม และสุขภัณฑ์

- รายละเอียดตามระบุในแบบขยายห้องน้ำ-ส้วม สุขภัณฑ์ และอุปกรณ์ประกอบ
- การเดินท่อน้ำประปา-ท่อน้ำทิ้ง-ท่อน้ำส้วม ให้เป็นไปตามงานวิศวกรรมสุขาภิบาล

ช. งานสี

- งานทาสีภายนอก สีทาผนังปูนใช้สีน้ำสำหรับทาสีภายนอก ตาม มอก.272-2531 สีทาภายนอกและไม้ ใช้สีน้ำมันตาม มอก. 327-2538
- งานทาสีภายใน สีทาผนังปูนใช้สีน้ำตาม มอก. 272-2531

หมายเหตุ วัสดุต่างๆดังกล่าวข้างต้น สามารถเปลี่ยนแปลงได้ตามความเหมาะสมและวัตถุประสงค์ของผู้ว่าจ้าง

2.4 งานวิศวกรรมสุขาภิบาล

ให้ติดตั้งตามแบบวิศวกรรมสุขาภิบาลและมาตรฐานการประปาฯ

2.4 งานวิศวกรรมไฟฟ้า

ให้ติดตั้งตามแบบวิศวกรรมไฟฟ้าและมาตรฐานการไฟฟ้าฯ



โครงการแบบอาคารเพื่อประชาชน
ไทยช่วยไทย

แบบ
บ้านผู้ประสบภัย 3 ห้องสุขารวม

สำนักสถาปัตยกรรม
111-1
ผู้อำนวยการสำนัก

สถาปัตยกรรม	สถาปนิก
	สถาปนิก
	สถาปนิก
	สถาปนิก

สำนักวิศวกรรมโครงสร้างและงานระบบ
111-1
ผู้อำนวยการสำนัก

วิศวกรรม	วิศวกร
โครงสร้าง	วิศวกร
วิศวกรรมไฟฟ้า	วิศวกร
และเครื่องกล	วิศวกร
วิศวกรรม	วิศวกร
สุขาภิบาล	วิศวกร

อนุมัติ
111-1
(นายสว่าง ศรีสุคนธ์)
อธิบดีกรมโยธาธิการและผังเมือง

แสดงแบบ
รายการประกอบแบบ

มาตรฐาน

วัน/เดือน/ปี 21 พ.ย. 2546

เลขที่แบบ ม.บ.462099

แผ่นที่ A-02	จำนวนแผ่น 12
-----------------	-----------------

หมายเหตุ แบบที่แสดงอยู่นี้ได้รับการยืมส่วน เพื่อใช้แสดงผลทางหน้าจอเท่านั้น สำหรับแบบที่ใช้ขออนุญาตก่อสร้าง ให้ถ่ายสำเนาจากหนังสือแบบบ้าน

รายละเอียดพื้น


- พ.1 พื้นวิ้วบอร์ด หน้า 0.02 ม. วางบนตงเหล็ก
พ.2 พื้น ค.ส.ล. ผสมน้ำยากันซึม ผิวขัดมันเรียบ

รายละเอียดผนัง

- พ.1 ผนังวิ้วบอร์ด โครงเคร่าเหล็ก
พ.2 ผนังคอนกรีตบล็อก ฉาบเรียบขัดมัน
พ.3 ผนังแผ่นสังกะสี โครงเคร่าเหล็ก

หมายเหตุ

- ผู้รับเหมาต้องเป็นเพียงตัวอย่างเพื่อประมาณราคา
- ค่าก่อสร้างส่วนประกอบอาคารเท่านั้น
- ส่วนรายละเอียดของสถานที่จริง
- ให้กำหนดรายละเอียดของก่อสร้าง
- รางระบายน้ำให้ต่อลงบ่อพักภายนอก หรือที่ที่กำหนดให้

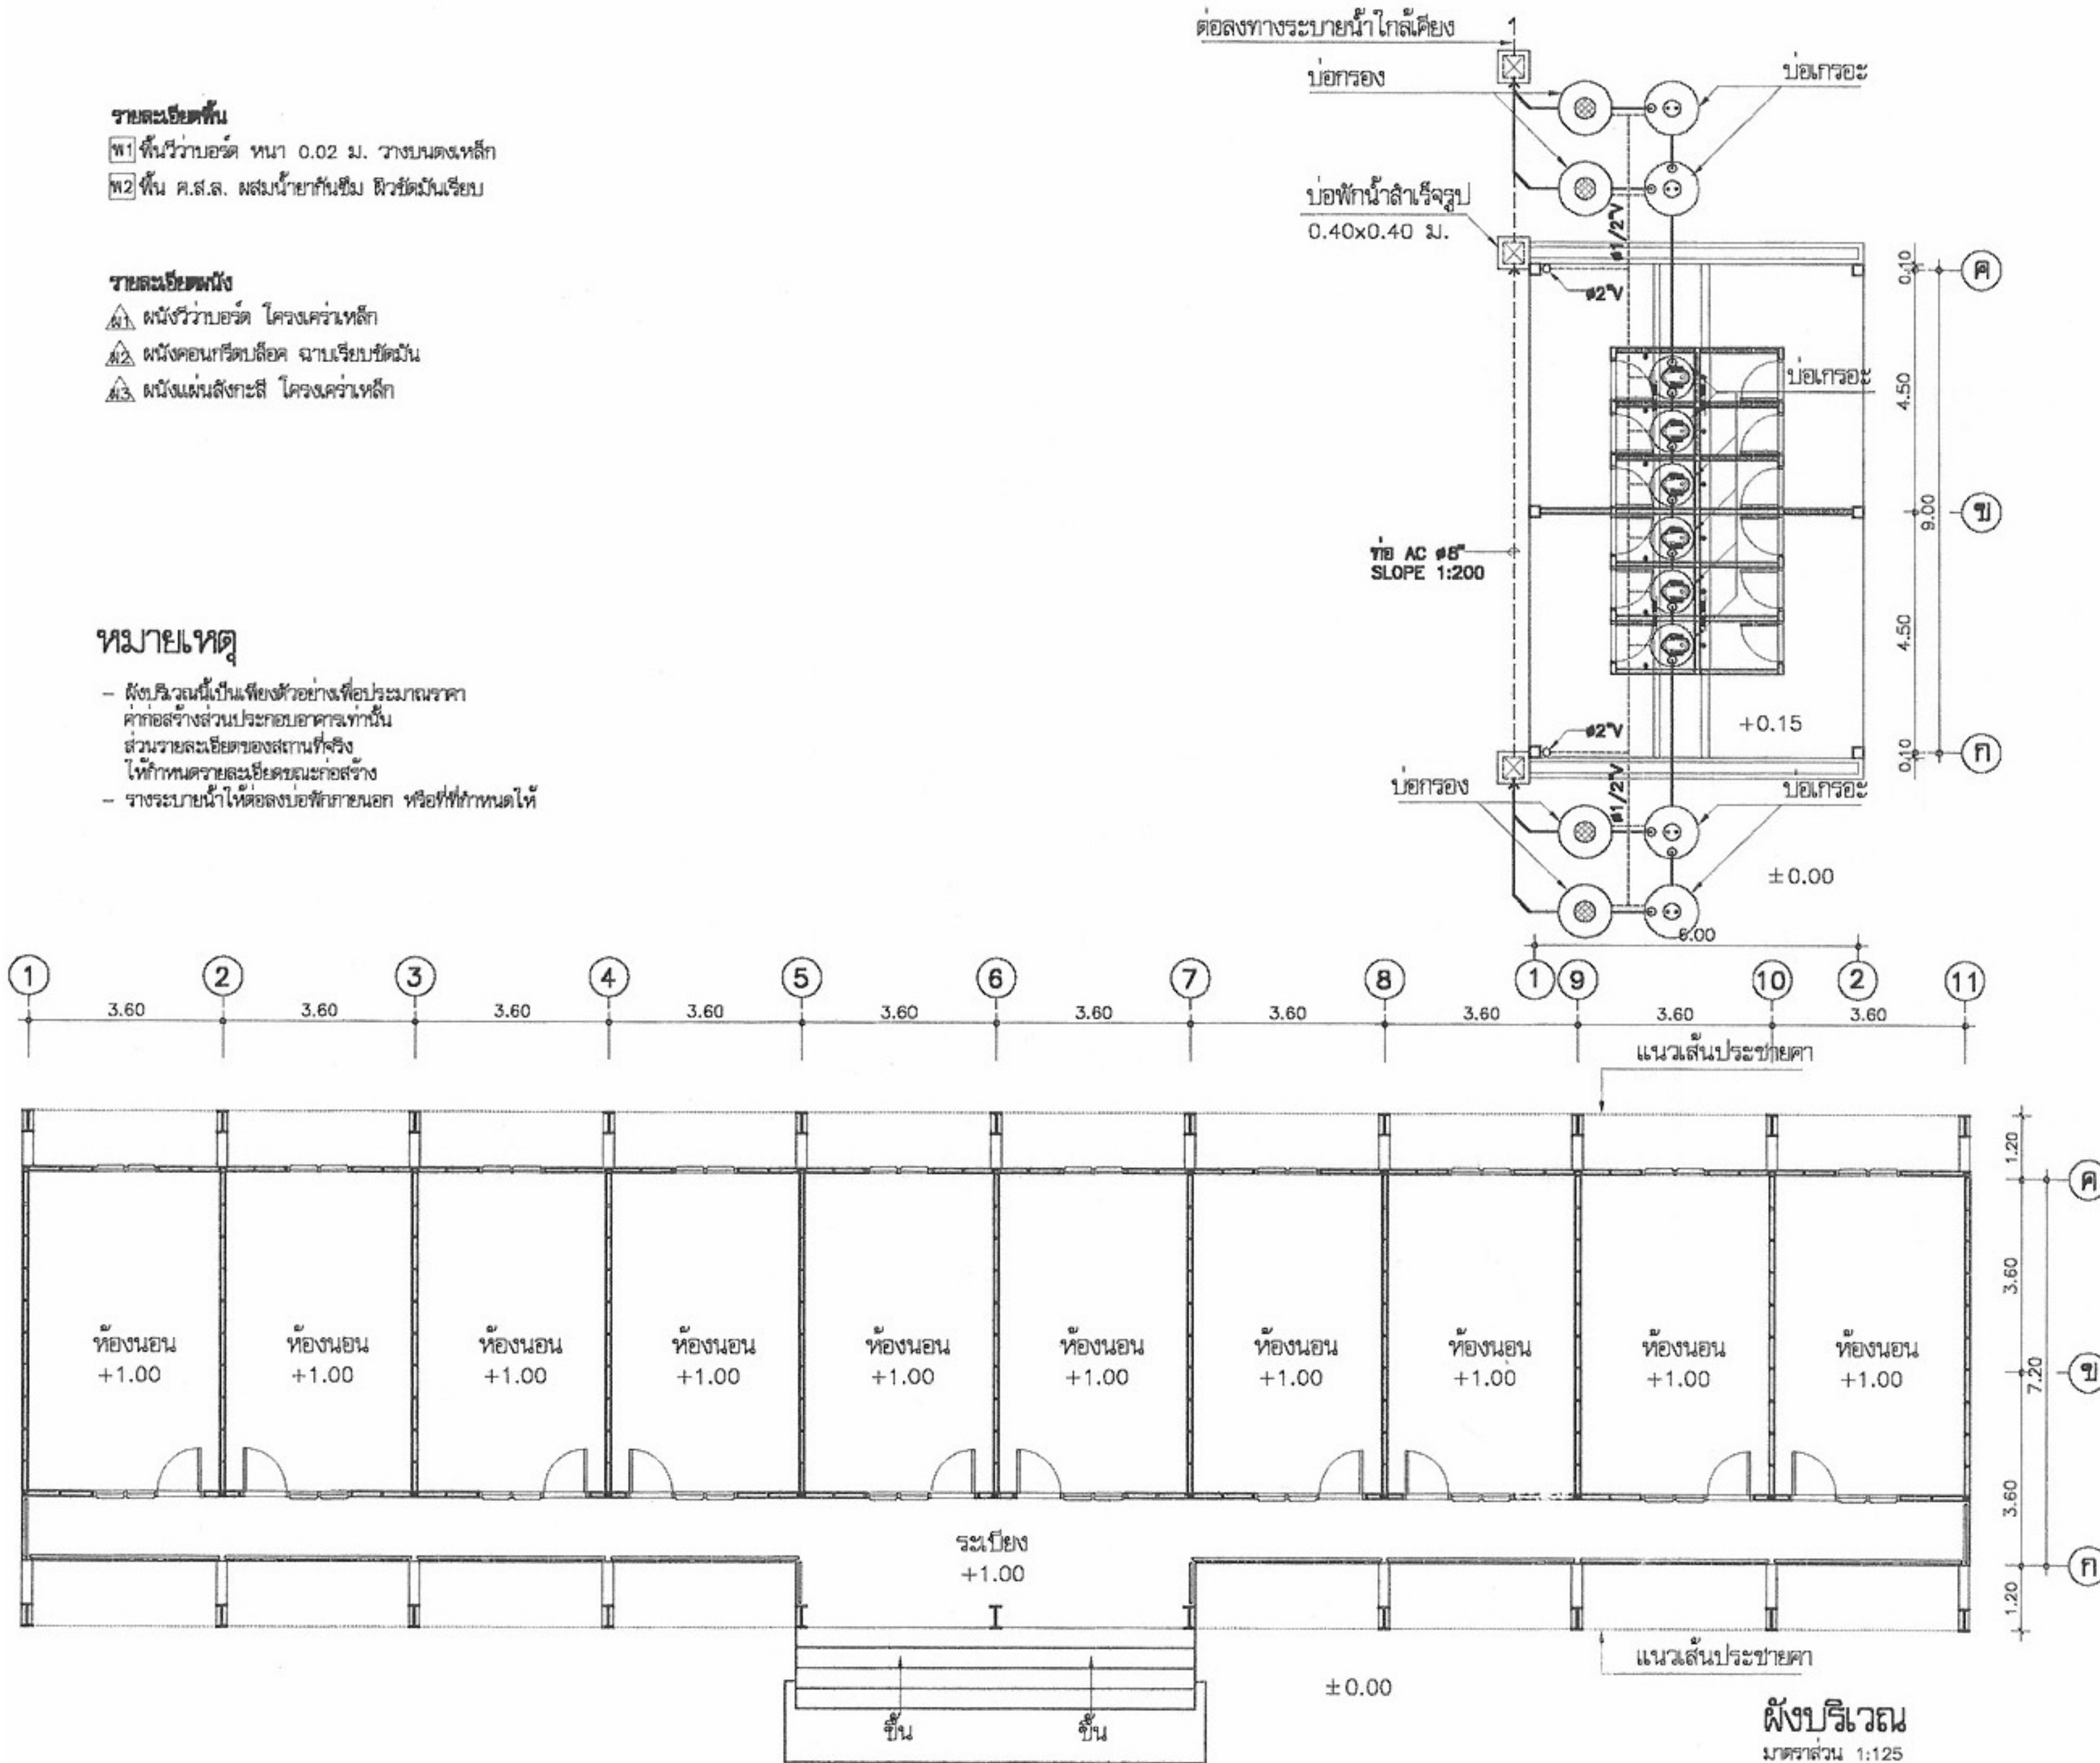

โครงการแบบอาคารเพื่อประชาชน
ไทยช่วยไทย

แบบ

บ้านผู้ประสบภัย 3 ห้องสุขารวม

สำนักสถาปัตย์กรรม

ผู้ควบคุมการก่อสร้าง

สถาปัตย์กรรม

สถาปนิก
สถาปนิก
สถาปนิก
สถาปนิก

สำนักวิศวกรรม โครงสร้างและงานระบบ

ผู้ควบคุมการก่อสร้าง

วิศวกรรม

วิศวกร
วิศวกร

วิศวกรรมไฟฟ้า

วิศวกร
วิศวกร

วิศวกรรม

วิศวกร
วิศวกร

สุขาภิบาล

วิศวกร
วิศวกร

อนุมัติ

(นายสว่าง ศรีสุคนธ์)

แสดงแบบ

อธิบดีกรมโยธาธิการและผังเมือง

ผังบริเวณ

ผังบริเวณ

มาตราส่วน

1:125

วัน/เดือน/ปี

21 พ.ย. 2546

เลขที่แบบ

ม.บ.462099


แผ่นที่

จำนวนแผ่น

A-03

12

หมายเหตุ แบบที่แสดงอยู่นี้ได้รับการยืมส่วน เพื่อใช้แสดงผลทางหน้าจอเท่านั้น สำหรับแบบที่ใช้ขออนุญาตก่อสร้าง ให้ถ่ายสำเนาจากหนังสือแบบบ้าน

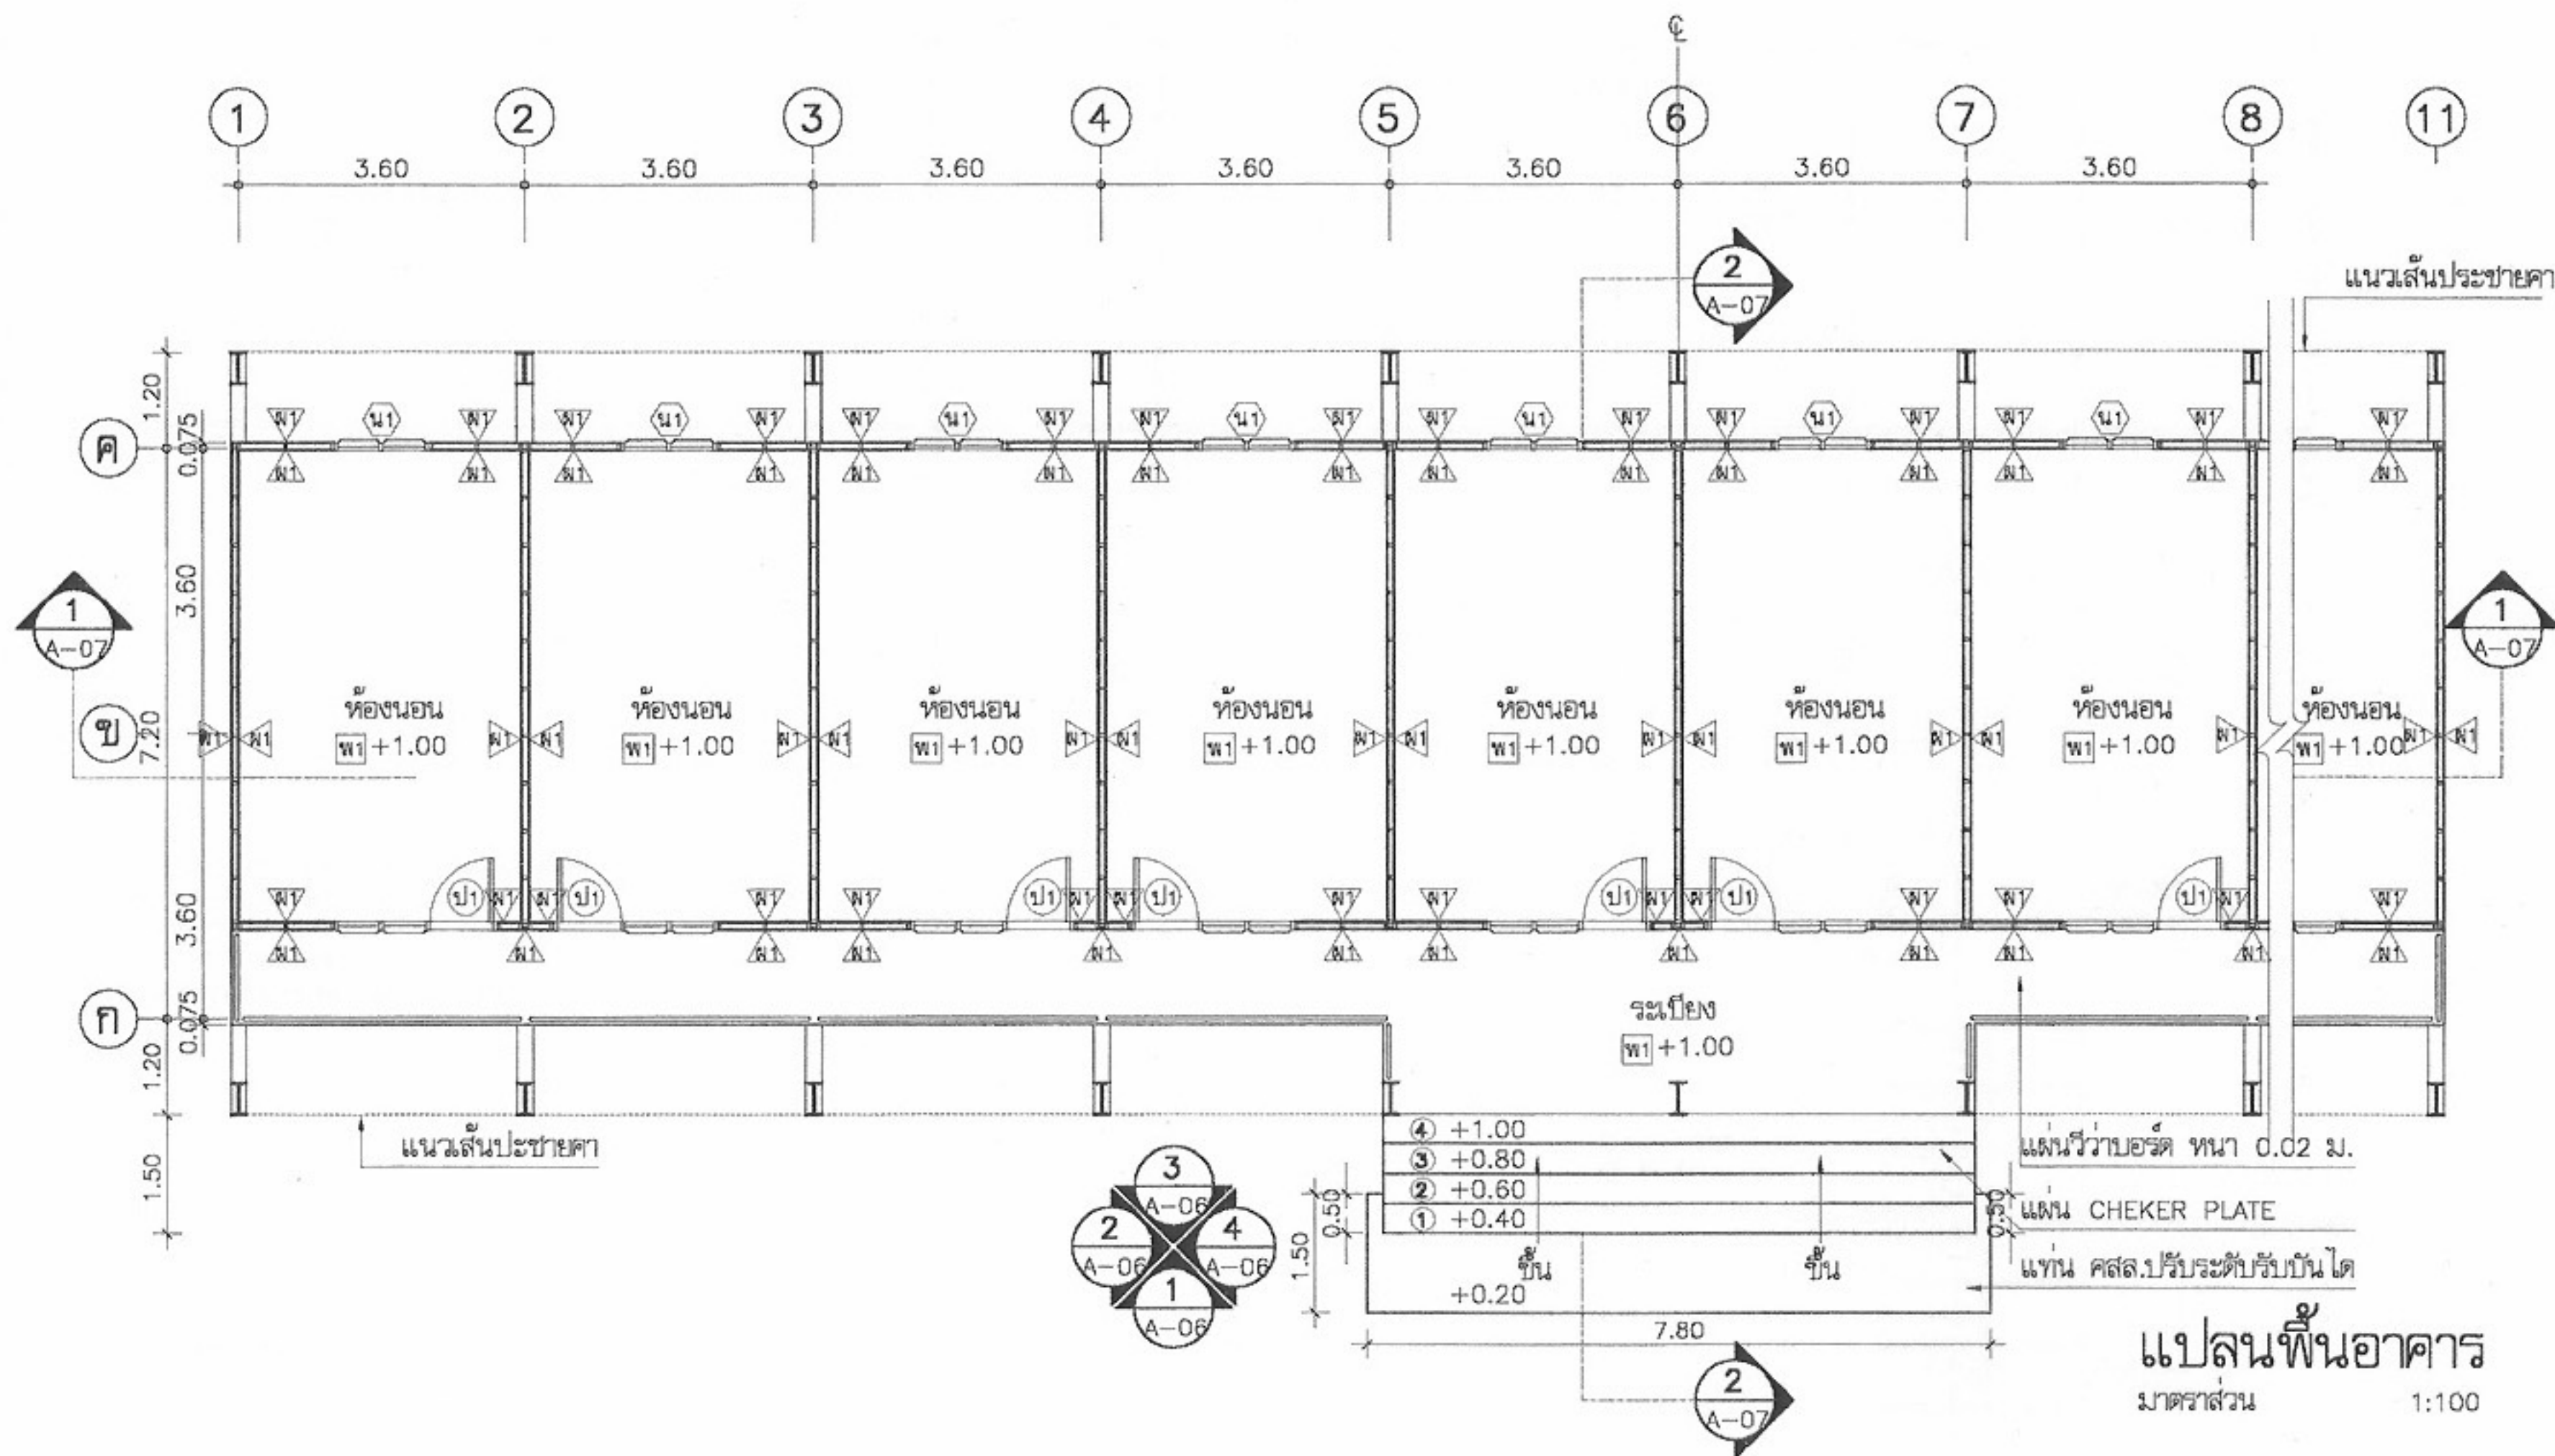

โครงการแบบอาคารเพื่อประชาชน
ไทยช่วยไทย

แบบ

บ้านผู้ประสบภัย 3 ห้องสุขารวม

สำนักสถาปัตยกรรม

11/11/11
ผู้อำนวยการสำนัก

สถาปนิก

สถาปนิก
สถาปนิก
สถาปนิก
สถาปนิก

สำนักวิศวกรรมโครงสร้างและงานระบบ

11/11/11
ผู้อำนวยการสำนัก

วิศวกร

วิศวกร

โครงสร้าง

วิศวกร

วิศวกรไฟฟ้า

วิศวกร

และเครื่องกล

วิศวกร

วิศวกร

วิศวกร

สุขาภิบาล

วิศวกร

อนุมัติ

11/11/11
(นายสว่าง ศรีสุก)

อธิบดีกรมโยธาธิการและผังเมือง

แสดงแบบ

แปลนพื้นที่อาคาร

มาตราส่วน 1:100

วัน/เดือน/ปี 21 พ.ย. 2546

เลขที่แบบ ม.บ.462099


แผ่นที่

A-04

จำนวนแผ่น

12

หมายเหตุ แบบที่แสดงอยู่นี้ได้รับการยืมส่วน เพื่อใช้แสดงผลทางหน้าจอเท่านั้น สำหรับแบบที่ใช้ขออนุญาตก่อสร้าง ให้ถ่ายสำเนาจากหนังสือแบบบ้าน

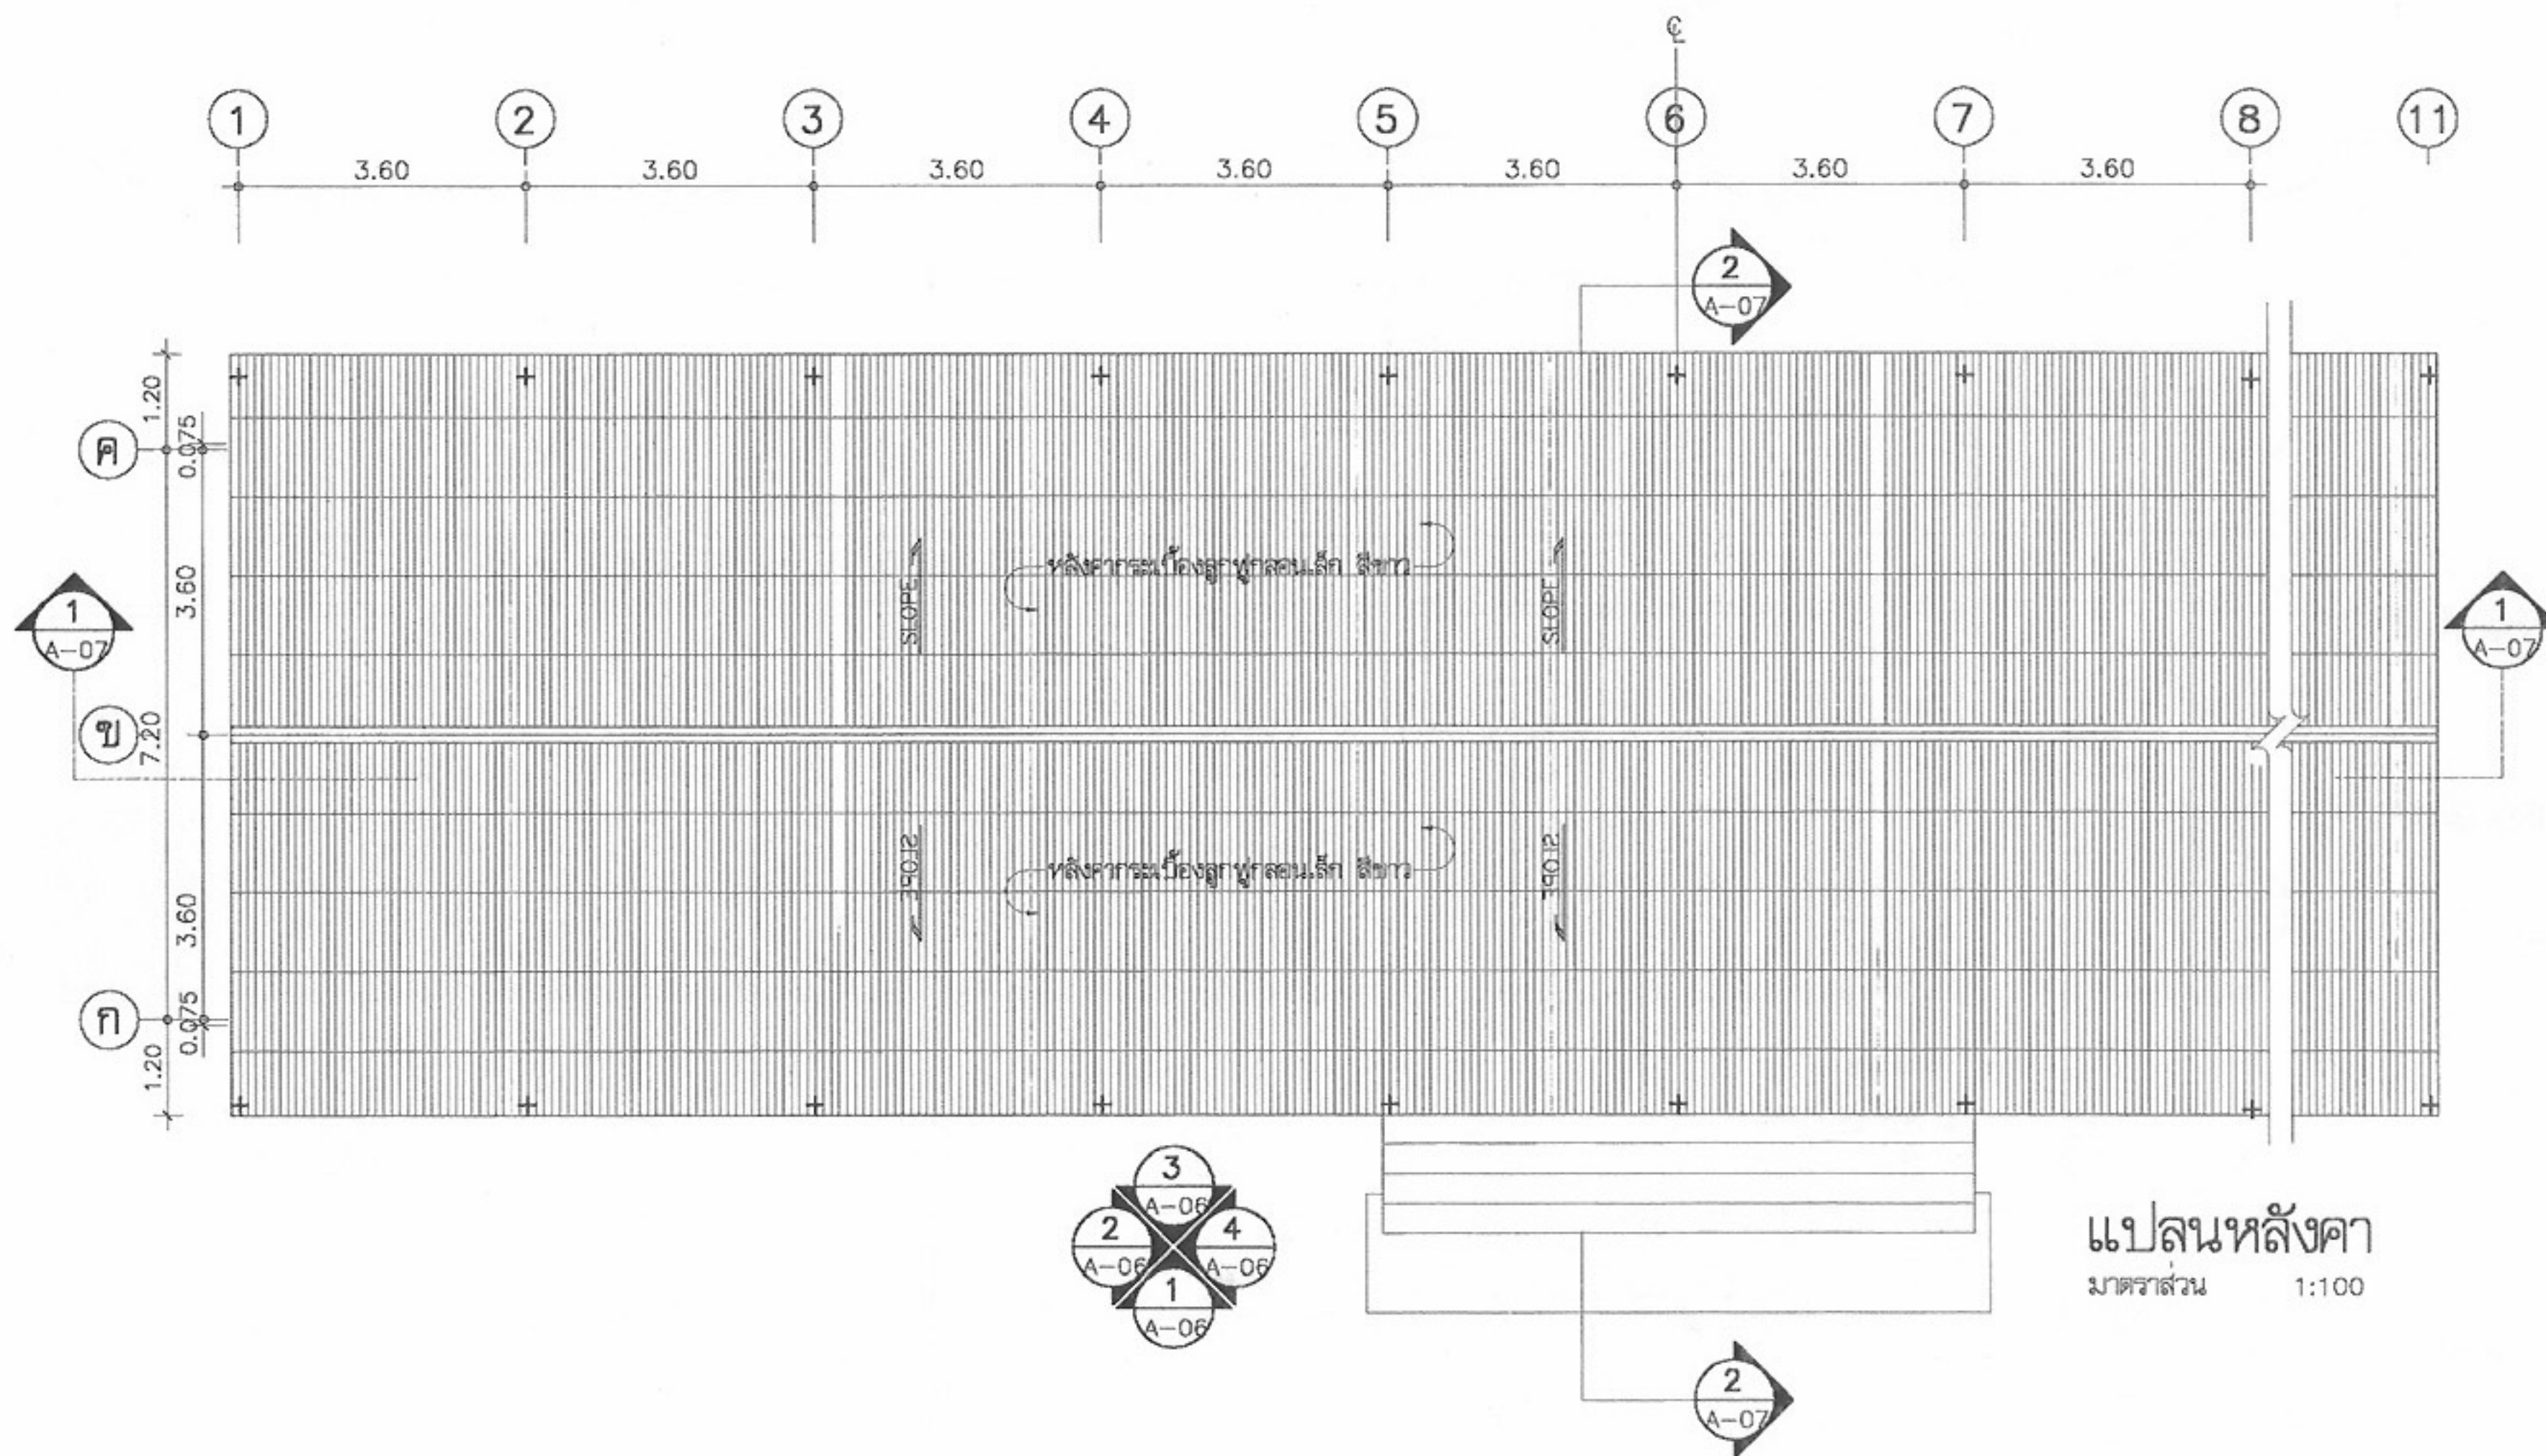

แปลนหลังคา
มาตราส่วน 1:100



โครงการแบบอาคารเพื่อประชาชน
ไทยช่วยไทย

แบบ
บ้านผู้ประสบภัย 3 ห้องสุขารวม

สำนักสถาปัตยกรรม
ผู้ควบคุมการก่อสร้าง

สถาปนิก
สถาปนิก
สถาปนิก
สถาปนิก

สำนักวิศวกรรมโครงสร้างและงานระบบ
ผู้ควบคุมการก่อสร้าง

วิศวกรรม
โครงสร้าง
วิศวกรรมไฟฟ้า
และเครื่องกล
วิศวกรรม
สุขาภิบาล

อนุมัติ
(นายสว่าง ศิริสุนทร)
อธิบดีกรมโยธาธิการและผังเมือง

แสดงแบบ
แปลนหลังคา





มาตราส่วน 1:100

วัน/เดือน/ปี 21 พ.ย. 2546

เลขที่แบบ ม.บ.462099

แผ่นที่ A-05 จำนวนแผ่น 12

หมายเหตุ แบบที่แสดงอยู่นี้ได้รับการยืมส่วน เพื่อใช้แสดงผลทางหน้าจอเท่านั้น สำหรับแบบที่ใช้ขออนุญาตก่อสร้าง ให้ถ่ายสำเนาจากหนังสือแบบบ้าน

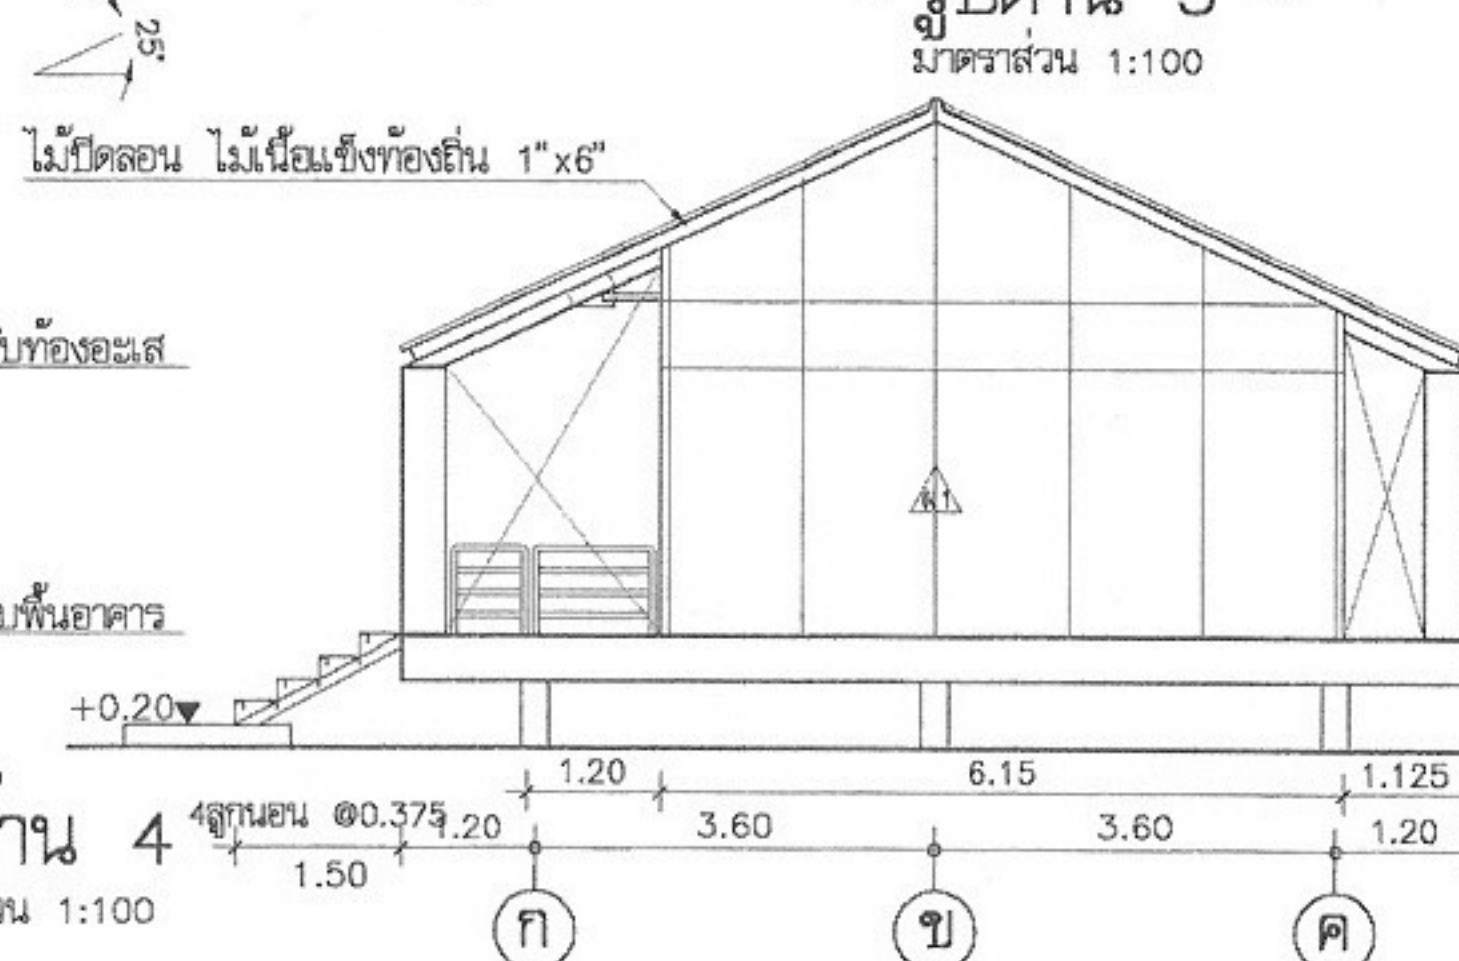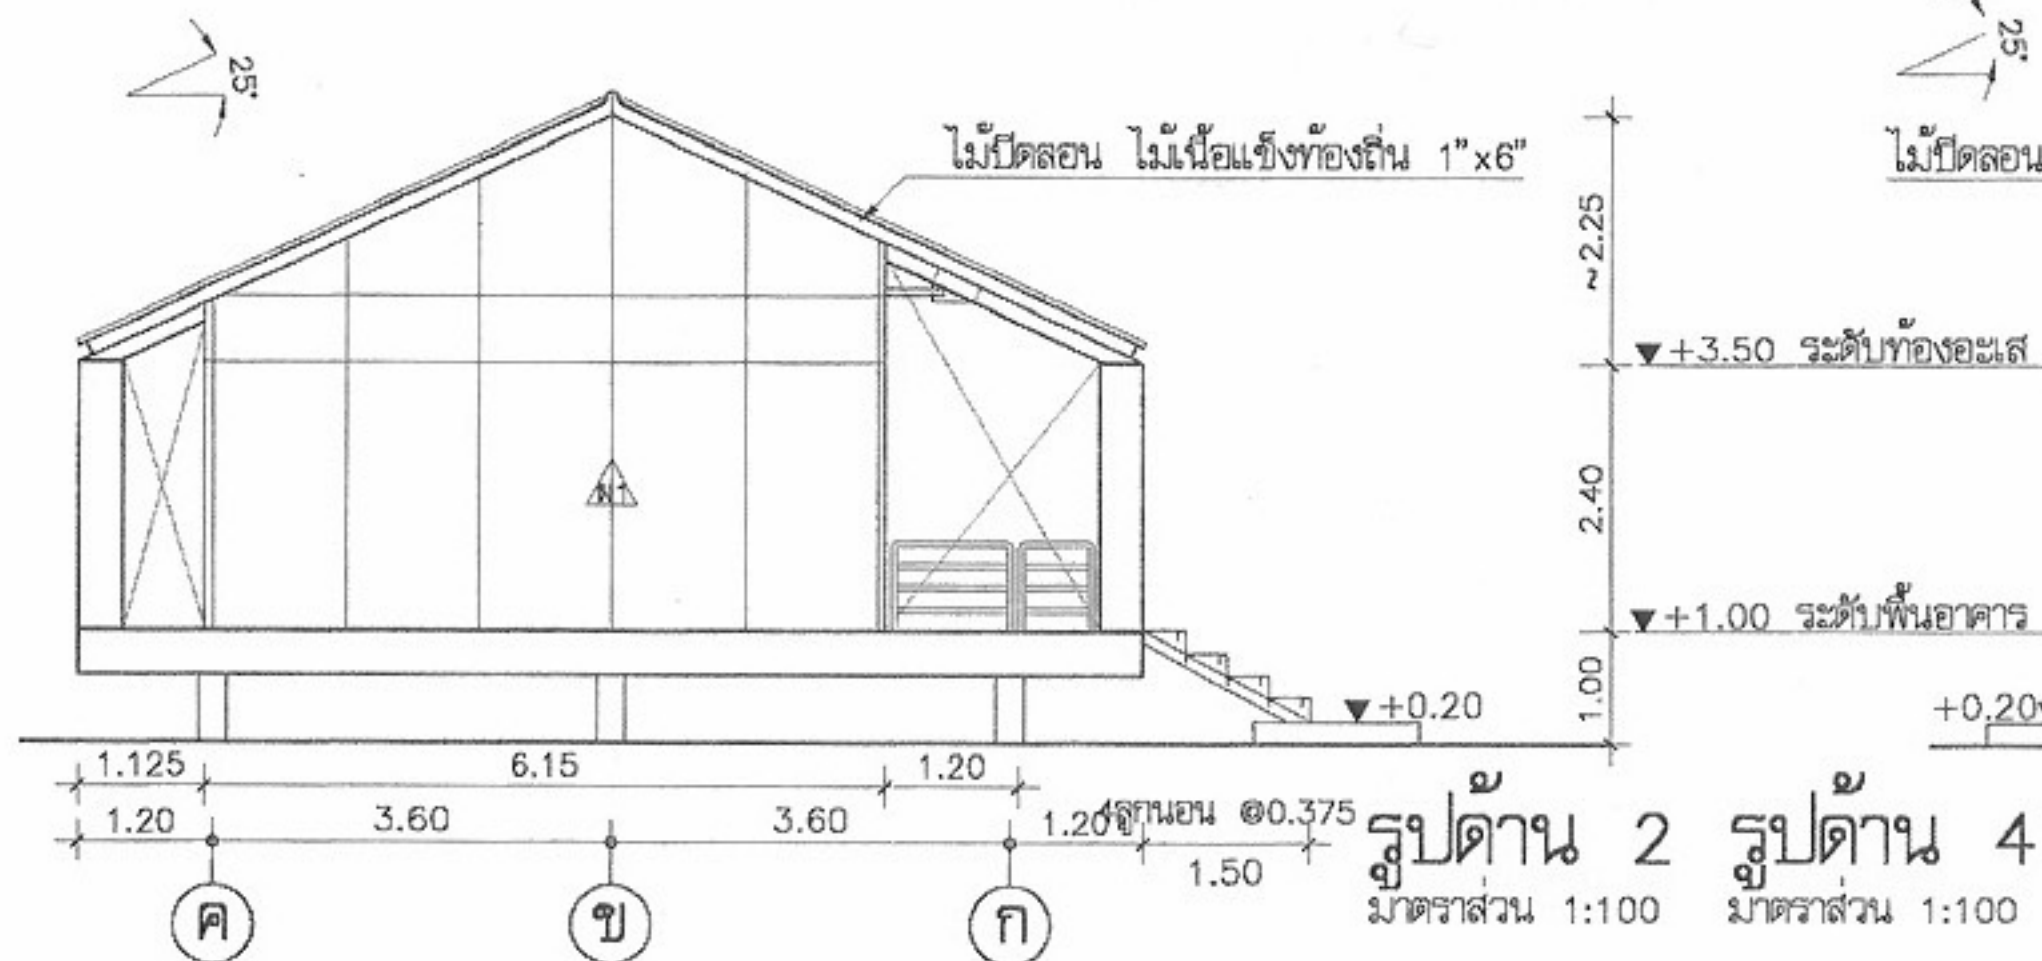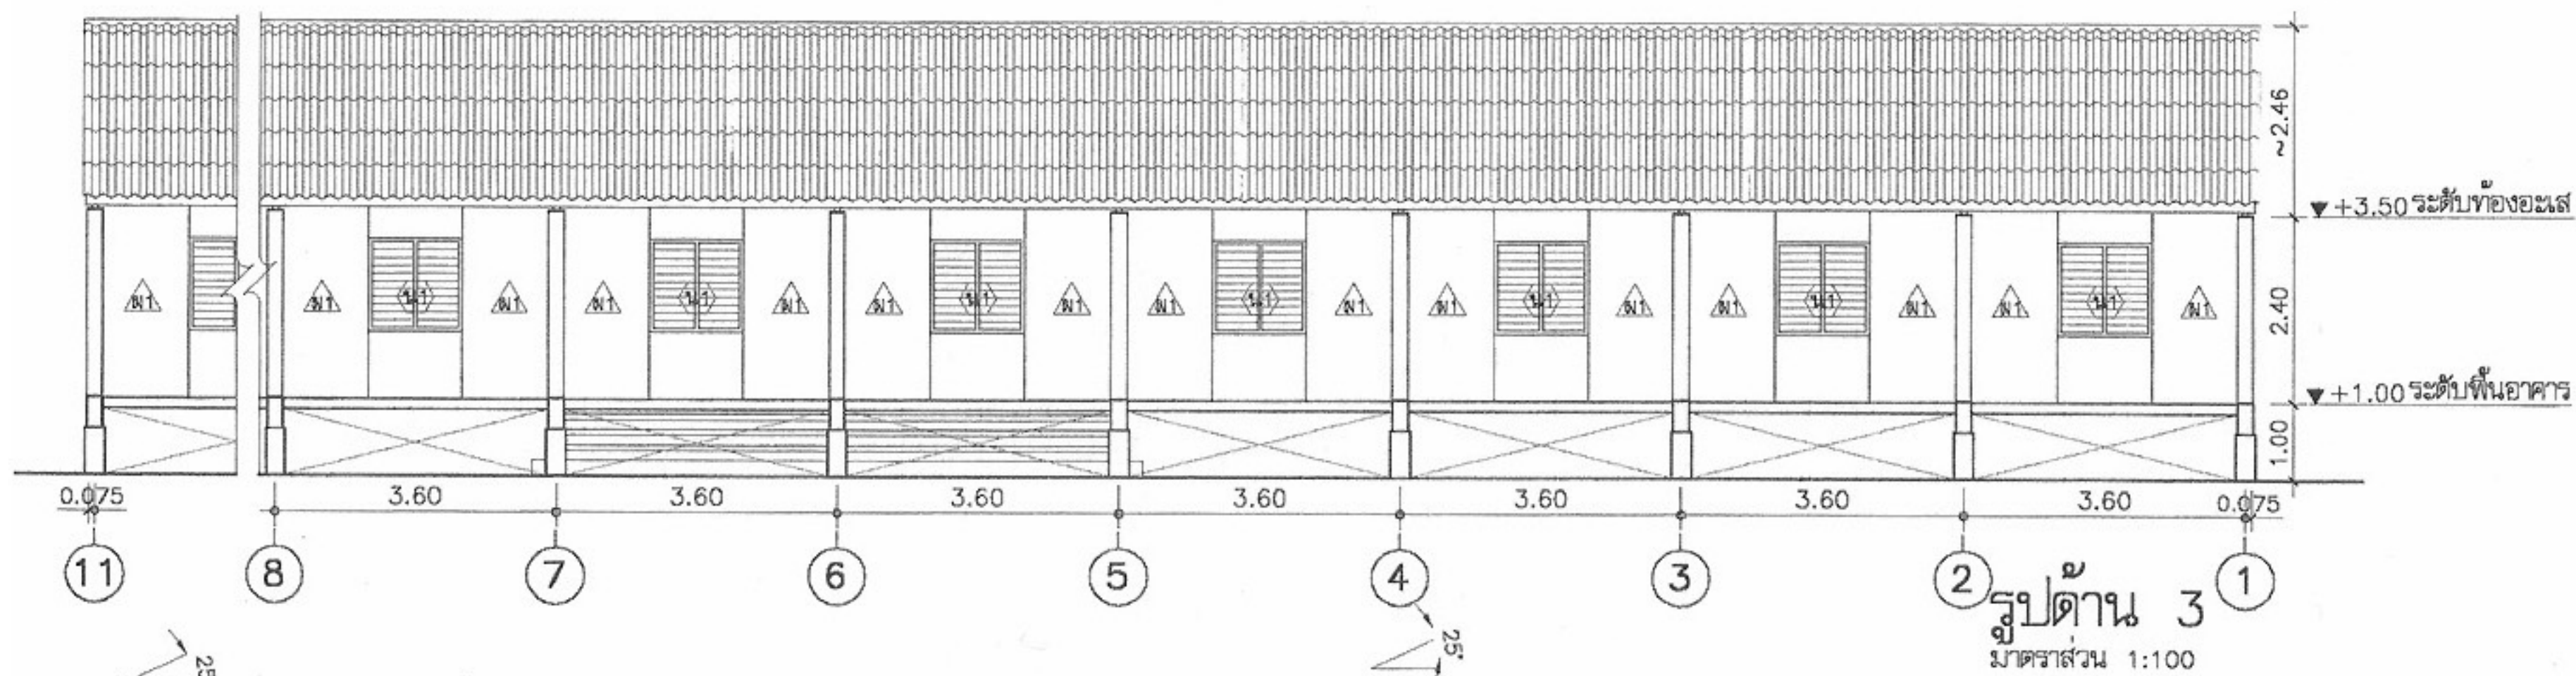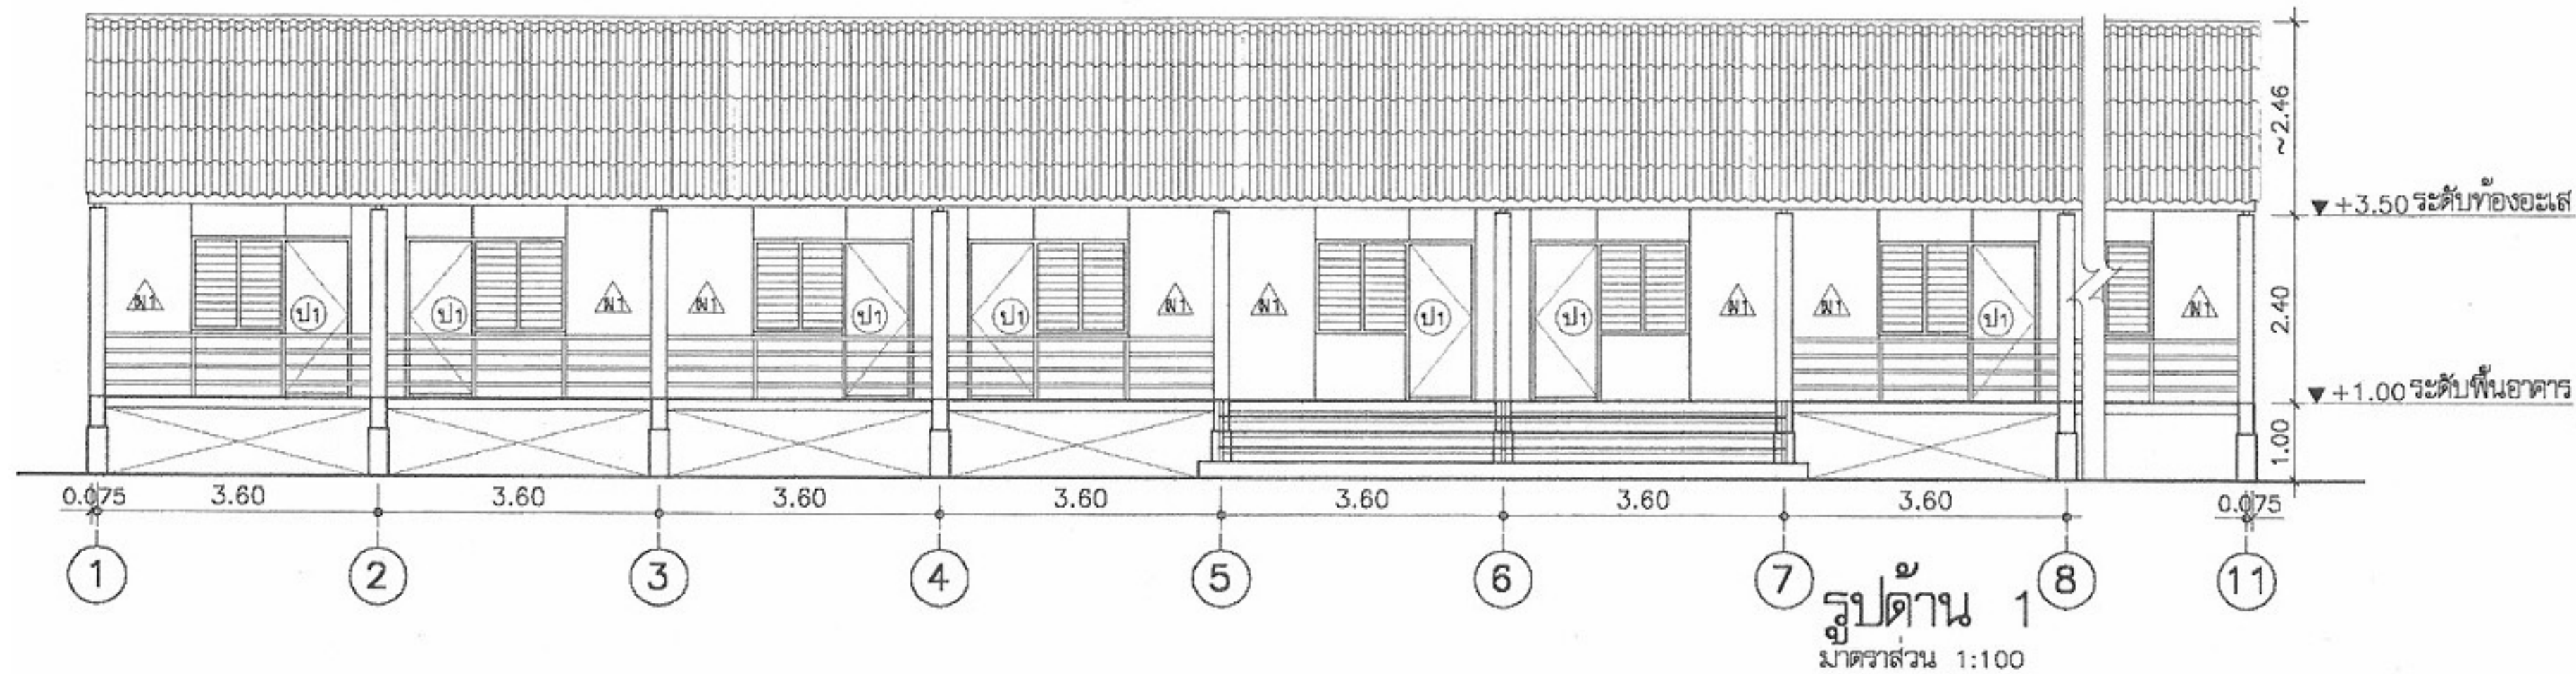

โครงการแบบอาคารเพื่อประชาชน

ไทยช่วยไทย

แบบ

บ้านผู้ประสบภัย 3 ห้องสุขารวม

สำนักสถาปัตยกรรม

ผู้ควบคุมการออกแบบ

สถาปัตยกรรม

สถาปนิก
สถาปนิก
สถาปนิก
สถาปนิก

สำนักวิศวกรรมโครงสร้างและงานระบบ

ผู้ควบคุมการออกแบบ

วิศวกรรม

วิศวกร
วิศวกร

วิศวกรรมไฟฟ้า

วิศวกร
วิศวกร

และเครื่องกล

วิศวกร
วิศวกร

วิศวกรรม

วิศวกร
วิศวกร

ผู้ควบคุมการ

วิศวกร

อนุมัติ

(นายสว่าง ศรีสุก)

อธิบดีกรมโยธาธิการและผังเมือง

แสดงแบบ

รูปด้าน 1,2,3,4

มาตราส่วน 1:100

วัน/เดือน/ปี 21 พ.ย. 2546

เลขที่แบบ ม.บ.462099

แผ่นที่

A-06

จำนวนแผ่น







12

หมายเหตุ แบบที่แสดงอยู่นี้ได้รับการยืมส่วน เพื่อใช้แสดงผลทางหน้าจอเท่านั้น สำหรับแบบที่ใช้ขออนุญาตก่อสร้าง ให้ถ่ายสำเนาจากหนังสือแบบบ้าน

- 1 บานพับ ประตูดังกล่าวให้ติดตั้งบานพับโลหะเคลือบขี้น้ำมันหนา 1/2 นิ้ว
- 2 กุญแจล็อกปิด ใช้บานพับทรงกลมเป็นโลหะชุบโครเมียม ล็อคติดประตูดังกล่าว
- 3 ปุ่มยางกันชน ติดตั้งประตูดังกล่าว
- 4 ที่ยึดประตู เป็นโลหะชุบโครเมียม ติดประตูดังกล่าว
- 5 บานม้วนลวด เป็นบานม้วนลวดอลูมิเนียม กรอบอลูมิเนียม ติดตั้งบานประตูห้องนอน

1 บานมั่งลาด เป็นบานมั่งลาดอลูมิเนียม กรอบอลูมิเนียม ติดตั้งบานประตูห้องนอน

- ไม่วางกบสำหรับประดู-หน้าต่าง ใช้ไม้เนื้อแข็งตามบัญชี มยธ.
ขนาดวงกบที่ไม่ได้ระบุไว้ในแบบให้ใช้ขนาด 2"x4" ทั้งหมด
- ถ้าไม่ใช้ไม้ให้ใช้วงกบเหล็ก ,กรอบบานเหล็ก ,หรือวงกบอลูมิเนียม
,กรอบบานอลูมิเนียม ,ลูกฟักอลูมิเนียม อุปกรณ์ตามมาตรฐานของบริษัทผู้ผลิต

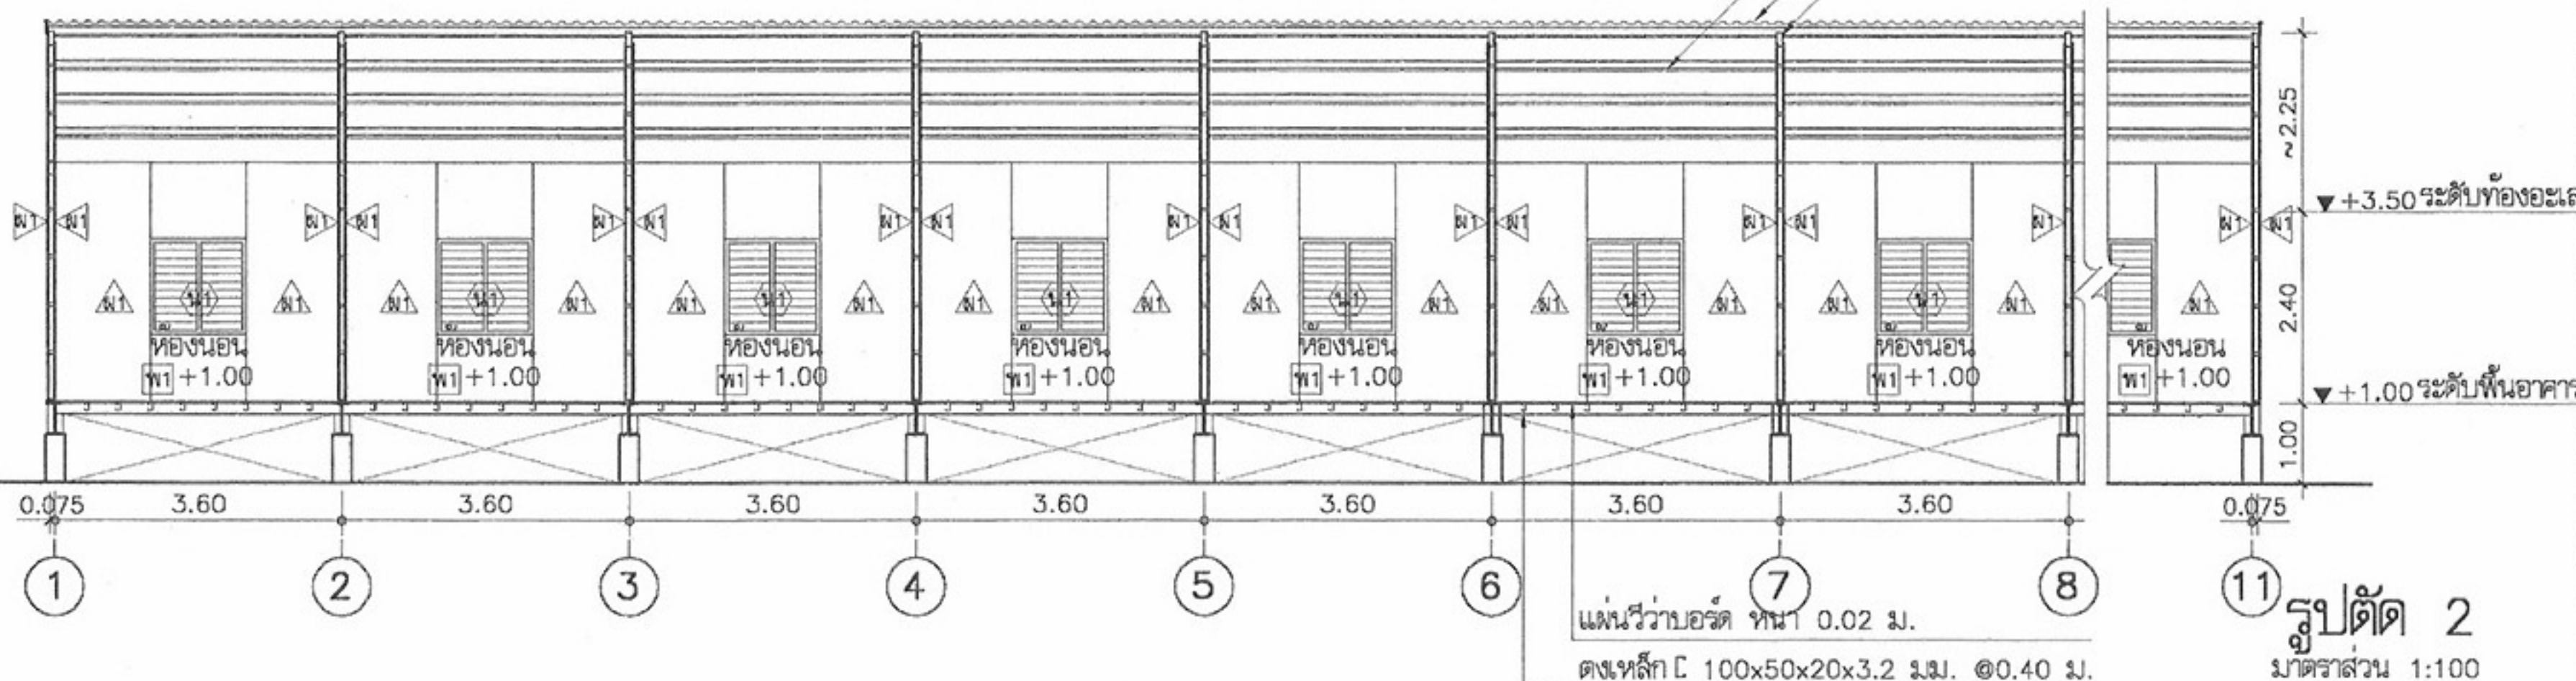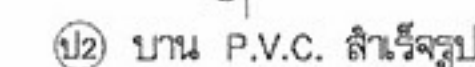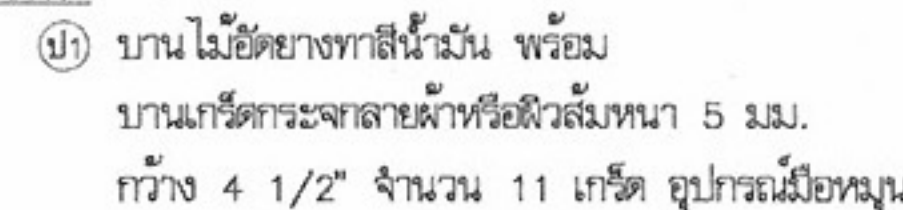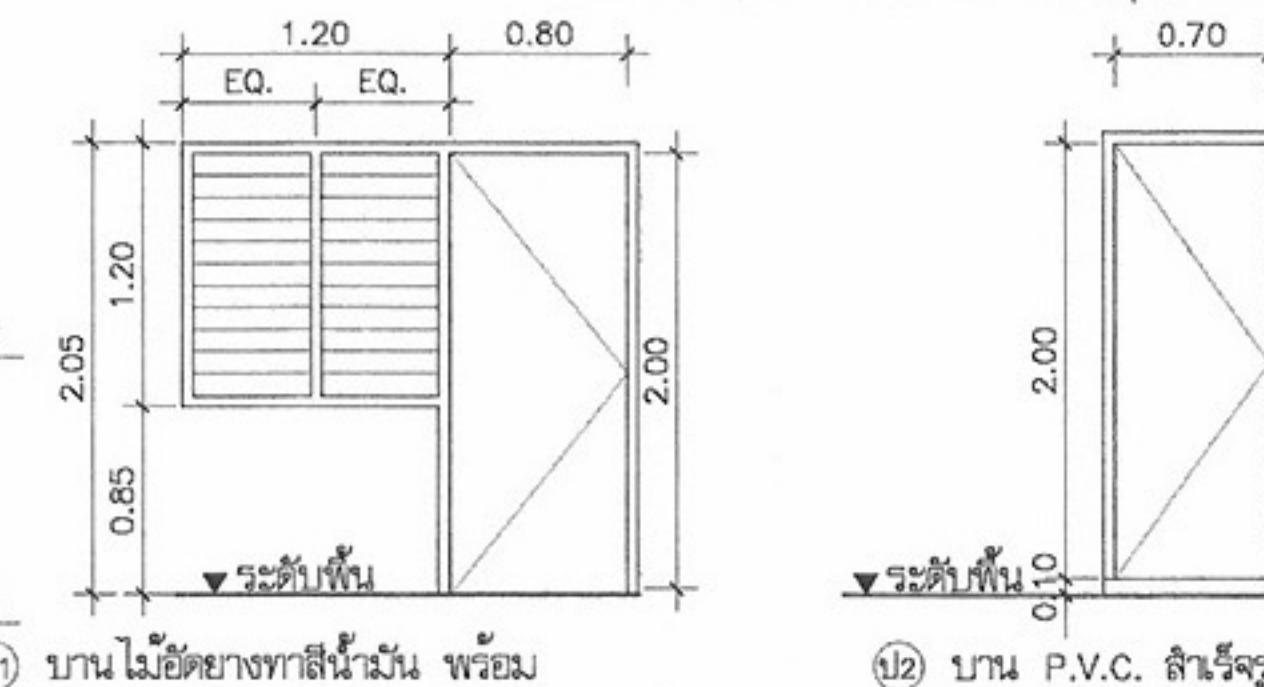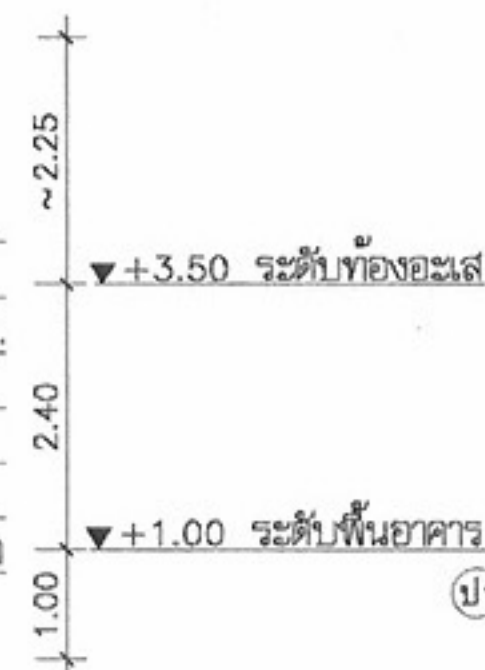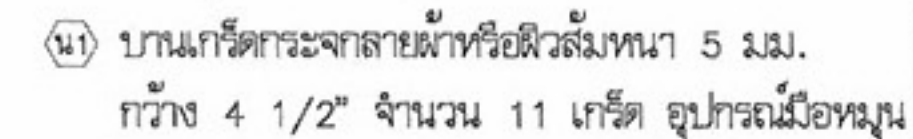

โครงการแบบอาคารเพื่อประชาชน

ไทยช่วยไทย

437

บ้านผู้ประสนกัย 3 ห้องสุกรวม

สำนักสภามัธยมศึกษา

สถาบันวิชาการ	
---------------	--

1

1

สำนักวิศวกรรมโครงสร้างและงานระบบ

1

๖๒๖

ໂຕຈຸນຊົງ

အိမ်ကုသမှု၊ ငါးဖမ်း

பெரிய அளவுக்குள்ளே

Summary:

[illegible][illegible]

五

(นายสว่าง ศรีสกุล)

อธิบดีกรมโยธาธิการและผังเมือง

ແຮ່ປຸງແປງ

รูปตัด 1,2 ,
ขยายประต-หน้าต่าง

มาตราส่วน 1:100

21 頁, 2546



เลขที่แบบ ม.บ.462099

เลขที่	๒
--------	---

A-07

12

หมายเหตุ แบบที่แสดงอยู่นี้ได้รับการย่อส่วน เพื่อใช้แสดงผลทางหน้าจอเท่านั้น สำหรับแบบที่ใช้ขออนุญาตก่อสร้าง ให้ถ่ายสำเนาจากหนังสือแบบบ้าน

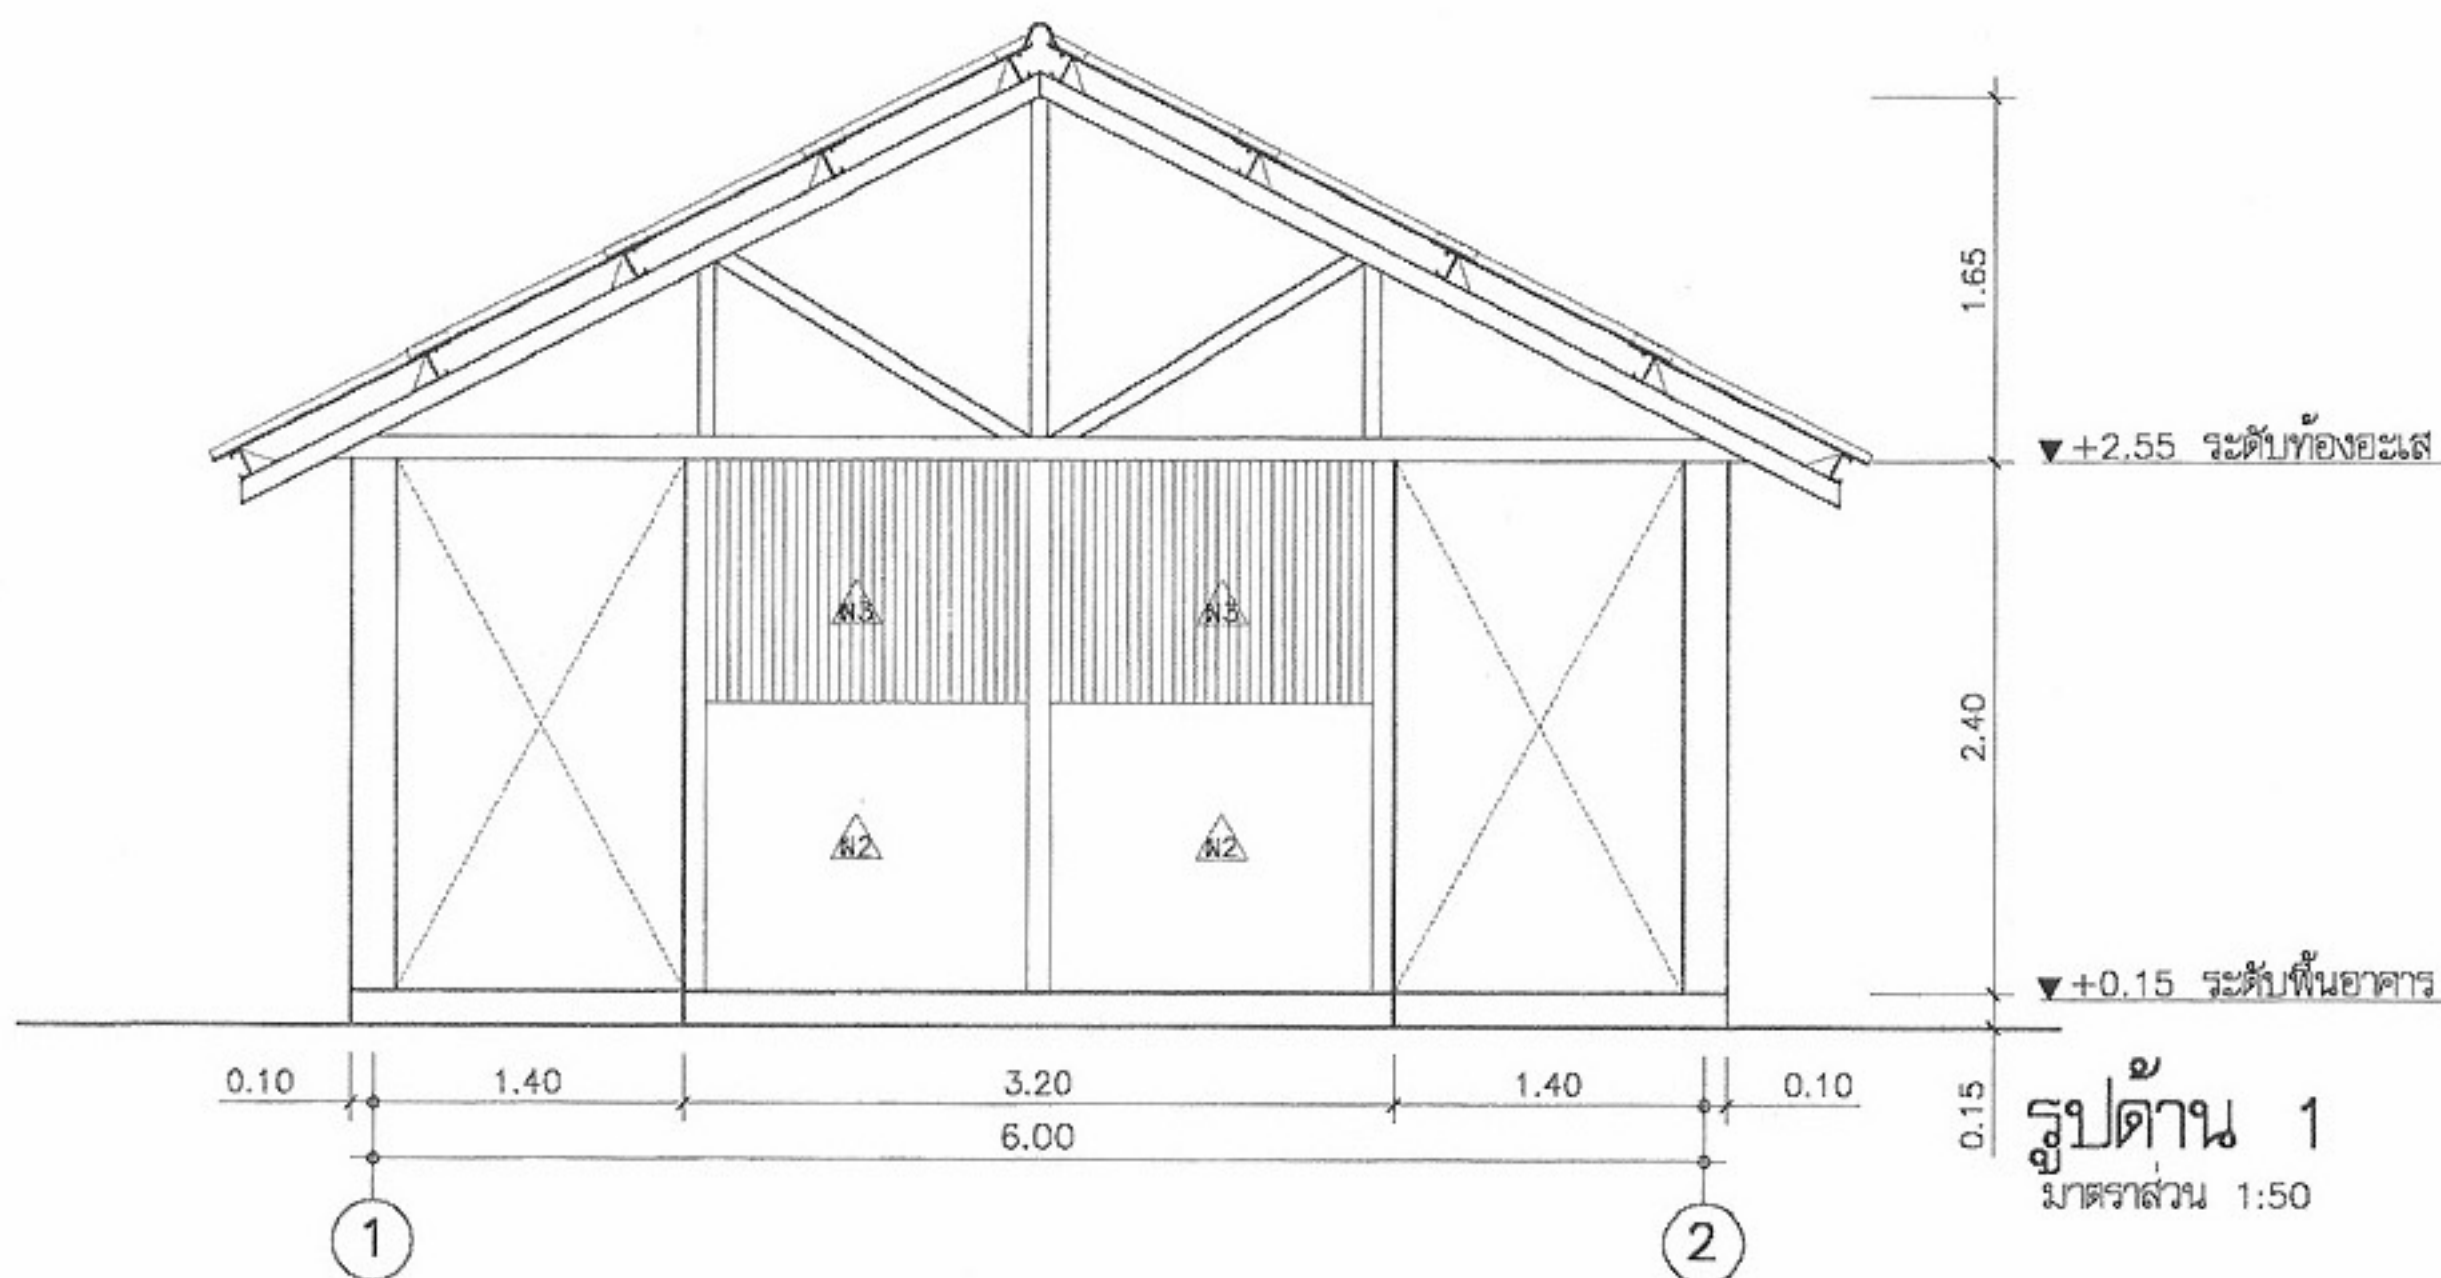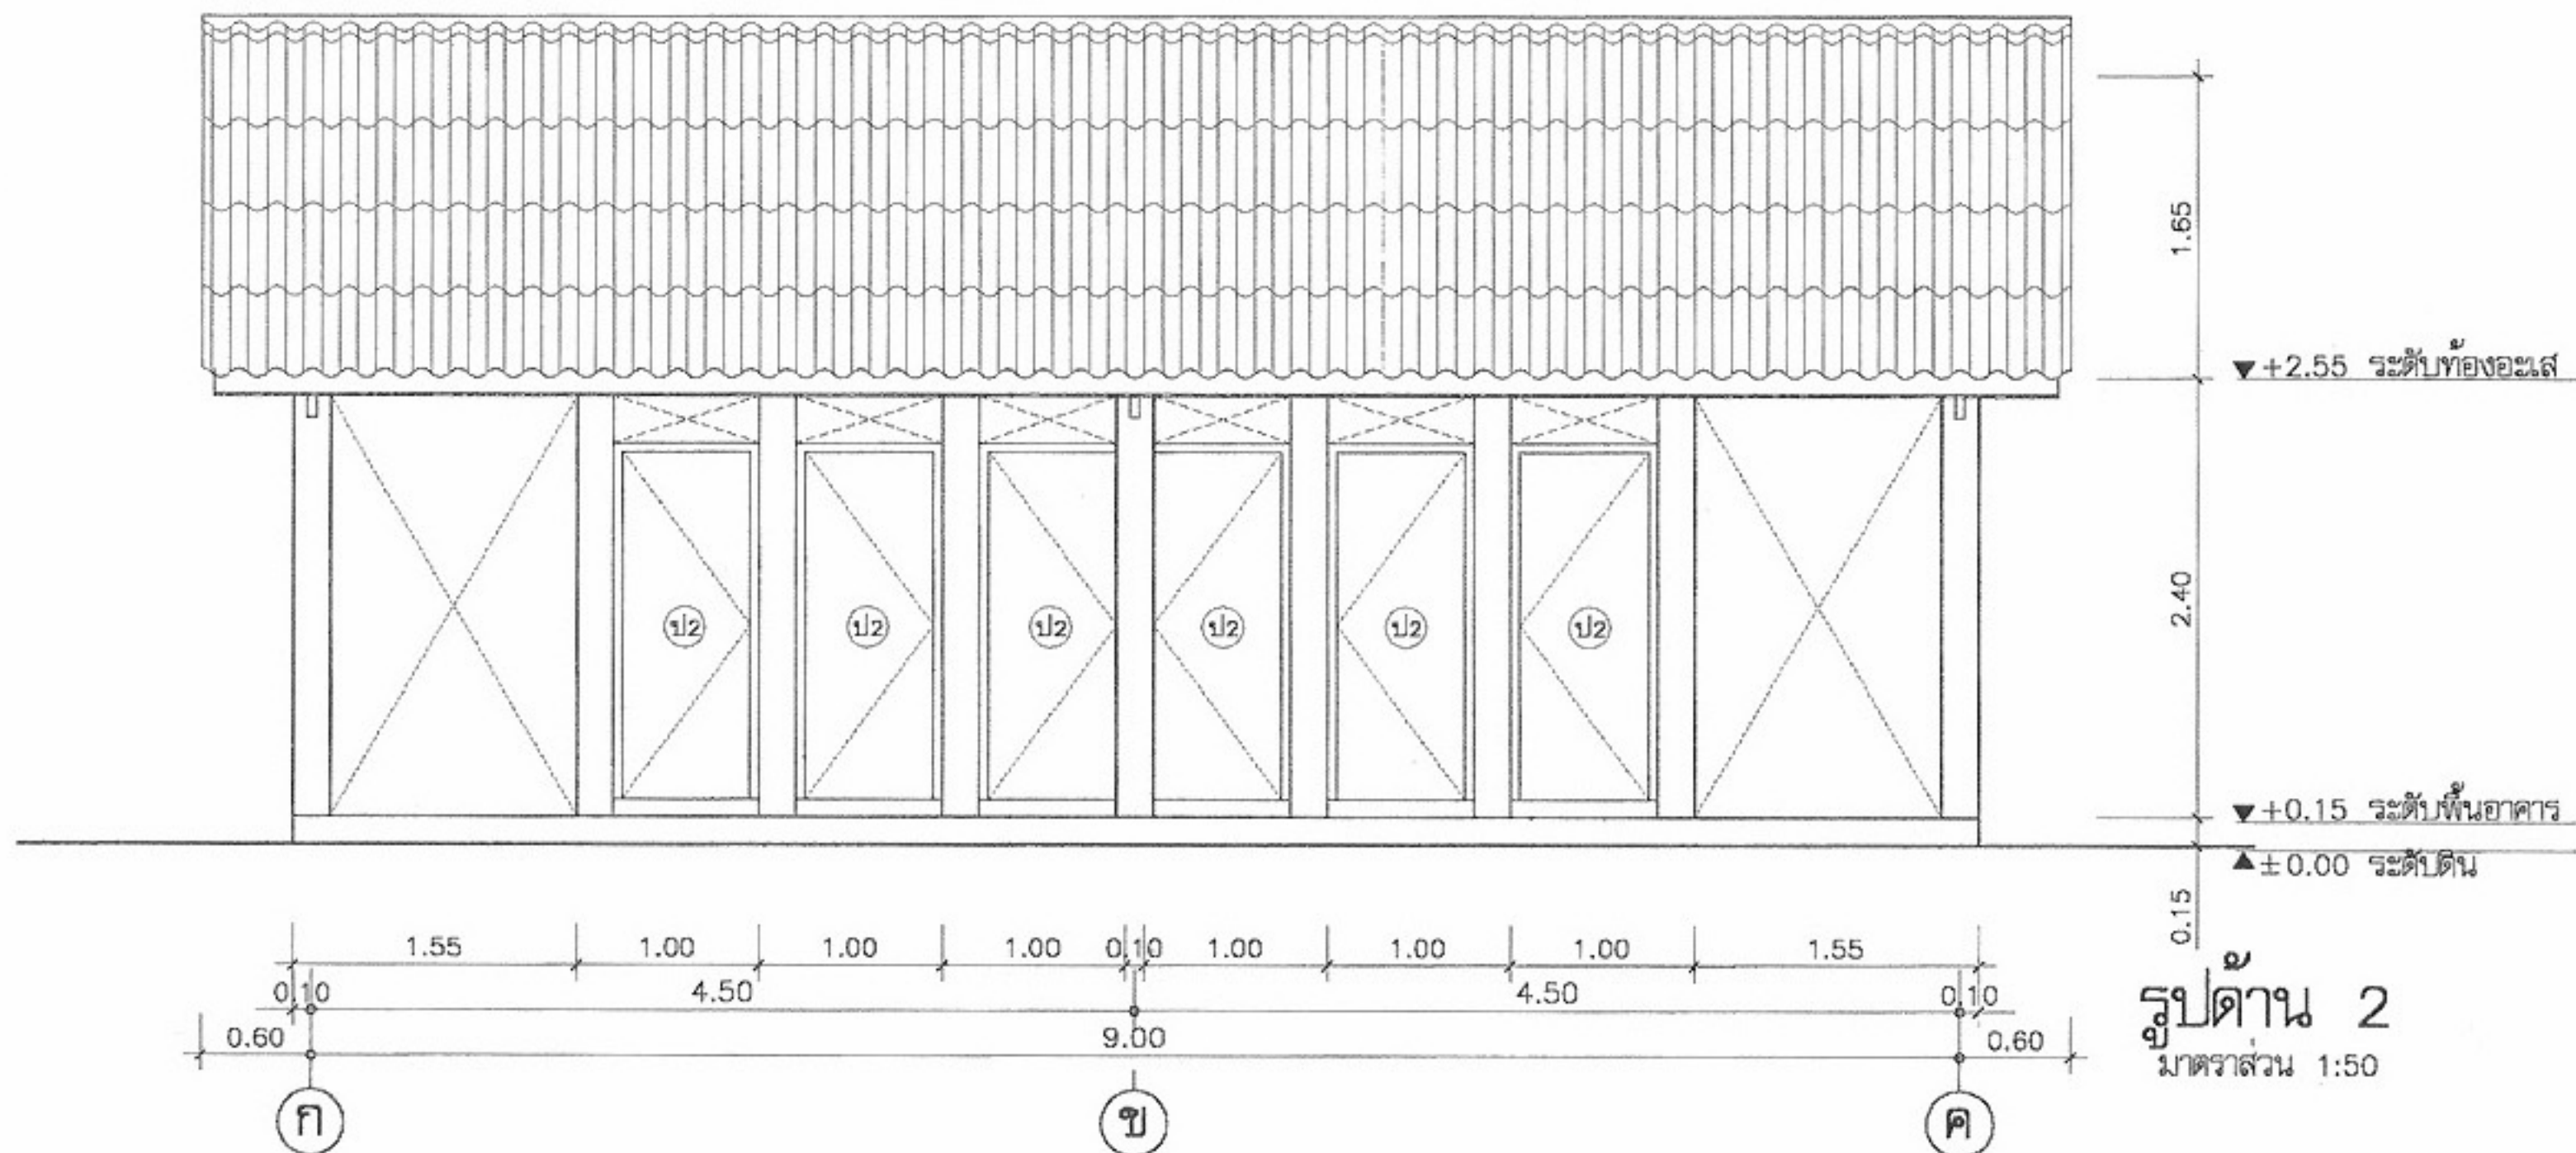

โครงการแบบอาคารเพื่อประชาชน
ไทยช่วยไทย

แบบ

บ้านผู้ประสบภัย 3 ห้องสุขารวม

สำนักสถาปัตยกรรม

ผู้ช่วยการสำนัก

สถาปัตยกรรม

สถาปนิก
สถาปนิก
สถาปนิก
สถาปนิก

สำนักวิศวกรรมโครงสร้างและงานระบบ

ผู้ช่วยการสำนัก

วิศวกรรม

วิศวกร

โครงสร้าง

วิศวกร

วิศวกรรมไฟฟ้า

วิศวกร

และเครื่องกล

วิศวกร

วิศวกรรม

วิศวกร

สุขาภิบาล

วิศวกร

อนุมัติ

(นายสว่าง ศรีสุก)

อธิบดีกรมโยธาธิการและผังเมือง

แสดงแบบ

รูปด้าน 1,2

มาตราส่วน 1:50

วัน/เดือน/ปี 21 พ.ย. 2546

เลขที่แบบ ม.บ.462099



แผ่นที่










A-09

จำนวนแผ่น

12

หมายเหตุ แบบที่แสดงอยู่นี้ได้รับการยืมส่วน เพื่อใช้แสดงผลทางหน้าจอเท่านั้น สำหรับแบบที่ใช้ขออนุญาตก่อสร้าง ให้ถ่ายสำเนาจากหนังสือแบบบ้าน

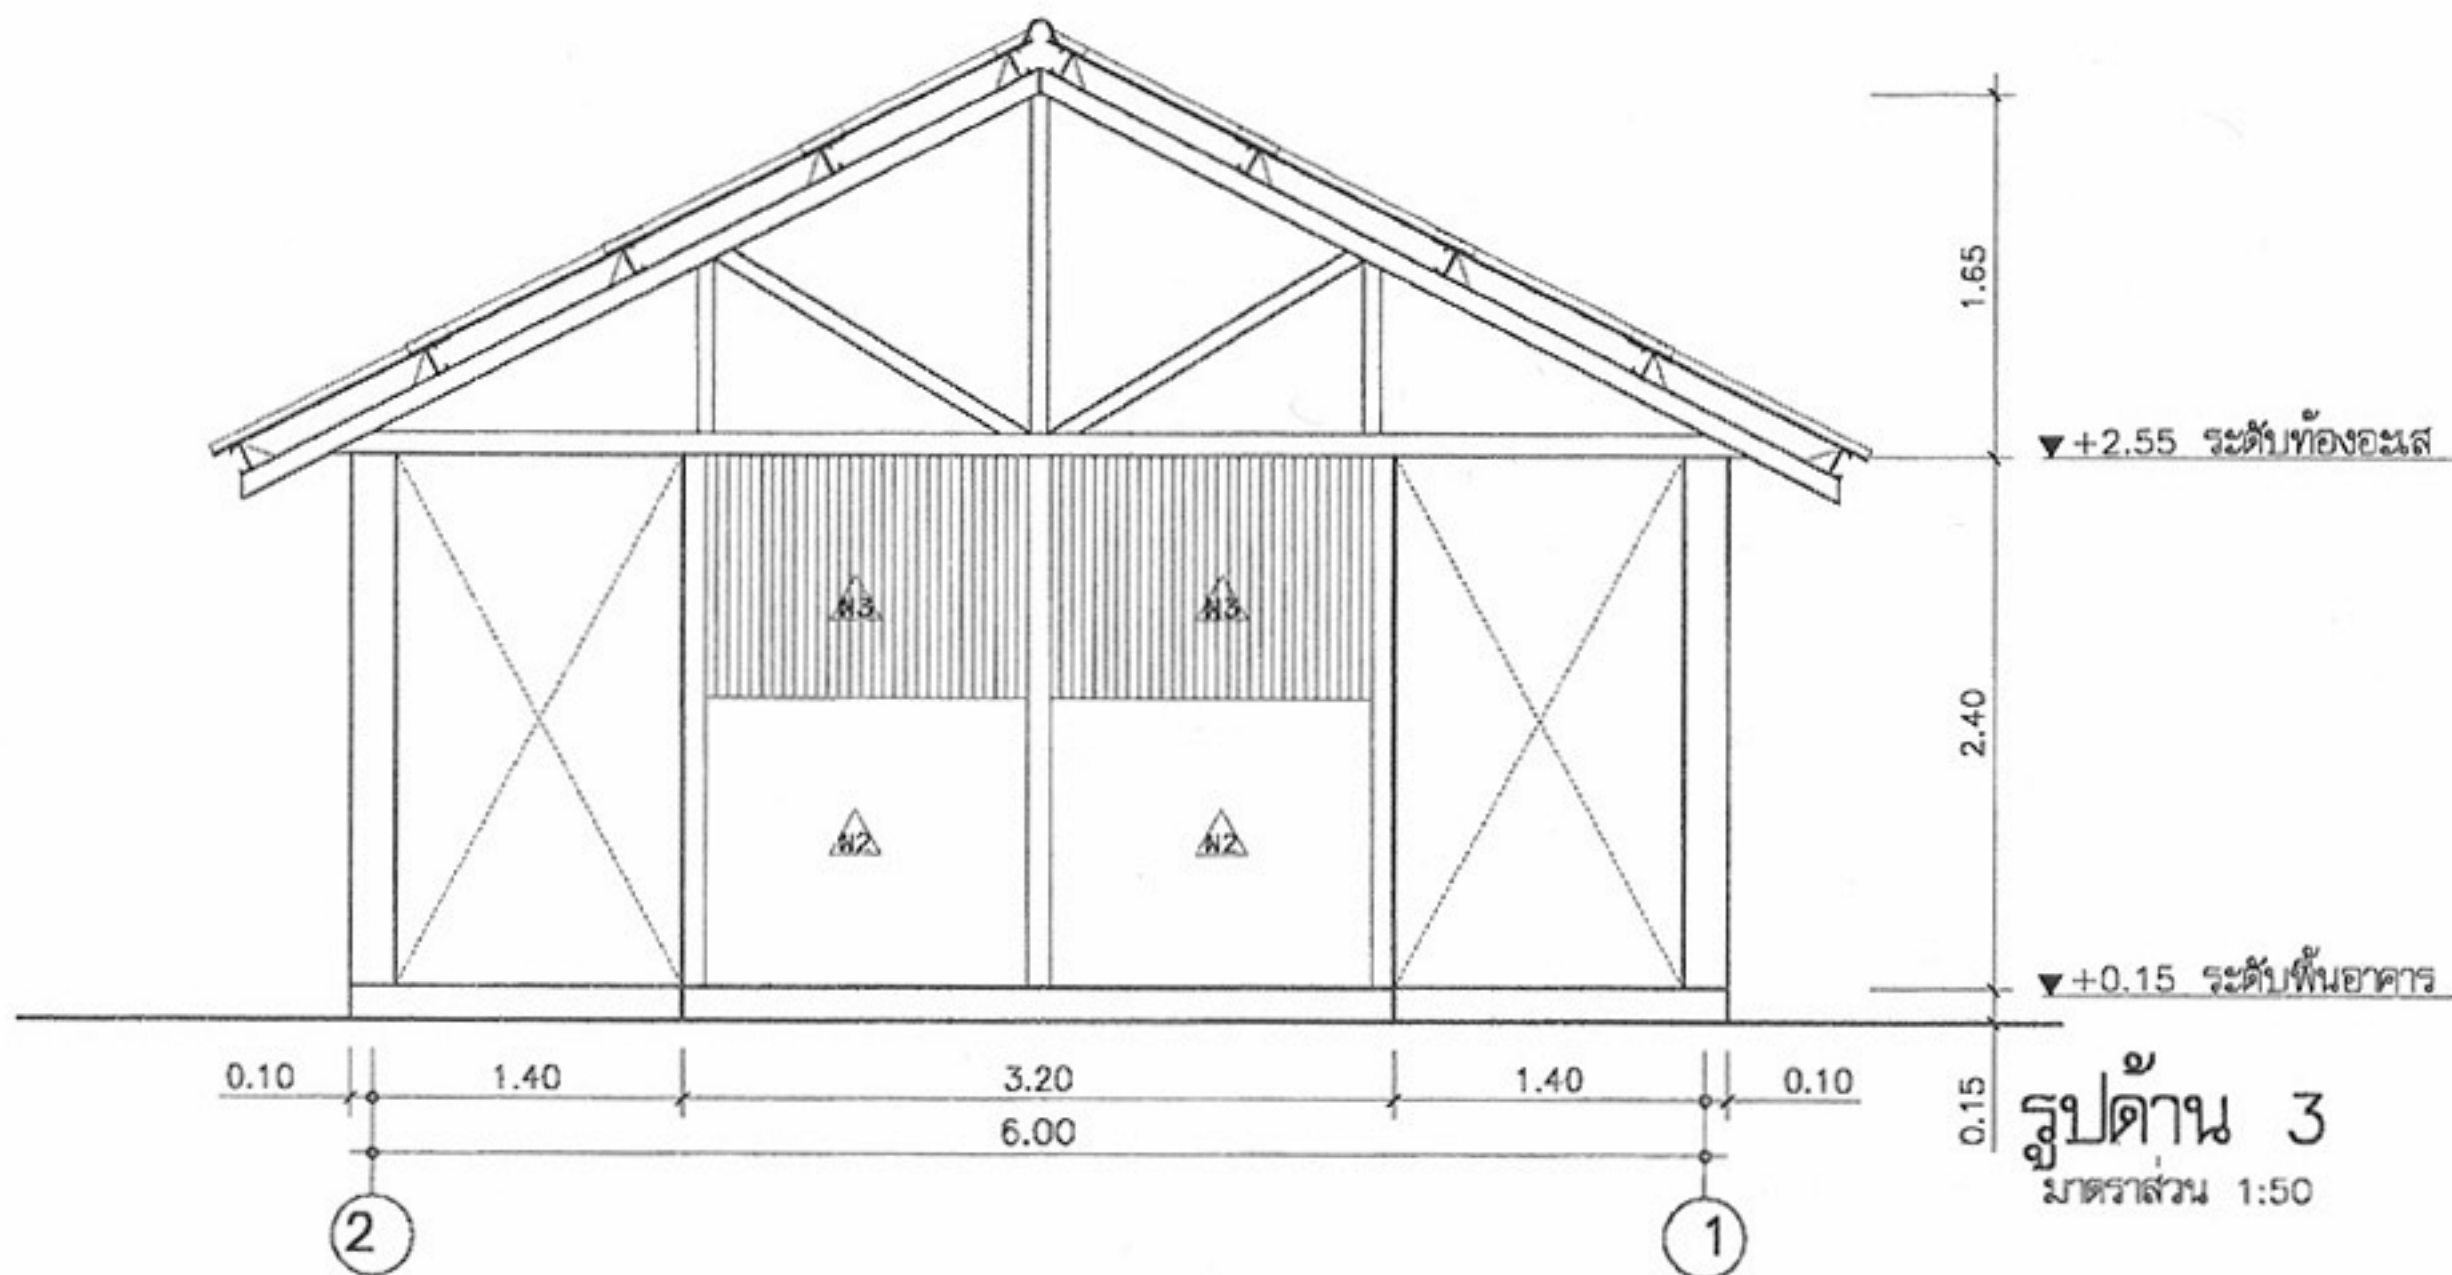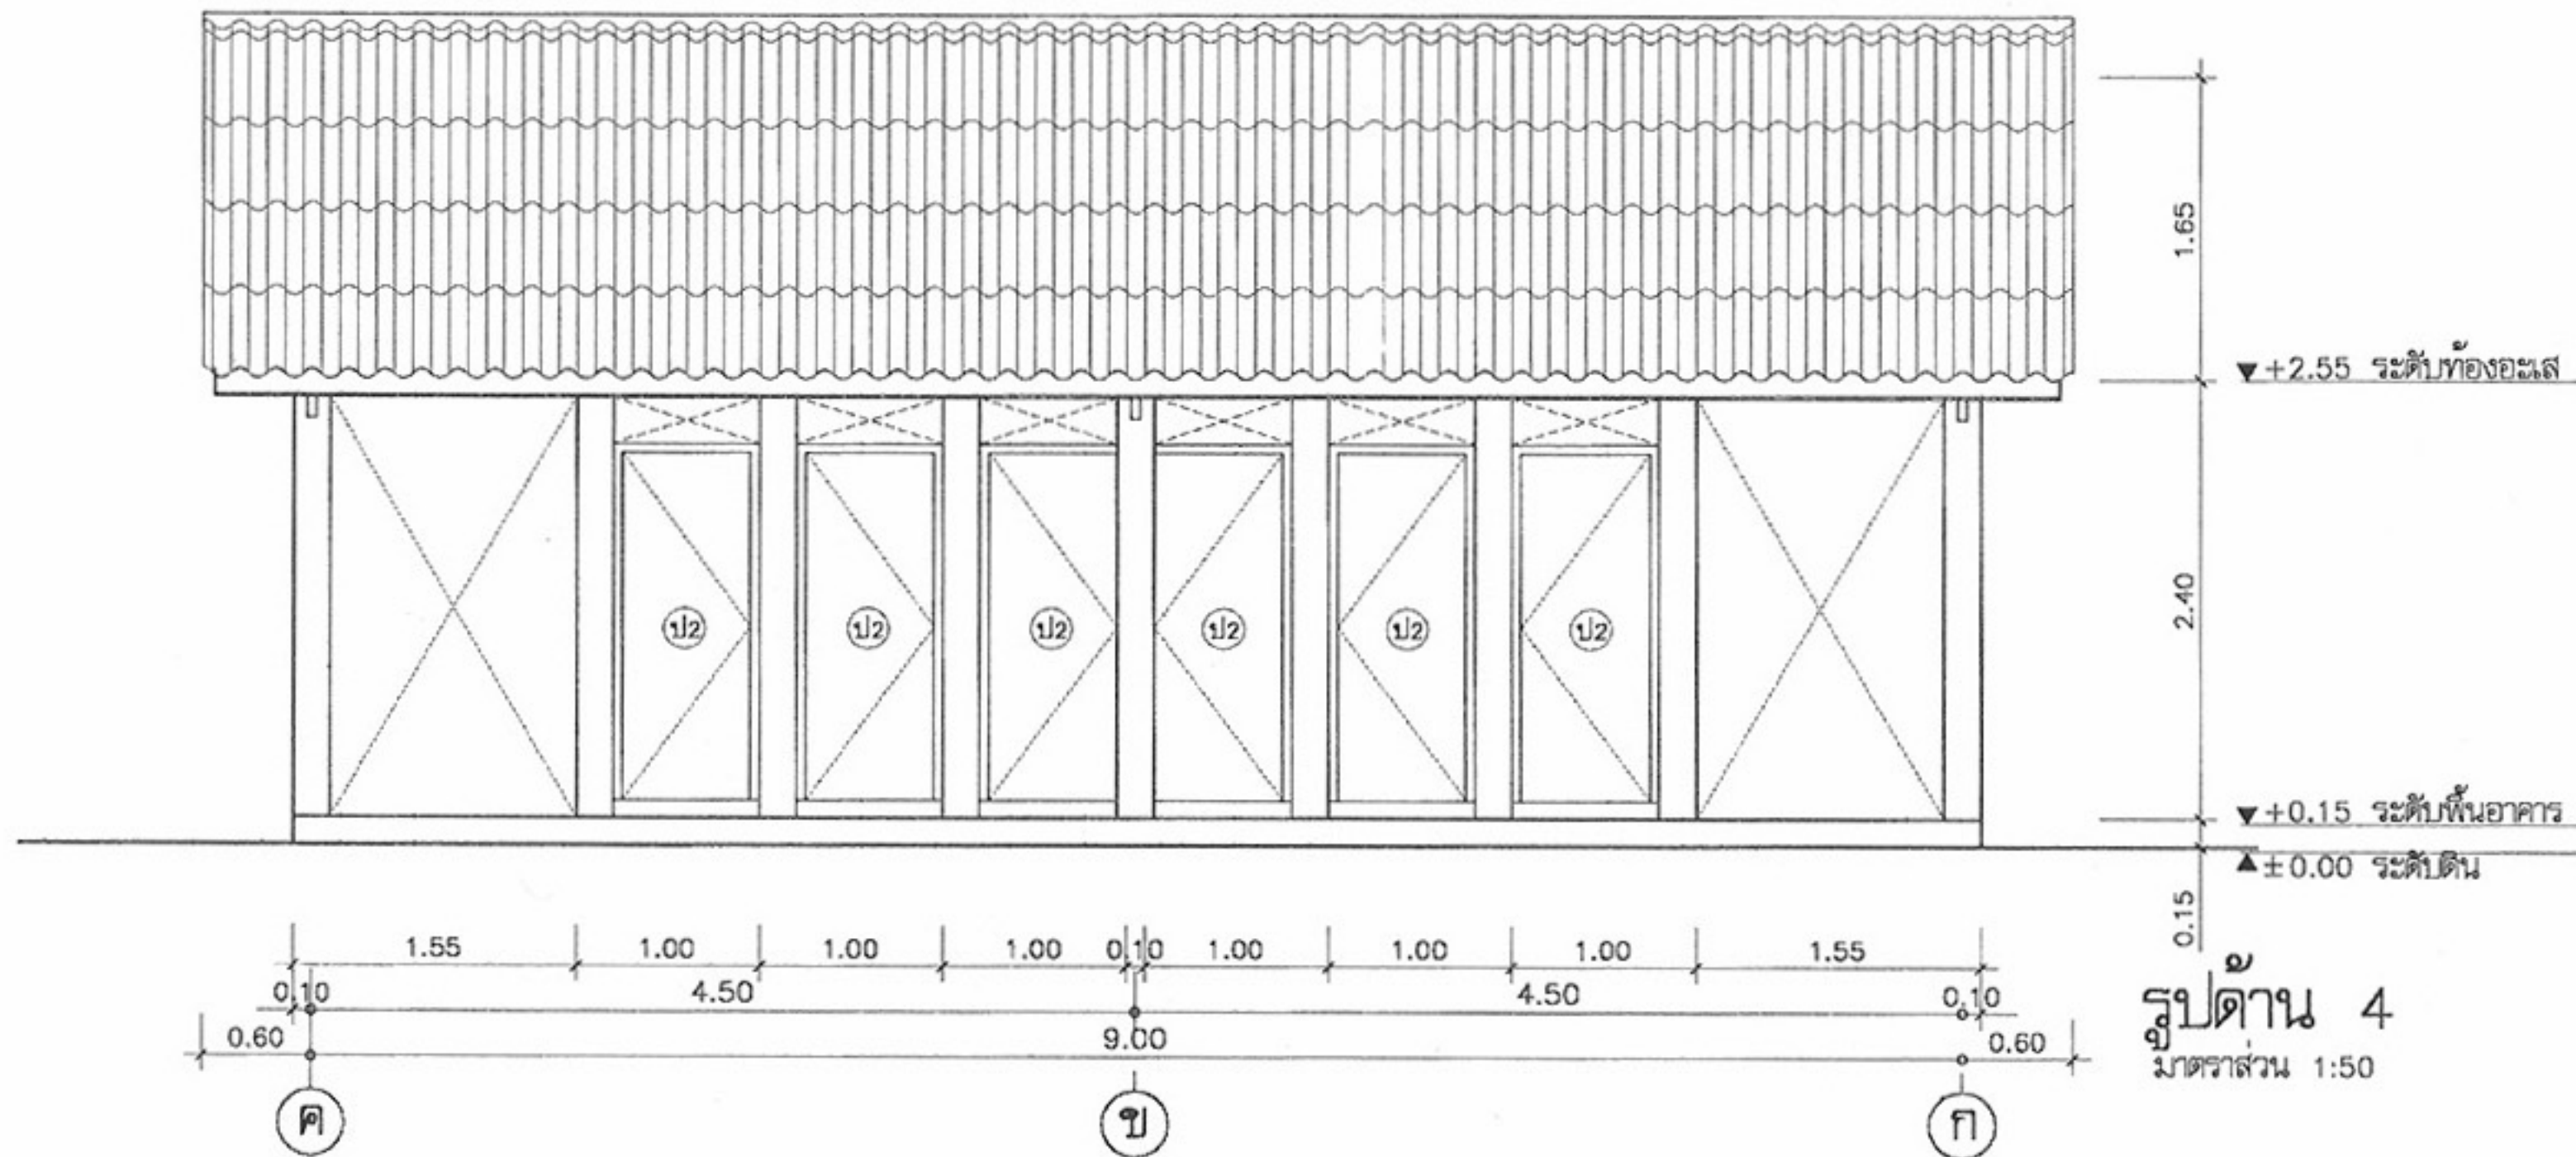

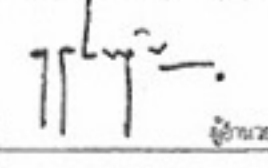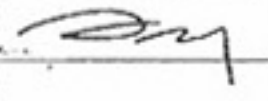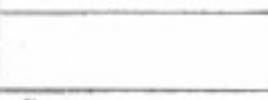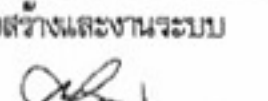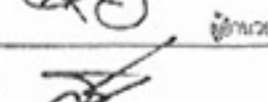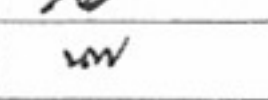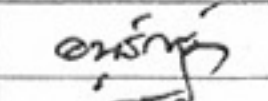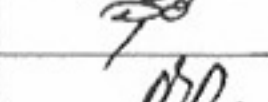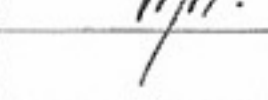	
โครงการแบบอาคารเพื่อประชาชน ไทยช่วยไทย	
แบบ บ้านผู้ประสบภัย 3 ห้องสุขารวม	
เจ้าหน้าที่โครงการ 	ผู้ควบคุมการดำเนินงาน 
สถาปนิก 	สถาปนิก 
เจ้าหน้าที่วิศวกรรมโครงสร้างและงานระบบ 	
วิศวกร โครงสร้าง 	วิศวกร ไฟฟ้า 
วิศวกร ไฟฟ้า และเครื่องกล 	วิศวกร สุขาภิบาล 
อนุมัติ 	
(นายสว่าง ศรีสุกัน) อธิบดีกรมโยธาธิการและผังเมือง	
แสดงแบบ รูปด้าน 3,4	
มาตรฐาน 1:50	
วัน/เดือน/ปี 21 พ.ย. 2546	
เลขที่แบบ ม.บ.462099	
แผ่นที่ A-10	จำนวนแผ่น 12

หมายเหตุ แบบที่แสดงอยู่นี้ได้รับการยืมส่วน เพื่อใช้แสดงผลทางหน้าจอตานั้น สำหรับแบบที่ใช้ขออนุญาตก่อสร้าง ให้ถ่ายสำเนาจากหนังสือแบบบ้าน



โครงการแบบอาคารเพื่อประชาชน
ไทยช่วยไทย

แบบ
บ้านผู้ประสบภัย 3 ห้องสุขารวม

สำนักสถาปัตย์กรรม
[Signature]

สถาปัตย์กรรม
[Signature]
สถาปัตย์
สถาปัตย์
สถาปัตย์

สำนักวิศวกรรมโครงสร้างและงานระบบ
[Signature]

วิศวกรรม
โครงสร้าง
วิศวกรรมไฟฟ้า
และเครื่องกล
วิศวกรรม
สุขาภิบาล
[Signatures]

อนุมัติ
[Signature]
(นายสว่าง ศรีสุคนธ์)
อธิบดีกรมโยธาธิการและผังเมือง



แสดงแบบ
รูปตัด 1,2

มาตราส่วน 1:50


วัน/เดือน/ปี 21 พ.ย. 2546

เลขที่แบบ ม.บ.462099

แผ่นที่ A-11 จำนวนแผ่น 12

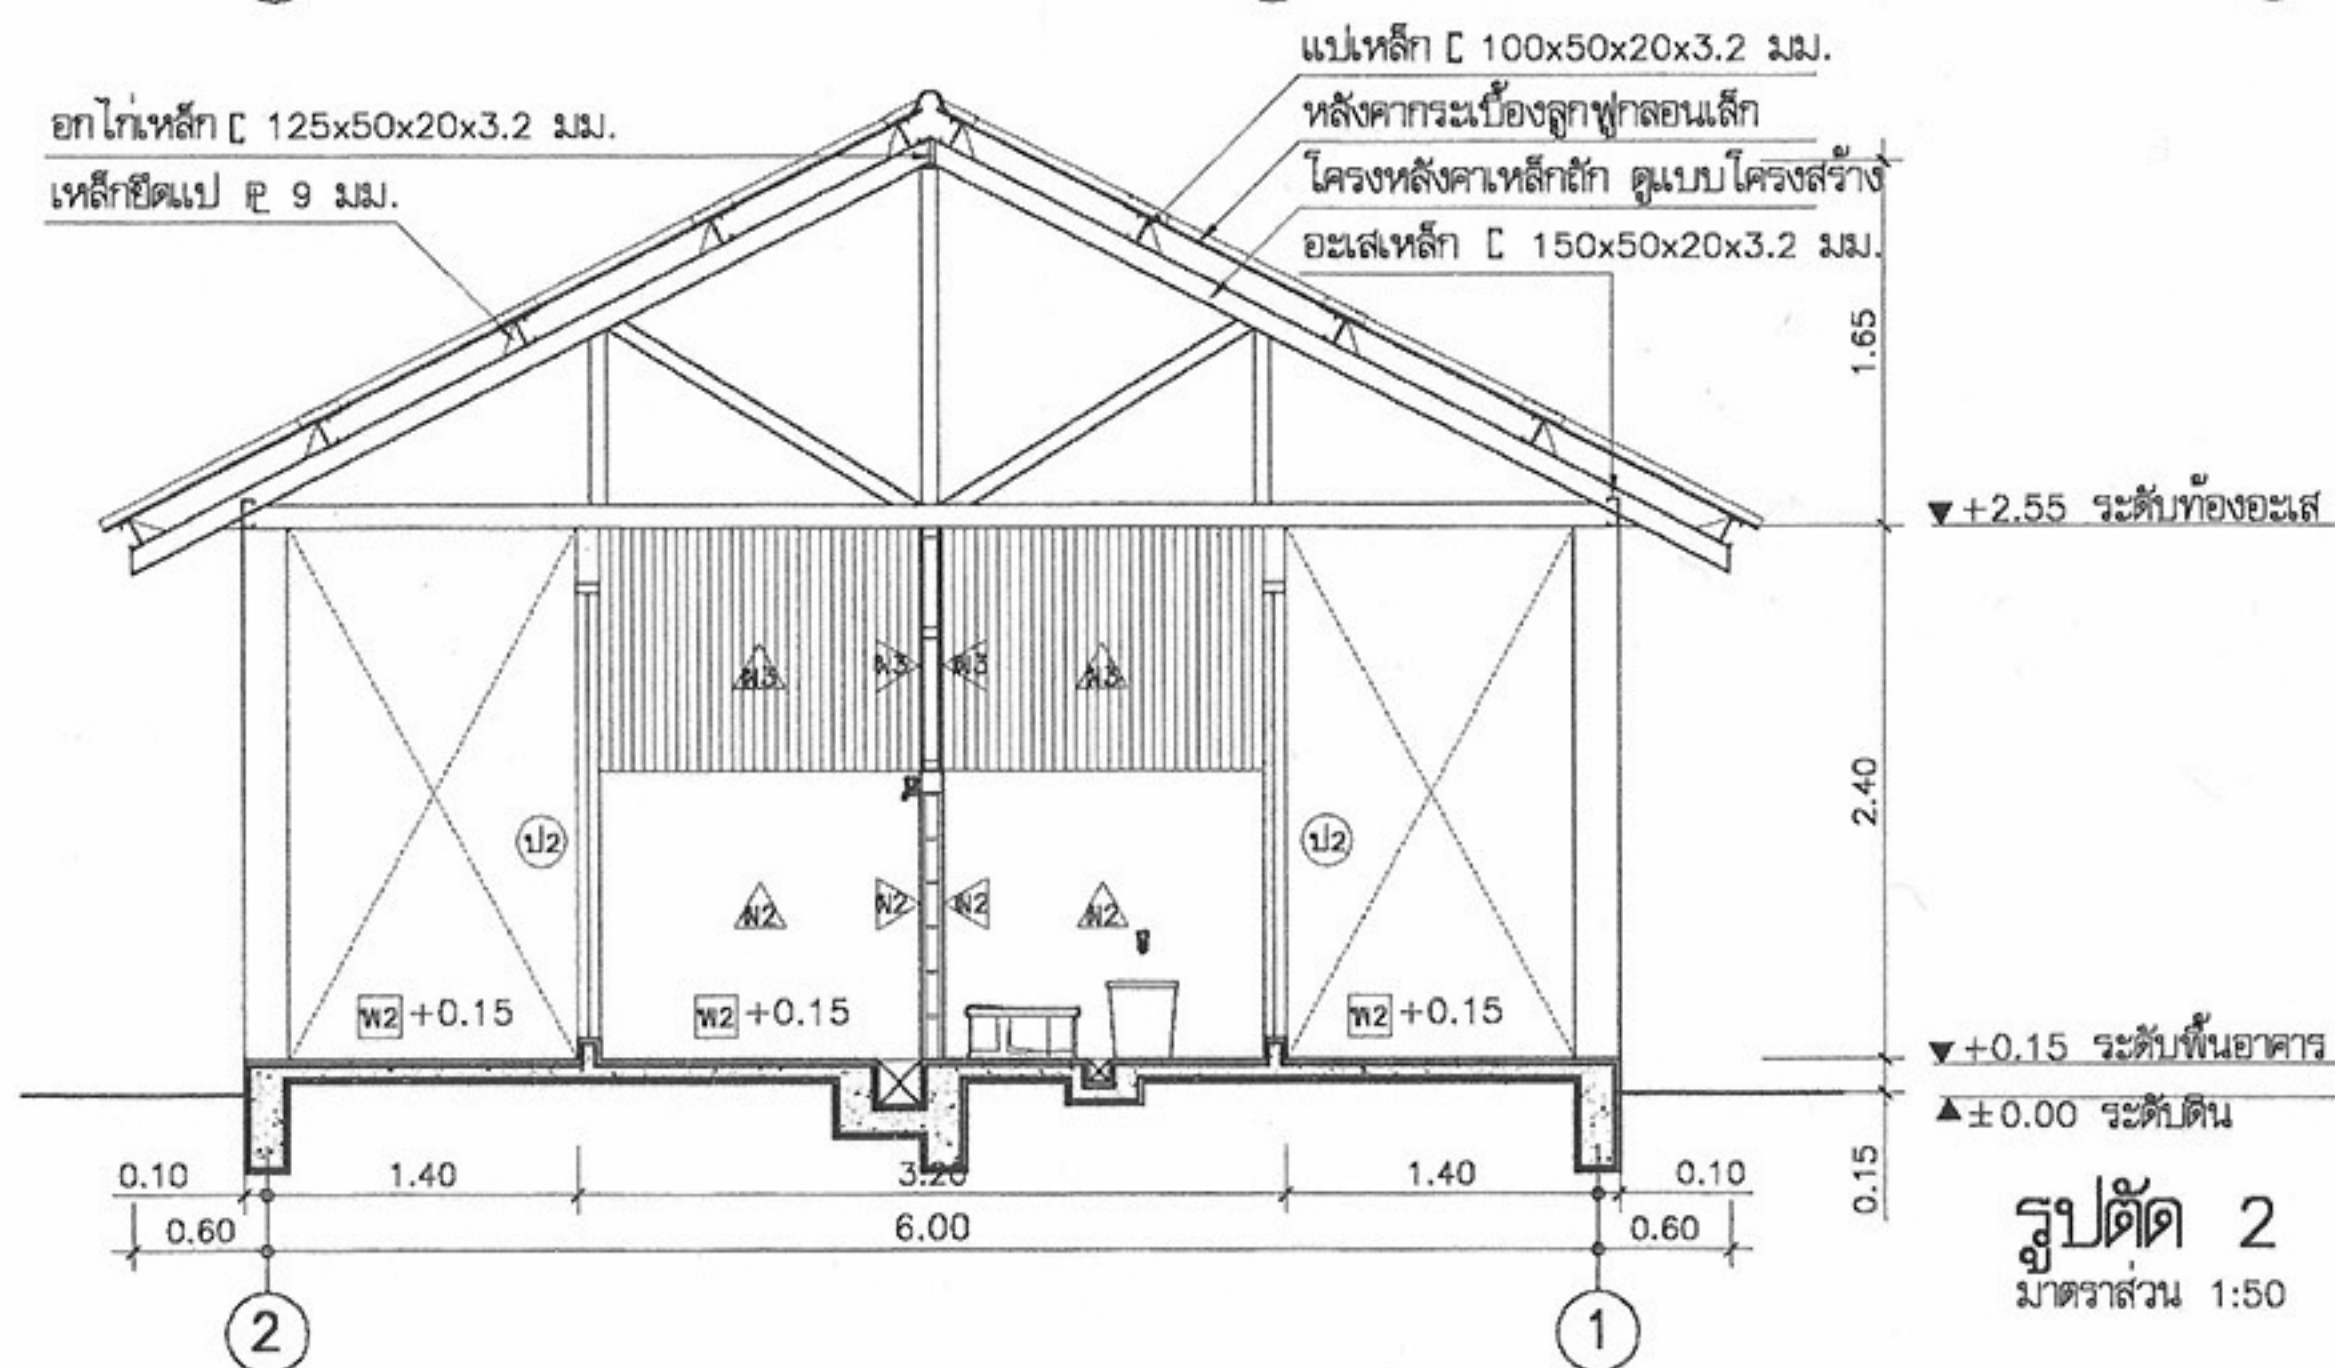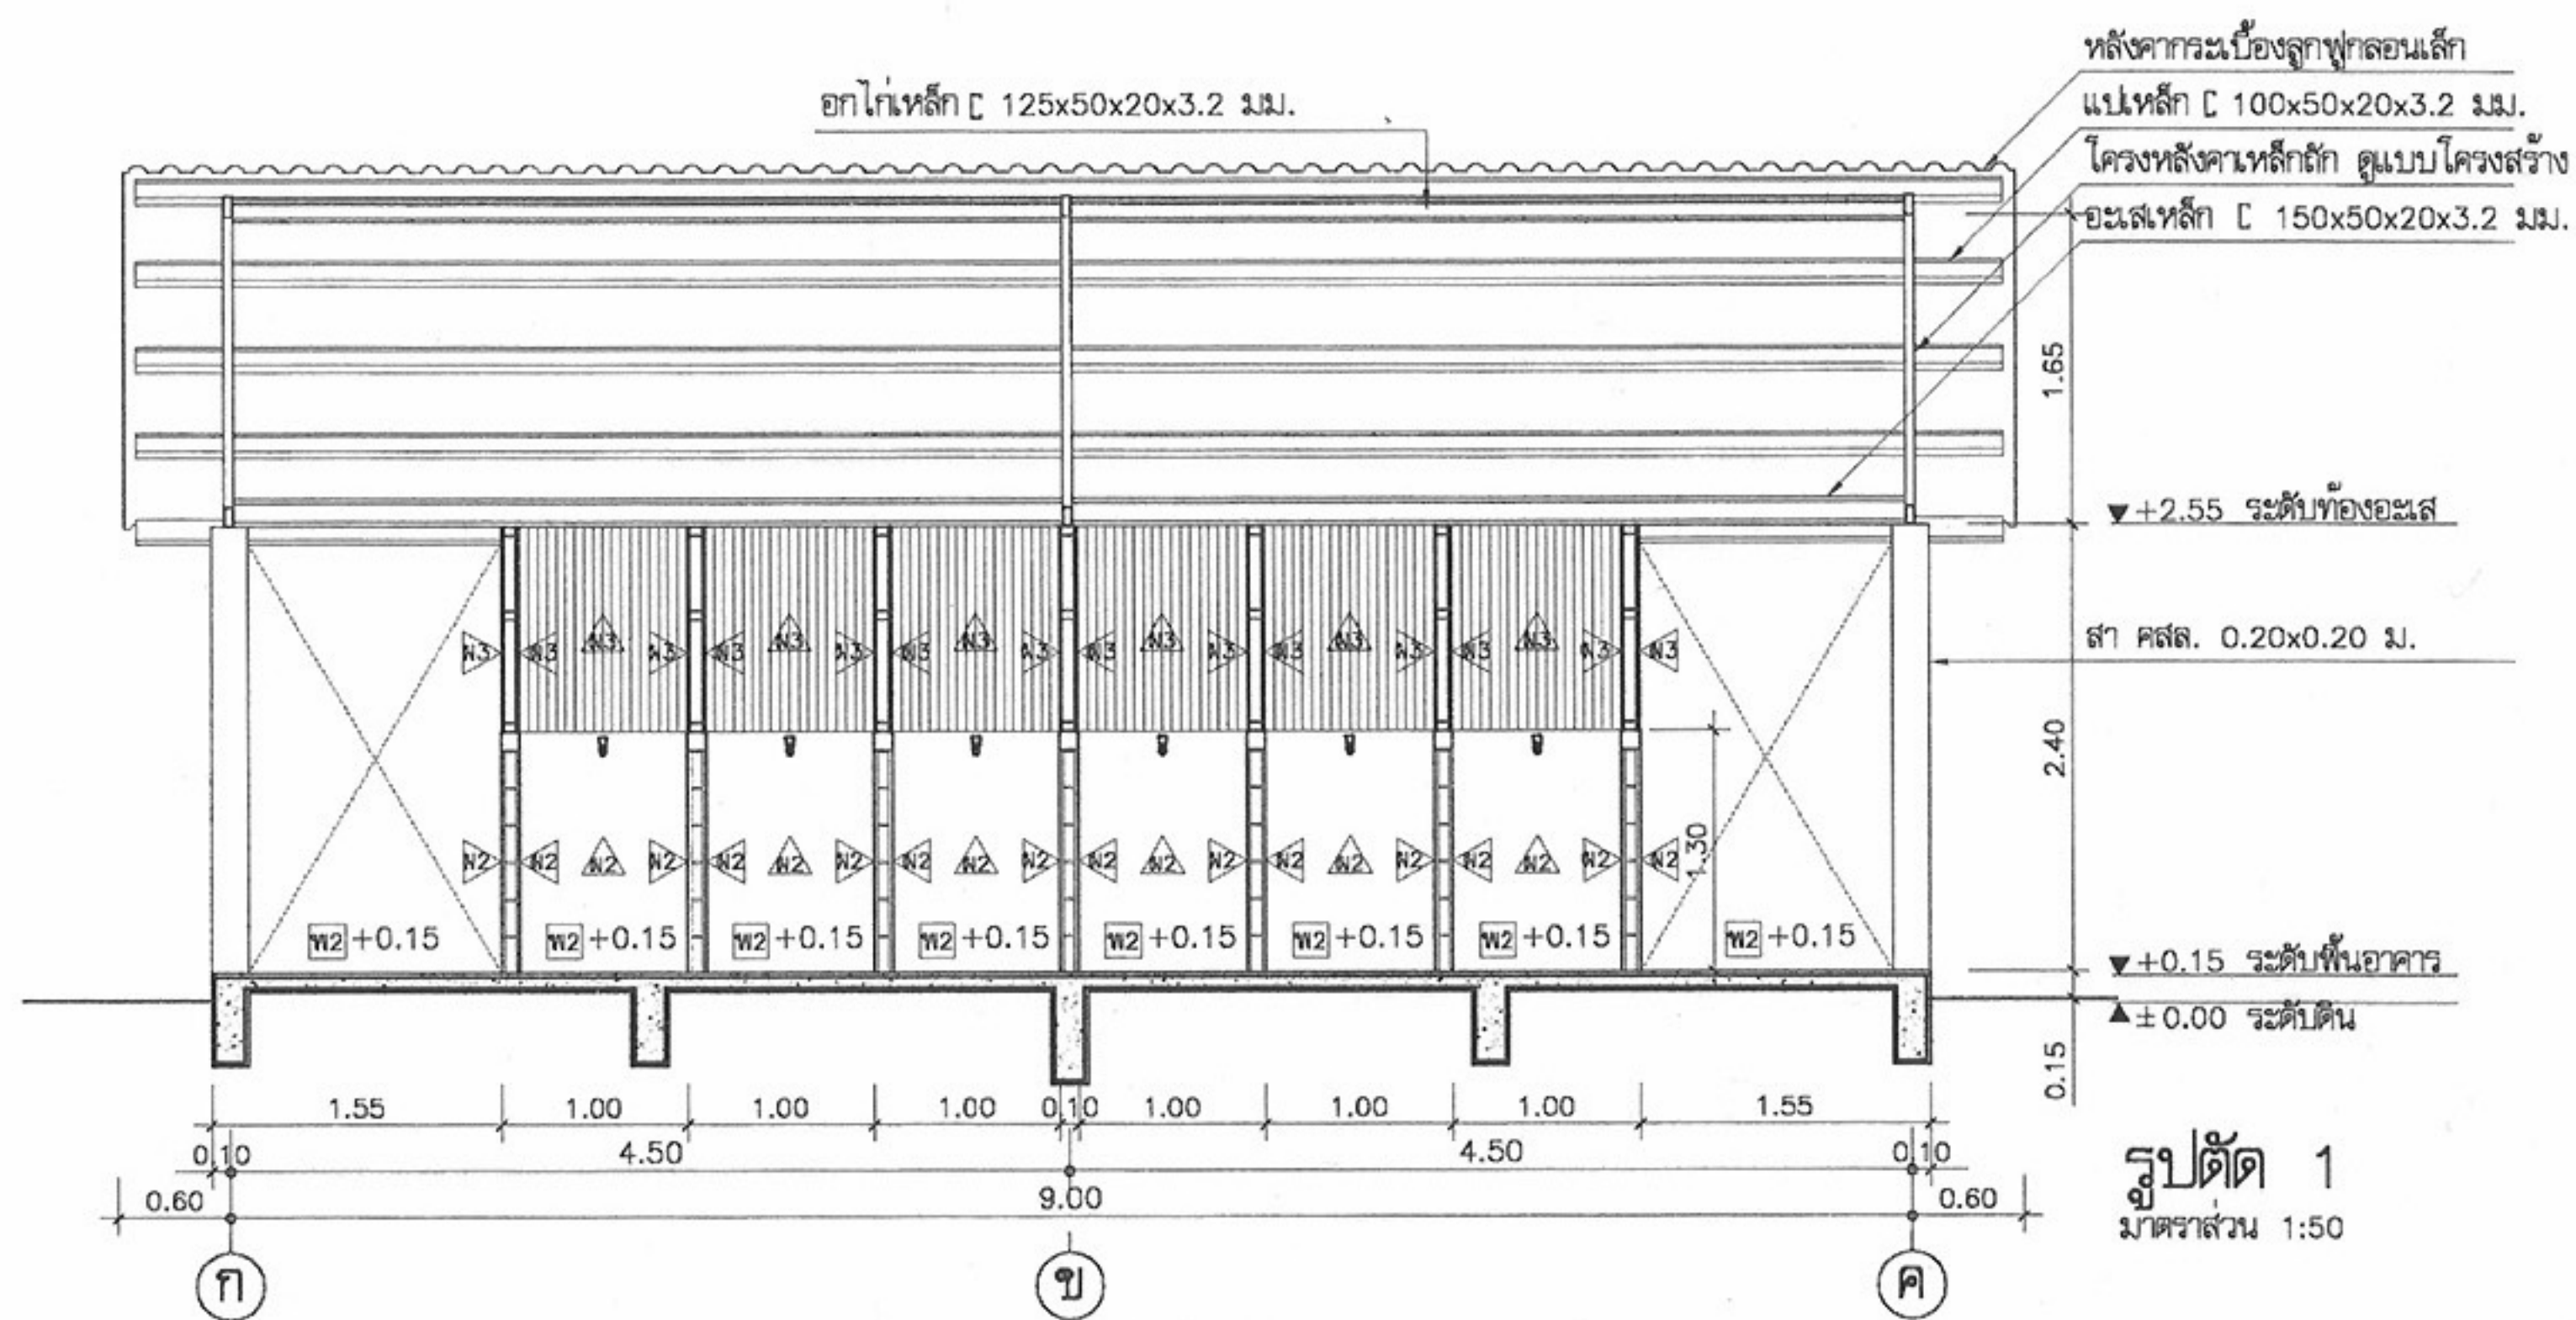


หมายเหตุ แบบที่แสดงอยู่นี้ได้รับการยืมส่วน เพื่อใช้แสดงผลทางหน้าจอนี้เท่านั้น สำหรับแบบที่ใช้ขออนุญาตก่อสร้าง ให้ถ่ายสำเนาจากหนังสือแบบบ้าน

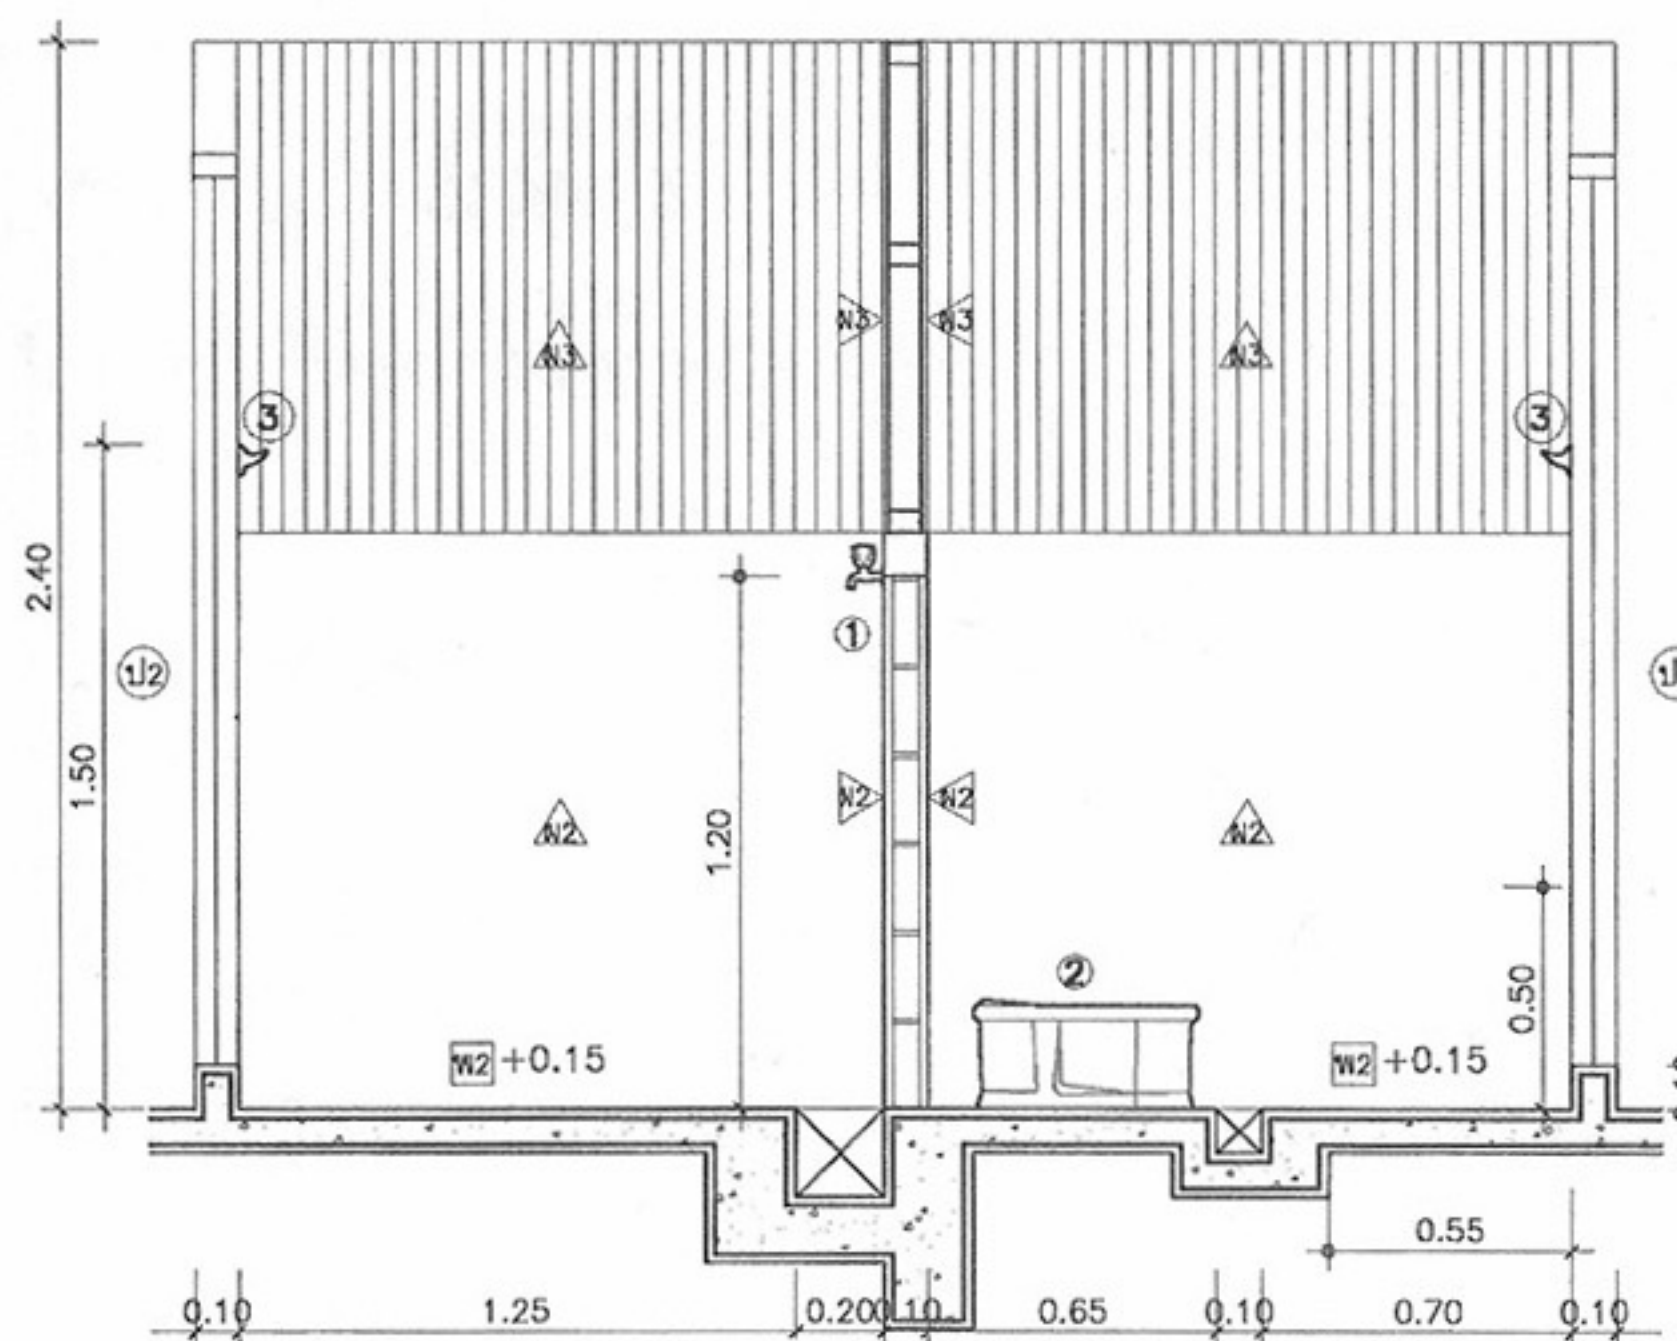


รูปตัด 1-1
มาตราส่วน 1:25

รูปตัด 2-2
มาตราส่วน 1:25

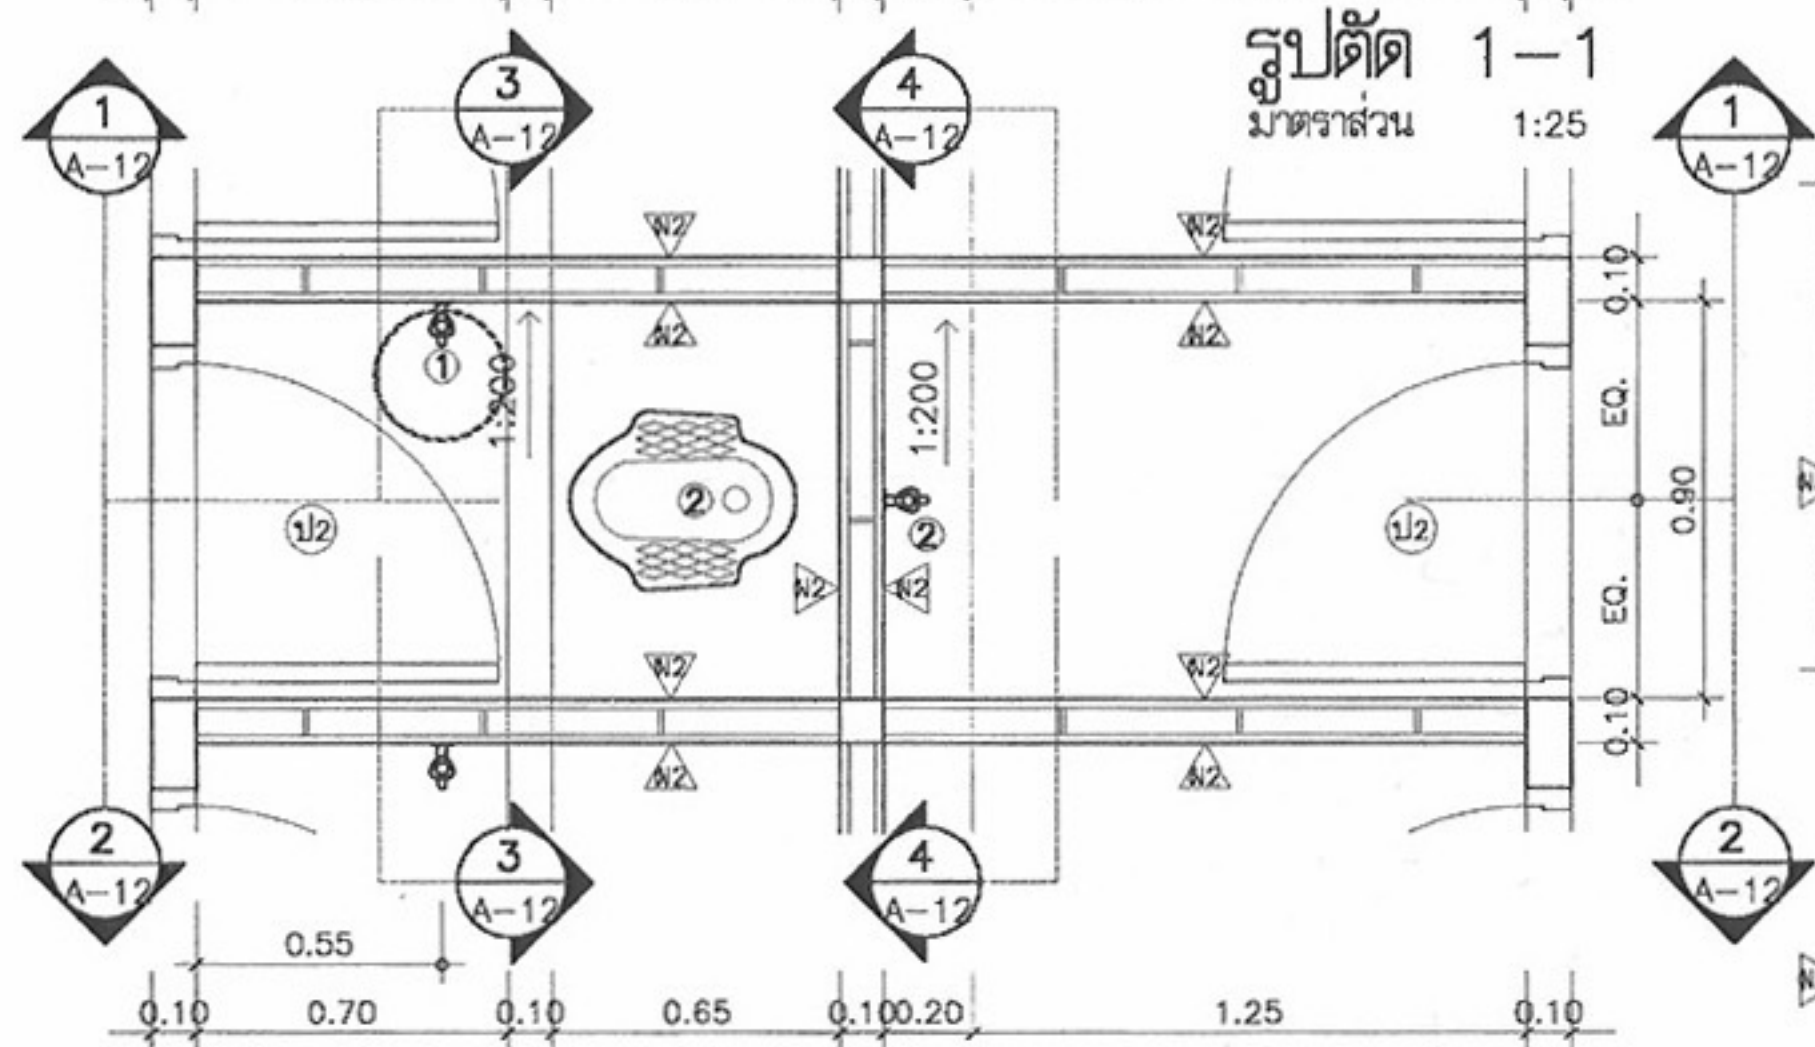

รายการอุปกรณ์ห้องน้ำ

รูปตัด 3-3
มาตราส่วน 1:25

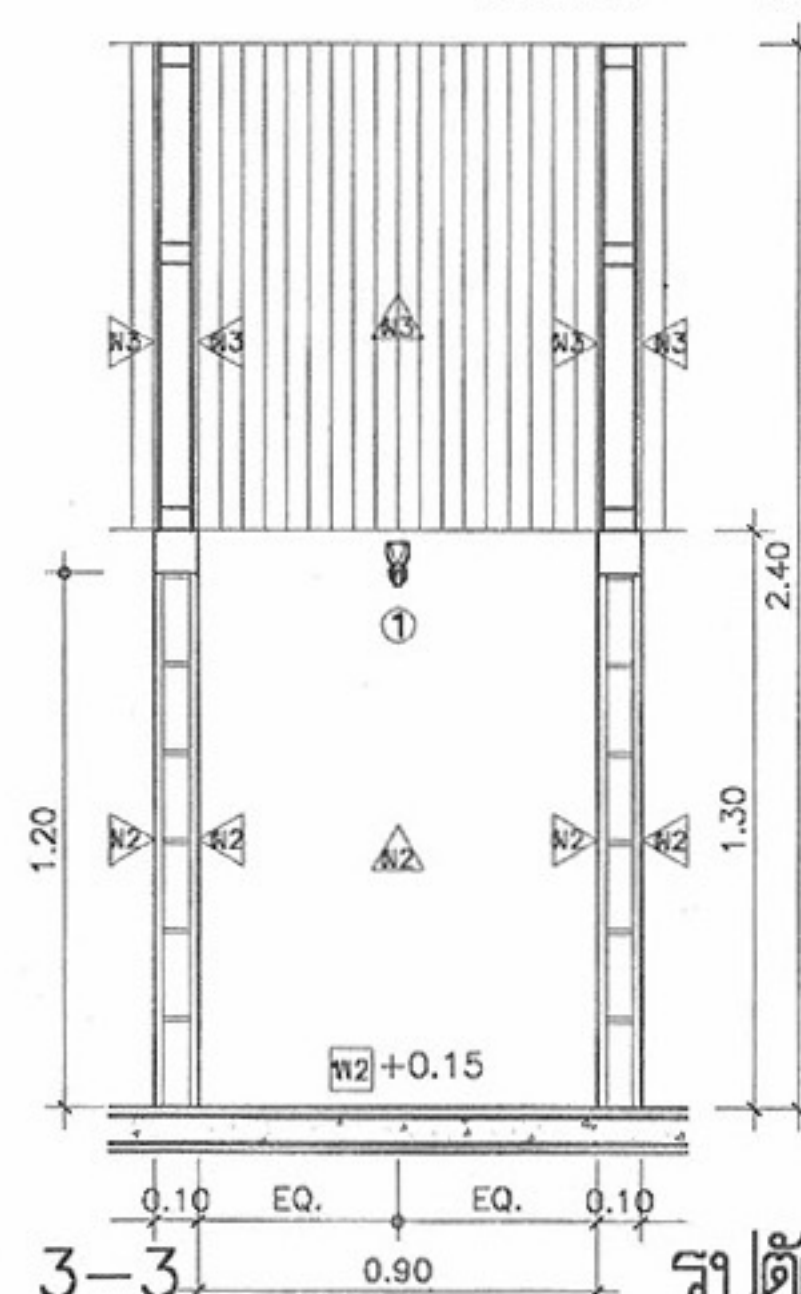

รูปตัด 4-4
มาตราส่วน 1:25



โครงการแบบอาคารเพื่อประชาชน

ไทยช่วยไทย

449,071

บ้านประสาธน์ 3 ห้องสุขารวม

สำนักงานส่งเสริมการค้าในต่างประเทศ

[illegible]

สำนักวิศวกรรมโครงสร้างและงานระบบ

ปัญหาการ

โดยนิติน

“สงครามไฟฟ้า”

แบบจำลอง

အကျဉ်းချုပ်

สหกรณ์

စာမျက်နှာ ၁၀

(นายสว่าง ศรีศุภน)
อธิบดีกรมโยธาธิการและผังเมือง

UNION

ขยายห้องน้ำ

บทที่ 1: 1:25

วัน/เดือน/ปี 21 พ.ย. 2546

เลขที่แบบ ม.บ.462099

แผ่นที่
A-12

จำนวนแผ่น	12
-----------	----

หมายเหตุ แบบที่แสดงอยู่นี้ได้รับการย่อส่วน เพื่อใช้แสดงผลทางหน้าจอเท่านั้น สำหรับแบบที่ใช้ขออนุญาตก่อสร้าง ให้ถ่ายสำเนาจากหนังสือแบบบ้าน

รายการประกอบแบบ


ให้ใช้ มยธ.101-106 เป็นรายการประกอบแบบและมีรายการเฉพาะแบบดังนี้

- 1.คอนกรีตให้ใช้ ค2(f_c ทรงกระบอก=200ksc)
- 2.เหล็กเสริมคอนกรีต ให้ใช้เหล็กเส้นกลม SR-24(f_y =2400ksc)
- 3.เหล็กรูปพรรณ ที่จะนำมาใช้ต้องมีคุณสมบัติดังต่อไปนี้
 - 3.1 ใช้เหล็กที่มีคุณสมบัติเป็นไปตามมาตรฐาน ASTM-A36 หรือเทียบเท่า
 - 3.2 การต่อเชื่อมให้ทำการต่อเชื่อมด้วยการเชื่อมไฟฟ้า(Arc Welding) โดยรอบทุกจุด
 - 3.3 เหล็กที่นำมาใช้จะต้องปราศจากสนิมรุม ไม่บิดงอหรือเสียรูป
 - 3.4 ให้ทำสีกันสนิมประเภท Lead Oxide อย่างน้อย 2 ชั้น
 - 3.5 รายละเอียดจุดเชื่อมต่อระหว่างโครงสร้างเหล็กส่วนต่างๆ สามารถดัดแปลงแก้ไขโดยวิศวกรผู้ควบคุมงานได้ หากทำการก่อสร้างจริงแล้วเกิดปัญหา ไม่สามารถทำตามแบบที่แสดงได้

4.ฐานราก

- 4.1 ในกรณีที่ดินบริเวณก่อสร้าง รับน้ำหนักปลอดภัยได้ไม่น้อยกว่า 8 ตันต่อตารางเมตร ให้ใช้ฐานรากแผ่
- 4.2 ในกรณีที่ดินบริเวณก่อสร้าง รับน้ำหนักปลอดภัยได้น้อยกว่า 8 ตันต่อตารางเมตร ให้ใช้ฐานรากตอกเข็ม และ หากใช้ฐานรากแบบตอกเข็ม เสริมที่นำมาใช้ต้องมีคุณสมบัติ ดังต่อไปนี้
 - 4.2.1 เป็นเสาเข็มเหล็กเหลี่ยมกลวงขนาด 0.15x0.15 มีความยาว 6.00 เมตร
 - 4.2.2 รับน้ำหนักปลอดภัยได้ไม่น้อยกว่า 1.7 ตัน/ตัน

5.รายละเอียดหรือคุณลักษณะของวัสดุ หรืออุปกรณ์ในแบบ หรือในรายการประกอบแบบ ซึ่งที่ระบุหรือมีได้ระบุไว้ หากมีการกำหนดมาตรฐานผลิตภัณฑ์อุตสาหกรรมแล้ว ให้ไปตามมาตรฐานผลิตภัณฑ์อุตสาหกรรมนั้น

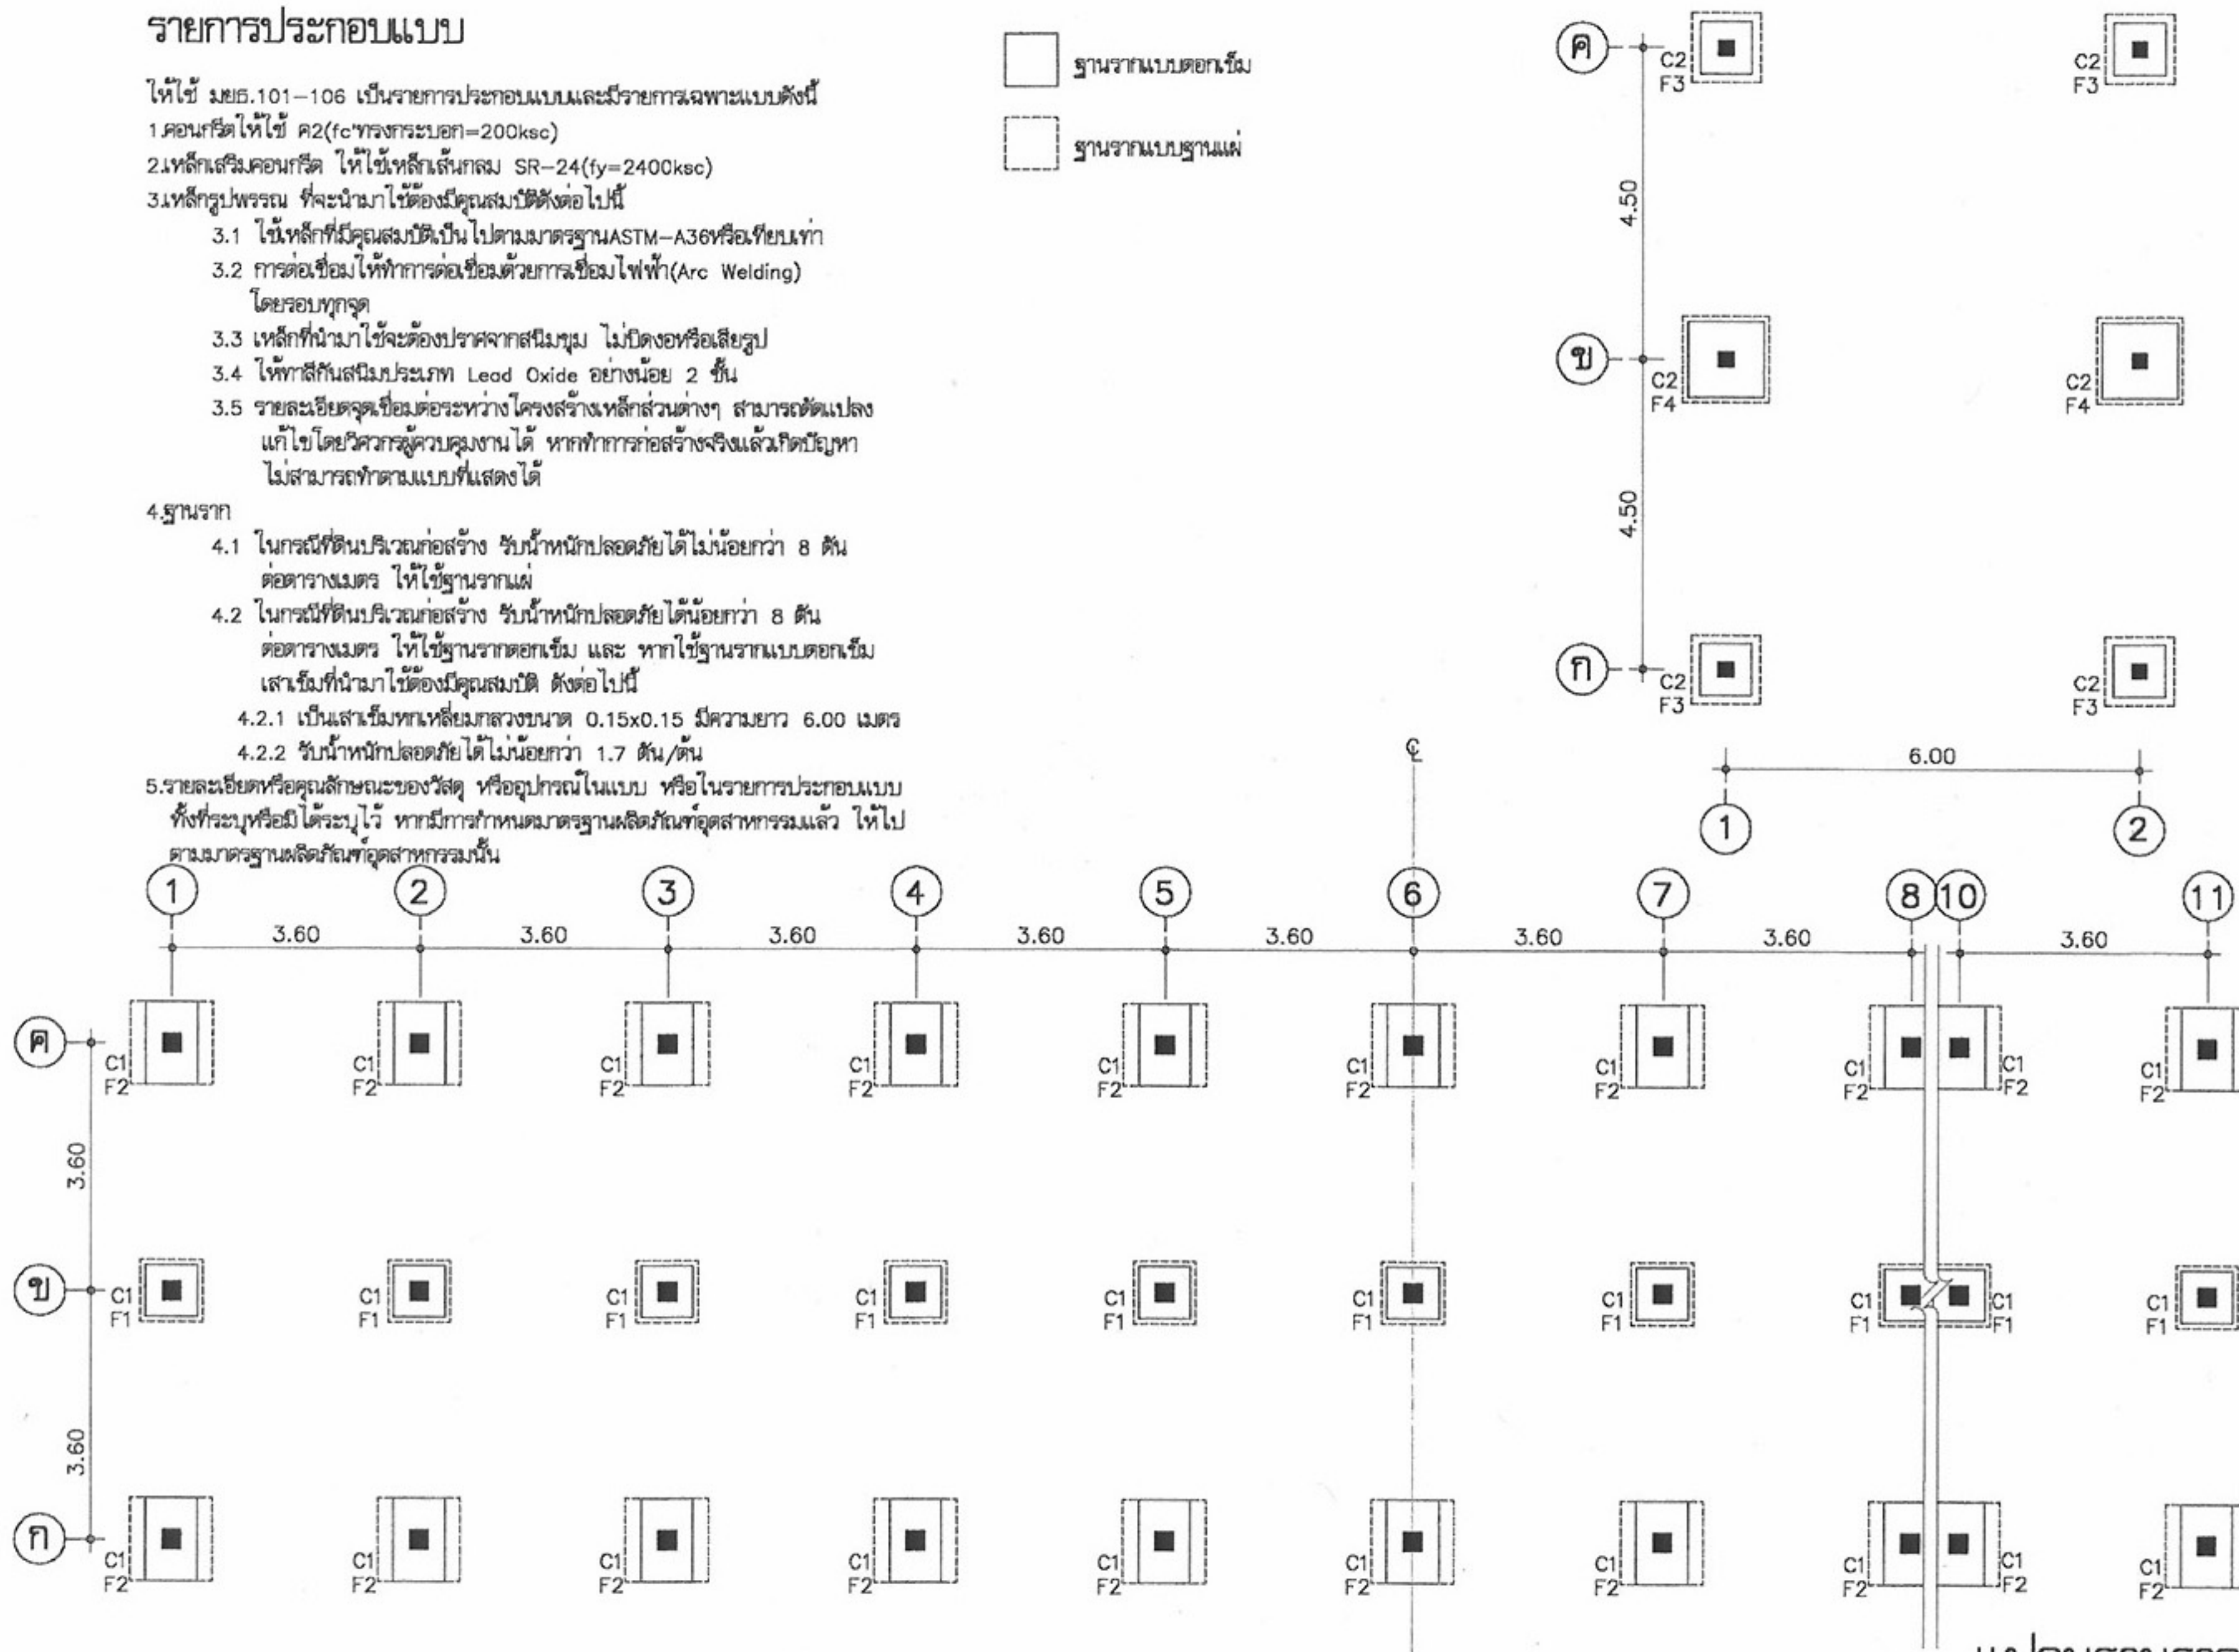

แปลนฐานราก
มาตราส่วน 1:100

โครงการแบบอาคารเพื่อประชาชน ไทยช่วยไทย	
แบบ บ้านผู้ประสบภัย 3 ห้องสุขารวม	
สำนักสถาปัตยกรรม 	
สถาปัตยกรรม	
สำนักวิศวกรรมโครงสร้างและงานระบบ	
วิศวกรรม	
โครงสร้าง	
วิศวกรรมไฟฟ้าและเครื่องกล	
วิศวกรรมสุขาภิบาล	
อนุมัติ 	
(นายสว่าง ศรีสุกัน) อธิบดีกรมโยธาธิการและผังเมือง	
แปลนฐานราก	
มาตราส่วน	1:100
วัน/เดือน/ปี	21 พ.ย. 2546
เลขที่แบบ	ม.บ.462099
แผ่นที่	จำนวนแผ่น
S-01	8

หมายเหตุ แบบที่แสดงอยู่นี้ได้รับการย่อส่วน เพื่อใช้แสดงผลทางหน้าจอเท่านั้น สำหรับแบบที่ใช้ขออนุญาตก่อสร้าง ให้ถ่ายสำเนาจากหนังสือแบบบ้าน



โครงการแบบอาคารเพื่อประชาชน
ไทยช่วยไทย

แบบ
บ้านผู้ประสบภัย 3 ห้องสุขารวม

สำนักสถาปัตยกรรม
ผู้ควบคุมการก่อสร้าง

สถาปนิก	สถาปนิก
สถาปนิก	สถาปนิก
สถาปนิก	สถาปนิก

สำนักวิศวกรรมโครงสร้างและงานระบบ
ผู้ควบคุมการก่อสร้าง

วิศวกรรม	วิศวกร
โครงสร้าง	วิศวกร
วิศวกรรมไฟฟ้า	วิศวกร
และเครื่องกล	วิศวกร
วิศวกรรม	วิศวกร
สุขาภิบาล	วิศวกร

อนุมัติ
(นายสว่าง ศรีสุกัน)
อธิบดีกรมโยธาธิการและผังเมือง

แสดงแบบ
แปลน เสา คาน พื้น

มาตราส่วน	1:100
วัน/เดือน/ปี	21 พ.ย. 2546
เลขที่แบบ	ม.บ.462099
แผ่นที่	จำนวนแผ่น
S-02	8



หมายเหตุ

B1= WF 150x150x7x10 มม.

B2= WF 400x200x8x13 มม.

B3= C 125x65x6x8 มม.



CX= WF400x200x8x13 มม.

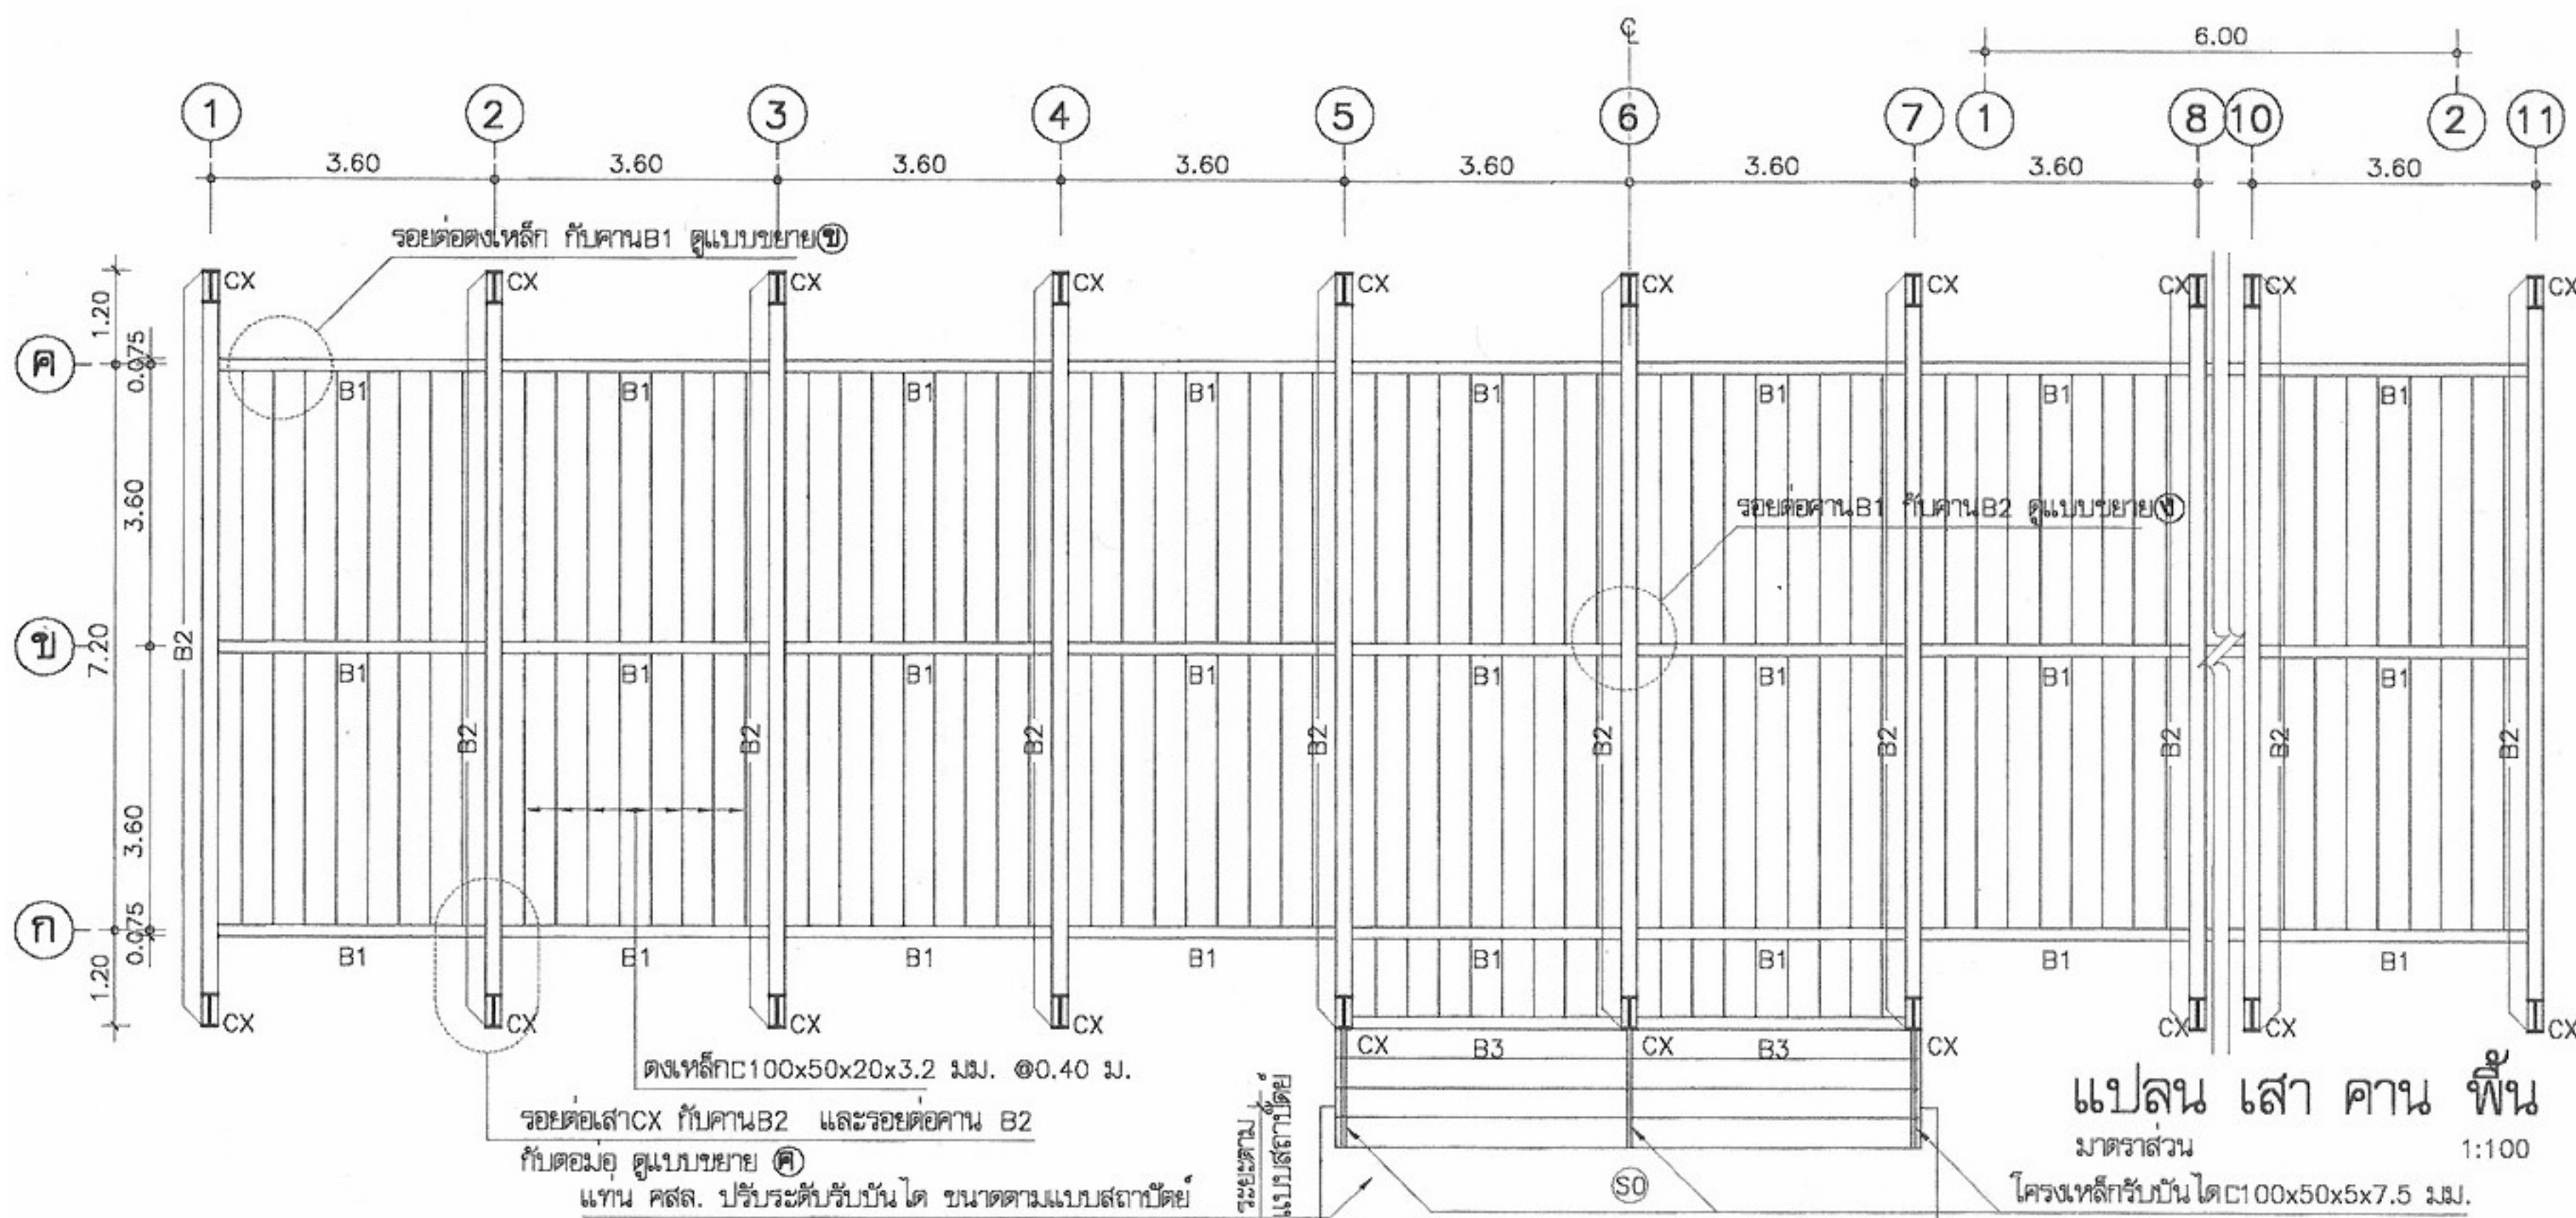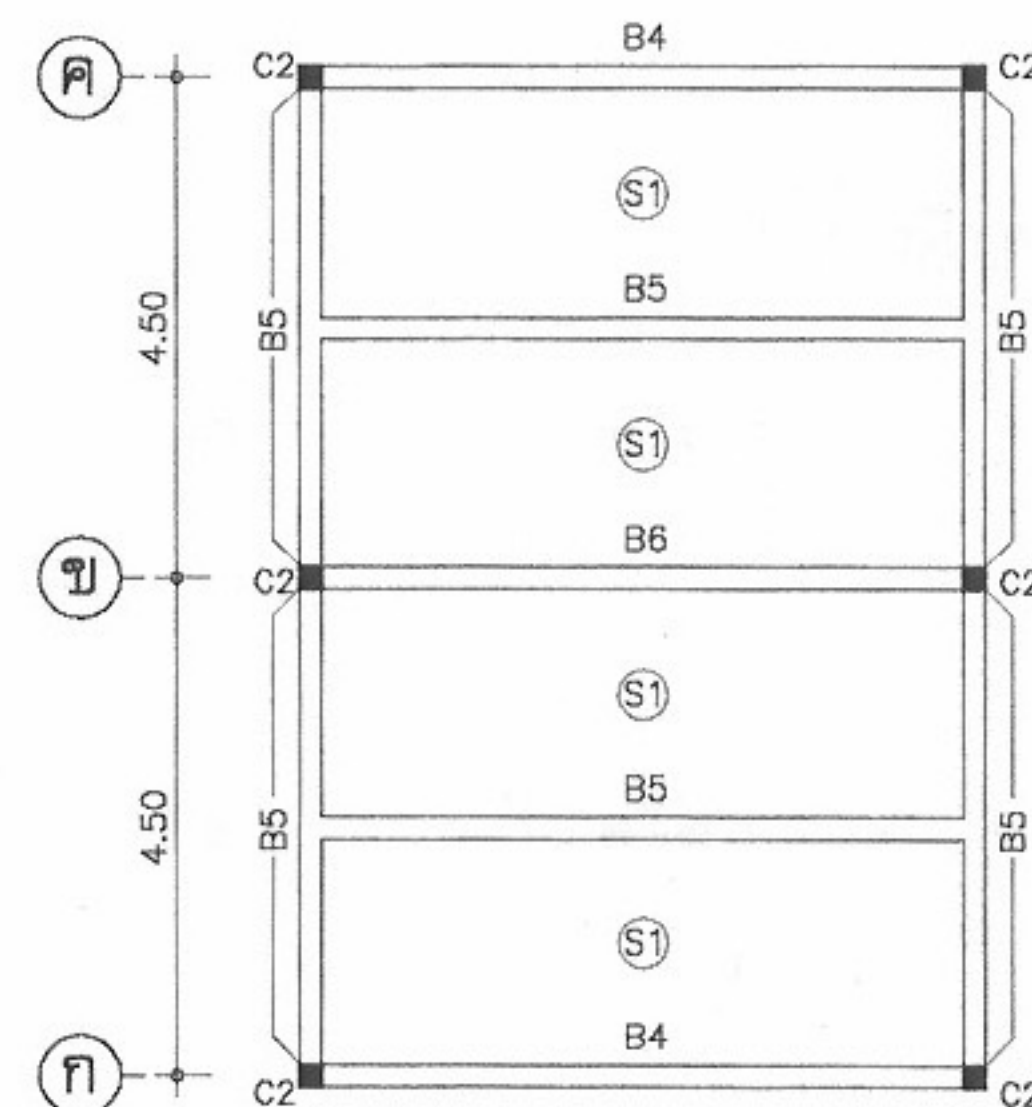

หมายเหตุ แบบที่แสดงอยู่นี้ได้รับการยืมส่วน เพื่อใช้แสดงผลทางหน้าจอนี้ สำหรับแบบที่ใช้ขออนุญาตก่อสร้าง ให้ถ่ายสำเนาจากหนังสือแบบบ้าน

หมายเหตุ

- A= แปเหล็ก C100x50x20x3.2 มม. @1.00 ม.
D= แปเหล็ก C125x50x20x3.2 มม. @1.00 ม.
E= ออสเหล็ก C150x50x20x3.2 มม.
F= ยกไก่เหล็ก C125x50x20x3.2 มม.

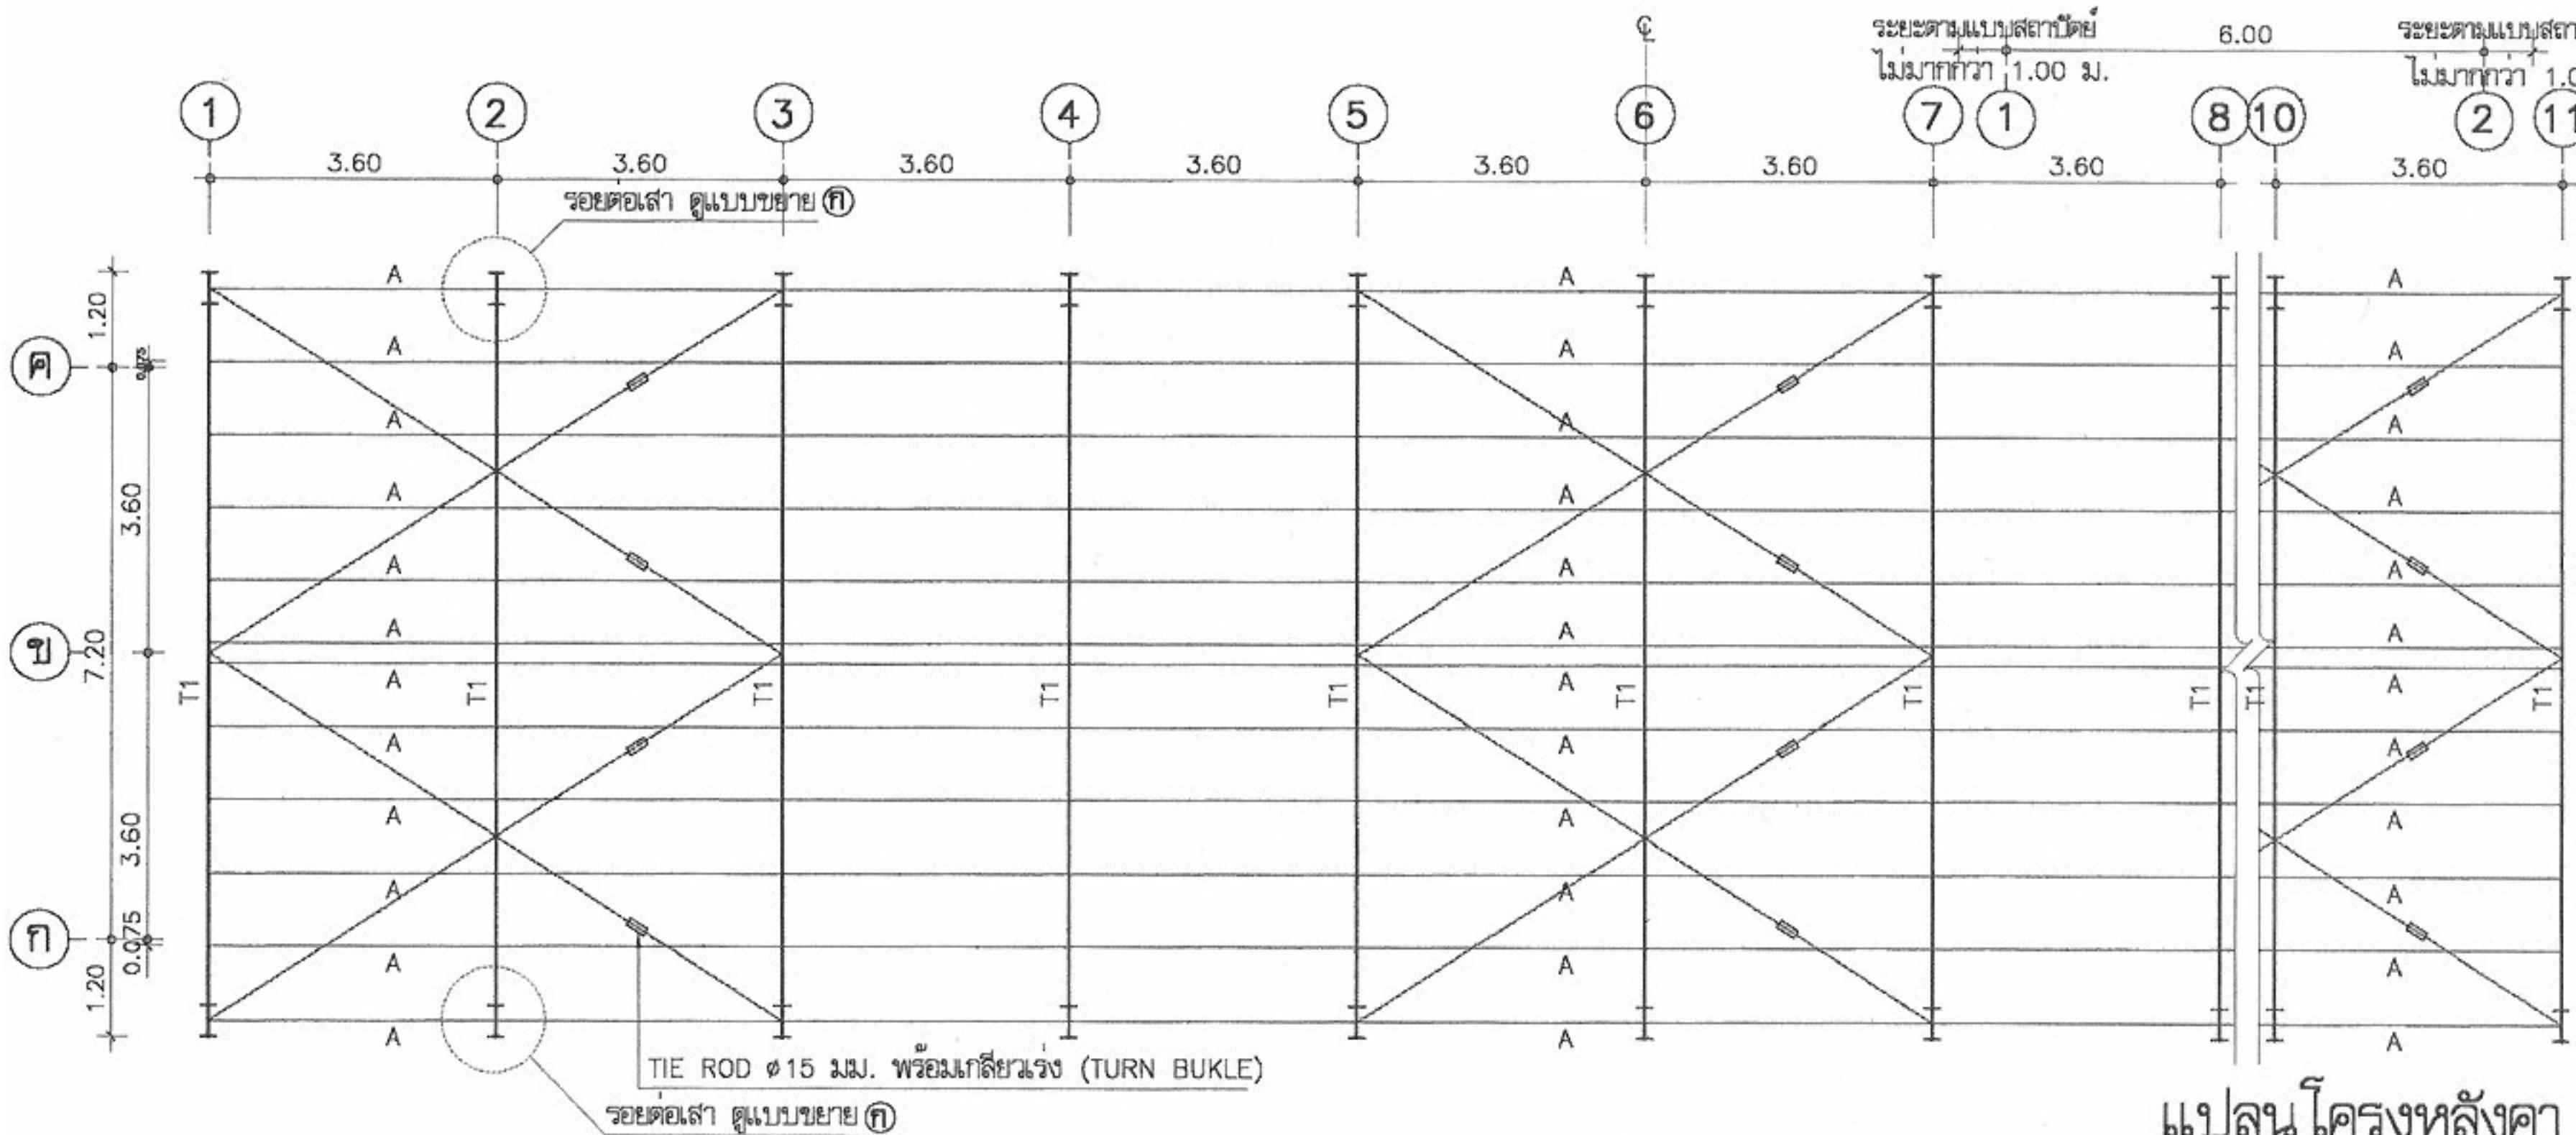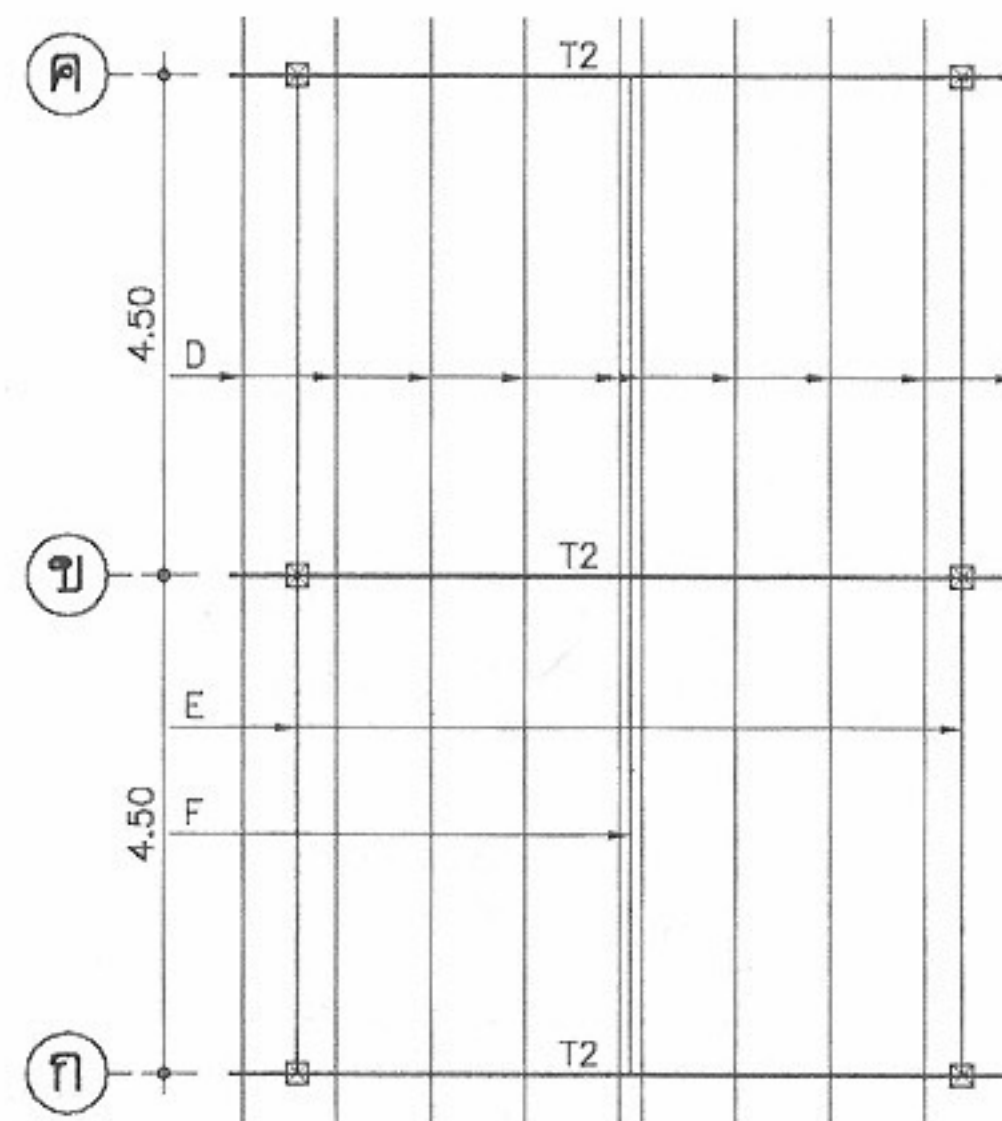

แปลนโครงหลังคา
มาตราส่วน 1:100



โครงการแบบอาคารเพื่อประชาชน
ไทยช่วยไทย

แบบ

บ้านผู้ประสบภัย 3 ห้องสุขารวม

สำนักสถาปัตย์กรรม

ผู้ควบคุมการก่อสร้าง

สถาปัตย์กรรม

สถาปนิก
สถาปนิก
สถาปนิก
สถาปนิก

สำนักวิศวกรรมโครงสร้างและงานระบบ

ผู้ควบคุมการก่อสร้าง

วิศวกรรม

วิศวกร

โครงสร้าง

วิศวกร

วิศวกรรมไฟฟ้า

วิศวกร

และเครื่องกล

วิศวกร

วิศวกรรม

วิศวกร

สุขาภิบาล

วิศวกร

อนุมัติ

(นายสว่าง ศรีสุกัน)

อธิบดีกรมโยธาธิการและผังเมือง

แสดงแบบ

แปลนโครงหลังคา

มาตราส่วน 1:100

วัน/เดือน/ปี 21 พ.ย. 2546

เลขที่แบบ ม.บ.462099


แผ่นที่

S-03


จำนวนแผ่น

8


หมายเหตุ แบบที่แสดงอยู่นี้ได้รับการยืมส่วน เพื่อใช้แสดงผลทางหน้าจอเท่านั้น สำหรับแบบที่ใช้ขออนุญาตก่อสร้าง ให้ถ่ายสำเนาจากหนังสือแบบบ้าน

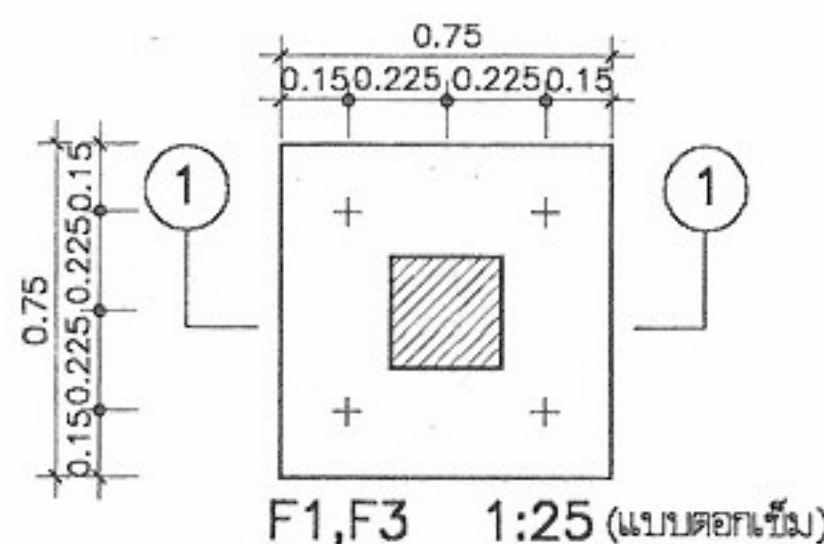


F1, F3 1:25 (แบบตอกเข็ม)

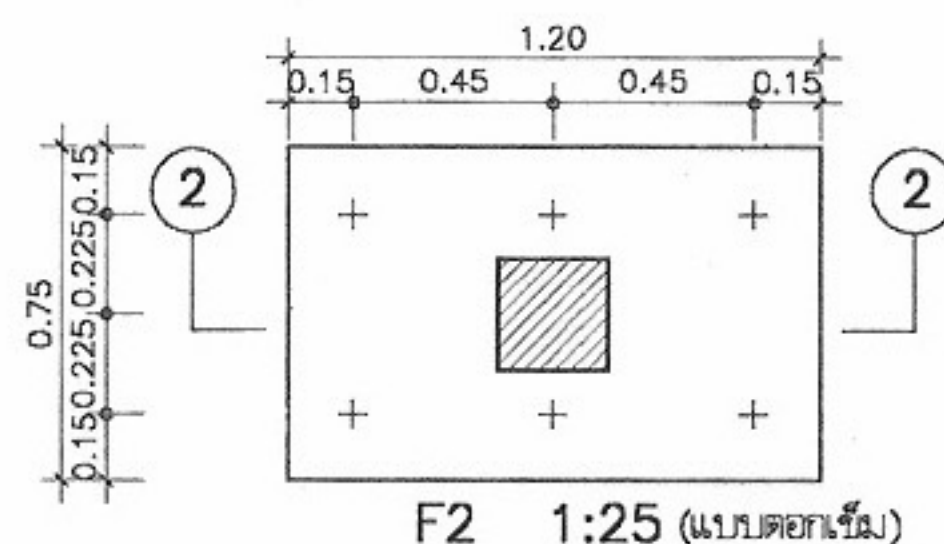


F2 1:25 (แบบตอกเข็ม)

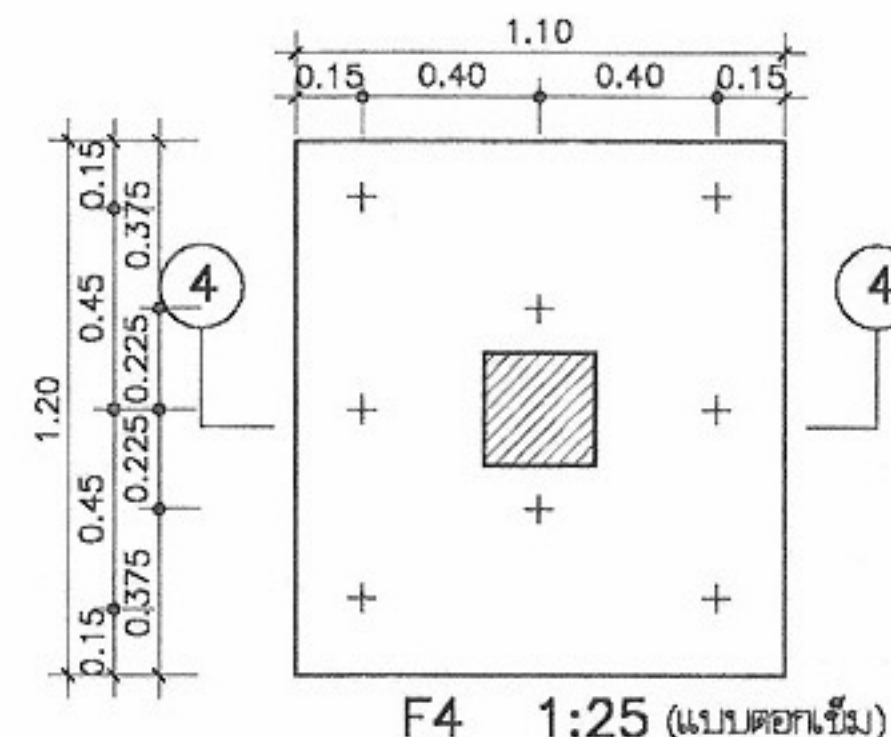


F4 1:25 (แบบตอกเข็ม)

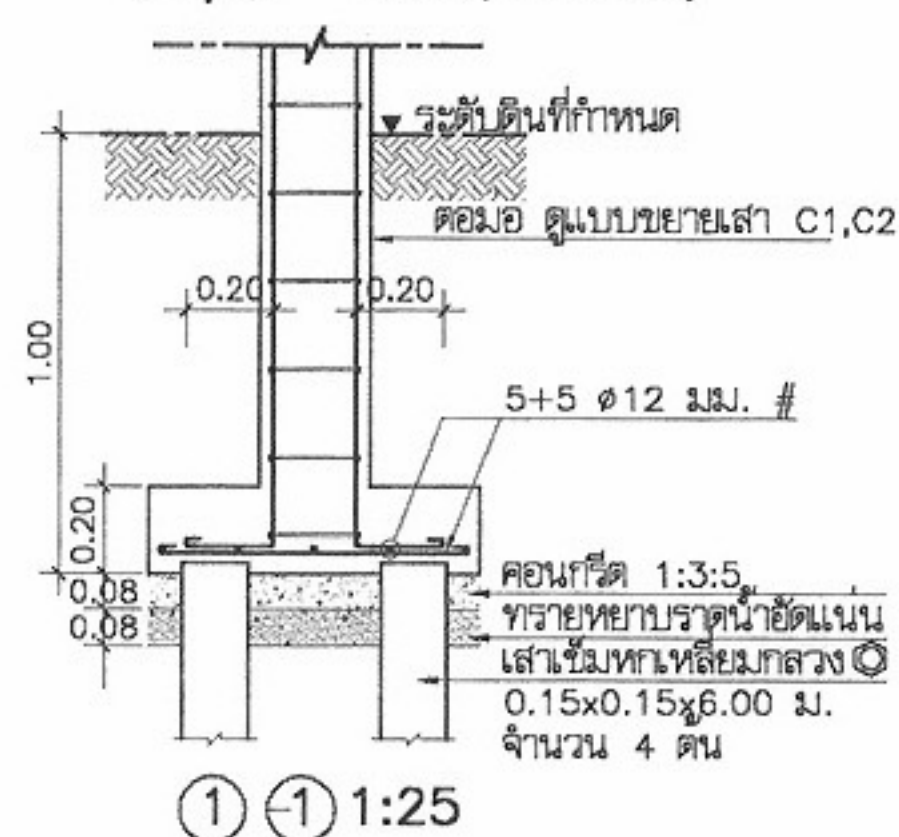


①-① 1:25

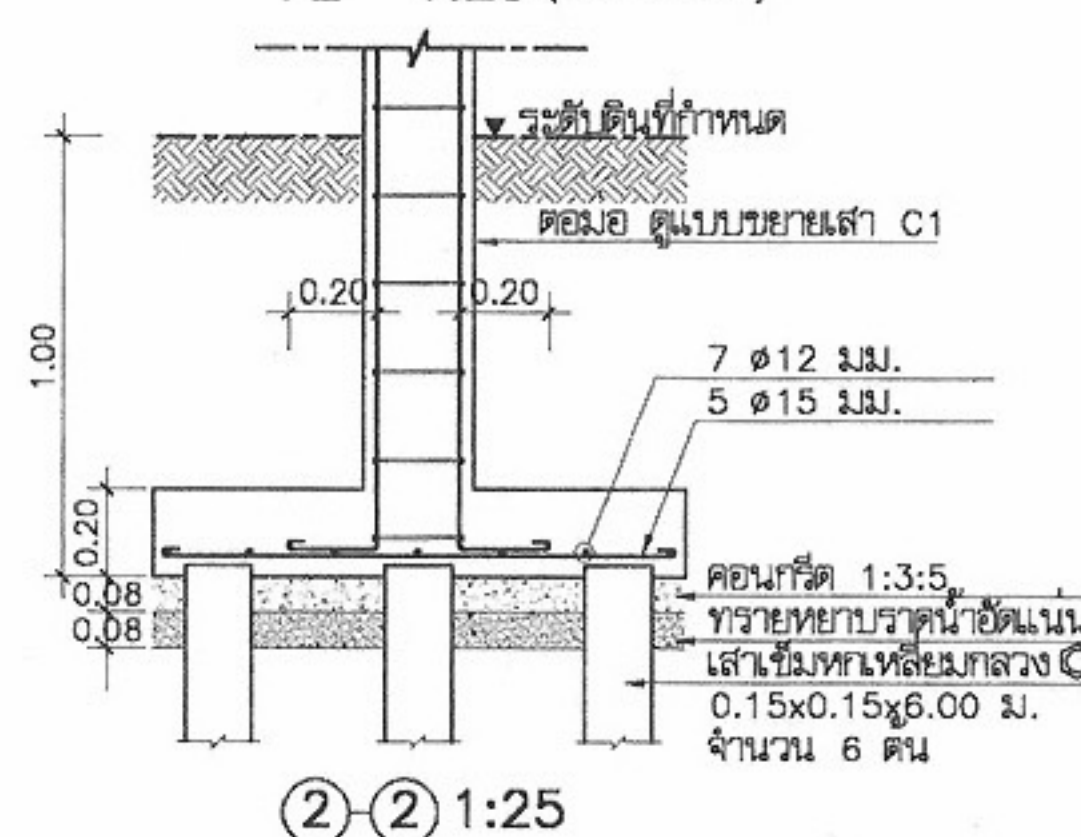


②-② 1:25

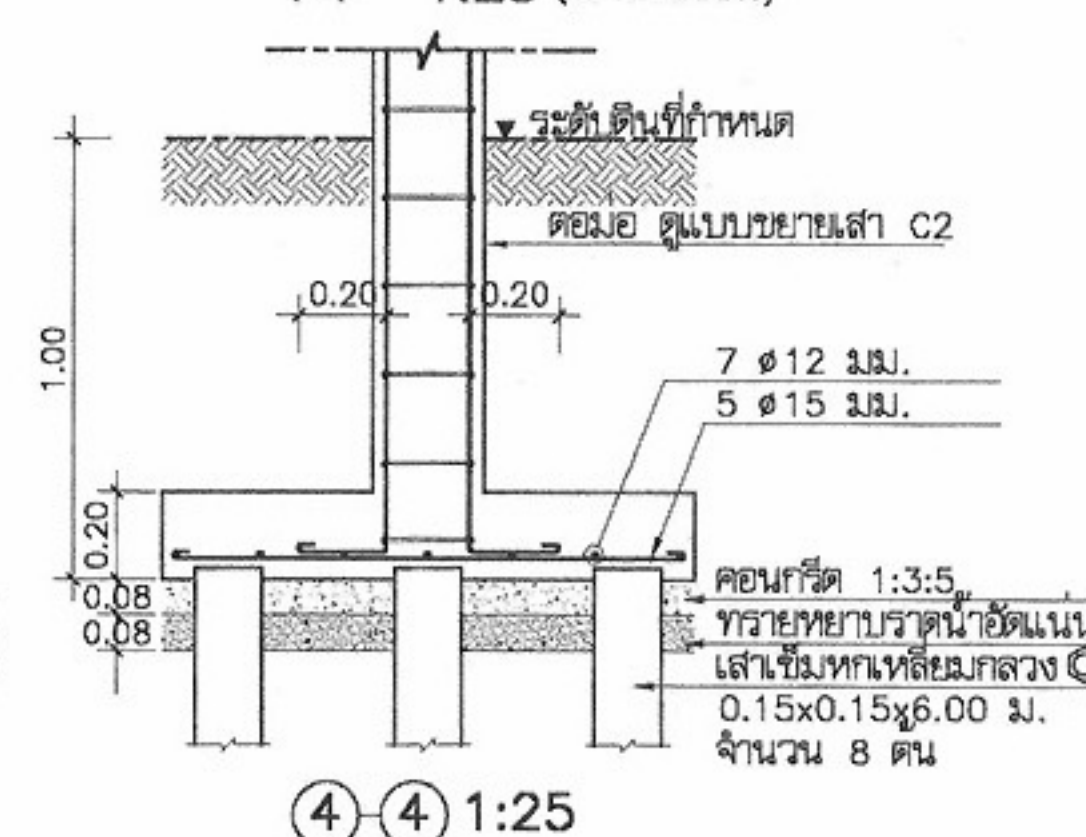

④-④ 1:25

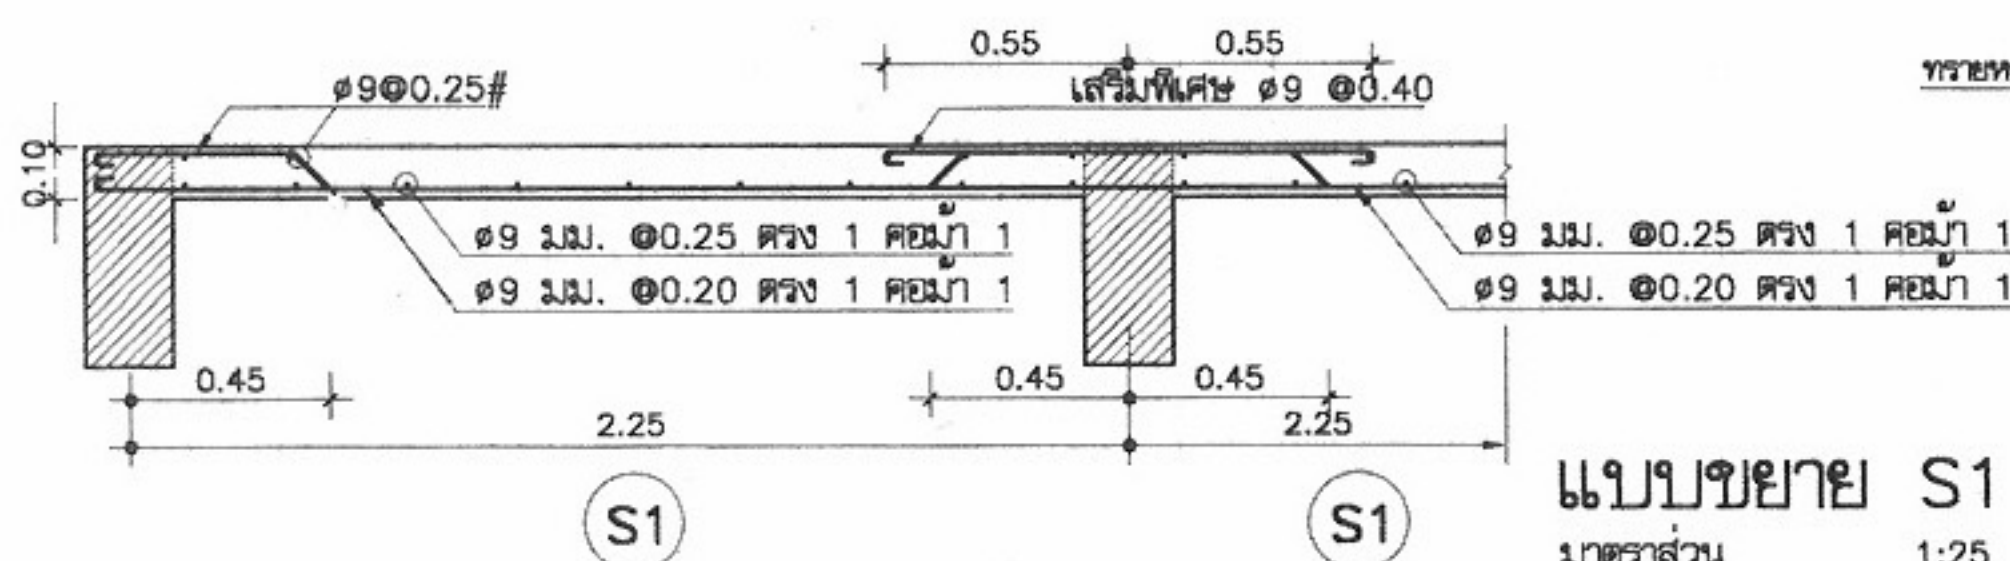

แบบขยาย S1
มาตราส่วน 1:25

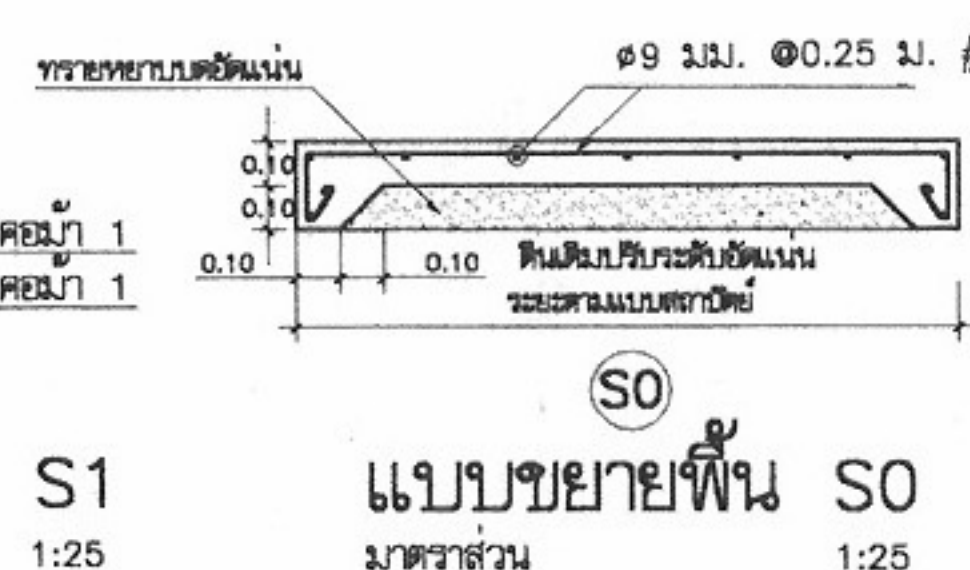

แบบขยายพื้น S0
มาตราส่วน 1:25



โครงการแบบอาคารเพื่อประชาชน
ไทยช่วยไทย

แบบ
บ้านผู้ประสบภัย 3 ห้องสุขารวม

สำนักสถาปัตยกรรม
๗๗-

สถาปนิก
สถาปนิก
สถาปนิก
สถาปนิก

สำนักวิศวกรรมโครงสร้างและงานระบบ
๗๗

วิศวกรรม
โครงสร้าง

วิศวกรรมไฟฟ้า
และเครื่องกล

วิศวกรรม
สุขาภิบาล

อนุมัติ
(นายสว่าง ศรีสุกัน)
อธิบดีกรมโยธาธิการและผังเมือง

แสดงแบบ
ขยายฐานราก
ขยายพื้น


มาตราส่วน 1:25

วัน/เดือน/ปี 21 พ.ย. 2546


เลขที่แบบ ม.บ.462099

แผ่นที่ S-04 จำนวนแผ่น 8


หมายเหตุ แบบที่แสดงอยู่นี้ได้รับการยืมส่วน เพื่อใช้แสดงผลทางหน้าจอเท่านั้น สำหรับแบบที่ใช้ขออนุญาตก่อสร้าง ให้ถ่ายสำเนาจากหนังสือแบบบ้าน

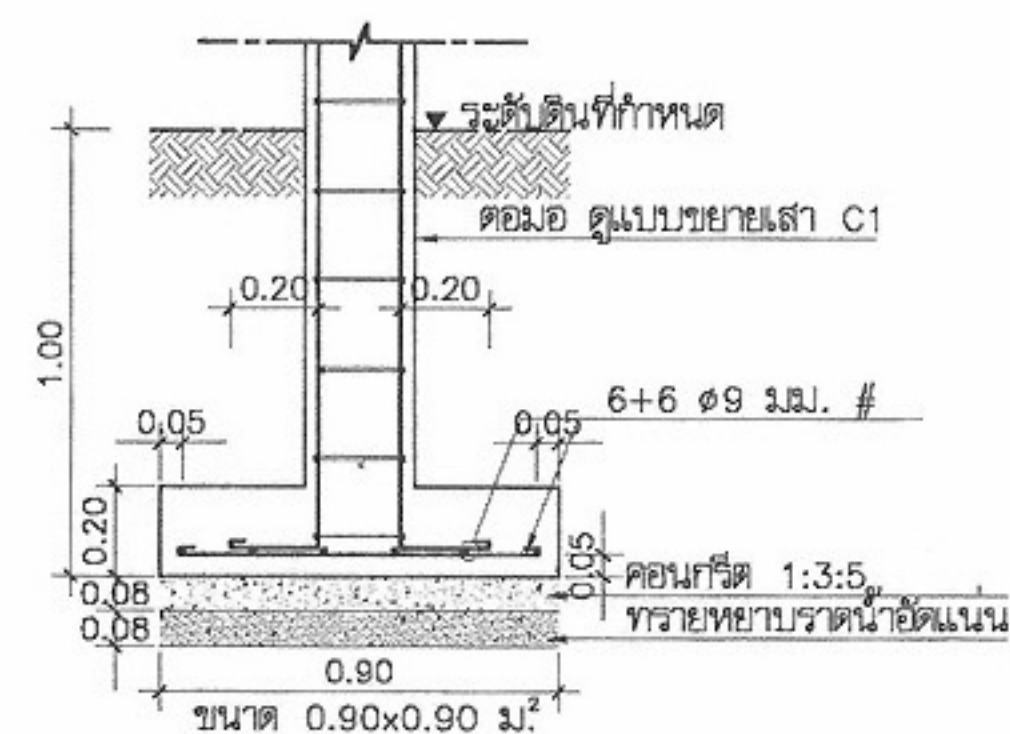


F1 1:25 (แบบฐานแผ่)

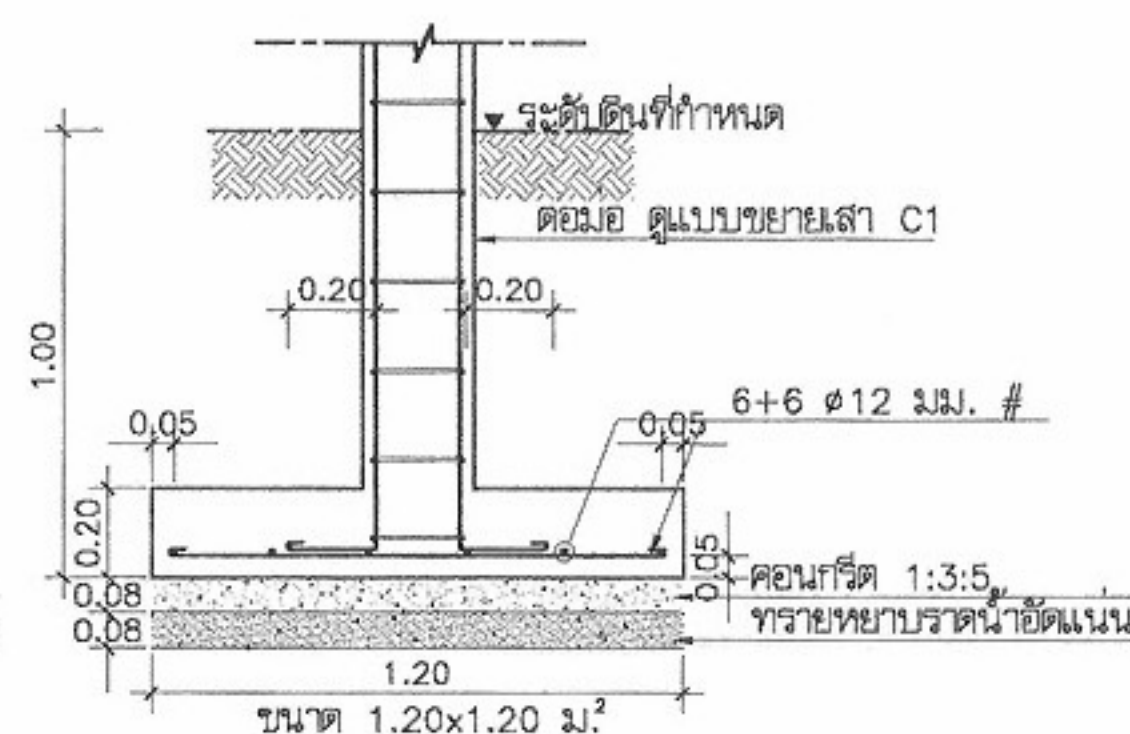


F2 1:25 (แบบฐานแผ่)

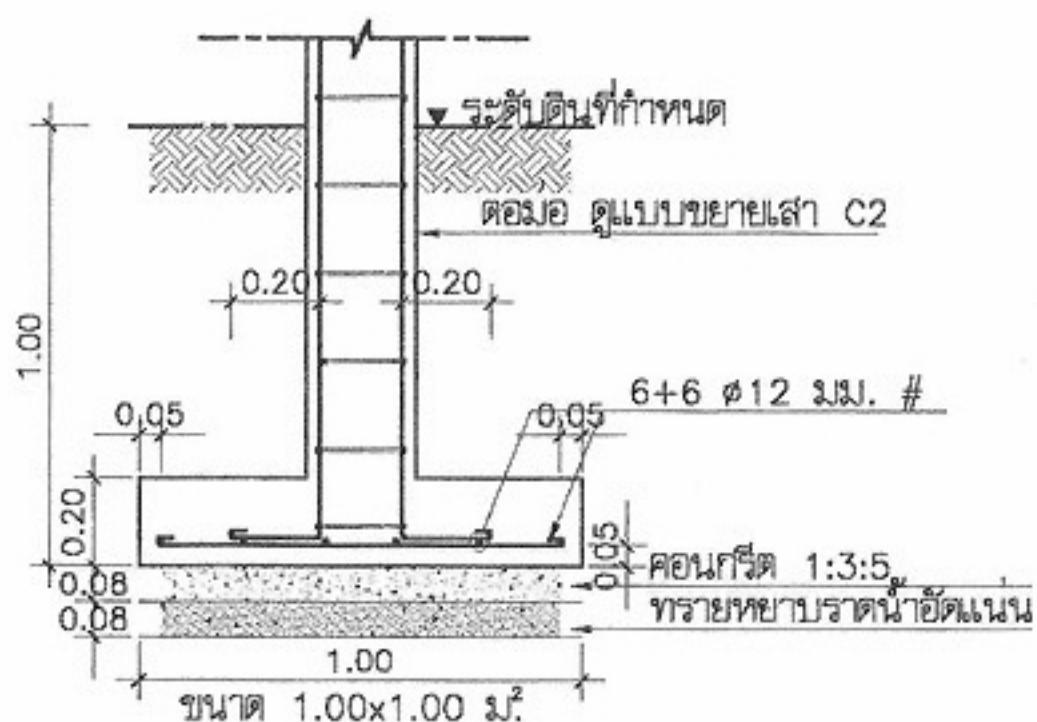


F3 1:25 (แบบฐานแผ่)

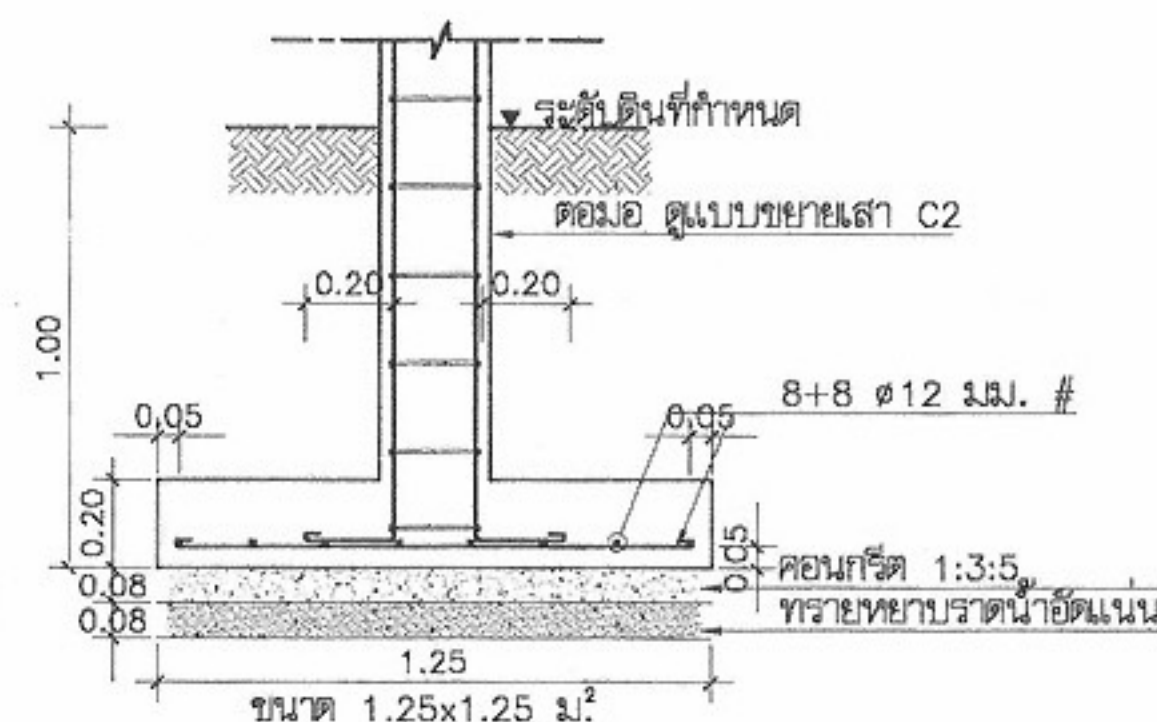


F4 1:25 (แบบฐานแผ่)

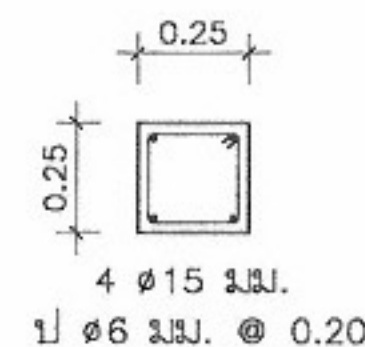


C-1
(ฐานราก-หลังคา)

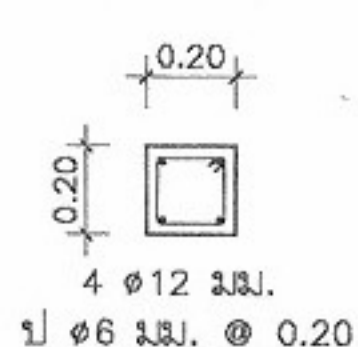


C-2
(ฐานราก-หลังคา)

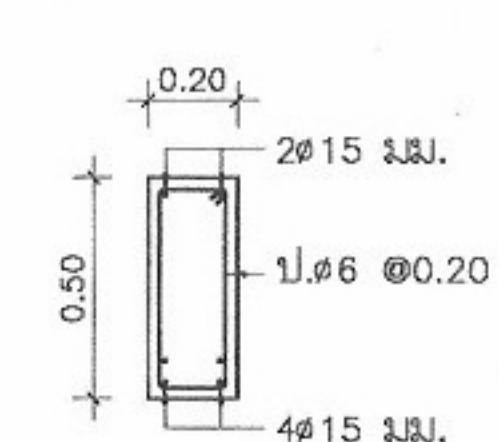

B4 1:25

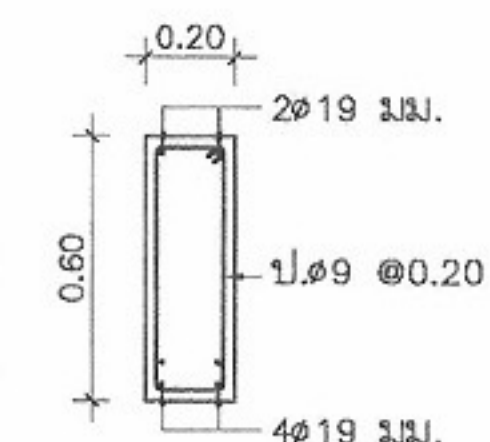


B6 1:25

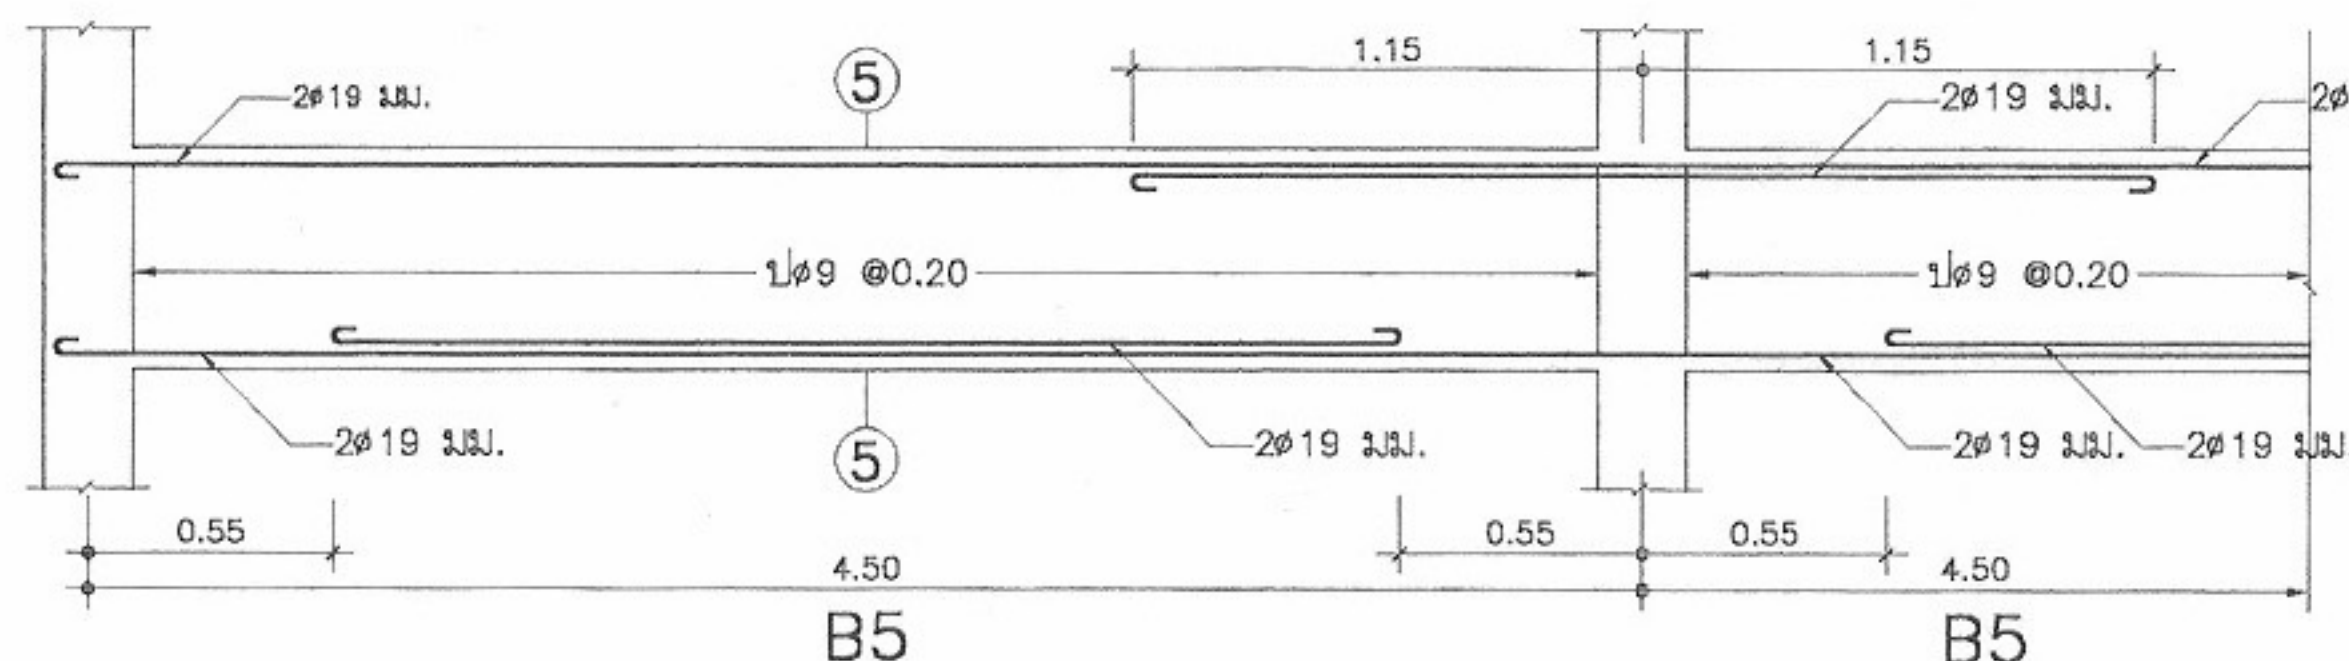

B5

B5

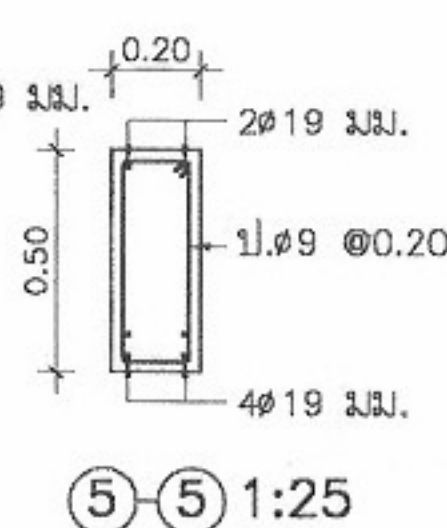

5-5 1:25



โครงการแบบอาคารเพื่อประชาชน

ไทยช่วยไทย

แบบ

บ้านผู้ประสบภัย 3 ห้องสุขารวม

สำนักสถาปัตยกรรม

ผู้ควบคุมการก่อสร้าง

สถาปนิก

สถาปนิก

สำนักวิศวกรรมโครงสร้างและงานระบบ

ผู้ควบคุมการก่อสร้าง

วิศวกร

วิศวกร

วิศวกรไฟฟ้า

วิศวกร

และเครื่องกล

วิศวกร

วิศวกร

วิศวกร

อนุมัติ

(นายสว่าง ศรีสุคนธ์)

อธิบดีกรมโยธาธิการและผังเมือง

แสดงแบบ

ขยายฐานราก
ขยายคาน

มาตราส่วน 1:25

วัน/เดือน/ปี 21 พ.ย. 2546

เลขที่แบบ ม.บ.462099







แผ่นที่

S-05

จำนวนแผ่น

8

หมายเหตุ แบบที่แสดงอยู่นี้ได้รับการยืมส่วน เพื่อใช้แสดงผลทางหน้าจอเท่านั้น สำหรับแบบที่ใช้ขออนุญาตก่อสร้าง ให้ถ่ายสำเนาจากหนังสือแบบบ้าน

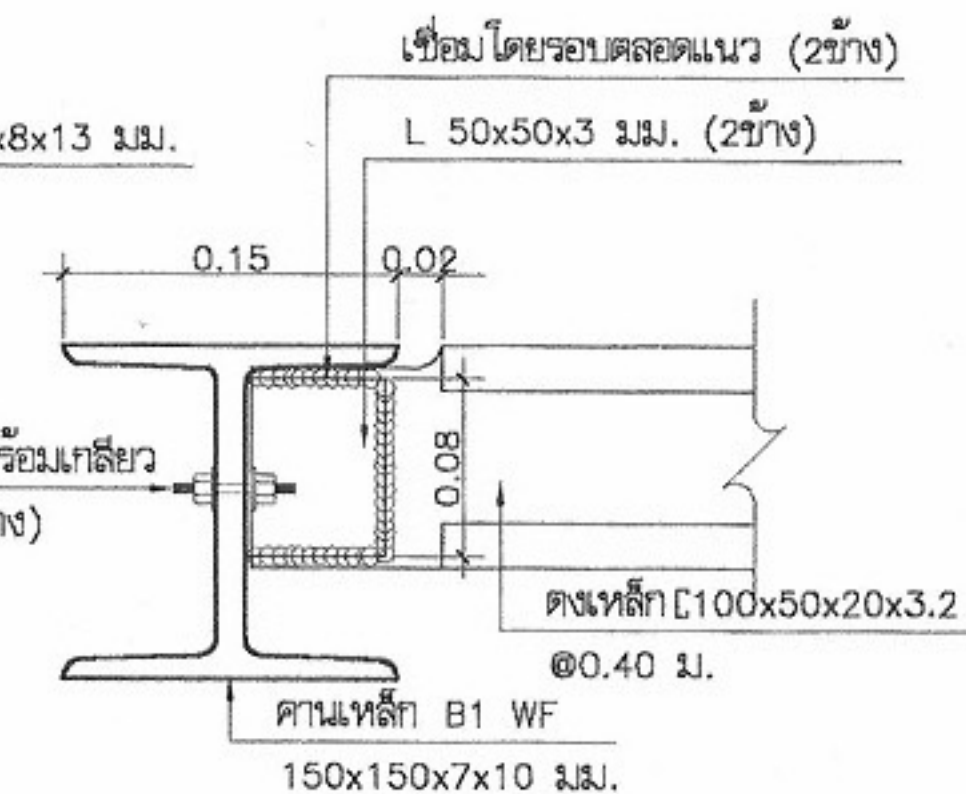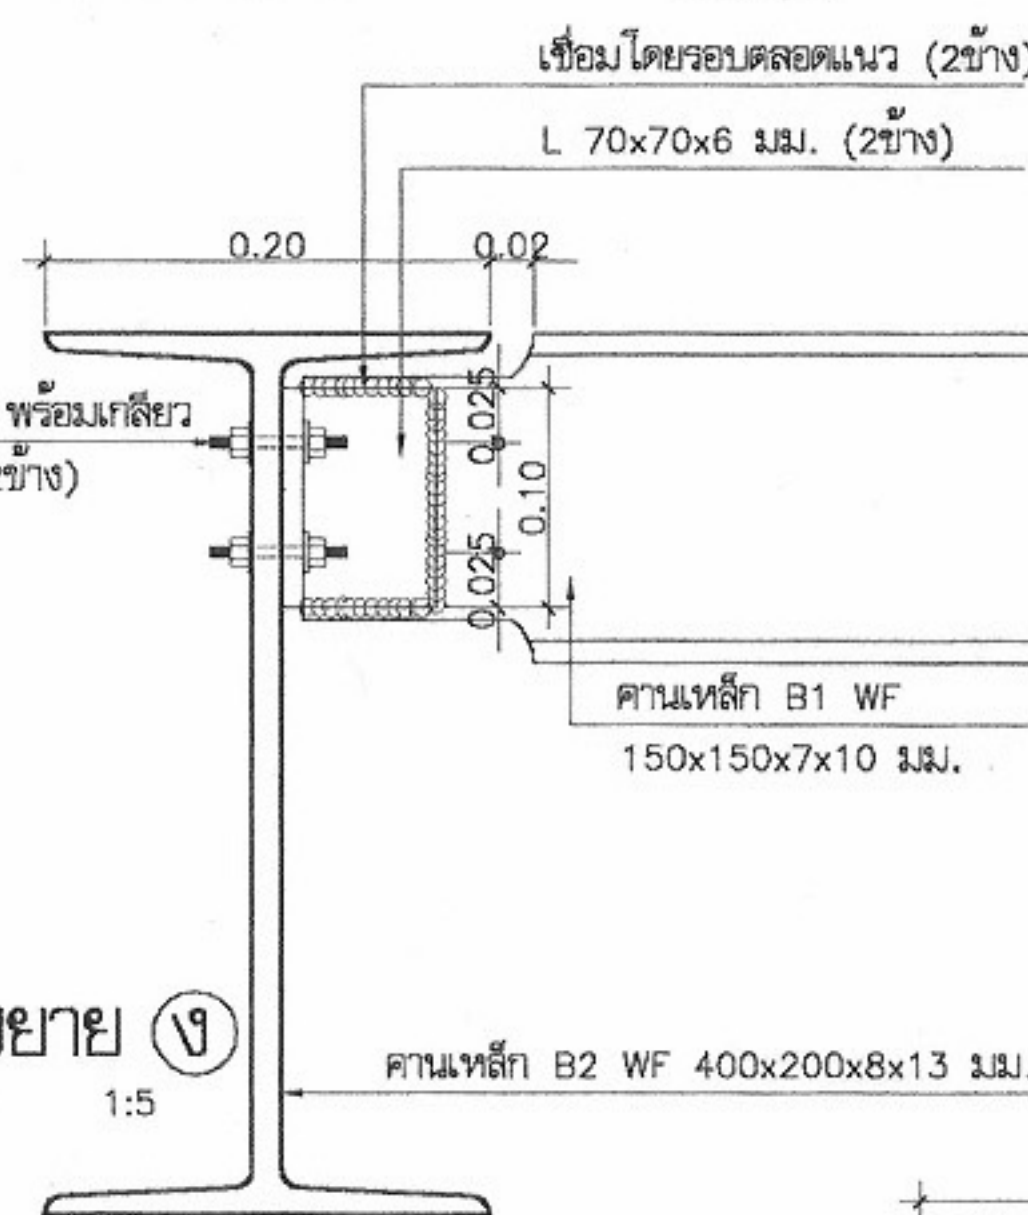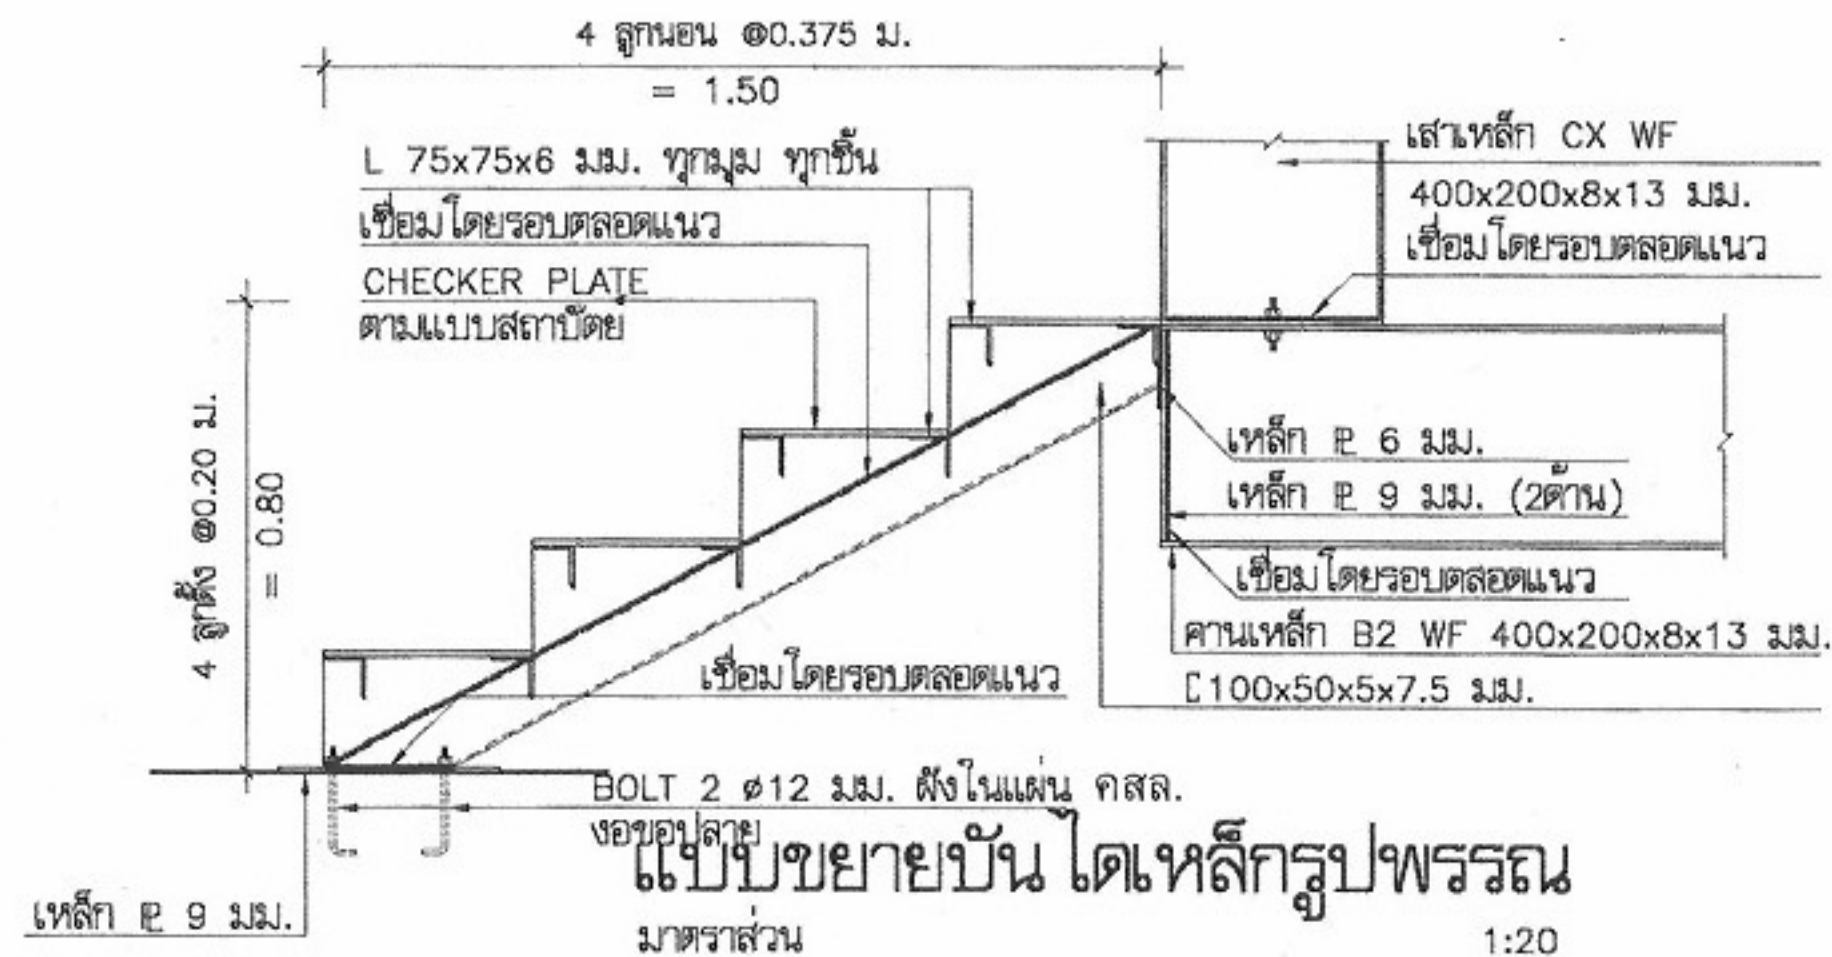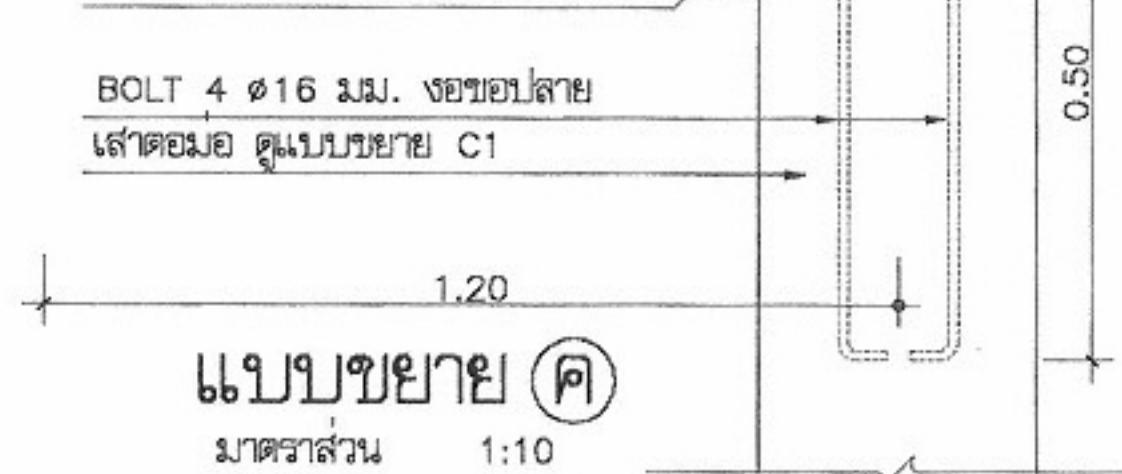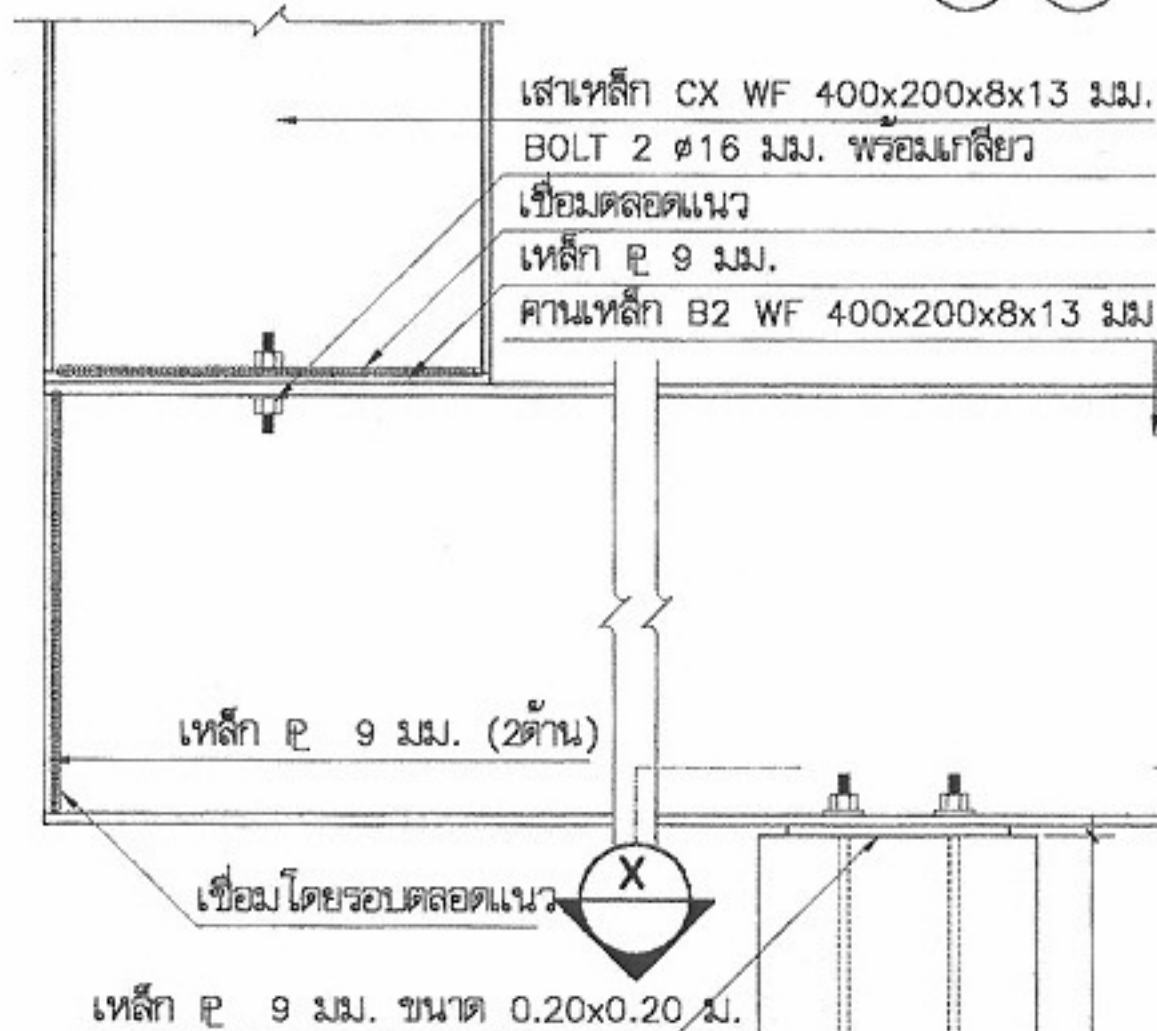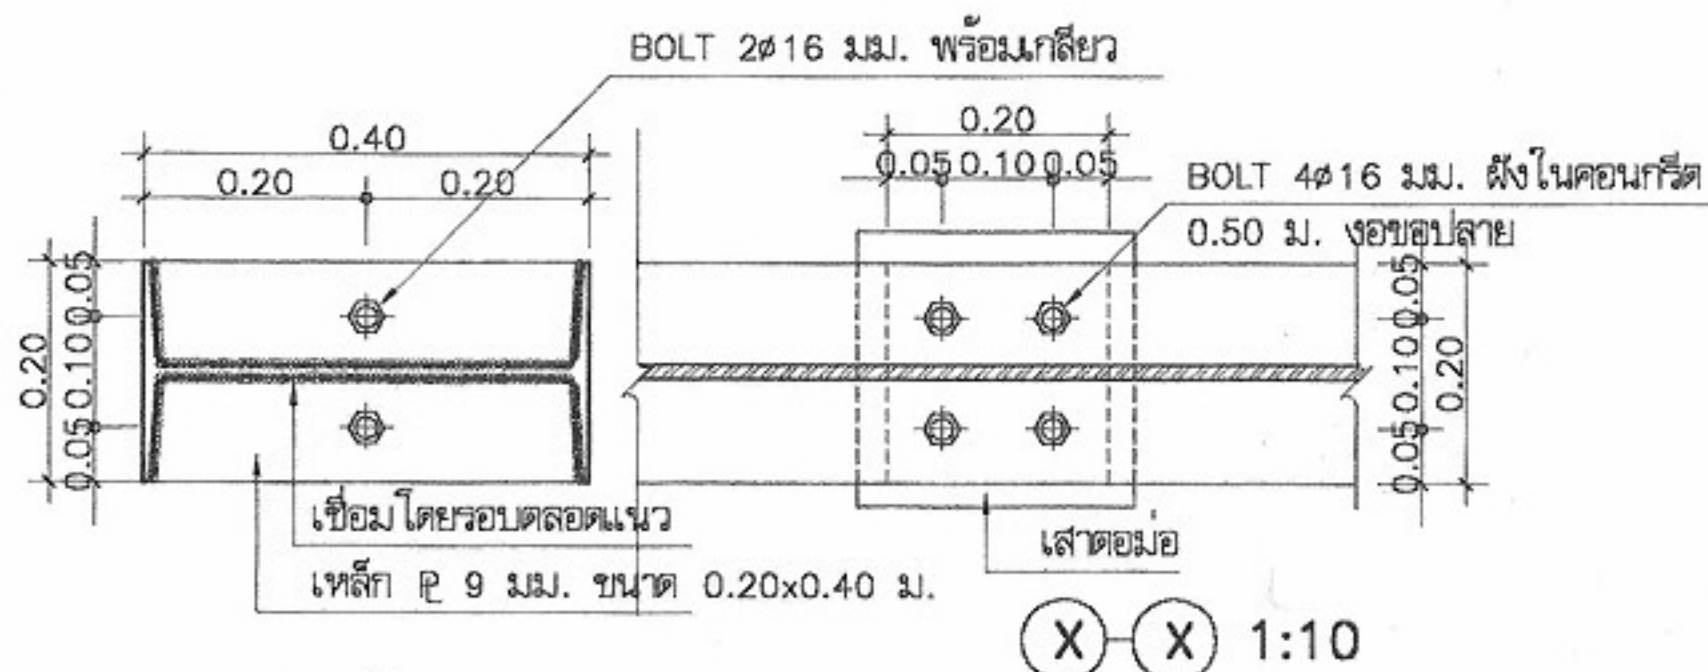

โครงการแบบอาคารเพื่อประชาชน
ไทยช่วยไทย

แบบ
บ้านผู้ประสบภัย 3 ห้องสุขารวม

สำนักสถาปัตย์กรรม
ผู้ควบคุมการก่อสร้าง

สถาปัตย์กรรม
สถาปนิก
สถาปนิก
สถาปนิก
สถาปนิก

สำนักวิศวกรรมโครงสร้างและงานระบบ
ผู้ควบคุมการก่อสร้าง

วิศวกรรม
โครงสร้าง
วิศวกรรมไฟฟ้า
และเครื่องกล
วิศวกรรม
สุขาภิบาล

อนุมัติ
(นายสว่าง ศรีสุกัน)
อธิบดีกรมโยธาธิการและผังเมือง

แสดงแบบ
ขยายโครงสร้าง



มาตรฐาน 1:10

วัน/เดือน/ปี 21 พ.ย. 2546


เลขที่แบบ ม.บ.462099

แผ่นที่ S-06 จำนวนแผ่น 8


หมายเหตุ แบบที่แสดงอยู่นี้ได้รับการยืมส่วน เพื่อใช้แสดงผลทางหน้าจอเท่านั้น สำหรับแบบที่ใช้ขออนุญาตก่อสร้าง ให้ถ่ายสำเนาจากหนังสือแบบบ้าน

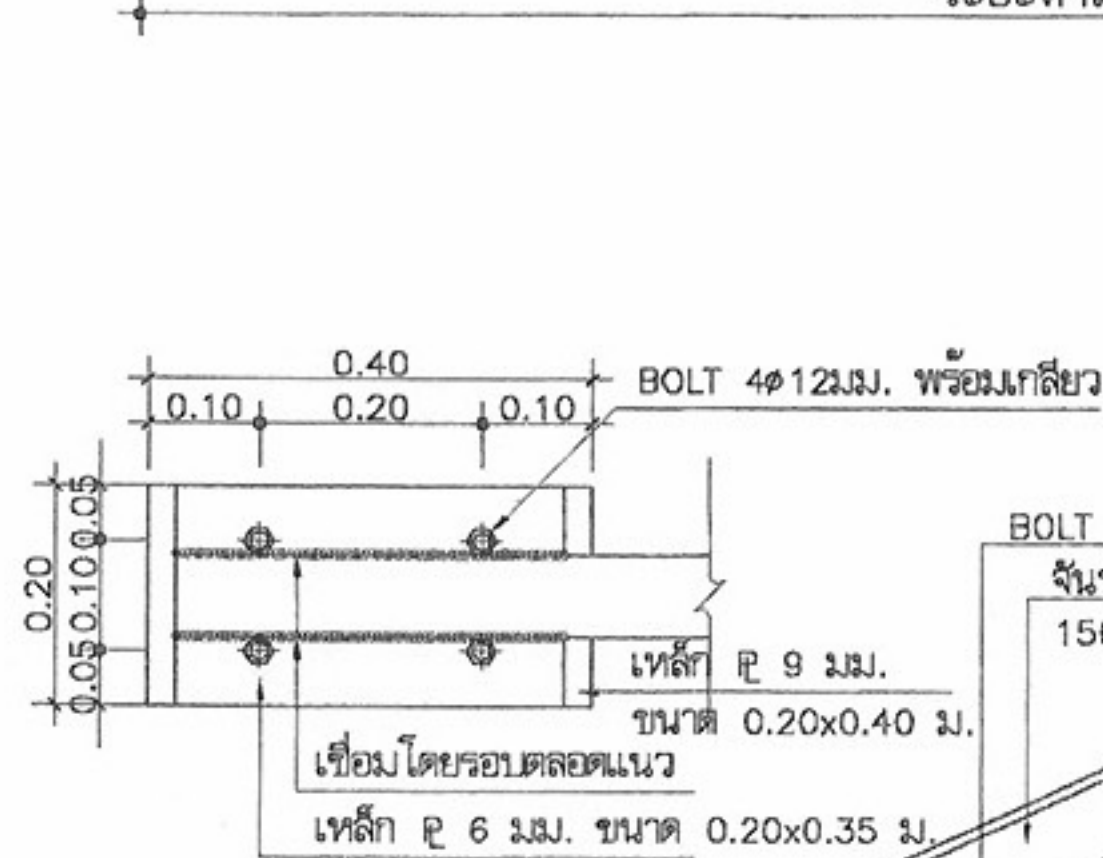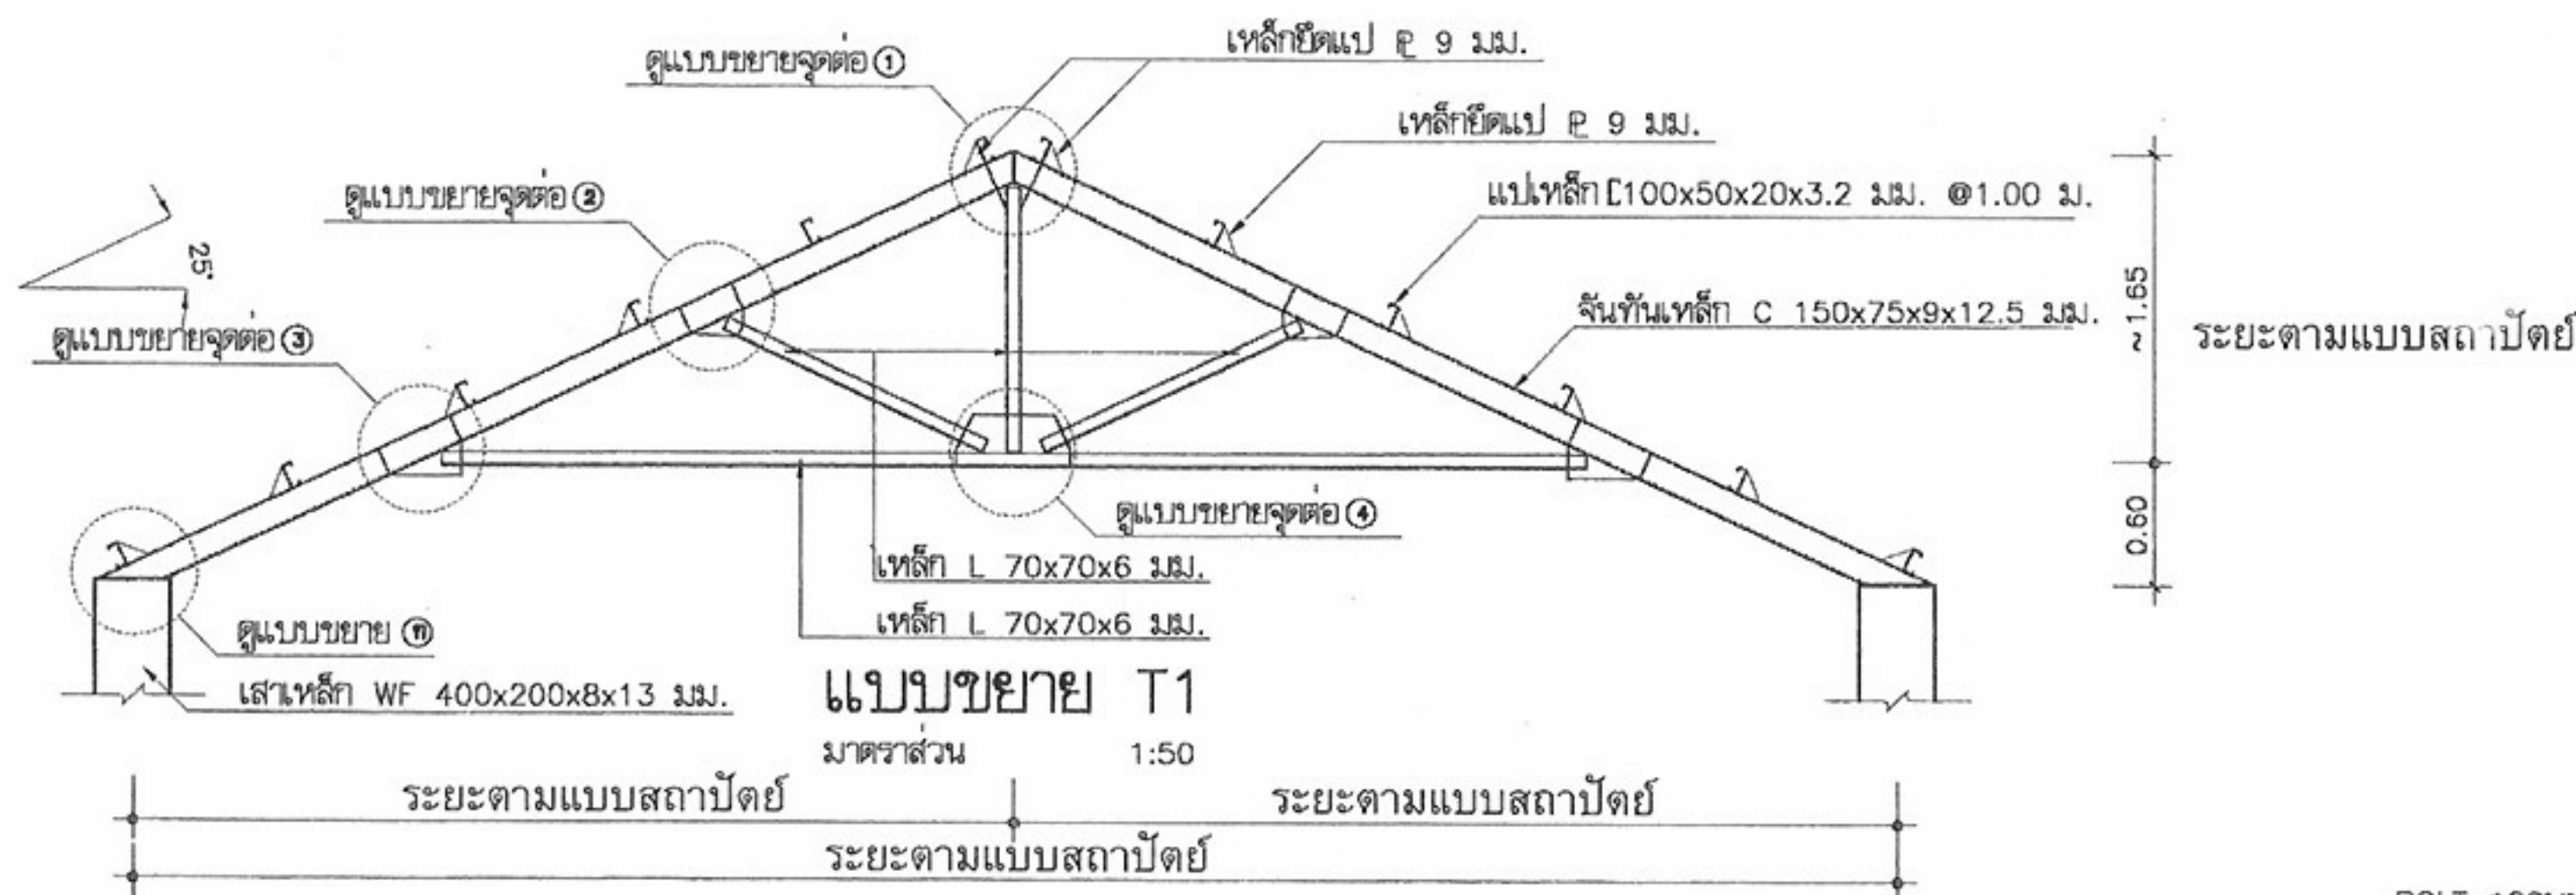


แบบขยายจุดต่อ ②
มาตราส่วน 1:10

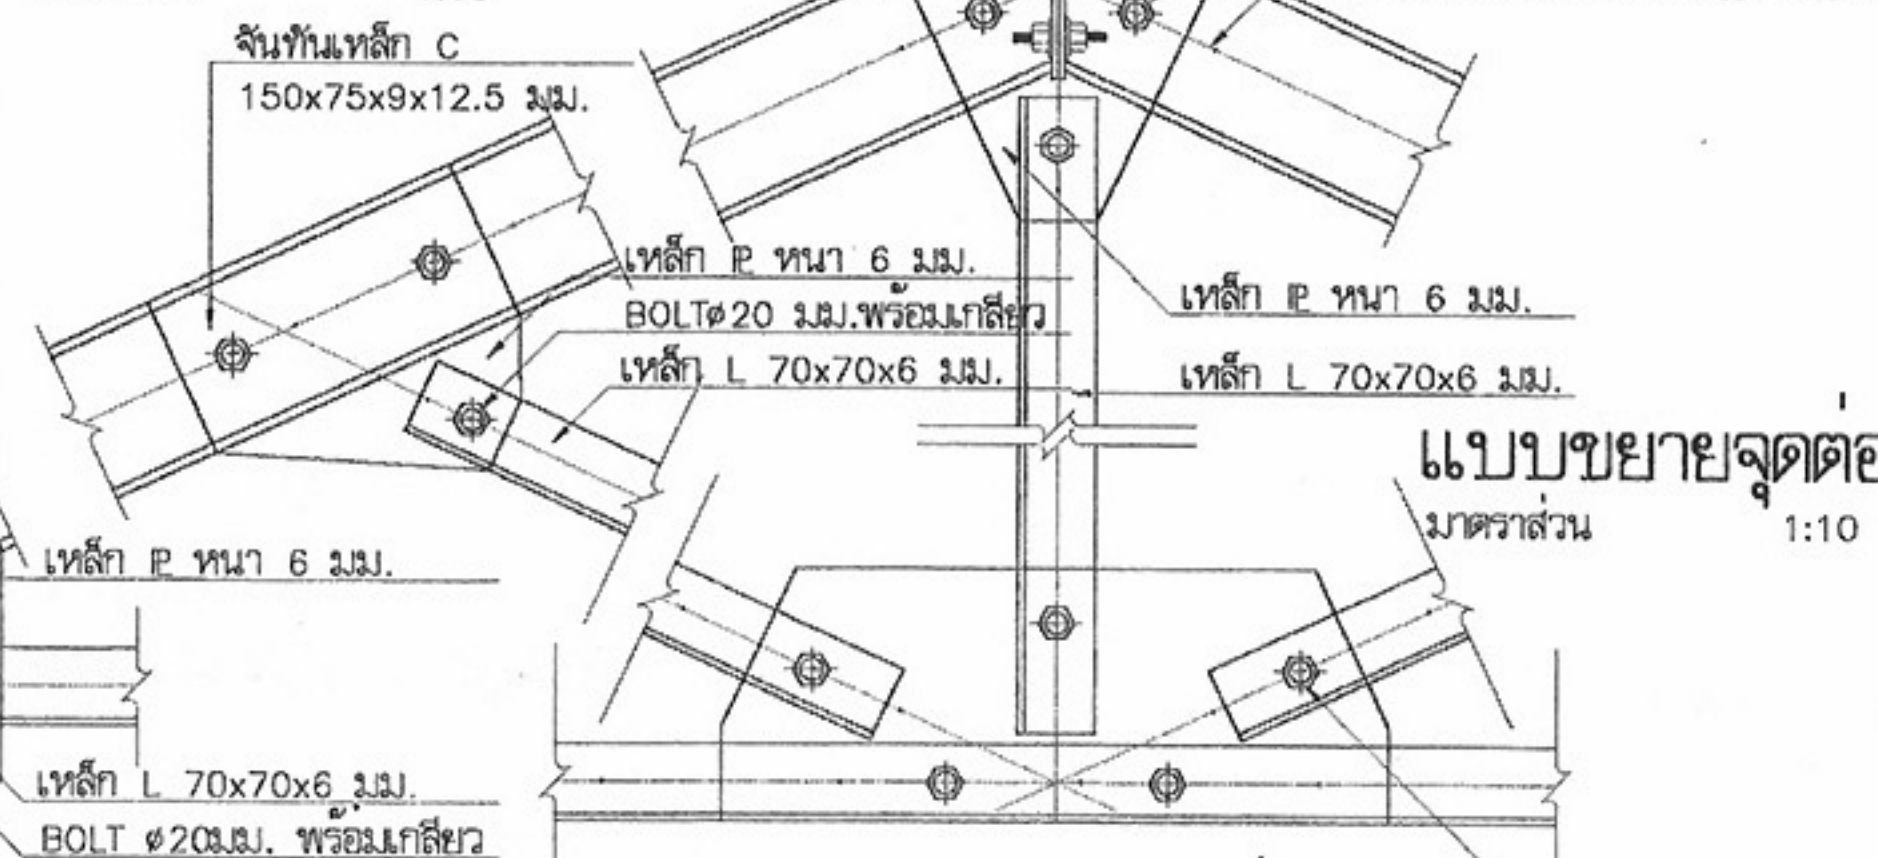

แบบขยายจุดต่อ ③
มาตราส่วน 1:10

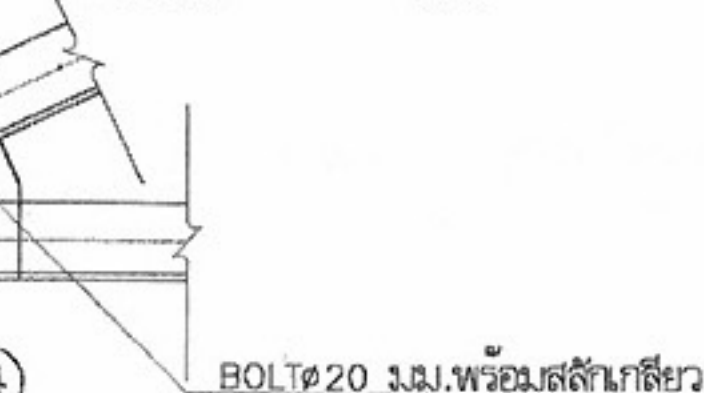

แบบขยายจุดต่อ ④
มาตราส่วน 1:10

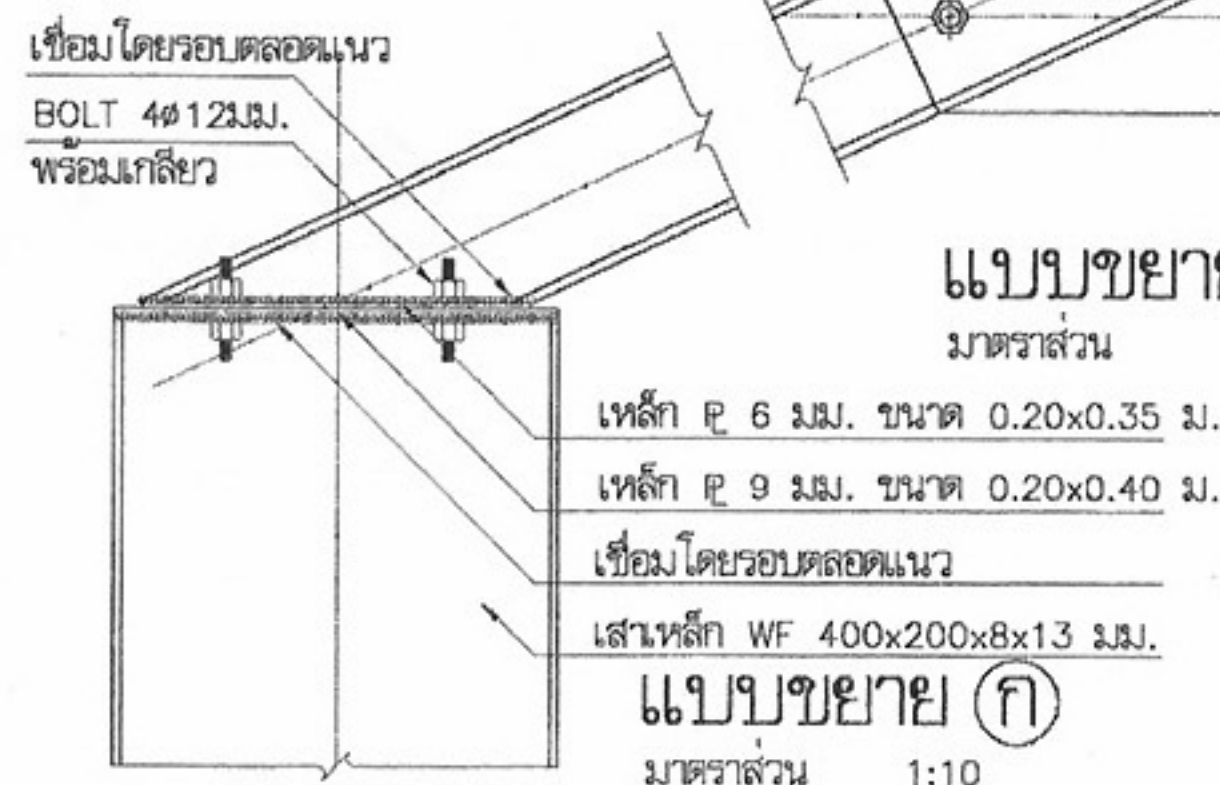

โครงการแบบอาคารเพื่อประชาชน
ไทยช่วยไทย

บ้านผู้ประสบภัย 3 ห้องสุขารวม

สำนักสถาปัตยกรรม
ผู้อำนวยการสำนักงาน

สถาปนิก
ผู้ออกแบบ
ตรวจสอบ
ตรวจสอบ
ตรวจสอบ

สำนักวิศวกรรมโครงสร้างและงานระบบ
ผู้อำนวยการสำนักงาน


วิศวกร
โครงสร้าง
วิศวกรไฟฟ้า
และเครื่องกล
วิศวกร
สุขาภิบาล

อนุมัติ
(นายสว่าง ศรีสุกัน)
อธิบดีกรมโยธาธิการและผังเมือง


แสดงแบบ
ขยายโครงสร้างหลังคา T1

มาตราส่วน 1:50
วัน/เดือน/ปี 21 พ.ย. 2546
เลขที่แบบ ม.บ.462099
แผ่นที่ S-07 จำนวนแผ่น 8




หมายเหตุ แบบที่แสดงอยู่นี้ได้รับการยืมส่วน เพื่อใช้แสดงผลทางหน้าจอเท่านั้น สำหรับแบบที่ใช้ขออนุญาตก่อสร้าง ให้ถ่ายสำเนาจากหนังสือแบบบ้าน

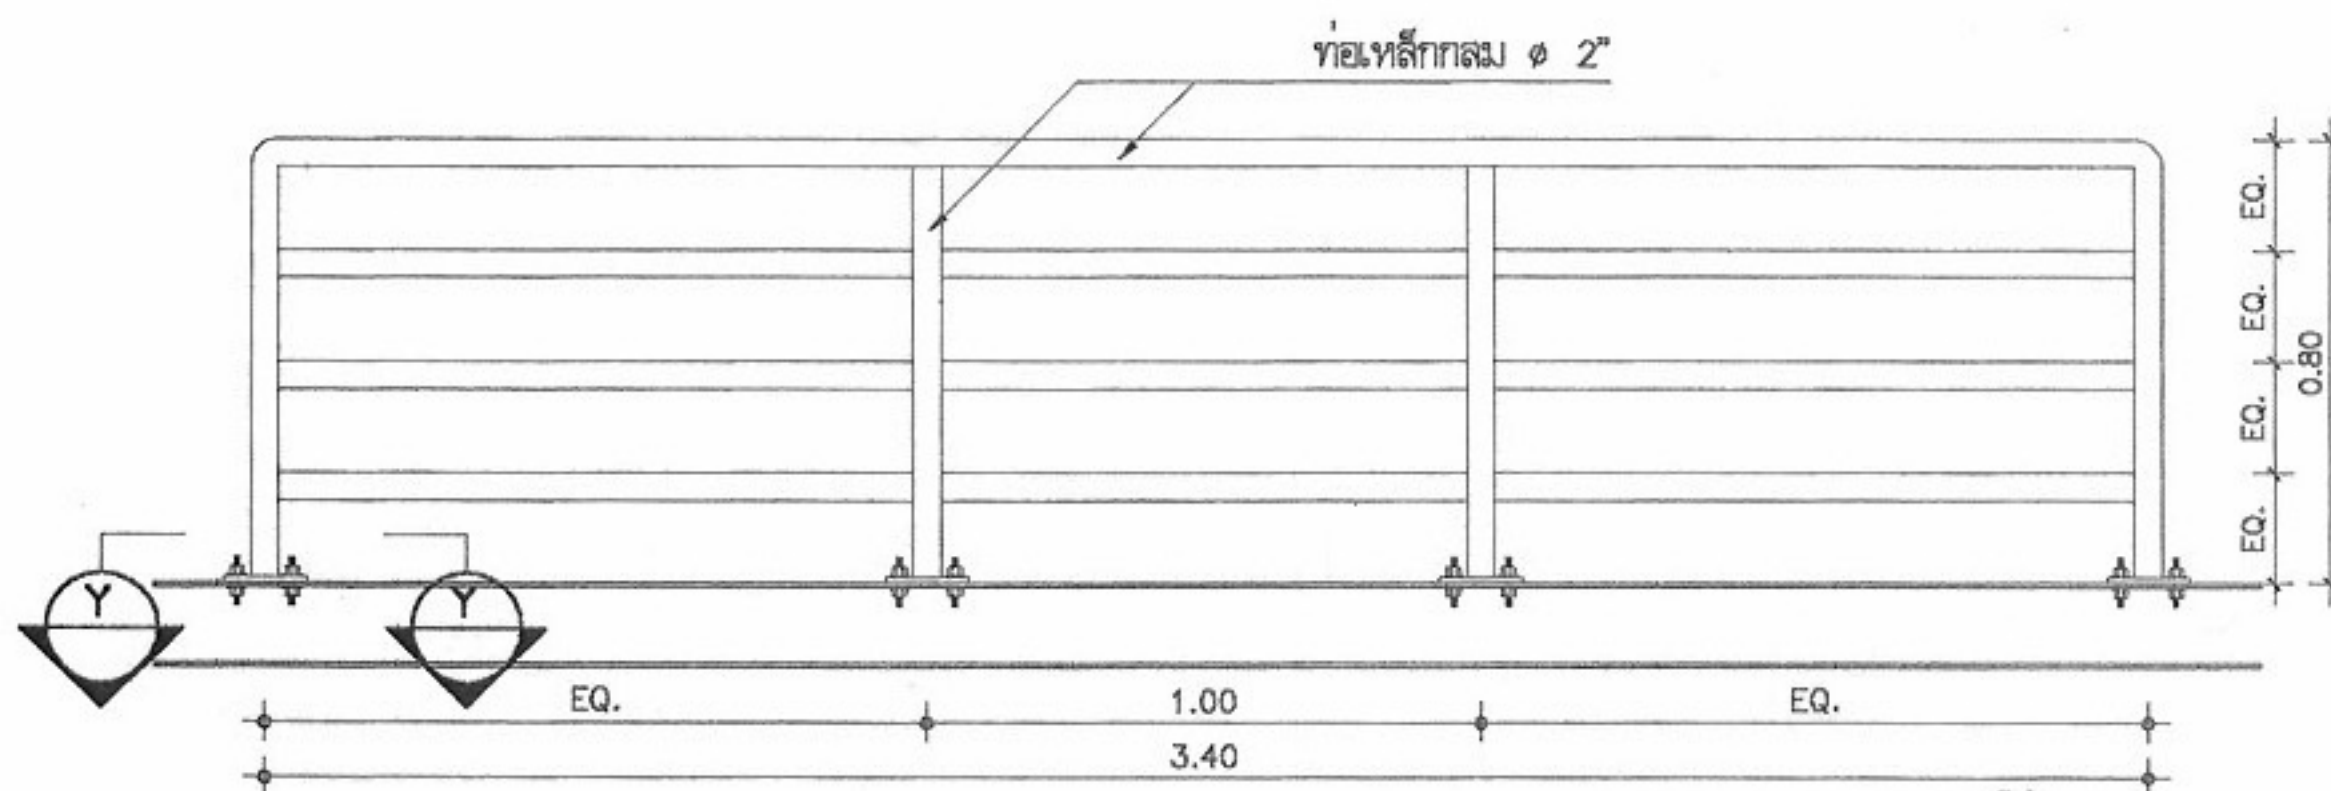


แบบขยายราวกันตก
มาตราส่วน 1:20

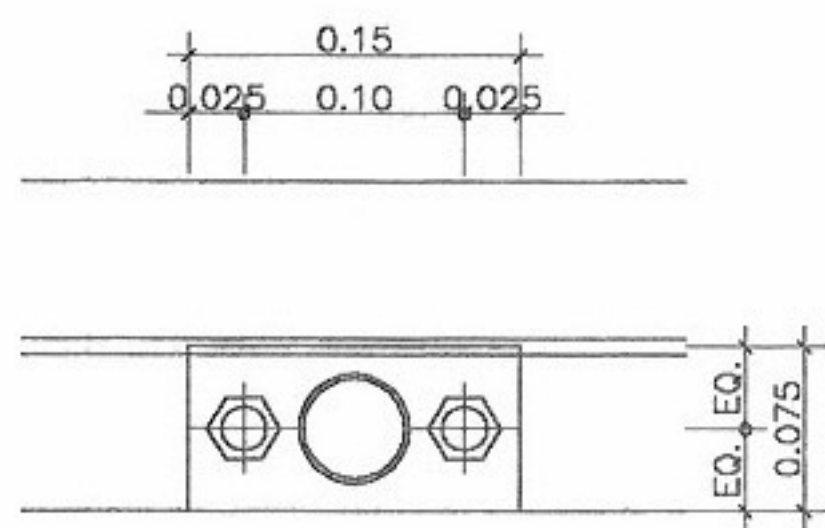

Y-Y 1:5

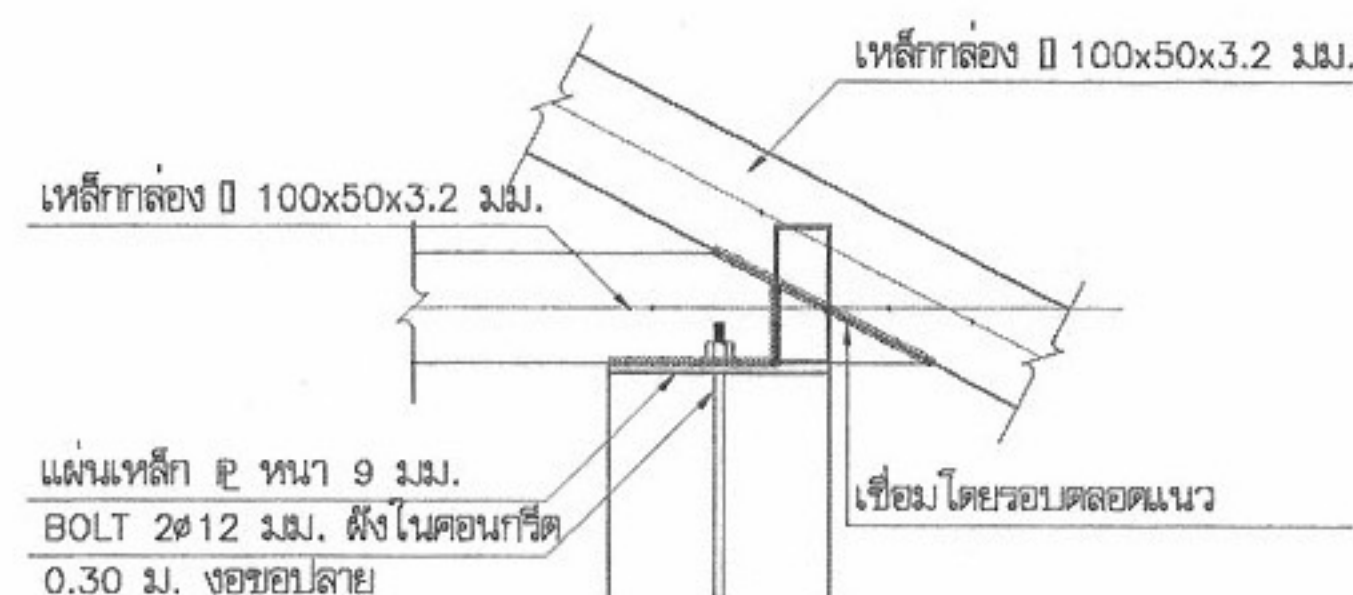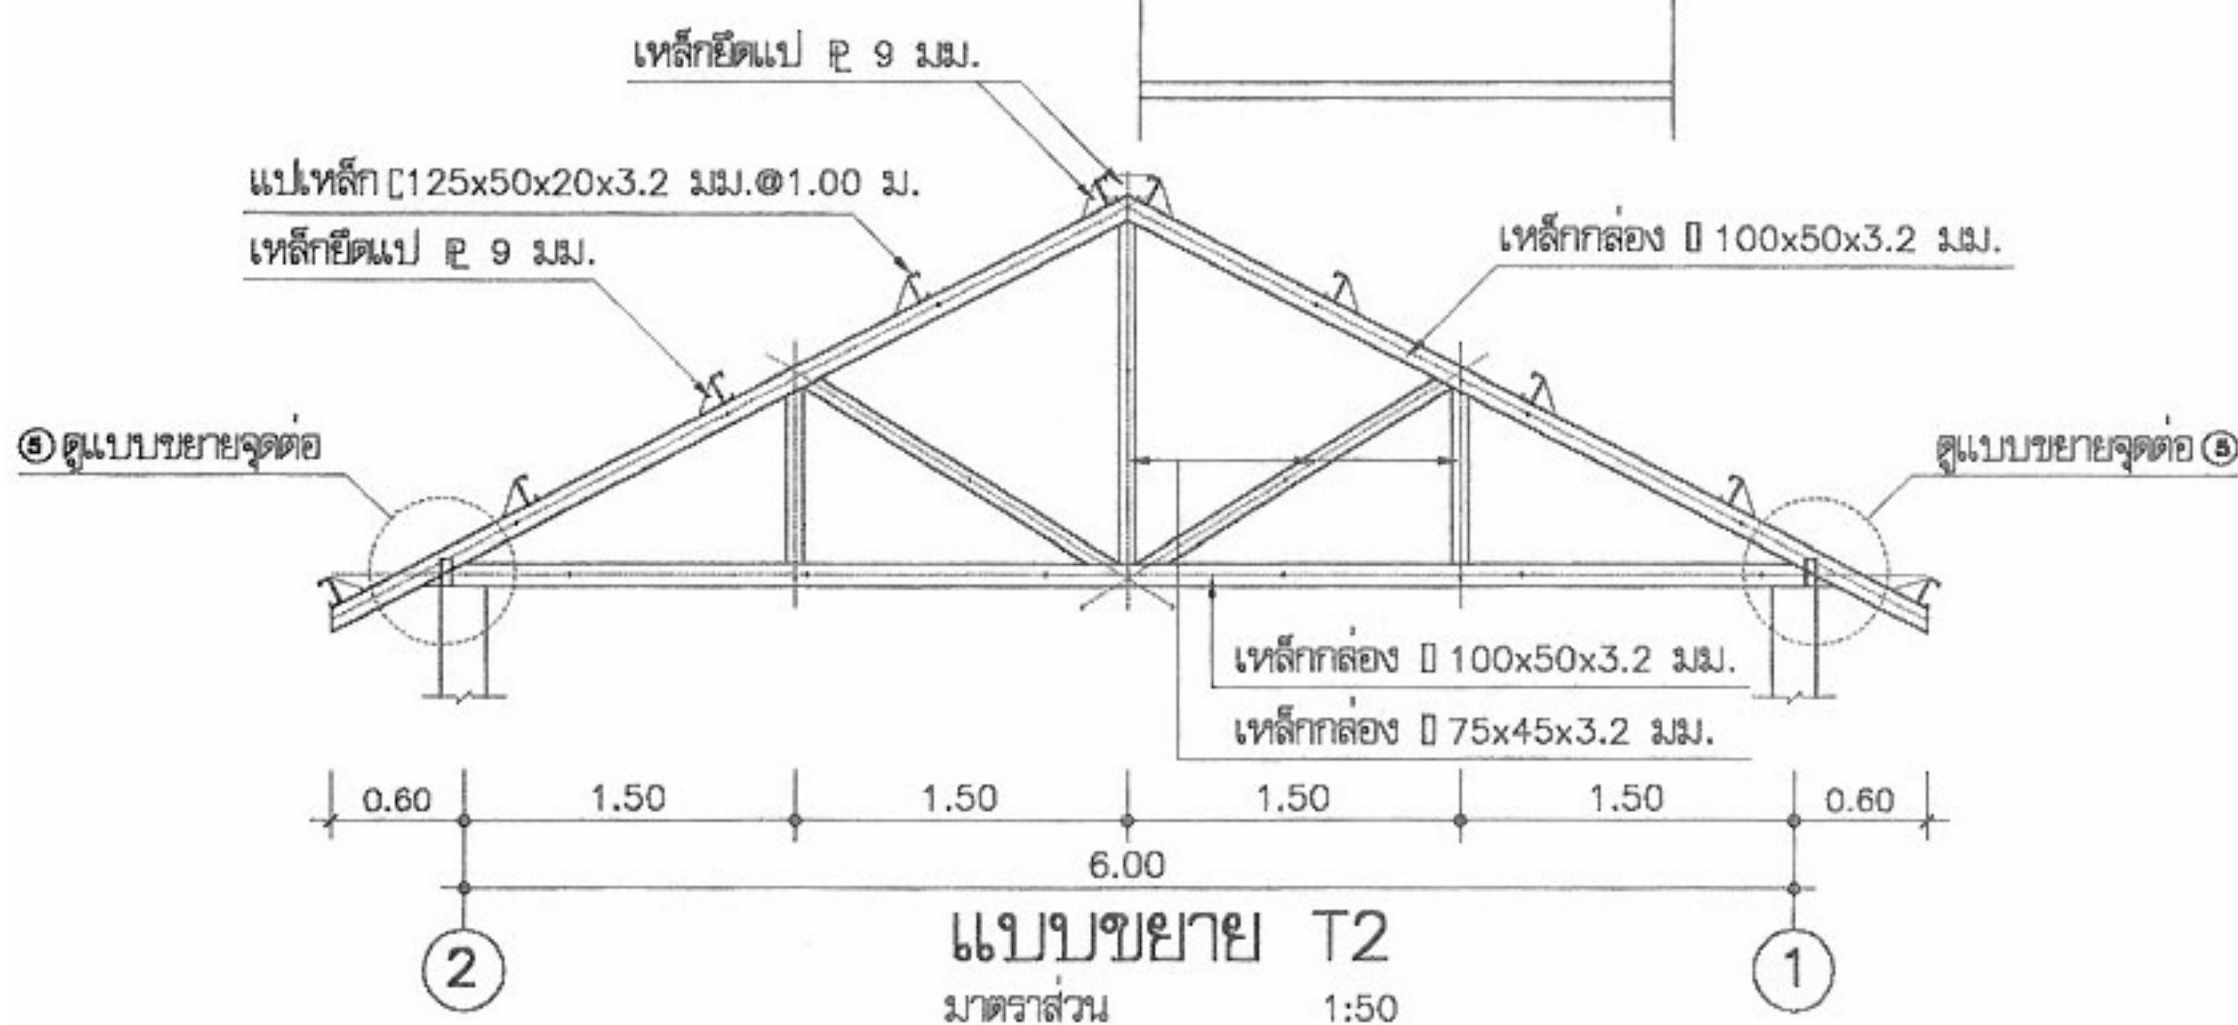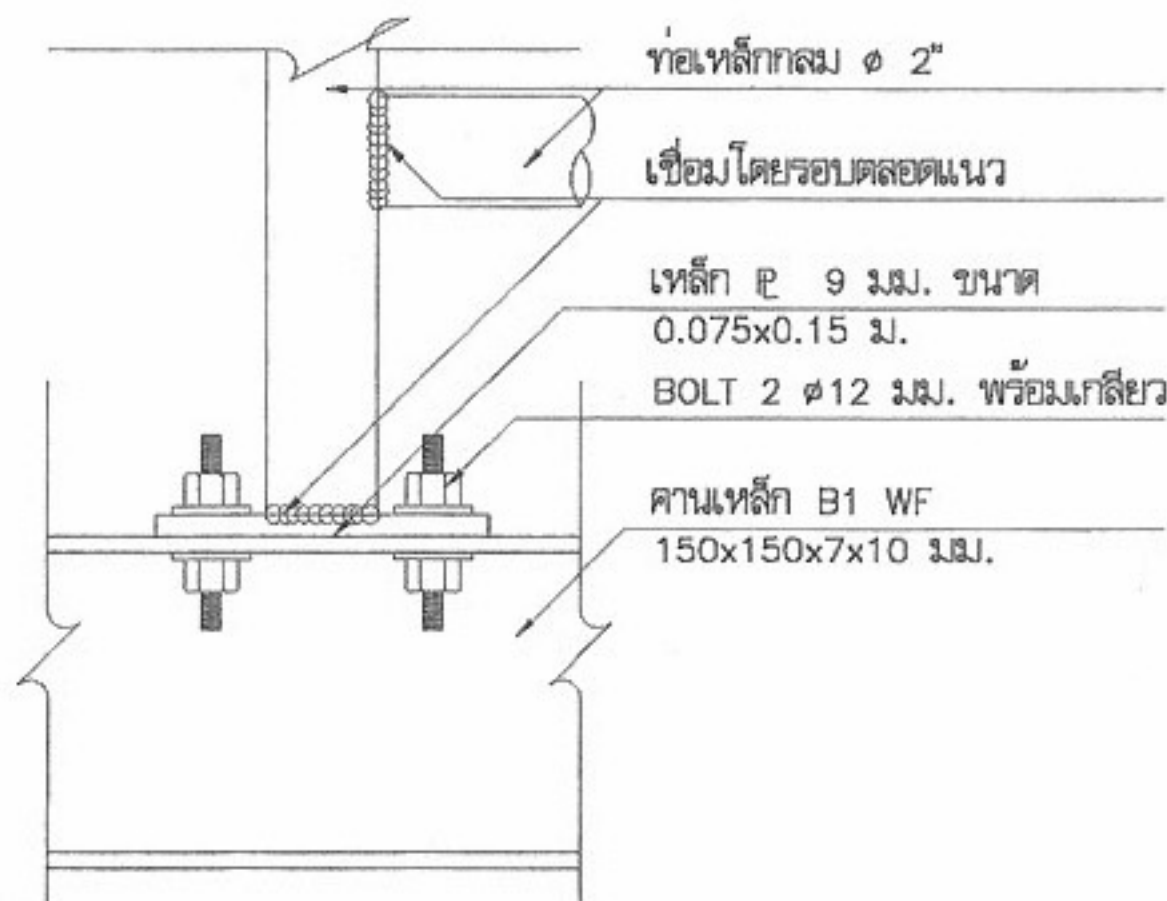

Z-Z 1:10

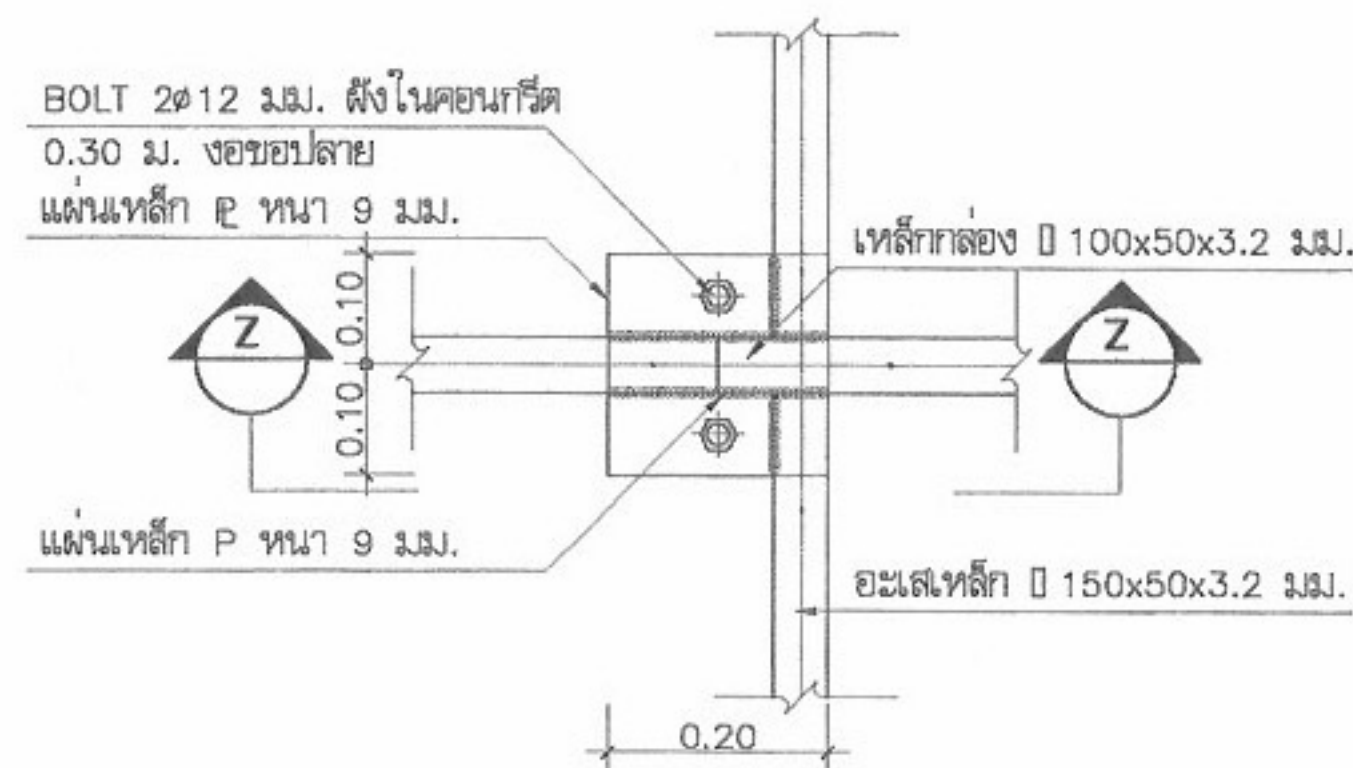

แบบขยายจุดต่อ ๑
มาตราส่วน 1:10



โครงการมอบอาคารเพื่อประชาชน
ไทยช่วยไทย

แบบ
บ้านผู้ประสบภัย 3 ห้องสุขารวม

สำนักสถาปัตย์กรรม
ผู้ควบคุมการก่อสร้าง

สถาปัตย์กรรม
สถาปนิก
สถาปนิก
สถาปนิก
สถาปนิก

สำนักวิศวกรรมโครงสร้างและงานระบบ
ผู้ควบคุมการก่อสร้าง

วิศวกรรม
โครงสร้าง
วิศวกรรมไฟฟ้า
และเครื่องกล
วิศวกรรม
สุขาภิบาล


อนุมัติ
(นายสว่าง ศรีสุกัน)
อธิบดีกรมโยธาธิการและผังเมือง

แสดงแบบ
ขยายโครงสร้างคานา T2
ขยายราวกันตก

มาตราส่วน 1:50
วัน/เดือน/ปี 21 พ.ย. 2546
เลขที่แบบ ม.บ.462099
แผ่นที่ S-08 จำนวนแผ่น 8

หมายเหตุ แบบที่แสดงอยู่นี้ได้รับการยืมส่วน เพื่อใช้แสดงผลทางหน้าจอเท่านั้น สำหรับแบบที่ใช้ขออนุญาตก่อสร้าง ให้ถ่ายสำเนาจากหนังสือแบบบ้าน

สัญลักษณ์

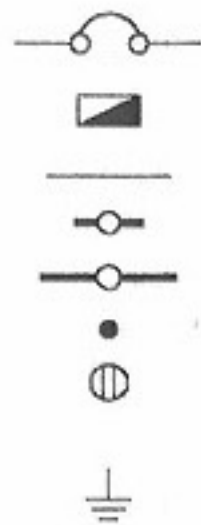

CIRCUIT BREAKER

แผงสวิตช์อัตโนมัติ (LP) ติดผนัง

สายไฟฟ้าเดินลอยยึดด้วยเข็มขัดรัดสาย ทุกระยะประมาณ 0.10 ม.

ดวงโคมฟลูออเรสเซนต์ กล่องเหล็กเปลือย หลอด 1-18 W ติดเพดานหรือผนัง

ดวงโคมฟลูออเรสเซนต์ กล่องเหล็กเปลือย หลอด 1-36 W ติดเพดานหรือผนัง

สวิตช์เดี่ยว ขนาด 16A-250V ติดผนังเรียบผนังหรือข้างเสาสูง 1.30 ม.


ตัวรับคู่ ขนาด 16A-250V แบบ UNIVERSAL ชนิดมีขาเดินและม่านนิรภัย

พร้อมกลองติดผนังสูงจากพื้น 0.50 เมตร


หลักสายดินทองแดงหุ้มเหล็กขนาด ๑5/8 นิ้ว ยาว 2.40 เมตร

รายละเอียด

- ในการติดตั้ง ผู้รับจ้างต้องปฏิบัติตามกฎระเบียบข้อบังคับของการไฟฟ้า
- วัสดุอุปกรณ์ที่ใช้
 - 2.1 แผงสวิตช์อัตโนมัติเป็นผลิตภัณฑ์ของ SQUARE D, ABB, MEM, CLIPSAL, TICINO, SIEMENS, MG, HANGER
 - 2.2 CIRCUIT BREAKER เป็นผลิตภัณฑ์ของ SQUARE D, ABB, MEM, CLIPSAL, TICINO, SIEMENS, MG, HANGER
 - 2.3 ดวงโคมไฟฟ้าเป็นผลิตภัณฑ์ภายในประเทศที่มีเครื่องหมายการค้า โดยมีอุปกรณ์ประกอบดังนี้
 - หลอดฟลูออเรสเซนต์ มอก.236-2533
 - ขั้วรับหลอดและขั้วรับสวิตช์ มอก.344-2530
 - สวิตช์ มอก.183-2528
 - บัลลาสต์ มอก.23-2521
 - 2.4 สายไฟฟ้าเป็นผลิตภัณฑ์ มอก.11-2531
 - 2.5 สวิตช์และตัวรับไฟฟ้า เป็นผลิตภัณฑ์ของ NATIONAL, ABB, TICINO, CLIPSAL
- หากมิได้กำหนดไว้เป็นอย่างอื่น ชนิดและขนาดของสายไฟฟ้าให้ใช้ดังนี้
 - 3.1 สายวงจรย่อยแสงสว่าง ใช้สาย 2x2.5 sq.mm. VAF.
 - 3.2 สายแยกจากสวิตช์เข้าดวงโคม สายระหว่างดวงโคม ใช้สาย 2x1.5 sq.mm. VAF.
 - 3.3 สายวงจรตัวรับไฟฟ้า ใช้สาย 2x2.5/G1.5 VAF-GRD
 - 3.4 สายบ่อน สายประธาน ขนาดตามแบบ

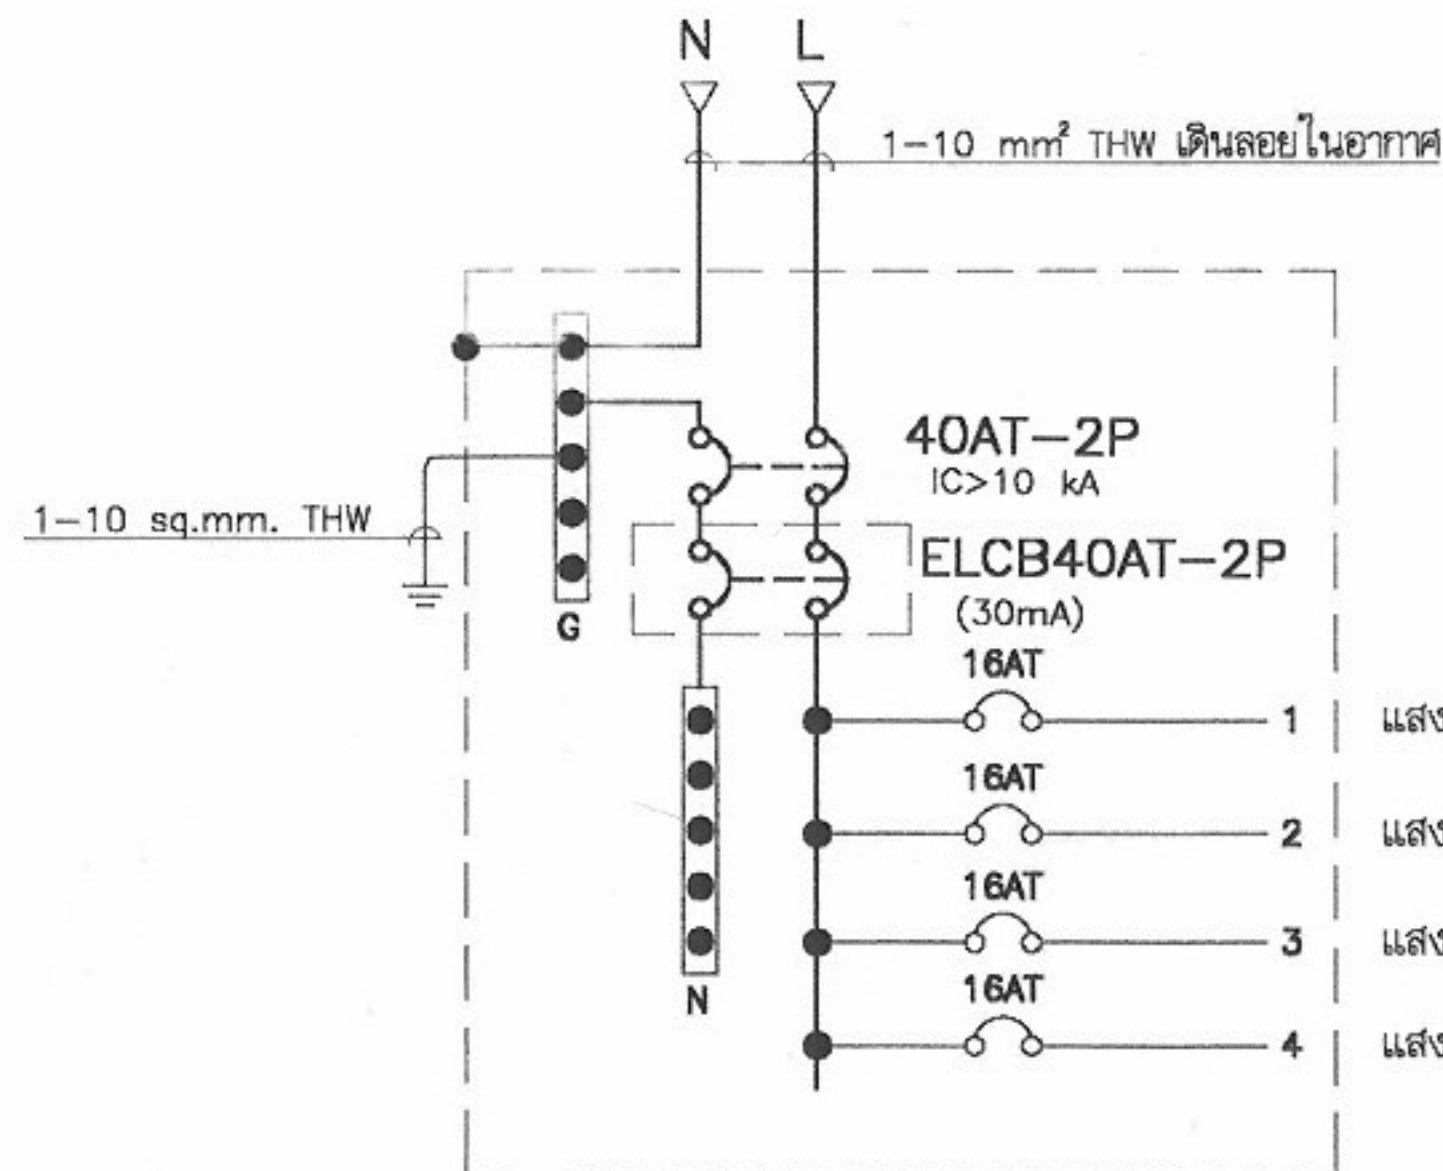

แผงสวิตช์ LP
บ้านเรือนแถว

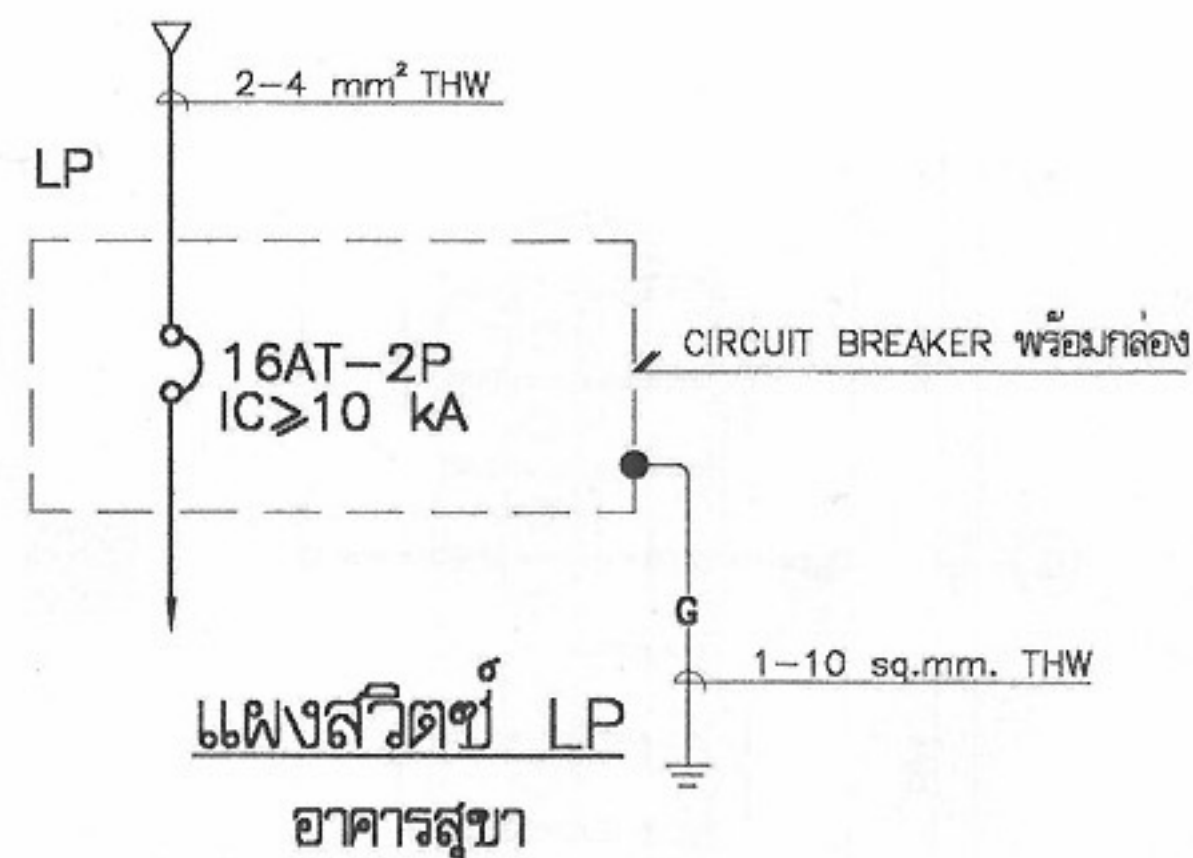

โครงการแบบอาคารเพื่อประชาชน

ไทยช่วยไทย

แบบ

บ้านผู้ประสบภัย 3 ห้องสุขารวม

สำนักสถาปัตยกรรม

ผู้ควบคุมการดำเนินงาน

สถาปนิก

สถาปนิก

สำนักวิศวกรรมโครงสร้างและงานระบบ

ผู้ควบคุมการดำเนินงาน

วิศวกร

วิศวกร

วิศวกรไฟฟ้า

วิศวกร

และเครื่องกล

วิศวกร

วิศวกร

วิศวกร

สถาปนิก

วิศวกร

อนันต์

(นายสว่าง ศรีสุกัน)

อธิบดีกรมโยธาธิการและผังเมือง

แสดงแบบ

สัญลักษณ์,รายละเอียด

,DIAGRAM แปลนไฟฟ้า


มาตราส่วน 1:100

วัน/เดือน/ปี 21 พ.ย. 2546

เลขที่แบบ ม.บ.462099

แผ่นที่ E-01 จำนวนแผ่น 02

หมายเหตุ แบบที่แสดงอยู่นี้ได้รับการยืมส่วน เพื่อใช้แสดงผลทางหน้าจอเท่านั้น สำหรับแบบที่ใช้ขออนุญาตก่อสร้าง ให้ถ่ายสำเนาจากหนังสือแบบบ้าน

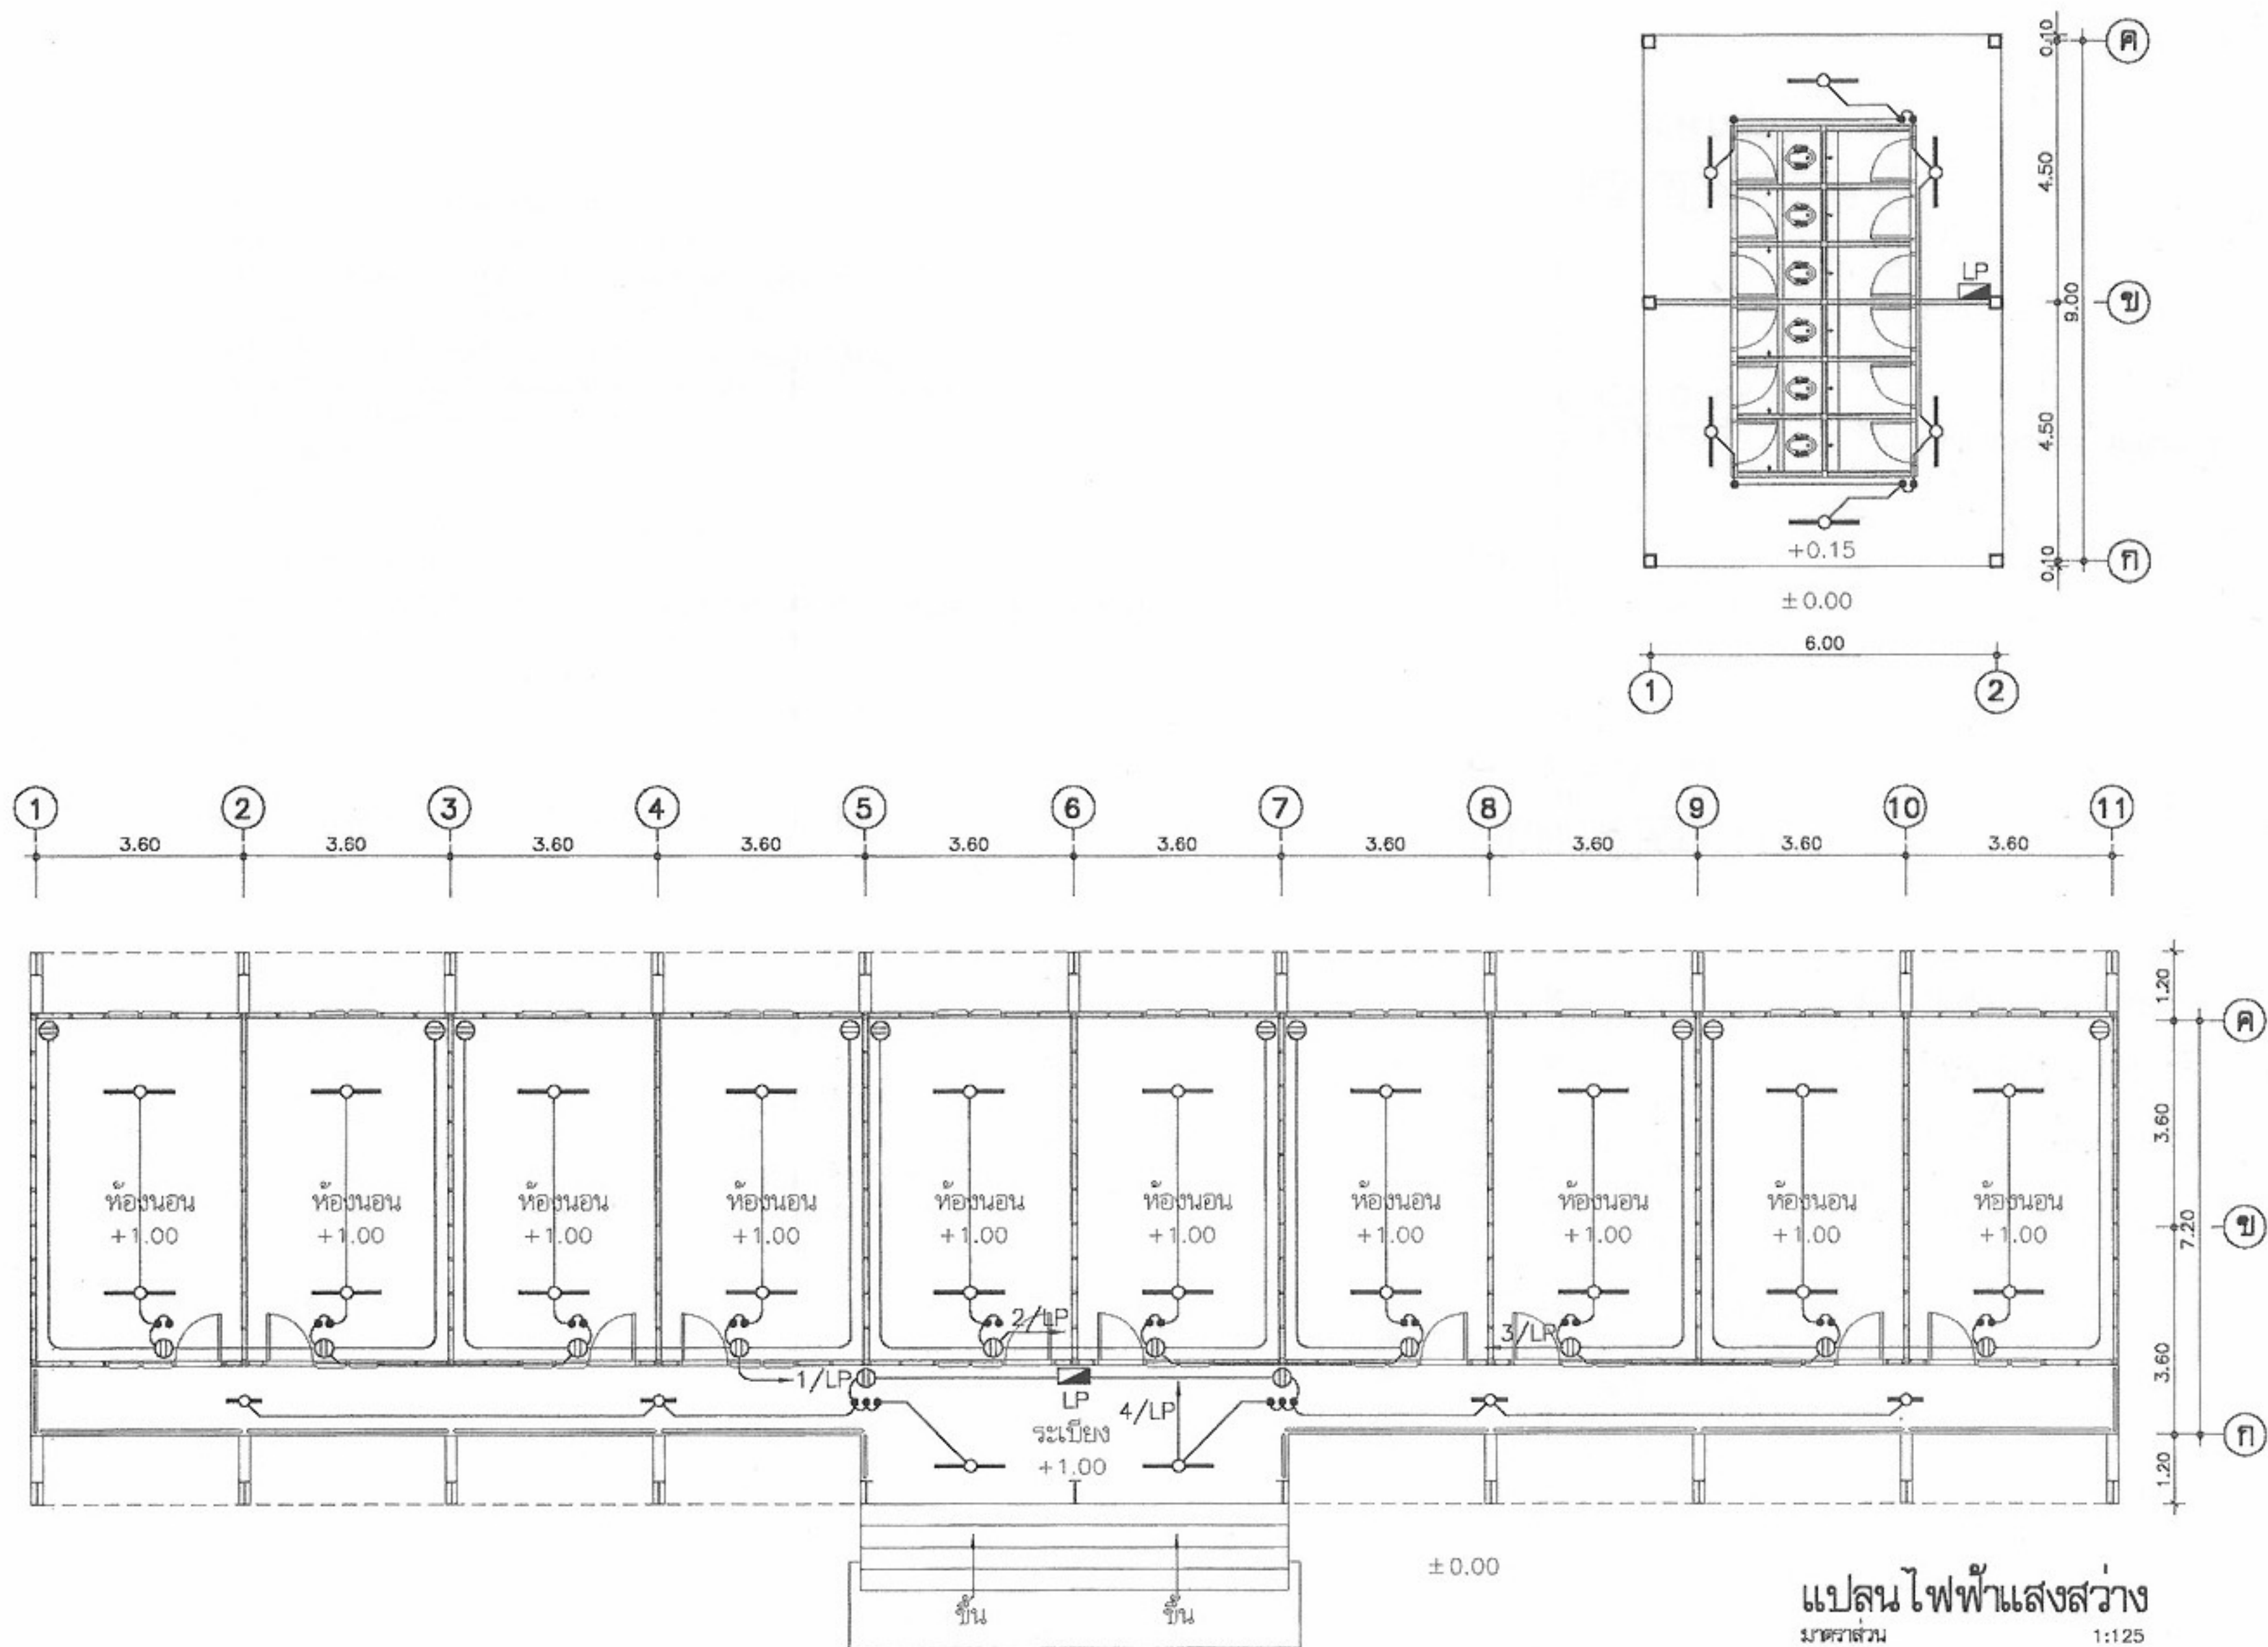

โครงการแบบอาคารเพื่อประชาชน

ไทยช่วยไทย

แบบ

บ้านผู้ประสบภัย 3 ห้องสุขารวม

สำนักสถาปัตยกรรม

ผู้ควบคุมการออกแบบ

สถาปนิก

สถาปนิก
สถาปนิก
สถาปนิก
สถาปนิก

สำนักวิศวกรรมโครงสร้างและงานระบบ

ผู้ควบคุมการออกแบบ

วิศวกรรม

วิศวกร

โครงสร้าง

วิศวกร

วิศวกรรมไฟฟ้า

วิศวกร

และเครื่องกล

วิศวกร

วิศวกรรม

วิศวกร

สุขาภิบาล

วิศวกร

อนุมัติ

(นายสว่าง ศรีสกุล)

อธิบดีกรมโยธาธิการและผังเมือง

แสดงแบบ

แปลนไฟฟ้าแสงสว่าง

มาตราส่วน 1:100

วัน/เดือน/ปี 21 พ.ย. 2546

เลขที่แบบ ม.บ.462099

แผ่นที่



E-02

จำนวนแผ่น

02

หมายเหตุ แบบที่แสดงอยู่นี้ได้รับการยืมส่วน เพื่อใช้แสดงผลทางหน้าจอเท่านั้น สำหรับแบบที่ใช้ขออนุญาตก่อสร้าง ให้ถ่ายสำเนาจากหนังสือแบบบ้าน

ชนิด	วัสดุท่อ
ท่อประปา CW	PVC ขึ้น 13.5
ท่อน้ำโสโครก S	PVC ขึ้น 8.5 ลาดเอียงไม่น้อยกว่า 1:75
ท่อน้ำทิ้ง W	PVC ขึ้น 8.5 ลาดเอียงไม่น้อยกว่า 1:75
ท่ออากาศ V	PVC ขึ้น 8.5

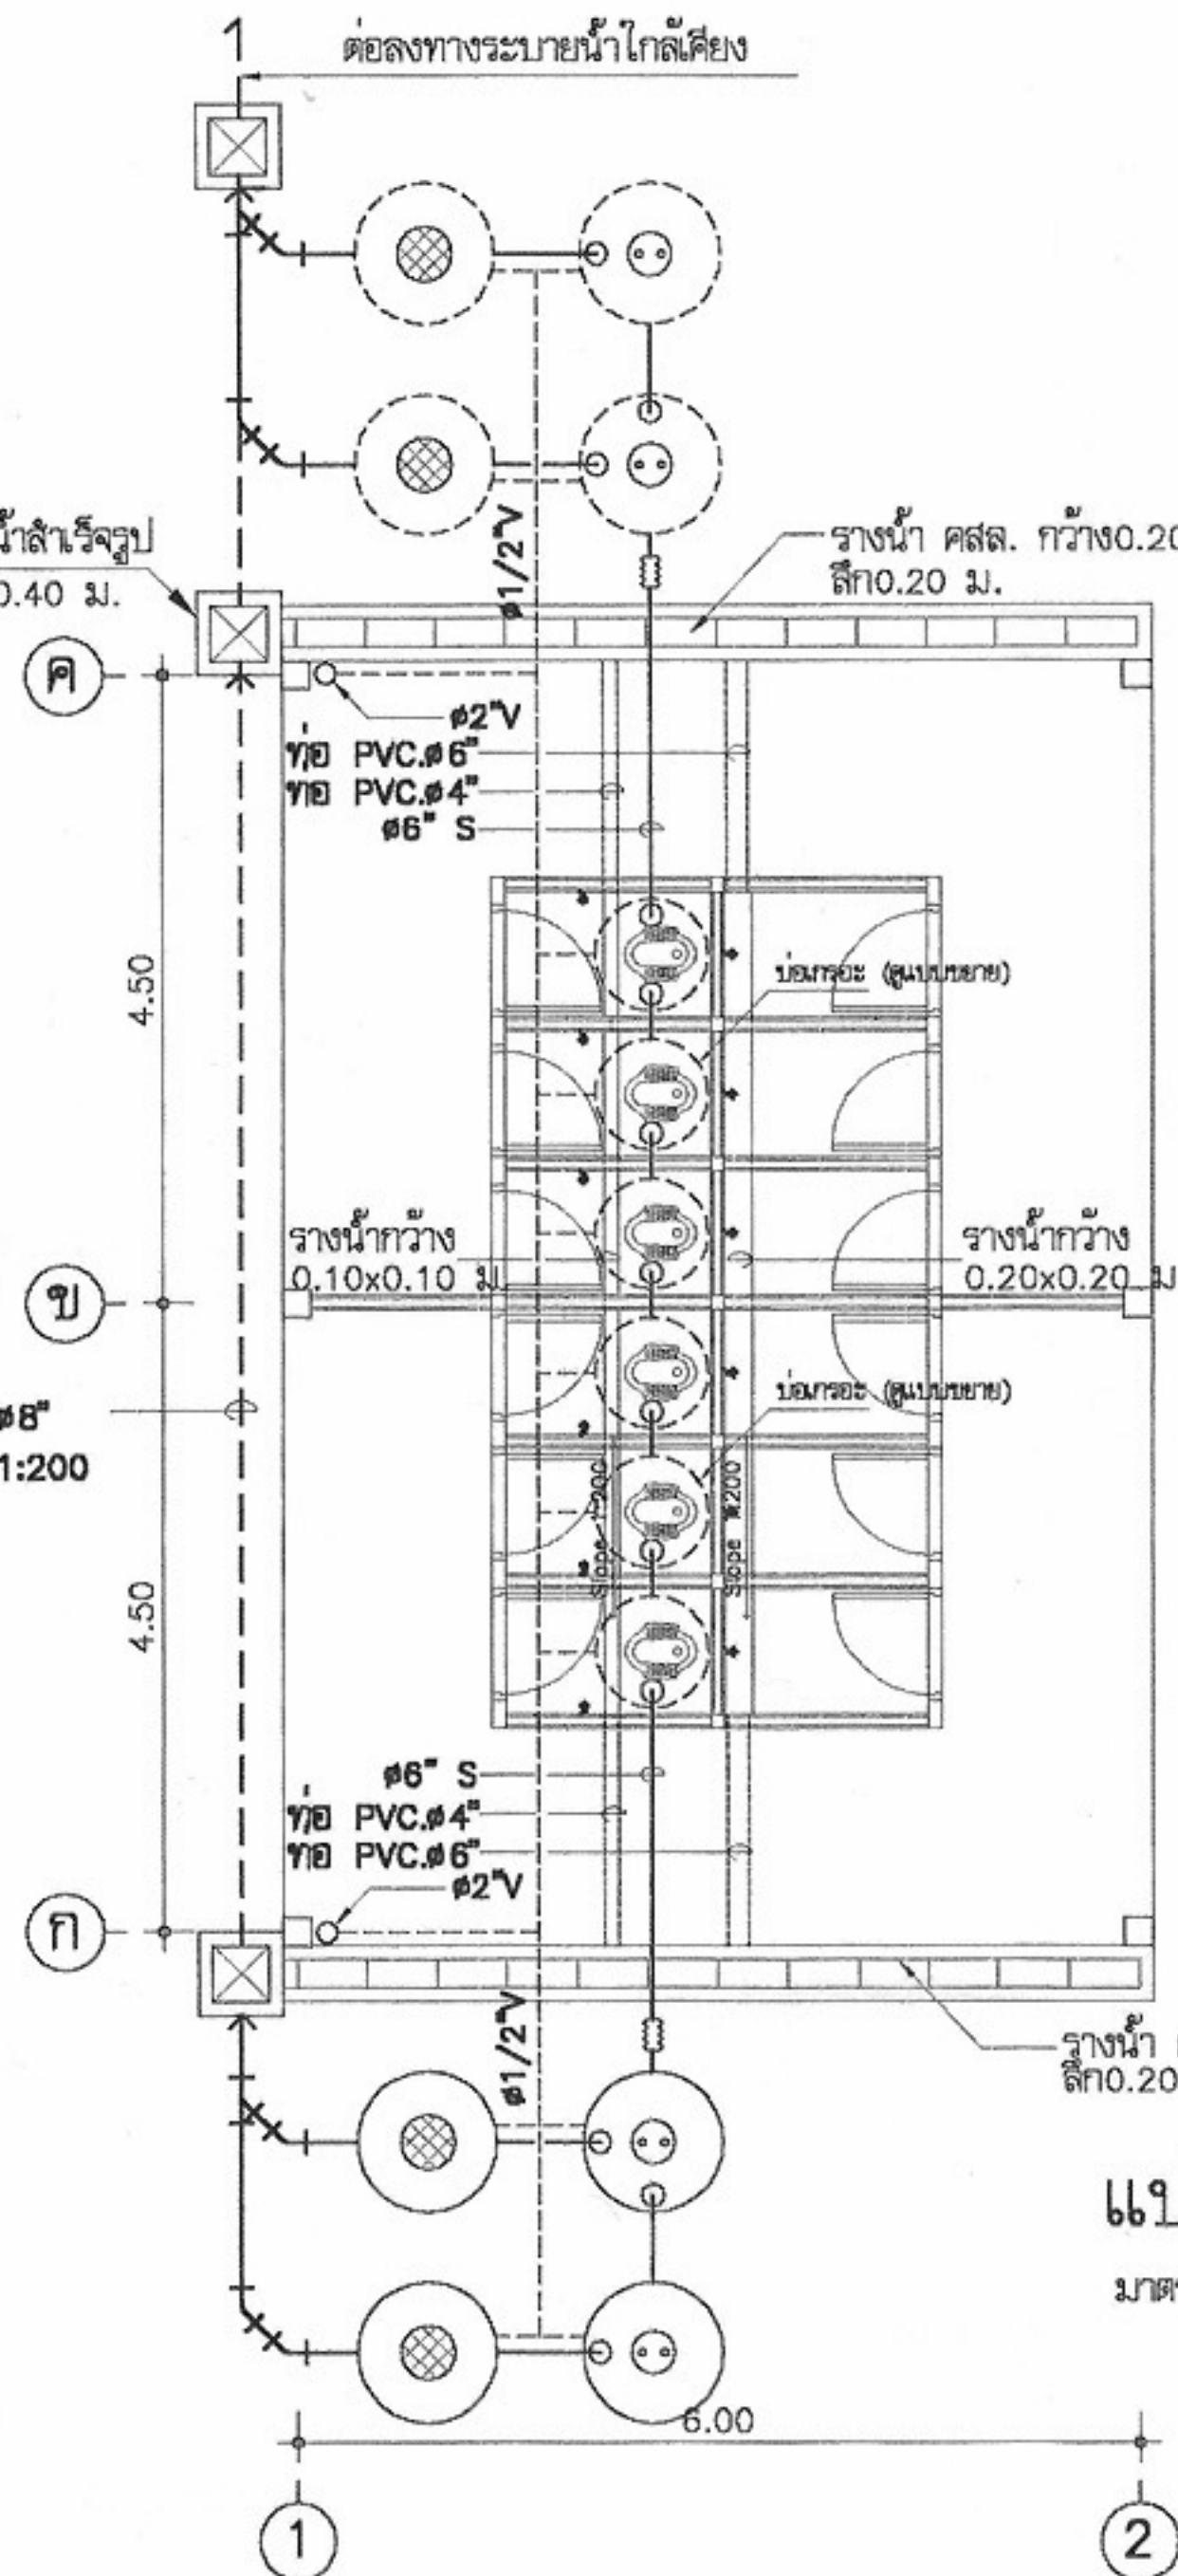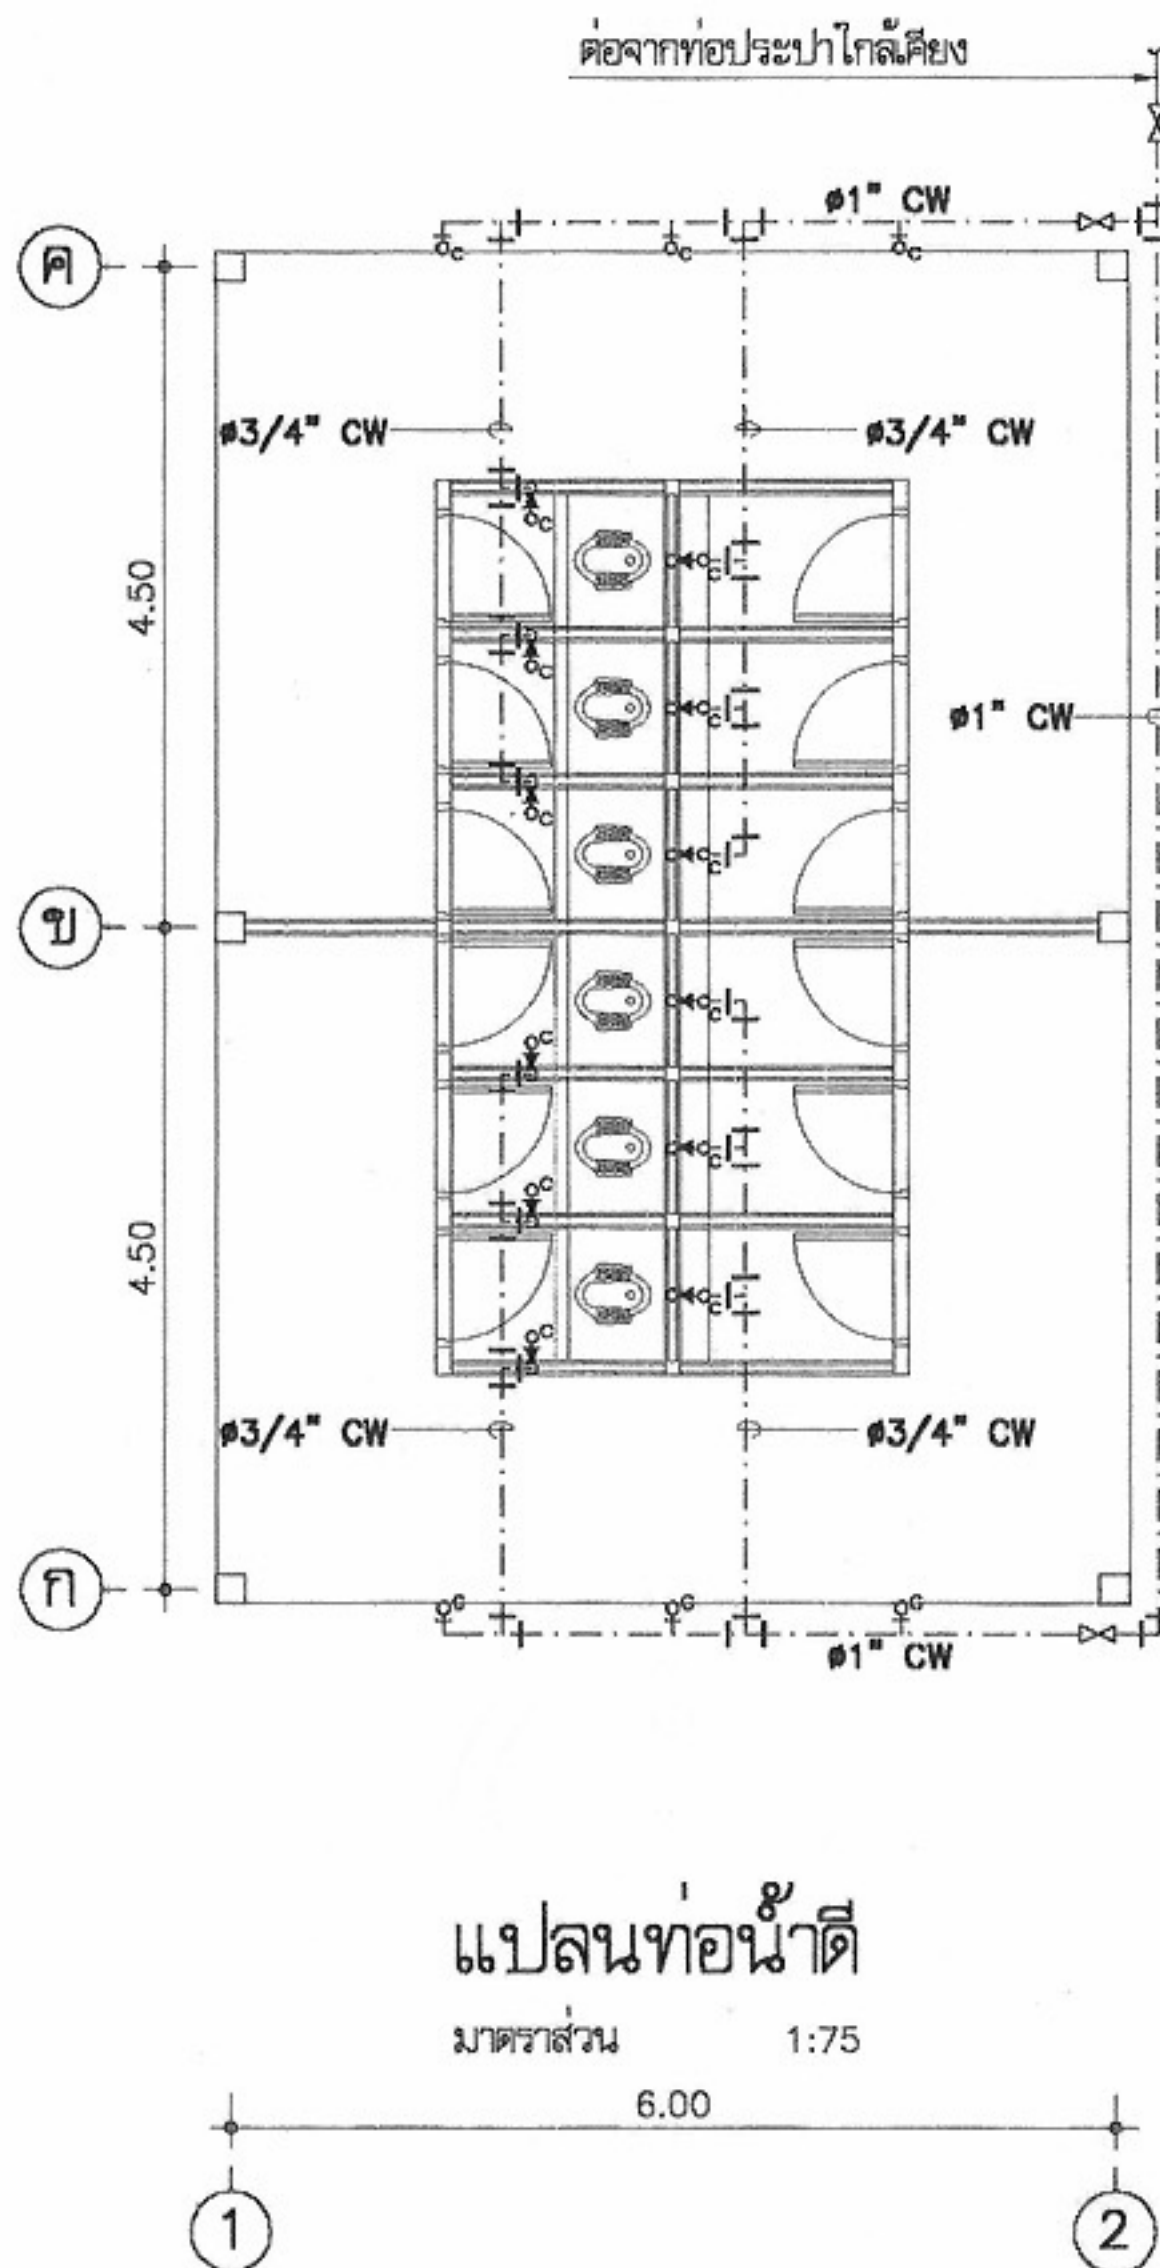

สัญลักษณ์

- บ่อกรองน้ำสำเร็จรูป ขนาด ความจุรวมไม่น้อยกว่า 2 m.³ ผลิตจาก PP, AQUA, DOS หรือเทียบเท่า
- บ่อกรองน้ำอากาศสำเร็จรูป ขนาด ความจุรวมไม่น้อยกว่า 2 m.³ ผลิตจาก PP, AQUA, DOS หรือเทียบเท่า
- ⊠ บ่อพักน้ำทิ้งสำเร็จรูป ขนาด 40x40cm
- (M) มาตรฐานน้ำ 1/2"
- X ประตุน้ำ 1/2"
- ขั้วต่ออ่อน
- ก้อนน้ำ
- RD ROOF DRAIN
- RL RAIN LEADER
- ⊠ FD FLOOR DRAIN
- FCO FLOOR CLEAN OUT
- CW COLD WATER
- V VENT
- S SOIL
- W WASTE



โครงการแบบอาคารเพื่อประชาชน

ไทยช่วยไทย

แบบ

บ้านผู้ประสบภัย 3 ห้องสุขารวม

สำนักสถาปัตย์กรรม

ผู้ควบคุมการก่อสร้าง

สถาปัตย์กรรม

สถาปัตย์
สถาปัตย์
สถาปัตย์
สถาปัตย์

สำนักวิศวกรรมโครงสร้างและงานระบบ

ผู้ควบคุมการก่อสร้าง

วิศวกรรม

วิศวกร

โครงสร้าง

วิศวกร

วิศวกรรมไฟฟ้า

วิศวกร

และเครื่องกล

วิศวกร

วิศวกรรม

วิศวกร

สุขาภิบาล

วิศวกร

อนุมัติ

(นายสว่าง ศรีสุคนธ์)

อธิบดีกรมโยธาธิการและผังเมือง

แสดงแบบ

ขยายห้องน้ำ

มาตราส่วน 1:75

วัน/เดือน/ปี 21 พ.ย. 2546

เลขที่แบบ ม.บ.462099




แผ่นที่

SN-01


จำนวนแผ่น

02

หมายเหตุ แบบที่แสดงอยู่นี้ได้รับการยืมส่วน เพื่อใช้แสดงผลทางหน้าจอเท่านั้น สำหรับแบบที่ใช้ขออนุญาตก่อสร้าง ให้ถ่ายสำเนาจากหนังสือแบบบ้าน

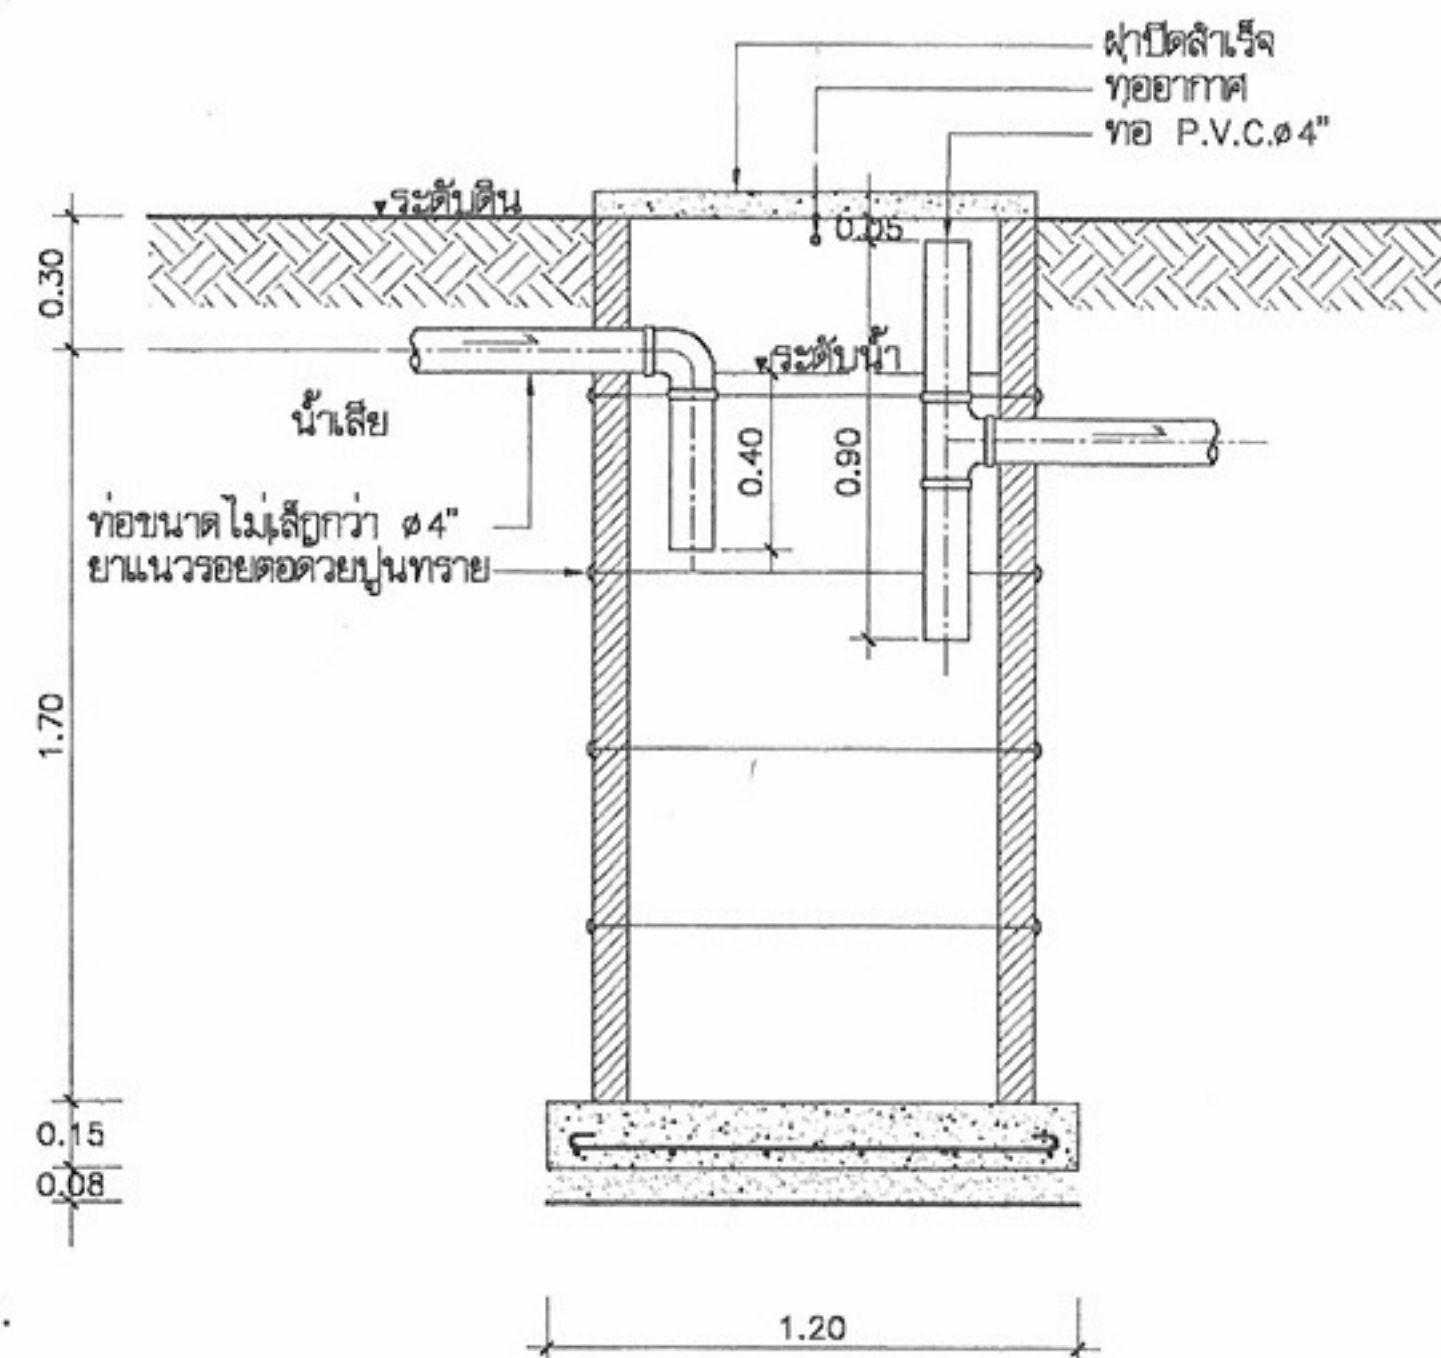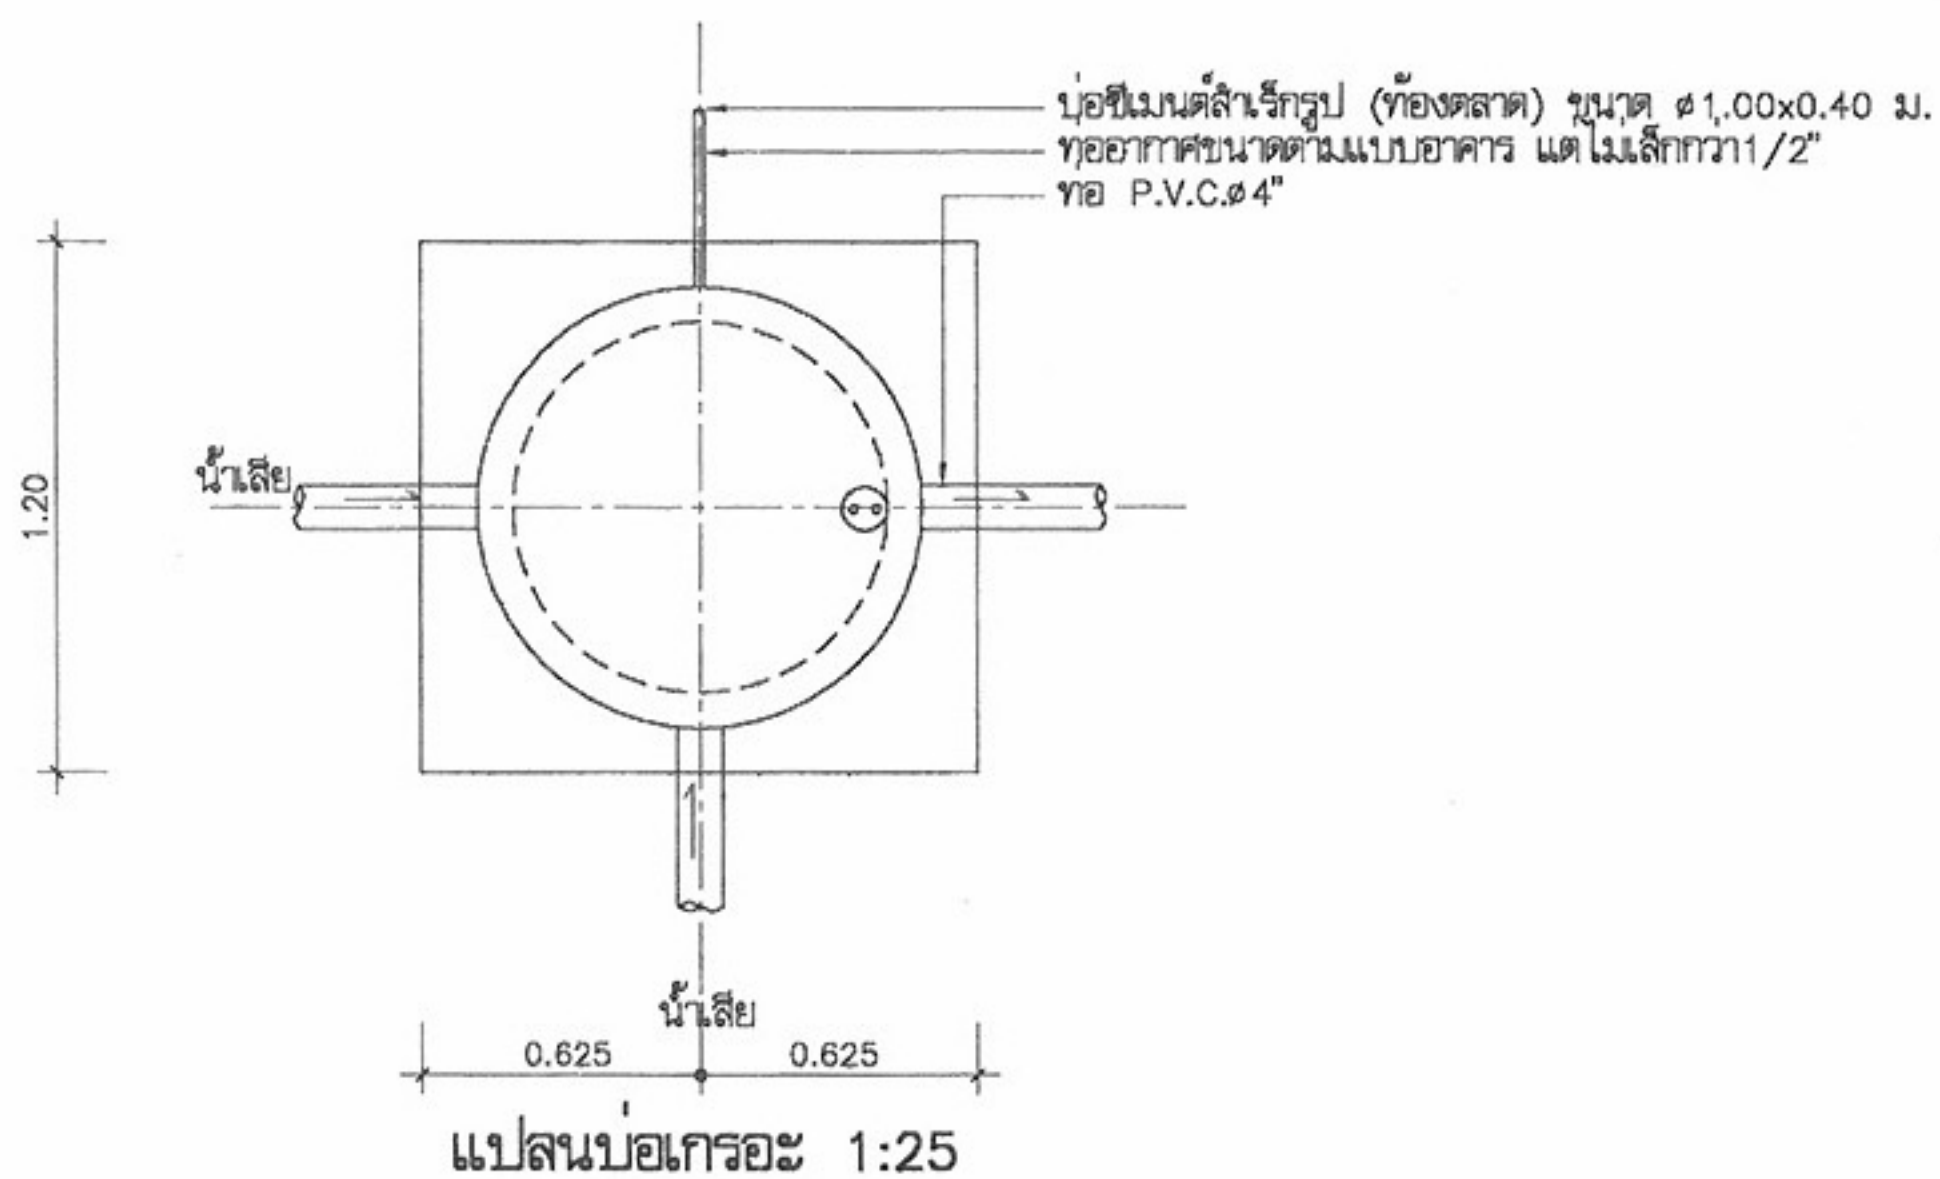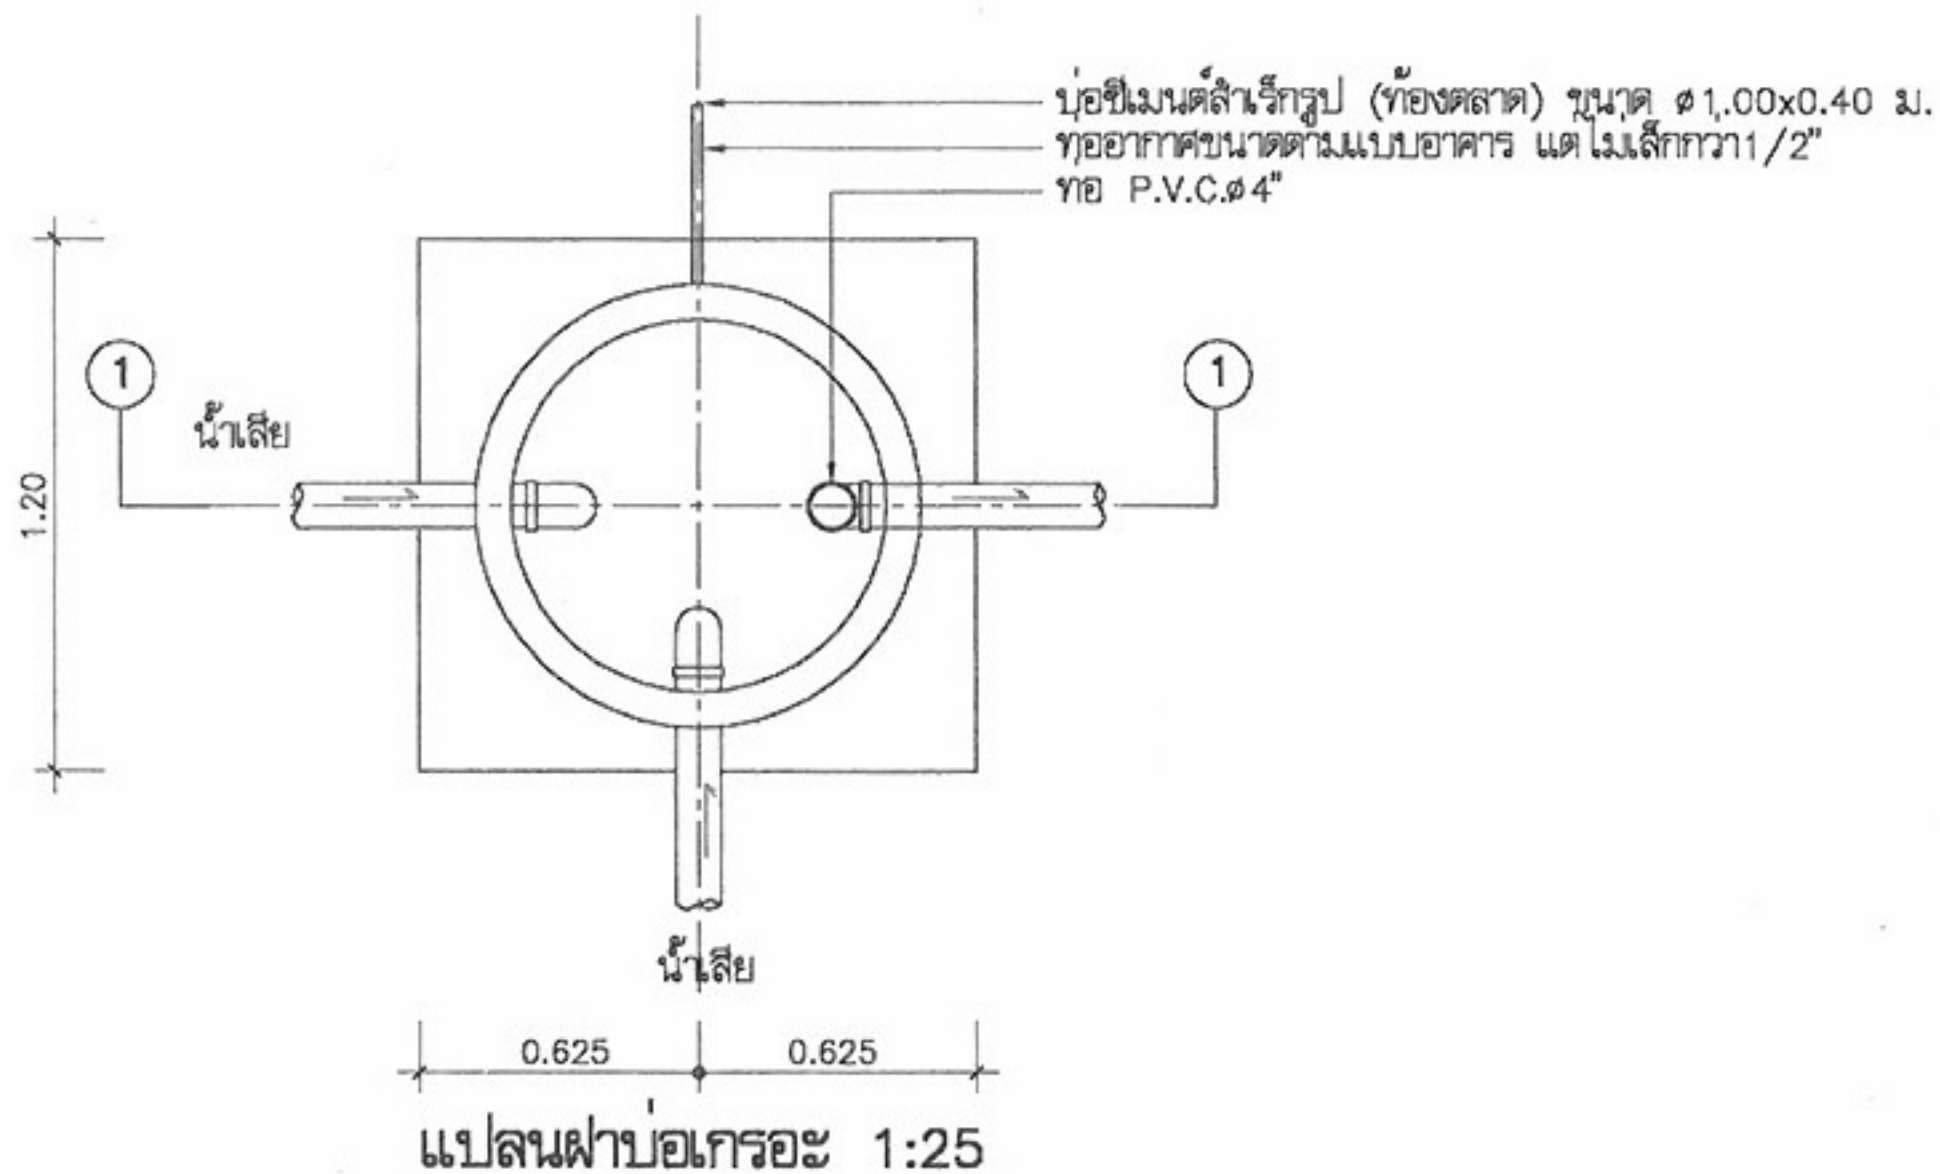

รูปตัด ①-① 1:25

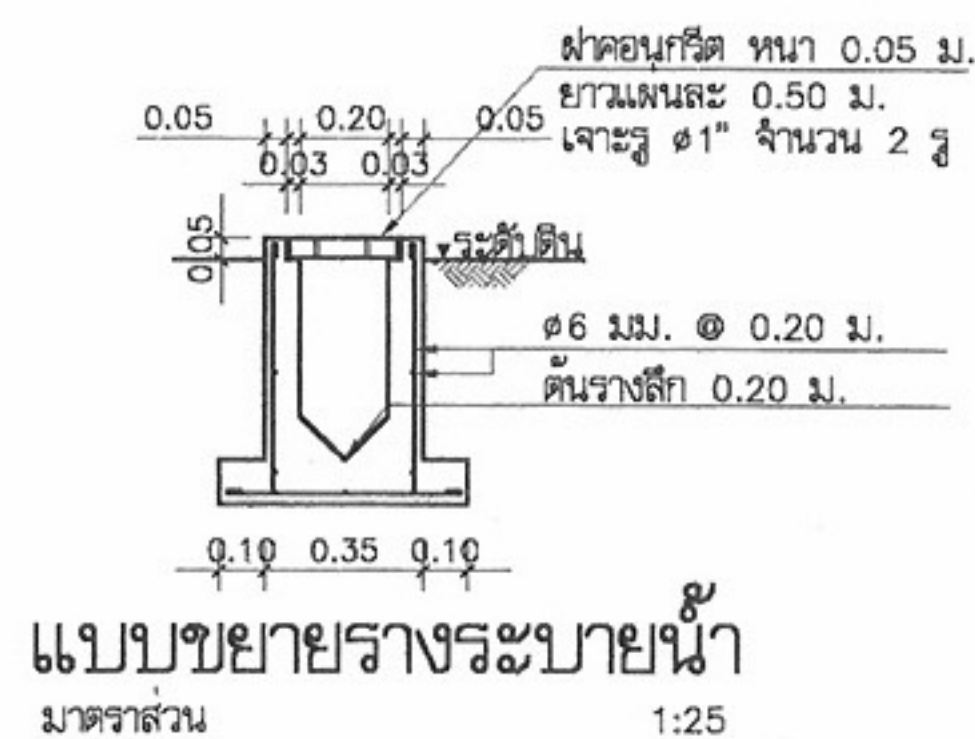

โครงการแบบอาคารเพื่อประชาชน

ไทยช่วยไทย

แบบ

บ้านผู้ประสบภัย 3 ห้องสุขารวม

สำนักสถาปัตยกรรม

ผู้ควบคุมการดำเนินงาน

สถาปนิก

สถาปนิก

สำนักวิศวกรรมโครงสร้างและงานระบบ

ผู้ควบคุมการดำเนินงาน

วิศวกร

วิศวกร

วิศวกรไฟฟ้า

วิศวกร

และเครื่องกล

วิศวกร

วิศวกร

วิศวกร

สุขาภิบาล

วิศวกร

อนุมัติ

(นายสว่าง ศรีสกุล)

อธิบดีกรมโยธาธิการและผังเมือง

แสดงแบบ

ขยายบ่อเกรอะ

มาตราส่วน

1:25

วัน/เดือน/ปี

21 พ.ย. 2546

เลขที่แบบ

ม.บ.462099

แผ่นที่

SN-02

จำนวนแผ่น

02

หมายเหตุ แบบที่แสดงอยู่นี้ได้รับการยืมส่วน เพื่อใช้แสดงผลทางหน้าจอตานั้น สำหรับแบบที่ใช้ขออนุญาตก่อสร้าง ให้ถ่ายสำเนาจากหนังสือแบบบ้าน