


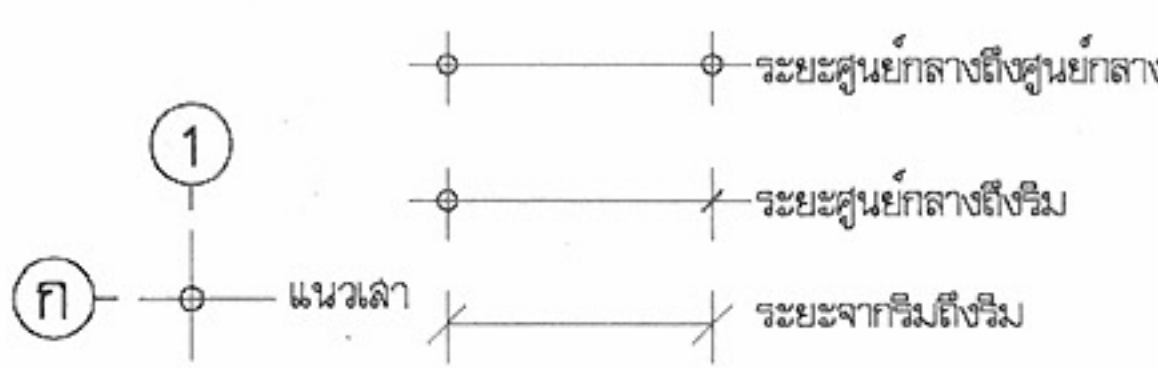

บ้านครอบครัวไทยเป็นสุข ๘

รายการแบบสถาปัตยกรรม (A)	รายการแบบโครงสร้าง (S)	รายการสัญลักษณ์ประกอบแบบ	
A-01 สารบัญแบบ,สัญลักษณ์ประกอบแบบ A-02 รายการประกอบแบบ A-03 ผังบริเวณ A-04 แปลนพื้นที่ชั้นล่าง A-05 แปลนพื้นที่ชั้นบน A-06 ,แปลนหลังคา A-07 รูปด้าน 1,2 A-08 รูปด้าน 3,4 A-09 รูปตัด 1,2 A-10 แบบขยายบันได A-11 แบบขยายห้องน้ำ 1 A-12 แบบขยายห้องน้ำ 2 A-13 แบบขยายห้องน้ำ 3 A-14 แบบขยายห้องน้ำ 4 A-15 แบบขยายห้องน้ำ 5 A-16 แบบขยายประตู-หน้าต่าง A-17 แบบขยายทั่วไป	S-01 แปลนฐานรากและเสาตอม่อ S-02 แปลน เสา คานและพื้น ชั้นล่าง S-03 แปลน เสา คานและพื้น ชั้นบน S-04 แปลนโครงสร้างหลังคา S-05 แบบขยายการเสริมเหล็ก ฐานราก,ตอม่อ S-06 แบบขยายการเสริมเหล็กใน พื้น S-07 แบบขยายการเสริมเหล็กใน คาน ,บันได ค.ส.ล.	 ① ใช้กำหนดหมายเลขประตู ในแบบเพื่ออ้างอิงถึง ① ใช้กำหนดหมายเลขหน้าต่าง ในแบบเพื่ออ้างอิงถึง 1- A-NO. แบบขยายทั่วไป A-NO. แผ่นที่ ที่อ้างอิงไปถึง N ทิศเหนือ 3 1,2,3,4 ชื่อรูปด้าน แสดงทิศทางตามแนวข้อบอ 2 A-NO. A-NO. A-NO. A-NO. 1 A-NO. แผ่นที่ ที่อ้างอิงไปถึง A A-NO. ชื่อรูปตัดอาคาร A-NO. แผ่นที่ ที่อ้างอิงไปถึง ผนังก่ออิฐครึ่งแผ่น ผนังกระฉก คอนกรีต กระฉก เหล็ก ดิน ไม้แต่งผิว SLOPE 1:100 แนวเฉียงลาด	 โครงการแบบอาคารเพื่อประชาชน ครอบครัวไทยเป็นสุข แบบ บ้านครอบครัวไทยเป็นสุข 8 สำนักสถาปัตยกรรม สถาปัตยกรรม สำนักวิศวกรรมโครงสร้างและงานระบบ วิศวกรรม โครงสร้าง วิศวกรรมไฟฟ้า และเครื่องกล วิศวกรรม สุขาภิบาล อนุมัติ (นายสว่าง ศรีสุกัน) อธิบดีกรมโยธาธิการและผังเมือง แสดงแบบ สารบัญแบบ สัญลักษณ์ประกอบแบบ มาตราส่วน วัน/เดือน/ปี 21 พ.ย. 2546 เลขที่แบบ ม.บ.462126 แผ่นที่ A-01 จำนวนแผ่น 17
	รายการแบบวิศวกรรมไฟฟ้า(E)	E-01 สัญลักษณ์,รายละเอียด E-02 DIAGRAM E-03 แปลนไฟฟ้าแสงสว่าง-สื่อสาร ชั้นล่าง E-04 แปลนไฟฟ้าแสงสว่าง-สื่อสาร ชั้นบน E-05 ผังเดินรับไฟฟ้า,โทรศัพท์และทีวี ชั้นล่าง E-06 ผังเดินรับไฟฟ้า,โทรศัพท์และทีวี ชั้นบน	
	รายการแบบวิศวกรรมสุขาภิบาล(SN)	SN-01 แปลนสุขาภิบาล ชั้นล่าง SN-02 แปลนสุขาภิบาล ชั้นบน SN-03 แบบขยายห้องน้ำ ,สัญลักษณ์	

หมายเหตุ แบบที่แสดงอยู่นี้ได้รับการย่อส่วน เพื่อใช้แสดงผลทางหน้าจอเท่านั้น สำหรับแบบที่ใช้ขออนุญาตก่อสร้าง ให้ถ่ายสำเนาจากหนังสือแบบบ้าน

รายการประกอบแบบอาคารบ้านครอบครัวไทยเป็นสุข

1. วัตถุประสงค์

กรมโยธาธิการและผังเมืองมีความประสงค์ทำการออกแบบอาคารเพื่อประชาชนตามดำริของ ฯพณฯนายกรัฐมนตรี และเป็นไปตามนโยบายรัฐบาลเพื่อบริการประชาชน โดยไม่คิดค่าบริการ ออกแบบใดๆทั้งสิ้น

2. รายละเอียดประกอบแบบ

2.1 การวางผังและระดับ

ผู้รับจ้างจะต้องทำการวางผังระดับมาตรฐานให้ถูกต้องเรียบร้อยตามกฎหมายควบคุมอาคาร ก่อนดำเนินการต่อไป

2.2 งานฐานรากและโครงสร้าง ค.ส.ล.

ตามที่ได้กำหนดไว้ในแบบและรายการวิศวกรรมโครงสร้าง ส่วนรายละเอียดอื่นๆ ให้ดำเนินการ ตามมาตรฐานงานก่อสร้าง มยธ.101-มยธ.106

2.3 งานสถาปัตยกรรม

ก. งานพื้น

- พื้น ค.ส.ล. ทำผิวขัดมันเรียบ หรือผิวขัดหยาบ ใช้ปูนซีเมนต์ตามมาตรฐาน เลขที่ มอก.15 เล่มที่ 1-2532
- พื้น ค.ส.ล. ปูกระเบื้องเคลือบผิวด้าน ขนาด 8"x8" หรือ 12"x12" ตามแบบระบุ ใช้กระเบื้องเซรามิกผิวเคลือบด้าน ตามมาตรฐาน มอก. 37-2529 น้ำยากันซึม ใช้ของ ที่ผลิตในประเทศ
- พื้น ค.ส.ล. ปูไม้เนื้อแข็ง 1"x4" ดีเข้าลิ้น ใช้ไม้เนื้อแข็ง เช่น ไม้มะค่า ไม้แดง หรือไม้เต็ง 1"x4" อบเข้าลิ้นอัดสนิท ขัดให้เรียบ แล้วเคลือบด้วยน้ำยาเคลือบเงาไม้ บัวเชิงผนังใช้บัวไม้ขนาด 3/4"x4"

หมายเหตุ การเตรียมผิวพื้นและการปูกระเบื้องให้ทำตามมาตรฐานวิชาชีพช่างที่ดี

ข. งานผนัง

- ผนังทั่วไปก่ออิฐฉาบปูนฉาบเรียบ อิฐต้องเป็นอิฐที่แกร่ง เสาสูงเสมอ ไม่บิดเบี้ยว ต้องพรมน้ำให้ชุ่มก่อนก่อ
- การก่อชนคาน เสา หรือเอ็น ค.ส.ล. ต้องเสียบเหล็ก 6 มม. ทุกระยะไม่เกิน 40 ซม. โดยยื่นออกมา 25 ซม. และฝังในเสา คาน 10 ซม.
- การก่อชนกันเป็นมุม การก่อเว้นช่องสำหรับประตูหน้าต่าง และทุกระยะเกิน 2 ม. ตาม ความยาวของผนังหรือทุกระยะเกิน 3 ม. ให้ทำเอ็น หรือทับหลัง ค.ส.ล. หนาเท่าผนัง กว้าง 15 ซม. เสียบเหล็ก 2 RB 6 มม. @ 0.20 ม.

ค. งานฝ้า

- ฝ้าเพดานแผ่นยิปซัมบอร์ดหนา 9 มม. ชนิดมีแผ่นอลูมิเนียมฟอยล์ ชนิดธรรมดา ชนิดกัน ความชื้น ผลิตในประเทศตามมาตรฐาน มอก. เลขที่ 219-2524 ยานวรอยต่อด้วย ปลาสเตอร์ยิปซัม โครงโครงเหล็กทูลงกึ่งกลี ๑0.40x1.00 หรือ 1.20 ม.
- ฝ้าชายคาไม้เนื้อแข็ง 1/2"x2" เว้นร่อง 0.5 ซม. โครงโครงไม้เนื้อแข็ง 1 1/2"x3" ๑0.60 ม. มอนฝ้าไม้เนื้อแข็ง 3/4"x2" ภายในบุตาข่ายกันแมลง

ง. งานหลังคา

- โครงหลังคา ตามที่ได้กำหนดไว้ในแบบและรายการวิศวกรรมโครงสร้าง
- วัสดุหลังคา กระเบื้องคอนกรีต ที่ผลิตภายในประเทศ

จ. งานประตู-หน้าต่าง และอุปกรณ์

- รายละเอียดตามระบุในแบบขยายประตู-หน้าต่าง และอุปกรณ์
- ติดตั้งมุ้งลวดในช่อง กรอบบานอลูมิเนียมสีดำ

ฉ. งานห้องน้ำ-ส้วม และสุขภัณฑ์

- รายละเอียดตามระบุในแบบขยายห้องน้ำ-ส้วม สุขภัณฑ์ และอุปกรณ์ประกอบ
- การเดินท่อน้ำประปา-ท่อน้ำทิ้ง-ท่อน้ำส้วม ให้เป็นไปตามงานวิศวกรรมสุขาภิบาล

ช. งานสี

- งานทาสีภายนอก สีทาผนังปูนใช้สีอะคริลิก 100% สีทางานเหล็กและไม้ ใช้สีน้ำมันตาม มอก. 327-2538
- งานทาสีภายใน สีทาผนังปูนใช้สีน้ำตาม มอก. 272-2531

หมายเหตุ วัสดุต่างๆดังกล่าวข้างต้น สามารถเปลี่ยนแปลงได้ตามความเหมาะสมและวัตถุประสงค์ ของผู้ว่าจ้าง

2.4 งานวิศวกรรมสุขาภิบาล

ให้ติดตั้งตามแบบวิศวกรรมสุขาภิบาลและมาตรฐานการประปาฯ

2.4 งานวิศวกรรมไฟฟ้า

ให้ติดตั้งตามแบบวิศวกรรมไฟฟ้าและมาตรฐานการไฟฟ้าฯ



โครงการแบบอาคารเพื่อประชาชน

ครอบครัวไทยเป็นสุข

แบบ

บ้านครอบครัวไทยเป็นสุข 8

สำนักสถาปัตยกรรม

๗๒-๕
ผู้อำนวยการสำนัก

สถาปัตยกรรม

สถาปนิก

สถาปนิก

สถาปนิก

สถาปนิก

สำนักวิศวกรรมโครงสร้างและงานระบบ

ผู้อำนวยการสำนัก

วิศวกรรม

วิศวกร

โครงสร้าง

วิศวกร

วิศวกรรมไฟฟ้า

วิศวกร

และเครื่องกล

วิศวกร

วิศวกรรม

วิศวกร

สุขาภิบาล

วิศวกร

อนุมัติ

๗๒-๕

(นายสว่าง ศรีสุกัน)

อธิบดีกรมโยธาธิการและผังเมือง

แสดงแบบ

รายการประกอบแบบ

มาตรฐาน

วัน/เดือน/ปี 21 พ.ย. 2546

เลขที่แบบ ม.บ.462126


แผ่นที่

A-02

จำนวนแผ่น

17

หมายเหตุ แบบที่แสดงอยู่นี้ได้รับการยืมส่วน เพื่อใช้แสดงผลทางหน้าจอเท่านั้น สำหรับแบบที่ใช้ขออนุญาตก่อสร้าง ให้ถ่ายสำเนาจากหนังสือแบบบ้าน

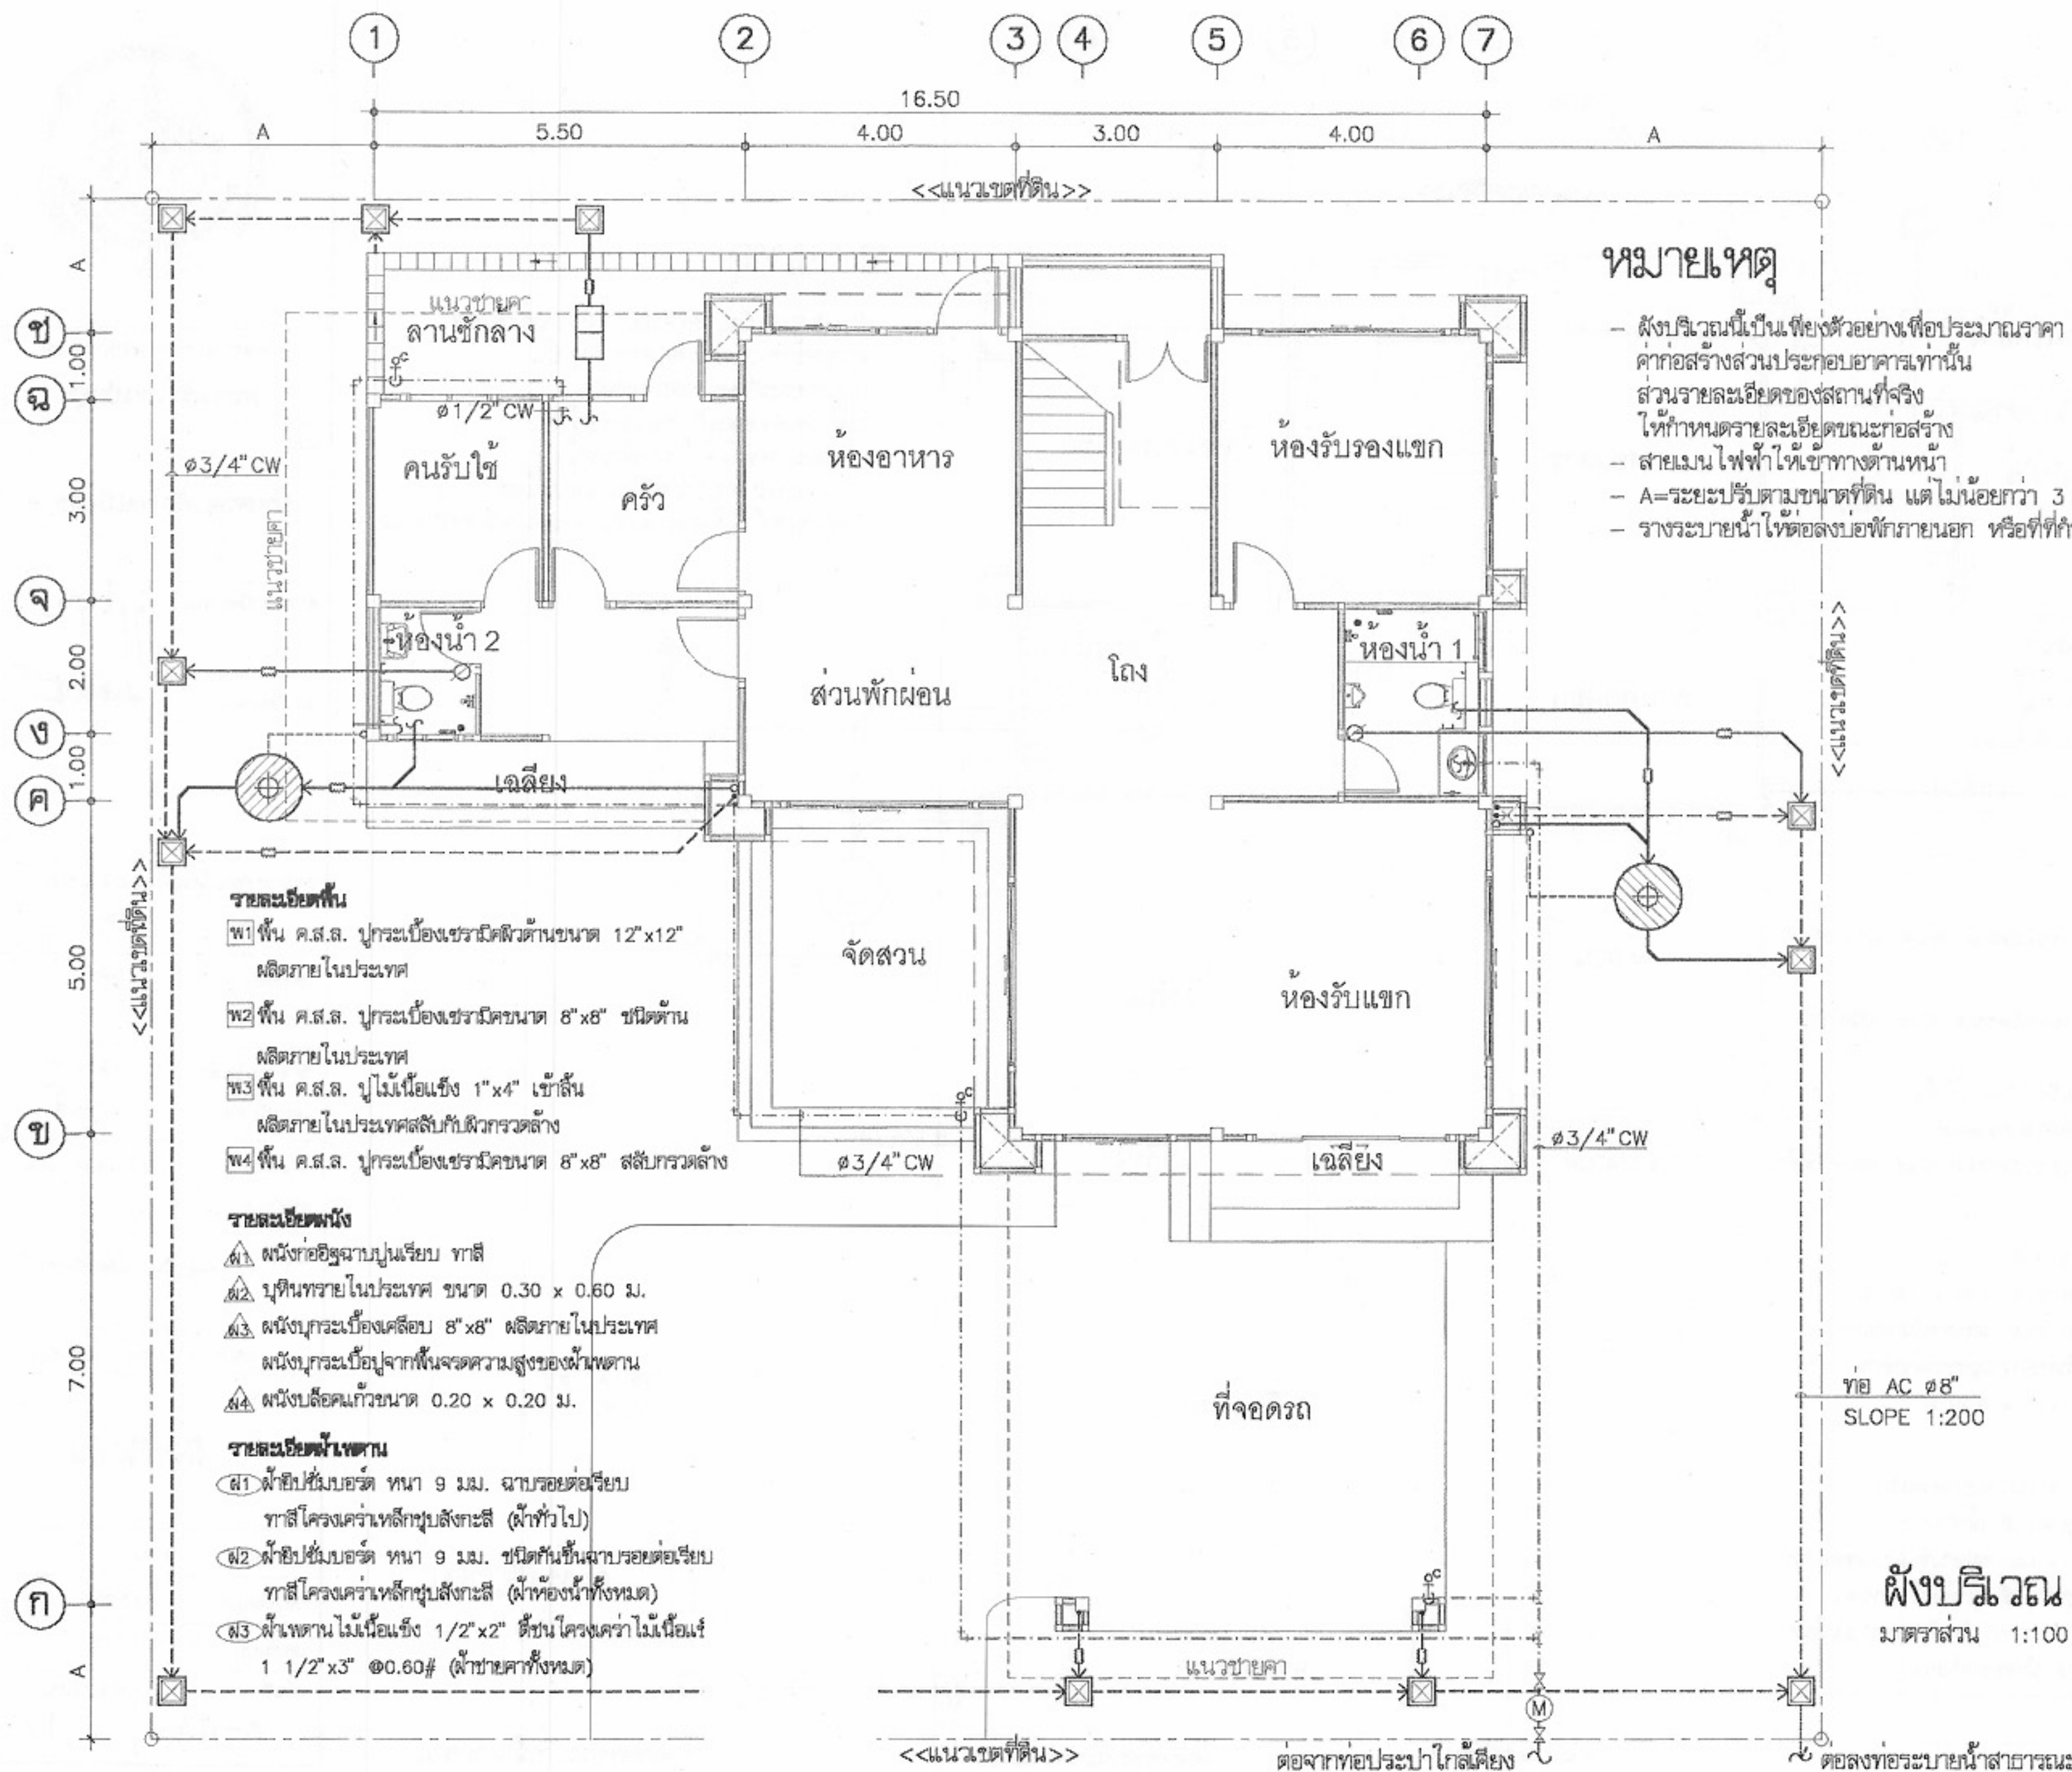

หมายเหตุ

- ผังบริเวณนี้เป็นเพียงตัวอย่างเพื่อประมาณราคา
- ค่าก่อสร้างส่วนประกอบอาคารเท่านั้น
- ส่วนรายละเอียดของสถานที่จริง
- ให้กำหนดรายละเอียดขณะก่อสร้าง
- สายเมนไฟฟ้าให้เข้าทางด้านหน้า
- A=ระยะปรับตามขนาดที่ดิน แต่ไม่น้อยกว่า 3 ม.
- รางระบายน้ำให้ต่อลงบ่อพักภายนอก หรือที่ที่กำหนดให้



โครงการแบบอาคารเพื่อประชาชน

ครอบครัวไทยเป็นสุข

แบบ

บ้านครอบครัวไทยเป็นสุข 8

สำนักสถาปัตยกรรม

77-7-
ผู้อำนวยการสำนัก

สถาปนิก

สถาปนิก

สถาปนิก

สถาปนิก

สถาปนิก

สถาปนิก

สำนักวิศวกรรม โครงสร้างและงานระบบ

ผู้อำนวยการสำนัก

วิศวกรรม

วิศวกร

โครงสร้าง

วิศวกร

วิศวกรรมไฟฟ้า

วิศวกร

และเครื่องกล

วิศวกร

วิศวกรรม

วิศวกร

สุขาภิบาล

วิศวกร

อนุมัติ

(นายสว่าง ศรีสุกัน)

อธิบดีกรมโยธาธิการและผังเมือง

แสดงแบบ

ผังบริเวณ

มาตราส่วน

1:100

วัน/เดือน/ปี

21 พ.ย. 2546

เลขที่แบบ

ม.บ.462126



แผ่นที่

จำนวนแผ่น

A-03

17

หมายเหตุ แบบที่แสดงอยู่นี้ได้รับการยืมส่วน เพื่อใช้แสดงผลทางหน้าจอเท่านั้น สำหรับแบบที่ใช้ขออนุญาตก่อสร้าง ให้ถ่ายสำเนาจากหนังสือแบบบ้าน

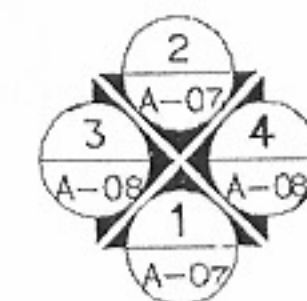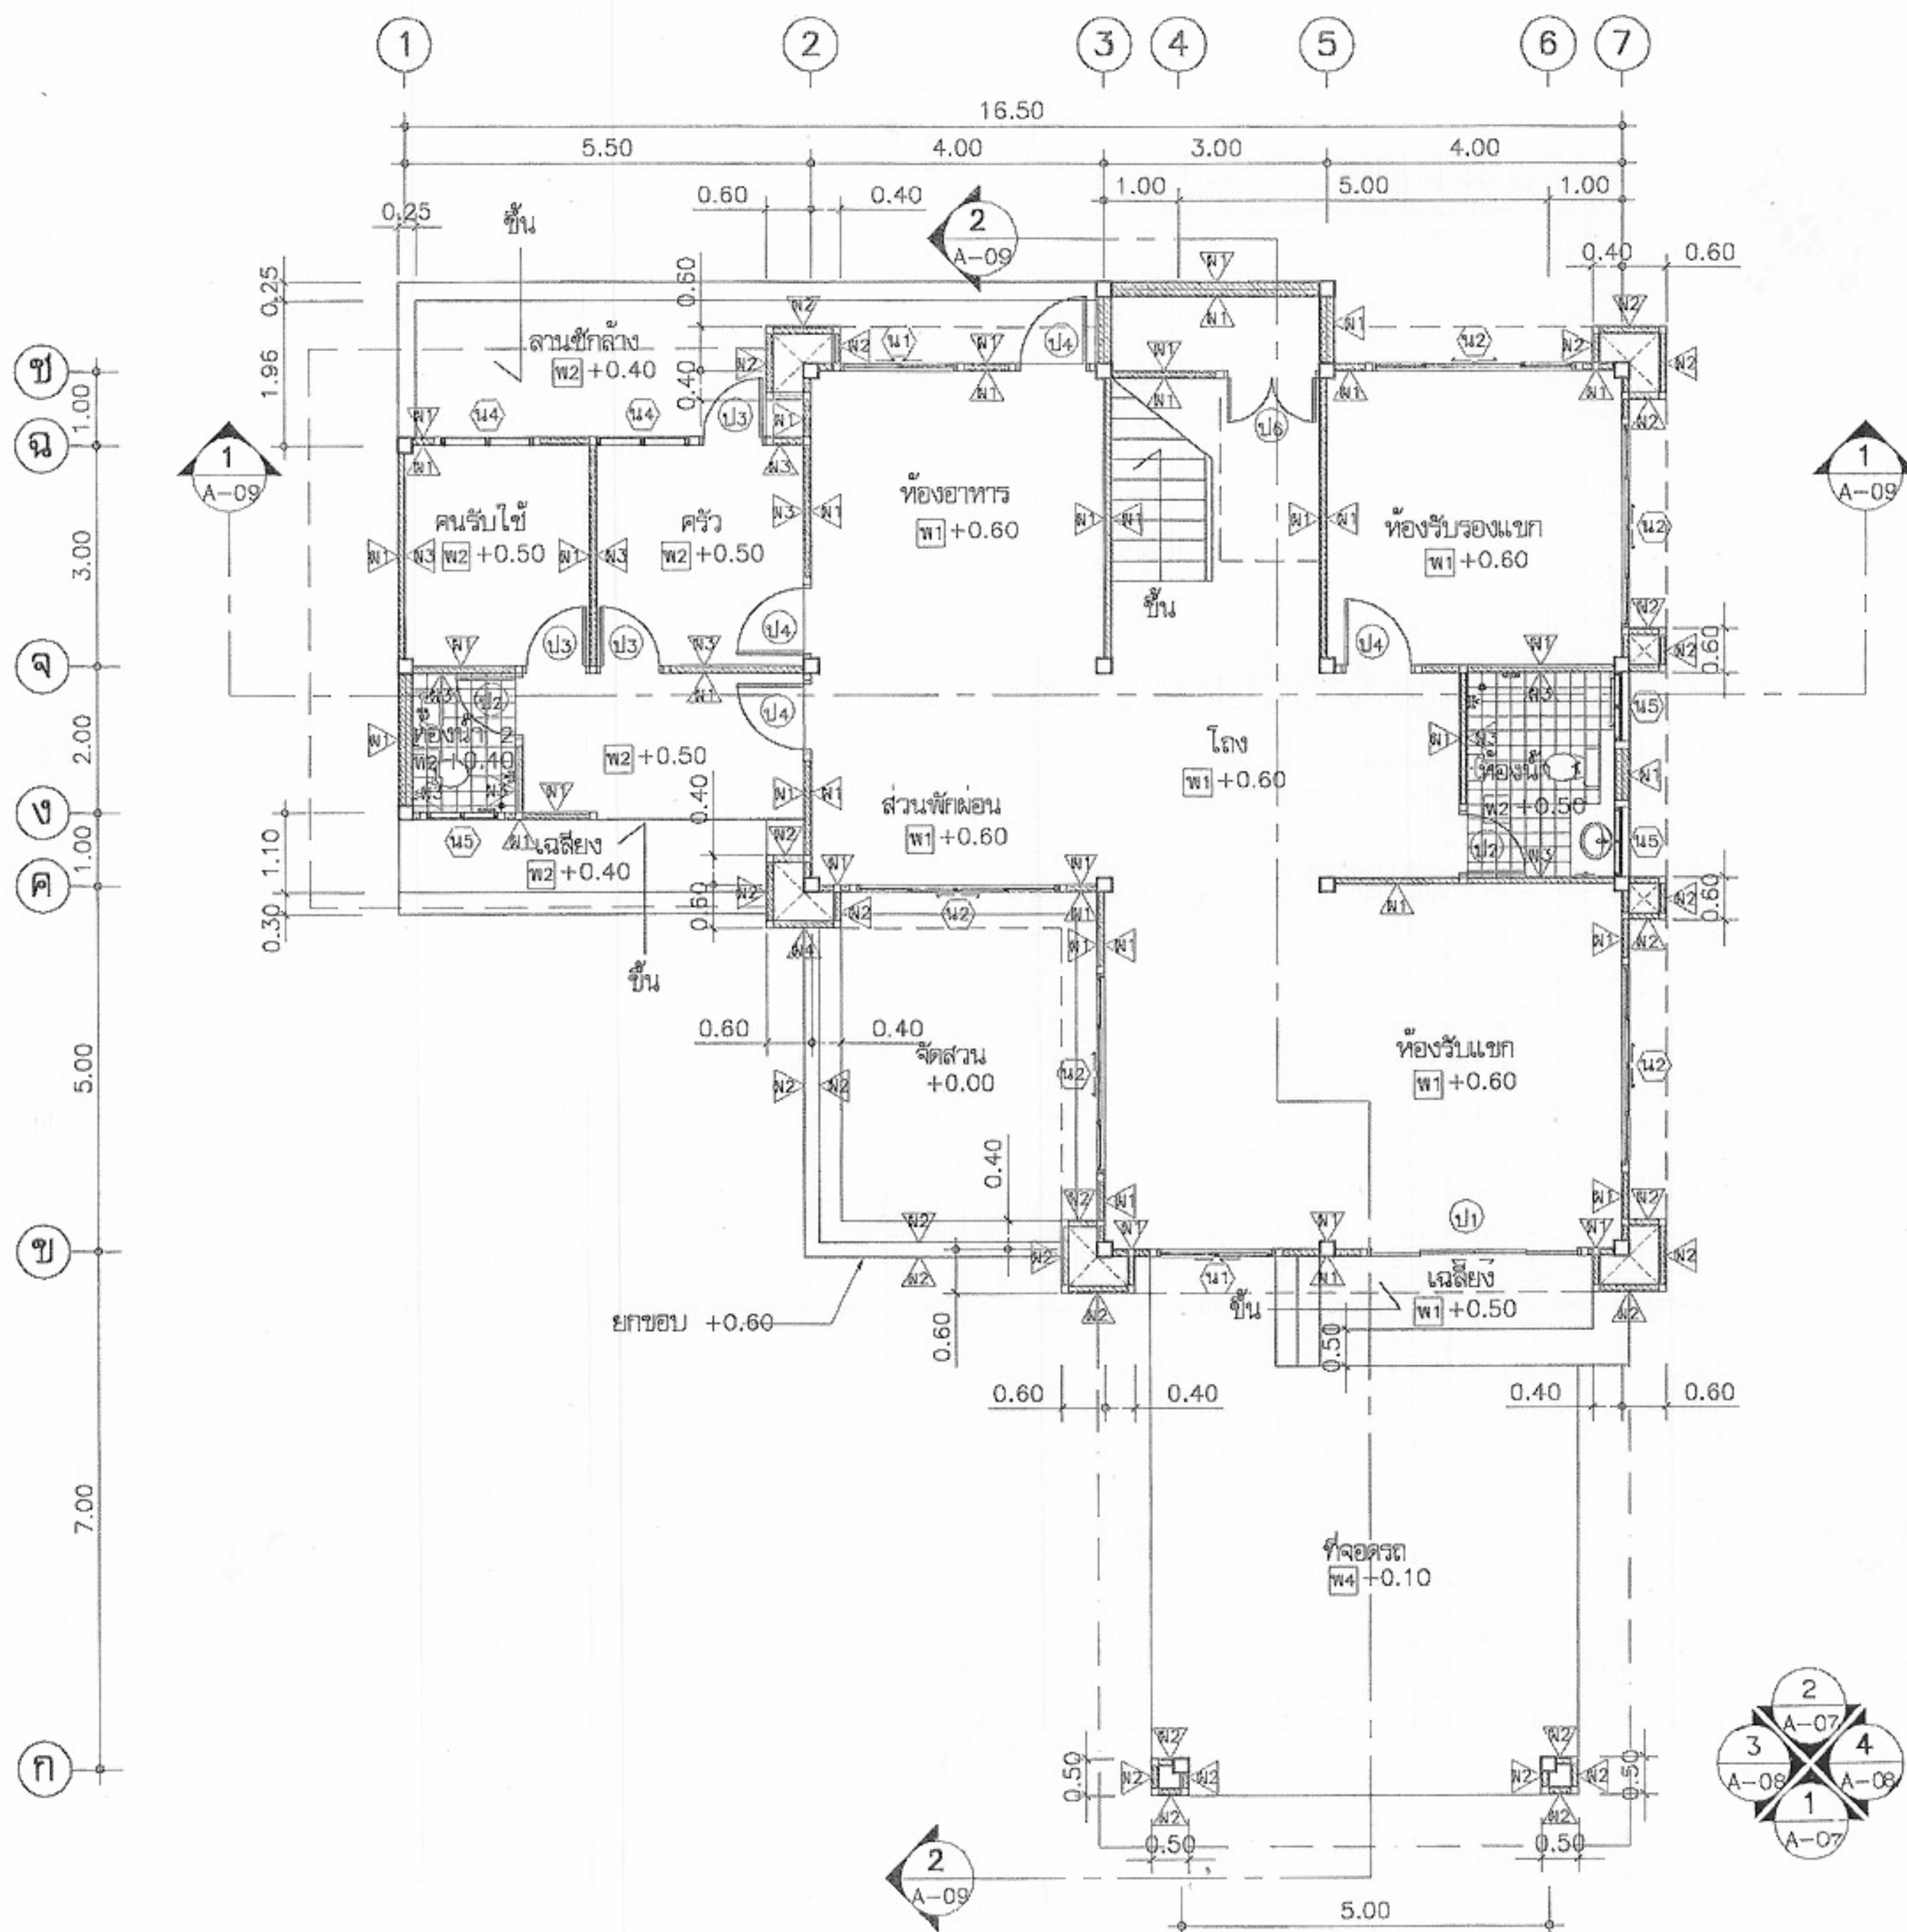

แปลนพื้นที่ชั้นล่าง
มาตราส่วน 1:100



โครงการแบบอาคารเพื่อประชาชน
ครอบครัวไทยเป็นสุข

แบบ
บ้านครอบครัวไทยเป็นสุข 8

สำนักสถาปัตยกรรม
ผู้ควบคุมการก่อสร้าง

สถาปัตยกรรม
ผู้ควบคุมการก่อสร้าง

สำนักวิศวกรรมโครงสร้างและงานระบบ
ผู้ควบคุมการก่อสร้าง

วิศวกรรม
โครงสร้าง

วิศวกรรมไฟฟ้า
และเครื่องกล

วิศวกรรม
สุขาภิบาล

อนุมัติ
(นายสว่าง ศรีสุกัน)
อธิบดีกรมโยธาธิการและผังเมือง



แสดงแบบ
แปลนพื้นที่ชั้นล่าง

มาตราส่วน 1:100
วัน/เดือน/ปี 21 พ.ย. 2546

เลขที่แบบ ม.บ.462126
แผ่นที่ จำนวนแผ่น

A-04 17

หมายเหตุ แบบที่แสดงอยู่นี้ได้รับการยืมส่วน เพื่อใช้แสดงผลทางหน้าจอเท่านั้น สำหรับแบบที่ใช้ขออนุญาตก่อสร้าง ให้ถ่ายสำเนาจากหนังสือแบบบ้าน

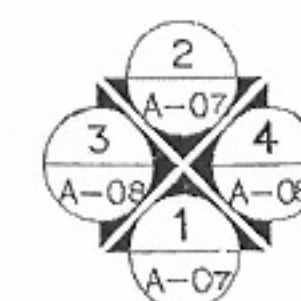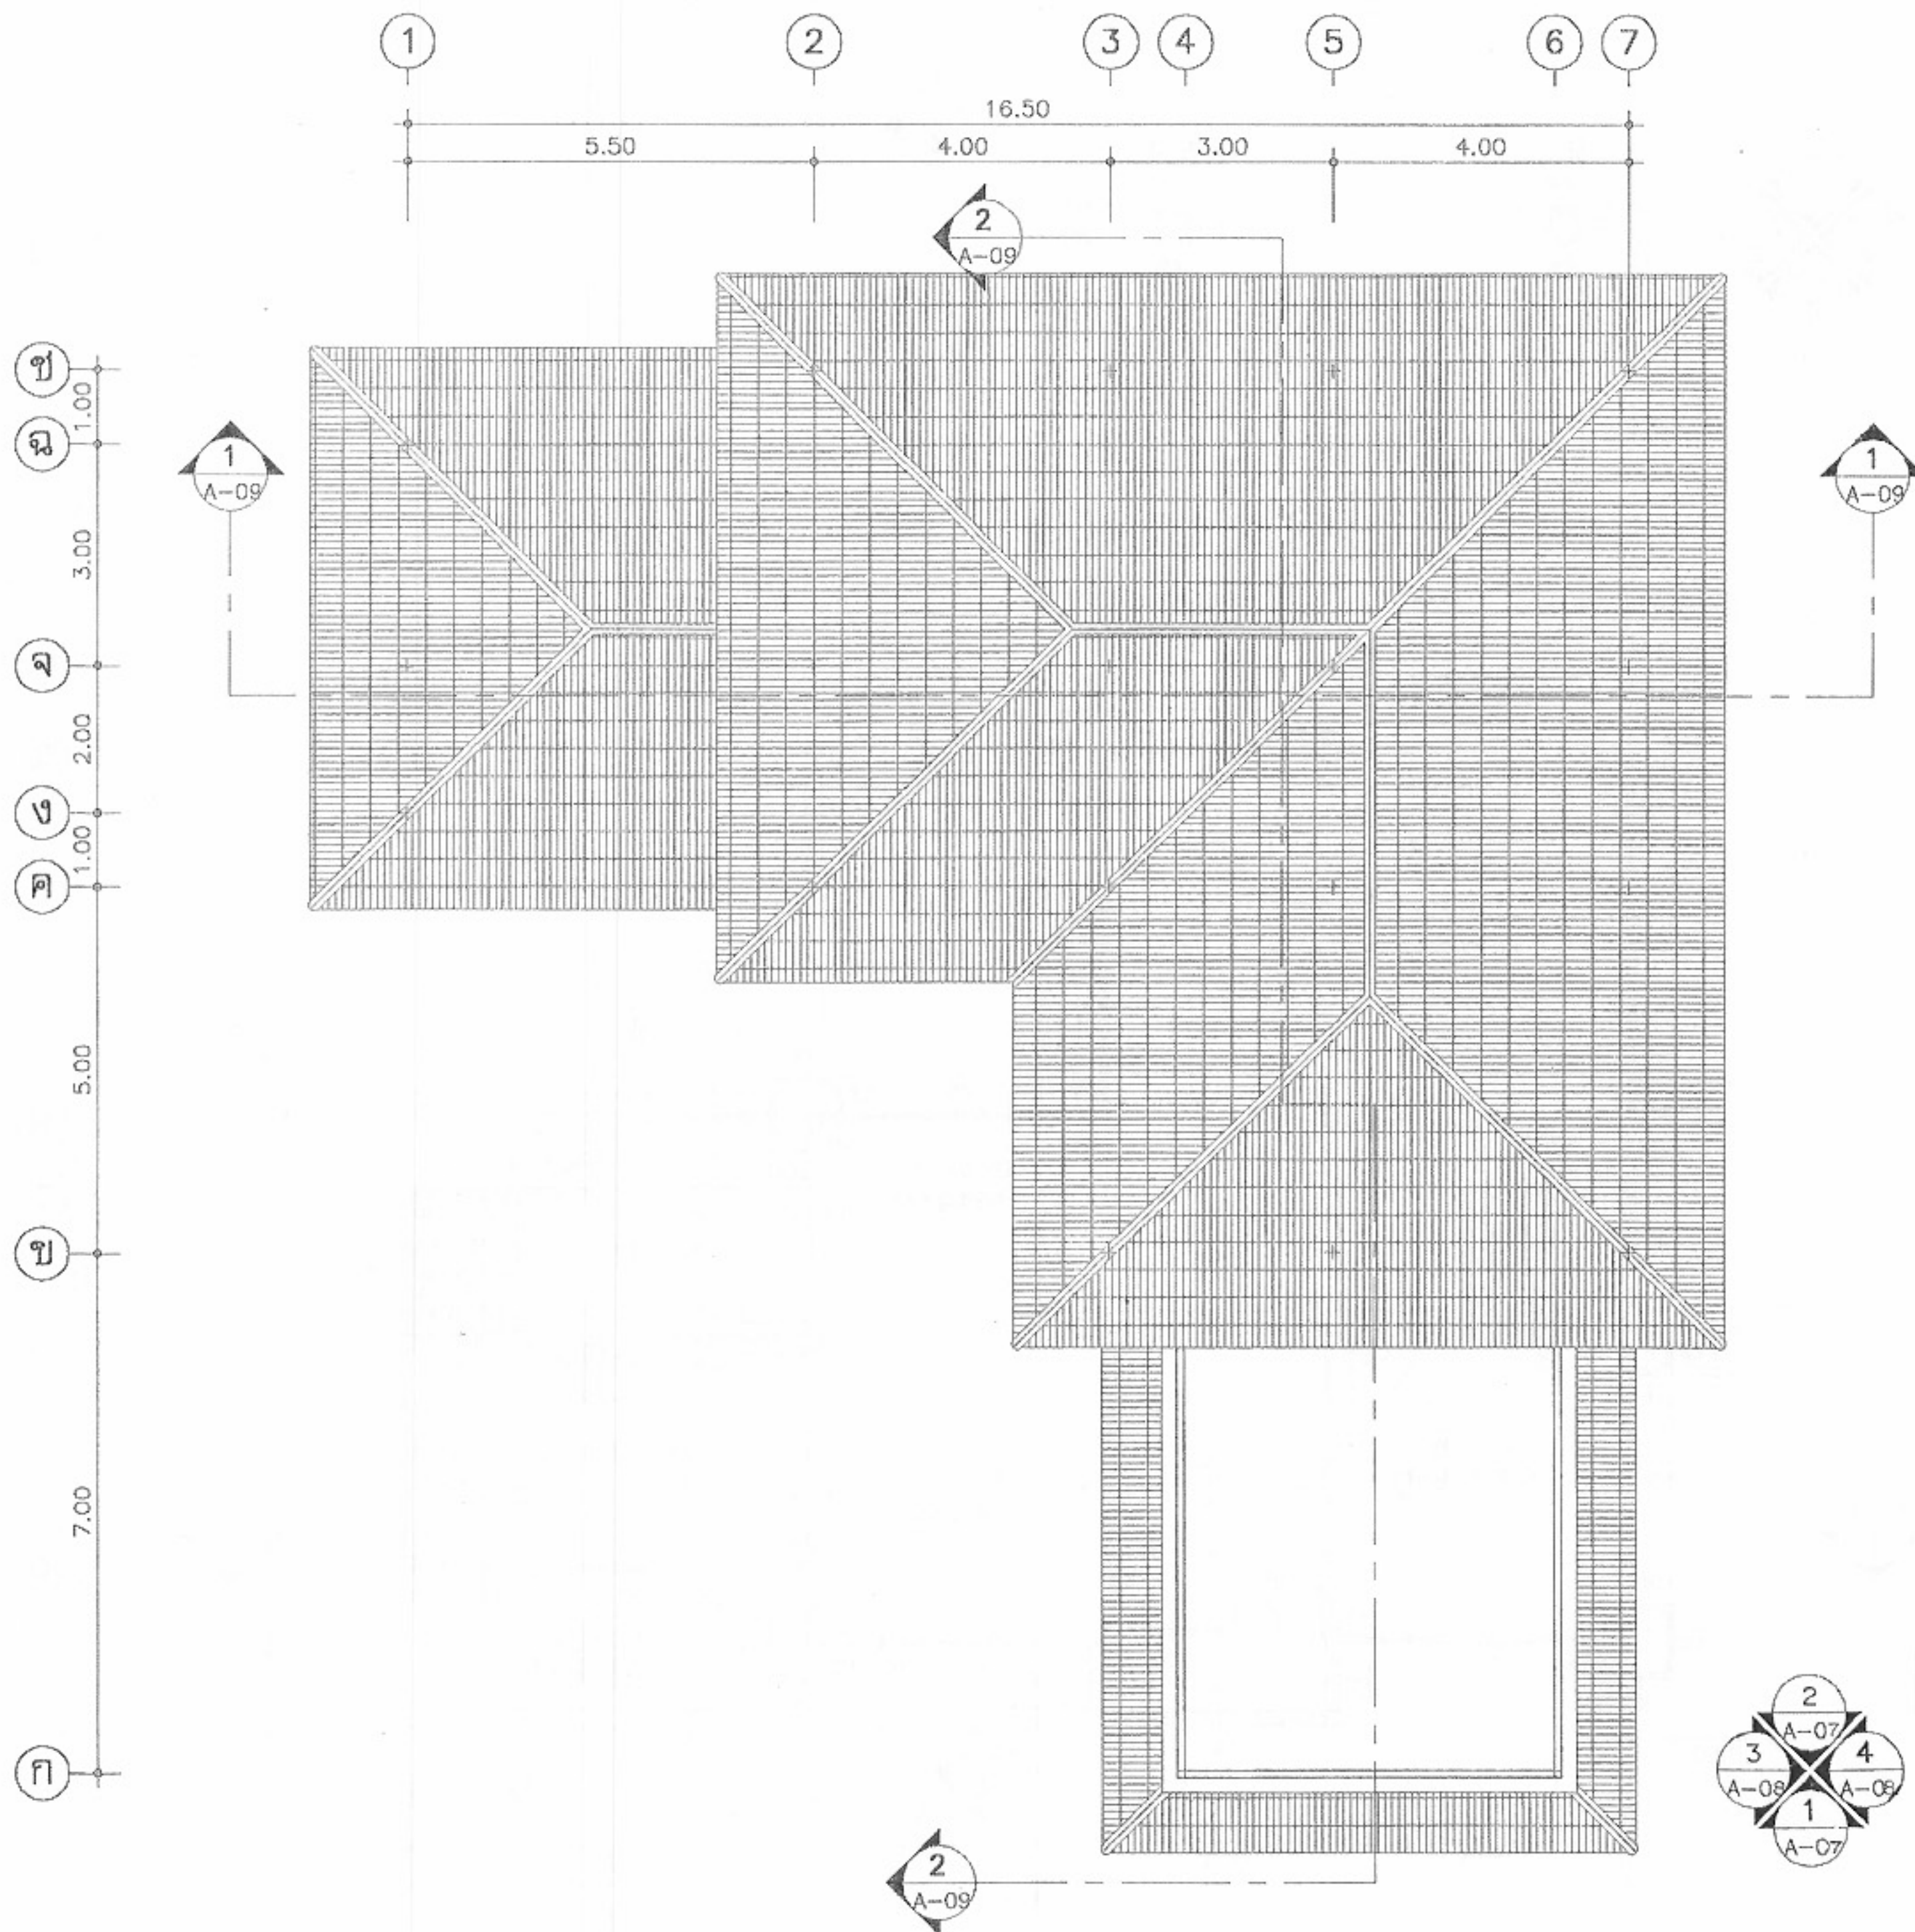

แปลนหลังคา
มาตราส่วน 1:100



โครงการแบบอาคารเพื่อประชาชน
ครอบครัวไทยเป็นสุข

แบบ
บ้านครอบครัวไทยเป็นสุข 8

สำนักสถาปัตยกรรม
ก.ก.ก. ผู้อำนวยการสำนัก

สถาปัตยกรรม		สถาปนิก
		สถาปนิก
		สถาปนิก
		สถาปนิก

สำนักวิศวกรรมโครงสร้างและระบบ
อ.อ. ผู้อำนวยการสำนัก

วิศวกรรม	ว.ว.	วิศวกร
โครงสร้าง		วิศวกร
วิศวกรรมไฟฟ้า	อ.พ.ร.	วิศวกร
และเครื่องกล		วิศวกร
วิศวกรรม	ป.ว.อ.	วิศวกร
สุขาภิบาล		วิศวกร

อนุมัติ

(นายสว่าง ศิริสุนทร)
อธิบดีกรมโยธาธิการและผังเมือง

แสดงแบบ
แปลนหลังคา

มาตราส่วน 1:100

วัน/เดือน/ปี 21 พ.ย. 2546

เลขที่แบบ ม.บ.462126

แผ่นที่ A-06	จำนวนแผ่น 17
-----------------	-----------------

หมายเหตุ แบบที่แสดงอยู่นี้ได้รับการยืมส่วน เพื่อใช้แสดงผลทางหน้าจอเท่านั้น สำหรับแบบที่ใช้ขออนุญาตก่อสร้าง ให้ถ่ายสำเนาจากหนังสือแบบบ้าน



รูปด้าน 1
มาตราส่วน 1:100



รูปด้าน 2
มาตราส่วน 1:100



โครงการแบบอาคารเพื่อประชาชน
ครอบครัวไทยเป็นสุข

แบบ
บ้านครอบครัวไทยเป็นสุข 8

สำนักสถาปัตยกรรม
ผู้ควบคุมการออกแบบ

สถาปนิก	สถาปนิก
สถาปนิก	สถาปนิก
สถาปนิก	สถาปนิก
สถาปนิก	สถาปนิก

สำนักวิศวกรรมโครงสร้างงานระบบ
ผู้ควบคุมการออกแบบ

วิศวกรรม	วิศวกร
โครงสร้าง	วิศวกร
วิศวกรรมไฟฟ้า	วิศวกร
และเครื่องกล	วิศวกร
วิศวกรรม	วิศวกร
สุขาภิบาล	วิศวกร

อนุมัติ
(นายสว่าง ศรีสุกัน)
อธิบดีกรมโยธาธิการและผังเมือง

แสดงแบบ
รูปด้าน 1,2

มาตราส่วน 1:100

วัน/เดือน/ปี 21 พ.ย. 2546

เลขที่แบบ ม.บ.462126

แผ่นที่	จำนวนแผ่น
A-07	17



รูปด้าน 3
มาตราส่วน 1:100



รูปด้าน 4
มาตราส่วน 1:100



โครงการแบบอาคารเพื่อประชาชน
ครอบครัวไทยเป็นสุข

แบบ
บ้านครอบครัวไทยเป็นสุข 8

สำนักสถาปัตยกรรม
ผู้ควบคุมการออกแบบ

สถาปัตยกรรม	สถาปนิก
	สถาปนิก
	สถาปนิก
	สถาปนิก

สำนักวิศวกรรมโครงสร้างและงานระบบ
ผู้ควบคุมการออกแบบ

วิศวกรรม	วิศวกร
โครงสร้าง	วิศวกร
วิศวกรรมไฟฟ้า	วิศวกร
และเครื่องกล	วิศวกร
วิศวกรรม	วิศวกร
สุขาภิบาล	วิศวกร

อนุมัติ
(นายสว่าง ศรีสกุล)
อธิบดีกรมโยธาธิการและผังเมือง



แสดงแบบ
รูปด้าน 3,4

มาตราส่วน 1:100

วัน/เดือน/ปี 21 พ.ย. 2546

เลขที่แบบ ม.บ.462126

แผ่นที่ A-08	จำนวนแผ่น 17
-----------------	-----------------

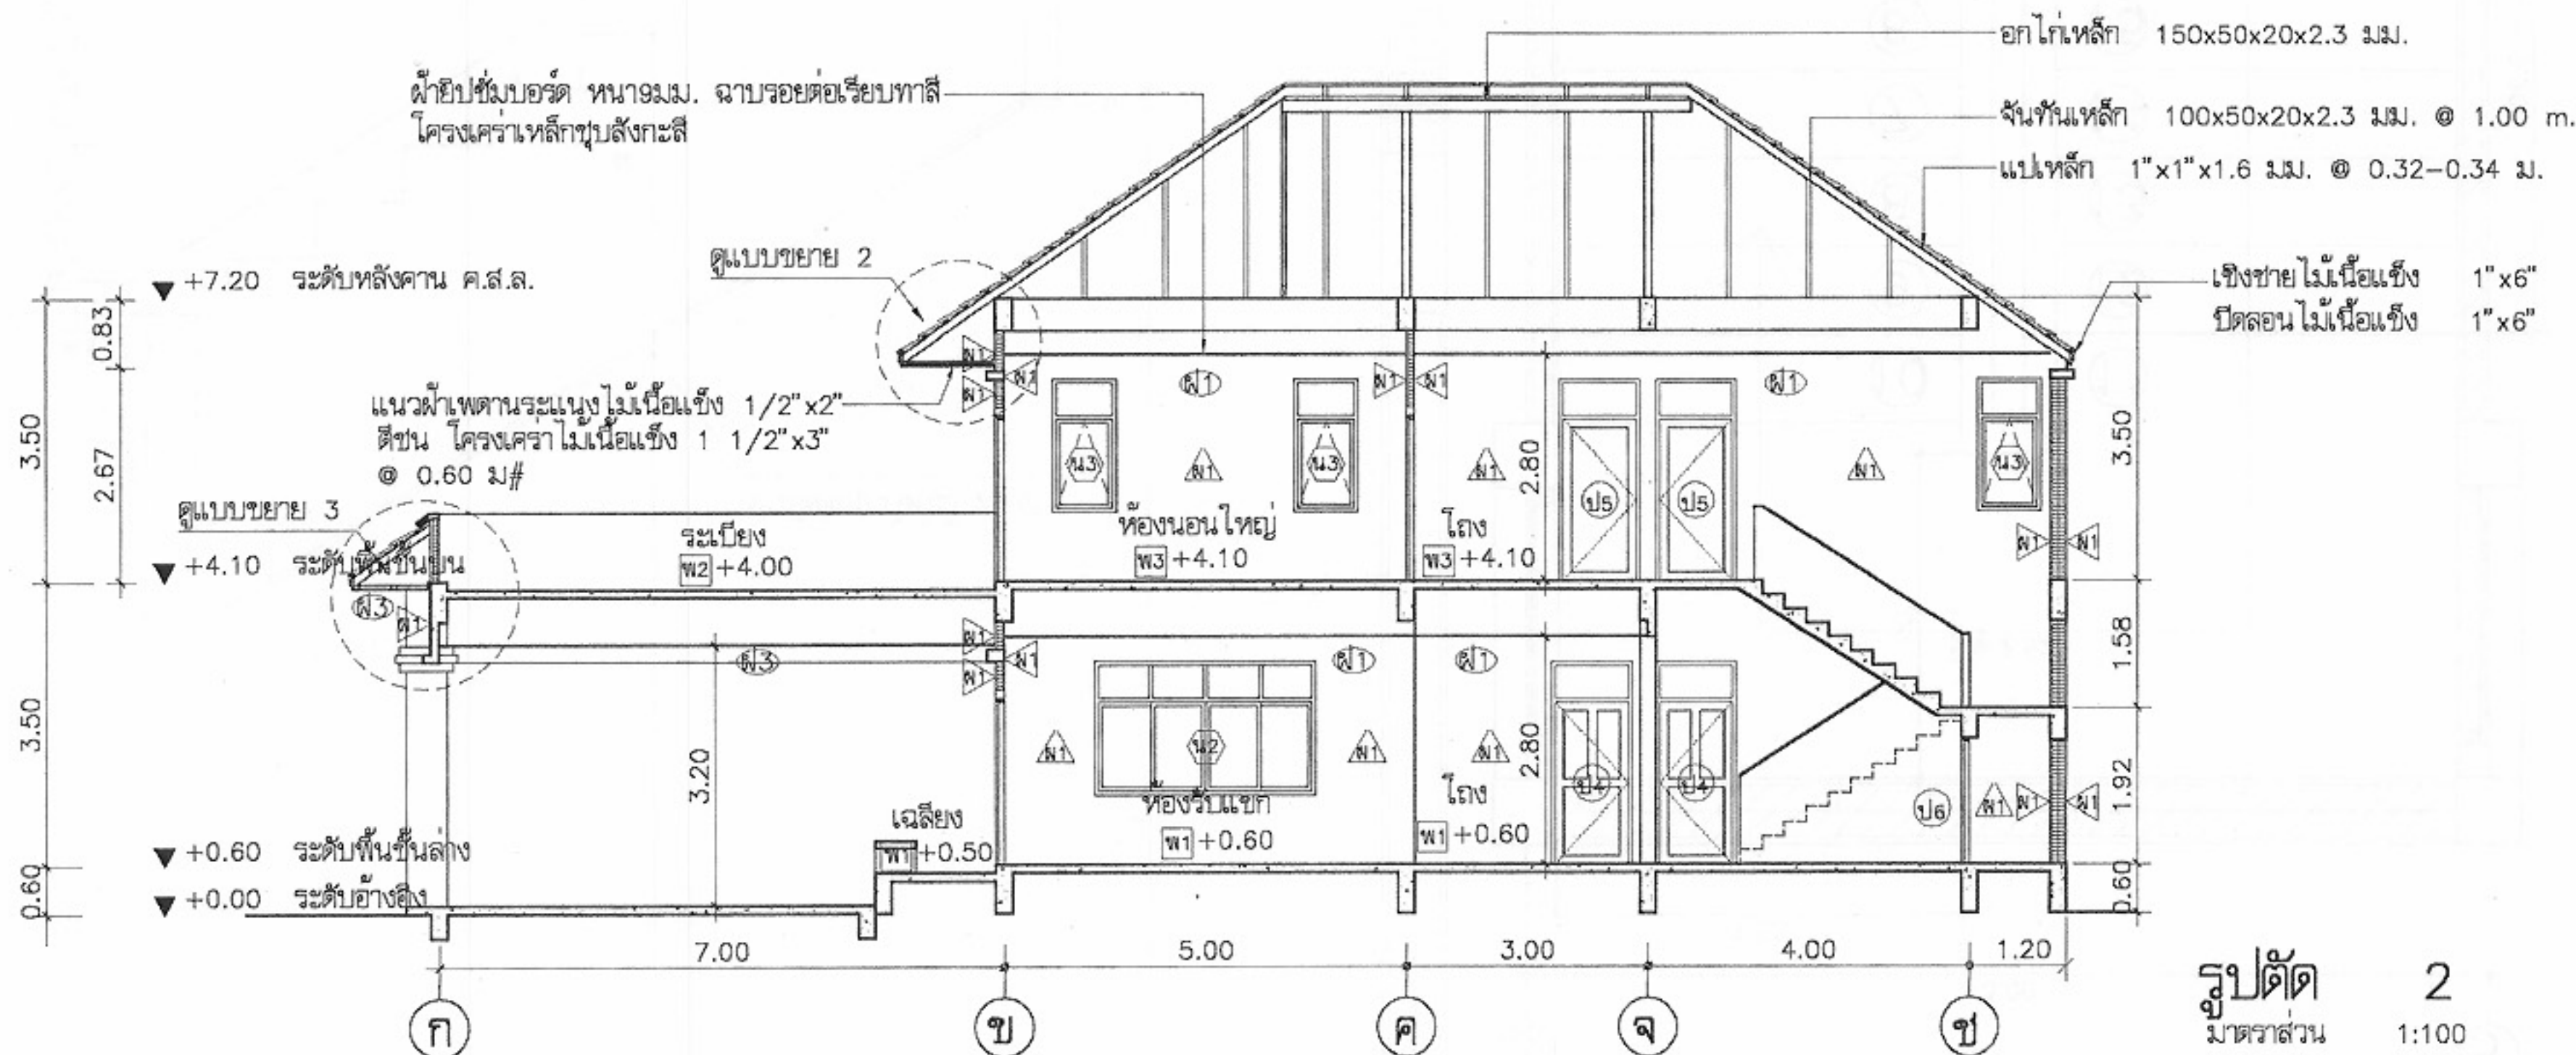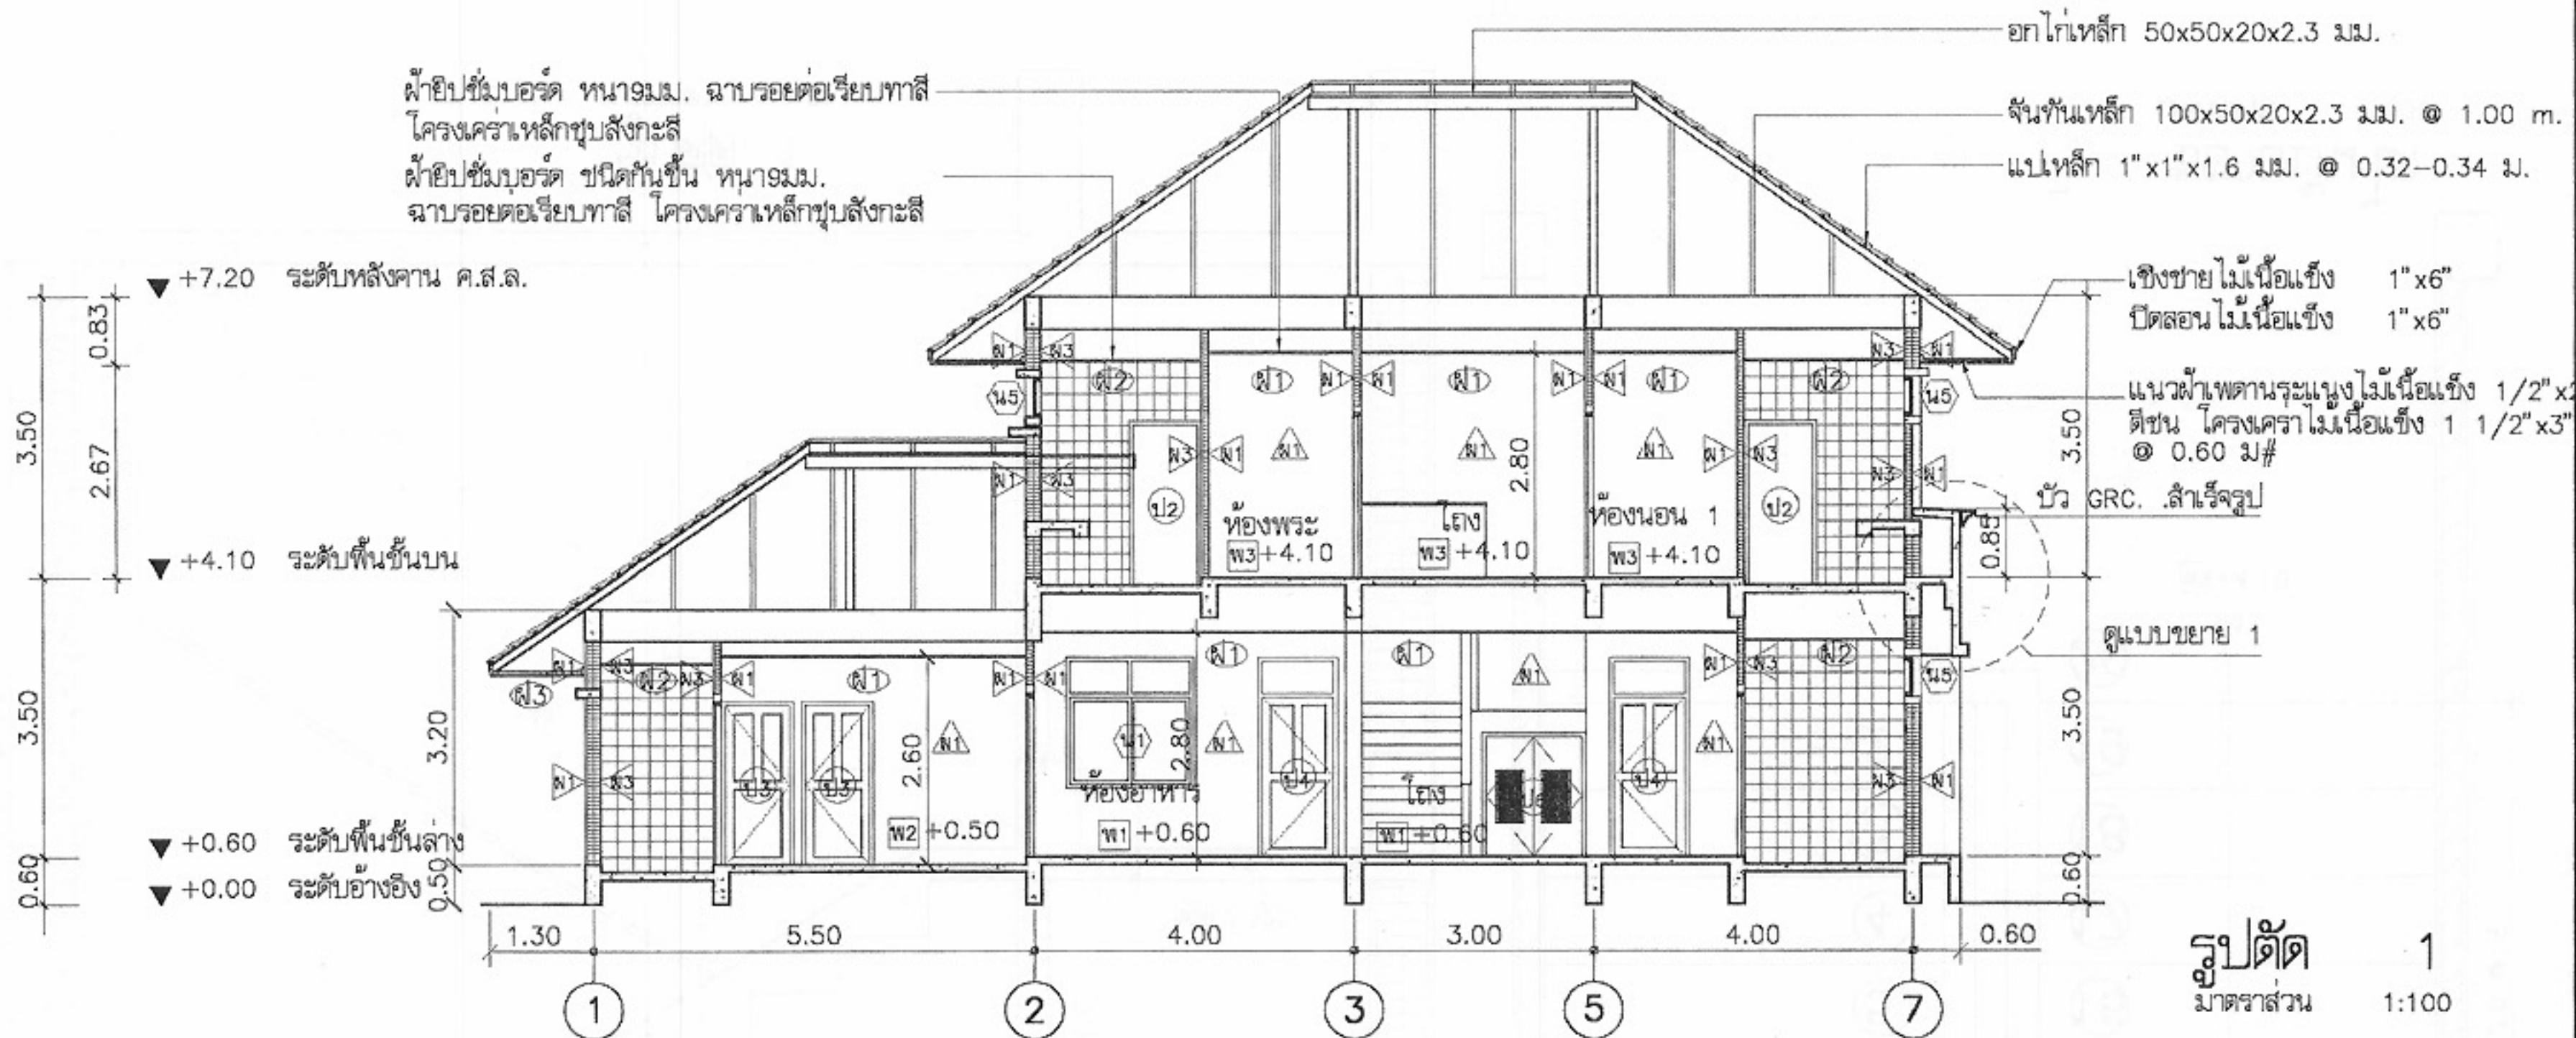

โครงการแบบอาคารเพื่อประชาชน
ครอบครัวไทยเป็นสุข

แบบ
บ้านครอบครัวไทยเป็นสุข 8

สำนักสถาปัตย์กรรม
 777-
 ผู้อำนวยการสำนัก

สถาปัตย์กรรม	สถาปนิก
	สถาปนิก
	สถาปนิก
	สถาปนิก

สำนักวิศวกรรมโครงสร้างและงานระบบ
 ผู้อำนวยการสำนัก


วิศวกรรม	วิศวกร
โครงสร้าง	วิศวกร
วิศวกรรมไฟฟ้า	วิศวกร
และเครื่องกล	วิศวกร
วิศวกรรม	วิศวกร
สุขาภิบาล	วิศวกร

อนุมัติ
 (นายสว่าง ศรีสุกัน)
 อธิบดีกรมโยธาธิการและผังเมือง



แสดงแบบ
รูปตัด 1,2

มาตรฐาน	1:100
วัน/เดือน/ปี	21 พ.ย. 2546
เลขที่แบบ	ม.บ.462126
แผ่นที่	จำนวนแผ่น
A-09	17

หมายเหตุ แบบที่แสดงอยู่นี้ได้รับการยืมส่วน เพื่อใช้แสดงผลทางหน้าจอเท่านั้น สำหรับแบบที่ใช้ขออนุญาตก่อสร้าง ให้ถ่ายสำเนาจากหนังสือแบบบ้าน

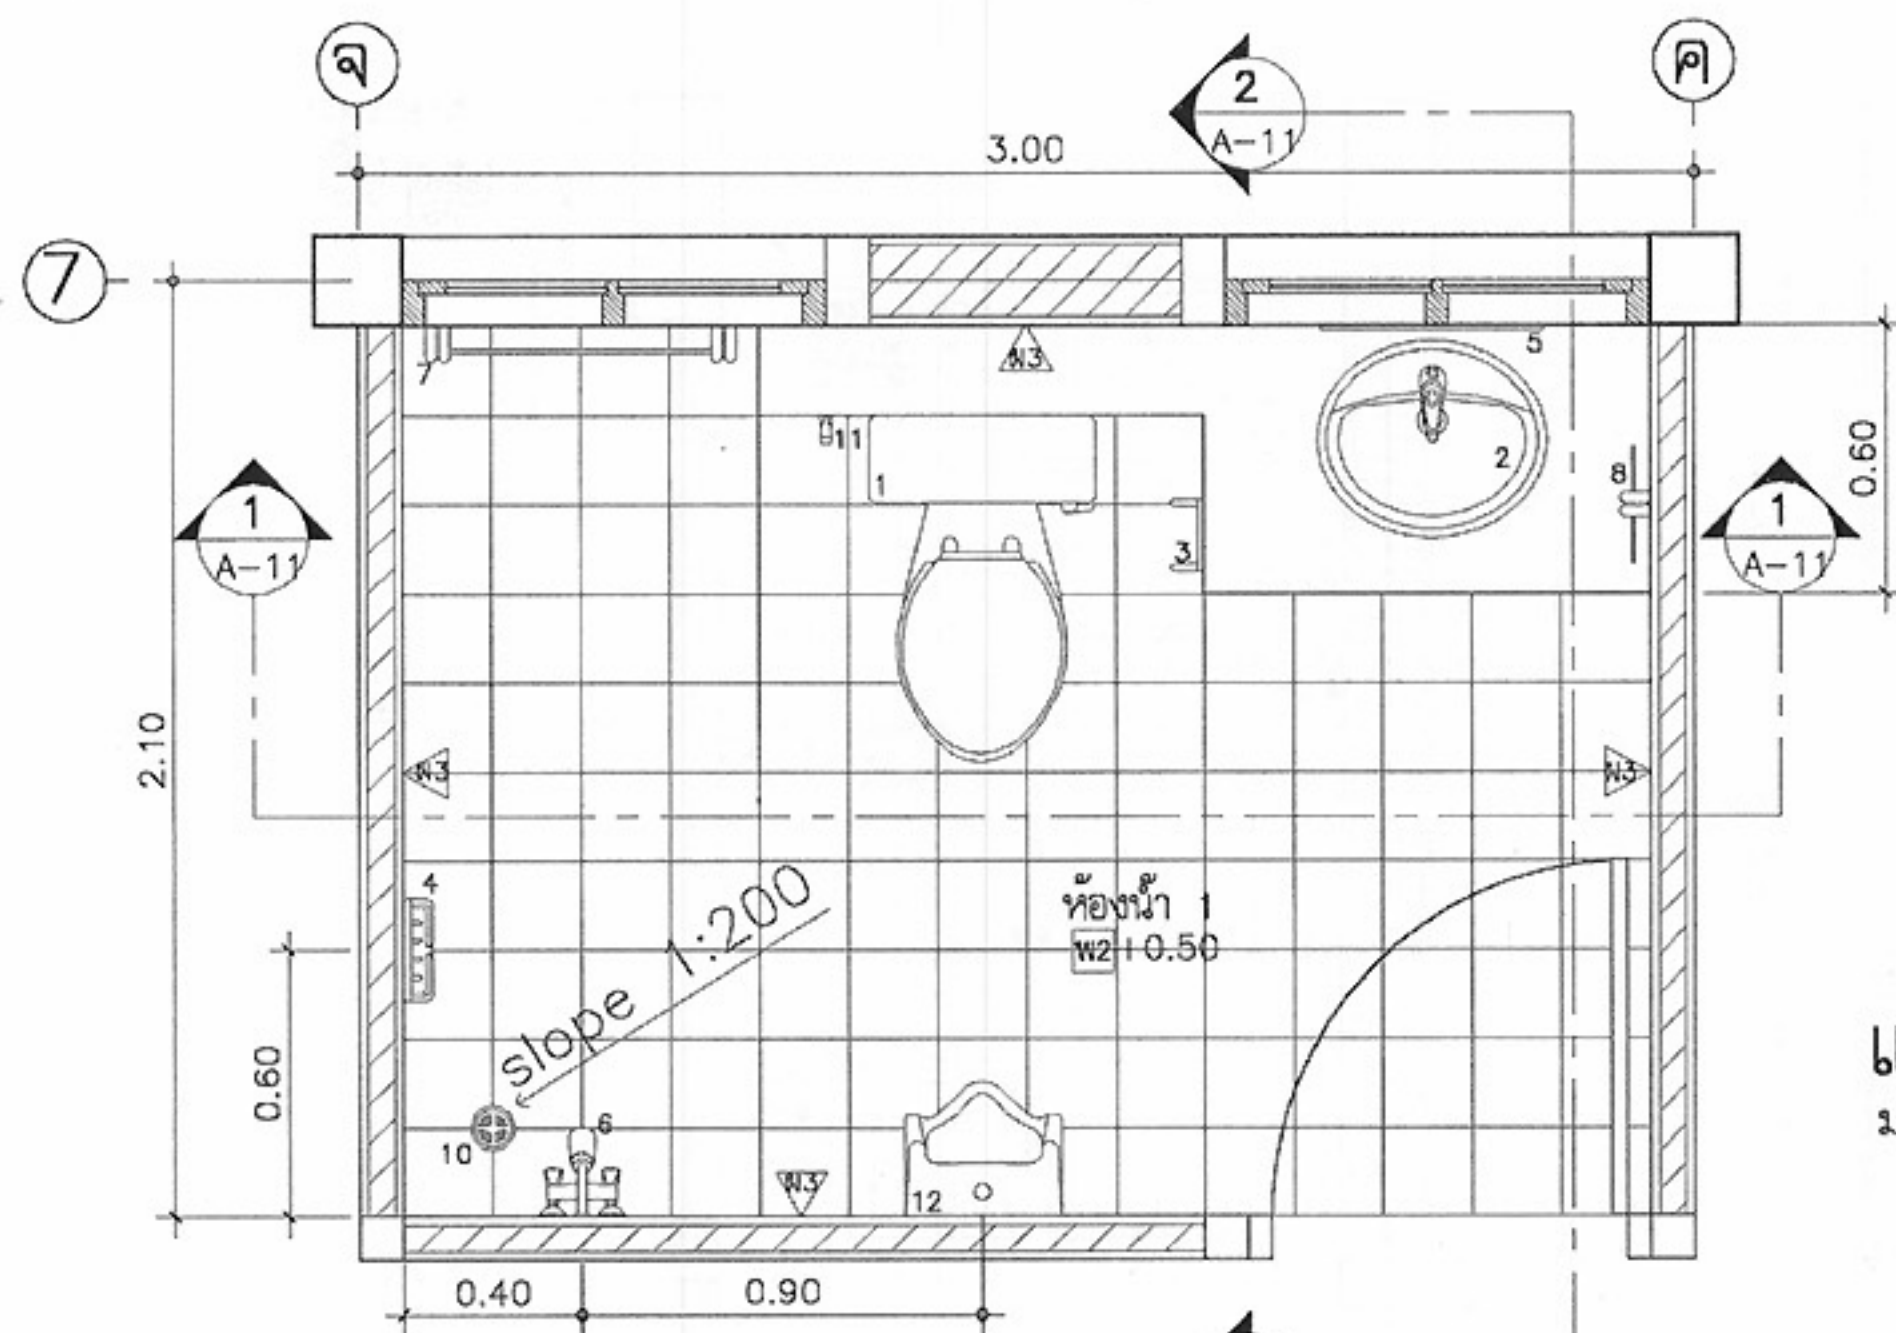

แบบขยายห้องน้ำ 1
มาตราส่วน 1:25

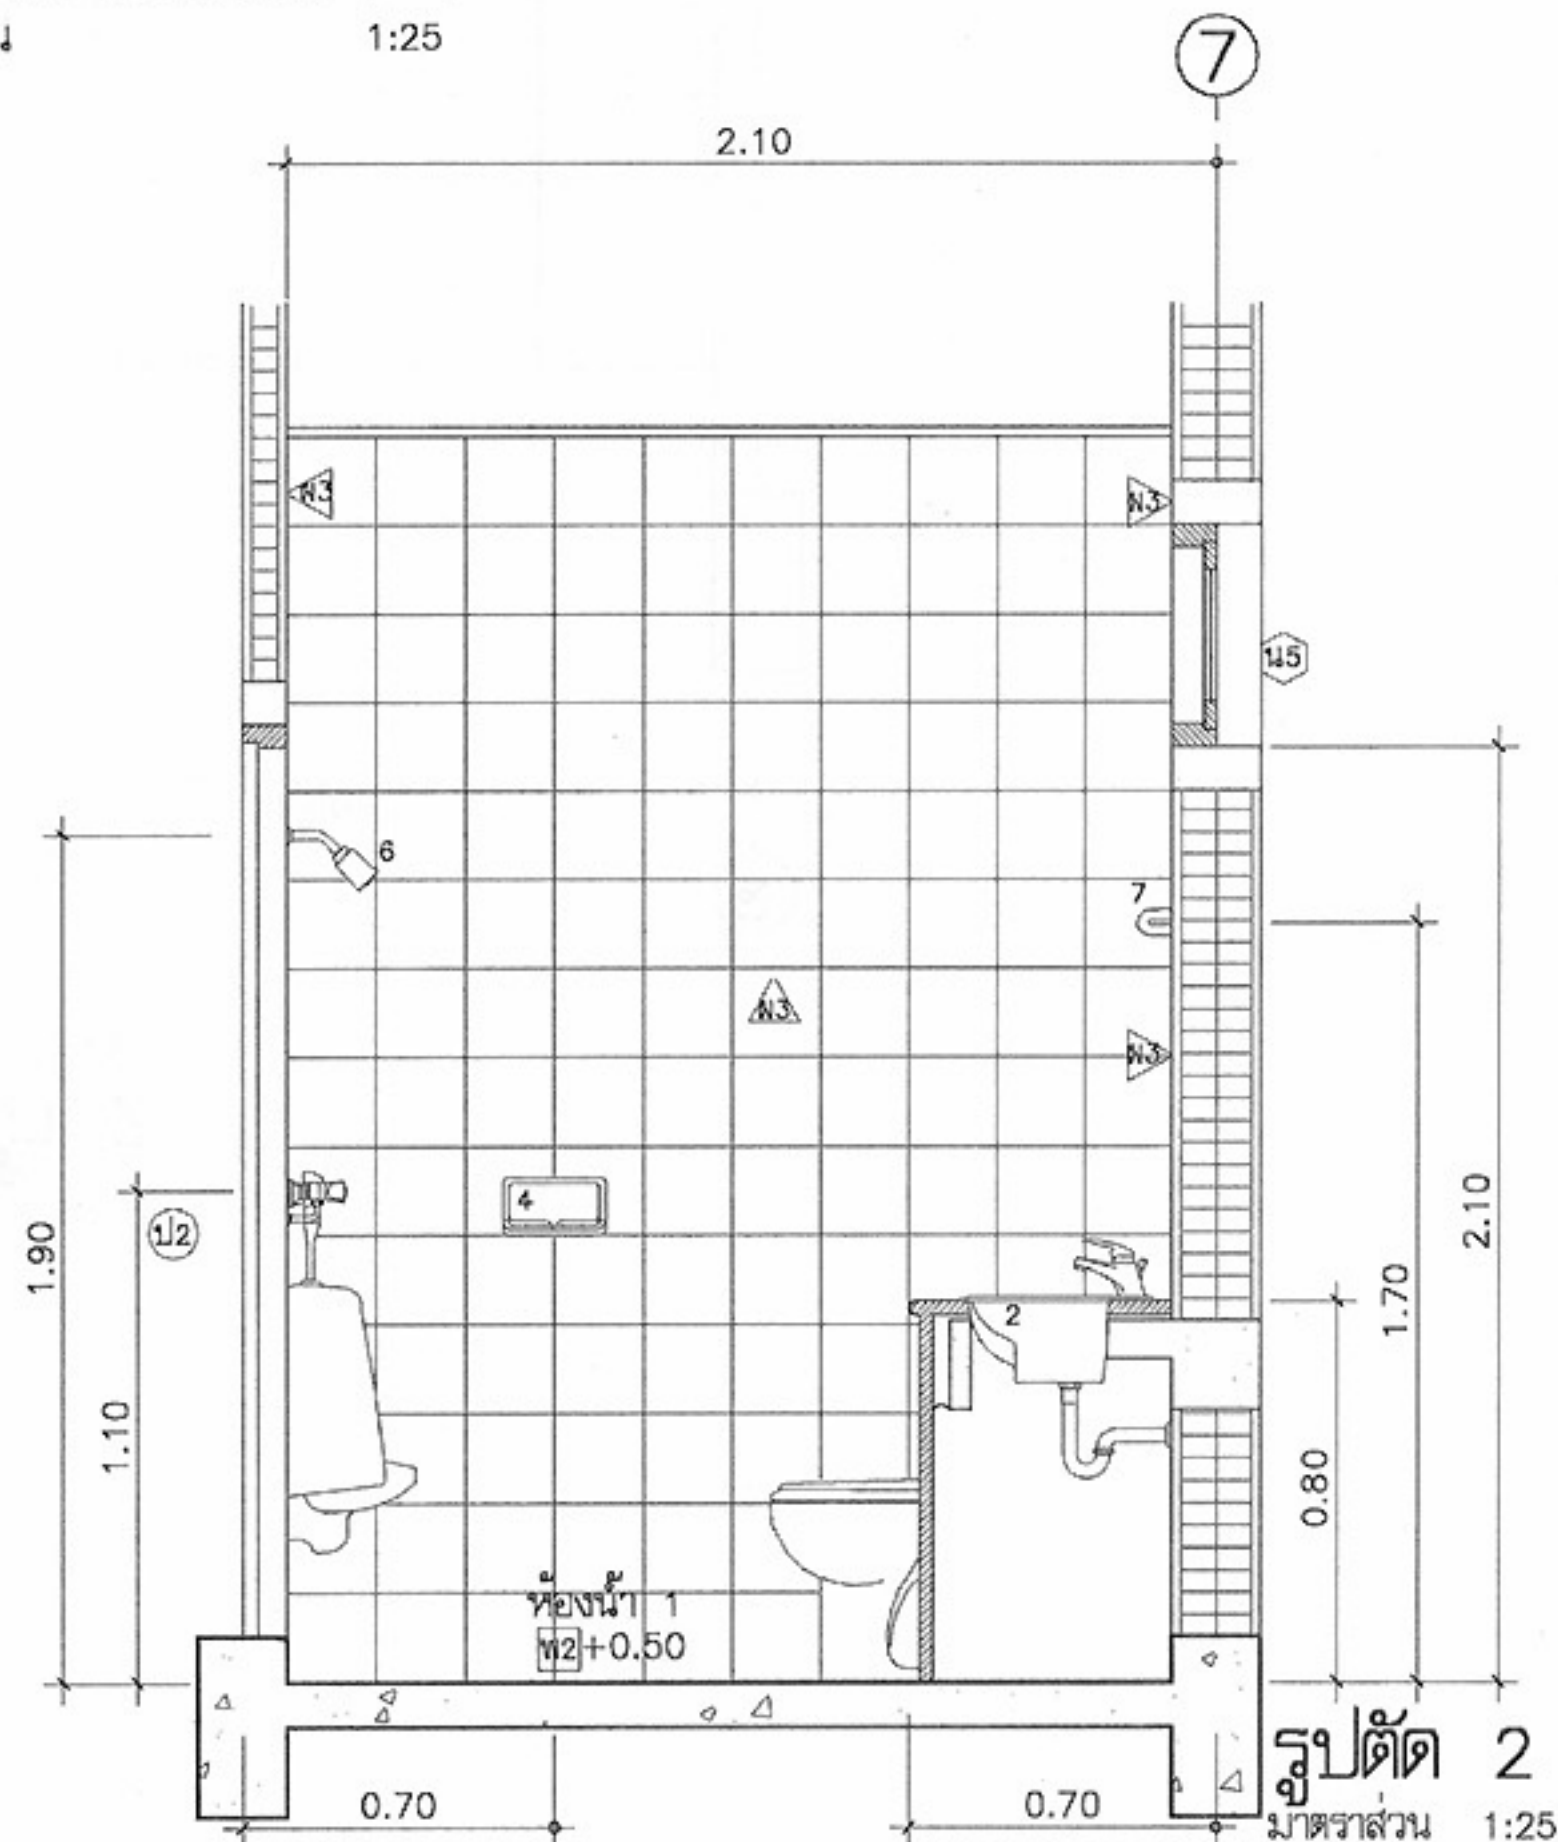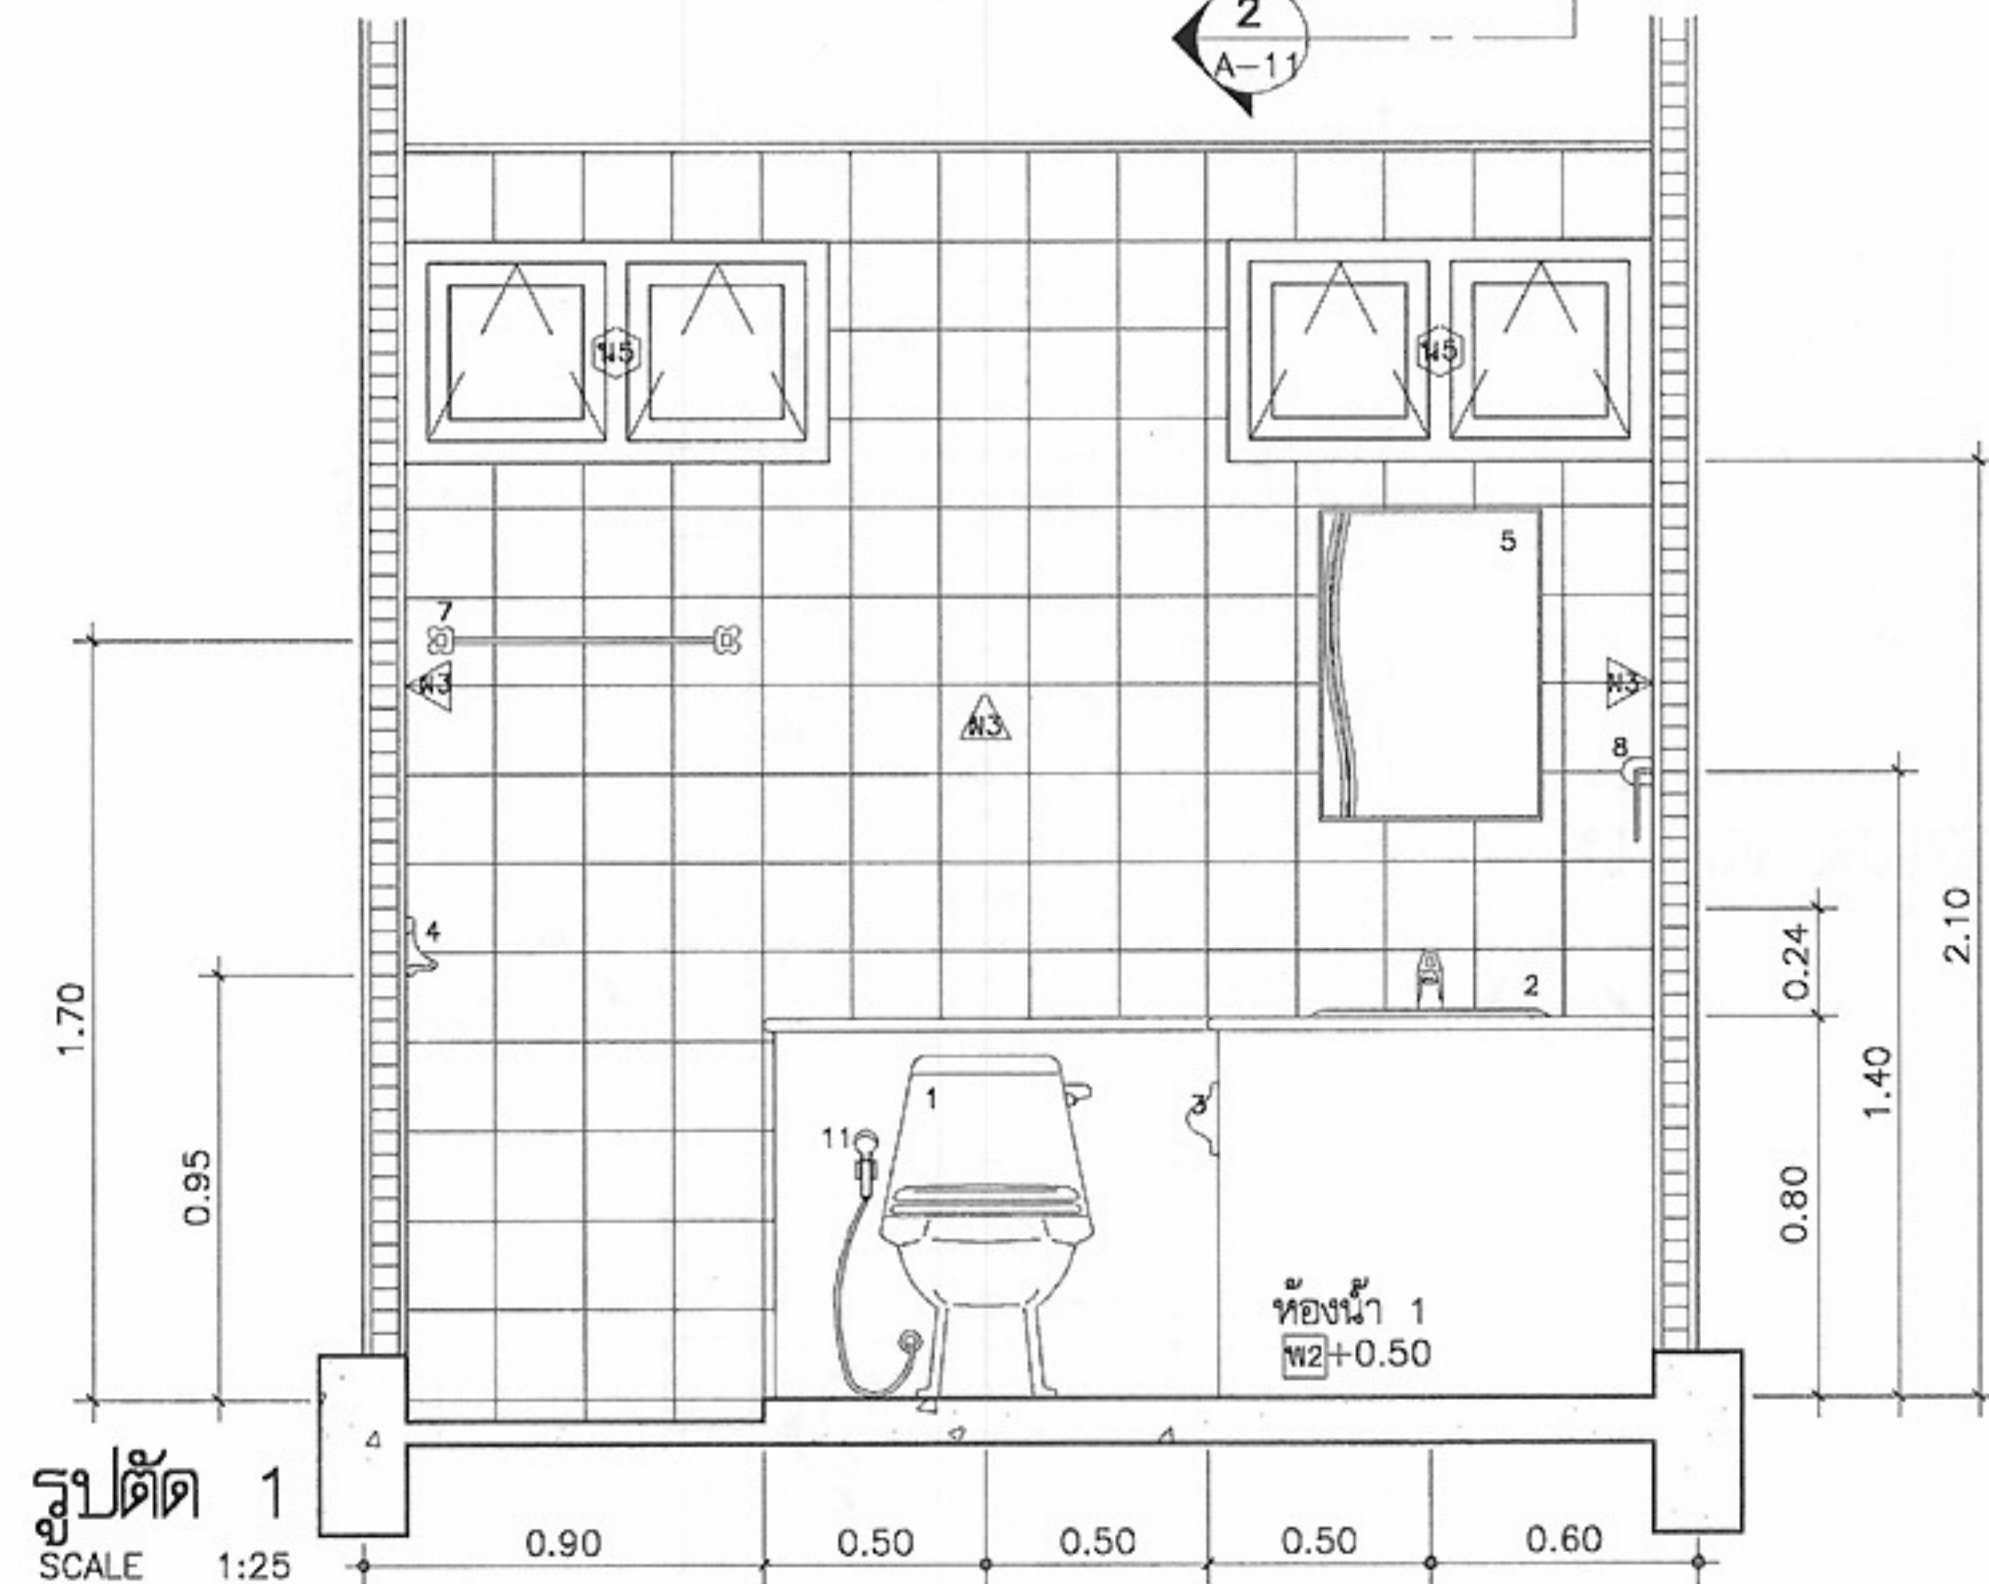

โครงการแบบอาคารเพื่อประชาชน
ครอบครัวไทยเป็นสุข

แบบ
บ้านครอบครัวไทยเป็นสุข 8

สำนักสถาปัตยกรรม
ผู้ควบคุมการออกแบบ

สถาปนิก
สถาปนิก
สถาปนิก
สถาปนิก

สำนักวิศวกรรมโครงสร้างและงานระบบ
ผู้ควบคุมการออกแบบ

วิศวกรรม
โครงสร้าง
วิศวกรรมไฟฟ้า
และเครื่องกล
วิศวกรรม
สุขาภิบาล

อนุมัติ
(นายสว่าง ศรีสุกัน)
อธิบดีกรมโยธาธิการและผังเมือง

แสดงแบบ
ขยายห้องน้ำ 1


มาตราส่วน 1:25

วัน/เดือน/ปี 21 พ.ย. 2546

เลขที่แบบ ม.บ.462126


แผ่นที่ A-11 จำนวนแผ่น 17

หมายเหตุ แบบที่แสดงอยู่นี้ได้รับการยืมส่วน เพื่อใช้แสดงผลทางหน้าจอเท่านั้น สำหรับแบบที่ใช้ขออนุญาตก่อสร้าง ให้ถ่ายสำเนาจากหนังสือแบบบ้าน

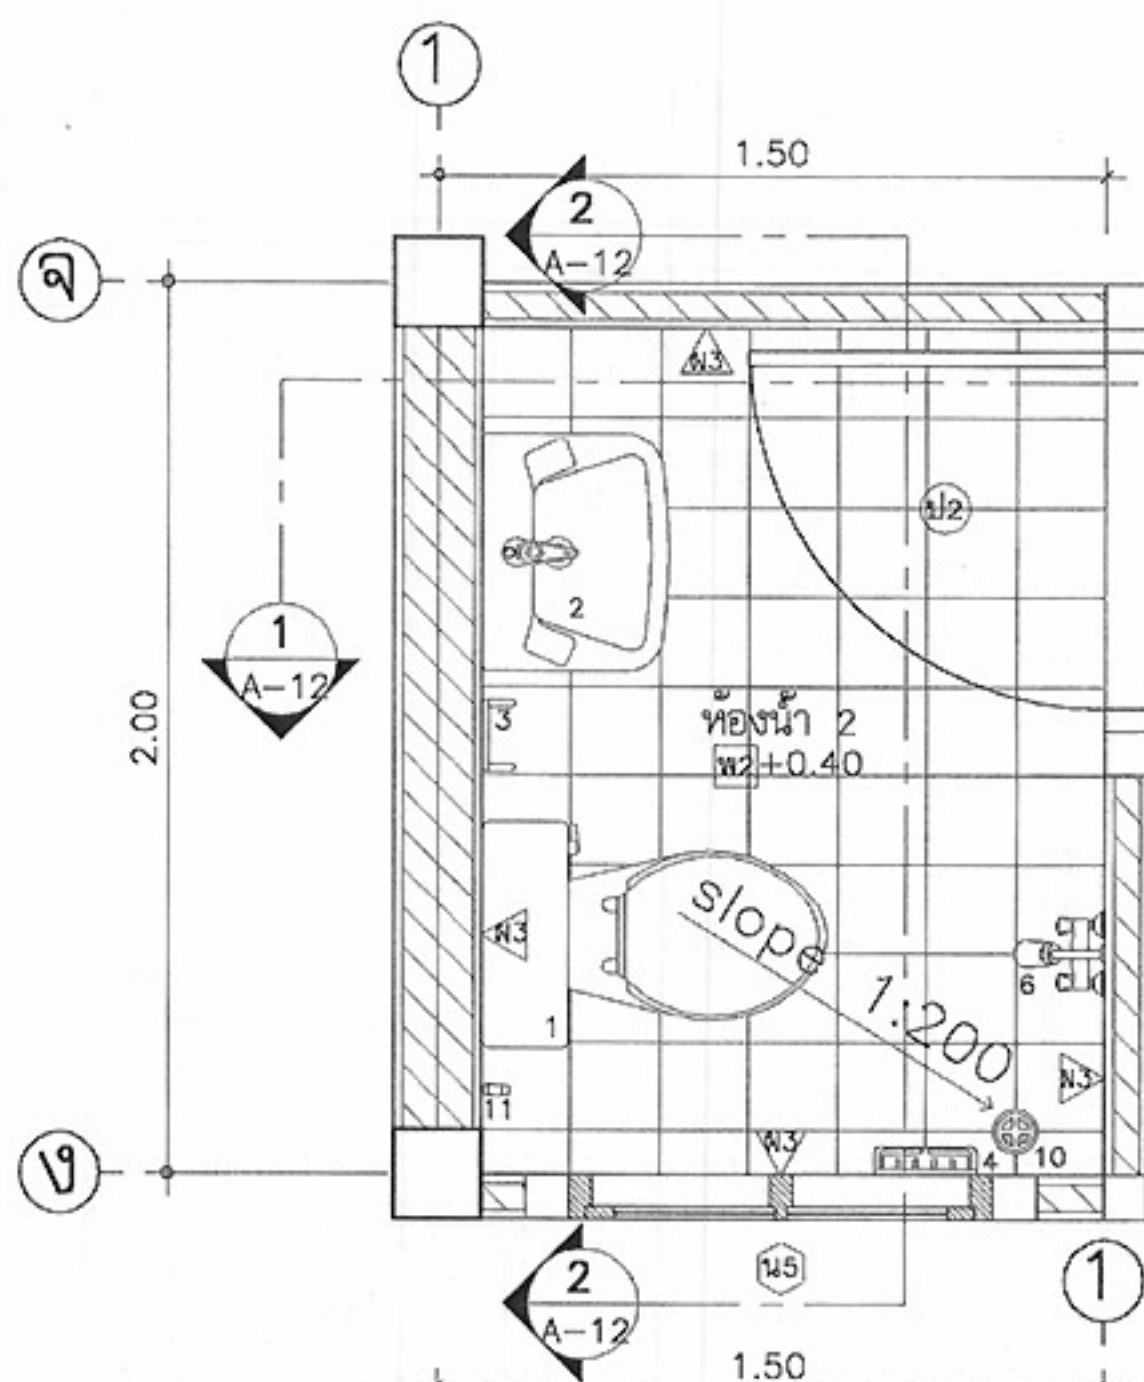

รูปตัด 1
มาตราส่วน 1:25

แบบขยายห้องน้ำ 2
มาตราส่วน 1:25

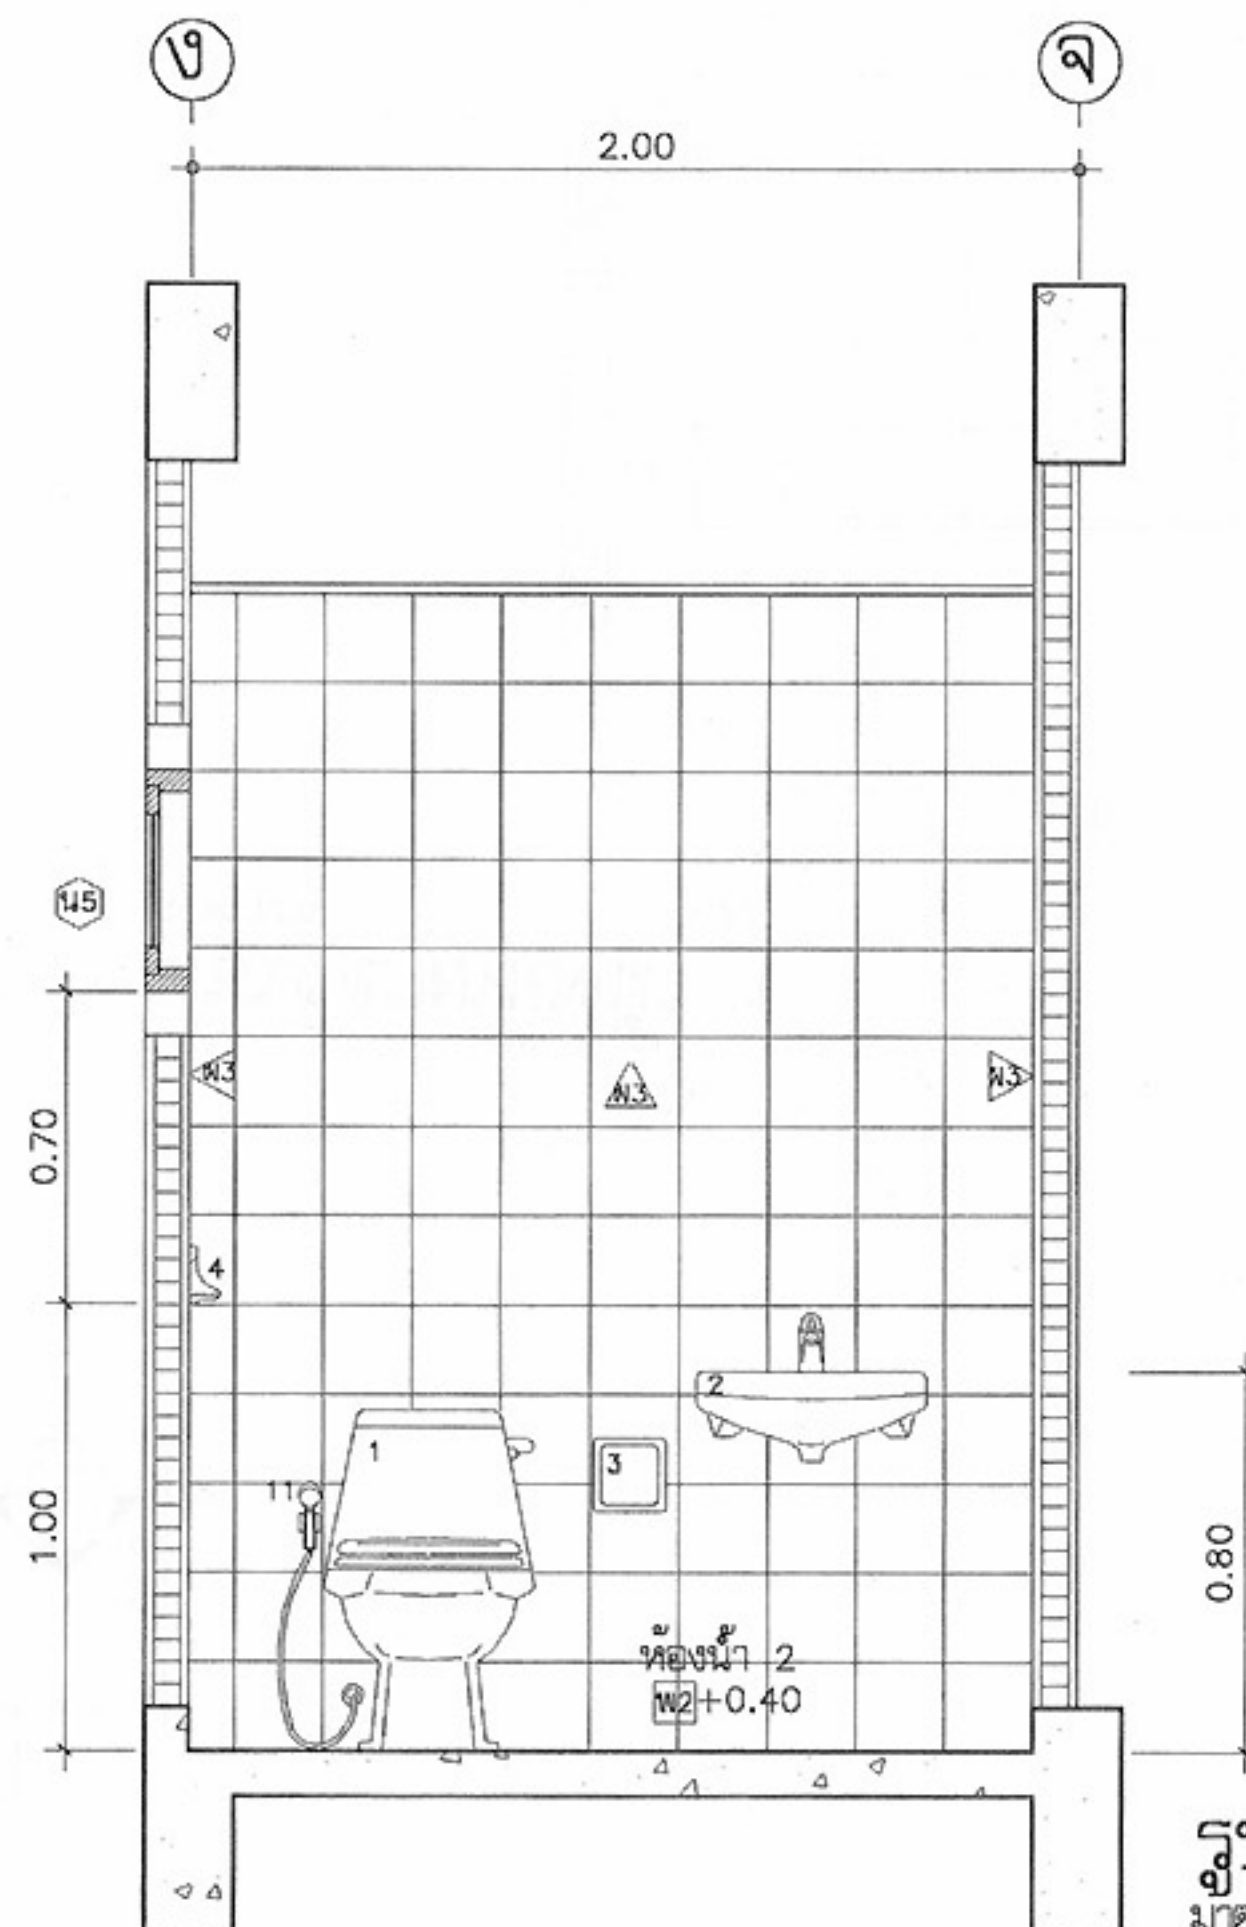

รูปตัด 2
มาตราส่วน 1:25



โครงการแบบอาคารเพื่อประชาชน
ครอบครัวไทยเป็นสุข

แบบ
บ้านครอบครัวไทยเป็นสุข 8

สำนักสถาปัตยกรรม
ผู้ควบคุมการออกแบบ

สถาปัตยกรรม
สถาปนิก
สถาปนิก
สถาปนิก
สถาปนิก

สำนักวิศวกรรมโครงสร้างและงานระบบ
ผู้ควบคุมการออกแบบ

วิศวกรรม
โครงสร้าง
วิศวกรรมไฟฟ้า
และเครื่องกล
วิศวกรรม
สุขาภิบาล

อนุมัติ
(นายสว่าง ศรีสุคนธ์)
อธิบดีกรมโยธาธิการและผังเมือง

แสดงแบบ
ขยายห้องน้ำ 2



มาตราส่วน 1:25

วัน/เดือน/ปี 21 พ.ย. 2546

เลขที่แบบ ม.บ.462126

แผ่นที่ A-12 จำนวนแผ่น 17

หมายเหตุ แบบที่แสดงอยู่นี้ได้รับการยืมส่วน เพื่อใช้แสดงผลทางหน้าจอเท่านั้น สำหรับแบบที่ใช้ขออนุญาตก่อสร้าง ให้ถ่ายสำเนาจากหนังสือแบบบ้าน

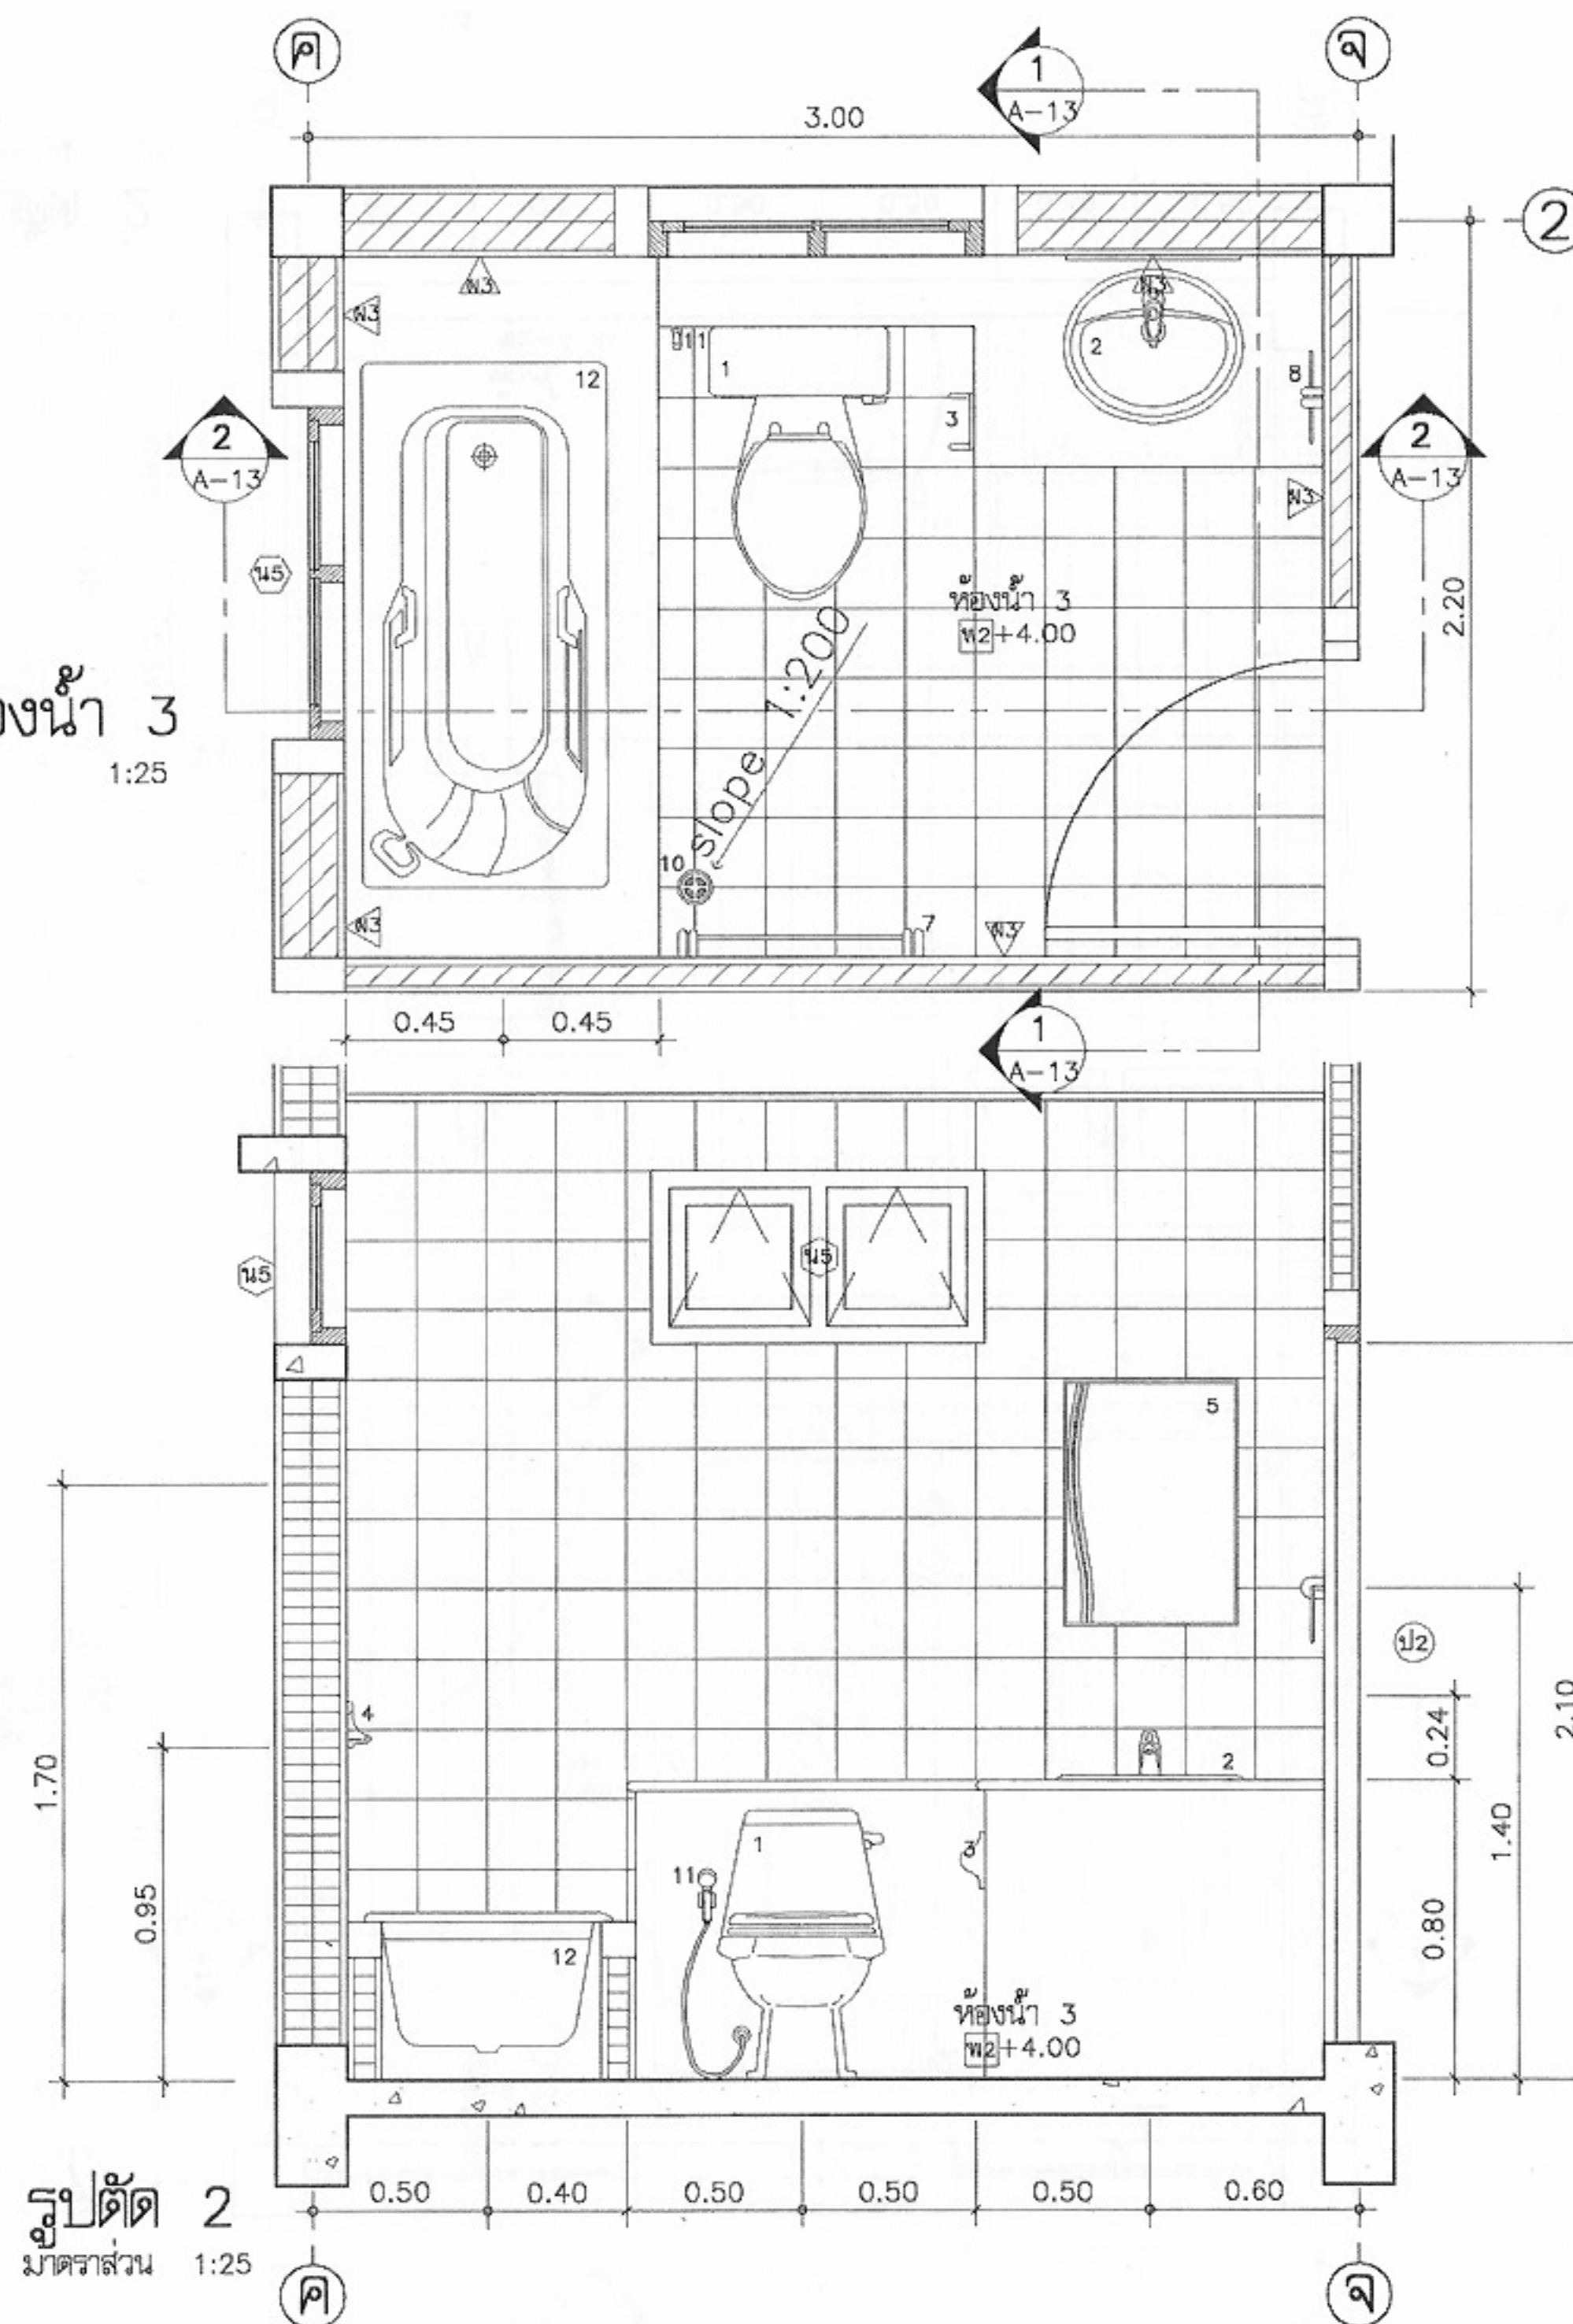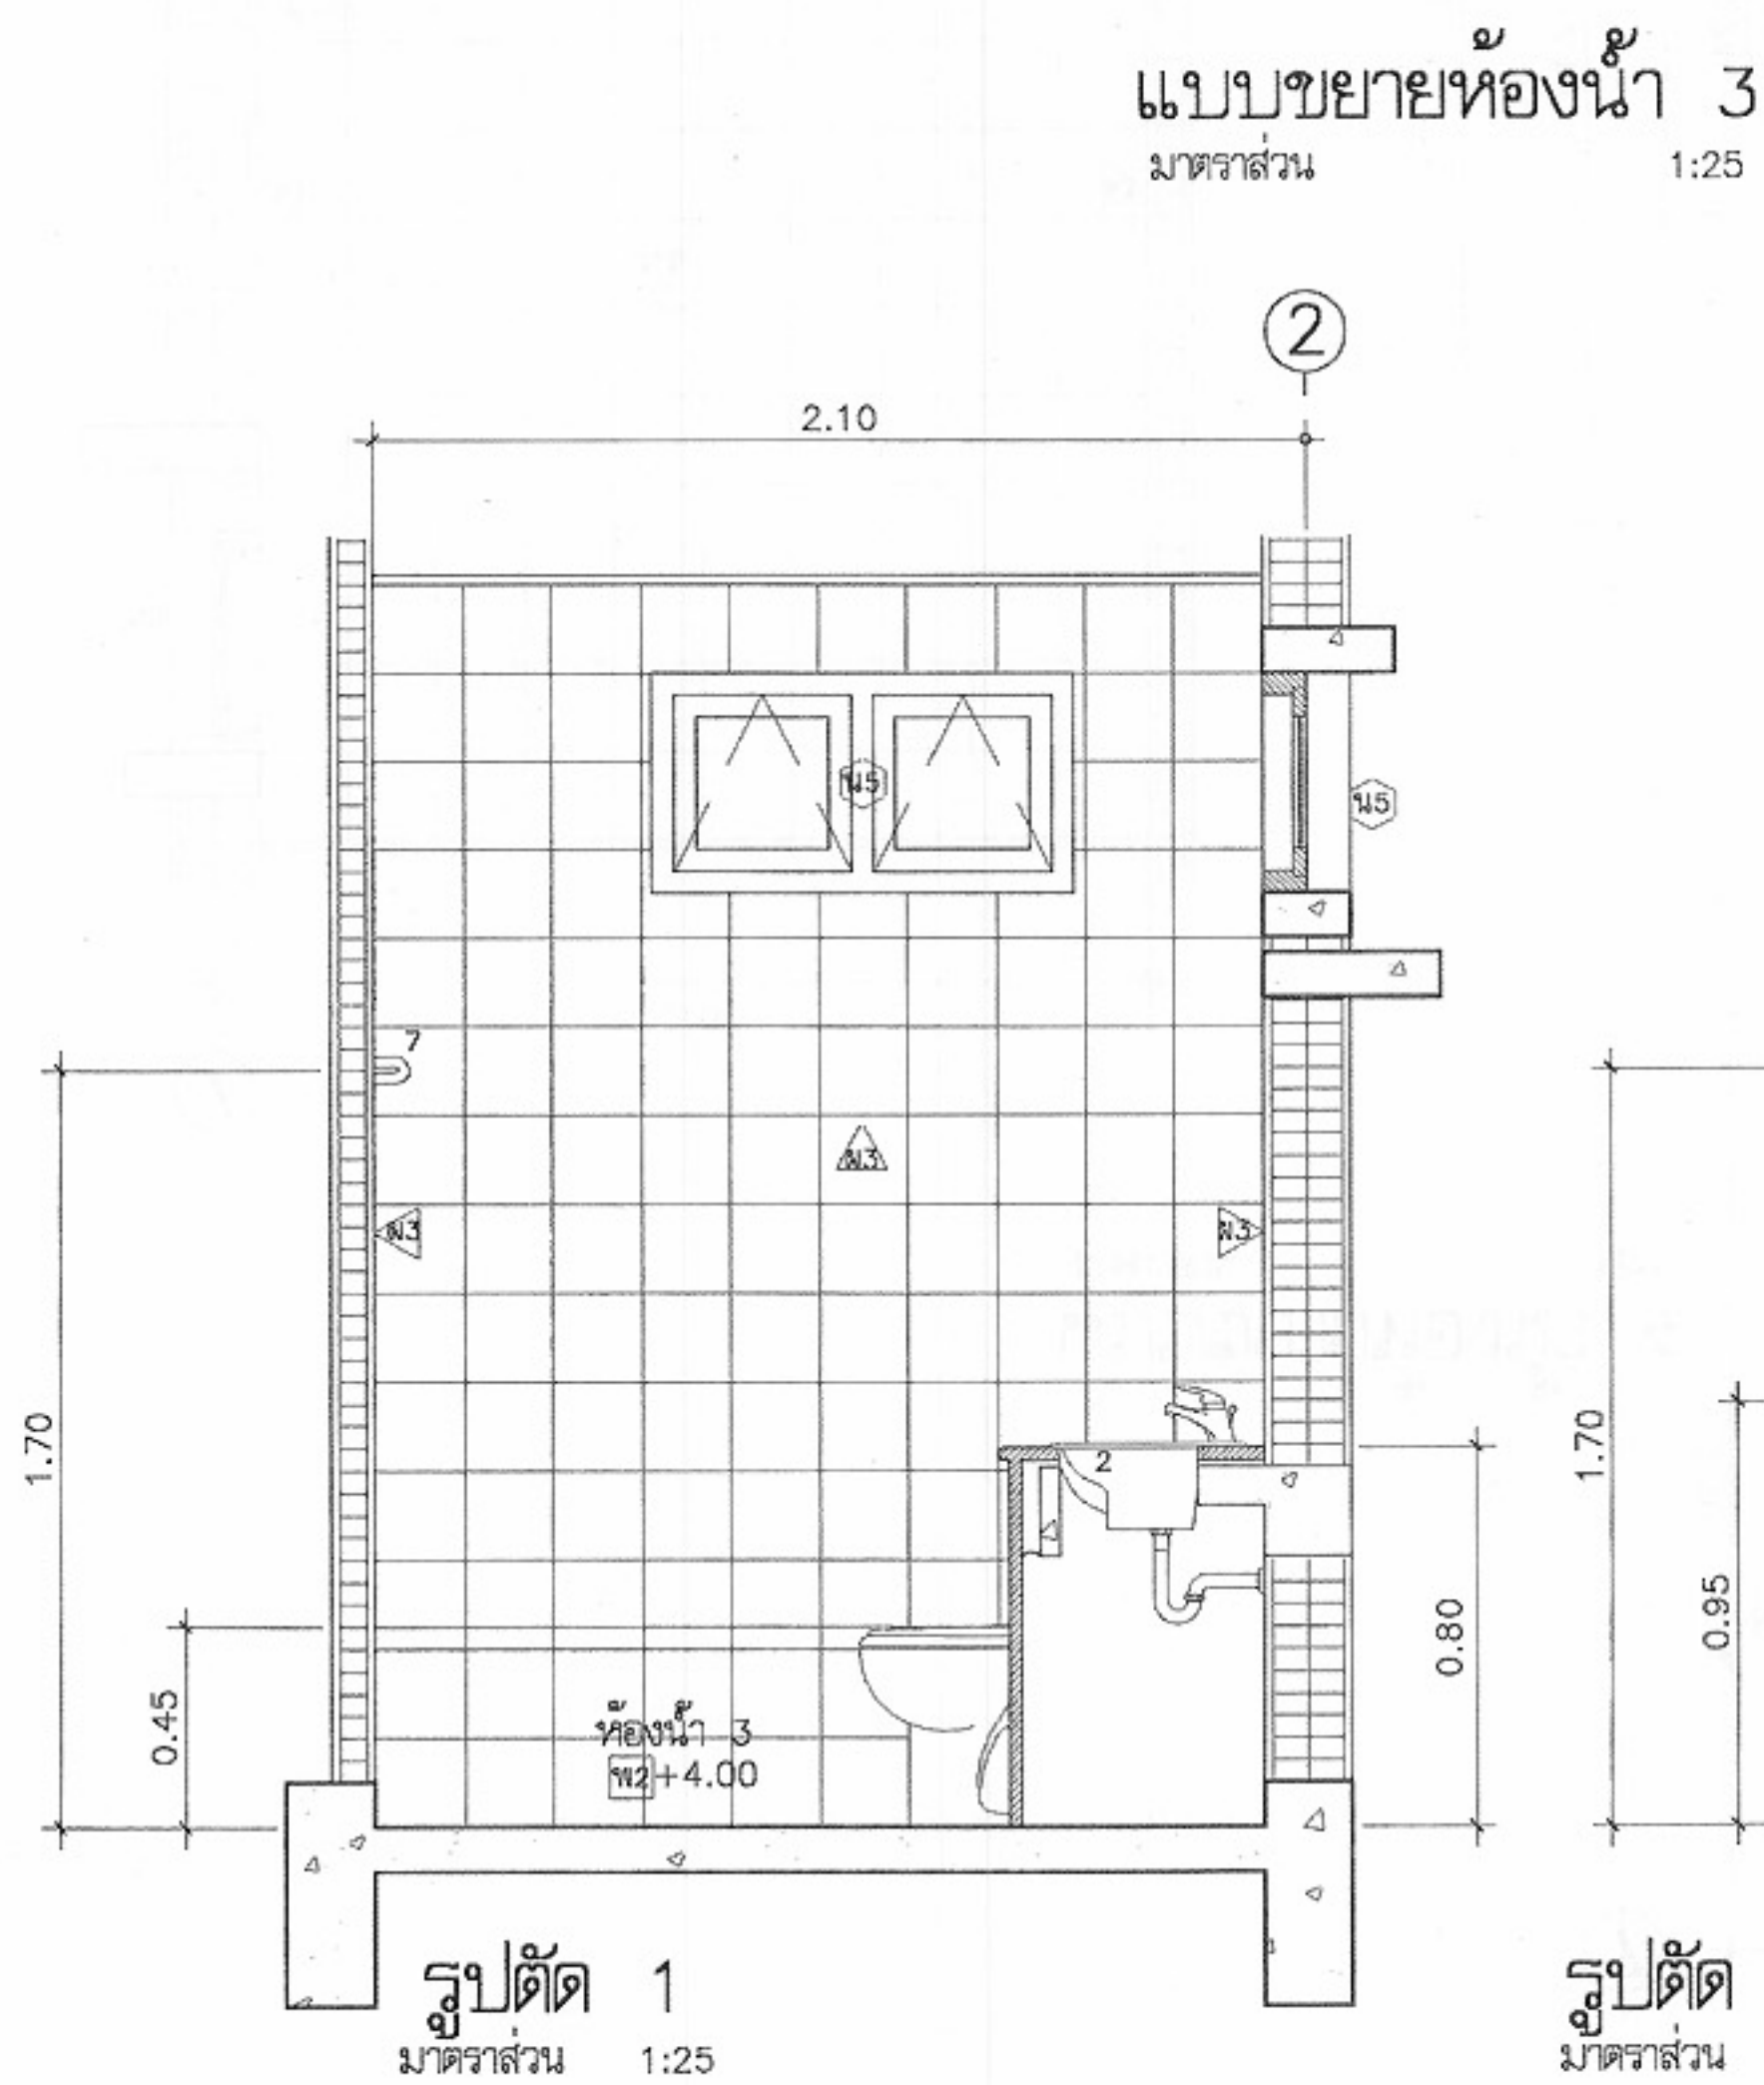

โครงการแบบอาคารเพื่อประชาชน

ครอบครัวไทยเป็นสุข

แบบ

บ้านครอบครัวไทยเป็นสุข 8

สำนักสถาปัตยกรรม

๗๖๖-๖๖๖

ผู้อำนวยการสำนัก

สถาปัตยกรรม

๗๖๖-๖๖๖

สถาปนิก

สถาปนิก

สถาปนิก

สถาปนิก

สำนักวิศวกรรมโครงสร้างและงานระบบ

๗๖๖-๖๖๖

ผู้อำนวยการสำนัก

วิศวกรรม

๗๖๖-๖๖๖

วิศวกร

โครงสร้าง

๗๖๖-๖๖๖

วิศวกร

วิศวกรรมไฟฟ้า

๗๖๖-๖๖๖

วิศวกร

และเครื่องกล

๗๖๖-๖๖๖

วิศวกร

วิศวกรรม

๗๖๖-๖๖๖

วิศวกร

สุขาภิบาล

๗๖๖-๖๖๖

วิศวกร

อนุมัติ

๗๖๖-๖๖๖

(นายสว่าง ศรีสุคนธ์)

อธิบดีกรมโยธาธิการและผังเมือง

แสดงแบบ

ขยายห้องน้ำ 3

มาตราส่วน

1:25

วัน/เดือน/ปี

21 พ.ย. 2546

เลขที่แบบ

ม.บ.462126


แผ่นที่

A-13

จำนวนแผ่น

17

หมายเหตุ แบบที่แสดงอยู่นี้ได้รับการยืมส่วน เพื่อใช้แสดงผลทางหน้าจอเท่านั้น สำหรับแบบที่ใช้ขออนุญาตก่อสร้าง ให้ถ่ายสำเนาจากหนังสือแบบบ้าน

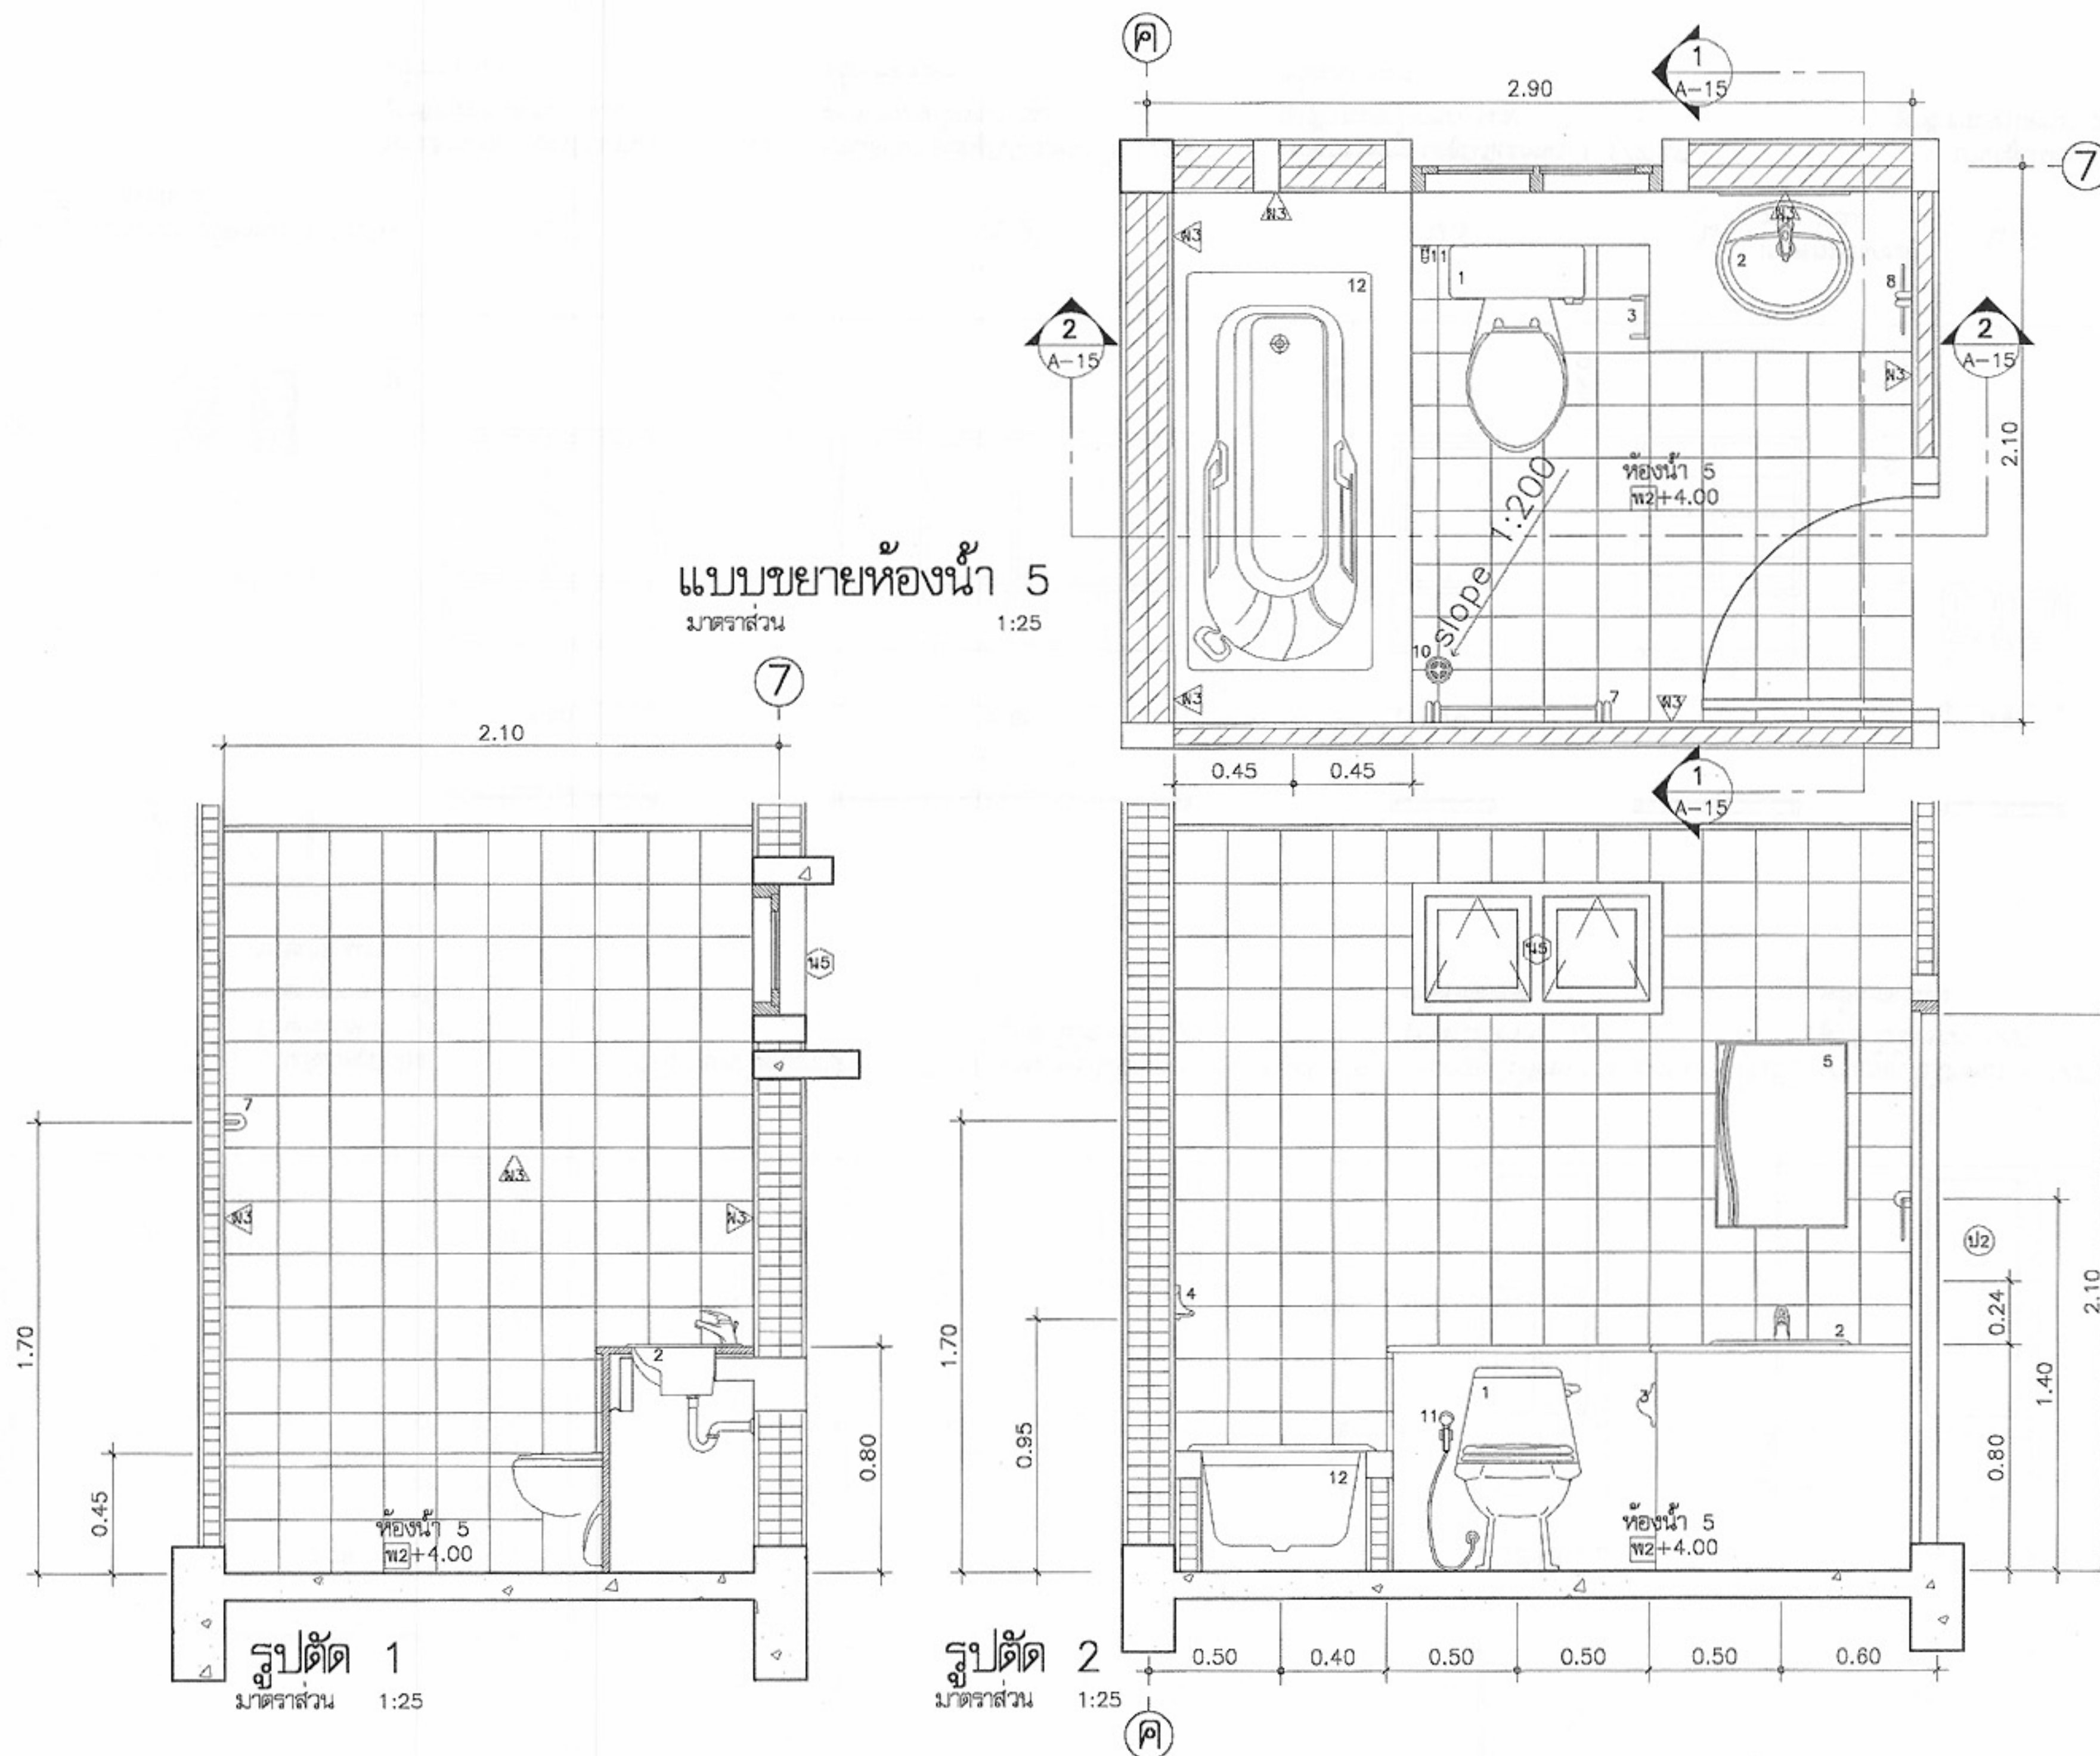

โครงการแบบอาคารเพื่อประชาชน
ครอบครัวไทยเป็นสุข

แบบ
บ้านครอบครัวไทยเป็นสุข 8

สำนักสถาปัตย์กรรม
ผู้ควบคุมการดำเนินงาน

สถาปัตย์กรรม
สถาปนิก
สถาปนิก
สถาปนิก
สถาปนิก

สำนักวิศวกรรมโครงสร้างและงานระบบ
ผู้ควบคุมการดำเนินงาน

วิศวกรรม
โครงสร้าง
วิศวกรรมไฟฟ้า
และเครื่องกล
วิศวกรรม
สุขาภิบาล

อนุมัติ
(นายสว่าง ศิริสุนทร)
อธิบดีกรมโยธาธิการและผังเมือง

แสดงแบบ
ขยายห้องน้ำ 5


มาตราส่วน 1:25

วัน/เดือน/ปี 21 พ.ย. 2546


เลขที่แบบ ม.บ.462126

แผ่นที่ A-15 จำนวนแผ่น 17

หมายเหตุ แบบที่แสดงอยู่นี้ได้รับการยืมส่วน เพื่อใช้แสดงผลทางหน้าจอเท่านั้น สำหรับแบบที่ใช้ขออนุญาตก่อสร้าง ให้ถ่ายสำเนาจากหนังสือแบบบ้าน

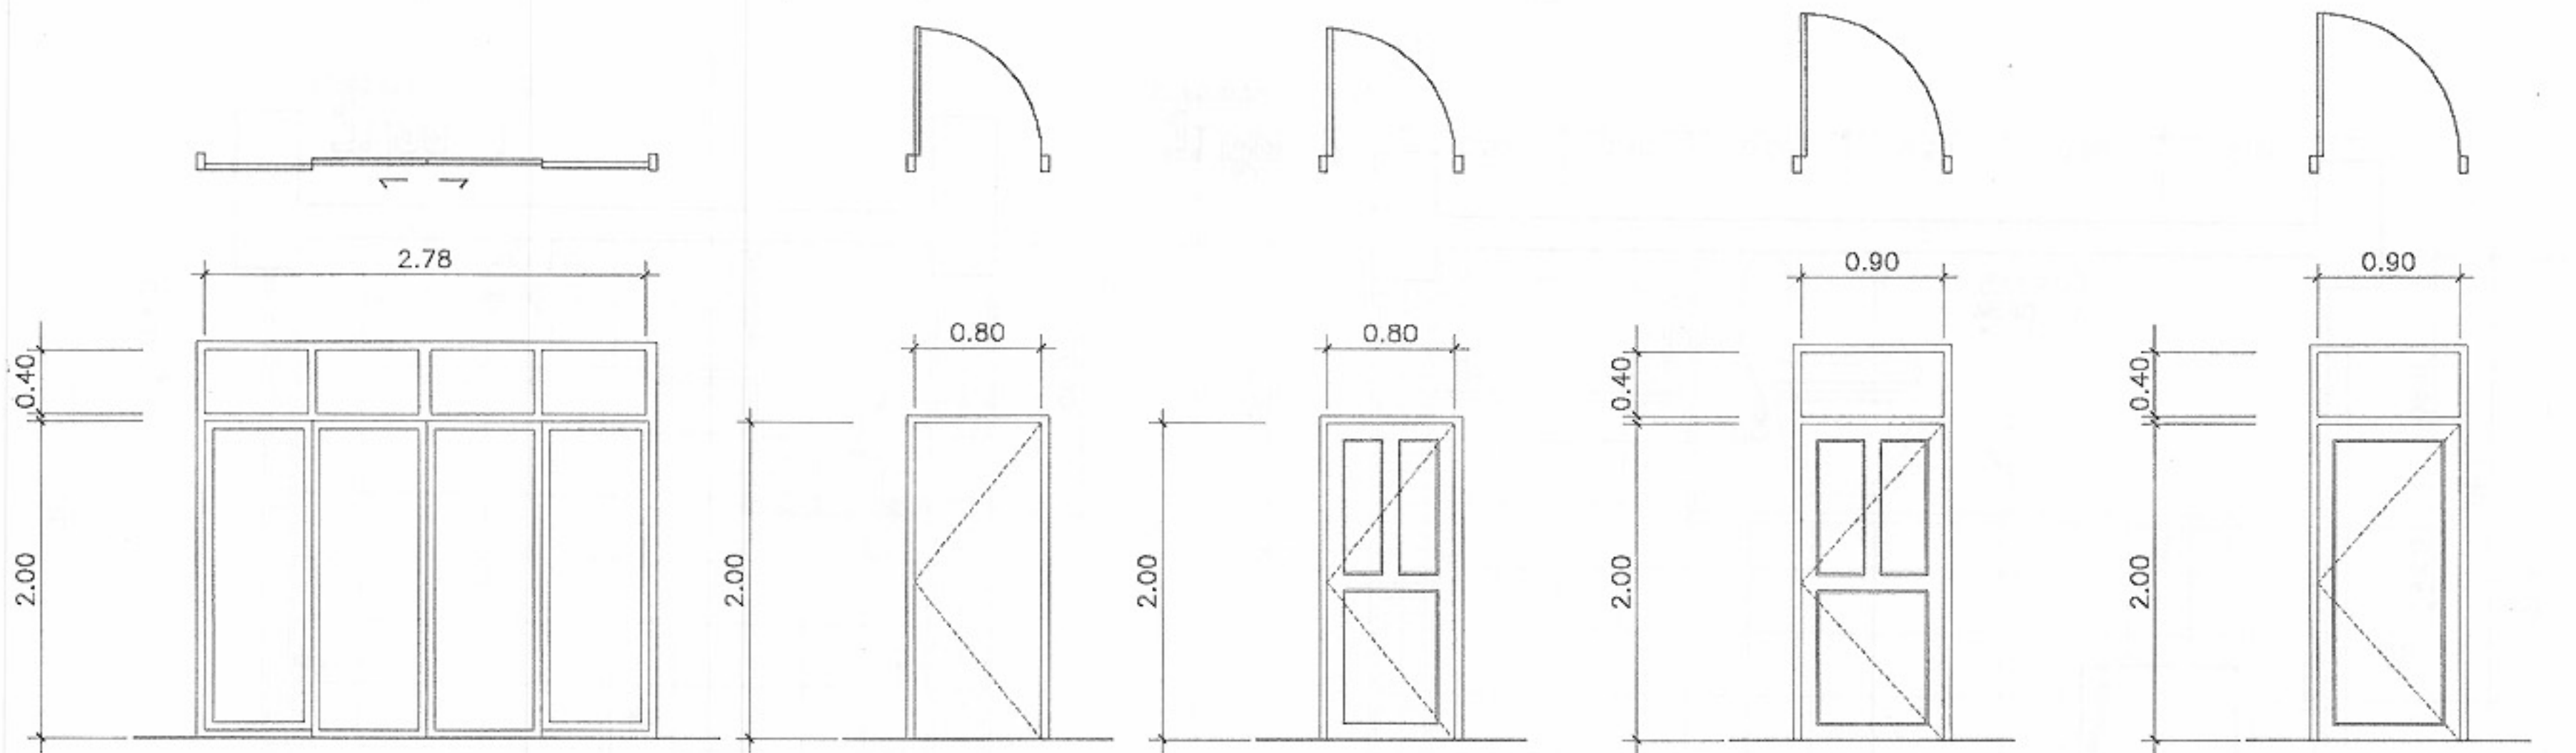

- ป1 บานเลื่อนอลูมิเนียม บานกรอบหนา 1/2" พร้อมอุปกรณ์รางเลื่อน พร้อมช่องแสง
- ป2 บานไฟเบอร์กลาส
- ป3 บานกรอบไม้สักหนา 1 1/2"x4" ลูกล็อกไม้สักหนา 1/2"
- ป4 บานกรอบไม้สักหนา 1 1/2"x4" ลูกล็อกไม้สักหนา 1/2" พร้อมช่องแสง
- ป5 บานกรอบไม้สักหนา 1 1/2"x4" ลูกล็อกไม้สักหนา 1/2" พร้อมช่องแสง

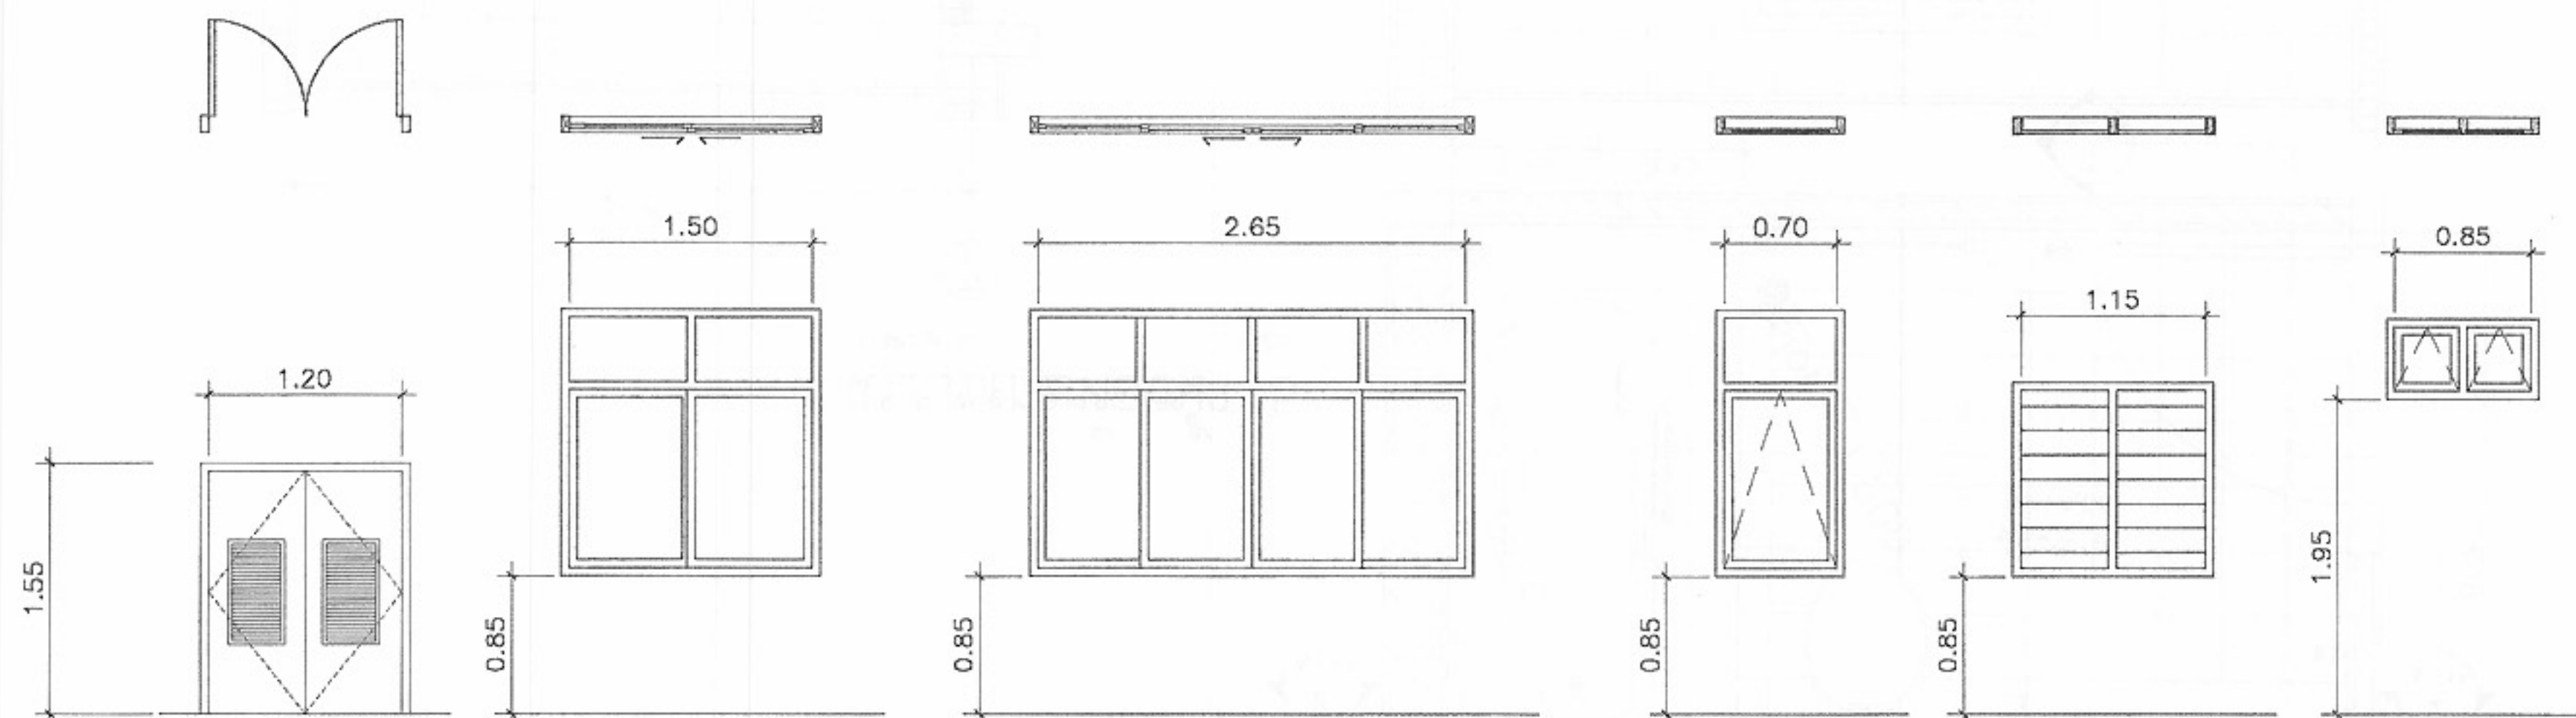

- ป6 บานกรอบไม้สักหนา 1 1/2"x4" บานเกล็ดไม้
- น1 บานเลื่อนกรอบอลูมิเนียมหนา 1 1/2"x3" ลูกล็อกกระจกใสหนา 5มม. พร้อมช่องแสง
- น2 บานเลื่อนกรอบอลูมิเนียมหนา 1 1/2"x3" ลูกล็อกกระจกใสหนา 5มม. พร้อมช่องแสง
- น3 บานกระทุ้งกรอบอลูมิเนียมหนา 1 1/2"x3" ลูกล็อกกระจกใสหนา 5มม. พร้อมช่องแสง
- น4 เกล็ดกระจกใสหนา 5มม.
- น5 บานอลูมิเนียม ลูกล็อกกระจกใสหนา 5มม.



โครงการแบบอาคารเพื่อประชาชน
ครอบครัวไทยเป็นสุข

แบบ
บ้านครอบครัวไทยเป็นสุข 8

สำนักสถาปัตย์กรรม
ผู้ควบคุมการก่อสร้าง

สถาปัตย์กรรม
ผู้ควบคุมการก่อสร้าง

สำนักวิศวกรรมโครงสร้างและงานระบบ
ผู้ควบคุมการก่อสร้าง

วิศวกรรม
โครงสร้าง
วิศวกรรมไฟฟ้า
และเครื่องกล
วิศวกรรม
สุขาภิบาล

อนุมัติ
(นายสว่าง ศรีสุคนธ์)
อธิบดีกรมโยธาธิการและผังเมือง

แสดงแบบ
ขยายประตู-หน้าต่าง

มาตราส่วน 1:50
วัน/เดือน/ปี 21 พ.ย. 2546
เลขที่แบบ ม.ป.462126
แผ่นที่ A-16 จำนวนแผ่น 17

หมายเหตุ แบบที่แสดงอยู่นี้ได้รับการยืมส่วน เพื่อใช้แสดงผลทางหน้าจอตานั้น สำหรับแบบที่ใช้ขออนุญาตก่อสร้าง ให้ถ่ายสำเนาจากหนังสือแบบบ้าน



โครงการแบบอาคารเพื่อประชาชน
ครอบครัวไทยเป็นสุข

แบบ
บ้านครอบครัวไทยเป็นสุข 8


สำนักสถาปัตยกรรม	๗๒๖๖	ผู้อำนวยการสำนัก
สถาปนิก	๗๒๖๖	สถาปนิก
		สถาปนิก
		สถาปนิก
		สถาปนิก

สำนักวิศวกรรมโครงสร้างและงานระบบ	๗๒๖๖	ผู้อำนวยการสำนัก
วิศวกรรม	๗๒๖๖	วิศวกร
โครงสร้าง		วิศวกร
วิศวกรรมไฟฟ้า	๗๒๖๖	วิศวกร
และเครื่องกล	๗๒๖๖	วิศวกร
วิศวกรรม	๗๒๖๖	วิศวกร
สุขาภิบาล	๗๒๖๖	วิศวกร


อนุมัติ
(นายสว่าง ศรีสกุล)
อธิบดีกรมโยธาธิการและผังเมือง

แสดงแบบ
ขยายทั่วไป

มาตรฐาน	1:20
วัน/เดือน/ปี	21 พ.ย. 2546
เลขที่แบบ	ม.บ.462126
แผ่นที่	จำนวนแผ่น
A-17	17

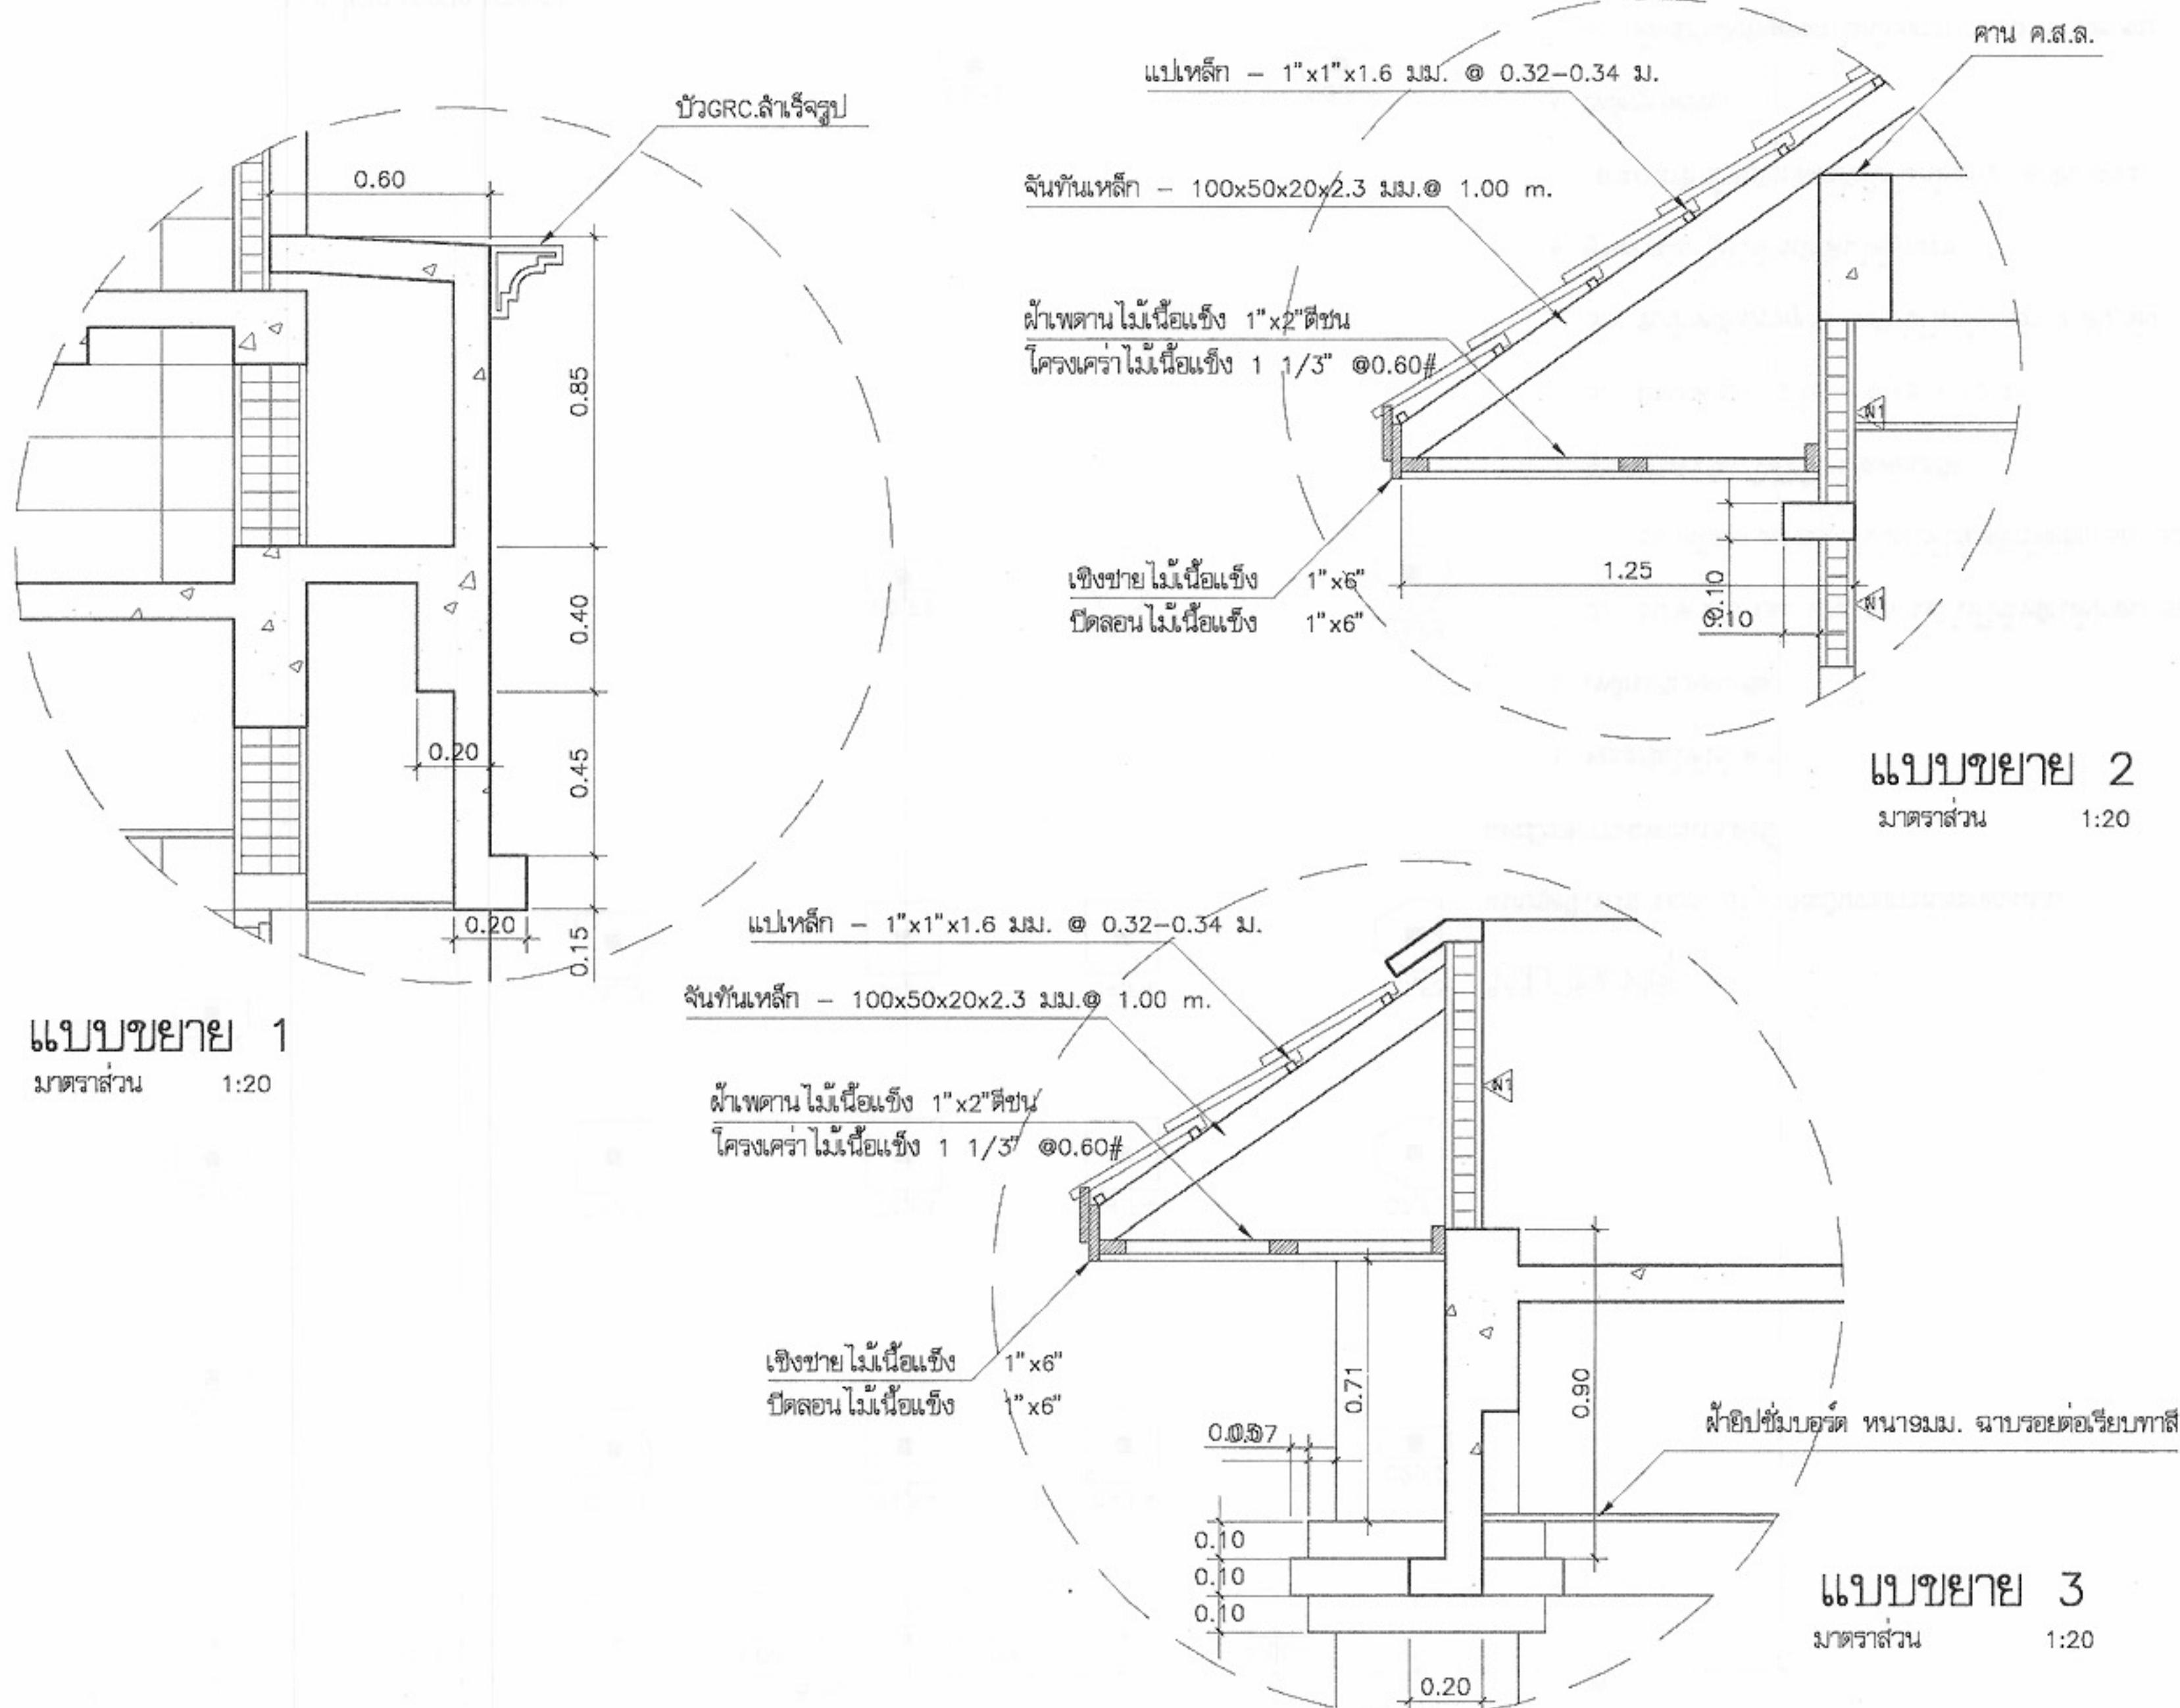

หมายเหตุ แบบที่แสดงอยู่นี้ได้รับการยืมส่วน เพื่อใช้แสดงผลทางหน้าจอเท่านั้น สำหรับแบบที่ใช้ขออนุญาตก่อสร้าง ให้ถ่ายสำเนาจากหนังสือแบบบ้าน

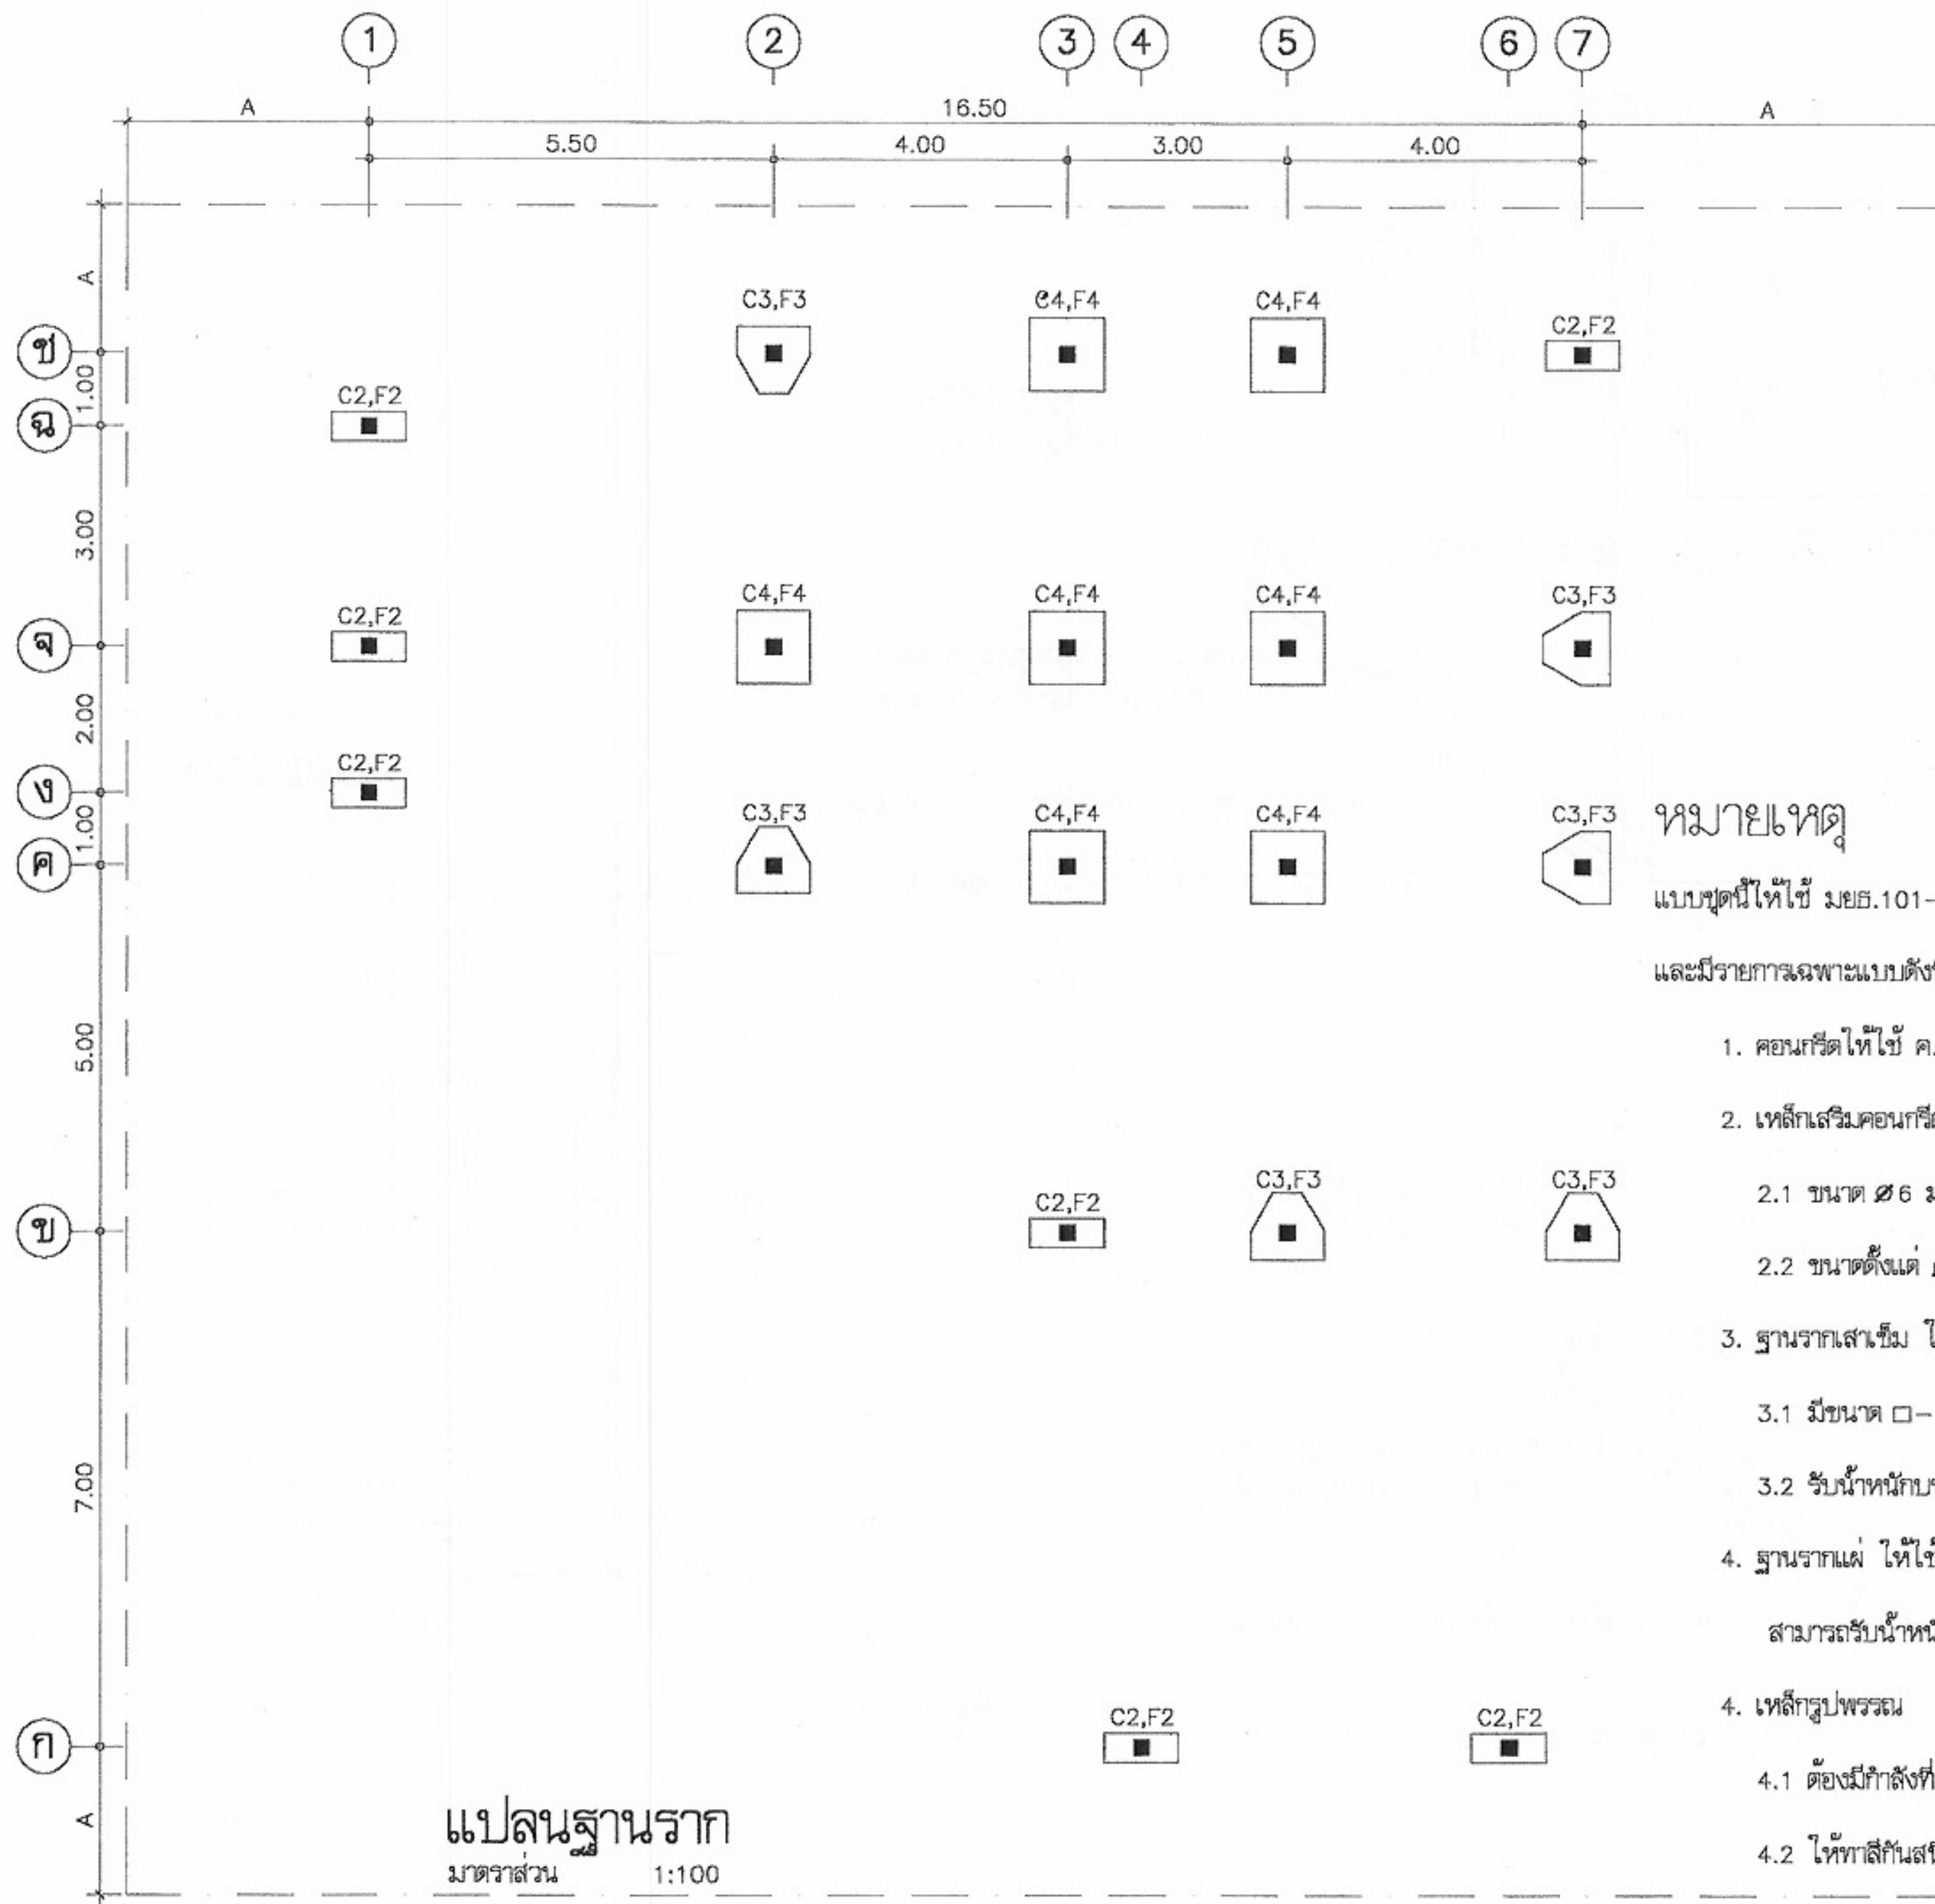

หมายเหตุ

แบบชุดนี้ให้ใช้ มยธ.101-108เป็นรายการประกอบแบบ

และมีรายการเฉพาะแบบดังนี้

1. คอนกรีตให้ใช้ ค.1
2. เหล็กเสริมคอนกรีต
 - 2.1 ขนาด ๘6 มม. และ ๘9 มม. ให้ใช้เหล็กเส้นกลม SR-24
 - 2.2 ขนาดตั้งแต่ ๑12 มม. ขึ้นไป ให้ใช้เหล็กข้ออ้อย SD-30
3. ฐานรากเสาเข็ม ให้ใช้เสาเข็มคอนกรีต
 - 3.1 มีขนาด □- 0.18 x 0.18 x 12 ม.
 - 3.2 รับน้ำหนักบรรทุกปลอดภัยได้ไม่น้อยกว่า 7 ตัน/ต้น
4. ฐานรากแผ่ ให้ใช้กรณีที่ดินได้ฐานราก

สามารถรับน้ำหนักบรรทุกปลอดภัยได้ไม่น้อยกว่า 8 ตัน/ตร.ม.
4. เหล็กรูปพรรณ
 - 4.1 ต้องมีกำลังจุดคานงไม่น้อยกว่า 2520 กก./ตร.ซม.
 - 4.2 ให้ทาสีกันสนิม 2 ครั้งก่อนทาสีจริง



โครงการแบบอาคารเพื่อประชาชน
ครอบครัวไทยเป็นสุข

แบบ
บ้านครอบครัวไทยเป็นสุข 8

สำนักสถาปัตยกรรม
ผู้อำนวยการสำนัก

สถาปนิก
ผู้ออกแบบ
สถาปนิก
สถาปนิก

สำนักวิศวกรรมโครงสร้างและงานระบบ
ผู้อำนวยการสำนัก

วิศวกรรม
โครงสร้าง
วิศวกร

วิศวกรรมไฟฟ้า
และเครื่องกล
วิศวกร

วิศวกรรม
สุขาภิบาล
วิศวกร

อนุมัติ
(นายสว่าง ศรีสุคนธ์)
อธิบดีกรมโยธาธิการและผังเมือง

แสดงแบบ
แปลนฐานราก


มาตราส่วน 1:100

วัน/เดือน/ปี 21 พ.ย. 2546

เลขที่แบบ ม.บ.462126

แผ่นที่ S-01 จำนวนแผ่น 07

หมายเหตุ แบบที่แสดงอยู่นี้ได้รับการยืมส่วน เพื่อใช้แสดงผลทางหน้าจอเท่านั้น สำหรับแบบที่ใช้ขออนุญาตก่อสร้าง ให้ถ่ายสำเนาจากหนังสือแบบบ้าน

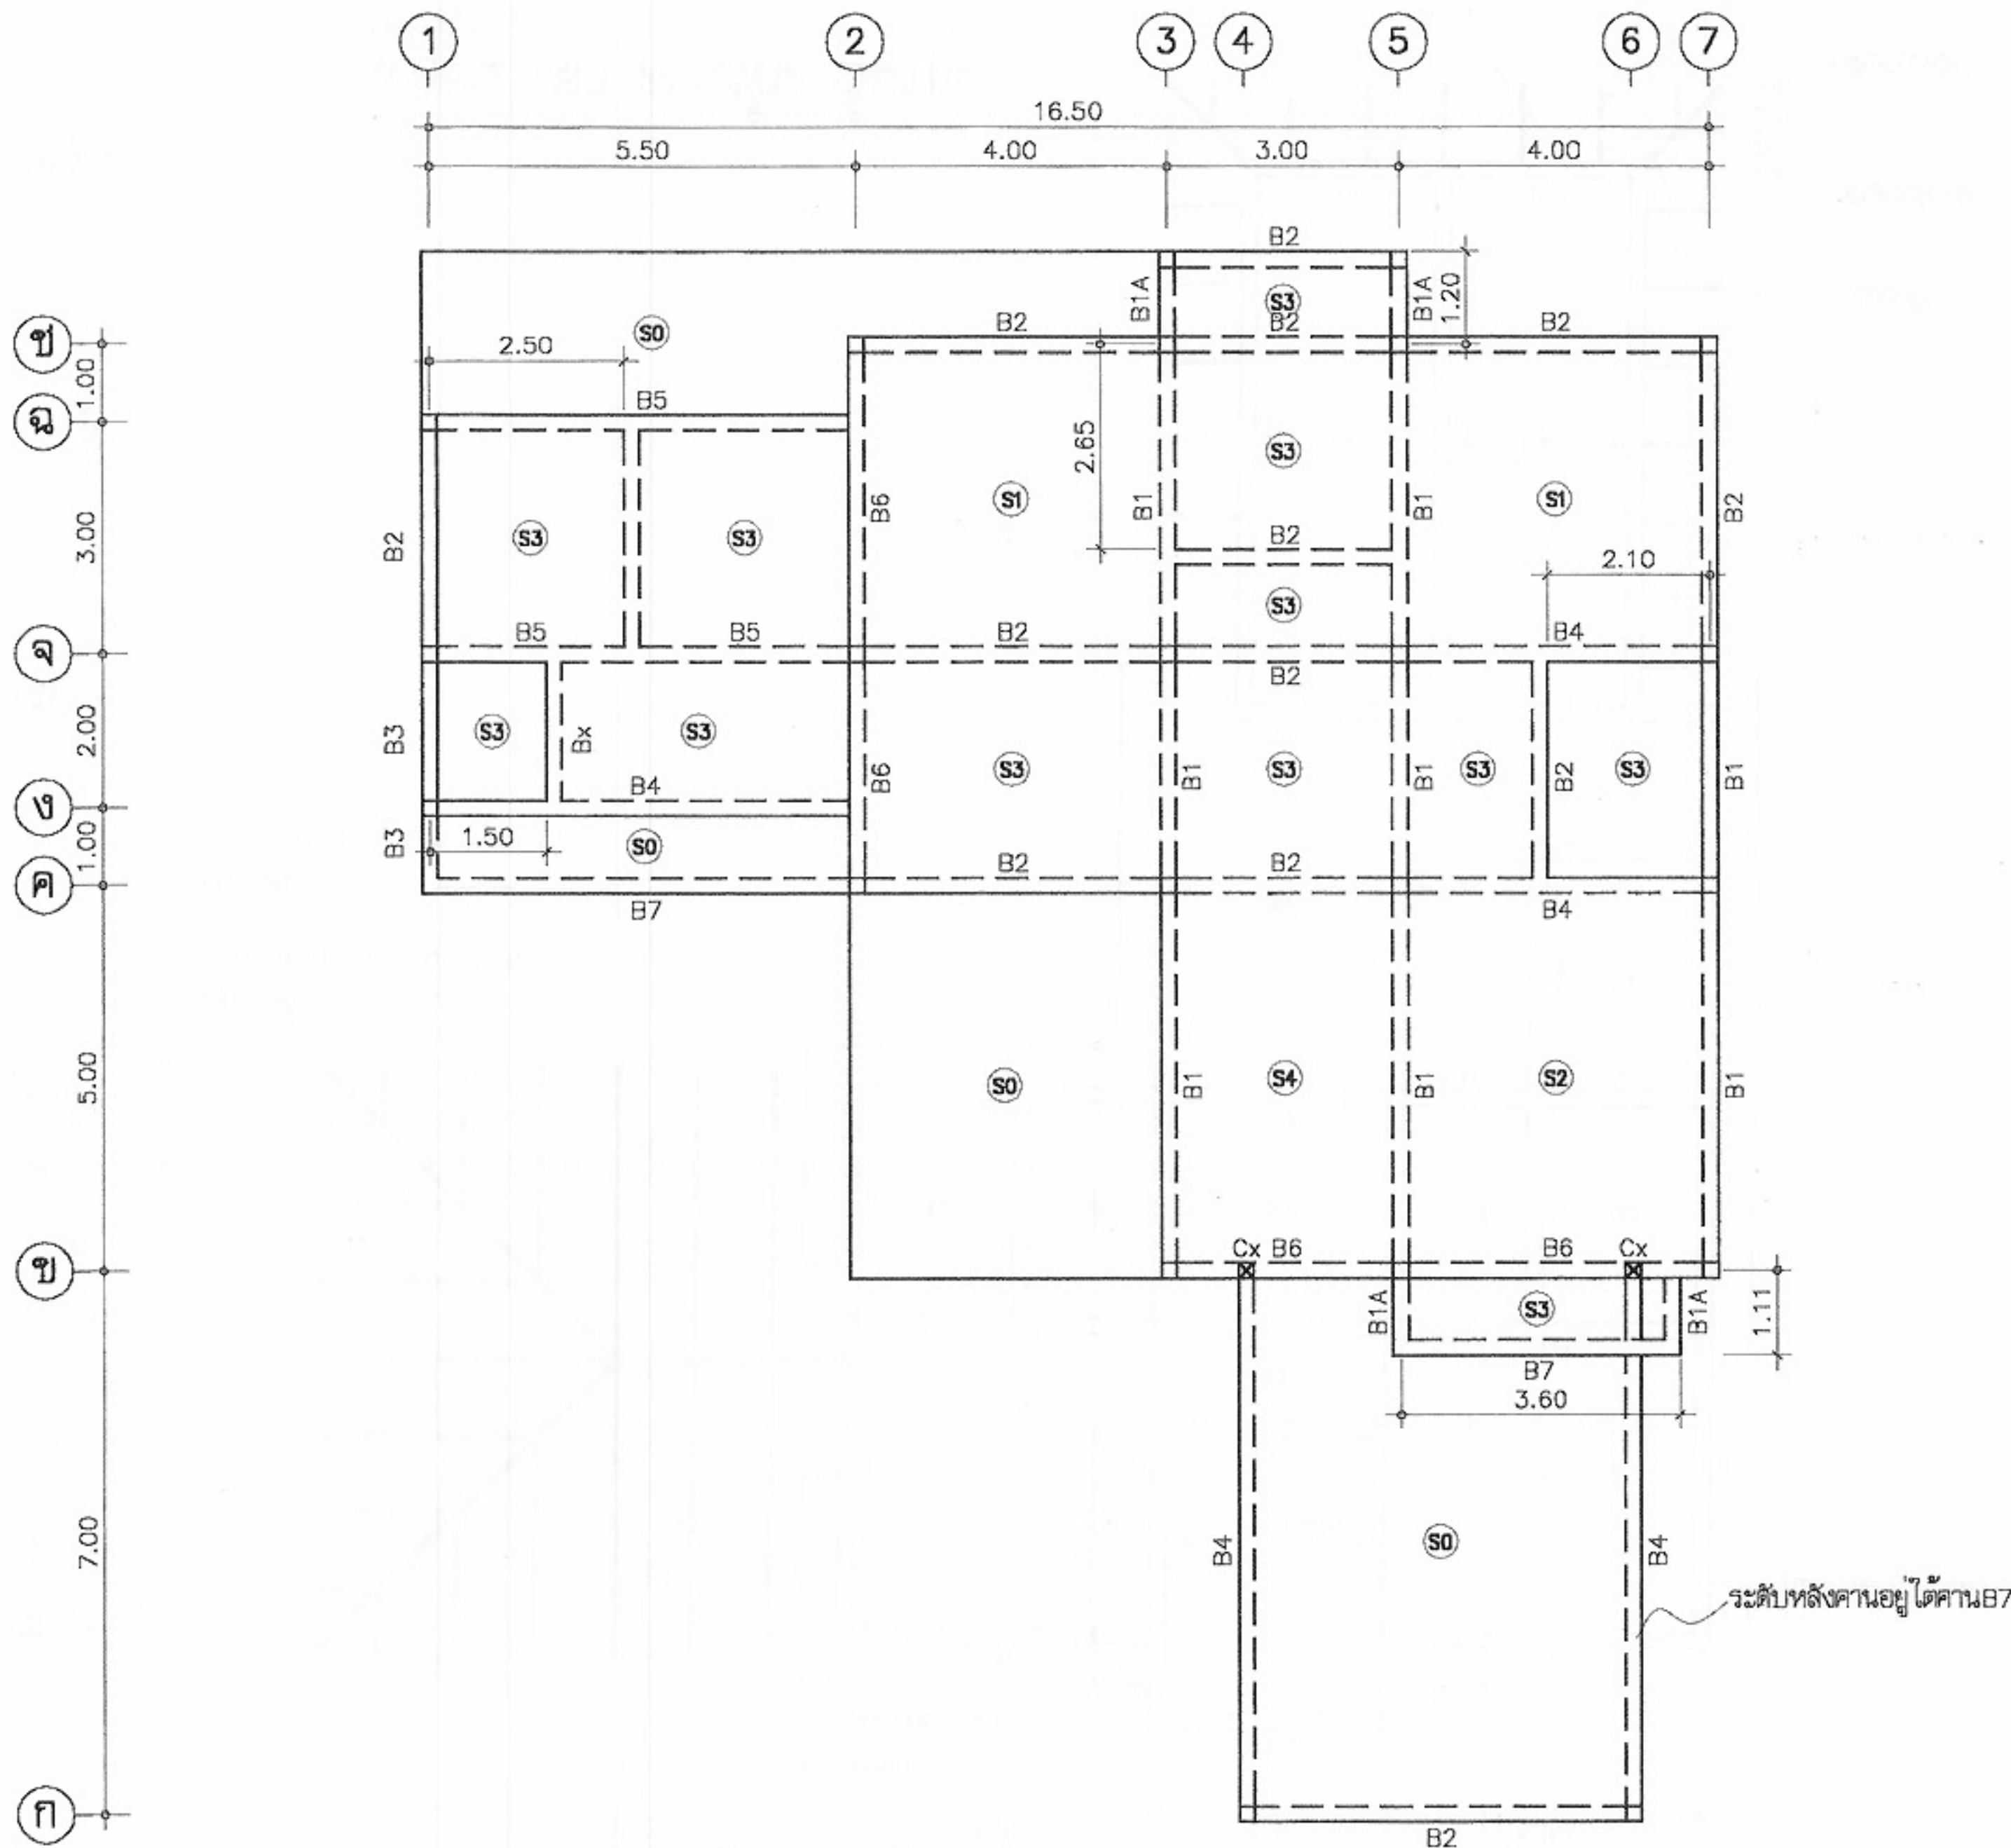

แปลนเสาคานพื้น ชั้นล่าง
มาตราส่วน 1:100



โครงการแบบอาคารเพื่อประชาชน

ครอบครัวไทยเป็นสุข

แบบ

บ้านครอบครัวไทยเป็นสุข 8

สำนักสถาปัตย์กรรม

๗๖๖-๖๖๖

สถาปัตย์กรรม

สถาปัตย์

สถาปัตย์

สถาปัตย์

สถาปัตย์

สำนักวิศวกรรมโครงสร้างและงานระบบ

๖๖๖-๖๖๖

วิศวกรรม

วิศวกร

โครงสร้าง

วิศวกร

วิศวกรรมไฟฟ้า

วิศวกร

และเครื่องกล

วิศวกร

วิศวกรรม

วิศวกร

สุขาภิบาล

วิศวกร

อนุมัติ

๖๖๖-๖๖๖

(นายสว่าง ศรีสุกัน)

อธิบดีกรมโยธาธิการและผังเมือง

แสดงแบบ

แปลน เสาคานพื้น
ชั้นล่าง

มาตราส่วน 1:100

วัน/เดือน/ปี 21 พ.ย. 2546

เลขที่แบบ ม.บ.462126


แผ่นที่

S-02

จำนวนแผ่น

07

หมายเหตุ แบบที่แสดงอยู่นี้ได้รับการยืมส่วน เพื่อใช้แสดงผลทางหน้าจอเท่านั้น สำหรับแบบที่ใช้ขออนุญาตก่อสร้าง ให้ถ่ายสำเนาจากหนังสือแบบบ้าน

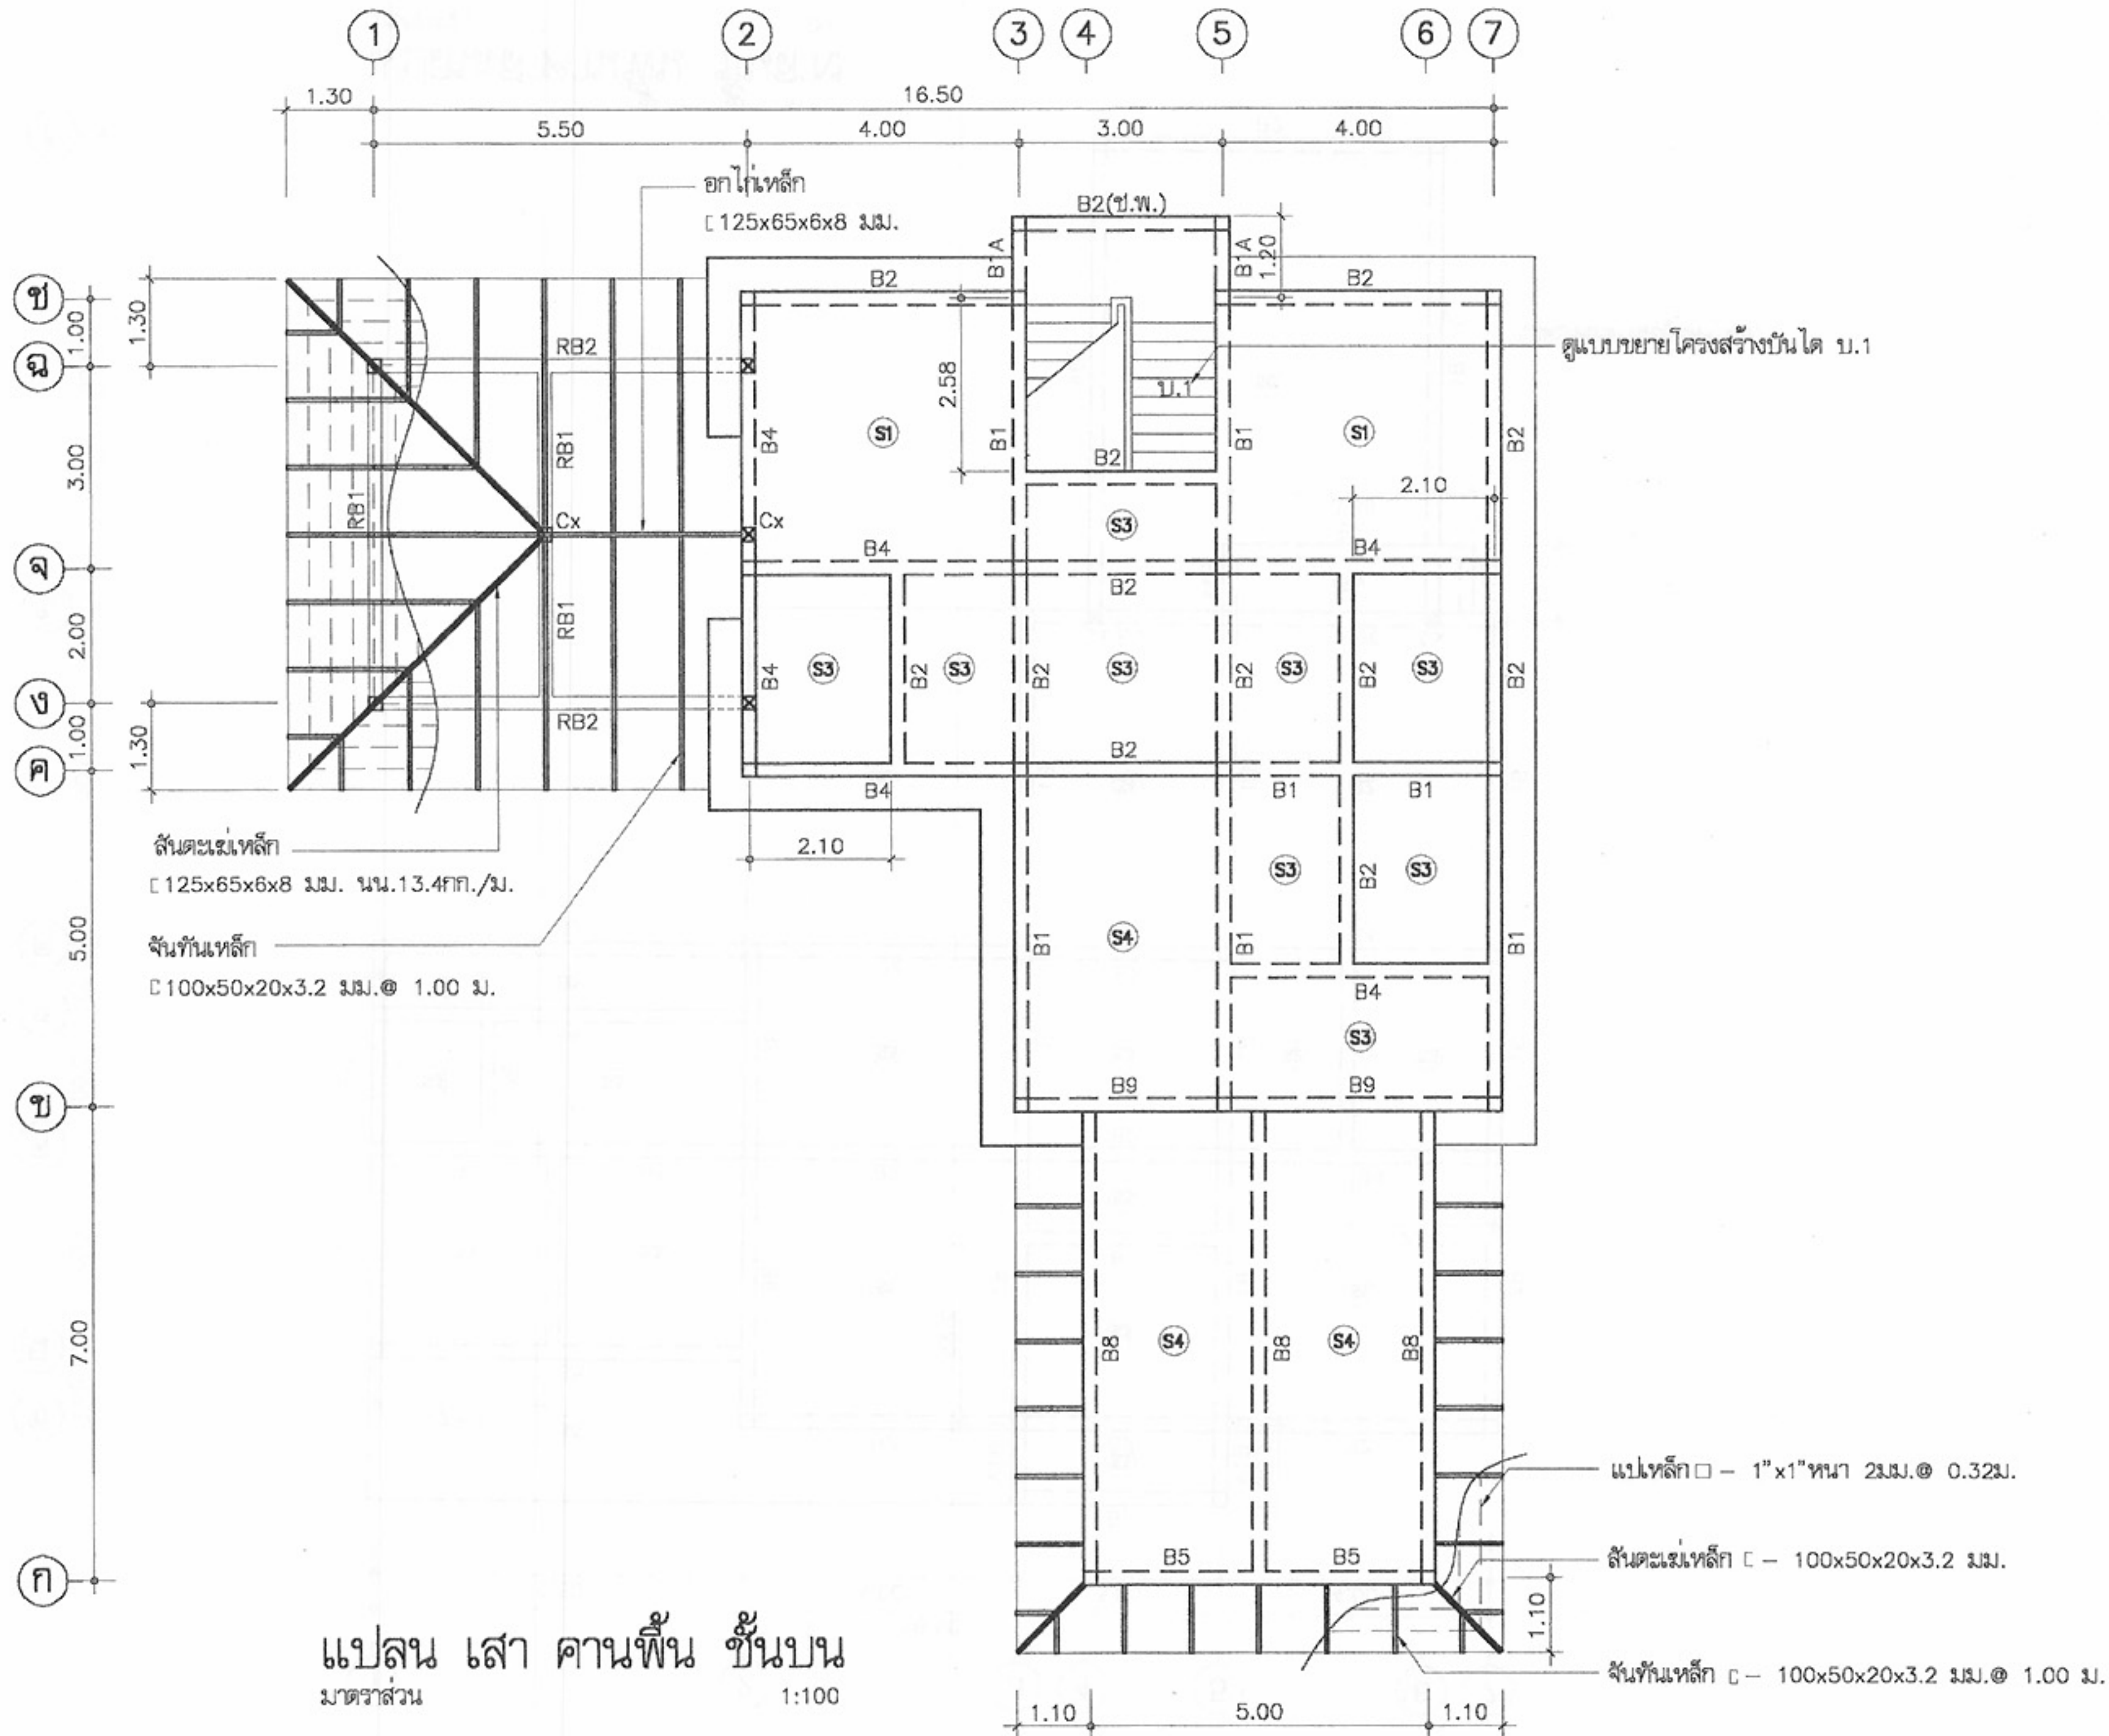

โครงการแบบอาคารเพื่อประชาชน
ครอบครัวไทยเป็นสุข

แบบ
บ้านครอบครัวไทยเป็นสุข 8

สำนักสถาปัตยกรรม
ผู้ควบคุมการปฏิบัติ

สถาปนิก
ผู้ออกแบบ
ผู้ออกแบบ
ผู้ออกแบบ
ผู้ออกแบบ

สำนักวิศวกรรมโครงสร้างและงานระบบ
ผู้ควบคุมการปฏิบัติ


วิศวกรรม
โครงสร้าง
วิศวกรรมไฟฟ้า
และเครื่องกล
วิศวกรรม
สุขาภิบาล
วิศวกร
วิศวกร
วิศวกร
วิศวกร
วิศวกร
วิศวกร

อนุมัติ
(นายสว่าง ศรีสกุล)
อธิบดีกรมโยธาธิการและผังเมือง

แสดงแบบ
แปลน เสา คานพื้น
ชั้นบน


มาตราส่วน 1:100
วัน/เดือน/ปี 21 พ.ย. 2546
เลขที่แบบ ม.บ.462126
แผ่นที่ S-03 จำนวนแผ่น 07

หมายเหตุ แบบที่แสดงอยู่นี้ได้รับการยืมส่วน เพื่อใช้แสดงผลทางหน้าจอตานั้น สำหรับแบบที่ใช้ขออนุญาตก่อสร้าง ให้ถ่ายสำเนาจากหนังสือแบบบ้าน

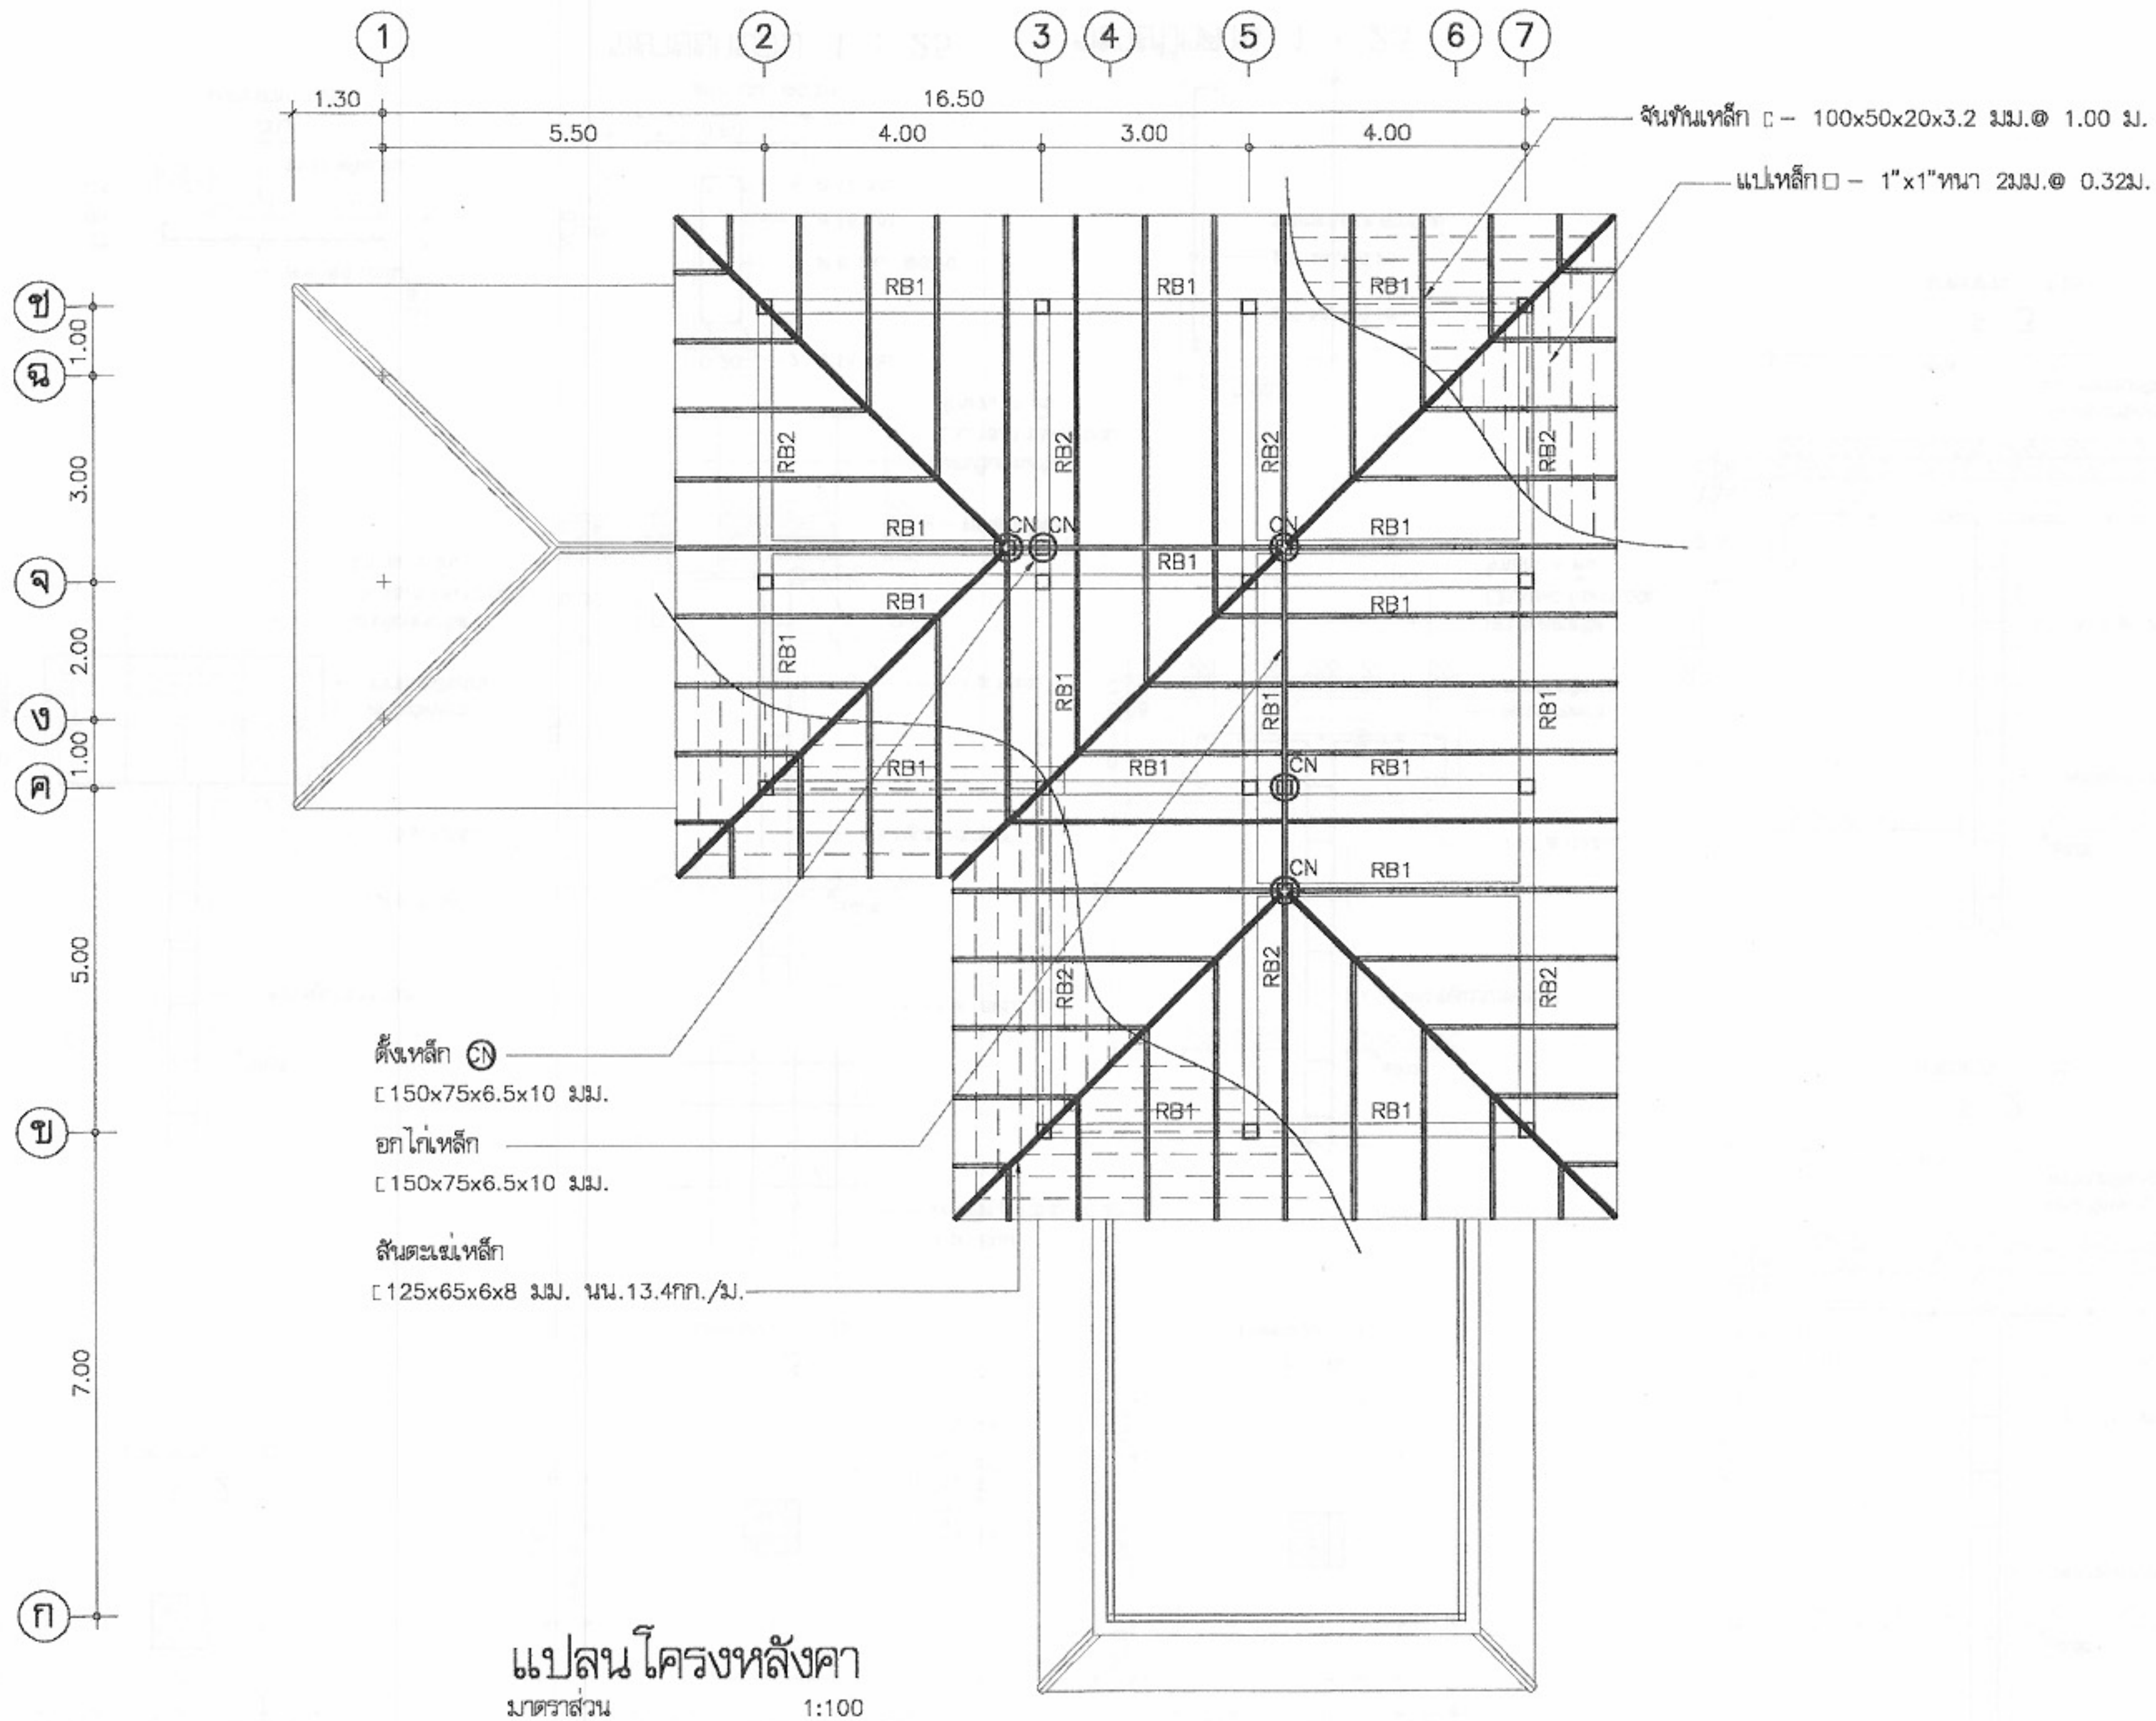


โครงการแบบอาคารเพื่อประชาชน ครอบครัวไทยเป็นสุข	
แบบ บ้านครอบครัวไทยเป็นสุข 8	
สำนักสถาปัตยกรรม	
สถาปนิก	สถาปนิก
สถาปนิก	สถาปนิก
สถาปนิก	สถาปนิก
สถาปนิก	สถาปนิก
สำนักวิศวกรรมโครงสร้างและงานระบบ	
วิศวกรรม	วิศวกร
โครงสร้าง	วิศวกร
วิศวกรรมไฟฟ้า	วิศวกร
และเครื่องกล	วิศวกร
วิศวกรรม	วิศวกร
สุขาภิบาล	วิศวกร
อนุมัติ	
(นายสว่าง ศรีสกุล) อธิบดีกรมโยธาธิการและผังเมือง	
แสดงแบบ แปลนโครงหลังคา	
มาตราส่วน	1:100
วัน/เดือน/ปี	21 พ.ย. 2546
เลขที่แบบ	ม.บ.462126
แผ่นที่	จำนวนแผ่น
S-04	07


หมายเหตุ แบบที่แสดงอยู่นี้ได้รับการยืมส่วน เพื่อใช้แสดงผลทางหน้าจอเท่านั้น สำหรับแบบที่ใช้ขออนุญาตก่อสร้าง ให้ถ่ายสำเนาจากหนังสือแบบบ้าน

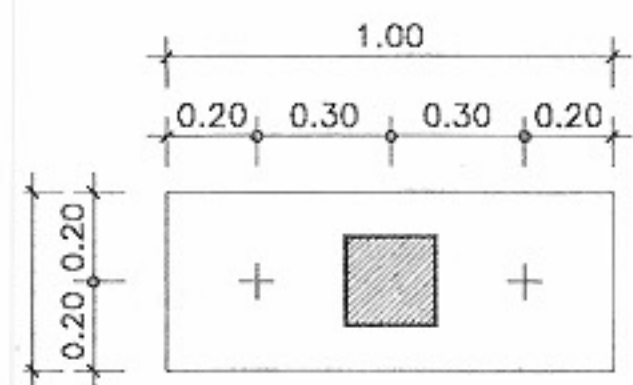





F 2
มาตราส่วน 1:25

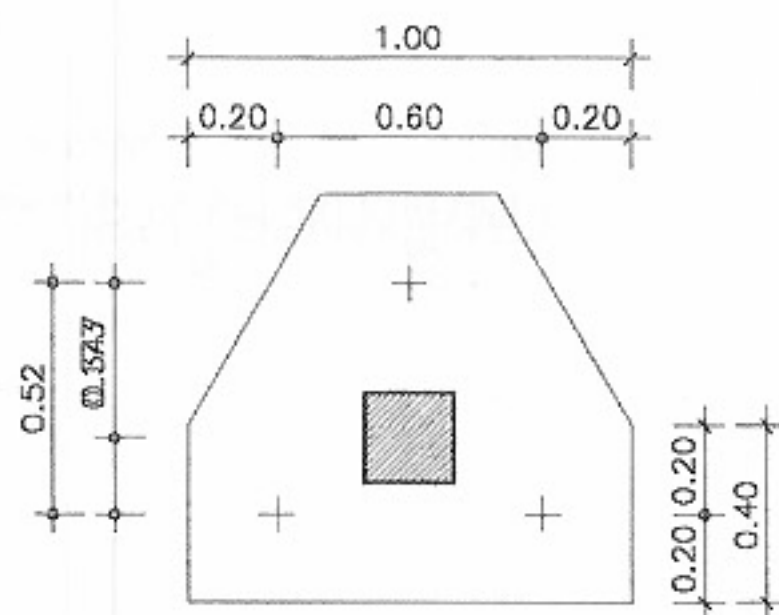


F 3
มาตราส่วน 1:25

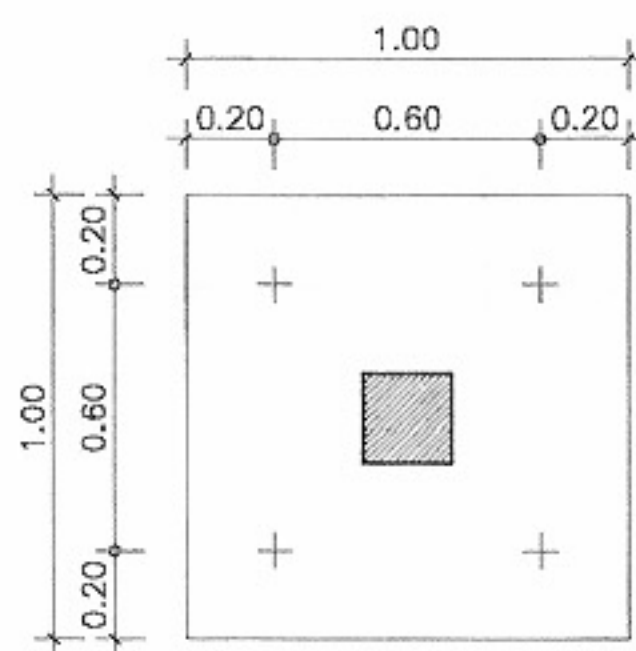


F 4
มาตราส่วน 1:25

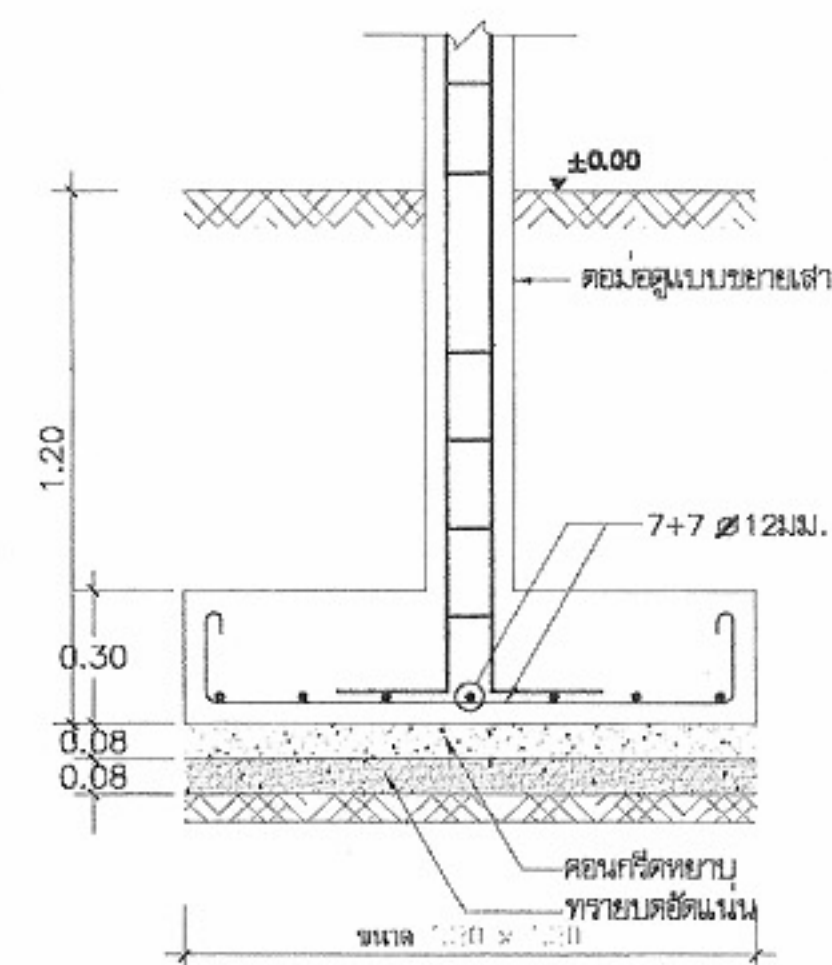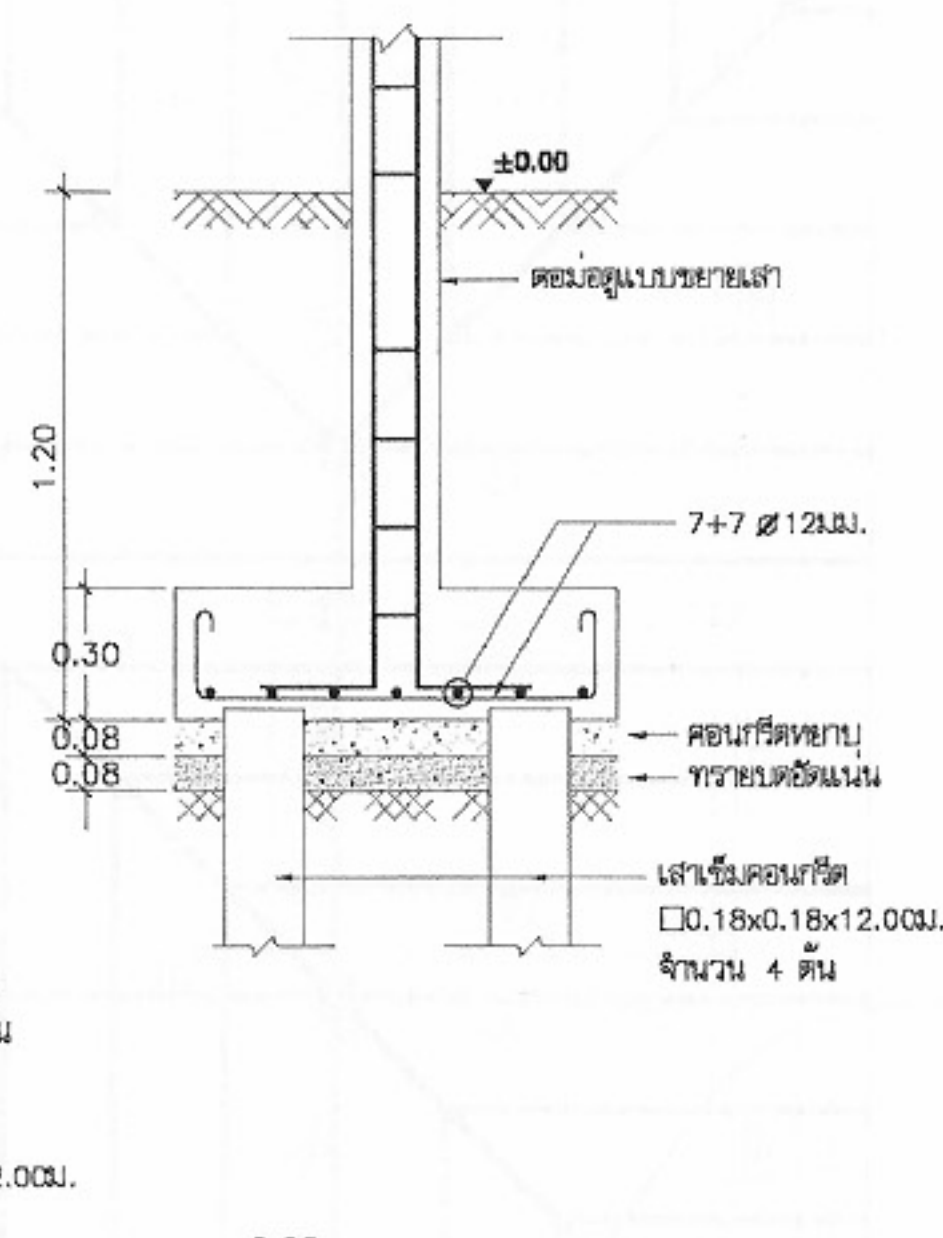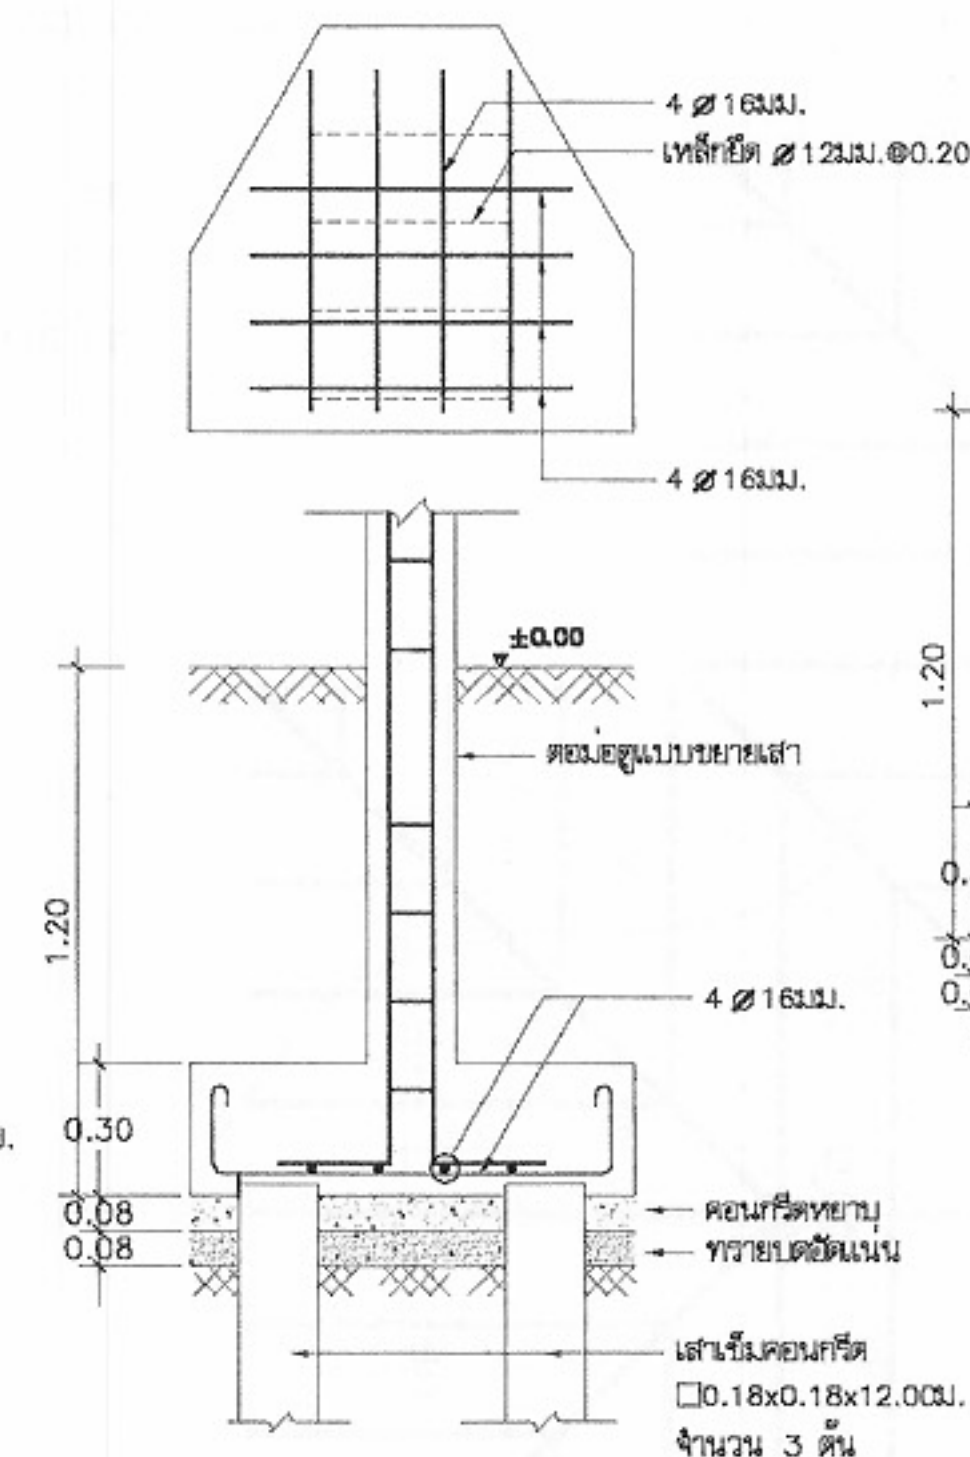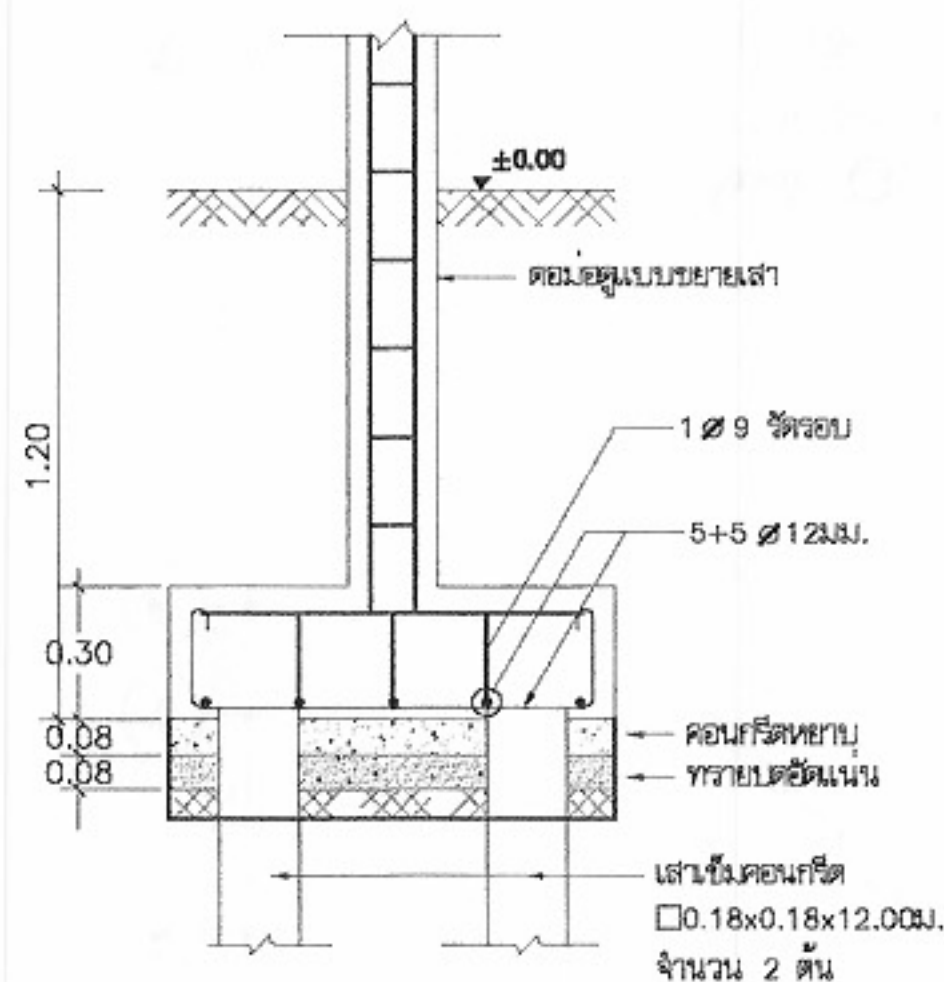


F 2
มาตราส่วน 1:25

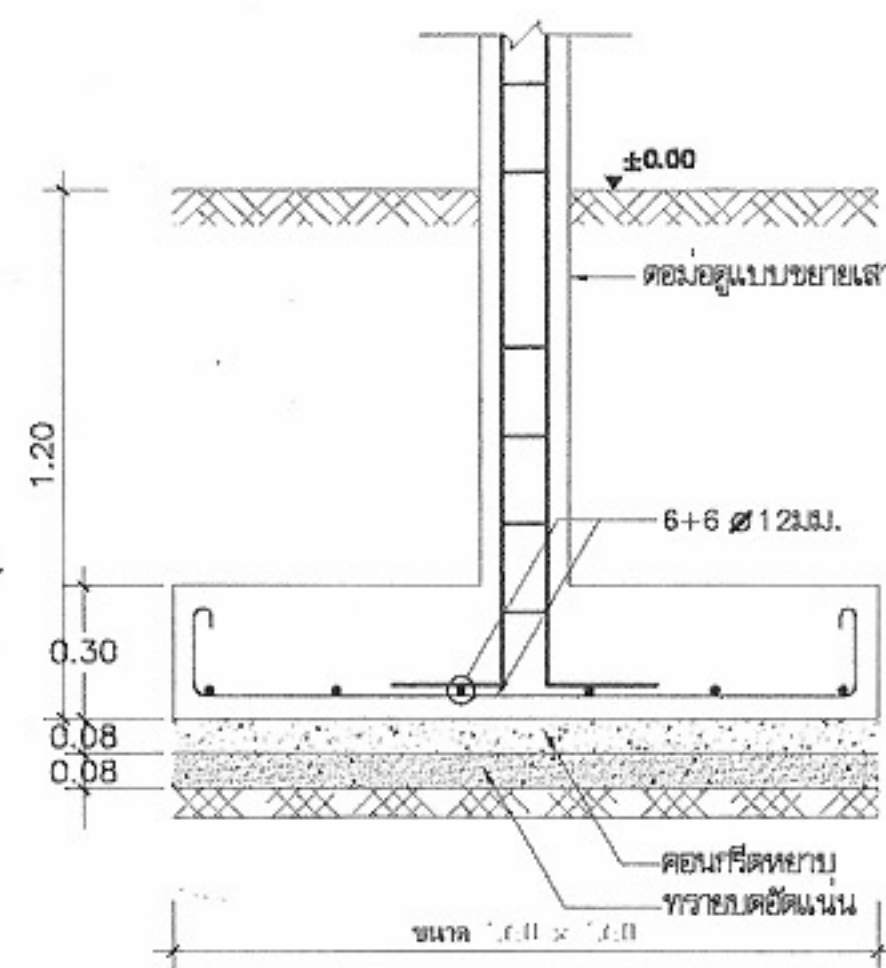


F 3
มาตราส่วน 1:25

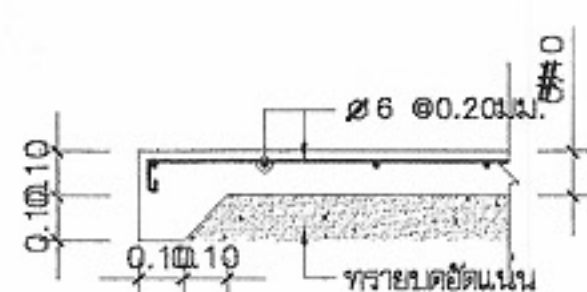

S0
มาตราส่วน 1:25

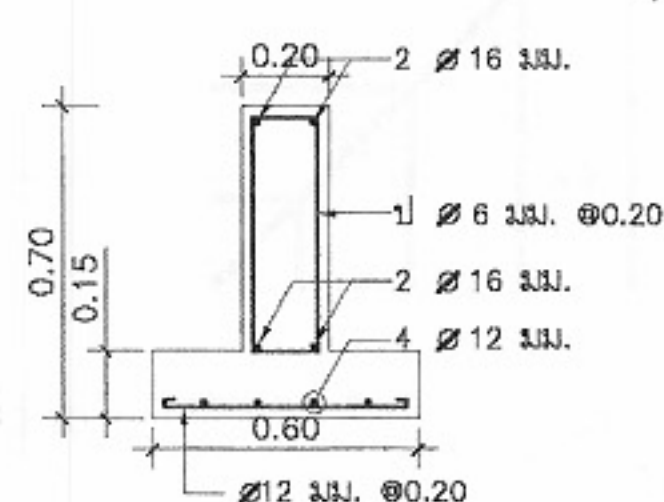

ขยายยกขอบ 1 : 25

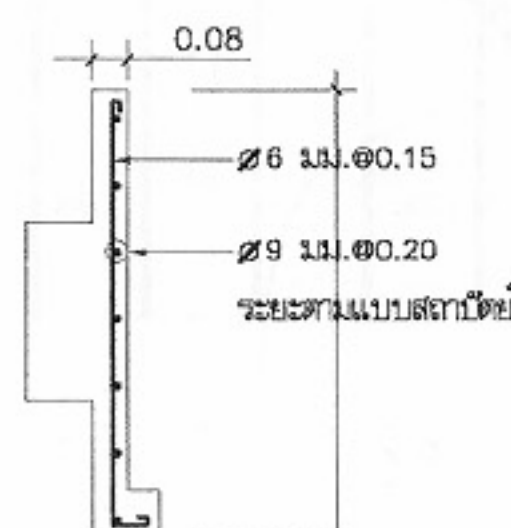

ขยายปีกคาน 1 : 25



โครงการแบบอาคารเพื่อประชาชน

ครอบครัวไทยเป็นสุข

แบบ

บ้านครอบครัวไทยเป็นสุข 8

สำนักสถาปัตย์กรรม

๗๗๖๖

สถาปัตย์กรรม

สถาปัตย์
สถาปัตย์
สถาปัตย์
สถาปัตย์

สำนักวิศวกรรมโครงสร้างและงานระบบ

๗๗๖๖

วิศวกรรม

วิศวกร
วิศวกร

วิศวกรรมไฟฟ้า

วิศวกร
วิศวกร

และเครื่องกล

วิศวกร
วิศวกร

วิศวกรรม

วิศวกร
วิศวกร

สุขาภิบาล

วิศวกร

อนุมัติ

๗๗๖๖

(นายสว่าง ศรีสุกัน)

อธิบดีกรมโยธาธิการและผังเมือง

แสดงแบบ

แบบขยายการเสริมเหล็ก
ฐานราก ,ตอม่อ

มาตราส่วน 1:25

วัน/เดือน/ปี 21 พ.ย. 2546

เลขที่แบบ ม.บ.462126









แผ่นที่

S-05

จำนวนแผ่น

07

หมายเหตุ แบบที่แสดงอยู่นี้ได้รับการยืมส่วน เพื่อใช้แสดงผลทางหน้าจอเท่านั้น สำหรับแบบที่ใช้ขออนุญาตก่อสร้าง ให้ถ่ายสำเนาจากหนังสือแบบบ้าน

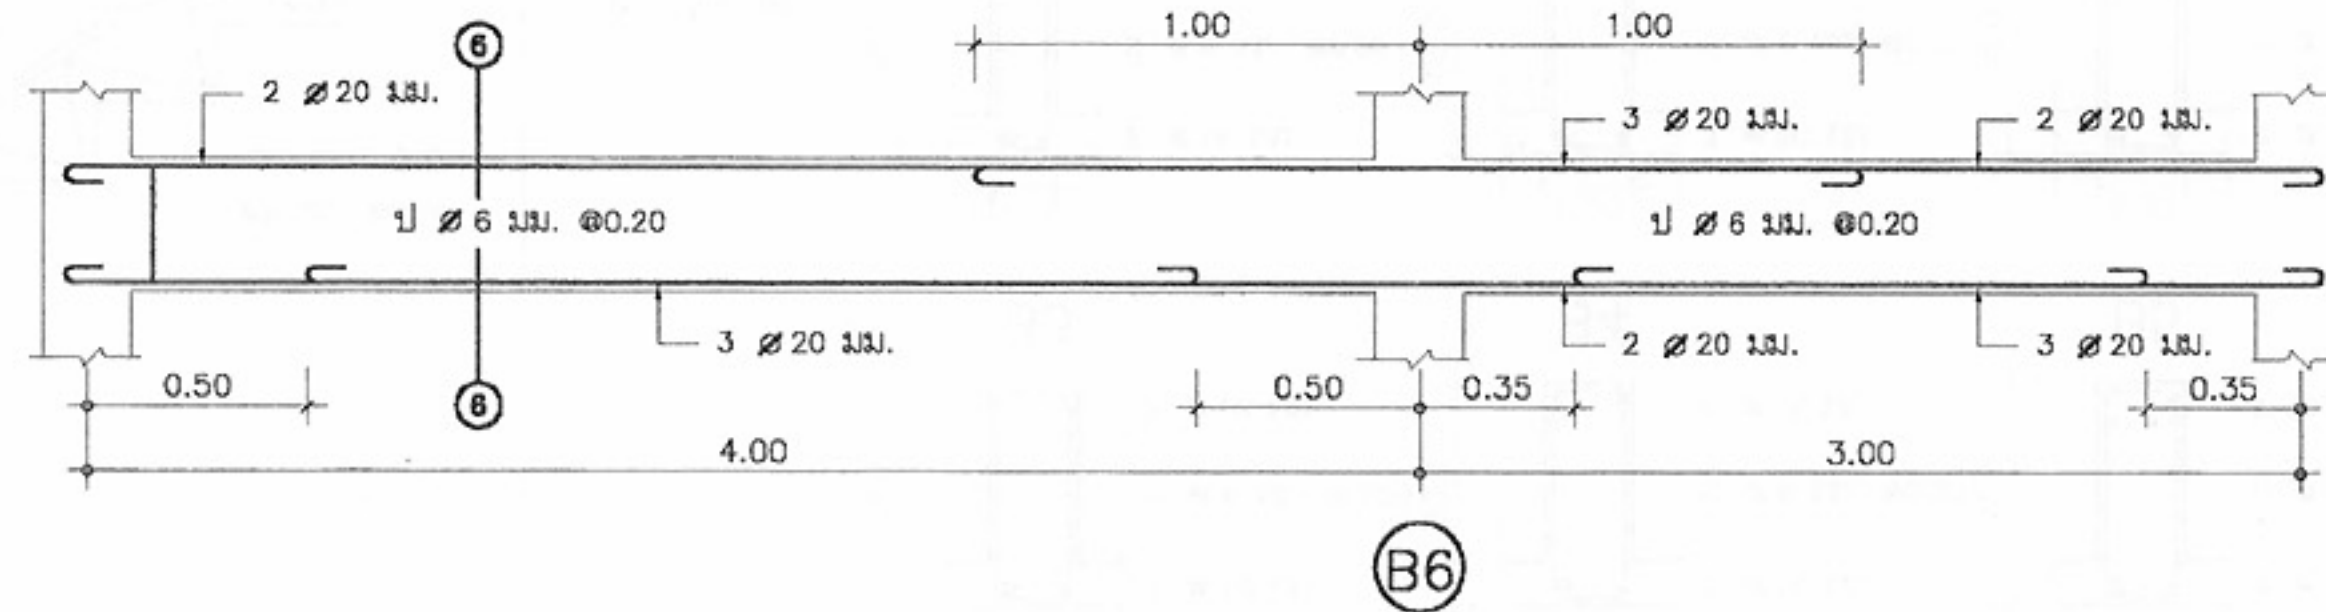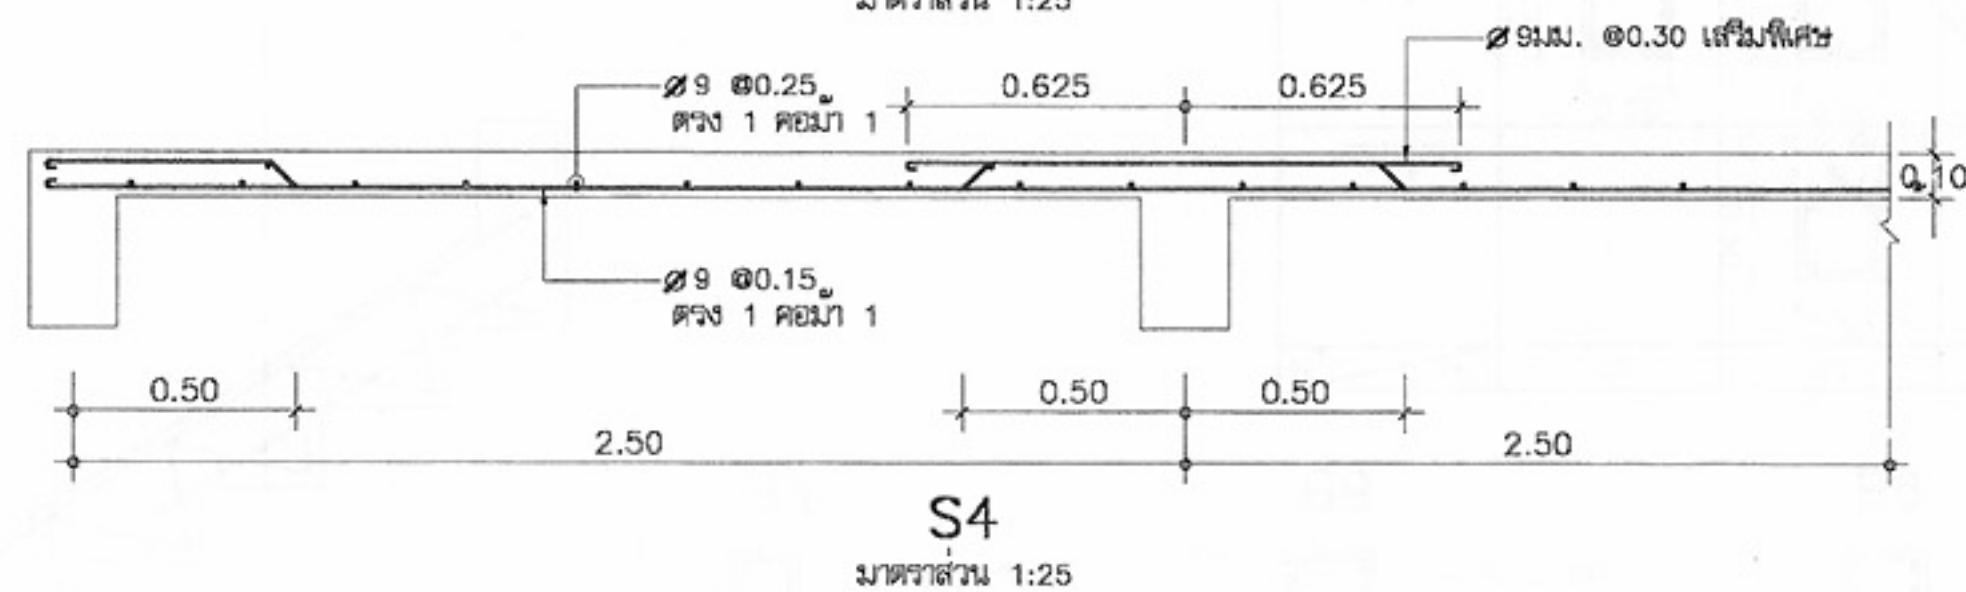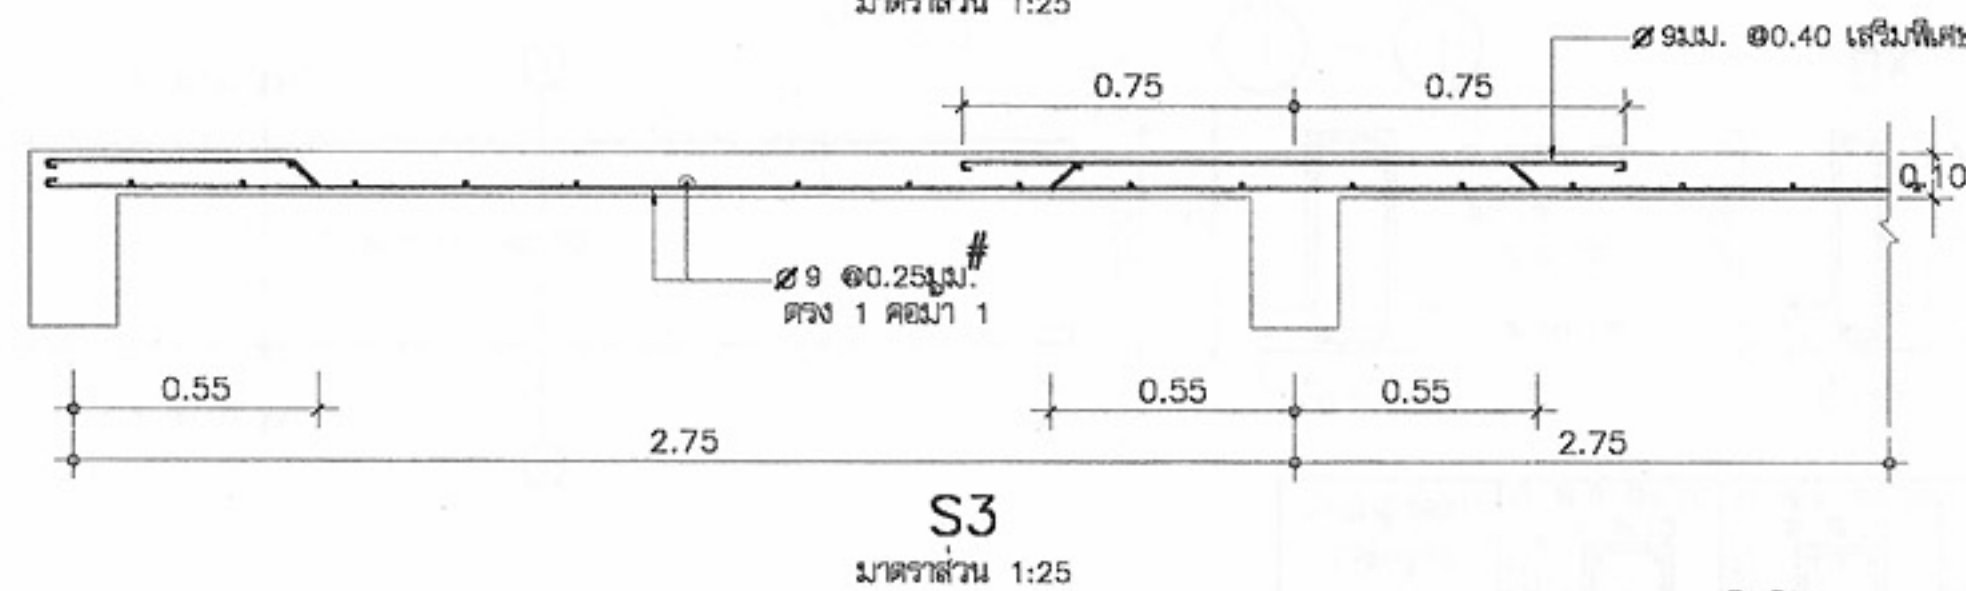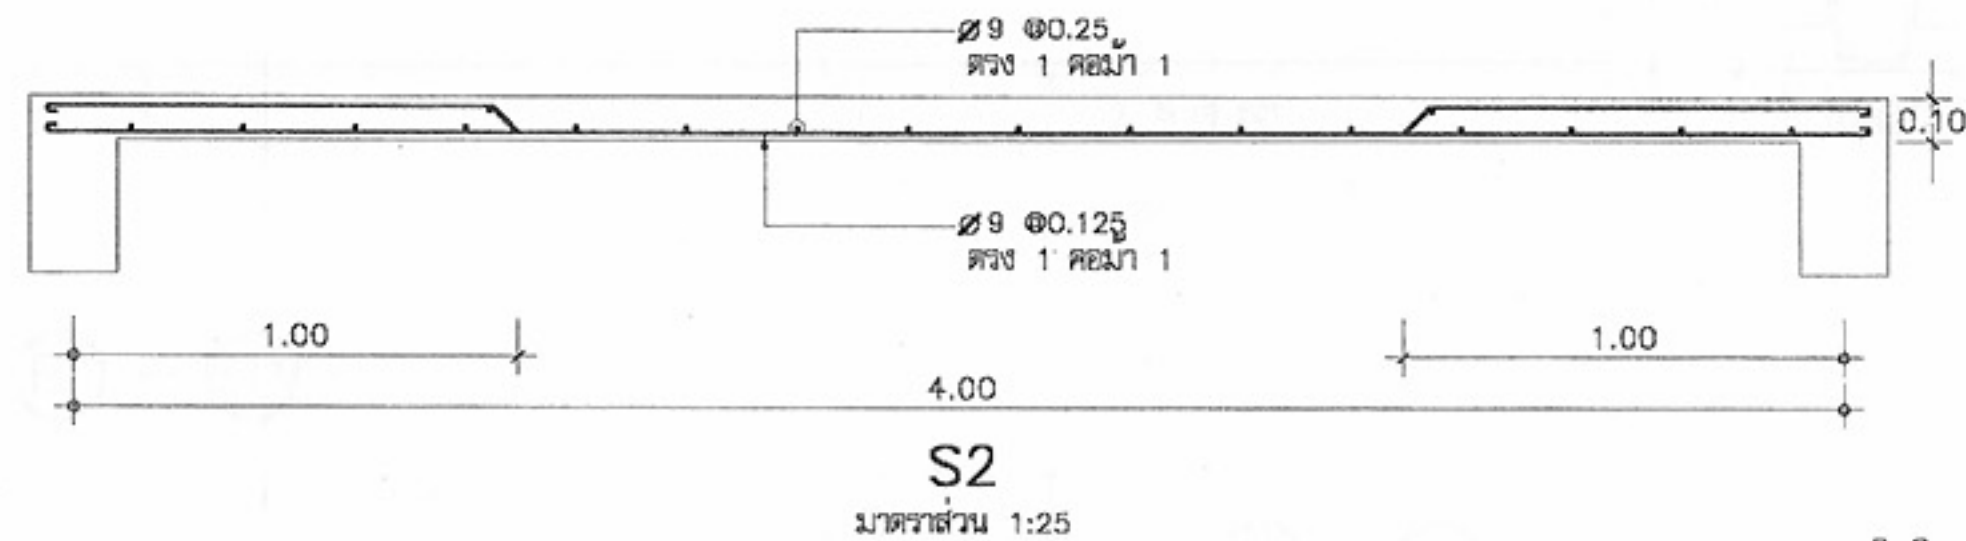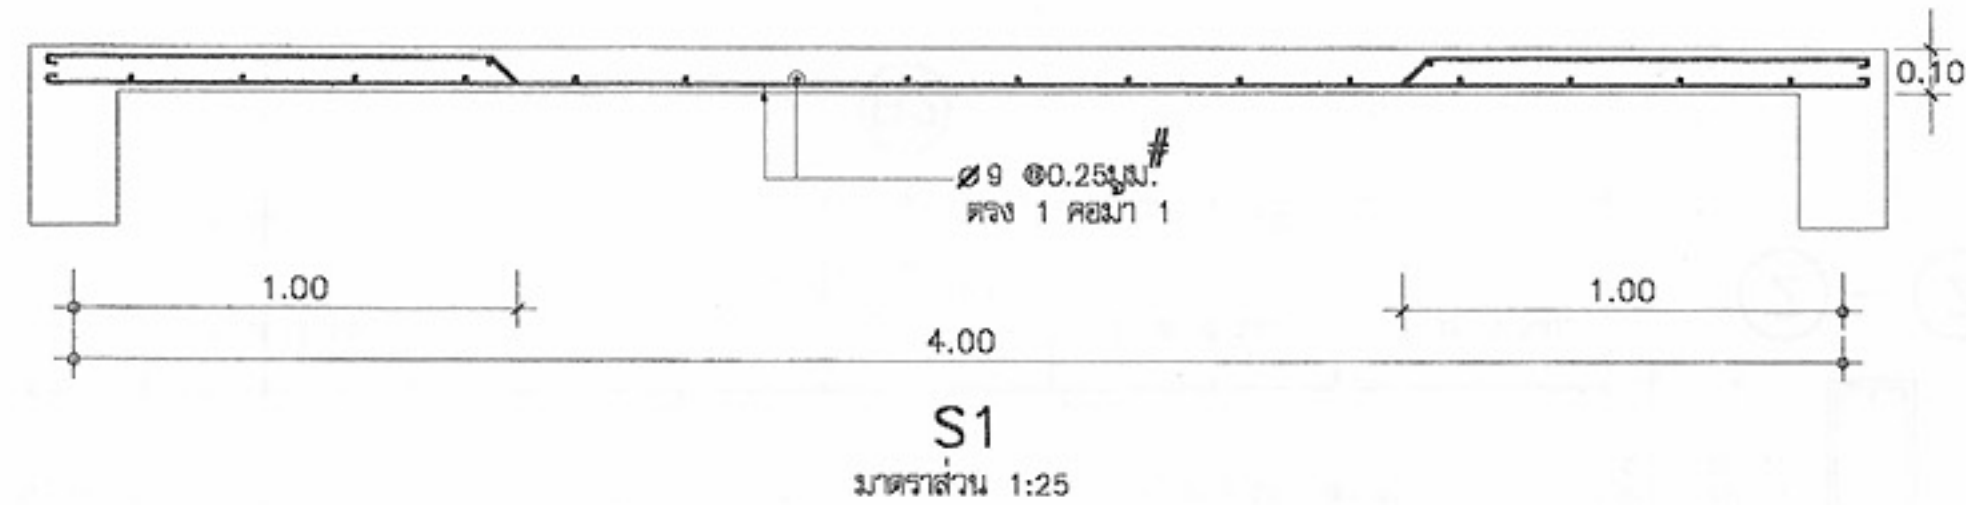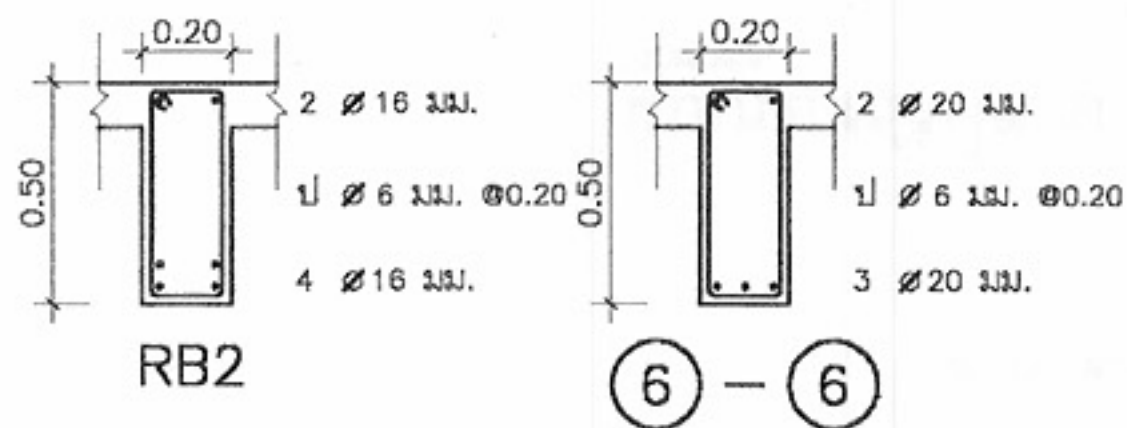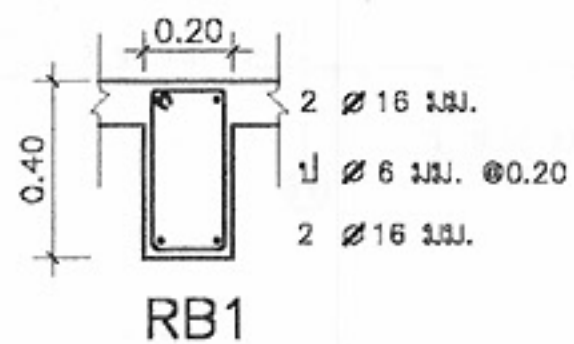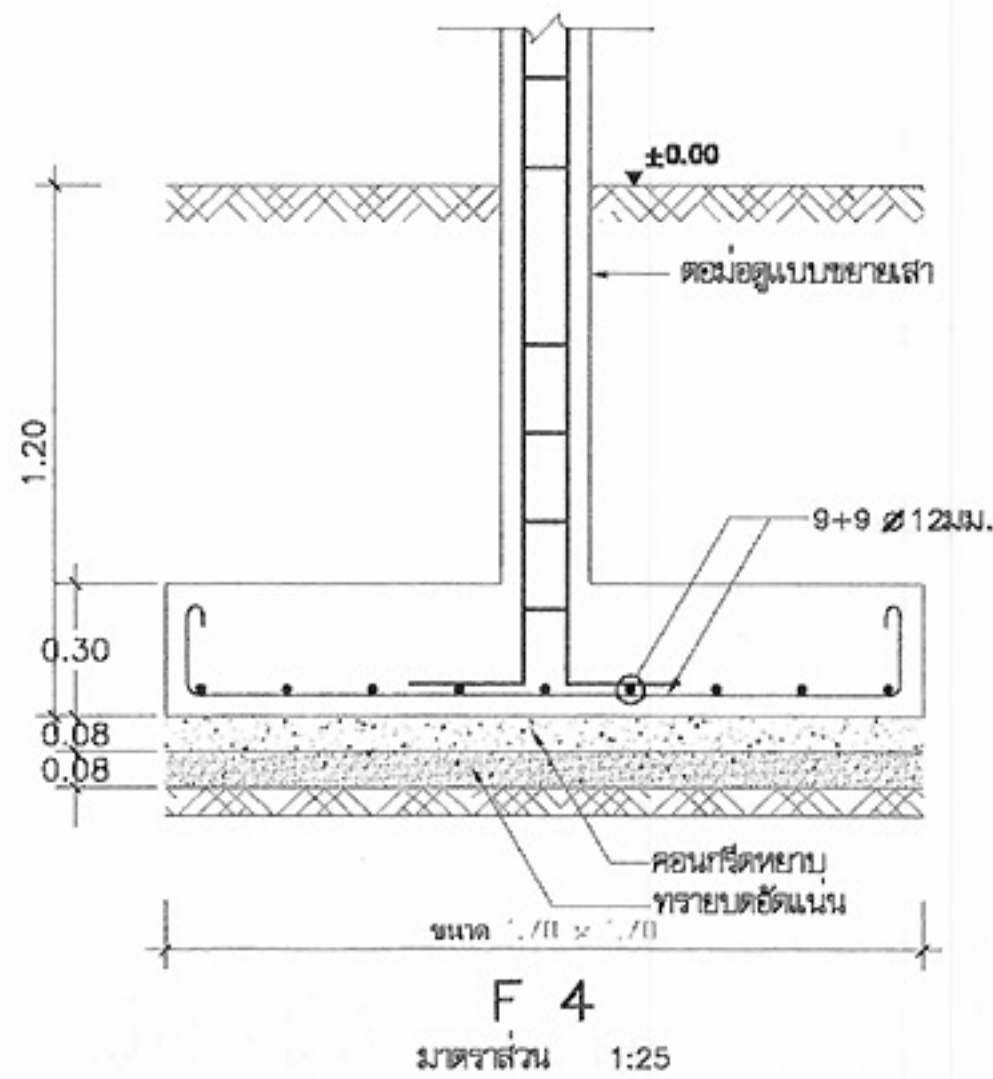

โครงการแบบอาคารเพื่อประชาชน

ครอบครัวไทยเป็นสุข

แบบ

บ้านครอบครัวไทยเป็นสุข 8

สำนักสถาปัตย์กรรม

11-1-25
ผู้อำนวยการสำนัก

สถาปัตย์กรรม

สถาปัตย์
สถาปัตย์
สถาปัตย์
สถาปัตย์

สำนักวิศวกรรมโครงสร้างและงานระบบ

ผู้อำนวยการสำนัก

วิศวกรรม

วิศวกร

โครงสร้าง

วิศวกร

วิศวกรรมไฟฟ้า

วิศวกร

และเครื่องกล

วิศวกร

วิศวกรรม

วิศวกร

สุขาภิบาล

วิศวกร

อนุมัติ

11-1-25

(นายสว่าง ศรีสุกัน)

อธิบดีกรมโยธาธิการและผังเมือง

แสดงแบบ

แบบขยายการเสริมเหล็ก
ใน พื้น

มาตราส่วน 1:25

วัน/เดือน/ปี 21 พ.ย. 2546

เลขที่แบบ ม.บ.462126






แผ่นที่

S-06

จำนวนแผ่น

07

หมายเหตุ แบบที่แสดงอยู่นี้ได้รับการยืมส่วน เพื่อใช้แสดงผลทางหน้าจอเท่านั้น สำหรับแบบที่ใช้ขออนุญาตก่อสร้าง ให้ถ่ายสำเนาจากหนังสือแบบบ้าน

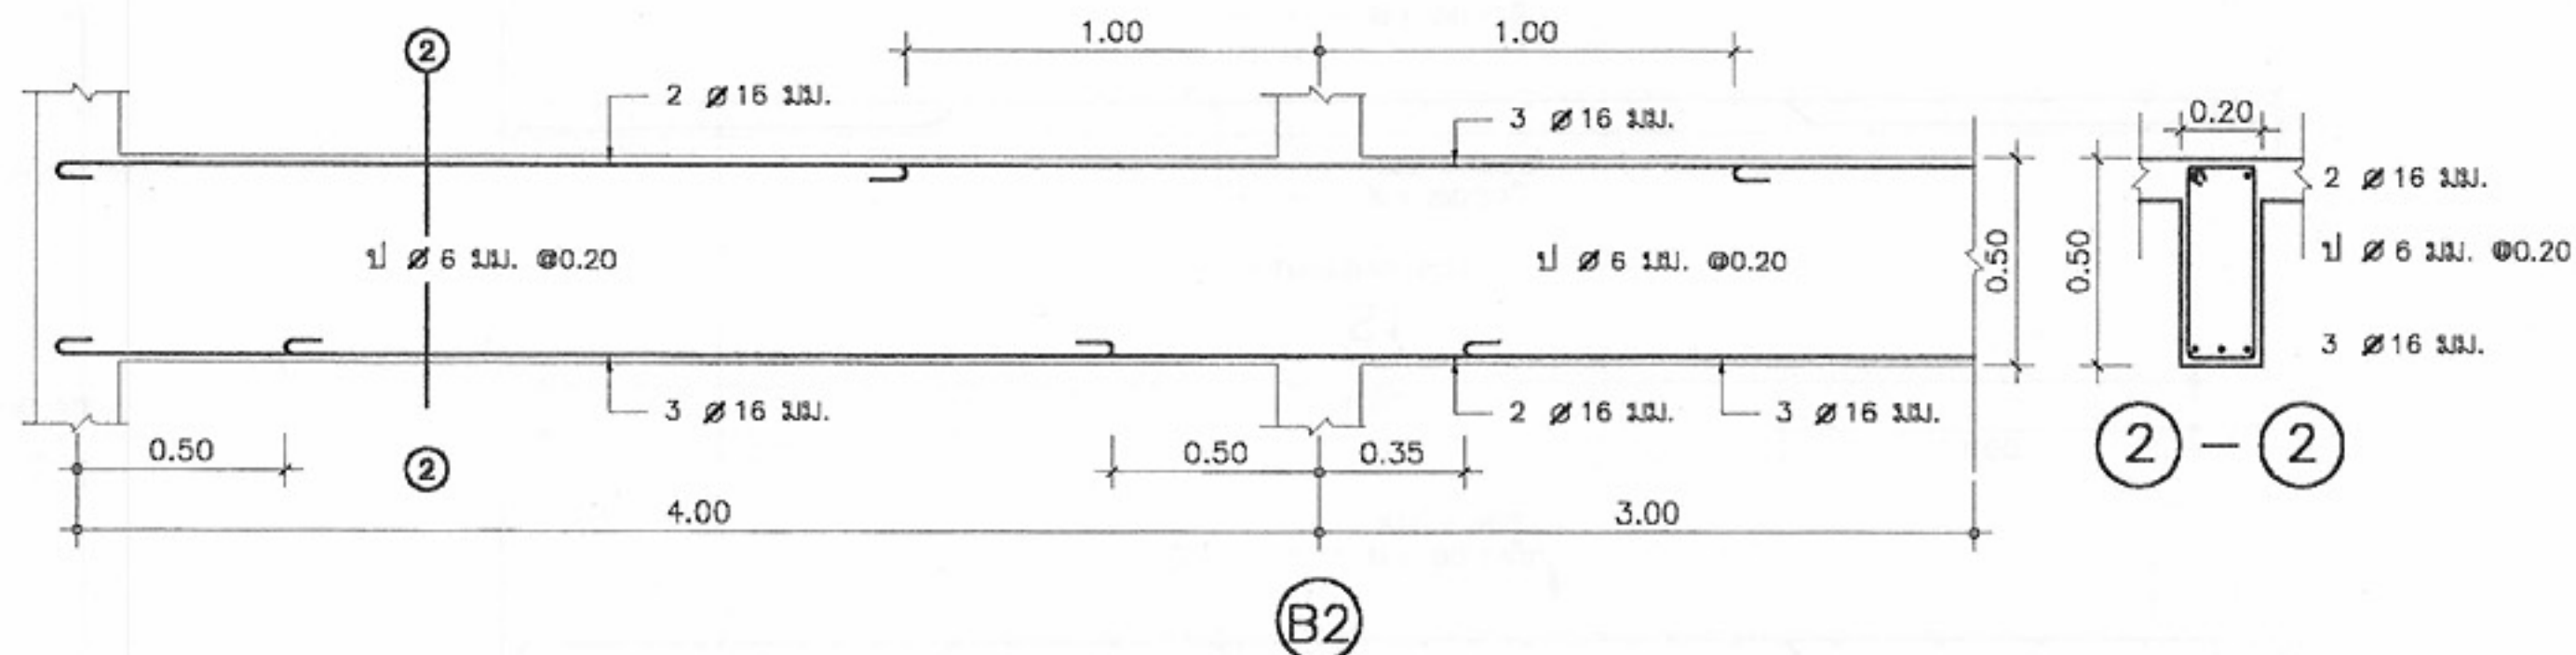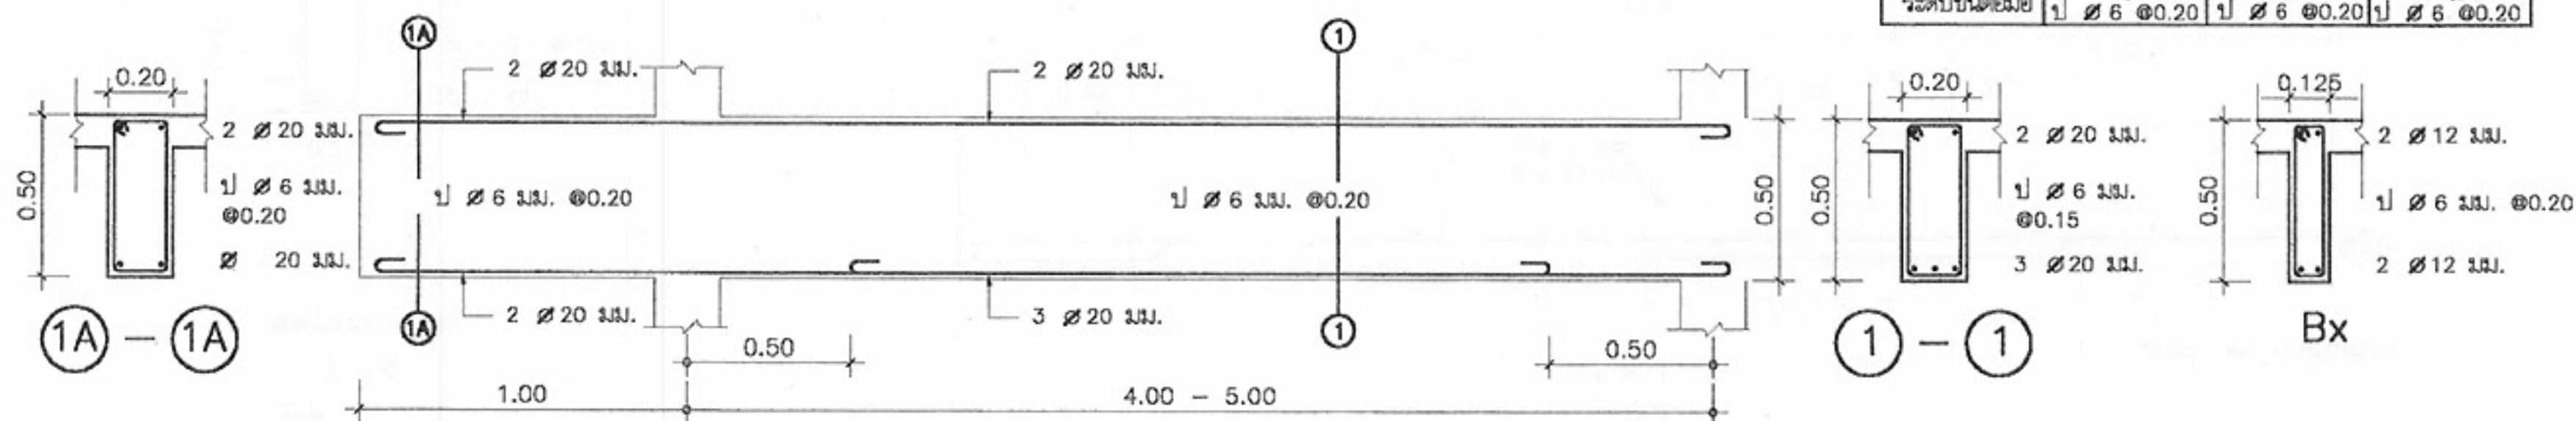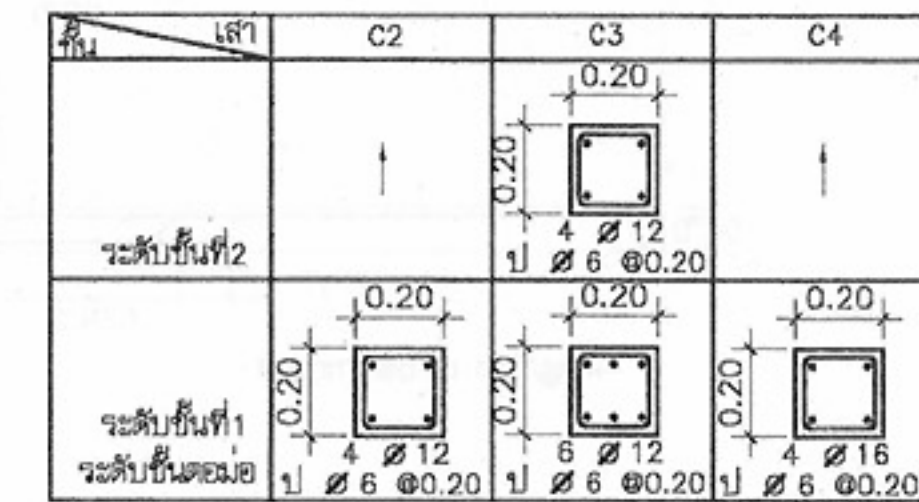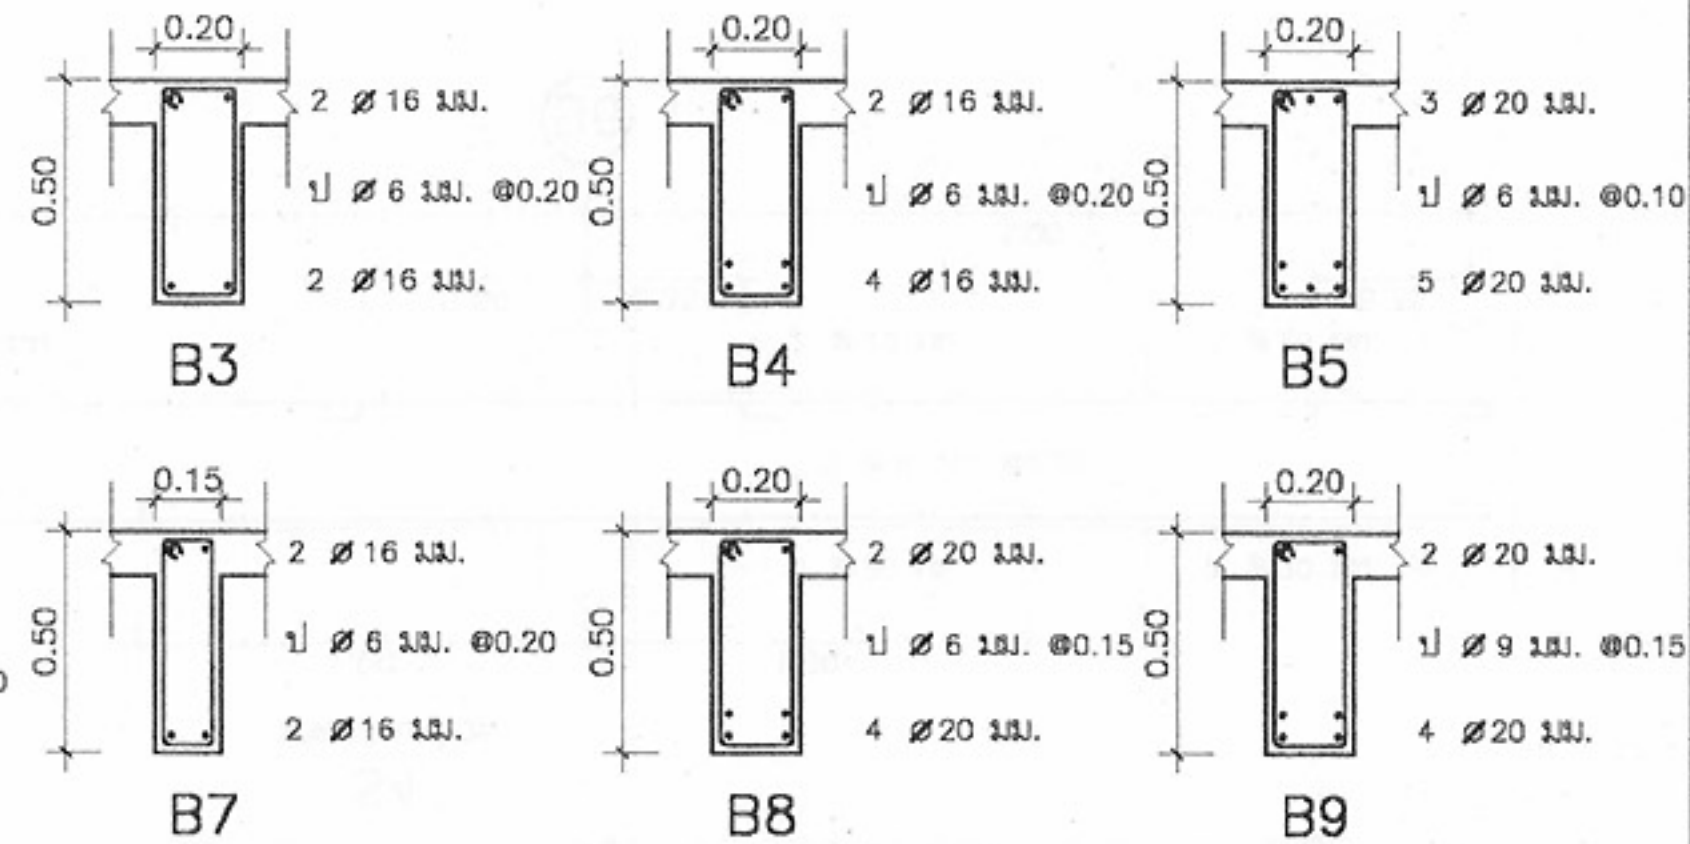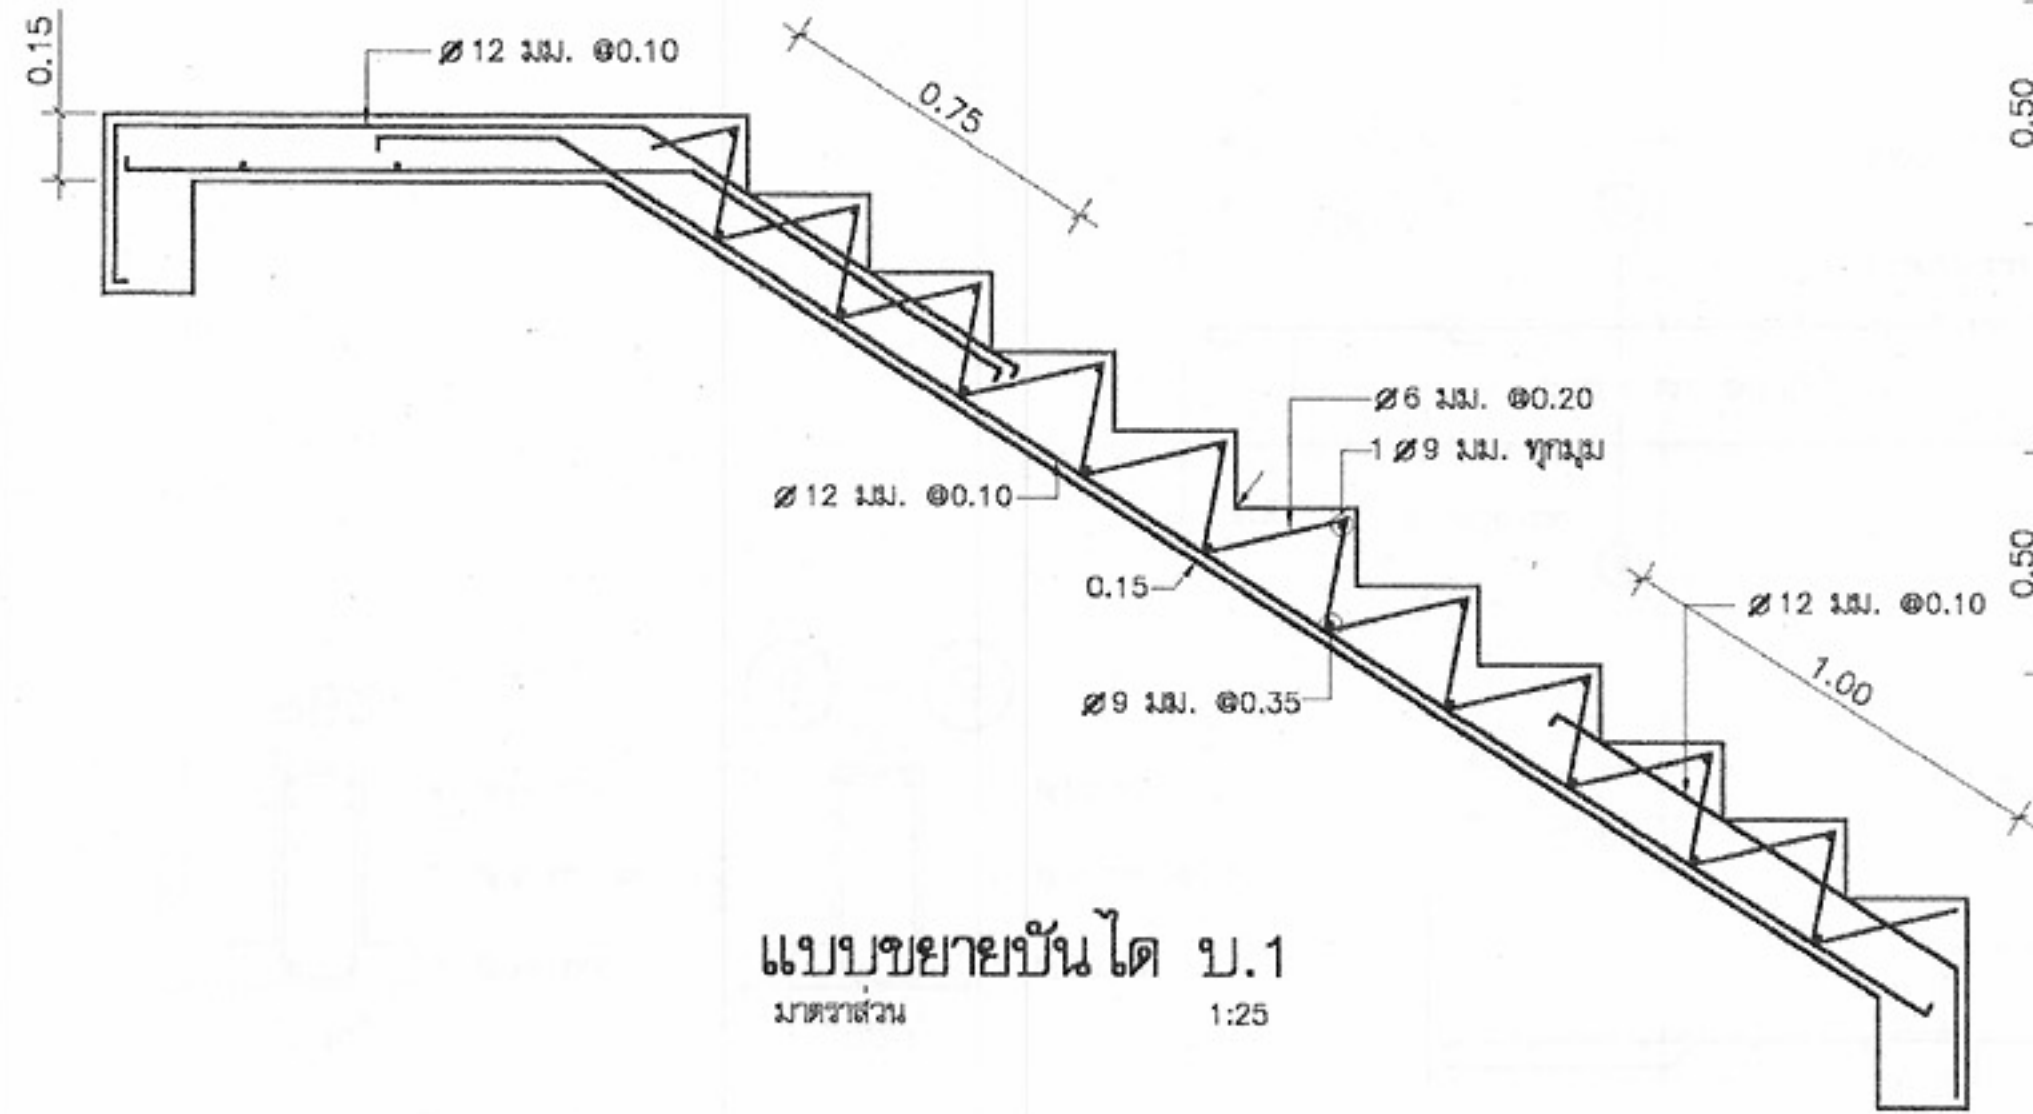

โครงการแบบอาคารเพื่อประชาชน
ครอบครัวไทยเป็นสุข

แบบ
บ้านครอบครัวไทยเป็นสุข 8

สำนักสถาปัตย์กรรม
11-11-11
ผู้อำนวยการสำนัก

สถาปัตย์กรรม
สถาปนิก
สถาปนิก
สถาปนิก
สถาปนิก

สำนักวิศวกรรมโครงสร้างและระบบ
11-11-11
ผู้อำนวยการสำนัก

วิศวกรรม
โครงสร้าง
วิศวกรรมการไฟฟ้า
และเครื่องกล
วิศวกรรมการ
สุขาภิบาล
วิศวกร
วิศวกร
วิศวกร
วิศวกร
วิศวกร

อนุมัติ
11-11-11
(นายสว่าง ศรีสกุล)
อธิบดีกรมโยธาธิการและผังเมือง

แสดงแบบ
แบบขยายการเสริมเหล็ก
ใน คาน, บันได ค.ส.ล.

มาตราส่วน 1:25

วัน/เดือน/ปี 21 พ.ย. 2546

เลขที่แบบ ม.บ.462126

แผ่นที่ S-07 จำนวนแผ่น 07

หมายเหตุ แบบที่แสดงอยู่นี้ได้รับการยืมส่วน เพื่อใช้แสดงผลทางหน้าจอเท่านั้น สำหรับแบบที่ใช้ขออนุญาตก่อสร้าง ให้ถ่ายสำเนาจากหนังสือแบบบ้าน

สัญลักษณ์ระบบไฟฟ้า

	CIRCUIT BREAKER
	แผงสวิตช์ตัดตอนอัตโนมัติ ติดผนังสูงจากพื้น 1.80 เมตร ถึงส่วนบนสุด
	ดวงโคม DOWNLIGHT ขนาด ๕ 6 นิ้ว หลอด SUPERLUX 1-100W ติดผนังฝ้าเพดาน
	ดวงโคม DOWNLIGHT ขนาด ๕ 6 นิ้ว หลอด COMPACT FLUORESCENT 1-11W ติดผนังฝ้าเพดาน
	ดวงโคมแก้วชาลาเปา ขนาด ๕ 8 นิ้ว หลอด INCANDESCENT 1-40W ติดฝ้าเพดาน
	ดวงโคมไฟผนังขาอูมิเนียม ขนาด ๕ 10 นิ้ว หลอด COMPACT FLUORESCENT 1-18W ติดผนังสูงกำหนดในงาน
	ดวงโคมครอบแก้วทรงกลม หลอด FLUORESCENT 1-32W ติดฝ้าเพดาน
	ดวงโคมห้อยเพดาน หลอด INCANDESCENT ติดแขวนเพดาน
	ดวงโคมฟลูออเรสเซนต์ กล่องเหล็กเปลี่ยน หลอด 1-18W ติดเพดานหรือผนัง
	ดวงโคมฟลูออเรสเซนต์ กล่องเหล็กเปลี่ยน หลอด 1-36W ติดเพดานหรือผนัง
	กริ่งสัญญาณ นูไทน ชนิด 250Vac ติดผนังต่ำจากเพดาน 0.20 เมตร
	• สวิตช์เดี่ยวขนาด 16A-250V ติดผนังเรียบผนังหรือข้างเสา สูงจากพื้น 1.30 เมตร
	• สวิตช์กริ่งสัญญาณชนิดกันน้ำ ขนาด 10A-250V ติดผนังหรือข้างเสา สูงจากพื้น 1.80 เมตร
	• สวิตช์หรี่ไฟ (DIMMER SWITCH) ขนาด 800W ติดผนังเรียบผนังหรือข้างเสา สูงจากพื้น 1.30 เมตร
	• ตัวรับไฟฟ้าคู่มือดิน (UNIVERSAL TYPE) ชนิดมีมันนิรภัย ขนาด 16A-250V ติดผนังเรียบผนังหรือข้างเสา สูงจากพื้น 0.30 ม.
	① กล่องต่อสายไฟฟ้า
	≡ หลักสายดินทองแดง ขนาด ๕ 5/8" ยาว 2.40 เมตร
	— สายไฟฟ้าเดินร้อยในท่อสายไฟโลหะ ผิวผนังคอนกรีตและ/หรือซ่อนในฝ้า
	→ สายเมนวงจรรย่อย
	→> สายไฟฟ้าเดินต่อไป

สัญลักษณ์ระบบทีวี

	TAB-OFF 4 WAY
	SPLITTER 4 WAY
	ตัวรับทีวี ติดผนังเรียบผนังหรือข้างเสา

สัญลักษณ์ระบบโทรศัพท์


	กล่องต่อสายโทรศัพท์
	ตัวรับโทรศัพท์ชนิด RJ-11 ติดผนังเรียบผนังหรือข้างเสา

รายละเอียด


- ในการติดตั้ง ผู้รับจ้างต้องปฏิบัติตามกฎระเบียบข้อบังคับของการไฟฟ้า
- วัสดุอุปกรณ์ที่ใช้
 - 2.1 แผงสวิตช์อัตโนมัติเป็นผลิตภัณฑ์ของ SQUARE D, ABB, MEM, CLIPSAL
TICINO, SIEMENS, MG, HAGER
 - 2.2 CIRCUIT BREAKER เป็นผลิตภัณฑ์ของ SQUARE D, ABB, MEM, CLIPSAL
TICINO, SIEMENS, MG, HAGER
 - 2.3 ดวงโคมไฟฟ้าเป็นผลิตภัณฑ์ภายในประเทศที่มีเครื่องหมายการค้าโดยมีอุปกรณ์ประกอบดังนี้
 - หลอดฟลูออเรสเซนต์ มอก. 236-2533
 - ขั้วรับหลอดและขั้วรับสตาฟเตอร์ มอก. 344-2530
 - สตาฟเตอร์ มอก. 183-2528
 - บัสบาร์ มอก. 23-2521
 - 2.4 สายไฟฟ้าเป็นผลิตภัณฑ์ มอก. 11-2531
 - 2.5 สวิตช์และตัวรับไฟฟ้า เป็นผลิตภัณฑ์ของ NATIONAL, ABB, TICINO, CLIPSAL
- หากมิได้กำหนดไว้เป็นอย่างอื่น ชนิดและขนาดของสายไฟให้ใช้ดังนี้
 - 3.1 สายเมนวงจรรย่อย (HOME RUN) ใช้สาย 2.5 sq.mm. THW.
 - 3.2 สายไฟระหว่างดวงโคม และสายจากสวิตช์เข้าดวงโคม ใช้สาย 2.5 sq.mm. THW.
 - 3.3 สายวงจรมัดรับและสายดิน ใช้สาย 2.5 sq.mm. THW.

โครงการแบบอาคารเพื่อประชาชน ครอบครัวไทยเป็นสุข	
แบบ บ้านครอบครัวไทยเป็นสุข 8	
สำนักสถาปัตยกรรม	ผู้อำนวยการ
สถาปัตยกรรม	สถาปนิก
	สถาปนิก
	สถาปนิก
สำนักวิศวกรรมโครงสร้างและงานระบบ	ผู้อำนวยการ
วิศวกรรม	วิศวกร
โครงสร้าง	วิศวกร
วิศวกรรมไฟฟ้า	วิศวกร
และเครื่องกล	วิศวกร
วิศวกรรม	วิศวกร
สุขาภิบาล	วิศวกร
อนุมัติ (นายสว่าง ศรีสุกัน) อธิบดีกรมโยธาธิการและผังเมือง	
แสดงแบบ สัญลักษณ์,รายละเอียด	
มาตราส่วน	
วัน/เดือน/ปี	21 พ.ย. 2546
เลขที่แบบ	ม.บ.462126
แผ่นที่	จำนวนแผ่น
E-01	06

หมายเหตุ แบบที่แสดงอยู่นี้ได้รับการยืมส่วน เพื่อใช้แสดงผลทางหน้าจอเท่านั้น สำหรับแบบที่ใช้ขออนุญาตก่อสร้าง ให้ถ่ายสำเนาจากหนังสือแบบบ้าน

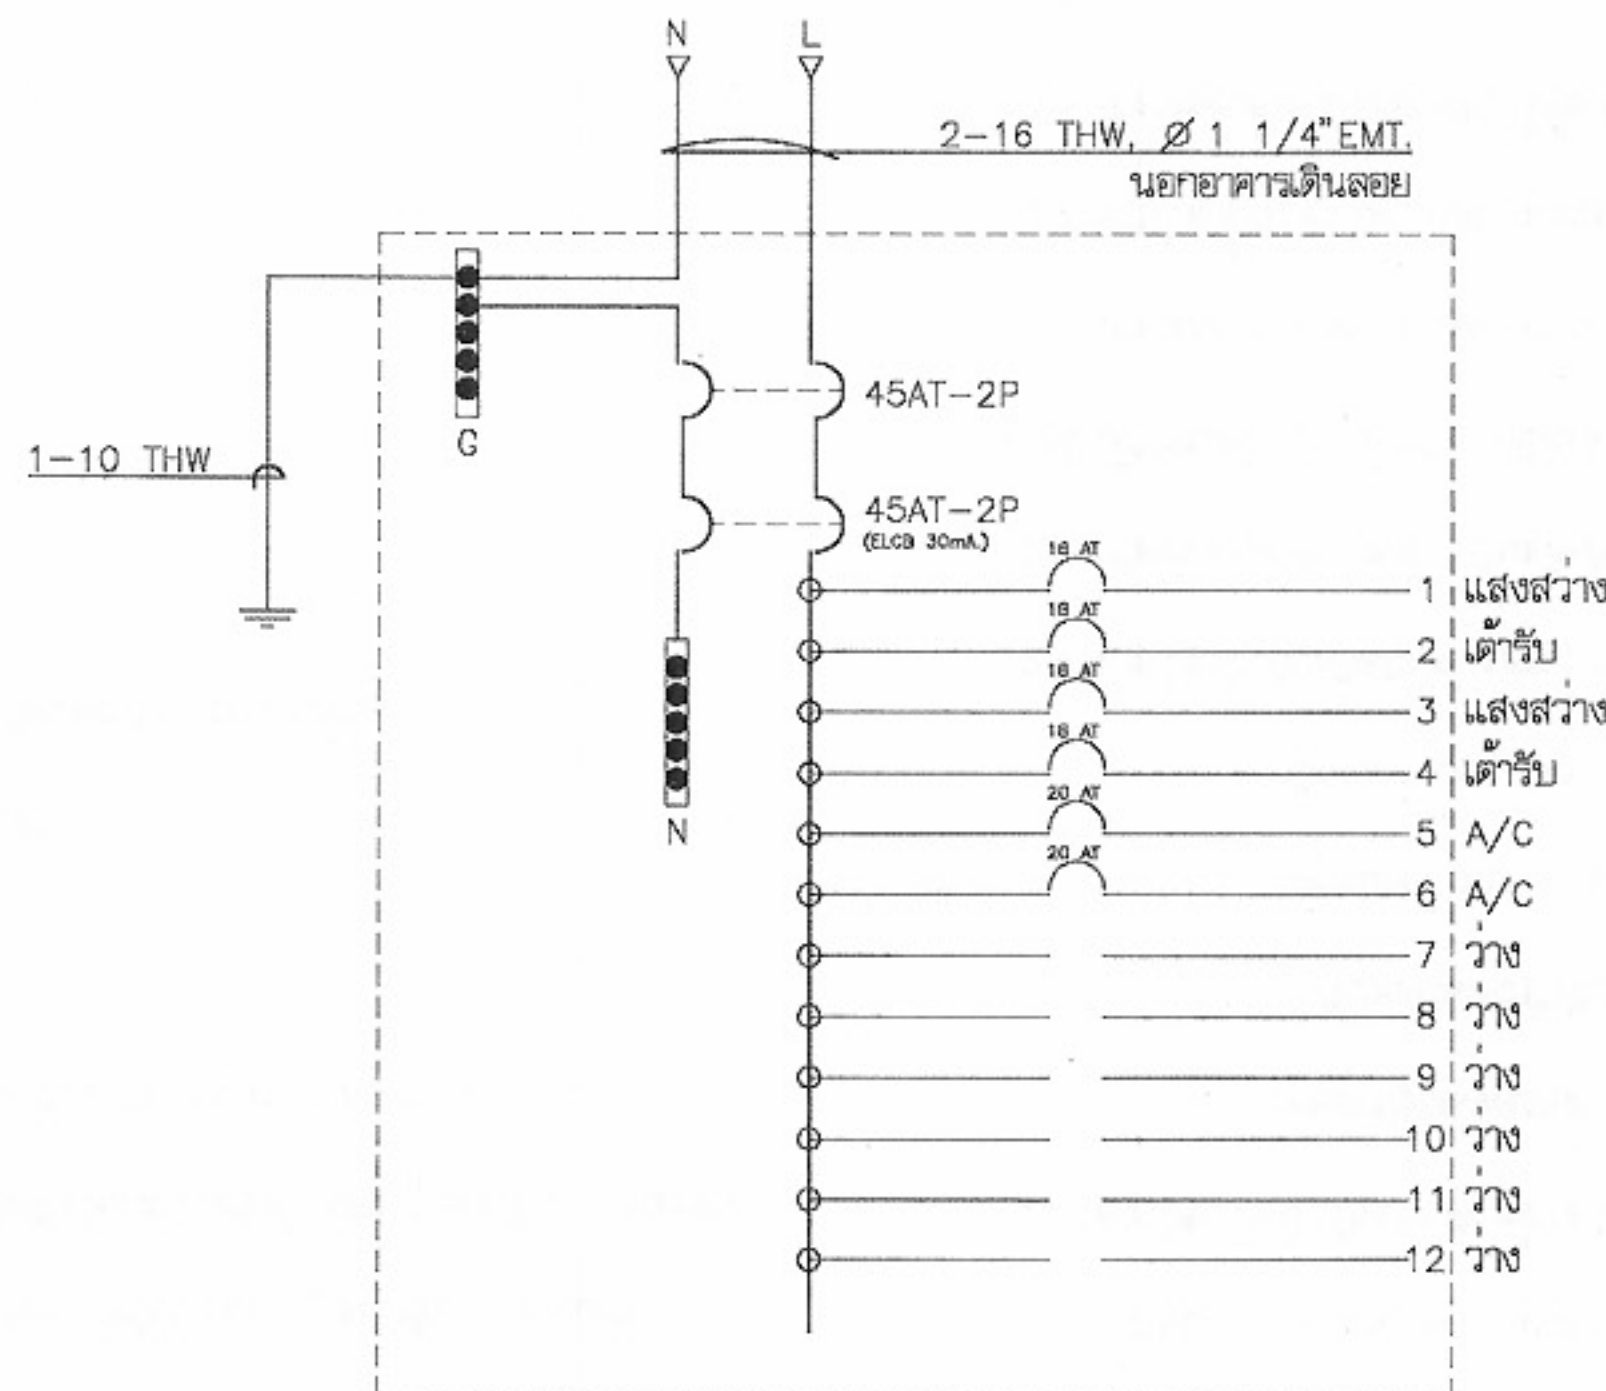

รายละเอียดแผง L

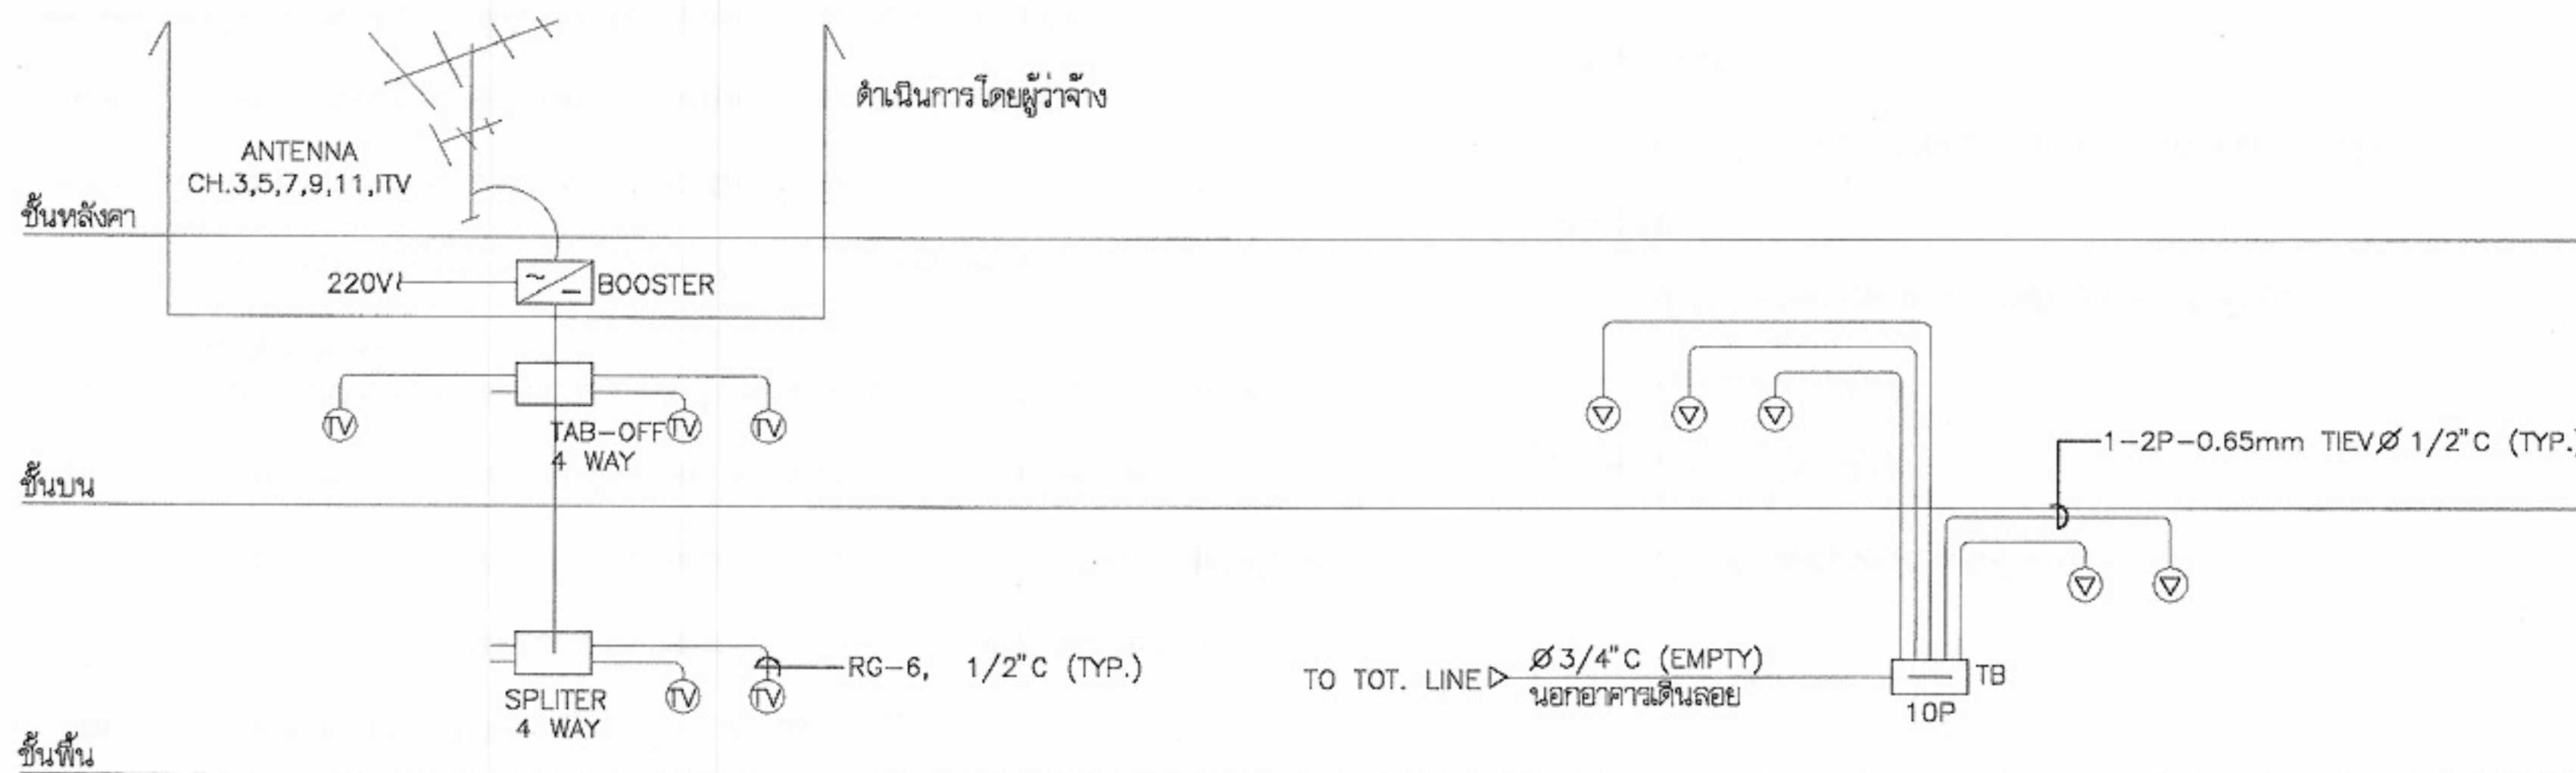

TV RISER DIAGRAM

TELEPHONE RISER DIAGRAM



โครงการแบบอาคารเพื่อประชาชน

ครอบครัวไทยเป็นสุข

แบบ

บ้านครอบครัวไทยเป็นสุข 8

สำนักสถาปัตยกรรม

77-77-77

สถาปัตยกรรม

สถาปนิก

สถาปนิก

สถาปนิก

สถาปนิก

สำนักวิศวกรรมโครงสร้างและงานระบบ

77-77-77

วิศวกรรม

วิศวกร

โครงสร้าง

วิศวกร

วิศวกรรมไฟฟ้า

วิศวกร

และเครื่องกล

วิศวกร

วิศวกรรม

วิศวกร

สุขาภิบาล

วิศวกร

อนุมัติ

77-77-77

(นายสว่าง ศรีสุคนธ์)

อธิบดีกรมโยธาธิการและผังเมือง

แสดงแบบ

DIAGRAM

มาตรฐาน

วัน/เดือน/ปี

21 พ.ย. 2546

เลขที่แบบ

ม.บ.462126


แผ่นที่

จำนวนแผ่น

E-02

06

หมายเหตุ แบบที่แสดงอยู่นี้ได้รับการยืมส่วน เพื่อใช้แสดงผลทางหน้าจอเท่านั้น สำหรับแบบที่ใช้ขออนุญาตก่อสร้าง ให้ถ่ายสำเนาจากหนังสือแบบบ้าน

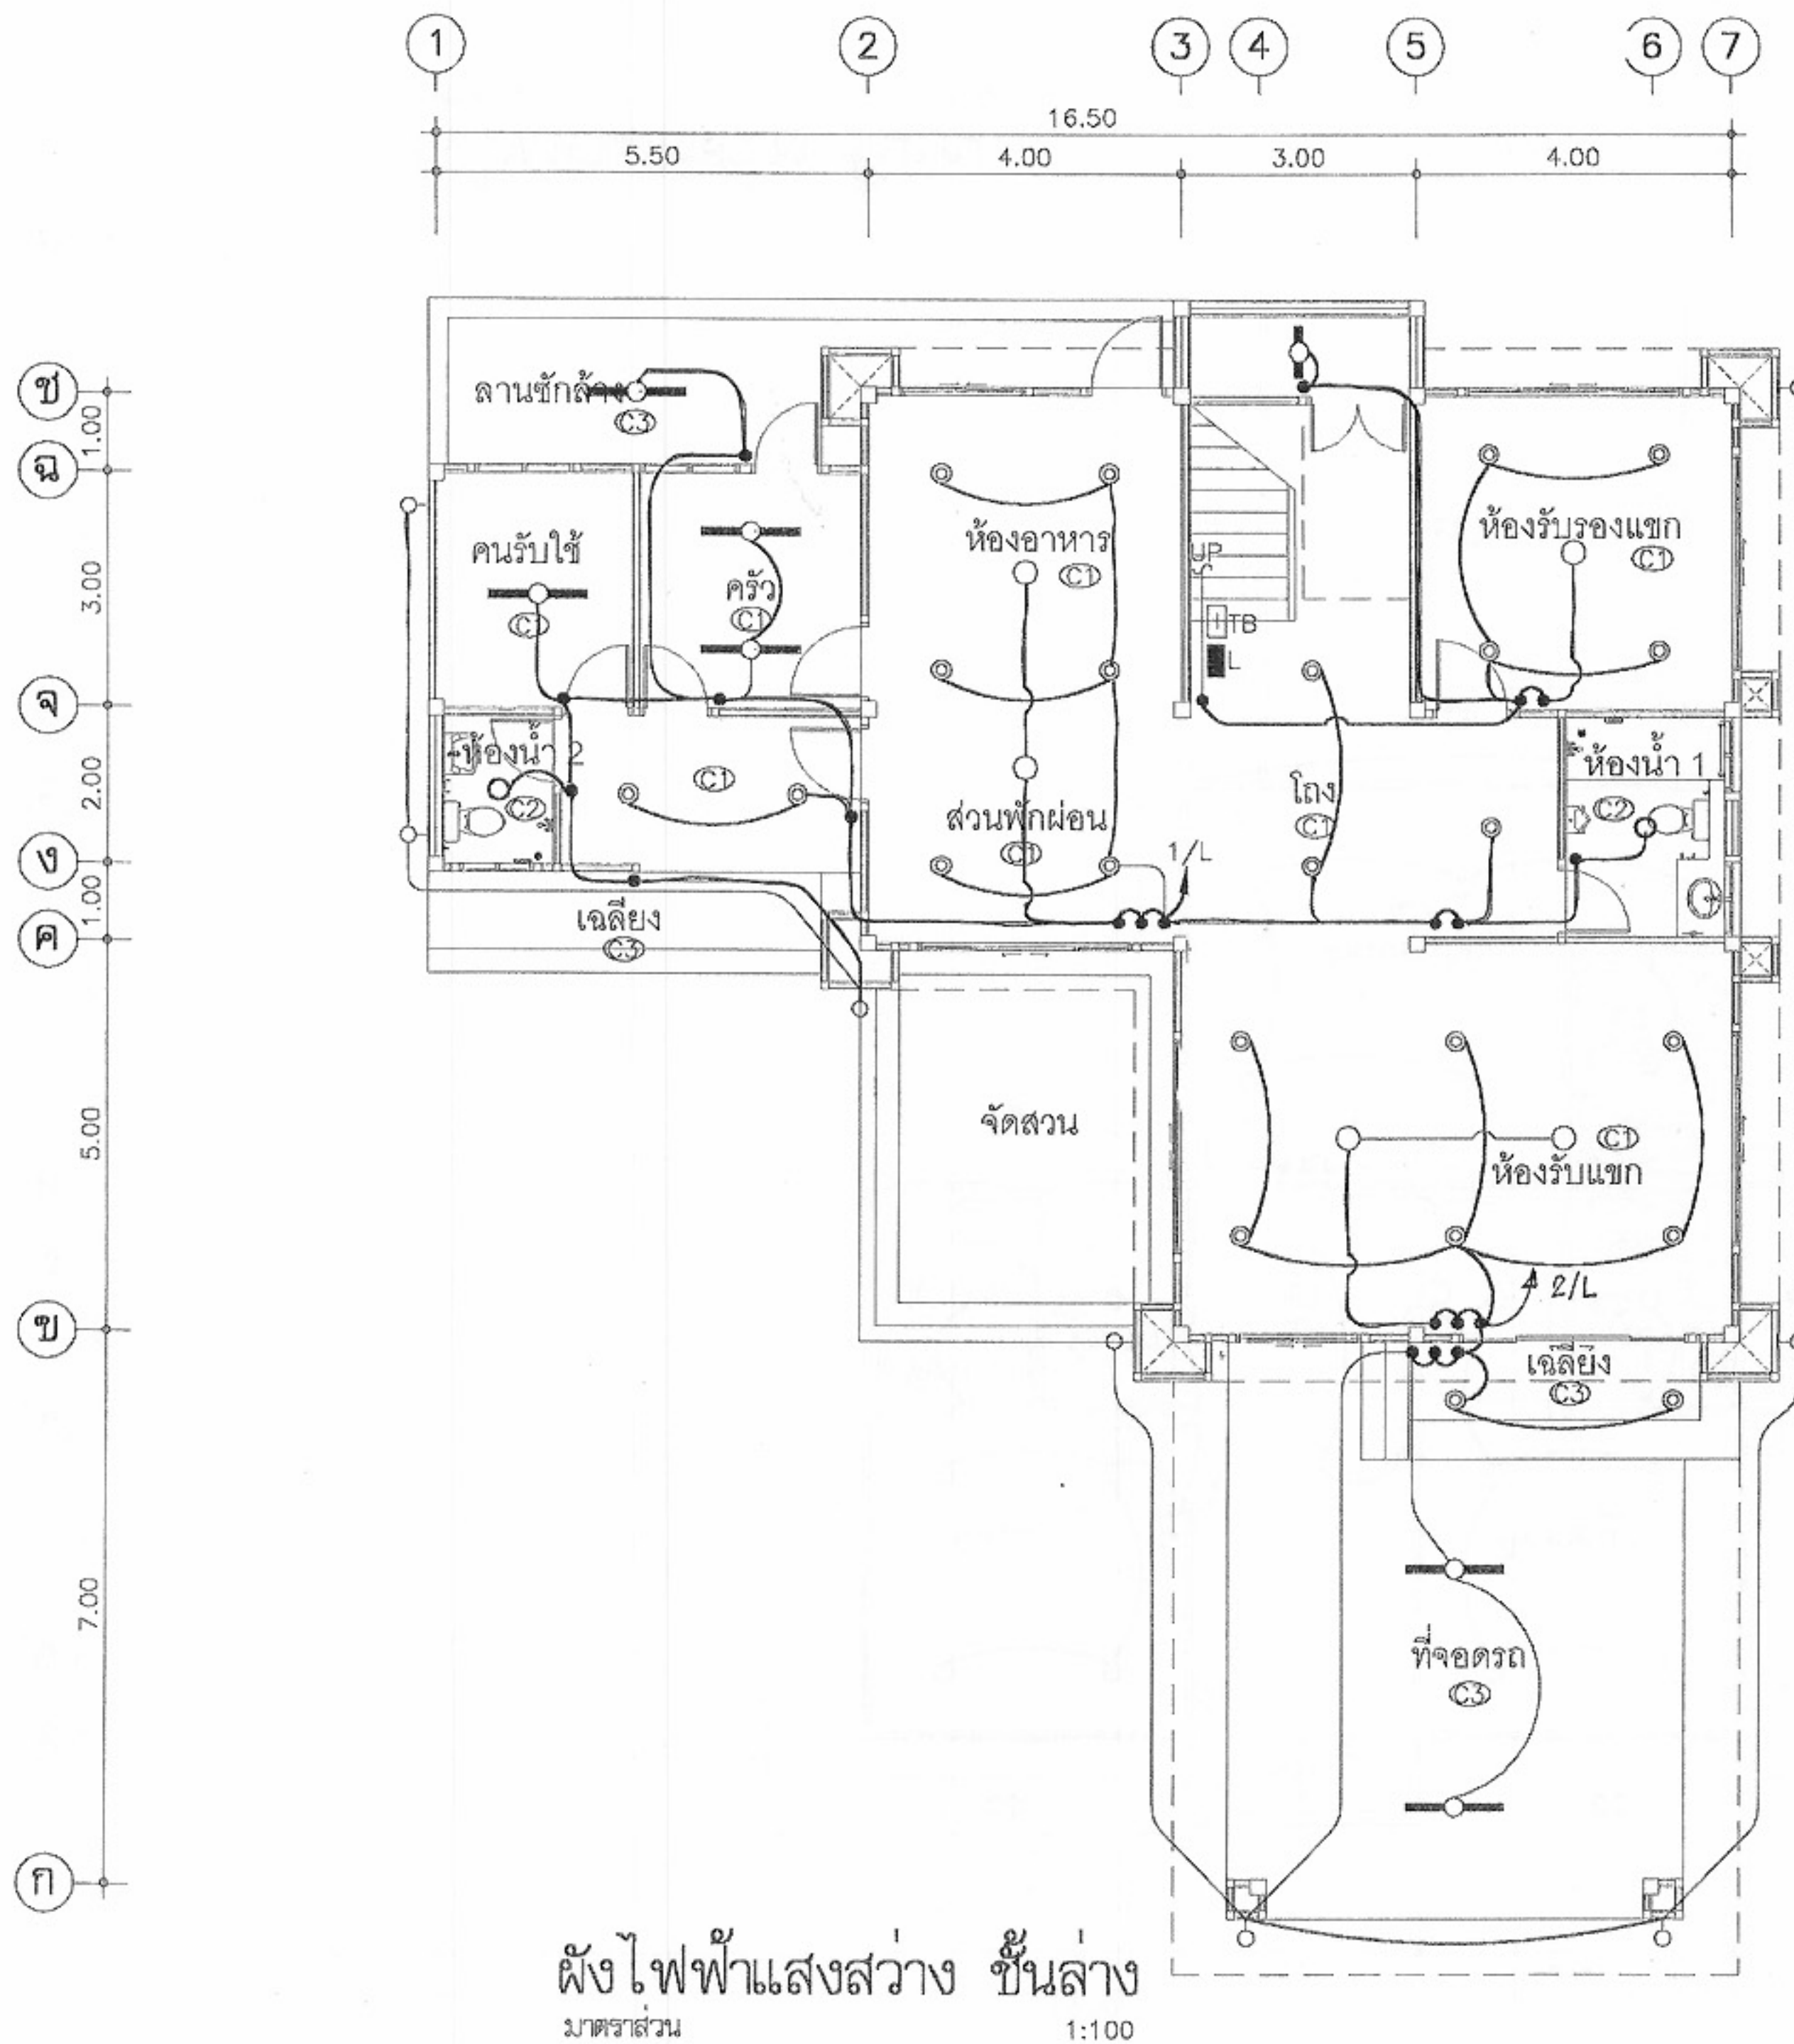

โครงการแบบอาคารเพื่อประชาชน
ครอบครัวไทยเป็นสุข

แบบ
บ้านครอบครัวไทยเป็นสุข 8

สำนักสถาปัตยกรรม
ผู้ควบคุมการออกแบบ

สถาปัตยกรรม
ผู้ควบคุมการออกแบบ

สำนักวิศวกรรมโครงสร้างและงานระบบ
ผู้ควบคุมการออกแบบ

วิศวกรรม
โครงสร้าง

วิศวกรรมไฟฟ้า
และเครื่องกล

วิศวกรรม
สุขาภิบาล

อนุมัติ
(นายสว่าง ศิริสุนทร)
อธิบดีกรมโยธาธิการและผังเมือง

แสดงแบบ
แปลนไฟฟ้าแสงสว่าง
ชั้นล่าง


มาตราส่วน 1:100

วัน/เดือน/ปี 21 พ.ย. 2548

เลขที่แบบ ม.บ.462126

แผ่นที่ E-03 จำนวนแผ่น 06

หมายเหตุ แบบที่แสดงอยู่นี้ได้รับการยืมส่วน เพื่อใช้แสดงผลทางหน้าจอเท่านั้น สำหรับแบบที่ใช้ขออนุญาตก่อสร้าง ให้ถ่ายสำเนาจากหนังสือแบบบ้าน

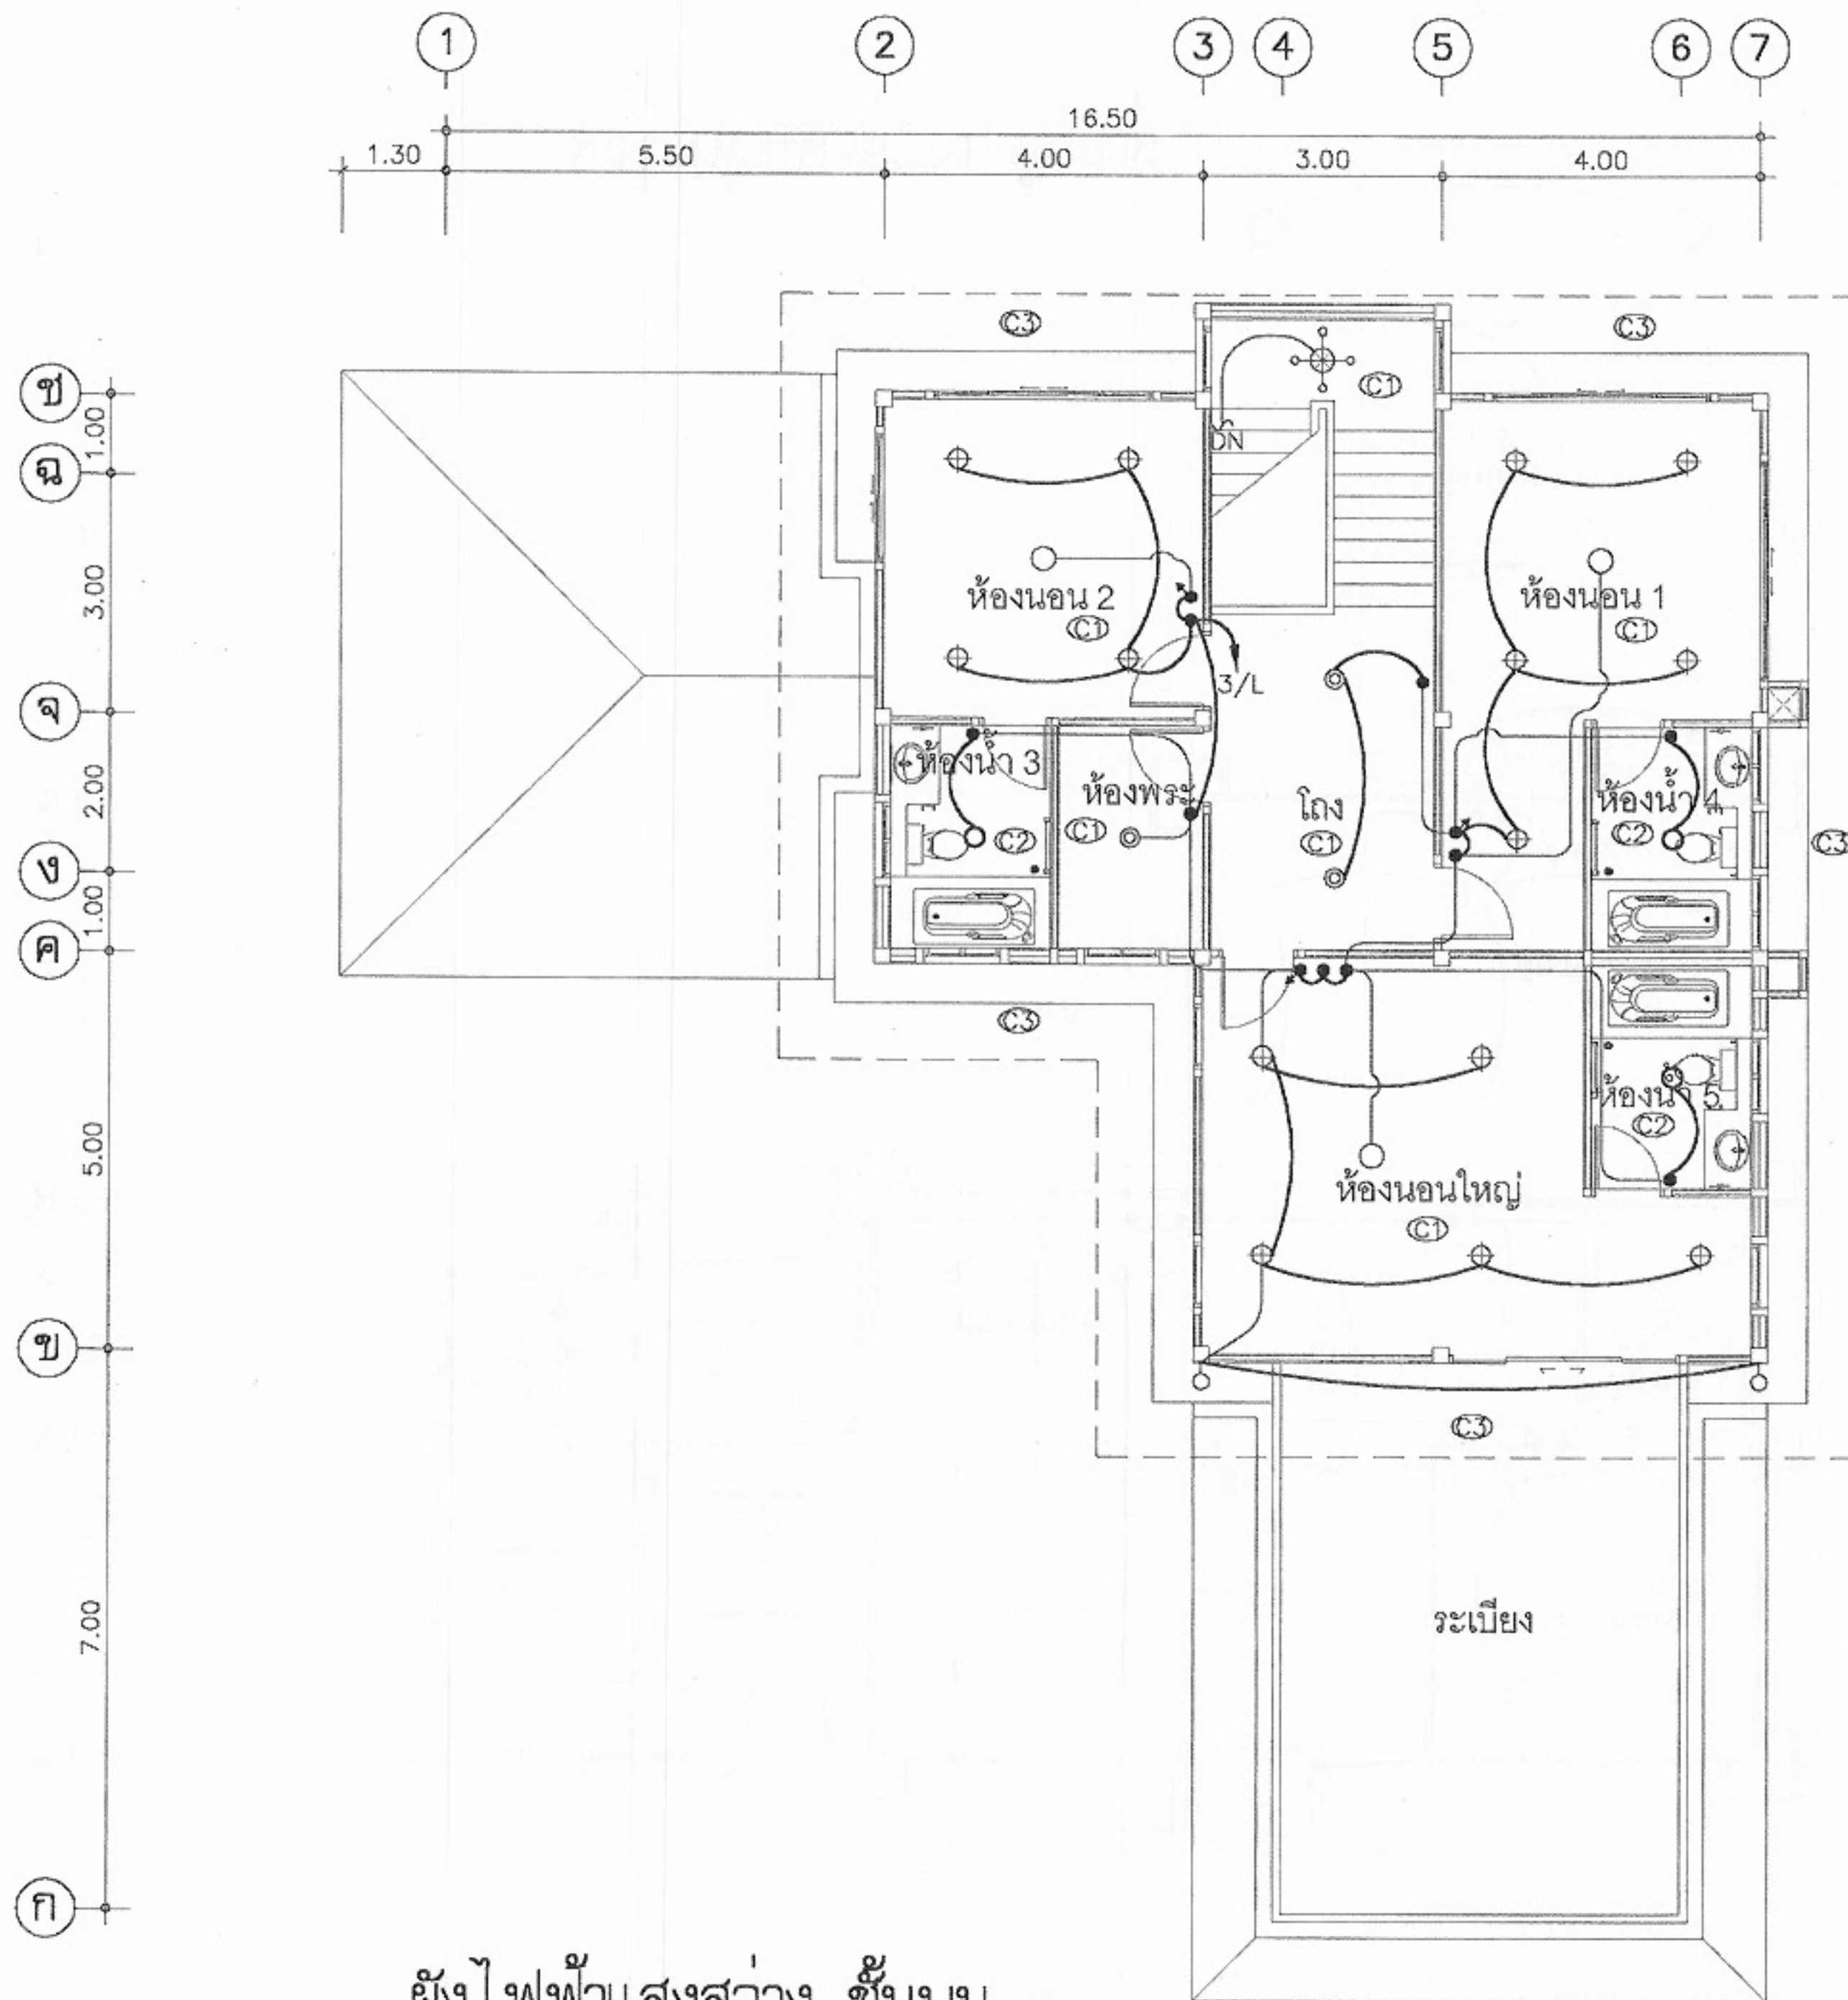

ผังไฟฟ้าแสงสว่าง ชั้นบน
มาตราส่วน 1:100

	
โครงการแบบอาคารเพื่อประชาชน ครอบครัวไทยเป็นสุข	
แบบ บ้านครอบครัวไทยเป็นสุข 8	
สำนักสถาปัตยกรรม	๗๒๖-๖๖๖๖ ผู้อำนวยการสำนัก
สถาปนิก	๖๖๖๖ สถาปนิก สถาปนิก สถาปนิก สถาปนิก
สำนักวิศวกรรมโครงสร้างและงานระบบ	
วิศวกร โครงสร้าง	๗๗ วิศวกร วิศวกร
วิศวกรไฟฟ้า และเครื่องกล	๖๖๖ วิศวกร วิศวกร
วิศวกร สุขาภิบาล	๖๖๖๖๖๖ วิศวกร วิศวกร
อนุมัติ (นายสว่าง ศรีสกุล) อธิบดีกรมโยธาธิการและผังเมือง	
แสดงแบบ แปลนไฟฟ้าแสงสว่าง ชั้นบน	
มาตราส่วน	1:100
วัน/เดือน/ปี	21 พ.ย. 2546
เลขที่แบบ	ม.บ.462126
แผ่นที่ E-04	จำนวนแผ่น 06

หมายเหตุ แบบที่แสดงอยู่นี้ได้รับการยืมส่วน เพื่อใช้แสดงผลทางหน้าจอเท่านั้น สำหรับแบบที่ใช้ขออนุญาตก่อสร้าง ให้ถ่ายสำเนาจากหนังสือแบบบ้าน



ผังเดินรับไฟฟ้า, โทรศัพท์และทีวี ชั้นล่าง
มาตราส่วน 1:100



โครงการแบบอาคารเพื่อประชาชน

ครอบครัวไทยเป็นสุข

แบบ

บ้านครอบครัวไทยเป็นสุข 8

สำนักสถาปัตยกรรม

๗๗-๖๖
ผู้อำนวยการสำนัก

สถาปนิก

๗๗-๖๖
สถาปนิก

สถาปนิก

๗๗-๖๖
สถาปนิก

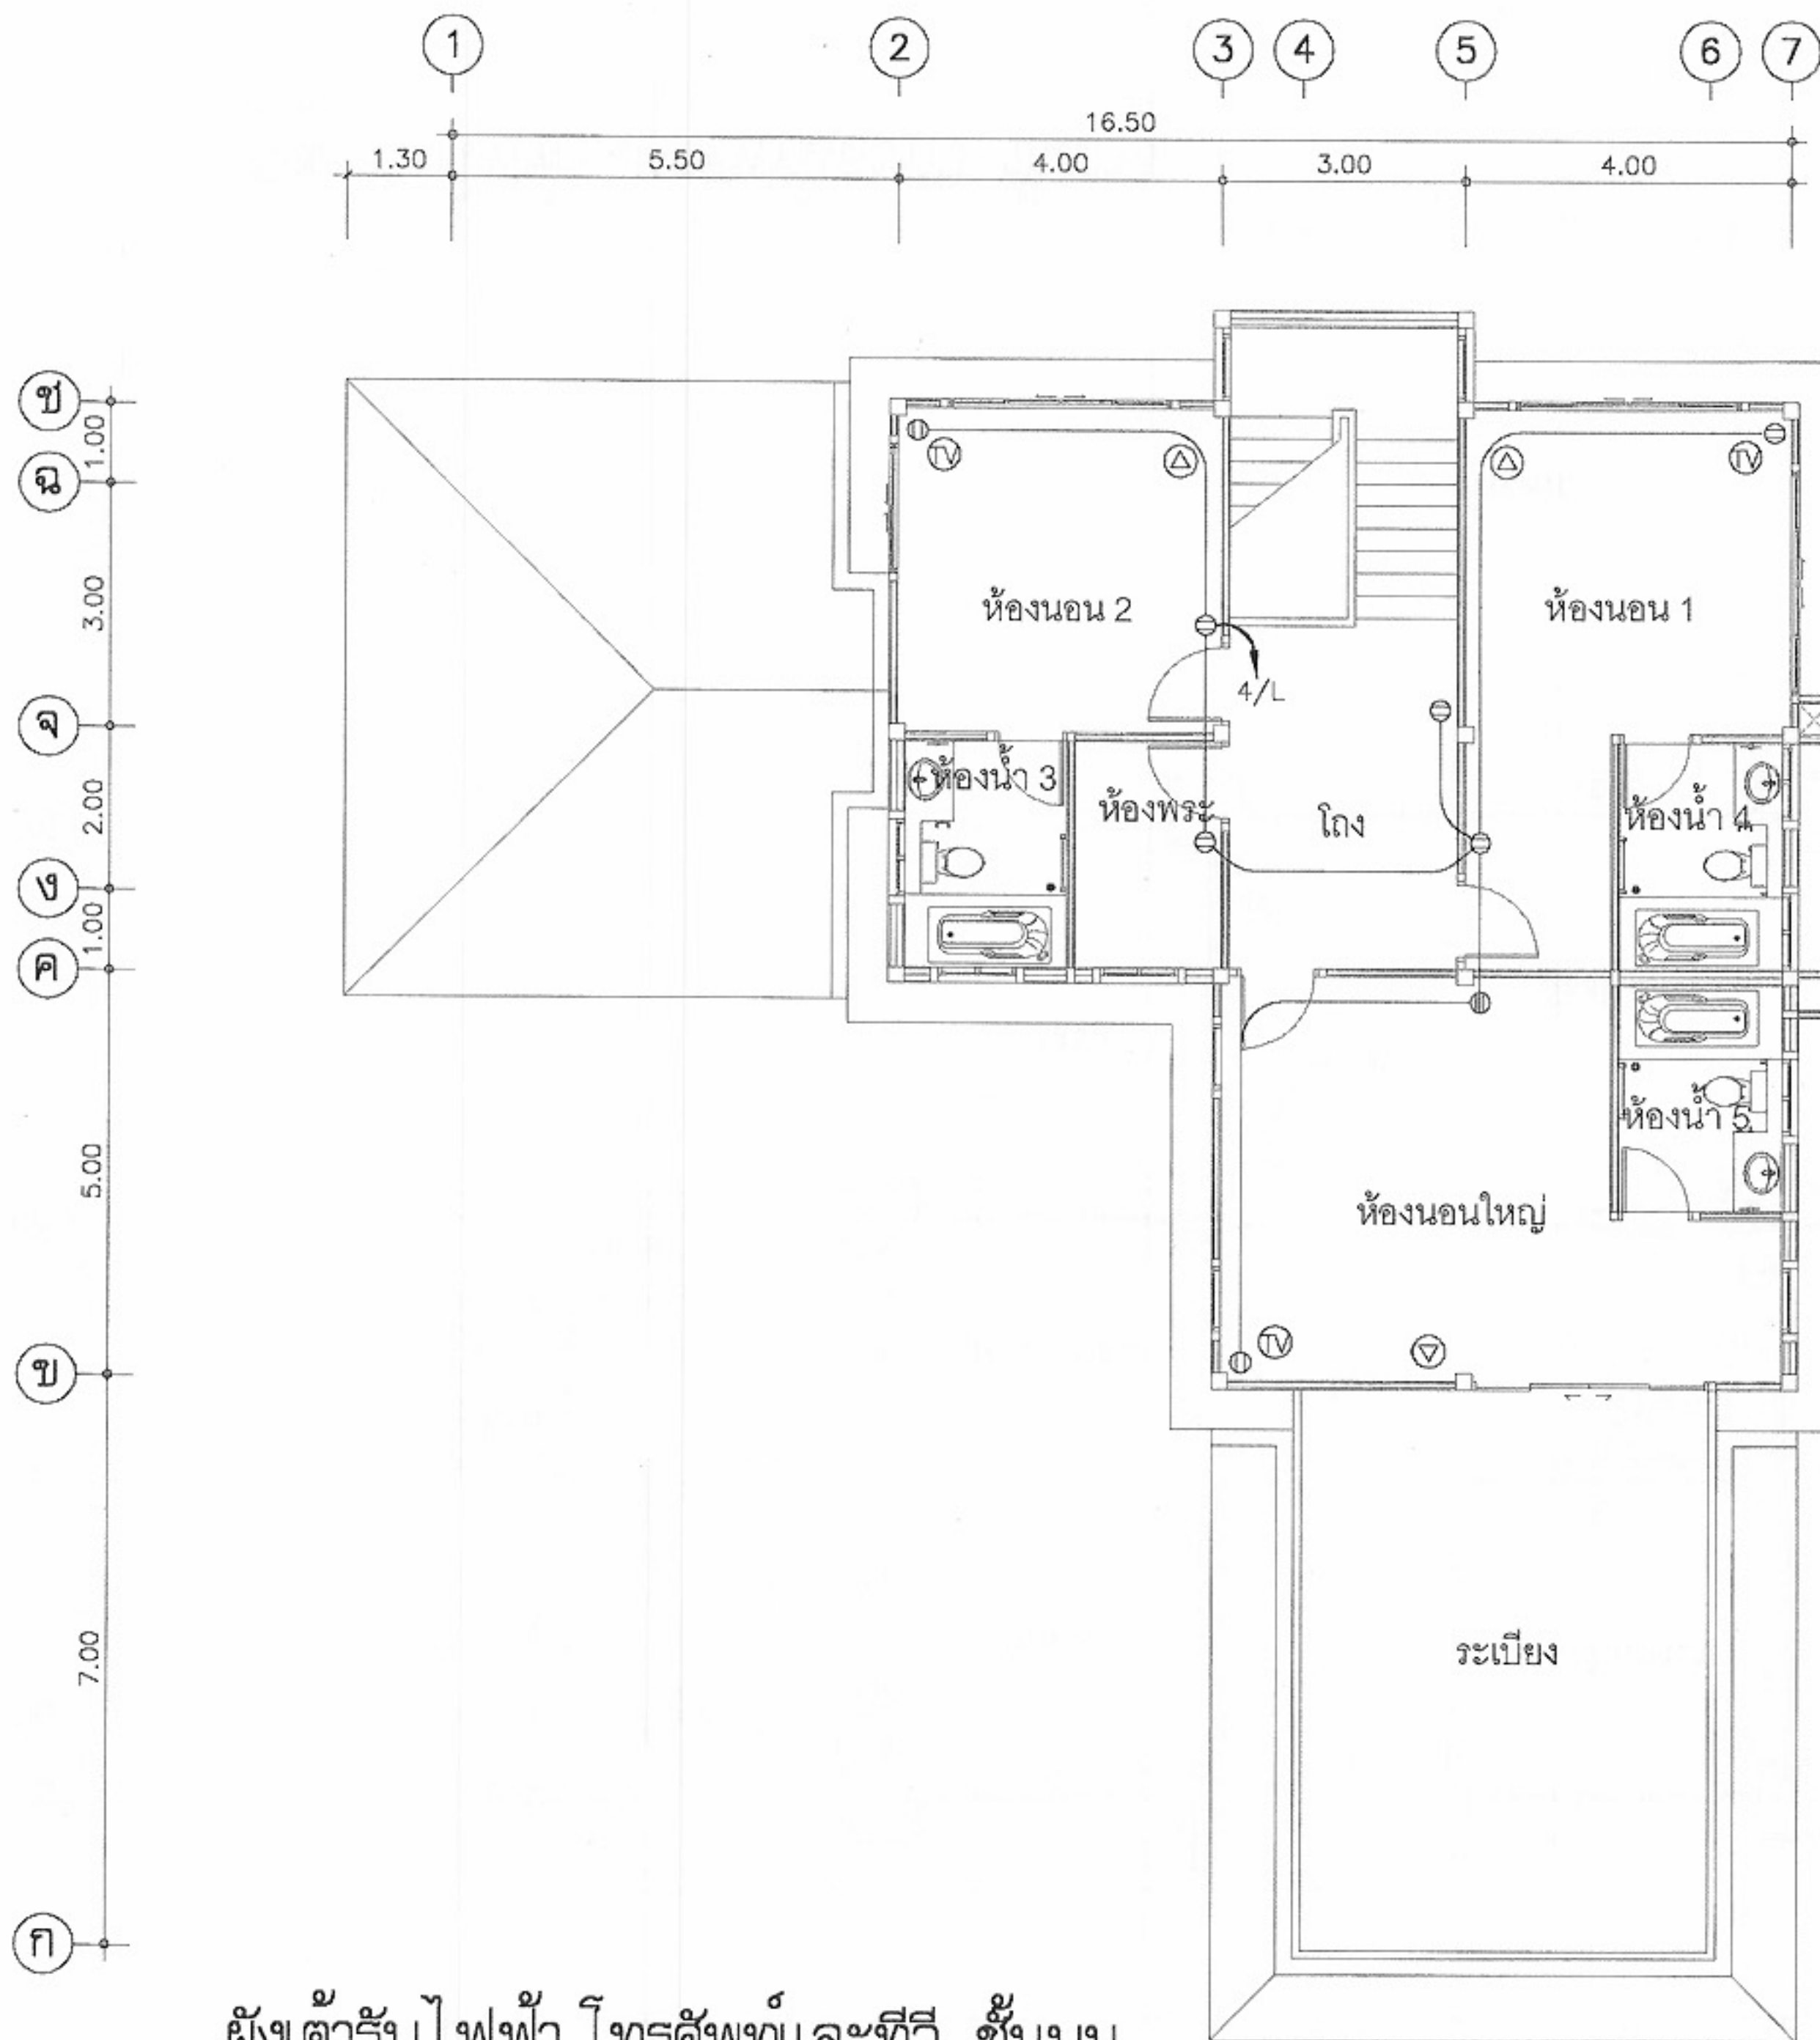

ผังเต้ารับไฟฟ้า, โตรศัพทและทีวี ชั้นบน
มาตราส่วน 1:100



โครงการแบบอาคารเพื่อประชาชน
ครอบครัวไทยเป็นสุข

แบบ
บ้านครอบครัวไทยเป็นสุข 8

สำนักสถาปัตยกรรม
ผู้ควบคุมการออกแบบ

สถาปัตยกรรม	สถาปนิก
	สถาปนิก
	สถาปนิก
	สถาปนิก

สำนักวิศวกรรมโครงสร้างและงานระบบ
ผู้ควบคุมการออกแบบ

วิศวกรรม	วิศวกร
โครงสร้าง	วิศวกร
วิศวกรรมไฟฟ้า	วิศวกร
และเครื่องกล	วิศวกร
วิศวกรรม	วิศวกร
สุขาภิบาล	วิศวกร

อนุมัติ
(นายสว่าง ศิริสุนทร)
อธิบดีกรมโยธาธิการและผังเมือง

แสดงแบบ
แปลนเต้ารับไฟฟ้า
โทรศัพทและTV ชั้นบน


มาตราส่วน 1:100






วัน/เดือน/ปี 21 พ.ย. 2546

เลขที่แบบ ม.บ.462126


แผ่นที่ E-06	จำนวนแผ่น 06
--------------	--------------

หมายเหตุ แบบที่แสดงอยู่นี้ได้รับการยืมส่วน เพื่อใช้แสดงผลทางหน้าจอเท่านั้น สำหรับแบบที่ใช้ขออนุญาตก่อสร้าง ให้ถ่ายสำเนาจากหนังสือแบบบ้าน

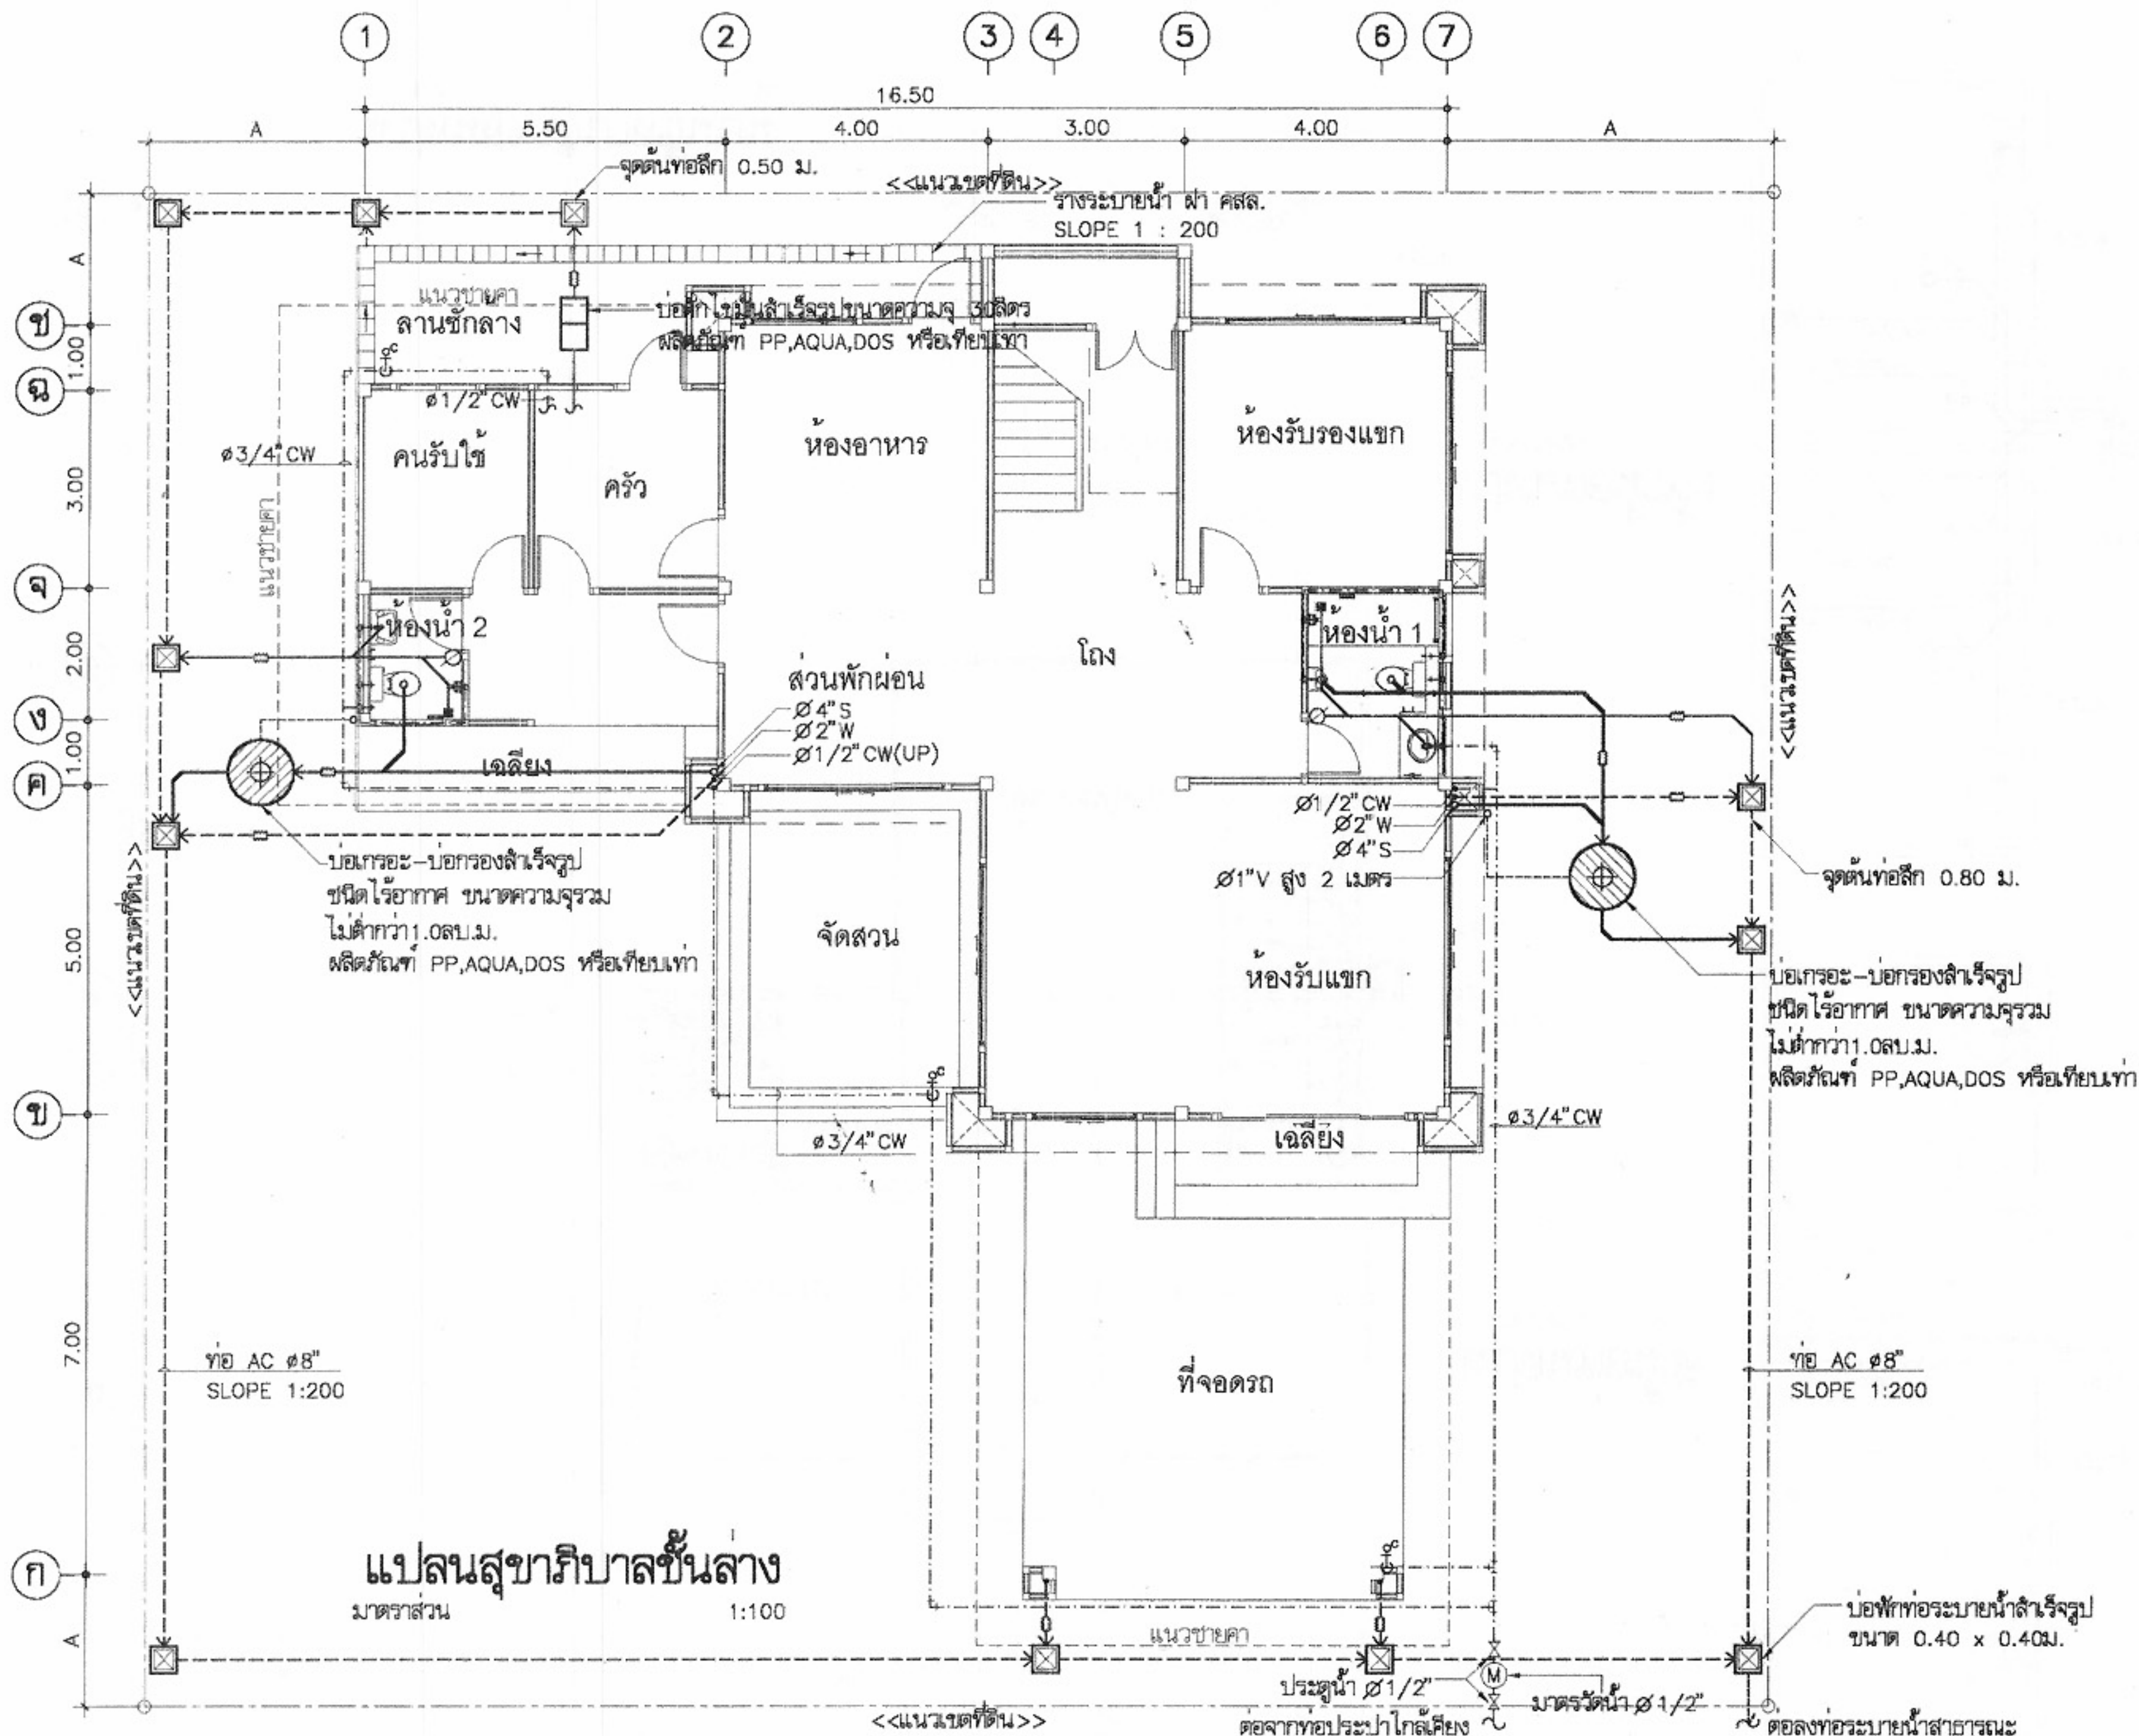


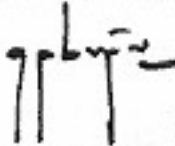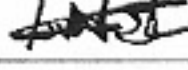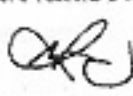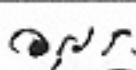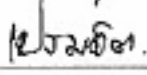โครงการแบบอาคารเพื่อประชาชน		
ครอบครัวไทยเป็นสุข		
แบบ		
บ้านครอบครัวไทยเป็นสุข 8		
สำนักสถาปัตย์กรรม		 ผู้อำนวยการสำนัก
สถาปัตย์กรรม		สถาปนิก
		สถาปนิก
		สถาปนิก
		สถาปนิก
สำนักวิศวกรรมโครงสร้างและงานระบบ		
		ผู้อำนวยการสำนัก
วิศวกรรม		วิศวกร
โครงสร้าง		วิศวกร
วิศวกรรมไฟฟ้า		วิศวกร
และเครื่องกล		วิศวกร
วิศวกรรม		วิศวกร
สุขาภิบาล		วิศวกร
อนุมัติ		
		
(นายสว่าง ศรีสุคนธ์)		
อธิบดีกรมโยธาธิการและผังเมือง		
แสดงแบบ		
แปลนสุขาภิบาลชั้นล่าง		
มาตราส่วน	1:100	
วัน/เดือน/ปี	21 พ.ย. 2546	
เลขที่แบบ	ม.บ.462126	
แผ่นที่	จำนวนแผ่น	
SN-01	03	


หมายเหตุ แบบที่แสดงอยู่นี้ได้รับการยืมส่วน เพื่อใช้แสดงผลทางหน้าจอเท่านั้น สำหรับแบบที่ใช้ขออนุญาตก่อสร้าง ให้ถ่ายสำเนาจากหนังสือแบบบ้าน

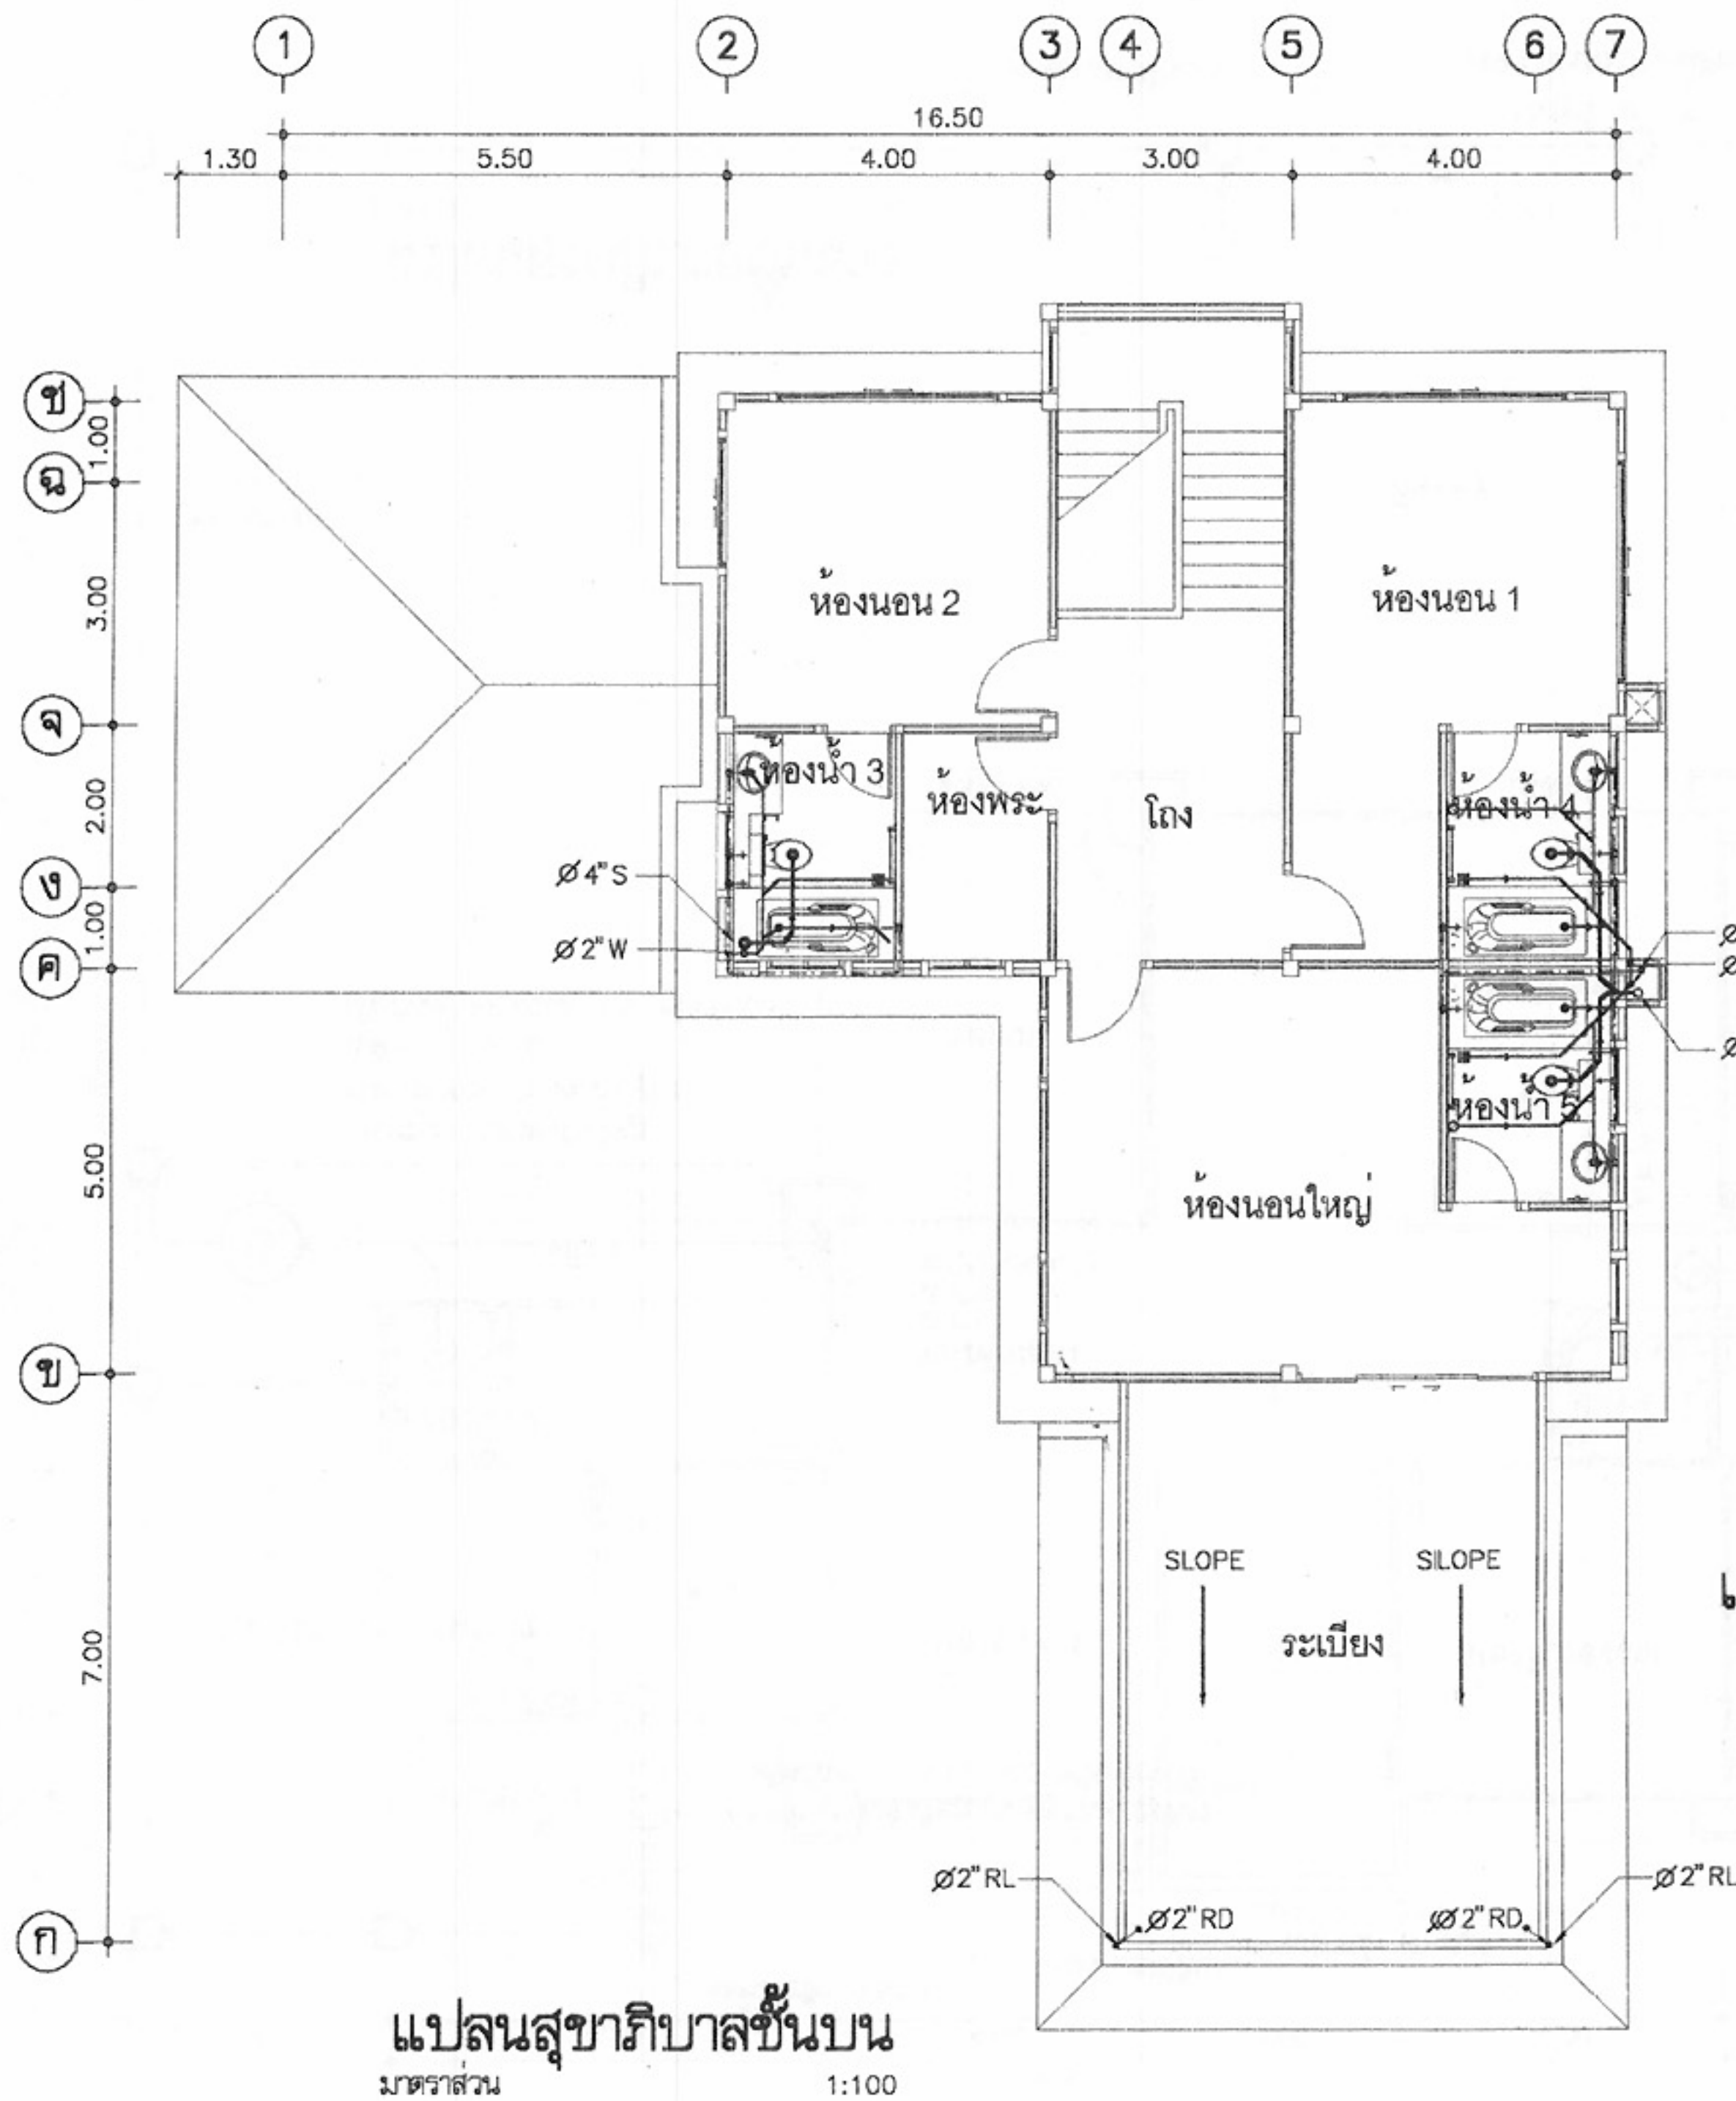

แปลนท่อน้ำดี
มาตราส่วน 1:50

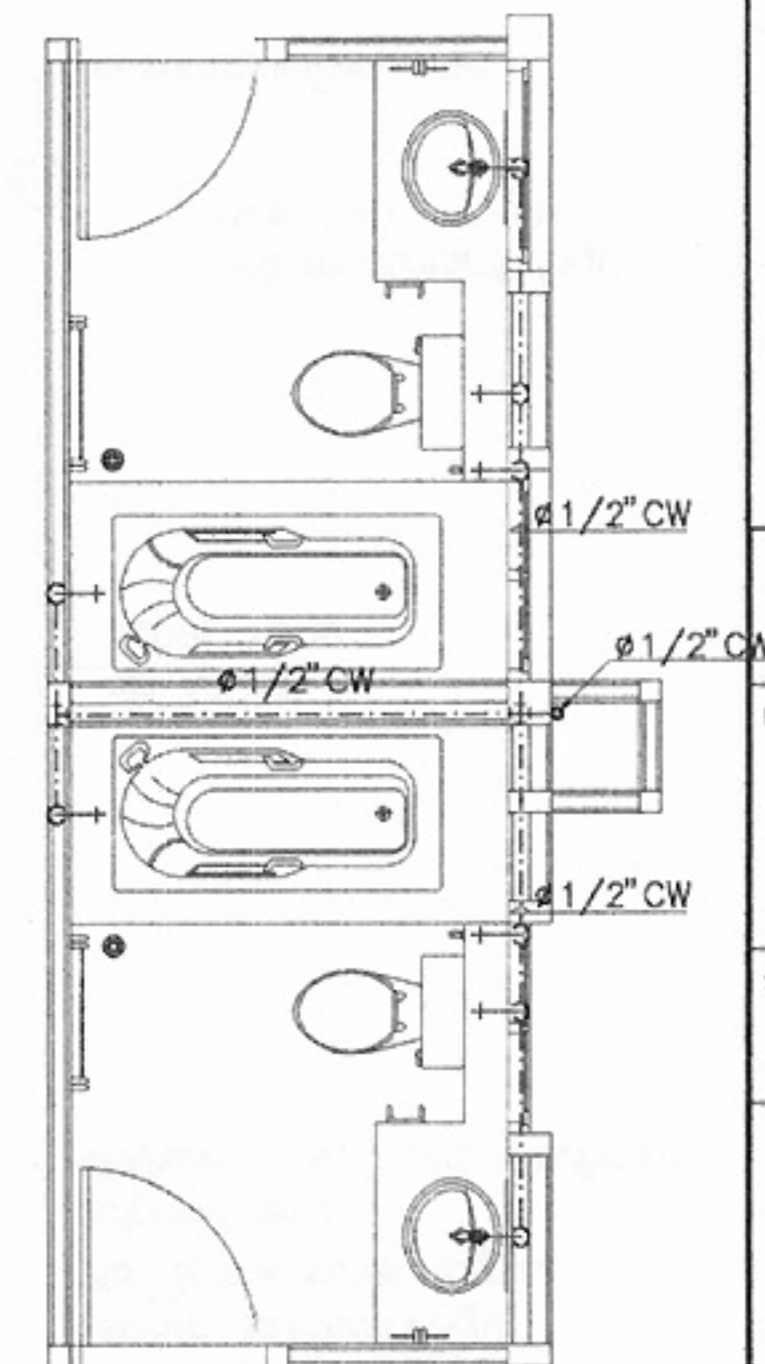

แปลนท่อน้ำทิ้ง
มาตราส่วน 1:50

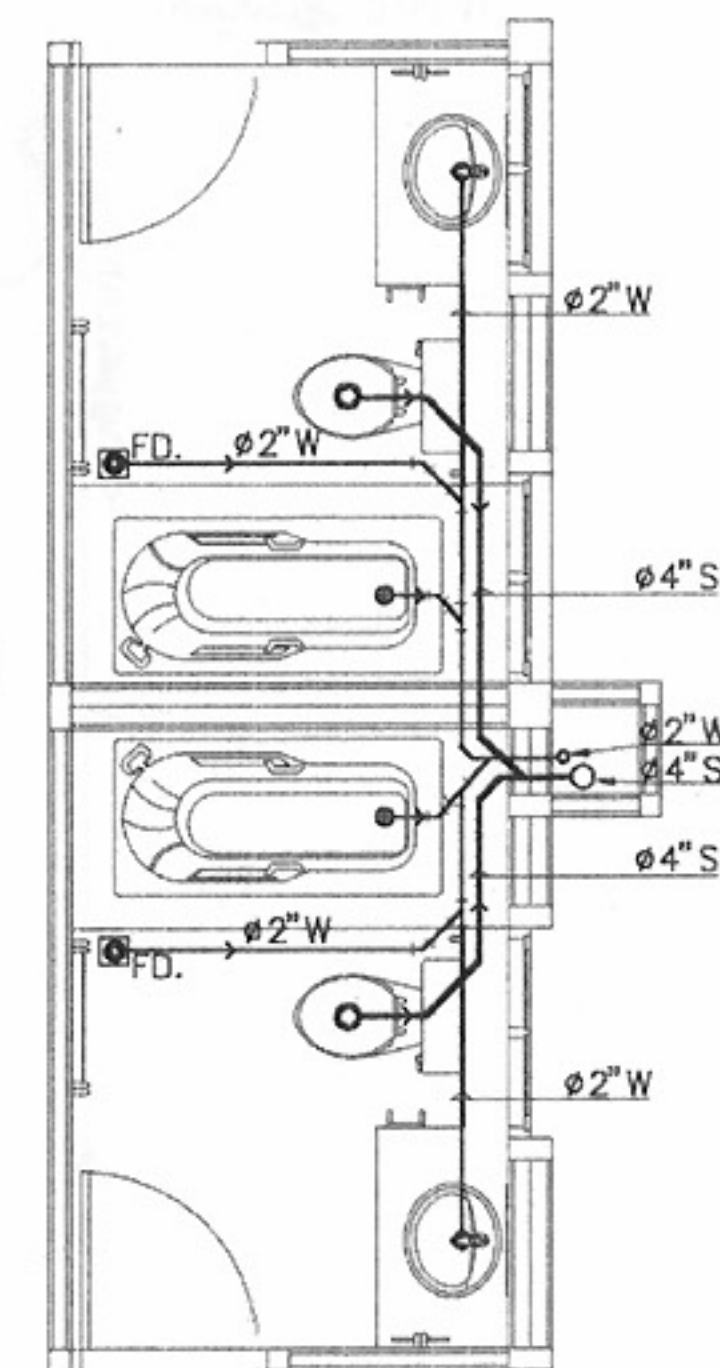

โครงการแบบอาคารเพื่อประชาชน
ครอบครัวไทยเป็นสุข

แบบ
บ้านครอบครัวไทยเป็นสุข 8

สำนักสถาปัตยกรรม
๗๖๖๖

สถาปนิก
สถาปนิก
สถาปนิก
สถาปนิก

สำนักวิศวกรรมโครงสร้างและงานระบบ
ผู้อำนวยการ

วิศวกรรม
โครงสร้าง
วิศวกรรมไฟฟ้า
และเครื่องกล
วิศวกรรม
สุขาภิบาล

อนุมัติ
(นายสว่าง ศรีสุกัน)
อธิบดีกรมโยธาธิการและผังเมือง

แสดงแบบ
แปลนสุขาภิบาลชั้นบน

มาตราส่วน 1:100

วัน/เดือน/ปี 21 พ.ย. 2546

เลขที่แบบ ม.บ.462126


แผ่นที่ SN-02 จำนวนแผ่น 03

หมายเหตุ แบบที่แสดงอยู่นี้ได้รับการยืมส่วน เพื่อใช้แสดงผลทางหน้าจอเท่านั้น สำหรับแบบที่ใช้ขออนุญาตก่อสร้าง ให้ถ่ายสำเนาจากหนังสือแบบบ้าน

สัญลักษณ์



บ่อเกรอะ-บ่อกรองสำเร็จรูป ชนิดไร้อากาศ
ขนาดความจุรวมไม่น้อยกว่า 1 m³
ผลิตจาก PP, AQUA, DOS
หรือเทียบเท่า

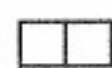

บ่อดักไขมัน จุไม่น้อยกว่า 30 ลิตร
ผลิตจาก PP, AQUA, DOS
หรือเทียบเท่า




บ่อบำบัดน้ำทิ้งสำเร็จรูป ขนาด 40x40 cm




มาตรวัดน้ำ 1/2"



ประตุน้ำ 1/2"

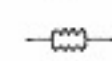

ข้อต่ออ่อน

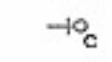


ก๊อกสนาม


○ RD ROOF DRAIN
○ RL RAIN LEADER
□ FD FLOOR DRAIN
○ FCO FLOOR CLEAN OUT

— CW — COLD WATER
— V — VENT
— S — SOIL
— W — WASTE


ชนิด	วัสดุท่อ
ท่อประปา CW	PVC ขึ้น 13.5
ท่อน้ำโสโครก S	PVC ขึ้น 8.5 สาดเอียงไม่น้อยกว่า 1:75
ท่อน้ำทิ้ง W	PVC ขึ้น 8.5 สาดเอียงไม่น้อยกว่า 1:75
ท่ออากาศ V	PVC ขึ้น 8.5

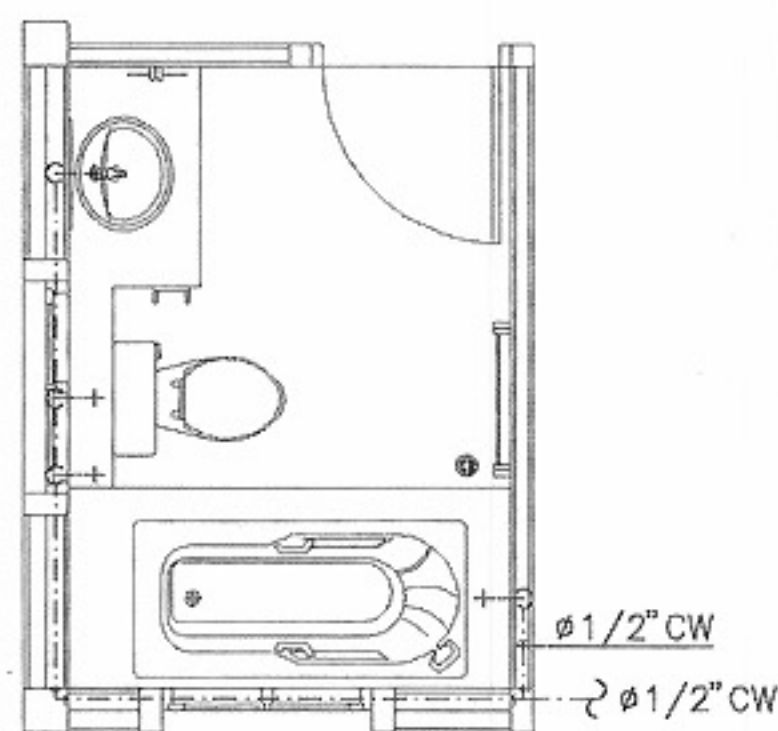


แปลนท่อน้ำดี
มาตราส่วน 1:50

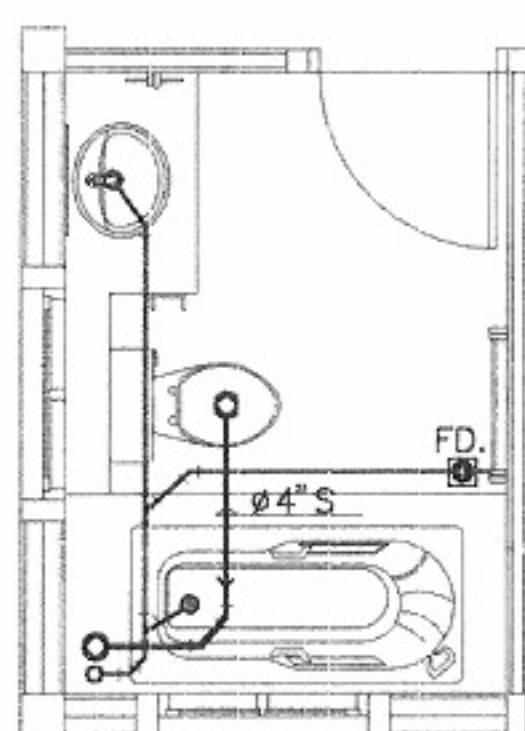


แปลนท่อน้ำทิ้ง
มาตราส่วน 1:50

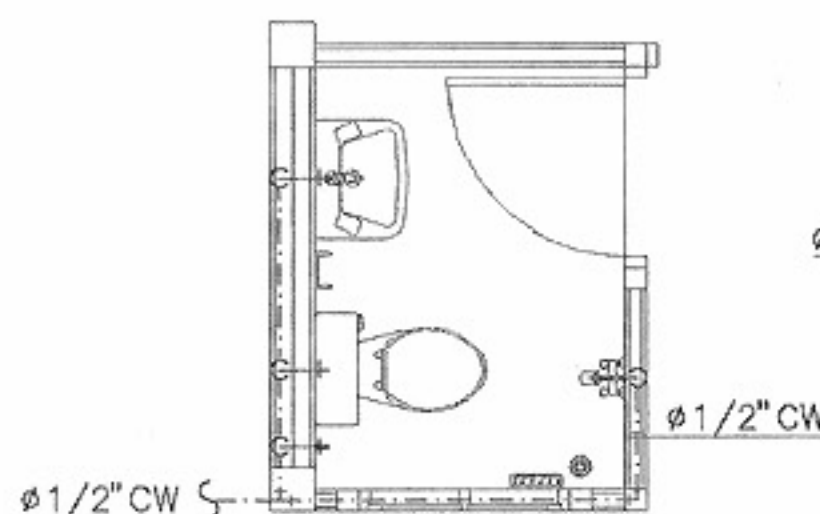


แปลนท่อน้ำดี
มาตราส่วน 1:50

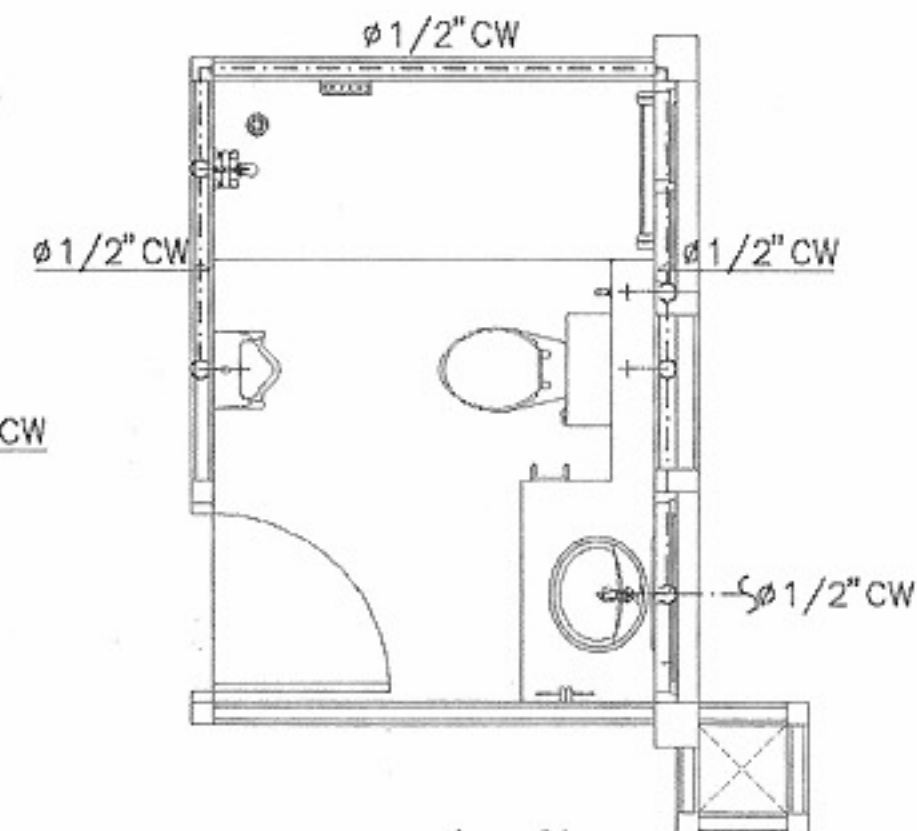

แปลนท่อน้ำดี
มาตราส่วน 1:50

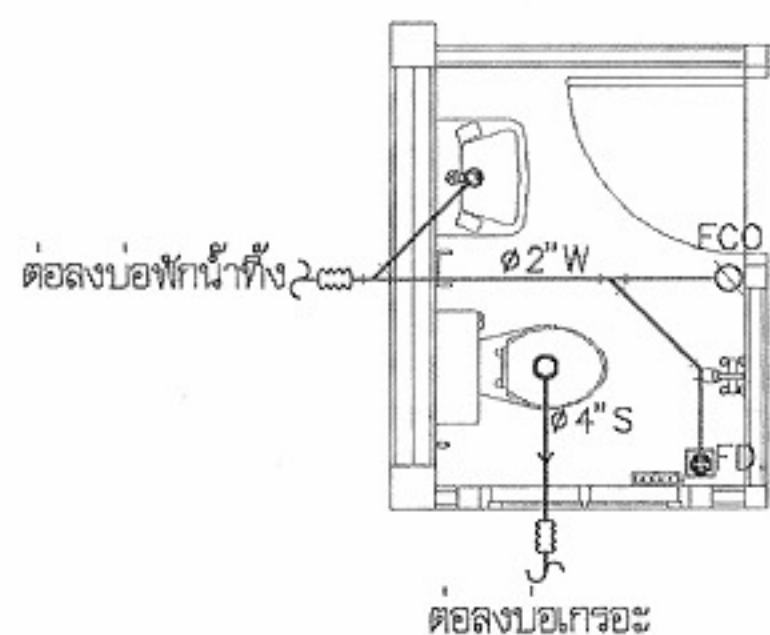

แปลนท่อน้ำทิ้ง
มาตราส่วน 1:50

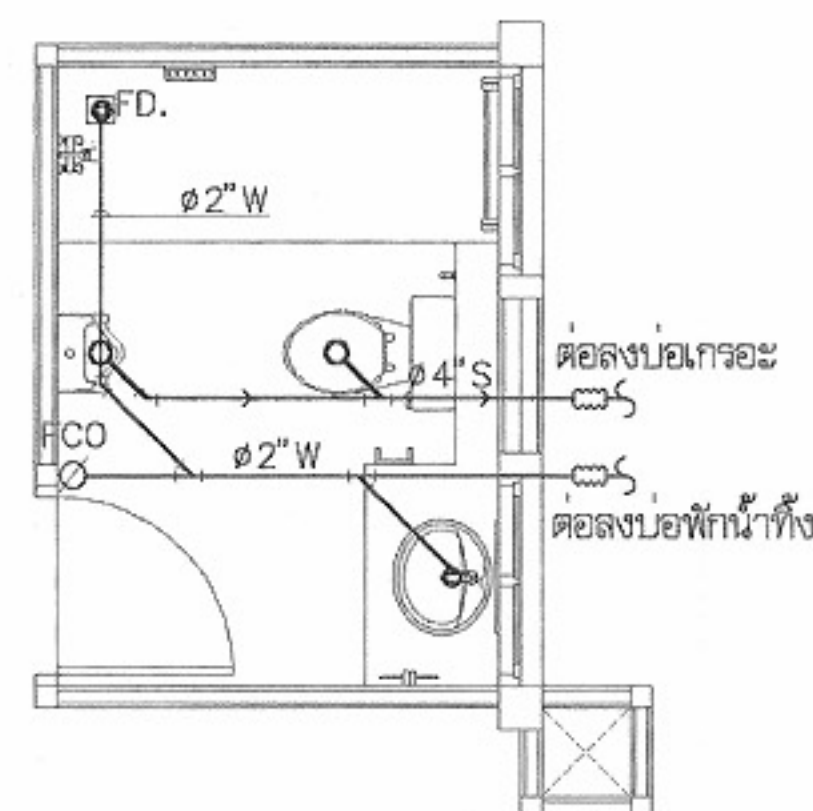

แปลนท่อน้ำทิ้ง
มาตราส่วน 1:50



โครงการแบบอาคารเพื่อประชาชน

ครอบครัวไทยเป็นสุข

แบบ

บ้านครอบครัวไทยเป็นสุข 8

สำนักสถาปัตยกรรม

๗๗-๗๗
ผู้อำนวยการสำนัก

สถาปนิก

สถาปนิก

สถาปนิก

สถาปนิก

สถาปนิก

สถาปนิก

สถาปนิก

สถาปนิก

สถาปนิก

สถาปนิก

สำนักวิศวกรรมโครงสร้างและงานระบบ

ผู้อำนวยการสำนัก

วิศวกร

วิศวกร

โครงสร้าง

วิศวกร

วิศวกรไฟฟ้า

วิศวกร

และเครื่องกล

วิศวกร

วิศวกร

วิศวกร

สุขาภิบาล

วิศวกร

อนุมัติ

(นายสว่าง ศรีสกุล)

อธิบดีกรมโยธาธิการและผังเมือง

แสดงแบบ

ขยายห้องน้ำ
สัญลักษณ์

มาตราส่วน

1:50

วัน/เดือน/ปี

21 พ.ย. 2546

เลขที่แบบ

ม.บ.462126

แผ่นที่

SN-03

จำนวนแผ่น

03

หมายเหตุ แบบที่แสดงอยู่นี้ได้รับการยืมส่วน เพื่อใช้แสดงผลทางหน้าจอเท่านั้น สำหรับแบบที่ใช้ขออนุญาตก่อสร้าง ให้ถ่ายสำเนาจากหนังสือแบบบ้าน