

แบบบ้านसानฟัน ของขวัญปีใหม่ คนไทยมีความสุข



บ้านห่วงใยไทยประชาชนใจ ๑

กรมโยธาธิการและผังเมือง กระทรวงมหาดไทย




๒ ห้องนอน ๒ ห้องน้ำ


สารบัญ

แบบบ้านसानฝัน ของขวัญปีใหม่ คนไทยมีความสุข

บ้านห่วงใยไทย ประชาสุขใจ 1

	หน้า		หน้า
แบบสถาปัตยกรรม		บัญชีแสดงปริมาณวัสดุและแรงงานที่ใช้ในการก่อสร้าง (BOQ)	45
● แผ่นที่ A – 01 ถึงแผ่นที่ A – 21	1	หลักเกณฑ์และข้อกำหนดในผังบริเวณประกอบการขออนุญาตก่อสร้างอาคาร	55
แบบวิศวกรรมโครงสร้าง			
● แผ่นที่ S – 01 ถึงแผ่นที่ S – 10	22		
แบบวิศวกรรมสุขาภิบาล			
● แผ่นที่ SN – 01 ถึงแผ่นที่ SN – 08	32		
แบบวิศวกรรมไฟฟ้า			
● แผ่นที่ EE – 01 ถึงแผ่นที่ EE – 04	40		
แบบวิศวกรรมเครื่องกล			
● แผ่นที่ M – 01	44		

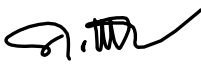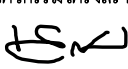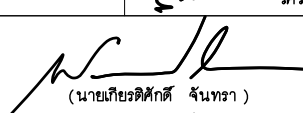รายการประกอบแบบอาคารบ้านห้วยไทยประชาสุโข 1. วัตถุประสงค์ กรมโยธาธิการและผังเมืองดำเนินการออกแบบอาคารบ้านห้วยไทยประชาสุโขเพื่อประชาชนตามคำขอของ ฯพณฯนายกรัฐมนตรี และเป็นไปตามนโยบายรัฐบาลเพื่อบริการประชาชนโดยไม่คิดค่าบริการออกแบบใดๆ ทั้งสิ้น 2. รายละเอียดประกอบแบบ 2.1 การวางผังและระดับ ผู้รับจ้างจะต้องการทำวางผังบริเวณให้ถูกต้องเรียบร้อยตามกฎหมายควบคุมอาคารและกำหนดระดับของอาคารและระดับพื้นที่ก่อสร้างต้องมีความลาดเอียงเพื่อการระบายน้ำตามรูปแบบรายการที่กำหนด ก่อนดำเนินการต่อไป 2.2 งานสถาปัตยกรรม ก. งานพื้น - พื้น ค.ส.ล. ทำผิวขัดมันเรียบ หรือผิวขัดหยาบ ให้แต่งระดับผิว ค.ส.ล. ด้วยปูนทรายให้เรียบสม่ำเสมอ หรือมีความลาดเอียงไปสู่ด้านนอกอาคาร - พื้น ค.ส.ล. ปูกระเบื้องเซรามิค ผิวด้าน ขนาด 8”x8” หรือ 12”x12” ตามแบบระบุ พื้นห้องน้ำใช้กระเบื้องเซรามิคผิวด้าน ตาม มอก. 2508–2555 น้ำยากันซึม ใช้ของที่ผลิตในประเทศ - พื้น ค.ส.ล. ปูไม้เนื้อแข็ง 1”x4” ตีเข้าลิ้น ใช้ไม้เนื้อแข็ง เช่น ไม้มะค่า ไม้แดง หรือไม้เต็ง 1”x4” อบเข้าลิ้นอัดสนิท ขัดให้เรียบแล้วเคลือบด้วยน้ำยาเคลือบเงาไม้ หมายเหตุ – การเตรียมผิวพื้นและการปูกระเบื้องให้ทำตามมาตรฐานวิชาชีพที่ดี - บริเวณพื้นต่างระดับระหว่างค้ำระดับ +0.47 และ +0.50 ให้ทำทางลาดสำหรับรถขึ้น ข. งานผนัง - ผนังทั่วไปก่ออิฐมวลเบ่ครึ่งแผ่น อิฐต้องเป็นอิฐที่แกร่ง เผาสุกเสมอ ไม่บิดเบี้ยวต้องพรมน้ำให้ชุ่มก่อนก่อ - การก่อชนคาน เสา หรือเอ็น ค.ส.ล. ต้องเรียบเหล็ก RB6 มม. ทูกระยะไม่เกิน 40 ซม. โดยยื่นออกมา 25 ซม. และฝังในเสาหรือคาน ค.ส.ล. 10 ซม. - การก่อชนกันเป็นมุม การก่อเว้นช่องสำหรับติดตั้งประตูหน้าต่าง และทุกระยะที่เกิน 2 เมตร ของความสูงผนังและทุกระยะที่เกิน 3 เมตร ของความยาวผนังให้ทำเอ็น หรือทับหลัง ค.ส.ล. หนาเท่าผนังที่ก่อสร้างและกว้าง 10 ซม. เสริมเหล็ก 2–RB6 มม.และมีปลอกเหล็ก RB6 @0.20 ม. - ผนังปูกระเบื้องเซรามิค ขนาดตามแบบรายการที่ระบุ ใช้กระเบื้องดินเผาเคลือบชนิดผนังภายใน ตาม มอก. 2508–2555 ค. งานฝ้าเพดาน - ให้ใช้ฝ้าเพดานตามรูปแบบรายการที่ระบุ - ใช้โครงคร่าวเหล็กชุบสังกะสี สำหรับยึดแผ่นฝ้า ตาม มอก.863–2532 ติดตั้งตามมาตรฐานผู้ผลิต ง. งานหลังคา - โครงหลังคา ตามที่ได้กำหนดไว้ในรูปแบบและรายการวิศวกรรมโครงสร้าง - วัสดุหลังคา กระเบื้อง ลอนคู่ (ชนิดลอนสั้น) ตาม มอก. 1407–2540 ติดตั้งตามมาตรฐานผู้ผลิต จ. งานประตู- หน้าต่าง และอุปกรณ์ - รายละเอียดตามระบุในแบบขยายประตู- หน้าต่าง และอุปกรณ์ - ประตู- หน้าต่างอลูมิเนียม ใช้อลูมิเนียม ตาม มอก. 284–2530 เคลือบผิวด้วยสีผง POLAR POWDER COAT POLYESTER - ประตูบานเปิดทั่วไปใช้บานพับประตู ผลิตภัณฑ์ ตาม มอก. 759–2531 ขนาด 4x3” บานละ 3 จุด ติดตั้งตามกรรมวิธีผู้ผลิต - กลอนทั่วไปใช้กลอนโลหะชุบโครเมียม ผลิตภัณฑ์ภายในประเทศ - กุญแจลูกบิดทั่วไป ใช้แบบลิ้นคู่ ล็อคได้ ผิว SATIN CHROME ประเภท STANDARD DUTY รูปทรง ORBIT ผลิตภัณฑ์ภายในประเทศ ฉ. งานห้องน้ำ- ส้วม และสุขภัณฑ์ - รายละเอียดตามระบุในแบบขยายห้องน้ำ- ส้วม สุขภัณฑ์ และอุปกรณ์ประกอบ - การเดินท่อน้ำประปา– ท่อน้ำทิ้ง– ท่อส้วม ให้เป็นไปตามรูปแบบและรายการวิศวกรรมสุขาภิบาล ช. งานสี - งานทาสีผนังคอนกรีต- ปูนภายนอก - สีรองพื้น ใช้สีรองพื้นสำหรับปูนใหม่ ผลิตภัณฑ์เดียวกับสีทับหน้า - สีทับหน้า ใช้สีอะคริลิค 100% กึ่งเงาทั้งด้านสำหรับทาภายนอก ตาม มอก. 2321–2549 - งานทาสีผนังคอนกรีต- ปูนภายใน - สีรองพื้น ใช้สีรองพื้นสำหรับปูนใหม่ ผลิตภัณฑ์เดียวกับสีทับหน้า - สีทับหน้า ใช้สีอะคริลิค 100% สำหรับทาภายใน ตาม มอก. 272–2549 เกรด A - งานทาสีฝ้าภายนอก ไม้ไฟเบอร์ซีเมนต์บอร์ด ไม้สังเคราะห์ - สีรองพื้น ใช้สีรองพื้นสำหรับปูนเก่า - หรือสีรองพื้นสำหรับไฟเบอร์ซีเมนต์บอร์ดผลิตภัณฑ์เดียวกับสีทับหน้า - สีทับหน้า ใช้สีอะคริลิค 100 % สำหรับทาไม้สังเคราะห์หรือไฟเบอร์ซีเมนต์บอร์ด - งานทาสีเหล็กและไม้ - สีรองพื้น ใช้สีรองพื้นเหล็กกันสนิม - หรือสีรองพื้นกันยางไม้ (ALUMINIUM WOOD PRIMER) ผลิตภัณฑ์เดียวกับสีทับหน้า - สีทับหน้า ใช้สีน้ำมัน ตาม มอก.327–2538 - งานทาสีพื้นไม้ปาร์เก้ - สีรองพื้น และสีทับหน้า ใช้สีโพรยูรีเทนสำหรับพื้นไม้ ดำเนินการตามมาตรฐานผู้ผลิต วิธีการและขั้นตอนการทาสี ให้ทารองพื้น 1 เที่ยว สีทับหน้า 2 เที่ยว โดยส่วนผสมใช้ตามมาตรฐานผู้ผลิต หมายเหตุ วัสดุต่างๆดังกล่าวข้างต้น สามารถเปลี่ยนแปลงได้ตามความเหมาะสมและวัตถุประสงค์ของผู้ว่าจ้าง	 แบบบ้านสถานพื้นของขงวุฒิปใหม่คนไทยมีความสุข แบบบ้านห้วยไทยประชาสุโข 1 สำนักงานสถาปัตยกรรม  ผู้อำนวยการสำนัก สถาปัตยกรรม  สถาปนิก  สถาปนิก สำนักวิศวกรรมโครงสร้างและงานระบบ  ผู้อำนวยการสำนัก วิศวกรรม  วิศวกร โครงสร้าง วิศวกร วิศวกรรม  วิศวกร สุขาภิบาล วิศวกร วิศวกรรม  วิศวกร ไฟฟ้า  วิศวกร วิศวกรรม  วิศวกร เครื่องกล  วิศวกร  (นายเกียรติศักดิ์ จันทร์) วิศวกรใหญ่  (นายมงคล สุดประเสริฐ) อธิบดีกรมโยธาธิการและผังเมือง แสดงแบบ รายการประกอบแบบ มาตราส่วน – วัน/เดือน/ปี 19/10/59 เลขที่แบบ AR 58237 A–02 21
---	---

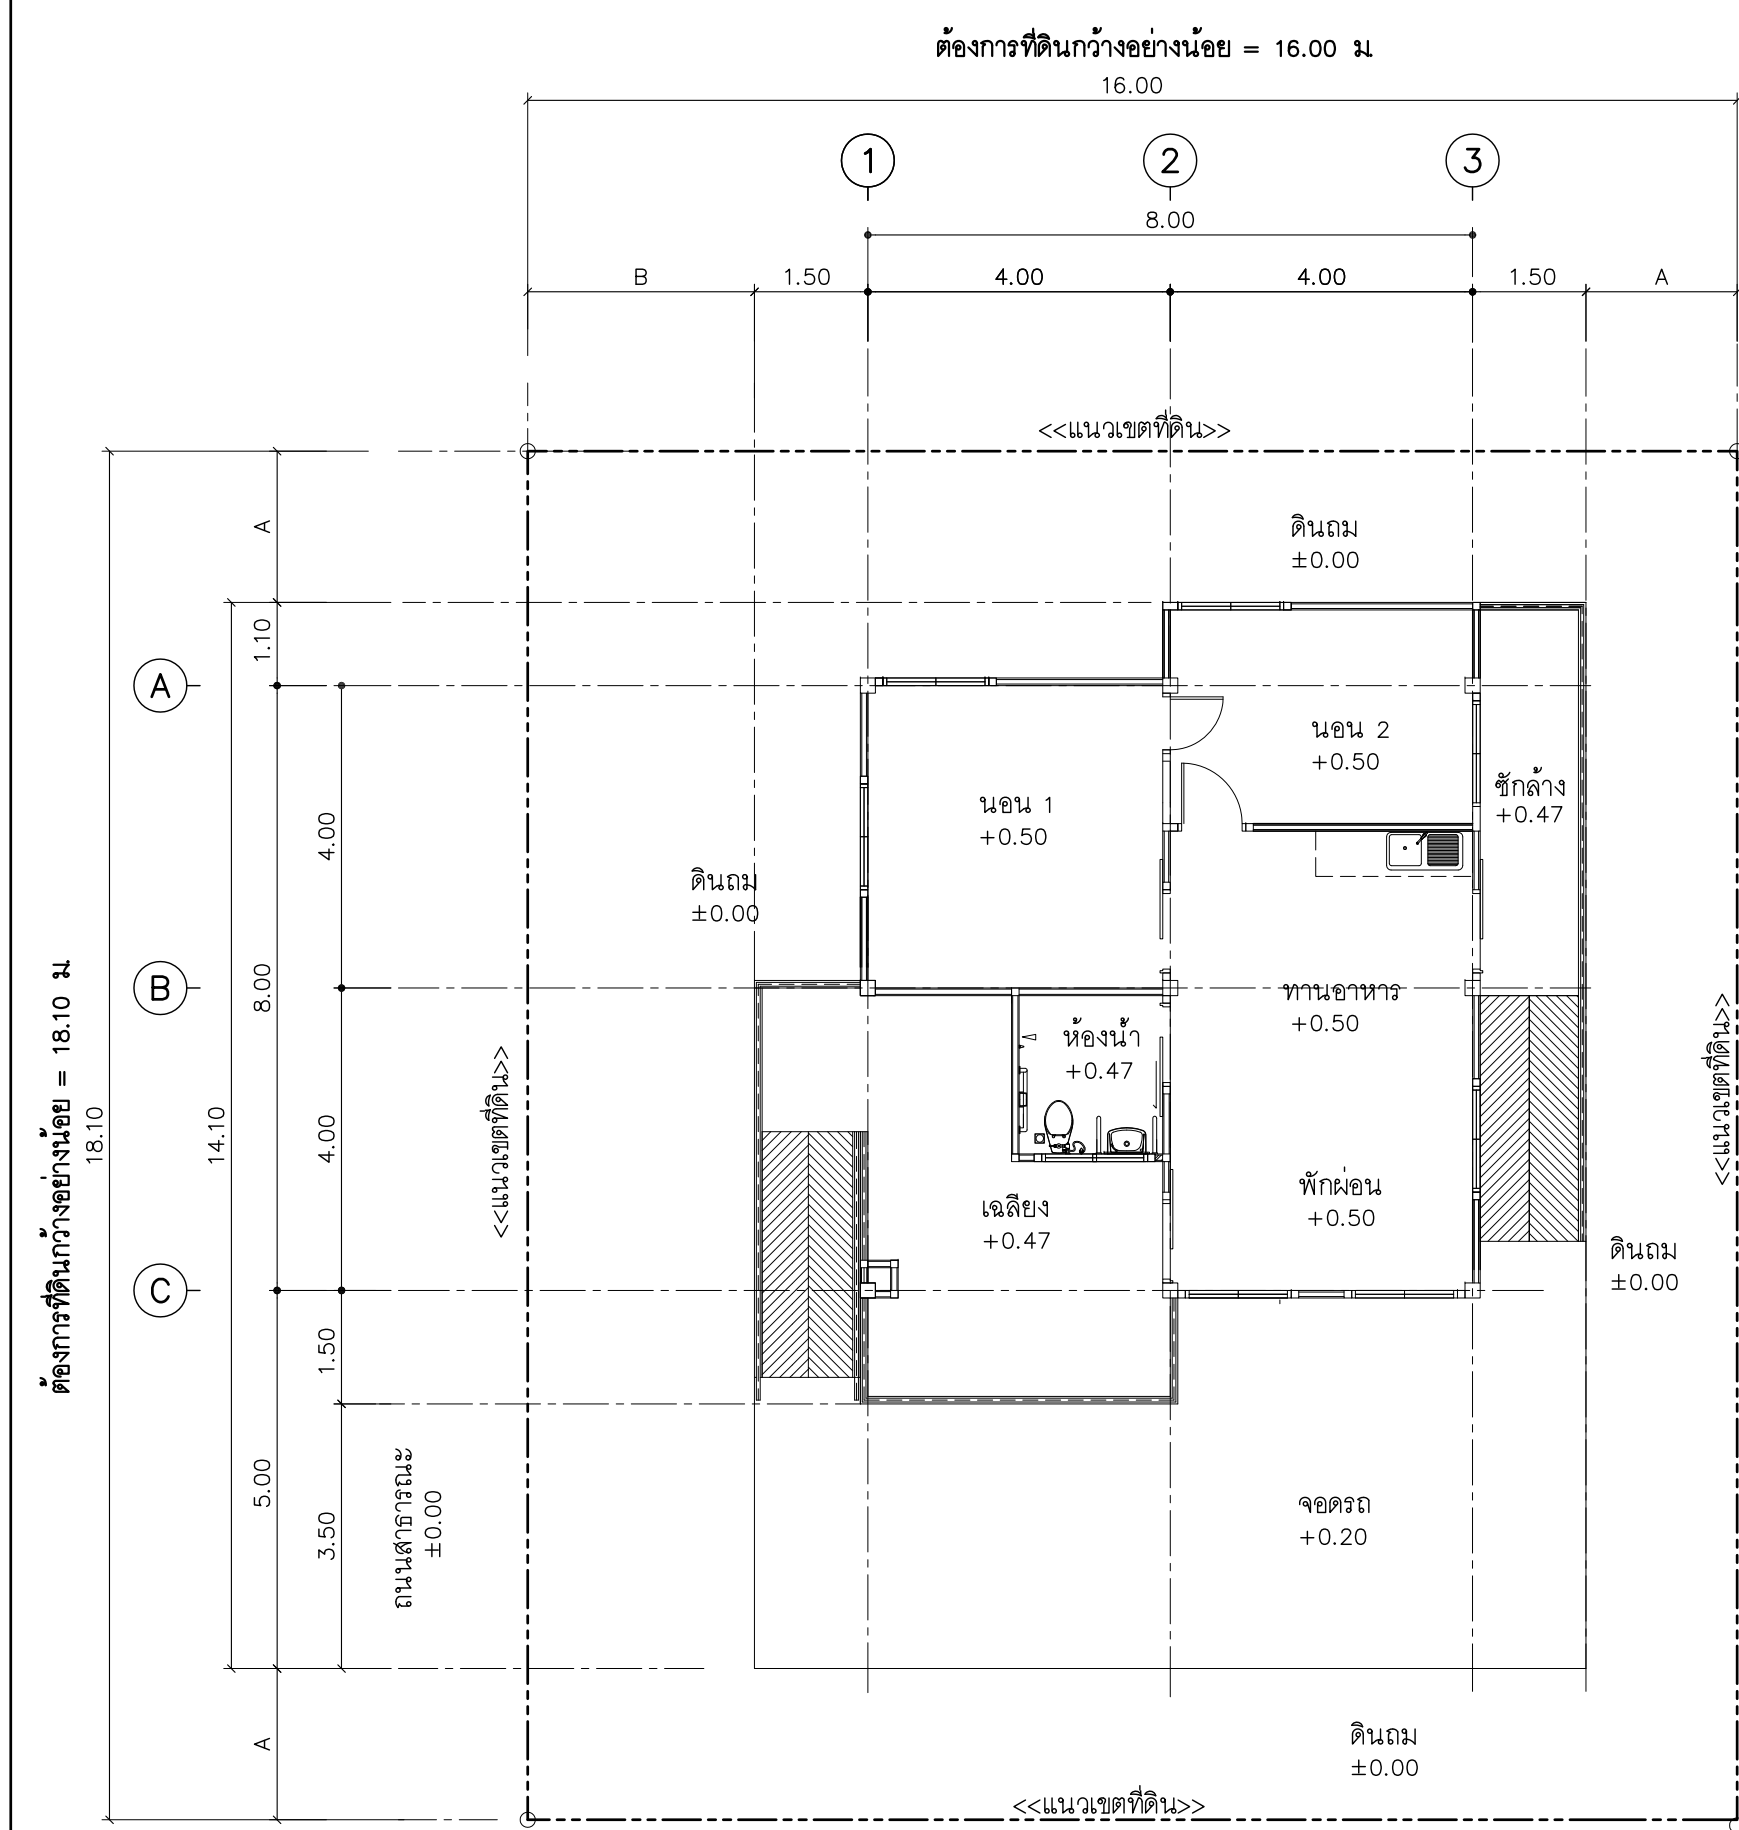

ผังบริเวณ

มาตราส่วน

1 : 100

หมายเหตุ

- ผังบริเวณนี้เป็นเพียงตัวอย่างเพื่อประมาณราคา ค่าก่อสร้างส่วนประกอบอาคารเท่านั้น
- ส่วนรายละเอียดของสถานที่จริง ให้กำหนดรายละเอียดขณะก่อสร้าง
- สายเมนไฟฟ้าให้เข้าทางด้านหน้า
- A=ระยะปรับตามขนาดที่ดิน แต่ไม่น้อยกว่า 2 ม หรือตามที่กฎหมายกำหนด
- B=ระยะปรับตามขนาดที่ดิน แต่ไม่น้อยกว่า 3 ม หรือตามที่กฎหมายกำหนด
- รางระบายน้ำให้ต่อลงบ่อพักภายนอก หรือที่ที่กำหนดให้
- ตำแหน่ง ถังบำบัดน้ำเสีย บ่อพักน้ำทิ้ง บ่อดักไขมัน แนวท่อ น้ำดี น้ำเสีย และท่อโสโครก ให้ดูแบบสุขาภิบาล



แบบบ้านसानฝัน
ของขวัญปีใหม่
คนไทยมีความสุข

แบบ
บ้านห่วงใยไทยประชาสุใจ 1

สำนักสถาปัตยกรรม
ผู้อำนวยการสำนัก

สถาปัตยกรรม
สถาปนิก

สำนักวิศวกรรมโครงสร้างและงานระบบ
ผู้อำนวยการสำนัก

วิศวกรรม
วิศวกร

โครงสร้าง
วิศวกร

วิศวกรรม
วิศวกร

สุขาภิบาล
วิศวกร

วิศวกรรม
วิศวกร

ไฟฟ้า
วิศวกร

วิศวกรรม
วิศวกร

เครื่องกล
วิศวกร


แสดงแบบ
ผังบริเวณ

มาตราส่วน -

วัน/เดือน/ปี 19/10/59

เลขที่แบบ AR 58237


A-03 21

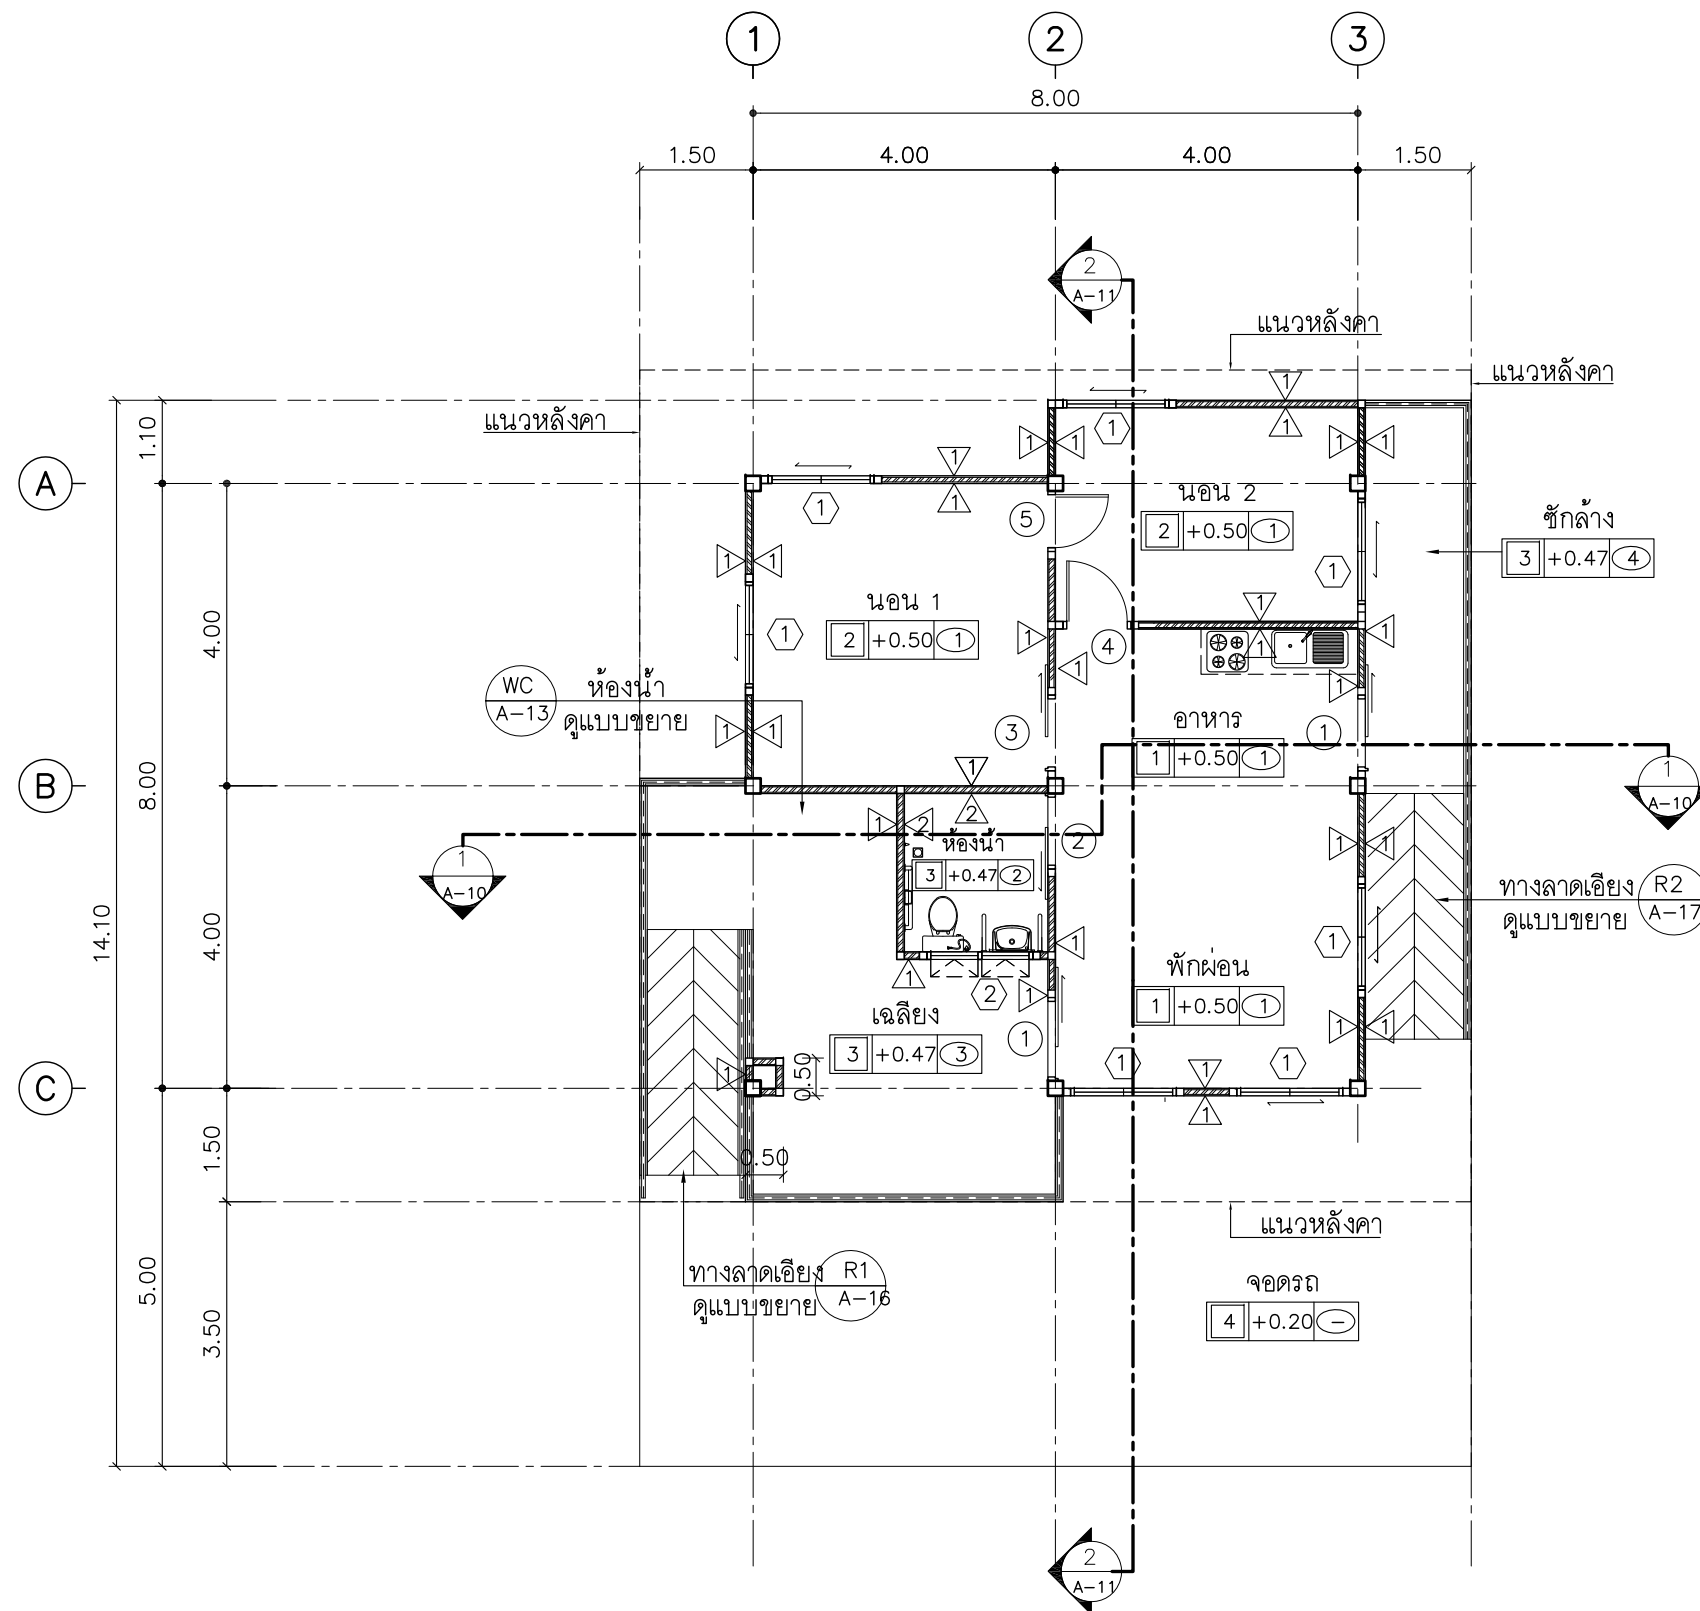

แปลนพื้นที่ 1

มาตราส่วน

1 : 100

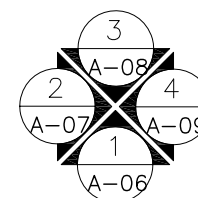

แบบบ้านสถานพื้น
ของขวัญใหม่
คนไทยมีความสุข

แบบ
บ้านห่วงใยไทยประชาสุขใจ 1

สำนักสถาปัตยกรรม

[Signature]

ผู้อำนวยการสำนัก

สถาปัตยกรรม

[Signature]

สถาปนิก

[Signature]

สถาปนิก

สำนักวิศวกรรมโครงสร้างและงานระบบ

[Signature]

ผู้อำนวยการสำนัก

วิศวกรรม

[Signature]

วิศวกร

โครงสร้าง

[Signature]

วิศวกร

วิศวกรรม

[Signature]

วิศวกร

สุขาภิบาล

[Signature]

วิศวกร

วิศวกรรม

[Signature]

วิศวกร

ไฟฟ้า

[Signature]

วิศวกร

วิศวกรรม

[Signature]

วิศวกร

เครื่องกล

[Signature]

วิศวกร

[Signature]
(นายเกียรติศักดิ์ จันทร์ตรา)
วิศวกรใหญ่

อนุมัติ

[Signature]
(นายสมชาย สดประเสริฐ)
อธิบดีกรมโยธาธิการและผังเมือง

แสดงแบบ

แปลนพื้นที่ 1

มาตราส่วน

—

วัน/เดือน/ปี


19/10/59

เลขที่แบบ

AR 58237

A-04


21

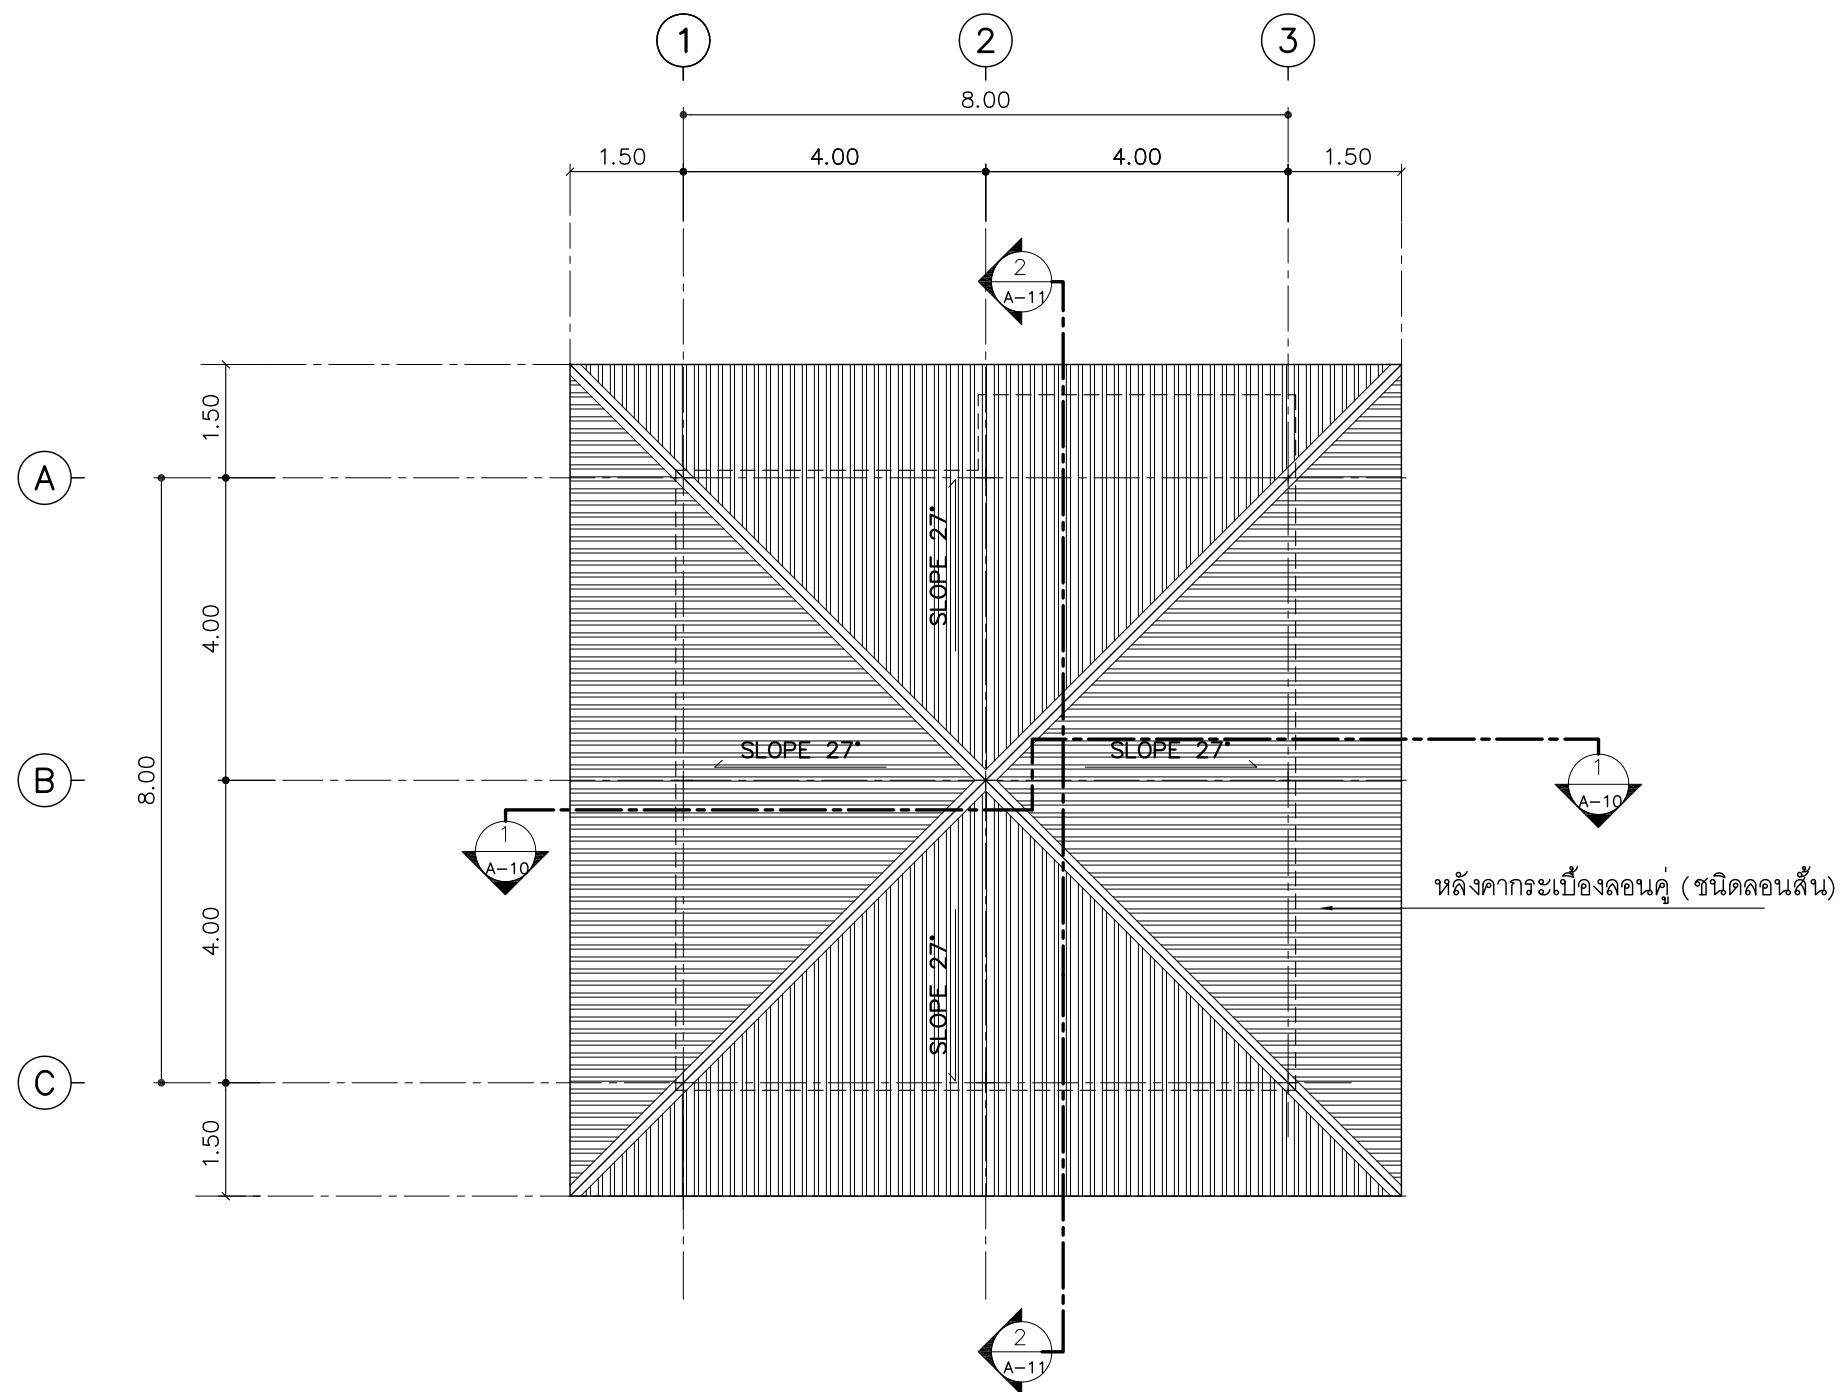

แปลนหลังคา

มาตราส่วน

1 : 100

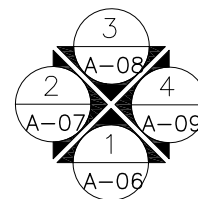

แบบบ้านसानฝัน
ของขวัญปีใหม่
คนไทยมีความสุข

แบบ
บ้านห่วงใยไทยประชาสุใจ 1

สำนักสถาปัตยกรรม
ผู้ช่วยการสำนัก

สถาปัตยกรรม
สถาปนิก

สำนักวิศวกรรมโครงสร้างและงานระบบ
ผู้ช่วยการสำนัก

วิศวกรรม
วิศวกร

โครงสร้าง
วิศวกร

วิศวกรรม
วิศวกร

สุขาภิบาล
วิศวกร

วิศวกรรม
วิศวกร

ไฟฟ้า
วิศวกร

วิศวกรรม
วิศวกร

เครื่องกล
วิศวกร


(นายเกียรติศักดิ์ จันทรา)
วิศวกรใหญ่

อนุมัติ
(นายมงคล สดประเสริฐ)
อธิบดีกรมโยธาธิการและผังเมือง

แสดงแบบ
แปลนหลังคา

มาตราส่วน -
วัน/เดือน/ปี 19/10/59
เลขที่แบบ AR 58237

A-05 21

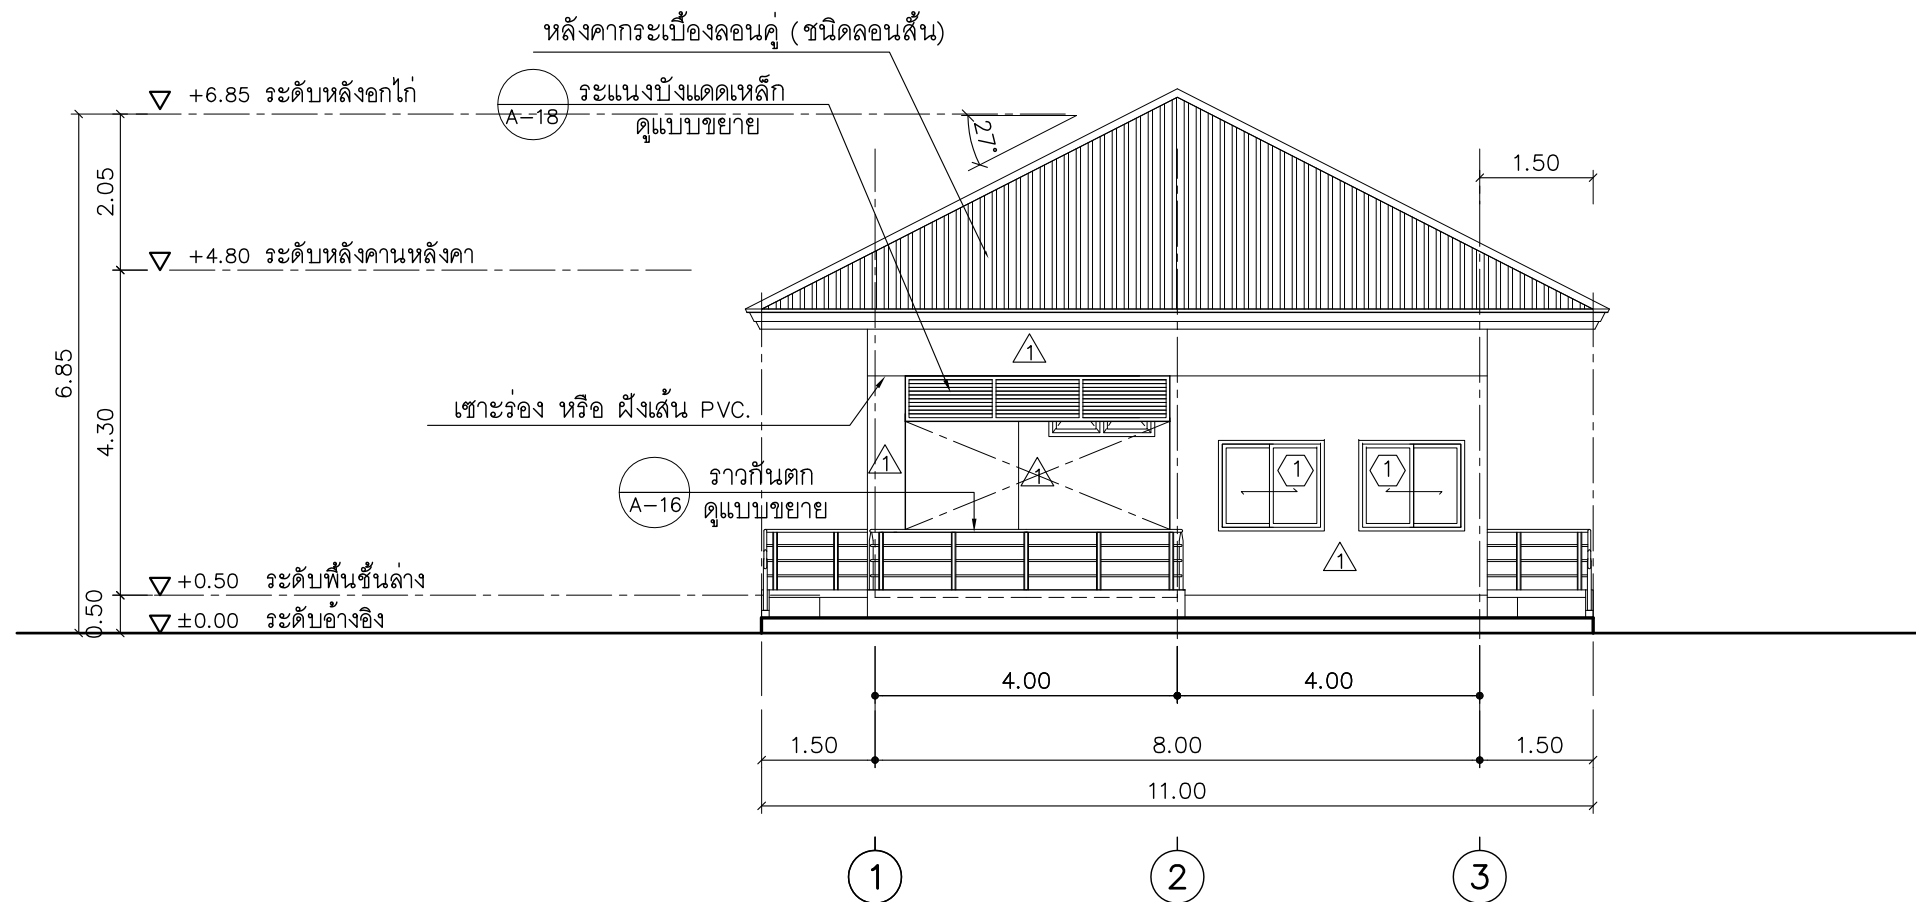

รูปด้าน 1

มาตราส่วน

1 : 100



แบบบ้านสถานพื้น
ของขงขงขงขง
คนไทยมีความสุข

แบบ
บ้านขงขงขงขงขงขง 1

สำนักสถาปัตยกรรม
ผู้ดำเนินการสำนัก

สถาปัตยกรรม
สถาปนิก

สำนักวิศวกรรมโครงสร้างและงานระบบ
ผู้ดำเนินการสำนัก

วิศวกรรม
วิศวกร

โครงสร้าง
วิศวกร

วิศวกรรม
วิศวกร

สุขาภิบาล
วิศวกร

วิศวกรรม
วิศวกร

ไฟฟ้า
วิศวกร

วิศวกรรม
วิศวกร

เครื่องกล
วิศวกร

(นายเกียรติศักดิ์ จันทร์ตรา)
วิศวกรใหญ่

อนุมัติ
(นายสมชาย สดประเสริฐ)
อธิบดีกรมโยธาธิการและผังเมือง

แสดงแบบ
รูปด้าน 1

มาตราส่วน -
วัน/เดือน/ปี 19/10/59
เลขที่แบบ AR 58237

A-06 21



แบบบ้านसानฝัน
ของขวัญปีใหม่
คนไทยมีความสุข

แบบ
บ้านห่วงใยไทยประชาสุขใจ 1

สำนักสถาปัตยกรรม
ผู้ดำเนินการสำนัก

สถาปัตยกรรม
สถาปนิก
สถาปนิก

สำนักวิศวกรรมโครงสร้างและงานระบบ
ผู้ดำเนินการสำนัก

วิศวกรรม
วิศวกร
โครงสร้าง
วิศวกร

วิศวกรรม
วิศวกร
สุขาภิบาล
วิศวกร

วิศวกรรม
วิศวกร
ไฟฟ้า
วิศวกร

วิศวกรรม
วิศวกร
เครื่องกล
วิศวกร

(นายเกียรติศักดิ์ จันทรา)
วิศวกรใหญ่

อนุมัติ
(นายมงคล สดประเสริฐ)
อธิบดีกรมโยธาธิการและผังเมือง


แสดงแบบ
รูปด้าน 2

มาตราส่วน -


วัน/เดือน/ปี 19/10/59

เลขที่แบบ AR 58237

A-07 21

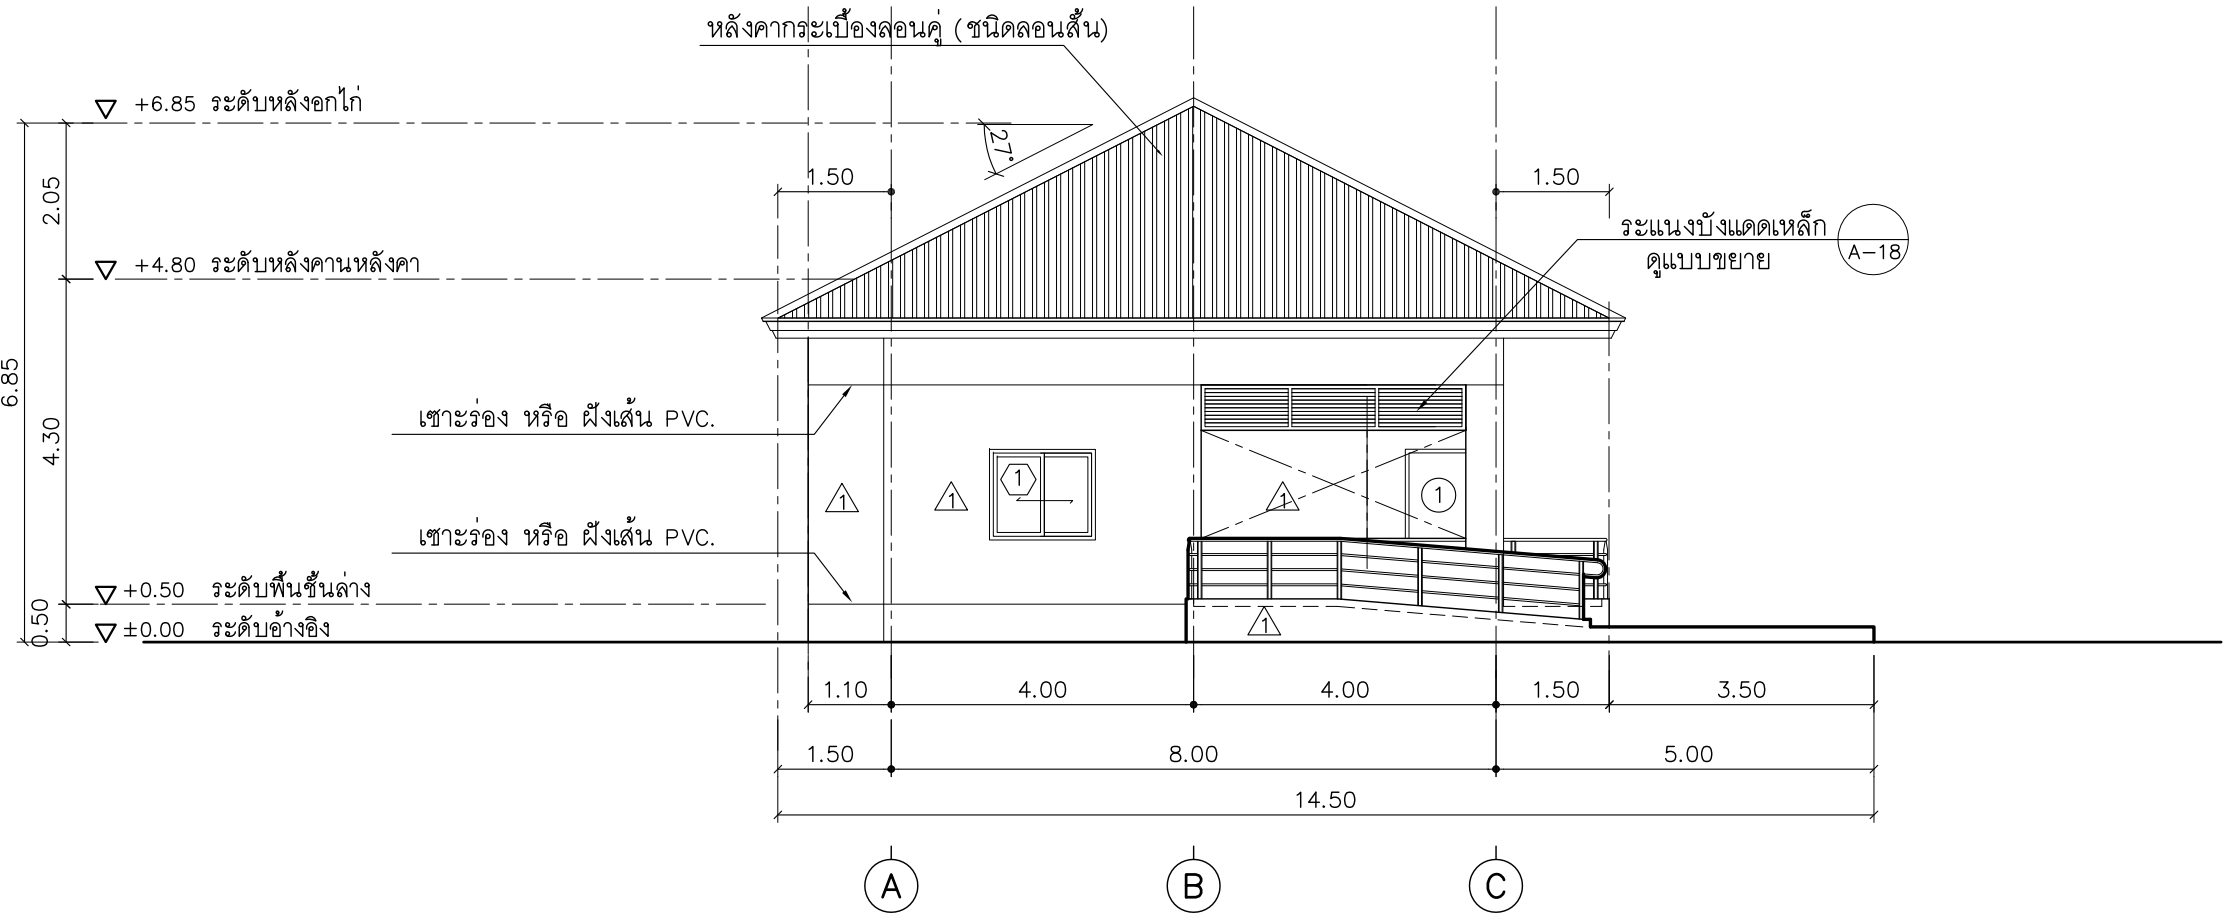

รูปด้าน 2
มาตราส่วน 1 : 100

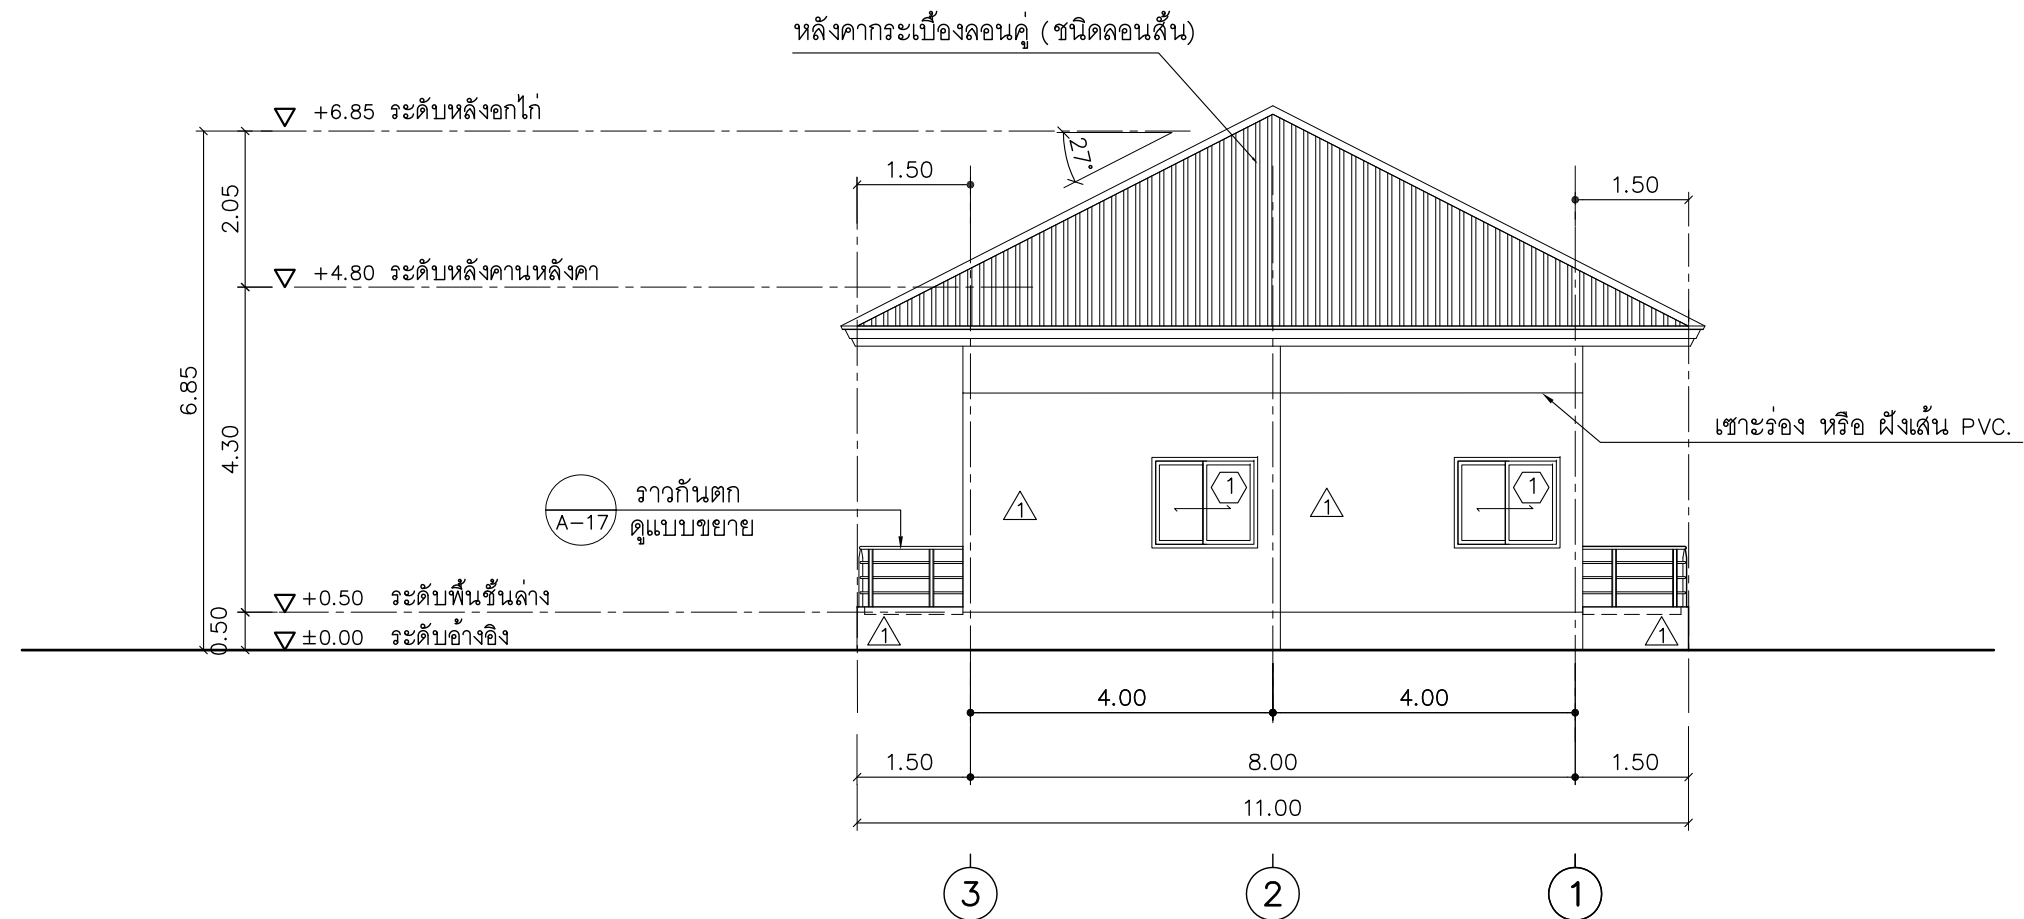

รูปด้าน 3

มาตราส่วน

1 : 100




แบบบ้านสถานพื้น
ของขวัญปีใหม่
คนไทยมีความสุข

แบบ
บ้านห่วงใยไทยประชารัฐใจ 1

สำนักสถาปัตยกรรม

 ผู้อำนวยกา

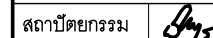สถาปัตยกรรม  สถาปนิก


 สถาปนิก


สำนักวิศวกรรมโครงสร้างและงานระบบ

 ผู้อำนวยกา

วิศวกรรม  วิศวกร

โครงสร้าง  วิศวกร

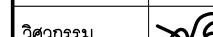วิศวกรรม  วิศวกร

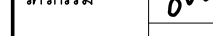
สุขาภิบาล  วิศวกร

วิศวกรรม  วิศวกร

ไฟฟ้า  วิศวกร

วิศวกรรม  วิศวกร

เครื่องกล  วิศวกร

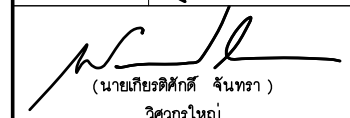
(นายเกียรติศักดิ์ จันทรา)
วิศวกรใหญ่

อนุมัติ

(นายมงคล สดประเสริฐ)
อธิบดีกรมโยธาธิการและผังเมือง


แสดงแบบ
รูปด้าน 3

มาตราส่วน -

วัน/เดือน/ปี 19/10/59

เลขที่แบบ AR 58237

A-08 21

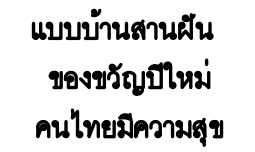

สำนักสถาปัตยกรรม



ผู้อำนวยการสำนัก

สถาปัตยกรรม		สถาปนิก
		สถาปนิก

สำนักวิศวกรรมโครงสร้างและงานระบบ



ผู้อำนวยการสำนัก

วิศวกรรม	✓	วิศวกร
โครงสร้าง		วิศวกร

วิศวกรรม	วิศวกร
สุขาภิบาล	วิศวกร

วิศวกรรม		วิศวกร
ไฟฟ้า		วิศวกร

วิศวกรรวม		วิศวกร
เครื่องกล		วิศวกร

(นายเกียรติศักดิ์ จันทรา)
วิศวกรใหญ่

อนันต์

(นายมนฑล สุตประเสริฐ)

อธิบดีกรมโยธาธิการและผังเมือง

แสดงแบบ


รูปด้าน 4

มาตราส่วน	—
-----------	---

วัน/เดือน/ปี	19/10/59
เลขที่แบบ	AR 58237

A-09	21
------	----



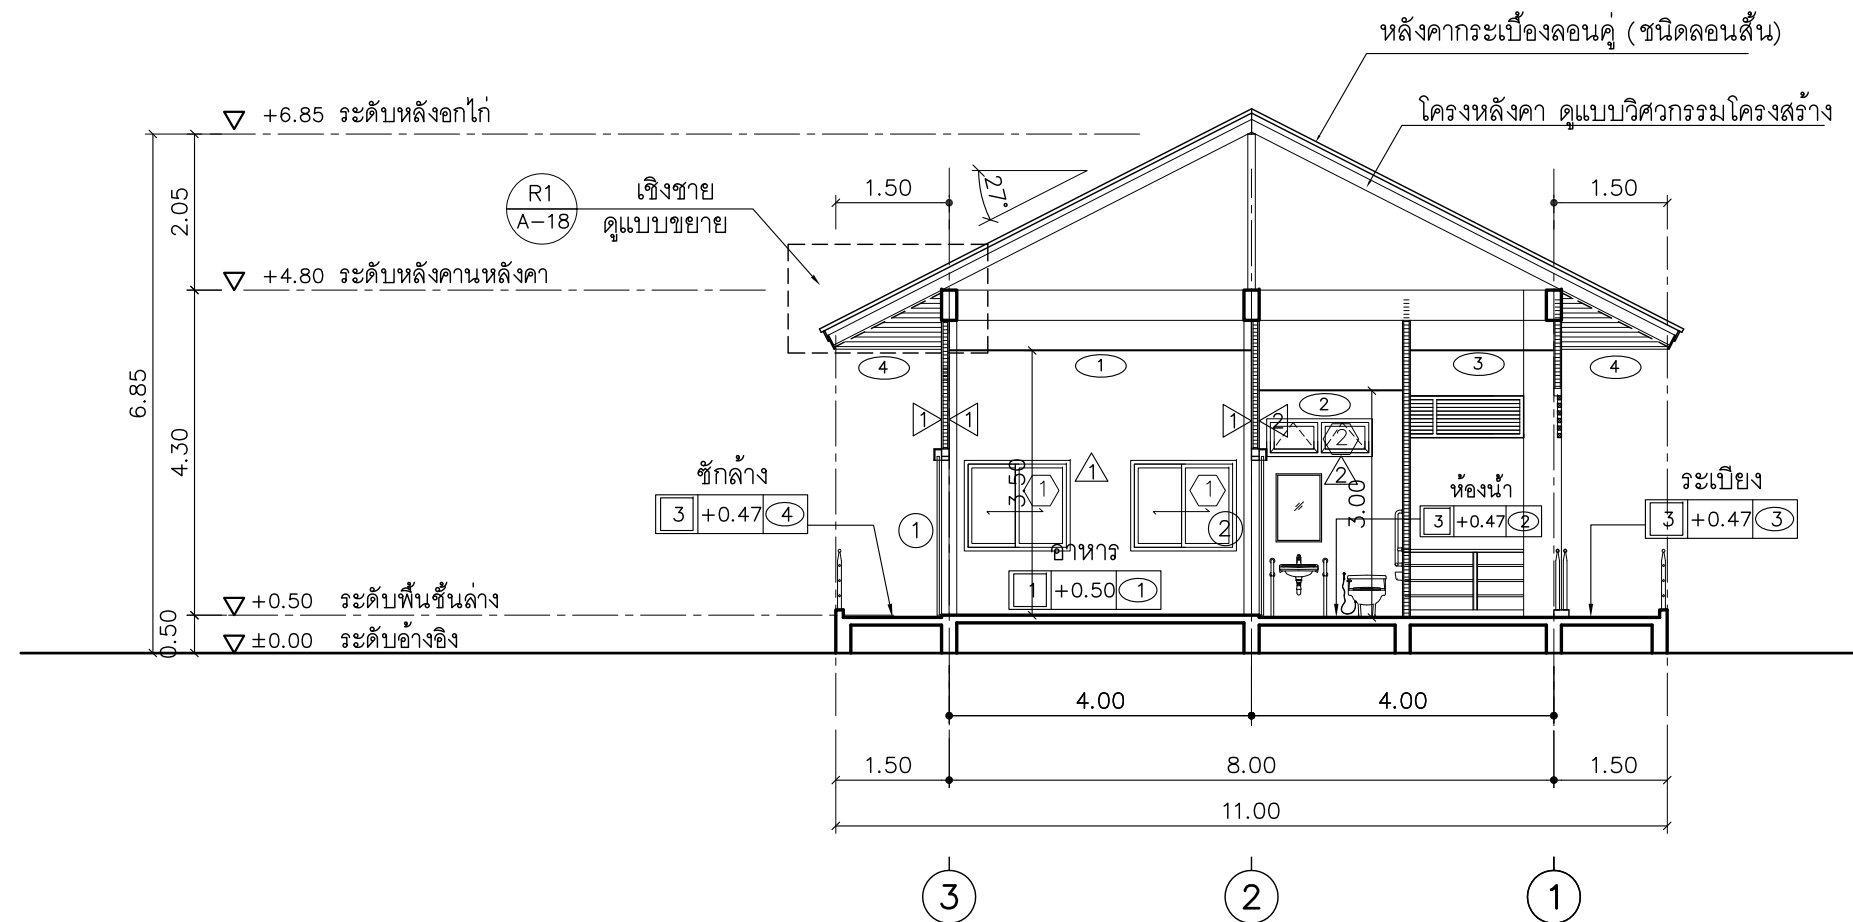

รูปตัด 1

มาตราส่วน

1 : 100



แบบบ้านสถานพื้น
ของขวัญปีใหม่
คนไทยมีความสุข

แบบ
บ้านห่วงใยไทยประชารัฐใจ 1

สำนักสถาปัตยกรรม
ผู้ดำเนินการสำนัก

สถาปัตยกรรม
สถาปนิก

สำนักวิศวกรรมโครงสร้างและงานระบบ
ผู้ดำเนินการสำนัก

วิศวกรรม
วิศวกร

โครงสร้าง
วิศวกร

วิศวกรรม
วิศวกร

สุขาภิบาล
วิศวกร

วิศวกรรม
วิศวกร

ไฟฟ้า
วิศวกร

วิศวกรรม
วิศวกร


เครื่องกล
วิศวกร

อนุมัติ
(นายมงคล สดประเสริฐ)
อธิบดีกรมโยธาธิการและผังเมือง

แสดงแบบ
รูปตัด 1

มาตราส่วน
วัน/เดือน/ปี 19/10/59
เลขที่แบบ AR 58237

A-10 21

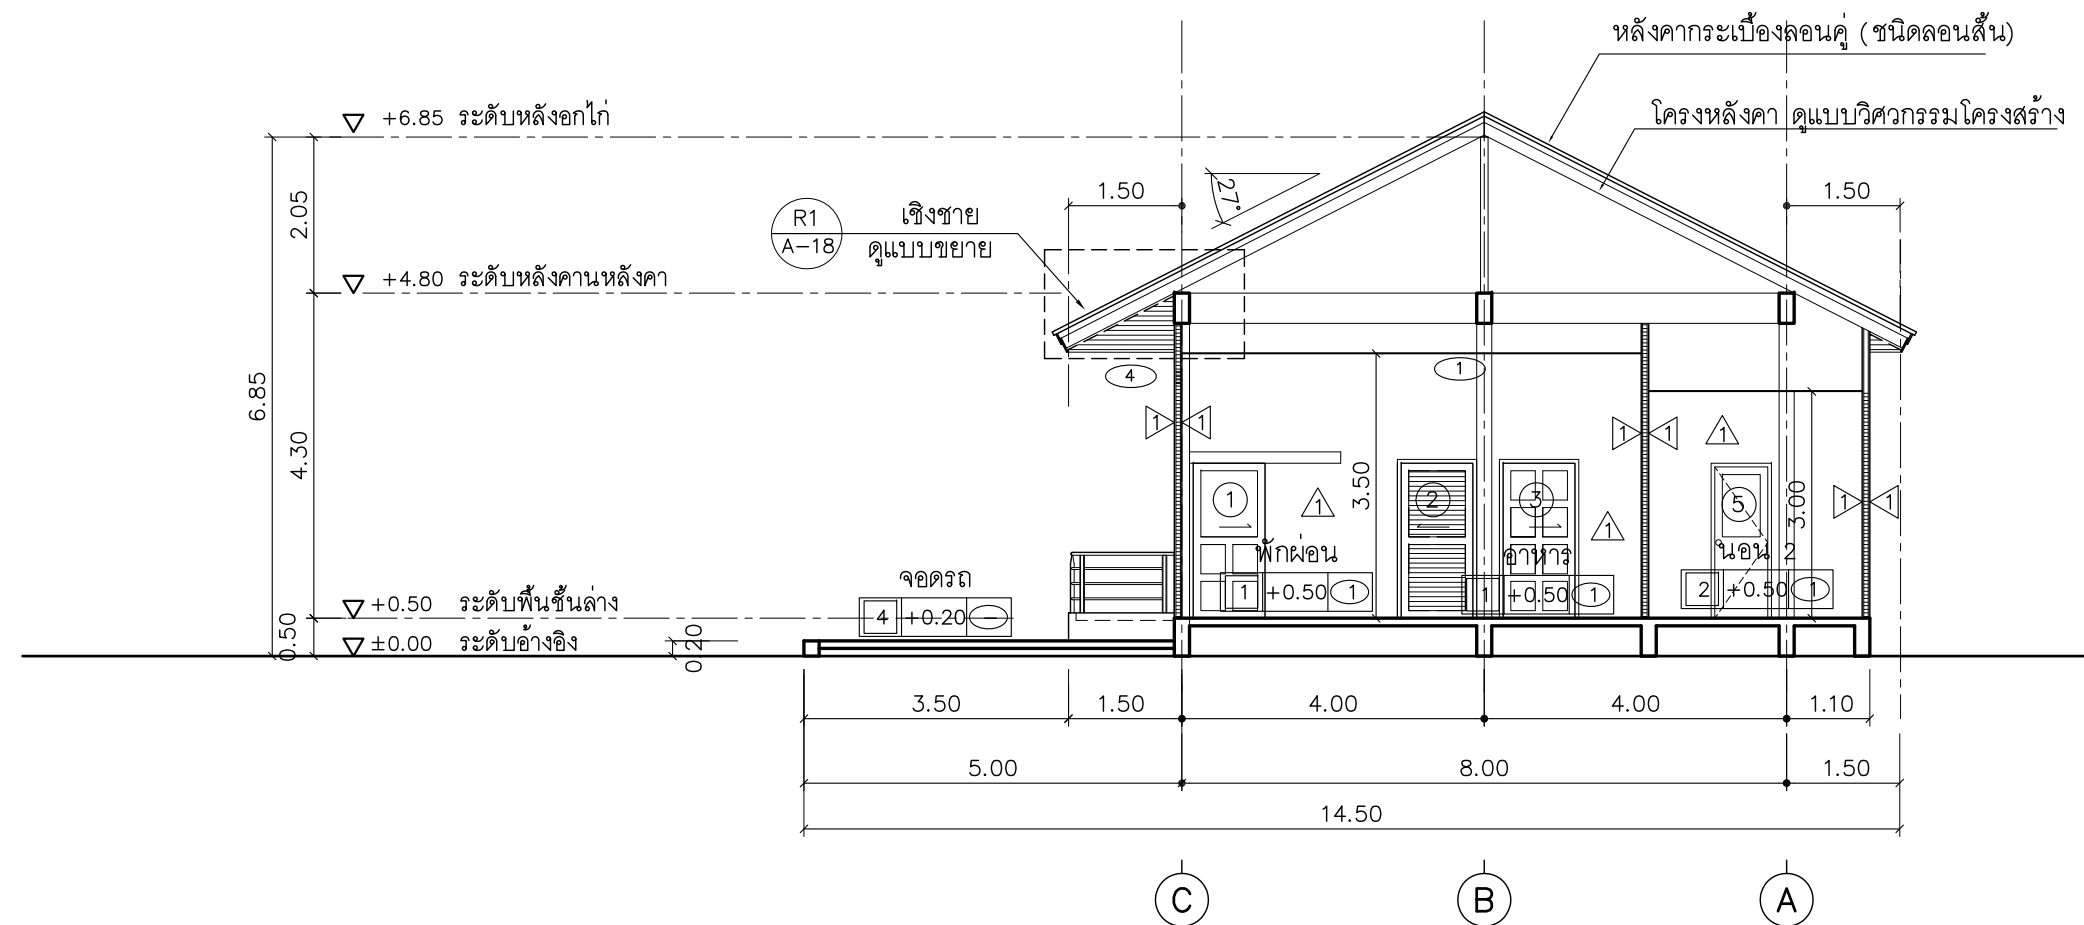

รูปตัด 2

มาตราส่วน

1 : 100



แบบบ้านसानฝัน
ของขวัญปีใหม่
คนไทยมีความสุข

แบบ
บ้านห่วงใยไทยประชาสุใจ 1

สำนักสถาปัตยกรรม
ผู้อำนวยกาสร้าน

สถาปัตยกรรม
สถาปนิก

สำนักวิศวกรรมโครงสร้างและงานระบบ
ผู้อำนวยกาสร้าน

วิศวกรรม
วิศวกร

โครงสร้าง
วิศวกร

วิศวกรรม
วิศวกร

สุขาภิบาล
วิศวกร

วิศวกรรม
วิศวกร

ไฟฟ้า
วิศวกร

วิศวกรรม
วิศวกร
















เครื่องกล
วิศวกร

อนุมัติ
(นายมงคล สดประเสริฐ)
อธิบดีกรมโยธาธิการและผังเมือง

แสดงแบบ
รูปตัด 2


มาตราส่วน
วัน/เดือน/ปี 19/10/59
เลขที่แบบ AR 58237

A-11 21

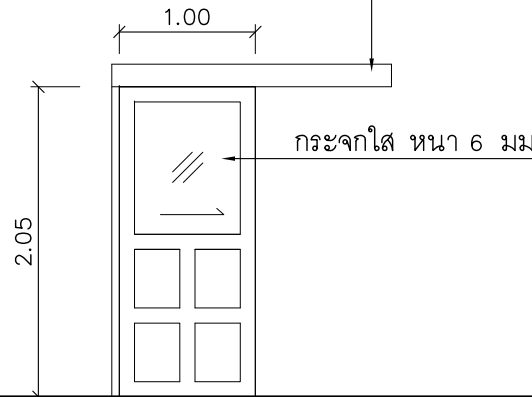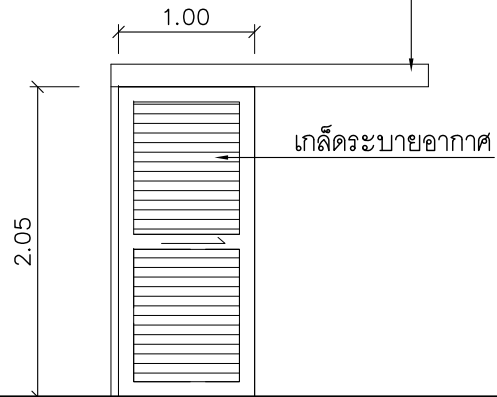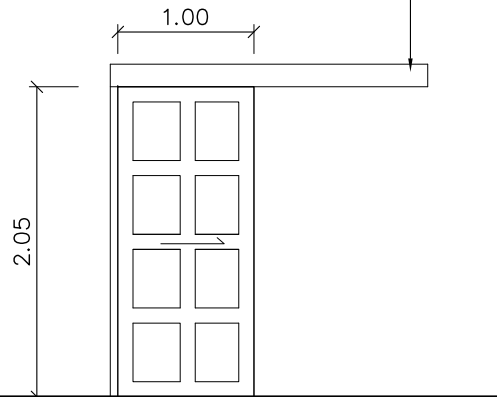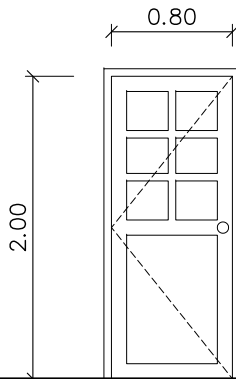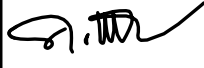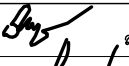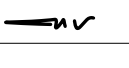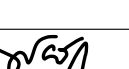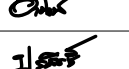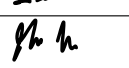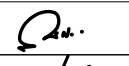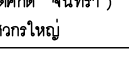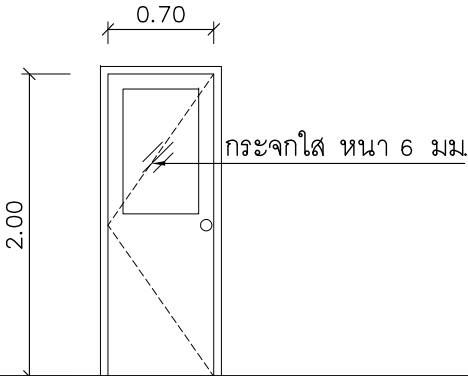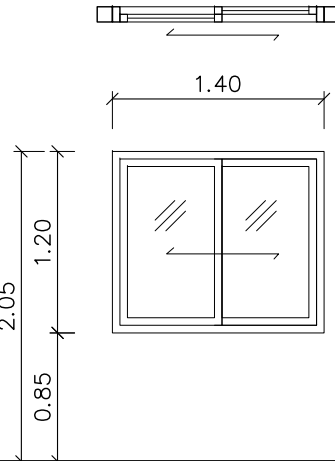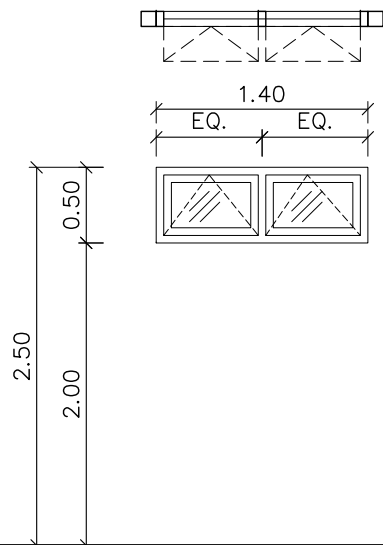กล่องรางประตูกรุด้วยไม้อัดสักทำสี ติดตั้ง DOOR STOPPER ภายในราง 		กล่องรางประตูกรุด้วยไม้อัดสักทำสี ติดตั้ง DOOR STOPPER ภายในราง 		กล่องรางประตูกรุด้วยไม้อัดสักทำสี ติดตั้ง DOOR STOPPER ภายในราง 				 แบบบ้านसानฝัน ของขวัญปีใหม่ คนไทยมีความสุข แบบ บ้านห่วงใยไทยประชาสุใจ 1 สำนักสถาปัตยกรรม ผู้อำนวยการสำนัก สถาปัตยกรรม สถาปนิก สถาปนิก สำนักวิศวกรรมโครงสร้างและงานระบบ ผู้อำนวยการสำนัก วิศวกรรม วิศวกร โครงสร้าง วิศวกร วิศวกรรม วิศวกร สุขาภิบาล วิศวกร วิศวกรรม วิศวกร ไฟฟ้า วิศวกร วิศวกรรม วิศวกร เครื่องกล วิศวกร  (นายเกียรติศักดิ์ จันทรา) วิศวกรใหญ่ อนุมัติ  (นายมงคล สดประเสริฐ) อธิบดีกรมโยธาธิการและผังเมือง แสดงแบบ แบบขยายประตู แบบขยายหน้าต่าง มาตราส่วน - วัน/เดือน/ปี 19/10/59 เลขที่แบบ AR 58237 A-12 21
①		②		③		④		
ชนิดบาน	บานเปิดเดี่ยว	ชนิดบาน	บานเปิดเดี่ยว	ชนิดบาน	บานเปิดเดี่ยว	ชนิดบาน	บานเปิดเดี่ยว	
วงกบ	ไม้เนื้อแข็ง 2" x 4"	วงกบ	วงกบ PVC.	วงกบ	ไม้เนื้อแข็ง 2" x 4"	วงกบ	ไม้เนื้อแข็ง 2" x 4"	
กรอบบาน	-	กรอบบาน	-	กรอบบาน	-	กรอบบาน	-	
บาน	บานประตูสำเร็จรูป HDF.	บาน	บานประตูสำเร็จรูป HDF.	บาน	บานประตู PVC.	บาน	บานประตูสำเร็จรูป HDF.	
อุปกรณ์	อุปกรณ์ประตูบานเลื่อน ครบชุด	อุปกรณ์	อุปกรณ์ประตูบานเลื่อน ครบชุด	อุปกรณ์	อุปกรณ์ประตูบานเลื่อน ครบชุด	อุปกรณ์	ลูกบิด , มาตรฐานครบชุด	
หมายเหตุ	ติดตั้งบริเวณ ห้องครัว , ห้องนอน	หมายเหตุ	ติดตั้งบริเวณ ห้องครัว , ห้องนอน	หมายเหตุ	ติดตั้งบริเวณห้องน้ำ	หมายเหตุ	ติดตั้งบริเวณ ห้องครัว , ห้องนอน	
								
⑤		1		2				
ชนิดบาน	บานเปิดเดี่ยว	ชนิดบาน	บานเลื่อนสลับ	ชนิดบาน	บานกระทุ้ง	ชนิดบาน		
วงกบ	ไม้เนื้อแข็ง 2" x 4"	วงกบ	อลูมิเนียมอบสีขาว	วงกบ	อลูมิเนียมอบสีขาว	วงกบ		
กรอบบาน	-	กรอบบาน	อลูมิเนียมอบสีขาว	กรอบบาน	อลูมิเนียมอบสีขาว	กรอบบาน		
บาน	บานประตูสำเร็จรูป HDF.	บาน	กระจกใส หนา 6มม.	บาน	กระจกใส หนา 6มม.	บาน		
อุปกรณ์	ลูกบิด , มาตรฐานครบชุด	อุปกรณ์	มาตรฐานครบชุด	อุปกรณ์	มาตรฐานครบชุด	อุปกรณ์		
หมายเหตุ	ติดตั้งบริเวณห้องนอน	หมายเหตุ		หมายเหตุ		หมายเหตุ		

มาตรฐานสัญลักษณ์และรายการสัญลักษณ์


สัญลักษณ์	รายการสัญลักษณ์
WC.1	โถส้วมแบบนั่งราบ อุปกรณ์ครบชุด
WC.2	โถส้วมแบบนั่งยอง
LAV.1	อ่างล้างหน้าแบบฝักหรือตั้งบนเคาน์เตอร์ พร้อมอุปกรณ์ครบชุด
LAV.2	อ่างล้างหน้าแบบแขวนผนัง พร้อมอุปกรณ์ครบชุด
F1	ก๊อกอ่างล้างหน้า
PH.	ที่ใส่กระดาษชำระ
UR.	โถปัสสาวะชาย
HS.	ชุดสายฉีดชำระ
M.	กระจกเงาอย่างดี หน้า 5 มม.
TR.	ราวแขวนผ้า
SP.	ที่วางสบู่
SW.	ฝักบัวสายอ่อน อุปกรณ์ครบชุด
K.	ก๊อกล้างพื้น
FD.	ฝาปิดรูระบายน้ำทั้งที่พื้น ชนิดมีตะแกรงและที่ดักกลิ่น
หมายเหตุ	

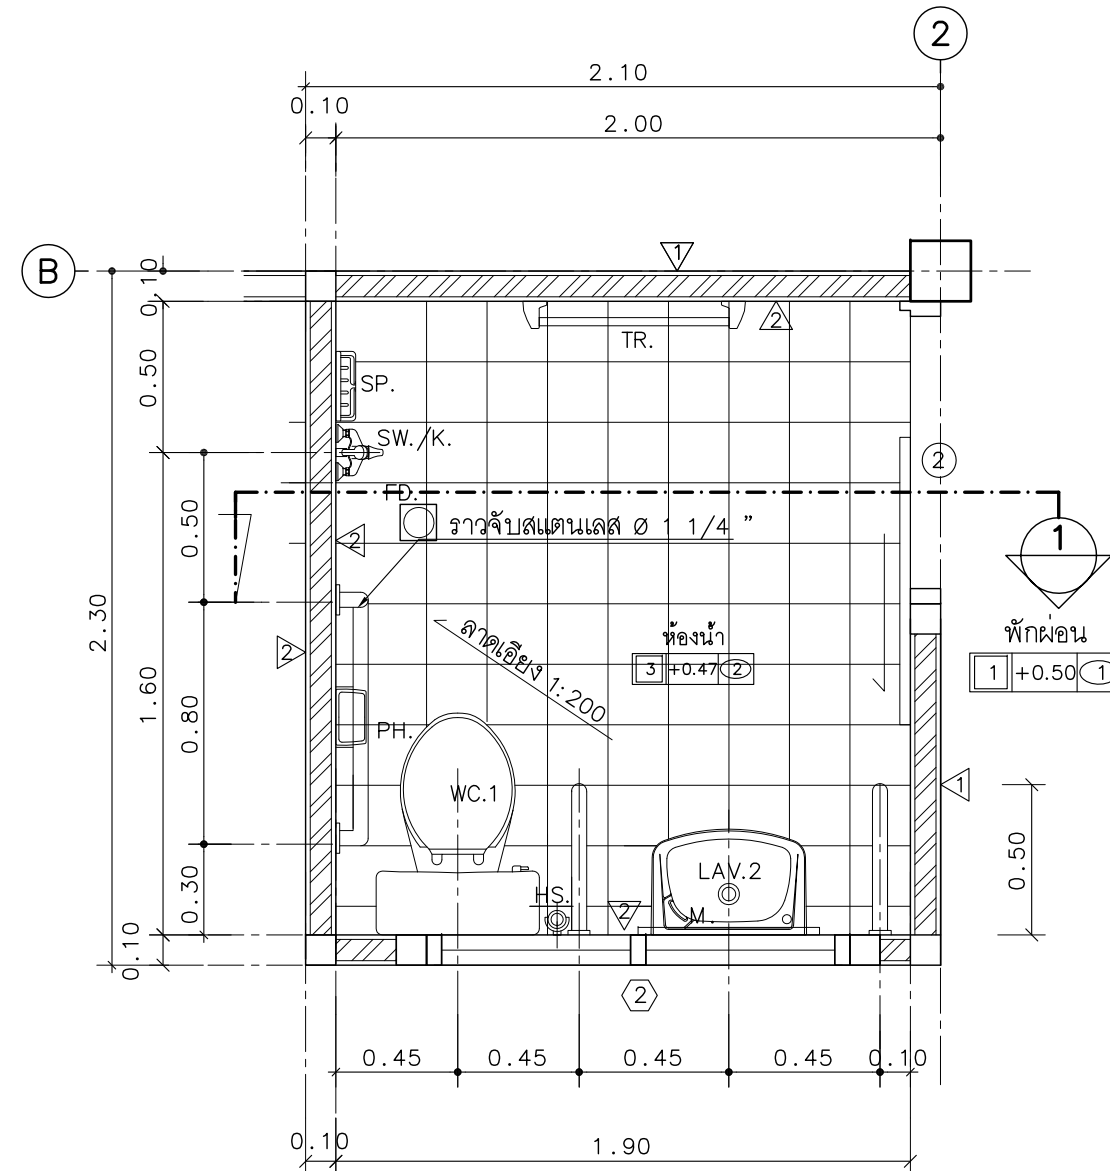

แปลนห้องน้ำ WC.

มาตราส่วน

1 : 25

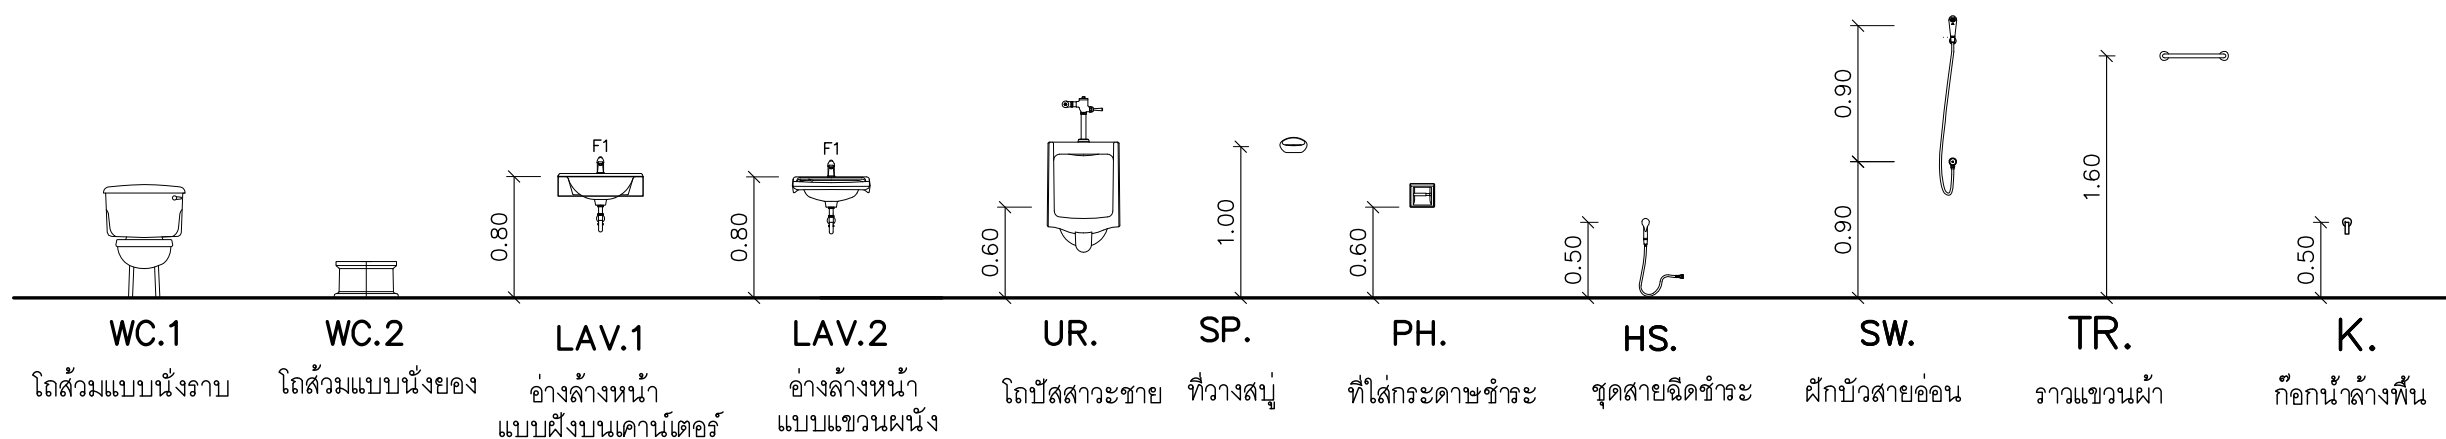

มาตรฐานระดับการติดตั้งสัญลักษณ์

มาตราส่วน

1 : 50



แบบบ้านสถานพื้น
ของขวัญปีใหม่
คนไทยมีความสุข

แบบ
บ้านห่วงใยไทยประชาสุใจ 1

สำนักสถาปัตยกรรม
ผู้ดำเนินการสำนัก

สถาปัตยกรรม
สถาปนิก

สำนักวิศวกรรมโครงสร้างและงานระบบ
ผู้ดำเนินการสำนัก

วิศวกรรม
วิศวกร

โครงสร้าง
วิศวกร

วิศวกรรม
วิศวกร

สุขาภิบาล
วิศวกร

วิศวกรรม
วิศวกร

ไฟฟ้า
วิศวกร

วิศวกรรม
วิศวกร


เครื่องกล
วิศวกร

แสดงแบบ
รายการประกอบแบบห้องน้ำ
แบบขยายห้องน้ำ WC.

มาตราส่วน
วัน/เดือน/ปี 19/10/59

เลขที่แบบ AR 58237

A-13 21

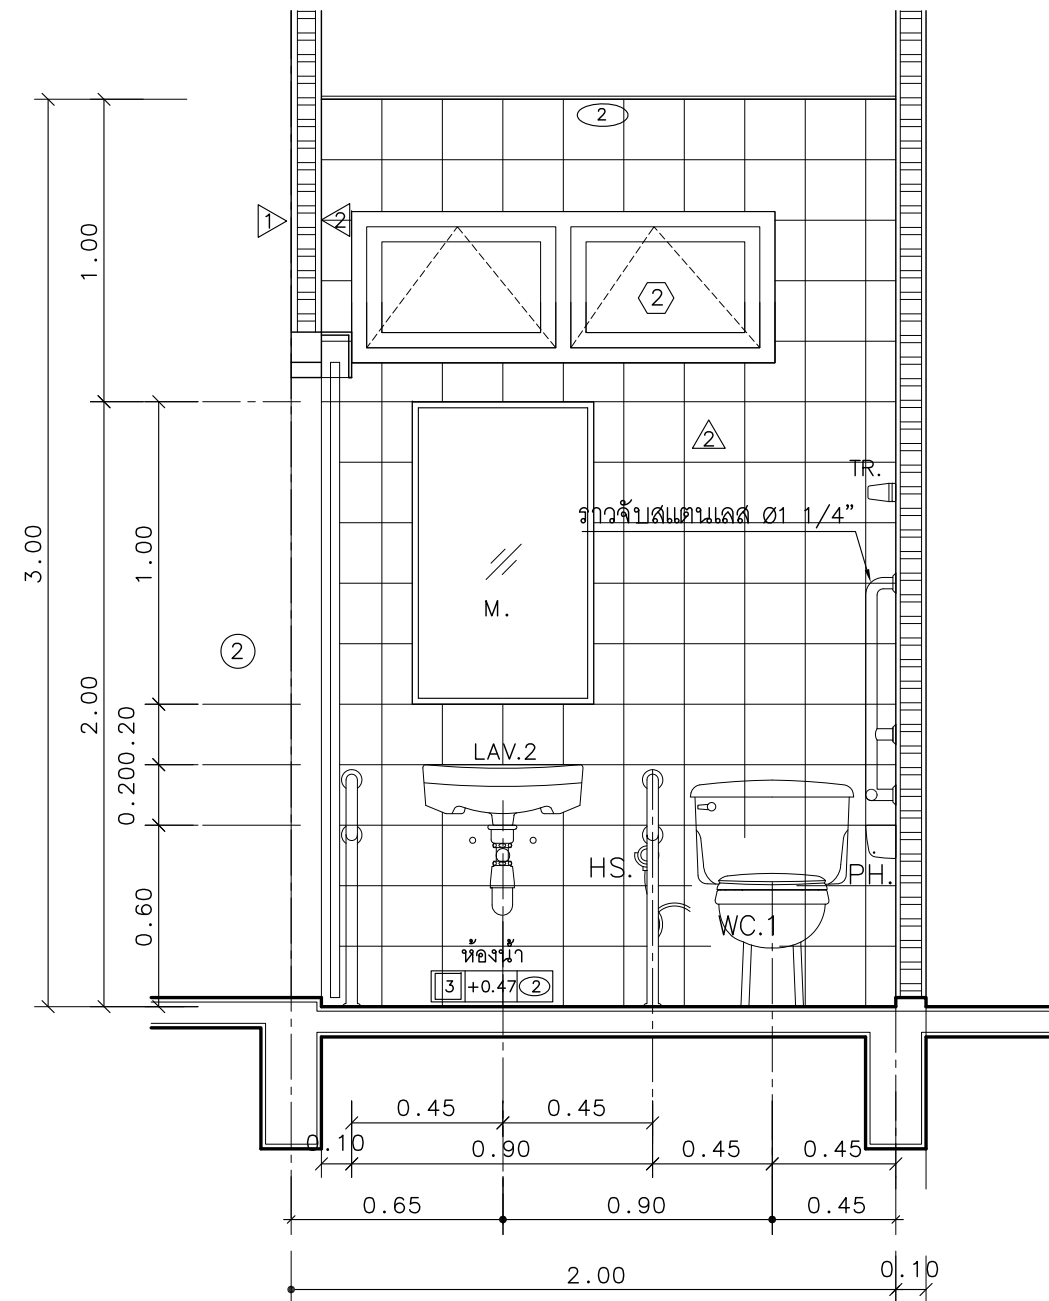

รูปตัดห้องน้ำ WC.

มาตราส่วน

1 : 25



แบบบ้านสถานพื้น
ของขวัญปีใหม่
คนไทยมีความสุข

แบบ
บ้านห่วงใยไทยประสาสุขใจ 1

สำนักสถาปัตยกรรม
ผู้ดำเนินการสำนัก

สถาปัตยกรรม
สถาปนิก

สำนักวิศวกรรมโครงสร้างและงานระบบ
ผู้ดำเนินการสำนัก

วิศวกรรม
วิศวกร

โครงสร้าง
วิศวกร

วิศวกรรม
วิศวกร

สุขาภิบาล
วิศวกร

วิศวกรรม
วิศวกร

ไฟฟ้า
วิศวกร

วิศวกรรม
วิศวกร


เครื่องกล
วิศวกร

อนุมัติ
(นายมนตรี สดประเสริฐ)
อธิบดีกรมโยธาธิการและผังเมือง


แสดงแบบ
แบบขยายห้องน้ำ WC.

มาตราส่วน -
วัน/เดือน/ปี 19/10/59
เลขที่แบบ AR 58237

A-14 21

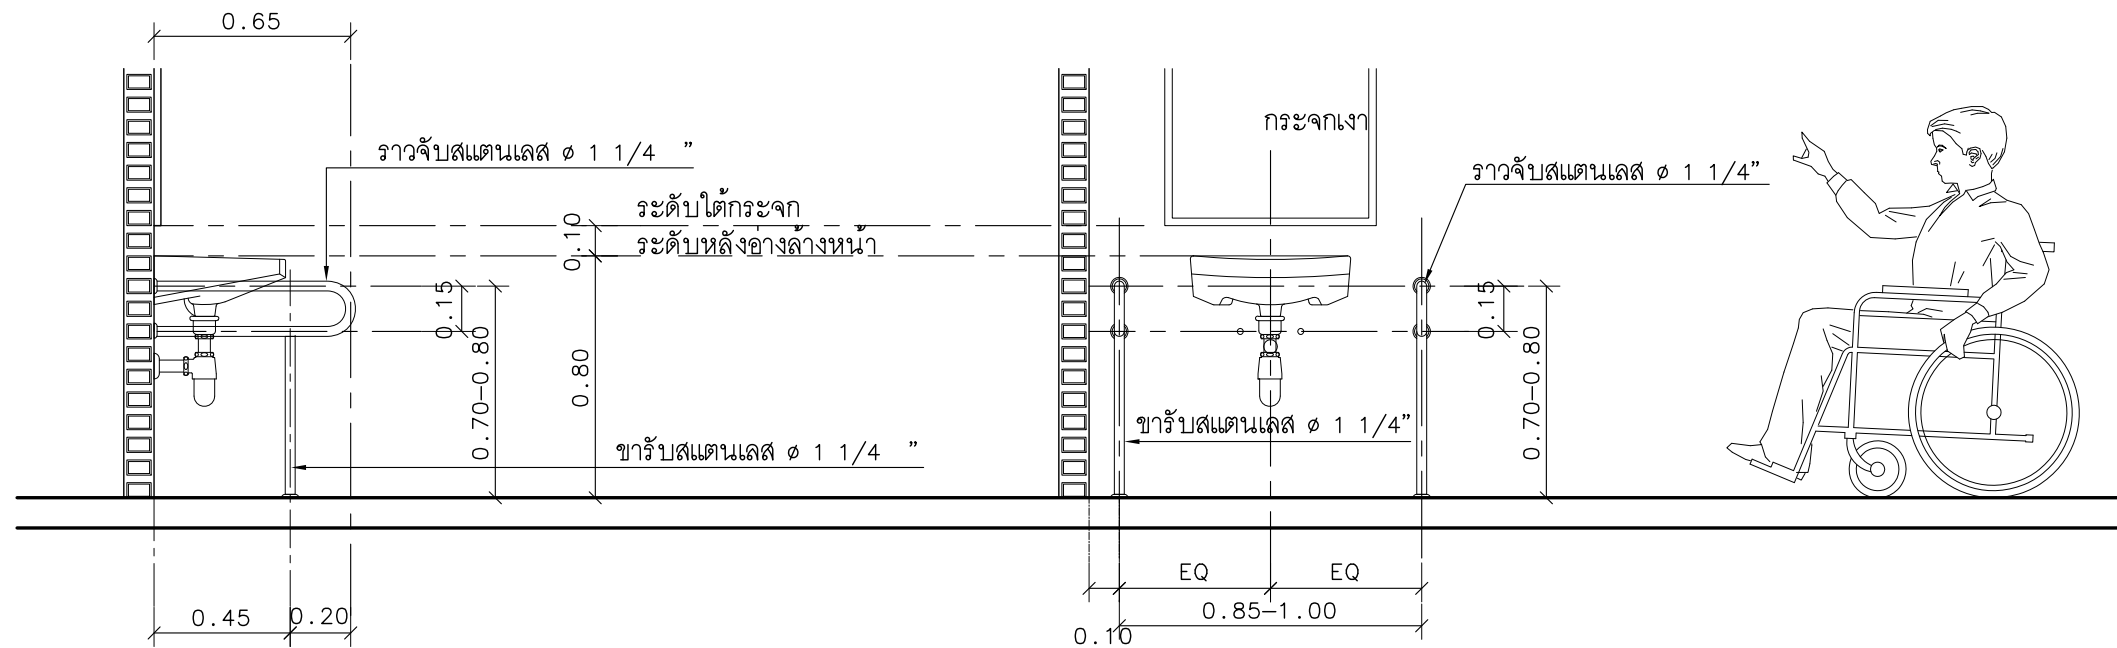

แบบขยายการติดตั้งราวทรงตัวสำหรับอ่างล้างหน้า
มาตราส่วน 1: 25

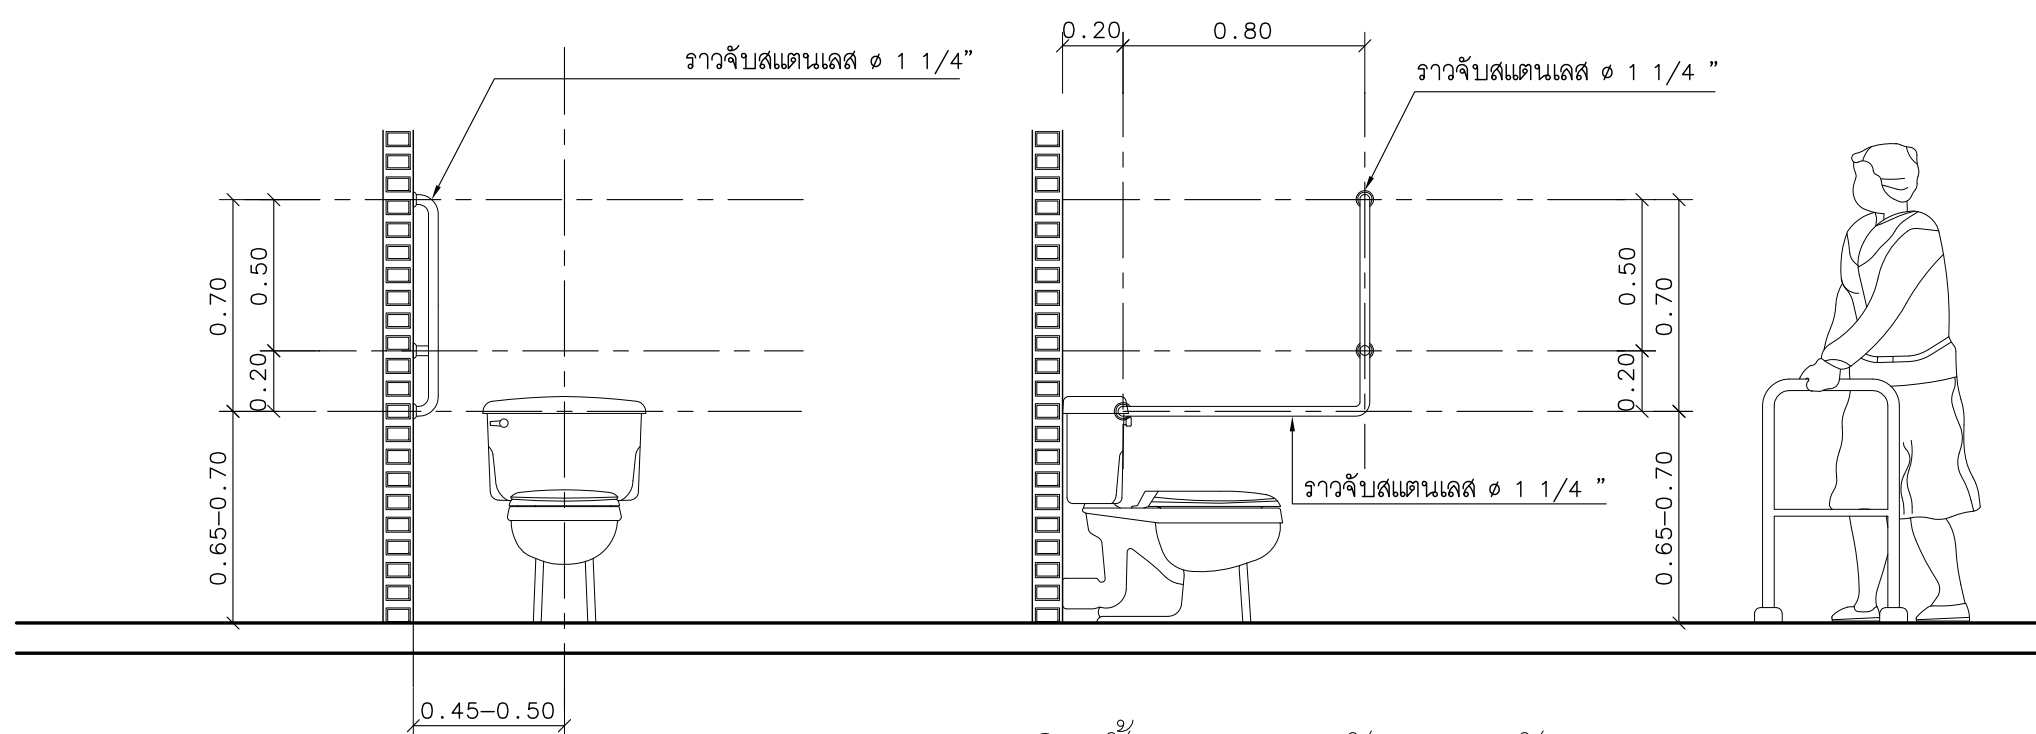

แบบขยายการติดตั้งราวทรงตัวแบบตัว L
มาตราส่วน 1: 25

แบบมาตรฐานการติดตั้งราวทรงตัวในห้องน้ำคนพิการ



แบบบ้านสานฝัน ของขวัญปีใหม่ คนไทยมีความสุข

แบบ
บ้านห่วงใยไทยประชาสุใจ 1

สำนักสถาปัตยกรรม
ผู้อำนวยการสำนัก

สถาปัตยกรรม
สถาปนิก

สำนักวิศวกรรมโครงสร้างและงานระบบ
ผู้อำนวยการสำนัก

วิศวกรรม
วิศวกร

โครงสร้าง
วิศวกร

วิศวกรรม
วิศวกร

สุขาภิบาล
วิศวกร

วิศวกรรม
วิศวกร

ไฟฟ้า
วิศวกร

วิศวกรรม
วิศวกร

เครื่องกล
วิศวกร

(นายเกียรติศักดิ์ จันทรา)
วิศวกรใหญ่

อนุมัติ
(นายมงคล สุดประเสริฐ)
อธิบดีกรมโยธาธิการและผังเมือง

แสดงแบบ
แบบมาตรฐานการติดตั้ง
ราวทรงตัวในห้องน้ำคนพิการ

มาตราส่วน -
วัน/เดือน/ปี 19/10/59
เลขที่แบบ AR 58237

A-15 21



แบบบ้านสถานพื้น
ของขงขงขงขง
คนไทยมีความสุข

แบบ
บ้านขงขงขงขงขงขง 1

สำนักสถาปัตยกรรม
ผู้ดำเนินการสำนัก

สถาปัตยกรรม
สถาปนิก

สำนักวิศวกรรมโครงสร้างและงานระบบ
ผู้ดำเนินการสำนัก

วิศวกรรม
วิศวกร

โครงสร้าง
วิศวกร

วิศวกรรม
วิศวกร

สุขาภิบาล
วิศวกร

วิศวกรรม
วิศวกร

ไฟฟ้า
วิศวกร

วิศวกรรม
วิศวกร

เครื่องกล
วิศวกร

(นายเกียรติศักดิ์ จันทร์ตรา)
วิศวกรใหญ่

อนุมัติ
(นายมงคล สดุดะประเสริฐ)
อธิบดีกรมโยธาธิการและผังเมือง

แสดงแบบ
แบบขยายทางลาดเอียง R.1


มาตราส่วน -

วัน/เดือน/ปี 19/10/59

เลขที่แบบ AR 58237

A-16

21

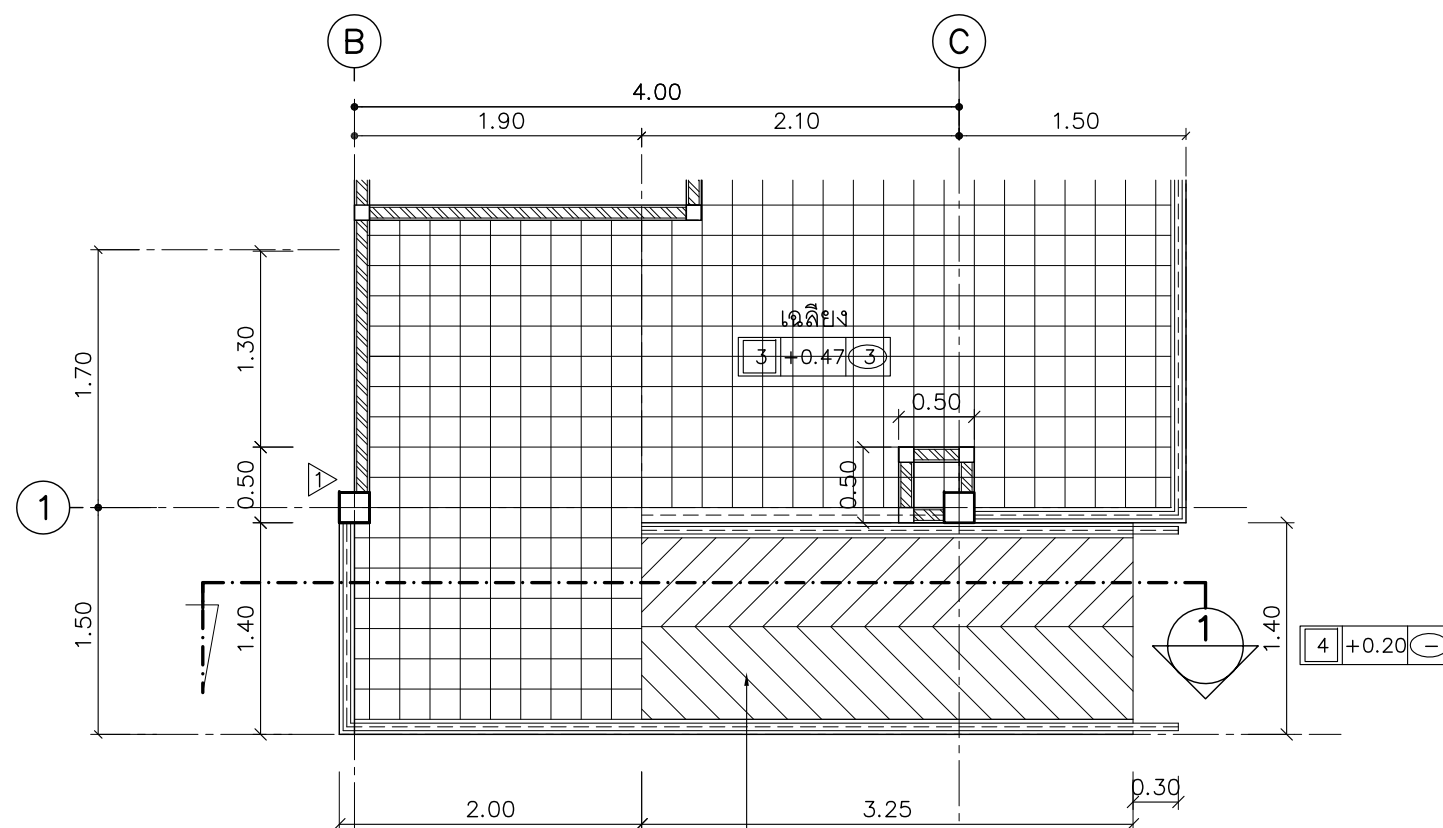


แปลนทางลาดเอียง R.1

มาตราส่วน

1: 50


พื้นทางลาด ค.ส.ล. ผิวทำกรวดล่าง
เสาขวง 1.5x1 ซม. @ 0.10 ม.

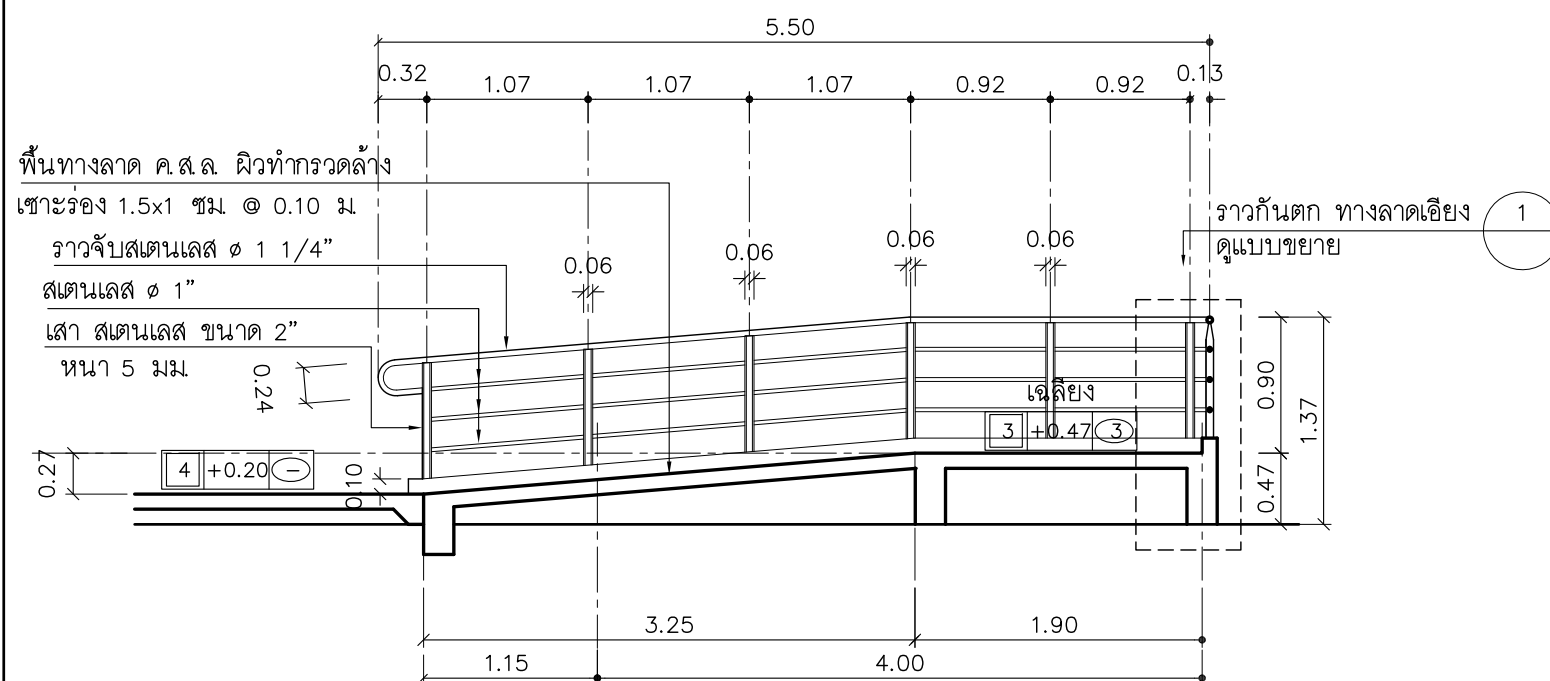

รูปตัดทางลาดเอียง R.1

มาตราส่วน




1 : 50

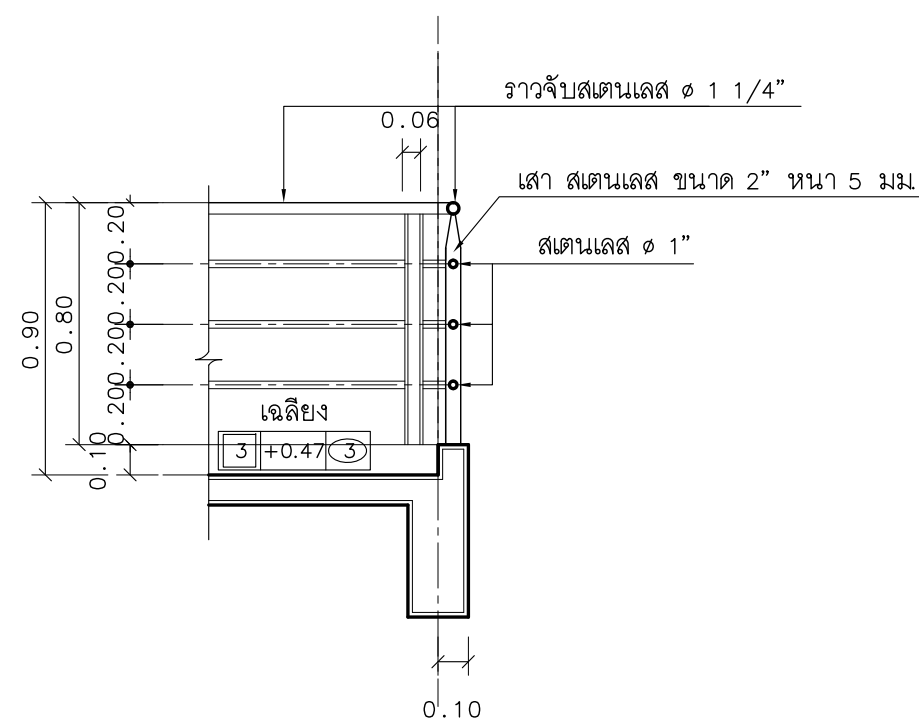

แบบขยายราวกันตก

SCALE

1: 25

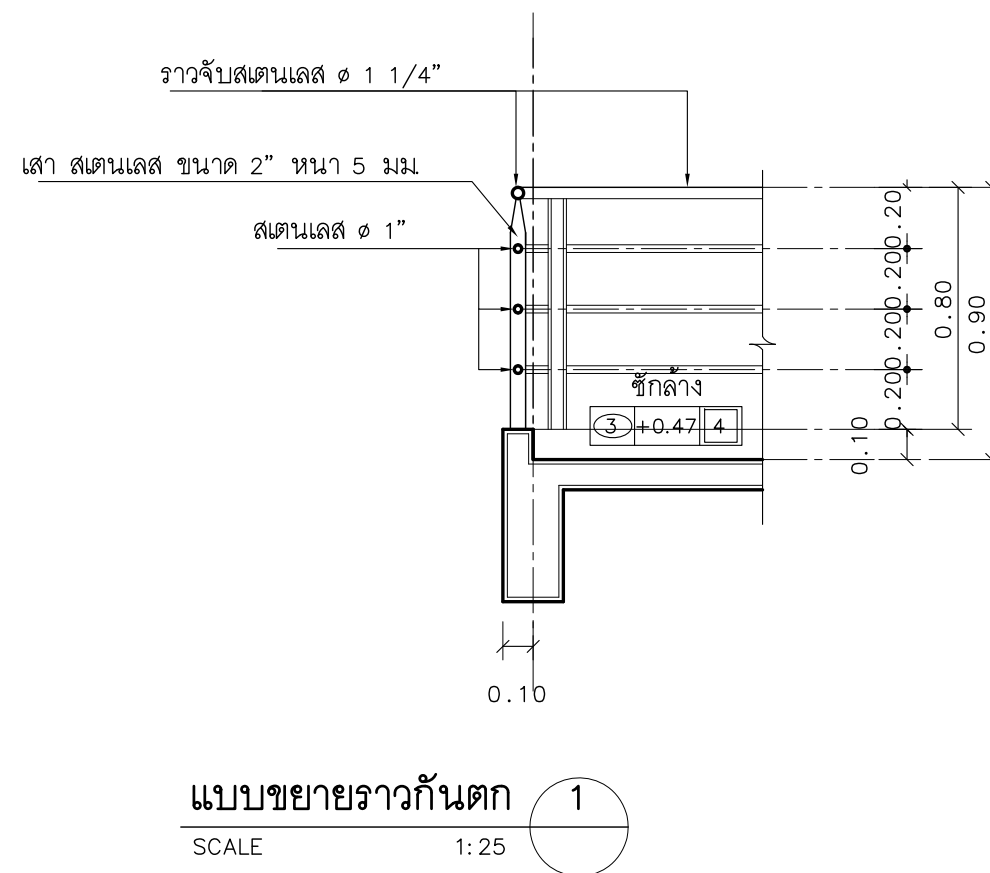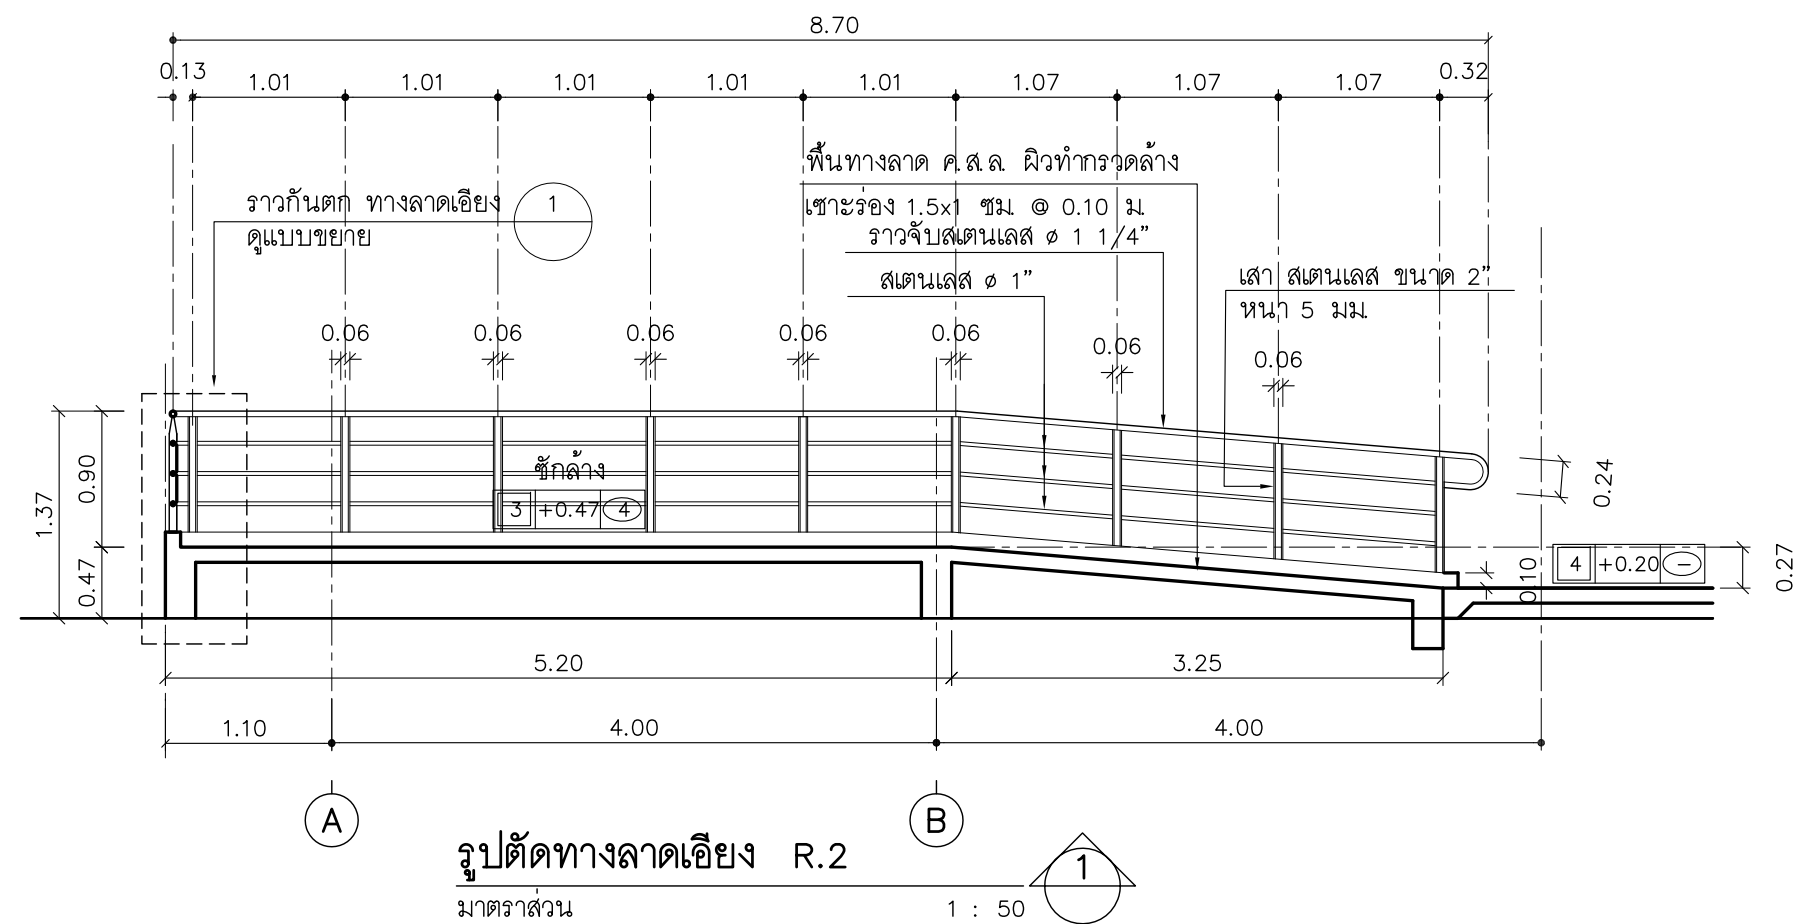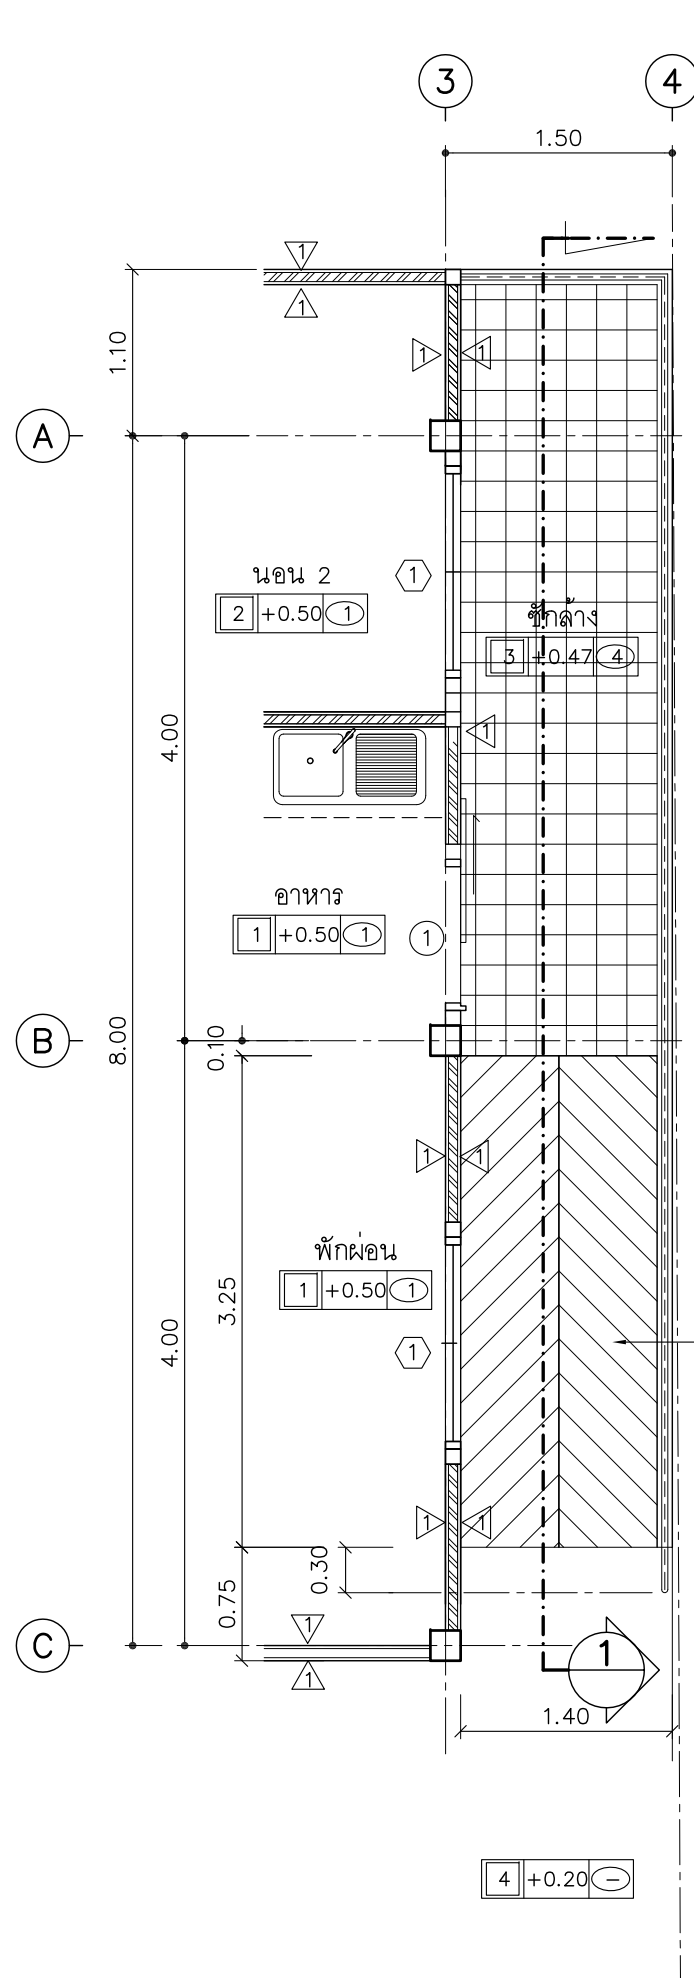

แบบบ้านसानฝัน
ของขวัญปีใหม่
คนไทยมีความสุข

แบบ
บ้านท่งไผ่ไทยประชาสุขใจ 1

สำนักสถาปัตยกรรม

ผู้อำนวยการสำนัก

สถาปัตยกรรม		สถาปนิก
-------------	---	---------

	 สถาปนิก
สำนักวิศวกรรมโครงสร้างและงานระบบ	

ผู้ดำเนินการสำนัก

วิศวกรรวม	— นว วิศวกร
วิศวกร	

โครงการ	วิศวกรรม
วิศวกรรม	วิศวกรรม

	๗	มหาวิทยาลัยราชภัฏวชิรญาณดุสิต
สุขาภิบาล		วิศวกรรม

วิศวกรรม		วิศวกร
หน้า ๗		

ไฟฟ้า	วิศวกรรม
วิศวกรรม	วิศวกรรม

เครื่องกล	Q.	วิศวกร
-----------	----	--------


(Director, Tamil Nadu Sahitya Akademi)

๐๐๑๕๕

[Signature]

(นายมนฑล สุตประเสริฐ)
อธิบดีกรมโยธาธิการและผังเมือง



แบบขยายทางลาดเอียง R.2

มาตราส่วน	—
ฉบับ/เดือน/ปี	19/10/59

เลขที่แบบ	AR 58237
-----------	----------

A-17	21
------	----

A-17	21
------	----

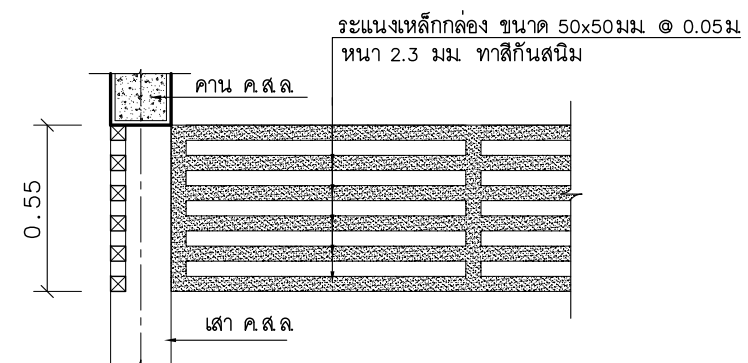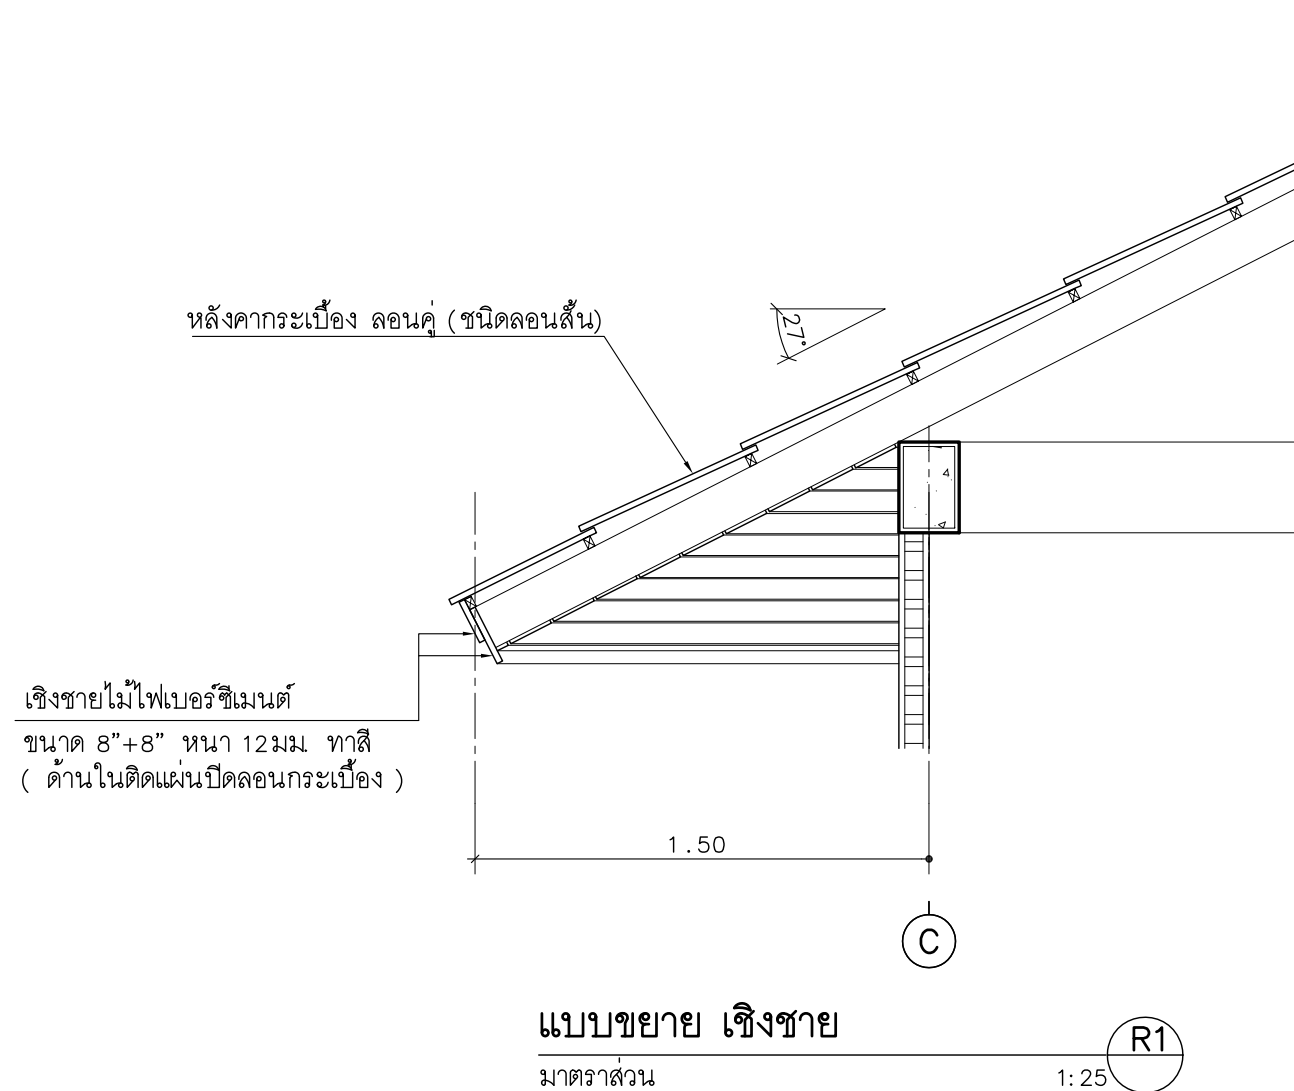

แบบขยาย ระแนงบังแดดเหล็ก

มาตราส่วน 1:25 1



แบบบ้านसानฝัน
ของขวัญปีใหม่
คนไทยมีความสุข

แบบ
บ้านห่วงใยไทยประชาสุใจ 1

สำนักสถาปัตยกรรม
ผู้ช่วยการสำนัก

สถาปัตยกรรม สถาปนิก
สถาปนิก

สำนักวิศวกรรมโครงสร้างและงานระบบ
ผู้ช่วยการสำนัก

วิศวกรรม วิศวกร
โครงสร้าง วิศวกร

วิศวกรรม วิศวกร
สุขาภิบาล วิศวกร

วิศวกรรม วิศวกร
ไฟฟ้า วิศวกร

วิศวกรรม วิศวกร
เครื่องกล วิศวกร

(นายเกียรติศักดิ์ จันทรา)
วิศวกรใหญ่

อนุมัติ
(นายมงคล สุดประเสริฐ)
อธิบดีกรมโยธาธิการและผังเมือง

แสดงแบบ
แบบขยาย เชิงชาย
แบบขยาย ระแนงบังแดด

มาตราส่วน -

วัน/เดือน/ปี 19/10/59

เลขที่แบบ AR 58237

A-18 21



แบบบ้านสานฝัน
ของขวัญปีใหม่
คนไทยมีความสุข

แบบ
บ้านห่วงใยไทยประชาสุใจ 1

สำนักสถาปัตยกรรม
ผู้ช่วยการสำนัก

สถาปัตยกรรม
สถาปนิก

สำนักวิศวกรรมโครงสร้างและงานระบบ
ผู้ช่วยการสำนัก

วิศวกรรม
วิศวกร

โครงสร้าง
วิศวกร

วิศวกรรม
วิศวกร

สุขาภิบาล
วิศวกร

วิศวกรรม
วิศวกร

ไฟฟ้า
วิศวกร

วิศวกรรม
วิศวกร


เครื่องกล
วิศวกร

แสดงแบบ
แบบขยายประตูรั้วบ้าน


มาตราส่วน
วัน/เดือน/ปี 19/10/59

เลขที่แบบ AR 58237


A-19 21

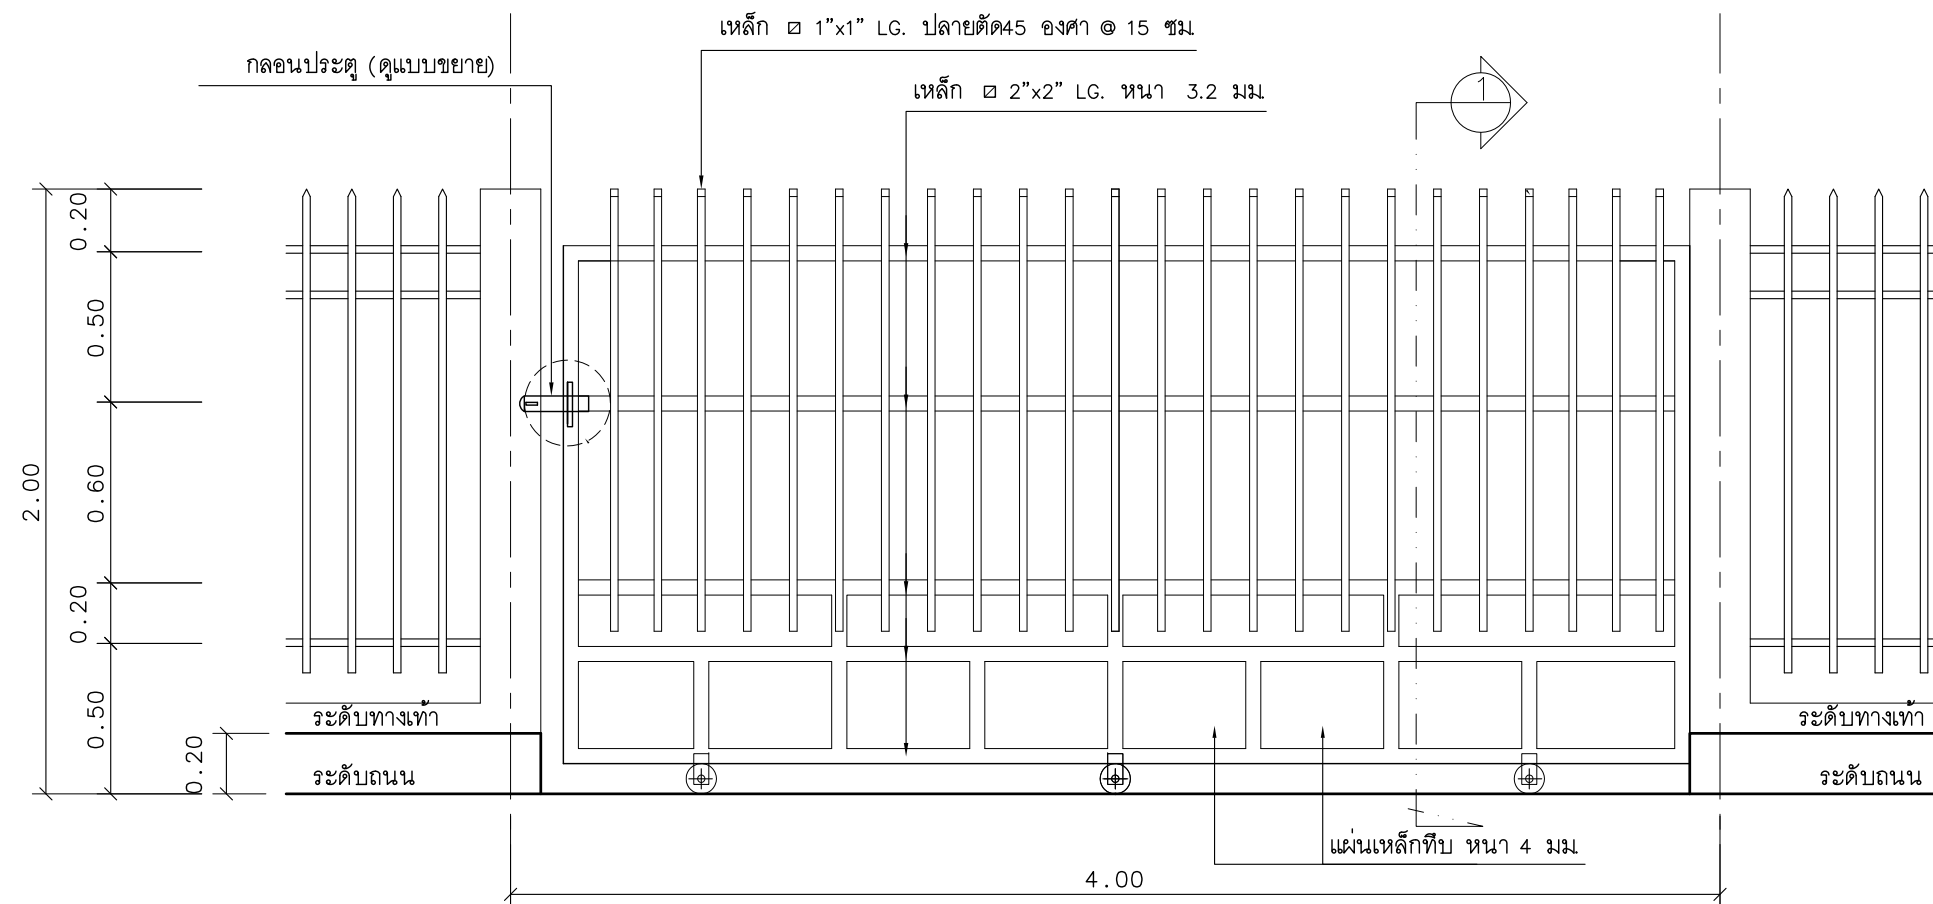

รูปด้านหน้า
มาตราส่วน 1:25

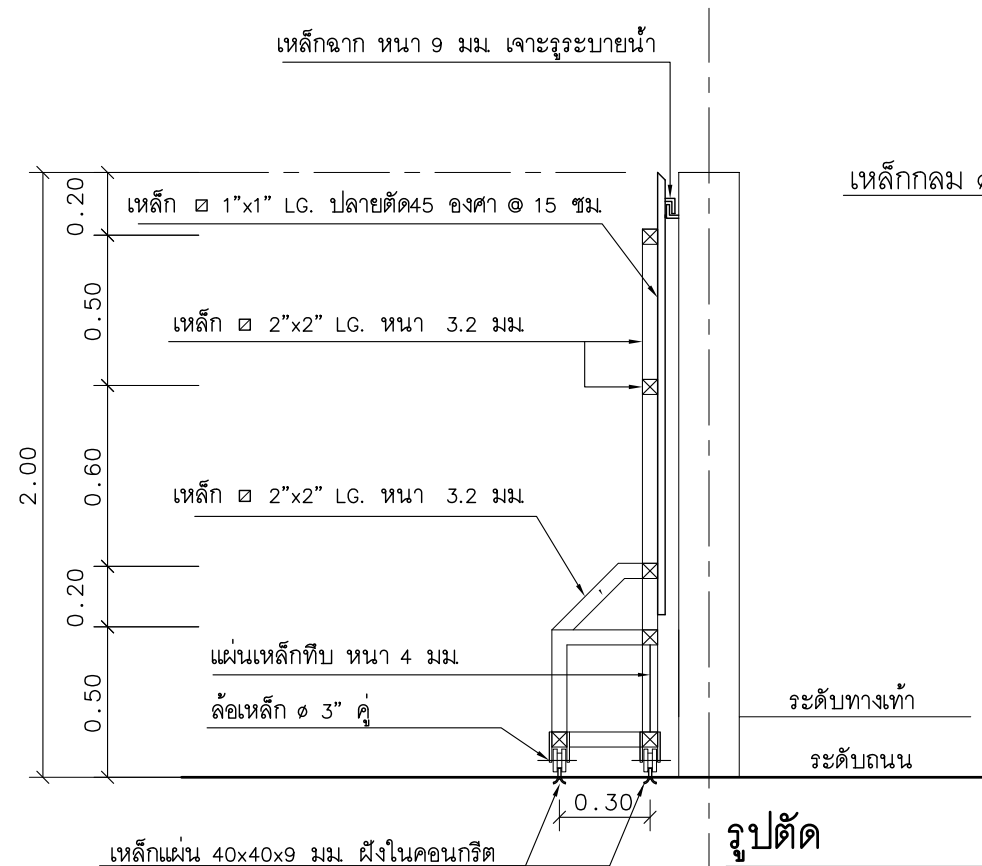


รูปตัด
มาตราส่วน 1:25

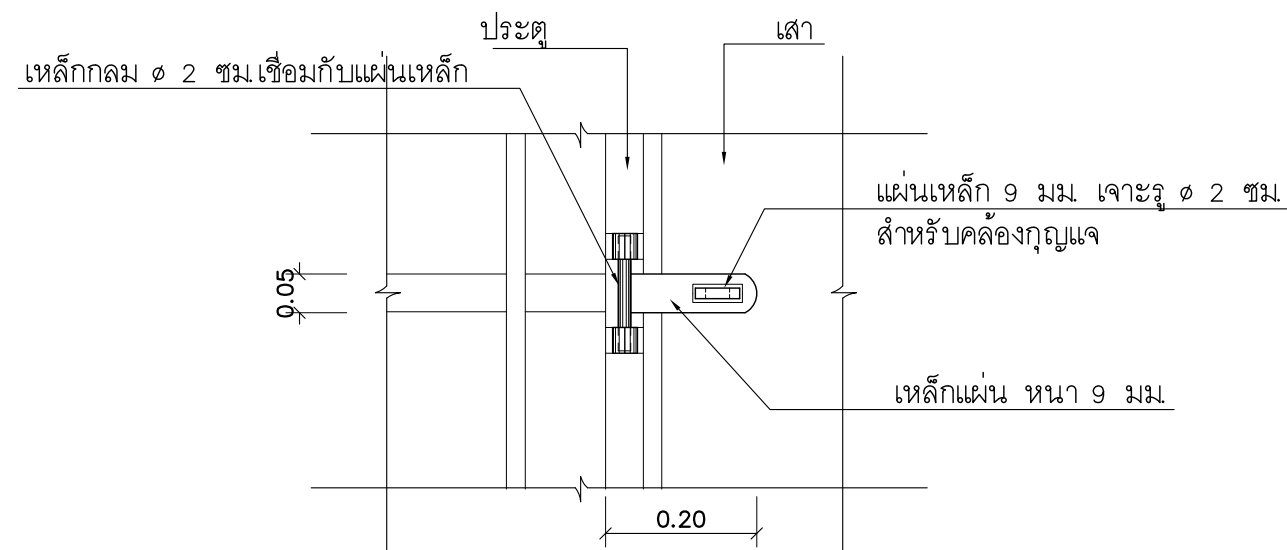


แบบขยายกลอนประตู
มาตราส่วน 1:10

แบบขยายประตูรั้วบ้าน

มาตราส่วน


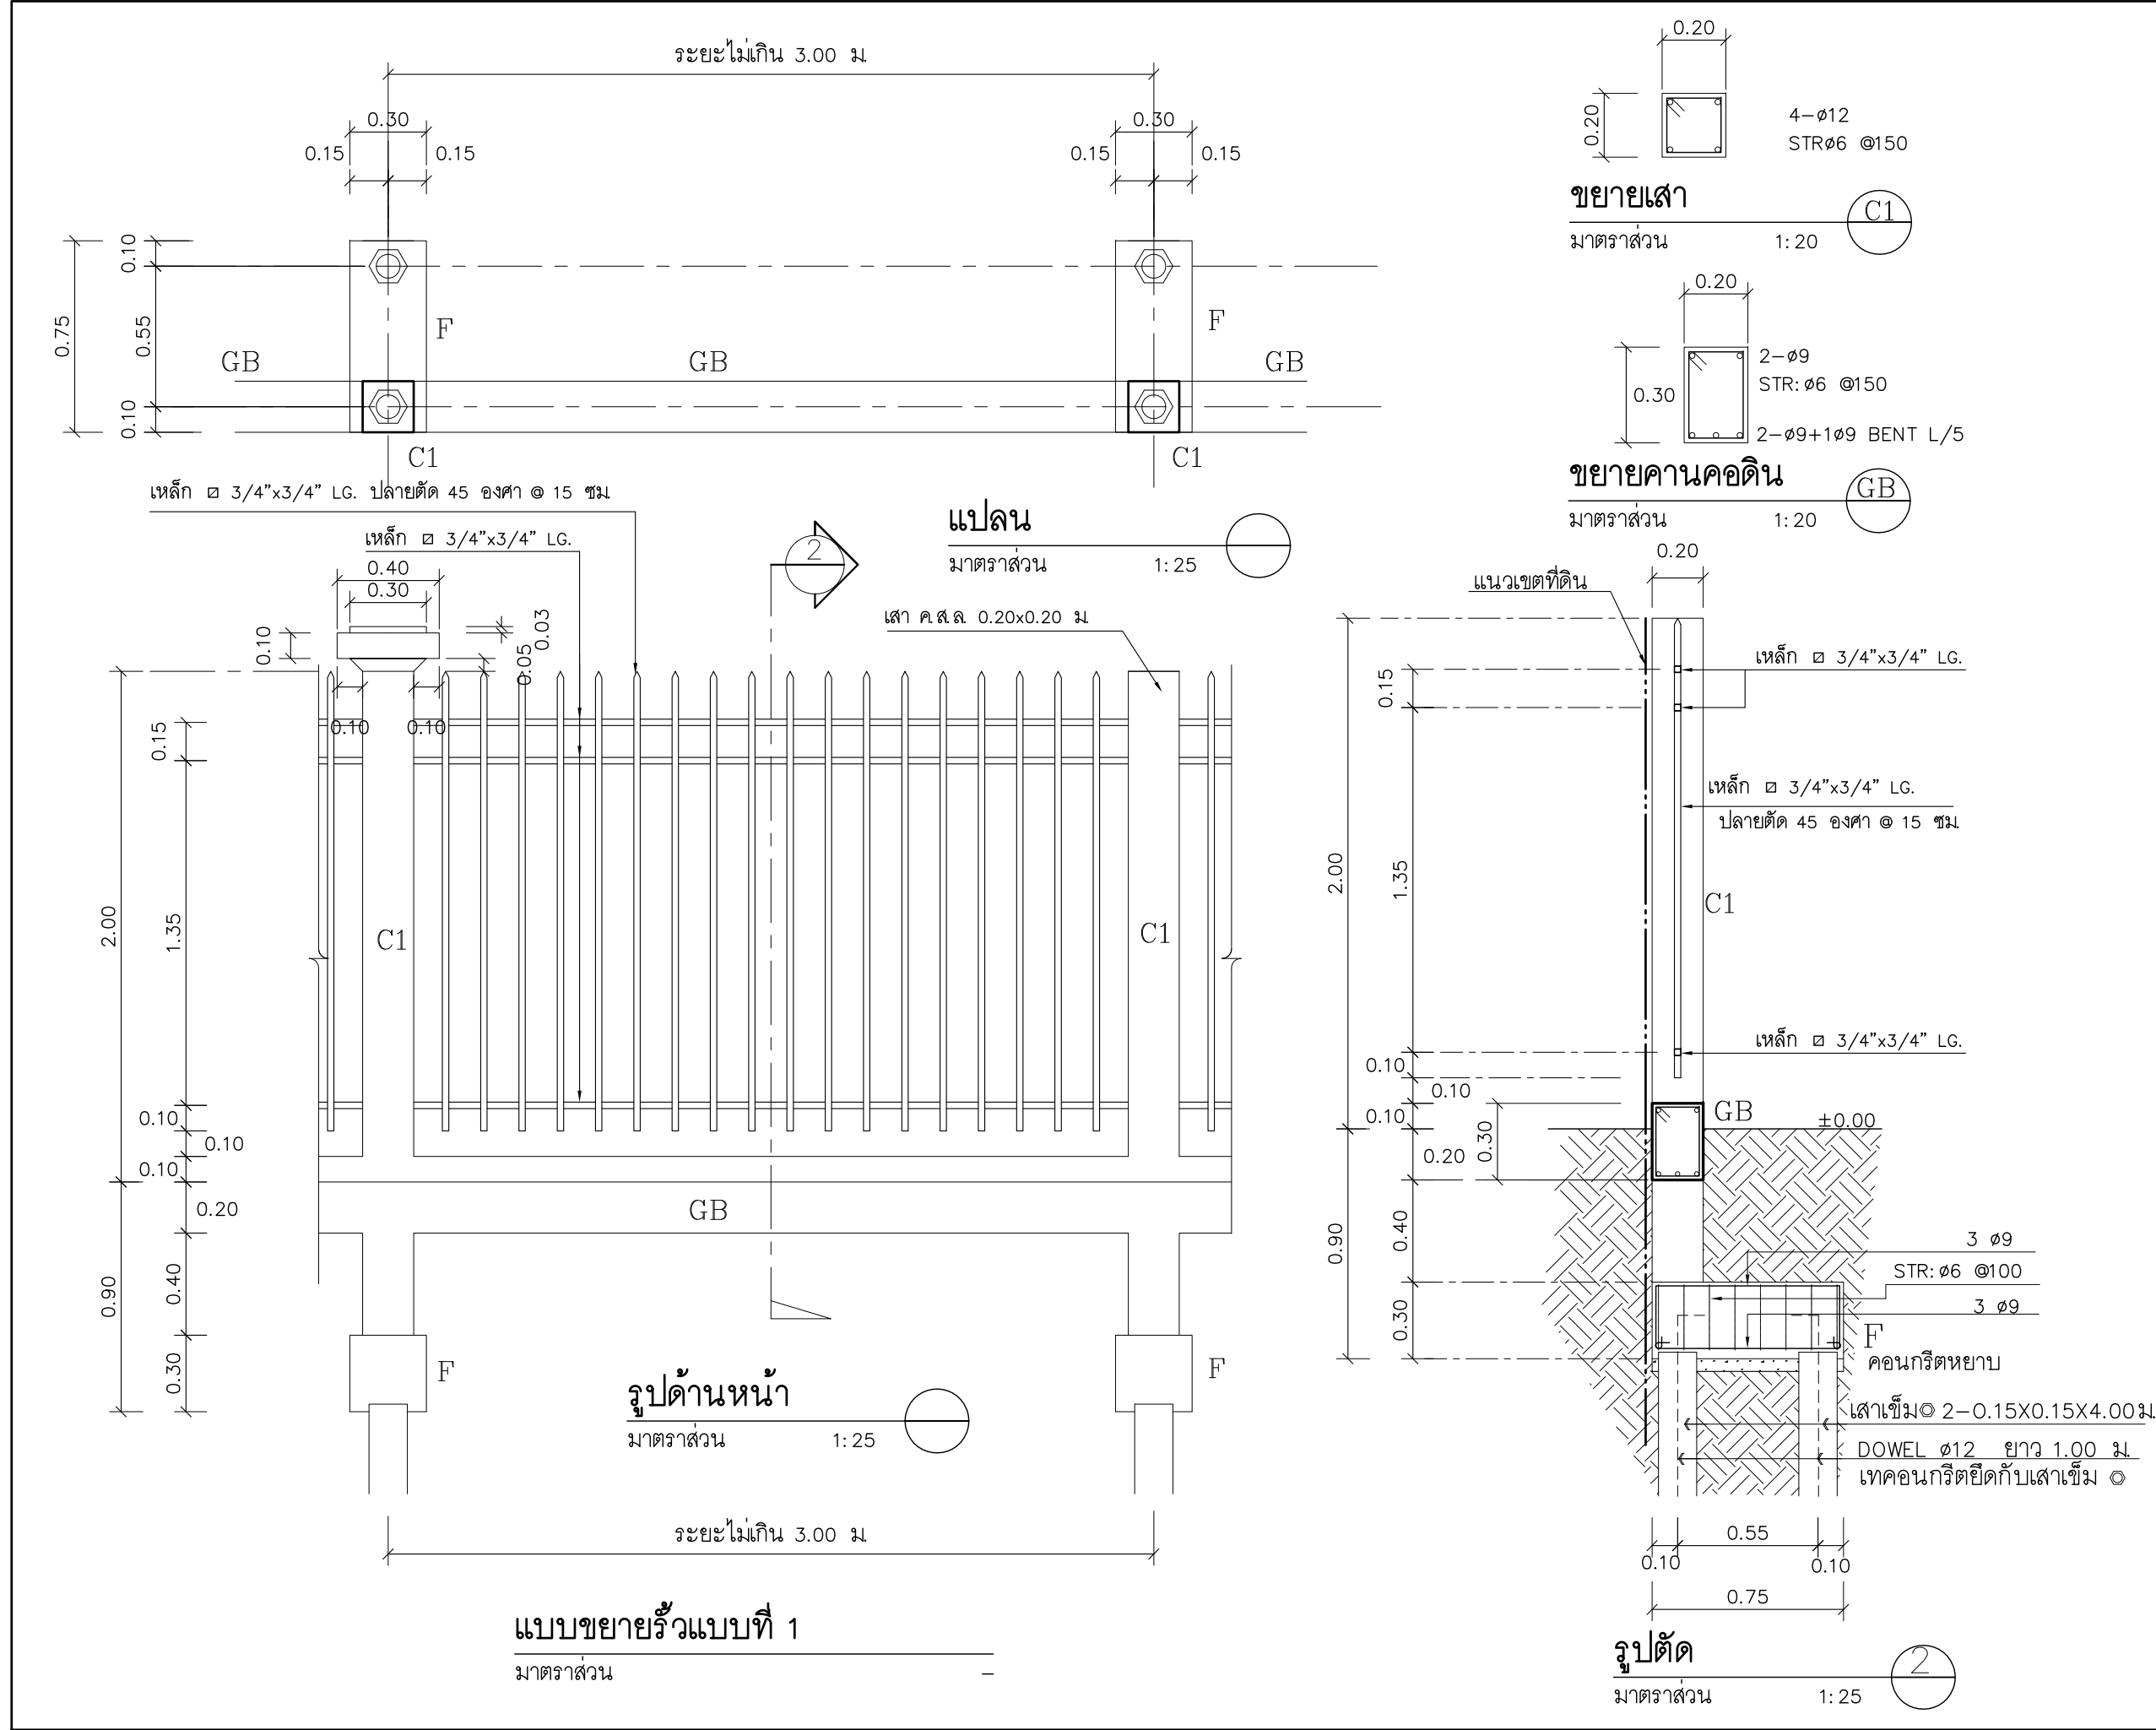


แบบบ้านसानฝัน ของขวัญปีใหม่ คนไทยมีความสุข	
แบบ บ้านห่วงใยไทยประชาสุใจ 1	
สำนักสถาปัตยกรรม ผู้อำนวยการสำนัก	
สถาปัตยกรรม	 สถาปนิก
สถาปัตยกรรม	 สถาปนิก
สำนักวิศวกรรมโครงสร้างและงานระบบ ผู้อำนวยการสำนัก	
วิศวกรรม	 วิศวกร
โครงสร้าง	 วิศวกร
วิศวกรรม	 วิศวกร
สุขาภิบาล	 วิศวกร
วิศวกรรม	 วิศวกร
ไฟฟ้า	 วิศวกร
วิศวกรรม	 วิศวกร
เครื่องกล	 วิศวกร
 (นายเกียรติศักดิ์ จันทรา) วิศวกรใหญ่	
อนุมัติ (นายมงคล สดประเสริฐ) อธิบดีกรมโยธาธิการและผังเมือง	
แสดงแบบ แบบขยาย รื้อแบบที่ 1	
มาตราส่วน -	
วัน/เดือน/ปี 19/10/59	
เลขที่แบบ AR 58237	
A-20	21

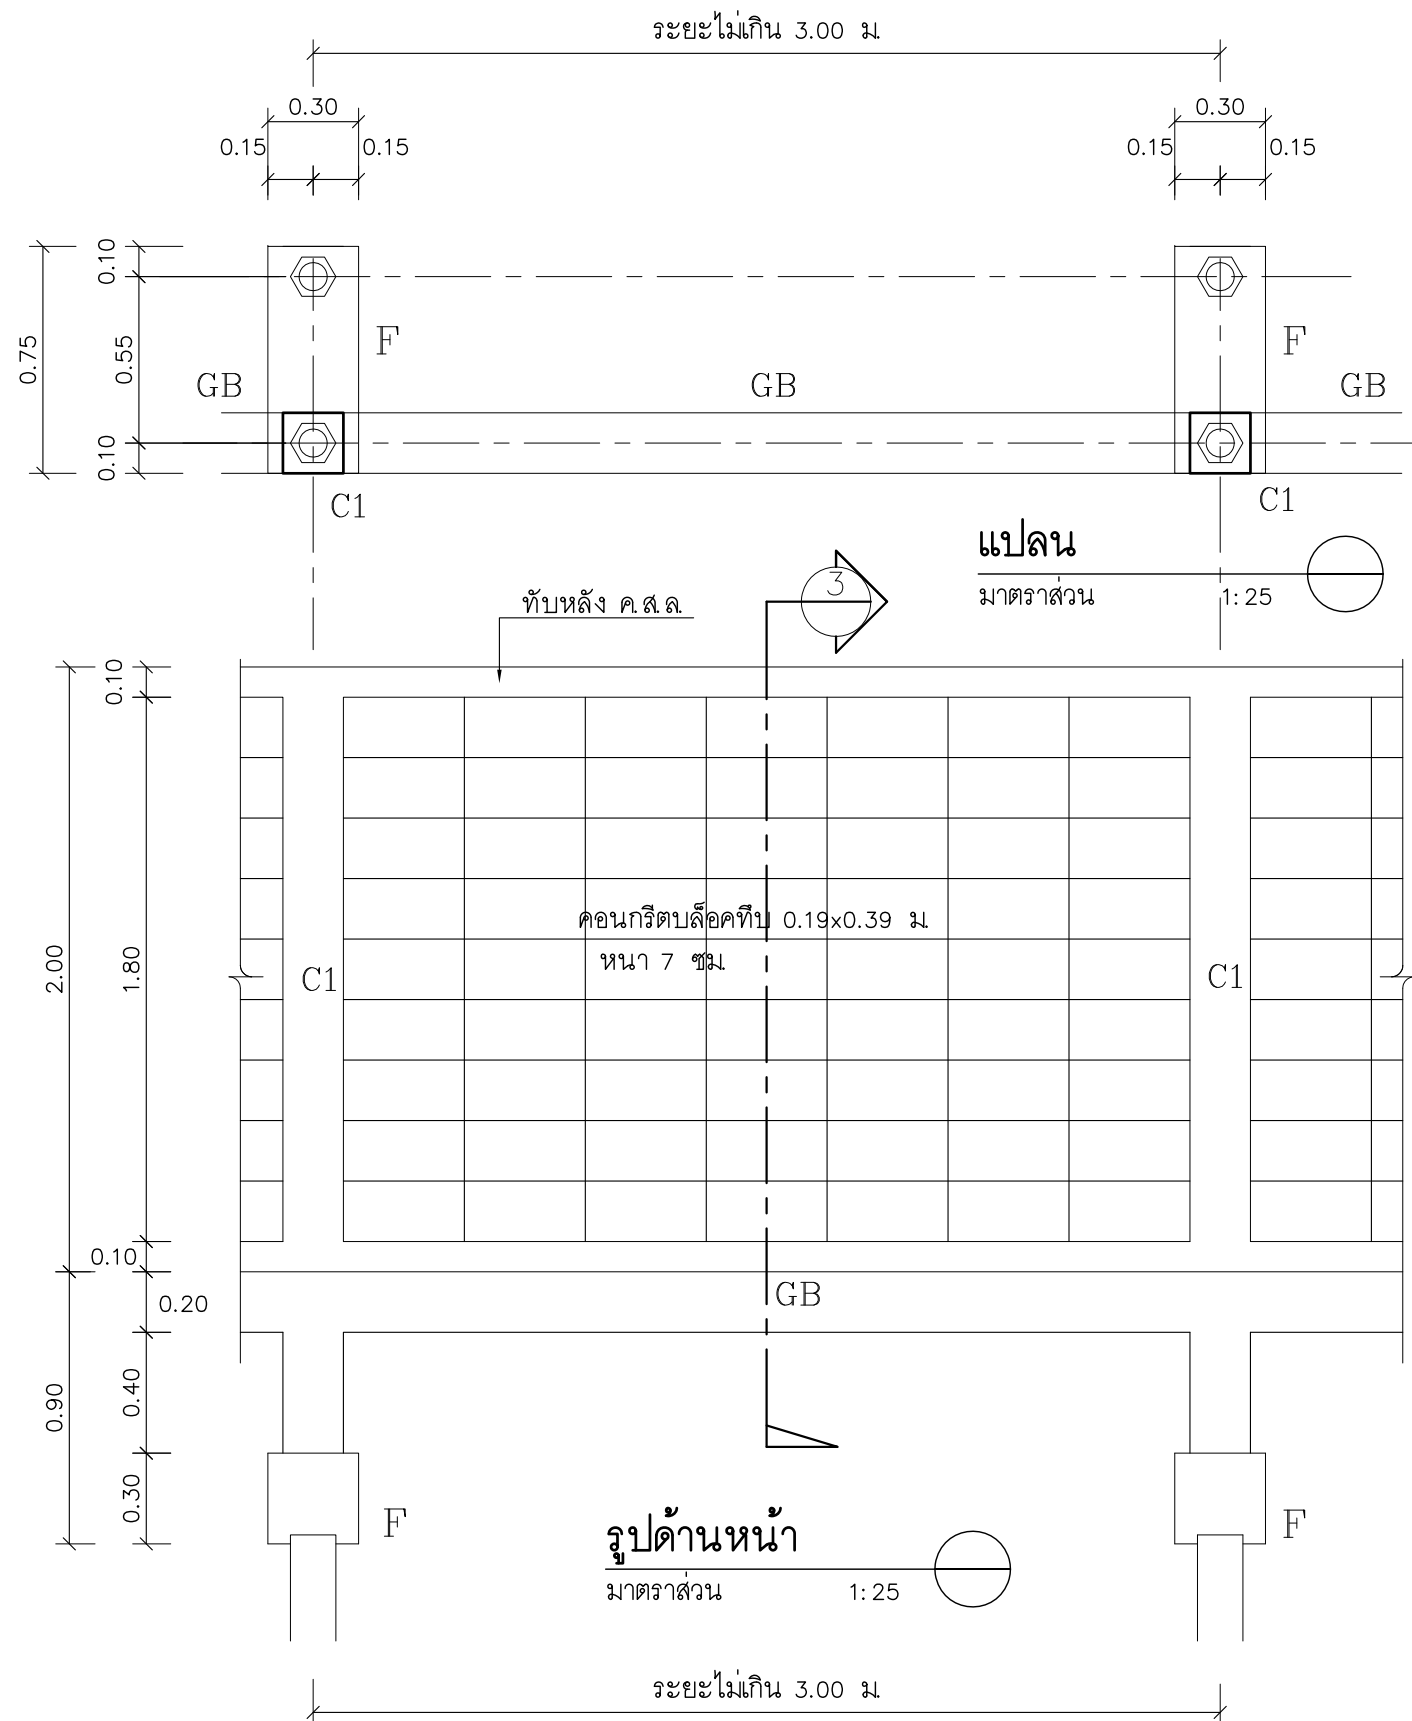



แบบขยายรื้อแบบที่ 2

มาตราส่วน

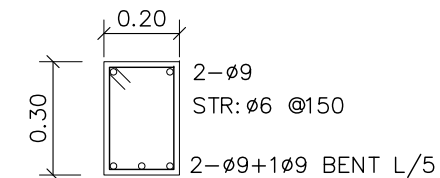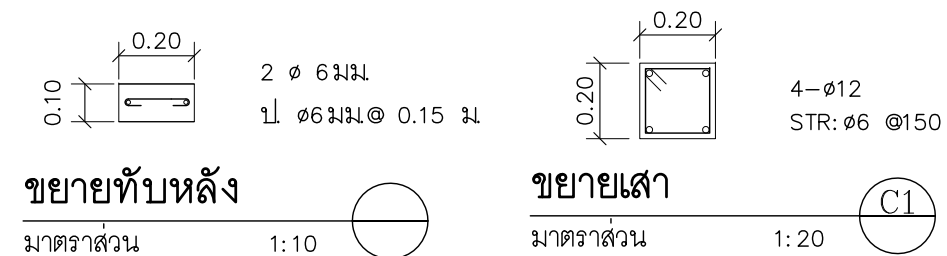

ขยายคานคอดิน

มาตราส่วน

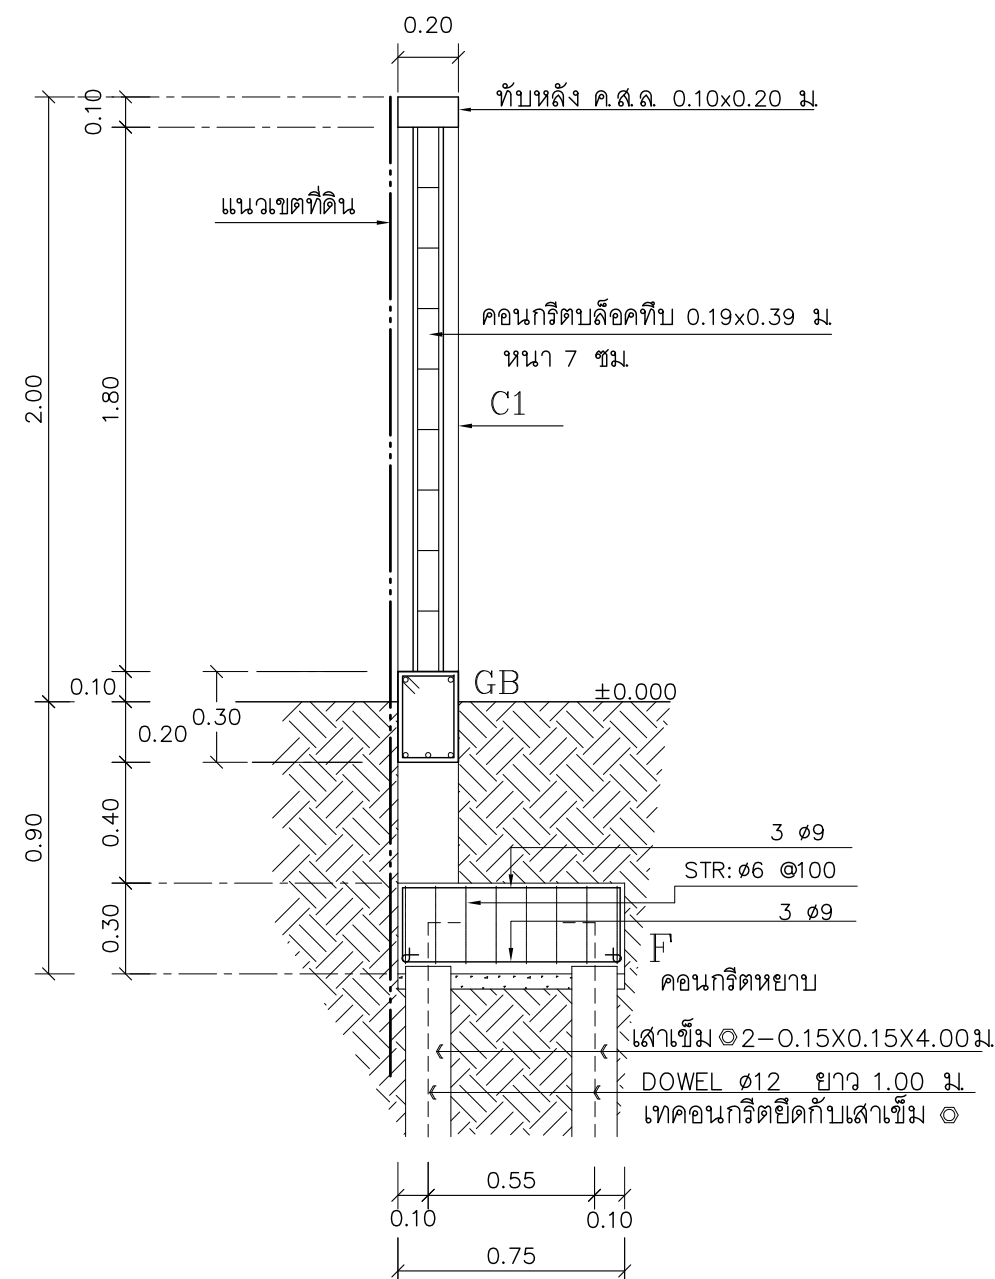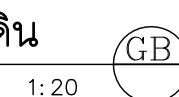

รูปตัด

มาตราส่วน

1:25



แบบบ้านสานฝัน
ของขวัญปีใหม่
คนไทยมีความสุข

แบบ
บ้านห่วงใยไทยประชาสุใจ 1

สำนักสถาปัตยกรรม

ผู้ช่วยการสำนัก

สถาปัตยกรรม

สถาปนิก

สำนักวิศวกรรมโครงสร้างและงานระบบ

ผู้ช่วยการสำนัก

วิศวกรรม

วิศวกร

โครงสร้าง

วิศวกร

วิศวกรรม

วิศวกร

สุขาภิบาล

วิศวกร

วิศวกรรม

วิศวกร

ไฟฟ้า

วิศวกร

วิศวกรรม

วิศวกร

เครื่องกล

วิศวกร

(นายเกียรติศักดิ์ จันทรา)
วิศวกรใหญ่

อนุมัติ
(นายมงคล สดประเสริฐ)
อธิบดีกรมโยธาธิการและผังเมือง

แสดงแบบ

แบบขยาย รื้อแบบที่ 2

มาตราส่วน -

วัน/เดือน/ปี 19/10/59

เลขที่แบบ AR 58237

A-21

21

สำรบัญแบบวิศวกรรมโครงสร้าง

[illegible]

รายการประกอบแบบงานโครงสร้าง

ให้ใช้มาตรฐานกรมโยธาธิการและผังเมือง มยผ. 1101-52 ถึง 1106-52 เป็นรายการประกอบแบบทั่วไปและมีรายการเฉพาะแบบดังนี้

1. คอนกรีต
หากไม่ได้มีการระบุไว้เป็นอย่างอื่นแล้ว ชนิดคอนกรีตให้ใช้ ค.3 โดยมีกำลังอัดประลัยของแท่งคอนกรีตรูปทรงกระบอกมาตรฐานที่อายุ 28 วัน ไม่น้อยกว่า 210 กก./ตร.ซม.
2. เหล็กเส้นเสริมคอนกรีต
 - 2.1 เหล็กเส้นขนาดเส้นผ่านศูนย์กลาง ๑6 มม. และ ๑9 มม. ให้ใช้เหล็กเส้นกลม SR-24 (ความต้านแรงดึงที่จุดครากไม่น้อยกว่า 2,400 กก./ตร.ซม.)
 - 2.2 เหล็กเส้นขนาดเส้นผ่านศูนย์กลางตั้งแต่ ๑2 มม. ขึ้นไปให้ใช้เหล็กเส้นข้ออ้อย SD-40 หรือ SD-40T (ความต้านแรงดึงที่จุดครากไม่น้อยกว่า 4,000 กก./ตร.ซม.)
3. งานฐานราก
 - 3.1 เสาค้ำ ให้ใช้เสาค้ำคอนกรีต ขนาดไม่น้อยกว่าหกเหลี่ยมกลวง ๑-0.15 ม. ความยาวในการประมาณราคา 6.00 ม. รับน้ำหนักปลอดภัยได้ไม่น้อยกว่า 1.7 ตัน/ต้น
 - 3.2 ในกรณีที่ดินฐานรากสามารถรับหน่วยแรงแบกทานที่ยอมให้ได้ไม่น้อยกว่า 6 ตัน/ตร.ม. ให้ยกเลิกเสาค้ำได้ฐานรากทั้งหมด ส่วนในกรณีที่ดินฐานรากสามารถรับหน่วยแรงแบกทานที่ยอมให้ได้ไม่น้อยกว่า 6 ตัน/ตร.ม. ให้ก่อสร้างโดยใช้เสาค้ำตามแบบ ทั้งนี้ความยาวของเสาค้ำอาจเปลี่ยนแปลงตามสภาพของชั้นดิน โดยเสาค้ำจะต้องสามารถรับน้ำหนักปลอดภัยได้ไม่น้อยกว่า 1.7 ตัน/ต้น
 - 3.3 การเลือกใช้ชนิดฐานรากที่มีเสาค้ำหรือไม่มีเสาค้ำ ควรเลือกใช้ชนิดใดชนิดหนึ่งเท่านั้นภายในอาคารเดียวกัน
4. เหล็กโครงสร้างรูปพรรณ
 - 4.1 ต้องมีความต้านแรงดึงที่จุดครากไม่น้อยกว่า 2,400 กก./ตร.ซม.
 - 4.2 เหล็กโครงสร้างรูปพรรณที่นำมาใช้ต้องปราศจากสนิมขุม ไม่บิดงอเสียรูป
 - 4.3 หากไม่ได้มีการระบุในแบบแปลนรายละเอียด การต่อเชื่อมเหล็กโครงสร้างรูปพรรณให้ต่อเชื่อมด้วยไฟฟ้า (ARC WELDING) ตลอดแนวสัมผัส โดยรอบที่ต่อเชื่อม และรอยต่อต้องแข็งแรงไม่น้อยกว่าความแข็งแรงของเหล็กโครงสร้างรูปพรรณที่นำมาต่อกัน
 - 4.4 ให้หาสิ่กัสนิมประเภท LEAD OXIDE อย่างน้อย 2 ชั้น ก่อนทาสีจริง
5. แปเหล็กสำเร็จรูป
 - 5.1 แปสำเร็จรูปต้องมีความหนาตั้งแต่ 0.55 มม. ขึ้นไป
 - 5.2 ต้องผ่านกระบวนการชุบสังกะสีบนผิวเหล็กเป็นแบบจุ่มร้อน (HOT DIP) เคลือบหนาไม่น้อยกว่า 180 กรัม/ตารางเมตร ตามมาตรฐาน มอก. 50
 - 5.3 การติดตั้งให้เป็นไปตามมาตรฐานหรือคำแนะนำของผู้ผลิต
6. ในการก่อสร้างโครงสร้างคอนกรีตเสริมเหล็กที่สัมผัสดินหรือน้ำ พื้นลาดฟ้า พื้นหลังคา และถังเก็บน้ำ ให้ใช้คอนกรีตผสมน้ำยากันซึม ซึ่งอัตราส่วนผสมและกรรมวิธีการใช้งานให้เป็นไปตามมาตรฐานหรือคำแนะนำของผู้ผลิต
7. รายละเอียดหรือคุณสมบัติของวัสดุหรืออุปกรณ์ในแบบหรือในรายการประกอบแบบ ทั้งที่ระบุหรือไม่ได้ระบุไว้ หากมีการกำหนดมาตรฐานผลิตภัณฑ์อุตสาหกรรมแล้วให้เป็นไปตามมาตรฐานผลิตภัณฑ์อุตสาหกรรมนั้น



แบบบ้านसानฝัน
ของขวัญปีใหม่
คนไทยมีความสุข

แบบ
บ้านท่งไผ่ไทยประจักษ์ใจ 1

สำนักสถาปัตยกรรม

ผู้อำนวยความสะดวก

สถาปัตยกรรม		สถาปนิก
		สถาปนิก

สำนักวิศวกรรมโครงสร้างและงานระบบ



ผู้อำนวยการสำนัก

วิศวกรรม		วิศวกร

โครงสร้าง	วิศวกร
วิศวกร	วิศวกร

วัดวกรรรม	๘๘/๑	วัดวกร
สุขาภิบาล		วัดวกร

วิศวกร		
วิศวกร		วิศวกร

ไฟฟ้า	15.5	วิศวกร
	11.1	

วิศวกรรม	<i>Ph h</i>	วิศวกร
เครื่องกล	<i>Pi</i>	

วันที่รับแจ้ง	เลขที่	วัดการ
		

(นายเกียรติศักดิ์ จันทรา)
อธิบดีกรมการปกครอง

อนุมัติ

(นายมนทล สุดประเสริฐ)

อธิบดีกรมโยธาธิการและผังเมือง
แสดงแบบ

สารบัญแบบ


នាយករដ្ឋមន្ត្រី

มาตราสวน	—
วัน/เดือน/ปี	19/10/59

เลขที่แบบ	S59041
-----------	--------

5	01	10
---	----	----

S-01	10
------	----

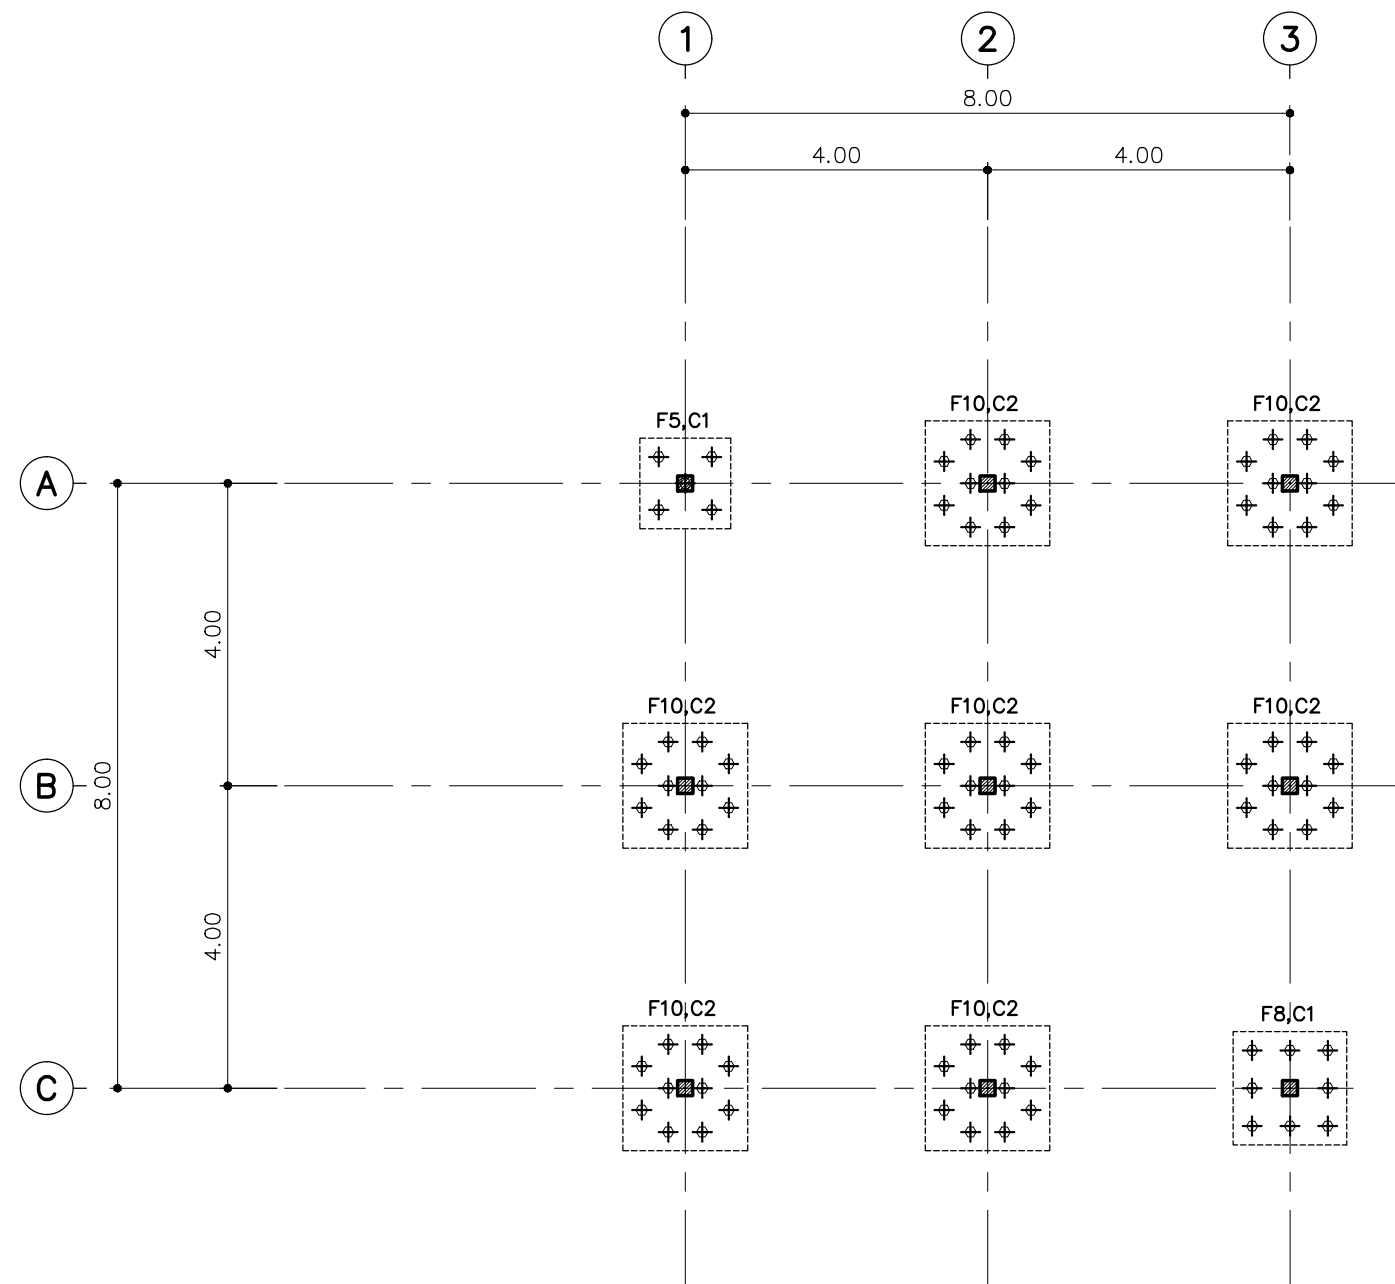

แปลนฐานราก เสาตอม่อ
มาตราส่วน 1:100



แบบบ้านसानฝัน
ของขวัญปีใหม่
คนไทยมีความสุข

แบบ
บ้านห่วงใยไทยประชาสุขใจ 1

สำนักสถาปัตยกรรม
ผู้ชำนาญการสำนัก

สถาปัตยกรรม
สถาปนิก

สำนักวิศวกรรมโครงสร้างและงานระบบ
ผู้ชำนาญการสำนัก

วิศวกรรม
วิศวกร

โครงสร้าง
วิศวกร

วิศวกรรม
วิศวกร

สุขาภิบาล
วิศวกร

วิศวกรรม
วิศวกร

ไฟฟ้า
วิศวกร

วิศวกรรม
วิศวกร

เครื่องกล
วิศวกร


(นายเกียรติศักดิ์ จันทรา)
วิศวกรใหญ่

อนุมัติ
(นายมงคล สุตประเสริฐ)
อธิบดีกรมโยธาธิการและผังเมือง

แสดงแบบ
แปลนฐานราก เสาตอม่อ

มาตราส่วน 1:100
วัน/เดือน/ปี 19/10/59
เลขที่แบบ S59041

S-02 10

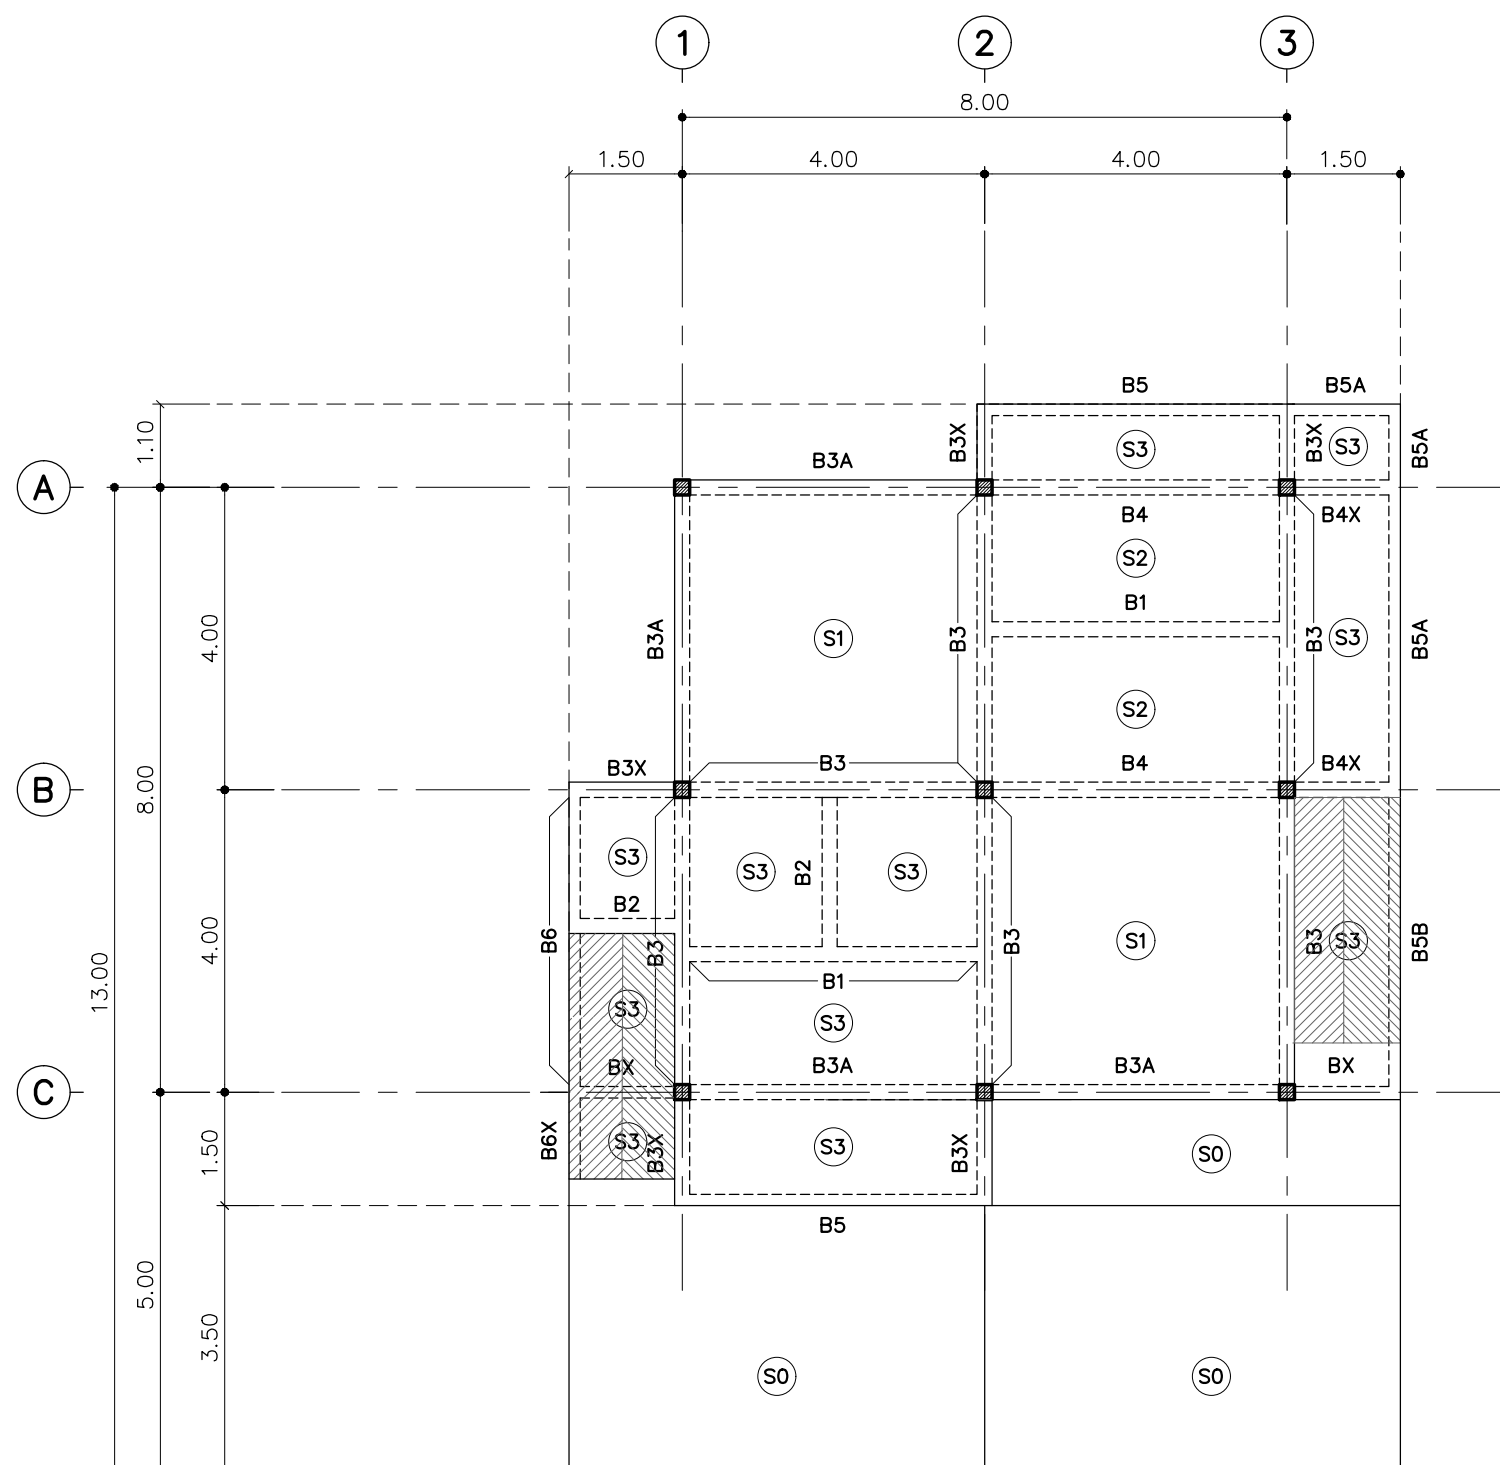

แปลนเสา คาน และพื้น

มาตราส่วน

1:100



แบบบ้านसानฝัน
ของขวัญปีใหม่
คนไทยมีความสุข

แบบ
บ้านห่วงใยไทยประชาสุขใจ 1

สำนักสถาปัตยกรรม
ผู้ชำนาญการสำนัก

สถาปัตยกรรม
สถาปนิก
สถาปนิก

สำนักวิศวกรรมโครงสร้างและงานระบบ
ผู้ชำนาญการสำนัก

วิศวกรรม
วิศวกร
โครงสร้าง
วิศวกร

วิศวกรรม
วิศวกร
สุขาภิบาล
วิศวกร

วิศวกรรม
วิศวกร
ไฟฟ้า
วิศวกร

วิศวกรรม
วิศวกร
เครื่องกล
วิศวกร

(นายเกียรติศักดิ์ จันทรา)
วิศวกรใหญ่

อนุมัติ
(นายมนอชาล สุดประเสริฐ)
อธิบดีกรมโยธาธิการและผังเมือง


แสดงแบบ
แปลนเสา คาน และพื้น

มาตราส่วน 1:100

วัน/เดือน/ปี 19/10/59

เลขที่แบบ S59041

S-03 10

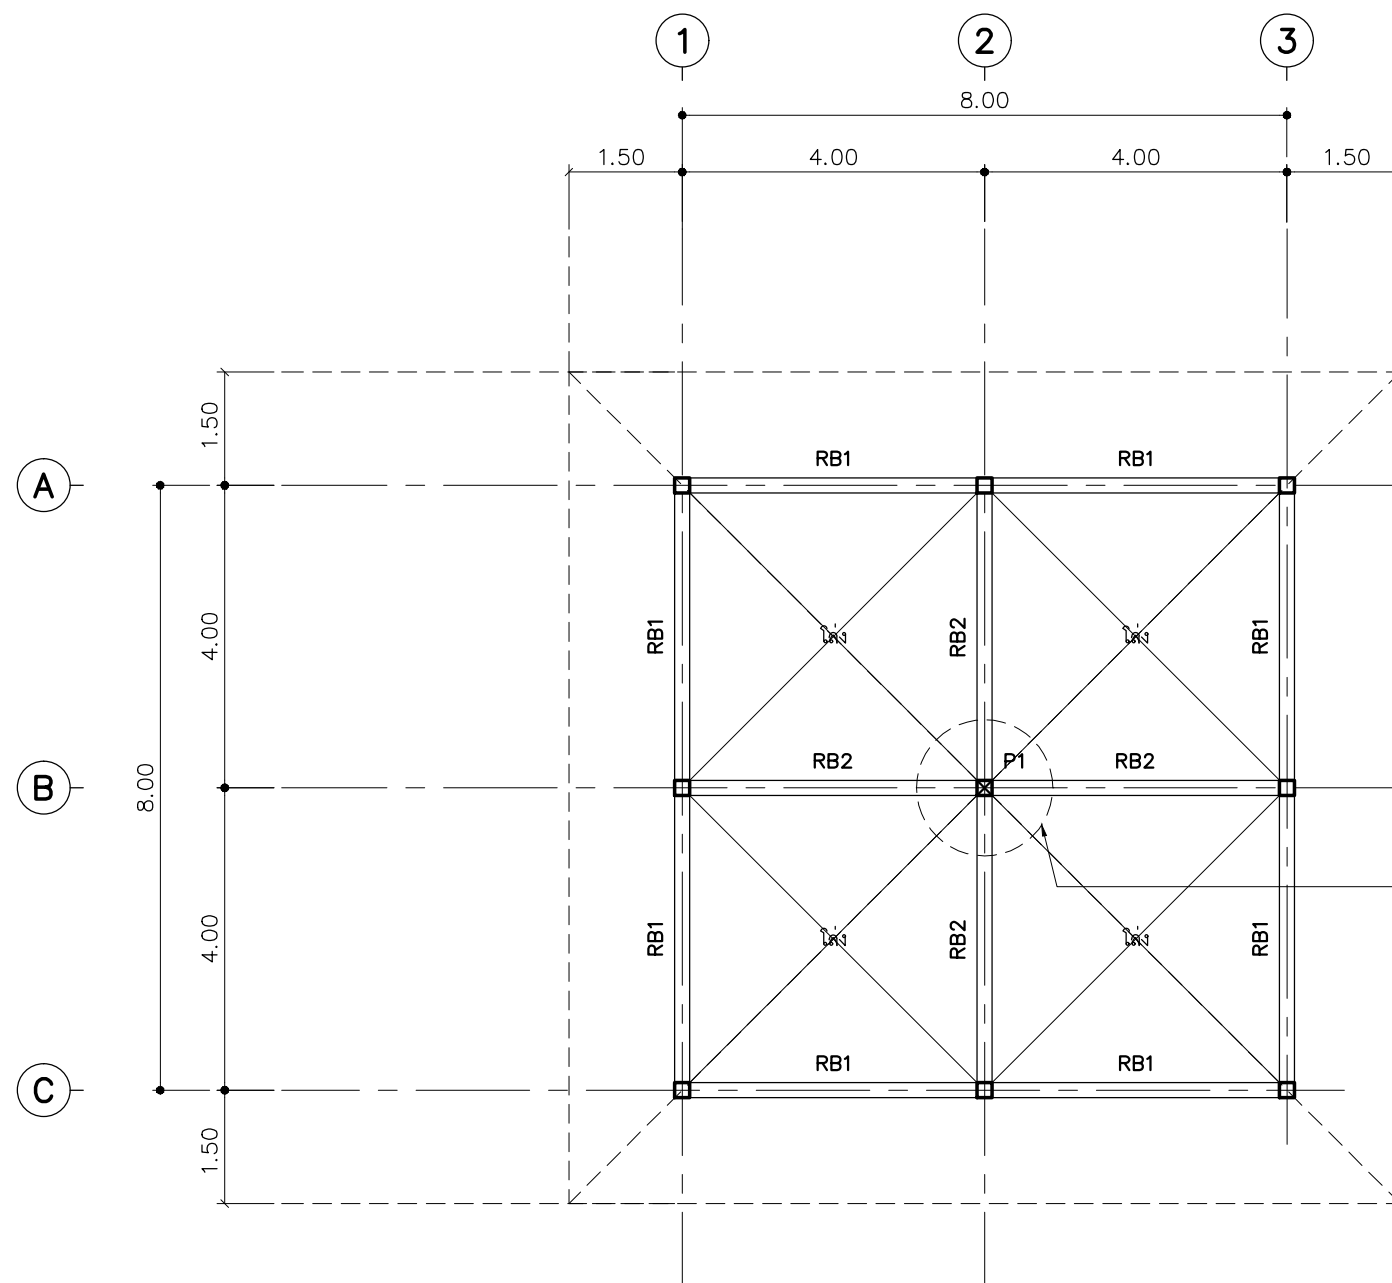

แปลนเสา คานอะเส
มาตราส่วน 1:100

ดูแบบขยายฐานรับเสาดั้งหลัก (P1) รับโครงหลังคา



แบบบ้านสถานพื้น
ของขวัญปีใหม่
คนไทยมีความสุข

แบบ
บ้านห่วงใยไทยประชาสุขใจ 1

สำนักสถาปัตยกรรม
ผู้ชำนาญการสำนัก

สถาปัตยกรรม
สถาปนิก

สำนักวิศวกรรมโครงสร้างและงานระบบ
ผู้ชำนาญการสำนัก

วิศวกรรม
วิศวกร

โครงสร้าง
วิศวกร

วิศวกรรม
วิศวกร

สุขาภิบาล
วิศวกร

วิศวกรรม
วิศวกร

ไฟฟ้า
วิศวกร

วิศวกรรม
วิศวกร

เครื่องกล
วิศวกร


(นายเกียรติศักดิ์ จันทรา)
วิศวกรใหญ่

อนุมัติ
(นายมงคล สุตประเสริฐ)
อธิบดีกรมโยธาธิการและผังเมือง

แสดงแบบ
แปลนเสา คานอะเส

มาตราส่วน 1:100
วัน/เดือน/ปี 19/10/59
เลขที่แบบ S59041

S-04 10

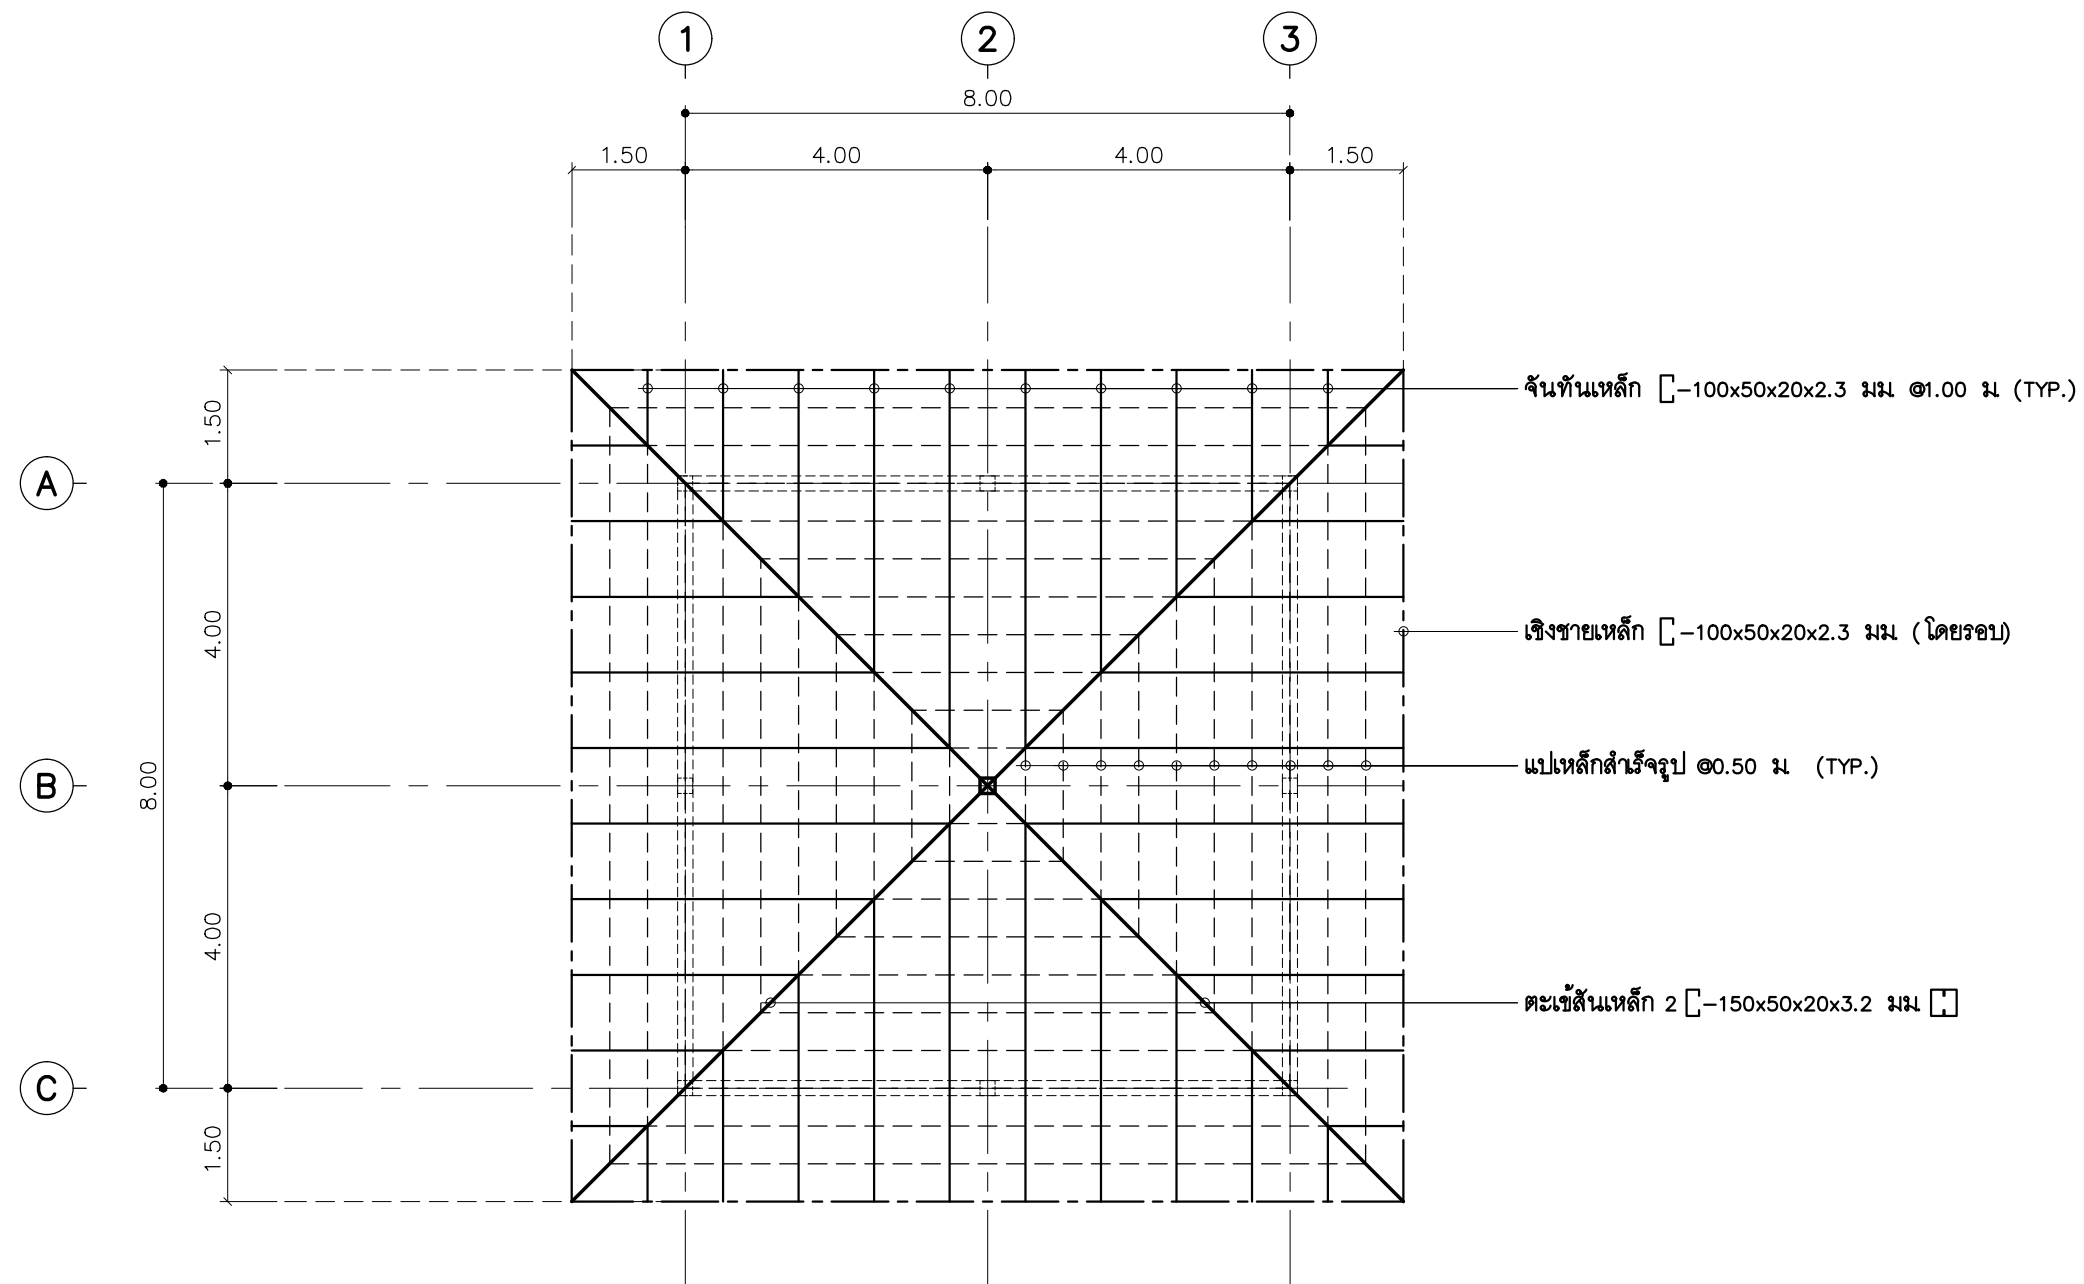

หมายเหตุ

P1 = ดั้งเหล็ก 2 $\square -150 \times 50 \times 20 \times 3.2$ มม

แปลนโครงหลังคา

มาตราส่วน

1:100



แบบบ้านसानฝัน
ของขวัญปีใหม่
คนไทยมีความสุข

แบบ
บ้านห่วงใยไทยประชาสุขใจ 1

สำนักสถาปัตยกรรม

ผู้ช่วยการสำนัก

สถาปนิก

สถาปนิก

สำนักวิศวกรรมโครงสร้างและงานระบบ

ผู้ช่วยการสำนัก

วิศวกร

วิศวกร

วิศวกร

วิศวกร

วิศวกร

วิศวกร

วิศวกรใหญ่

อนุมัติ

(นายมงคล สดประเสริฐ)

อธิบดีกรมโยธาธิการและผังเมือง

แสดงแบบ


แปลนโครงหลังคา

มาตราส่วน 1:100

วัน/เดือน/ปี 19/10/59

เลขที่แบบ S59041

S-05 10

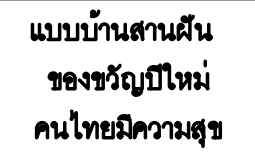

สำนักสถาปัตยกรรม



ผู้อำนวยการสำนัก

สำนักวิศวกรรมโครงสร้างและงานระบบ

๒๕๓

ผู้อำนวยการสำนัก

วิศวกรรม		วิศวกร
โครงสร้าง		วิศวกร
วิศวกรรม		วิศวกร
สุขาภิบาล		วิศวกร
วิศวกรรม		วิศวกร
ไฟฟ้า		วิศวกร
วิศวกรรม		วิศวกร
เครื่องกล		วิศวกร

(นายเกียรติศักดิ์ จันทรา)
วิศวกรใหญ่

อนุนันตี



(นายสมณฑล สุตประเสริฐ)

อธิบดีกรมโยธาธิการและผังเมือง



แสดงแบบ	F5, F8
---------	--------


มาตราส่วน	1:25
-----------	------

วัน/เดือน/ปี 19/10/59

เลขที่แบบ S59041

S-06	10
------	----

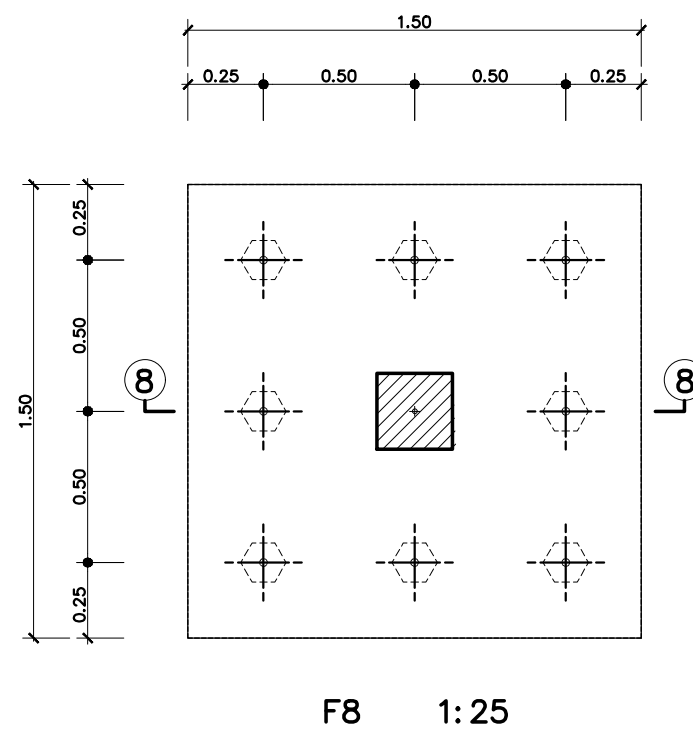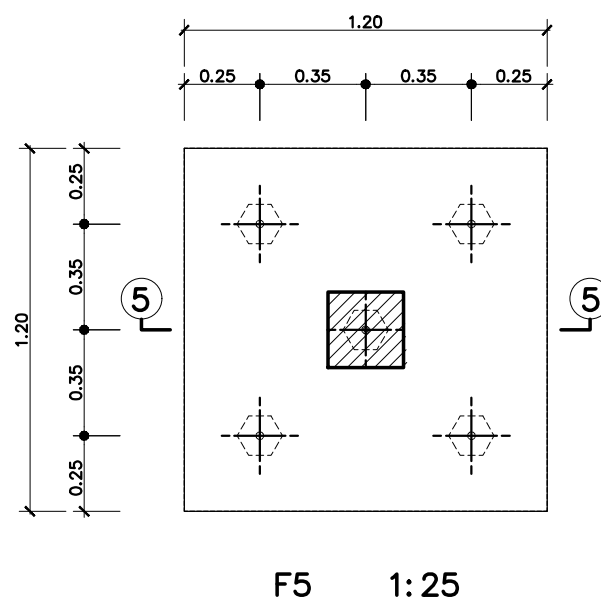

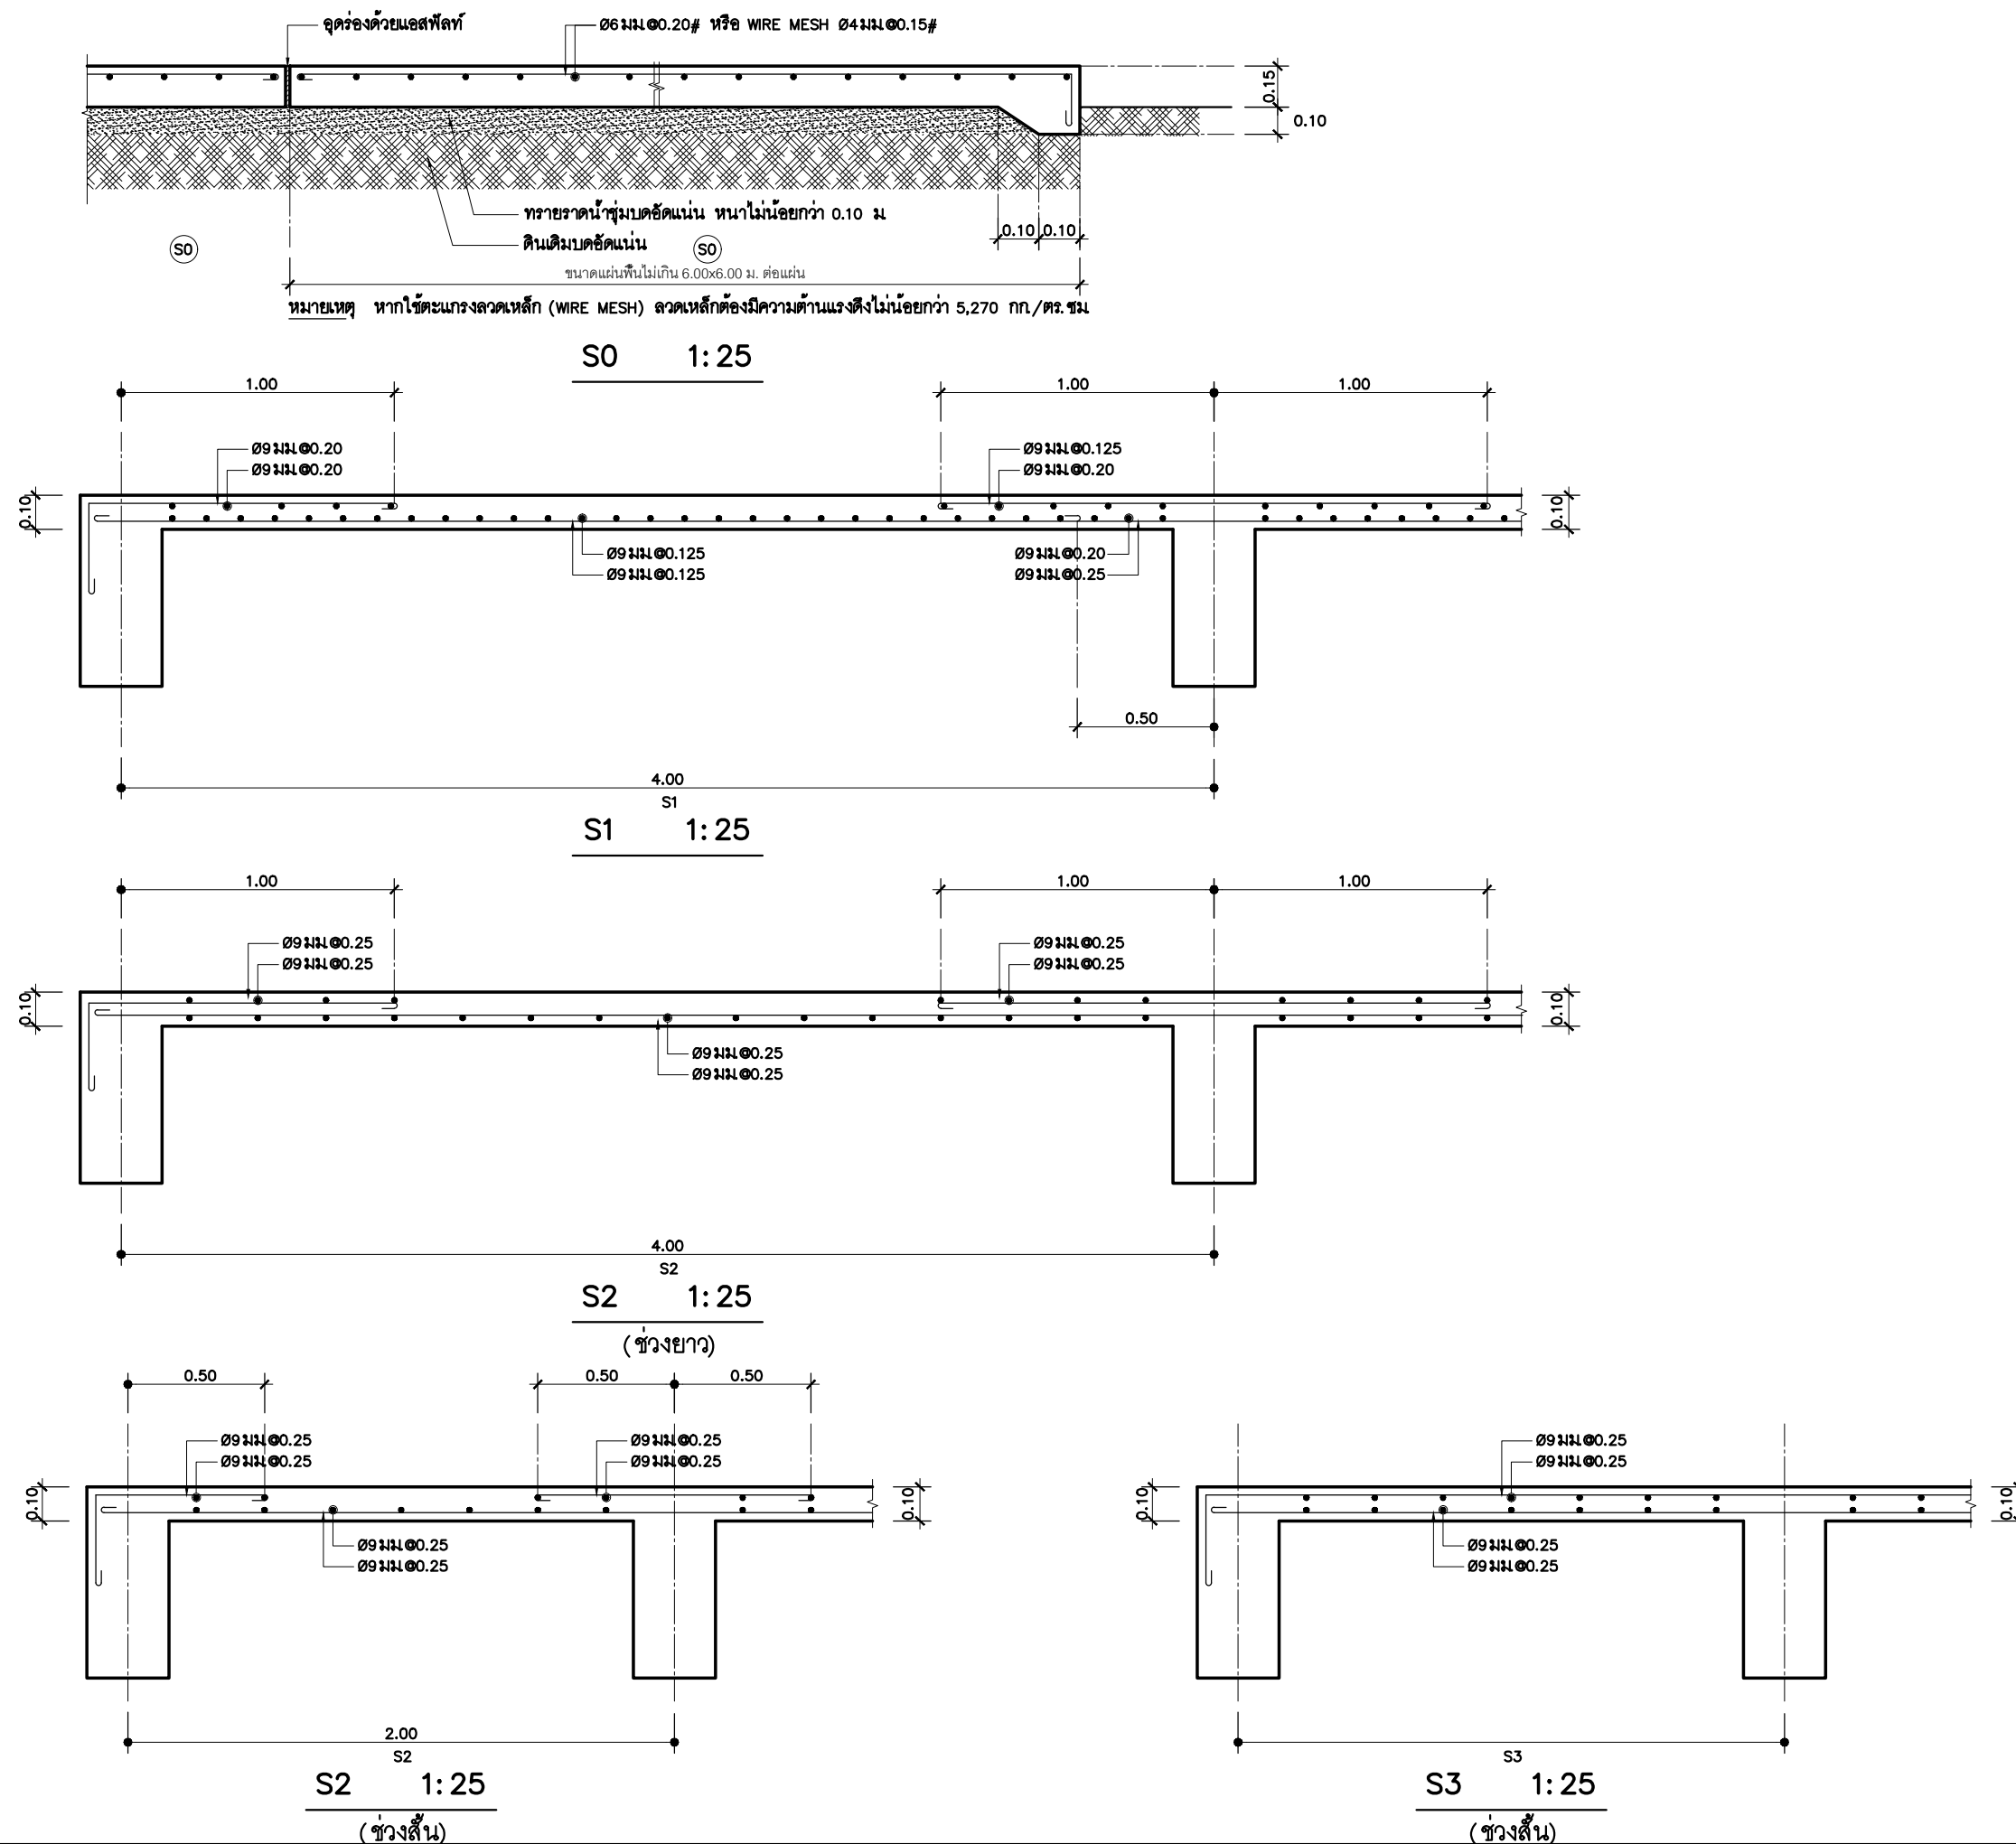

**แบบบ้านสานฝัน
ของขวัญปีใหม่
คนไทยมีความสุข**

แบบ
บ้านห่วงใยไทยประชาสุขใจ 1

สำนักสถาปัตยกรรม



ผู้อำนวยการสำนัก

สถาปัตยกรรม		สถาปนิก
		สถาปนิก

สำนักวิศวกรรมโครงสร้างและงานระบบ



ผู้อำนวยการสำนัก

วิศวกรรม	 วิศวกร
โครงสร้าง	วิศวกร

วิศวกรรม		วิศวกร
สุขาภิบาล		วิศวกร

วิศวกรรม		วิศวกร
ไฟฟ้า		วิศวกร

วิศวกรรวม		วิศวกร
เครื่องกล		วิศวกร

(นายเกียรติศักดิ์ จันทรา)
วิศวกรใหญ่

อนันต์

(นายมนฑล ฤทธิธรรม)

อธิบดีกรมโยธาธิการและผังเมือง

แสดงแบบ

$S_0, S_1 - S_3$

มาตราส่วน	1: 25
-----------	-------

วัน/เดือน/ปี 19/10/59

เลขที่แบบ S59041

S-08	10
------	----



แบบบ้านสานฝัน
ของขวัญปีใหม่
คนไทยมีความสุข

แบบ
บ้านห่วงใยไทยประชาสุขใจ 1

สำนักสถาปัตยกรรม
ผู้ชำนาญการสำนัก

สถาปนิก
สถาปนิก

สำนักวิศวกรรมโครงสร้างและงานระบบ
ผู้ชำนาญการสำนัก

วิศวกรรม	วิศวกร
โครงสร้าง	วิศวกร
วิศวกรรม	วิศวกร
สุขาภิบาล	วิศวกร
วิศวกรรม	วิศวกร
ไฟฟ้า	วิศวกร
วิศวกรรม	วิศวกร
เครื่องกล	วิศวกร

(นายเกียรติศักดิ์ จันทรา)
วิศวกรใหญ่

อนุมัติ
(นายมงคล สุตประเสริฐ)
อธิบดีกรมโยธาธิการและผังเมือง


แสดงแบบ
B1 - B5A



มาตราส่วน 1: 25

วัน/เดือน/ปี 19/10/59




เลขที่แบบ S59041

S-09 10




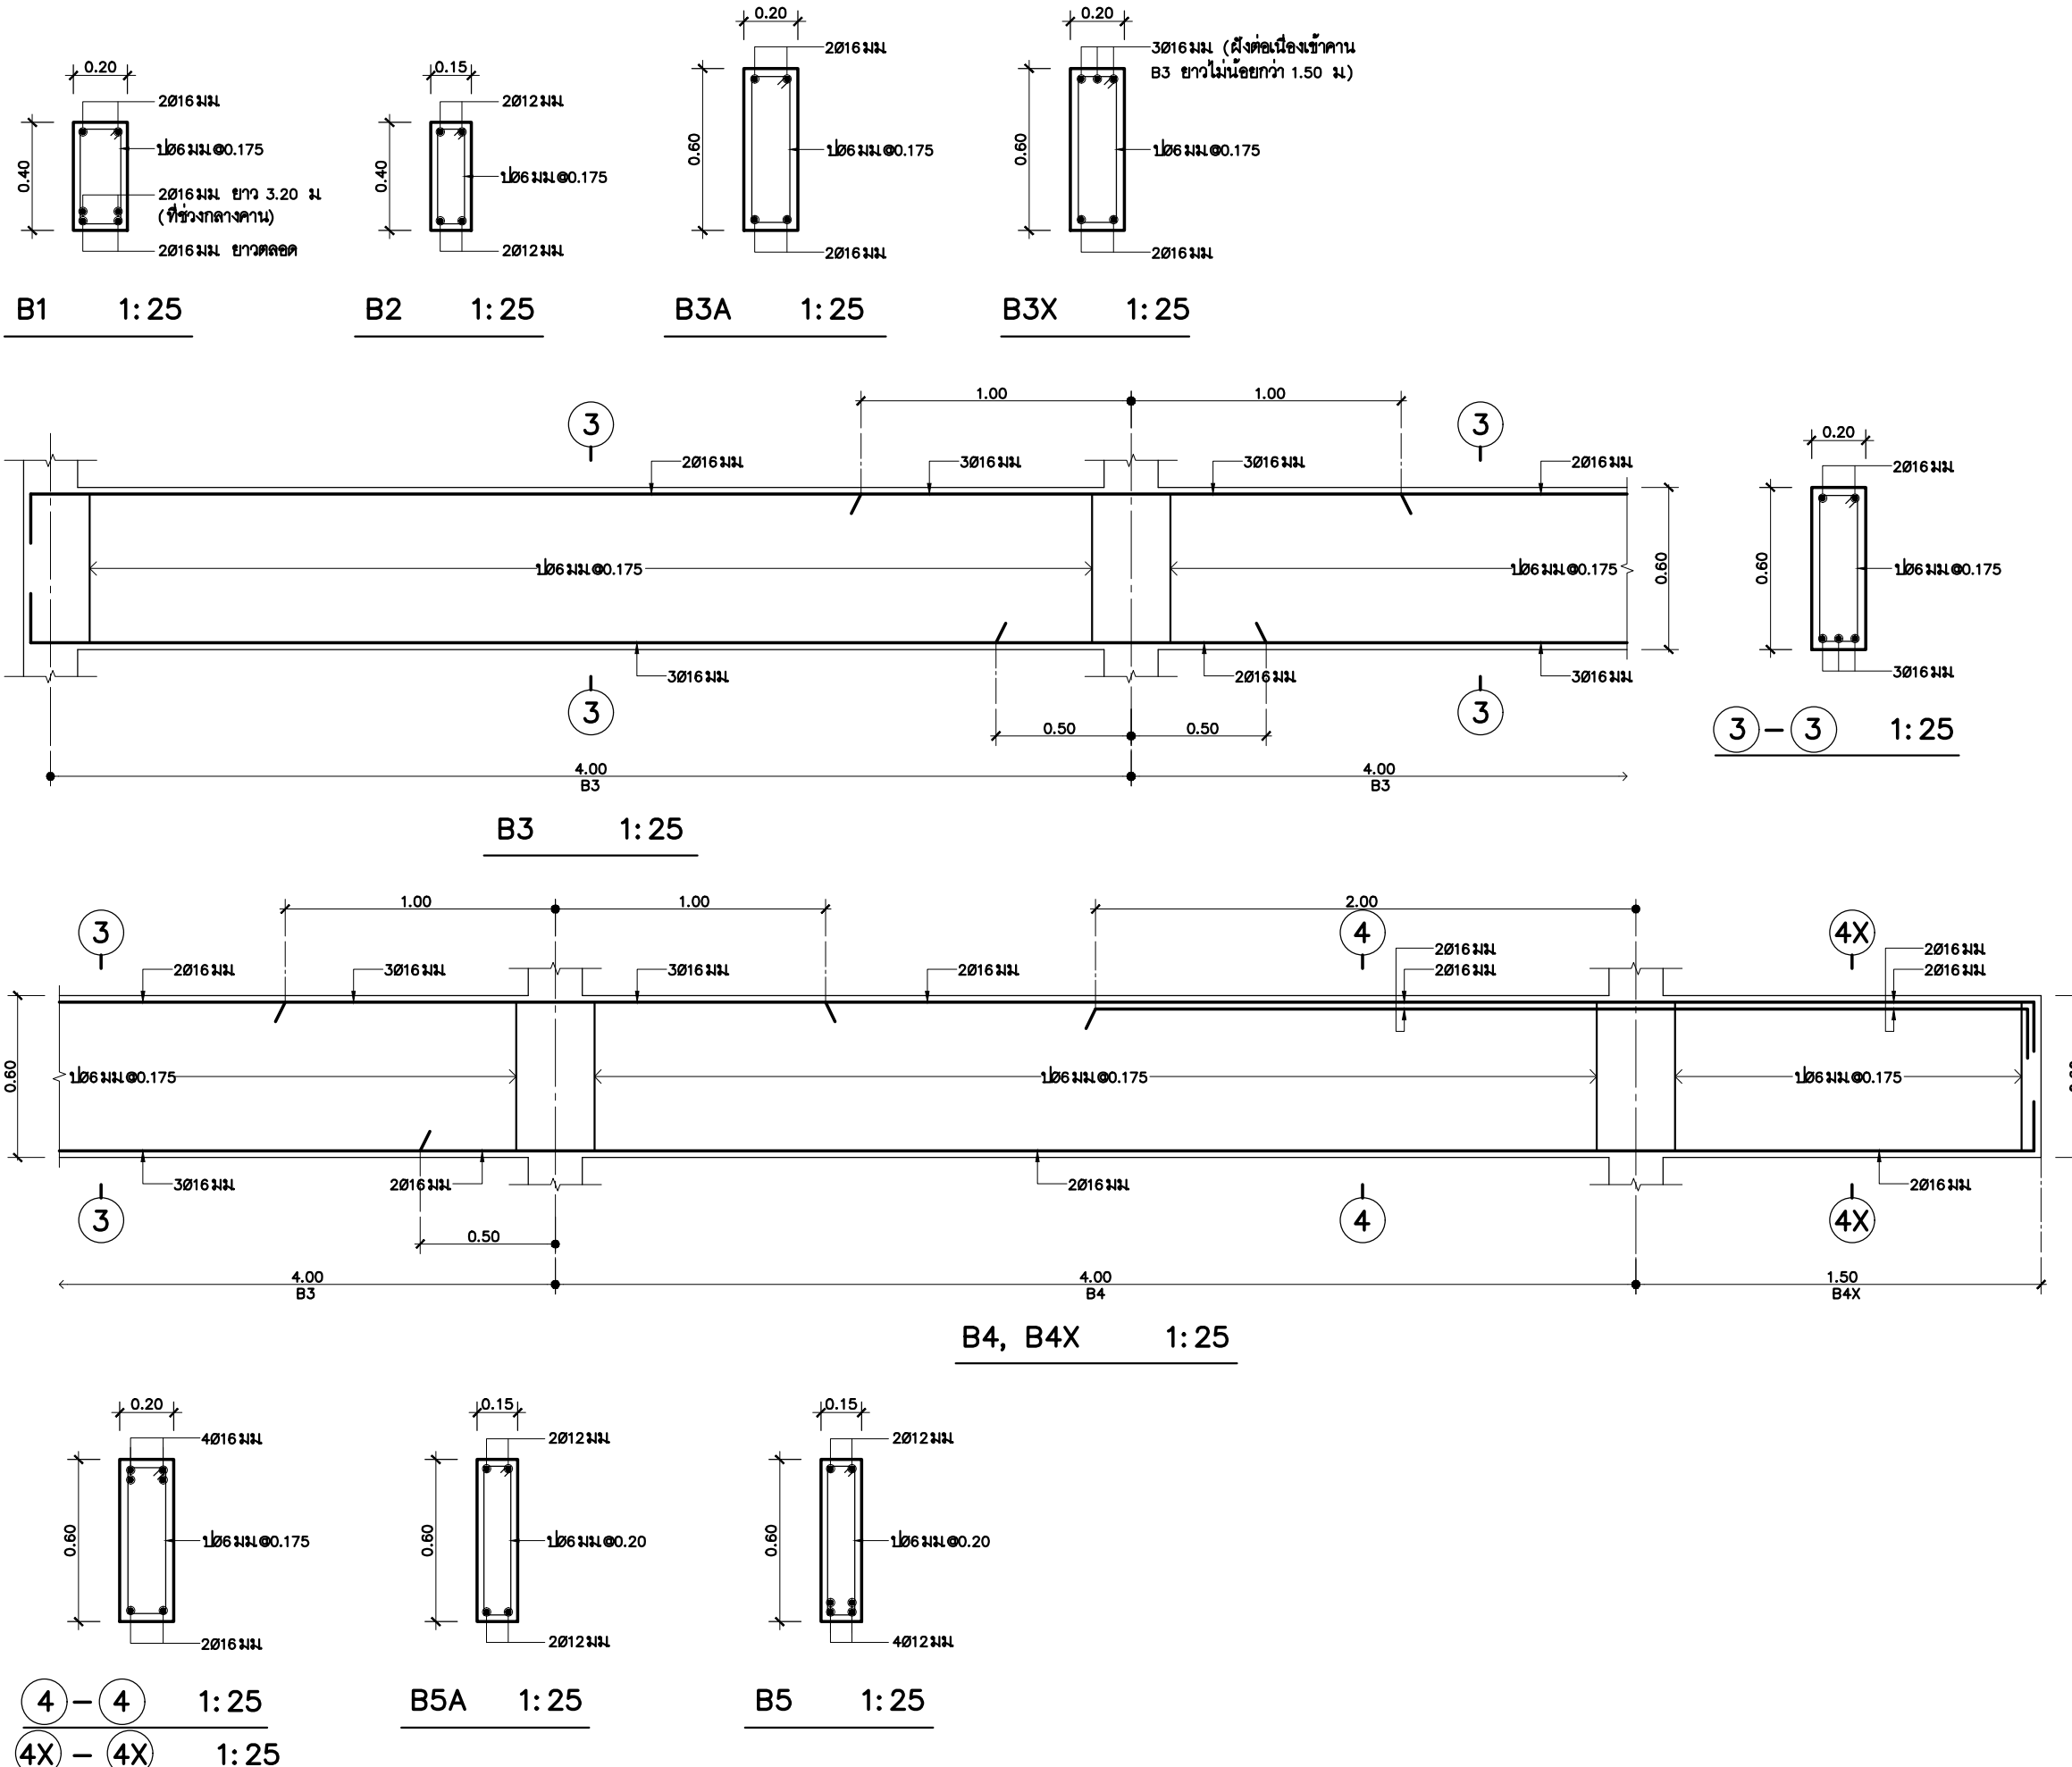


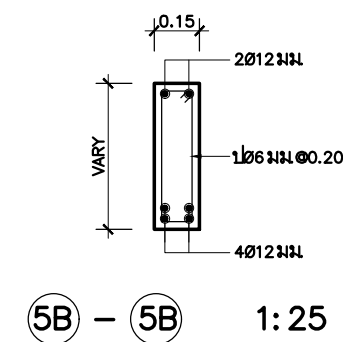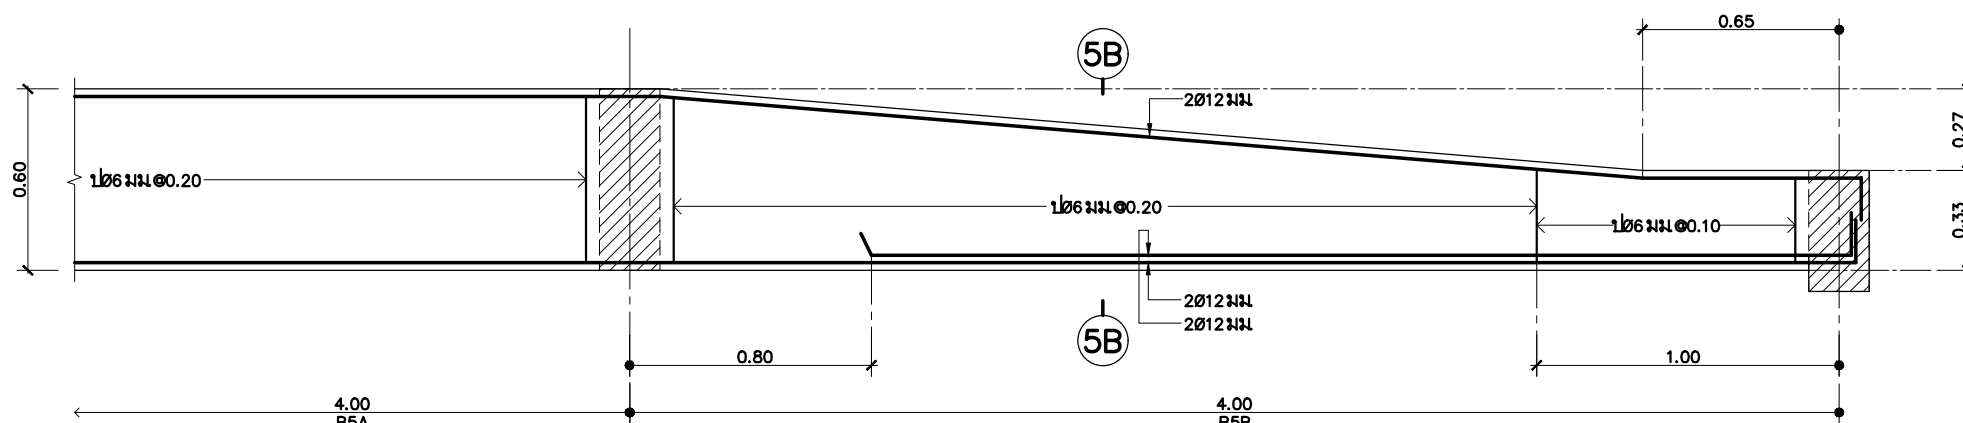

B5B 1: 25

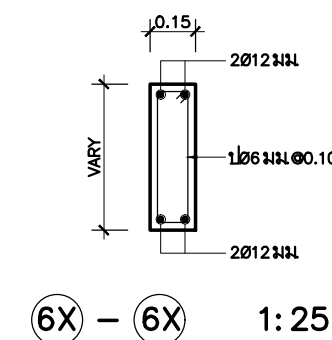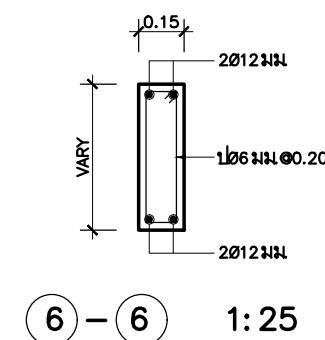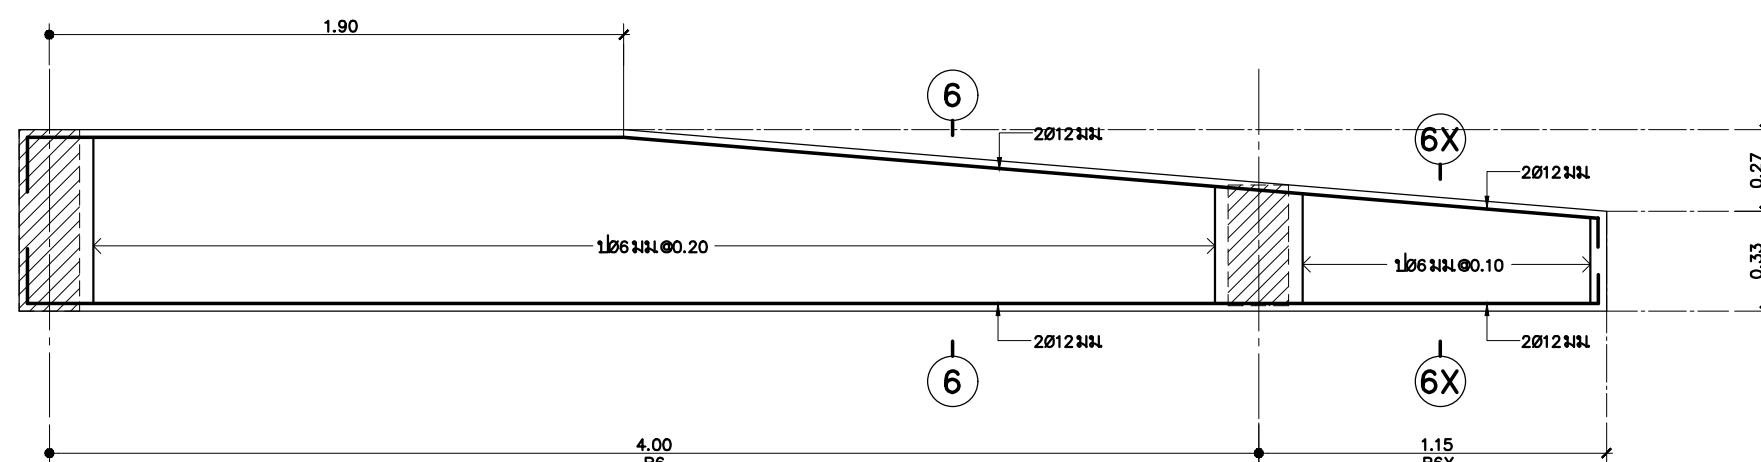

B6, B6X 1: 25

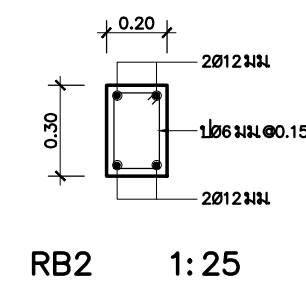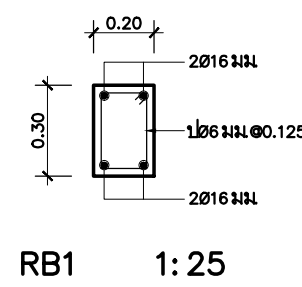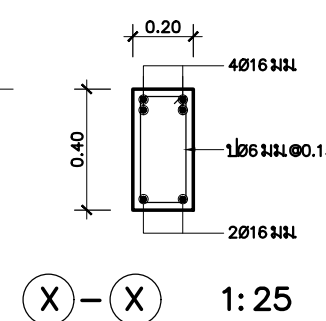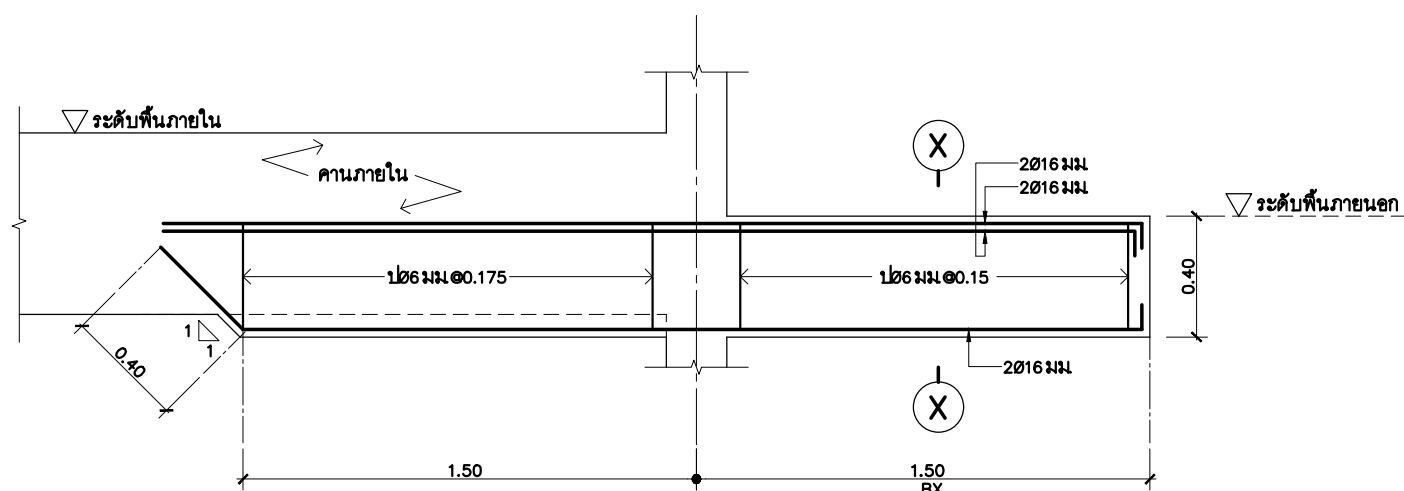

BX 1: 25

RB1 1: 25

RB2 1: 25



แบบบ้านसानฝัน
ของขวัญปีใหม่
คนไทยมีความสุข

แบบ
บ้านห่วงใยไทยประชาสุขใจ 1

สำนักสถาปัตยกรรม
ผู้ชำนาญการสำนัก

สถาปัตยกรรม
สถาปนิก

สำนักวิศวกรรมโครงสร้างและงานระบบ
ผู้ชำนาญการสำนัก

วิศวกรรม
วิศวกร

โครงสร้าง
วิศวกร

วิศวกรรม
วิศวกร

สุขาภิบาล
วิศวกร

วิศวกรรม
วิศวกร

ไฟฟ้า
วิศวกร

วิศวกรรม
วิศวกร

เครื่องกล
วิศวกร

อนุมัติ
(นายมงคล สดประเสริฐ)
อธิบดีกรมโยธาธิการและผังเมือง




































แสดงแบบ
B5B - B6X, BX,
RB1, RB2

มาตราส่วน 1: 25
วัน/เดือน/ปี 19/10/59
เลขที่แบบ S59041

S-10 10

สารบัญแบบระบบสุขาภิบาล		
แผ่นที่	แสดงแบบ	เลขที่แบบ
SN-01	สารบัญแบบและสัญลักษณ์ระบบสุขาภิบาล	SN - 59025
SN-02	รายการประกอบแบบ (แผ่นที่ 1)	SN - 59025
SN-03	รายการประกอบแบบ (แผ่นที่ 2)	SN - 59025
SN-04	แปลนระบบสุขาภิบาลพื้น	SN - 59025
SN-05	แบบขยายระบบสุขาภิบาลห้องน้ำ	SN - 59025
SN-06	แบบขยายการติดตั้งท่อ (แผ่นที่ 1)	SN - 59025
SN-07	แบบขยายการติดตั้งท่อ (แผ่นที่ 2)	SN - 59025
SN-08	แบบขยายการติดตั้งท่อ (แผ่นที่ 3)	SN - 59025


ชนิดท่อที่ใช้ในการก่อสร้าง			
ท่อ	สัญลักษณ์	ชนิดท่อ	ความลาดในแนวนอน
โสโครก	S	ท่อ PVC ชั้น 8.5 ตามมาตรฐาน มอก. 17 - 2532	1 : 75
ระบายน้ำทิ้ง	W	ท่อ PVC ชั้น 8.5 ตามมาตรฐาน มอก. 17 - 2532	1 : 75
ระบายอากาศ	V	ท่อ PVC ชั้น 8.5 ตามมาตรฐาน มอก. 17 - 2532	-
ประปา	CW	ท่อ PVC ชั้น 13.5 ตามมาตรฐาน มอก. 17 - 2532	-
ท่อระบายน้ำ	-	ท่อคอนกรีตท้องตลาด	ตามแบบ
น้ำทิ้งจากครัว	K	ท่อ PVC ชั้น 8.5 ตามมาตรฐาน มอก. 17 - 2532	1 : 75

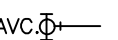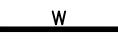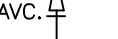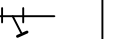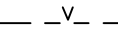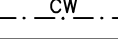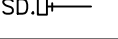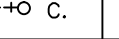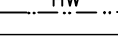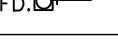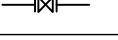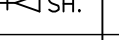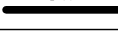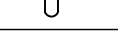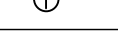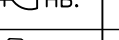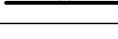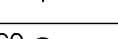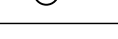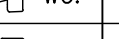  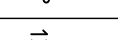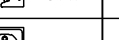 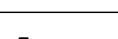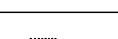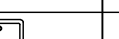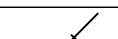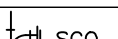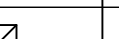    สัญลักษณ์ประกอบแบบระบบสุขาภิบาล							
สัญลักษณ์	ความหมาย	สัญลักษณ์	ความหมาย	สัญลักษณ์	ความหมาย	สัญลักษณ์	ความหมาย
	ท่อระบายน้ำโสโครก		ท่อระบายน้ำฝนแนวตั้ง		ฝาเปิดท่อระบายอากาศ		หัวกระโหลกพร้อมตะแกรงกรอง
	ท่อระบายน้ำเสีย		รูระบายน้ำฝนรูปโดม		ฝาเปิดท่อระบายอากาศ		ตะแกรงกรองผง (STRAINER)
	ท่อระบายอากาศ		รูระบายน้ำฝนแบบเรียบ		ฝาเปิดท่อระบายอากาศ ชนิดออกด้านข้าง		เครื่องสูบน้ำเพิ่มแรงดัน
	ท่อน้ำประปา		รูระบายน้ำด้านข้าง		ท่ออากาศผ่านหลังคา		ก๊อกน้ำ , ก๊อกสนาม
	ท่อน้ำร้อน		รูระบายน้ำทิ้งที่พื้น		ประตูน้ำ GATE VALVE		ฝักบัว
	ท่อระบายน้ำเสียรวม		รูระบายน้ำทิ้งที่พื้น		BALL VALVE		สายฉีดชำระ
	ท่อระบายน้ำฝน		จุดเปิดล้างท่อนบนพื้น		มาตรวัดน้ำ		ส้วม
	ท่อระบายน้ำจากครัว		จุดเปิดล้างท่อนบนพื้น		วาล์วลูกกลอย		โถปัสสาวะชาย
	ท่อระบายน้ำภายนอกอาคาร		จุดเปิดล้างท่อใต้พื้น		ประตูน้ำกันน้ำย้อนกลับ		อ่างล้างหน้า
	ท่อนอื่น		ปลั๊กอุดปลายท่อ		ข้อต่ออ่อนชนิดยางสังเคราะห์		อ่างชักล้าง
	สามทางที่วาย		จุดเปิดล้างท่อด้านข้าง		ข้อต่อลด		บ่อพักท่อระบายน้ำฝนฝาปิด คสล.



แบบบ้านसानฝัน
ของขวัญปีใหม่
คนไทยมีความสุข


แบบ
บ้านห่วงใยไทยประชาสุขใจ 1

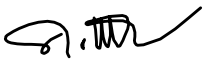สำนักสถาปัตยกรรม

ผู้อำนวยการสำนัก

สถาปัตยกรรม


สถาปนิก

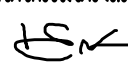
สถาปนิก

สำนักวิศวกรรมโครงสร้างและงานระบบ

ผู้อำนวยการสำนัก

วิศวกรรม


วิศวกร

โครงสร้าง


วิศวกร

วิศวกรรม


วิศวกร

สุขาภิบาล


วิศวกร

วิศวกรรม


วิศวกร

ไฟฟ้า



วิศวกร

วิศวกรรม


วิศวกร

เครื่องกล


วิศวกร

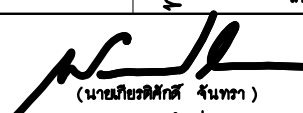
(นายเกียรติศักดิ์ จันทร์ขาว)
วิศวกรใหญ่


(นายสมณฑล สุคประเสริฐ)
อธิบดีกรมโยธาธิการและผังเมือง

แสดงแบบ
สารบัญแบบและสัญลักษณ์
ระบบสุขาภิบาล

มาตราส่วน -

วัน/เดือน/ปี 19/10/59

เลขที่แบบ SN-59025

SN-01

8

รายการประกอบแบบการเดินท่อภายในอาคาร

1. ข้อกำหนดทั่วไป

- 1.1 ท่อและอุปกรณ์ต่างๆ ที่นำมาใช้ ต้องเป็นของใหม่อยู่ในสภาพสามารถใช้งานได้ดี ไม่เคยนำไปใช้ที่อื่นมาก่อน และจะต้องดำเนินการติดตั้งตามคำแนะนำของบริษัทผู้ผลิตอย่างถูกต้อง
- 1.2 แบบและรายการที่แสดงไว้ เป็นเพียงแนวทางเท่านั้น ในทางปฏิบัติสามารถเสนอวิธีการอื่นที่ดีกว่า โดยไม่ขัดกับแนวทางที่กำหนดไว้ได้ แต่ต้องได้รับความเห็นชอบเป็นลายลักษณ์อักษรจากผู้ว่าจ้างเสียก่อน
- 1.3 สุขภัณฑ์ทุกจุดจะต้องมีการเดินท่อระบบสุขาภิบาลไปถึงในกรณีที่แบบแปลนมิได้แสดงรายละเอียดไว้ ให้ใช้ขนาดท่อและวิธีการปฏิบัติเช่นเดียวกับสุขภัณฑ์ชนิดเดียวกันกับจุดอื่นๆ
- 1.4 อุปกรณ์อื่นเช่น ประตูน้ำ ข้อต่อ ข้องอ ประตูน้ำก้นน้ำย้อนกลับ หรืออื่นๆ ที่จำเป็นต้องใช้ในการติดตั้งเพื่อให้งานดีขึ้นและถูกต้องตามหลักวิชาการ แม้มิได้ระบุไว้ในแบบ ผู้รับจ้างต้องจัดหาและทำการติดตั้งให้โดยไม่คิดราคาเพิ่ม
- 1.5 หลังจากเดินท่อสุขาภิบาลในช่องท่อแล้ว ที่ระดับพื้นแต่ละชั้นให้เทคอนกรีตเสริมเหล็กปิดช่องท่อให้เรียบร้อย
- 1.6 หากมีการประกาศกำหนดเป็นมาตรฐานผลิตภัณฑ์อุตสาหกรรม (มอก.) แล้ว ให้ใช้ผลิตภัณฑ์ที่ได้มาตรฐานผลิตภัณฑ์อุตสาหกรรม (มอก.) นั้นๆ ถ้ายังไม่มีผู้ผลิตได้รับมาตรฐาน ให้ใช้ผลิตภัณฑ์ผลิตได้เทียบเท่าแต่ยังไม่ได้รับตรามาตรฐานก็ได้

1.7 การจัดทำแบบ

- 1.7.1 ผู้รับจ้างต้องจัดทำแบบ SHOP DRAWING เสนอผู้ควบคุมงานของผู้ว่าจ้างอนุมัติก่อนดำเนินการ ซึ่งต้องยึดถือหลักวิชาและต้องไม่เป็นการตัดทอนหรือลดเนื้องานไปจากแบบทั้งนี้งานเพิ่มจาก SHOP DRAWING นี้จะขอคิดเงินหรือขยายเวลาเพิ่มไม่ได้ ยกเว้นได้รับอนุมัติจากผู้ว่าจ้าง
- 1.7.2 ก่อนส่งงานงวดสุดท้าย ผู้รับจ้างจะต้องส่งแบบ ASBUILT DRAWING ให้ผู้ว่าจ้าง 5 ชุด

1.8 วัสดุและอุปกรณ์ที่ต้องได้รับการอนุมัติก่อนดำเนินการติดตั้ง มีดังต่อไปนี้

- 1.8.1 ท่อและข้อต่อ
- 1.8.2 ข้องระบายน้ำทั้งที่พื้น, ข้องทำความสะอาดที่พื้น, ตะแกรงกันผงปิดช่องระบายน้ำฝน
- 1.8.3 เครื่องสูบน้ำ
- 1.8.4 อุปกรณ์ระบบบำบัดน้ำเสีย
- 1.8.5 อุปกรณ์ระบบดับเพลิง
- 1.8.6 ประตูน้ำต่างๆ

1.9 การเชื่อมต่อท่อประปาและท่อระบายน้ำจากภายนอกเข้ามายังอาคาร

- 1.9.1 ผู้รับจ้างจะต้องจัดหาและดำเนินการต่อท่อน้ำประปาจากภายนอกเข้ามายังโครงการ ถ้ามิได้ระบุไว้เป็นอย่างอื่น ค่าใช้จ่ายในการจัดหาท่อน้ำประปาและติดตั้งมาตรวัดน้ำ เป็นของผู้รับจ้างทั้งสิ้น (ทั้งนี้ไม่รวมถึงการขยายเขตการใช้น้ำประปา)
- 1.9.2 ผู้รับจ้างจะต้องดำเนินการต่อท่อระบายน้ำจากอาคารลงสู่ทางระบายน้ำภายนอกหรือทางระบายน้ำสาธารณะ ค่าใช้จ่ายในการขออนุญาต (ถ้ามี) และการต่อเชื่อมประสาณท่อ เป็นของผู้รับจ้างทั้งสิ้น

1.10 การรับประกัน

ผู้รับจ้างต้องรับประกันคุณภาพและสมรรถนะของเครื่องจักรและอุปกรณ์ภายในระยะเวลา 2 ปี นับจากวันที่ส่งมอบงานงวดสุดท้าย

2. ท่อและอุปกรณ์ท่อ ประตูน้ำและอุปกรณ์ประกอบ การเลือกใช้ท่อประเภทใด ให้ปฏิบัติตามรายการ

ประตูน้ำชนิดต่างๆ ต้องใช้ชนิดทนความดันใช้งานไม่น้อยกว่า Class 125

2.1 GATE VALVE ใช้กับงานระบบท่อประปา ใช้ชนิดทนความดันมากกว่าความดันใช้งานร้อยละ 50 แต่ต้องไม่น้อยกว่า Class 125

2.2 ประตูน้ำก้นน้ำย้อนกลับ (CHECK VALVE) ใช้กับงานระบบท่อประปา ใช้ชนิดทนความดันมากกว่าความดันใช้งานร้อยละ 50 แต่ต้องไม่น้อยกว่า Class 125

2.3 ก่อนต่อท่อแยกเข้าสุขภัณฑ์ ส้วมชนิดหม้อน้ำ อ่างล้างมือ สายฉีดชำระ อ่างล้างจาน ให้ติดตั้ง STOP VALVE ทุกจุดด้วย

3. การติดตั้ง การวางท่อ และการต่อท่อภายในอาคาร

3.1 การวางท่อ

3.1.1 การติดตั้งการวางและต่อท่อทุกชนิด จะต้องทำโดยไม่ให้เกิดความเครียดขึ้นกับท่อหรือทำให้ความมั่นคงแข็งแรงของอาคาร หรือส่วนหนึ่งส่วนใดของอาคารลดลง จะต้องมีการ ป้องกันการชำรุดของท่อเนื่องจากการขยายตัว หรือหดตัวของท่อและการทรุดตัวของอาคาร การติดตั้งการวางและการต่อท่อทุกชนิดจะต้องกระทำให้สามารถซ่อมแซมหรือเปลี่ยนได้โดยสะดวก

3.1.2 ท่อที่ติดตั้งในแนวดิ่งหรือแนวราบ จะต้องยึดหรือรัดท่อหรือแขวนท่อในระยะที่สามารถยึดหรือรัดท่อให้อยู่ในแนวหรือระดับที่ต้องการได้โดยตลอด

3.1.3 การวางท่อใต้พื้นชั้นล่าง ให้ยึดแขวนท่อเข้ากับพื้นชั้นล่าง โดยใช้เหล็กยึดท่อหรือเหล็กเสริมคอนกรีต พร้อมทั้งเทคอนกรีตหุ้มมิด หรือหล่อเป็นเนื้อเดียวกันกับพื้นชั้นล่าง


3.1.4 เมื่อเลิกหรือหยุดงานทุกครั้ง ผู้รับจ้างต้องอุดหรือปิดปลายสุดของท่อและอุปกรณ์ไว้ให้มิดชิด เพื่อป้องกันผง เศษขยะ ดินหรือสัตว์และอื่นๆเข้าไปในท่อ


3.1.5 ตำแหน่งที่มีการเปลี่ยนแปลงขนาดของท่อ ให้ใช้ข้อต่อลดเท่านั้น




แบบบ้านसानฝัน
ของขวัญปีใหม่
คนไทยมีความสุข


แบบ
บ้านห่วงใยไทยประชาชนใจ 1

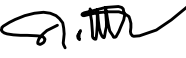
สำนักสถาปัตยกรรม
 ผู้อำนวยการสำนัก

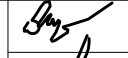สถาปัตยกรรม		สถาปนิก
		สถาปนิก

สำนักวิศวกรรมโครงสร้างและงานระบบ
 ผู้อำนวยการสำนัก

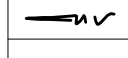วิศวกรรม		วิศวกร
โครงสร้าง		วิศวกร

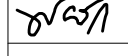วิศวกรรม		วิศวกร
สุขาภิบาล		วิศวกร

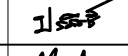วิศวกรรม		วิศวกร
ไฟฟ้า		วิศวกร

วิศวกรรม		วิศวกร
เครื่องกล		วิศวกร


(นายเกียรติศักดิ์ จันทร์หา) วิศวกรใหญ่

อนุมัติ

(นายสมณชาล สุคประเสริฐ) อธิบดีกรมโยธาธิการและผังเมือง


แสดงแบบ
รายการประกอบแบบ (แผ่นที่ 1)

มาตราส่วน —


วัน/เดือน/ปี 19/10/59

เลขที่แบบ SN-59025

SN-02	8
-------	---

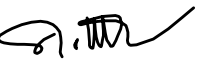3.1.6 ตำแหน่งที่มีการเปลี่ยนแปลงทิศทางของท่อ ให้ใช้อุปกรณ์ข้อต่อเท่านั้น โดยท่อ โลหะ ท่อระบายน้ำทิ้ง ให้ใช้เฉพาะข้อต่อชนิดสามทางวาย หรือสามทางทึบ แต่ห้ามใช้ข้อต่อสามทางจากโดยเด็ดขาด 3.1.7 การติดตั้งประตุน้ำกับท่อที่เดินใต้ดินนั้น ก้านวาล์วจะต้องอยู่เหนือระดับดิน หรือติดตั้งใน VALVE BOX					
3.2 อุปกรณ์แขวนท่อและรองรับท่อ ที่แขวนท่อ (HANGER) และที่รองรับท่อ (SUPPORTS) ให้ใช้ผลิตภัณฑ์สำเร็จรูปที่ได้ ทั้งนี้ต้องได้รับอนุมัติจากผู้ควบคุมงานก่อนนำไปใช้งาน					
4. งานวางท่อระบบระบายน้ำนอกอาคาร 4.1 การเตรียมพื้นที่ ผู้รับจ้างจะต้องเตรียมพื้นที่ในส่วนที่จะทำการก่อสร้างวางท่อ บ่อพักให้ เป็นที่เรียบร้อยก่อนดำเนินการก่อสร้าง การดำเนินงานหากจำเป็นต้องมีการประสานงาน การขอ อนุญาตกับหน่วยงานที่เกี่ยวข้อง การรื้อถอน โยกย้าย สิ่งกีดขวางและการขอมกลับให้เหมือนเดิม ค่าใช้จ่ายในการดำเนินงานทั้งหมดเป็นของผู้รับจ้าง การดำเนินงานในการรื้อถอนโยกย้ายสิ่งกีดขวาง ต่างๆ ผู้รับจ้างจะต้องปฏิบัติด้วยความระมัดระวังมิให้เกิดความเสียหายกับส่วนอื่นที่เกี่ยวข้อง สัมพันธ์กัน หรือเป็นการล่อแหลมที่จะก่อให้เกิดอุบัติเหตุ ผู้รับจ้างจะต้องปฏิบัติงานให้เป็นที เรียบร้อยก และไม่เป็นอุปสรรคต่อผู้สัญจร 4.2 การขุดคูวางท่อ 4.2.1 การขุดคูวางท่อ ให้ขุดเป็นคูเปิด ความกว้าง ตามขนาดของท่อและอุปกรณ์ ในกรณีที่อาจเกิดอันตรายเนื่องจากคูที่ขุดพังทลาย ผู้รับจ้างจะต้องตอกเข็มทำเชื่อนและ ค้ำยันให้แข็งแรงเพียงพอ ความลึกของคูให้ลึกกว่าระดับกันท่อน้อยกว่า 10 ซม. พื้นรองดินให้ กระทุ้งแน่นและปรับเรียบสม่ำเสมอ มีความลาดตามระดับความลาดของท่อที่กำหนดและรองพื้น ด้วยทรายหุ้มน้ำอัดแน่น 4.3 การวางท่อ 4.3.1 การก่อสร้างวางท่อจะต้องทำในที่แห้ง ผู้รับจ้างจะต้องจัดเตรียมอุปกรณ์ต่างๆ ที่จำเป็นในการ สูบน้ำในคู วางท่อให้แห้งอยู่ตลอดเวลาจนกว่าจะวางท่อแล้วเสร็จและคอนกรีตอยู่ตัว น้ำที่สูบน้ำจาก วางท่อจะต้องต่อท่อหรือวางรับน้ำระบายลงแหล่งน้ำให้เป็นทีเรียบร้อย ไม่ก่อความรำคาญ ต่อผู้สัญจร 4.3.2 ท่อน้ำมาใช้อก่อสร้างวางท่อ จะต้องเป็นท่อใหม่ไม่แตกร้าวหรือชำรุดเสียหาย เมื่อก่อสร้างวาง ท่อเสร็จในแต่ละครั้งจะต้องทำความสะอาดผิวภายในท่อให้เรียบร้อยก่อนที่จะทำการเชื่อมต่อท่อ				4.4 การถมกลบท่อ 4.4.1 ท่อที่จะถมกลบจะต้องผ่านการตรวจสอบว่าถูกต้อง เป็นไปตาม ข้อกำหนดจึงจะทำการถมกลบท่อส่วนนั้นได้ 4.4.2 ในการถมกลบผู้รับจ้างจะต้องอัดหรือกระทุ้งดินให้แน่น การปฏิบัติงานจะต้องระมัดระวัง มิให้เกิดอันตรายกับท่อที่วางไว้แล้ว 4.4.3 วัสดุที่ใช้ในการถมกลบ ให้ใช้วัสดุที่ได้จากการขุดรองดิน ซึ่งเป็นดินหรือทราย ห้ามกลบ ด้วยหินหรืออิฐหรือวัสดุอื่นใดที่มีลักษณะคล้ายคลึงกัน 4.4.4 วัสดุที่เหลือจากการถมกลบท่อจะต้องทำการขนย้ายไปจากบริเวณก่อสร้าง ห้ามกองทิ้งไว้เป็นที่ กีดขวางทางสัญจร 4.4.5 เมื่อถมกลบท่อเสร็จเรียบร้อยแล้ว ให้ผู้รับจ้างดำเนินการขอมกลับในส่วนที่ได้ขุดทำลาย รื้อ โยกย้าย (เช่น ผิวดิน เสาไฟฟ้า สายเคเบิล ท่อประปา ทางเท้า ฯลฯ) ให้เรียบร้อยเหมือนเดิมทุก ประการ หรือรับดำเนินการก่อสร้างตามรายละเอียดที่กำหนดไว้ในแบบให้เรียบร้อยโดยเร็ว	
5. การทดสอบและการทำความสะอาดระบบท่อ เมื่อทำการติดตั้งระบบต่างๆ เป็นทีเรียบร้อยแล้ว จะต้องทำการทดสอบระบบต่างๆ ก่อนการส่งงาน ในการทดสอบจะต้องแจ้งให้คณะกรรมการตรวจการจ้างตรวจสอบด้วย อุปกรณ์และค่าใช้จ่ายต่างๆ ในการ ทดสอบ ผู้รับจ้างจะต้องจัดหาและดำเนินการเองทั้งหมด 5.1 ระบบประปา การทดสอบจะต้องทดสอบระบบทั้งหมดให้สามารถรับความดันไม่มากกว่าความดัน 75 psi ไม่น้อยกว่า 2 ชม. หากความดันไม่ลดและไม่มีการรั่วซึม จึงถือว่าใช้ได้ 5.2 ระบบระบายน้ำทิ้ง น้ำโสโครก สามารถทำการทดสอบได้โดยใช้น้ำ ให้ปิดช่องทั้งหลายของส่วนที่ต้องการทดสอบให้แน่น ยกเว้นช่องที่อยู่ระดับ สูงสุดแล้วเติมน้ำล้นออกทางนี้ แต่ละส่วนของท่อจะต้องได้รับการทดสอบภายใต้ความดัน ไม่ต่ำกว่าความดันน้ำ 3 ม. แล้วก็น้ำไว้เป็นเวลาไม่น้อยกว่า 2 ชม. โดยที่น้ำไม่ซึมหรือ รั่วจึงถือว่าใช้ได้ 5.3 หลังจากทำความสะอาดภายในถังเก็บน้ำด้วยน้ำสำหรับบริโภคจนสะอาดแล้ว ให้เติมน้ำจน เต็มถังแล้วทำการฆ่าเชื้อด้วยคลอรีนน้ำ เข้มข้น 10% โดยใช้ที่อัตราส่วน 50 ซีซี ต่อน้ำ 1 ลบ.ม. (หากใช้ที่ความเข้มข้นอื่นให้ปรับอัตราส่วนได้) โดยให้แช่น้ำทิ้งไว้ 1 คืน แล้วล้างออก					
		แบบบ้านसानฝัน ของขวัญปีใหม่ คนไทยมีความสุข			
แบบ บ้านห่วงใยไทยประชาสุขใจ 1		สำนักสถาปัตยกรรม  ผู้อำนวยการสำนัก			
สถาปัตยกรรม		 สถาปนิก  สถาปนิก			
สำนักวิศวกรรมโครงสร้างและงานระบบ  ผู้อำนวยการสำนัก					
วิศวกรรม		 วิศวกร			
โครงสร้าง		วิศวกร			
วิศวกรรม		 วิศวกร			
สุขาภิบาล		วิศวกร			
วิศวกรรม		 วิศวกร			
ไฟฟ้า		 วิศวกร			
วิศวกรรม		 วิศวกร			
เครื่องกล		 วิศวกร			
 (นายเกียรติศักดิ์ จันทร์หา) วิศวกรใหญ่					
อนุมัติ  (นายสมณชาล สุตะประเสริฐ) อธิบดีกรมโยธาธิการและผังเมือง					
แสดงแบบ					
รายการประกอบแบบ (แผ่นที่ 2)					
มาตราส่วน —					
วัน/เดือน/ปี 19/10/59					
เลขที่แบบ SN-59025					
SN-03		8			

ต้องการที่ดินกว้างอย่างน้อย = 18.10 ม.

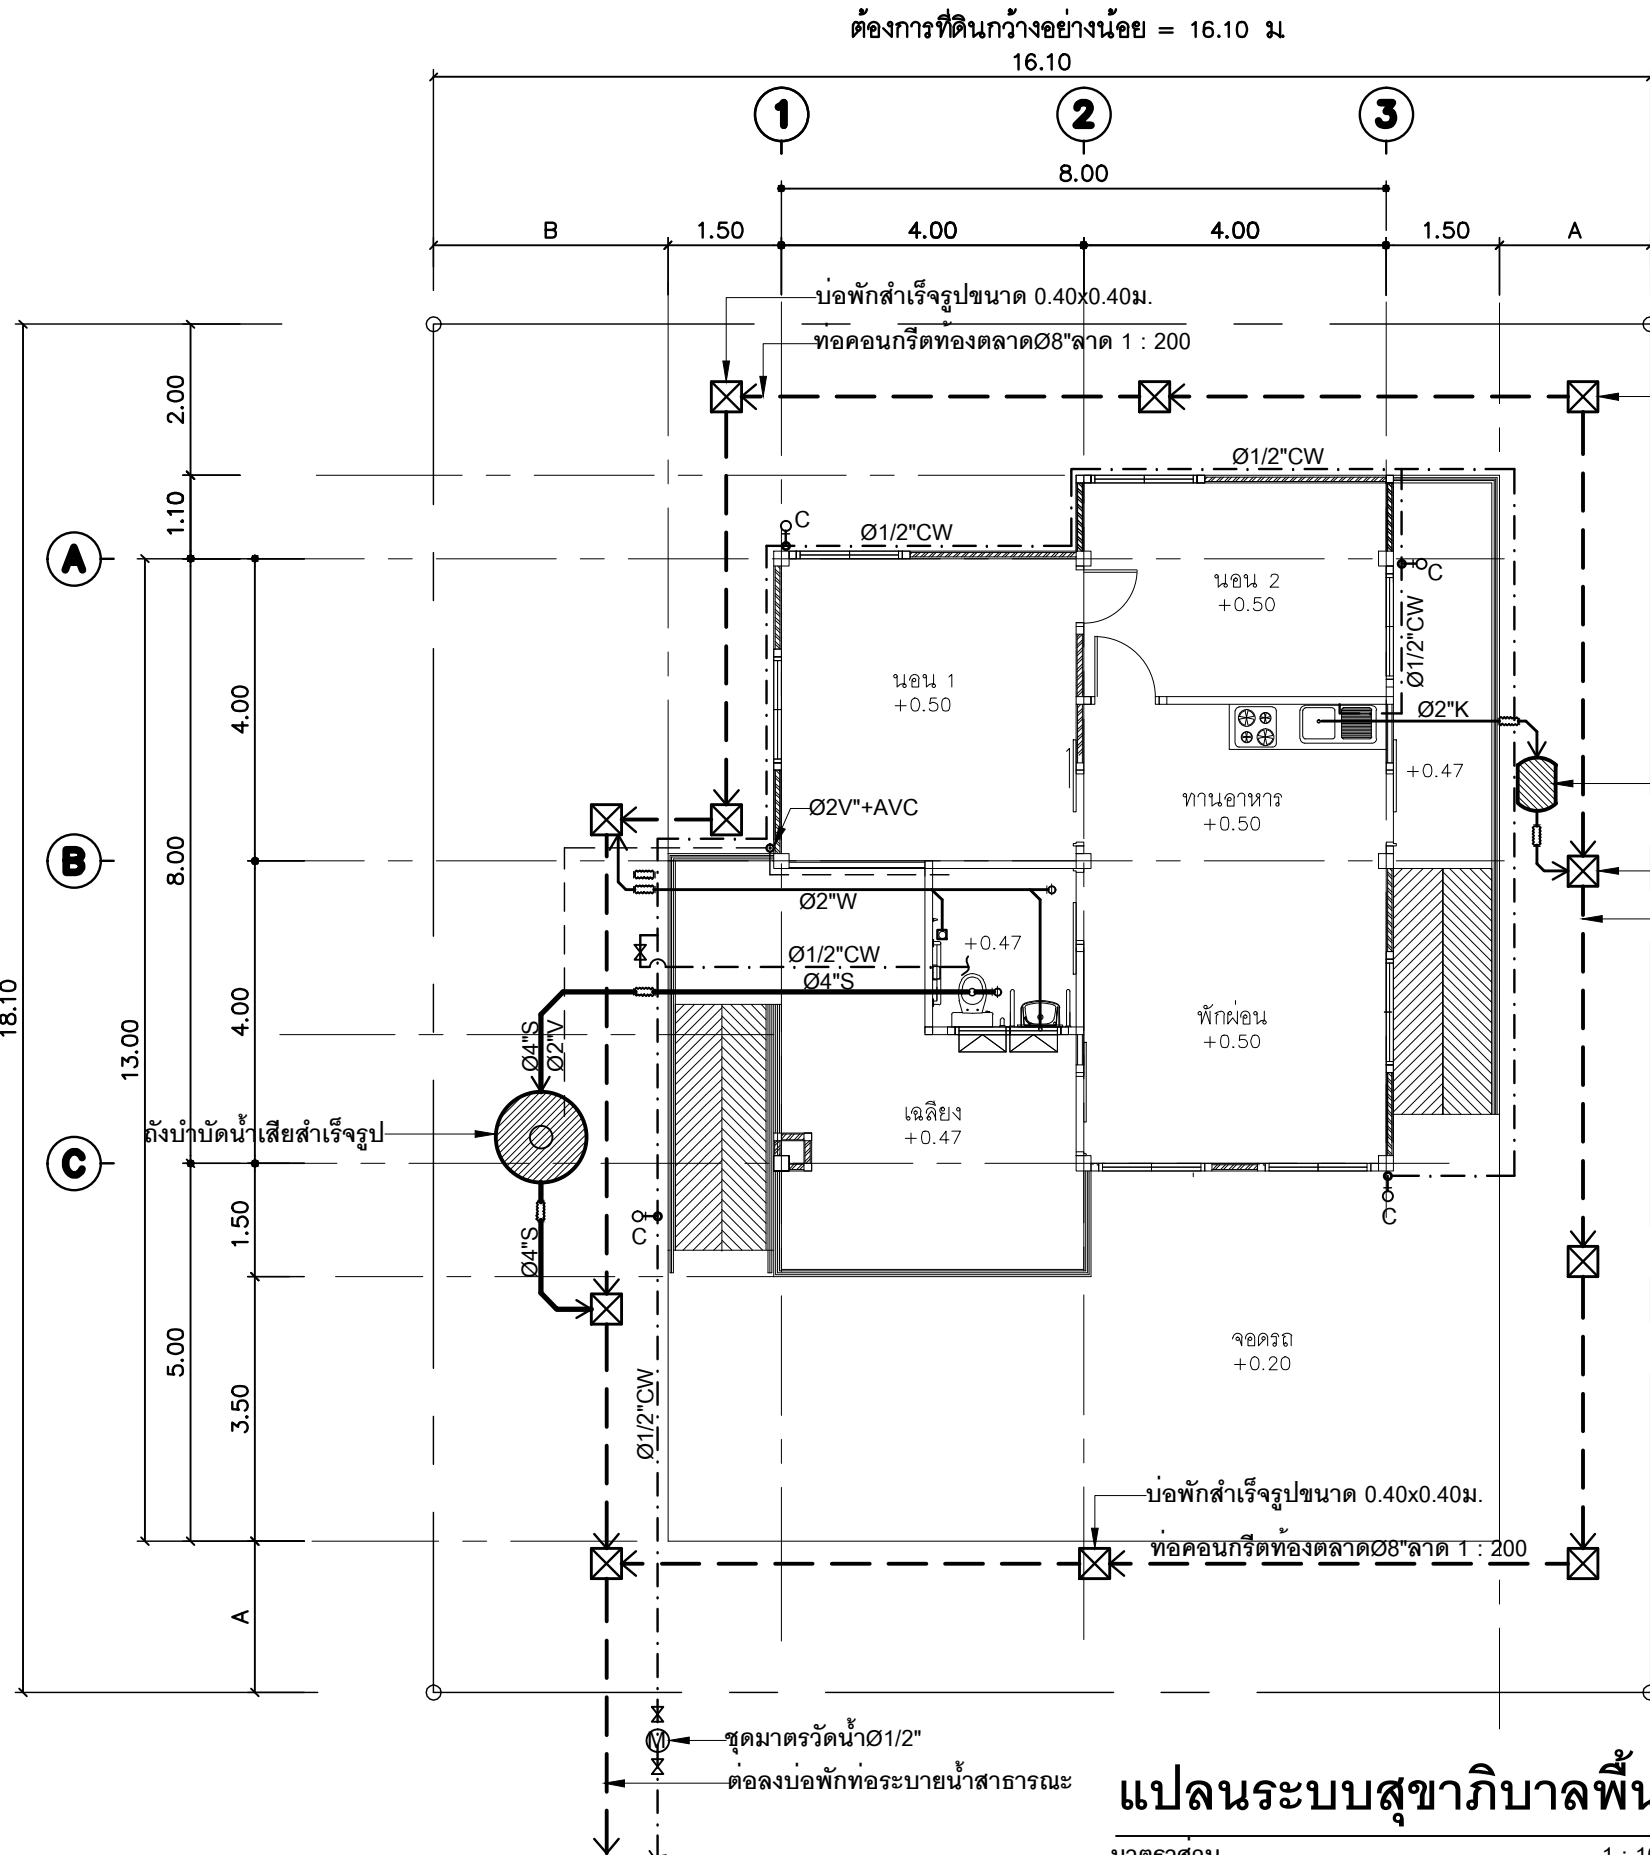

แปลนระบบสุขาภิบาลพื้น

มาตราส่วน

1 : 100

ถึงบำบัดน้ำเสียสำเร็จรูป

- ชนิดเกราะ-กรองไร้อากาศ
- ปริมาตรส่วนเกราะไม่น้อยกว่า 1 ลบ.ม.
- ปริมาตรส่วนกรองไร้อากาศไม่น้อยกว่า 0.3 ลบ.ม.
- ผลิตภัณฑ์ PP, AQUA, DOS, HICLEAR, TREAT หรือเทียบเท่า
- การติดตั้งเป็นไปตามมาตรฐานผู้ผลิต

ถึงดักไขมันสำเร็จรูป

- ชนิดฝังดิน
- มีขนาดความจุไม่น้อยกว่า 50 ลิตร
- ผลิตภัณฑ์ PP, AQUA, DOS, HICLEAR, TREAT หรือเทียบเท่า
- การติดตั้งเป็นไปตามมาตรฐานผู้ผลิต



แบบบ้านसानฝัน
ของขวัญปีใหม่
คนไทยมีความสุข

แบบ
บ้านห่วงใยไทยประชาสุขใจ 1

สำนักสถาปัตยกรรม
ผู้อำนวยการสำนัก

สถาปัตยกรรม
สถาปนิก

สำนักวิศวกรรมโครงสร้างและงานระบบ
ผู้อำนวยการสำนัก

วิศวกรรม
วิศวกร

โครงสร้าง
วิศวกร

วิศวกรรม
วิศวกร

สุขาภิบาล
วิศวกร

ไฟฟ้า
วิศวกร

วิศวกรรม
วิศวกร

เครื่องกล
วิศวกร


แสดงแบบ
แปลนระบบสุขาภิบาลพื้น

มาตราส่วน
-

วัน/เดือน/ปี 19/10/59

เลขที่แบบ SN-59025

SN-04 8

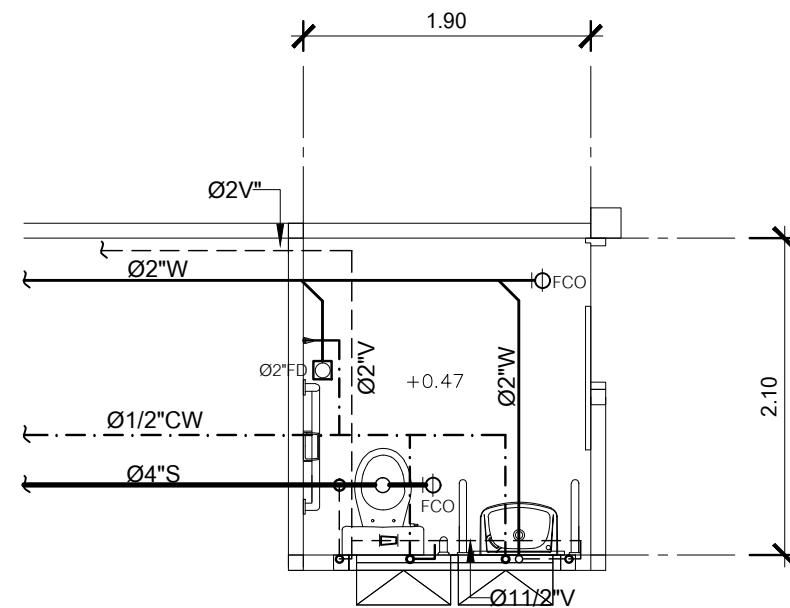

แปลนระบบสุขาภิบาลห้องน้ำ
มาตราส่วน 1 : 50
(ท่อประปาเดินใต้พื้น)

ขนาดท่อย่อยที่ต่อเข้าสู่ชักันท์					
ชักันท์	สัญลักษณ์	ขนาดท่อ (นิ้ว)			
		CW.	S.	V.	W.
โถส้วม (FT.)	WC.	1/2	4	2	-
โถส้วม (FV.)	WC1.	1	4	2	-
อ่างล้างหน้า	LAV.	1/2	-	1 1/2	2
โถปัสสาวะชาย	UR.	3/4	2	1 1/2	-
ฝักบัว	SH.	1/2	-	-	-
กอน้ำ	C.	1/2	-	-	-
อ่างล้าง	SINK.	1/2	-	1 1/2	2
ช่องระบายน้ำทั้งที่พื้น	FD.	-	-	-	2



แบบบ้านसानฝัน
ของขวัญปีใหม่
คนไทยมีความสุข

แบบ
บ้านห่วงใยไทยประชาสุขใจ 1

สำนักสถาปัตยกรรม
ผู้อำนวยการสำนัก

สถาปัตยกรรม
สถาปนิก
สถาปนิก

สำนักวิศวกรรมโครงสร้างและงานระบบ
ผู้อำนวยการสำนัก

วิศวกรรม
วิศวกร
วิศวกร

วิศวกรรม
สุขาภิบาล
วิศวกร

วิศวกรรม
ไฟฟ้า
วิศวกร

วิศวกรรม
เครื่องกล
วิศวกร

(นายเกียรติศักดิ์ จันทร์ทอง)
วิศวกรใหญ่

อนุมัติ
(นายสมณชาติ สุกประเสริฐ)
อธิบดีกรมโยธาธิการและผังเมือง


แสดงแบบ
แบบขยายระบบสุขาภิบาลห้องน้ำ

มาตราส่วน 1:50


วัน/เดือน/ปี 19/10/59

เลขที่แบบ SN-59025

SN-05 8

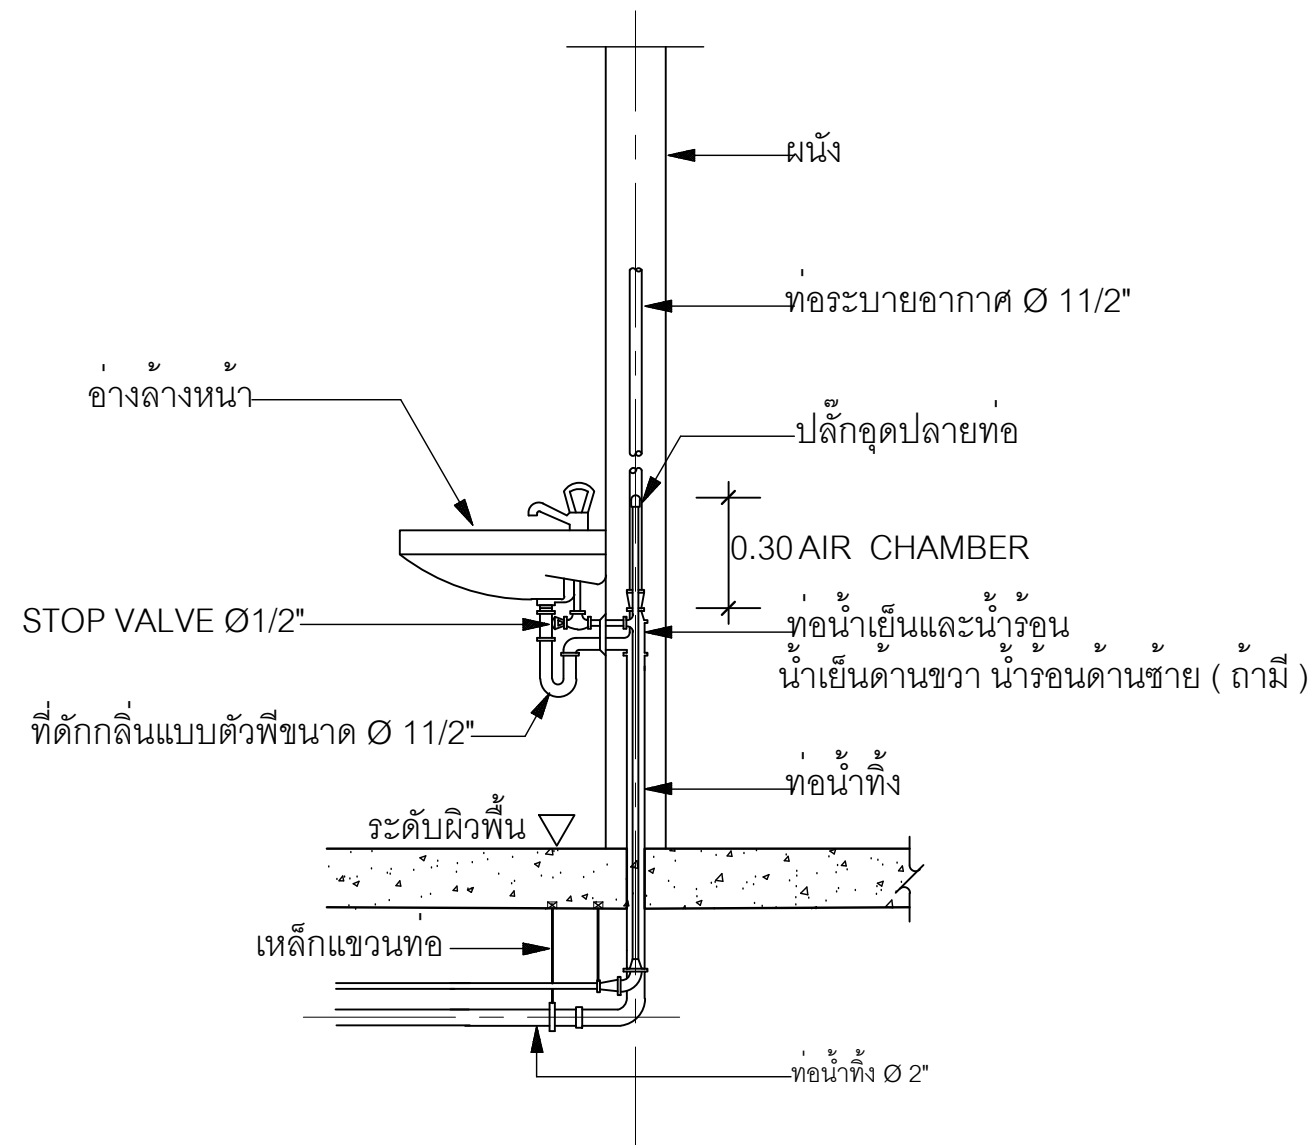

อ่างล้างหน้า (LAV)

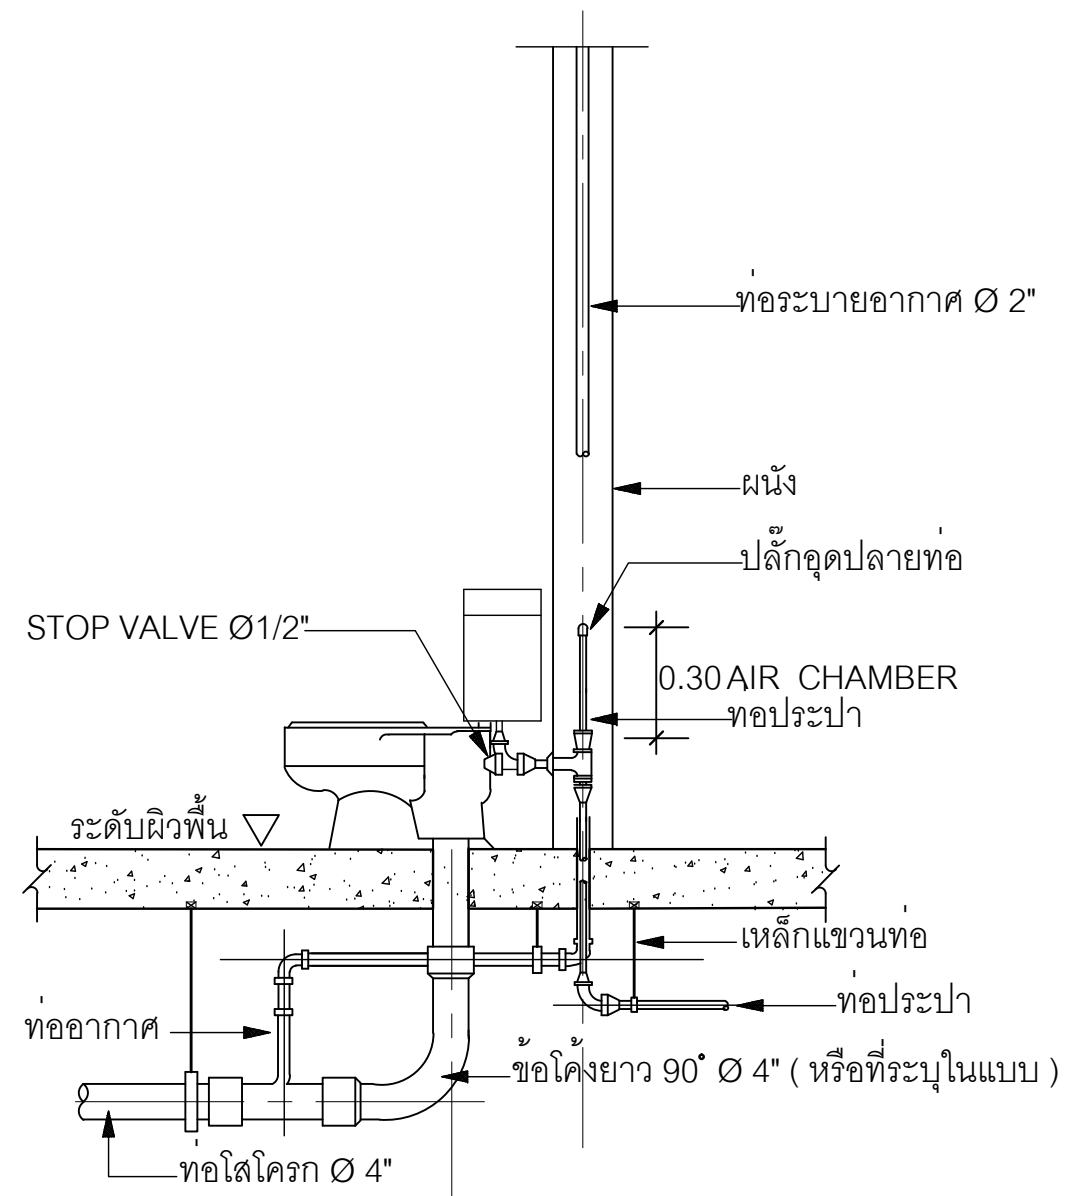

ส่วนชนิดถังน้ำล้าง (FLUSH TANK)



แบบบ้านसानฝัน
ของขวัญปีใหม่
คนไทยมีความสุข

แบบ
บ้านห่วงใยไทยประสาสุขใจ 1

สำนักสถาปัตยกรรม
ผู้ออกแบบ

สถาปัตยกรรม
สถาปนิก

สำนักวิศวกรรมโครงสร้างและงานระบบ
ผู้ออกแบบ

วิศวกรรม
วิศวกร

โครงสร้าง
วิศวกร

วิศวกรรม
วิศวกร

สุขาภิบาล
วิศวกร

วิศวกรรม
วิศวกร

ไฟฟ้า
วิศวกร

วิศวกรรม
วิศวกร

เครื่องกล
วิศวกร


อนุมัติ
(นายสมชาย อดิธรรม)

แสดงแบบ
แบบขยายการติดตั้งท่อ (แผ่นที่ 1)

มาตราส่วน
วัน/เดือน/ปี 19/10/59

เลขที่แบบ SN-59025


SN-06 8

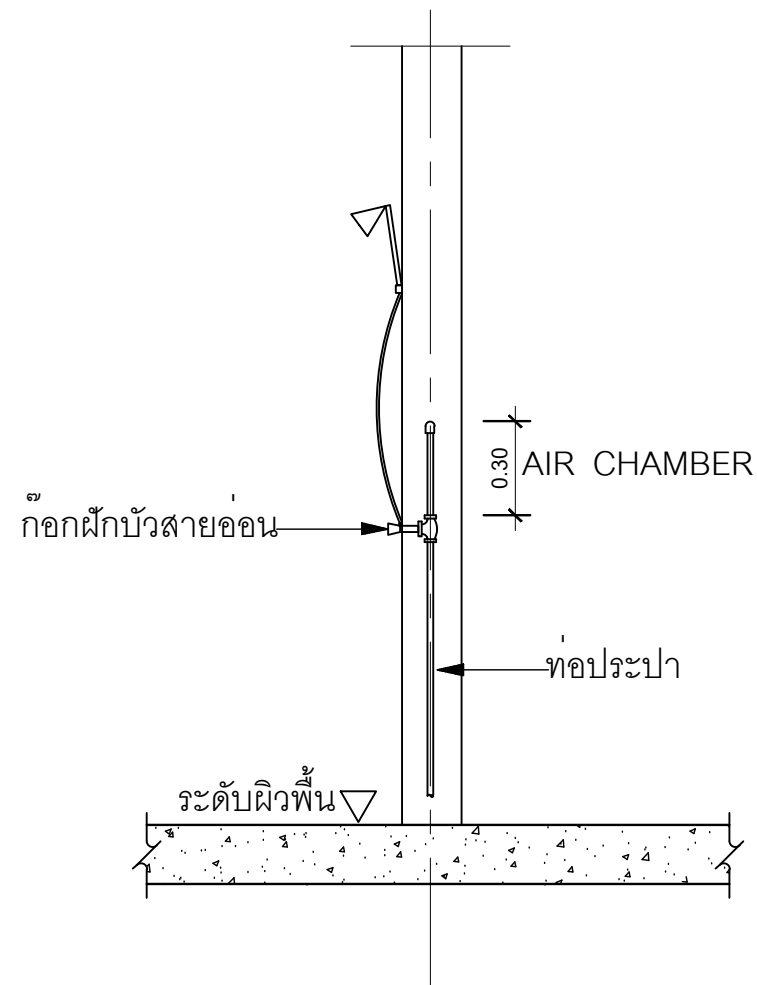


ฝักบัวอาบน้ำ (SH)

หมายเหตุ

- ขนาดท่อต่าง ๆ ให้เป็นไปตามแบบเฉพาะของอาคารนั้น ๆ หากแบบเฉพาะนั้น ๆ มิได้ระบุขนาดของท่อไว้ ให้ใช้ตามแบบมาตรฐานนี้
- ขนาดท่อ AIR CHAMBER ให้มีขนาดเส้นผ่านศูนย์กลางท่อไม่น้อยกว่าท่อประปาที่ต่อกับสุขภัณฑ์นั้น ๆ

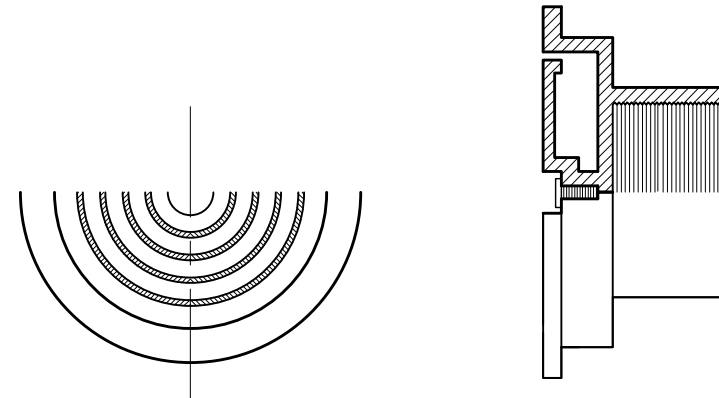

แบบขยายฝาปิดท่อระบายอากาศ (AVC)

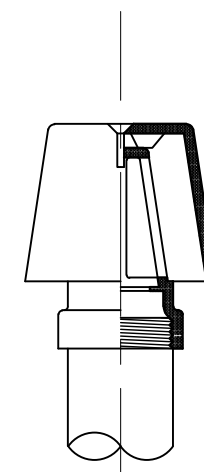

ท่ออากาศแนวดิ่ง

แบบขยายฝาปิดท่อระบายอากาศ (AVC)



แบบบ้านसानฝัน
ของขวัญปีใหม่
คนไทยมีความสุข

แบบ
บ้านห่วงใยไทยประชาสุขใจ 1

สำนักสถาปัตยกรรม
ผู้อำนวยการสำนัก

สถาปัตยกรรม
สถาปนิก
สถาปนิก

สำนักวิศวกรรมโครงสร้างและงานระบบ
ผู้อำนวยการสำนัก

วิศวกรรม
วิศวกร
โครงสร้าง
วิศวกร

วิศวกรรม
วิศวกร
สุขาภิบาล
วิศวกร

วิศวกรรม
วิศวกร
ไฟฟ้า
วิศวกร

วิศวกรรม
วิศวกร
เครื่องกล
วิศวกร

(นายเกียรติศักดิ์ จันทร์ทอง)
วิศวกรใหญ่

อนุมัติ
(นายสมณชาติ สุกประเสริฐ)
อธิบดีกรมโยธาธิการและผังเมือง

แสดงแบบ



แบบขยายการติดตั้งท่อ (แผ่นที่ 2)

มาตราส่วน -



วัน/เดือน/ปี 19/10/59

เลขที่แบบ SN-59025

SN-07 8

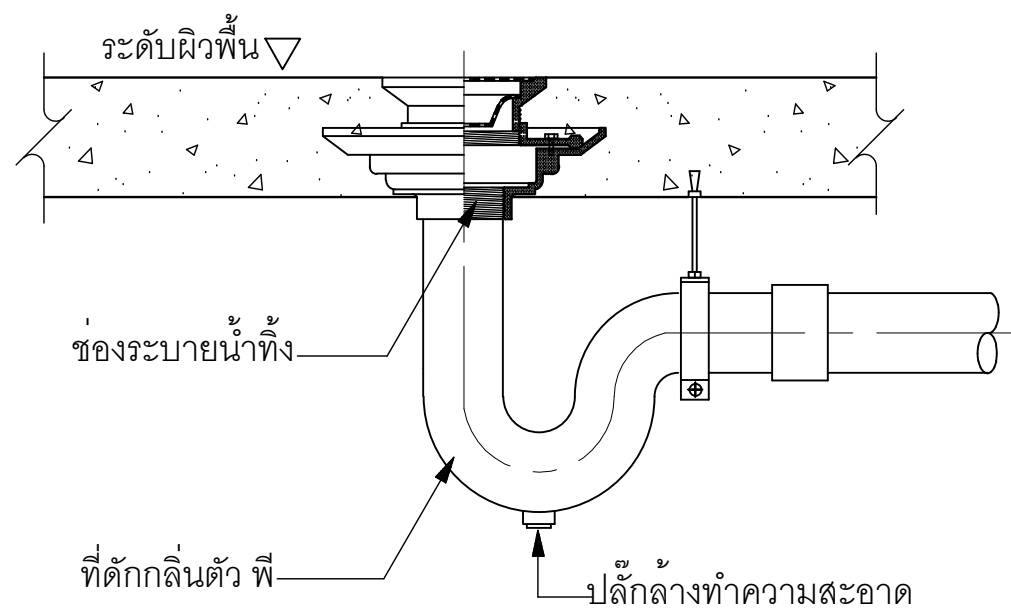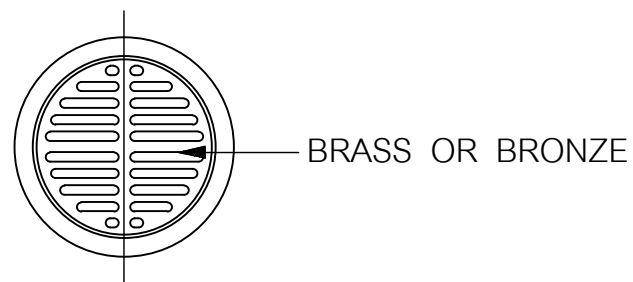

ช่องระบายน้ำทิ้งที่พื้น (FD)

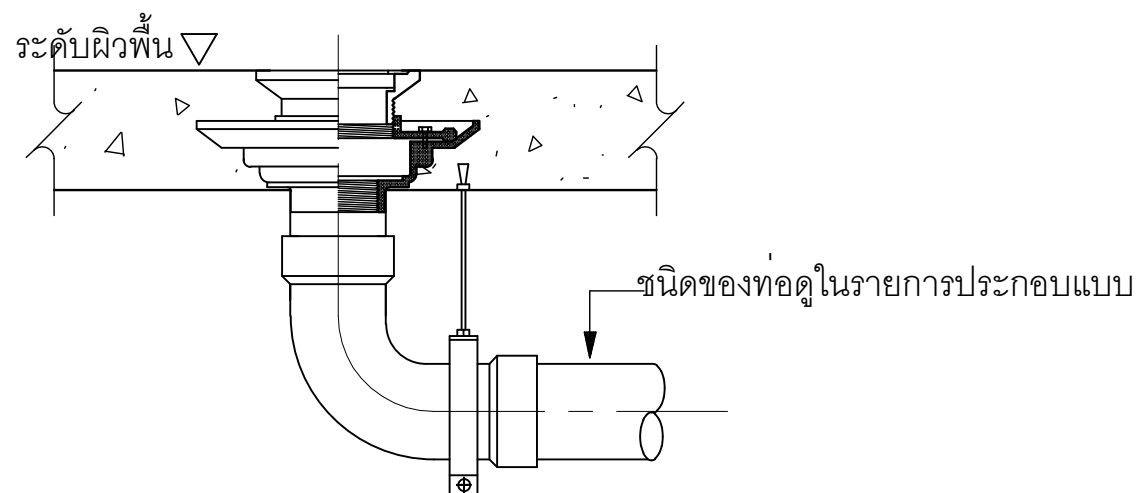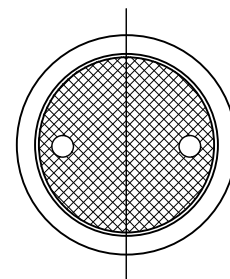


ช่องสำหรับทำความสะอาดท่อที่พื้น (FCO)



แบบบ้านसानฝัน
ของขวัญปีใหม่
คนไทยมีความสุข

แบบ
บ้านห่วงใยไทยประชาสุใจ 1

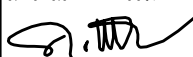สำนักสถาปัตยกรรม
 ผู้อำนวยการสำนัก

สถาปัตยกรรม  สถาปนิก
 สถาปนิก

สำนักวิศวกรรมโครงสร้างและงานระบบ
 ผู้อำนวยการสำนัก

วิศวกรรม  วิศวกร

โครงสร้าง  วิศวกร

วิศวกรรม  วิศวกร

สุขาภิบาล  วิศวกร

วิศวกรรม  วิศวกร

ไฟฟ้า  วิศวกร

วิศวกรรม  วิศวกร

เครื่องกล  วิศวกร


(นายเกียรติศักดิ์ จันทร์ตรา)
วิศวกรใหญ่

อนุมัติ

(นายสมณชาติ สุกประเสริฐ)
อธิบดีกรมโยธาธิการและผังเมือง

แสดงแบบ
แบบขยายการติดตั้งท่อ (แผ่นที่ 3)

มาตราส่วน —

วัน/เดือน/ปี 19/10/59

เลขที่แบบ SN-59025

SN-08 8




๑ |
บ้านห้วยไทยประชาสู่ใจ 1


สารบัญแบบงานระบบไฟฟ้า

สัญลักษณ์งานระบบไฟฟ้า

สารบัญแบบ	แสดงแบบ	สัญลักษณ์	รายละเอียด
EE-01	สารบัญแบบงานระบบไฟฟ้า รายละเอียดข้อกำหนด	⊕	ดวงโคมดาวไลท์ (DOWNLIGHT) ขนาด ๑100 มม. ขอบสีขาว ติดฝังฝ้าเพดาน
EE-02	รายละเอียดแผงเมนสวิตช์		หลอดแอลอีดี ขั้วเกลียว (ขั้ว E27) ขนาด 7 วัตต์ ความสว่างไม่น้อยกว่า 600 ลูเมน
EE-03	แปลนไฟฟ้าแสงสว่าง		
EE-04	แปลนเต้ารับไฟฟ้า	≡	ดวงโคม LED TUBE (T8) แบบเปลือย ติดลอย หลอด 1-10 วัตต์ ความสว่าง 800 ลูเมน
		≡	ดวงโคม LED TUBE (T8) แบบเปลือย ติดลอย หลอด 1-20 วัตต์ ความสว่าง 1,600 ลูเมน
		•	สวิตช์ทางเดียว 16A 250V 1 สวิตช์ พร้อมฝาครอบ PVC ติดฝังเรียบผนังสูงจากพื้น 1.30 ม.
		Ⓜ	กล่องต่อสายสำหรับเครื่องทำน้ำอุ่น ติดฝังเรียบผนังสูงจากพื้น 1.80 เมตร หรือตามความเหมาะสม
		⊖	เต้ารับไฟฟ้าคู่ มีขาติน 16A 250V พร้อมฝาครอบ 3 ช่อง ติดฝังเรียบผนังระดับความสูงตามแบบ
		LP	แผงเมนสวิตช์ ติดผนังสูงจากพื้น 1.80 เมตร ถึงส่วนบนสุด
รายละเอียดข้อกำหนด 1. การติดตั้ง ให้เป็นไปตามมาตรฐานการติดตั้งทางไฟฟ้าสำหรับประเทศไทย ของ วสท. ฉบับล่าสุด 2. ข้อกำหนดการเดินสายไฟฟ้า 2.1 สายวงจรย่อยแสงสว่าง สายแยกจากสวิตช์เข้าดวงโคม และสายระหว่างดวงโคม ใช้สาย IEC 01 ขนาด 2.5 ตร.มม. เดินในท่อร้อยสายอะลูมิเนียมพีวีซี (uPVC) 2.2 สายวงจรย่อยเต้ารับไฟฟ้า และสายระหว่างเต้ารับไฟฟ้า ใช้สาย IEC 01 ขนาด 2.5 ตร.มม. เดินในท่อร้อยสายอะลูมิเนียมพีวีซี (uPVC) 2.3 รหัสสีของสายไฟฟ้า - สายมีเฟ (L) ใช้สายสีน้ำตาล - สายศูนย์ หรือ สายนิวทรัล (N) ใช้สายสีฟ้า - สายดิน (G) ใช้สายสีเขียว 3. รายชื่อตัวอย่างผลิตภัณฑ์วัสดุอุปกรณ์ไฟฟ้า 3.1 แผงเมนสวิตช์ และเซอร์กิตเบรกเกอร์ : ABB, BTICINO, SCHNEIDER, SIEMENS 3.2 ดวงโคมไฟฟ้า : L&E, PHILIPS, SECO, TEI, X-TRA BRITE, VICTOR, WINLIGHT, METROLIGHT 3.3 หลอดไฟฟ้า : OSRAM, PHILIPS, TOSHIBA 3.4 สวิตช์ เต้ารับไฟฟ้า : BTICINO, PANASONIC, SCHNEIDER, SIEMENS 3.5 ท่อร้อยสายไฟฟ้าโลหะ : มอก.770-2533 อาทิ BLUE EGLE, DIAWA, PANASONIC, UI 3.6 ท่อร้อยสายไฟฟ้าอะลูมิเนียมพีวีซีแข็ง : มอก.216-2524 3.7 ท่อร้อยสายไฟฟ้าอะลูมิเนียมเอชดีพีอี (HDPE) : มอก.982-2533 3.8 ท่อร้อยสายไฟฟ้าอะลูมิเนียมพีวีซี (uPVC) : BOSS, CLIPSAL, HACO 3.9 สายไฟฟ้า : มอก.11-2553 BANGKOK CABLE, DRAKA, PHELPS DODGE, THAI YAZAKI S.SUPER CABLE			

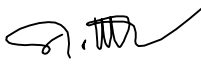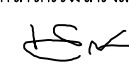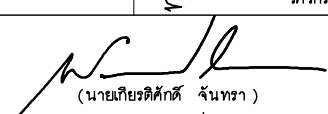

แบบบ้านसानฝัน ของขวัญปีใหม่ คนไทยมีความสุข	
แบบ บ้านห้วยไทยประชาสู่ใจ 1	
สำนักสถาปัตยกรรม  ผู้อำนวยการสำนัก	
สถาปัตยกรรม	สถาปนิก  สถาปนิก
สำนักวิศวกรรมโครงสร้างและงานระบบ  ผู้อำนวยการสำนัก	
วิศวกรรม	วิศวกร 
โครงสร้าง	วิศวกร
วิศวกรรม	วิศวกร 
สุขาภิบาล	วิศวกร
วิศวกรรม	วิศวกร 
ไฟฟ้า	วิศวกร 
วิศวกรรม	วิศวกร 
เครื่องกล	วิศวกร 
 (นายเกียรติศักดิ์ จันทรา) วิศวกรใหญ่	
อนุมัติ  (นายมงคล สดประเสริฐ) อธิบดีกรมโยธาธิการและผังเมือง	
แสดงแบบ สารบัญแบบงานระบบไฟฟ้า สัญลักษณ์งานระบบไฟฟ้า และรายละเอียดข้อกำหนด	
มาตราส่วน —	
วัน/เดือน/ปี 19/10/59	
เลขที่แบบ EE 59048	
EE-01	4

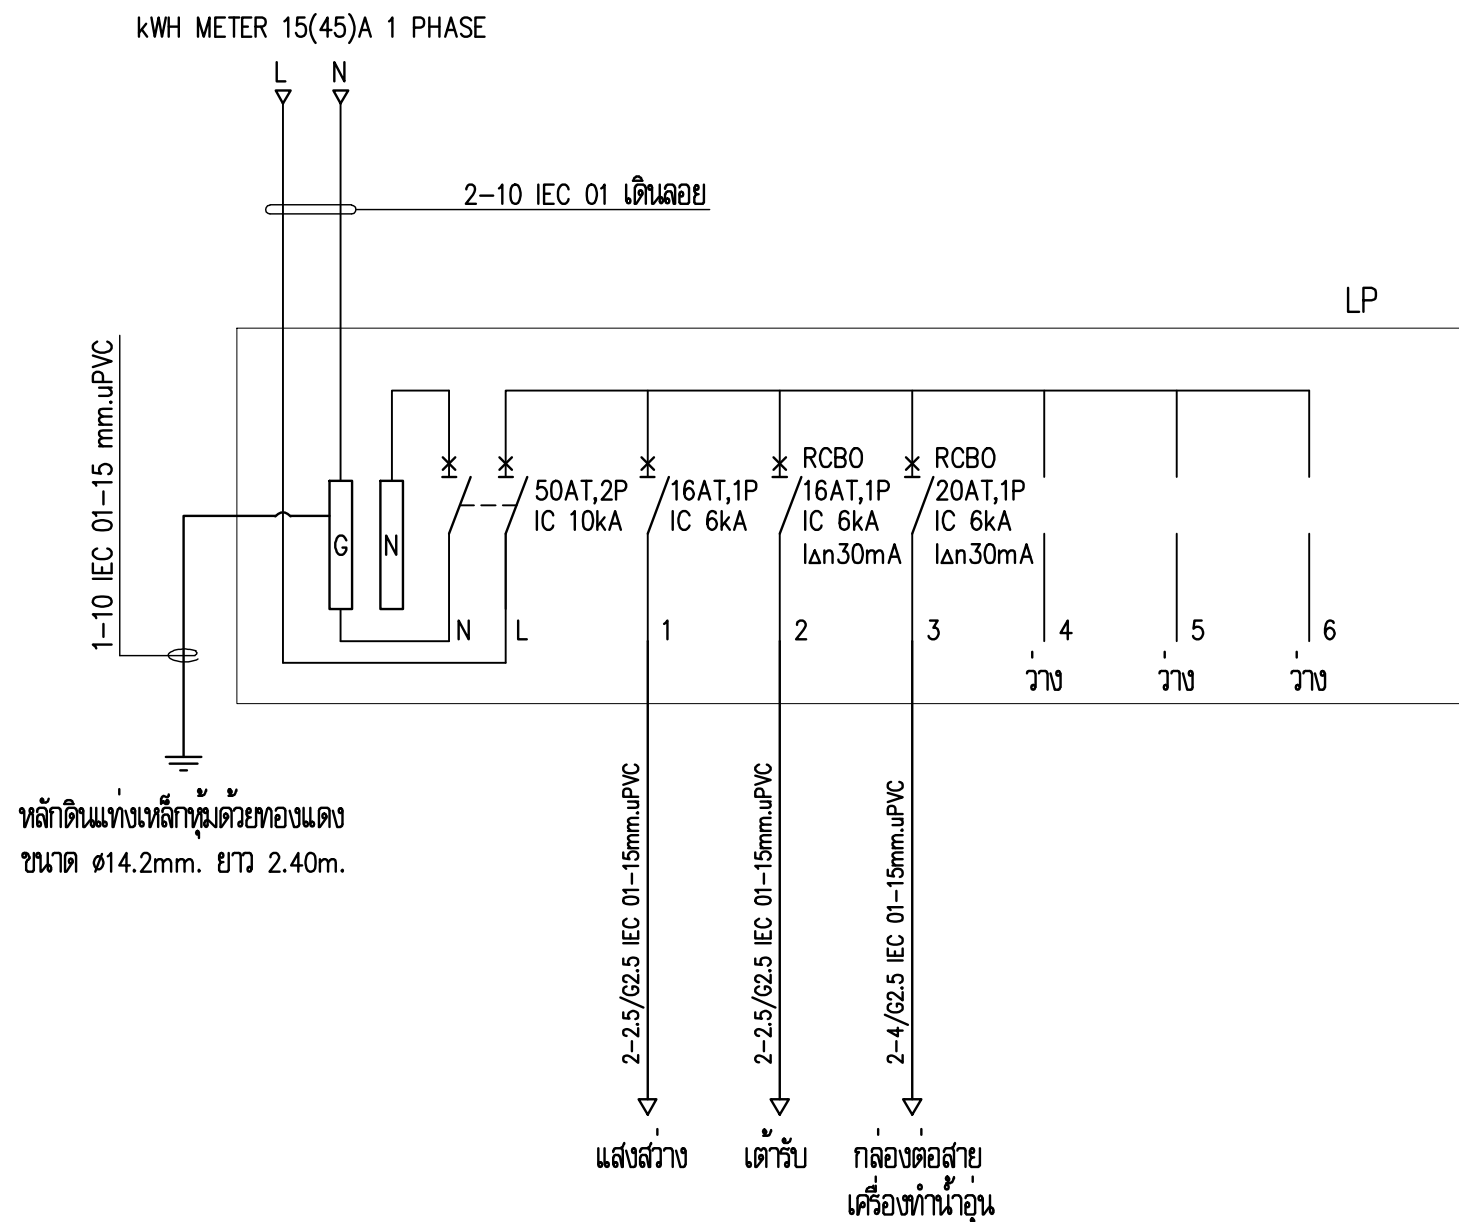

รายละเอียดแผนเมนลวด

หมายเหตุ

-RCBO หมายถึง เซอร์กิตเบรกเกอร์ชนิดมีเครื่องตัดไฟในตัว



แบบบ้านसानฝัน
ของขวัญปีใหม่
คนไทยมีความสุข

แบบ
บ้านห่วงใยไทยประชาสุขใจ 1

สำนักสถาปัตยกรรม
ผู้อำนวยกา

สถาปัตยกรรม
สถาปนิก

สำนักวิศวกรรมโครงสร้างและงานระบบ
ผู้อำนวยกา

วิศวกรรม
วิศวกร

โครงสร้าง
วิศวกร

วิศวกรรม
วิศวกร

สุขาภิบาล
วิศวกร

วิศวกรรม
วิศวกร

ไฟฟ้า
วิศวกร

วิศวกรรม
วิศวกร

เครื่องกล
วิศวกร

(นายเกียรติศักดิ์ จันทรา)
วิศวกรใหญ่

อนุมัติ
(นายมนทล สดประเสริฐ)
อธิบดีกรมโยธาธิการและผังเมือง


แสดงแบบ
รายละเอียดแผนเมนลวด

มาตราส่วน -

วัน/เดือน/ปี 19/10/59

เลขที่แบบ EE 59048

EE-02 4

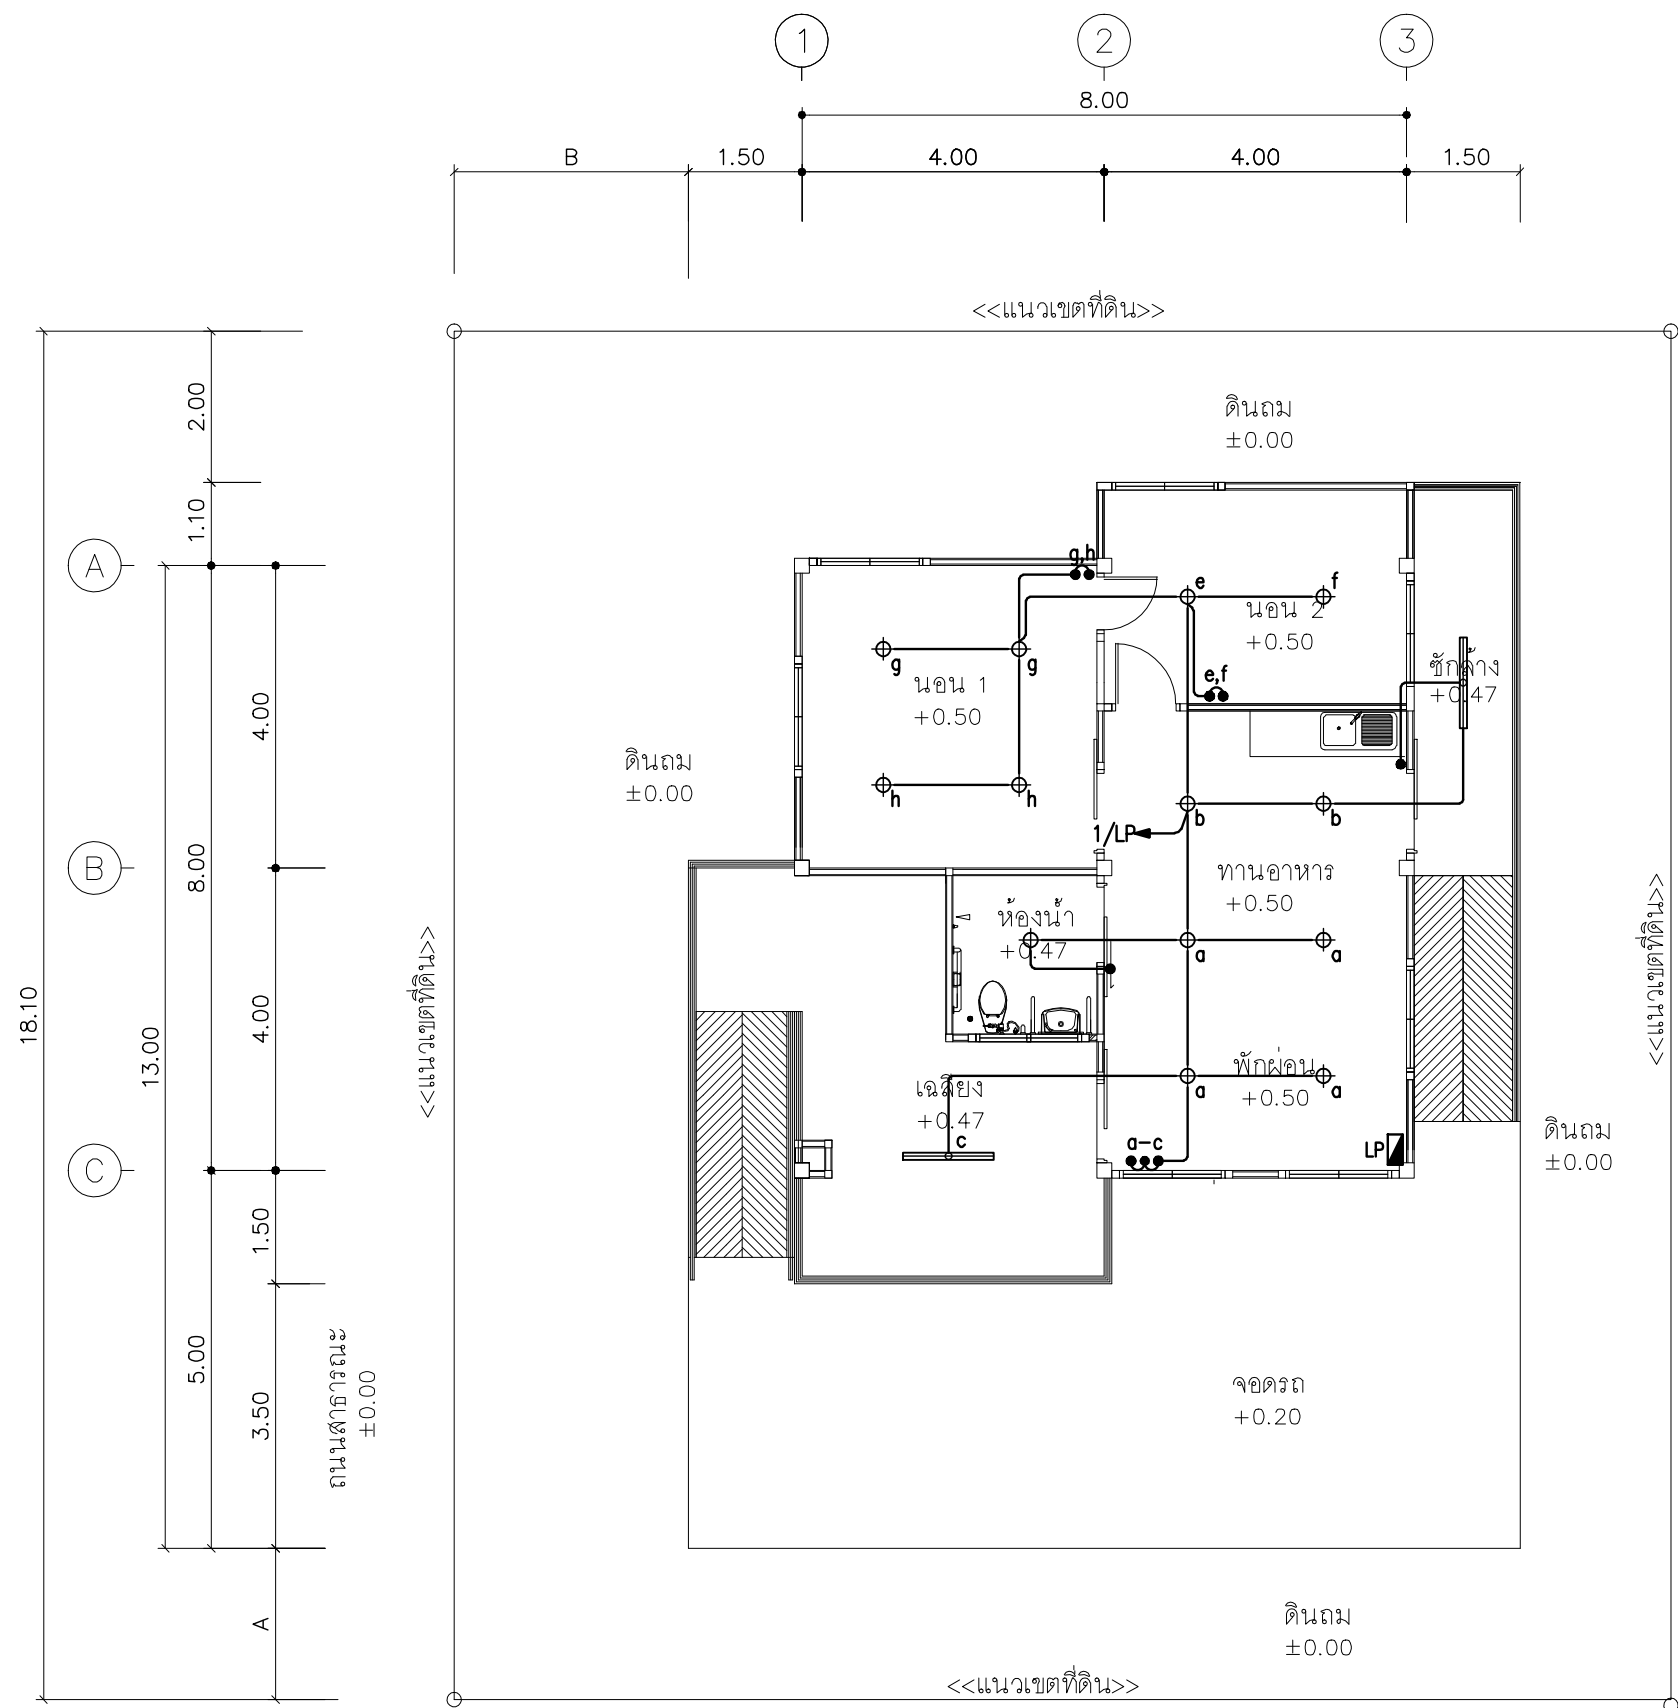

แผนผังไฟฟ้าแสงสว่าง 1:100



แบบบ้านसानฝัน
ของขวัญปีใหม่
คนไทยมีความสุข

แบบ
บ้านห่วงใยไทยประชาสุขใจ 1

สำนักสถาปัตยกรรม
ผู้อำนวยความสะดวก

สถาปัตยกรรม สถาปนิก
สถาปนิก

สำนักวิศวกรรมโครงสร้างและงานระบบ
ผู้อำนวยความสะดวก

วิศวกรรม วิศวกร
โครงสร้าง วิศวกร

วิศวกรรม วิศวกร
สุขาภิบาล วิศวกร

วิศวกรรม วิศวกร
ไฟฟ้า วิศวกร

วิศวกรรม วิศวกร
เครื่องกล วิศวกร

(นายเกียรติศักดิ์ จันทรา)
วิศวกรใหญ่

อนุมัติ
(นายสมเดช สดประเสริฐ)
อธิบดีกรมโยธาธิการและผังเมือง


แสดงแบบ
แปลนไฟฟ้าแสงสว่าง

มาตราส่วน -

วัน/เดือน/ปี 19/10/59

เลขที่แบบ EE 59048

EE-03 4

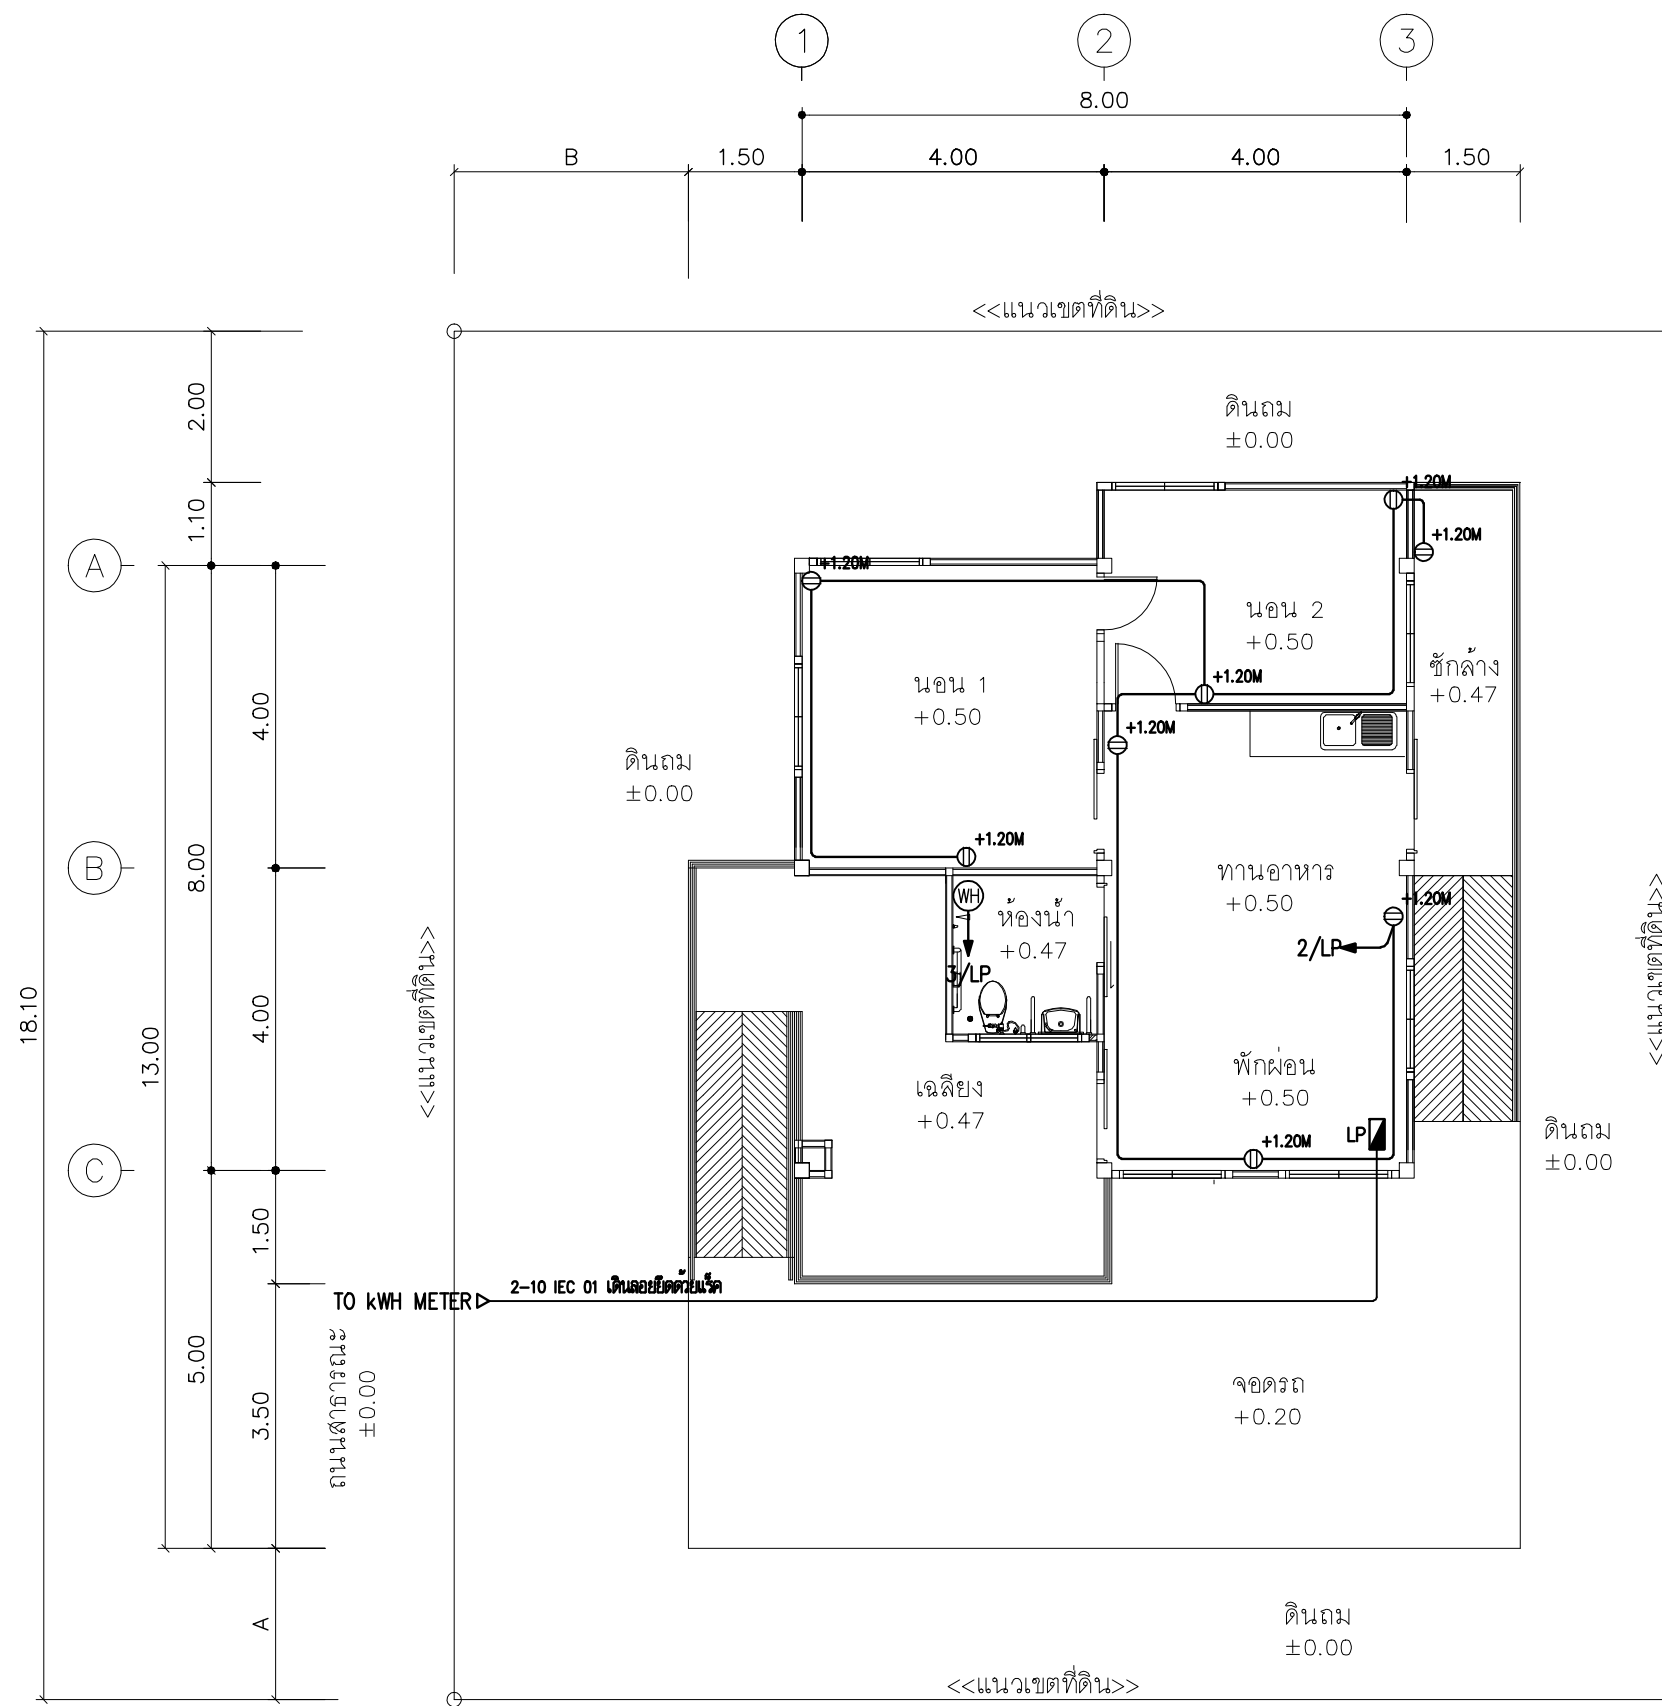

หมายเหตุ

- กรณีต้องการติดตั้งสายโทรศัพท์ภายใน ให้ใช้สายโทรศัพท์ภายในชนิด TIEV 4C-0.65mm เดินท่อร้อยสาย uPVC
- กรณีต้องการติดตั้งสายอากาศทีวีและจานดาวเทียม ให้ใช้สายชนิด RG 6 เดินท่อร้อยสาย uPVC
- กรณีต้องการติดตั้งเครื่องปรับอากาศ ให้ใช้สายไฟดังต่อไปนี้

ขนาด (BTU/hr.)	เซอร์กิตเบรกเกอร์วงจรย่อย	สายไฟฟ้า
ไม่เกิน 12,000	16AT,1P IC 6kA	2-2.5/G2.5 IEC 01-15 mm.uPVC
ไม่เกิน 18,000	20AT,1P IC 6kA	2-2.5/G2.5 IEC 01-15 mm.uPVC

แปลนตัวรับไฟฟ้า 1:100



แบบบ้านसानฝัน
ของขวัญปีใหม่
คนไทยมีความสุข

แบบ
บ้านห่วงใยไทยประชาชนใจ 1

สำนักสถาปัตยกรรม
ผู้อำนวยความสะดวก

สถาปัตยกรรม
สถาปนิก

สำนักวิศวกรรมโครงสร้างและงานระบบ
ผู้อำนวยความสะดวก

วิศวกรรม
วิศวกร

โครงสร้าง
วิศวกร

วิศวกรรม
วิศวกร

สุขาภิบาล
วิศวกร

วิศวกรรม
วิศวกร

ไฟฟ้า
วิศวกร

วิศวกรรม
วิศวกร


เครื่องกล
วิศวกร

แสดงแบบ
แปลนตัวรับไฟฟ้า

มาตราส่วน
วัน/เดือน/ปี 19/10/59

เลขที่แบบ EE 59048

EE-04 4

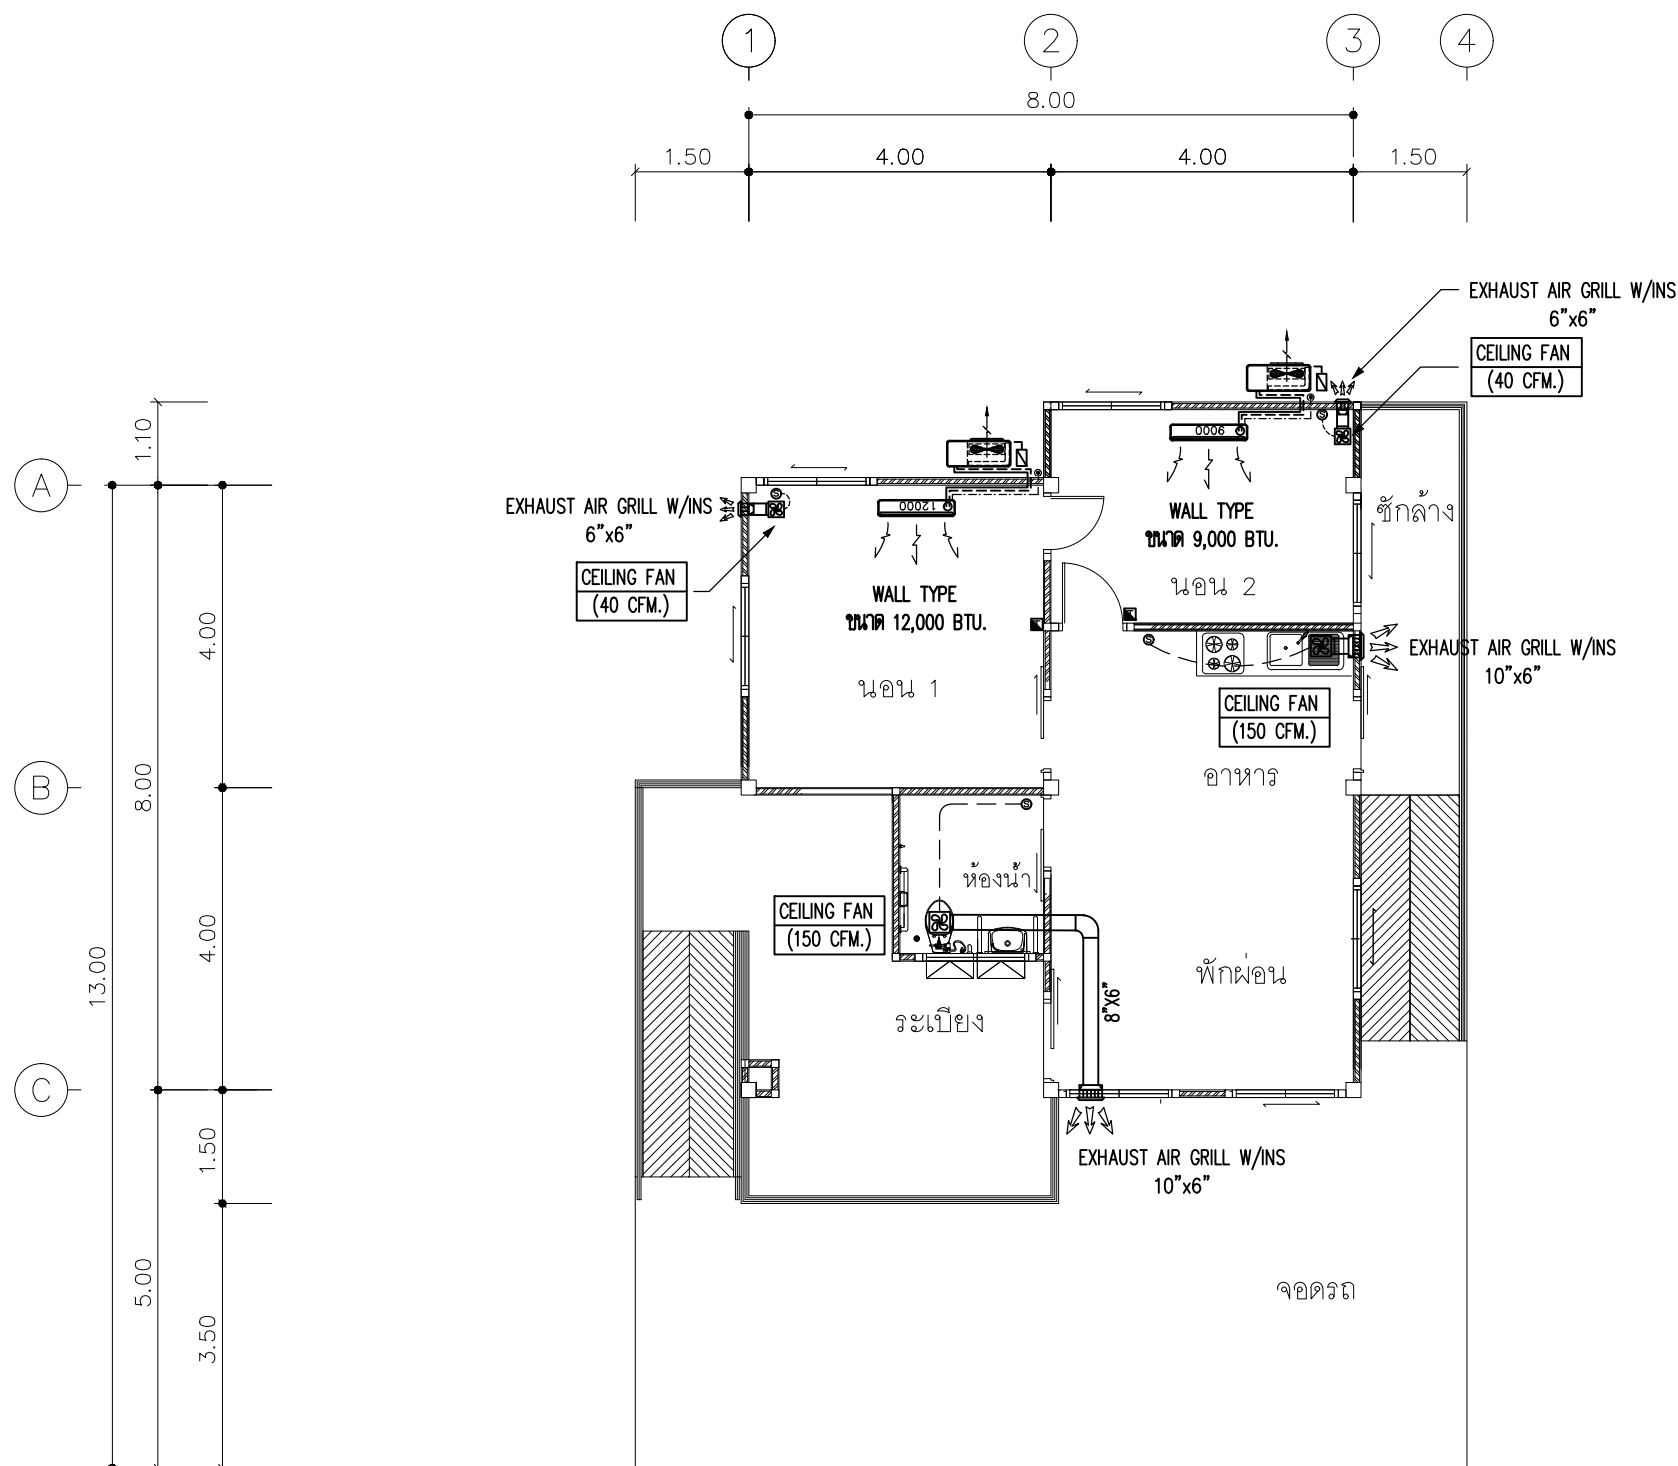

ตำแหน่งติดตั้งเครื่องปรับอากาศและพัดลมระบายอากาศที่แนะนำ ชั้นที่ 1
 มาตรฐาน 1 : 100



แบบบ้านसानฝัน
 ของขวัญปีใหม่
 คนไทยมีความสุข

แบบ
 บ้านห่วงใยไทยประชาสุขใจ 1

สำนักสถาปัตยกรรม
 ผู้อำนวยการสำนัก

สถาปัตยกรรม
 สถาปนิก
 สถาปนิก

สำนักวิศวกรรมโครงสร้างและงานระบบ
 ผู้อำนวยการสำนัก

วิศวกรรม
 วิศวกร
 โครงสร้าง
 วิศวกร

วิศวกรรม
 วิศวกร
 สุขาภิบาล
 วิศวกร

วิศวกรรม
 วิศวกร
 ไฟฟ้า
 วิศวกร

วิศวกรรม
 วิศวกร
 เครื่องกล
 วิศวกร

(นายเกียรติศักดิ์ จันทรา)
 วิศวกรใหญ่

อนุมัติ
 (นายสมชาย สดประเสริฐ)
 อธิบดีกรมโยธาธิการและผังเมือง

แสดงแบบ
 ตำแหน่งติดตั้งเครื่องปรับอากาศ
 และพัดลมระบายอากาศที่แนะนำ
 ชั้นที่ 1

มาตรฐาน 1:100

วัน/เดือน/ปี 19/10/59

เลขที่แบบ M 59030

M-01 1

รายงานปริมาณราคาค่าก่อสร้าง บ้านห่วงใยไทยประชาชน 1 โครงการแบบบ้านเพื่อประชาชน

สถานที่ก่อสร้างทั่วไป

แบบเลขที่ 559041, AR 58237, SN 59025, SN-01 ถึง SN-08, EE 59048, M59030

રાણપ્રકાશભટ્ટ

กองมาตรฐานราคากลาง กรมโยธาธิการและผังเมือง

ประธานาธิบดี

ประมาณการโดย

பா : 3577

[illegible]

5954 บ้านห้วยไทยเประชาสัย โครงการแบบบ้านเพื่อประชาชน

แผ่นที่ 1 / 20

รายงานการศึกษาค่าก่อสร้าง บ้านหลังใหญ่ไทยประชาติขิง 1 โครงการแบบบ้านเพื่อประชาชน

สถานที่ก่อสร้างทั่วไป

แบบเลขที่ S59041 ,AR 58237 ,SN 59025 ,SN-01 ถึง SN-08 ,EE 59048 ,M59030

รายการเลขที่

กองมหาเศรษฐีธนาคารกลาง กรมโยธาธิการและผังเมือง

ประธานาธิบดี

ประมาณการได้

பா : ௩௬௩௩

ลำดับที่	รายการ	จำนวน	หน่วย	ราคาวัสดุ		ค่าแรงงาน		รวมค่าวัสดุ และค่าแรงงาน	หมายเหตุ
				ราคาหน่วยละ	จำนวนเงิน	ราคาหน่วยละ	จำนวนเงิน		
1	หมวดงานโครงสร้าง								
1.1	เสาเข็มเหล็กเหลี่ยมกลาง ขนาด 0.15 ม. ยาว 6.00 ม.	83	ต้น						
1.2	ชุดดิน	35	ลบ.ม.						
1.3	ทรายราดน้ำอัดแน่น	7	ลบ.ม.						
1.4	คอนกรีตหยาบ	1	ลบ.ม.						
1.5	คอนกรีตโครงสร้าง fc' 210 ksc. (ทรงกระบอกที่ 28 วัน)	4	ลบ.ม.						
1.6	คอนกรีตโครงสร้าง fc' 210 ksc. (ทรงกระบอกที่ 28 วัน) เติมน้ำขึ้น	33	ลบ.ม.						
1.7	แบบหล่อคอนกรีต	235	ตร.ม.						
	ค่าแรงแบบหล่อคอนกรีต	294	ตร.ม.						
	ค่าขึ้นแบบหล่อคอนกรีต	70	ลบ.ฟ.						
	เสาตัว	38	ต้น						
1.8	ตะปู	74	กก.						
1.9	เหล็ก SR 24 dia. 6 มม.	419	กก.						
	dia. 9 มม.	906	กก.						
	เหล็ก SD 40 dia. 12 มม.	581	กก.						
	dia. 16 มม.	866	กก.						

รายการประมาณการค่าก่อสร้าง บ้านหลังเยี่ยงพระธาตุขี้เงิน 1 โครงการแบบบ้านเพื่อประชาชน

สถานที่ก่อสร้างทั่วไป

แบบเลขที่ S59041 ,AR 58237 ,SN 59025 ,SN-01 ถึง SN-08 ,EE 59048 ,M59030

การเลือก

กองมาตรฐานราคากลาง กรมโยธาธิการและผังเมือง

พระอภัยมณี

ประมาณการโดย

หน้า : ๓๕๗

[illegible]

5954 บ้านห้วยไทยเประชาสัย โครงการแบบบ้านเพื่อประชาชน

แผ่นที่ 3 / 20

รายการประมาณการค่าก่อสร้าง บ้านหลังเยี่ยงพระธาตุสุโขทัย 1 โครงการแบบบ้านเพื่อประชาชน

สถานที่ก่อสร้างทั่วไป

แบบเลขที่ S59041 ,AR 58237 ,SN 59025 ,SN-01 ถึง SN-08 ,EE 59048 ,M59030

การปลูกพืช

กองมหาเศรษฐีธนาคารกลาง กรมโยธาธิการและผังเมือง

ประธานาธิบดี

ประมาณการโดย

พจน : ๖๕๖๗

[illegible]

รายงานปริมาณราคาค่าก่อสร้าง บ้านหลังใหญ่ไทยประชาชนใบ 1 โครงการแบบบ้านเพื่อประชาชน

สถานที่ก่อสร้างทั่วไป

แบบเลขที่ 559041, AR 58237, SN 59025, SN-01 ถึง SN-08, EE 59048, M59030

รายการเลขที่

กองมาตรฐานราคากลาง กรมโยธาธิการและผังเมือง

ประธานาธิบดี

ประมาณการโดย

เพลง : ธรรม

[illegible]

5954 บ้านห้วยไทยเประชาสัย โครงการแบบบ้านเพื่อประชาชน

แผ่นที่ 5 / 20

รายงานประเมินค่าก่อสร้าง บ้านห่วงใยไทยประชาชน 1 โครงการแบบบ้านเพื่อประชาชน

สถานที่ก่อสร้างทั่วไป

แบบเลขที่ S59041 ,AR 58237 ,SN 59025 ,SN-01 ถึง SN-08 ,EE 59048 ,M59030

รายการเลขที่

กองมหาเศรษฐีธนาคารกลาง กรมโยธาธิการและผังเมือง

ประธานาธิบดี

ประมาณการได้

เพลง : 32 เพลง

[illegible]

ลำดับที่	รายการ	จำนวน	หน่วย	ราคาวัสดุ		ค่าแรงงาน		รวมค่าวัสดุและค่าแรงงาน	หมายเหตุ
				ราคาหน่วยละ	จำนวนเงิน	ราคาหน่วยละ	จำนวนเงิน		
3	งานผนังและตกแต่งผนัง								
	- ผนังก่ออิฐครึ่งแผ่น	173	ตร.ม.						
	- เสาคอนกรีตและเสาเอ็นทับหลัง ค.ส.ล. 0.10x0.10	115	ม.						
	- ฉาบปูนเรียบผนัง	338	ตร.ม.						
	- ฉาบปูนเรียบโครงสร้าง	117	ตร.ม.						
	- ผนังบุกระเบื้องเซรามิค 8"x8"	22	ตร.ม.						
4	งานตกแต่งผิวพื้น								
	- ผิวพื้นปูกระเบื้องเซรามิค 12"x12"	25	ตร.ม.						
	- ผิวพื้นปูไม้ปาร์เก้ ขนาด 1"x4" รวมปูนทรายขัดเรียบ	28	ตร.ม.						
	- ผิวพื้นปูกระเบื้องเซรามิค 8"x8"	33	ตร.ม.						
	- ผิวพื้น ค.ส.ล. ขัดเรียบ	48	ตร.ม.						
	- ผิวพื้นกรวดล้างชะร่อง 1.5 ซม.	9	ตร.ม.						
	- บัวเชิงผนังหนาไม่ไฟเบอร์ซีเมนต์หน้ากว้าง 4" หนา 12 ม.ม.	41	ม.						
	รวมงานข้อ 4								

ลำดับที่	รายการ	จำนวน	หน่วย	ราคาวัสดุ		ค่าแรงงาน		รวมค่าวัสดุและค่าแรงงาน	หมายเหตุ
				ราคาหน่วยละ	จำนวนเงิน	ราคาหน่วยละ	จำนวนเงิน		
5	งานประตูหน้าต่าง								
	- ป 1	2	ชุด						
	- ป 2	1	ชุด						
	- ป 3	1	ชุด						
	- ป 4	1	ชุด						
	- ป 5	1	ชุด						
	- น 1	7	ชุด						
	- น 2	1	ชุด						
	รวมงานข้อ 5								
6	งานสุขภัณฑ์ อุปกรณ์ประกอบห้องน้ำ ห้องส้วม (เคลือบขาว)								
	- โถ้วมนั่งราปพร้อมอุปกรณ์	1	ชุด						
	- อ่างล้างหน้าแบบแขวนผนังพร้อมอุปกรณ์	1	ชุด						
	- ที่ใส่กระดาษชำระ	1	ชุด						
	- ชุดสายฉีดชำระ	1	ชุด						
	- กระจกเงาอย่างดีหนา 5 ม.ม.	7	ตร.ฟ.						
	- ราวแขวนผ้า	1	ชุด						

รายงานปริมาณราคาค่าก่อสร้าง บ้านห่วงใยไทยประชาชน 1 โครงการแบบบ้านเพื่อประชาชน

สถานที่ก่อสร้างทั่วไป

แบบเลขที่ 559041, AR 58237, SN 59025, SN-01 ถึง SN-08, EE 59048, M59030

રાણપ્રકાશભટ્ટ

กองมาตรฐานราคากลาง กรมโยธาธิการและผังเมือง

ประธานาธิบดี

นาง : ดิฉัน

กรมการที่ดิน

[illegible]

5954 บ้านห้วยไทรไทยประชาสุขใจ โครงการแบบบ้านเพื่อประชาชน

แผ่นที่ 9 / 20

รายงานการศึกษาค่าก่อสร้าง บ้านหลังใหญ่ไทยประชาติขิง 1 โครงการแบบบ้านเพื่อประชาชน

สถานที่ก่อสร้างทั่วไป

แบบเลขที่ S59041 ,AR 58237 ,SN 59025 ,SN-01 ถึง SN-08 ,EE 59048 ,M59030

รายการเลขที่

กองมหาเศรษฐีธนาคารกลาง กรมโยธาธิการและผังเมือง

ประธานาธิบดี

ស្រុក : បា

กรมการปกครอง

ลำดับที่	รายการ	จำนวน	หน่วย	ราคาวัสดุ		ค่าแรงงาน		รวมค่าวัสดุและค่าแรงงาน	หมายเหตุ
				ราคาหน่วยละ	จำนวนเงิน	ราคาหน่วยละ	จำนวนเงิน		
8	งานบัดเตล็ด								
	- ราวกันตก สแตนเลส	29	ม.						
	- ระแนงเหล็กบั้งแดด	7	ตร.ม.						
รวมงานข้อ 8									

รายงานปริมาณการคาดการณ์ค่าก่อสร้าง บ้านหนึ่งเยื้องประเทศไทยประจำปี 1 โครงการแบบบ้านเพื่อประชาชน

สถานที่ก่อสร้างทั่วไป

แบบเลขที่ 559041, AR 58237, SN 59025, SN-01 ถึง SN-08, EE 59048, M59030

នាយករដ្ឋមន្ត្រី

กองมาตรฐานราคากลาง กรมโยธาธิการและผังเมือง

พระอภัยมณี

ประมาณการโดย

นาง : ๒๕๗๗

[illegible]

5954 บ้านห้วยไทยเประชาสัย โครงการแบบบ้านเพื่อประชาชน

แผ่นที่ 11 / 20

รายการประมาณการค่าก่อสร้าง บ้านหลังเยี่ยงพระธาตุสุโขทัย 1 โครงการแบบบ้านเพื่อประชาชน

สถานที่ก่อสร้างทั่วไป

แบบเลขที่ 559041, AR 58237, SN 59025, SN-01 ถึง SN-08, EE 59048, M59030

રાણપ્રકાશભટ્ટ

กองมหาเศรษฐีธนาคารกลาง กรมโยธาธิการและผังเมือง

ประธานาธิบดี

ประมาณการโดย

ហេតុ : ១៥៧

ลำดับที่	รายการ	จำนวน	หน่วย	ราคาวัสดุ		ค่าแรงงาน		รวมค่าวัสดุ และค่าแรงงาน	หมายเหตุ
				ราคาหน่วยละ	จำนวนเงิน	ราคาหน่วยละ	จำนวนเงิน		
1	ระบบท่อน้ำโพลีเอทิลีน ท่อน้ำทิ้ง ท่ออากาศ								
1.1	งานเดินท่อน้ำโพลีเอทิลีน ท่อน้ำทิ้ง ท่ออากาศ (ท่อ PVC 8.5)								
	- ขนาด Dia. 2"	24	เมตร						
	- ขนาด Dia. 4"	12	เมตร						
1.2	ข้อต่อ ข้องอ สวมทาง	1	lot						
1.3	FCO								
	- ขนาด Dia. 2"	1	ชุด						
	- ขนาด Dia. 4"	1	ชุด						
1.4	FD. ขนาด Dia. 2"	1	ตัว						
1.5	AVC . ขนาด Dia. 2"	1	ชุด						
1.6	ข้อต่ออ่อนยางแวนรืดสแตนเลส								
	- ขนาด Dia. 2"	4	ชุด						
	- ขนาด Dia. 4"	2	ชุด						
	ยอดรวมตามข้อ 1								

รายการประมาณการค่าก่อสร้าง บ้านหลังเยี่ยงพระธาตุขี้เงิน 1 โครงการแบบบ้านเพื่อประชาชน

สถานที่ก่อสร้างทั่วไป

แบบเลขที่ 559041, AR 58237, SN 59025, SN-01 ถึง SN-08, EE 59048, M59030

នាយករដ្ឋមន្ត្រី

กองมาตรฐานราคากลาง กรมโยธาธิการและผังเมือง

ประเทศไทย

ประมาณการโดย

นาง : ดิฉัน

[illegible]

5954 บ้านห้วยไทรไทยประชาสุขใจ โครงการแบบบ้านเพื่อประชาชน

แผ่นที่ 13 / 20

รายการประมาณการค่าก่อสร้าง บ้านหลังเยี่ไทยประชูปละข้อที่ 1 โครงการแบบบ้านเพื่อประชาชน

สถานที่ก่อสร้างทั่วไป

แบบเลขที่ 559041, AR 58237, SN 59025, SN-01 ถึง SN-08, EE 59048, M59030

રાણપ્રકાશભટ્ટ

กองมหาเศรษฐีธนาคารกลาง กรมโยธาธิการและผังเมือง

ประธานาธิบดี

ประมาณการโดย

ហេតុ : ព្រឹត្តិ

[illegible]

รายการประมาณการค่าก่อสร้าง บ้านหลังเยี่ยงพระธาตุขี้เงิน 1 โครงการแบบบ้านเพื่อประชาชน

สถานที่ก่อสร้างทั่วไป

แบบเลขที่ 559041, AR 58237, SN 59025, SN-01 ถึง SN-08, EE 59048, M59030

รายการเลขที่

กองมาตรฐานราคากลาง กรมโยธาธิการและผังเมือง

พระอภัยมณี

ประมาณการโดย

หน้า : ๑๕๗

[illegible]

5954 บ้านห้วยไทยเประชาสัย โครงการแบบบ้านเพื่อประชาชน

แผ่นที่ 15 / 20

รายการประมาณการค่าก่อสร้าง บ้านหลังเยี่ยงพระธาตุสุโขทัย 1 โครงการแบบบ้านเพื่อประชาชน

สถานที่ก่อสร้างทั่วไป

แบบเลขที่ 559041,AR 58237,SN 59025,SN-01 ถึง SN-08,EE 59048,M59030

รายการเลขที่

กองมหาเศรษฐีธนาคารกลาง กรมโยธาธิการและผังเมือง

ประธานาธิบดี

ประมาณการโดย

ประเภท : วรรณคดี

[illegible]

ลำดับที่	รายการ	จำนวน	หน่วย	ราคาวัสดุ		ค่าแรงงาน		รวมค่าวัสดุและค่าแรงงาน	หมายเหตุ
				ราคาหน่วยละ	จำนวนเงิน	ราคาหน่วยละ	จำนวนเงิน		
4.1.1	แผงย่อยและ เซอร์กิตเบรกเกอร์ LP								
	- แผงย่อย 6 ช่อง พร้อมเมน 50AT 2P IC10kA	1	Set						
	- Miniaiture CB 20AT 1P IC6kA	2	Set						
	- Miniaiture CB 16AT 1P IC6kA	1	Set						
	- Miniaiture CB RCBO 1 n30mA 16AT 1P IC6kA	1	Set						
	- GROUND SYSTEM	1	Set						
	- KILOWATT HOUR METER 15(45)A 1 PHASE	1	Set						
	\\ รวมแผงย่อยและ เซอร์กิตเบรกเกอร์								
4.1.2	ท่อร้อยสาย และรางเดินสายไฟฟ้า								
	- uPVC 1/2" (15 mm.)	136	m						
	- FITTING & SUPPORT & ACCESSORIES	1	Lot						
	\\ รวมท่อร้อยสาย และรางเดินสายไฟฟ้า								

ลำดับที่	รายการ	จำนวน	หน่วย	ราคาวัสดุ		ค่าแรงงาน		รวมค่าวัสดุและค่าแรงงาน	หมายเหตุ
				ราคาหน่วยละ	จำนวนเงิน	ราคาหน่วยละ	จำนวนเงิน		
4.1.3	สายไฟฟ้า								
	- IEC 01 10 SQ.MM.	35	m						
	- IEC01 2.5 SQ.MM.	360	m						
	- ACCESSORIES	1	Lot						
	\\ รวมสายไฟฟ้า								
4.1.4	ดวงโคมพรอมอุปกรณ์								
	- ดวงโคมดาวไลน์ (DOWNLIGHT) ขนาด Ø100 มม. ขอบสีขาว ติดฝังฝ้าเพดาน	13	Set						
	หลอดแอลอีดี ชั่วถาวร (ชื่อ E27) ขนาด 7-7.5 วัตต์ ความสว่างไม่น้อยกว่า 600 ลูเมน								
	- ดวงโคมฟลูออเรสเซนต์แบบเปลือย ติดลอย หลอด 1-36 วัตต์ ความสว่างไม่น้อยกว่า 2,600 ลูเมน	2	Set						
	\\ รวมดวงโคมพรอมอุปกรณ์								

รายงานปริมาณราคาค่าก่อสร้าง บ้านหลังใหญ่ไทยประชาชนใบ 1 โครงการแบบบ้านเพื่อประชาชน

สถานที่ก่อสร้างทั่วไป

กองมาตรฐานราคากลาง กรมโยธาธิการและผังเมือง

ประมาณการโดย

แบบเลขที่ 559041, AR 58237, SN 59025, SN-01 ถึง SN-08, EE 59048, M59030

รายการเว็บไซต์

ประเทศไทย

ประเภท : บทกวี

[illegible]

5954 บ้านห้วยไผ่ไทยประชาสุขใจ โครงการแบบบ้านเพื่อประชาชน

แผ่นที่ 19 / 20

54

รายงานประเมินค่าก่อสร้าง บ้านห่วงใยไทยประชาชนชุดที่ 1 โครงการแบบบ้านเพื่อประชาชน

สถานที่ก่อสร้างทั่วไป

กองมาตรฐานราคากลาง กรมโยธาธิการและผังเมือง

ประมาณการได้

แบบเลขที่ 559041 ,AR 58237 ,SN 59025 ,SN-01 ถึง SN-08 ,EE 59048 ,M59030

รายการเลือก

ประเภทวิชาเศรษฐศาสตร์

ประเภท : ๓๕๓

[illegible]

5954 บ้านห้วยไทยประชาสุขใจ โครงการแบบบ้านเพื่อประชาชน

แผ่นที่ 20 / 20

หลักเกณฑ์และข้อกำหนดในผังบริเวณประกอบการขออนุญาตก่อสร้างอาคาร

สำหรับอาคารพักอาศัยประเภทบ้านเดี่ยว ไม่เกิน 2 ชั้น

1. ผังบริเวณ

ต้องแสดงลักษณะที่ตั้ง ขอบเขตที่ดิน ขอบนอกของอาคารที่มีอยู่แล้ว ระยะห่างระหว่างจากขอบนอกของอาคารถึงเขตที่ดินทุกด้าน ระยะห่างระหว่างอาคารต่างๆที่มีอยู่แล้ว และที่ขออนุญาตในขอบเขตที่สาธารณะอาคารในที่ดินข้างเคียง และแสดงทางระบายน้ำออกจากอาคารไปสู่ทางระบายน้ำสาธารณะ พร้อมทิศทางน้ำไหลและส่วนลาด

2. บ่อเกรอะ บ่อซึม

- ต้องอยู่ห่างจากแม่น้ำ คู คลอง หรือแหล่งน้ำสาธารณะไม่น้อยกว่า 10 เมตร
- บ่อเกรอะต้องมีลักษณะที่มีดซิดน้ำซึมผ่านไม้ได้

3. ทางระบายน้ำ

ทางระบายน้ำจากอาคารสู่แหล่งรองรับน้ำทั้งต้องสามารถตรวจสอบได้ และมีส่วนลาดเอียงไม่ต่ำกว่า 1 ใน 200 ถ้าเป็นท่อปิดต้องมีเส้นผ่านศูนย์กลางภายในไม่น้อยกว่า 10 เซนติเมตร มีบ่อพักทุกมุมเลี้ยวและทุกระยะไม่เกิน 12 เมตร หรือทุกระยะไม่เกิน 24 เมตร ถ้าท่อปิดมีเส้นผ่านศูนย์กลางภายในตั้งแต่ 60 เซนติเมตรขึ้นไป ถ้าเป็นทางระบายน้ำแบบอื่นต้องมีความกว้างภายในที่ขอบบนสุดไม่น้อยกว่า 10 เซนติเมตร

4. ที่ว่างปราศจากสิ่งปกคลุม

ต้องมีที่ว่างปราศจากสิ่งปกคลุมไม่น้อยกว่า 30 ใน 100 ส่วนของพื้นที่ชั้นที่มากที่สุด เว้นแต่ถ้าไม่ได้ใช้พักอาศัยให้มีที่ว่างไม่น้อยกว่า 10 ใน 100 ส่วน

5. แนวร่นของอาคาร

5.1 กรณีก่อสร้างอาคารใกล้ถนนสาธารณะ

สำหรับบ้านเดี่ยวสูงไม่เกิน 2 ชั้น

- ถ้าถนนสาธารณะกว้างน้อยกว่า 6 เมตร ให้ร่นแนวอาคารห่างจากกึ่งกลางถนนสาธารณะอย่างน้อย 3 เมตร - ถ้าถนนสาธารณะกว้างตั้งแต่ 10 เมตรขึ้นไปแต่ไม่ถึง 20 เมตร ให้ร่นแนวอาคารห่างจากกึ่งกลางถนนสาธารณะอย่างน้อย 1 ใน 10 ของความกว้างของถนนนั้น
- ถ้าถนนสาธารณะกว้างตั้งแต่ 20 เมตรขึ้นไป ให้ร่นแนวอาคารห่างจากเขตถนนสาธารณะอย่างน้อย 2 เมตร

5.2 กรณีก่อสร้างอาคารใกล้แหล่งน้ำสาธารณะ

- ถ้าแหล่งน้ำสาธารณะกว้างน้อยกว่า 10 เมตร ให้ร่นแนวอาคารจากแหล่งน้ำสาธารณะไม่น้อยกว่า 3 เมตร
- ถ้าแหล่งน้ำสาธารณะกว้างตั้งแต่ 10 เมตรขึ้นไป ให้ร่นแนวอาคารจากเขตแหล่งน้ำสาธารณะไม่น้อยกว่า 6 เมตร
- ถ้าเป็นแหล่งน้ำขนาดใหญ่ เช่น บึง ทะเลสาบ หรือทะเล ให้ร่นแนวอาคารจากเขตแหล่งน้ำสาธารณะไม่น้อยกว่า 12 เมตร

6. ความสูงของอาคาร

ความสูงของอาคารที่จุดใดๆ ต้องไม่เกินสองเท่าของระยะราบจากจุดนั้นไปตั้งฉากกับแนวเขตด้านตรงข้ามของถนนสาธารณะที่อยู่ใกล้อาคารที่สุด

7. ระยะห่างของอาคารกับเขตพื้นดิน กรณีผนังอาคารมีประตู หน้าต่าง ช่องระบายอากาศ ช่องแสงหรือระเบียง

7.1 ผนังอาคารส่วนที่สูงไม่เกิน 9 เมตร ต้องอยู่ห่างเขตที่ดินไม่น้อยกว่า 2 เมตร

7.2 ผนังอาคารส่วนที่สูงเกิน 9 เมตร แต่ไม่เกิน 23 เมตร ต้องอยู่ห่างเขตที่ดินไม่น้อยกว่า 3 เมตร

8. ระยะห่างของอาคารกับเขตที่ดิน กรณีผนังทึบ

ต้องอยู่ห่างเขตที่ดินไม่น้อยกว่า 50 เซนติเมตร เว้นแต่จะก่อสร้างชิดเขตที่ดินโดยได้รับความยินยอมเป็นหนังสือจากเจ้าของที่ดินด้านนั้น และสร้างได้สูงไม่เกิน 15 เมตร

9. การก่อสร้างอาคารใกล้อาคารอื่นในที่ดินเจ้าของเดียวกัน

9.1 ผนังของอาคารด้านที่มีหน้าต่าง ประตู ช่องระบายอากาศหรือช่องแสง หรือระเบียงของอาคารต้องมีระยะห่างจากผนังของอาคารอื่นด้านที่มีหน้าต่าง ประตู ช่องระบายอากาศหรือช่องแสง หรือระเบียงของอาคาร ดังต่อไปนี้

(ก) อาคารที่มีความสูงไม่เกิน 9 เมตร ผนังหรือระเบียงของอาคารต้องอยู่ห่างจากผนัง หรือระเบียงของอาคารอื่นที่มีความสูงไม่เกิน 9 เมตร ไม่น้อยกว่า 4 เมตร

(ข) อาคารที่มีความสูงไม่เกิน 9 เมตร ผนังหรือระเบียงของอาคารต้องอยู่ห่างจากผนัง หรือระเบียงของอาคารอื่นที่มีความสูงเกิน 9 เมตร แต่ไม่ถึง 23 เมตร ไม่น้อยกว่า 5 เมตร

(ค) อาคารที่มีความสูงเกิน 9 เมตร แต่ไม่ถึง 23 เมตร ผนังหรือระเบียงของอาคารต้องอยู่ห่างจากผนังหรือระเบียงของอาคารอื่นที่มีความสูงเกิน 9 เมตร แต่ไม่ถึง 23 เมตร ไม่น้อยกว่า 6 เมตร

9.2 ผนังของอาคารด้านที่เป็นผนังทึบต้องมีระยะห่างจากผนังของอาคารอื่นด้านที่มีหน้าต่าง ประตู ช่องระบายอากาศหรือช่องแสง หรือระเบียงของอาคาร ดังต่อไปนี้

(ก) อาคารที่มีความสูงไม่เกิน 15 เมตร ผนังของอาคารต้องอยู่ห่างจากผนังหรือระเบียงของอาคารอื่นที่มีความสูงไม่เกิน 9 เมตร ไม่น้อยกว่า 2 เมตร

(ข) อาคารที่มีความสูงไม่เกิน 15 เมตร ผนังของอาคารต้องอยู่ห่างจากผนังหรือระเบียงของอาคารอื่นที่มีความสูงเกิน 9 เมตร แต่ไม่ถึง 23 เมตร ไม่น้อยกว่า 3 เมตร

10. การขออนุญาตก่อสร้างในเขตสภาพตำบลหรือเขตองค์การบริหารส่วนตำบล

แต่ไม่อยู่ในบริเวณพื้นที่ห้ามก่อสร้างอาคารบางชนิดตามกฎหมายว่าด้วยการควบคุมอาคาร ถ้าเป็นอาคารอยู่อาศัยไม่เกิน 2 ชั้นที่มีพื้นที่ไม่เกิน 150 ตารางเมตร หรือรั้ว กำแพง ประตู ในแบบเฉพาะแผนผังบริเวณ และสำเนาเอกสารสิทธิในที่ดินพร้อมคำขอ

หลักเกณฑ์เพิ่มเติมสำหรับการขออนุญาตก่อสร้างในเขตกรุงเทพมหานคร

1. ที่ว่างรอบอาคาร

- บ้านพักอาศัยที่มีพื้นที่เกิน 300 ตารางเมตร ที่สูงไม่เกิน 15 เมตร ต้องมีที่ว่างโดยรอบอาคารไม่น้อยกว่า 1 เมตร

คณะผู้จัดทำโครงการแบบบ้านसानฝัน ของขวัญปีใหม่ คนไทยมีความสุข

ที่ปรึกษา

๑. นายมณฑล สุตประเสริฐ อธิบดีกรมโยธาธิการและผังเมือง
๒. นายเกียรติศักดิ์ จันทรา วิศวกรใหญ่
๓. นางสาวศิริภา วาระเลิศ รองอธิบดีกรมโยธาธิการและผังเมือง
๔. นายโอฬาร ศักย์โรจน์กุล รองอธิบดีกรมโยธาธิการและผังเมือง
๕. นายสมชาย เมธวัฒน์ธรากุล รองอธิบดีกรมโยธาธิการและผังเมือง
๖. นายพิชัย อุทัยเชษฐา รองอธิบดีกรมโยธาธิการและผังเมือง

คณะทำงานกำกับดูแล

๑. นายคธาทิพย์ เอี่ยมกมลลา
๒. นายเสถียร เจริญเหรียญ
๓. นายอิทธิราช กนกเวชยันต์
๔. นายสุธี ปิ่นไพลี
๕. นายวิจิต อรุณมานะกุล
๖. นายสุเทพ พิทักษ์พรมงคล
๗. นายนภดล สวาสต์ญาติ
๘. นายชาญวิทย์ สิริสุนทรานนท์
๙. นายดุขฎิ เจริญลาภ
๑๐. นายจิรศักดิ์ ภู่วิไลวัฒน์กิจ
๑๑. นายพีรพงศ์ จันทรา
๑๒. นายวิรัชต์ ทองรวย
๑๓. นายกนก สุจริตสัณชัย
๑๔. นายนิเวศน์ ลำเลิศลักษณ์ชัย
๑๕. นายสมชาติ จิตใหญ่
๑๖. นายสุนทร น้ำเพชร

คณะทำงานออกแบบและประมาณราคา

สำนักสถาปัตยกรรม

๑. นายสุภาพ เนถาวร
๒. นายถิรวิทย์ เทพไชย
๓. นางสาวนิติมา คุดตะสิงคี
๔. นางสาวพิมพ์สิริ เหมโสกะณะ
๕. นางสาวอารียา ศุภโชคพาณิชย์
๖. นางสาววรมน แสนชมภู
๗. นางสาวจุฑารัตน์ โชติเวทย์ศิลป์
๘. นายภูวณัฐ คงสมโอษฐ์
๙. นางสาวพรรณวรรณ สุขทรศนี
๑๐. นายปกรณ์ อินทะกนก

สำนักวิศวกรรมโครงสร้างและงานระบบ

๑. นางสาวอดิษฐ์ สิ้นศิลาเกตุ
๒. นายวัชรินทร์ เกิดบุญชู
๓. นายอรชาติ พาชีศรีพาพล
๔. นายสรพงษ์ พันคง
๕. นายณัฐพงษ์ พรสง่า
๖. นายอาทิตย์พร พรสุทธาวงศ์
๗. นายพงศ์พันธ์ พรหมจันทร์

กองมาตรฐานราคากลาง

๑. นายวรสันต์ อิฐรัตน์
๒. นายวิโรจน์ ส่งสกุลชัย
๓. นายสุรพล กุหลาบศรี
๔. นายสุบรรณ วงศ์คำจันทร์
๕. นายสุรัช สิริโกชนพาณิชย์
๖. นายเลิศศักดิ์ จงธรรม
๗. นายธรรมบุญ คุ่มภัย
๘. นายธนดล อยู่สำราญ
๙. นายปิติ นีซัง
๑๐. นายมานะชัย ศรสุรินทร์
๑๑. นายอรรถกร พันปี
๑๒. นายศราวุธ น้อยสุวรรณ
๑๓. นายจตุพล อินทร
๑๔. นายพุดตาล น้อยวัน
๑๕. นายวินิจ เรือนแก้ว
๑๖. นายศรัณย์ สุขเกิด
๑๗. นายวีรภัทร ว่องไว
๑๘. นางสาวกรพินธ์ คชินทร

คณะทำงานประสานงาน

๑. นางสาวสุภัทรา ชัยเทวารัณย์
๒. นางภัททิรา สุริวรรณ


พิมพ์ครั้งที่ ๓ : ตุลาคม ๒๕๕๙

พิมพ์ที่ : ศูนย์สื่อและสิ่งพิมพ์แก้วเจ้าจอม มหาวิทยาลัยราชภัฏสวนสุนันทา

แบบบ้านसानฟัน ของขวัญปีใหม่ คนไทยมีความสุข

กรมโยธาธิการและผังเมือง กระทรวงมหาดไทย

บ้านห่วงใยไทยประชาชนใจ แบบที่ ๑

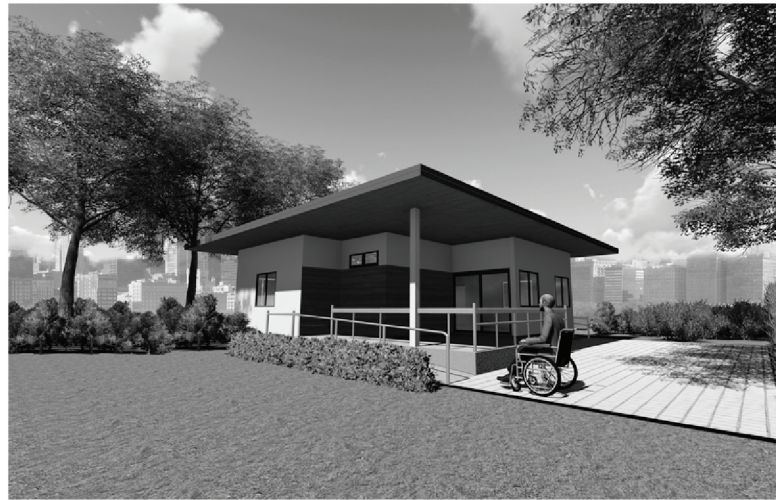

ขนาด ๘๐ ตร.ม
ฐานรากเสาเข็ม ๑,๒๔๒,๐๐๐ บาท

บ้านห่วงใยไทยประชาชนใจ แบบที่ ๒



ขนาด ๙๐ ตร.ม
ฐานรากเสาเข็ม ๑,๓๒๔,๐๐๐ บาท

แบบบ้านसानฟัน ของขวัญปีใหม่ คนไทยมีความสุข

กรมโยธาธิการและผังเมือง กระทรวงมหาดไทย

บ้านห่วงใยไทยประสาสุขใจ แบบที่ ๑



บ้านห่วงใยไทยประสาสุขใจ แบบที่ ๒

