



ตามนโยบายของ
หม่อมราชวงศ์สุขุมพันธุ์ บริพัตร
ผู้ว่าราชการกรุงเทพมหานคร
โดย สำนักการโยธา



แบบบ้านยืม... เพื่อประชาชน

100 แบบบ้านมาตรฐาน...
สวย ดี โดนใจ...
พร้อมปลูกสร้างได้ทันที

ห้ามพลาด!!! โอกาส...
ยืมรับ... บ้านใหม่
แบบ **บ้านสวย**
เลือกได้
ใน “โครงการแบบบ้านยืม...เพื่อประชาชน”

แบบ 100 แบบบ้าน
มาตรฐาน...
สวย ดี โดนใจ
พร้อมปลูก
สร้างได้ทันที
มีให้เลือก
หลากหลาย
ตอบสนอง
ทุกไลฟ์สไตล์คนเมือง

ภัทรวรรณ

ด้วยความอนุเคราะห์แบบจาก
บริษัท แลนด์ โฮม (ประเทศไทย) จำกัด

รายการประกอบแบบก่อสร้าง TYPE "M"



รายการประกอบแบบทั่วไป

- โครงสร้างบ้านทำด้วยไม้เป็นคอนกรีตเสริมเหล็กหล่อในที่ คือ เสา ฐานราก, เสา, คาน, พื้นชั้นล่าง - บน เป็นพื้น - สำเร็จรูป บางส่วนหล่อในที่ ขนาด และ รายละเอียด ตามแบบวิศวกรรม
- เสาชั้นบ้าน 2 ชั้น ใช้คอนกรีตอัดแรง รูปตัว I - 18 X 18 ซม ยาว 16 ม กระเบื้องบ้าน 2 ชั้น จะใช้เสาเข็มตาม - การคำนวณของวิศวกร
- หลังคา โครงหลังคาเหล็กรูปทรงม ทาดีกัลนิม TOA 2 ชั้น พร้อมฉนวนกันความร้อน 1 ชั้น มุงด้วยกระเบื้อง CPAC MONIER สีมาตรฐานบริษัท หรือ เทียบเท่า
- ผนังทั่วไปใช้อิฐมวลเบา จากปูนซีเมนต์ ทาดี ยาววันเมย์โซ่ ทำฉนวนกันความร้อนในแบบ
- ฝ้าเพดานภายใน แผ่นยิปซัมบอร์ด ทหนา 9 มม จากปูนซีเมนต์ ทาดี ความสูงจากพื้นถึงฝ้า 2.60 เมตร
- ภายนอกกระเบื้องแผ่นซีเมนต์ ทหนา 4 มม, ท้องฝ้า แผ่นยิปซัมบอร์ด ทหนา 9 มม วางบนโครงคร่าว T - BAR
- บันไดโครงคร่าวไม้จริง สาดทั้งบันได, ลูกนอนบันไดไม้จริง, เสา, ราวกันไถ, ลูกกรงบันไดไม้จริง
- สีทั่วไปใช้ SUPERCOAT ผสมของ ICI หรือ เทียบเท่า
- การป้องกันปลวก ใช้น้ำยาเคมีป้องกัน และการนำยากับปลวกบนไม้โครงคร่าวที่ทำเป็นไม้

รายการประกอบแบบการเปลี่ยนแปลงเพิ่มเติม

•หมายเหตุ : งานโครงการหลักฯ แปรงบรักษาระบบข้อผิดพลาดในค่าไฟฟ้า ความหนา 0.7 มม.

* ไม่มีรายการเปลี่ยนแปลง

สัญญาบัตรประกอบแบบสถาปัตยกรรม

สัญลักษณ์	ความหมาย
N	ทิศเหนือ
	1, 2, 3, 4 ชื่อรูปด้านกำหนดจากแปลน
	A หมายถึง ชื่อรูปด้าน
	A หมายถึง ชื่อแบบขยาย
	A หมายถึง ชื่อรูปตัด
	A หมายถึง แนวลาระยะจากศูนย์กลาง
+0000 , -0000	+0000 มีค่ามากได้ไม่เกินตัวเลขที่กำหนด , -0000 มีค่าน้อยได้ไม่เกินตัวเลขที่กำหนด
	B หมายถึง ระยะความยาวจากศูนย์กลางถึงศูนย์กลาง
	B หมายถึง ระยะความยาวจากริมถึงริม
	A หมายถึง ระยะความยาวจากศูนย์กลางถึงผนังริมนอก
	A หมายถึง ระยะความยาวจากศูนย์กลางถึงผนังริมใน
	1 หมายถึง รหัสประตู
	1 หมายถึง รหัสหน้าต่าง
	1 หมายถึง หมายเลขผนัง
	ผนังก่ออิฐครึ่งแผ่น จากปูน
	ผนังก่ออิฐเต็มแผ่น จากปูน
	ผนังก่ออิฐมวลเบา จากปูน
	ผนังก่ออิฐฉาบผิว ตามแบบระบุ
	ผนังแบบโครงคร่าวไม้แข็ง กรุวัสดุตามแบบระบุ
	ดิน
	คอนกรีต
	ทรายอัดแน่น
	หินตก
	ปูนฉาบเรียบ
	ปูนฉาบเรียบ
	ปูนฉาบเรียบ
	ปูนฉาบเรียบ
	ปูนฉาบเรียบ
	ปูนฉาบเรียบ

1/2565 [11/2/45]

บ้าน SMILE HOME

V.1 [11/2/45]

โครงการ
แบบบ้านยืมเพื่อประชาชน

ตามนโยบาย
ม.ร.ว. สุขุมพันธุ์ บริพัตร
ผู้ว่าราชการกรุงเทพมหานคร

โดยสำนักงานโยธา
กรุงเทพมหานคร

๗
๗๕๕๕๗๖

ได้รับความอนุเคราะห์แบบ
จาก
บริษัท แลนด์ โสม
(ประเทศไทย) จำกัด

บ้าน SMILE HOME
V.1 [11/2/45]




โครงการ
แบบบ้านยืมเพื่อประชาชน

ตามนโยบาย
ม.ร.ว. สุขุมพันธุ์ บริพัตร
ผู้ว่าราชการกรุงเทพมหานคร

โดยสำนักการโยธา
กรุงเทพมหานคร

ได้รับความอนุเคราะห์แบบ
จาก
บริษัท แลนด์ โสม
(ประเทศไทย) จำกัด

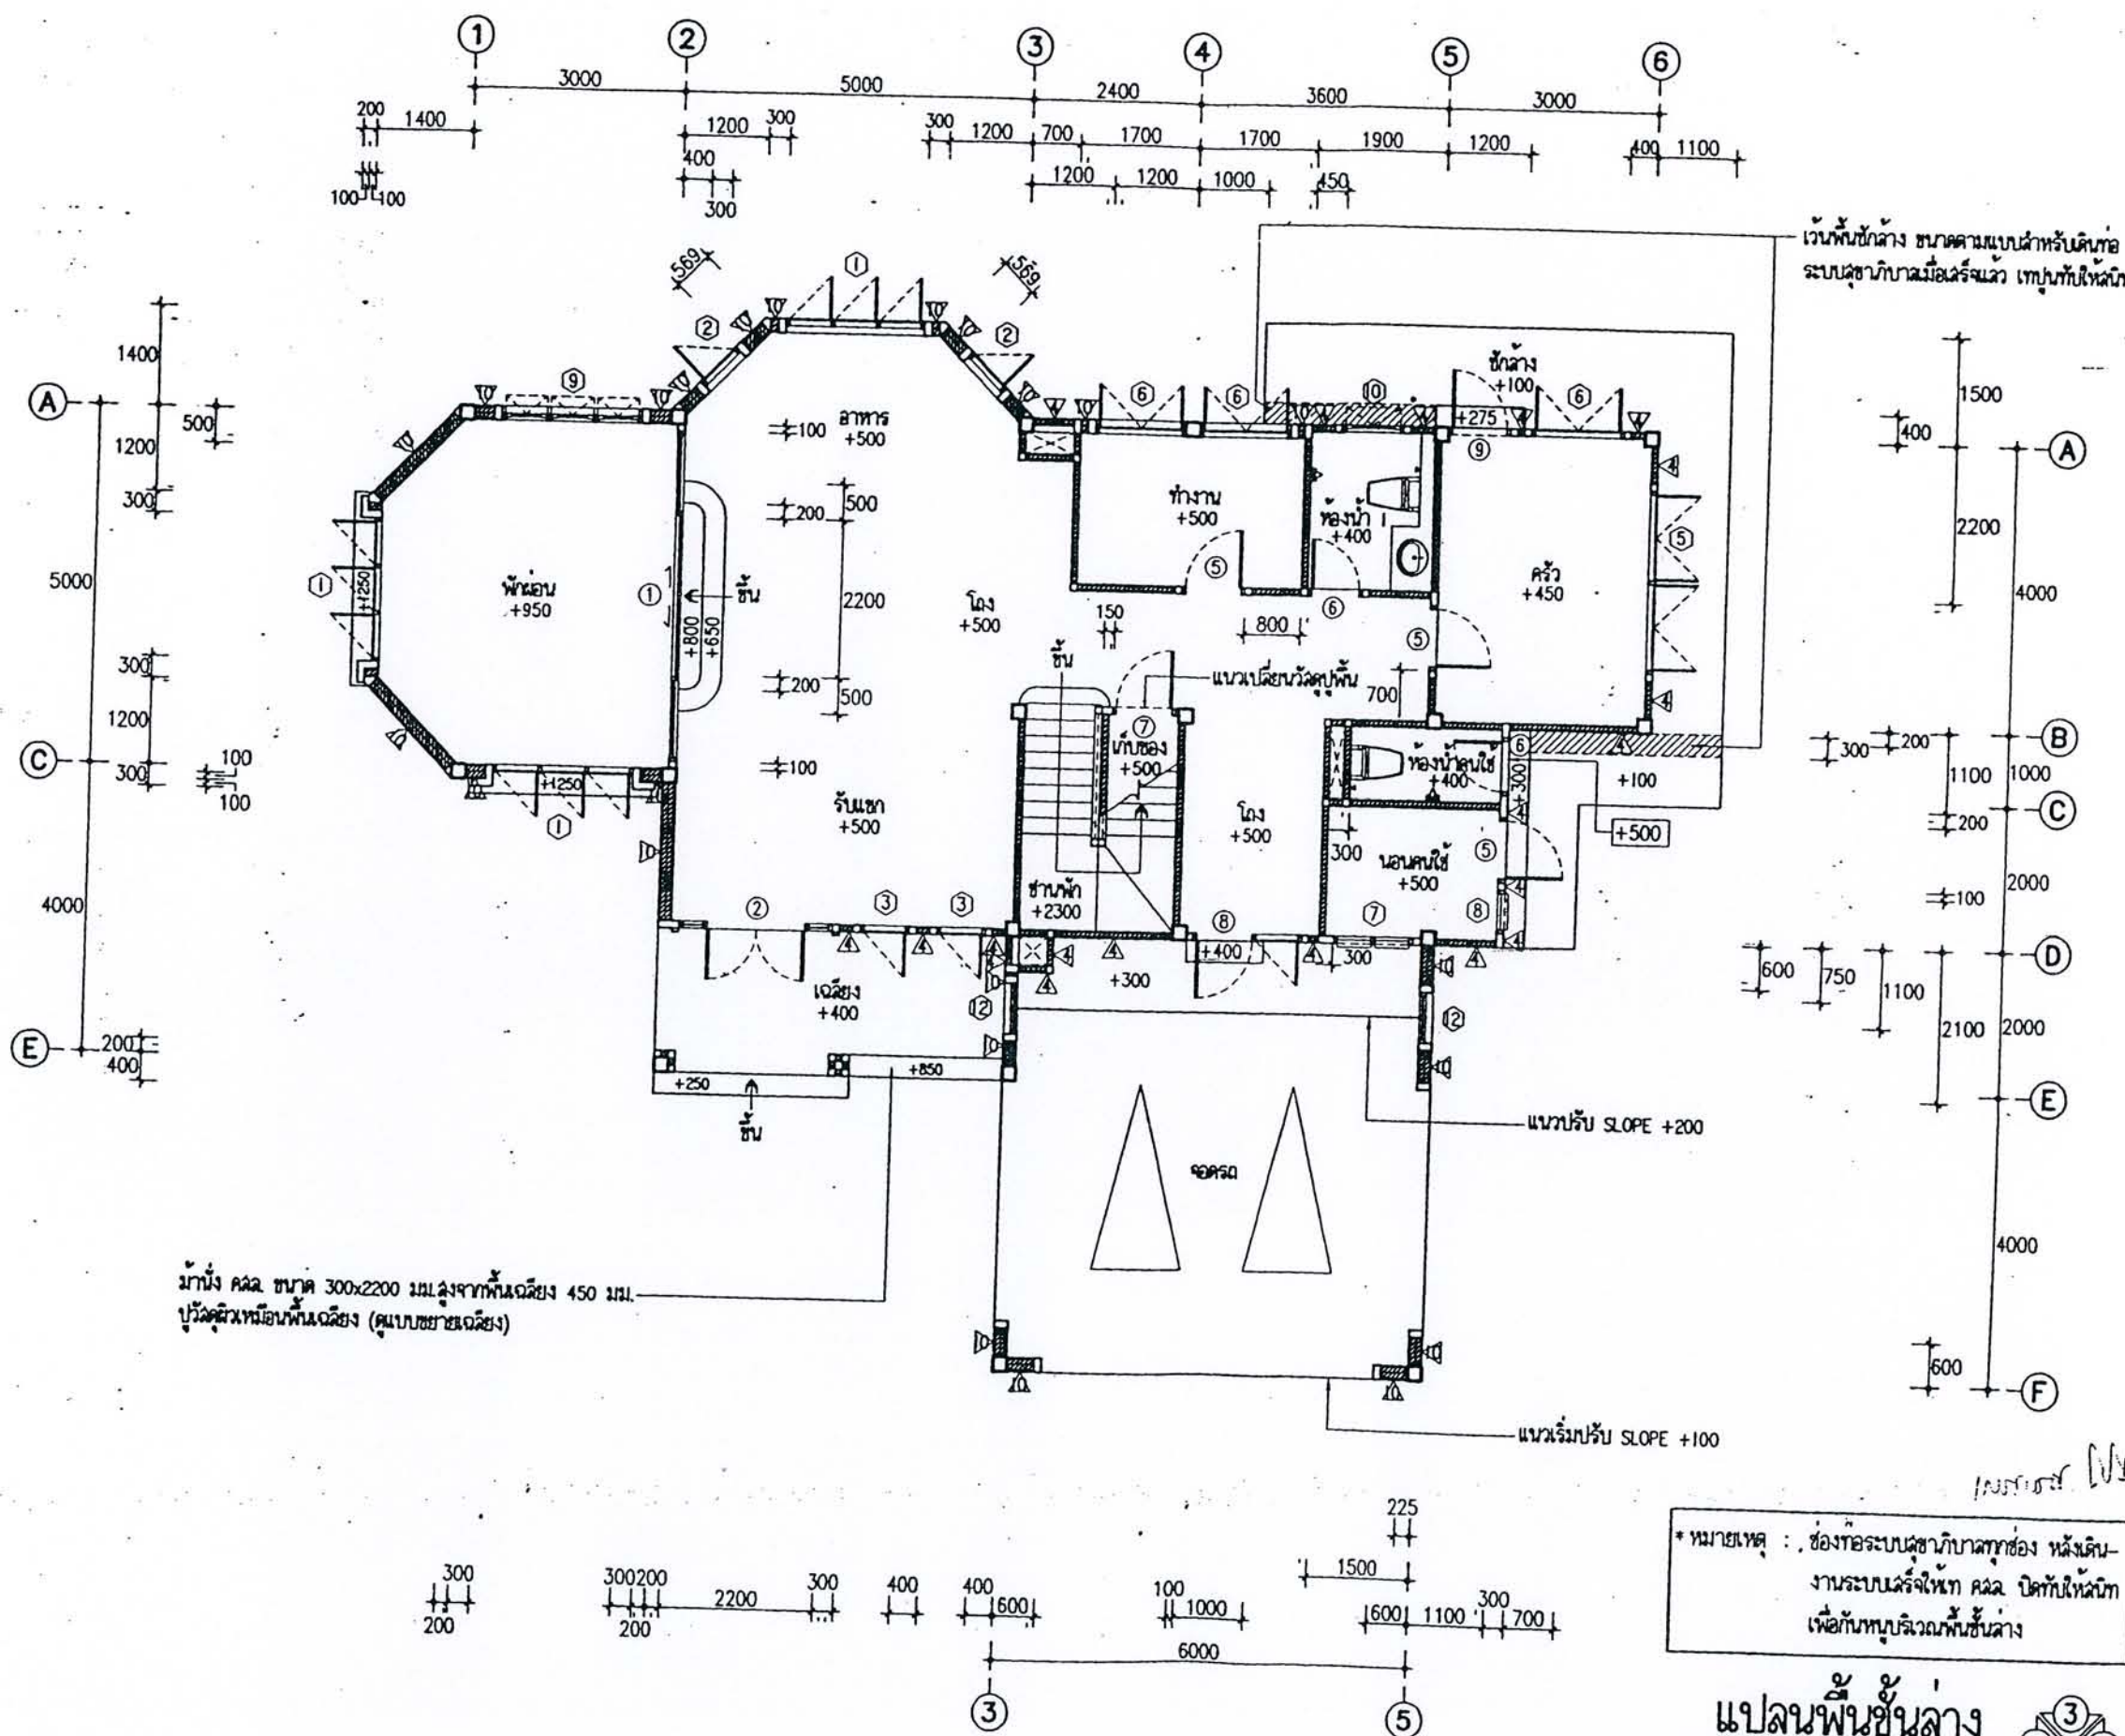


หมายเหตุ : ช่องที่ระบุขนาดอาคารห้อง หลังดิน-งานระบบเสร็จให้ทาสี ผนังให้สีเทา เพื่อกันท่อน้ำรั่วซึมขึ้นล่าง

แปลนพื้นที่ล่าง

มาตราส่วน 1 : 100



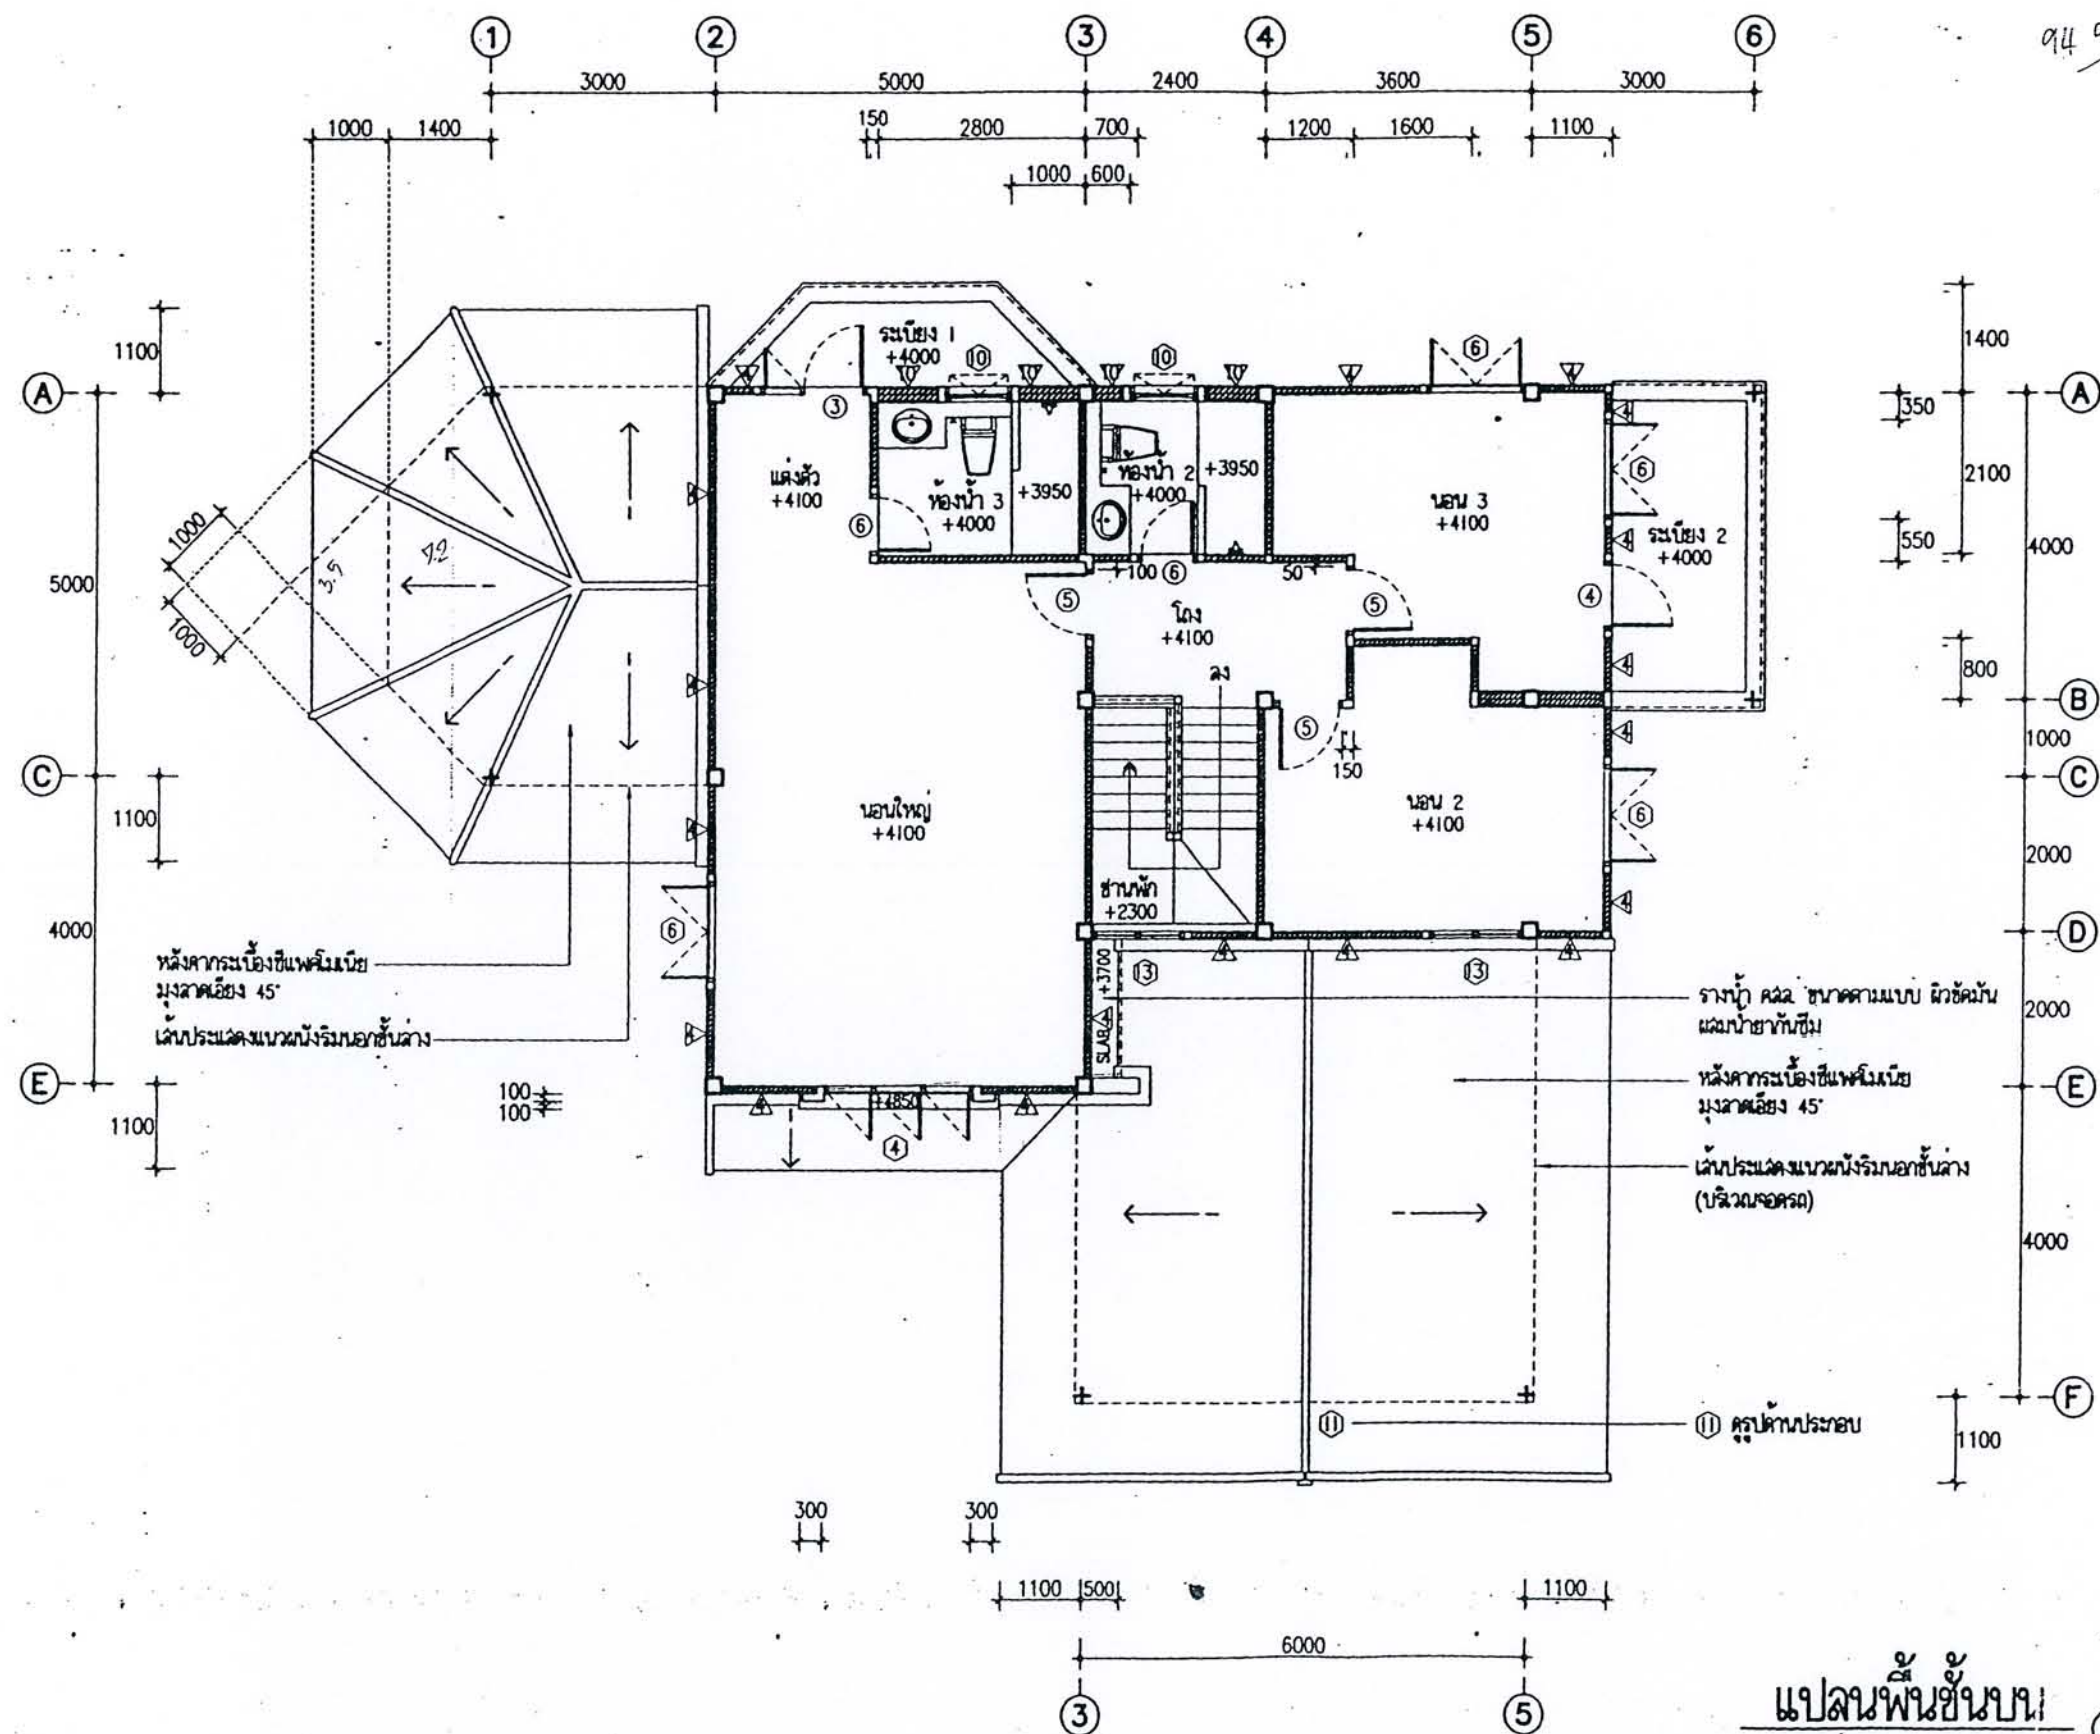

10.165 + 25.2 + 4.4 +

94 985 017.225



โครงการ
แบบบ้านยืมเพื่อประชาชน

ตามนโยบาย
ม.ร.ว. สุขุมพันธุ์ บริพัตร
ผู้ว่าราชการกรุงเทพมหานคร

โดยสำนักการโยธา
กรุงเทพมหานคร

แปลนพื้นที่
มาตราส่วน 1 : 100



ได้รับความอนุเคราะห์แบบ
จาก
บริษัท แลนด์ โฮม
(ประเทศไทย) จำกัด




โครงการ
แบบบ้านยืมเพื่อประชาชน

ตามนโยบาย
ม.ร.ว. สุขุมพันธุ์ บริพัตร
ผู้ว่าราชการกรุงเทพมหานคร

โดยสำนักงานโยธา
กรุงเทพมหานคร

ได้รับความอนุเคราะห์แบบ
จาก
บริษัท แลนด์ โสม
(ประเทศไทย) จำกัด

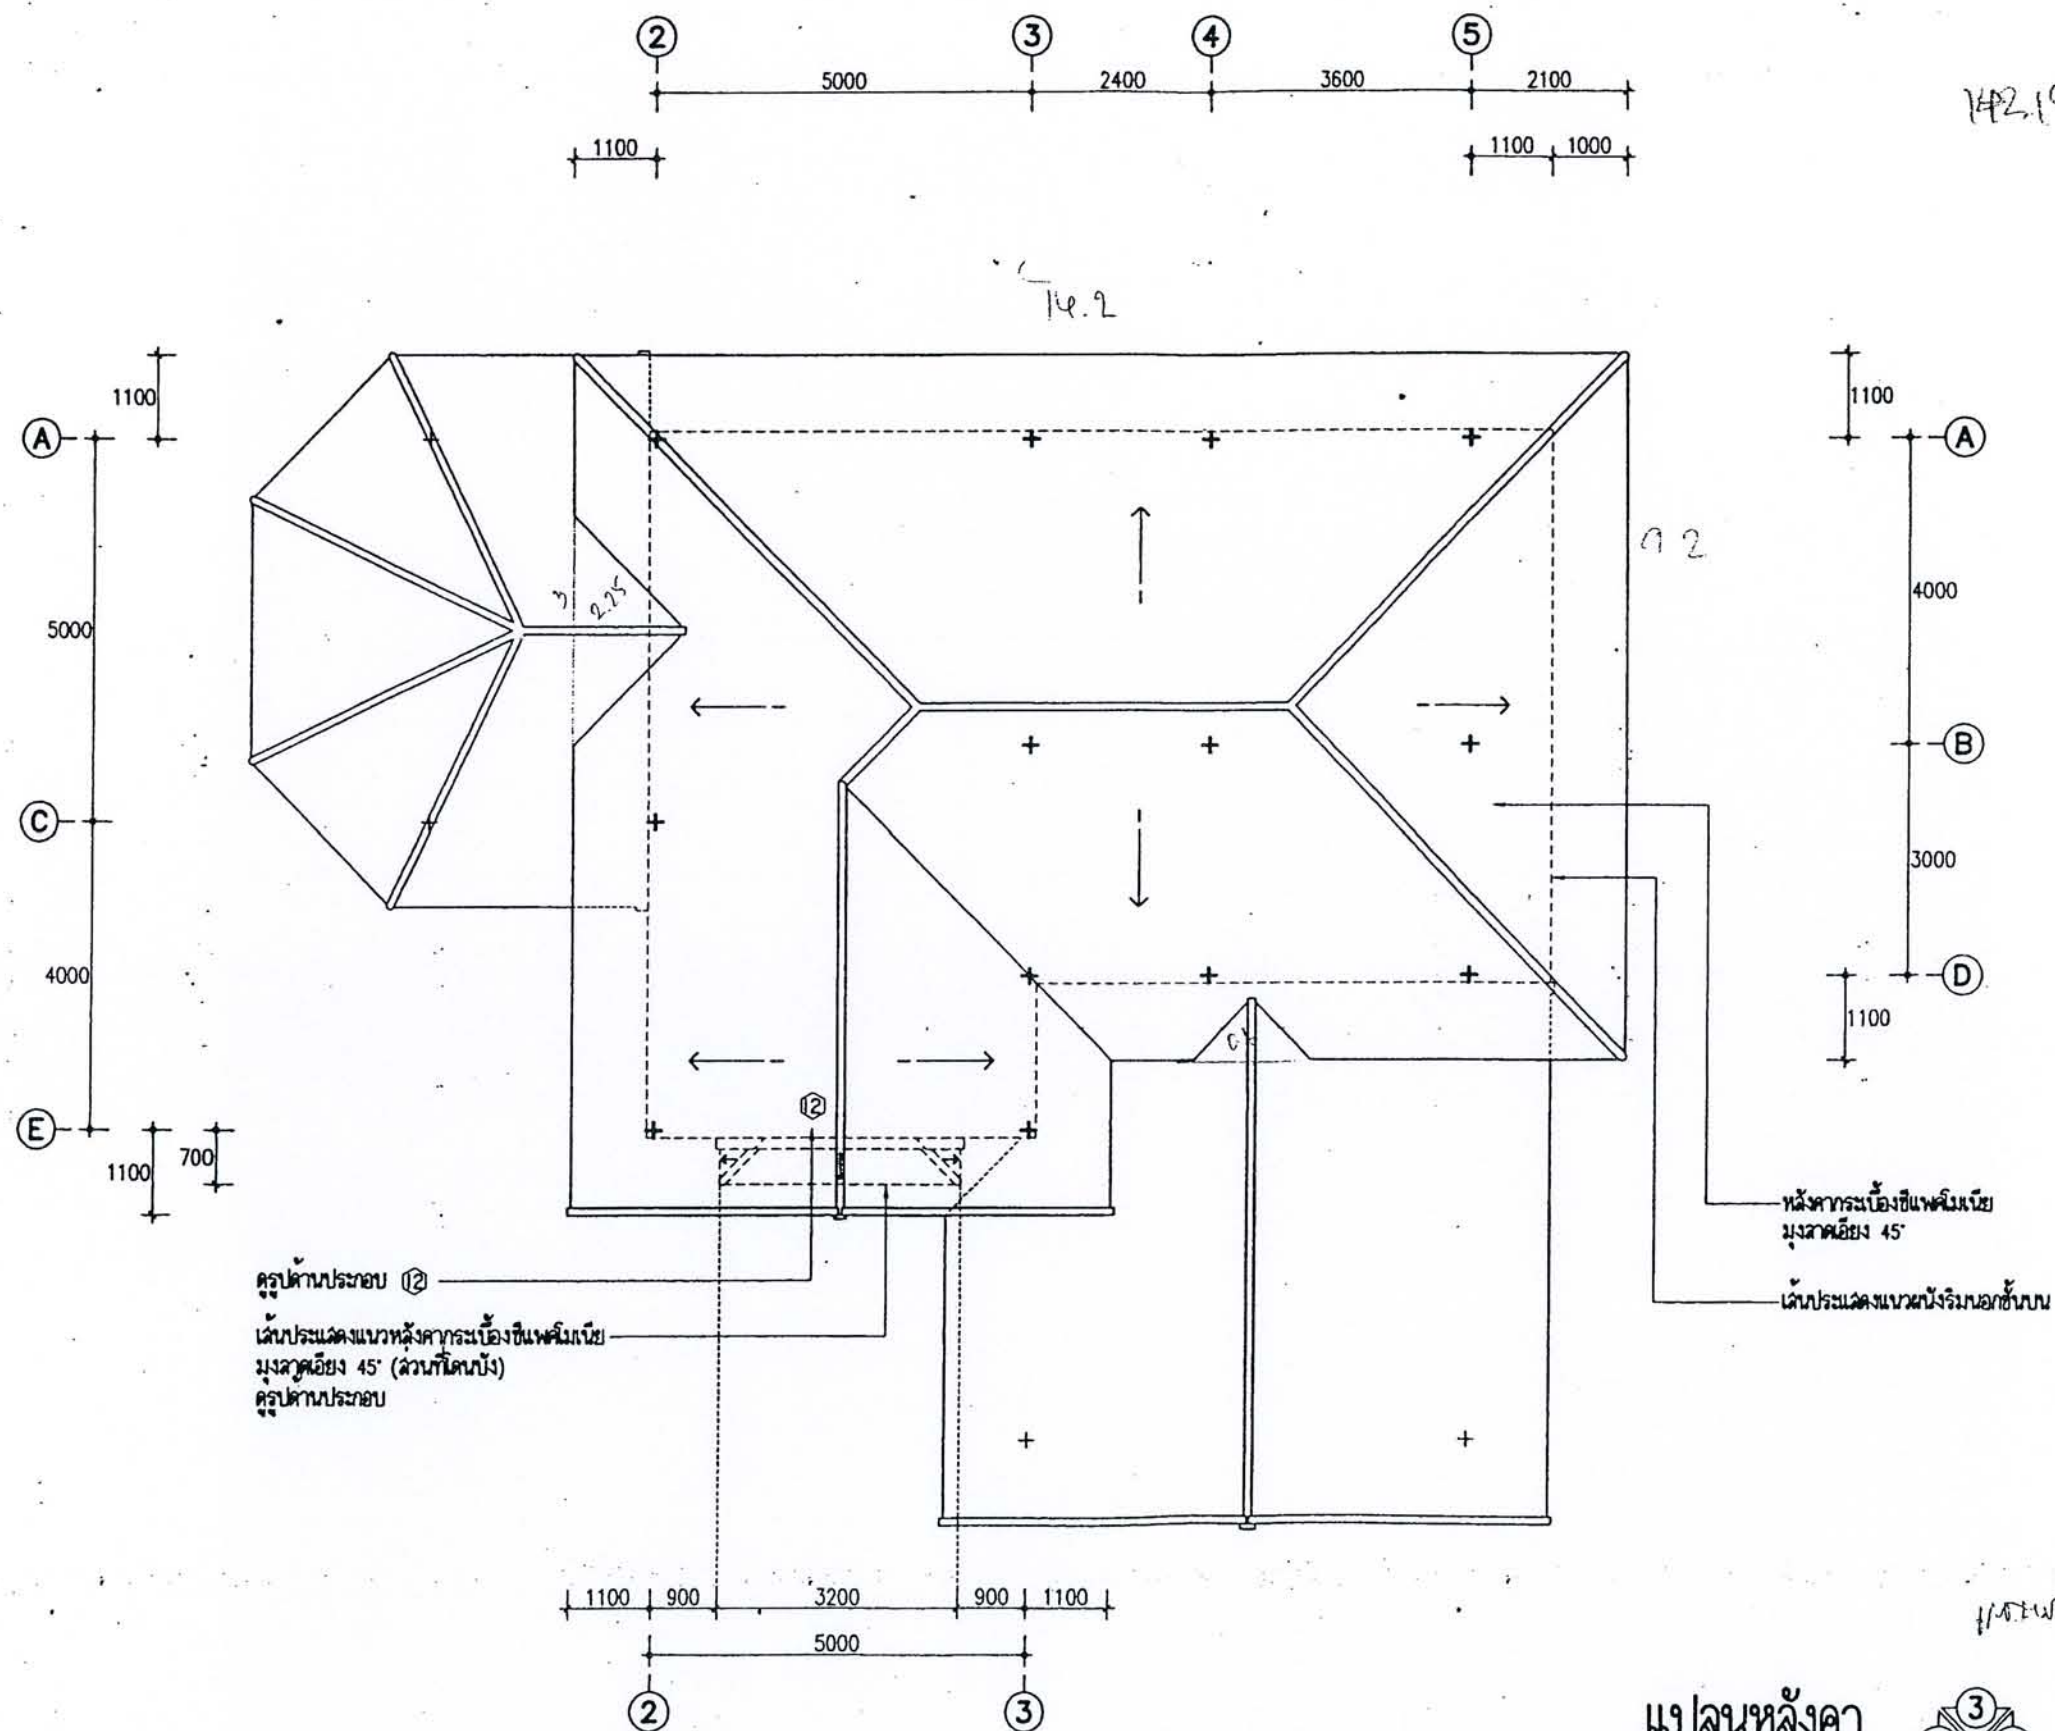


ได้รับความอนุเคราะห์แบบ
จาก
บริษัท แลนด์ โสม
(ประเทศไทย) จำกัด



โครงการ
แบบบ้านยืมเพื่อประชาชน

ตามนโยบาย
ม.ร.ว. สุขุมพันธุ์ บริพัตร
ผู้ว่าราชการกรุงเทพมหานคร

โดยสำนักการโยธา
กรุงเทพมหานคร

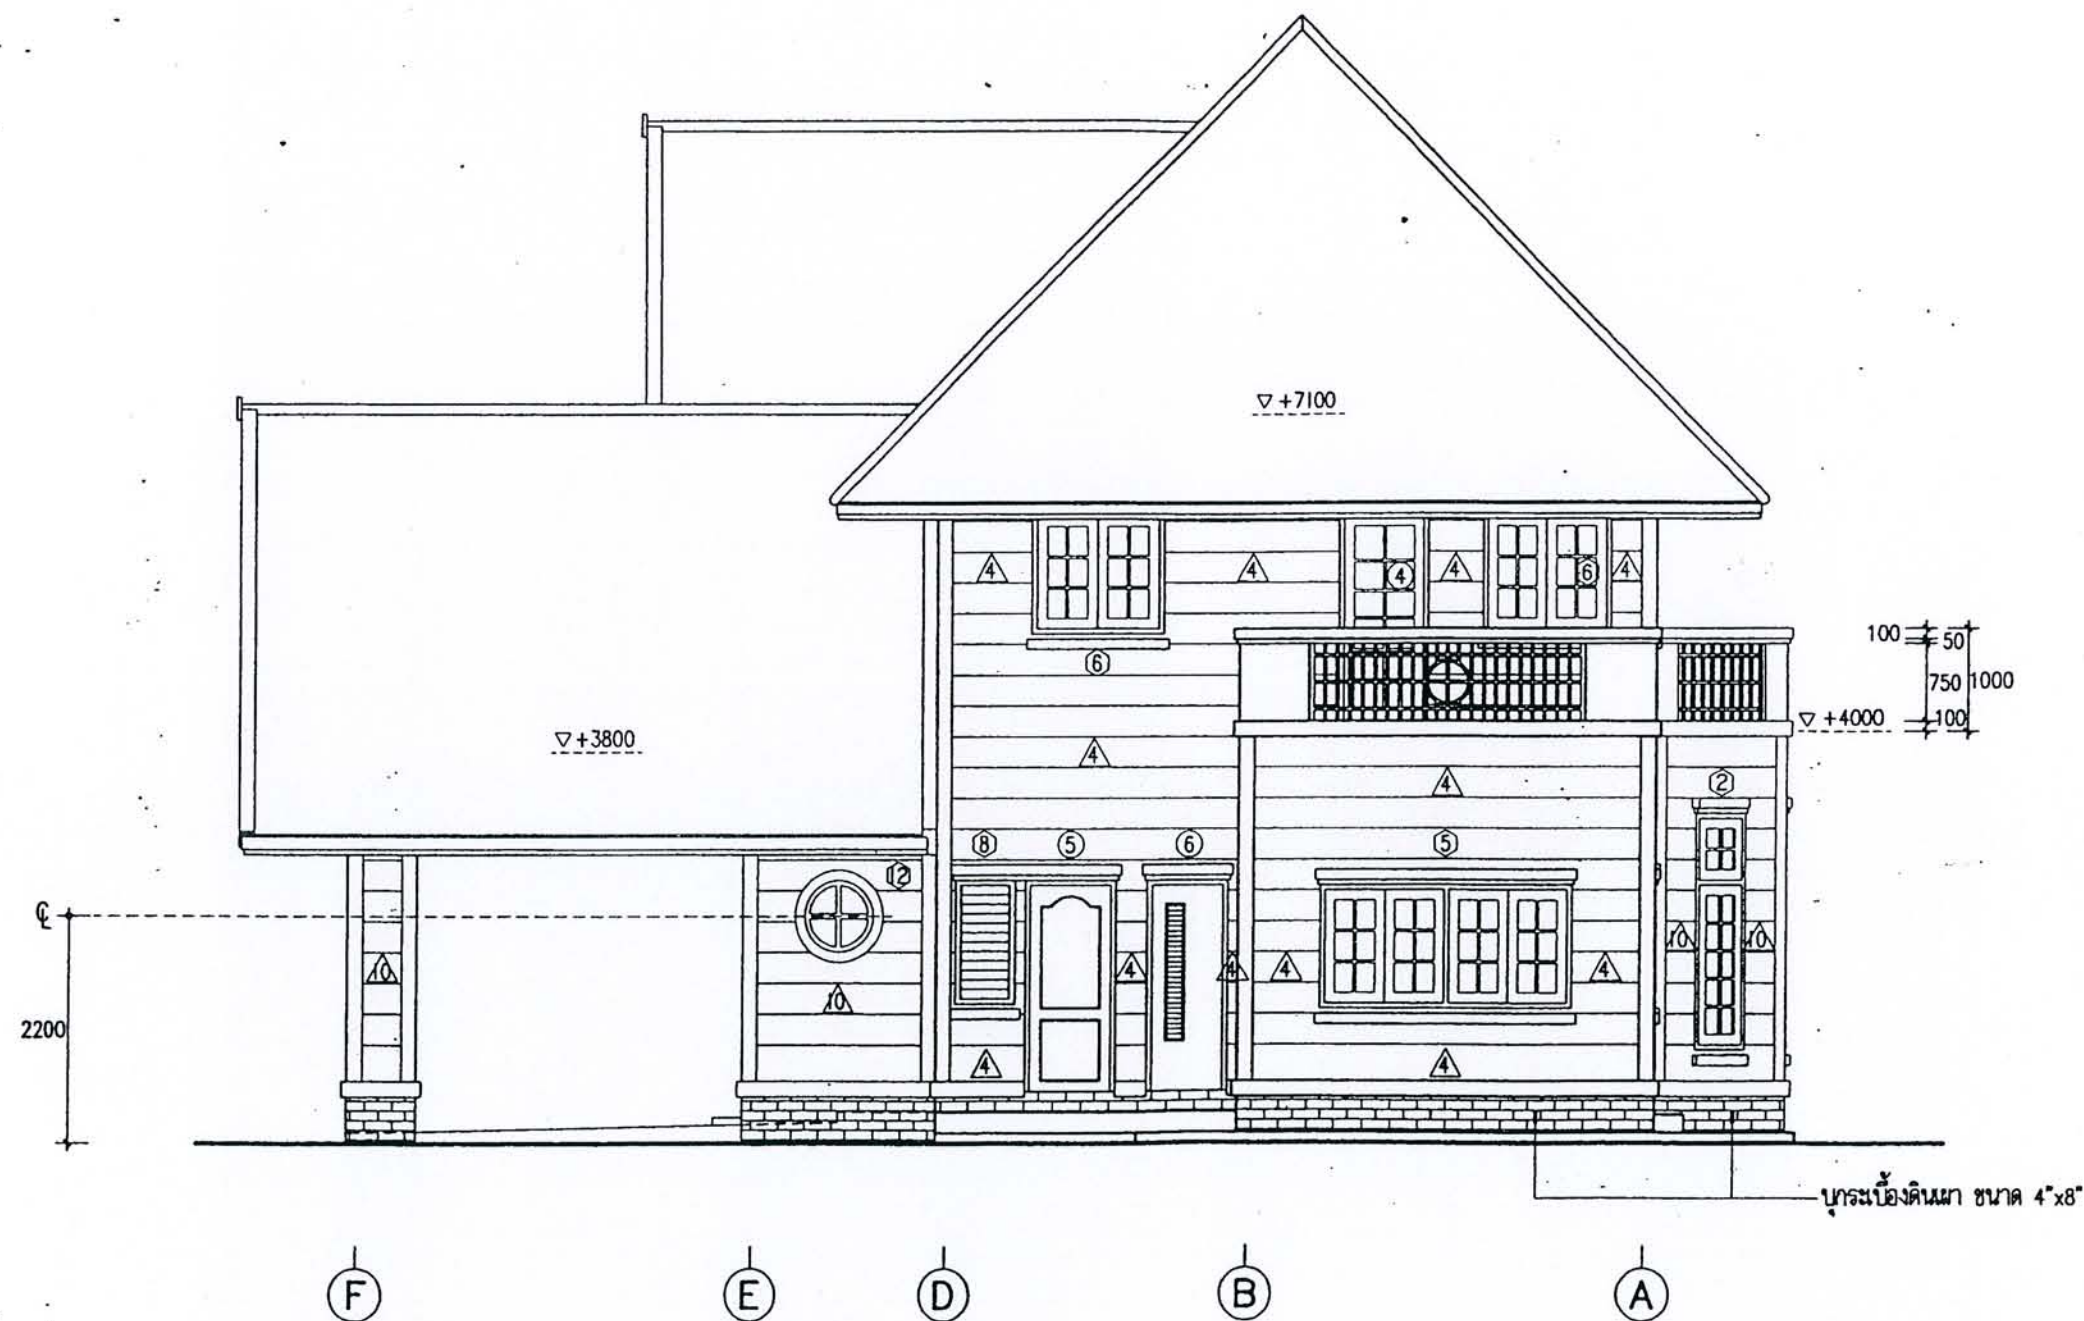

รูปด้าน 2
มาตราส่วน 1:75


ได้รับความอนุเคราะห์แบบ
จาก
บริษัท แลนด์ โยม
(ประเทศไทย) จำกัด



โครงการ
แบบบ้านยืมเพื่อประชาชน

ตามนโยบาย
ม.ร.ว. สุขุมพันธุ์ บริพัตร
ผู้ว่าราชการกรุงเทพมหานคร

โดยสำนักงานโยธา
กรุงเทพมหานคร

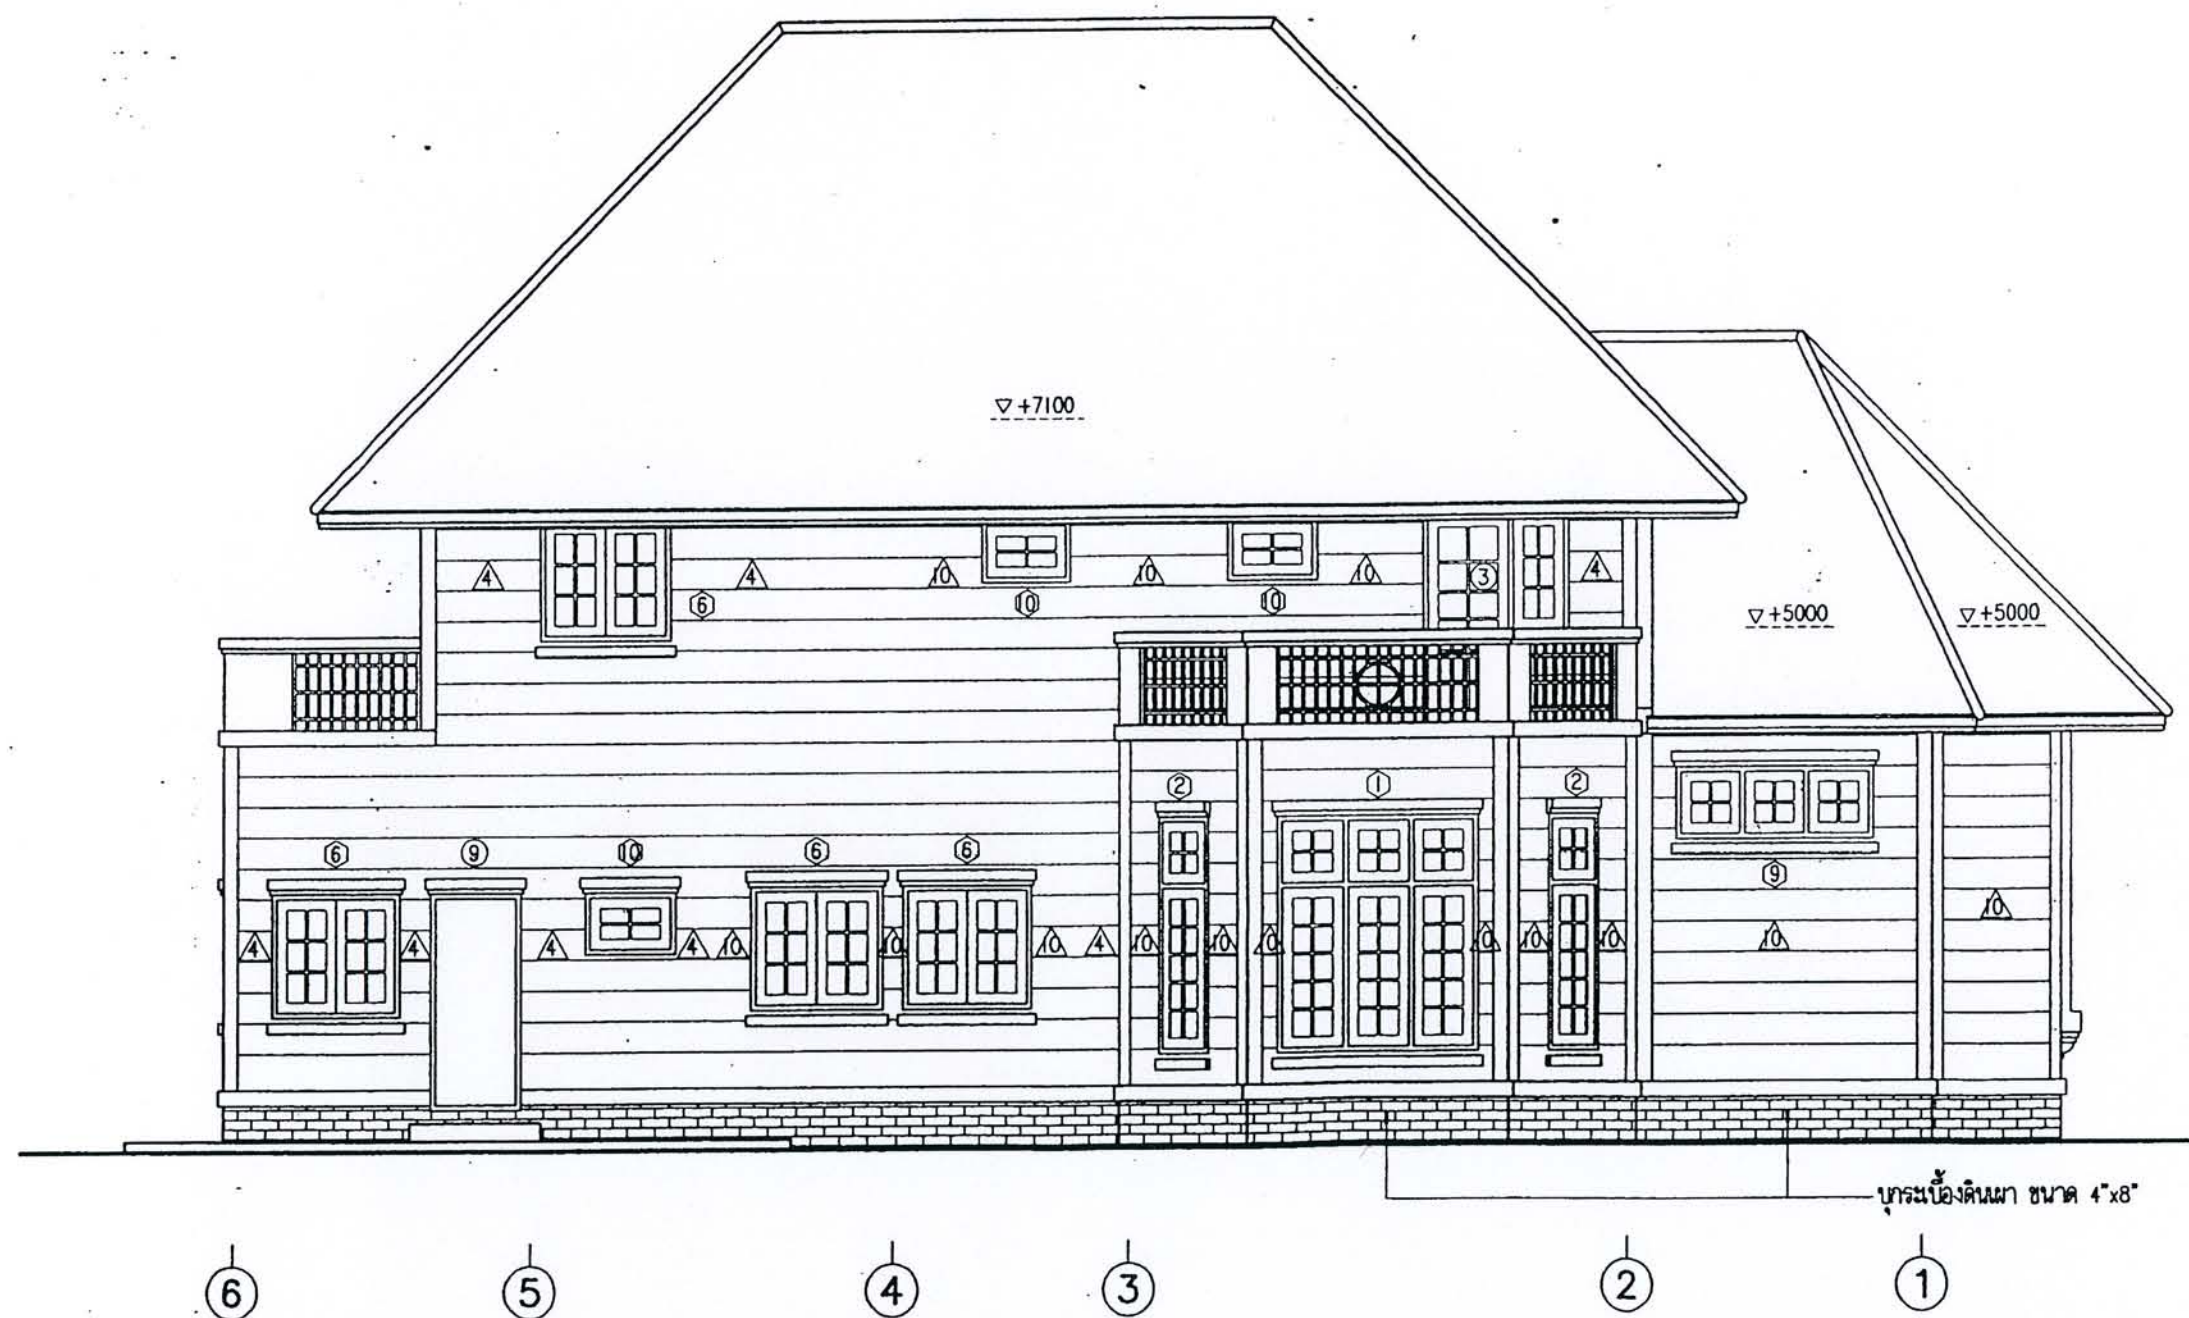

รูปด้าน 3
มาตราส่วน 1 : 75

ไม่พบ


ได้รับความอนุเคราะห์แบบ
จาก
บริษัท แลนด์ โสม
(ประเทศไทย) จำกัด



โครงการ
แบบบ้านยืมเพื่อประชาชน

ตามนโยบาย
ม.ร.ว. สุขุมพันธุ์ บริพัตร
ผู้ว่าราชการกรุงเทพมหานคร

โดยสำนักงานโยธา
กรุงเทพมหานคร

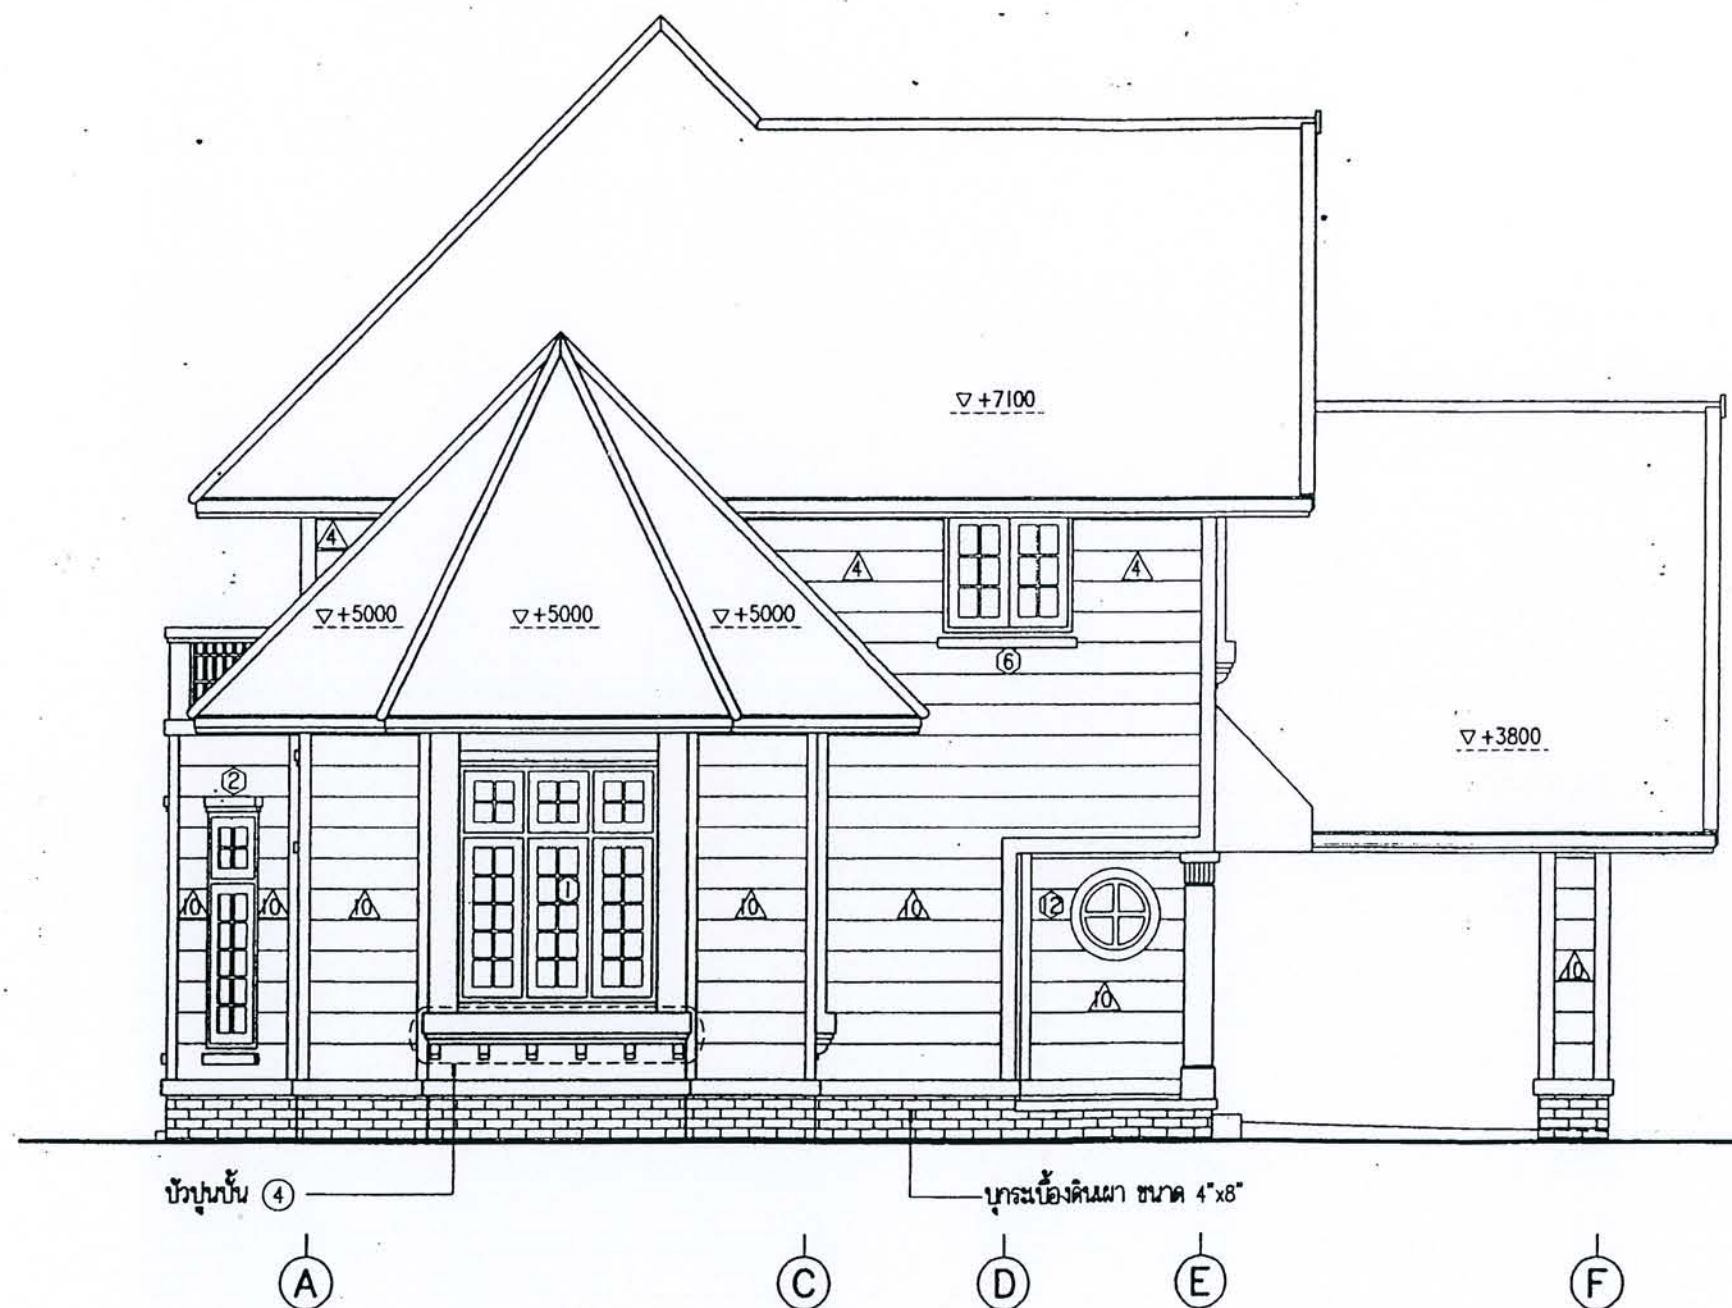

รูปด้าน 4
มาตราส่วน 1 : 75

หน้าแปลน 1/1

ได้รับความอนุเคราะห์แบบ
จาก
บริษัท แลนด์ โสแมท
(ประเทศไทย) จำกัด

สัญญาลักษณะประกอบแบบ "M"



รายการไฟฟ้า

สัญลักษณ์	ความหมาย	ขนาด - ยี่ห้อ - รุ่น
	แผงควบคุมไฟฟ้า	Square-D ขนาด 30 Amp. แผงควบคุมไฟฟ้าพร้อม เซอร์คิส เบรกเกอร์ 7 ชุด
	โคมไฟฟ้า	ครอบแก้วกลม ๑ 1/4" ผิวทึบหลอดฟลูออโรเรสเซนต์ 32 W. แบบกลมแสงสีขาว
	โคมไฟฟ้า	ครอบแก้วกลม ๑ 1/2" หลอดฟลูออโรเรสเซนต์ 60 W.
	หลอดฟลูออโรเรสเซนต์	รางหลอดฟลูออโรเรสเซนต์ ครอบหลอดฟลูออโรเรสเซนต์ ขนาด 1 X 20 W. แสงสีขาว
	หลอดฟลูออโรเรสเซนต์	รางหลอดฟลูออโรเรสเซนต์ ครอบหลอดฟลูออโรเรสเซนต์ ขนาด 1 X 40 W. แสงสีขาว
	ไฟโคมแขวนพดาน	โคมไฟแก้วผิวทึบ ๑ 1/2" หลอดฟลูออโรเรสเซนต์ 60 W.
	ไฟตั้งพื้น	โคมไฟตั้งพื้น 60 W. พานเหลี่ยม
	สวิทช์ไฟฟ้า	Single way ชนิดสวิทช์แบบ NATIONAL (ซองเท้) ติดตั้งสูงจากพื้น 1200 มม.
	สวิทช์ไฟฟ้า 2 ทาง	Two way ชนิดสวิทช์แบบ NATIONAL (ซองเท้) ติดตั้งสูงจากพื้น 1200 มม.
	ปลั๊กไฟ, เต้าเสียบ	ปลั๊กไฟแบบเรียบชนิดสวิทช์แบบ 2 เต้าเสียบต่อ 1 ชุด พร้อมสายดินตาม- การไฟฟ้า ติดตั้งสูงจากพื้น 200 มม. ของ NATIONAL (ซองเท้) ติดตั้งจากวงกบ 100 มม.
	ปลั๊กไฟ, เต้าเสียบ	ปลั๊กไฟแบบเรียบชนิดสวิทช์แบบ 2 เต้าเสียบต่อ 1 ชุด พร้อมสายดินตาม- การไฟฟ้า ติดตั้งสูงจากพื้น 1000 มม. ของ NATIONAL (ซองเท้) ติดตั้งจากวงกบ 100 มม.
	ปลั๊กไฟอากาศ TV.	ใช้สายอากาศ TV.RG-6 โดยเดินสายไปยังห้องนอนที่ติดตั้งแล้วที่สายปลั๊กไฟ 1 ม.
	โทรทัศน์	เดินสายตามมาตรฐานไฟฟ้า โดยเดินสายไปยังห้องนอนที่ติดตั้งแล้วที่สายปลั๊กไฟ 1 ม.
	สวิทช์แอร์	ตำแหน่งตามแบบ
	แสดงการเดินสายไฟแบบ-	สายไฟใช้สาย PVC. ของ YAZAKI หรือ BANGKOK CABLE
	เดินสาย	เดินสายตามลักษณะที่ปรากฏในแบบร่าง
		- สายไฟสำหรับ สวิทช์ไฟ ที่มิใช่ ขนาด 1.0 มม. ²
		- สายไฟสำหรับ ปลั๊กไฟ ที่มิใช่ ขนาด 2.5 มม. ² (แบบมีสายดิน)
		- สายไฟสำหรับ แอร์ ที่มิใช่ ขนาด 10.0 มม. ²
		- สายไฟสำหรับ เครื่องทำน้ำร้อน ที่มิใช่ ขนาด 10.0 มม. ²
		- สำหรับสายเมนใช้สาย PVC. ของ YAZAKI หรือ BANGKOK CABLE
		ขนาด 16.00 มม. ² ต่อห่างจากสายดินไม่เกิน 16000 มม.

หมายเหตุ :
 - ให้เดินสายดินตามกฎระเบียบของการไฟฟ้าอย่างถูกต้อง
 - ราคากำหนด 3,000,000 บาท ใช้ไฟ ขนาด 30 Amp. 2 สายของ Square-D พร้อมสายเมน
 ตู้เบรกเกอร์ 16 ช่อง
 - ราคากำหนด 5,000,000 บาท ใช้ไฟ ขนาด 50 Amp. 2 สายของ Square-D พร้อมสายเมน

รายการเปลี่ยนแปลงเพิ่มเติมไฟฟ้า

- * บ้านหลังนี้ใช้ไฟฟ้าขนาด 30 Amp. 2 สายของ Square-D พร้อมสายเมน ตู้เบรกเกอร์ 16 ช่อง
- * ระบบไฟฟ้า ท่อเดินสายไฟฟ้าใช้ระบบเดินสายไฟฟ้าร้อยท่อ เอสแอลเอ็นโอไฟฟ้าพาด และเดินสายไฟฟ้าร้อยท่อเอสแอลเอ็นโอ ในผนังทั้งหมด ตามใบ ป/ป 1/5.
- * ติดตั้งระบบ SAFETY สัญญาณเตือนภัยในบ้าน ยี่ห้อ VISONIC รุ่น POWER MAX ของอิสราเอล จำนวน 6 ชุด ตำแหน่งตาม-
ความเหมาะสมหน้าหน่วยงาน ตามใบ ป/ป 2/5.

นางสาว นิตยา

บ้าน SMILE HOME
V.1 [11/2/45]

โครงการ
แบบบ้านยืมเพื่อประชาชน

ตามนโยบาย
ม.ร.ว. สุขุมพันธุ์ บริพัตร
ผู้ว่าราชการกรุงเทพมหานคร

โดยสำนักงานโยธา
กรุงเทพมหานคร


ได้รับความอนุเคราะห์แบบ
จาก
บริษัท แลนด์ โฮม
(ประเทศไทย) จำกัด



โครงการ
แบบบ้านยืมเพื่อประชาชน

ตามนโยบาย
ม.ร.ว. สุขุมพันธุ์ บริพัตร
ผู้ว่าราชการกรุงเทพมหานคร

โดยสำนักงานโยธา
กรุงเทพมหานคร

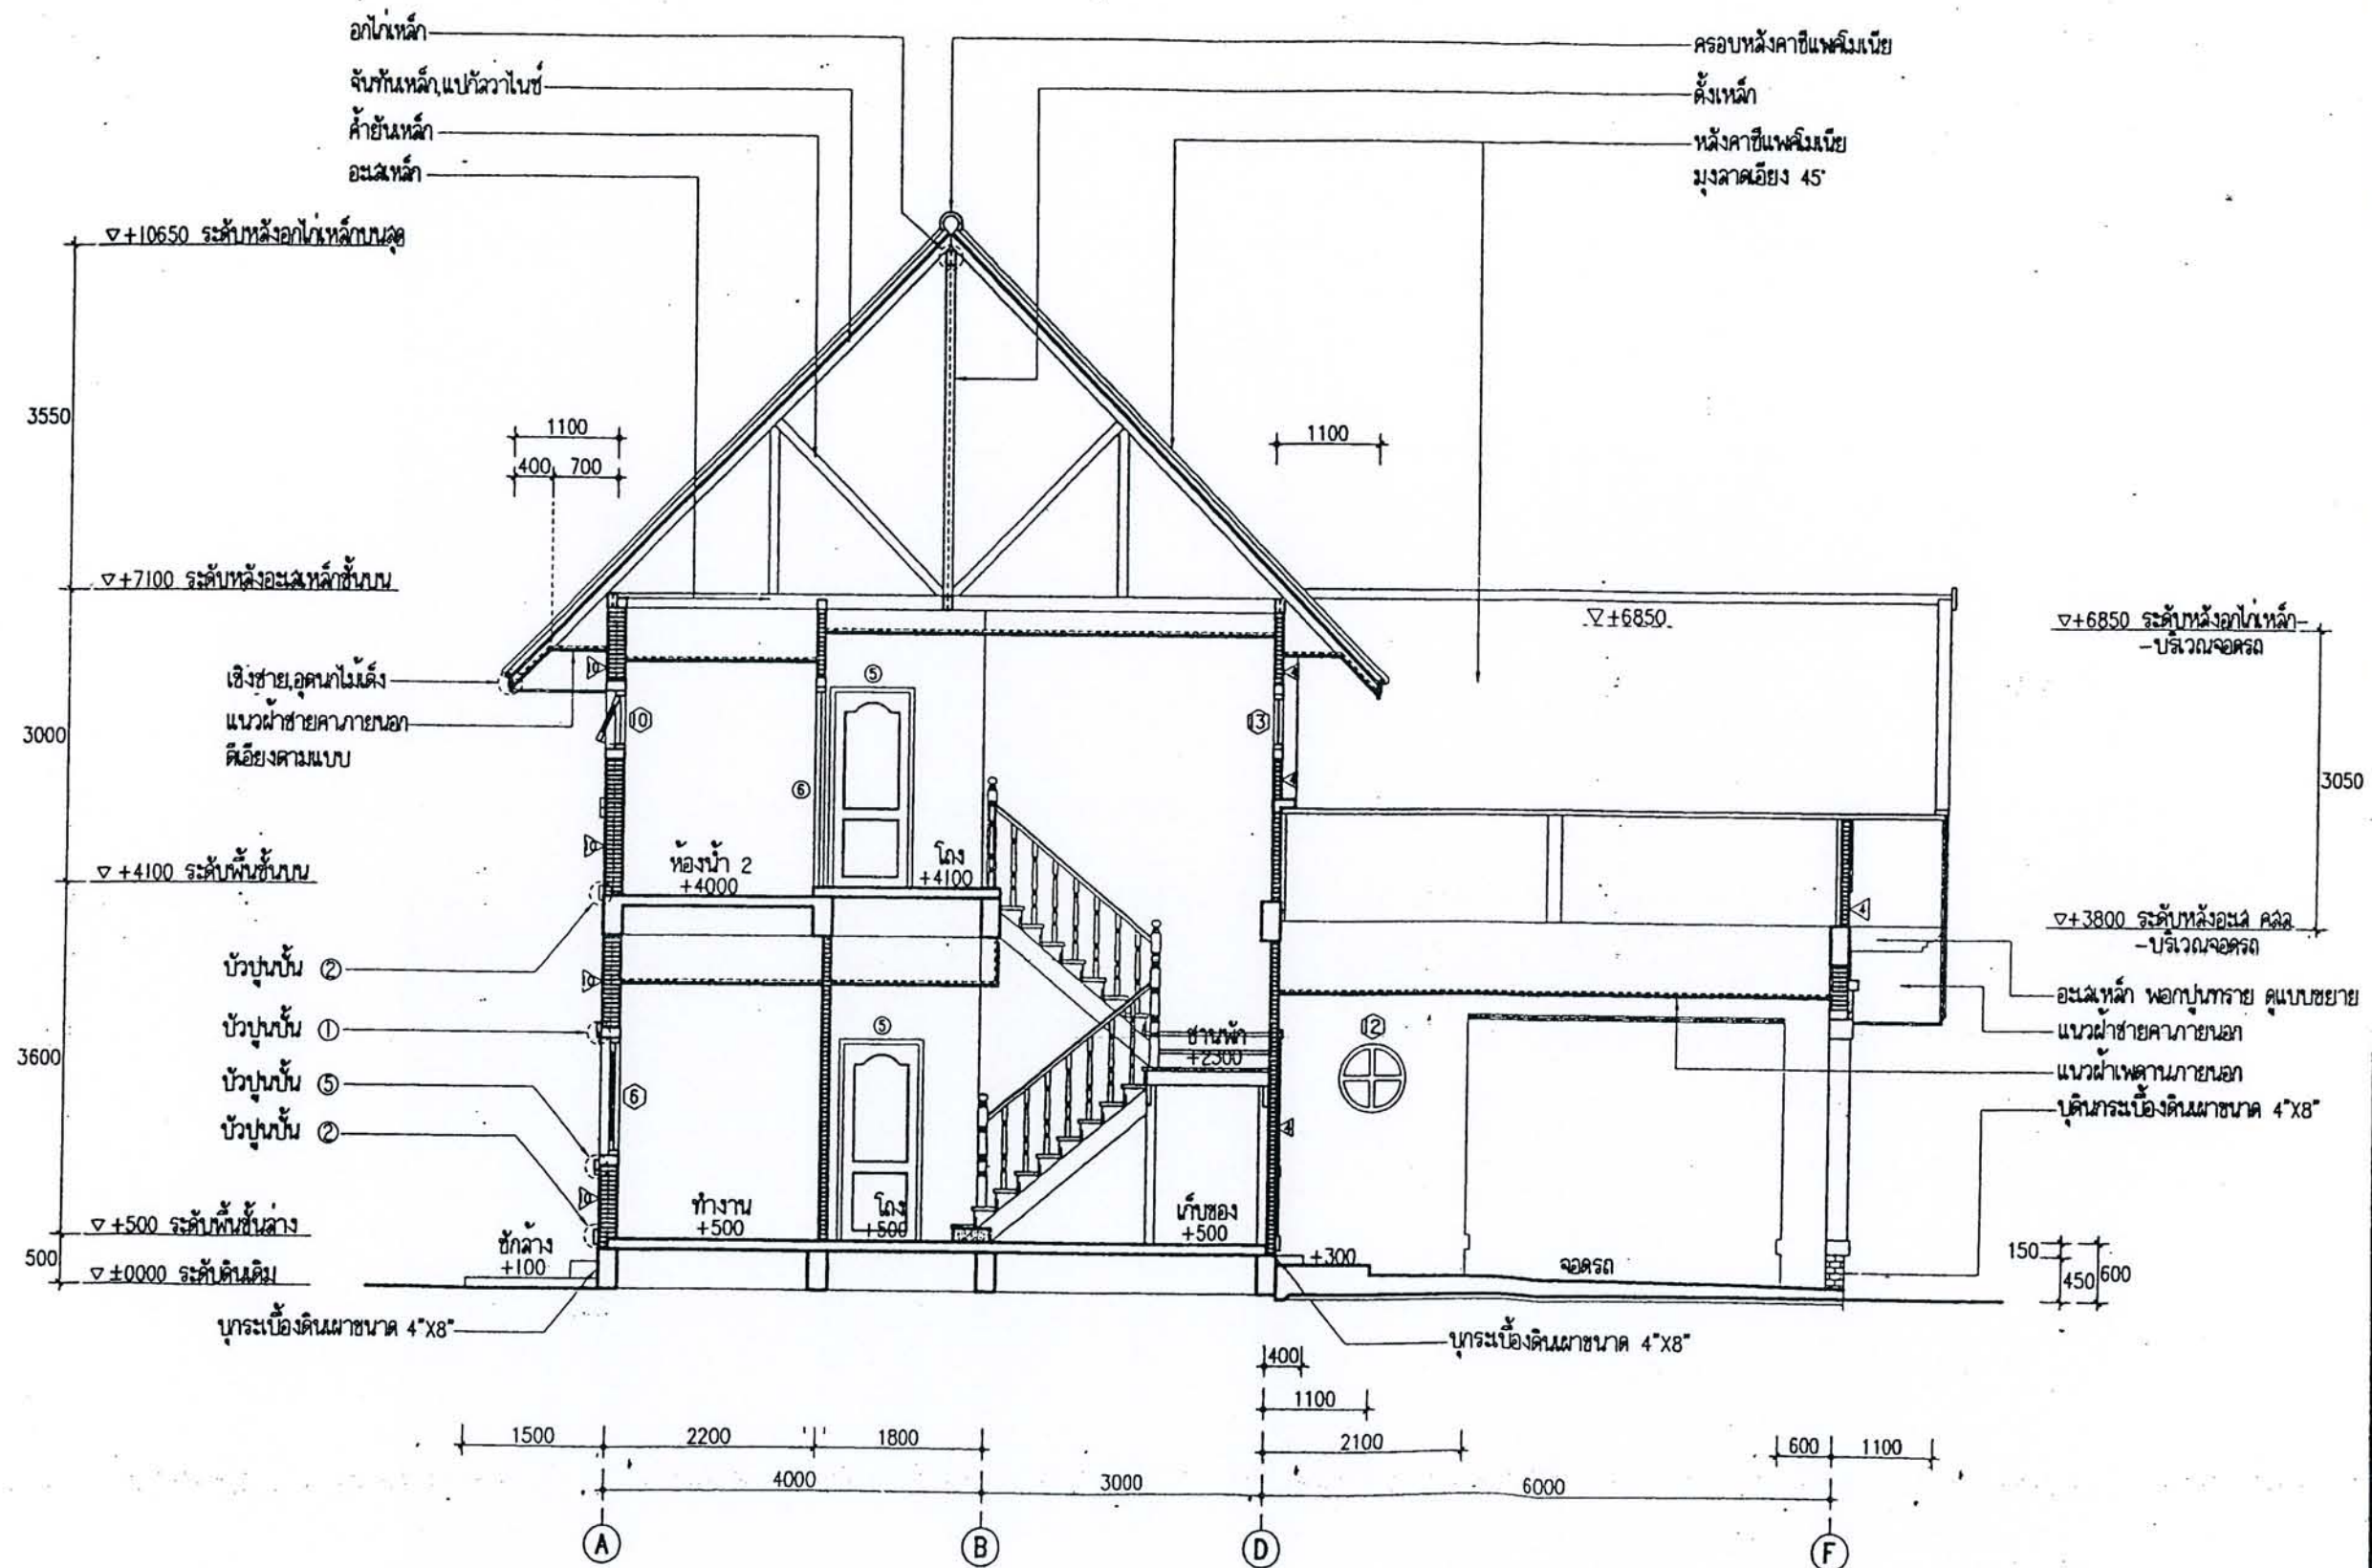

รูปตัด A-A
มาตราส่วน 1:75

ได้รับความอนุเคราะห์แบบ
จาก
บริษัท แลนด์ โสม
(ประเทศไทย) จำกัด




โครงการ
แบบบ้านยืมเพื่อประชาชน

ตามนโยบาย
ม.ร.ว. สุขุมพันธุ์ บริพัตร
ผู้ว่าราชการกรุงเทพมหานคร

โดยสำนักงานโยธา
กรุงเทพมหานคร

ได้รับความอนุเคราะห์แบบ
จาก
บริษัท แลนด์ โสม
(ประเทศไทย) จำกัด

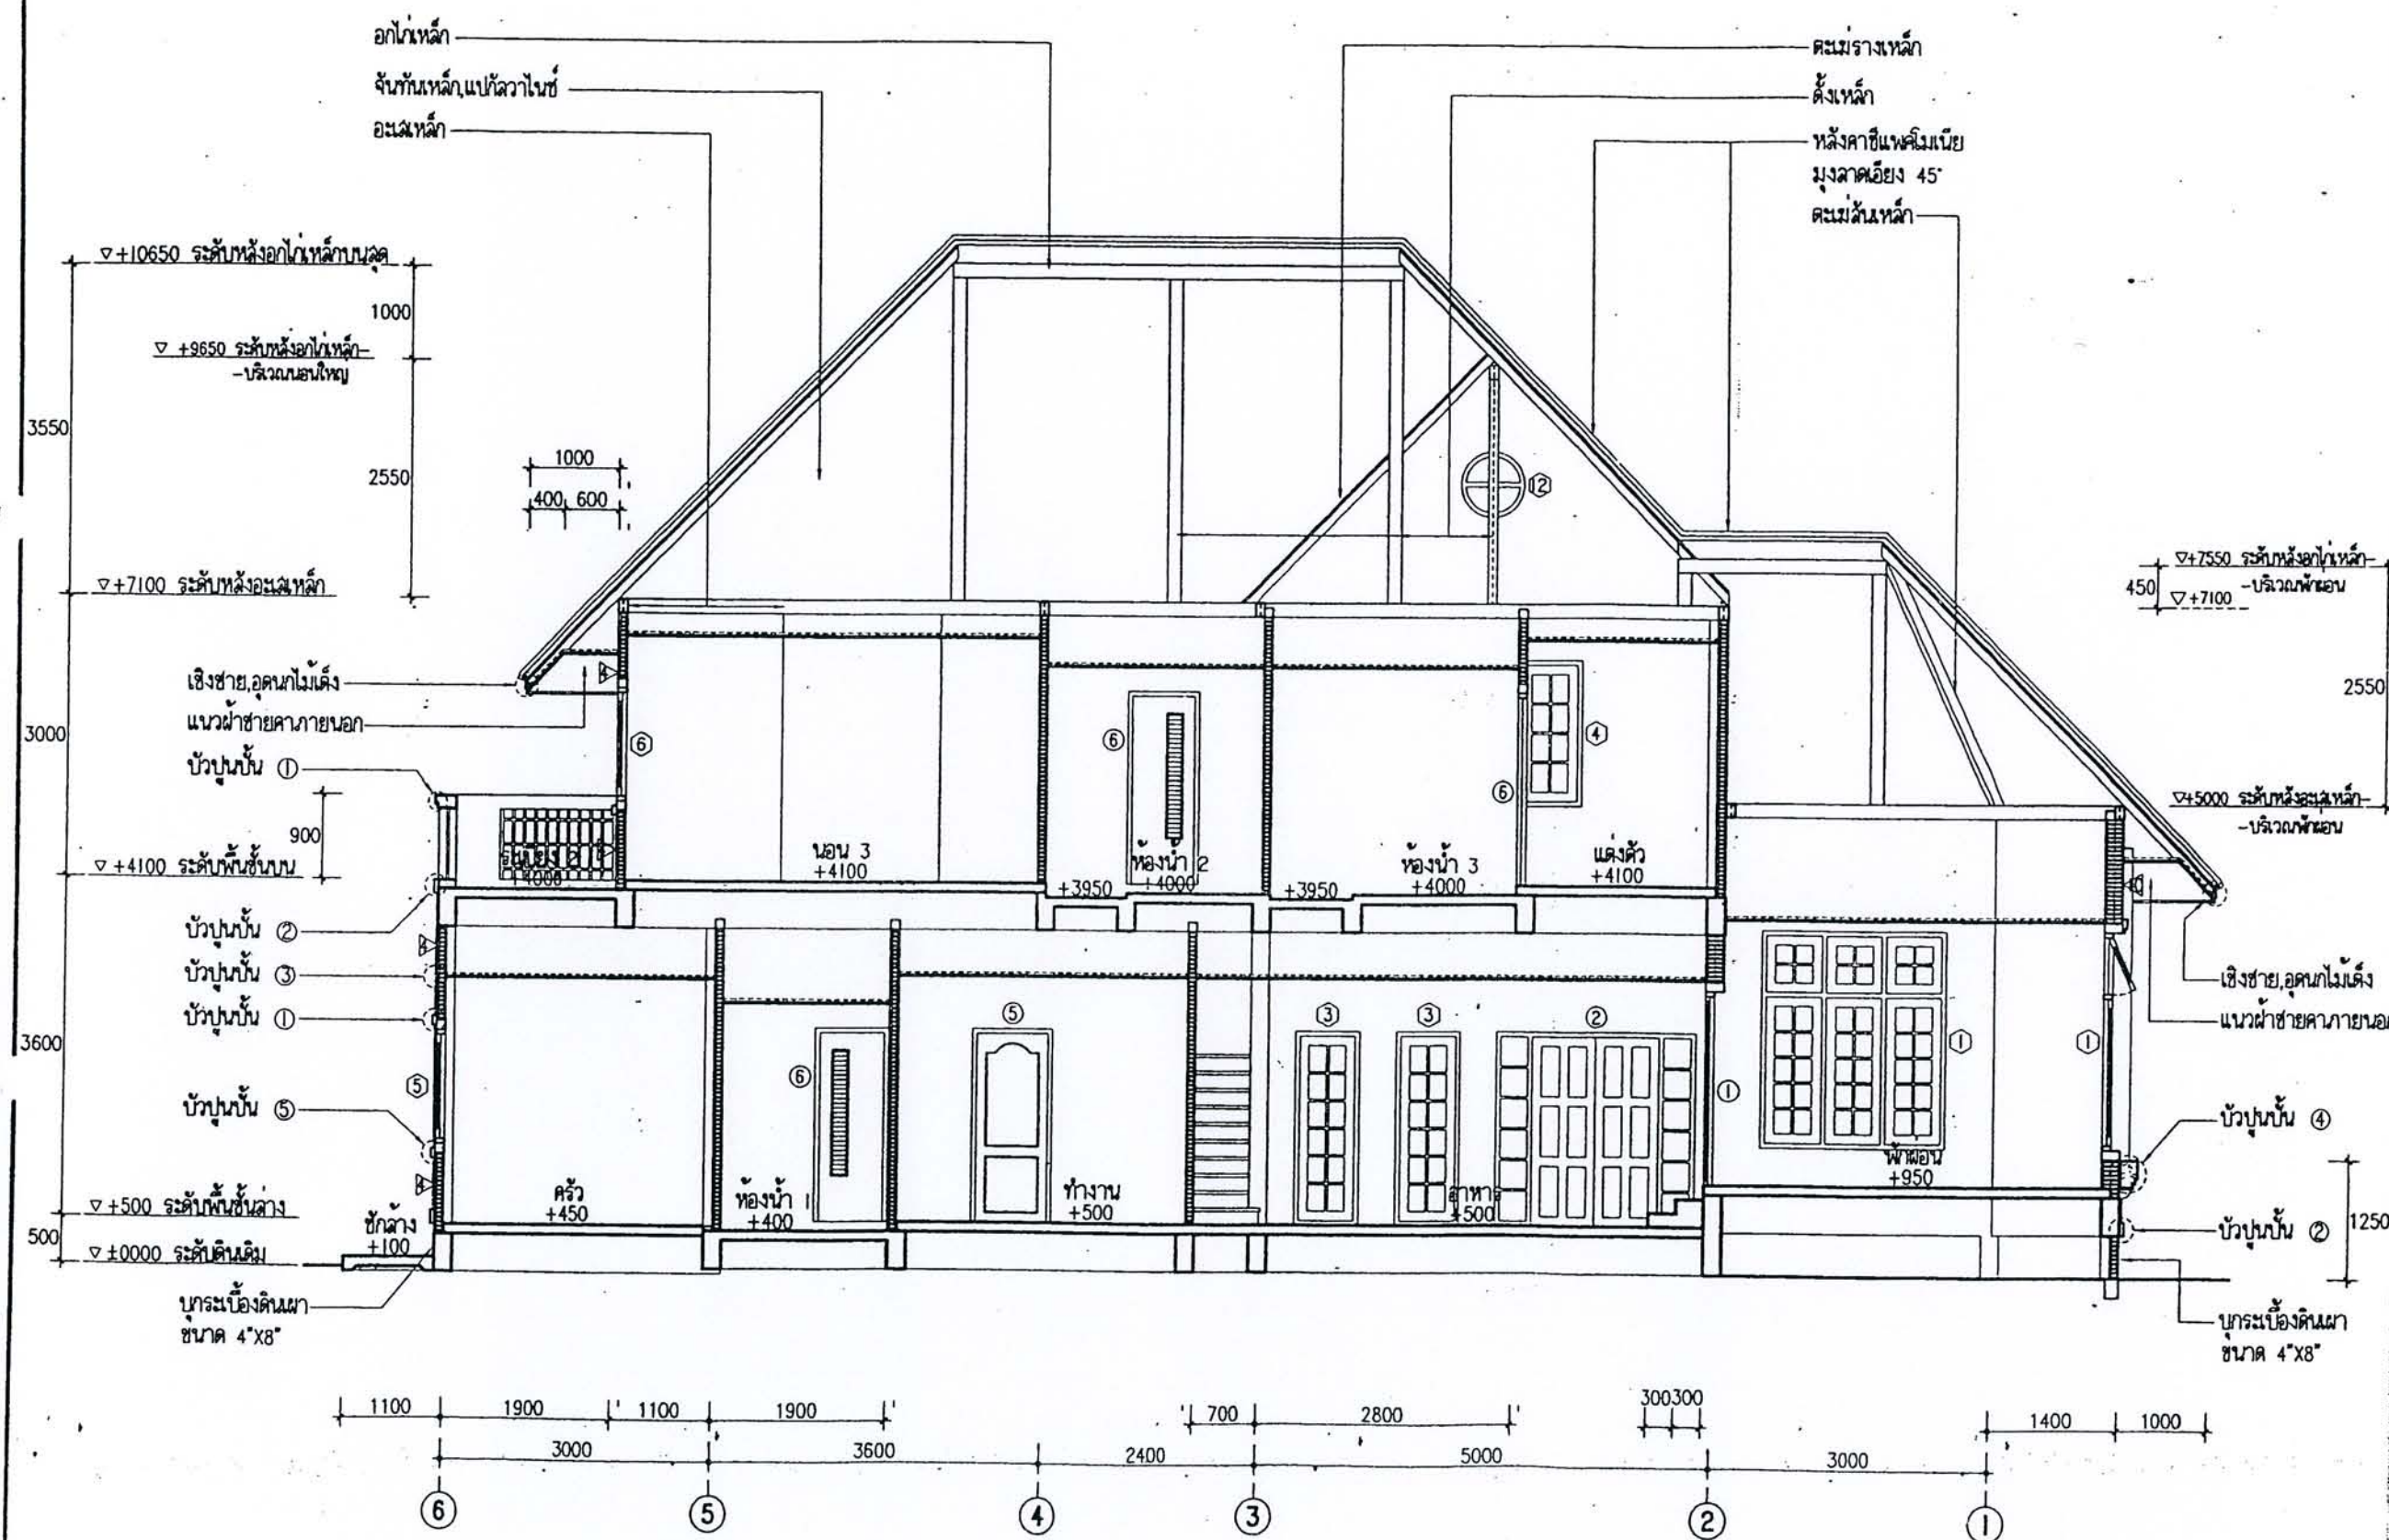


รูปตัด B-B
มาตรฐาน
1:75



โครงการ
แบบบ้านยืมเพื่อประชาชน


ตามนโยบาย
ม.ร.ว. สุขุมพันธุ์ บริพัตร
ผู้ว่าราชการกรุงเทพมหานคร

โดยสำนักงานโยธา
กรุงเทพมหานคร

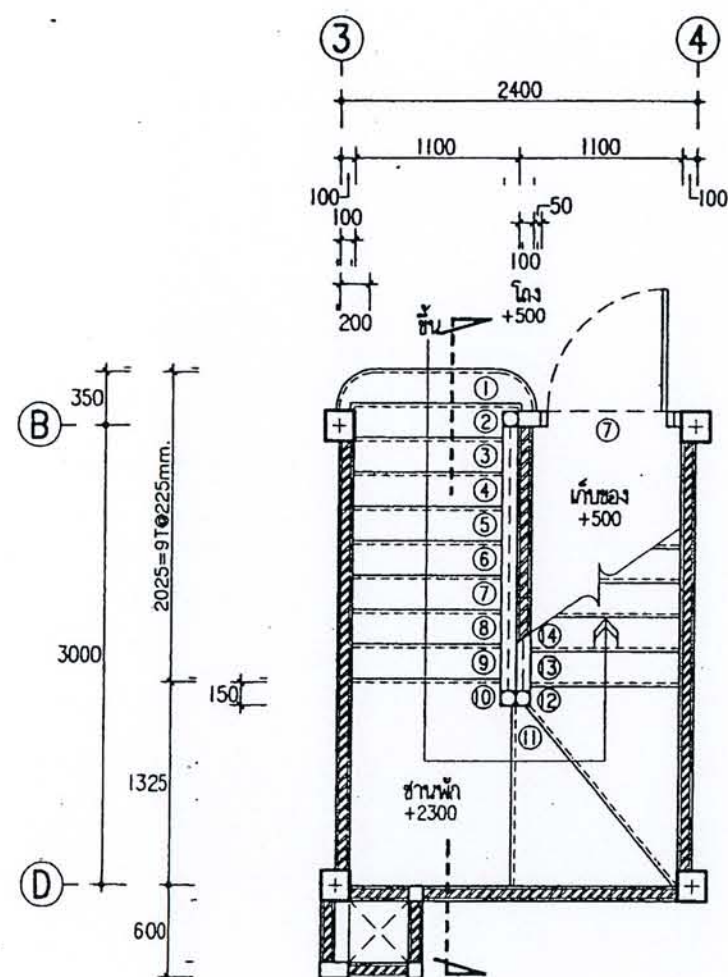

แปลนขยายบ้านได้ชั้นล่าง

มาตราส่วน 1:50

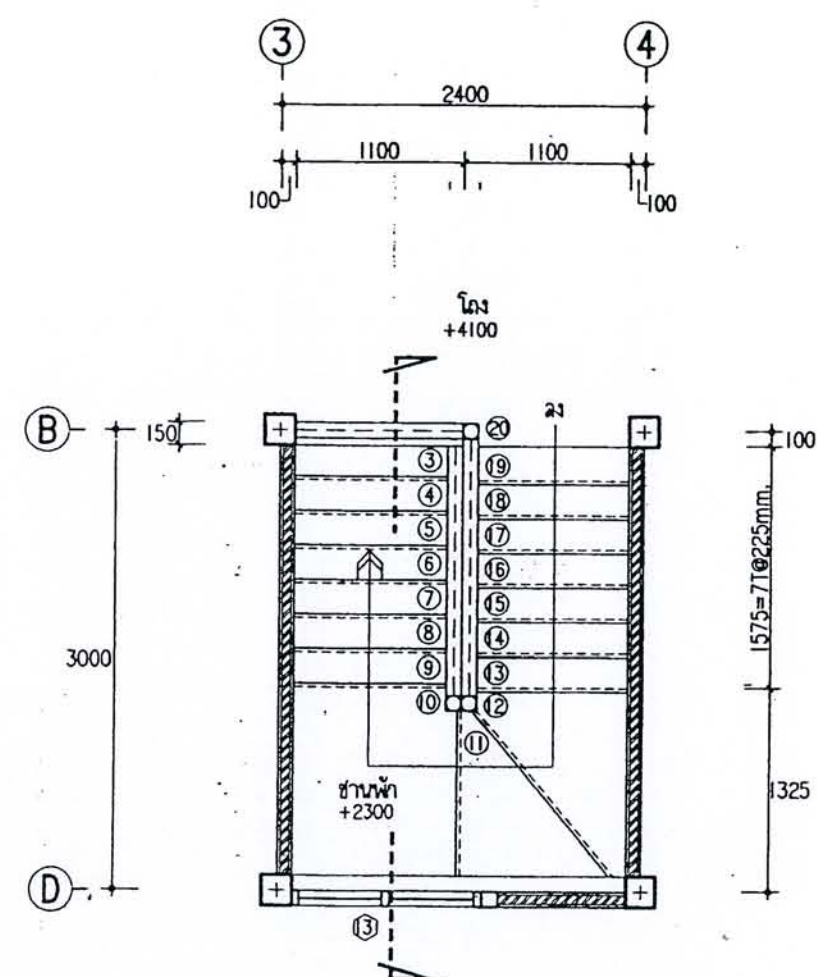

แปลนขยายบ้านได้ชั้นบน

มาตราส่วน 1:50


ได้รับความอนุเคราะห์แบบ
จาก
บริษัท แลนด์ โฮม
(ประเทศไทย) จำกัด



ตามนโยบาย
ม.ร.ว. สุขุมพันธุ์ บริพัตร
ผู้ว่าราชการกรุงเทพมหานคร

โดยสำนักการโยธา
กรุงเทพมหานคร

ได้รับความอนุเคราะห์แบบ
จาก
บริษัท แลนด์ โฮม
(ประเทศไทย) จำกัด

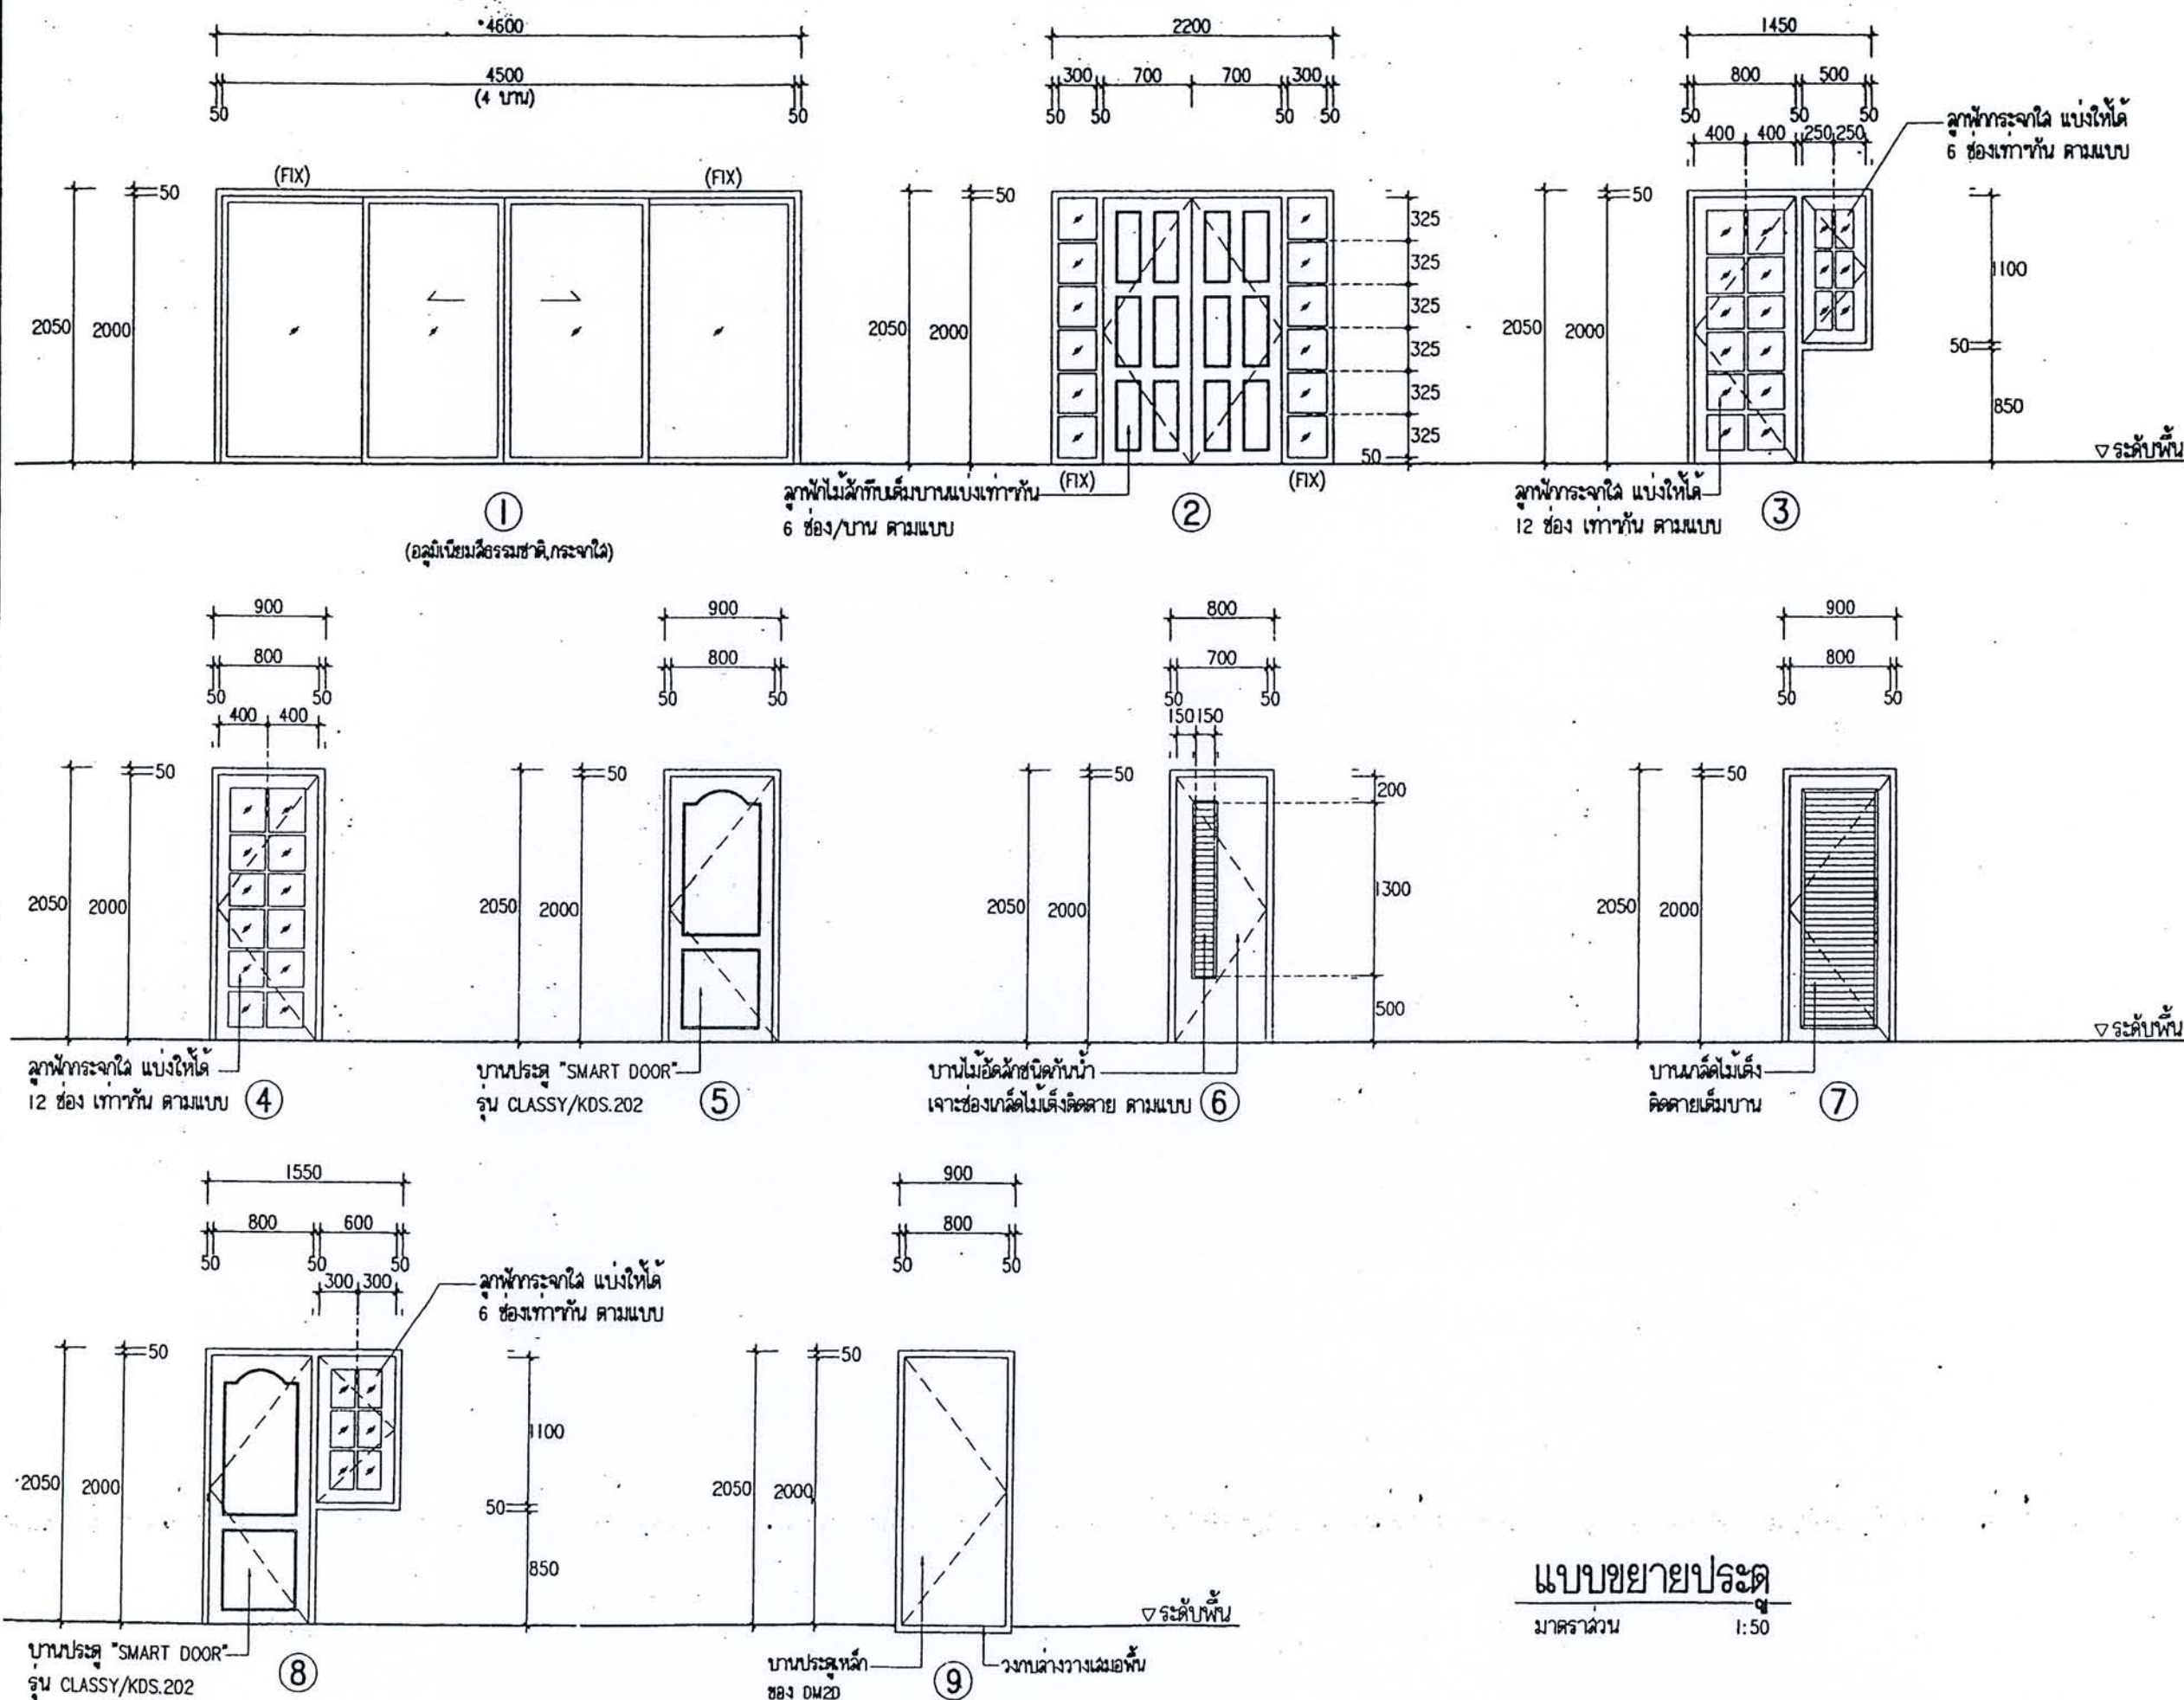




โครงการ
แบบบ้านยืมเพื่อประชาชน

ตามนโยบาย
ม.ร.ว. สุขุมพันธุ์ บริพัตร
ผู้ว่าราชการกรุงเทพมหานคร

โดยสำนักงานโยธา
กรุงเทพมหานคร

ได้รับความอนุเคราะห์แบบ
จาก
บริษัท แลนด์ โสม
(ประเทศไทย) จำกัด



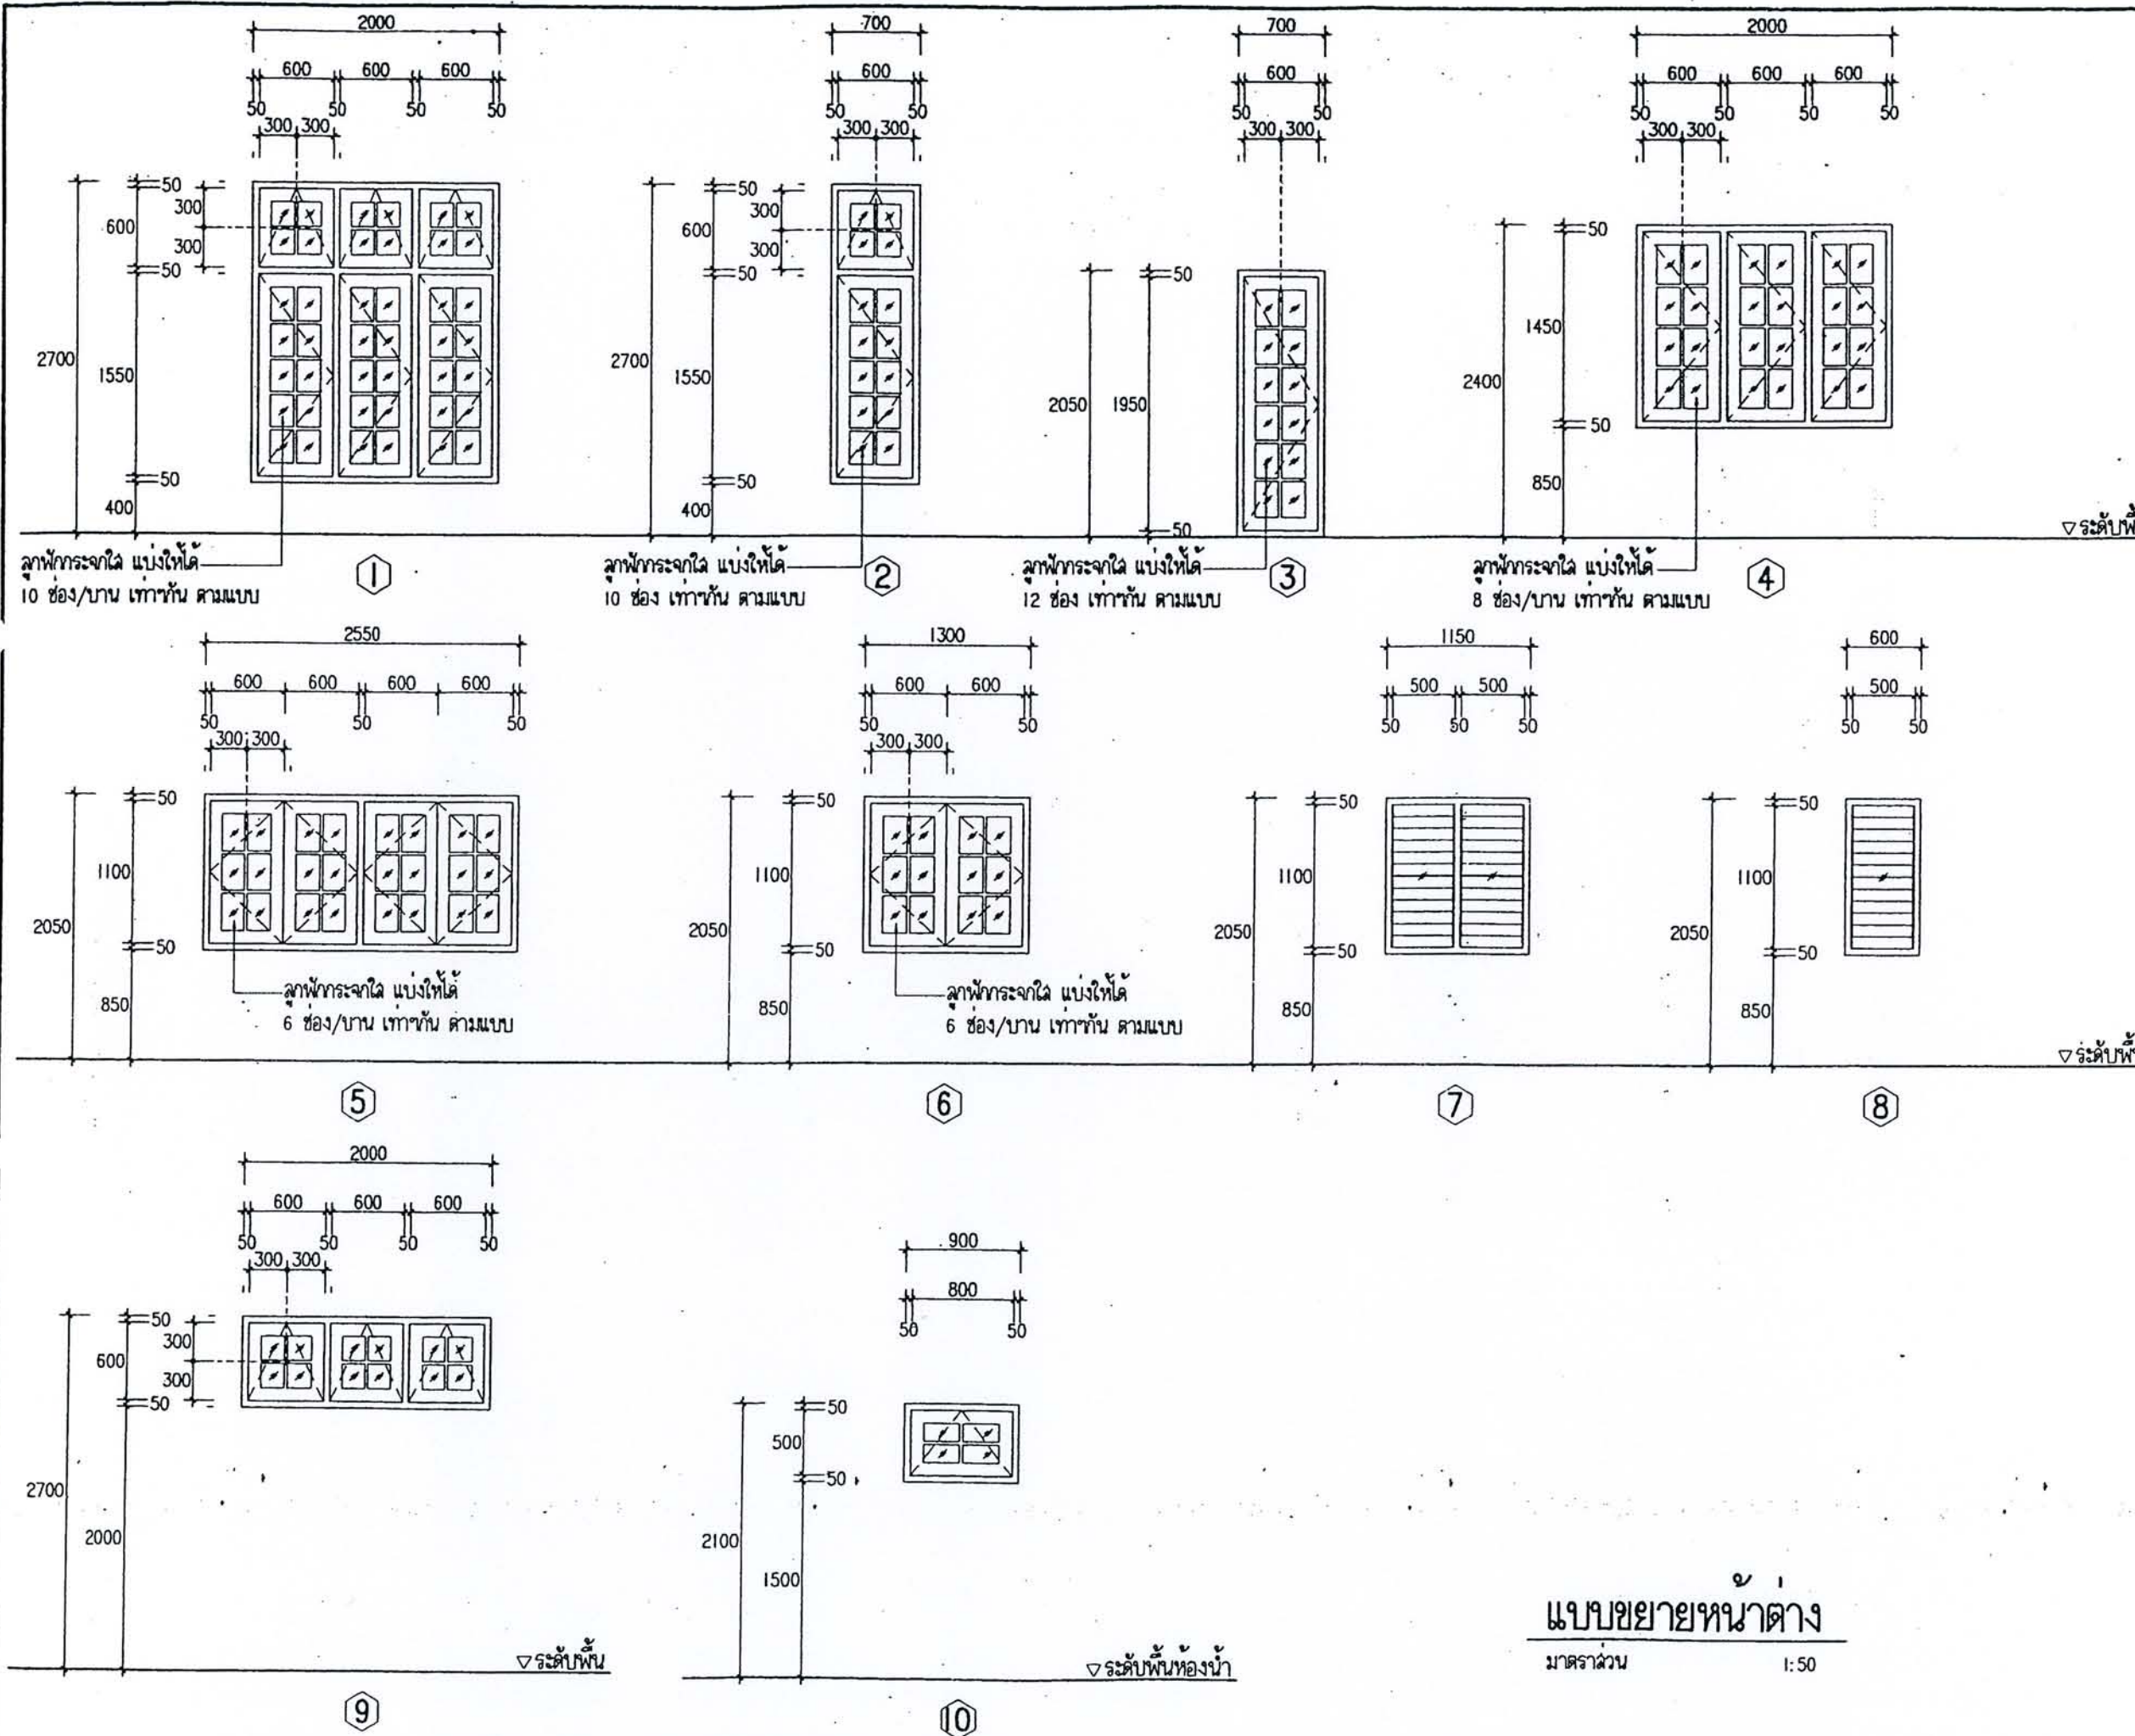




โครงการ
แบบบ้านยืมเพื่อประชาชน

ตามนโยบาย
ม.ร.ว. สุขุมพันธุ์ บริพัตร
ผู้ว่าราชการกรุงเทพมหานคร

โดยสำนักงานโยธา
กรุงเทพมหานคร

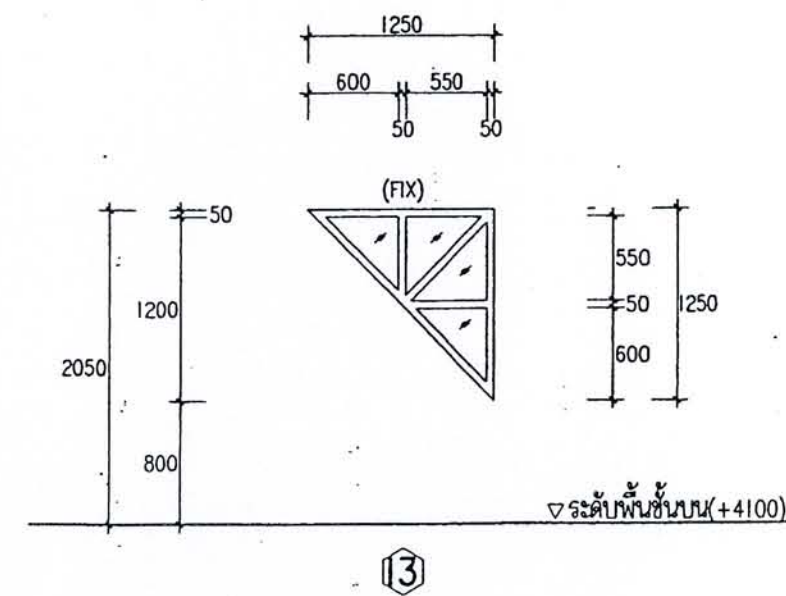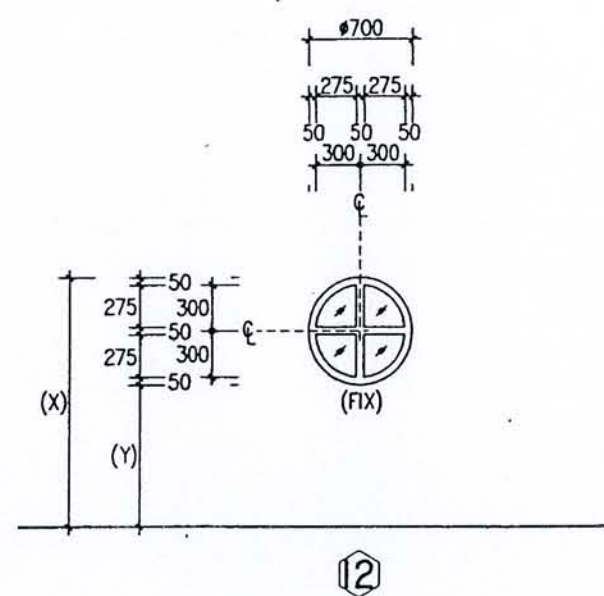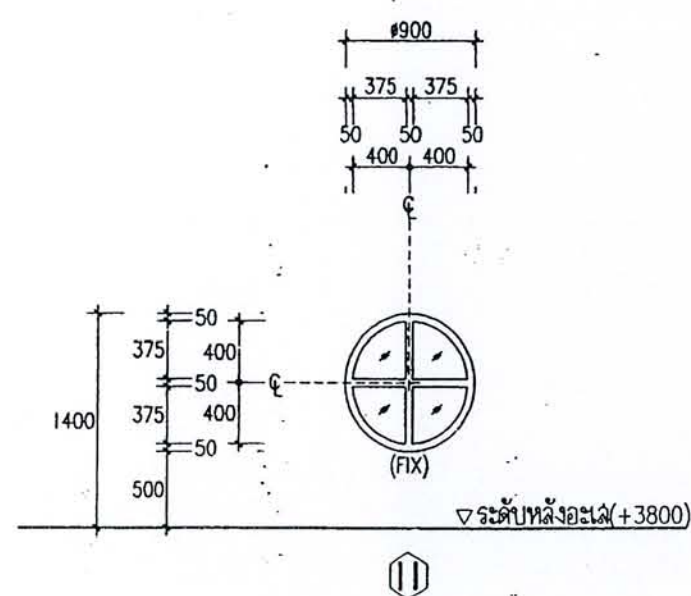


ห้อง	ระยะ mm.	(X)	(Y)
ห้องอะไหล่ใหญ่		1625	925
จอตรง		2550	1850

แบบขยายขนาดต่าง
มาตราส่วน 1:50

ได้รับความอนุเคราะห์แบบ
จาก
บริษัท แลนด์ โสภ
(ประเทศไทย) จำกัด



โดยสำนักการโยธา
กรุงเทพมหานคร

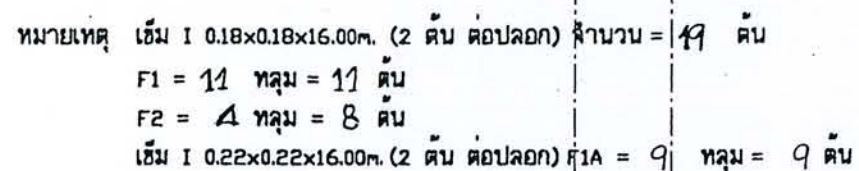

ผังโครงสร้างฐานราก
มาตราส่วน 1:100

ได้รับความอนุเคราะห์แบบ
จาก
บริษัท แลนด์ โสม
(ประเทศไทย) จำกัด




ตามนโยบาย
ม.ร.ว. สุขุมพันธุ์ บริพัตร
ผู้ว่าราชการกรุงเทพมหานคร

โดยสำนักการโยธา
กรุงเทพมหานคร

ได้รับความอนุเคราะห์แบบ

จาก
บริษัท แลนด์ โฮม
(ประเทศไทย) จำกัด

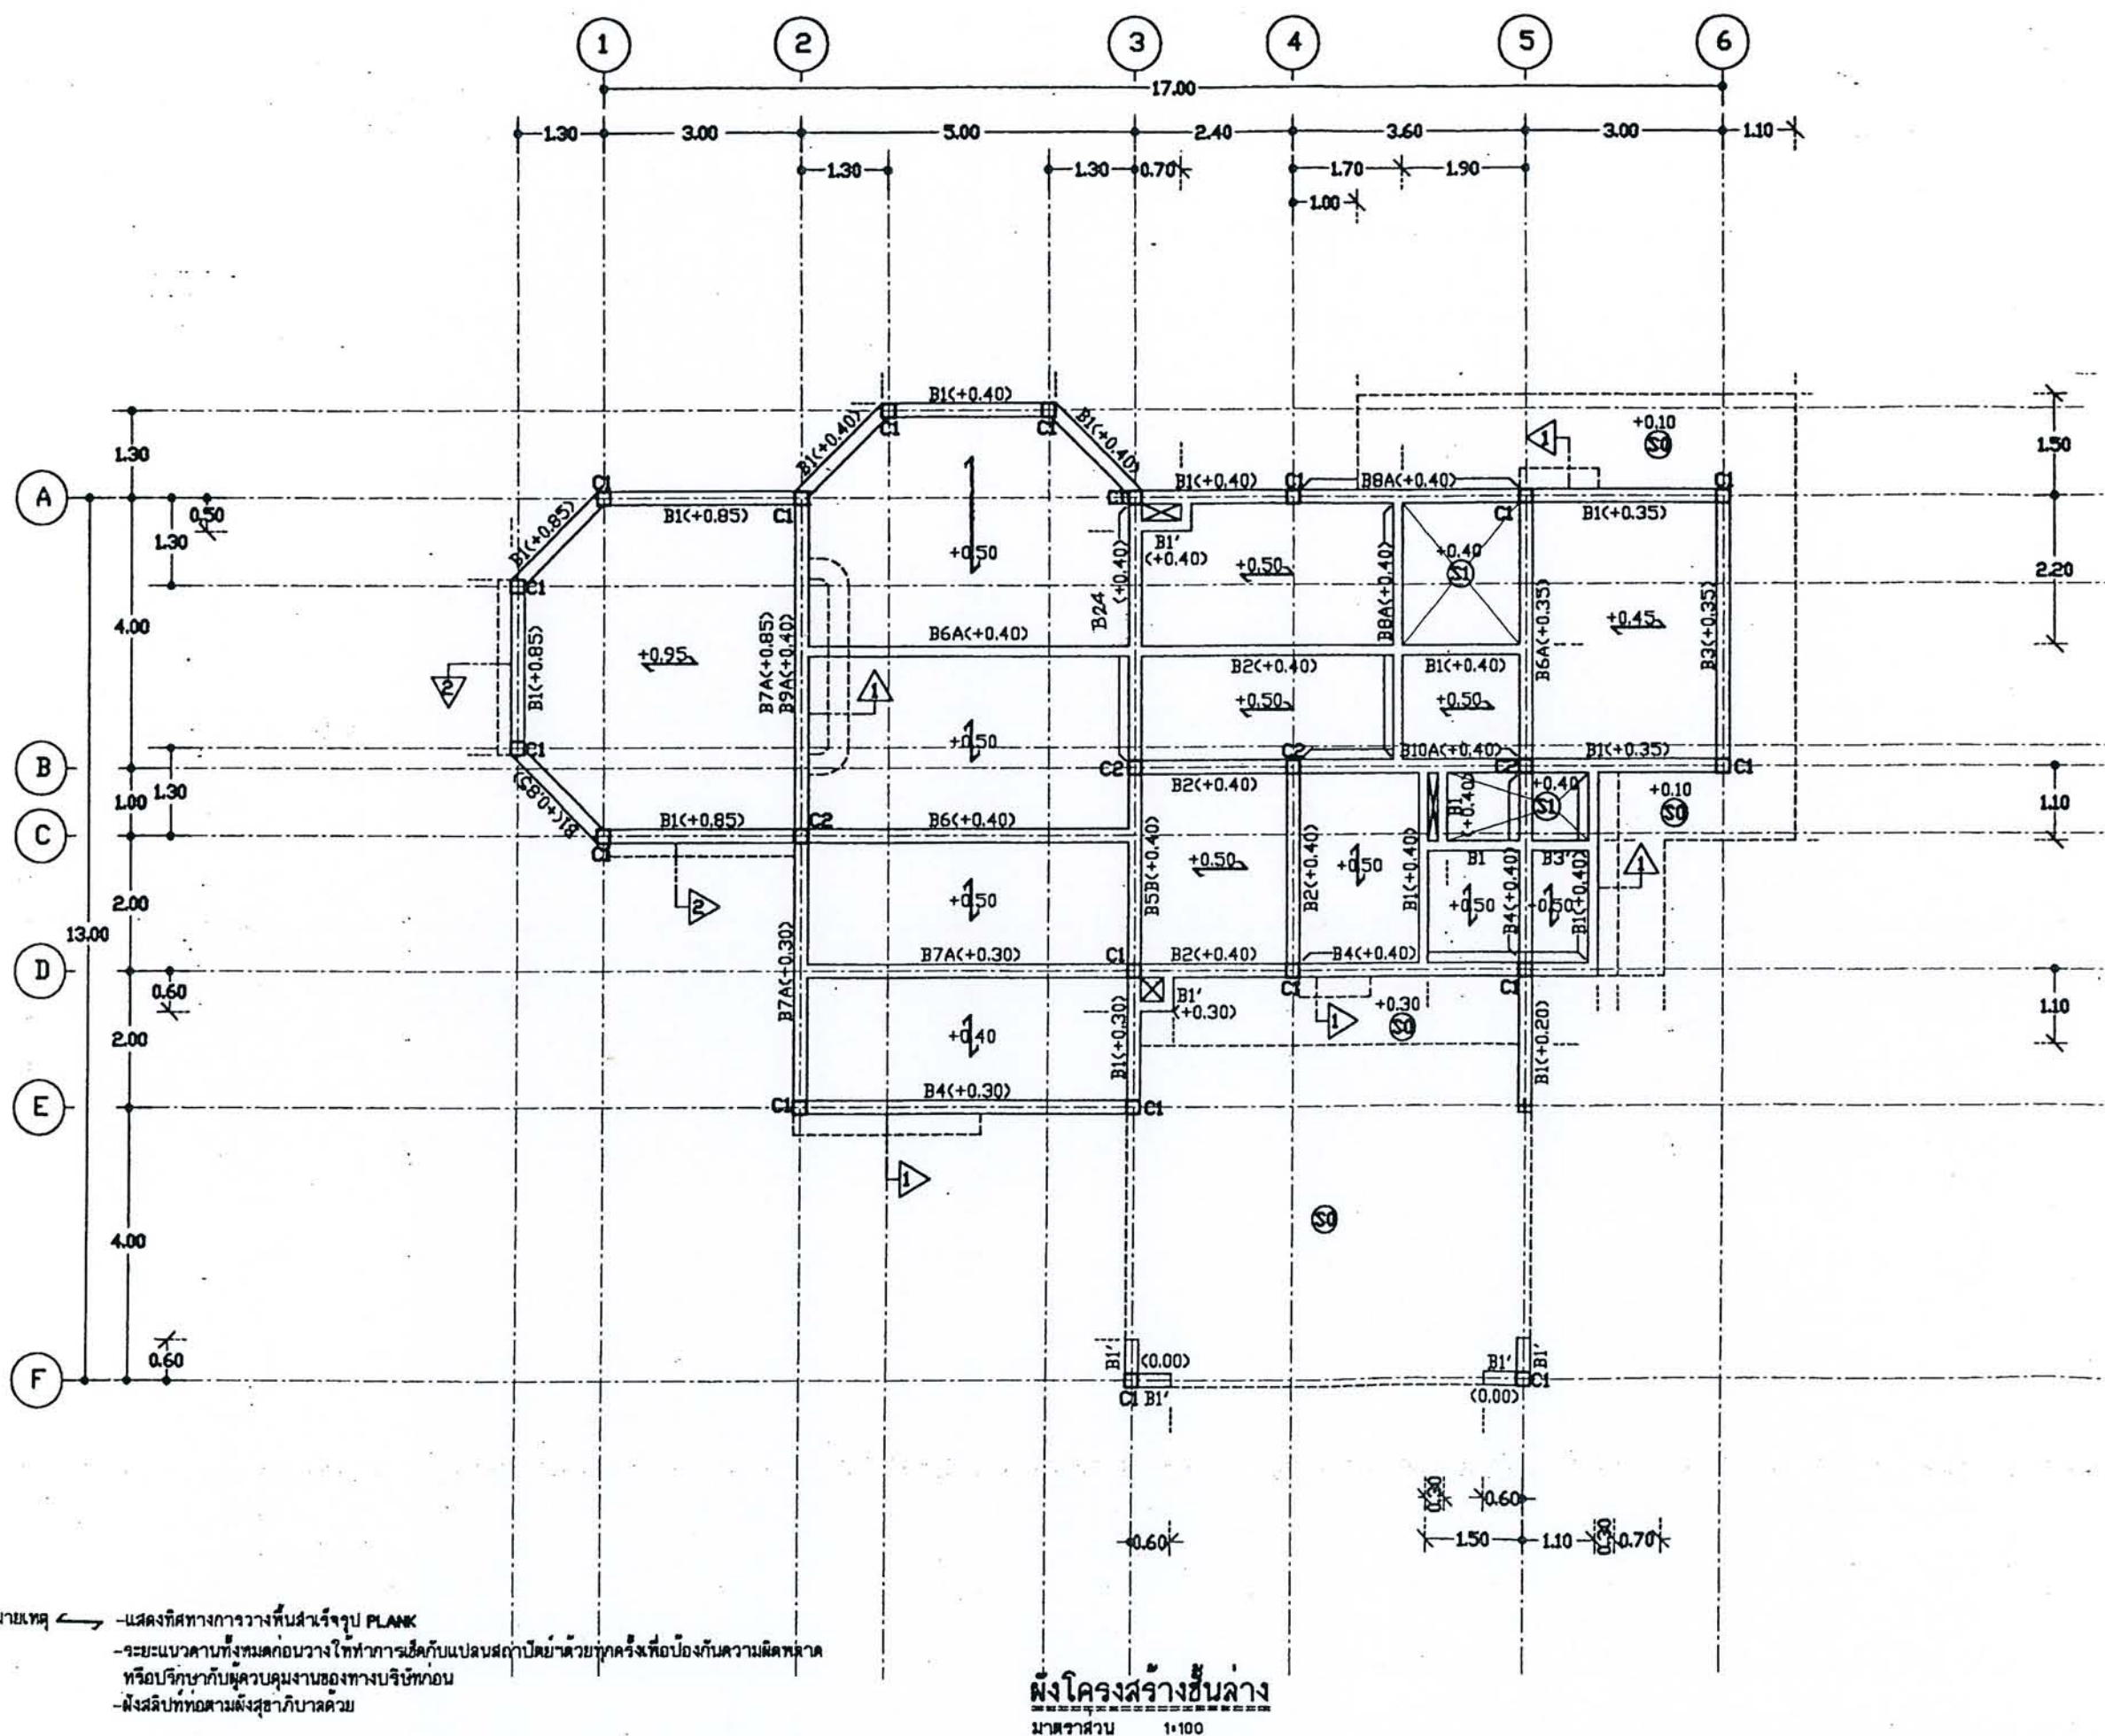



โครงการ
แบบบ้านยืมเพื่อประชาชน

ตามนโยบาย
ม.ร.ว. สุขุมพันธุ์ บริพัตร
ผู้ว่าราชการกรุงเทพมหานคร

โดยสำนักงานโยธา
กรุงเทพมหานคร

ผังโครงสร้างชั้นบน
มาตราส่วน 1:100

ได้รับความอนุเคราะห์แบบ
จาก
บริษัท แลนด์ ไสว
(ประเทศไทย) จำกัด




โครงการ
แบบบ้านยืมเพื่อประชาชน

ตามนโยบาย
ม.ร.ว. สุขุมพันธุ์ บริพัตร
ผู้ว่าราชการกรุงเทพมหานคร

โดยสำนักการโยธา
กรุงเทพมหานคร

ได้รับความอนุเคราะห์แบบ
จาก
บริษัท แลนด์ โสม
(ประเทศไทย) จำกัด

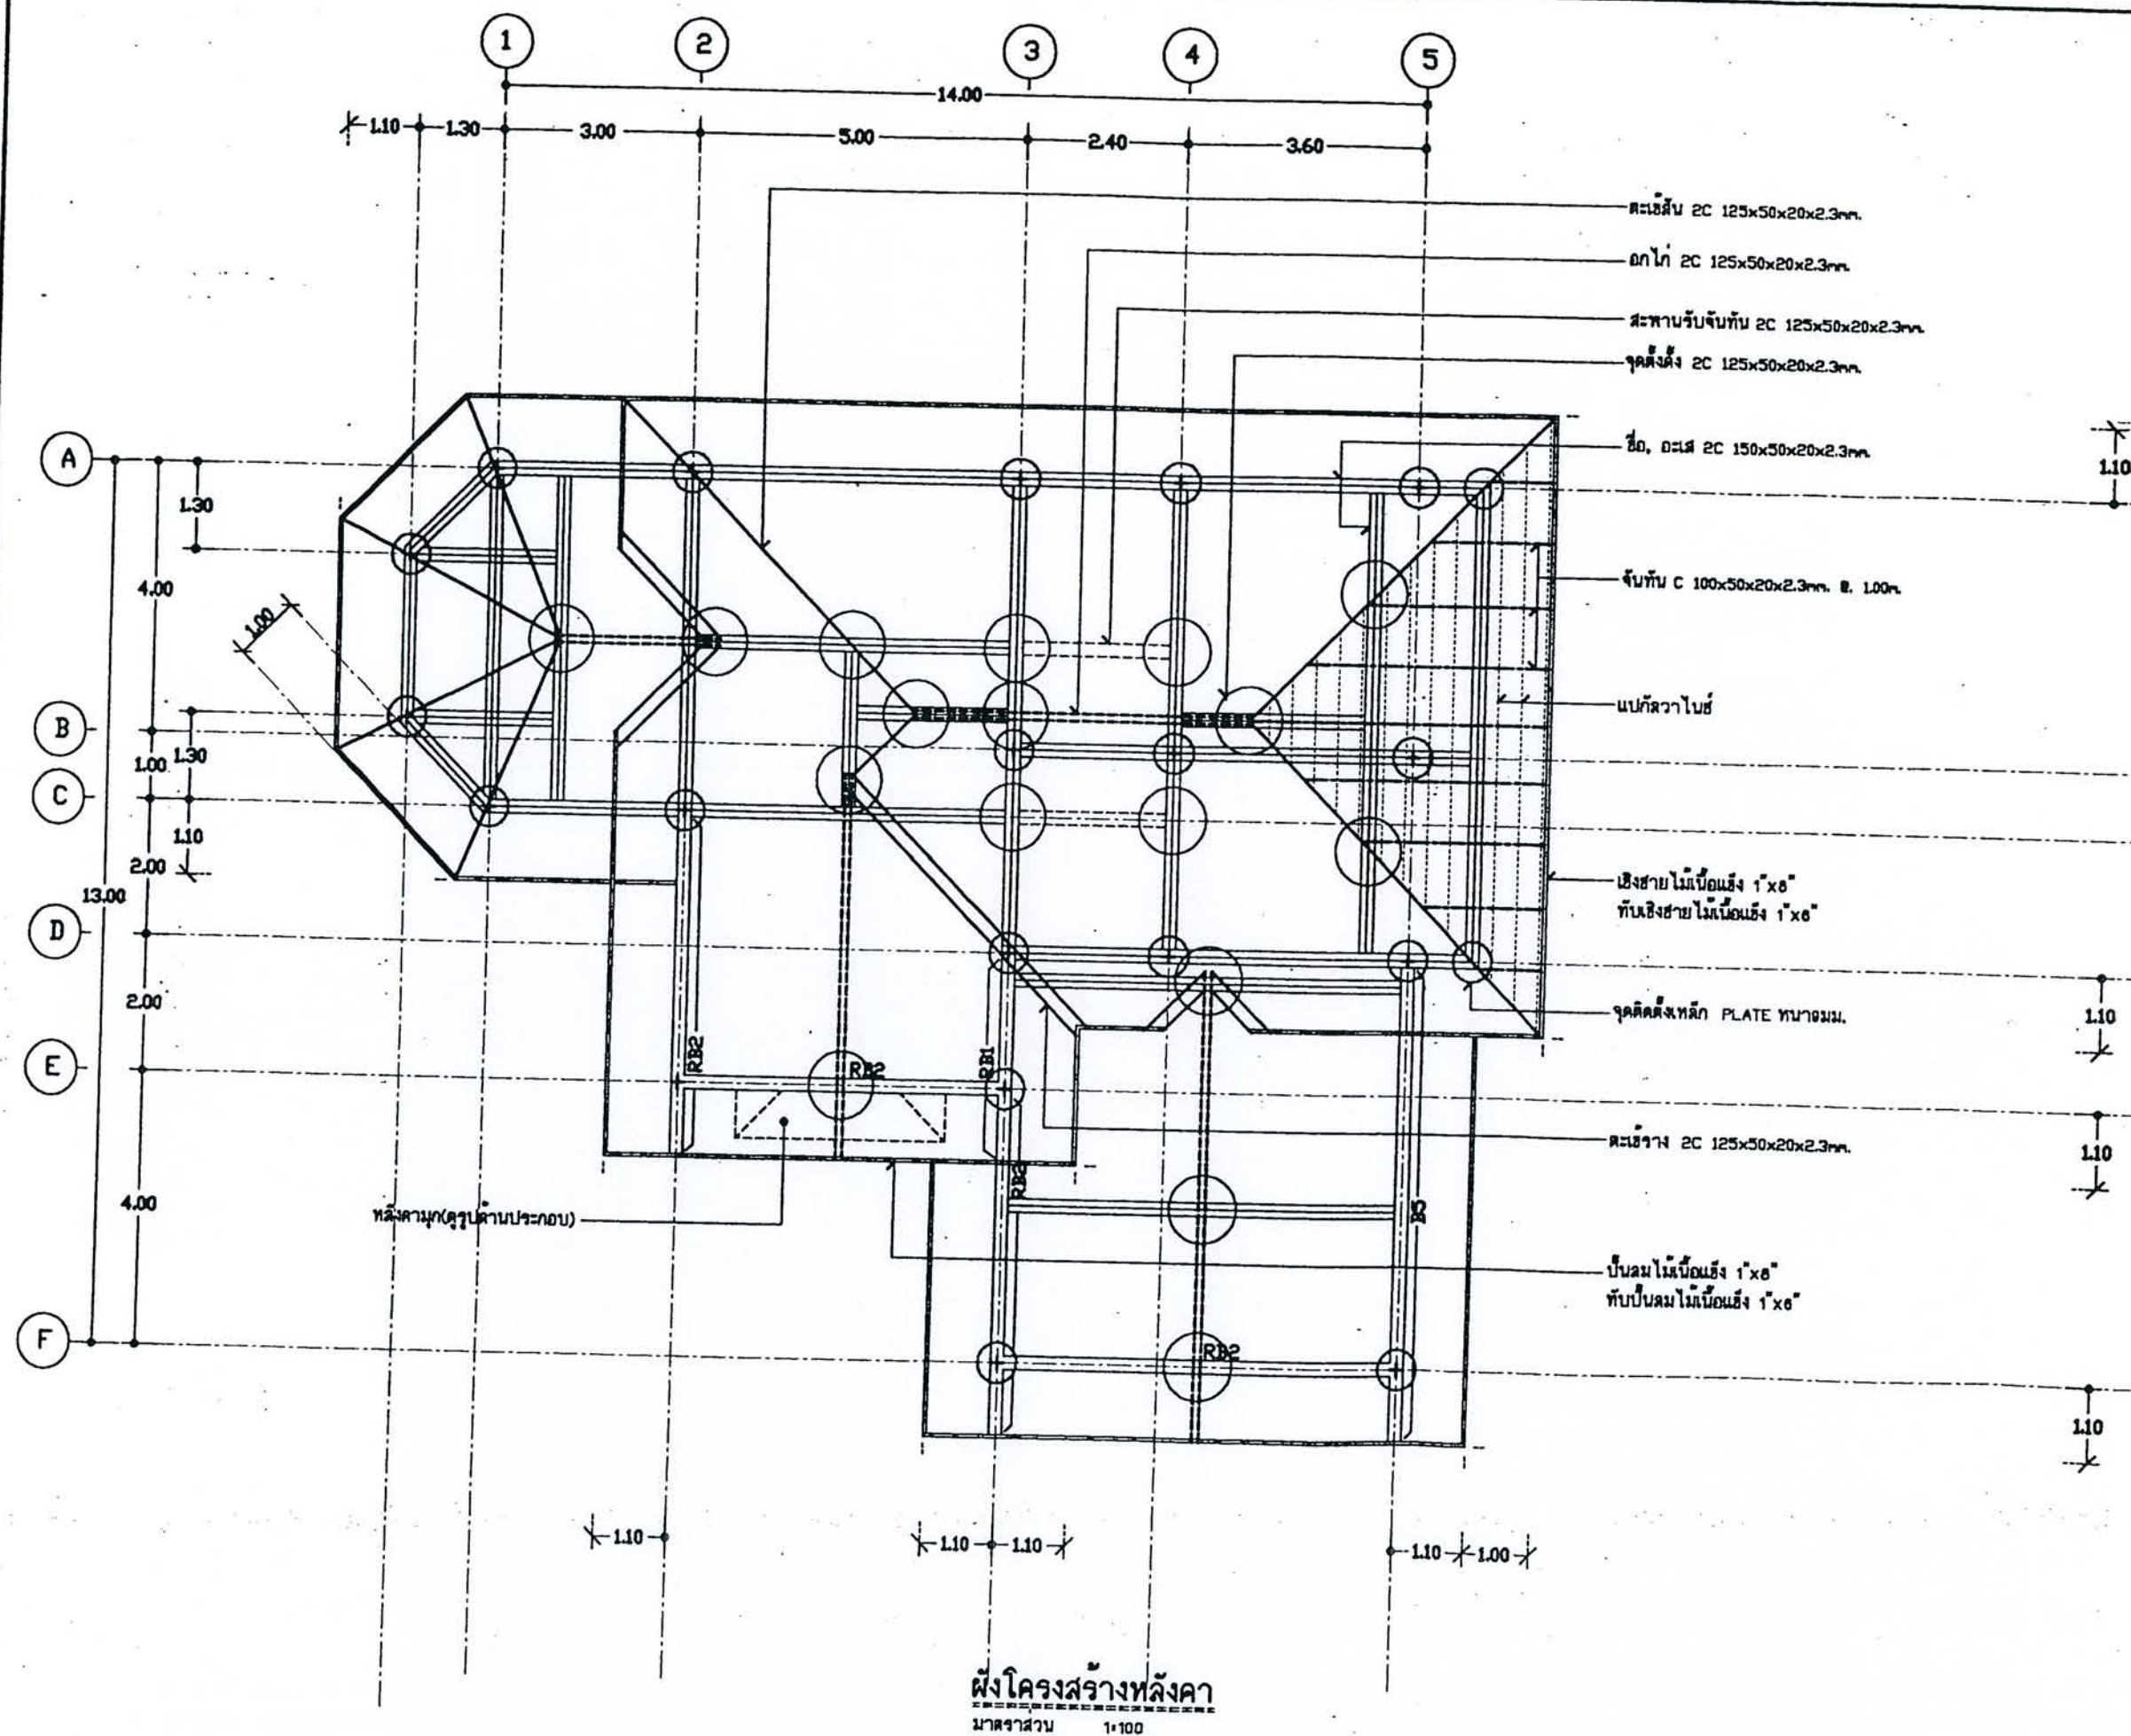





โครงการ
แบบบ้านยืมเพื่อประชาชน

ตามนโยบาย
ม.ร.ว. สุขุมพันธุ์ บริพัตร
ผู้ว่าราชการกรุงเทพมหานคร


โดยสำนักงานโยธา
กรุงเทพมหานคร

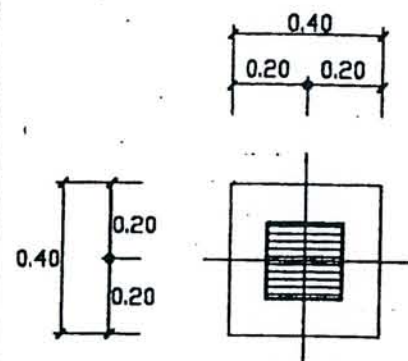


PLAN F1A

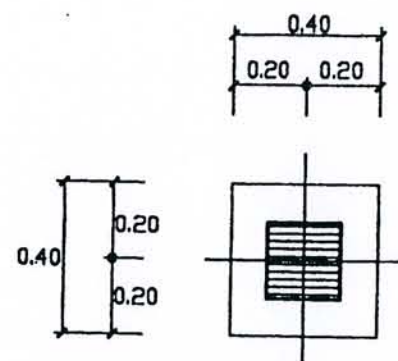


PLAN F1

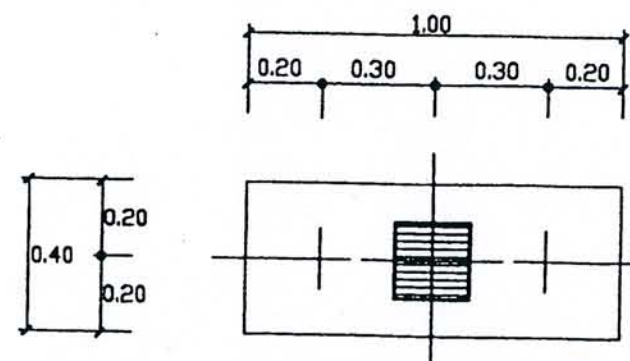


PLAN F2

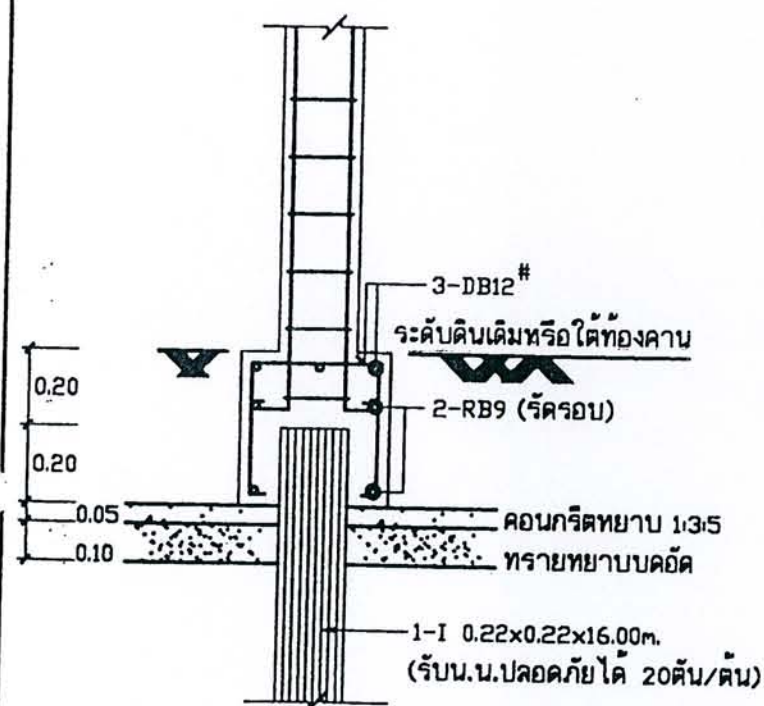

SECTION F1A 1:20

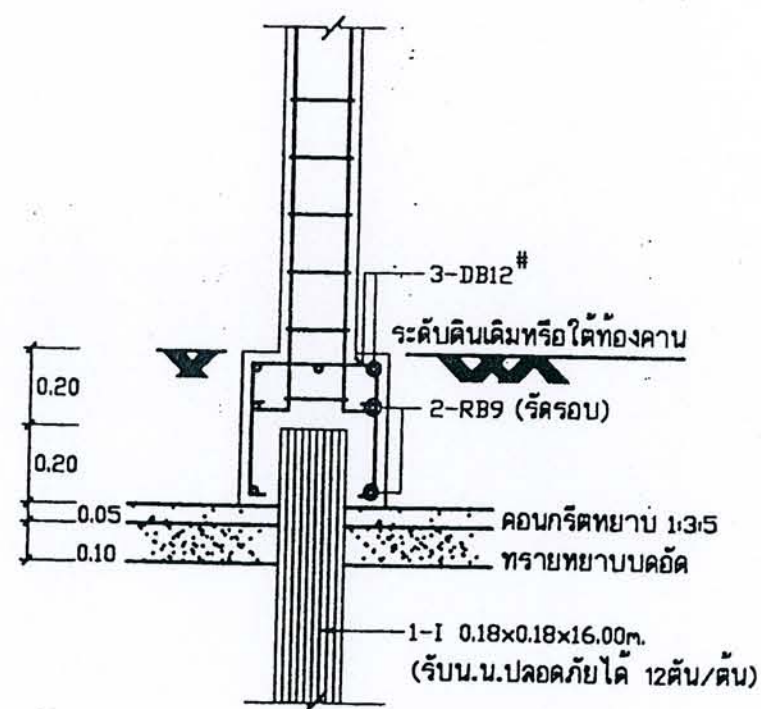

SECTION F1 1:20

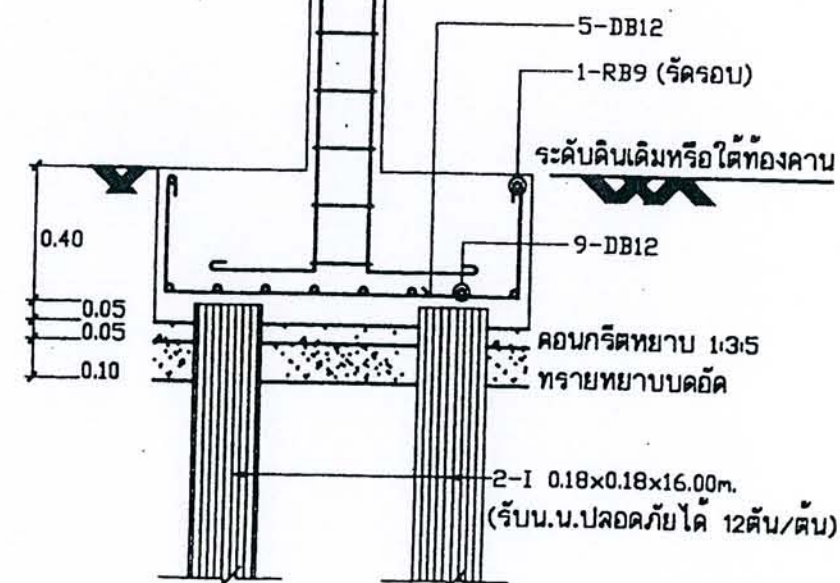

SECTION F2 1:20

ได้รับความอนุเคราะห์แบบ
จาก
บริษัท แลนด์ โสภ
(ประเทศไทย) จำกัด




โครงการ
แบบบ้านยืมเพื่อประชาชน

ตามนโยบาย
ม.ร.ว. สุขุมพันธุ์ บริพัตร
ผู้ว่าราชการกรุงเทพมหานคร

โดยสำนักงานโยธา
กรุงเทพมหานคร

FLOOR 2		
FLOOR 1		
FOOTING		
	C1	C2

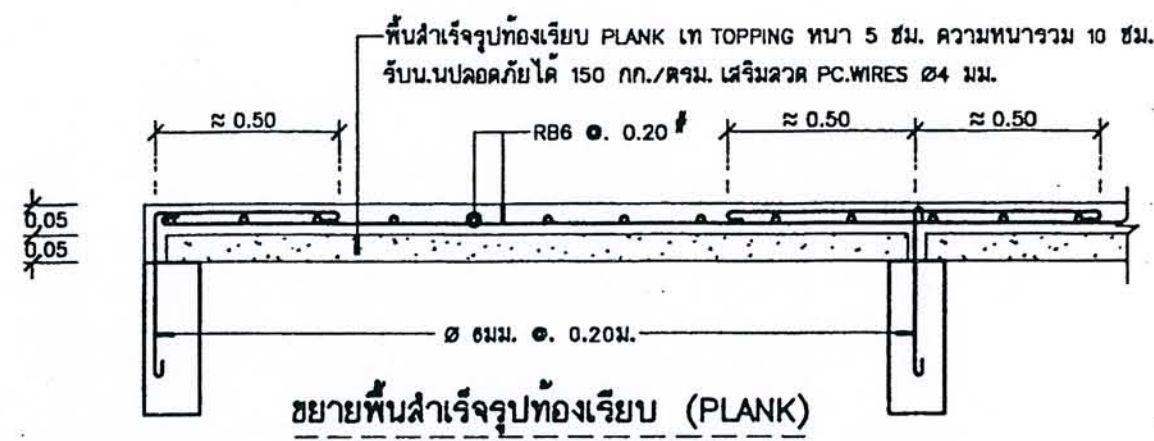

ตารางแสดงการรับน้ำหนักจร (LIVE LOAD)												
สำหรับพื้นสำเร็จรูปแบบท้องเรียบ PLANK ขนาดหน้าตัด 0.05x0.35 ม.												
N \ S	2.80	3.00	3.20	3.40	3.60	3.80	4.00	4.20	4.40	4.60	4.80	5.00
4	504											
5		532	464	400	350	300						
6							318	274				
7									305	300		
8											300	250

- หมายเหตุ - มีค้ำยันชั่วคราว
 - S = ระยะช่วงท้าวค้ำยันในถึงขอบในของคาน (CLEAR SPAN) หน่วยเป็นเมตร
 - N = จำนวนท้าวค้ำยัน ขนาด ๒ 4 มม.
 - ตัวเลขในตารางแสดงความสามารถในการรับน้ำหนักจรทุกหน่วยเป็น กก./ตารางเมตร

SECTION COLUMN 1:20


ได้รับความอนุเคราะห์แบบ
จาก
บริษัท แลนด์ โฮม
(ประเทศไทย) จำกัด




โครงการ
แบบบ้านยืมเพื่อประชาชน

ตามนโยบาย
ม.ร.ว. สุขุมพันธุ์ บริพัตร
ผู้ว่าราชการกรุงเทพมหานคร

โดยสำนักงานโยธา
กรุงเทพมหานคร

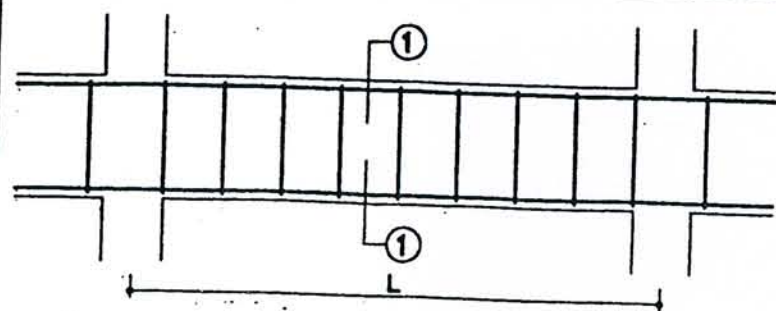


LONG SECTION

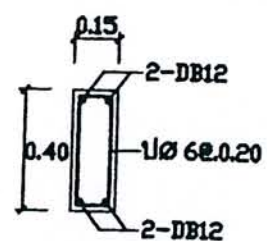


SECTION 1-1

B1

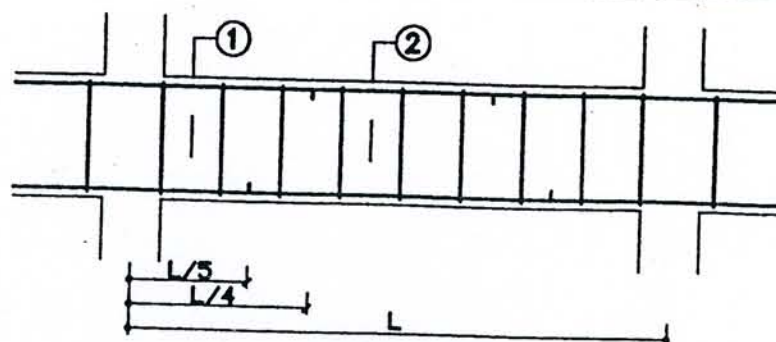


LONG SECTION

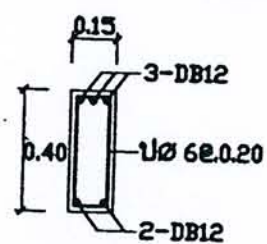


SECTION 1-1


B2

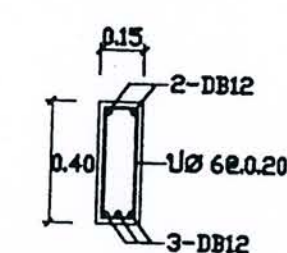

SECTION 2-2

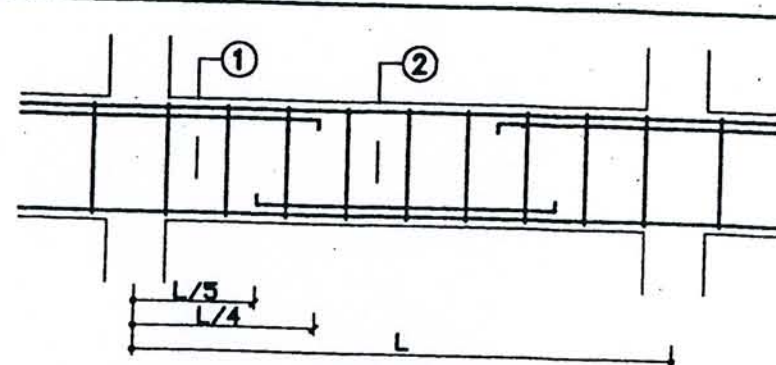


LONG SECTION

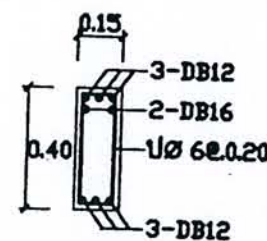


SECTION 1-1


B5

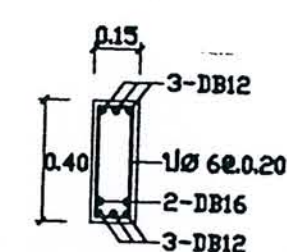

SECTION 2-2

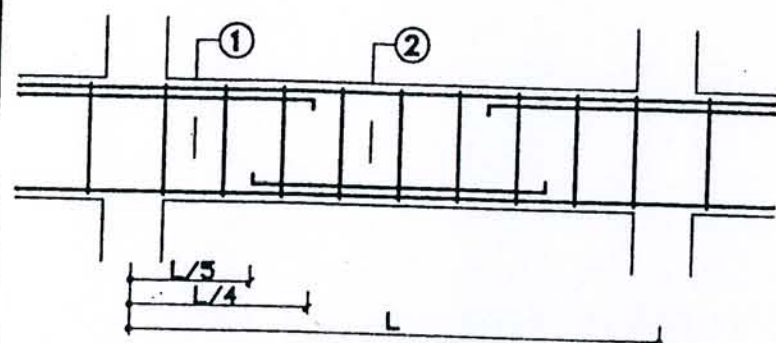


LONG SECTION

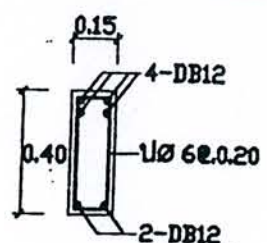


SECTION 1-1


B3

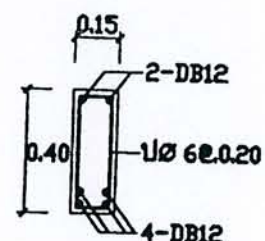

SECTION 2-2

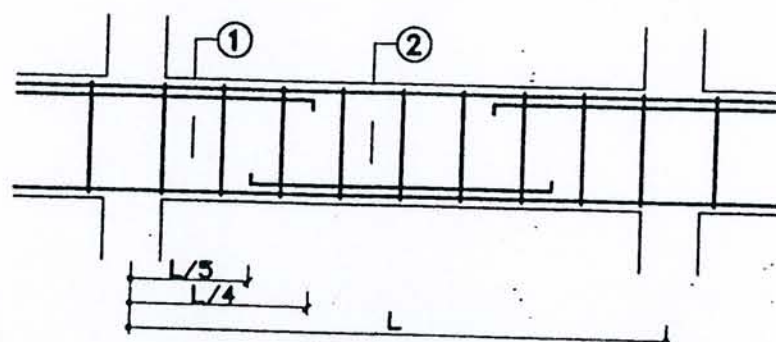


LONG SECTION

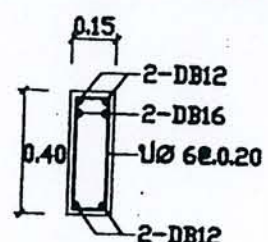


SECTION 1-1


B4

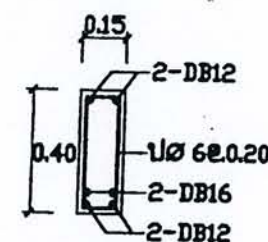

SECTION 2-2

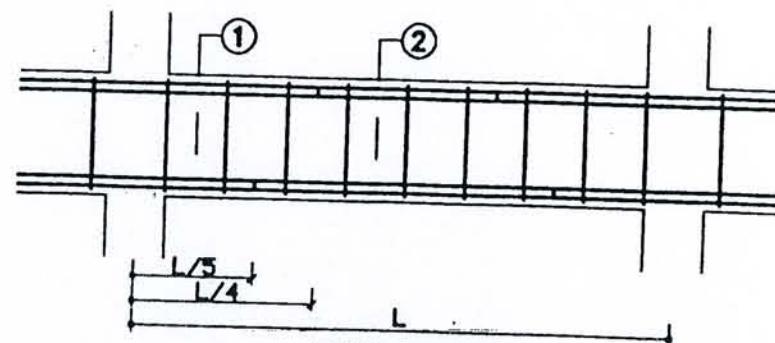


LONG SECTION

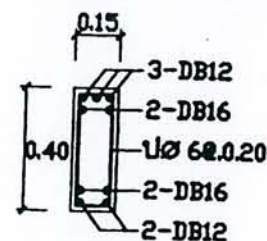


SECTION 1-1

B6

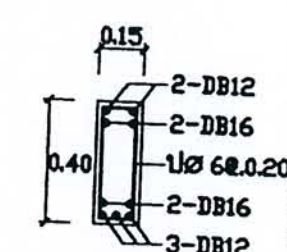


SECTION 2-2

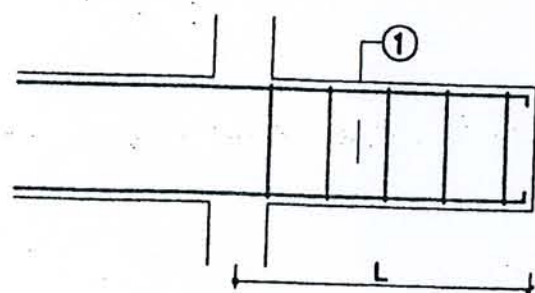


LONG SECTION

B1'

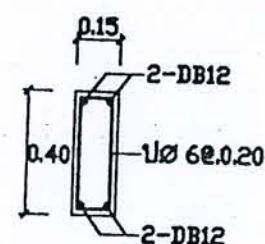


SECTION 1-1

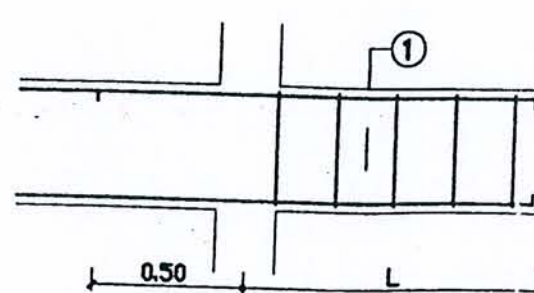


LONG SECTION

B2'

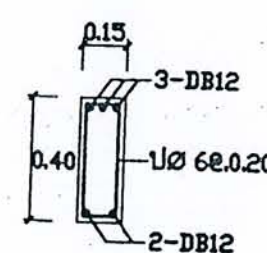

SECTION 1-1

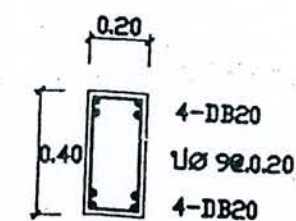

B24


ได้รับความอนุเคราะห์แบบ
จาก
บริษัท แลนด์ ไฮบ
(ประเทศไทย) จำกัด



โครงการ
แบบบ้านยืมเพื่อประชาชน

ตามนโยบาย
ม.ร.ว. สุขุมพันธุ์ บริพัตร
ผู้ว่าราชการกรุงเทพมหานคร

โดยสำนักงานโยธา
กรุงเทพมหานคร

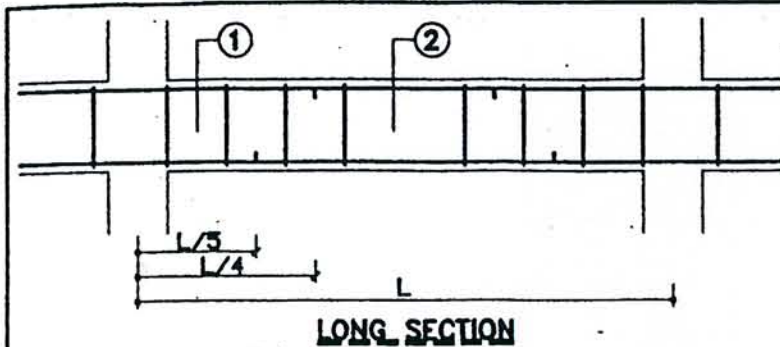


LONG SECTION




SECTION 1-1

RB2

SECTION 2-2

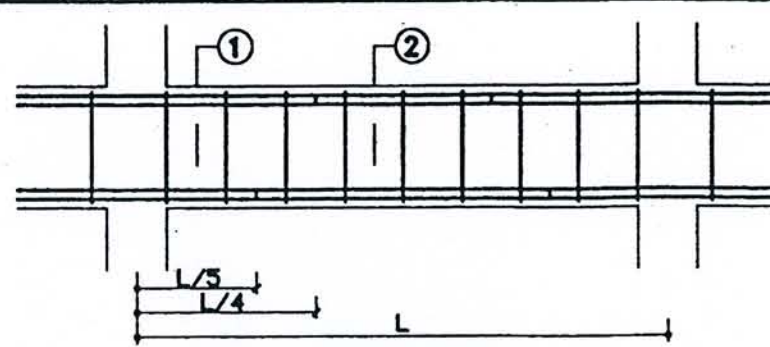


LONG SECTION

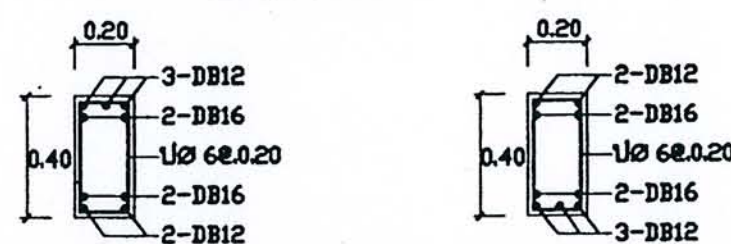


SECTION 1-1

B6A

SECTION 2-2

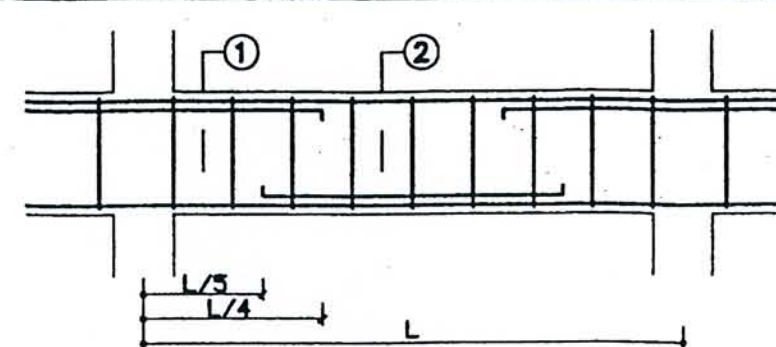


LONG SECTION

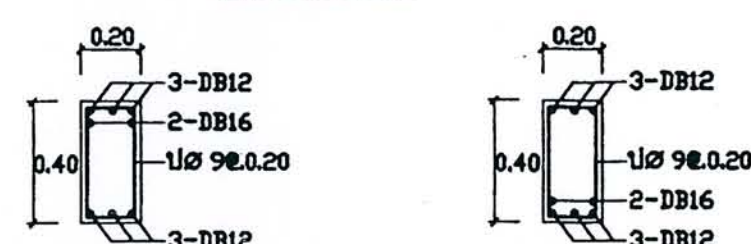


SECTION 1-1

B5B

SECTION 2-2

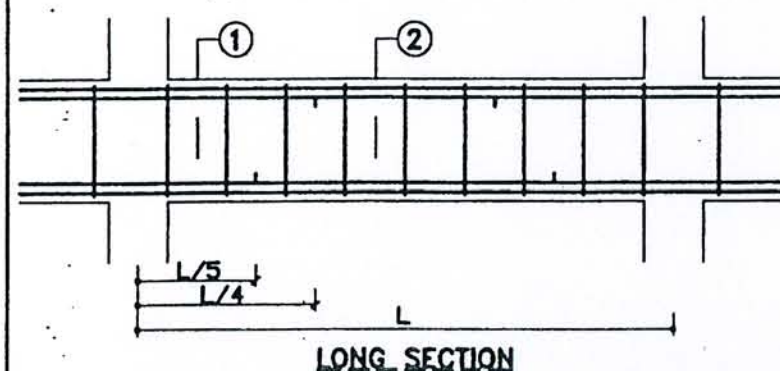


LONG SECTION

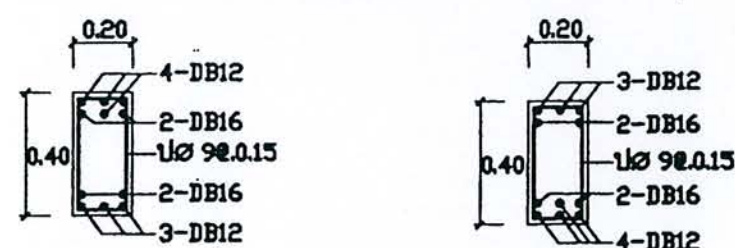


SECTION 1-1

B7A


SECTION 2-2

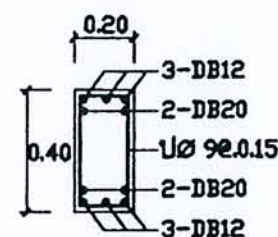


B8A

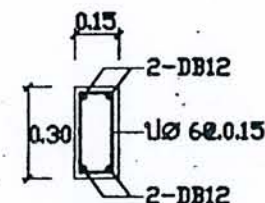

RB1

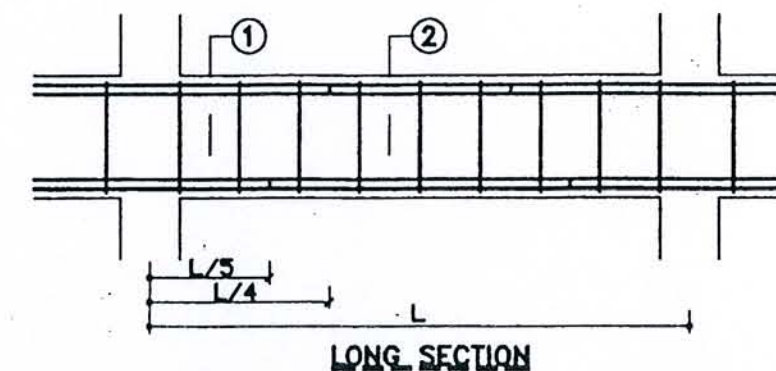


LONG SECTION

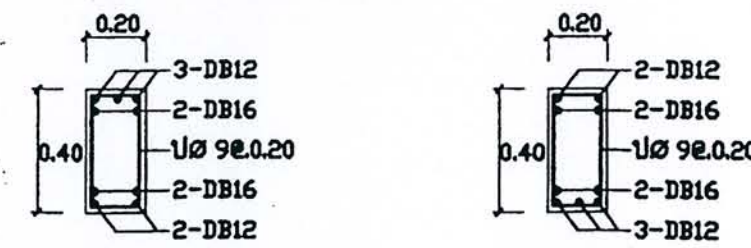


SECTION 1-1

B6B


SECTION 2-2

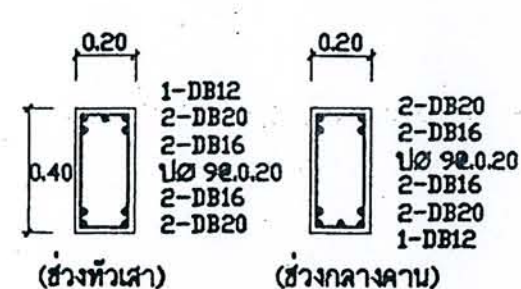

B9A

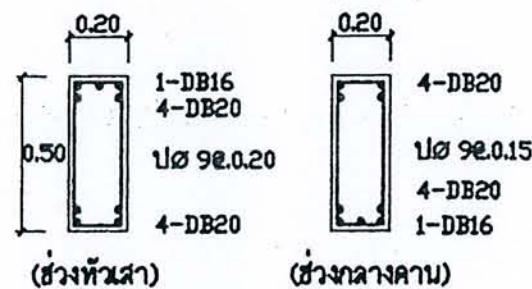


B18

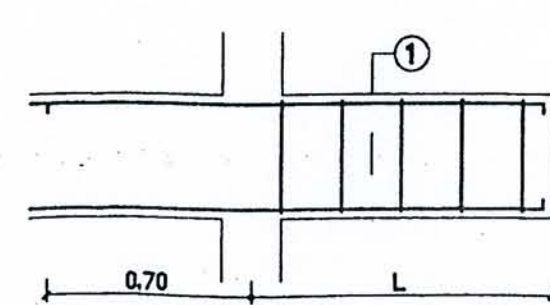

LONG SECTION

B3'

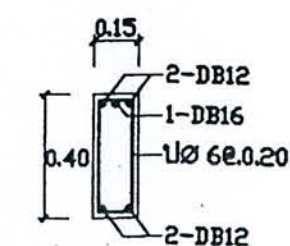

SECTION 1-1


ได้รับความอนุเคราะห์แบบ
จาก
บริษัท แลนด์ โฮม
(ประเทศไทย) จำกัด




โครงการ
แบบบ้านยืมเพื่อประชาชน

ตามนโยบาย
ม.ร.ว. สุขุมพันธุ์ บริพัตร
ผู้ว่าราชการกรุงเทพมหานคร


โดยสำนักงานโยธา
กรุงเทพมหานคร

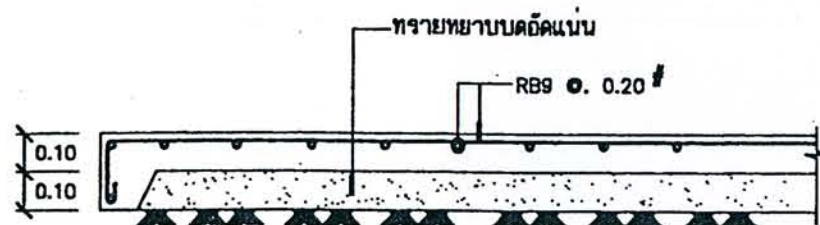


S0

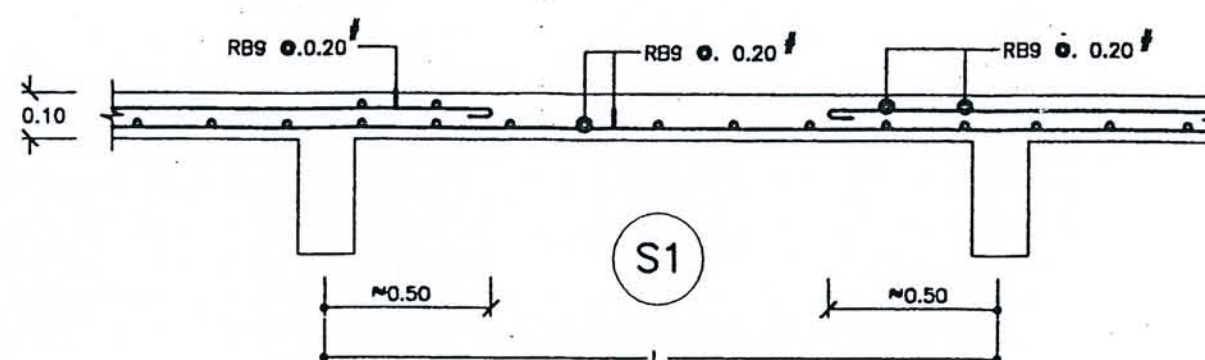


S1

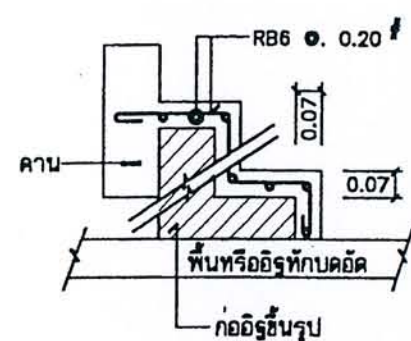


SECTION - 1
(ตามแบบโครงสร้างชั้นล่าง)

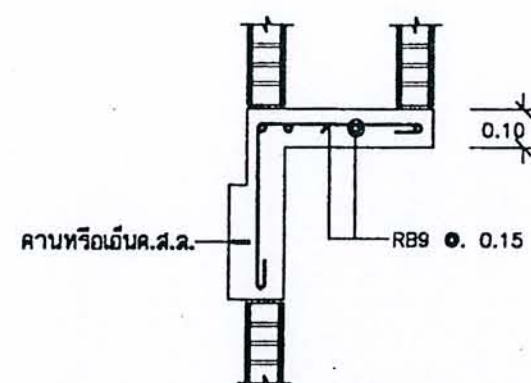


SECTION - 2
(ตามแบบโครงสร้าง)

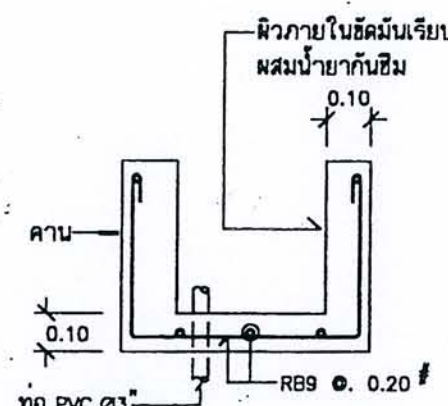


SECTION - 3
(ตามแบบโครงสร้างชั้นบน)

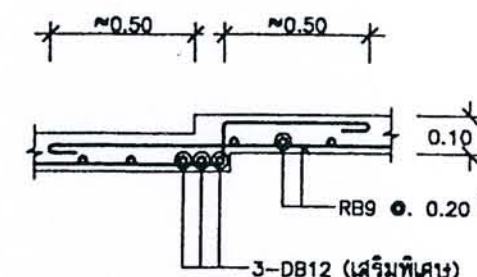


ขยายพื้นลดระดับ

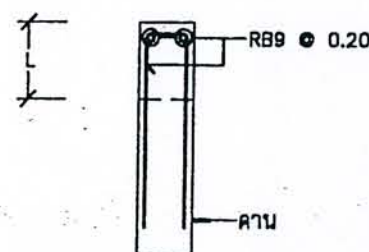

แบบขยายการทาบารับพื้น

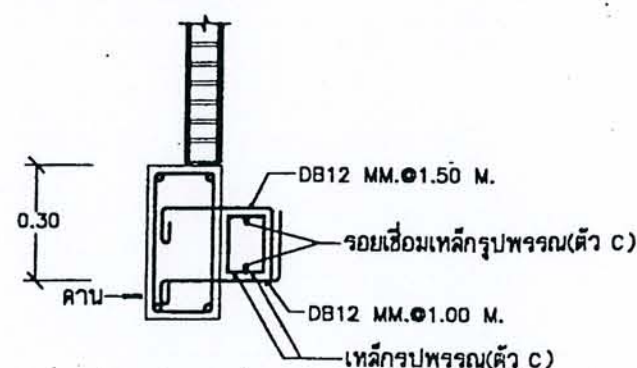

แบบขยายจุดที่มีหลังคารอบล่างติดผนัง

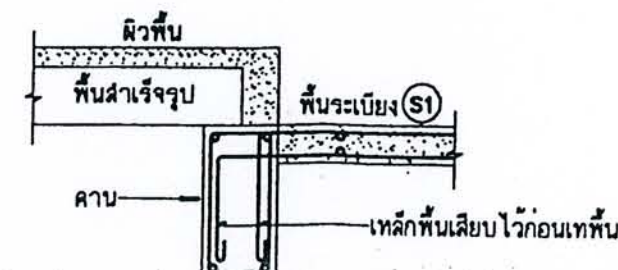

แบบขยายรอยต่อพื้นกับระเบียง


ได้รับความอนุเคราะห์แบบ
จาก
บริษัท แลนด์ ไส
(ประเทศไทย) จำกัด




ตามนโยบาย
ม.ร.ว. สุขุมพันธุ์ บริพัตร
ผู้ว่าราชการกรุงเทพมหานคร


โดยสำนักการโยธา
กรุงเทพมหานคร

ได้รับความอนุเคราะห์แบบ
จาก
บริษัท แลนด์ โสม
(ประเทศไทย) จำกัด

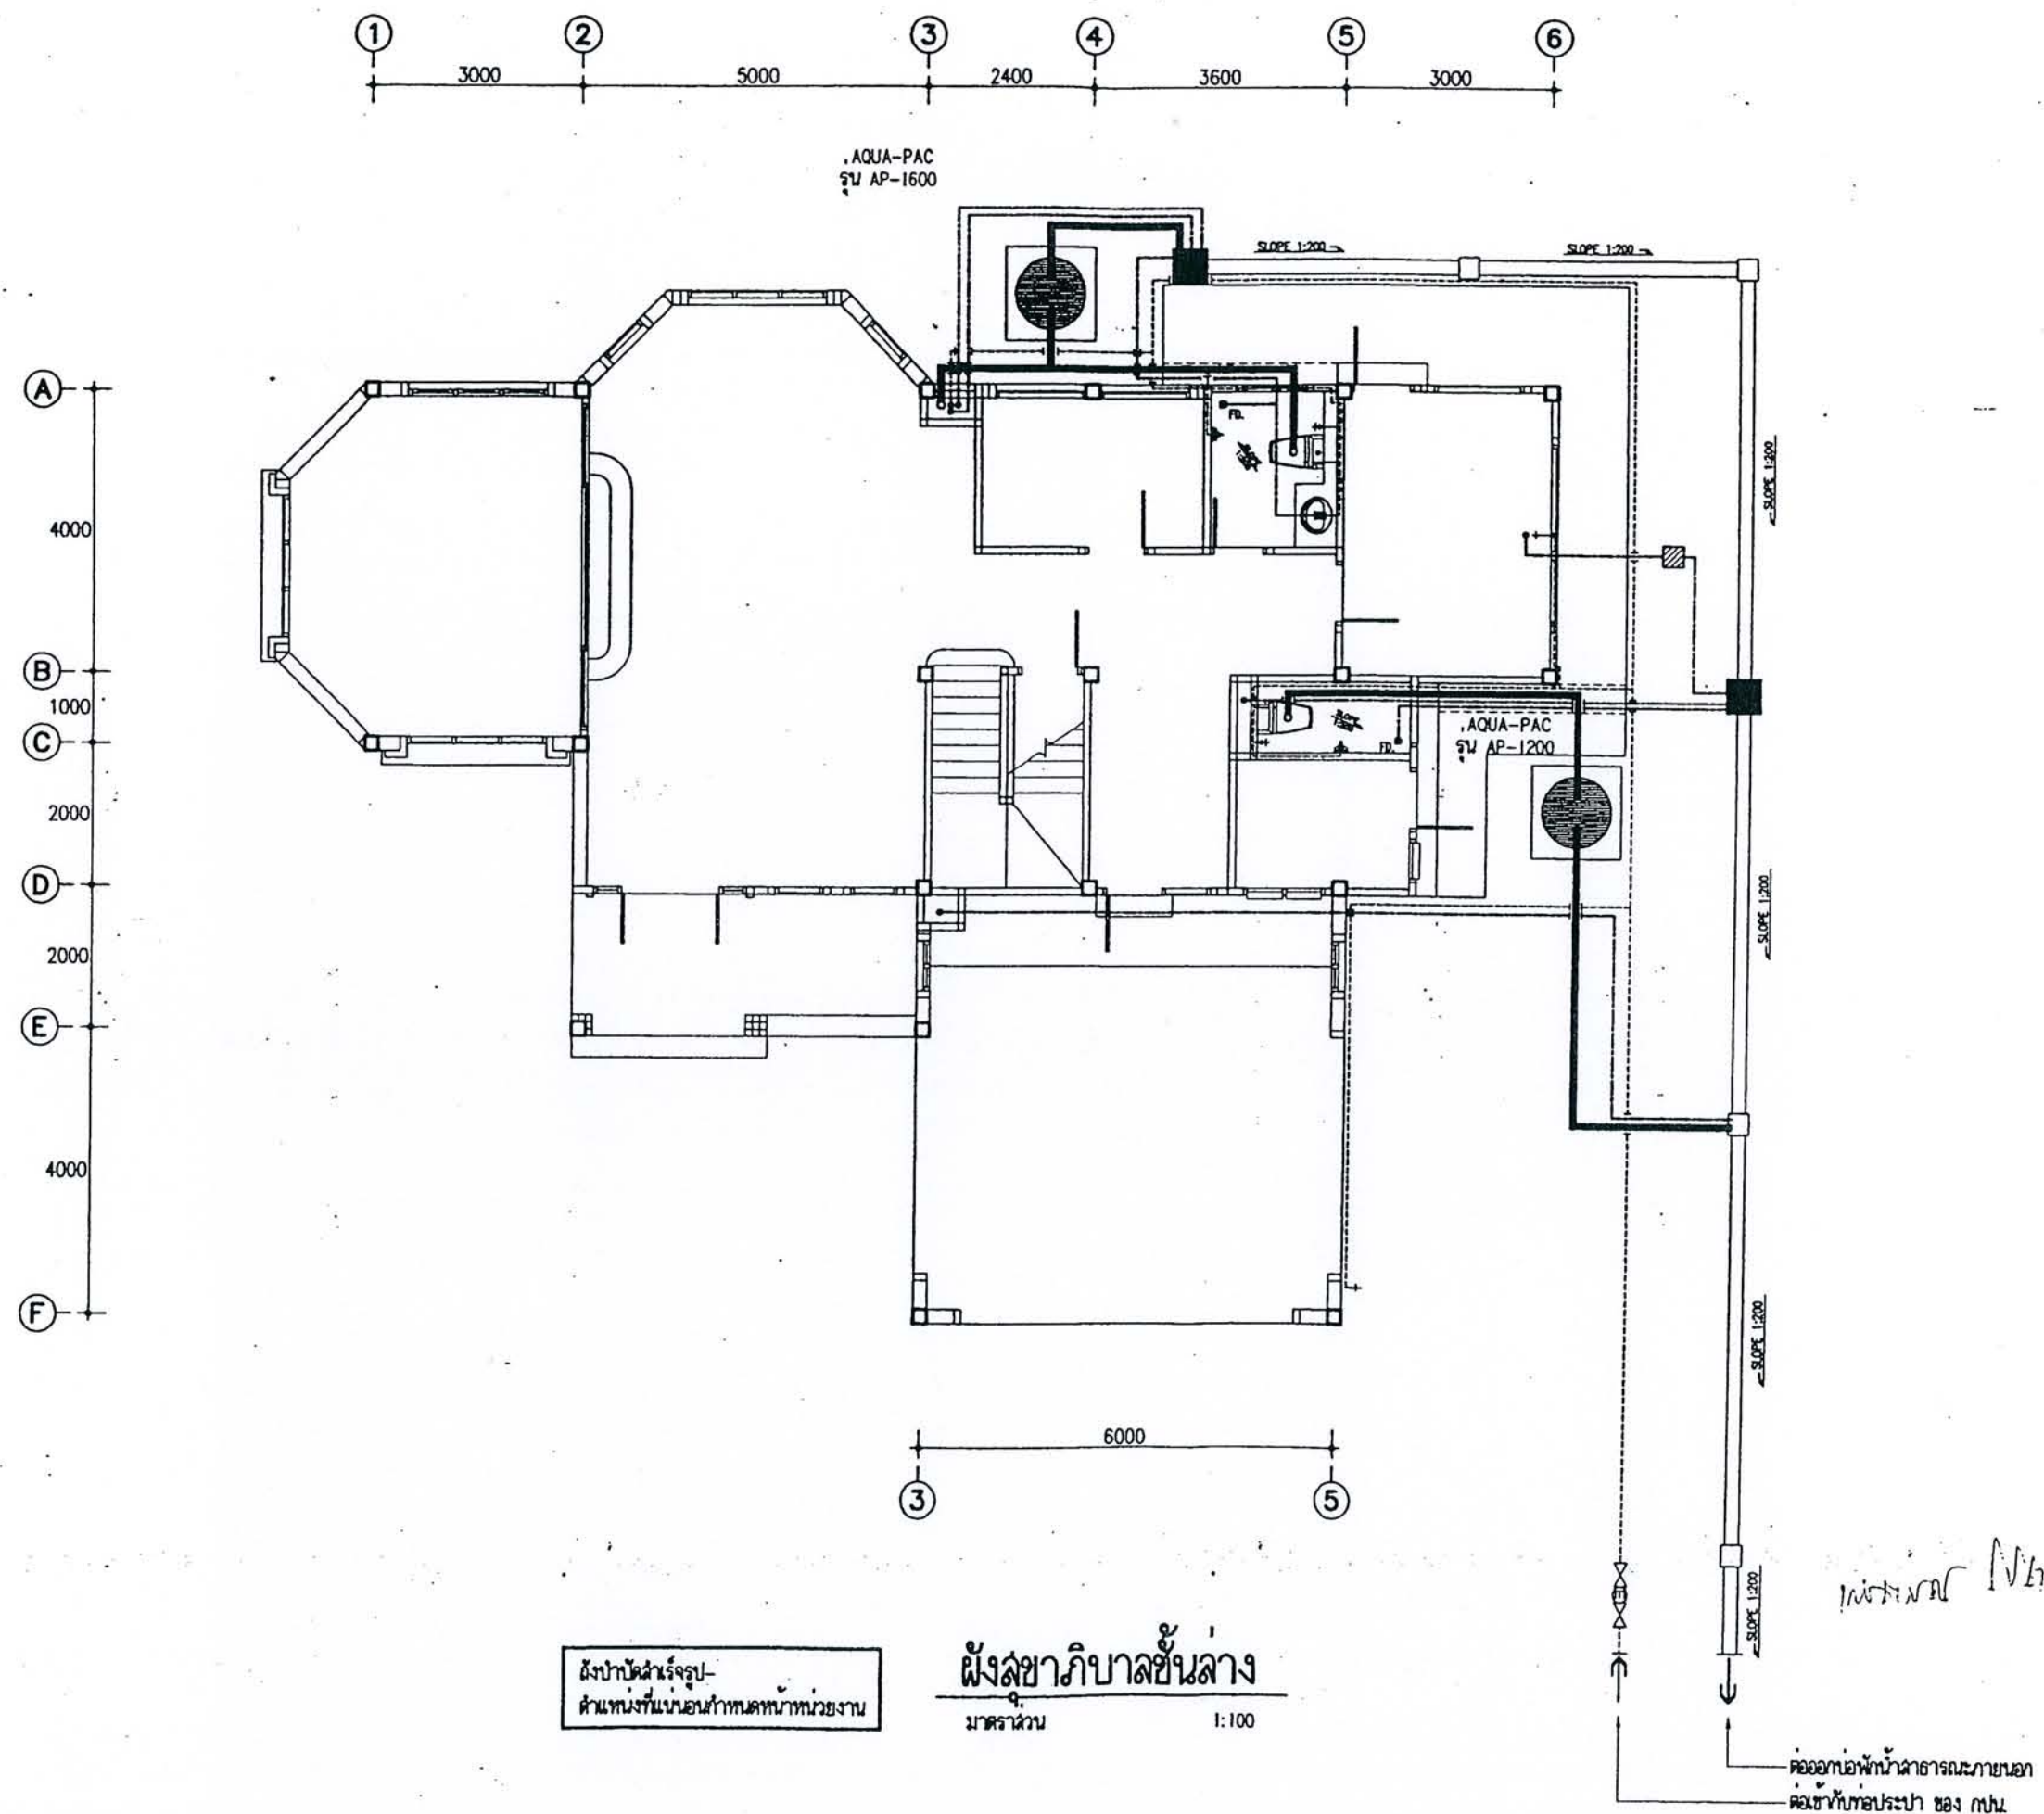

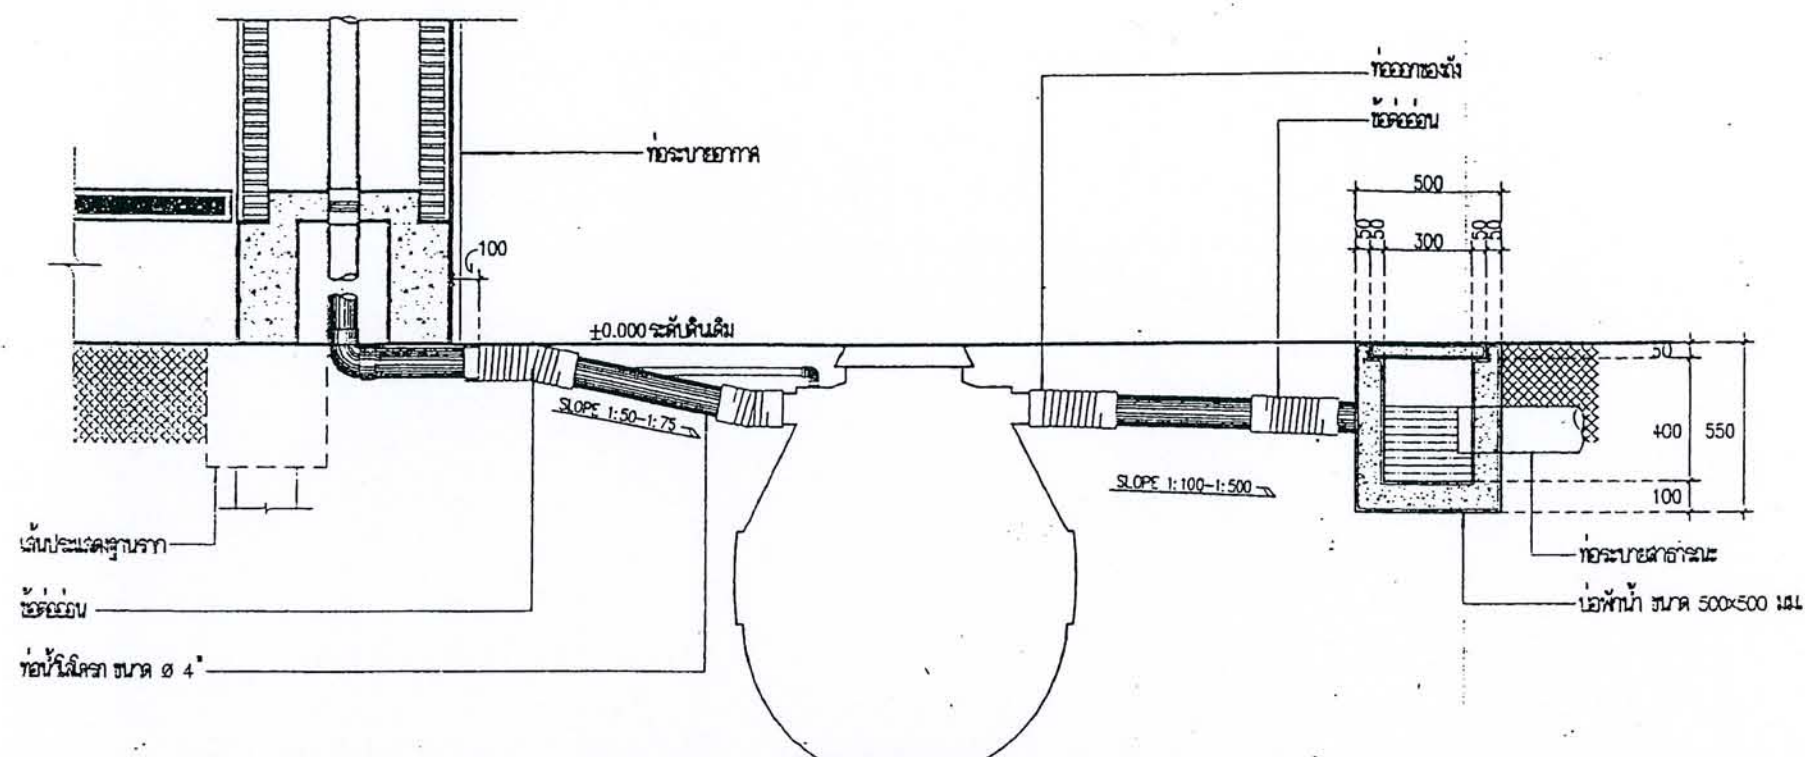

แบบขยายการวางท่อและตั้งระดับถังบำบัดลําเรือรูป
มาตรฐาน 1 : 25

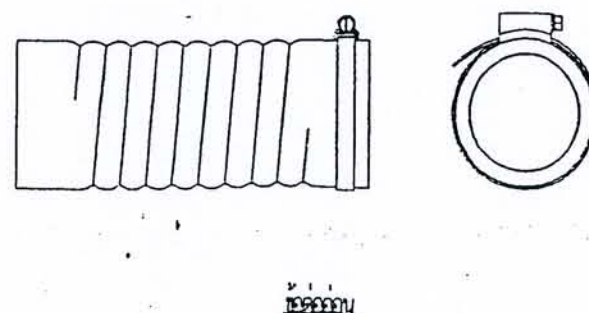





โครงการ
แบบบ้านยืมเพื่อประชาชน

ตามนโยบาย
ม.ร.ว. สุขุมพันธุ์ บริพัตร
ผู้ว่าราชการกรุงเทพมหานคร

โดยสำนักงานโยธา
กรุงเทพมหานคร

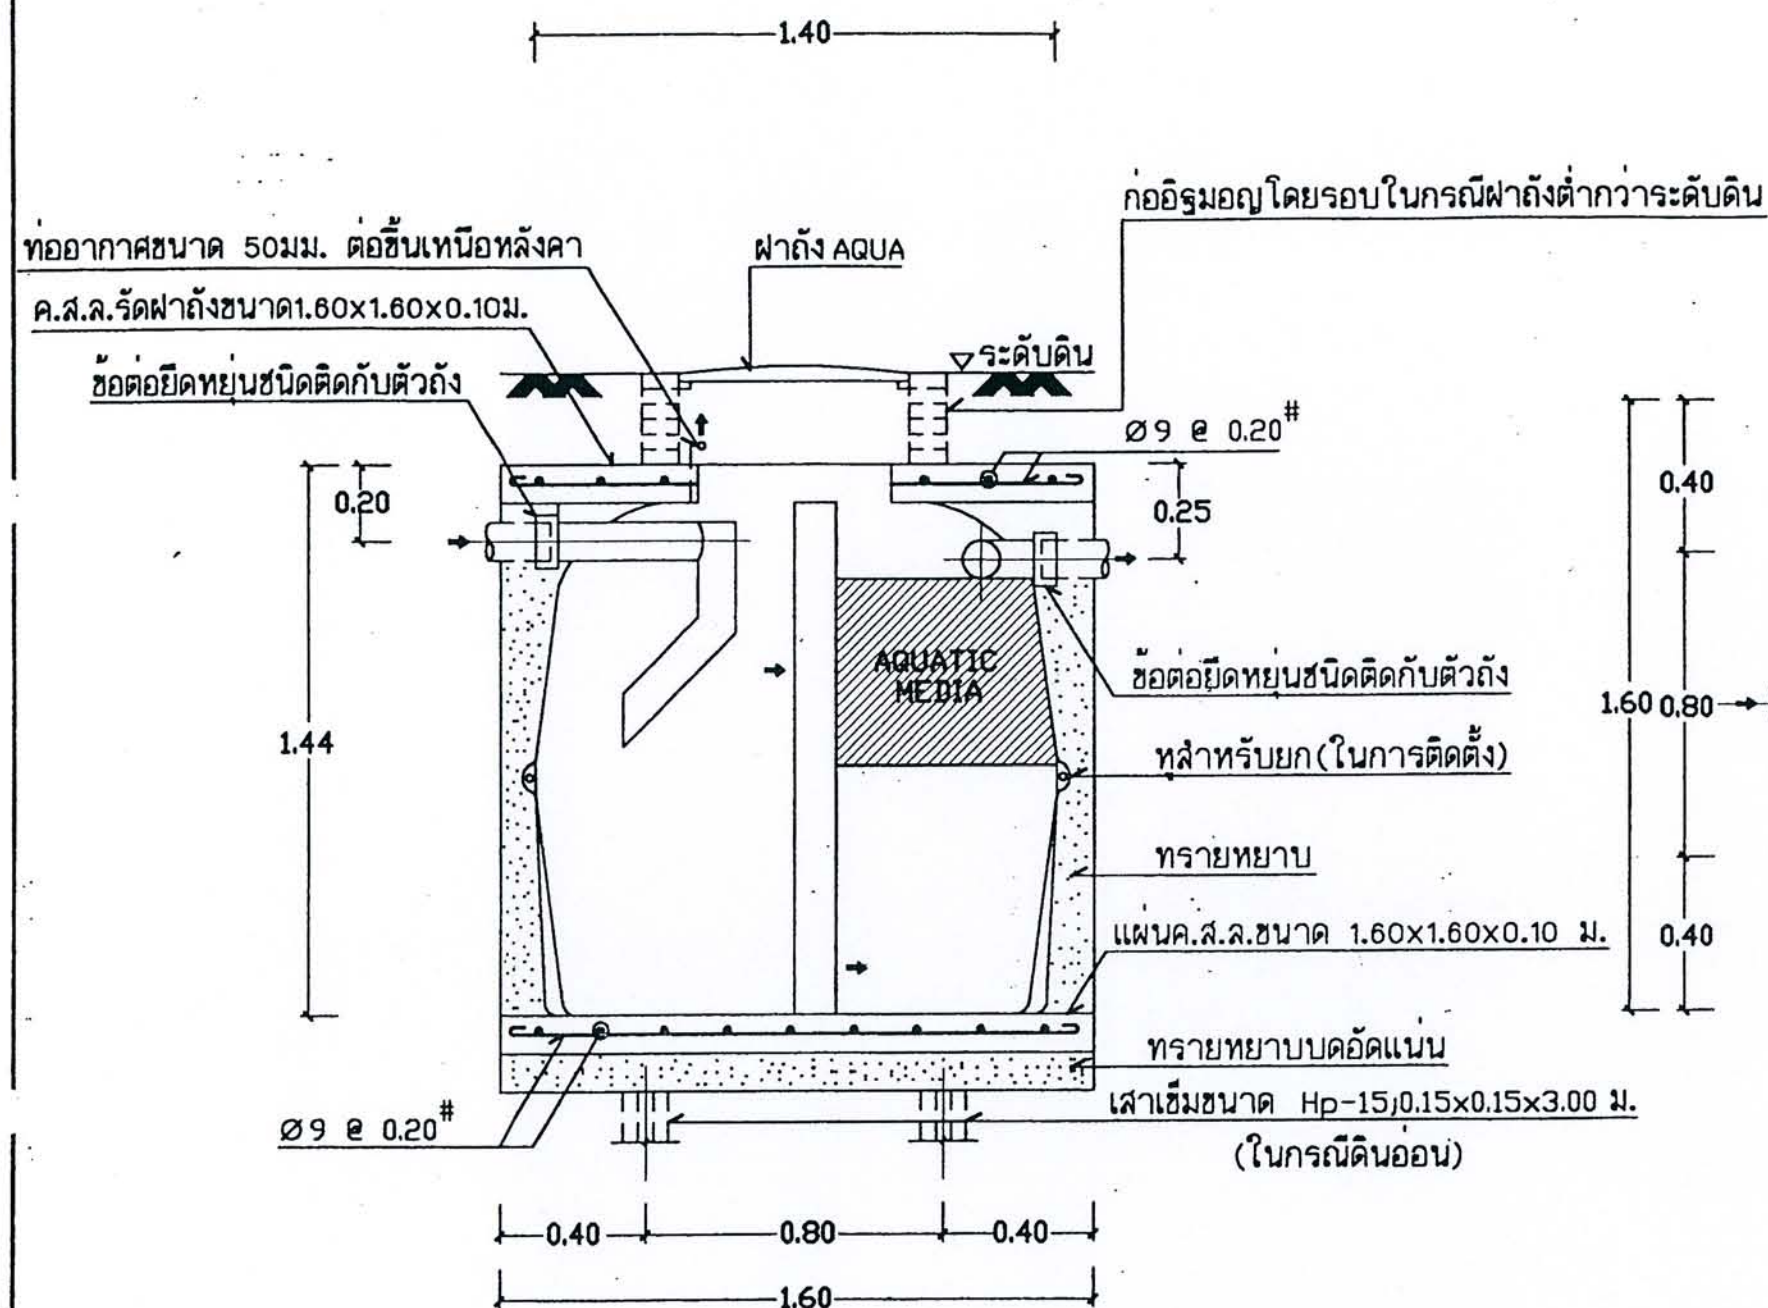

SECTION 1:20

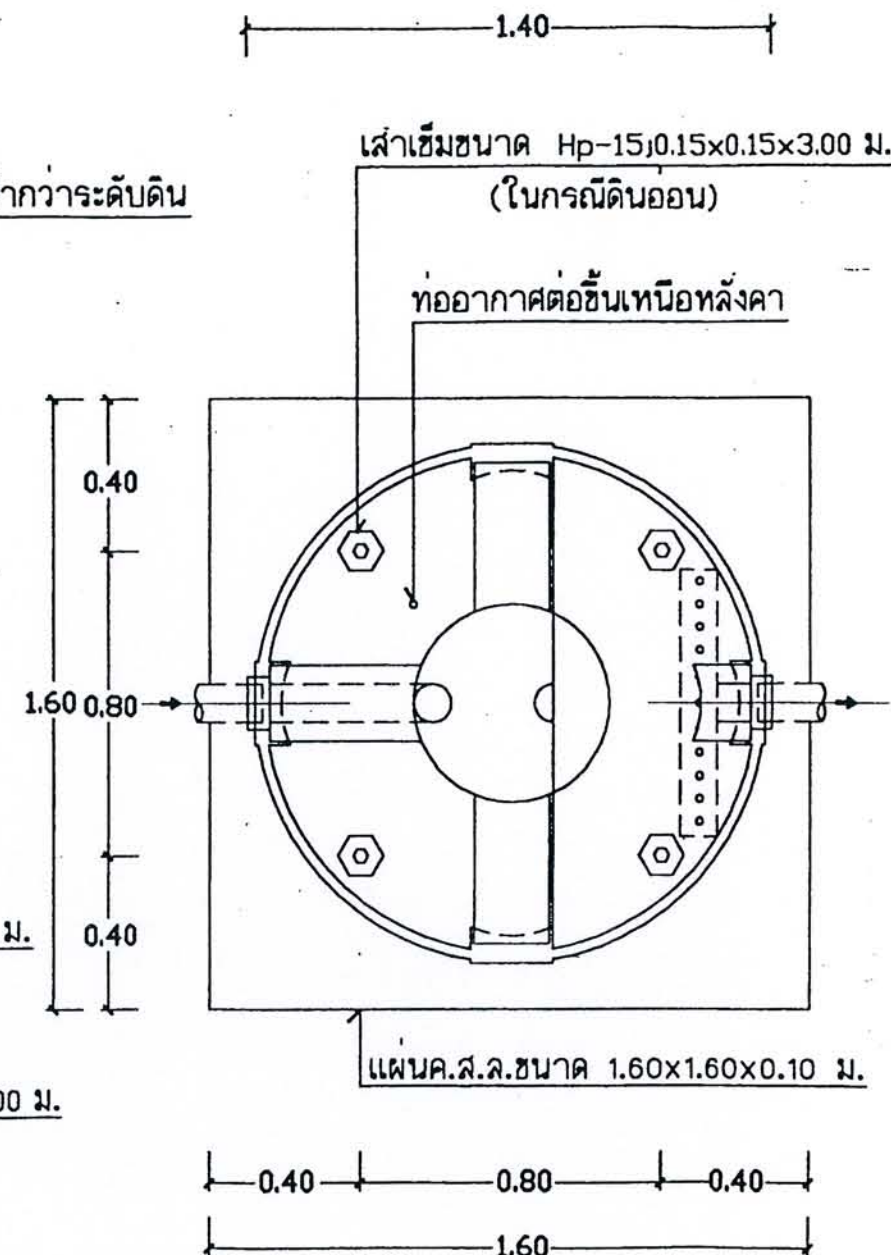

PLAN 1:20

AQUA-PAC (AP-1600)

ได้รับความอนุเคราะห์แบบ
จาก
บริษัท แลนด์ โฮม
(ประเทศไทย) จำกัด