



ตามนโยบายของ
หม่อมราชวงศ์สุขุมพันธุ์ บริพัตร
ผู้ว่าราชการกรุงเทพมหานคร
โดย สำนักการโยธา



ห้ามพลาด!!! โอกาส...
ยืมรับ... บ้านใหม่
พบ **บ้านสวย**
เลือกได้
ใน “โครงการแบบบ้านยืม...เพื่อประชาชน”


พบ 100 แบบบ้าน
มาตรฐาน...
สวย ดี โดนใจ
พร้อมปลูก
สร้างได้ทันที
ซีไอเลือก
หลากหลาย
ตอบสนอง
ทุกไลฟ์สไตล์คนเมือง

แบบบ้านยืม... เพื่อประชาชน

100 แบบบ้านมาตรฐาน...
สวย ดี โดนใจ...
พร้อมปลูกสร้างได้ทันที

กองกลาง 
สำนักการโยธา กรุงเทพมหานคร

แผนที่สังเขป

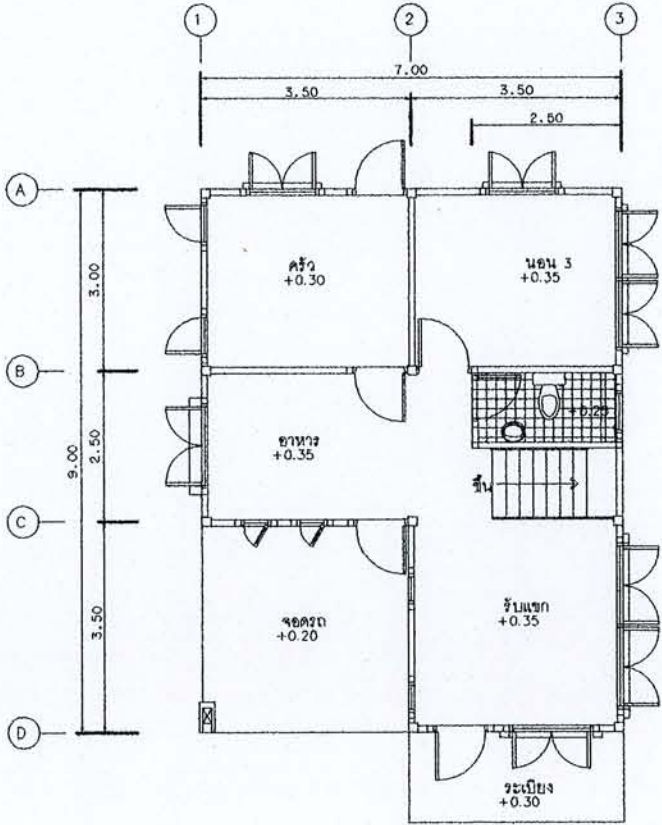

ผังบริเวณ

มาตราส่วน 1 : 125

-  - ถังใบโหล รุ่น BT-24E ของบริษัท พรีเมียร์ โปรดักส์ จำกัด หรือเทียบเท่า ดูแบบขยาย
-  - บ่อพักขนาด 0.40x0.40 m. (ดูแบบขยาย) ระยะห่างไม่เกิน 6.00 m.
-  - ท่อระบายน้ำ ขนาด | 0.20 m. SLOPE 1:200



สำนักงานโยธา
กรุงเทพมหานคร

โครงการ
แบบบ้านยืมเพื่อประชาชน

ตามนโยบาย

น.ร.สุเมธพันธ์ บริพัตร ผู้อำนวยการ
นายพชรพร เศรษฐกิจ รองผู้อำนวยการ
นายธีระชน มโนชัยบุตร รองผู้อำนวยการ
นายพงษ์ศักดิ์ เตมียาห์ ปลัดเขต

ผู้อำนวยการสำนักงานโยธา

นายจุฑาภรณ์ สำนวณ

รองผู้อำนวยการสำนักงานโยธา

นายทวีศักดิ์ เลิศประพันธ์

ผู้อำนวยการสำนักงานออกแบบ

นายจตุรงค์ สมนิยม

หัวหน้ากลุ่มงานสถาปัตยกรรม

นายสินธุ์ชัย บุญปักษ์

หัวหน้ากลุ่มงานวิศวกรรม

นายธีระยุทธ คงสวัสดิ์เกียรติ

สถาปนิก

นายปวิศ พิทักษ์

วิศวกรโครงสร้าง

วิศวกรไฟฟ้า

วิศวกรสุขาภิบาล

นางสาวณัฏฐา สมหอม

วิศวกรเครื่องกล

นายช่างเขียนแบบ

วาทิธรศรีปรีชา ประกิจ

แบบ บ้านทองหลาง

เจ้าของ

สถานที่

แบบแสดง

ผังบริเวณ

และแผนที่สังเขป

มาตราส่วน 1:125

FILE :

วันที่ 25 ธันวาคม 2553

คัดลอกแบบ

วาทิธรศรีปรีชา ประกิจ

รายการแก้ไขแบบ

แผ่นที่

A-02

รวมแผ่น

23



สำนักงานโยธา
กรุงเทพมหานคร

โครงการ
แบบบ้านยืมเพื่อประชาชน

ตามนโยบาย

ม.ร.ว.สุขุมพันธุ์ บริพัตร ผู้ว่าฯกทม.
นายพรเทพ เกษมทรัพย์ รองผู้ว่าฯกทม.
นายธีระชน มโนชัยปิยะกุล รองผู้ว่าฯกทม.
นายพงศ์ศักดิ์ เตเมธินันต์ ปลัดฯกทม.

ผู้อำนวยการสำนักงานโยธา
นายชุมพล สันภาพล
รองผู้อำนวยการสำนักงานโยธา
นายทวีศักดิ์ เลิศประพันธ์
ผู้อำนวยการสำนักงานออกแบบ
นายจตุรงค์ สมนิยม
หัวหน้ากลุ่มงานสถาปัตยกรรม
นายสินธุ์ชัย บุญปักษ์
หัวหน้ากลุ่มงานวิศวกรรม
นายธีระยุทธ คงสรรค์เสถียร

สถาปนิก
นายเป็ดพิท มีมาก
วิศวกรโครงสร้าง
วิศวกรไฟฟ้า
วิศวกรสุขาภิบาล
นางสาวมณีนีชา สมนิยม
วิศวกรเครื่องกล

นายช่างเขียนแบบ
วาทิรน้อยศรีปรีชา ประภัก

แบบ บ้านทดลอง
คำของ
สถานที่


แบบแสดง
แปลนพื้นชั้นล่าง

มาตราส่วน 1:75

FILE :
วันที่ 25 มิถุนายน 2553
คัดลอกแบบ
วาทิรน้อยศรีปรีชา ประภัก

แผ่นที่
A-03
จำนวน
23

รายการแก้ไขแบบ

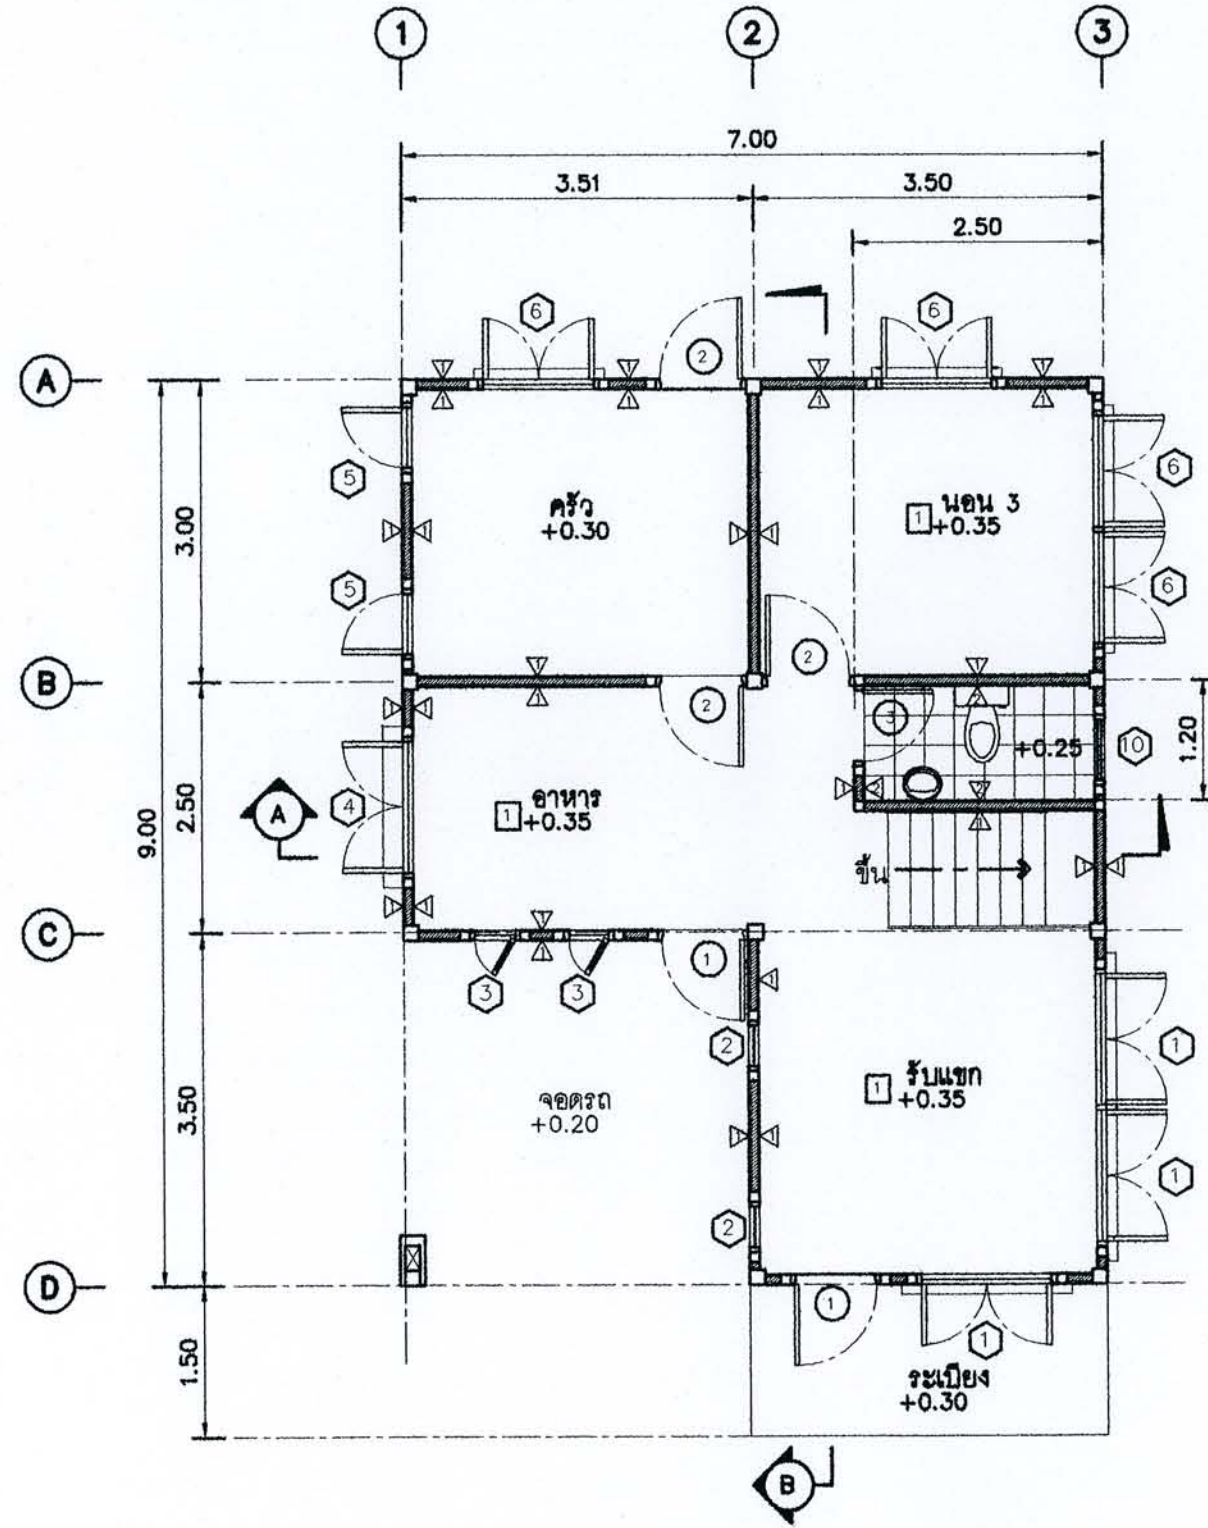

แปลนพื้นชั้นล่าง
มาตราส่วน 1:75





สำนักงานโยธา
กรุงเทพมหานคร

โครงการ
แบบบ้านยืมเพื่อประชาชน

ตามนโยบาย

ม.ร.ว.สุขุมพันธุ์ บริพัตร ผู้ว่าฯกทม.
นายพลเทพ ประยูรพิทักษ์ รองผู้ว่าฯกทม.
นายธีระชน มโนทิมศิริกุล รองผู้ว่าฯกทม.
นายพงษ์ศักดิ์ เศรษฐสินธุ์ ปลัดฯกทม.

ผู้อำนวยการสำนักการโยธา
นายจุมพล สันภาพล
รองผู้อำนวยการสำนักการโยธา
นายทวีศักดิ์ เกียรติประพันธ์
ผู้อำนวยการสำนักงานออกแบบ
นายจตุรงค์ สมนิยม
หัวหน้างานสถาปัตยกรรม
นายสินธุ์ชัย บุญนิกร
หัวหน้างานวิศวกรรม
นายธีระยุทธ คงสรรค์เกียรติ

สถาปนิก
นายปวิศ วัฒนา
วิศวกรโครงสร้าง
วิศวกรไฟฟ้า
วิศวกรสุขาภิบาล
นางสาวณณศิรา สมทอง
วิศวกรเครื่องจักร

นายช่างเขียนแบบ
ว่าที่ร้อยตรีปิศา ประภัก


แบบ
บ้านทองหลาง
เจ้าของ
สถานที่

แบบแสดง
แปลนพื้นชั้นบน

มาตราส่วน 1:75

FILE :
ชั้นปี 01
ชื่อโครงการ 2553
ชื่อโครงการ 2553
ว่าที่ร้อยตรีปิศา ประภัก

รายการแก้ไขแบบ

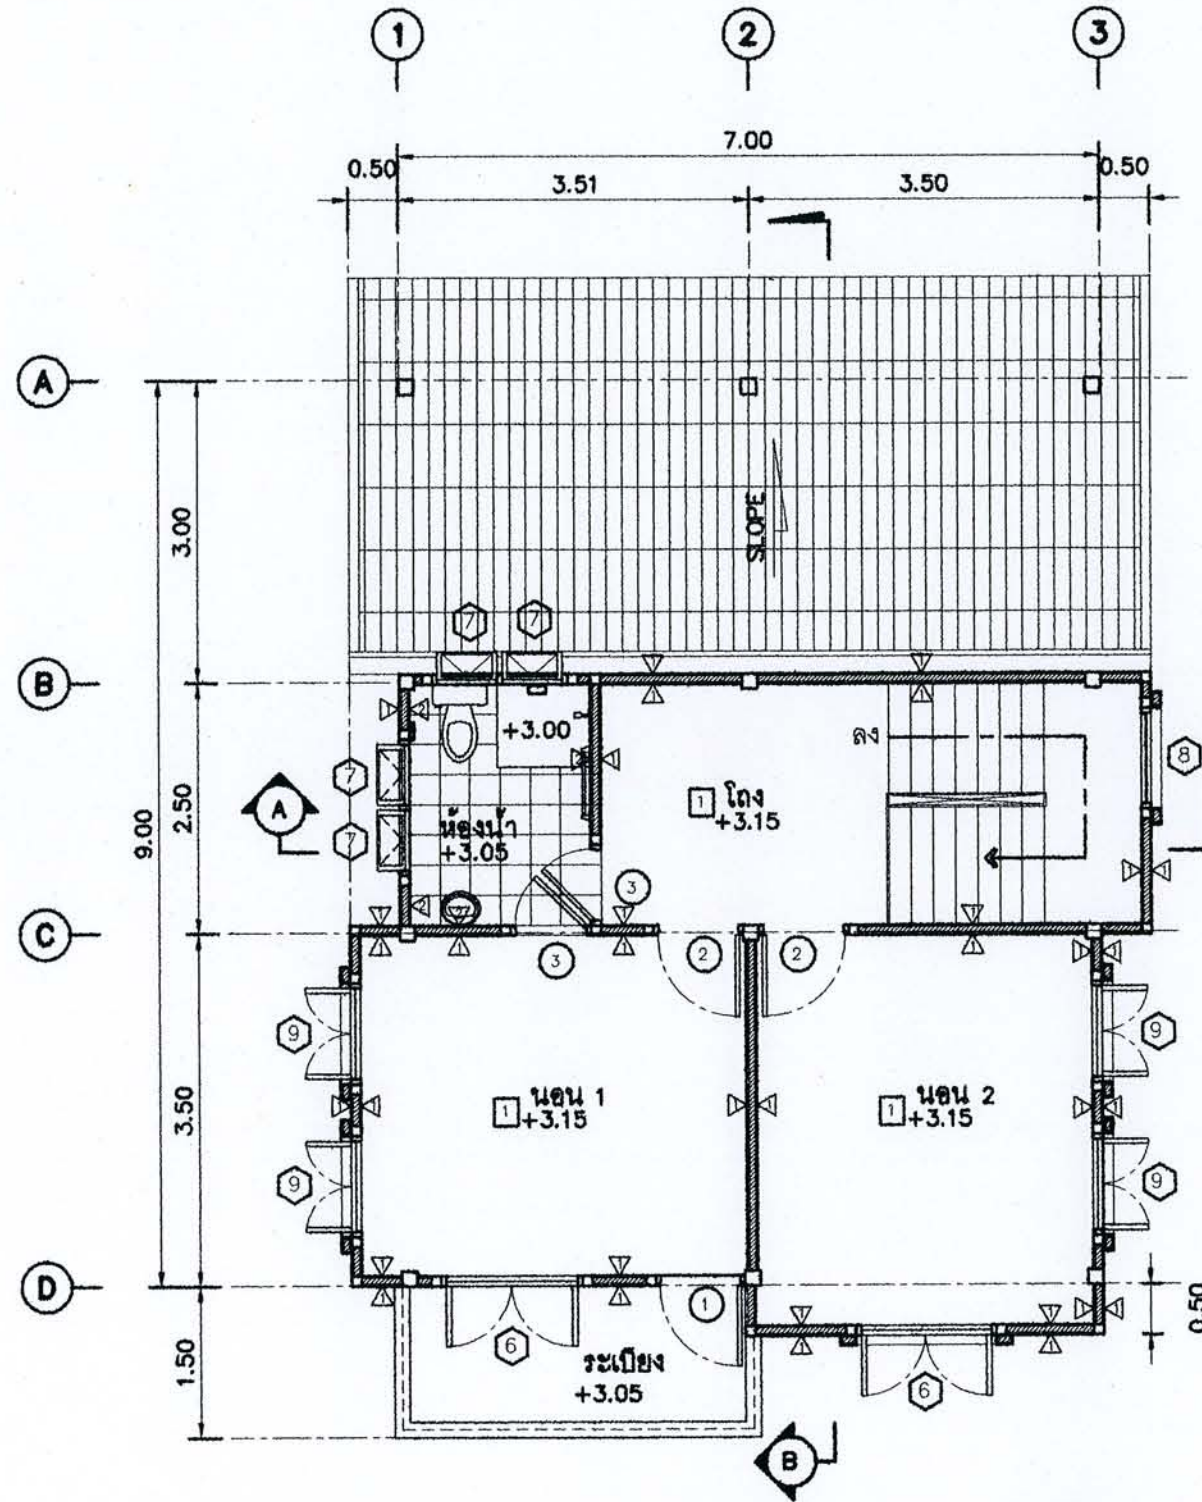

แปลนพื้นชั้นบน
มาตราส่วน 1:75





สำนักการโยธา
กรุงเทพมหานคร

โครงการ
แบบบ้านยืมเพื่อประชาชน

ตามนโยบาย

ม.ร.ว.สุขุมพันธุ์ บริพัตร ผู้ว่าฯกทม.
นายพรเทพ เศรษฐิน้อย รองผู้ว่าฯกทม.
นายธีระชน มโนชัยปิยะกุล รองผู้ว่าฯกทม.
นายพงษ์ศักดิ์ แสนสินดี ปลัดฯกทม.

ผู้อำนวยการสำนักการโยธา

นายจุมพล สำนวณกุล

รองผู้อำนวยการสำนักการโยธา

นายทวีศักดิ์ เลิศประพันธ์

ผู้อำนวยการสำนักงานออกแบบ

นายจตุรงค์ สมนิยม

หัวหน้ากลุ่มงานสถาปัตยกรรม

นายสินธุ์ชัย บุญบึกษ์

หัวหน้ากลุ่มงานวิศวกรรม

นายธีระยุทธ คงสรวคเศียร

สถาปนิก

นายวิสิทธิ์ มีมาก

วิศวกรโครงสร้าง

วิศวกรไฟฟ้า

วิศวกรสุขาภิบาล

นางสาวมณฑิลา สมหม่อม

วิศวกรเครื่องกล

นายช่างเขียนแบบ

ว่าที่ร้อยตรีปวิศา ประกิจ

แบบ
บ้านทองหลาง

เจ้าของ

สถานที่

แบบแสดง
แปลนหลังคา

มาตราส่วน 1:75


FILE : แผนที่

พื้นที่ 01กุมภาพันธ์ 2553 A-05

คัดลอกเป็นต้นฉบับ รวมแผ่น


ว่าที่ร้อยตรีปวิศา ประกิจ 23

รายการแก้ไขแบบ

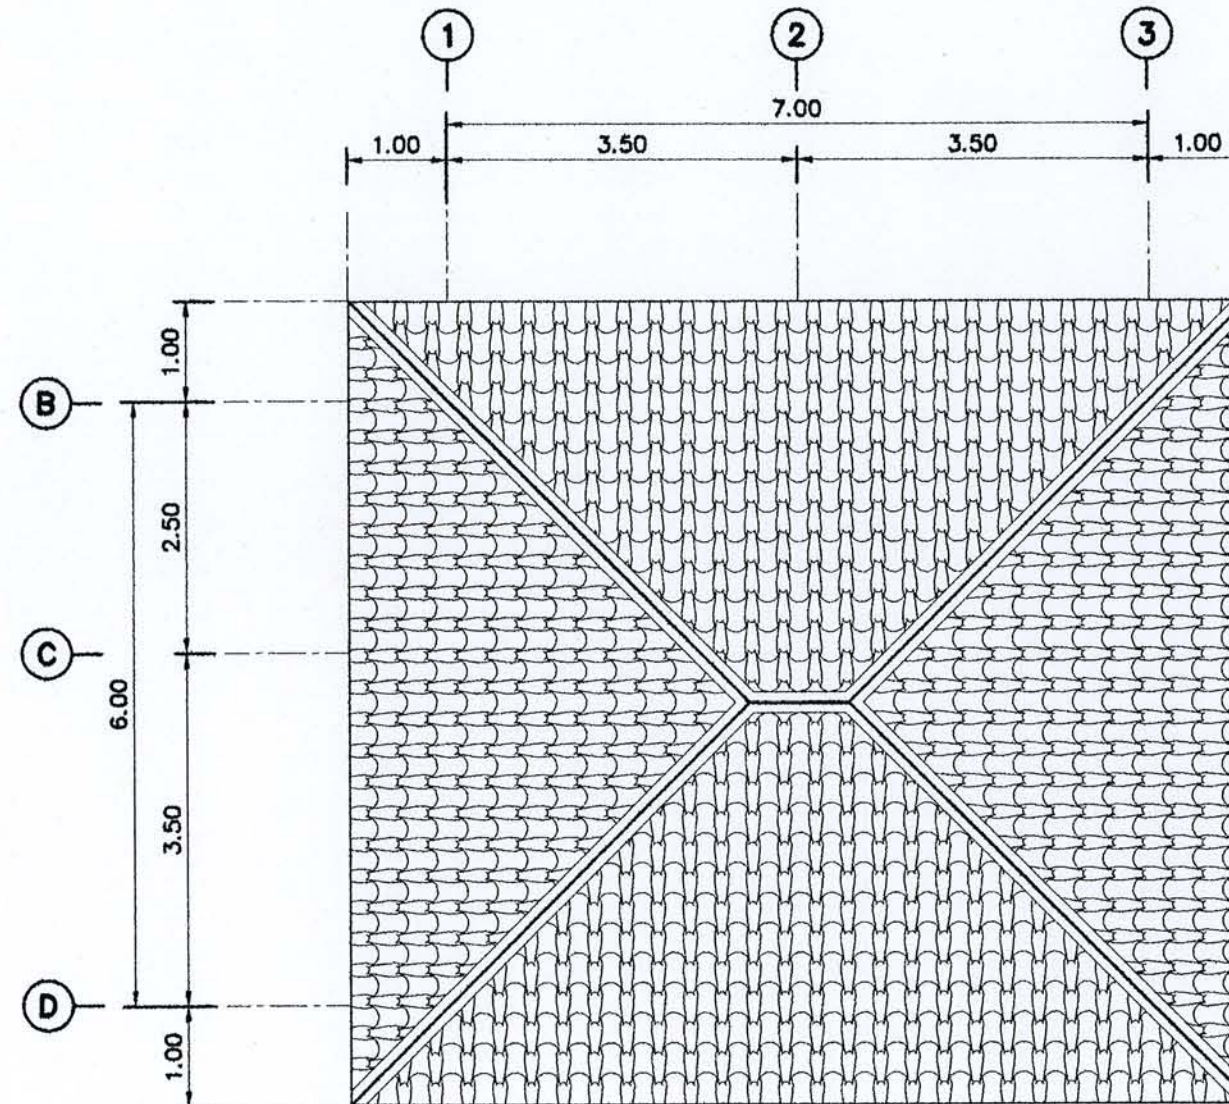

แปลนหลังคา

มาตราส่วน 1:75

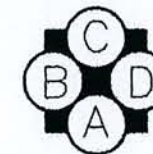



สำนักการโยธา
กรุงเทพมหานคร

โครงการ
แบบบ้านยืมเพื่อประชาชน

ตามนโยบาย

ม.ร.ว.สุขุมพันธุ์ บริพัตร ผู้ว่าฯกทม.
นายพรหม เจริญโพธิ์ รองผู้ว่าฯกทม.
นายธีระชน มโนทิมโพธิ์ รองผู้ว่าฯกทม.
นายพงษ์ศักดิ์ เทพจันทร์ ปลัดฯกทม.

ผู้อำนวยการสำนักการโยธา
นายจุมพล สำนวณ
รองผู้อำนวยการสำนักการโยธา
นายทวีศักดิ์ เกียรติพันธ์
ผู้อำนวยการสำนักงานออกแบบ
นายจตุรงค์ สมนิยม
หัวหน้างานสถาปัตยกรรม
นายสินธุ์ชัย บุญปักษ์
หัวหน้างานงานวิศวกรรม
นายธีระยุทธ คงสวัสดิ์เกียรติ

สถาปนิก
นายปวิศ ธีมาภ
วิศวกรโครงสร้าง
วิศวกรไฟฟ้า
วิศวกรสุขาภิบาล
นางสาวณณชรีฯ สมหนอง
วิศวกรเครื่องกล

นายช่างเขียนแบบ
ว่าที่ร้อยตรีวิชา ประกิจ


แบบ บ้านทดลองทาง
เจ้าของ
สถานที่

แบบแสดง
รูปด้านหน้า

มาตราส่วน 1:75

FILE :	แผ่นที่
วันที่ 2553	A-06
ติดต่อ ปรึกษาแบบ	รวมแผ่น
ว่าที่ร้อยตรีวิชา ประกิจ	23

รายการแก้ไขแบบ

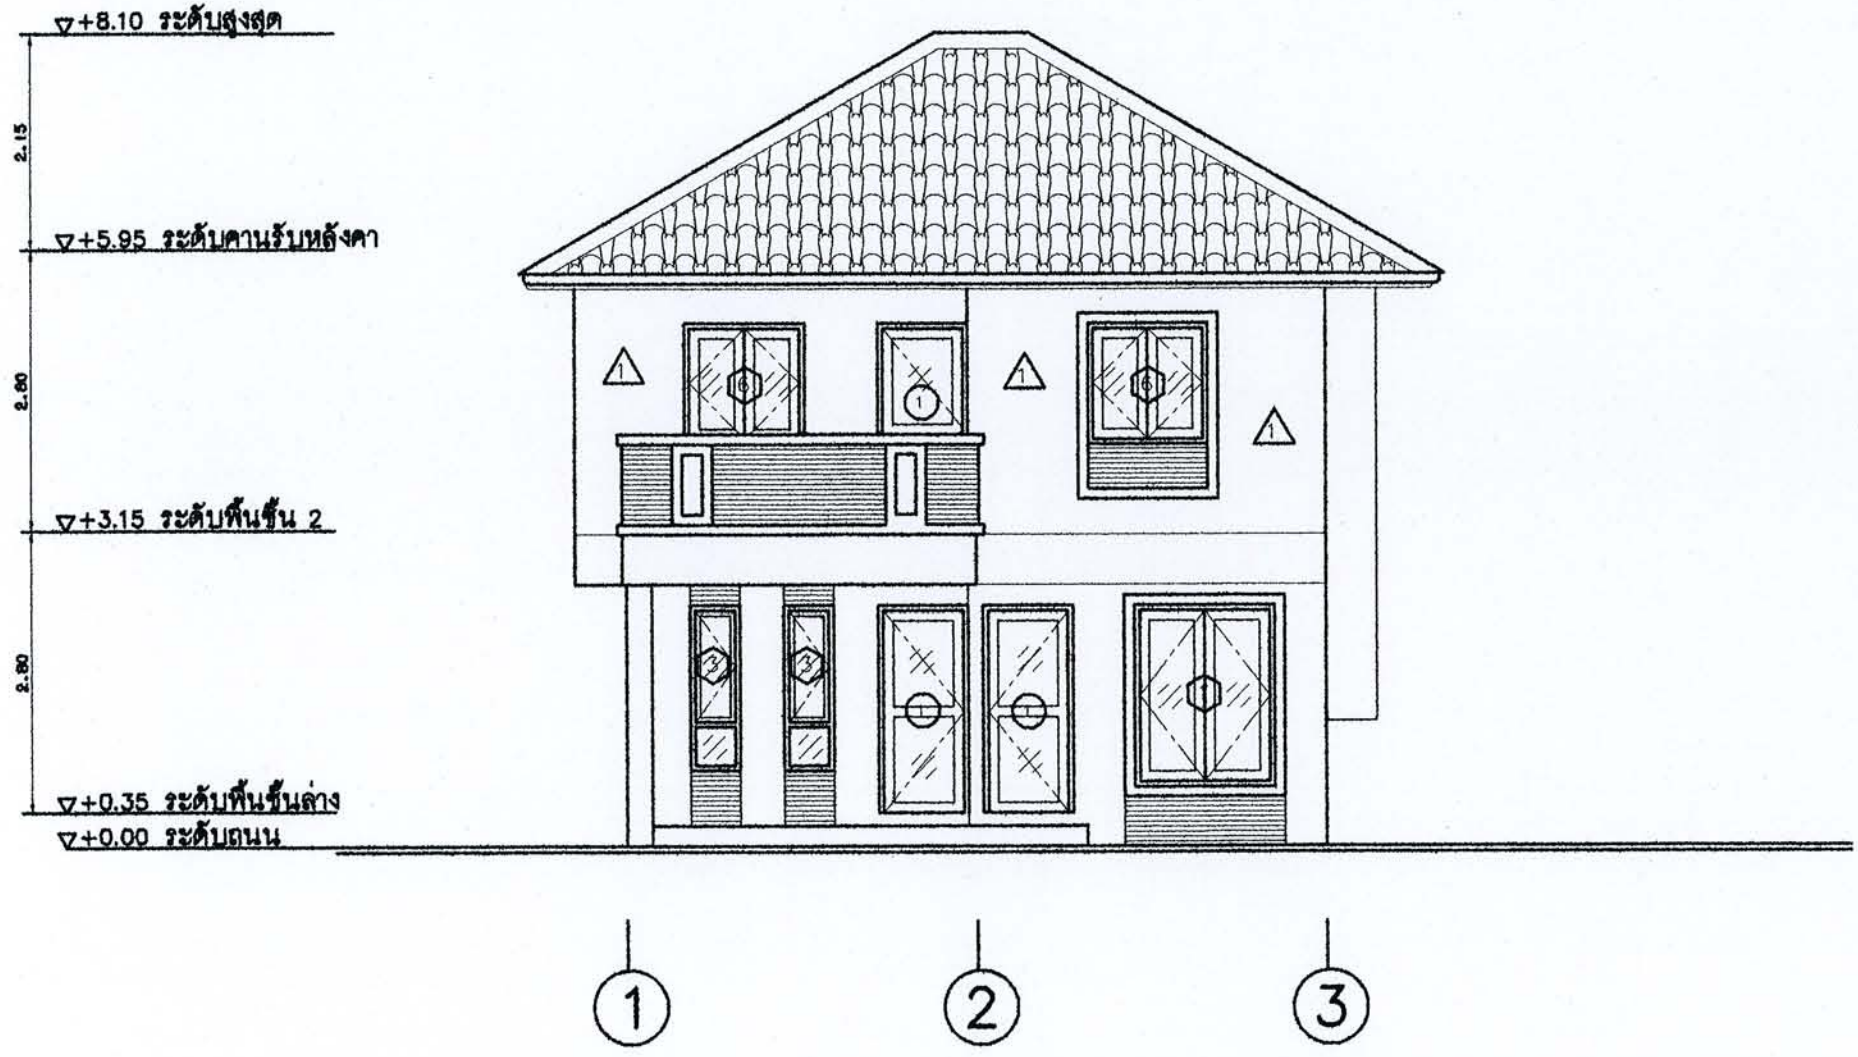

รูปด้านหน้า
มาตราส่วน 1 : 75



สำนักงานโยธา
กรุงเทพมหานคร

โครงการ
แบบบ้านยืมเพื่อประชาชน

ตามนโยบาย

น.ร.สุรพงษ์ ปรีติธนา ผู้ว่ากรม
นายพทท. เศรษฐกิจ รองผู้ว่ากรม
นายธีระชน นิมิตติบุตร รองผู้ว่ากรม
นายพงศ์ศิริกุล สมสันต์ ปลัดกรม

ผู้อำนวยการสำนักงานโยธา
นายชุมพล สันภาพ
รองผู้อำนวยการสำนักงานโยธา
นายวิศักดิ์ เลิศประพันธ์
ผู้อำนวยการสำนักงานออกแบบ
นายสุรศักดิ์ สันติธรรม
หัวหน้ากลุ่มงานสถาปัตยกรรม
นายสันติสุข บุญปักษ์
หัวหน้ากลุ่มงานวิศวกรรม
นายธีระยุทธ คงสรรค์เสถียร

สถาปนิก
นายปรีดิธ มีมาก

วิศวกรโครงสร้าง

วิศวกรไฟฟ้า

วิศวกรสุขาภิบาล

นางสาวมณฑิลา สมหอม

วิศวกรเครื่องกล

นายช่างเขียนแบบ

ว่าที่ร้อยตรีปรีชา ประกิจ

แบบ บ้านทองหลาง

พื้นที่

สถานที่

แบบแสดง
รูปด้านหลัง

มาตราส่วน 1:75


FILE :

วันที่ ๑๐ ตุลาคม ๒๕๕๓

คัดลอกแบบ

ว่าที่ร้อยตรีปรีชา ประกิจ

รายการแก้ไขแบบ

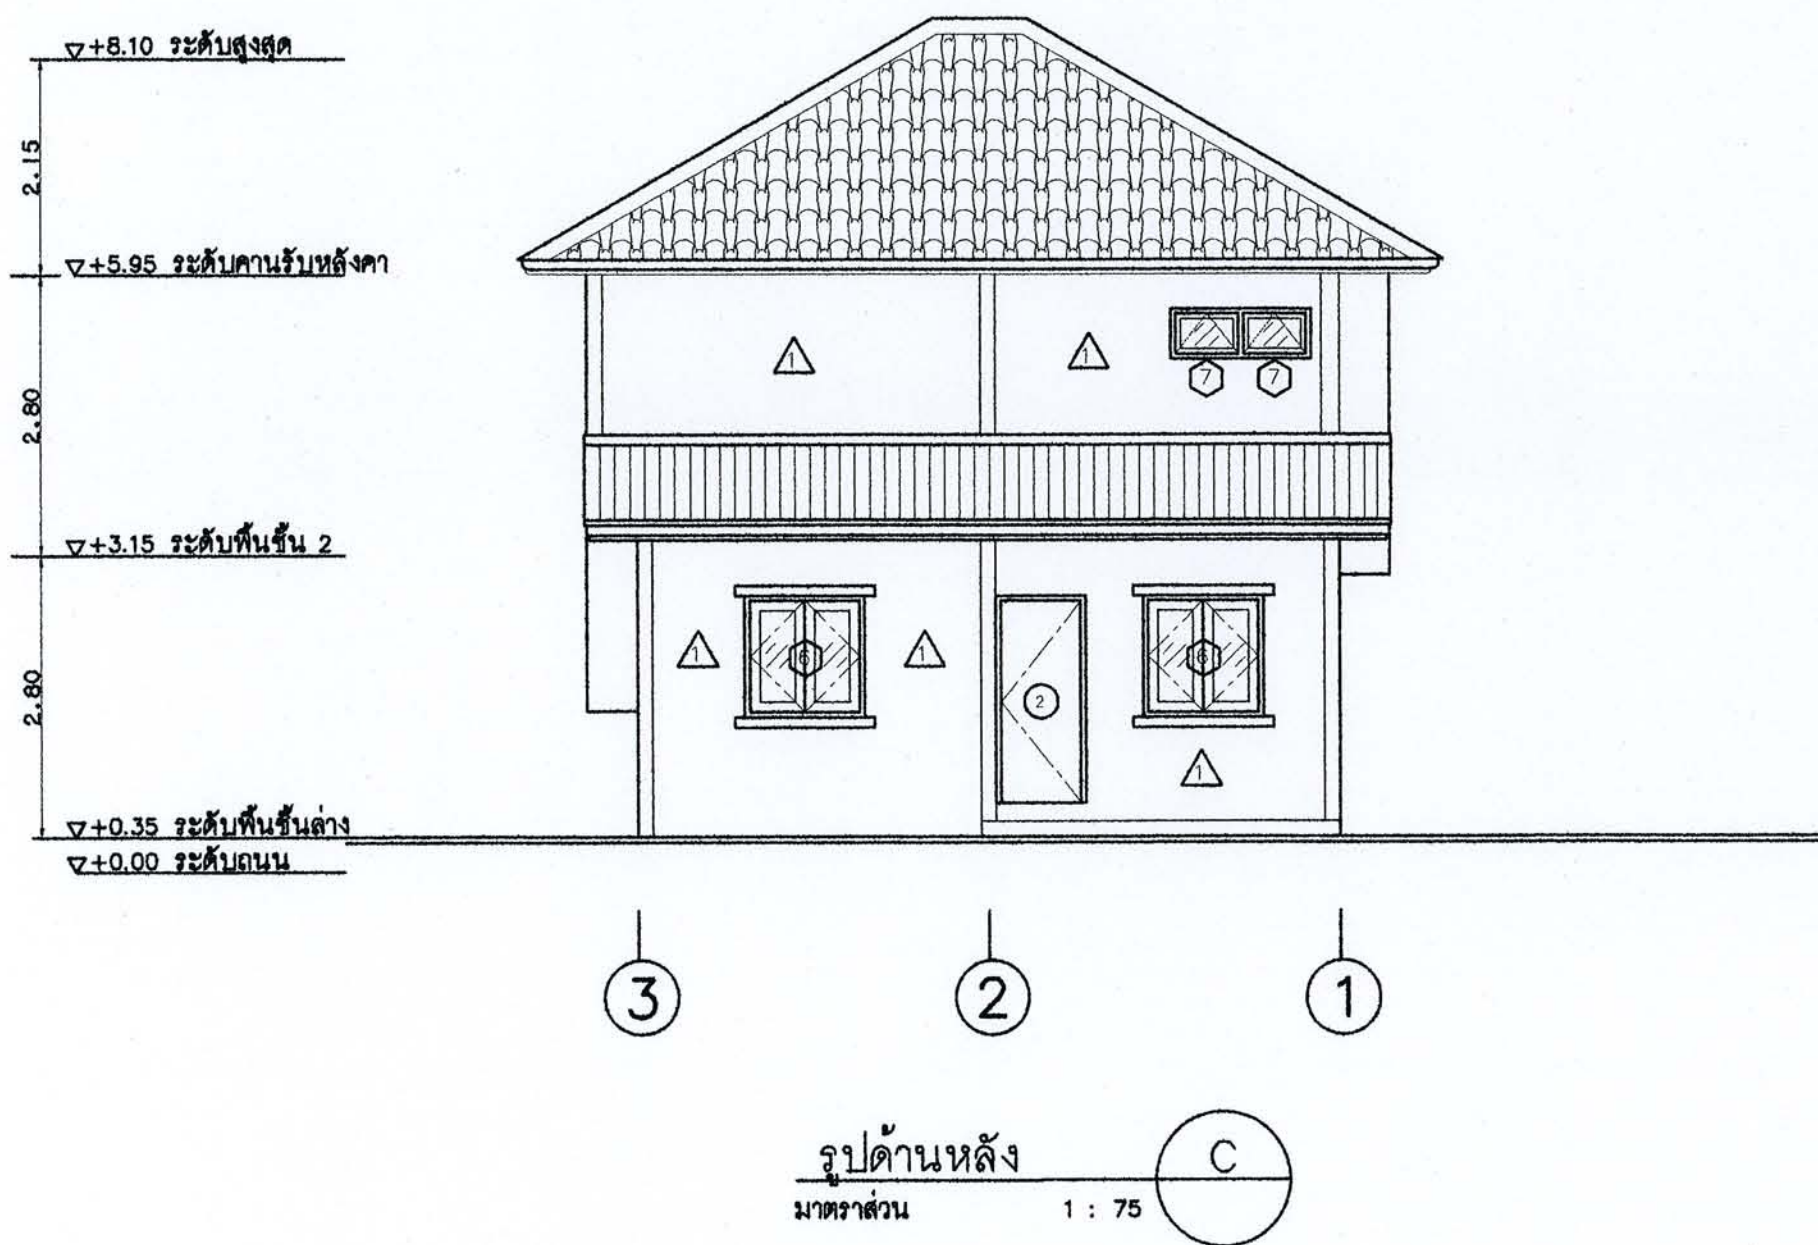



สำนักงานโยธา
กรุงเทพมหานคร

โครงการ
แบบบ้านยืมเพื่อประชาชน

ตามนโยบาย

ม.ร.ว.สุขุมพันธุ์ บริพัตร ผู้ว่าฯกทม.
นายแพทย์ เจริญศักดิ์ รองผู้ว่าฯกทม.
นายธีระชน มโนมัยพิบูลย์ รองผู้ว่าฯกทม.
นายพงศ์ศักดิ์ บุญสันต์ ปลัดฯกทม.

ผู้อำนวยการสำนักการโยธา

นายจุมพล สันภาพล

รองผู้อำนวยการสำนักการโยธา

นายทวิศักดิ์ เดชประพันธ์

ผู้อำนวยการสำนักงานออกแบบ

นายจตุรงค์ สมนิยม

หัวหน้ากลุ่มงานสถาปัตยกรรม

นายสินธุ์ชัย บุญบึกษ์

หัวหน้ากลุ่มงานวิศวกรรม

นายธีระยุทธ คงสรรค์เดียง

สถาปนิก

นายปรีดิท มิมาก

วิศวกรโครงสร้าง

วิศวกรไฟฟ้า

วิศวกรสุขาภิบาล

นางสาวเมณจิรา สมหอม

วิศวกรเครื่องกล

นายช่างเขียนแบบ

ว่าที่ร้อยตรีปรีชา ประกิจ

แบบ บ้านทรงหลัง

เจ้าของ

สถานที่

แบบแสดง

รูปด้านข้างขวา

มาตราส่วน 1:75

FILE :


วันที่ ๑๑ ตุลาคม ๒๕๕๓

ผู้จัดทำ ๒๕๕๓

ว่าที่ร้อยตรีปรีชา ประกิจ

๒๕๕๓

รายการแก้ไขแบบ

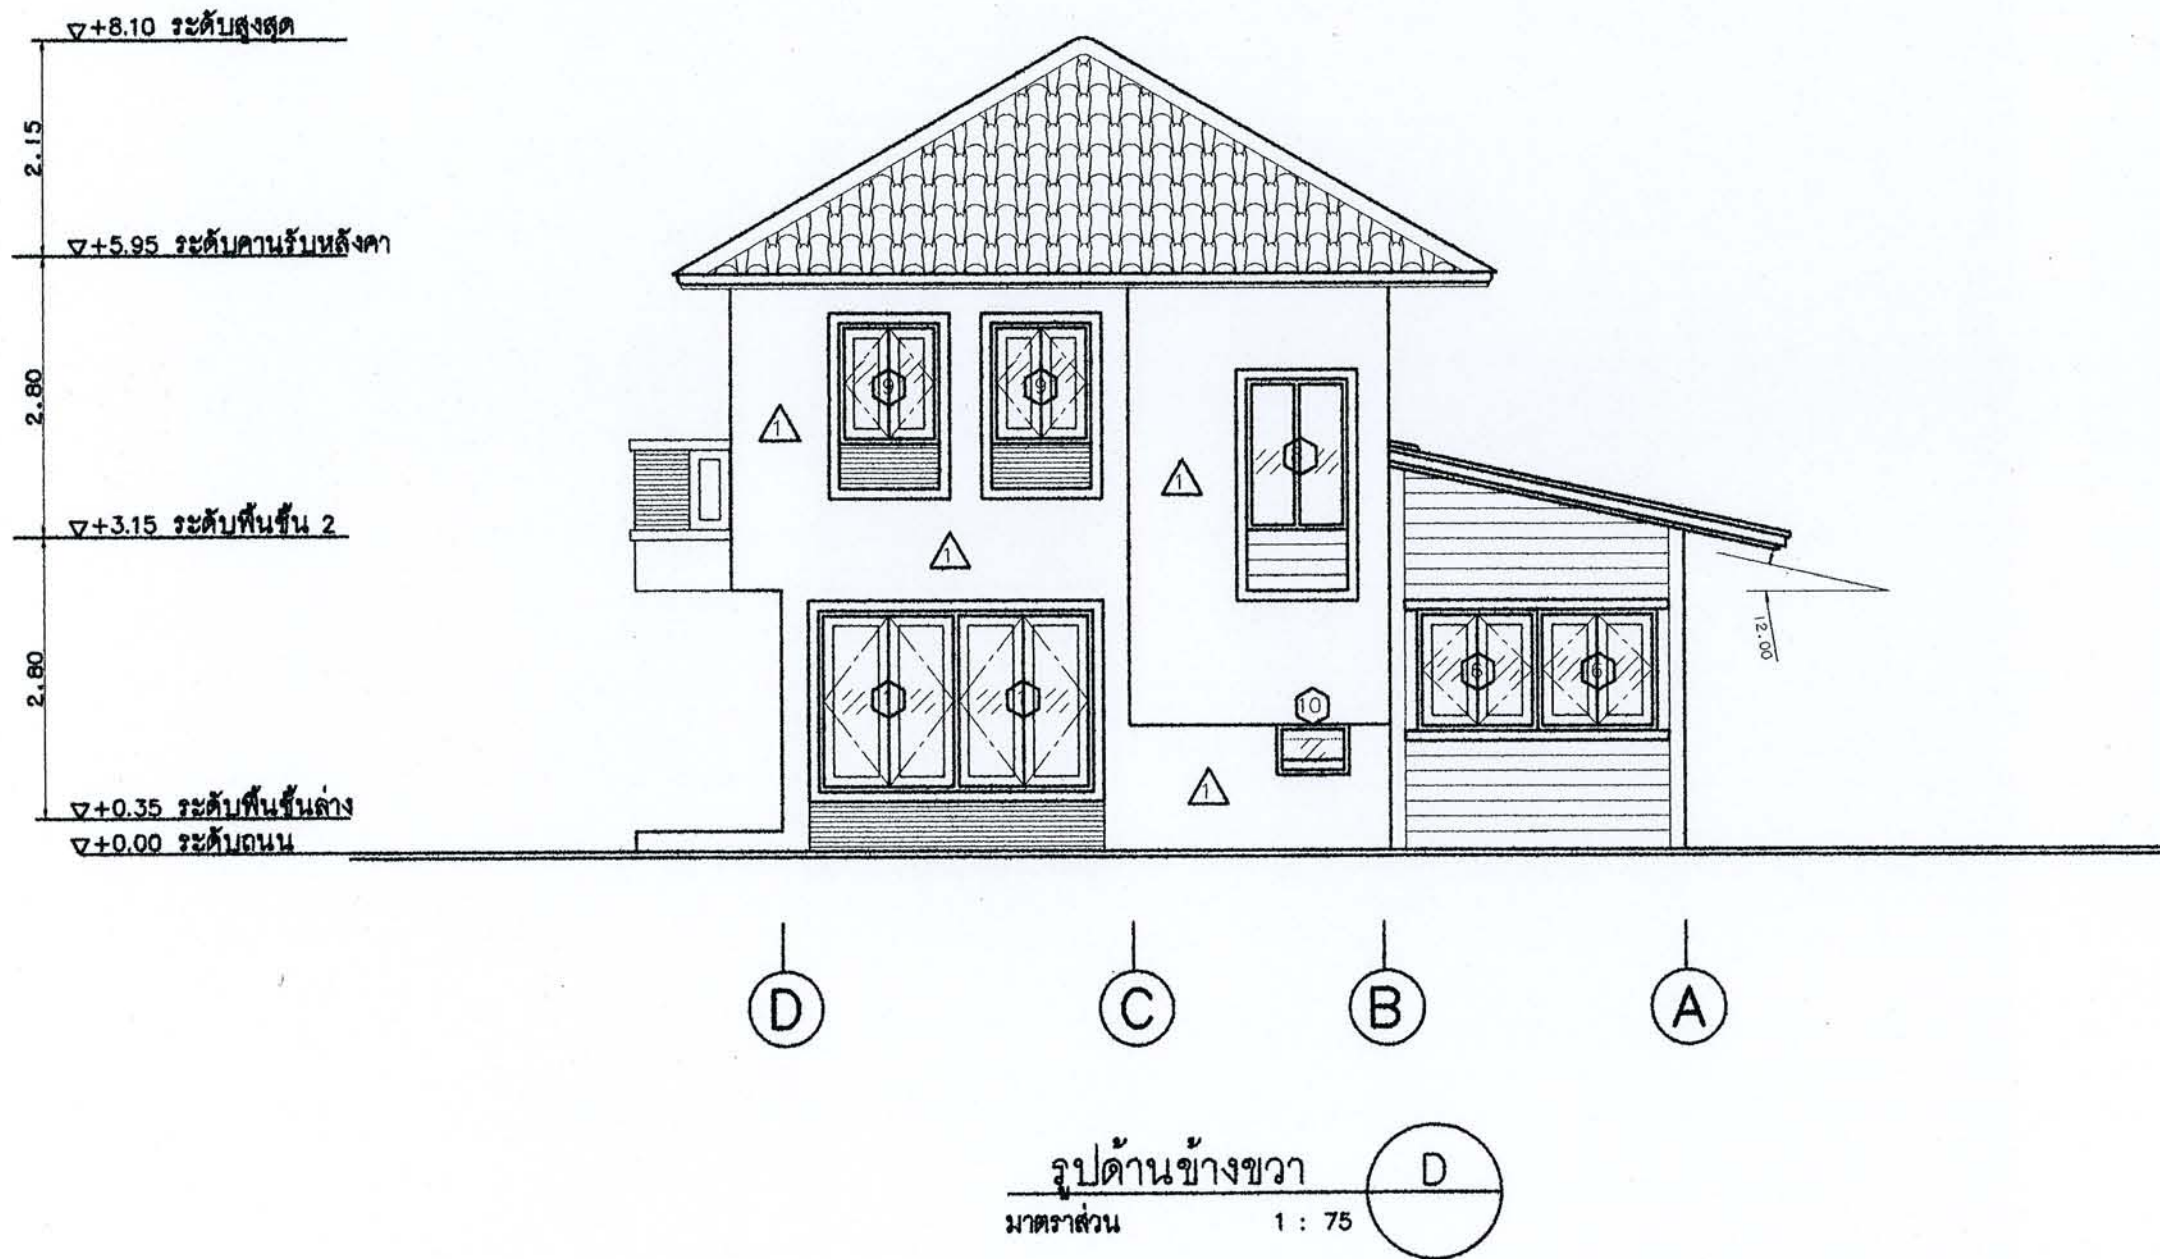

รูปด้านข้างขวา
มาตราส่วน 1 : 75



สำนักงานโยธา
กรุงเทพมหานคร

โครงการ
แบบบ้านยืมเพื่อประชาชน

ตามนโยบาย

ม.ร.ว.สุขุมพันธุ์ บริพัตร ผู้ว่าฯกทม.
นายพรเทพ เศรษฐินบุรี รองผู้ว่าฯกทม.
นายธีระชน มโนชัยพิบูลย์ รองผู้ว่าฯกทม.
นายทองศักดิ์ เทพสัสดี ปลัดฯกทม.

ผู้อำนวยการสำนักงานโยธา
นายจุมพล สันภาพล
รองผู้อำนวยการสำนักงานโยธา
นายทวีศักดิ์ เลิศประพันธ์
ผู้อำนวยการสำนักงานออกแบบ
นายสุรศักดิ์ สมนิยม
หัวหน้ากลุ่มงานสถาปัตยกรรม
นายสินธุ์ชัย บุญปักษ์
หัวหน้ากลุ่มงานวิศวกรรม
นายธีระยุทธ คงสวัสดิ์เดโช


สถาปนิก
นายวิฑิต มีมาก
วิศวกรโครงสร้าง
วิศวกรไฟฟ้า
วิศวกรสุขาภิบาล
นางสาวณณชรีฯ สมหอม
วิศวกรเครื่องกล
นายช่างเขียนแบบ
ว่าที่ร้อยตรีวิชา ประกิจ

แบบ
บ้านทองหลาง
คำขอ
สถานที่

แบบแสดง
รูปตัด
A
มาตราส่วน 1:75

FILE :
วันที่ 10 ตุลาคม 2553
คัดลอกแบบ
ว่าที่ร้อยตรีวิชา ประกิจ
แผ่นที่
A-10
รวมแผ่น
23

รายการแก้ไขแบบ

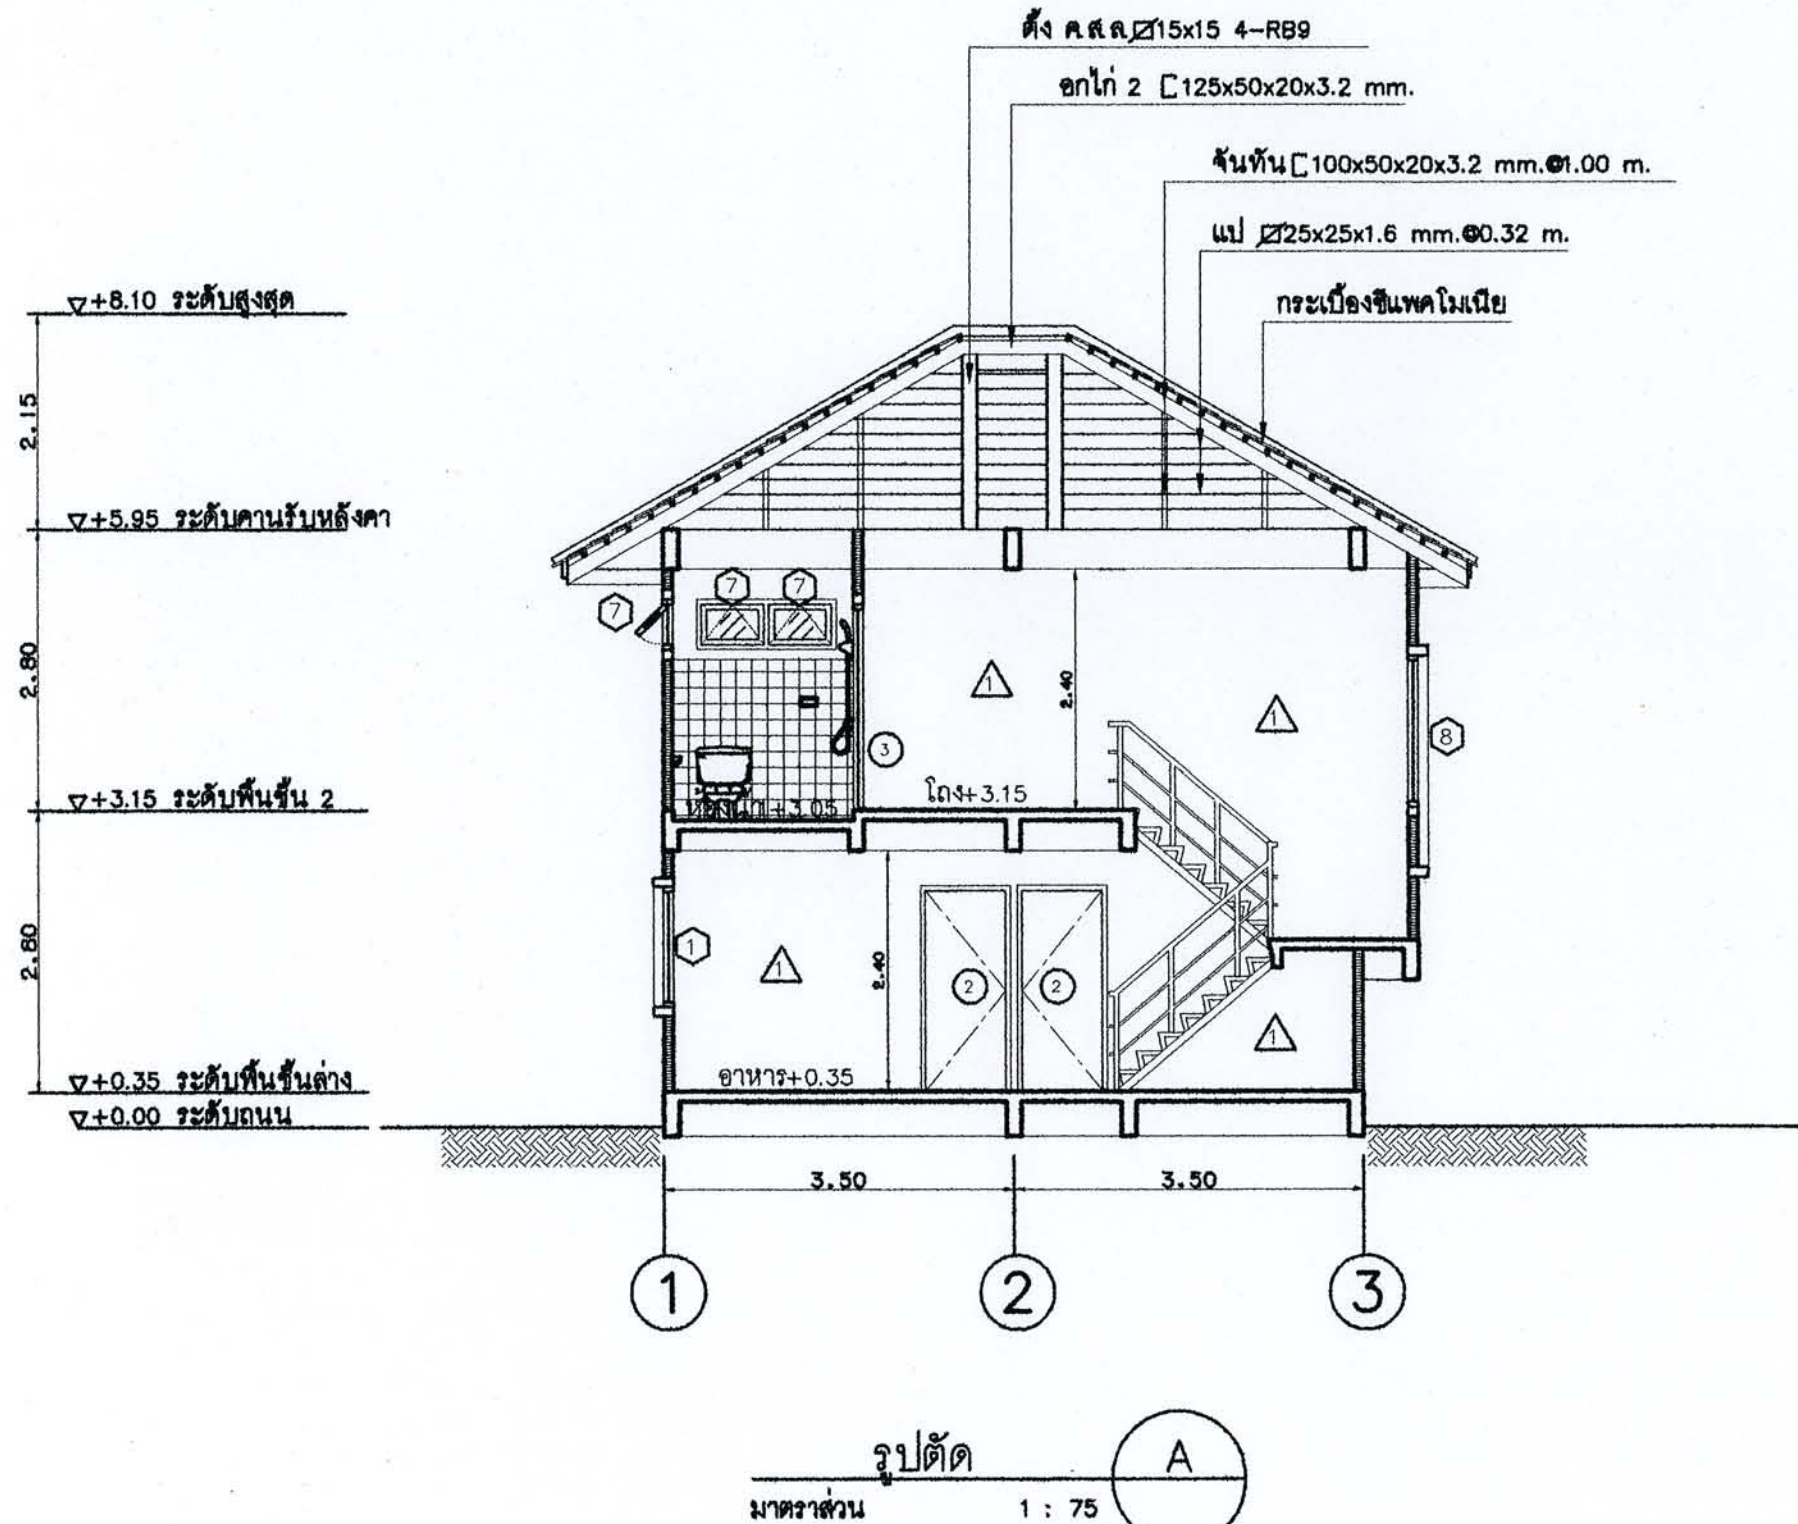



สำนักงานโยธา
กรุงเทพมหานคร

โครงการ
แบบบ้านยืมเพื่อประชาชน

ตามนโยบาย

ม.ร.ว.สุขุมพันธุ์ บริพัตร ผู้ว่าฯ กทม.
นายพรเทพ เศรษฐินธร รองผู้ว่าฯ กทม.
นายธีระชน มโนทิตะกุล รองผู้ว่าฯ กทม.
นายพงศ์ศักดิ์ เตเมธินันท์ ปลัดฯ กทม.

ผู้อำนวยการสำนักงานโยธา
นายชุมพล สว่างกุล
รองผู้อำนวยการสำนักงานโยธา
นายวิศักดิ์ เลิศประพันธ์
ผู้อำนวยการสำนักงานออกแบบ
นายสุรศักดิ์ สมนิยม
หัวหน้ากลุ่มงานสถาปัตยกรรม
นายสันติสุข บุญมีกิจ
หัวหน้ากลุ่มงานวิศวกรรม
นายธีระยุทธ คงสวัสดิ์ชัย

สถาปนิก
นายวิฑิต ธีรภาพ
วิศวกรโครงสร้าง
วิศวกรไฟฟ้า
วิศวกรสุขาภิบาล
นางสาวมณฑิรา สมหอม
วิศวกรเครื่องกล
นายช่างเขียนแบบ
ว่าที่ร้อยตรีวิชา ประกิจ


แบบ
บ้านทองหลาง
เจ้าของ
สถานที่

แบบแสดง
รูปตัด
B

มาตราส่วน 1:75

FILE :	แผ่นที่
วันที่ 25 มิถุนายน 2553	A-11
คัดลอกแบบ	รวมแผ่น
ว่าที่ร้อยตรีวิชา ประกิจ	23

รายการแก้ไขแบบ

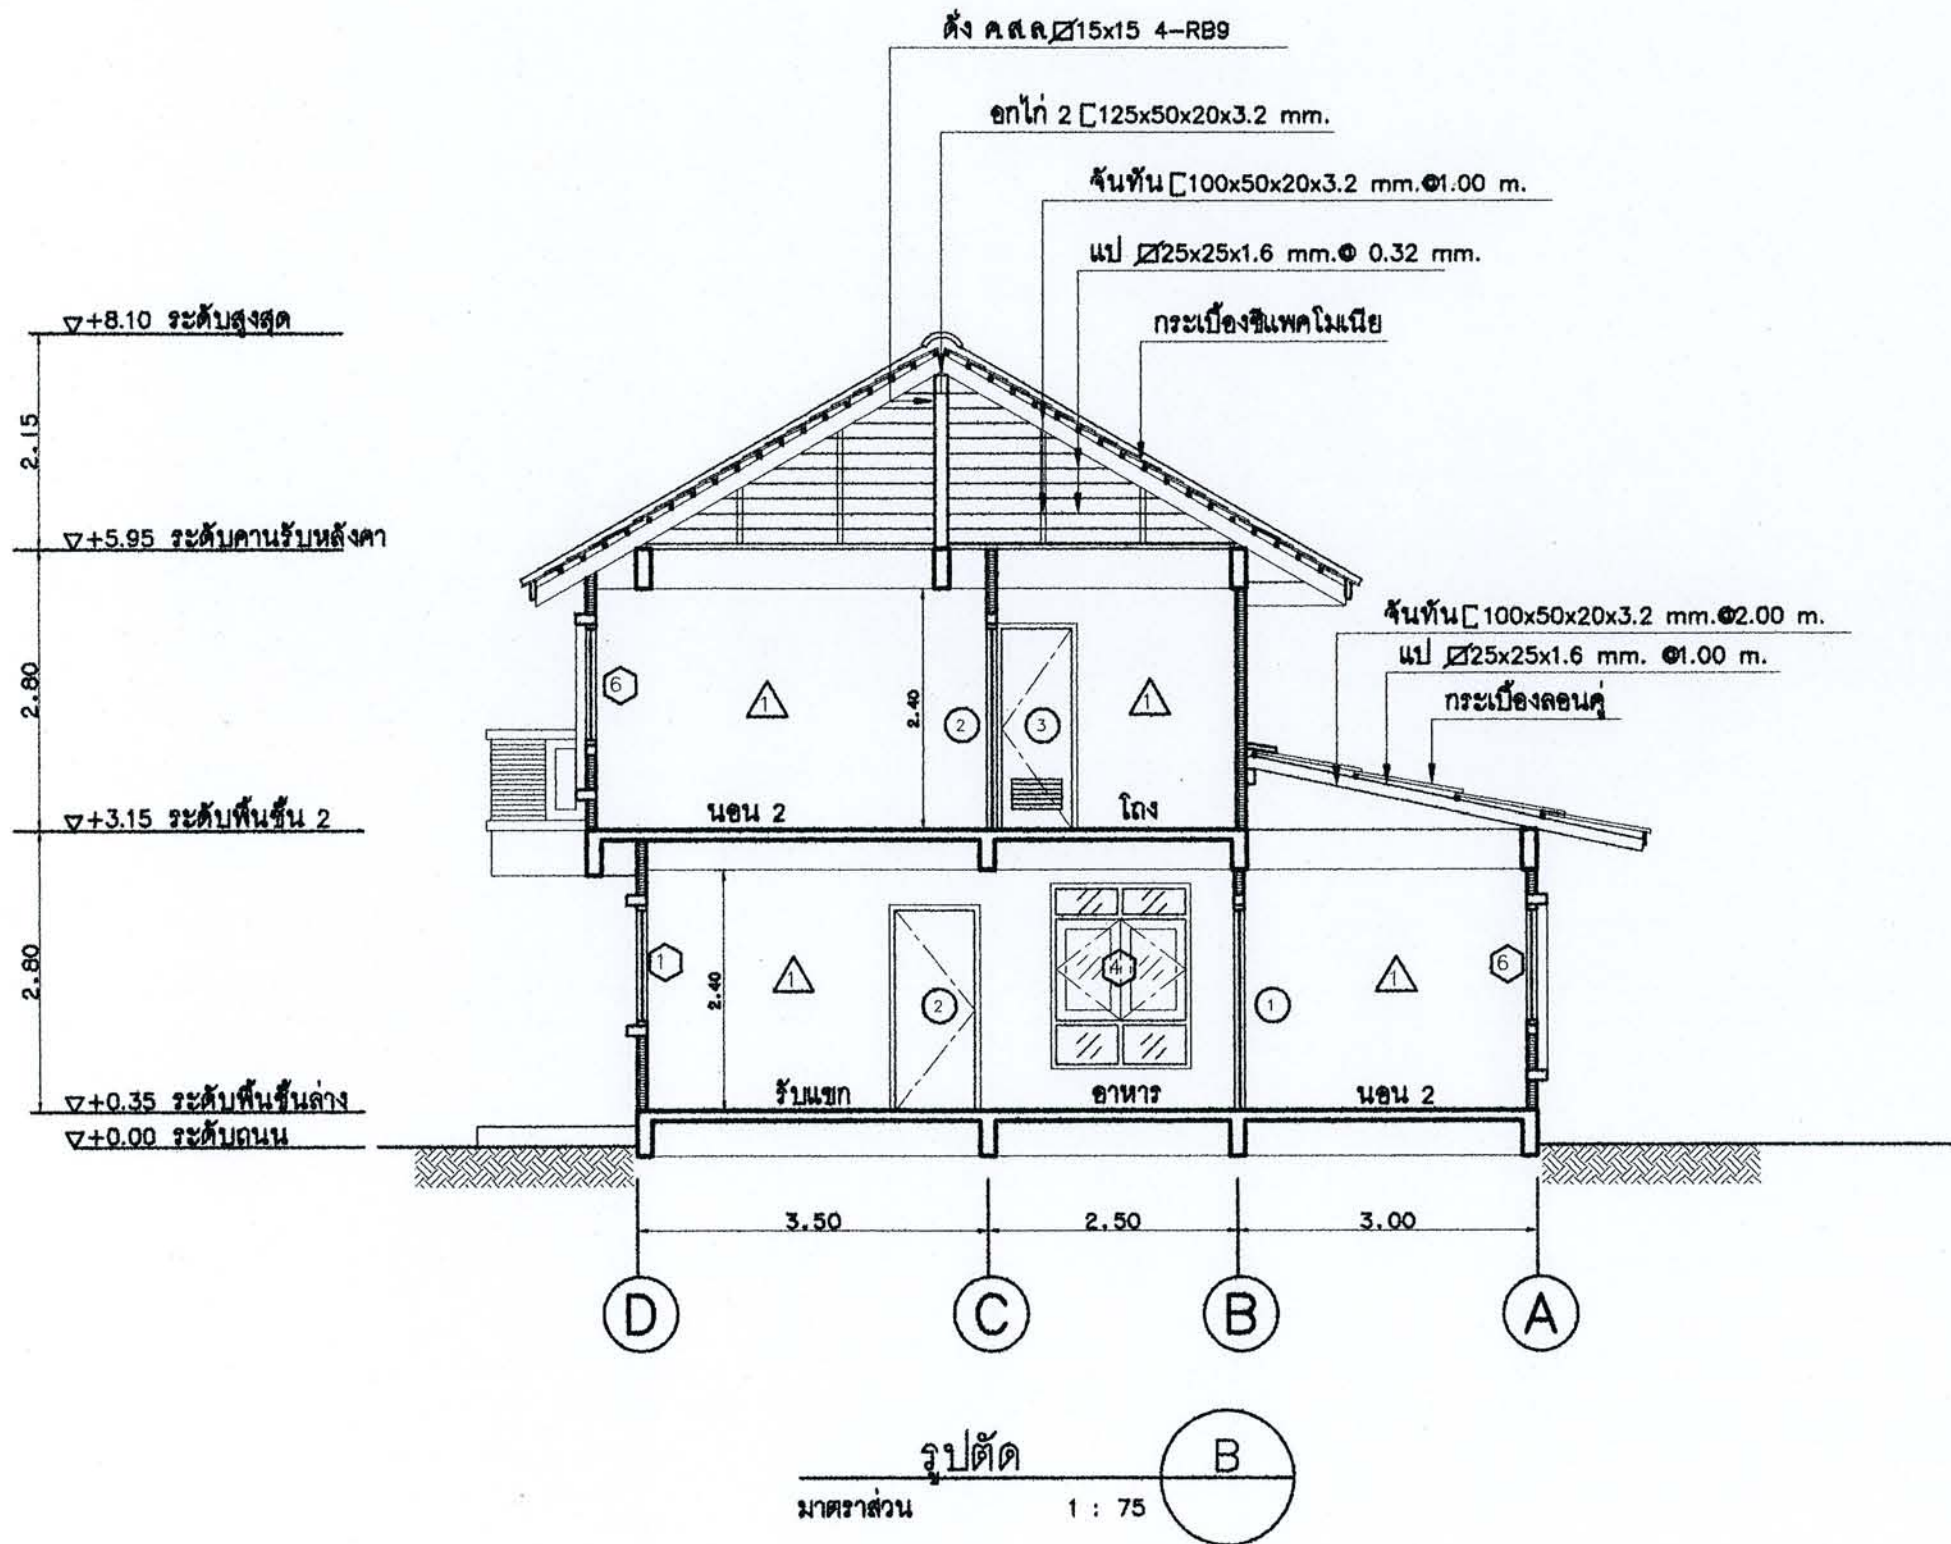



สำนักงานโยธา
กรุงเทพมหานคร

โครงการ
แบบบ้านยืมเพื่อประชาชน

ตามนโยบาย

ม.ร.ว.สุขุมพันธุ์ บริพัตร ผู้ว่าฯ กทม.
นายพรทศ เศรษฐไพฑูรย์ รองผู้ว่าฯ กทม.
นายธีระชน มโนชัยพิบูลย์ รองผู้ว่าฯ กทม.
นายพงษ์ศักดิ์ แสนลิ้นดี ปลัดฯ กทม.

ผู้อำนวยการสำนักงานโยธา
นายชุมพล สภาภักดิ์
รองผู้อำนวยการสำนักงานโยธา
นายทวีศักดิ์ เกียรติภินทร
ผู้อำนวยการสำนักงานออกแบบ
นายจรูญศักดิ์ สมนิโยม
หัวหน้ากลุ่มงานสถาปัตยกรรม
นายสินธุ์ชัย บุญปักษ์
หัวหน้ากลุ่มงานวิศวกรรม
นายธีระยุทธ คงสวัสดิ์ชัย

สถาปนิก
นายปริศนา นิมากร
วิศวกรโครงสร้าง
วิศวกรไฟฟ้า
วิศวกรสุขาภิบาล
นางสาวณณชรีฯ สมหอม
วิศวกรเครื่องกล

นายช่างเขียนแบบ
ว่าที่ร้อยตรีปรีชา ประกิจ


แบบ
บ้านทองหลาง
เจ้าของ
สถานที่

แบบแสดง
แบบขยายประตู หน้าต่าง

มาตราส่วน 1:50

FILE :
วันที่ 25 ธันวาคม 2553
คัดลอกแบบ
ว่าที่ร้อยตรีปรีชา ประกิจ
หน้า 23

รายการแก้ไขแบบ

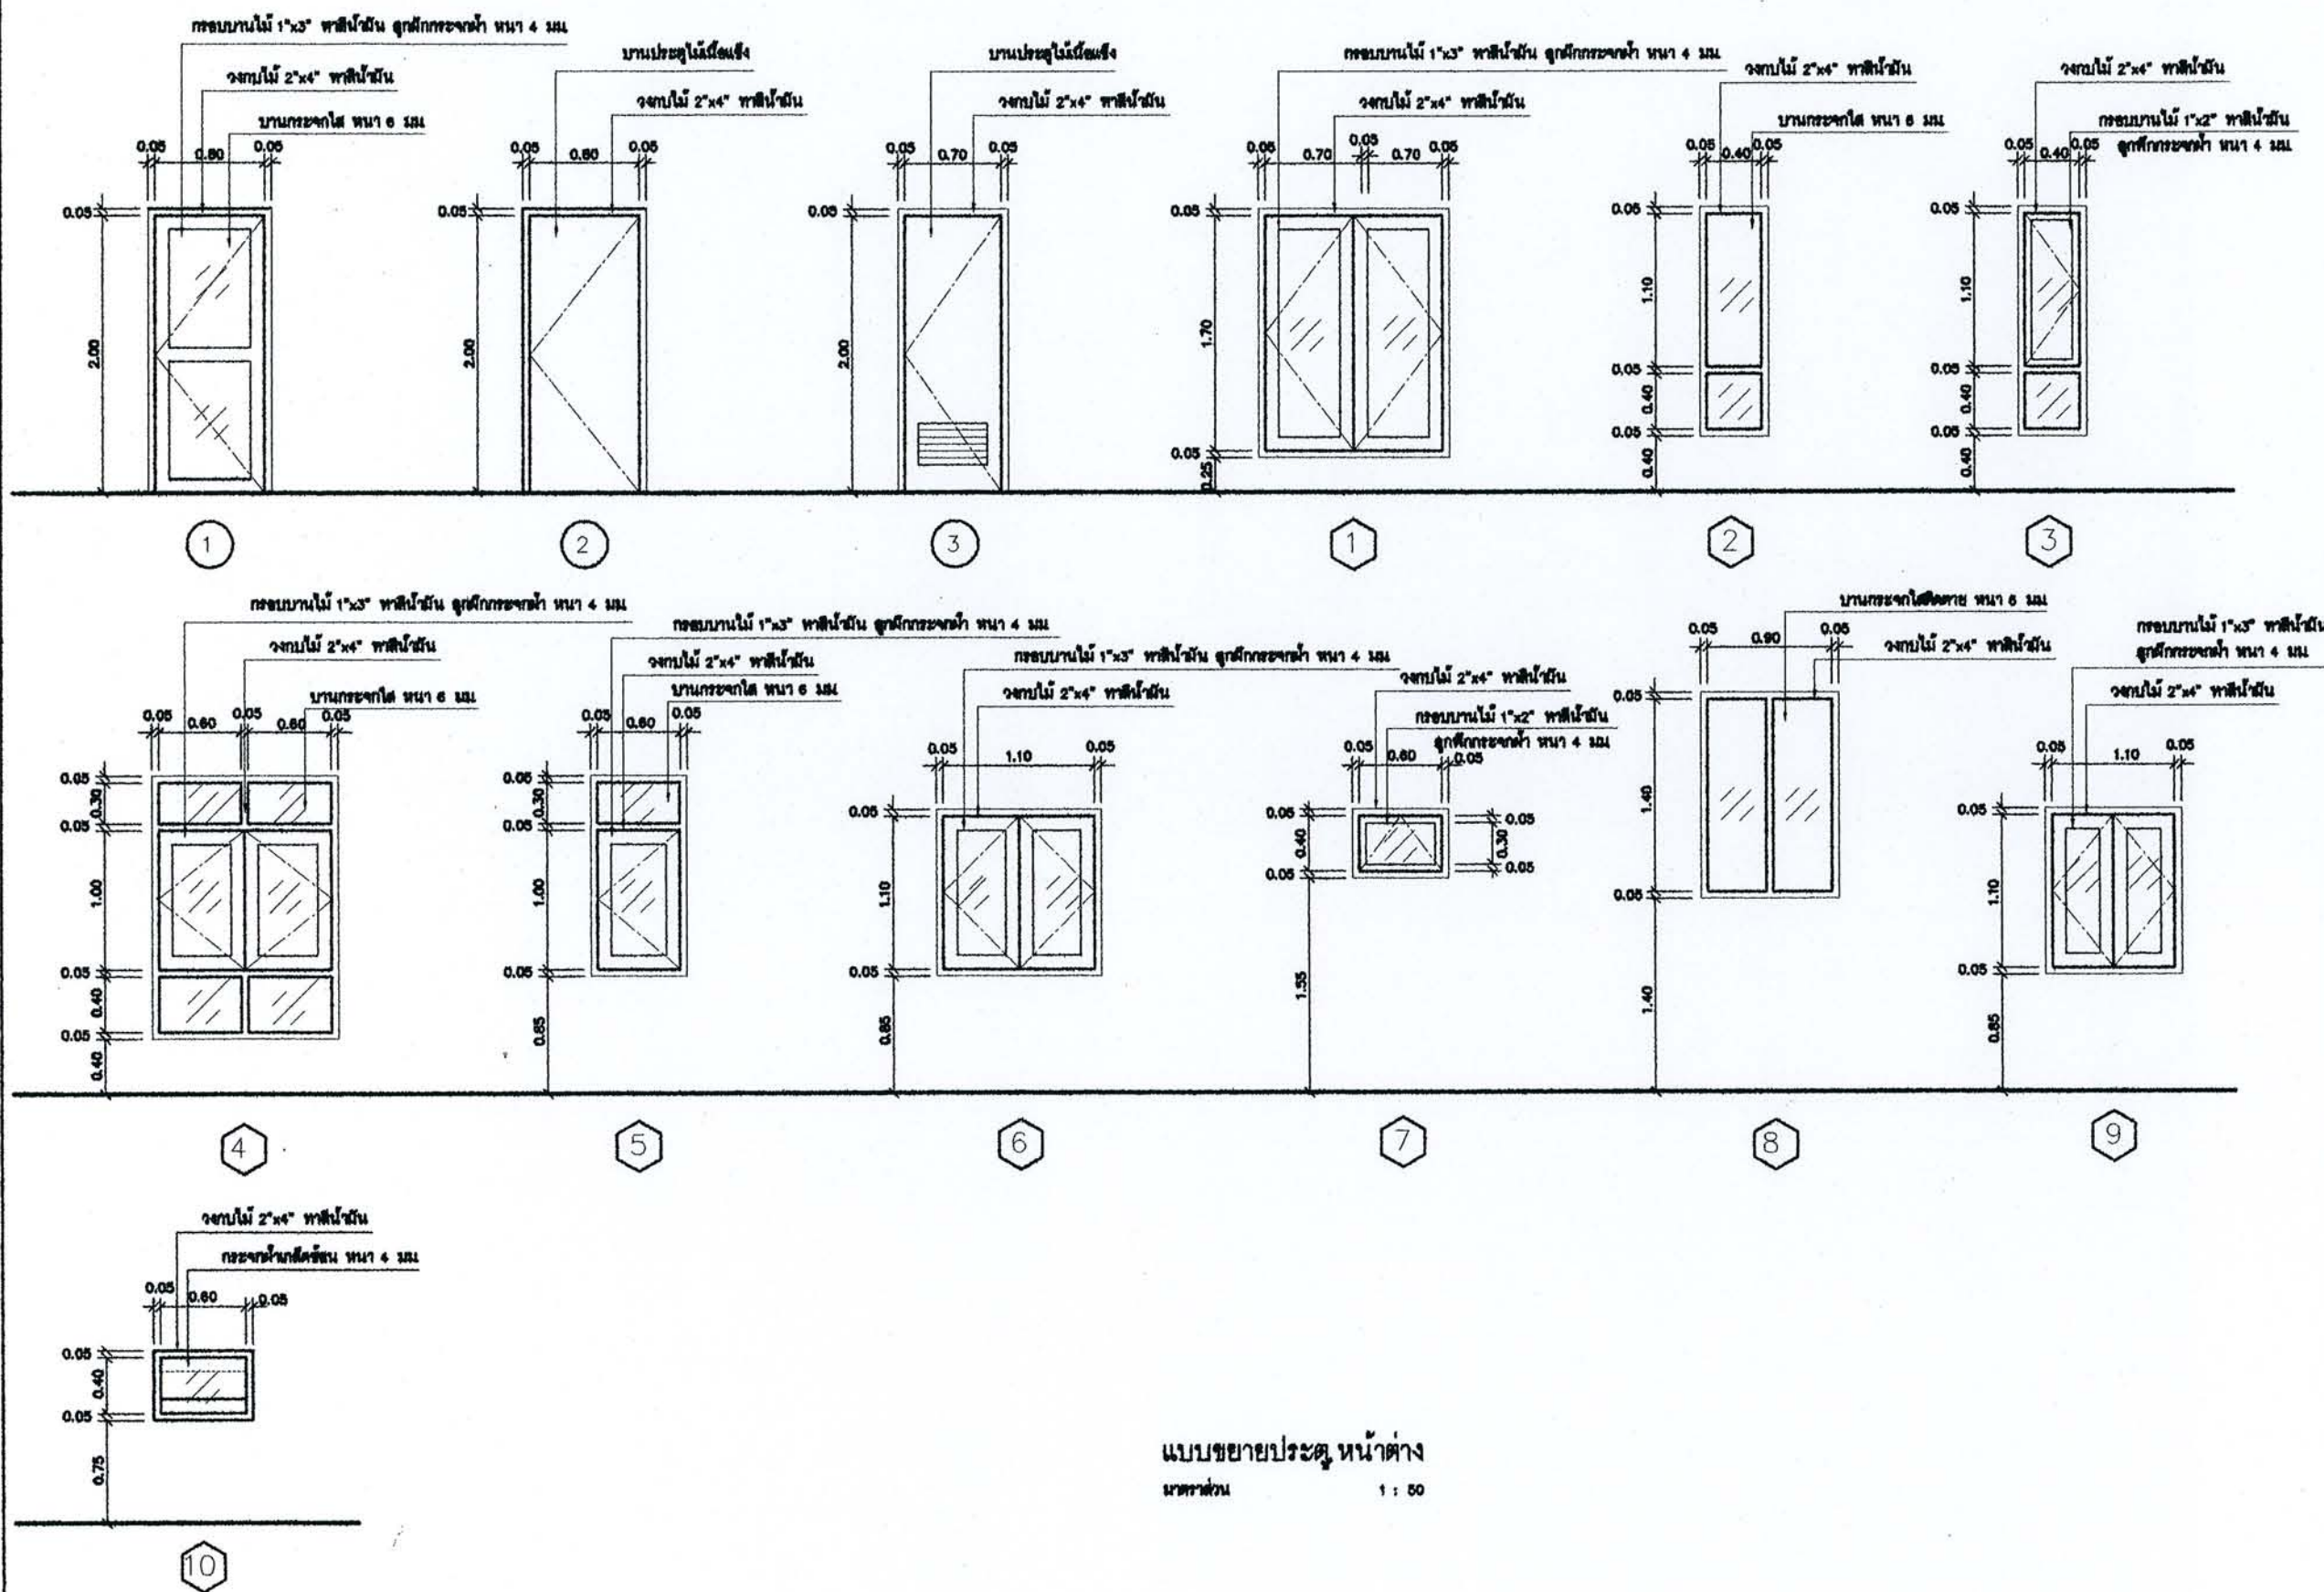

แบบขยายประตู หน้าต่าง
มาตราส่วน 1 : 50



สำนักงานโยธา
กรุงเทพมหานคร

โครงการ
แบบบ้านยืมเพื่อประชาชน

ตามนโยบาย

ม.ร.ว.สุขุมพันธุ์ บริพัตร ผู้ว่าฯ กทม.
นายพรเทพ เศรษฐิน้อย รองผู้ว่าฯ กทม.
นายธีระชน มโนชัยปิยะ รองผู้ว่าฯ กทม.
นายพงศ์ศักดิ์ แสนสันทน์ ปลัดฯ กทม.

ผู้ช่วยราชการสำนักงานโยธา
นายชุมพล คำภาทนต์
รองผู้อำนวยการสำนักงานโยธา
นายทวีศักดิ์ เลิศประพันธ์
ผู้ช่วยราชการสำนักงานออกแบบ
นายจตุรงค์ สมนิยม
หัวหน้ากลุ่มงานสถาปัตยกรรม
นายสินธุ์ชัย บุญปัทม
หัวหน้ากลุ่มงานวิศวกรรม
นายธีระยุทธ คงระวงศ์โยธา

สถาปนิก

นายปรีดิท มีมาก

วิศวกรโครงสร้าง

วิศวกรไฟฟ้า

วิศวกรสุขาภิบาล

นางสาววันจิรา สมทอม

วิศวกรเครื่องกล

นายช่างเขียนแบบ

ว่าที่ร้อยตรีปิศา ประจักษ์

แบบ บ้านทรงหลังคา

คำของ

สถานที่

แบบแสดง

แบบขยายบันได

มาตราส่วน 1 : 50

FILE :


วันที่ 25 ธันวาคม 2553

ชื่อโครงการ บ้านยืมแบบ

ว่าที่ร้อยตรีปิศา ประจักษ์


รวมคะแนน 23

รายการแก้ไขแบบ

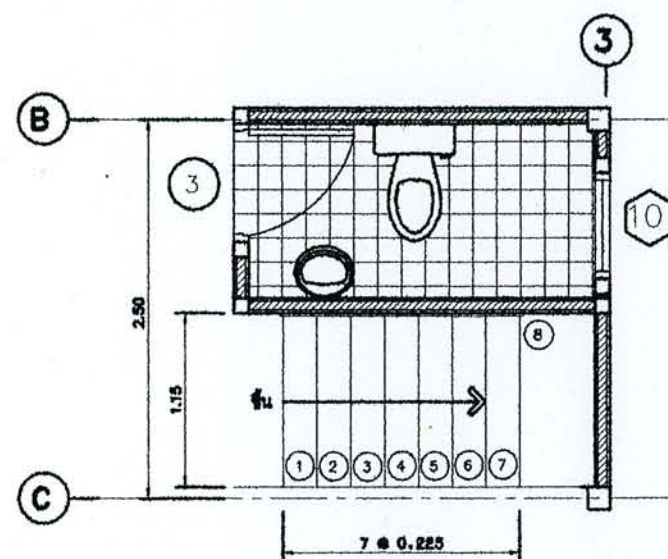


ขยายบันไดชั้นล่าง

มาตราส่วน 1 : 50

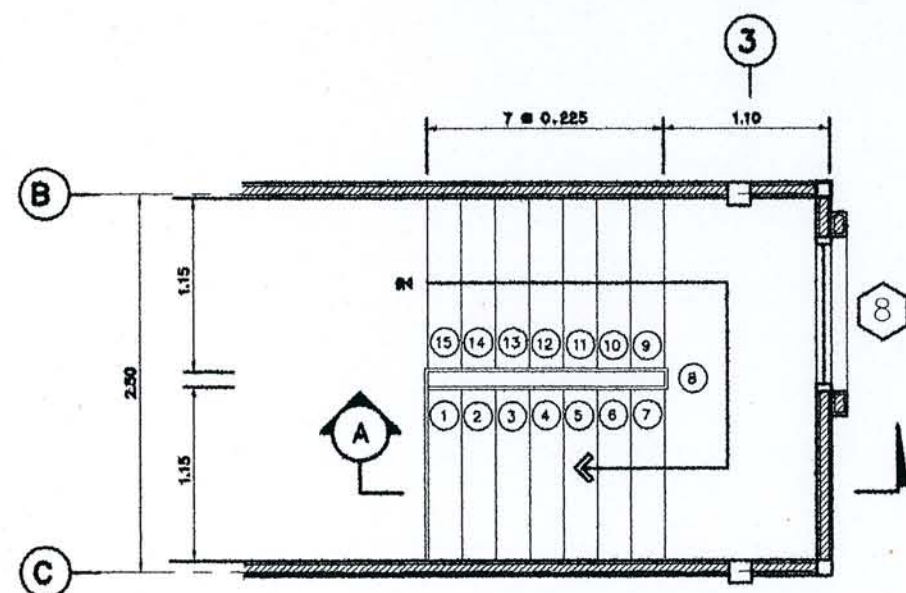

ขยายบันไดชั้นบน

มาตราส่วน 1 : 50

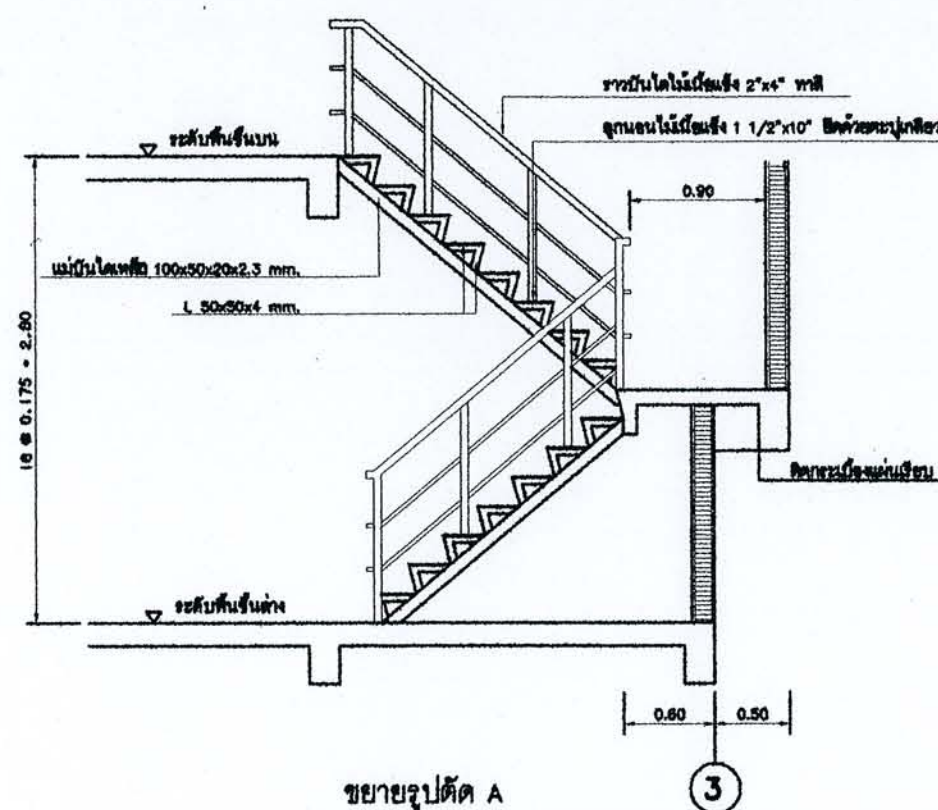

ขยายรูปตัด A

มาตราส่วน 1 : 50



สำนักงานโยธา
กรุงเทพมหานคร

โครงการ
แบบบ้านยืมเพื่อประชาชน

ตามนโยบาย

ม.ร.ว.สุขุมพันธุ์ บริพัตร ผู้ว่าฯกทม.
นายพรเทพ เศรษฐินชัย รองผู้ว่าฯกทม.
นายธีระชน มโนชัยพิบูลย์ รองผู้ว่าฯกทม.
นายพงษ์ศักดิ์ เศรษฐินชัย ปลัดฯกทม.

ผู้อำนวยการสำนักงานโยธา
นายชุมพล สภาพล
รองผู้อำนวยการสำนักงานโยธา
นายทวีศักดิ์ เดชประพันธ์
ผู้อำนวยการสำนักงานออกแบบ
นายจตุรงค์ สันติเยม
หัวหน้ากลุ่มงานสถาปัตยกรรม
นายสินธุ์ชัย บุญนิกร
หัวหน้ากลุ่มงานวิศวกรรม
นายธีระยุทธ คงระคิดเกียรติ

สถาปนิก
นายปรีดิท ธิมาภ
วิศวกรโครงสร้าง
วิศวกรไฟฟ้า
วิศวกรสุขาภิบาล
นางสาวมณฑิรา สมหอม
วิศวกรเครื่องกล

นายช่างเขียนแบบ
ว่าที่ร้อยตรีปริษา ประกิจ

แบบ
บ้านทองหลาง
เจ้าของ
สถานที่

แบบแสดง
แบบขยายห้องน้ำ
1


มาตราส่วน 1:25

FILE :
วันที่ 25 มิถุนายน 2553
คัดลอกแบบ
ว่าที่ร้อยตรีปริษา ประกิจ


แผ่นที่
A-14

รวมแผ่น
23

รายการแก้ไขแบบ

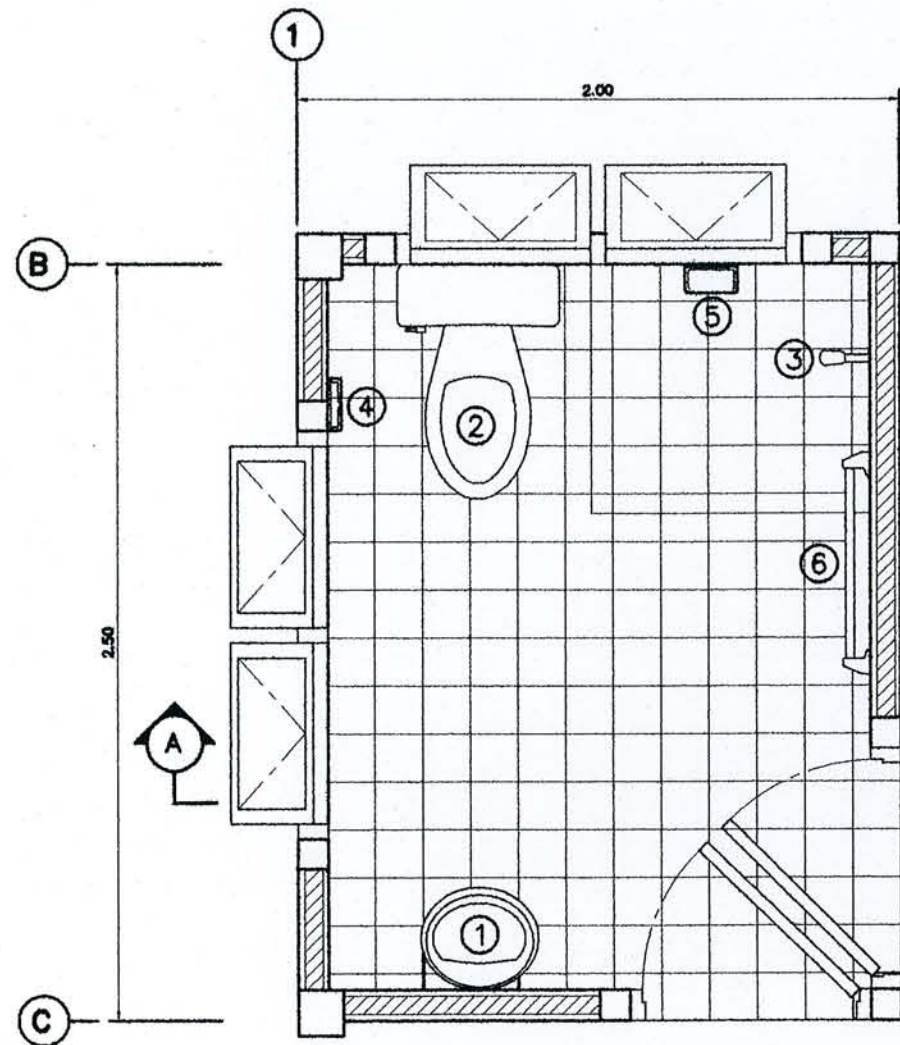

ขยายห้องน้ำ 1
มาตราส่วน 1 : 25

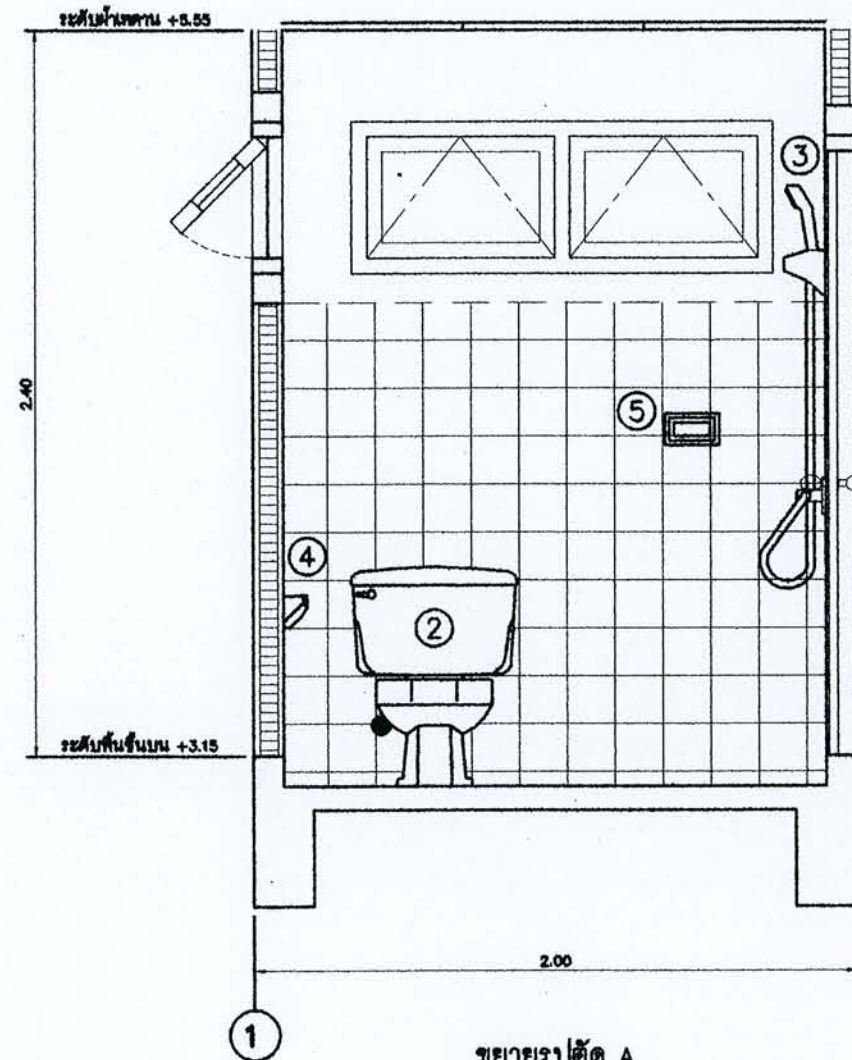

ขยายรูปตัด A
มาตราส่วน 1 : 25

รายการวัสดุภัณฑ์			
รหัส	รายการ	คิดตั้งสูงจากพื้น	หมายเหตุ
1.	อ่างล้างหน้า ชนิดรวมผนัง รุ่น สี	0.80	
2.	โถชักโครกชนิดนั่งราบ รุ่น สี		
3.	ฝักบัว ชนิดสายอ่อน รุ่น	1.80	
4.	ที่ใส่กระดาษชำระ รุ่น สี	0.45-0.50	
5.	ที่ใส่สบู่ ชนิดฝังในผนัง รุ่น สี	1.20	
6.	ราวแขวนผ้า	1.60	
7.	ก๊อกล้างพื้น 1/2"	0.45-0.50	
8.	กระจกเงาอย่างดี	1.70-1.80	
9.	โถชักโครกชนิดนั่งยอง รุ่น สี		
FD.	ดูระบายนํ้าที่พื้น ชนิดมีที่ดักผงและกลิ่น		



สำนักงานโยธา
กรุงเทพมหานคร

โครงการ
แบบบ้านยืมเพื่อประชาชน

ตามนโยบาย

น.ร.สุเมธพันธ์ บริพัตร ผู้อำนวยการ
นายพรเทพ เศรษฐกิจ รองผู้อำนวยการ
นายธีระชัย มโนชัยบุตร รองผู้อำนวยการ
นายพงษ์ศักดิ์ เสงี่ยมศักดิ์ ปลัดเขต

ผู้อำนวยการสำนักงานโยธา	
นายชุมพล สภาพล	
รองผู้อำนวยการสำนักงานโยธา	
นายทวีศักดิ์ เสือประพันธ์	
ผู้อำนวยการสำนักงานออกแบบ	
นายจตุรงค์ สมนิยม	
หัวหน้ากลุ่มงานสถาปัตยกรรม	
นายสินธุ์ชัย บุญเบิกชัย	
หัวหน้ากลุ่มงานวิศวกรรม	
นายธีระยุทธ คงสรรค์เสถียร	

สถาปนิก	
นายปรีดิศ มีมาก	
วิศวกรโครงสร้าง	
วิศวกรไฟฟ้า	
วิศวกรสุขาภิบาล	
นางสาวมณฑิรา สมหอม	
วิศวกรเครื่องกล	


นายช่างเขียนแบบ	
วาทิธรชัยปรีชา ประกิจ	

แบบ	บ้านทองหลาง
เจ้าของ	
สถานที่	

แบบแสดง	แบบขยายห้องน้ำ 2
มาตราส่วน	1:25

FILE :	แผ่นที่ A-15
วันที่ 01/01/2553	รวมแผ่น 23
คัดลอกแบบ	
วาทิธรชัยปรีชา ประกิจ	


รายการแก้ไขแบบ	
----------------	--

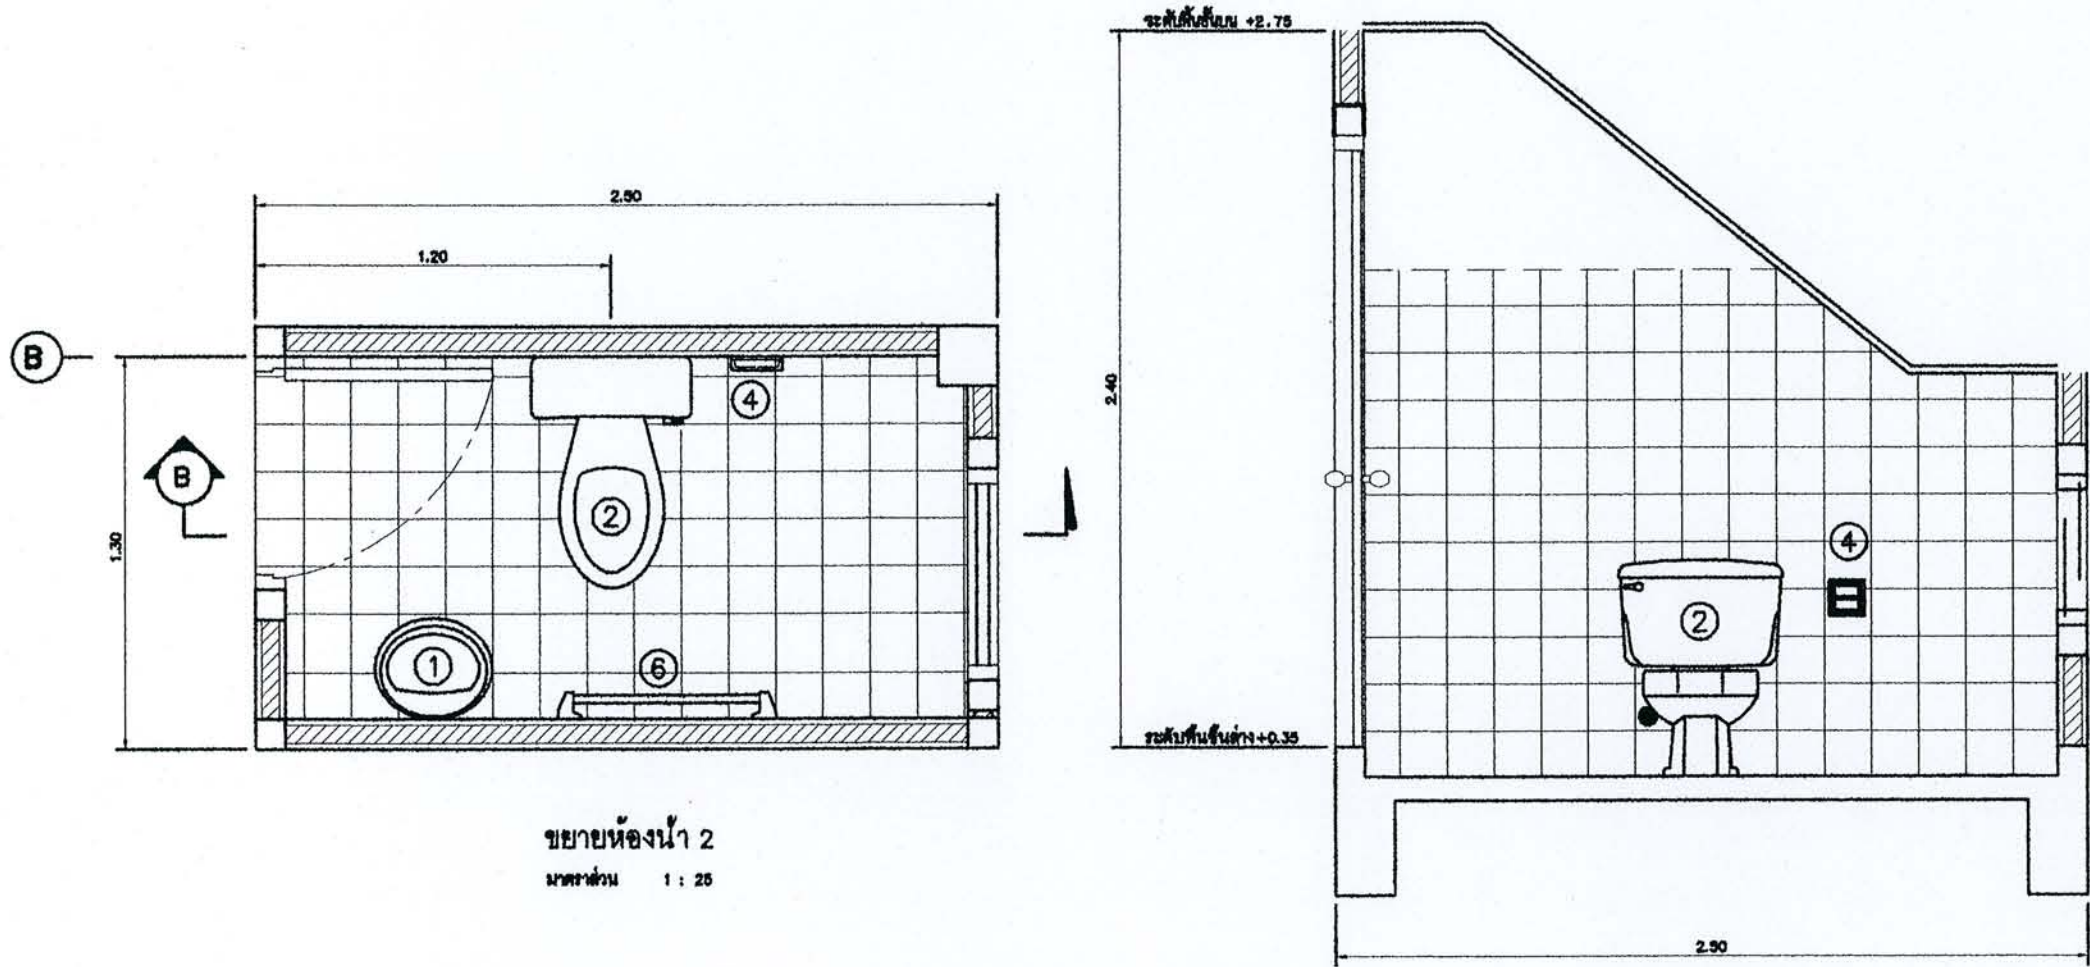

ขยายห้องน้ำ 2
มาตราส่วน 1 : 25


ขยายรูปตัด B
มาตราส่วน 1 : 25

รายการสุขภัณฑ์			
รหัส	รายการ	ติดตั้งจากพื้น	หมายเหตุ
1.	อ่างล้างหน้า ชนิดแขวนผนัง รุ่น สี	0.80	
2.	โถสุขภัณฑ์ชนิดนั่งราบ รุ่น สี		
3.	ฝักบัว ชนิดสายอ่อน รุ่น	1.80	
4.	ที่ใส่กระดาษชำระ รุ่น สี	0.45-0.50	
5.	ที่ใส่สบู่ ชนิดฝังในผนัง รุ่น สี	1.20	
6.	ราวแขวนผ้า	1.60	
7.	ก๊อกน้ำล้างพื้น 1/2"	0.45-0.50	
8.	กระจกเงาอ่าง	1.70-1.80	
9.	โถสุขภัณฑ์ชนิดนั่งยอง รุ่น สี		
FD.	รูระบายน้ำที่พื้น ชนิดมีที่ดักผมและกลิ่น		

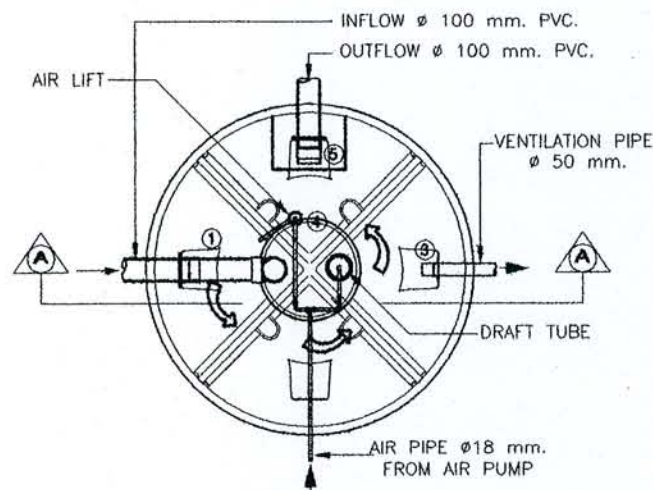


TOP-SECTION


- ① SOLIDS SEPARATION CHAMBER-1
- ② SOLIDS SEPARATION CHAMBER-2
- ③ AEROBIC CHAMBER-1
- ④ AEROBIC CHAMBER-2
- ⑤ SEDIMENTATION CHAMBER

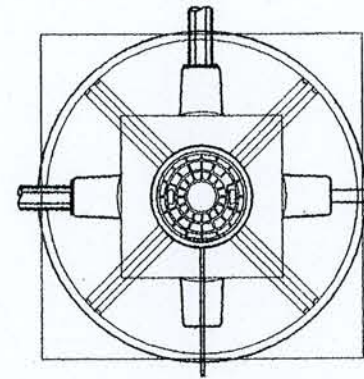


TOP-VIEW

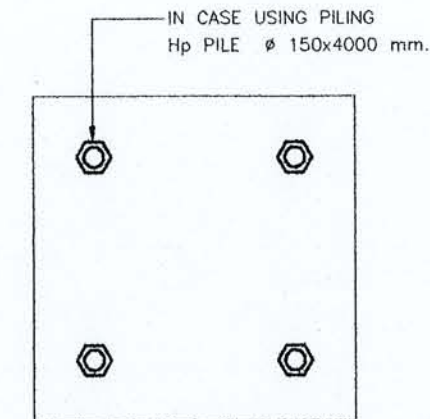

PLAN-PILE

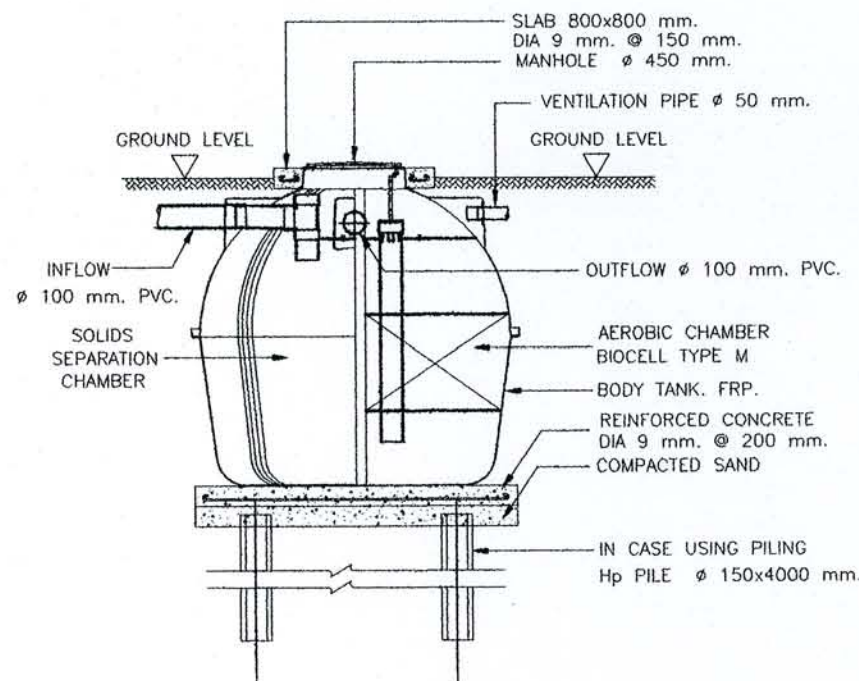

SECTION (A-A)

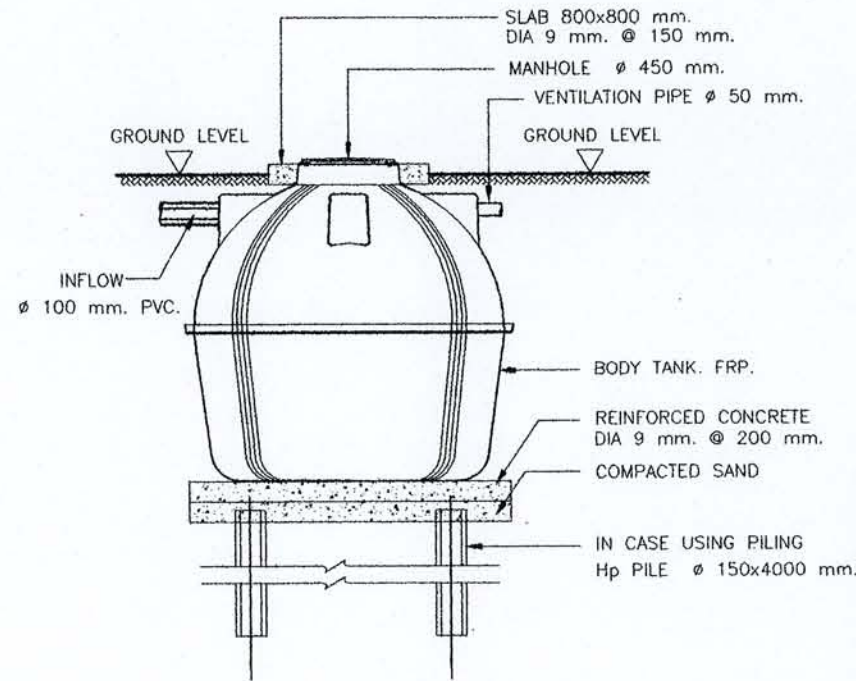

SIDE-VIEW

REMARK

PIPING AND FOUNDATION DESIGN, SHALL BE DETERMINED OR OMITTED BASED ON ACTUAL SOIL BEARING CAPACITY BY CONSULTING WITH CIVIL ENGINEER.

INSTALLATION FOR UNDER GARDEN AREA

BIOCELL MEDIA SPECIFICATION	
TYPE	M
SHAPE	EGG SHAPE HOLLOW SHELL
MAXIMUM I.D.; M.M. ϕ	45.0
LENGTH ; M.M.	54.0
MINIMUM I.D.; M.M. ϕ	30.0
SURFACE AREA ; M2	0.019677
MATERIAL	HDPE
SPECIFIC GRAVITY	0.964
SPECIFIC SURFACE AREA ; M2/M3.	170.72
VOID RATIO ; %	96.59

BIOTECH WASTEWATER TREATMENT TANK. SEPTIC AEROBIC FILTER TANK. MODEL BO-2200				
SCALE 1:30	STRUCTURAL ENGINEER	PITAKCHON	ENVIRONMENTAL SCIENCE	BAHMAN
DATE 17-08-2000	ENVIRONMENTAL ENGINEER	VICHAI POKHILUM	APPROVED BY	FUKUJI SEKENE
DWG. NO. BO-2200	ELECTRICAL ENGINEER	SOMHUEK	DRAWN BY	BAJIT

หมายเหตุ

ระบบบำบัดน้ำเสีย ใช้ถังบำบัดน้ำเสียสำเร็จรูป ขนาดและวิธีการติดตั้งดูตามแบบของบริษัทผู้ผลิตที่เลือกใช้



สำนักงานโยธา
กรุงเทพมหานคร

โครงการ
แบบบ้านยืมเพื่อประชาชน

ตามนโยบาย

น.ร.สุรพันธ์ บริพัตร ผู้ว่าฯกทม.
นายทศพร เศรษฐกิจ รองผู้ว่าฯกทม.
นายธีระชน มโนทิตะกุล รองผู้ว่าฯกทม.
นายพงษ์ศักดิ์ แสนจันทร์ ปลัดฯกทม.

ผู้อำนวยการสำนักงานโยธา
นายจุมพล สว่างพล
รองผู้อำนวยการสำนักงานโยธา
นายวิศักดิ์ เกียรติพันธ์
ผู้อำนวยการสำนักงานออกแบบ
นายจตุรงค์ สมนิยม
หัวหน้างานงานสถาปัตยกรรม
นายสินธุ์ชัย บุญปักษ์
หัวหน้างานงานวิศวกรรม
นายธีระยุทธ คงสวัสดิ์เกียรติ

สถาปนิก
นายปวิติท นิมาก

วิศวกรโครงสร้าง

วิศวกรไฟฟ้า

วิศวกรสุขาภิบาล

นางสาวณัฏฐา สมหม่อม
วิศวกรเครื่องกล

นายช่างเขียนแบบ
ว่าที่ร้อยตรีปรีชา ประกิจ

แบบ บ้านทองหลาง

เจ้าของ

สถานที่

แบบแสดง
แบบขยายถังบำบัด

ขนาดพื้นที่

FILE : แผนที่

วันที่ 17-08-2000 A-16

ออกแบบโดย นายจุมพล

ว่าที่ร้อยตรีปรีชา ประกิจ 23

รายการแก้ไขแบบ



สำนักงานโยธา
กรุงเทพมหานคร

โครงการ
แบบบ้านยืมเพื่อประชาชน

ตามนโยบาย

ม.ร.ว.สุขุมพันธุ์ บริพัตร ผู้ว่าฯกทม.
นายพรเทพ เศรษฐิน้อย รองผู้ว่าฯกทม.
นายธีรชน มโนชัยปิยะกุล รองผู้ว่าฯกทม.
นายพงษ์ศักดิ์ แสนสมันต์ ปลัดฯกทม.

ผู้อำนวยการสำนักงานโยธา

นายจุมพล สำนาค

รองผู้อำนวยการสำนักงานโยธา

นายทวีศักดิ์ เกศประพันธ์

ผู้อำนวยการสำนักงานออกแบบ

นายจตุรงค์ สมนิยม

หัวหน้ากลุ่มงานสถาปัตยกรรม

นายสินธุ์ชัย บุญบักย์

หัวหน้ากลุ่มงานวิศวกรรม

นายธีระยุทธ คงสรศักดิ์

สถาปนิก

นายปวิศ ธิมา

วิศวกรโครงสร้าง

วิศวกรไฟฟ้า

วิศวกรสุขาภิบาล

นางสาวมณฑิรา สมหอม

วิศวกรเครื่องกล

นายช่างเขียนแบบ

ว่าที่ร้อยตรีปวีณา ประกิจ

แบบ บ้านทองหลาง

เจ้าของ

สถานที่

แบบแสดง

แบบขยายบ่อพัก

มาตราส่วน 1:10

FILE :

วันที่ 25 พฤษภาคม 2553


คัดลอกแบบ

ว่าที่ร้อยตรีปวีณา ประกิจ


รวมแผ่น

23


รายการแก้ไขแบบ

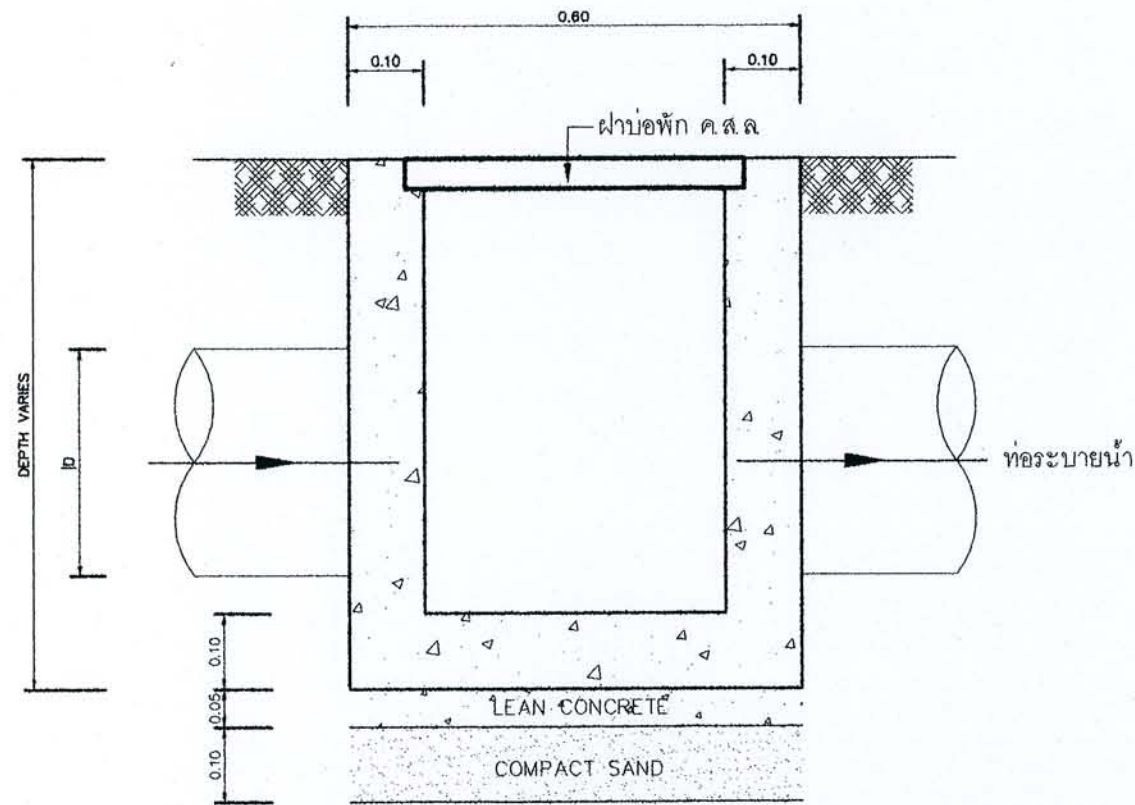


รูปตัด B-B
มาตราส่วน 1:10

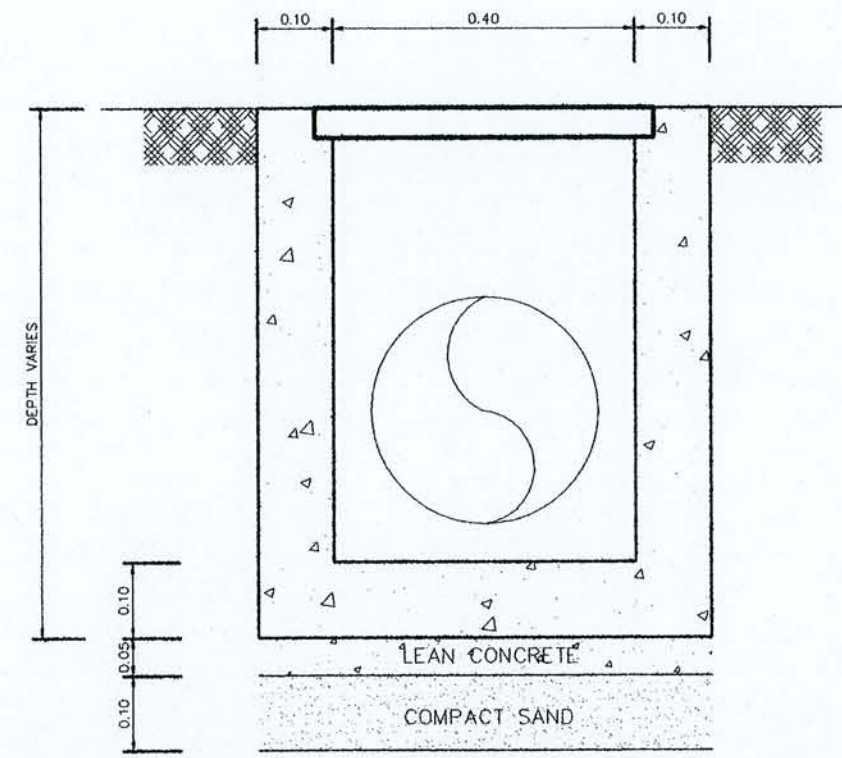

รูปตัด C-C
มาตราส่วน 1:10

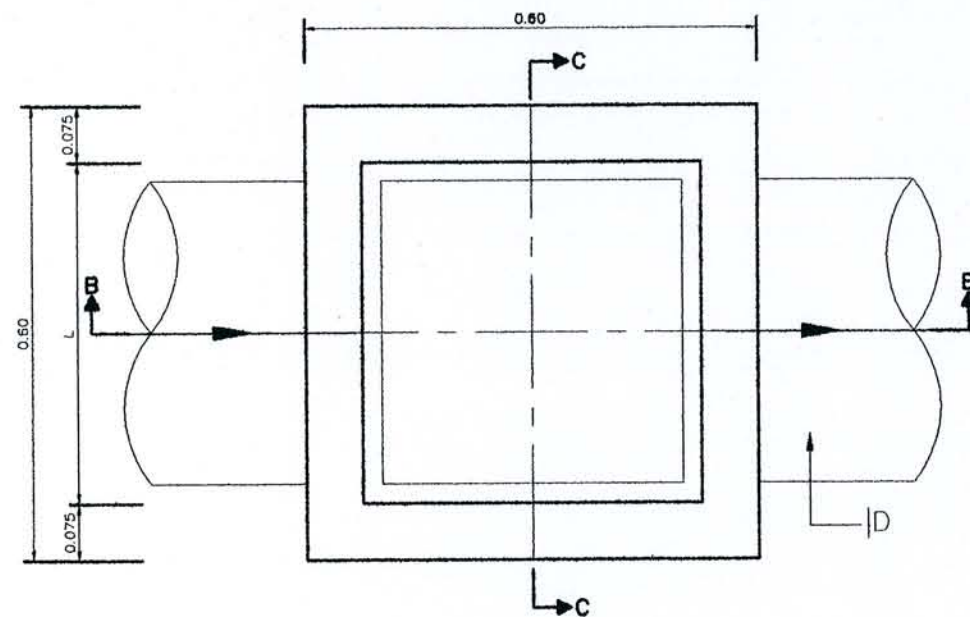

แบบขยายบ่อพักสำหรับรูปมาตรฐาน
มาตราส่วน 1:10

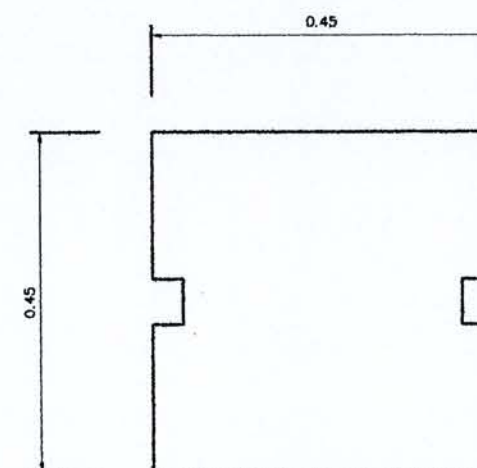

ฝาบ่อพัก ค.ส.ล.
มาตราส่วน 1:10



สำนักงานโยธา
กรุงเทพมหานคร

โครงการ
แบบบ้านยิมเพื่อประชาชน

ตามนโยบาย
ม.ร.ว.สุขุมพันธุ์ บริพัตร ผู้ว่าฯกทม.
นายพรเทพ เศรษฐินร้อย ร่องูวาทกม
นายธีระชน มโนชัยปิณฑ ร่องูวาทกม
นายพงศ์ศักดิ์ แสนลิ้น ปัดากกม


ผู้อำนวยการสำนักงานโยธา
นายชุมพล สำนกพล
รองผู้อำนวยการสำนักงานโยธา
นายทวีศักดิ์ เลิศประพันธ์
ผู้อำนวยการสำนักงานออกแบบ
นายจตุรงค์ สมนิยม
หัวหน้ากลุ่มงานสถาปัตยกรรม
นายดินสุชัย บุญปักษ์
หัวหน้ากลุ่มงานวิศวกรรม
นายธีระยุทธ คงสรศักดิ์

สถาปนิก
นายปรีดิท วัฒนา
วิศวกรโครงสร้าง
วิศวกรไฟฟ้า
วิศวกรสุขาภิบาล
นางสาวณณชิตา สมหอม
วิศวกรเครื่องกล
นายช่างเขียนแบบ
ว่าที่ร้อยตรีปรีชา ประกิจ


แบบ
บ้านทองหลาง
คำของ
สถานที่

แบบแสดง
แปลนเสาฐานราก
และแปลนคานพื้นชั้นล่าง
มาตราส่วน 1:75
FILE :
วันที่ 25 มิถุนายน 2553
ชุดเลข 01/2553
ว่าที่ร้อยตรีปรีชา ประกิจ
แผ่นที่ S-01
รวมแผ่น 23

รายการแก้ไขแบบ

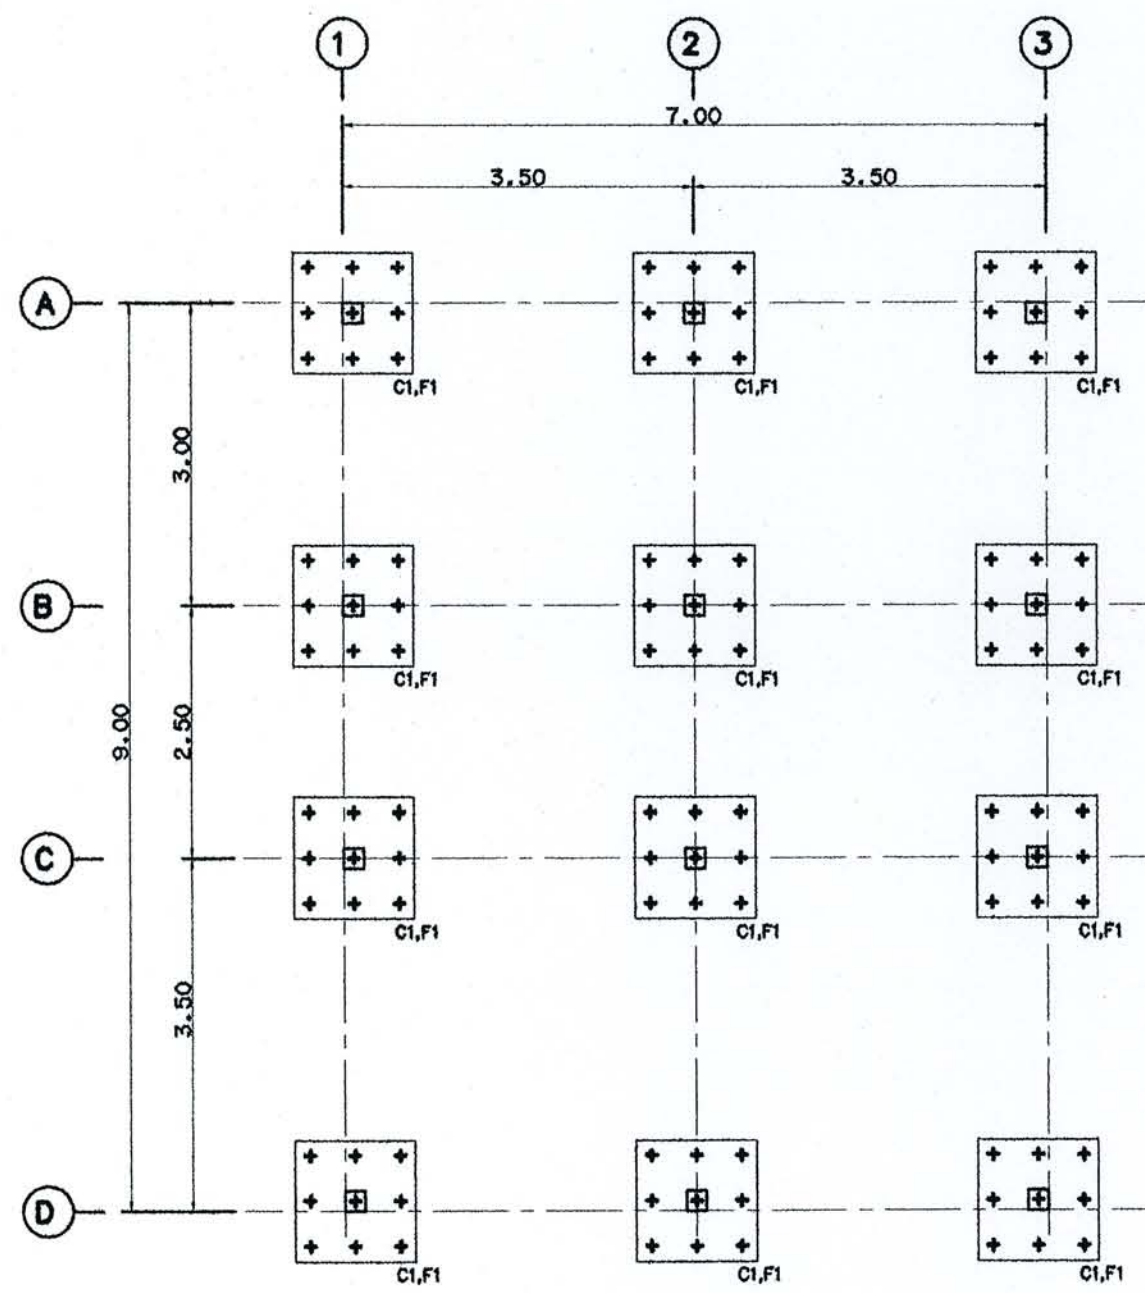

แปลนเสา , ฐานราก
มาตราส่วน 1 : 75

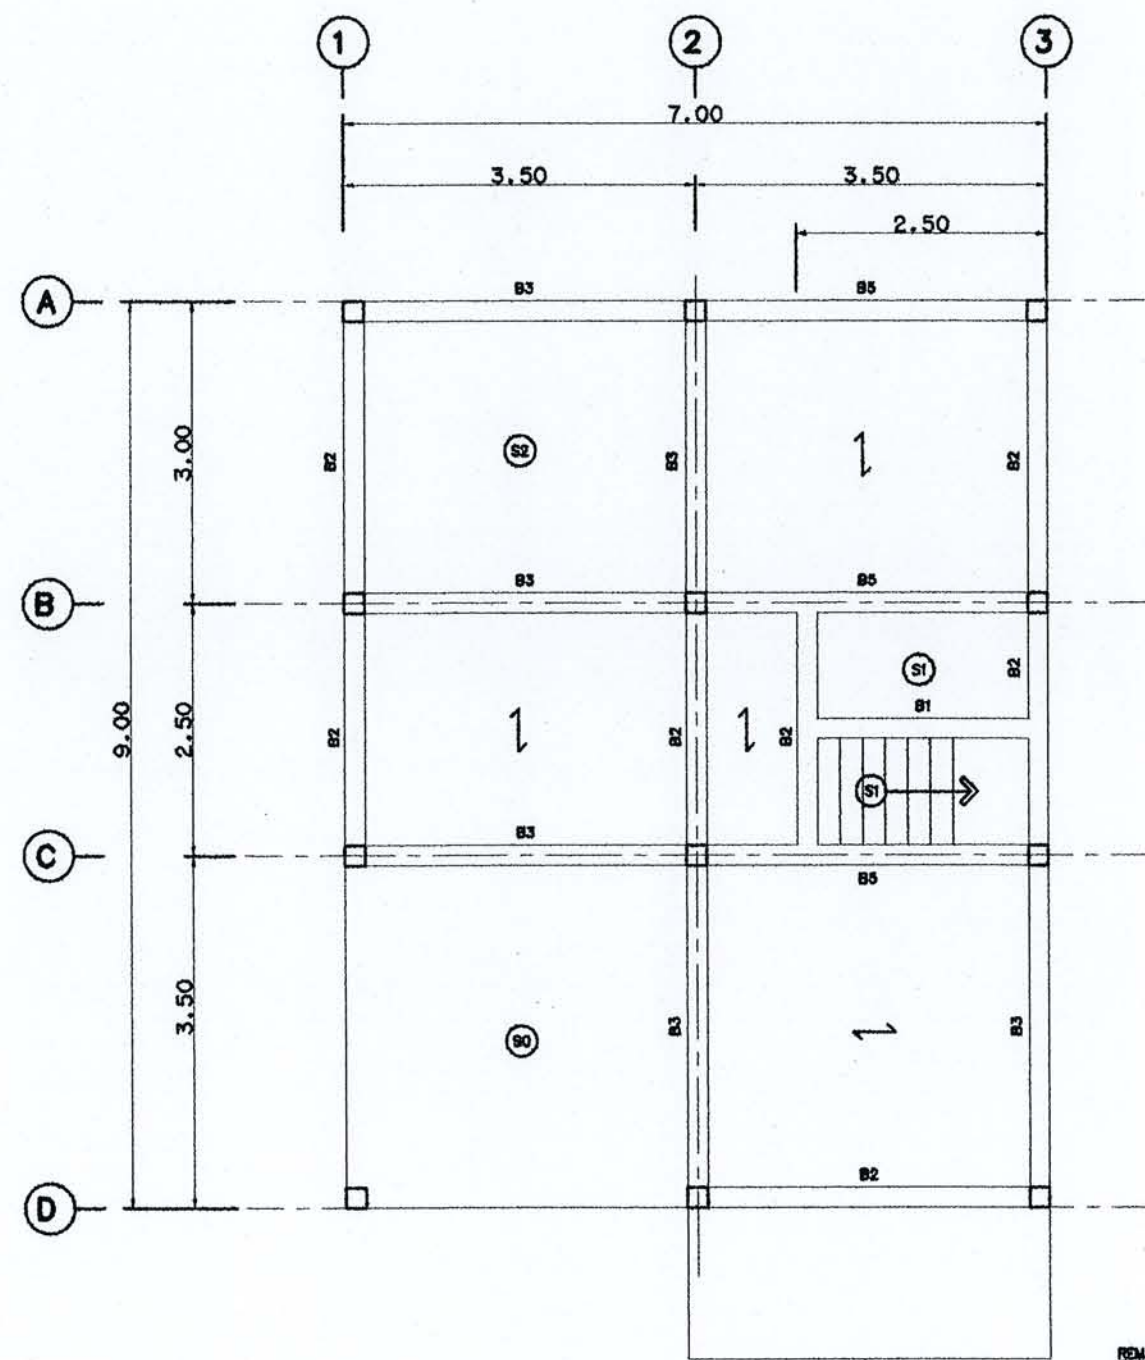

แปลนคานพื้นชั้นล่าง
มาตราส่วน 1 : 75

REMARK
→ SP SLAB



สำนักงานโยธา
กรุงเทพมหานคร

โครงการ
แบบบ้านยิมเพื่อประชาชน

ตามนโยบาย

น.ร.สุเมธพันธ์ บิณฑิต ผู้ว่าฯกทม.
นายพรเทพ เศรษฐกิจ รองผู้ว่าฯกทม.
นายธีระชน มโนชัยกุล รองผู้ว่าฯกทม.
นายพงษ์ศักดิ์ เตมียาห์ ปลัดฯกทม.

ผู้อำนวยการสำนักงานโยธา

นายสมศักดิ์ สว่างกุล

รองผู้อำนวยการสำนักงานโยธา

นายทวีศักดิ์ เลิศประพันธ์

ผู้อำนวยการสำนักงานออกแบบ

นายจตุรงค์ สมนิยม

หัวหน้ากองงานสถาปัตยกรรม

นายสันติชัย บุญปักษ์

หัวหน้ากองงานวิศวกรรม

นายธีระยุทธ คงธรรมาภัย

สถาปนิก

นายปรีดิศ มีมาก

วิศวกรโครงสร้าง

วิศวกรไฟฟ้า

วิศวกรสุขาภิบาล

นางสาวกมลทิศา สมทอง

วิศวกรเครื่องกล

นายช่างเขียนแบบ

ว่าที่ร้อยตรีปิศา ประกิจ

แบบ

บ้านทองหลาง

เจ้าของ

สถานที่

แบบแสดง

แปลนคานพื้นชั้นบน

มาตราส่วน 1:75

FILE :

ชั้นปี


เดือนพฤษภาคม 2553

โครงการบ้านพักแบบ

ว่าที่ร้อยตรีปิศา ประกิจ

23

รายการแก้ไขแบบ

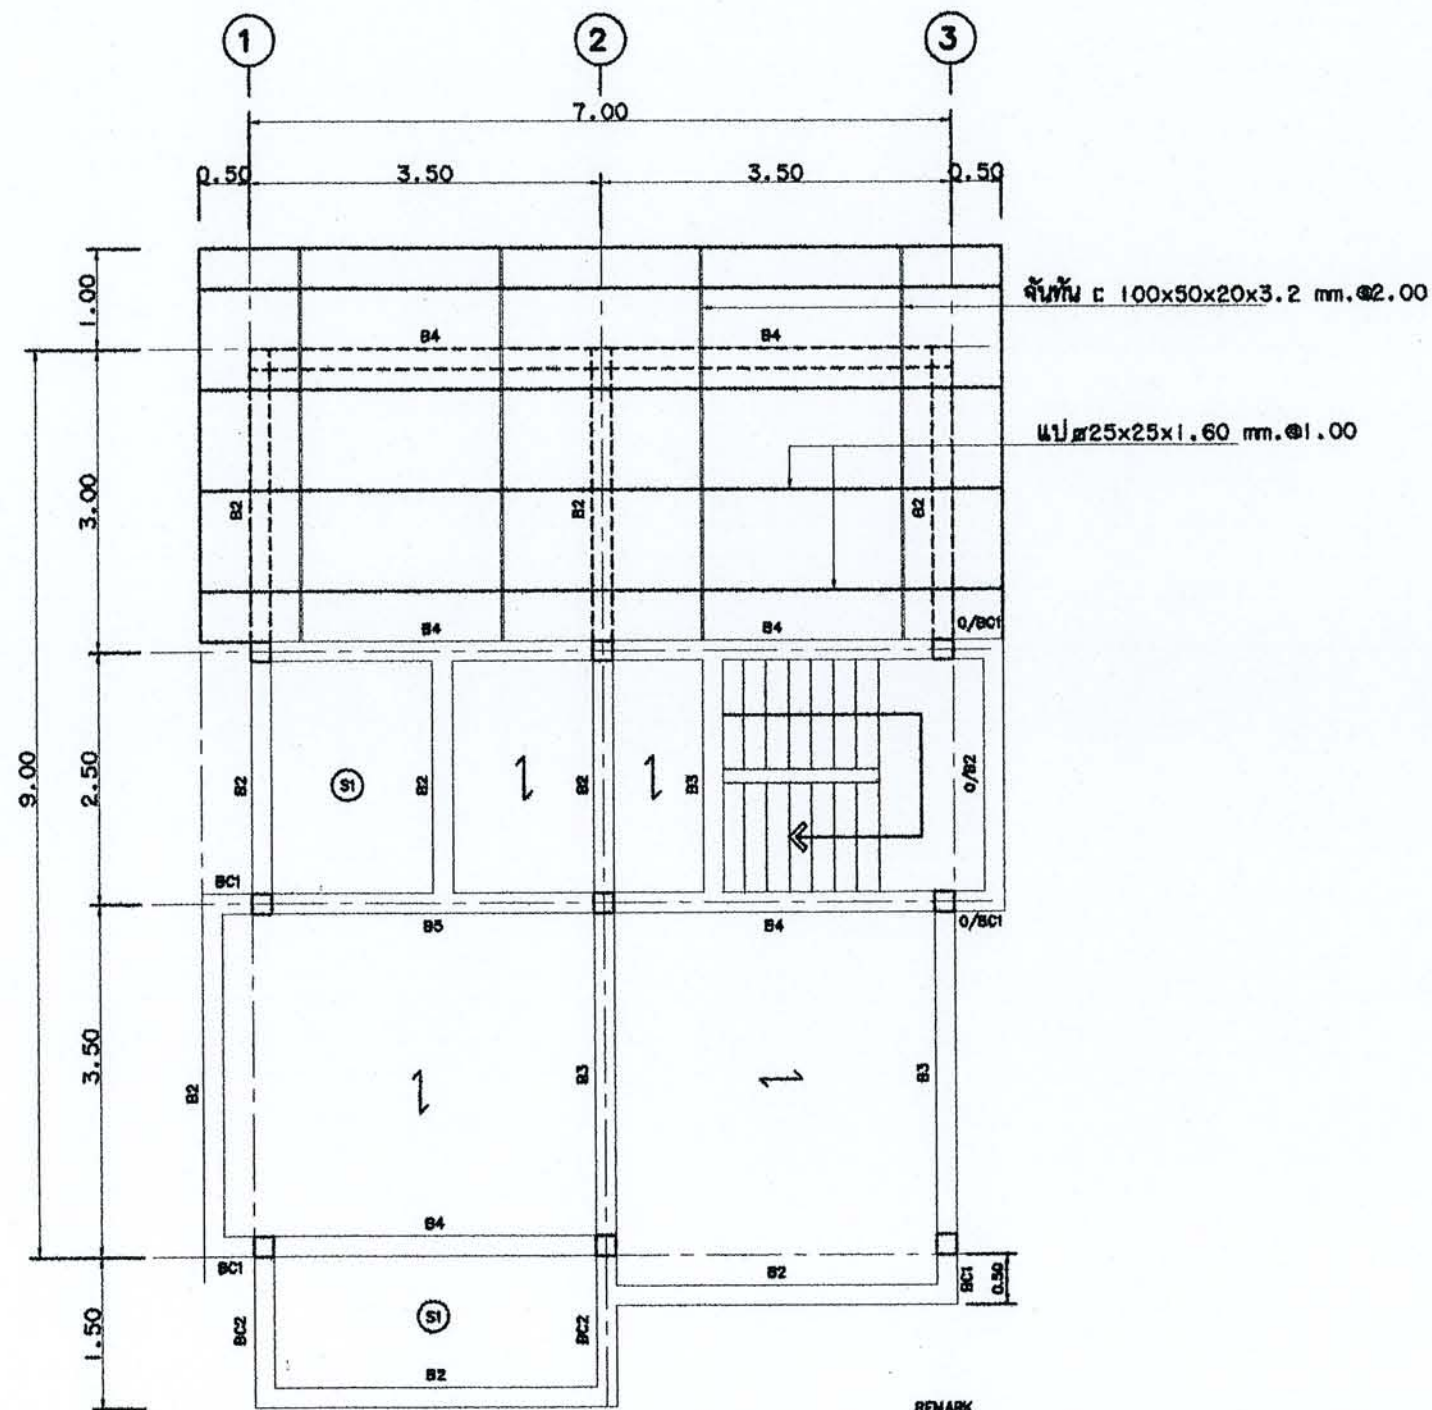

แปลนคานพื้นชั้นบน

มาตราส่วน 1 : 75



สำนักงานโยธา
กรุงเทพมหานคร

โครงการ
แบบบ้านยืมเพื่อประชาชน

ตามนโยบาย

ม.ร.ว.สุขุมพันธุ์ บริพัตร ผู้ว่าฯกทม.
นายพรเทพ เศรษฐิน นายช่างเทคนิค
นายธีระชน มโนวิทย์ นายช่างเทคนิค
นายพงศ์ศักดิ์ เสน่ห์ดี ปลัดฯกทม.

ผู้อำนวยการสำนักงานโยธา

นายจุมพล สว่างพล

รองผู้อำนวยการสำนักงานโยธา

นายทวิศักดิ์ เลิศประพันธ์

ผู้อำนวยการสำนักงานออกแบบ

นายจตุรงค์ สันติเยน

หัวหน้ากลุ่มงานสถาปัตยกรรม

นายสินธุ์ชัย บุญปักษ์

หัวหน้ากลุ่มงานวิศวกรรม

นายธีระยุทธ คงสรค์เดียง

สถาปนิก

นายปวิศ ธีมาก

วิศวกรโครงสร้าง

วิศวกรไฟฟ้า

วิศวกรสุขาภิบาล

นางสาวมณฑิรา สมหอม

วิศวกรเครื่องกล

นายช่างเขียนแบบ

วาทิธรศรีปรีชา ประกิจ

แบบ
บ้านทองหลาง

เจ้าของ

สถานที่

แบบแสดง

แปลน โครงหลังคา

มาตราส่วน 1:75

FILE :


วันที่ 15 มิถุนายน 2553

คัดลอกแบบ

วาทิธรศรีปรีชา ประกิจ

รวมแผ่น 23

รายการแก้ไขแบบ

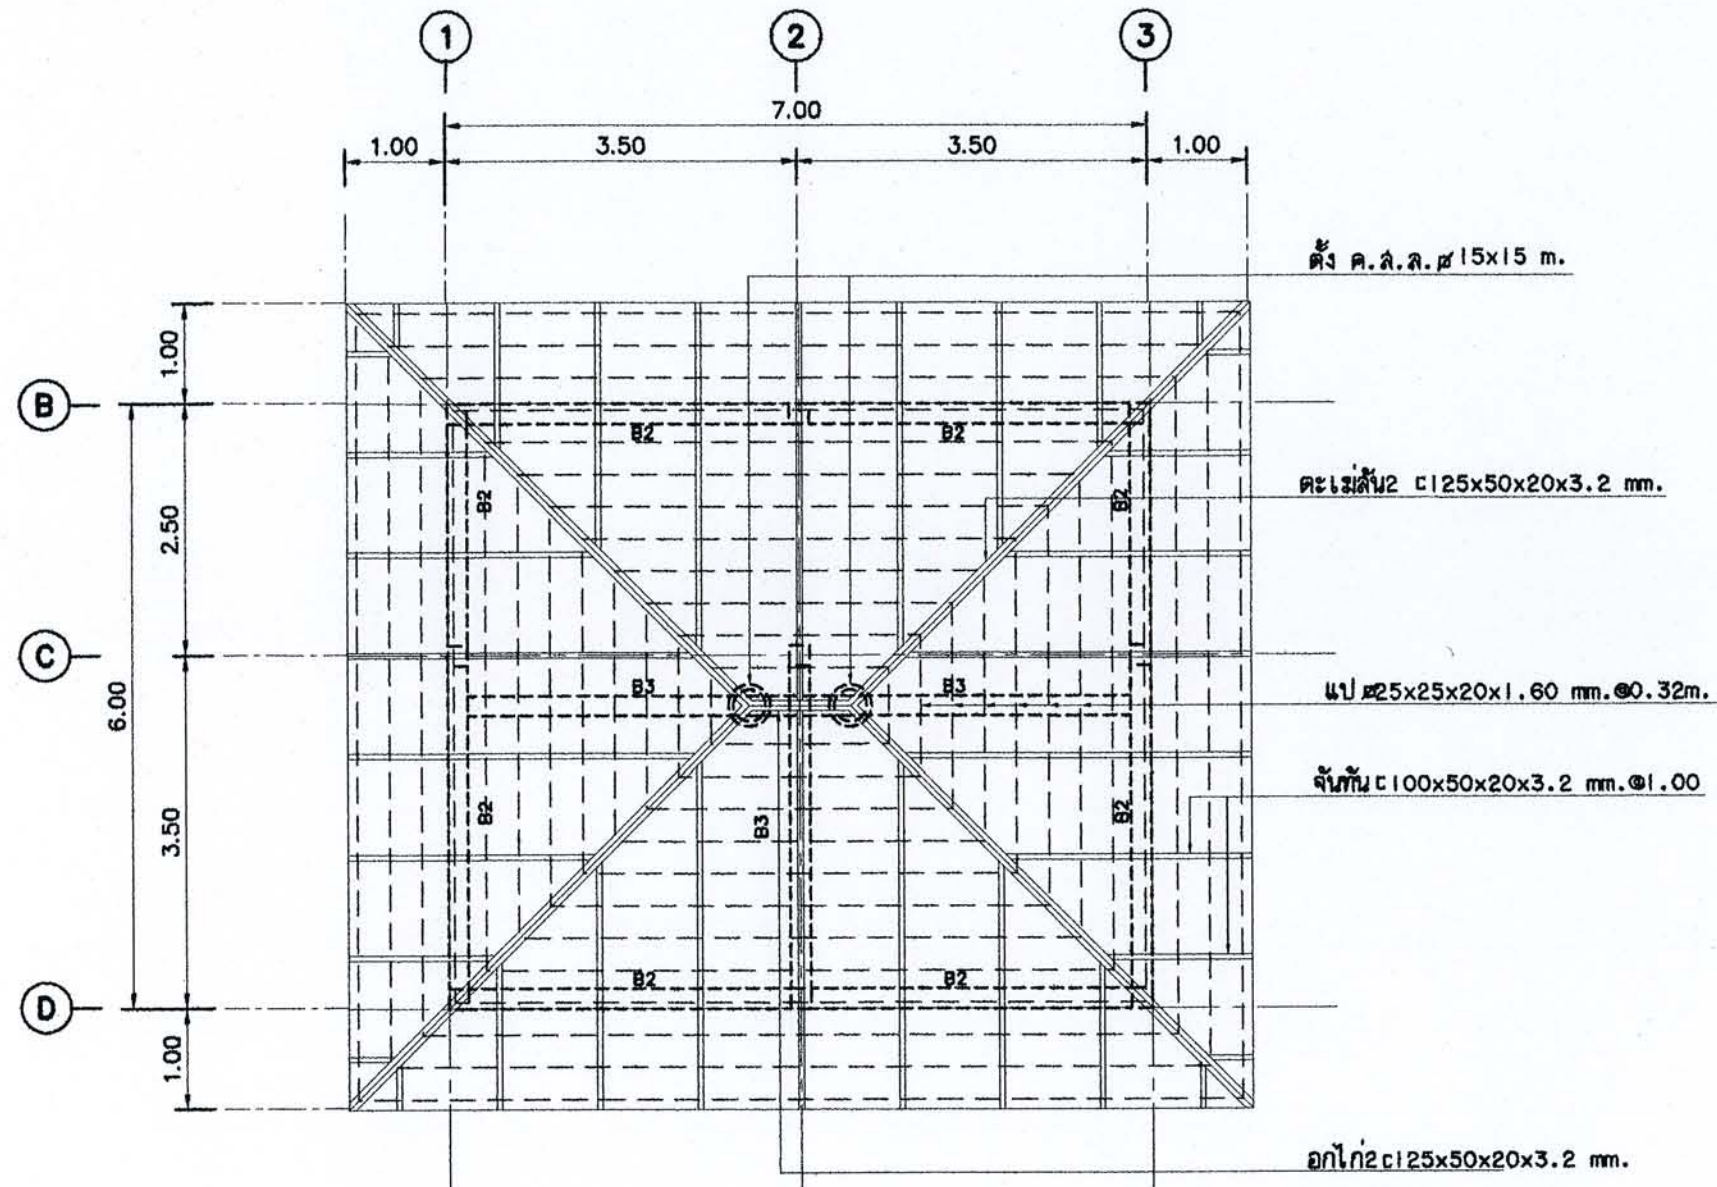

แปลน โครงหลังคา

มาตราส่วน 1 : 75



สำนักงานโยธา
กรุงเทพมหานคร

โครงการ
แบบบ้านยืมเพื่อประชาชน

ตามนโยบาย

ม.ร.ว.สุขุมพันธุ์ บริพัตร ผู้ว่าฯ กทม.
นายชัชชาติ สิทธิพันธุ์ รองผู้ว่าฯ กทม.
นายธีระชน นิมมิทธิ์ รองผู้ว่าฯ กทม.
นายพงศ์ศักดิ์ เตมียาภรณ์ ปลัดฯ กทม.

ผู้อำนวยการสำนักงานโยธา

นายจุมพล ศักดิ์ชาติ

รองผู้อำนวยการสำนักงานโยธา

นายวิศักดิ์ เกษประพันธ์

ผู้อำนวยการสำนักงานออกแบบ

นายจรูญ สันติเยม

หัวหน้างานสถาปัตยกรรม

นายสันติชัย บุญปักษ์

หัวหน้างานวิศวกรรม

นายธีระยุทธ คงสวัสดิ์เกียรติ

สถาปนิก

นายปวิศ ธิมาภ

วิศวกรโครงสร้าง

วิศวกรไฟฟ้า

วิศวกรสุขาภิบาล

นางสาวมณิศา สมพยอม

วิศวกรเครื่องกล

นายช่างเขียนแบบ

ว่าที่ร้อยตรีวิชา ประกิจ

แบบ
บ้านทองหลาง

เจ้าของ

สถานที่

แบบแสดง

แบบขยายพื้น, คาน

มาตราส่วน 1:20

FILE :

วันที่

วันที่ 2553


ชุดแบบ

ว่าที่ร้อยตรีวิชา ประกิจ


รวมแผ่น

23


รายการแก้ไขแบบ

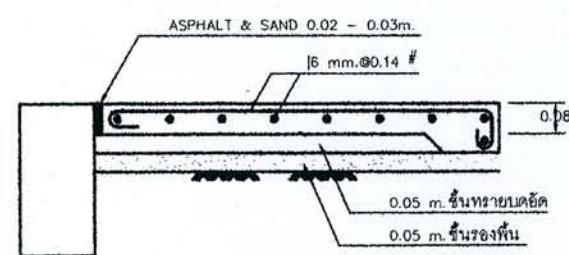


S0

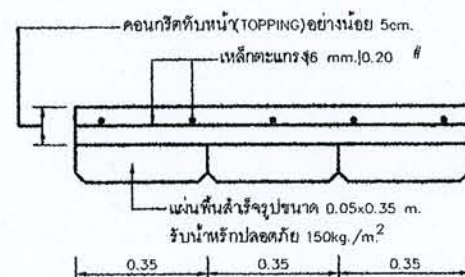


SP

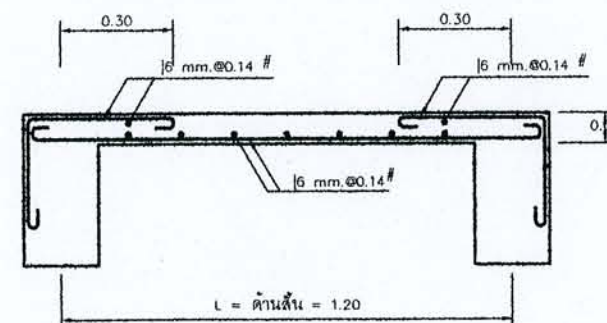


S1

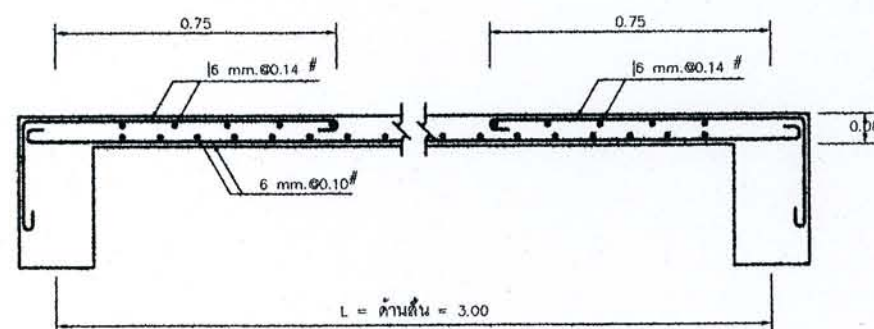


S2

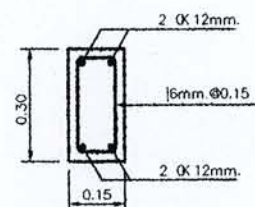


B1

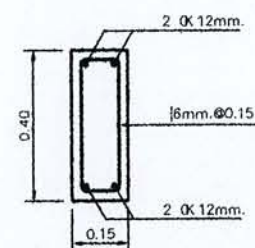


B2

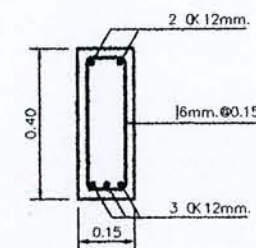


B3

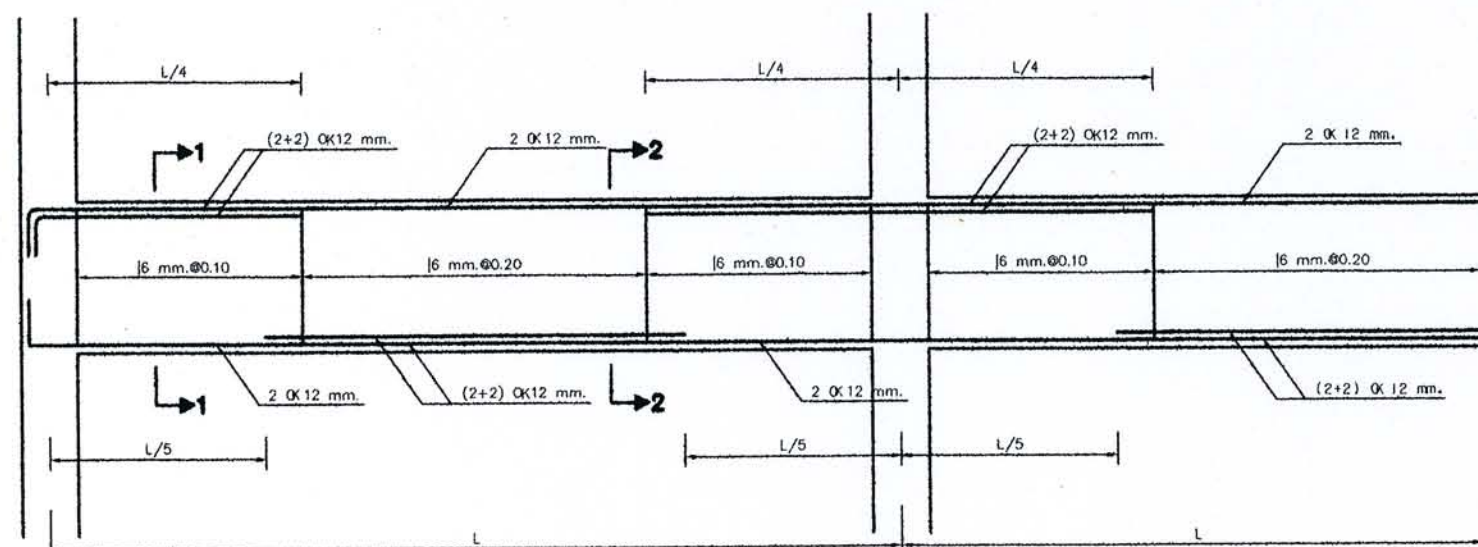

B4

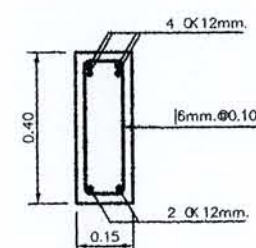

SECTION 1

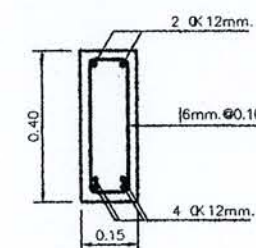

SECTION 2

แบบขยายพื้น, คาน
มาตราส่วน 1:20



สำนักงานโยธา
กรุงเทพมหานคร

โครงการ
แบบบ้านยืมเพื่อประชาชน

ตามนโยบาย

ม.ร.ว.สุขุมพันธุ์ บริพัตร ผู้ว่าฯกทม.
นายเทพไท เสนพงศ์ รองผู้ว่าฯกทม.
นายธีระชน มโนทิมบุตร รองผู้ว่าฯกทม.
นายพงศ์ศักดิ์ เสน่ห์นาค ปลัดฯกทม.

ผู้อำนวยการสำนักงานโยธา
นายจุฑามาศ สำนวณ
รองผู้อำนวยการสำนักงานโยธา
นายทวีศักดิ์ เติบประพันธ์
ผู้อำนวยการสำนักงานออกแบบ
นายจตุรงค์ สมนิยม
ผู้อำนวยการงานสถาปัตยกรรม
นายสินธุ์ชัย บุญปักษ์
ผู้อำนวยการงานวิศวกรรม
นายธีระยุทธ คงสวัสดิ์เกียรติ

สถาปนิก
นายปวิติ นิมาภ

วิศวกรโครงสร้าง

วิศวกรไฟฟ้า

วิศวกรสุขาภิบาล

นางสาวมณฑิรา สมหอม

วิศวกรเครื่องกล

นายช่างเขียนแบบ
ว่าที่ร้อยตรีปวีณา ประกิจ

แบบ บ้านทองแดง

คำขอ

สถานที่

แบบแสดง

แบบขยายคาน, เสา

และ

ขนาดส่วน 1:20



FILE :

วันที่ 1 มิถุนายน 2553 S-05


โดย วิศวกรเขียนแบบ

ว่าที่ร้อยตรีปวีณา ประกิจ


รายการแก้ไขแบบ

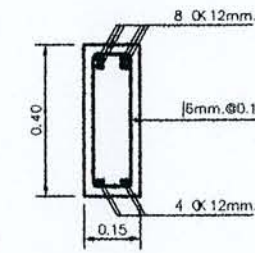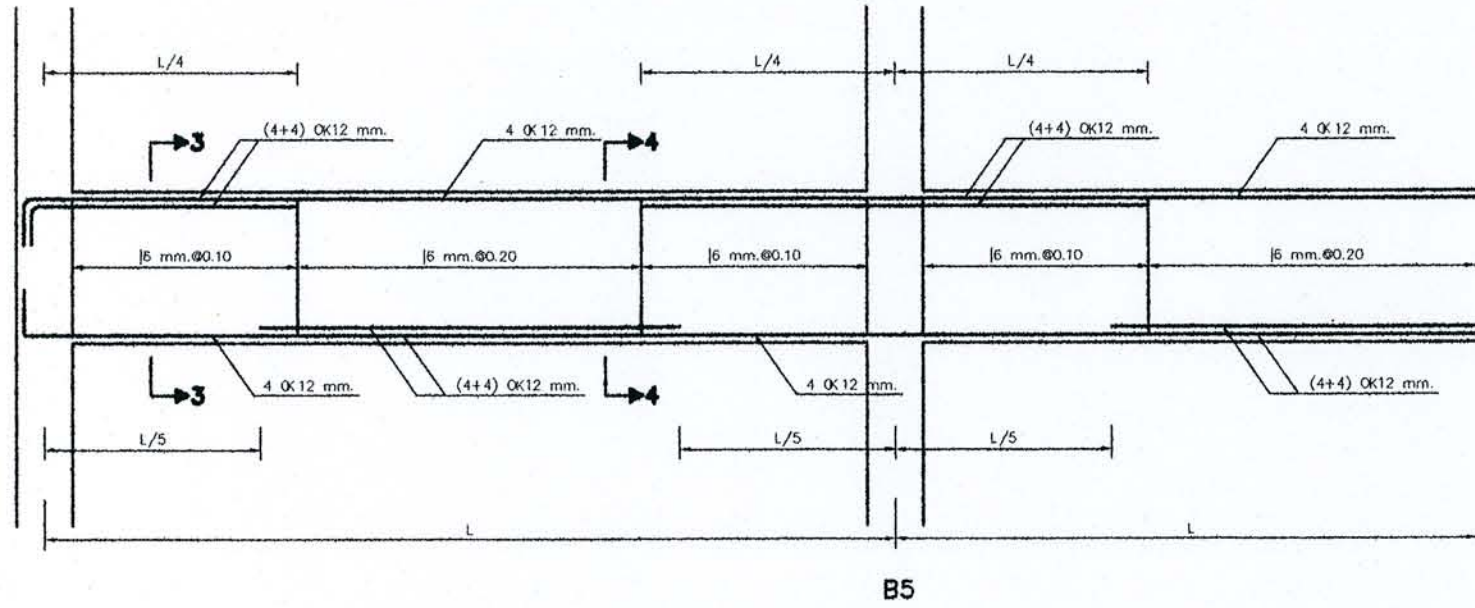


SECTION 3

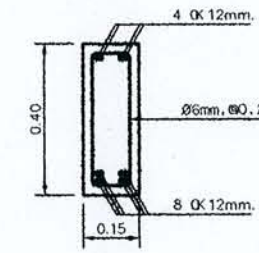


SECTION 4

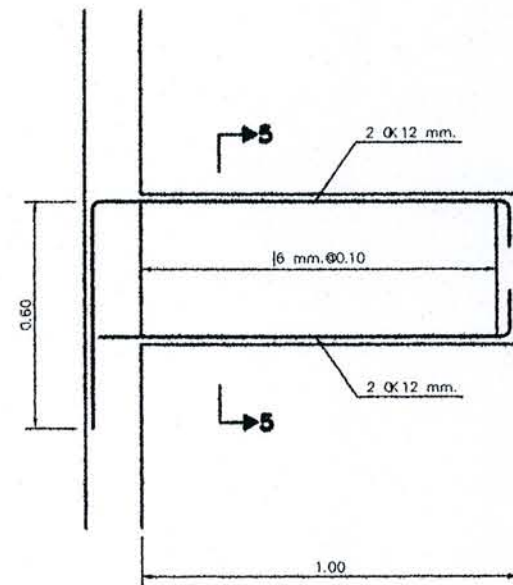


BC1

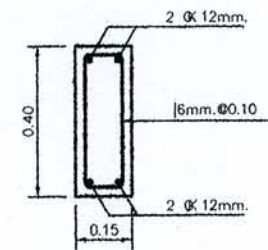

SECTION 5

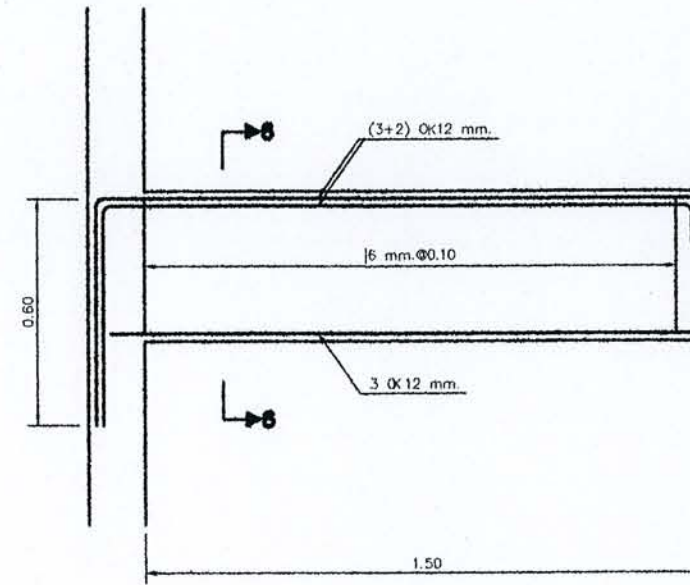


BC2

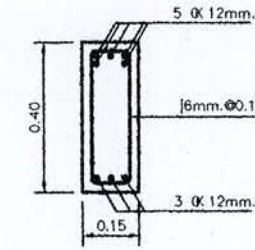


SECTION 6


เสาชั้น 2

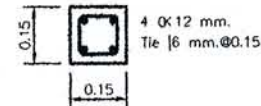

เสาชั้น 1

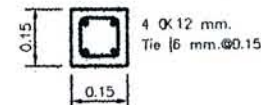

เสาตอม่อ

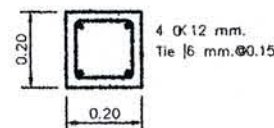

C1

แบบขยาย คาน, เสา
มาตรฐาน 1:20



สำนักงานโยธา
กรุงเทพมหานคร

โครงการ
แบบบ้านยืมเพื่อประชาชน

ตามนโยบาย

ม.ร.ว.สุขุมพันธุ์ บริพัตร ผู้ว่าฯกทม.
นายพรเทพ เตชะไพบูลย์ รองผู้ว่าฯกทม.
นายธีระชน มโนวิจิตรกุล รองผู้ว่าฯกทม.
นายพงศ์ศักดิ์ เศรษฐิน ปัสดาภรณ์

ผู้อำนวยการสำนักงานโยธา

นายจุมพล สันกาลาด

รองผู้อำนวยการสำนักงานโยธา

นายทวีศักดิ์ เลิศประพันธ์

ผู้อำนวยการสำนักงานออกแบบ

นายจตุรงค์ สันติธรรม

หัวหน้ากลุ่มงานสถาปัตยกรรม

นายสินธุ์ชัย บุญปักษ์

หัวหน้ากลุ่มงานวิศวกรรม

นายธีระยุทธ คงสวัสดิ์เกียรติ

สถาปนิก

นายปรีดิท ธีรภัก

วิศวกรโครงสร้าง

วิศวกรไฟฟ้า

วิศวกรสุขาภิบาล

นางสาวณิชา วัฒนสุข

วิศวกรเครื่องกล

นายช่างเขียนแบบ

ว่าที่ร้อยตรีปริษา ประกิจ

แบบ บ้านทองหลาง

เจ้าของ

สถานที่

แบบแสดง

แบบขยายฐานราก

มาตราส่วน 1:20

FILE :

วันที่

วันที่ 2553


ชนิดของบ้าน

ว่าที่ร้อยตรีปริษา ประกิจ


รวมหน้า

23

รายการแก้ไขแบบ

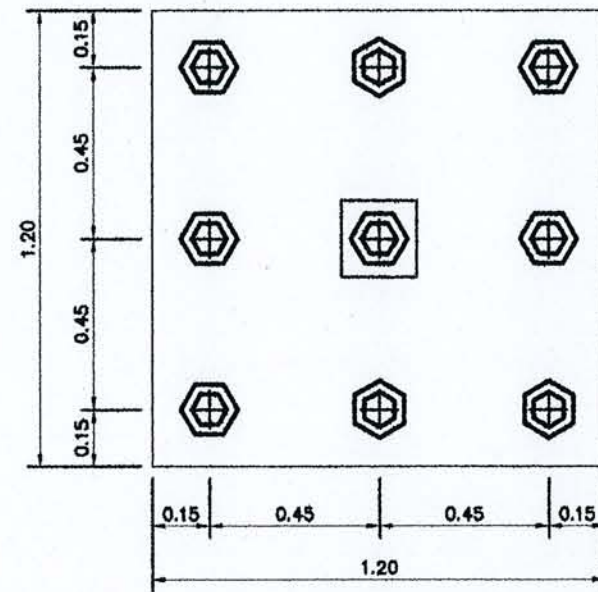

PLAN

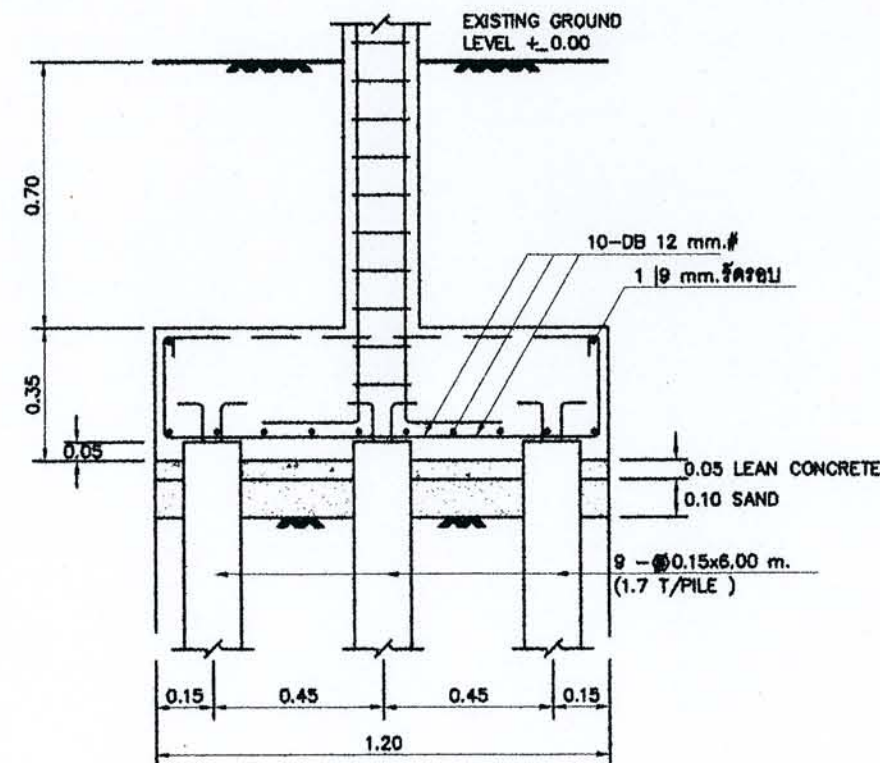

FOOTING " F1 "

SCALE

1 : 20