




ตามนโยบายของ
หม่อมราชวงศ์สุขุมพันธุ์ บริพัตร
ผู้ว่าราชการกรุงเทพมหานคร
โดย สำนักการโยธา

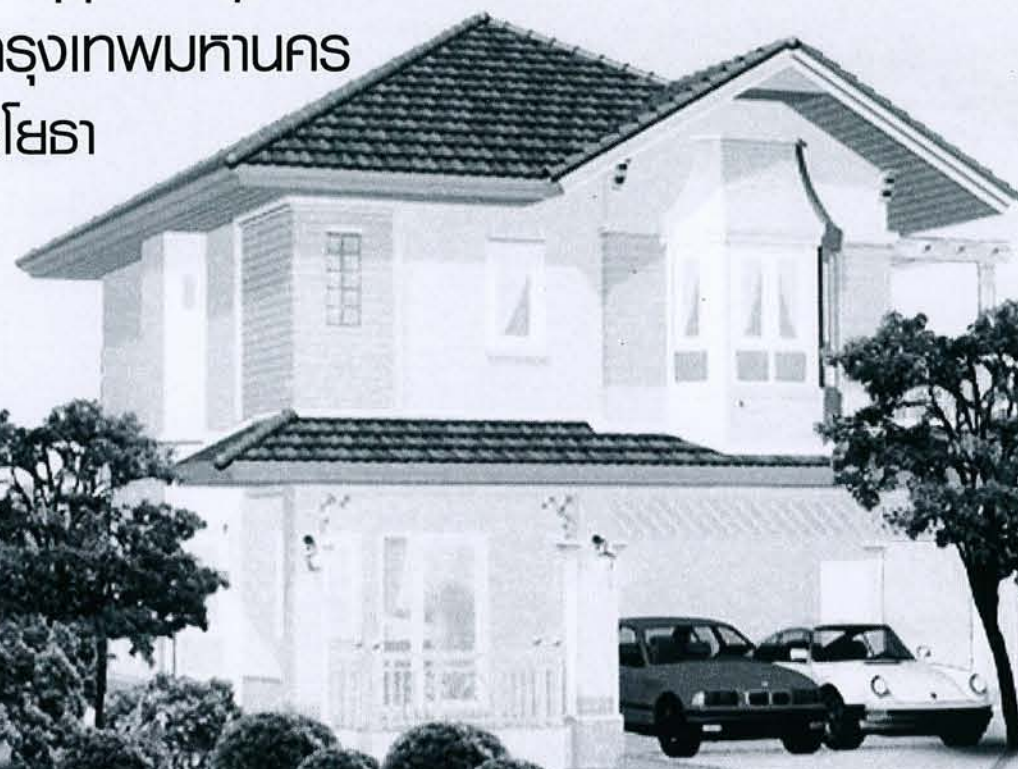

แบบบ้านยืม... เพื่อประชาชน

100 แบบบ้านมาตรฐาน...
สวย ดี โดนใจ...
พร้อมปลูกสร้างได้ทันที

ห้ามพลาด!!! โอกาส...
ยืมรับ... บ้านใหม่
แบบ **บ้านสวย**
เลือกได้
ใน “โครงการแบบบ้านยืม...เพื่อประชาชน”

แบบ 100 แบบบ้าน
มาตรฐาน...
สวย ดี โดนใจ
พร้อมปลูก
สร้างได้ทันที
มีให้เลือก
หลากหลาย
ตอบสนอง
ทุกไลฟ์สไตล์คนเมือง

ธรรมรักษา 
สำนักการโยธา กรุงเทพมหานคร

สัญลักษณ์แบบสถาปัตยกรรม	
สัญลักษณ์	รายการ
	แสดงทิศทางทางด้าน
	ดูรายละเอียด แผนที่ A-00
	แสดงแนวเสาแนวตามตั้ง A B
	แสดงแนวเสาแนวตามนอน 1
	แสดงแนวรูปตัด A B
	ดูรายละเอียด แผนที่ -
	แสดงระดับในรูปตัด
	แสดงระดับพื้นในรูปตัด
	แสดงข้อความ ลูกศรชี้ส่วนที่แสดงความหมาย
	แสดงแนวพิกัดเสา
	แสดงแนวเขตที่ดิน
	เส้นประ แสดงส่วนที่ถูกบัง หรือส่วนที่มองไม่เห็น
	ระยะจาก ศูนย์กลาง ถึง ศูนย์กลาง
	ระยะจาก ศูนย์กลาง ถึง ริม
	ระยะจาก ริม ถึง ริม
	แสดงแนวที่ถูกตัดขาด
	ช่องเปิดโล่ง
	ระดับดินเดิม
	คอนกรีตหยาบ, คอนกรีตเสริมเหล็ก
	ทราย
	ผนังก่ออิฐฉาบปูน ครึ่งแผ่น (แปลน)
	ผนังก่ออิฐฉาบปูน เต็มแผ่น (แปลน)
	ผนังก่ออิฐฉาบปูน ครึ่งแผ่น, เต็มแผ่น (รูปตัด)
	G, M, FIX
	กระจก. G= } M= } FIX=
	สัญลักษณ์ พื้น
	สัญลักษณ์ ผนัง
	สัญลักษณ์ ประตู
	สัญลักษณ์ หน้าต่าง
	สัญลักษณ์ ฝ้าเพดาน
	หิน
	ไม้โรยผิวไม้
	ไม้ไม่โรยผิวไม้

สัญลักษณ์แบบไฟฟ้า	
สัญลักษณ์	รายการ
	สวิตช์ทางเดียว รุ่น...ยี่ห้อ...
	สวิตช์ 2 ทาง รุ่น...ยี่ห้อ...
	ปลั๊กไฟ รุ่น...ยี่ห้อ...
	โทรศัพท์
	โทรทัศน์
	ไฟDOWNLIGHT
	ไฟกิ่ง
	หลอดไฟฟลูออเรสเซนต์
	หลอดไฟฟลูออเรสเซนต์แบบมีโคมครอบ
	BREAKER
	สายไฟ

สัญลักษณ์แบบสุขาภิบาล	
สัญลักษณ์	รายการ
	FLOOR DRAIN
	ท่อระบายน้ำฝน
	ท่อประปา
	ท่อโสโครก
	ท่อน้ำทิ้งซีเมนต์ใยหิน ขนาด 0.30 ม.
	ถังบำบัดน้ำเสีย AP 1600
	บ่อบำบัดน้ำทิ้ง

สัญลักษณ์ประกอบแบบ



สำนักการโยธา
กรุงเทพมหานคร

โครงการ
แบบบ้านยืมเพื่อประชาชน

ตามนโยบาย

ม.ร.ว.สุขุมพันธุ์ บริพัตร ผู้ว่าฯกทม.
นายพรเทพ เศรษฐกิจ รองผู้ว่าฯกทม.
นายธีระชน มโนวิจิตร รองผู้ว่าฯกทม.
นายพงศ์ศักดิ์ เศรษฐกิจ ปลัดฯกทม.

ผู้อำนวยการสำนักการโยธา

นายจุมพล สันกาลาด

รองผู้อำนวยการสำนักการโยธา

นายทวีศักดิ์ เลิศประพันธ์

ผู้อำนวยการสำนักงานออกแบบ

นายจตุรงค์ สมนิยม

หัวหน้างานสถาปัตยกรรม

นายสินธุ์ชัย บุญปักษ์

หัวหน้างานวิศวกรรม

นายธีระยุทธ คงสวัสดิ์เกียรติ

สถาปนิก

นายสินธุ์ชัย บุญปักษ์

วิศวกรโครงสร้าง

วิศวกรไฟฟ้า

วิศวกรสุขาภิบาล

นางสาวมณฑิรา สมหอม

วิศวกรเครื่องกล

นายช่างเขียนแบบ

นายประยูร อรรถจักร์

แบบ

(024) ธรรมรักษา

เจ้าของ

สถานที่

แบบแสดง

รายการประกอบแบบ

มาตราส่วน 1:75

FILE :

วันที่ 2553

คัดลอกแบบ

นายประยูร อรรถจักร์

แผ่นที่

A-01

รวมแผ่น

16

รายการแก้ไขแบบ

ตารางรายการวัสดุ

สัญลักษณ์	ความหมาย
รายการวัสดุพื้น	
F-1	พื้น ค.ส.ล. ผิวหน้าคอนกรีตขัดหยาบ
F-2	พื้น ค.ส.ล. ผิวหน้าถูกระเบียงเซรามิค ชนิดกันลื่นขนาด 0.40x0.40 ม
F-3	พื้น ค.ส.ล. ผิวหน้าถูกระเบียงเซรามิค ชนิดกันลื่นขนาด 0.60x0.60 ม
F-4	พื้น ค.ส.ล. ผสมน้ำยากันซึม ผิวหน้าถูกระเบียงเซรามิค ชนิดกันลื่นขนาด 0.40x0.40 ม
F-5	พื้น ค.ส.ล. ผสมน้ำยากันซึม ผิวหน้าถูกระเบียงเซรามิค ชนิดกันลื่นขนาด 0.30x0.30 ม
F-6	พื้น ค.ส.ล. ผิวหน้าถูไม้อปาเก้ ทาสีอะครีลิคและลงแว็ก
F-7	พื้น ค.ส.ล. ผสมน้ำยากันซึม ผิวหน้าถูกระเบียงเซรามิค ชนิดกันลื่นขนาด 0.30x0.30 ม
รายการวัสดุผนัง	
1	ผนังก่ออิฐฉาบ หรือส่วน ค.ส.ล. ทำผิวฉาบเรียบ ทาสีน้ำสำหรับทาภายนอก
2	ผนังระแนงเหล็กทาสี
3	ผนังก่ออิฐฉาบ หรือส่วน ค.ส.ล. ทำผิวฉาบเรียบ เชาะร่องตามแบบ ทาสีน้ำสำหรับทาภายนอก
4	ผนังก่ออิฐฉาบเรียบเต็มแผ่น กรุกระเบื้องเซรามิค ขนาด 0.20x0.20 ม
5	ผนังก่ออิฐฉาบ หรือส่วน ค.ส.ล. ทำผิวฉาบเรียบ ทาสีน้ำอะครีลิค 100% สำหรับทากายใน
6	ผนังก่ออิฐฉาบ หรือส่วน ค.ส.ล. กรุกระเบื้องเซรามิค ขนาด 0.20x0.20 ม
7	ผนังก่ออิฐฉาบเต็มแผ่น ทำผิวฉาบเรียบ ทาสีน้ำสำหรับทาภายนอก
8	ผนังก่ออิฐฉาบเต็มแผ่น ทำผิวฉาบเรียบ ทาสีน้ำอะครีลิค 100% สำหรับทากายใน
รายการวัสดุฝ้าเพดาน	
C-1	ฝ้าเพดาน GYP BOAREL 9 มม. ธรรมดา ฉาบรอยต่อเรียบ โครงโครงเหล็กชุบสังกะสี ระยะโครง 120 x 240 ซม. ทาสีน้ำอะครีลิค 100 %
C-2	ฝ้าเพดาน GYP BOAREL 9 มม. ทนชื้น ฉาบรอยต่อเรียบ โครงโครงเหล็กชุบสังกะสี ระยะโครง 40 x 120 ซม. ทาสีน้ำอะครีลิค 100 %
C-3	ฝ้าเพดานท้องพื้นโครงสกรู ค.ส.ล. ทาสีน้ำอะครีลิค 100 % สีขาว

หมายเหตุ

- งานเหล็กทั่วไปให้ทาสีกันสนิม 2 ครั้ง แล้วทาสีด้วยสีน้ำมันอีก 2 ครั้ง



สำนักงานนโยบาย
กรุงเทพมหานคร

โครงการ
แบบบ้านยืมเพื่อประชาชน

ตามนโยบาย

น.ร.สุมนพันธ์ ภิพิศ ผู้อำนวยการ
นายพรเทพ เศรษฐบุตร รองผู้อำนวยการ
นายธีระชน มโนธิตกุล รองผู้อำนวยการ
นายพงศ์ศักดิ์ เสงี่ยมศักดิ์ ปลัดเขต

ผู้อำนวยการสำนักงาน

นายจุฑามาศ สำนาค

รองผู้อำนวยการสำนักงาน

นายทวีศักดิ์ เลิศประพันธ์

ผู้อำนวยการสำนักงานเขต

นายจตุรงค์ สอนเนียม

หัวหน้างานสถาปัตยกรรม

นายสินธุ์ชัย บุญปักษ์

หัวหน้างานวิศวกรรม

นายธีระยุทธ คงสวัสดิ์เสถียร

สถาปนิก

นายสินธุ์ชัย บุญปักษ์

วิศวกรโครงสร้าง

วิศวกรไฟฟ้า

วิศวกรสุขาภิบาล

นางสาวมณฑิลา สมหอม

วิศวกรเครื่องกล

นายช่างเขียนแบบ

นายประจักษ์ อรรถจักร์

แบบ

(024) ธรรมรักษา

เจ้าของ

สถานที่

แบบแสดง

รายการวัสดุ

มาตราส่วน 1:75

FILE :

วันที่ 25 มิถุนายน 2553

ชนิดเอกสาร แบบร่าง

นายประจักษ์ อรรถจักร์

รวมแผ่น 16

รายการแก้ไขแบบ



สำนักงานนโยบาย
กรุงเทพมหานคร

โครงการ
แบบบ้านยืมเพื่อประชาชน

ตามนโยบาย

ม.ร.ว.สุรพันธ์ บริพัตร ผู้ว่าฯกทม.
นายแพทย์ พะทีปยศ รองผู้ว่าฯกทม.
นายธีระวัฒน์ นิ่มน้อม รองผู้ว่าฯกทม.
นายพงศ์ศักดิ์ สมเ็นต์ ปลัดฯกทม.

ผู้อำนวยการสำนักงานนโยบาย

นายจุมพล สำนาก

รองผู้อำนวยการสำนักงานนโยบาย

นายทวีศักดิ์ เลิศประพันธ์

ผู้อำนวยการสำนักงานออกแบบ

นายจตุรงค์ สนิเอม

หัวหน้างานสถาปัตยกรรม

นายสินธุ์ชัย บุญปักษ์

หัวหน้างานวิศวกรรม

นายธีระยุทธ คงสรค์เสถียร

สถาปนิก

นายสินธุ์ชัย บุญปักษ์

วิศวกรโครงสร้าง

วิศวกรไฟฟ้า

วิศวกรสุขาภิบาล

นางสาวณณจิรา สมหอม

วิศวกรเครื่องกล

นายช่างเขียนแบบ

นายประยูร อรรถจักร์

แบบ
(024) ธรรมรักษา

เจ้าของ

สถานที่

แบบแสดง
แปลนพื้นที่ชั้นล่าง

มาตราส่วน 1:75



FILE : 16

วันที่ 16 มิถุนายน 2553 A-04

โดย 16

นายประยูร อรรถจักร์

รายการแก้ไขแบบ

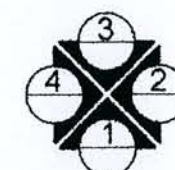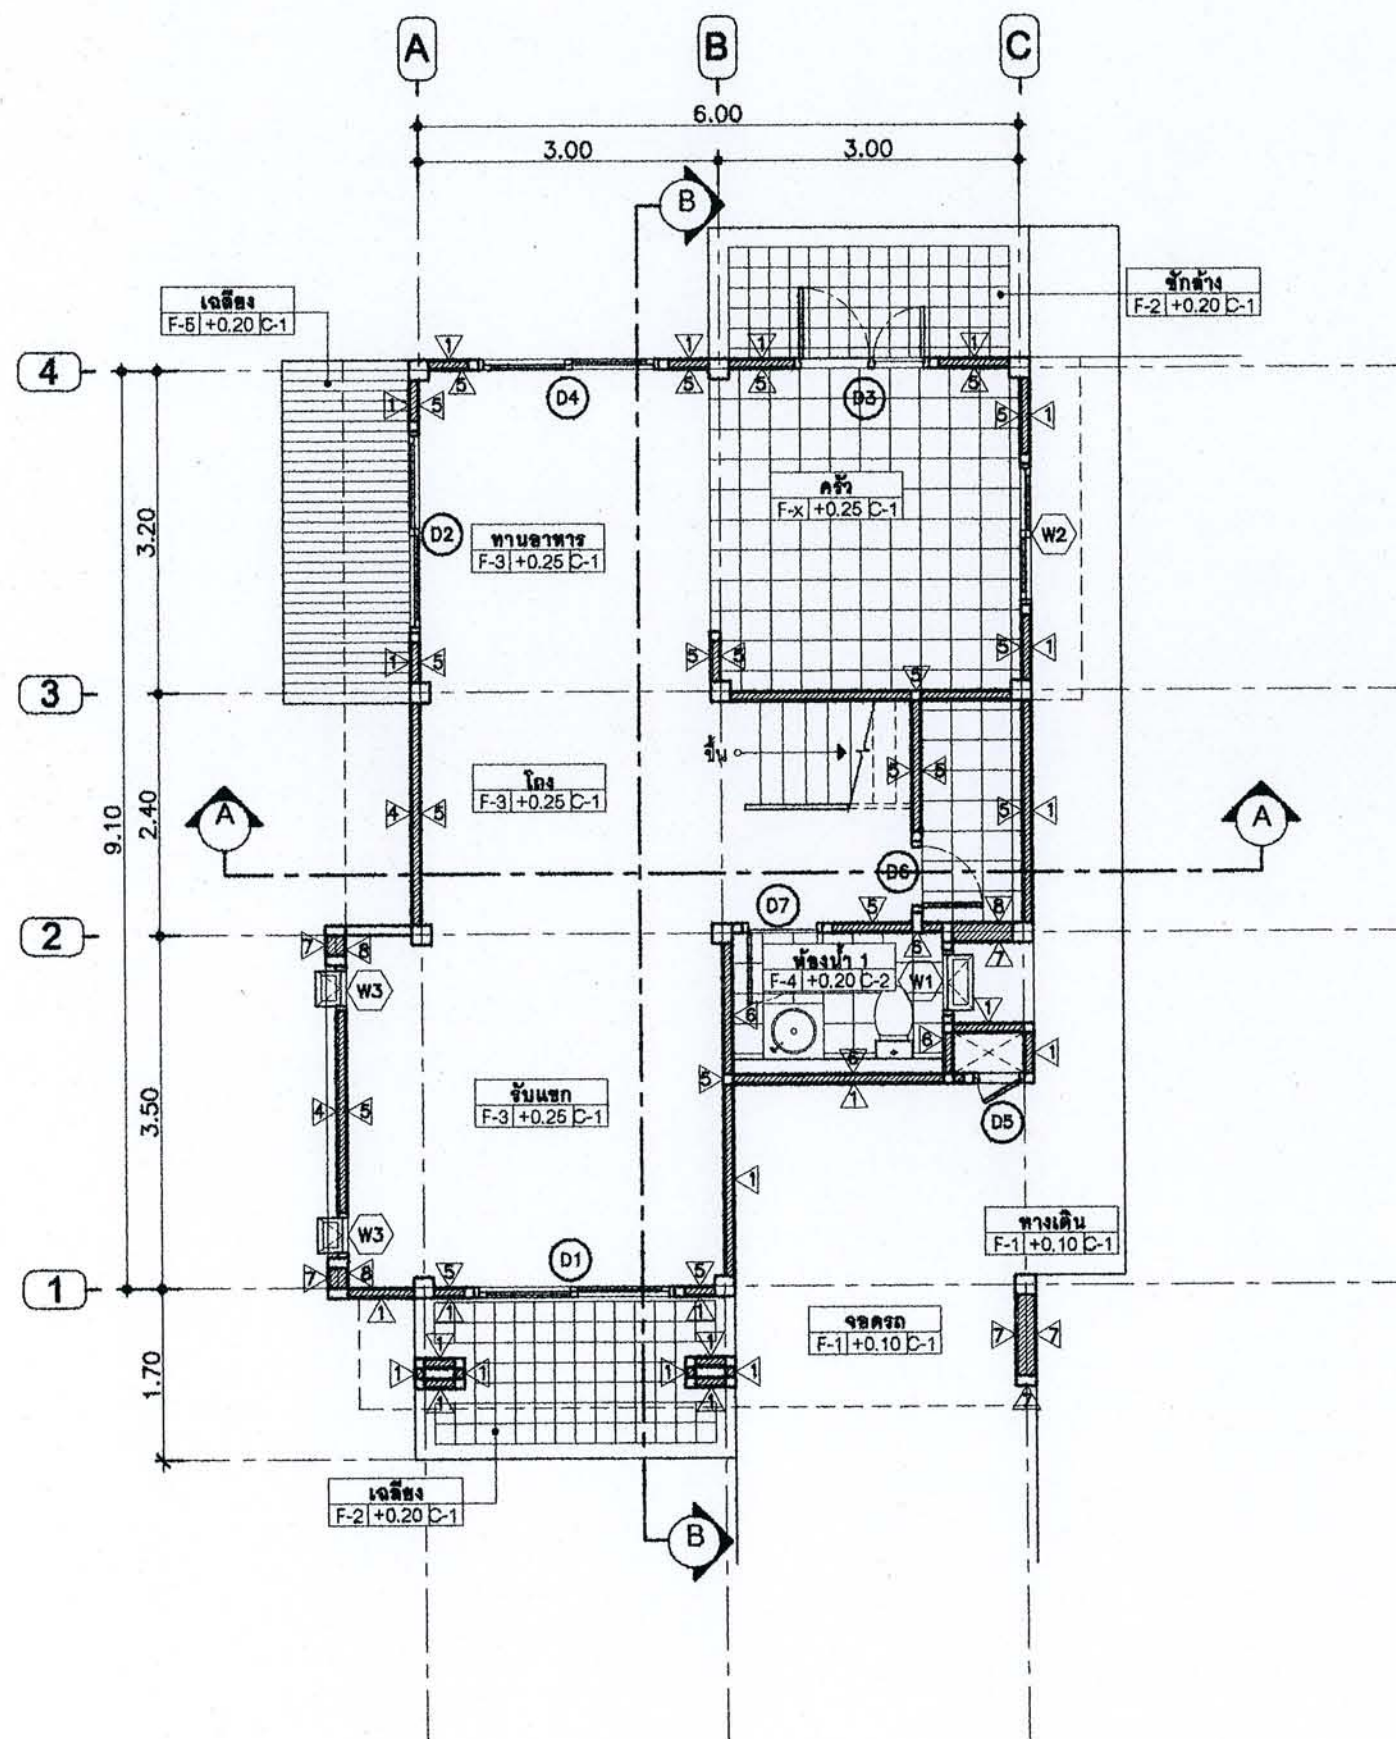

สัญลักษณ์ของรูปด้าน

ผังพื้นที่ชั้นล่าง

1:75



สำนักงานโยธา
กรุงเทพมหานคร

โครงการ
แบบบ้านยืมเพื่อประชาชน

ตามนโยบาย

ม.ร.ว.สุขุมพันธุ์ บริพัตร ผู้ว่าฯกทม.
นายพรเทพ เกษมทรัพย์ รองผู้ว่าฯกทม.
นายธีระชน มโนชัยปิยะ รองผู้ว่าฯกทม.
นายพงศ์ศักดิ์ เตเมธินาถ ปลัดฯกทม.



ผู้อำนวยการสำนักงานโยธา
นายจุฬพล สันภาพ
รองผู้อำนวยการสำนักงานโยธา
นายทวีศักดิ์ เดชประพันธ์
ผู้อำนวยการสำนักงานออกแบบ
นายจตุรงค์ สันเอี่ยม
หัวหน้ากลุ่มงานสถาปัตยกรรม
นายสินธุ์ชัย บุญปักษ์
หัวหน้ากลุ่มงานวิศวกรรม
นายธีระยุทธ คงสวรรค์

สถาปนิก
นายสินธุ์ชัย บุญปักษ์
วิศวกรโครงสร้าง
วิศวกรไฟฟ้า
วิศวกรสุขาภิบาล
นางสาวมณฑิรา สมน้อม
วิศวกรเครื่องกล
นายช่างเขียนแบบ
นายประยูร อรรณจักร

แบบ
(024) อรรณจักร
เจ้าของ
สถานที่

แบบแสดง
แปลนพื้นที่ขึ้นบน
มาตราส่วน 1:75
FILE :
วันที่ 1 มิถุนายน 2553
คัดลอกแบบ
นายประยูร อรรณจักร
แผ่นที่ A-05
รวมแผ่น 16


รายการแก้ไขแบบ

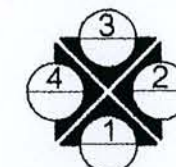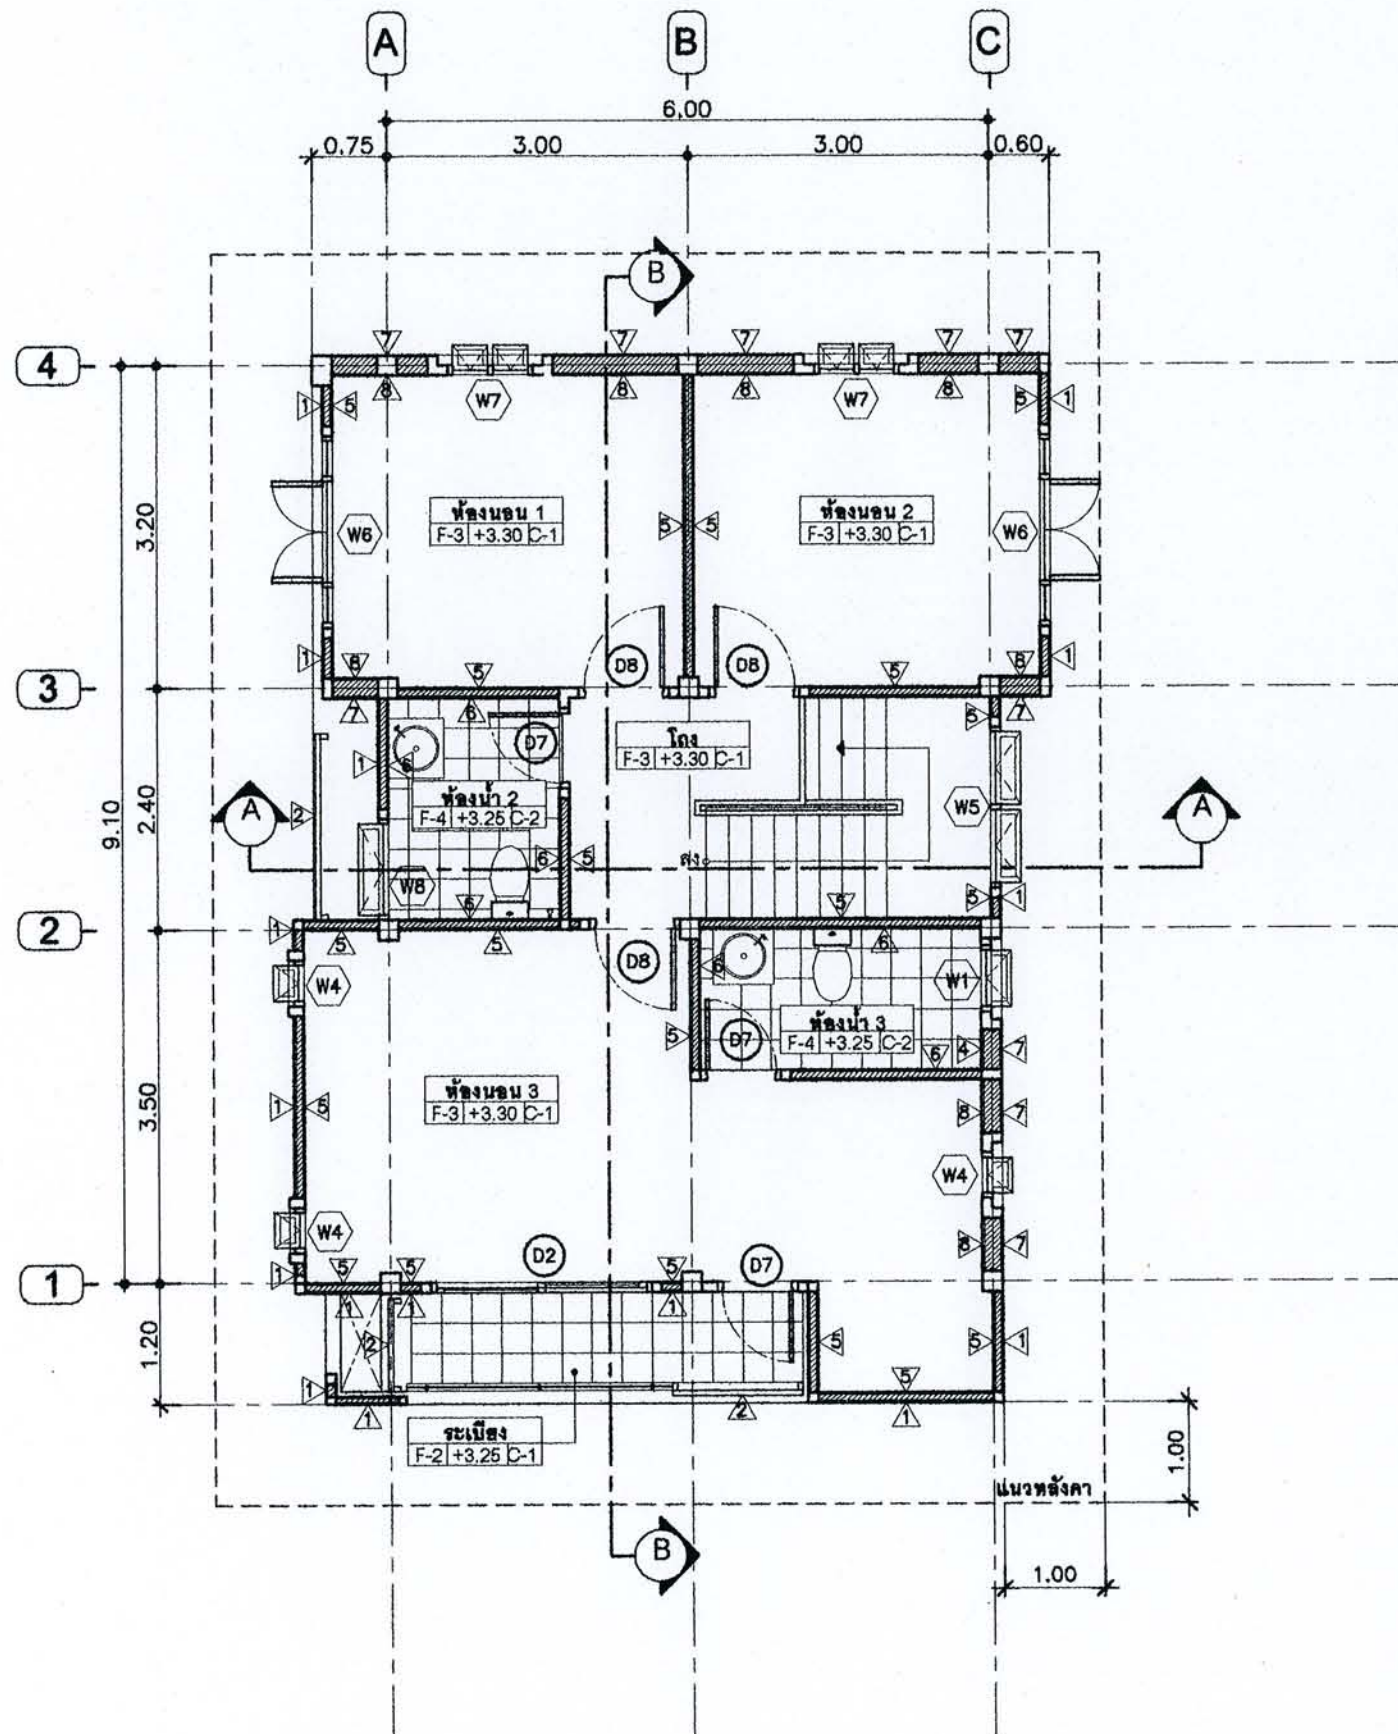

สัญลักษณ์ของรูปด้าน

ผังพื้นที่ขึ้นบน

มาตราส่วน 1:75

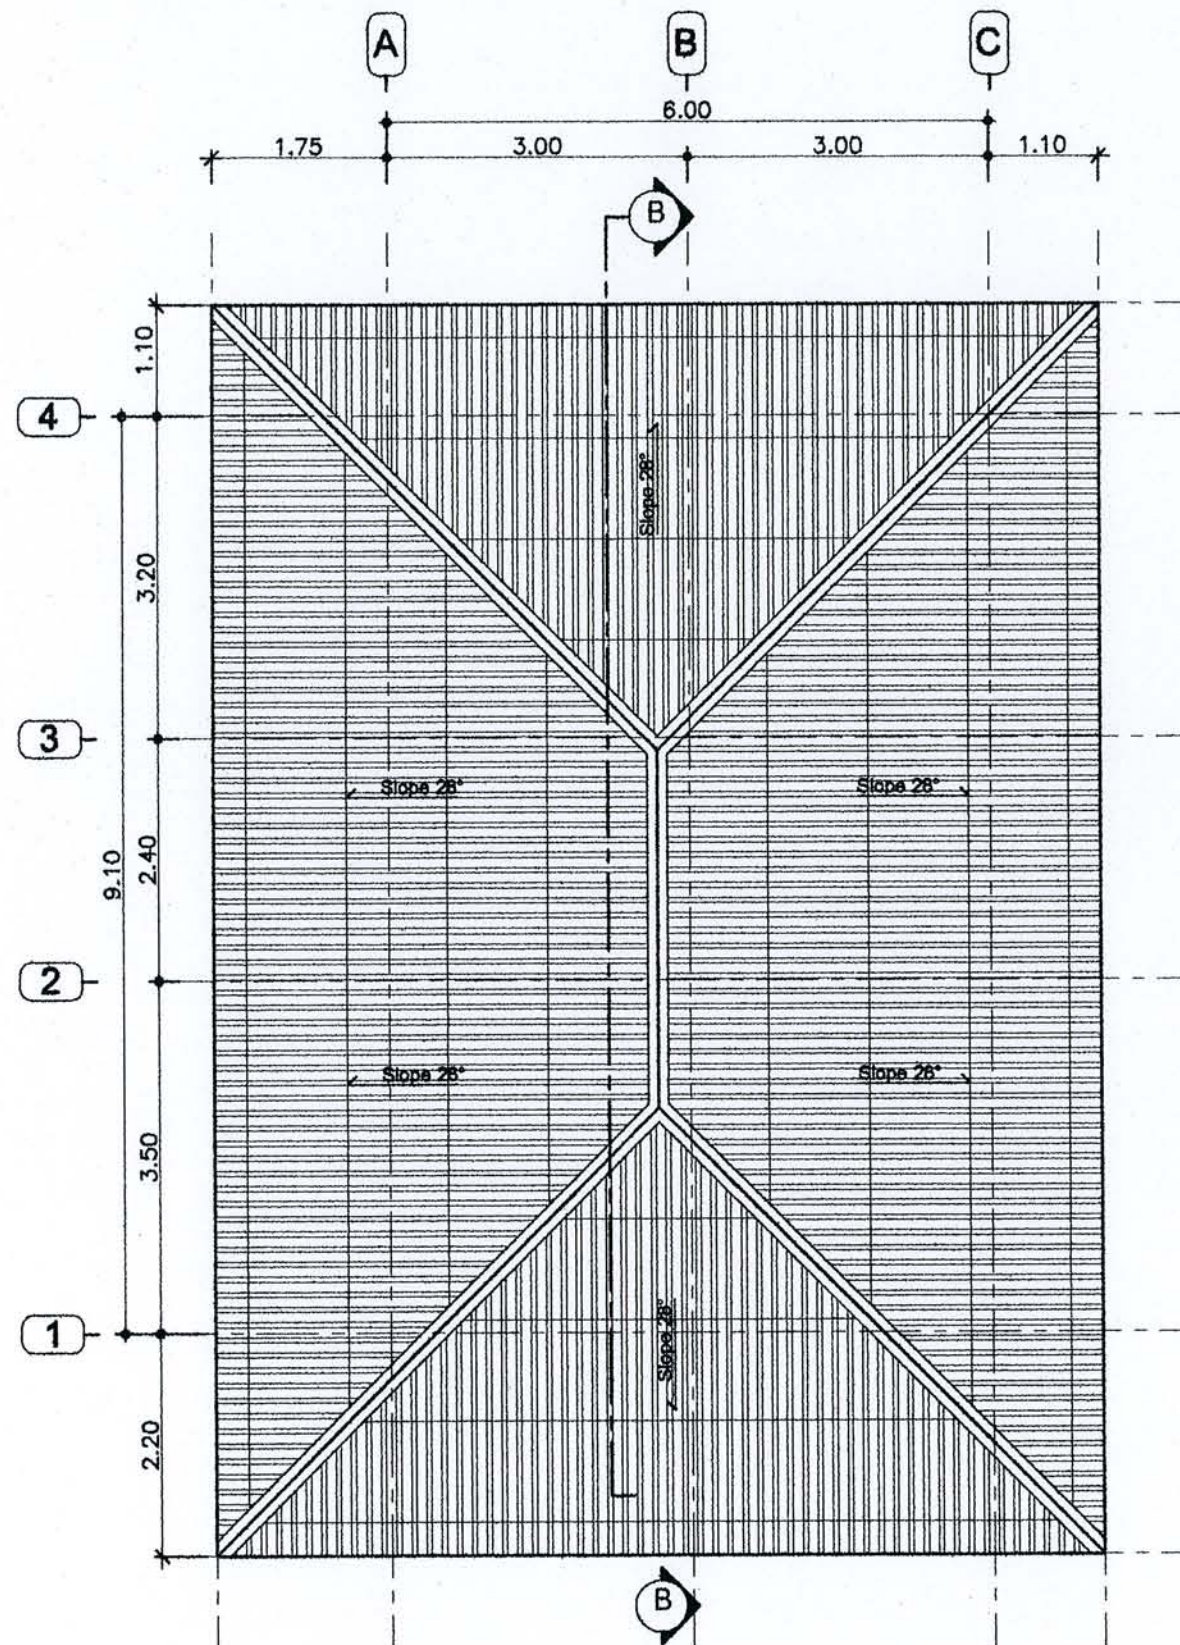

สำนักงานผังเมืองกรุงเทพมหานคร

ผังหลังคา

มาตราส่วน 1:75



สำนักงานผังเมืองกรุงเทพมหานคร

โครงการ
แบบบ้านยืมเพื่อประชาชน

คณบดี

นายสุเมธ ทรัพย์วิจิตร ผู้อำนวยการ
นายทศพร เกษมทรัพย์ รองผู้อำนวยการ
นายธีรวัฒน์ นิ่มนวล รองผู้อำนวยการ
นายพงษ์ศักดิ์ แสนจันทร์ ปลัด

ผู้อำนวยการสำนักงานผังเมือง
นายสุเมธ ทรัพย์วิจิตร
รองผู้อำนวยการสำนักงานผังเมือง
นายทศพร เกษมทรัพย์
ผู้อำนวยการสำนักงานเขต
นายสุเมธ ทรัพย์วิจิตร
ผู้อำนวยการสำนักงานเขต
นายสุเมธ ทรัพย์วิจิตร
ผู้อำนวยการสำนักงานเขต
นายสุเมธ ทรัพย์วิจิตร
ผู้อำนวยการสำนักงานเขต
นายสุเมธ ทรัพย์วิจิตร

สถาปนิก
นายสุเมธ ทรัพย์วิจิตร
วิศวกรโครงสร้าง

วิศวกรไฟฟ้า

วิศวกรสุขาภิบาล
นางสาวณัฏฐา สมทอง
วิศวกรเครื่องกล

นายช่างเขียนแบบ
นายประจักษ์ อรรถจักร์

แบบ
(024) ธรรมรักษา

เจ้าของ

สถานที่

แบบแสดง
แปลนหลังคา

ขนาดหน้า 1:75

FILE :
วันที่ 2553
คัดลอกแบบ
นายประจักษ์ อรรถจักร์

รายการแก้ไขแบบ



สำนักการโยธา
กรุงเทพมหานคร

โครงการ
แบบบ้านยืมเพื่อประชาชน

คานบนโยบาย

น.ร.สุรพันธ์ บริพัตร ผู้ว่าฯกทม.
นายแพทย์ เศรษฐกิจ ร่องฟ้าภรณ์
นายธีระชน มโนชัยกุล ร่องฟ้าภรณ์
นายพงศ์ศักดิ์ เสน่ห์ดี ปลัดฯกทม.

ผู้อำนวยการสำนักการโยธา

นายจุมพล สันภาพล

รองผู้อำนวยการสำนักการโยธา

นายทวีศักดิ์ เลิศประพันธ์

ผู้อำนวยการสำนักงานออกแบบ

นายจตุรงค์ สันติเยม

หัวหน้ากลุ่มงานสถาปัตยกรรม

นายสินธุ์ชัย บุญปักษ์

หัวหน้ากลุ่มงานวิศวกรรม

นายธีระยุทธ คงวรรคเดียง

สถาปนิก

นายสินธุ์ชัย บุญปักษ์

วิศวกรโครงสร้าง

วิศวกรไฟฟ้า

วิศวกรสุขาภิบาล

นางสาววรรณธิลา สมหอม

วิศวกรเครื่องกล

นายช่างเขียนแบบ

นายประยูร อรรณจักร

แบบ

(024) ธรรมรักษา

เจ้าของ

สถานที่

แบบแสดง

รูปด้าน ①

มาตราส่วน

1:75


FILE :

วันที่ 2553

คิดออก ปกป้องแบบ

นายประยูร อรรณจักร

รายการแก้ไขแบบ

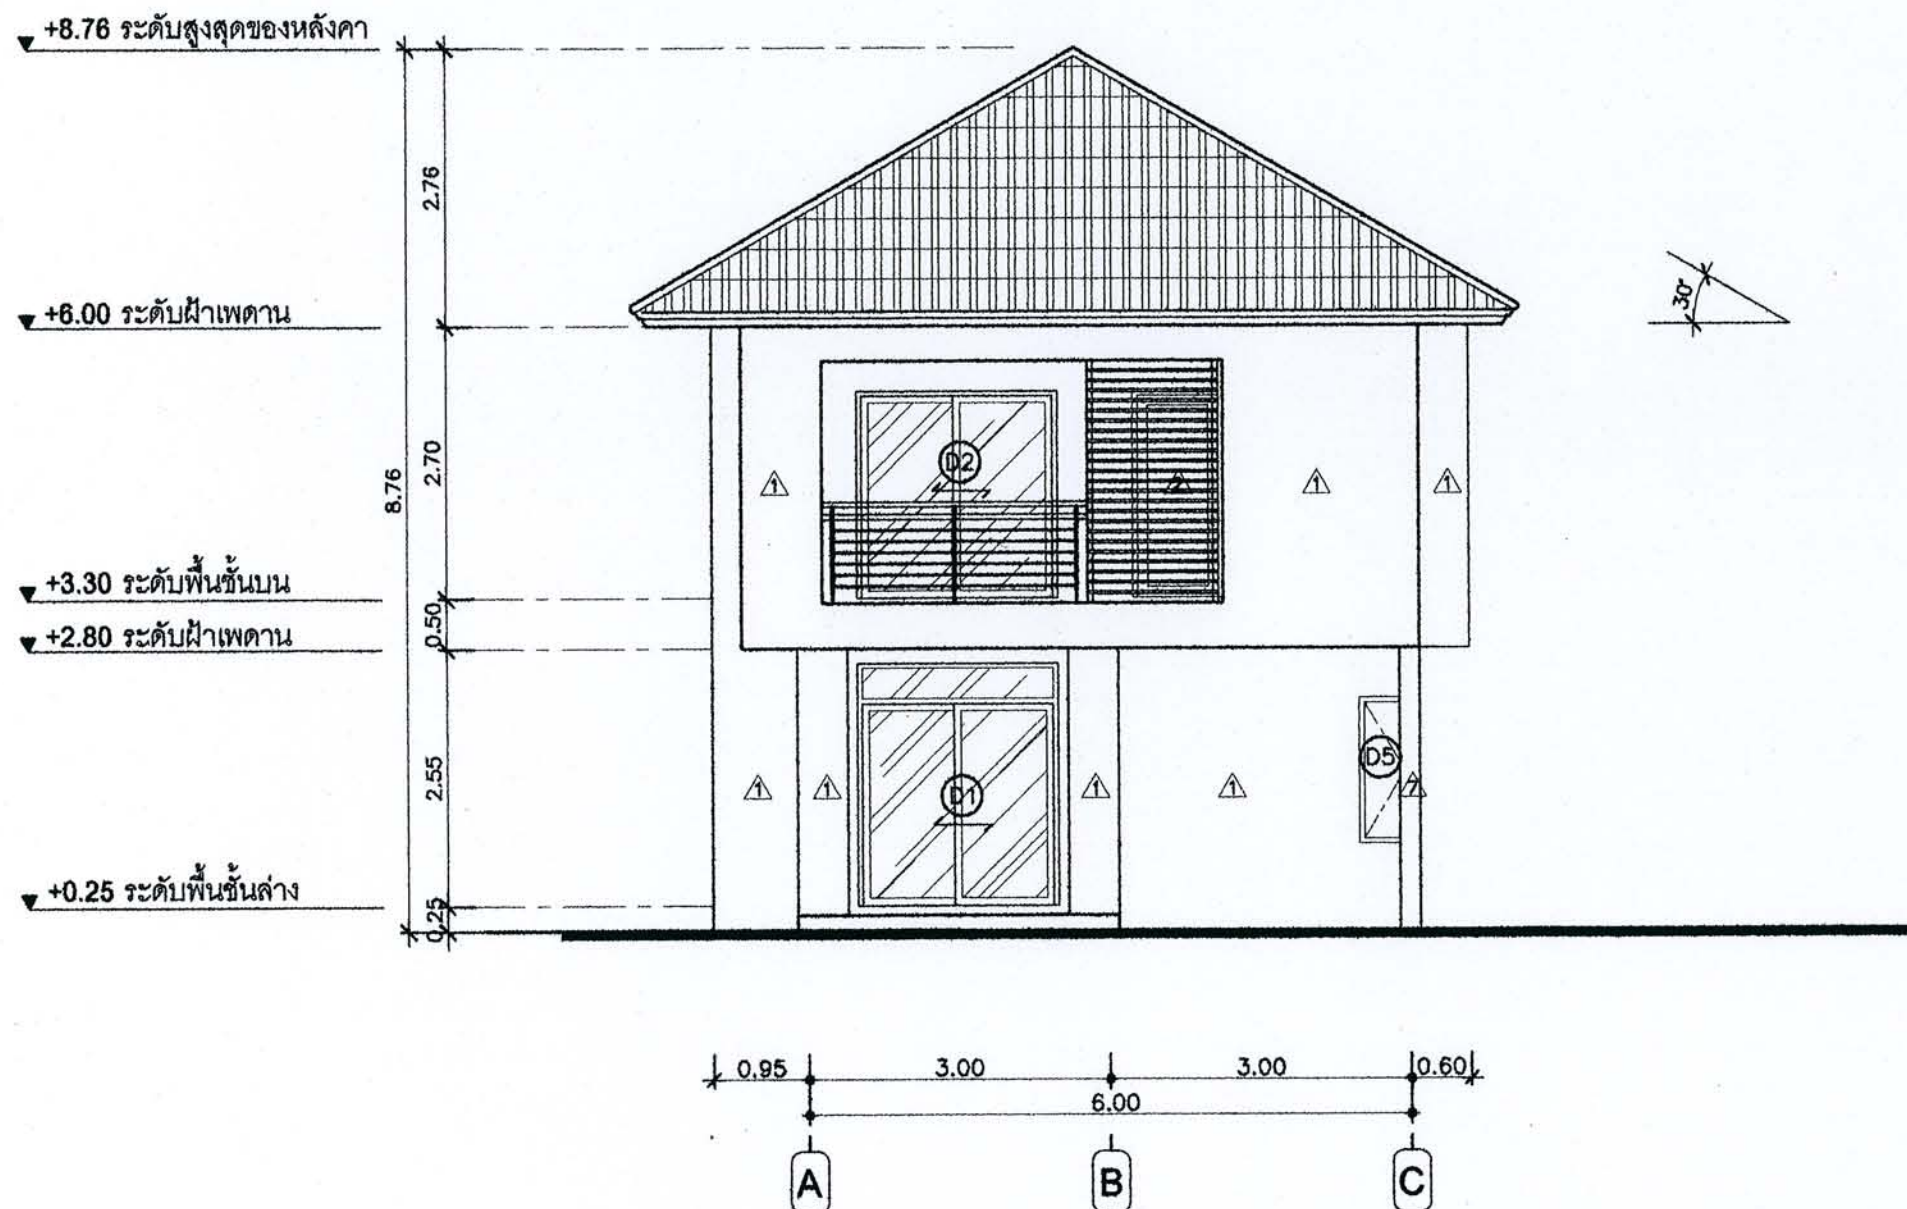

รูปด้าน 1

มาตราส่วน

1:75



สำนักงานโยธา
กรุงเทพมหานคร

โครงการ
แบบบ้านยืมเพื่อประชาชน

ตามนโยบาย

ม.ร.ว.สุขุมพันธุ์ บริพัตร ผู้ว่าฯกทม.
นายพรเทพ เศรษฐินชัย รองผู้ว่าฯกทม.
นายธีระชน มโนวิมลวิมลชัย รองผู้ว่าฯกทม.
นายพงษ์ศักดิ์ แสนลิ้นดี ปลัดฯกทม.

ผู้อำนวยการสำนักงานโยธา

นายจุมพล ลำภาพล

รองผู้อำนวยการสำนักงานโยธา

นายทวีศักดิ์ เลิศประพันธ์

ผู้อำนวยการสำนักงานออกแบบ

นายจตุรงค์ สันติธรรม

หัวหน้างานสถาปัตยกรรม

นายสินธุ์ชัย บุญปักษ์

หัวหน้างานวิศวกรรม

นายธีระยุทธ คงสวัสดิ์เกียรติ

สถาปนิก

นายสินธุ์ชัย บุญปักษ์

วิศวกรโครงสร้าง

วิศวกรไฟฟ้า

วิศวกรสุขาภิบาล

นางสาวมณฑิรา สมหอม

วิศวกรเครื่องกล

นายช่างเขียนแบบ

นายประยูร อรรถจักร์

แบบ
(024) ธรรมรักษา

เจ้าของ

สถานที่

แบบแสดง

รูปด้าน ②

มาตราส่วน 1:75


FILE : ผนัง

วันที่ 2553 A-08

คัดลอกแบบ

นายประยูร อรรถจักร์ 16

รายการแก้ไขแบบ

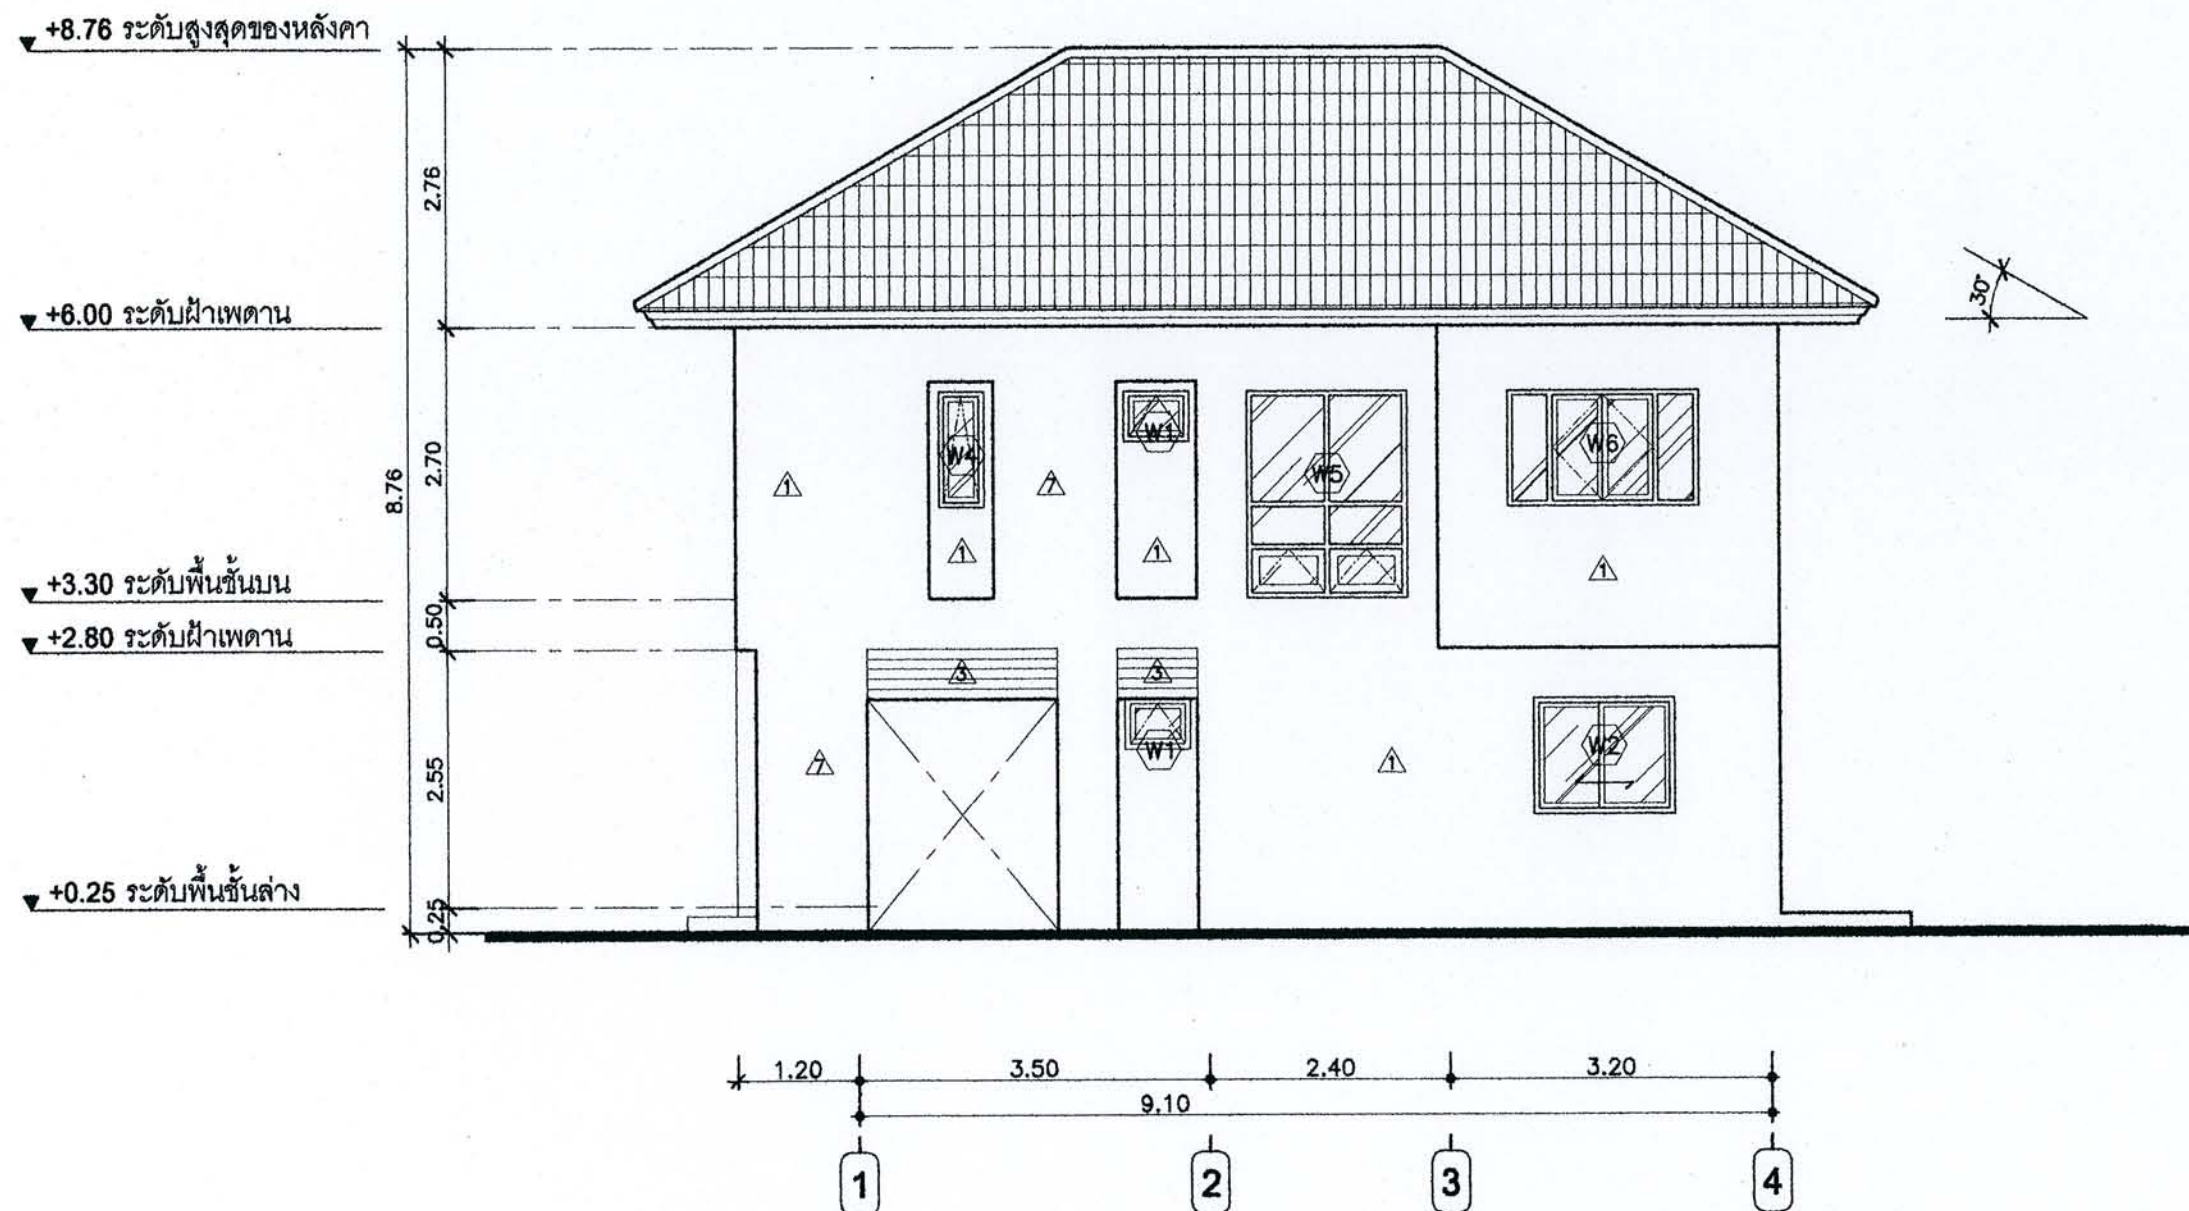

รูปด้าน 2

มาตราส่วน 1:75



สำนักงานการศึกษา
กรุงเทพมหานคร

โครงการ
แบบบ้านยืมเพื่อประชาชน

คานนโยนาช

น.ร.สุพจน์ นิลศิริ ผู้ว่าฯกทม.
นายแพทย์ เศรษฐ์ รอดูว่ากรม
นายธีระชน มโนวิทย์ รอดูว่ากรม
นายพงศ์ศักดิ์ เสงี่ยมศักดิ์ ปลัดฯกทม.

ผู้อำนวยการสำนักงาน

นายจุมพล ลำภาท
รองผู้อำนวยการสำนักงาน
นายทวีศักดิ์ เลิศประพันธ์
ผู้อำนวยการสำนักงาน
นายจตุรงค์ สนิม
หัวหน้างานสถาปัตยกรรม
นายสินธุ์ชัย บุญปักษ์
หัวหน้างานวิศวกรรม
นายธีระยุทธ คงสวัสดิ์

สถาปนิก

นายสินธุ์ชัย บุญปักษ์

วิศวกรโครงสร้าง

วิศวกรไฟฟ้า

วิศวกรสุขาภิบาล

นางสาวมณฑิรา สมหอม

วิศวกรเครื่องกล

นายช่างเขียนแบบ

นายประยูร อรรถจักร์

แบบ

(024) ธรรมชาติ

เจ้าของ

สถานที่

แบบแสดง

รูปด้าน ③

มาตราส่วน 1:75

FILE :


วันที่ 2553

ค.ศ. 2553

นายประยูร อรรถจักร์

16

รายการแก้ไขแบบ

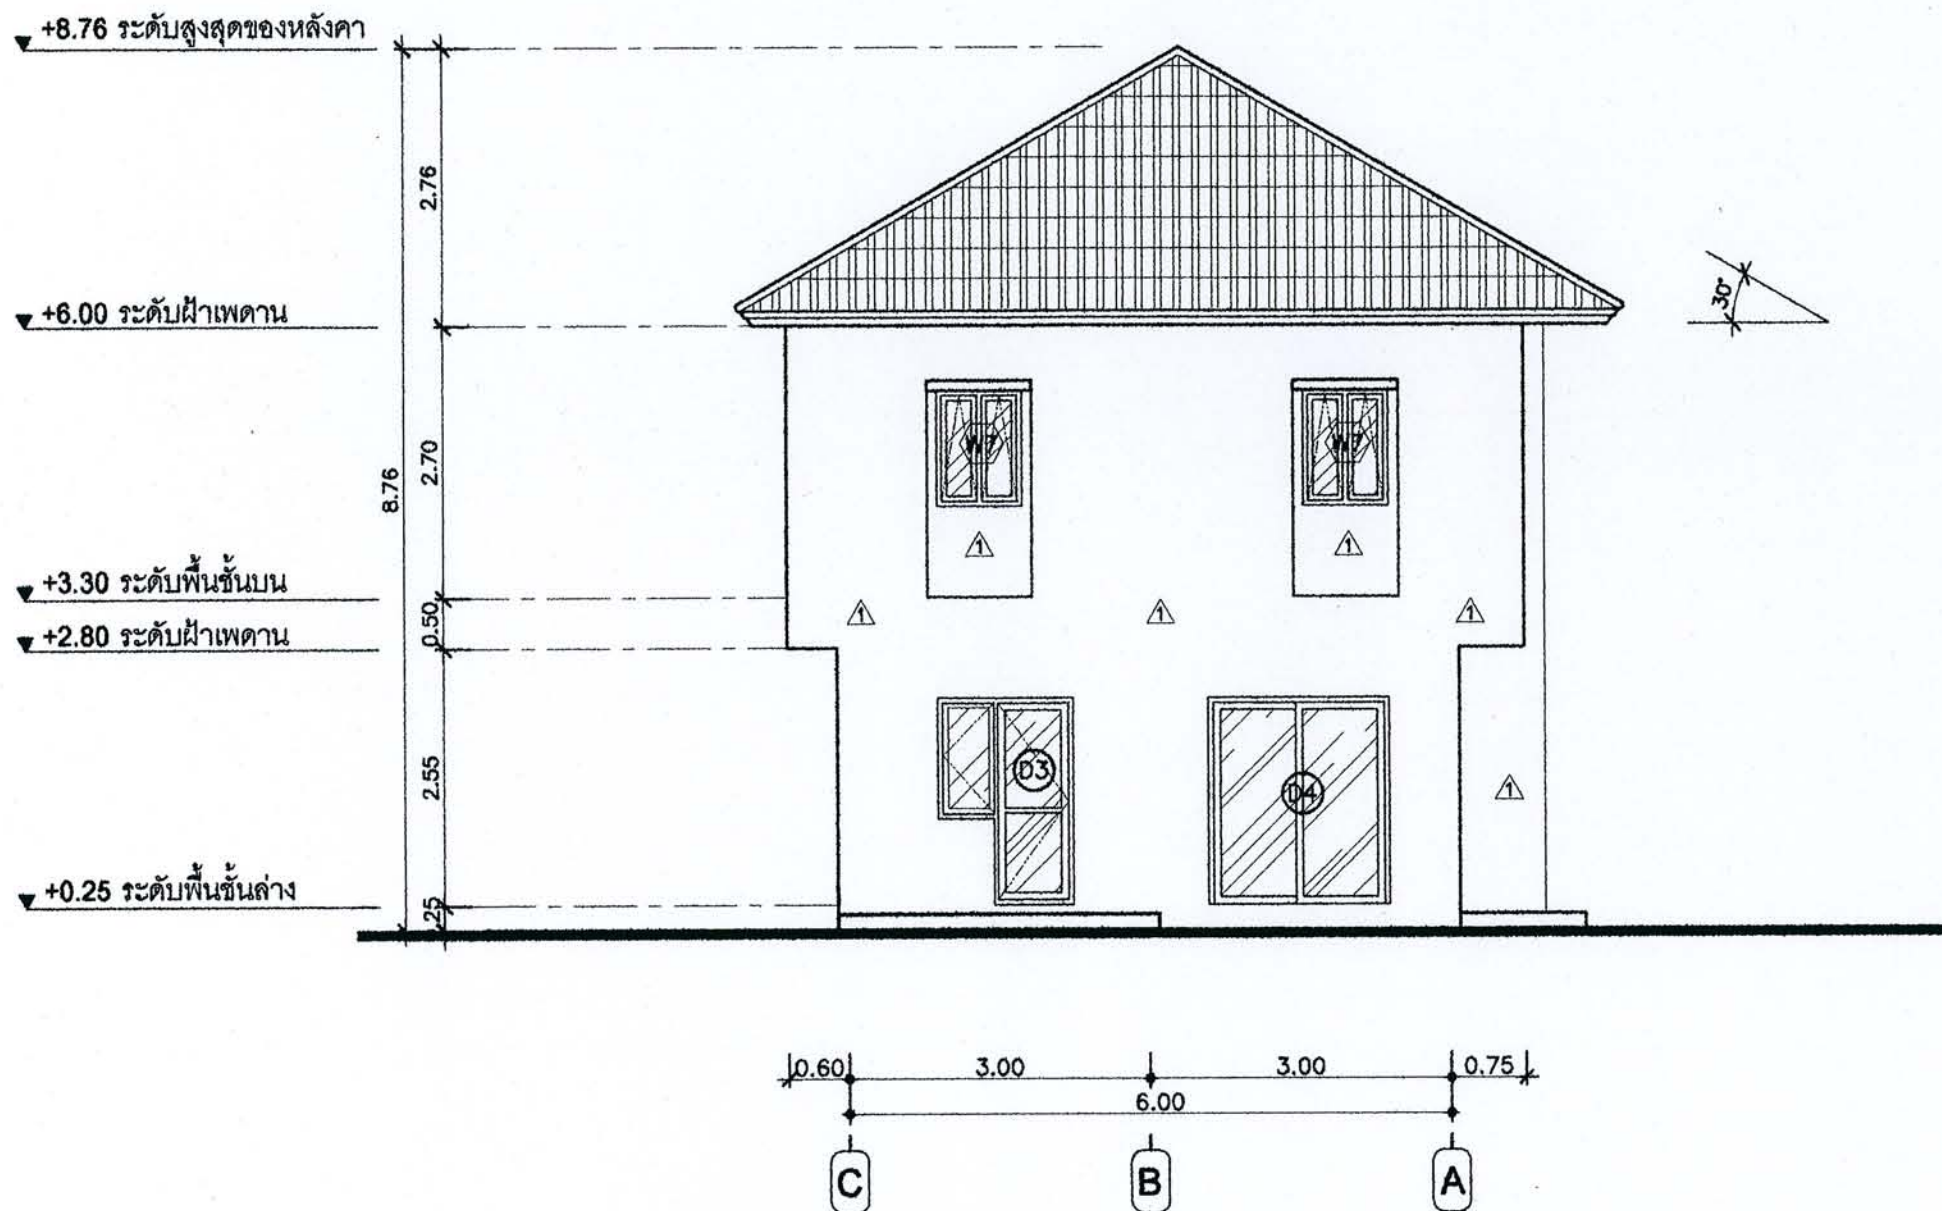

รูปด้าน 3

มาตราส่วน

1:75



สำนักงานสาธารณสุข
กรุงเทพมหานคร

โครงการ
แบบบ้านยืมเพื่อประชาชน

คณบดี

น.ร.สุเมธพันธ์ บริพัตร ผู้อำนวยการ
นายแพทย์ ตรีเทพ ตรีเทพย์ รองผู้อำนวยการ
นายธีระชน มโนชัยกุล รองผู้อำนวยการ
นายพงศ์ศักดิ์ แสนพันธ์ ปลัด

ผู้อำนวยการสำนักงาน

นายสุเมธพันธ์ บริพัตร

รองผู้อำนวยการสำนักงาน

นายแพทย์ ตรีเทพ ตรีเทพย์

ผู้อำนวยการสำนักงาน

นายแพทย์ ตรีเทพ ตรีเทพย์

ผู้อำนวยการสำนักงาน

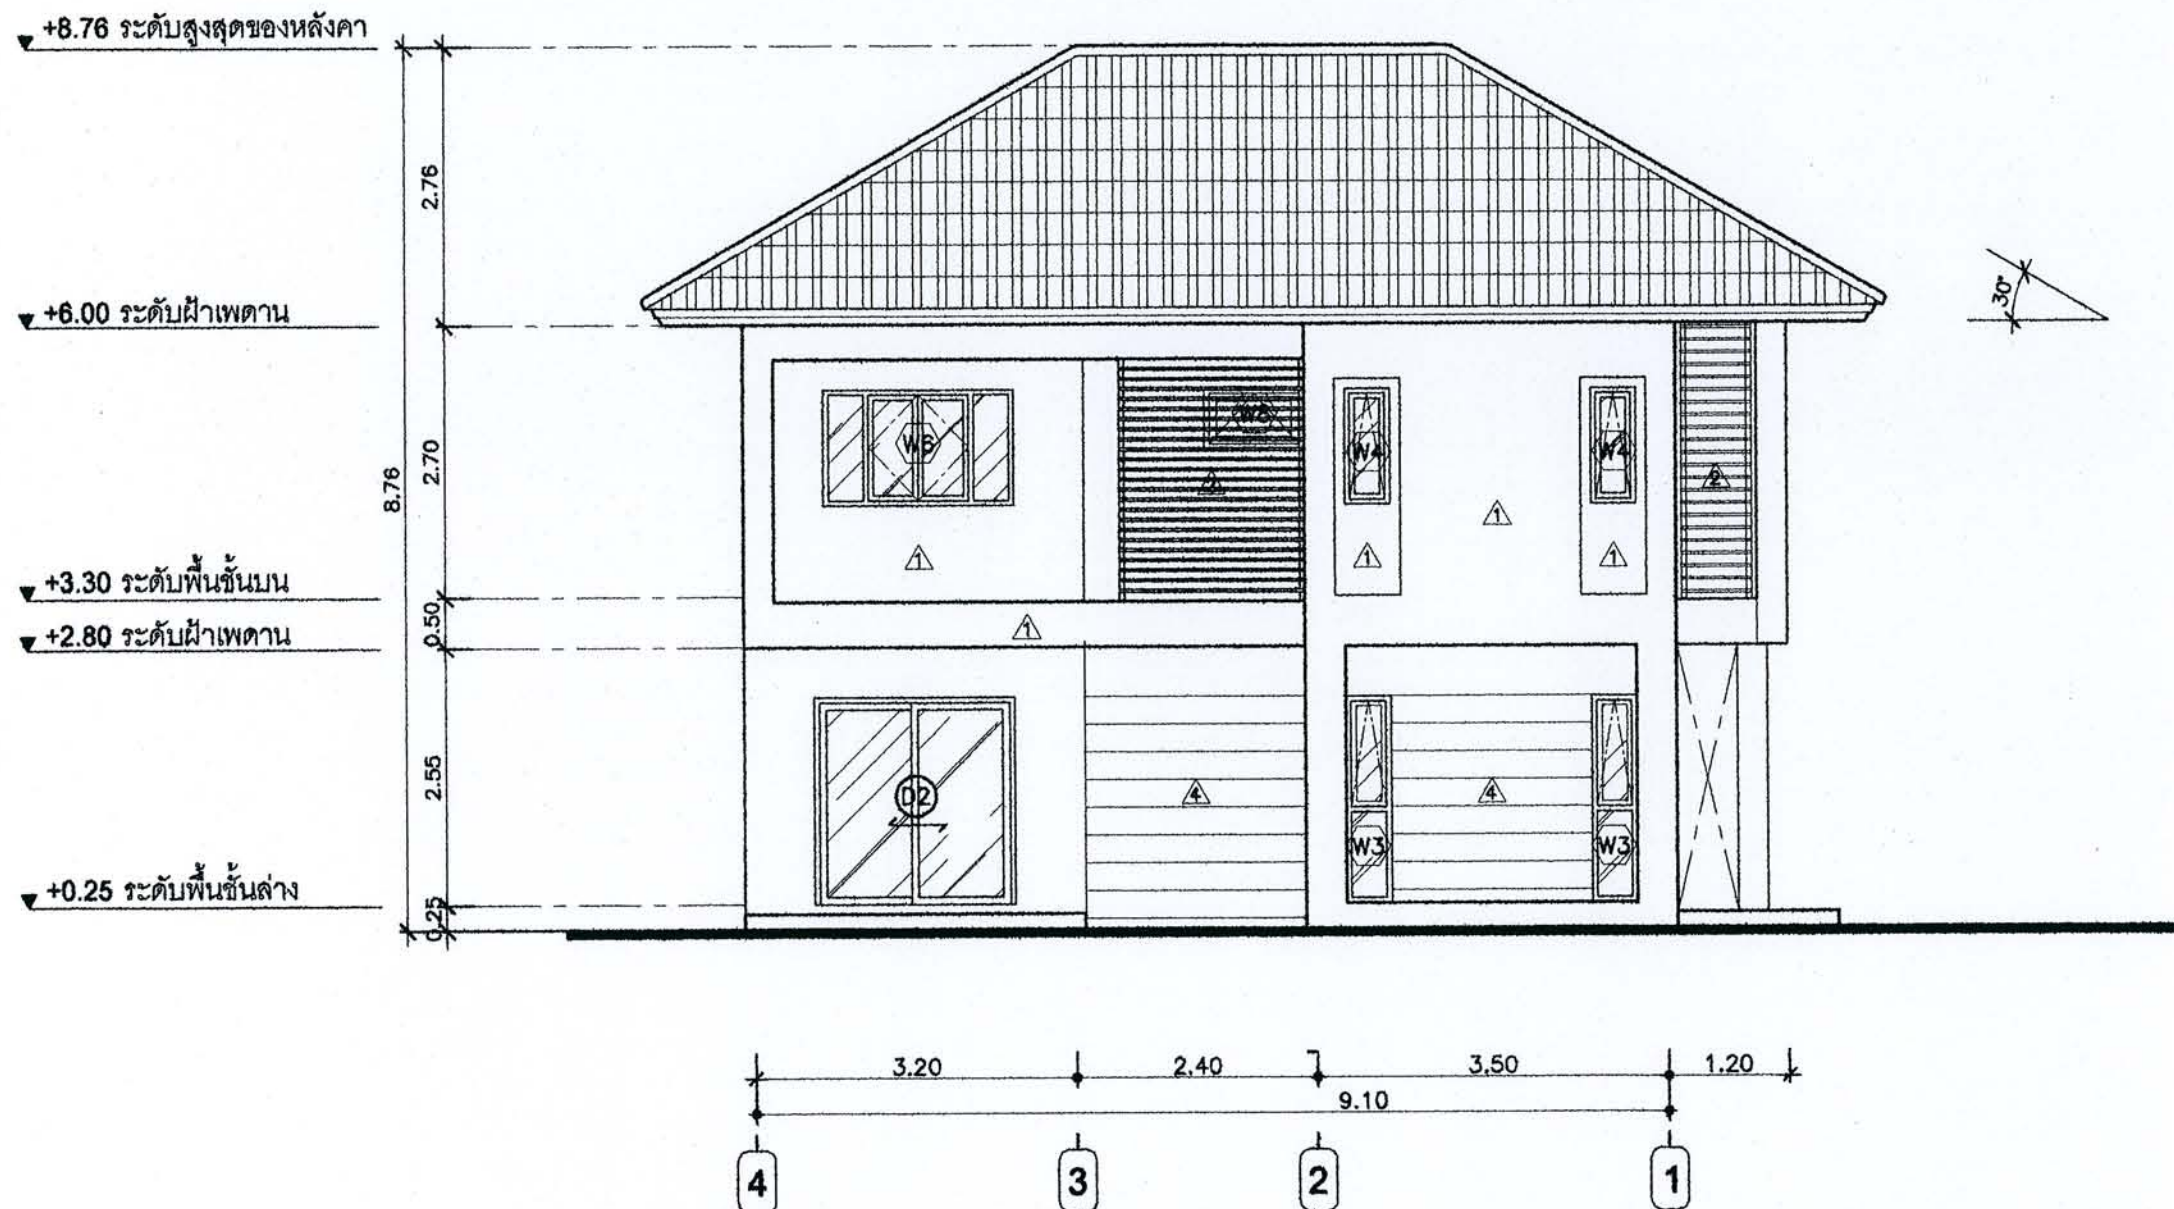

รูปด้าน 4

มาตราส่วน

1 : 75

แบบ (024) ธรรมรักษา

เจ้าของ

สถานที่

แบบแสดง

รูปด้าน 4

มาตราส่วน

1 : 75

FILE :

วันที่ 1 มิถุนายน 2553

แผ่นที่ A-10

คัดลอกแบบ

รวมแผ่น 16

นายประยูร อรรถจักร์

รายการแก้ไขแบบ



สำนักงานสาธารณสุข
กรุงเทพมหานคร

โครงการ
แบบบ้านยืมเพื่อประชาชน

คณนโยนาย

น.ร.สุเมธพันธ์ บริพัตร ผู้ว่าฯกทม.
นายแพทย์ เศรษฐกิจ ร้อยวัชรกุล
นายธีระชน มโนวิทย์ ร้อยวัชรกุล
นายแพทย์ศิริชัย เตมียะนันต์ ปศุสัตว์

ผู้อำนวยการสำนักงาน

นายจุมพล สำนาค
รองผู้อำนวยการสำนักงาน
นายวิศักดิ์ เลิศประพันธ์
ผู้อำนวยการสำนักงานเขต
นายจตุรงค์ สมนิยม
หัวหน้ากลุ่มงานสถาปัตยกรรม
นายสินธุ์ชัย บุญปักษ์
หัวหน้ากลุ่มงานวิศวกรรม
นายธีระยุทธ คงสรคเคียร

สถาปนิก

นายสินธุ์ชัย บุญปักษ์

วิศวกรโครงสร้าง

วิศวกรไฟฟ้า

วิศวกรสุขาภิบาล

นางสาวมณฑิรา สมหอม

วิศวกรเครื่องกล

นายช่างเขียนแบบ

นายประยูร อรรถจักร์

แบบ

(024) ธรรมรักษา

เจ้าของ

สถานที่

แบบแสดง

รูปตัด A-A

มาตราส่วน 1:75

FILE :


วันที่ 2553

คัดลอกแบบ

นายประยูร อรรถจักร์

16

รายการแก้ไขแบบ

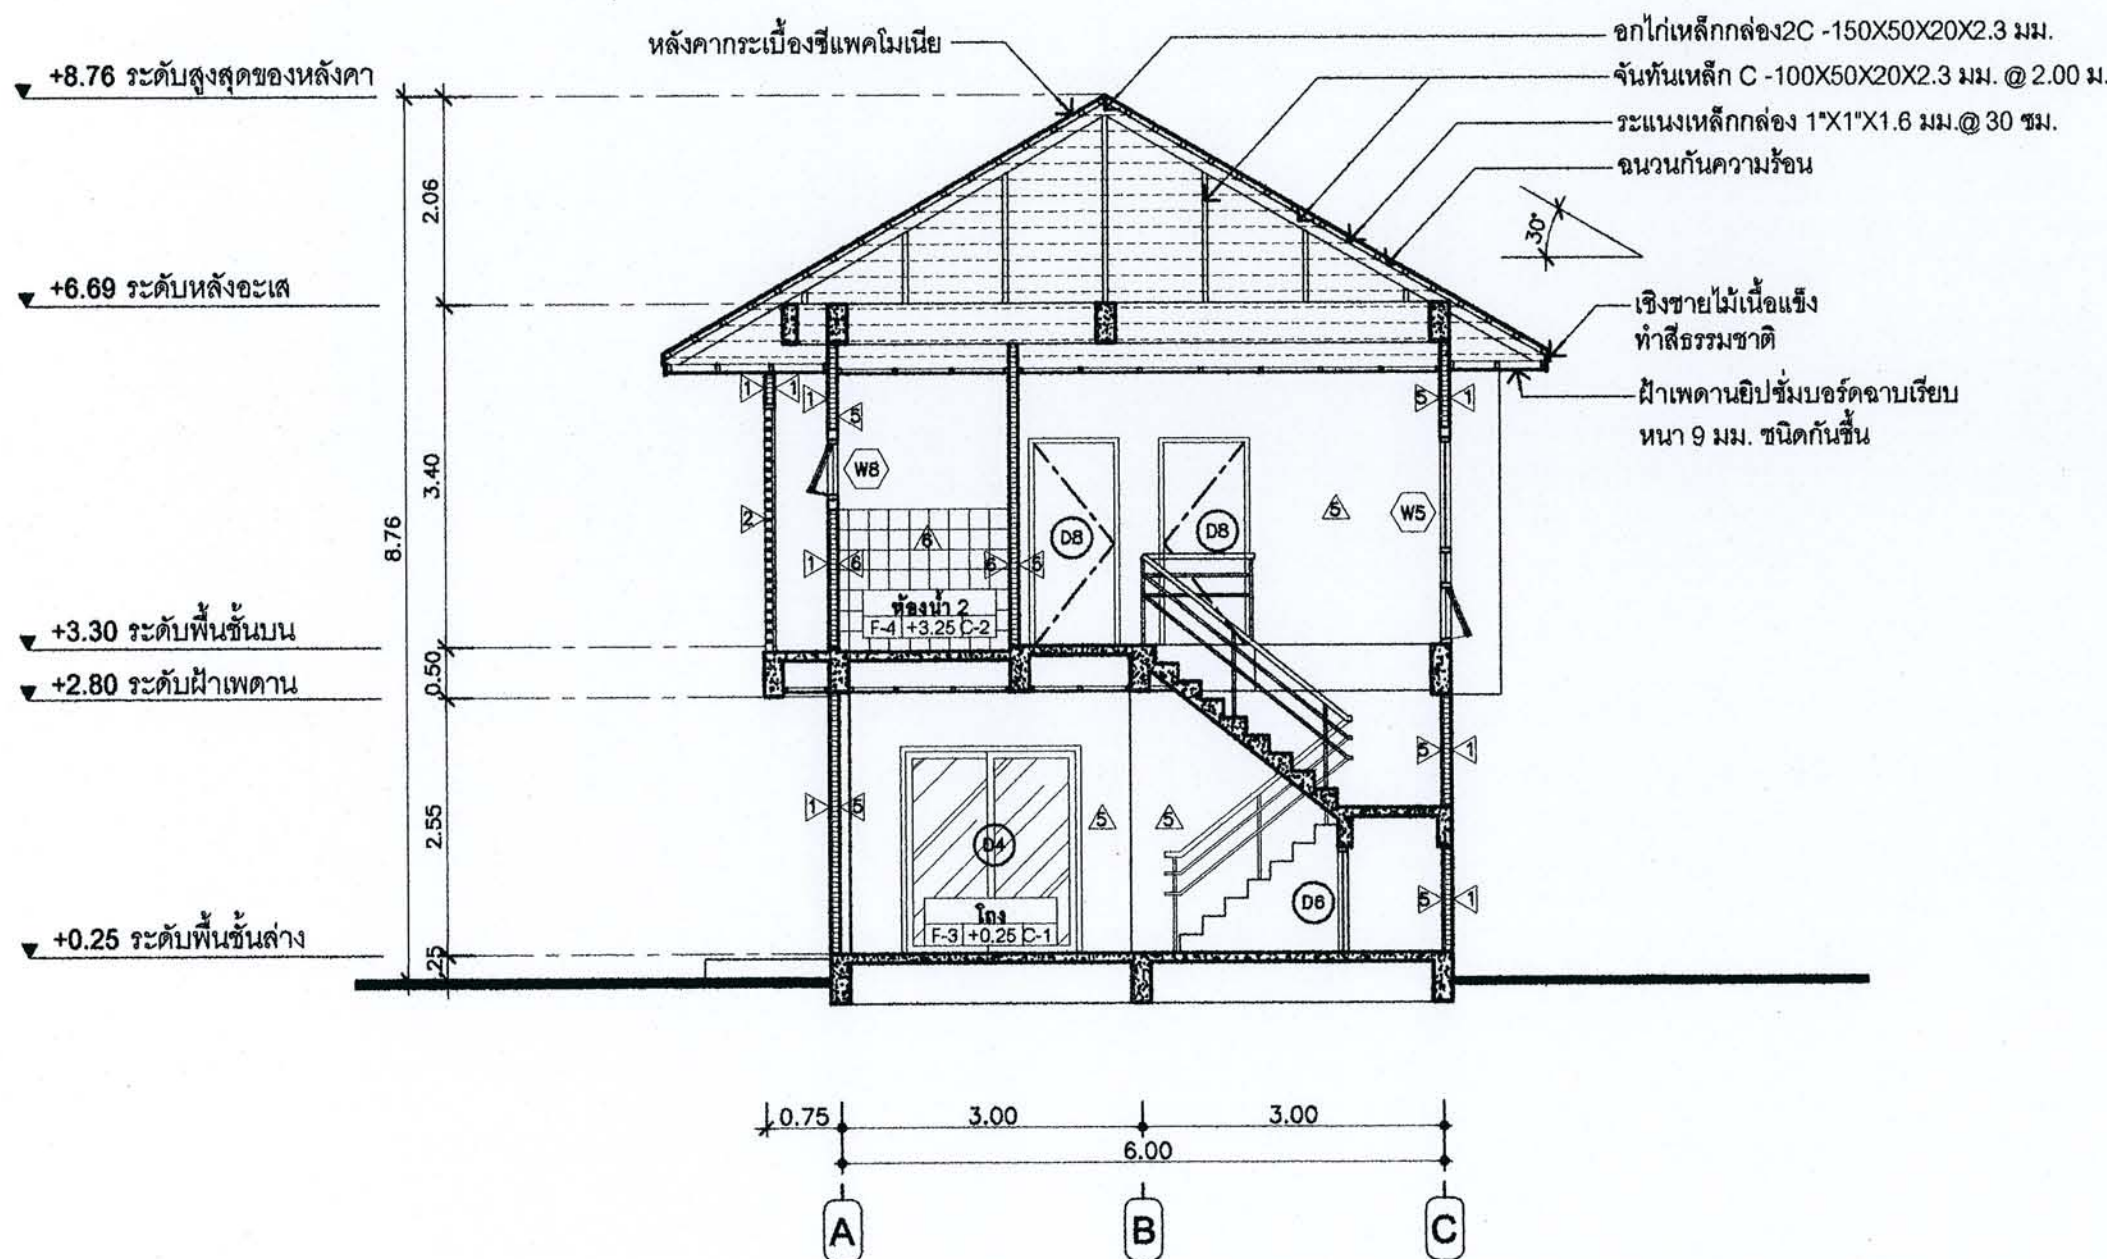

รูปตัด A-A

มาตราส่วน 1:75



สำนักงานสาธารณสุข
กรุงเทพมหานคร

โครงการ
แบบบ้านยืมเพื่อประชาชน

ตามนโยบาย

ม.ร.ว.สุขุมพันธุ์ บริพัตร ผู้ว่าฯ กทม.
นายแพทย์ เชนะโทณกุล รองผู้ว่าฯ กทม.
นายธีระชน มโนวิจิตรกุล รองผู้ว่าฯ กทม.
นายแพทย์ศักดิ์ชัย เตมียาเวส ปลัดฯ กทม.

ผู้อำนวยการสำนักงานโครงการ
นายจุมพล สว่างพล
รองผู้อำนวยการสำนักงานโครงการ
นายทวิศักดิ์ เดชประพันธ์
ผู้อำนวยการสำนักงานออกแบบ
นายจตุรงค์ สอนเนียม
หัวหน้ากลุ่มงานสถาปัตยกรรม
นายสินธุ์ชัย บุญปักษ์
หัวหน้ากลุ่มงานวิศวกรรม
นายธีระยุทธ คงระวีเดียง

สถาปนิก
นายสินธุ์ชัย บุญปักษ์

วิศวกรโครงสร้าง

วิศวกรไฟฟ้า

วิศวกรสุขาภิบาล

นางสาวฉวีณา ศรีสมุทร

วิศวกรโยธา

นายช่างเขียนแบบ

นายประจักษ์ อรรณพจักร

แบบ
(024) ธรรมรักษา

เจ้าของ

สถานที่

แบบแสดง
รูปตัด B-B

มาตราส่วน 1:75


FILE : หนาที่

วันที่ 1 มิถุนายน 2553 A-12

โดย ปรียา หุตะสิงห์ รวมหน้า

นายประจักษ์ อรรณพจักร 16

รายการงานในแบบ

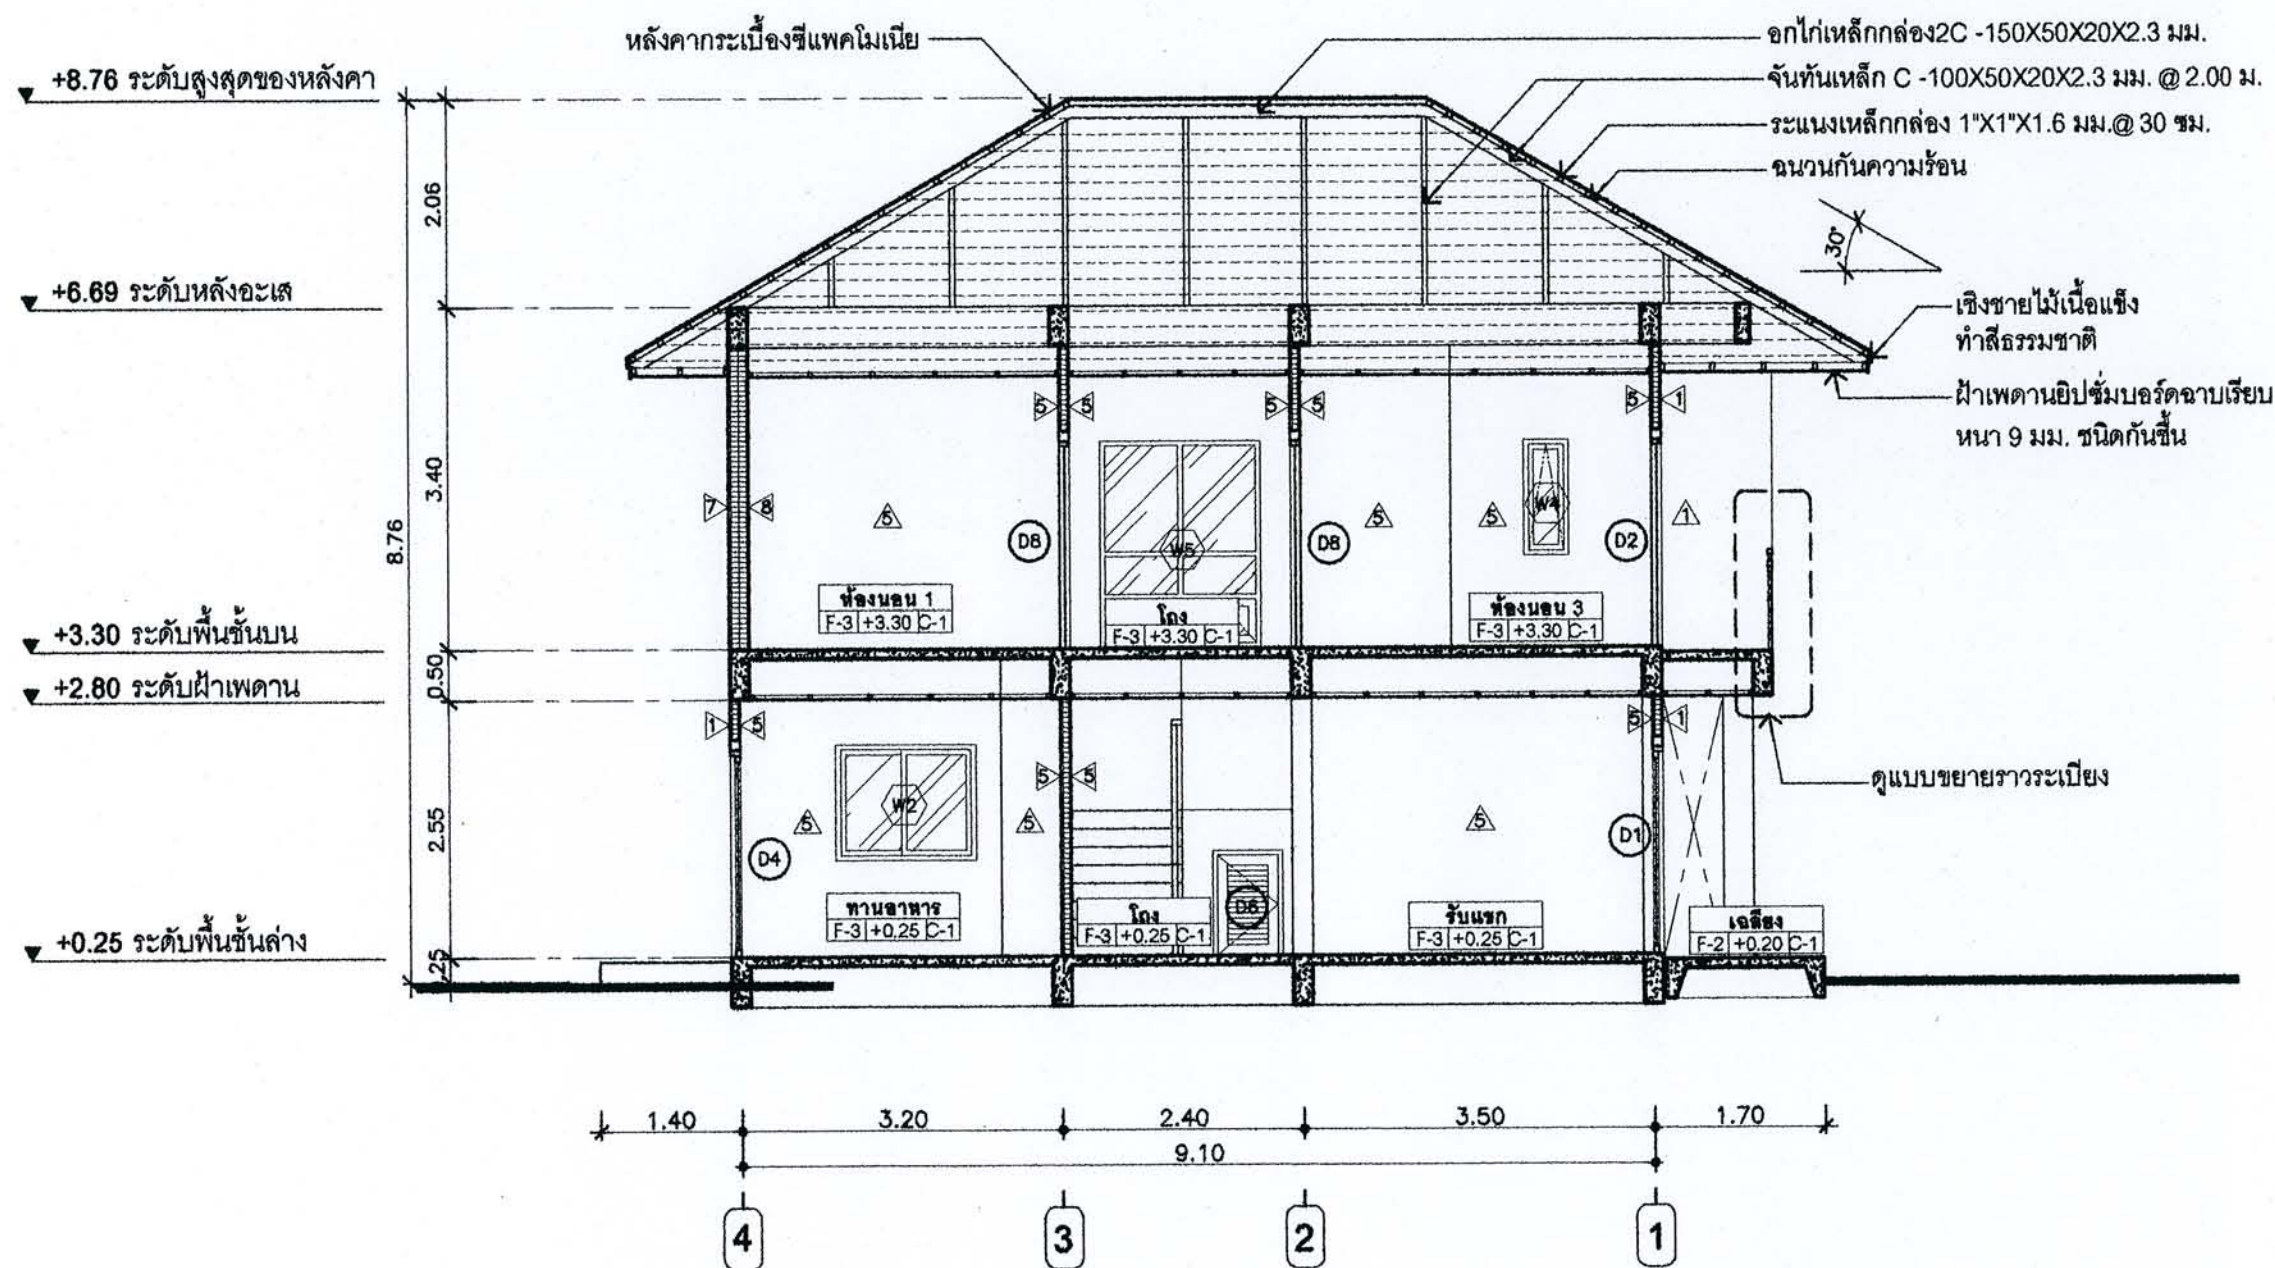

รูปตัด B-B

มาตราส่วน 1:75



สำนักงาน
กรุงเทพมหานคร

โครงการ
แบบบ้านยั่งยืนเพื่อประชาชน

คณบดี

ม.ร.ว.สุขุมพันธุ์ บริพัตร ผู้ว่าฯกทม.
นายพรเทพ เศรษฐกิจ รองผู้ว่าฯกทม.
นายธีระวัฒน์ นิลน้อยสินธุ์ รองผู้ว่าฯกทม.
นายพงศ์ศักดิ์ แสนสุภา ปลัดฯกทม.

ผู้อำนวยการสำนักงาน

นายจุมพล สันภาพ

รองผู้อำนวยการสำนักงาน

นายทวีศักดิ์ เลิศประพันธ์

ผู้อำนวยการสำนักงาน

นายจตุรงค์ สันติธรรม

หัวหน้างานสถาปัตยกรรม

นายสินธุ์ชัย บุญปักษ์

หัวหน้างานวิศวกรรม

นายธีระยุทธ คงสวัสดิ์ชัย

สถาปนิก

นายสินธุ์ชัย บุญปักษ์

วิศวกรโครงสร้าง

วิศวกรไฟฟ้า

วิศวกรสุขาภิบาล

นางสาววรรณิศา สมหอม

วิศวกรโยธา

นายราชกิจจานุเบกษา

นายประยูร อรรถจักร์

แบบ

(024) ธรรมรักษา

เจ้าของ

สถานที่

แบบแสดง

ขยายประตู

มาตราส่วน

1:50

FILE :

วันที่

มกราคม 2553

คัดลอกแบบ

นายประยูร อรรถจักร์

รายการแก้ไขแบบ

สัญลักษณ์	D1	D2	D3	D4
ชนิดบาน	-ประตูบานเลื่อนคู่	-ประตูบานเลื่อนคู่	-ประตู, หน้าต่างบานเปิดเดี่ยว	-ประตูบานเลื่อนคู่
วงกบ	- อลูมิเนียมขอบขาว 2"x4"	- อลูมิเนียมขอบขาว 2"x4"	-ไม้เนื้อแข็ง 2"x4" ทาสีน้ำมันสี...	- อลูมิเนียมขอบขาว 2"x4"
กรอบบาน	-อลูมิเนียมขอบขาว	-อลูมิเนียมขอบขาว	-ไม้ทำสีน้ำมันสี...	-อลูมิเนียมขอบขาว
ลูกพับ, ช่องแสง	-กระจกใสหนา 2 หุน	-กระจกใสหนา 2 หุน	-กระจกใสหนา 2 หุน	-กระจกใสหนา 2 หุน
อุปกรณ์ติดตั้ง	-มือจับ , ตัวล็อก	-มือจับ , ตัวล็อก	-มือจับ , ตัวล็อก	-มือจับ , ตัวล็อก
สัญลักษณ์	D5	D6	D7	D8
ชนิดบาน	-ประตูบานเปิดเดี่ยว	-ประตูบานเปิดเดี่ยว	-ประตูบานเปิดเดี่ยว	-ประตูบานเปิดเดี่ยว
วงกบ	-ไม้เนื้อแข็ง 2"x4" ทาสีน้ำมันสี...	-ไม้เนื้อแข็ง 2"x4" ทาสีน้ำมันสี...	-ไม้เนื้อแข็ง 2"x4" ทาสีน้ำมันสี...	-ไม้เนื้อแข็ง 2"x4" ทาสีน้ำมันสี...
กรอบบาน	-ไม้ทำสีน้ำมันสี...	-ไม้ทำสีน้ำมันสี...	-ไม้ทำสีน้ำมันสี...	-ไม้ทำสีน้ำมันสี...
ลูกพับ, ช่องแสง	-	-	-	-
อุปกรณ์ติดตั้ง	-มือจับ , ตัวล็อก	-มือจับ , ตัวล็อก	-มือจับ , ตัวล็อก	-มือจับ , ตัวล็อก



สำนักการโยธา
กรุงเทพมหานคร

โครงการ
แบบบ้านยิมเพื่อประชาชน

ตามนโยบาย

น.ร.สุจินต์ พันธุ์ ผู้ว่าฯ กทม.
นายทรงยศ หะทัยกุล รองผู้ว่าฯ กทม.
นายธีระชน นิ่มน้อยศิริกุล รองผู้ว่าฯ กทม.
นายพงษ์ศักดิ์ แสนสิน ปัสดาภรณ์

ผู้อำนวยการสำนักการโยธา
นายจุฑามาศ สันภาพล
รองผู้อำนวยการสำนักการโยธา
นายวิศักดิ์ เลิศประพันธ์
ผู้อำนวยการสำนักงานออกแบบ
นายจุฑามาศ สันภาพล
หัวหน้ากลุ่มงานสถาปัตยกรรม
นายสินธุ์ชัย บุญปักษ์
หัวหน้ากลุ่มงานวิศวกรรม
นายธีระยุทธ คงสรรค์เสถียร

สถาปนิก
นายสินธุ์ชัย บุญปักษ์

วิศวกรโครงสร้าง

วิศวกรไฟฟ้า

วิศวกรสุขาภิบาล

นางสาวรณนิจิรา สมน้อม

วิศวกรเครื่องกล

นายราชธิพนธ์

นายประจักษ์ ธรรมจักร

แบบ
(024) ธรรมจักร

เจ้าของ

สถานที่

แบบแสดง

ขยายหน้าต่าง

มาตราส่วน 1:50

FILE : A-14

วันที่ 2553


ออกแบบโดย

นายประจักษ์ ธรรมจักร

รวมแผ่น 16


รายการแก้ไขแบบ

สัญลักษณ์	W1	W2	W3	W4
ชนิดบาน	-หน้าต่างบานกระทุ้ง	-ประตูบานเลื่อนคู่	-หน้าต่างบานกระทุ้ง	-หน้าต่างบานกระทุ้ง
วงกบ	-ไม้เนื้อแข็ง 2"x4" ทาสีน้ำมันสี...	-อลูมิเนียมขอบขาว 2"x4"	-ไม้เนื้อแข็ง 2"x4" ทาสีน้ำมันสี...	-ไม้เนื้อแข็ง 2"x4" ทาสีน้ำมันสี...
กรอบบาน	-ไม้ทำสีน้ำมันสี...	-อลูมิเนียมขอบขาว	-ไม้ทำสีน้ำมันสี...	-ไม้ทำสีน้ำมันสี...
ลูกฟัก, ช่องแสง	-กระจกใสหนา 2 หุน	-กระจกใสหนา 2 หุน	-กระจกใสหนา 2 หุน	-กระจกใสหนา 2 หุน
อุปกรณ์ติดตั้ง	-มือจับ	-มือจับ , ตัวล็อก	-มือจับ , ตัวล็อก	-มือจับ , ตัวล็อก
สัญลักษณ์	W5	W6	W7	W8
ชนิดบาน	-หน้าต่างบานกระทุ้ง	-หน้าต่างบานเปิดคู่	-หน้าต่างบานกระทุ้ง	-หน้าต่างบานกระทุ้ง
วงกบ	-ไม้เนื้อแข็ง 2"x4" ทาสีน้ำมันสี...	-ไม้เนื้อแข็ง 2"x4" ทาสีน้ำมันสี...	-ไม้เนื้อแข็ง 2"x4" ทาสีน้ำมันสี...	-ไม้เนื้อแข็ง 2"x4" ทาสีน้ำมันสี...
กรอบบาน	-ไม้ทำสีน้ำมันสี...	-ไม้ทำสีน้ำมันสี...	-ไม้ทำสีน้ำมันสี...	-ไม้ทำสีน้ำมันสี...
ลูกฟัก, ช่องแสง	-กระจกใสหนา 2 หุน	-กระจกใสหนา 2 หุน	-กระจกใสหนา 2 หุน	-กระจกใสหนา 2 หุน
อุปกรณ์ติดตั้ง	-มือจับ , ตัวล็อก	-มือจับ , ตัวล็อก	-มือจับ , ตัวล็อก	-มือจับ , ตัวล็อก

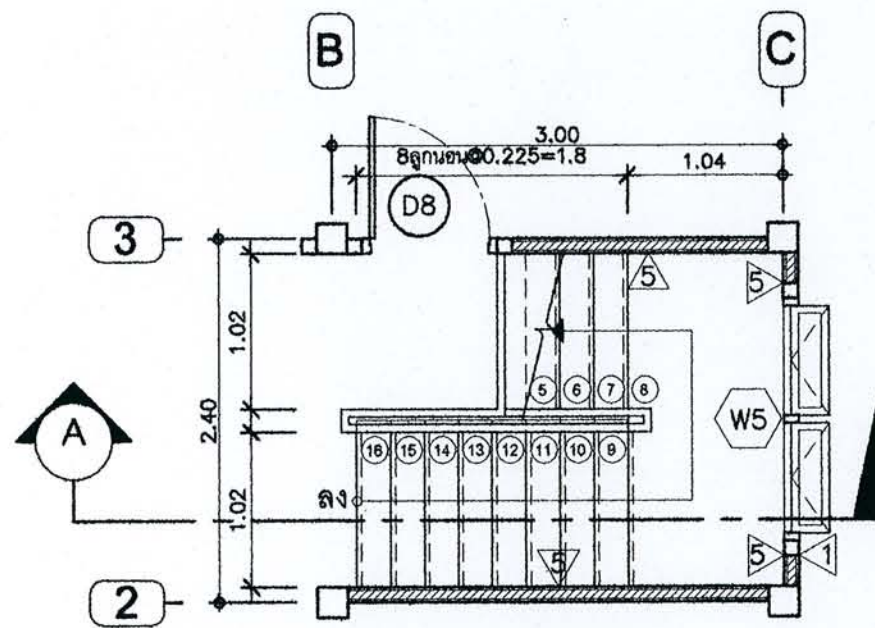


แบบขยายบันไดชั้นบน

มาตราส่วน 1 : 50

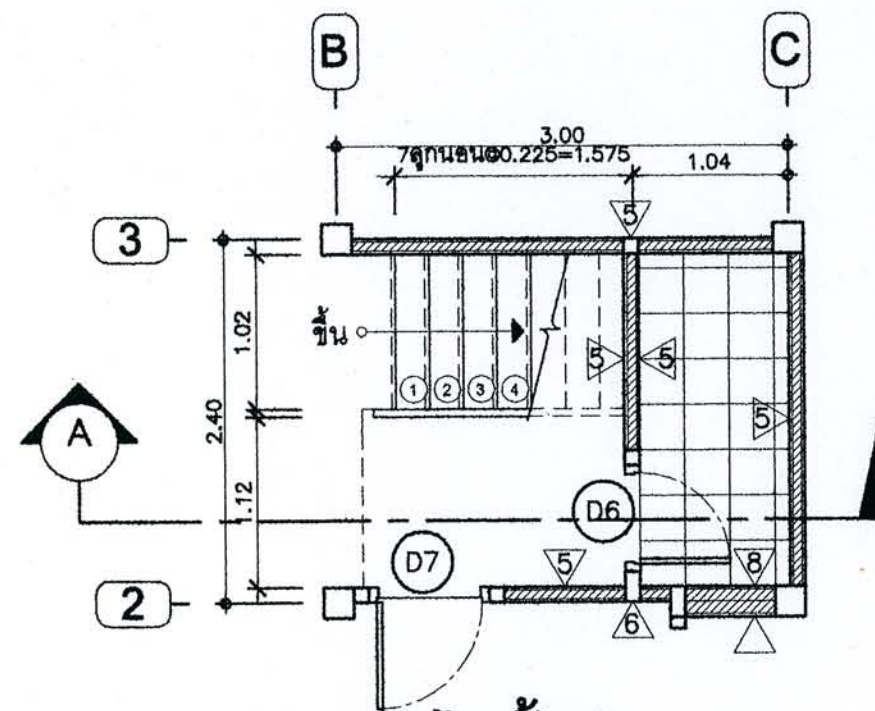

แบบขยายบันไดชั้นล่าง

มาตราส่วน 1 : 50

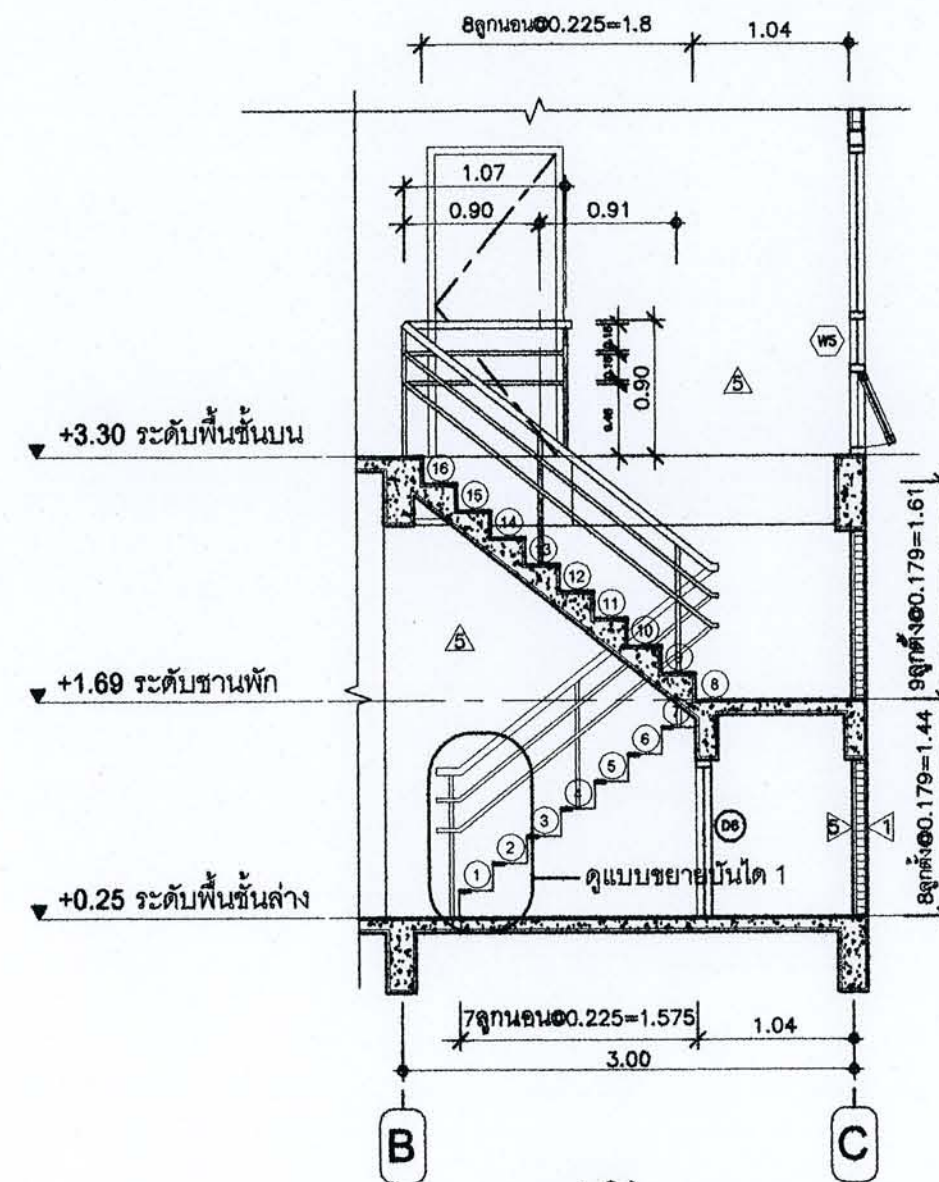

รูปตัด A

มาตราส่วน 1 : 50



สำนักงานคณะกรรมการ
การศึกษาแห่งชาติ

โครงการ
แบบบ้านขึ้นเพื่อประชาชน

ตามนโยบาย

ม.ร.ว.สุขุมพันธุ์ บริพัตร ผู้ว่าฯ กทม.
นายพรเทพ เศรษฐินันท์ รองผู้ว่าฯ กทม.
นายธีระวัฒน์ มโนทิตะกุล รองผู้ว่าฯ กทม.
นายพงษ์ศักดิ์ แสนจันทร์ ปลัดฯ กทม.

ผู้อำนวยการสำนักงานโครงการ
นายจุมพล คำภาพล
รองผู้อำนวยการสำนักงานโครงการ
นายทวีศักดิ์ เลิศประพันธ์
ผู้อำนวยการสำนักงานออกแบบ
นายจตุรงค์ สอนเนียม
หัวหน้างานสถาปัตย์กรรม
นายสินธุ์ชัย บุญปักษ์
หัวหน้างานวิศวกรรม
นายธีระยุทธ คงสวัสดิ์เกียรติ

สถาปนิก
นายสินธุ์ชัย บุญปักษ์

วิศวกรโครงสร้าง

วิศวกรไฟฟ้า

วิศวกรสุขาภิบาล

นางสาวมณฑิรา สมพยอม

วิศวกรเครื่องกล

นายช่างเขียนแบบ

นายประจักษ์ อรรถจักร์

แบบ (024) ธรรมรักษา

เจ้าของ

สถานที่

แบบแสดง
ขยายบันได

มาตราส่วน 1 : 50

FILE : แผนที่

วันที่ 2553 A-15

ออกแบบโดย

นายประจักษ์ อรรถจักร์ 16

รายการแก้ไขแบบ



สำนักงาน
กรุงเทพมหานคร

โครงการ
แบบบ้านยืมเพื่อประชาชน

คณนโยบาย

ม.ร.ว.สุขุมพันธุ์ บริพัตร ผู้ว่าฯ กทม.
นายพรเทพ เศรษฐกิจ รองผู้ว่าฯ กทม.
นายธีระวัฒน์ นิ่มน้อม รองผู้ว่าฯ กทม.
นายพงศ์ศักดิ์ เสงี่ยมพงศ์ ปลัดฯ กทม.

ผู้อำนวยการสำนักการโยธา

นายจุมพฏ สว่างกุล

รองผู้อำนวยการสำนักการโยธา

นายทวีศักดิ์ เลิศประพันธ์

ผู้อำนวยการสำนักงานออกแบบ

นายจตุรงค์ สอนเนียม

หัวหน้าสำนักงานสถาปัตย์กรรม

นายสินธุ์ชัย บุญปักษ์

หัวหน้ากลุ่มงานวิศวกรรม

นายธีระยุทธ คงสิริยศ

สถาปนิก

นายสินธุ์ชัย บุญปักษ์

วิศวกรโครงสร้าง

วิศวกรไฟฟ้า

วิศวกรสุขาภิบาล

นางสาวมณฑิรา สมหอม

วิศวกรเครื่องกล

นายช่างเขียนแบบ

นายประจักษ์ อรรถจักร์

แบบ (024) ธรรมรักษา

เจ้าของ

สถานที่

แบบแสดง

ขยายระบียง

มาตราส่วน 1:50

FILE :

วันที่ มิถุนายน 2553


คณนโยบาย

นายประจักษ์ อรรถจักร์

รวมแผ่น


16

รายการแก้ไขแบบ

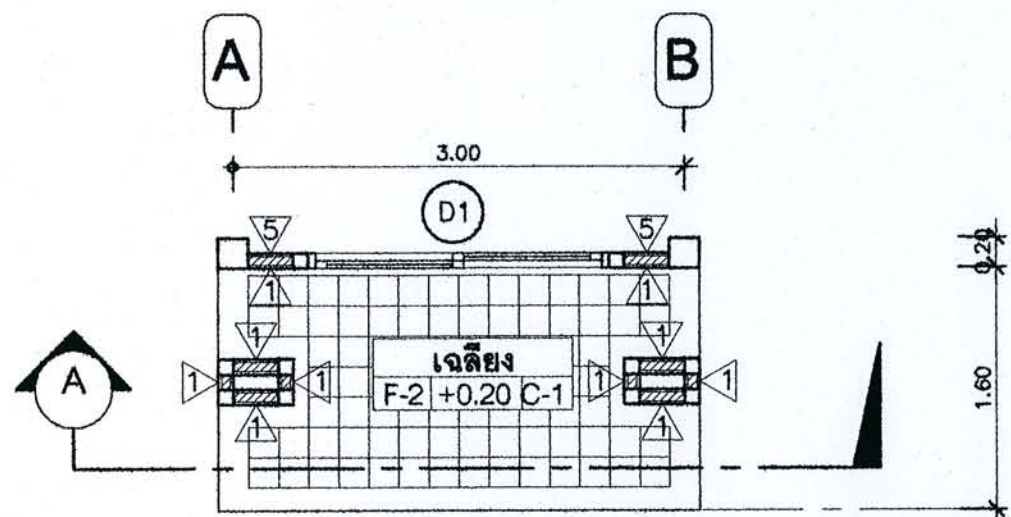


แบบขยายเจดียงหน้าบ้าน

มาตราส่วน 1:50

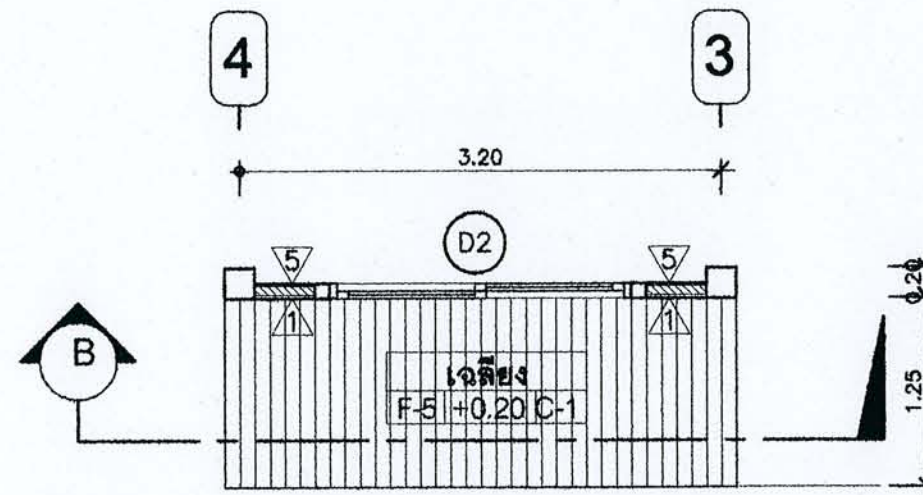


แบบขยายเจดียงห้องทานอาหาร

มาตราส่วน 1:50

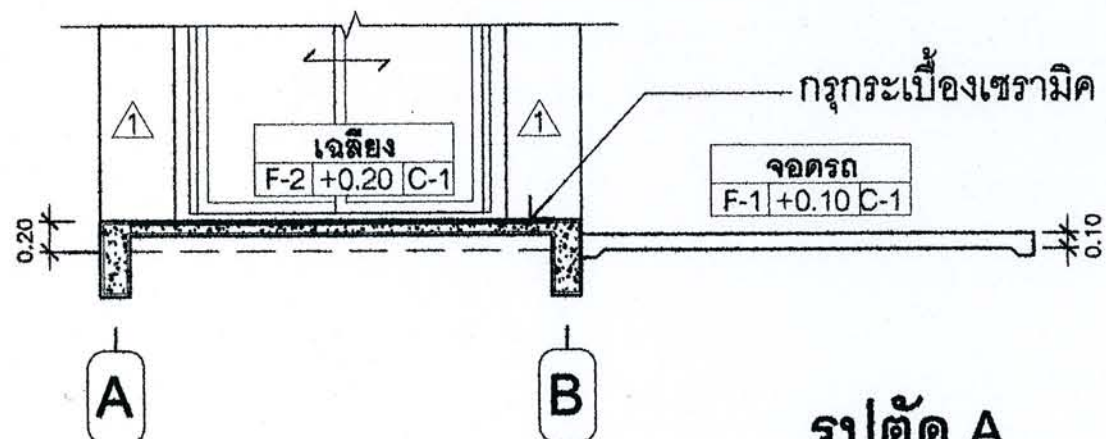

รูปตัด A

มาตราส่วน 1:50

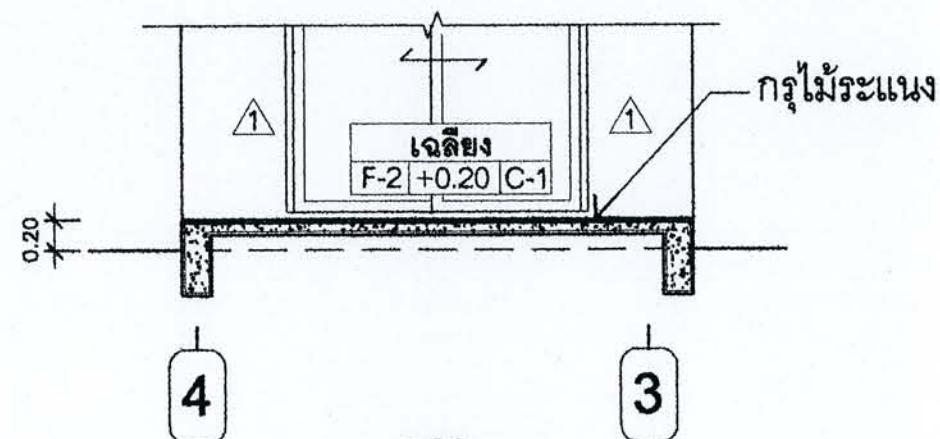

รูปตัด B

มาตราส่วน 1:50

รายการประกอบแบบโครงสร้าง

● คอนกรีต

กำลังอัดประลัยของแท่งคอนกรีตทรงกระบอกมาตรฐานขนาด ϕ 0.15 X 0.30 m. ที่อายุการบ่ม 28 วันจะต้องไม่ต่ำกว่า 210 กก./ซม² (โดยวิธีทดสอบมาตรฐาน)
คอนกรีตให้ใช้อัตราส่วนผสม 1:2:4 โดยปริมาตร และให้ใช้ปูนซีเมนต์ปอร์ตแลนด์ประเภท 1 ทราายให้ใช้ทรายสะอาด ปราศจากเปลือกหอย ชากสัตว์ ดิน หรือสิ่งอื่นใด
ซึ่งจะเป็นอันตรายต่อคุณภาพของคอนกรีต น้ำต้องเป็นน้ำสะอาดปราศจากกรด ด่าง ซึ่งสามารถดื่มกินได้ หิน ต้องเป็นหินจากโรงโม่หินซึ่งกำหนดให้ใช้หินเบอร์ 2 ซึ่งต้อง
มีความเหมาะสมสามารถให้คอนกรีตเกาะยึดได้ดี

ก่อนเทคอนกรีตทุกครั้ง จะต้องแจ้งให้ผู้ควบคุมงานทราบก่อนล่วงหน้าทุกครั้ง ทั้งนี้เพื่อทำการตรวจสอบแบบ โครงสร้างเหล็กเสริม จนเป็นที่เรียบร้อยแล้วจึงจะทำการเทคอนกรีตต่อไปได้
การทำงานจะต้องมีการกระทุ้ง เพื่อให้คอนกรีตรวมตัวกันได้ดี หลังการถอดแบบแล้วถ้าเกิดโพรงในเนื้อคอนกรีตซึ่งวิศวกรพิจารณาแล้วเห็นว่าป็นอันตรายต่อการรับน้ำหนัก ผู้รับจ้าง
จะต้องทำการทุบและเทส่วนใหม่ ตามคำแนะนำของวิศวกรโดยไม่มีข้อโต้แย้งใดๆ เมื่อทำการถอดแบบแล้ว จะต้องมีการบ่มคอนกรีตที่ถูกต้อง

การบ่มคอนกรีต เสา คาน ให้ใช้กระสอบป่าน ห่มให้ทั่วแล้วรดน้ำให้ชุ่มตลอดเวลา ไม่แบบ อ่างเสาคาน จะถอดหลังจากเทคอนกรีตแล้ว 48 ชั่วโมง ส่วนไม้แบบรับท้องคาน
ท้องพื้นจะถอดได้ต้องทิ้งไว้ไม่น้อยกว่า 14 วัน หลังจากเทคอนกรีตแล้วเสร็จ การบ่มส่วนที่เป็นพื้นคอนกรีต ให้ใช้ดินเหนียวกันขอบ โดยรอบแล้วทิ้งน้ำทิ้งไว้ 5 วัน ในระหว่างที่มี
การบ่มคอนกรีตห้ามมีน้ำหนักใดๆ มากดทับเป็นอันขาด

● เหล็กเสริมคอนกรีต

เหล็กเส้นเสริมคอนกรีตให้ใช้ตามมาตรฐานผลิตภัณฑ์อุตสาหกรรม มอก.24-2527 หรือที่มีคุณภาพเทียบเท่า

สำหรับเหล็กเส้นกลมผิวเรียบให้ใช้ GRADE SR-24 กำลังคลากไม่น้อยกว่า 2400 กก./ซม

สำหรับเหล็กข้ออ้อยให้ใช้ GRADE SD-30 กำลังคลากไม่น้อยกว่า 3000 กก./ซม

เหล็กเส้นเสริมคอนกรีตที่จะนำมาใช้งาน ต้องเป็นเหล็กใหม่ที่ไม่เคยผ่านการใช้งานใด ๆ มาก่อน ปราศจากสนิม น้ำมัน หรือสิ่งใดที่ผิวเหล็กซึ่งก่อให้เกิดอันตรายต่อการ
ยึดเหนี่ยวระหว่างเหล็กเสริมและคอนกรีต การงอข้อที่ปลายเหล็กจะต้องได้ขนาดตามมาตรฐานสากล สำหรับเหล็กข้ออ้อยให้ใช้การงอได้ไม่เกิน 90 องศา
ต้องหลีกเลี่ยงการดัดเหล็กเสริมใหม่ที่สุดเท่าที่จะทำได้ ถ้ามีความจำเป็นที่จะต้องดัดเหล็กให้ใช้วิธีการดัดที่ห้ามใช้วิธีการเชื่อม ระยะการดัดเหล็กจะต้องได้ตามมาตรฐาน
และมีระยะมากพอที่จะสามารถถ่ายแรงทั้งหมดที่เกิดขึ้นได้โดยปลอดภัย การดัดเหล็กให้กระทำในบริเวณที่เกิดอันตรายน้อยที่สุด และห้ามดัดเหล็กที่ตำแหน่งเดียวกัน

● เหล็กโครงสร้างรูปพรรณ

เหล็กโครงสร้างรูปพรรณให้ใช้ตามมาตรฐาน ASTM A-36 กำลังคลากของเหล็กเมื่อรับแรงดึงไม่น้อยกว่า 2500 กก./ซม

สลักเกลียวที่ใช้ต้องมีคุณภาพเทียบเท่ามาตรฐาน ASTM A-325 ชนิดสลักเกลียวกำลังสูง HIGH STRENGTH BOLT จำนวนสลักเกลียวอย่างน้อย 2 ตัวสำหรับรอยต่อที่ใช้สลักเกลียว
ลวดเชื่อมให้ใช้ชนิด E-60 xx ASTM สำหรับเหล็กที่มีความหนาไม่เกิน 4 มิลลิเมตร ขนาดของรอยเชื่อมมากที่สุดต้องไม่เกินความหนาเหล็ก (หากมิได้มีการระบุ)

และสำหรับเหล็กที่มีความหนามากกว่า 4 มิลลิเมตรขึ้นไป ขนาดของรอยเชื่อมมากที่สุดต้องไม่เกินความหนาเหล็กด้วย 2 มิลลิเมตร

การวัดระยะต่าง ๆ ของชิ้นส่วนโครงสร้างเหล็ก ให้วัดออกจากแนวจุดศูนย์กลางของหน้าตัดเหล็ก (CENTER LINE) หรือจากจุดที่แนวศูนย์กลางตัดกัน (WORK POINT)

● ฐานราก

ฐานรากเป็นฐานราก คสล. ขนาด ระยะให้ดูตามแบบโครงสร้าง การประกอบแบบให้ใช้ไม้แบบประกอบแบบห้ามมิให้แต่งดินทำแบบโดยเด็ดขาด ทั้งนี้รวมทั้งการประกอบแบบ
คานคอดินด้วย สำหรับเสาเข็มทุกเหลี่ยม 0.15 ม. ลึก 6.00 ม.

dk9jvgjHdglib,.eh=h9k,k9jko ACI 318 M-95 fy'cl'f.09Kik'9jwxouh


hptdkl'mk[gs]Hdglib,.eh=h9k,k9jko

ขนาดของ เหล็กเสริม	ระยะห่างสำหรับคอนกรีต ประเภท ค3			ระยะห่างสำหรับคอนกรีต ประเภท ค4		
	เหล็กเสริม รับแรงอัด (ซม.)	เหล็กเสริม รับแรงดึง เหล็กบน 5 (ซม.)	เหล็กอื่น ๆ (ซม.)	เหล็กเสริม รับแรงอัด (ซม.)	เหล็กบน 5 (ซม.)	เหล็กอื่น ๆ (ซม.)
RB6	30	40	40	30	40	40
RB9	30	40	40	30	40	40
DB10	30	65	50	30	55	45
DB12	33	80	60	35	65	50
DB16	45	100	80	45	85	65
DB20	55	125	100	55	100	85
DB25	70	200	150	70	170	130

* เหล็กบนหมายถึงเหล็กเสริมที่มีคอนกรีตหล่อหุ้มอยู่ใต้เหล็กเสริมหนาไม่น้อยกว่า 30 ซม.

การงอขอลายเหล็ก

การงอให้ใช้วิธีดัดแบบ ดังรูป

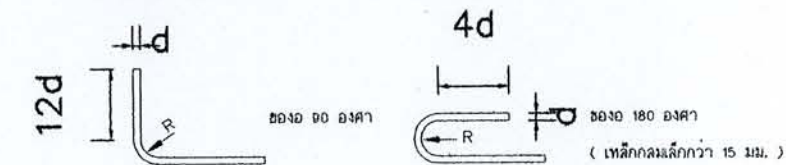

R ไม่น้อยกว่า 2.0 d สำหรับเหล็กเส้นกลม

R ไม่น้อยกว่า 2.5 d สำหรับเหล็กข้ออ้อย

การงอ 90 องศา ใช้ได้กับเหล็กข้ออ้อยทุกขนาด และเหล็กเส้นกลมขนาดตั้งแต่ 15 มม. ขึ้นไป

การงอเหล็กกลม คานและเสา ใช้เหล็กขนาด 8 มม. หรือ 9 มม. ให้ปฏิบัติตามนี้




4 d แต่ต้องไม่น้อยกว่า 3 ซม.

R = 2.0 ซม. สำหรับเหล็กแกนขนาดใหญ่กว่า

R = 1.5 สำหรับเหล็กแกนขนาด

R = 1.0 สำหรับเหล็กแกนขนาด

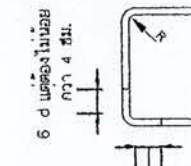

6 d แต่ต้องไม่น้อยกว่า 4 ซม.

25 มม.

19 มม. - 25 มม.

12 มม. - 16 มม.



สำนักงานโยธา
กรุงเทพมหานคร

โครงการ
แบบบ้านยืมเพื่อประชาชน

ตามนโยบาย

ม.ร.ว.สุขุมพันธุ์ บริพัตร ผู้ว่าฯกทม.
นายทศพร เศรษฐกิจ รองผู้ว่าฯกทม.
นายธีระชน มโนวิทย์กิจ รองผู้ว่าฯกทม.
นายพงศ์ภัค กสิสุขุม รองผู้ว่าฯกทม.
นายพงศ์ภัค กสิสุขุม รองผู้ว่าฯกทม.

ผู้อำนวยการสำนักงานโยธา
นายจตุรนต์ สันติสุข
รองผู้อำนวยการสำนักงานโยธา
นายทศพร เศรษฐกิจ
ผู้อำนวยการสำนักงานโยธา
นายจตุรนต์ สันติสุข
ผู้อำนวยการสำนักงานโยธา
นายธีระชน มโนวิทย์กิจ
ผู้อำนวยการสำนักงานโยธา
นายธีระชน มโนวิทย์กิจ
ผู้อำนวยการสำนักงานโยธา

สถาปนิก
นายธีระชน มโนวิทย์กิจ
นายธีระชน มโนวิทย์กิจ

วิศวกรโครงสร้าง
นายธีระชน มโนวิทย์กิจ
นายธีระชน มโนวิทย์กิจ

วิศวกรไฟฟ้า
นายธีระชน มโนวิทย์กิจ
นายธีระชน มโนวิทย์กิจ

วิศวกรสุขาภิบาล
นายธีระชน มโนวิทย์กิจ
นายธีระชน มโนวิทย์กิจ

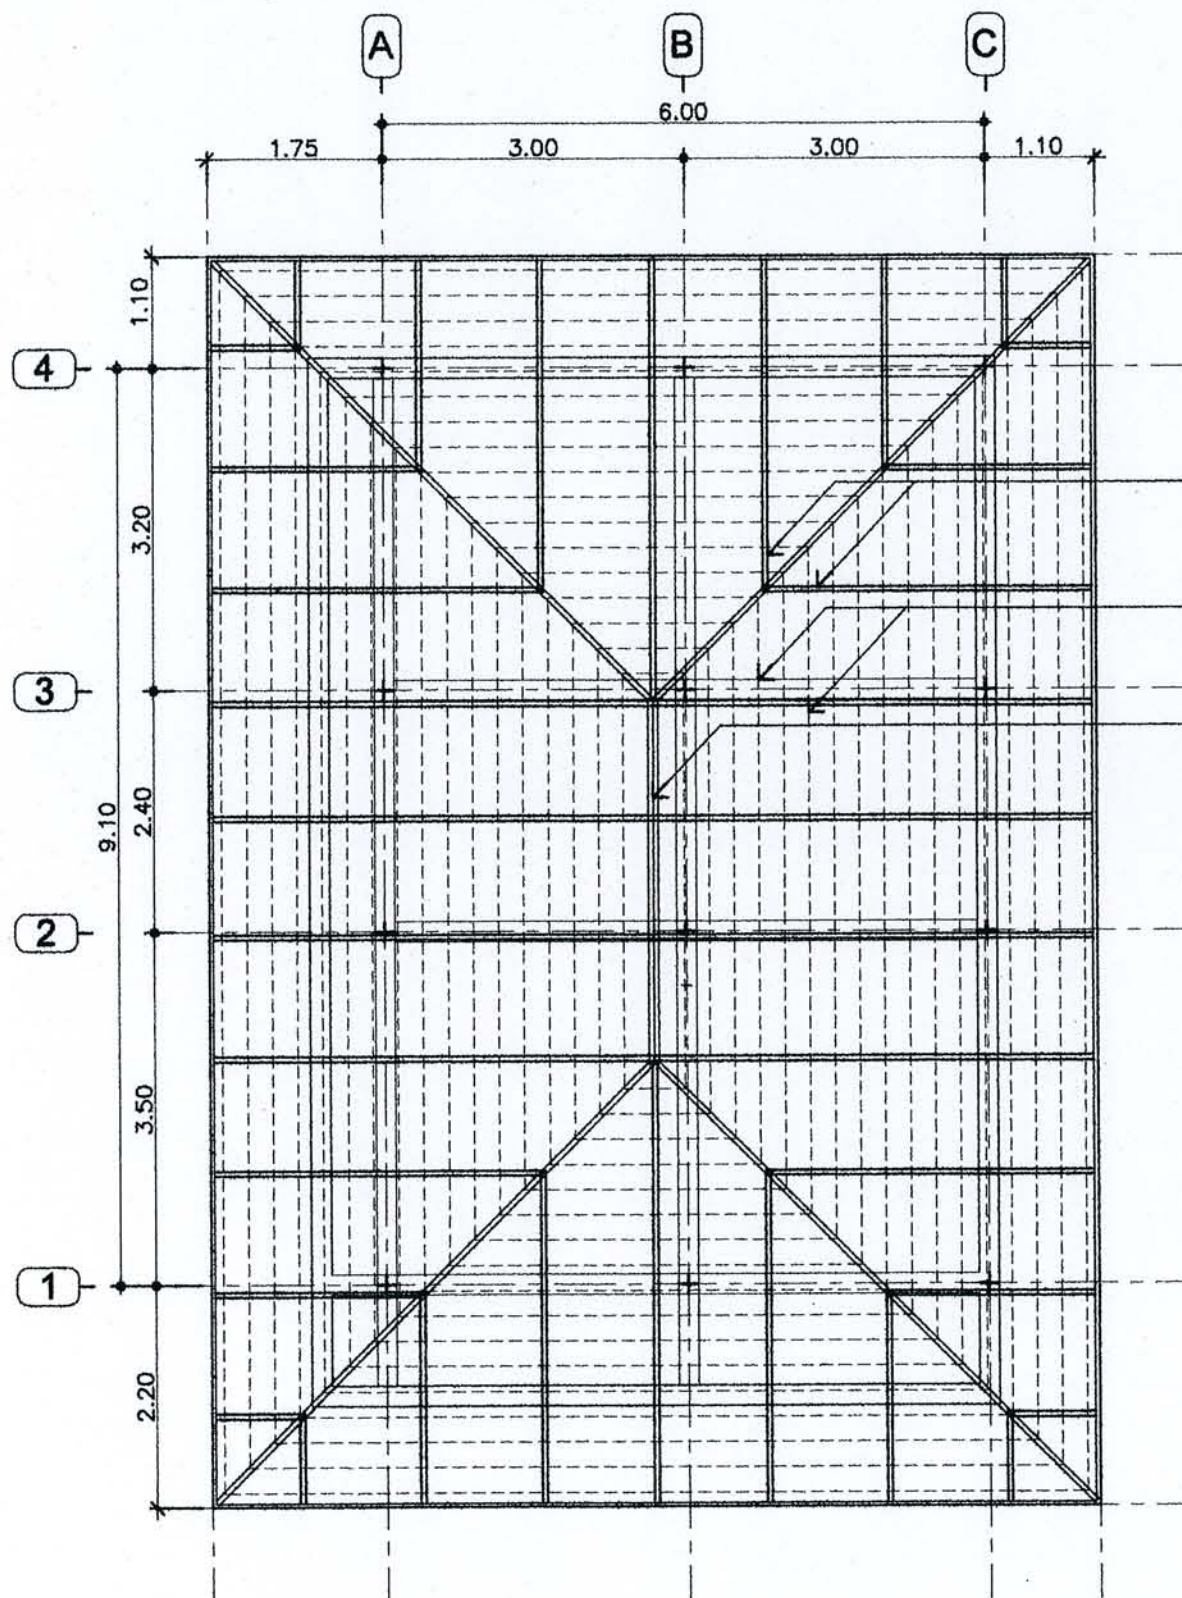

จันทันเหล็ก [-100x50x20x2.3 มม.@ 2.00 ม.

ระแนงเหล็กกล่อ 1"x1"x1.6 มม. @ 30 ซม.

อกไก่เหล็กกล่อ 2[-150x50x20x2.3 มม.

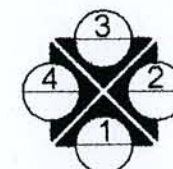

สัญลักษณ์ของรูปด้าน

ผังโครงสร้างหลังคา

มาตราส่วน

1:75



สำนักงาน
กรุงเทพมหานคร

โครงการ
แบบบ้านยืมเพื่อประชาชน

คณบดี

ม.ร.ว.สุจินต์ บริหาร
นายพรเทพ ตรีพิทักษ์ รองคณบดี
นายธีระชัย มโนทัศน์ รองคณบดี
นายพงศ์ศักดิ์ เสน่ห์ดี ปลัดคณบดี

ผู้อำนวยการสำนักงาน

นายจุฑามาศ คำภีร์
รองผู้อำนวยการสำนักงาน
นายทวีศักดิ์ เลิศประพันธ์
ผู้อำนวยการสำนักงาน
นายจตุรงค์ ลินเยี่ยม
ผู้อำนวยการสำนักงาน
นายสินธุ์ชัย บุญปักษ์
ผู้อำนวยการสำนักงาน
นายธีระยุทธ คงสรวิชัย

สถาปนิก

นายสินธุ์ชัย บุญปักษ์
วิศวกร โครงสร้าง

วิศวกรไฟฟ้า

วิศวกรสุขาภิบาล

นางสาวมณฑิรา สมหอม
วิศวกรเครื่องกล

นายช่างเขียนแบบ

นายประยูร อรรถจักร์

แบบ
(024) ธรรมรักษา

เจ้าของ

สถานที่

แบบแสดง
แปลน โครงสร้างหลังคา

ขนาดแผ่น 1:75



FILE : แผ่นที่

วันที่ 2553 S-02

คณบดี ธรรมรักษา

นายประยูร อรรถจักร์ 7

รายการแก้ไขแบบ

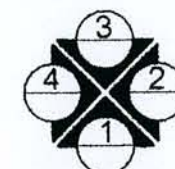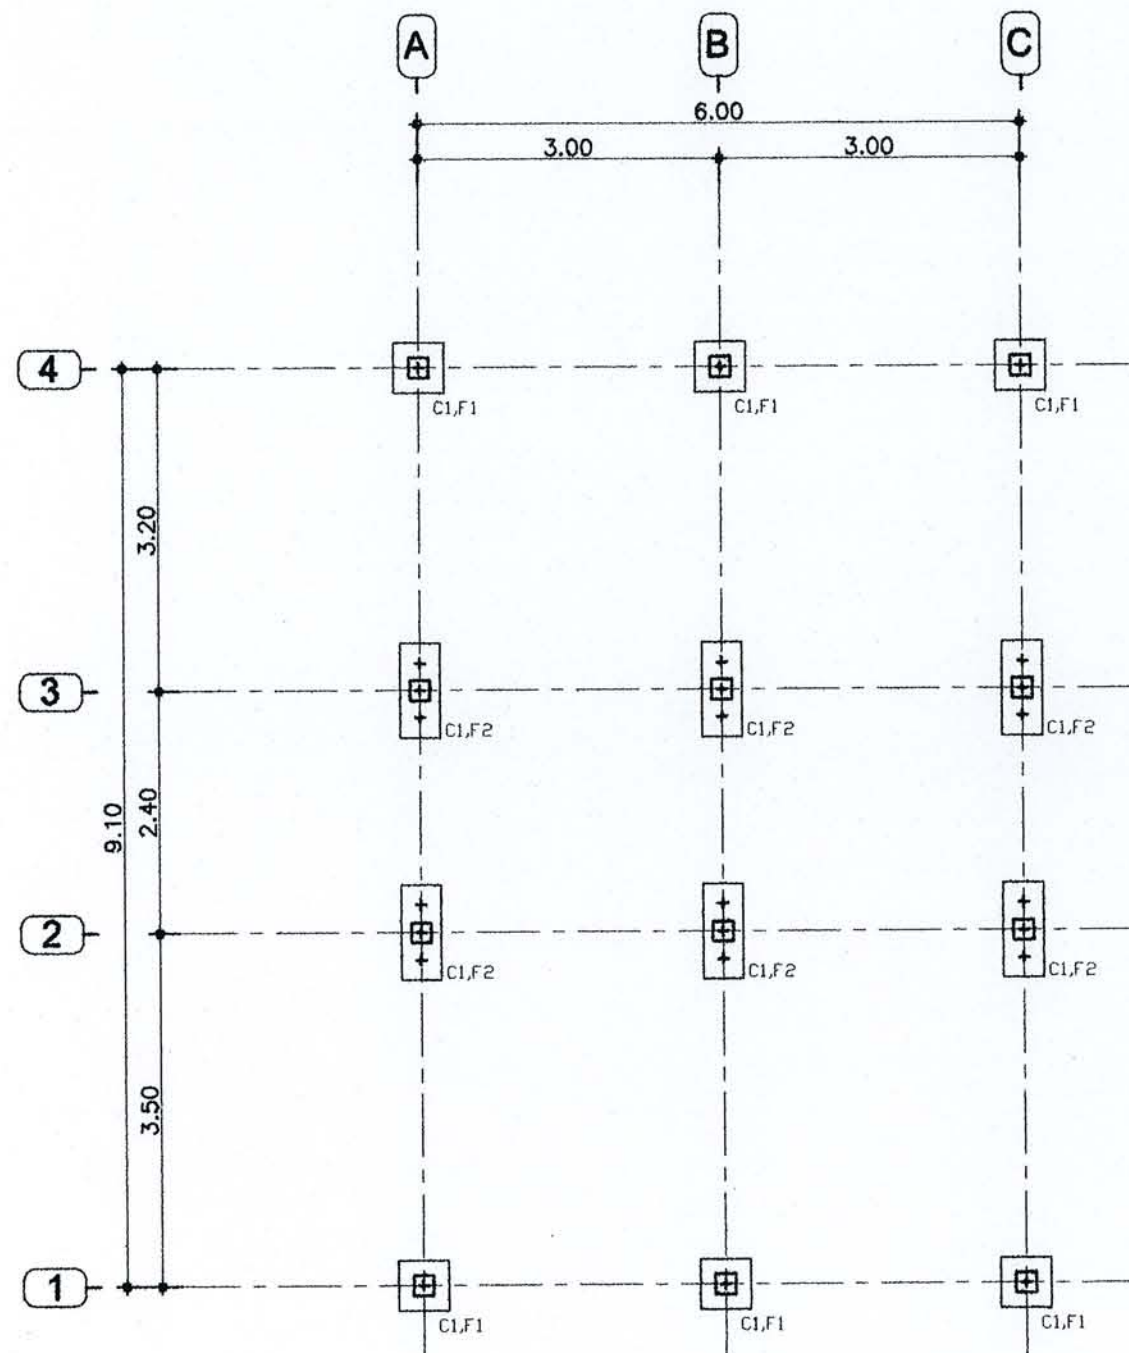

สัญลักษณ์ของรูปด้าน

ผังฐานราก

1:75



สำนักการโยธา
กรุงเทพมหานคร

โครงการ
แบบบ้านยืมเพื่อประชาชน

ตามนโยบาย

ม.ร.ว.สุขุมพันธุ์ ปลัดฯ ผู้ว่าฯ กทม.
นายพรหม เทชะไพฑูรย์ รองผู้ว่าฯ กทม.
นายธีระชน มโนทิม ปลัดฯ รองผู้ว่าฯ กทม.
นายพงศ์ศักดิ์ เสน่ห์วัฒนา ปลัดฯ กทม.

ผู้อำนวยการสำนักการโยธา

นายจุมพล สันกาลาคีรี

รองผู้อำนวยการสำนักการโยธา

นายวิศักดิ์ เลิศประพันธ์

ผู้อำนวยการสำนักงานออกแบบ

นายจตุรงค์ สมเทียม

หัวหน้างานงานสถาปัตย์กรรม

นายสินธุ์ชัย บุญปักษ์

หัวหน้างานงานวิศวกรรม

นายธีระยุทธ คงสวัสดิ์เกียรติ

สถาปนิก

นายสินธุ์ชัย บุญปักษ์

วิศวกร โครงสร้าง

วิศวกร ไฟฟ้า

วิศวกร สุขาภิบาล

นางสาวมณฑิรา สมพยอม

วิศวกรเครื่องกล

นายช่างเขียนแบบ

นายประยูร ธรรมจักร

แบบ

(024) ธรรมจักร

เจ้าของ

สถานที่

แบบแสดง

แปลนฐานราก

มาตราส่วน

1:75

FILE :

วันที่

มีนาคม 2553

ชื่อเอกสาร

แบบแปลน

นายประยูร ธรรมจักร

รายการแก้ไขแบบ


แผ่นที่

S-03

รวมแผ่น

7

รายการแก้ไขแบบ

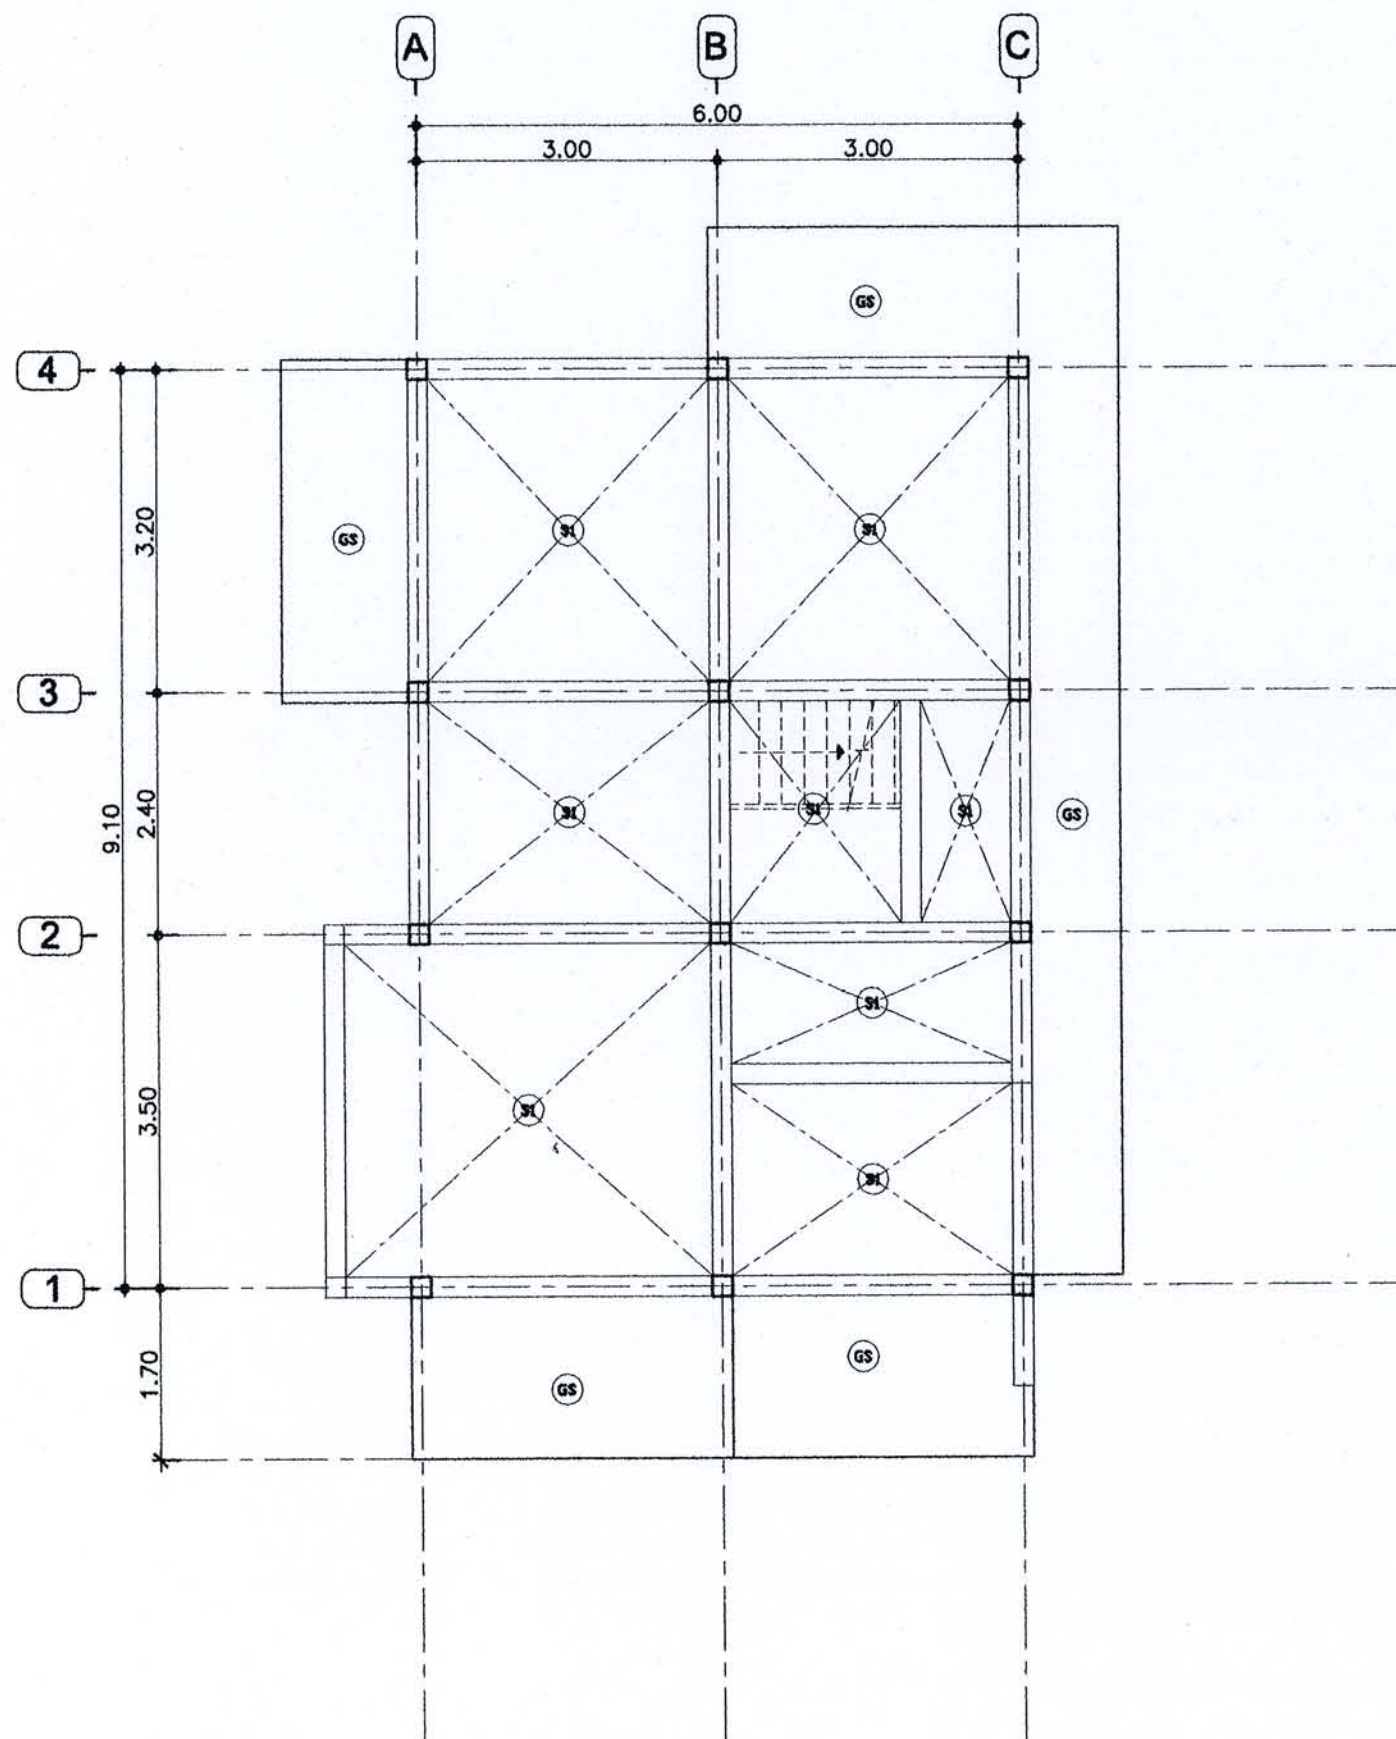

สัญลักษณ์ของรูปด้าน

ผังคานชั้นล่าง
1:75



สำนักงานนโยบาย
กรุงเทพมหานคร

โครงการ
แบบบ้านยิมเพื่อประชาชน

ตามนโยบาย

ม.ร.ว.สุขุมพันธุ์ บริพัตร ผู้ว่าฯ กทม.
นายพรเทพ เศรษฐ์ใหญ่ รองผู้ว่าฯ กทม.
นายธีระชน มโนทิตะกุล รองผู้ว่าฯ กทม.
นายพงศ์ศิวัช สอนัดดี ปลัดฯ กทม.

ผู้อำนวยการสำนักงานนโยบาย

นายจุมพล สันกาลาด

รองผู้อำนวยการสำนักงานนโยบาย

นายทวีศักดิ์ เดชประพันธ์

ผู้อำนวยการสำนักงานออกแบบ

นายจตุรงค์ สอนัดดี

หัวหน้างานควบคุมอาคาร

นายสินธุ์ชัย บุญปักษ์

หัวหน้างานควบคุมอาคาร

นายธีระยุทธ คงสวัสดิ์ชัย

สถาปนิก

นายสินธุ์ชัย บุญปักษ์

วิศวกรโครงสร้าง

วิศวกรไฟฟ้า

วิศวกรสุขาภิบาล

นางสาวณัชชา สมพยอม

วิศวกรโยธา

นายช่างเขียนแบบ

นายประจักษ์ ธรรมจักร

แบบ

(024) ธรรมจักร

เจ้าของ

สถานที่

แบบแสดง

ผังคานชั้นล่าง

มาตราส่วน 1:75

FILE :

วันที่ มิถุนายน 2553



โครงการบ้านยิม

นายประจักษ์ ธรรมจักร

แผ่นที่ S-04

รวมแผ่น 7

รายการแก้ไขแบบ

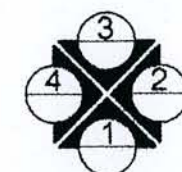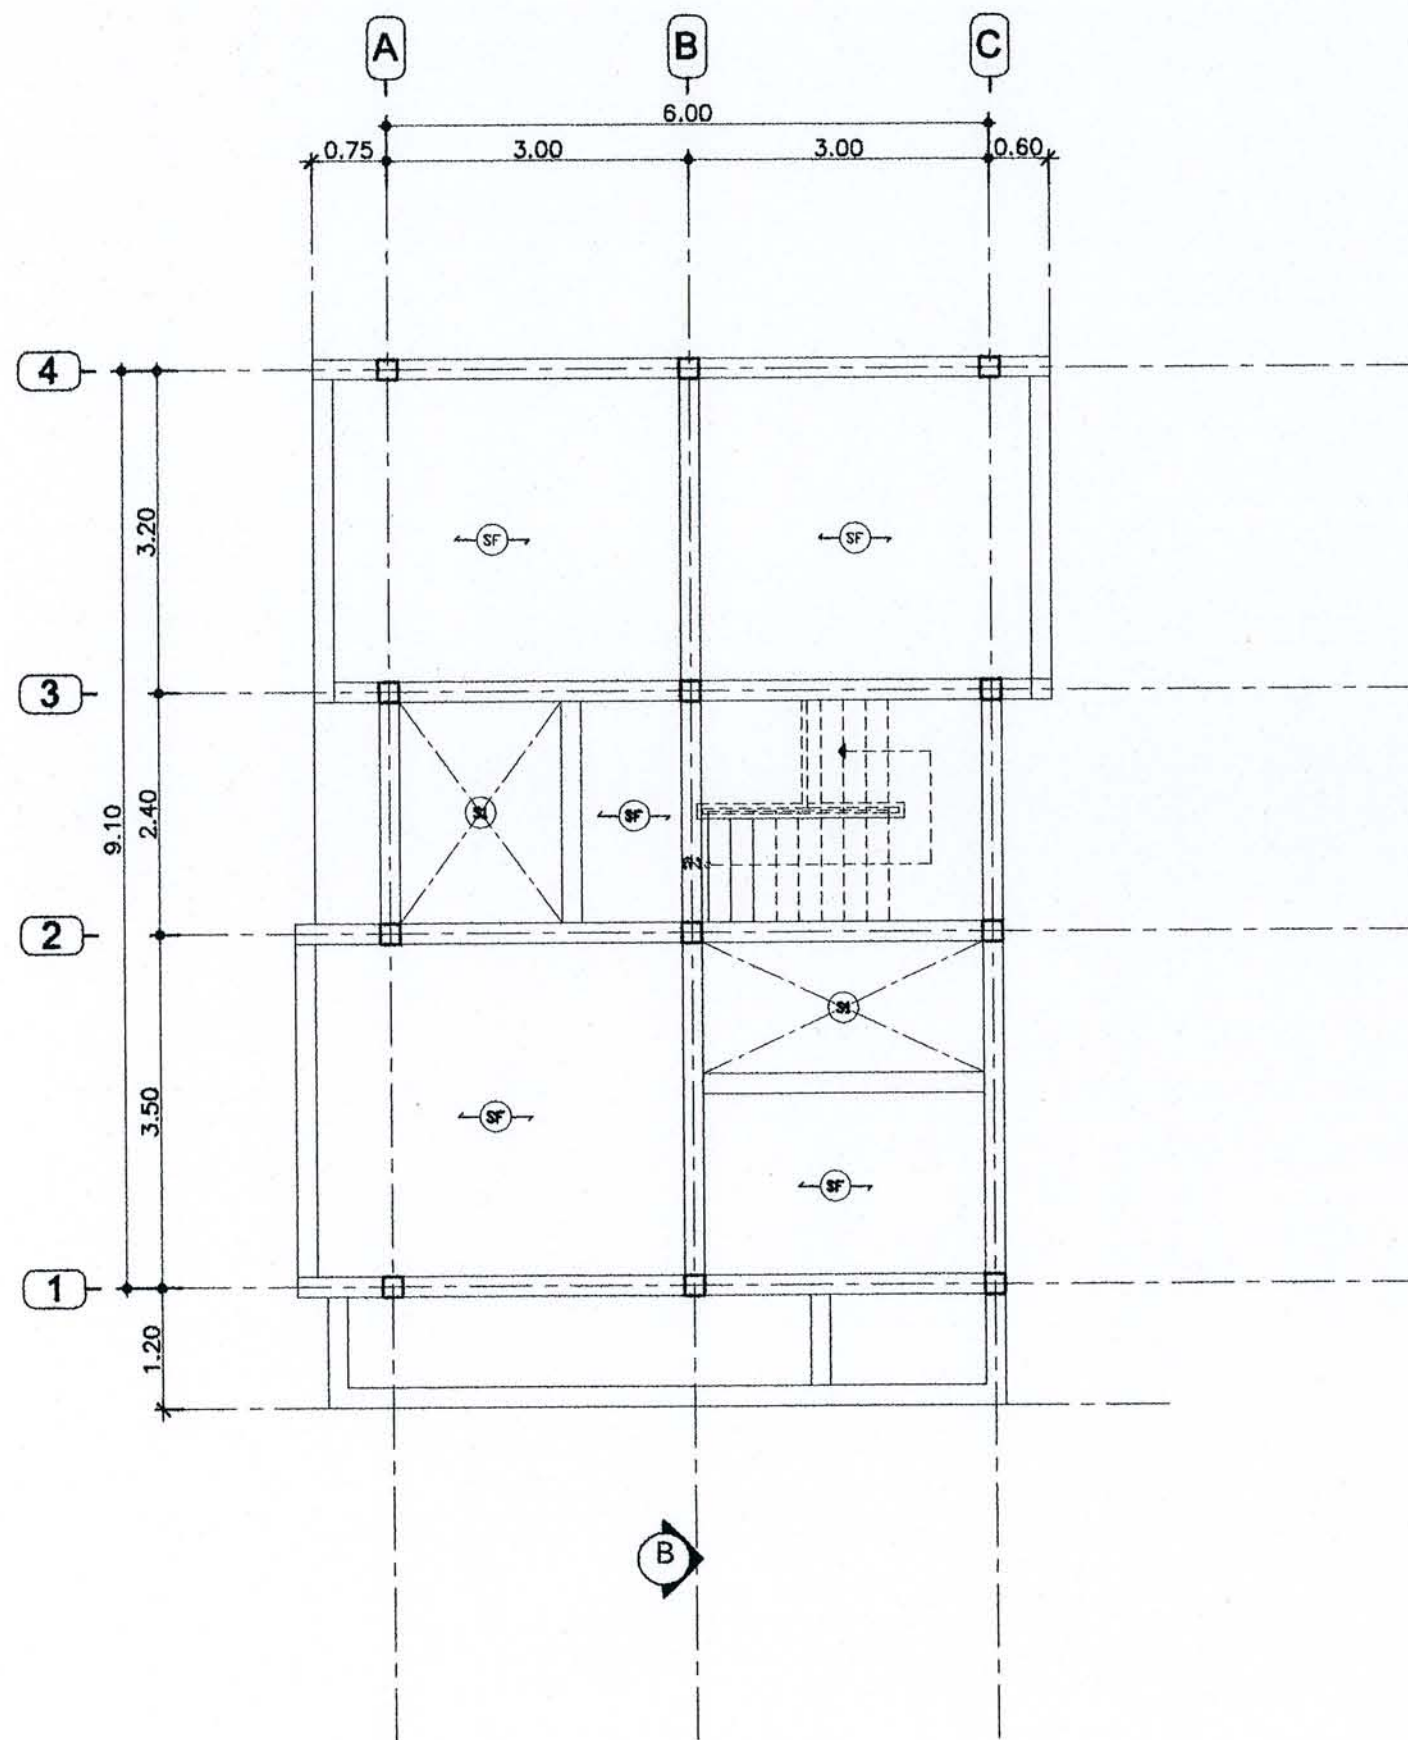

สัญลักษณ์มองรูปด้าน

ผังคานชั้นบน
มาตราส่วน 1:75



สำนักงานโยธา
กรุงเทพมหานคร

โครงการ
แบบบ้านยืมเพื่อประชาชน

ตามนโยบาย

ม.ร.ว.สุขุมพันธุ์ บริพัตร ผู้ว่าฯกทม.
นายพรเทพ เศรษฐกิจ รองผู้ว่าฯกทม.
นายธีระชน มโนวิทย์กิจ รองผู้ว่าฯกทม.
นายพงษ์ศักดิ์ แสนเพ็ญ ปลัดฯกทม.

ผู้อำนวยการสำนักงานโยธา

นายจุมพล สันภาพล

รองผู้อำนวยการสำนักงานโยธา

นายทวีศักดิ์ เลิศประพันธ์

ผู้อำนวยการสำนักงานออกแบบ

นายจตุรงค์ สันติธรรม

หัวหน้างานสถาปัตย์

นายสินธุ์ชัย บุญปักษ์

หัวหน้างานวิศวกรรม

นายธีระยุทธ คงสวัสดิ์

สถาปนิก

นายสินธุ์ชัย บุญปักษ์

วิศวกรโครงสร้าง

วิศวกรไฟฟ้า

วิศวกรสุขาภิบาล

นางสาวมณฑิรา สมพยอม

วิศวกรเครื่องกล

นายช่างเขียนแบบ

นายประยูร อรรถจักร์

แบบ (024) ธรรมรักษา

เจ้าของ

สถานที่

แบบแสดง

ผังคานชั้นสอง

มาตราส่วน 1:75

FILE : 000000

วันที่ 2553

ออกแบบโดย

นายประยูร อรรถจักร์

รายการแก้ไขแบบ



สำนักงาน
กรุงเทพมหานคร

โครงการ
แบบบ้านยืมเพื่อประชาชน

คานบดโยน

น.ร.สุเมธพันธ์ วิจิตร ผู้ว่าฯ
นายพรเทพ เศรษฐกิจ รองผู้ว่าฯ
นายธีระธรณ์ นนทบุรี รองผู้ว่าฯ
นายพงศ์ศักดิ์ แสนโคตร ปลัดฯ

ผู้อำนวยการสำนักงานโยธา

นายจุมพล คำภา

รองผู้อำนวยการสำนักงานโยธา

นายทวีศักดิ์ เลิศประพันธ์

ผู้อำนวยการสำนักงานออกแบบ

นายจตุรงค์ สอนิยม

ผู้อำนวยการงานสถาปัตยกรรม

นายสินธุ์ชัย บุญปักษ์

ผู้อำนวยการงานวิศวกรรม

นายธีระยุทธ คงสวัสดิ์

สถาปนิก

นายสินธุ์ชัย บุญปักษ์

วิศวกรโครงสร้าง

วิศวกรไฟฟ้า

วิศวกรสุขาภิบาล

นางสาวณัฏฐา สมพยอม

วิศวกรเครื่องกล

นายช่างเขียนแบบ

นายประจักษ์ อรรถจักร์

แบบ
(024) อรรถจักร์

เจ้าของ

สถานที่

แบบแสดง
แปลนพื้นที่ชั้นล่าง

มาตราส่วน 1:20

FILE : S-06



วันที่ 2553

คณบดี


นายประจักษ์ อรรถจักร์

7


รายการแก้ไขแบบ

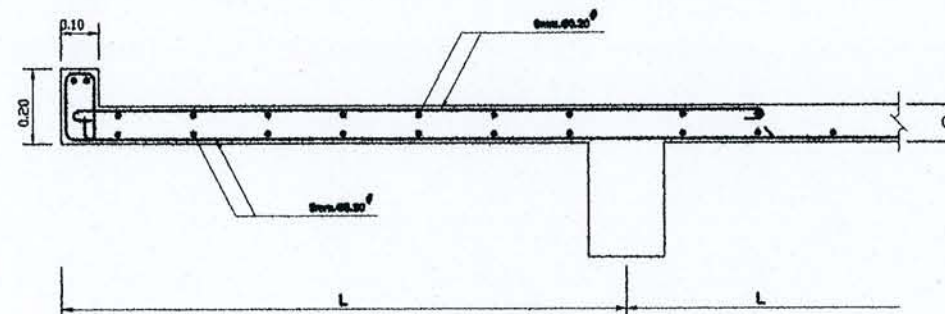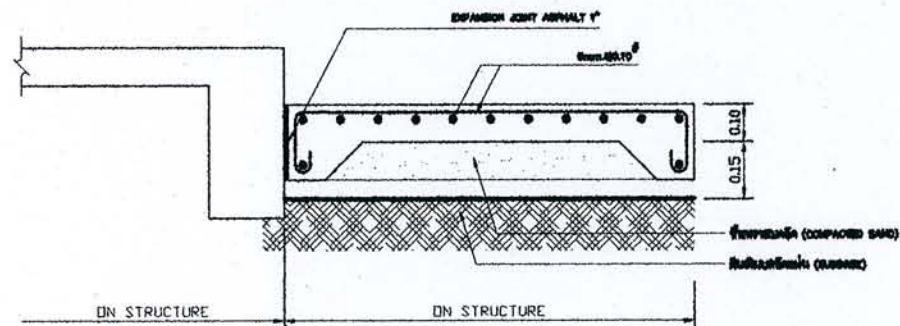


SB

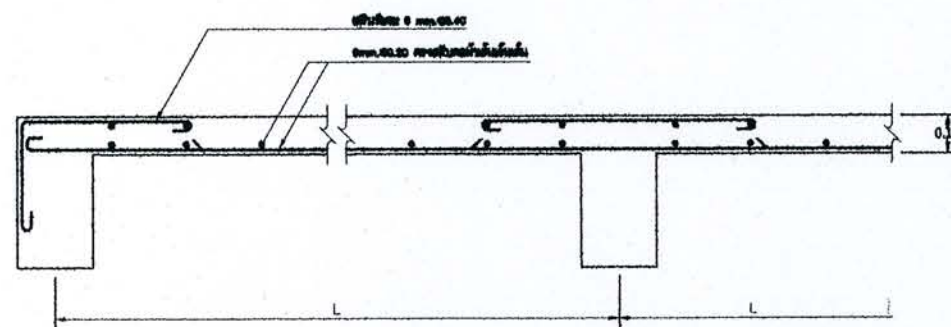


S1

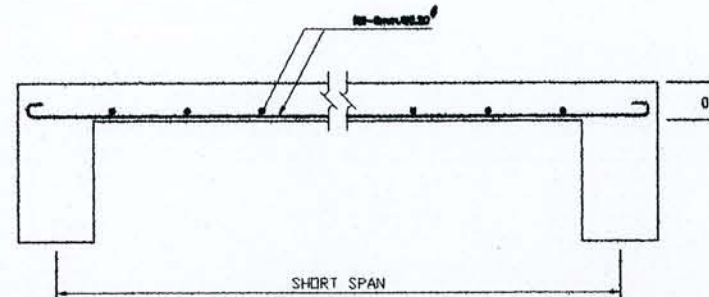


S2

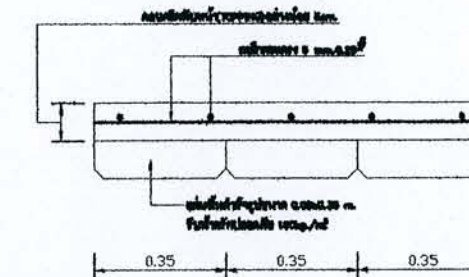


PS

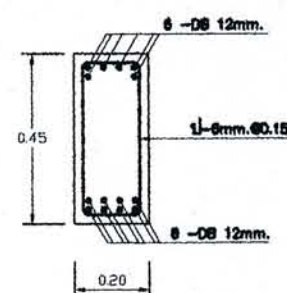


B1

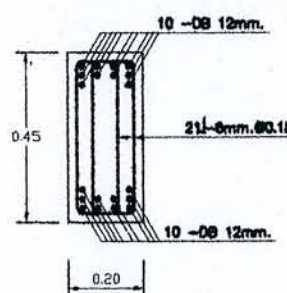


B2

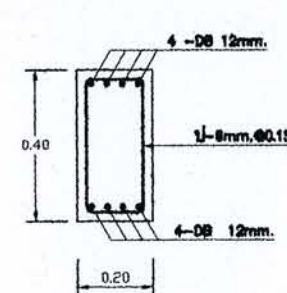


B2'

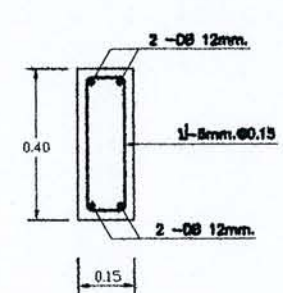


B3

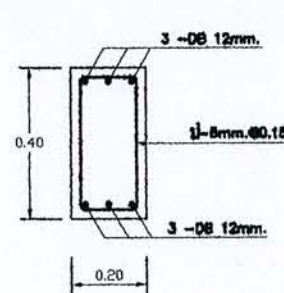


B4

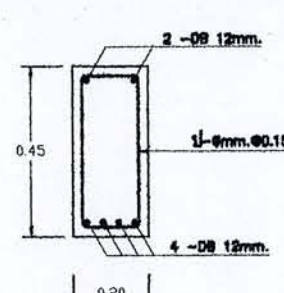


B5

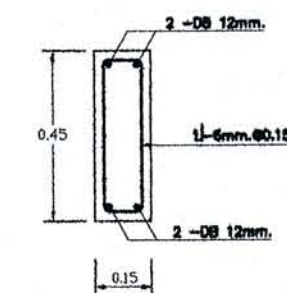


B6

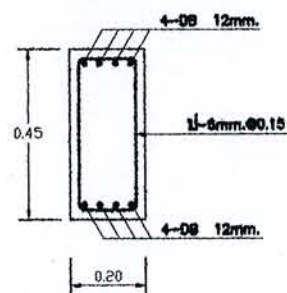


B7

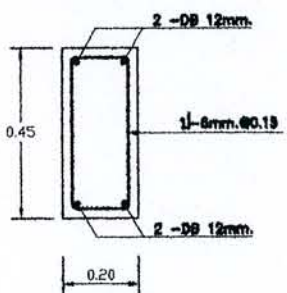


B8

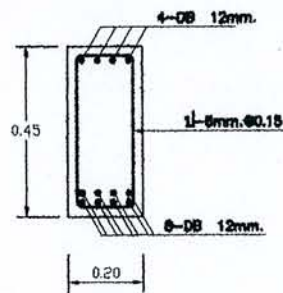


B9

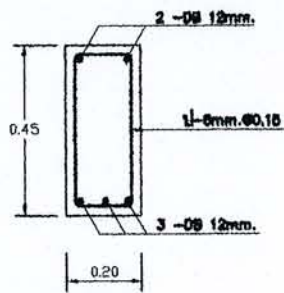


RB1

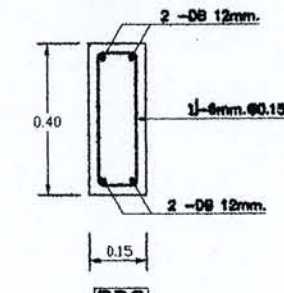


RB2

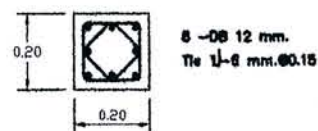


?????

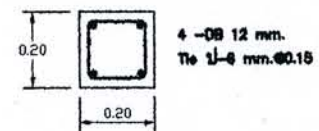


?????

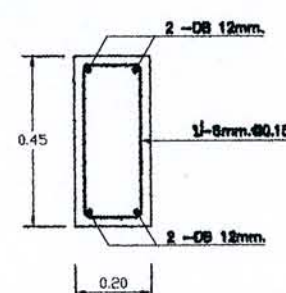

A - A

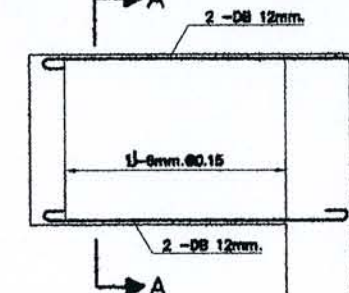


RB'

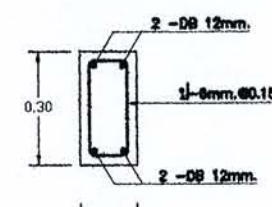


RB3


แบบขยายพื้น คานเสา
มาตราส่วน 1:20

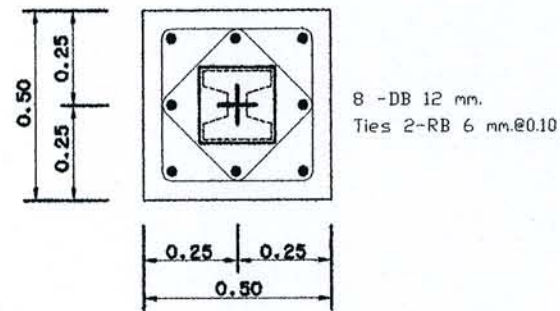


PLAN
SCALE 1 : 20

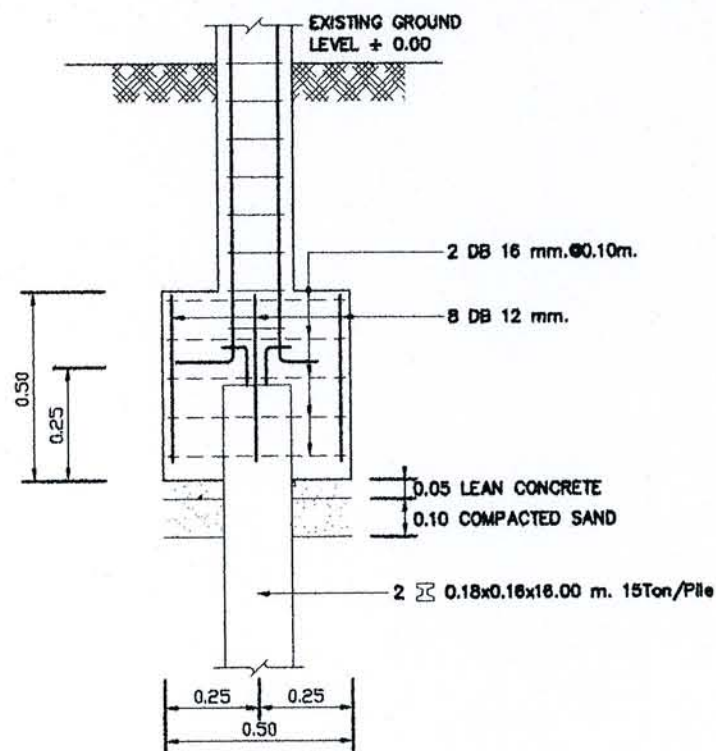

FOOTING " F1"
SCALE 1 : 20

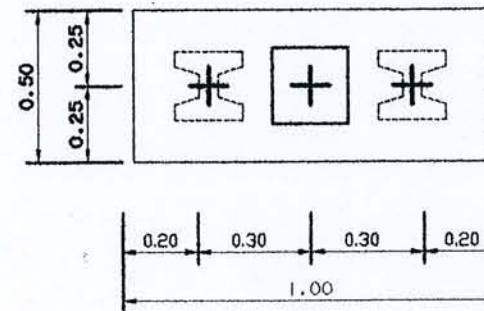

PLAN
SCALE 1 : 20

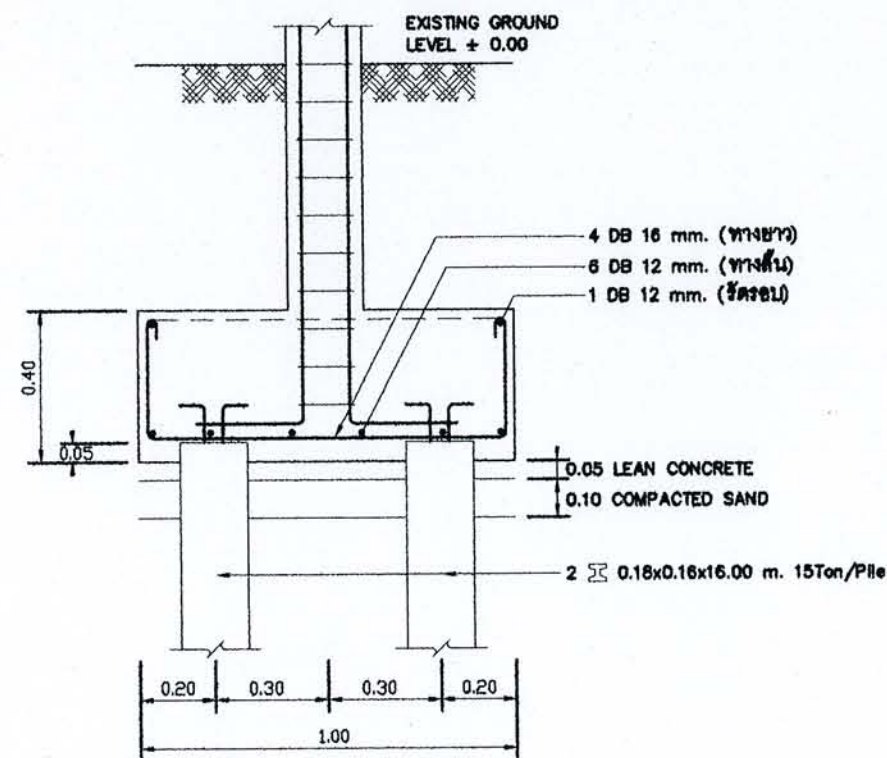

FOOTING " F2"
SCALE 1 : 20



สำนักงาน
กรุงเทพมหานคร

โครงการ
แบบบ้านยืมเพื่อประชาชน

ตามนโยบาย

ม.ร.ว.สุขุมพันธุ์ บริพัตร ผู้ว่าฯกทม.
นายทรงยศ เทระปญโญ รองผู้ว่าฯกทม.
นายธีระชน มโนวิทย์กิจ รองผู้ว่าฯกทม.
นายพงศ์ศิวัช วัฒนสินธุ์ ปลัดฯกทม.

ผู้อำนวยการสำนักงาน

นายจุมพล สว่างพล

รองผู้อำนวยการสำนักงาน

นายทวีศักดิ์ เลิศประพันธ์

ผู้อำนวยการสำนักงานออกแบบ

นายจตุรงค์ สมนิยม

หัวหน้างานสถาปัตย์

นายสินธุ์ชัย บุญปักษ์

หัวหน้างานวิศวกรรม

นายธีระยุทธ คงสวัสดิ์เกียรติ

สถาปนิก

นายสินธุ์ชัย บุญปักษ์

วิศวกรโครงสร้าง

วิศวกรไฟฟ้า

วิศวกรสุขาภิบาล

นางสาวณณจิรา สมหอม

วิศวกรเครื่องกล

นายช่างเขียนแบบ

นายประจักษ์ อรรถจักร์

แบบ (024) ธรรมชาติ

เจ้าของ

สถานที่

แบบแสดง

แปลนพื้นที่ชั้นล่าง

มาตราส่วน 1:20

FILE : S-07

วันที่ 2553

ออกแบบโดย

นายประจักษ์ อรรถจักร์

รวมแผ่น 7

รายการแก้ไขแบบ



สำนักงานโยธา
กรุงเทพมหานคร

โครงการ
แบบบ้านยืมเพื่อประชาชน

ตามนโยบาย

ม.ร.ว.สุขุมพันธุ์ บริพัตร ผู้ว่าฯกทม.
นายพรเทพ พรระโทธรย์ รองผู้ว่าฯกทม.
นายธีระชน มโนชัยพิบูลย์ รองผู้ว่าฯกทม.
นายพงศ์ศักดิ์ แสนสุทนต์ ปลัดฯกทม.

ผู้อำนวยการสำนักงานโยธา

นายจุมพล สันภาพล

รองผู้อำนวยการสำนักงานโยธา

นายทวีศักดิ์ เลิศประพันธ์

ผู้อำนวยการสำนักงานออกแบบ

นายจตุรงค์ สันเยี่ยม

หัวหน้างานสถาปัตยกรรม

นายสินธุ์ชัย บุญปักษ์

หัวหน้างานวิศวกรรม

นายธีระยุทธ คงสรวิศเคียร

สถาปนิก

นายสินธุ์ชัย บุญปักษ์

วิศวกรโครงสร้าง

วิศวกรไฟฟ้า


วิศวกรสุขาภิบาล

นางสาวมณีนีรา สมนาคม

วิศวกรเครื่องกล

นายช่างเขียนแบบ

นายประยูร ธรรมจักร

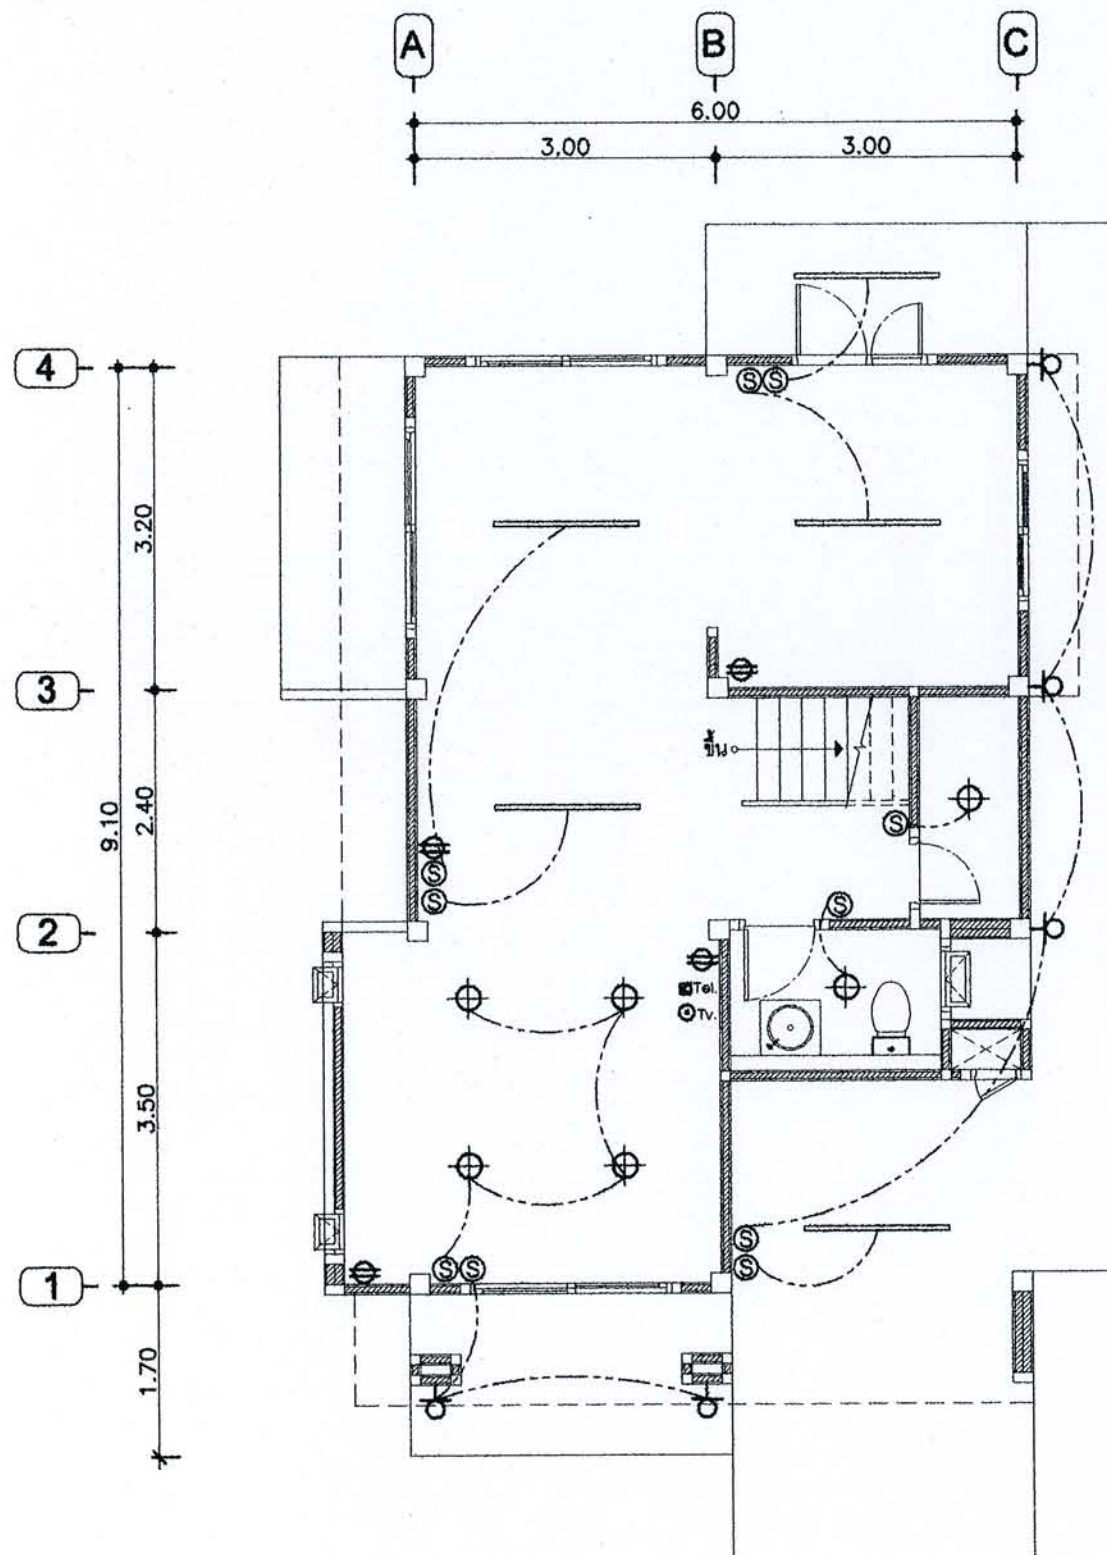

**หมายเหตุ ระดับความสูงที่กำหนดจากความสูงของพื้นห้อง

ผังไฟฟ้าชั้นล่าง

มาตราส่วน

1 : 75



สำนักงานสาธารณสุข
กรุงเทพมหานคร

โครงการ
แบบบ้านยิมเพื่อประชาชน

ตามนโยบาย

ม.ร.ว.สุขุมพันธุ์ บริพัตร ผู้ว่าฯกทม.
นายแพทย์ เสรฐภไพฑูรย์ รองผู้ว่าฯกทม.
นายธีระชน มโนวิทย์กุลชัย รองผู้ว่าฯกทม.
นายแพทย์ศิริชัย เกียรติถาวรกุล ปลัดฯกทม.

ผู้อำนวยการสำนักงานสาธารณสุข

นายจุมพล ล้ำกาฬ

รองผู้อำนวยการสำนักงานสาธารณสุข

นายทวีศักดิ์ เลิศประพันธ์

ผู้อำนวยการสำนักงานออกแบบ

นายจตุรงค์ สันติธรรม

หัวหน้างานสถาปัตยกรรม

นายสินธุ์ชัย บุญปักษ์

หัวหน้างานวิศวกรรม

นายธีระยุทธ คงสวัสดิ์เกียรติ

สถาปนิก

นายสินธุ์ชัย บุญปักษ์

วิศวกรโครงสร้าง

วิศวกรไฟฟ้า


วิศวกรสุขาภิบาล

นางสาวณัฏฐา สมพยอม

วิศวกรเครื่องกล

นายช่างเขียนแบบ

นายประจักษ์ อรรถจักร์

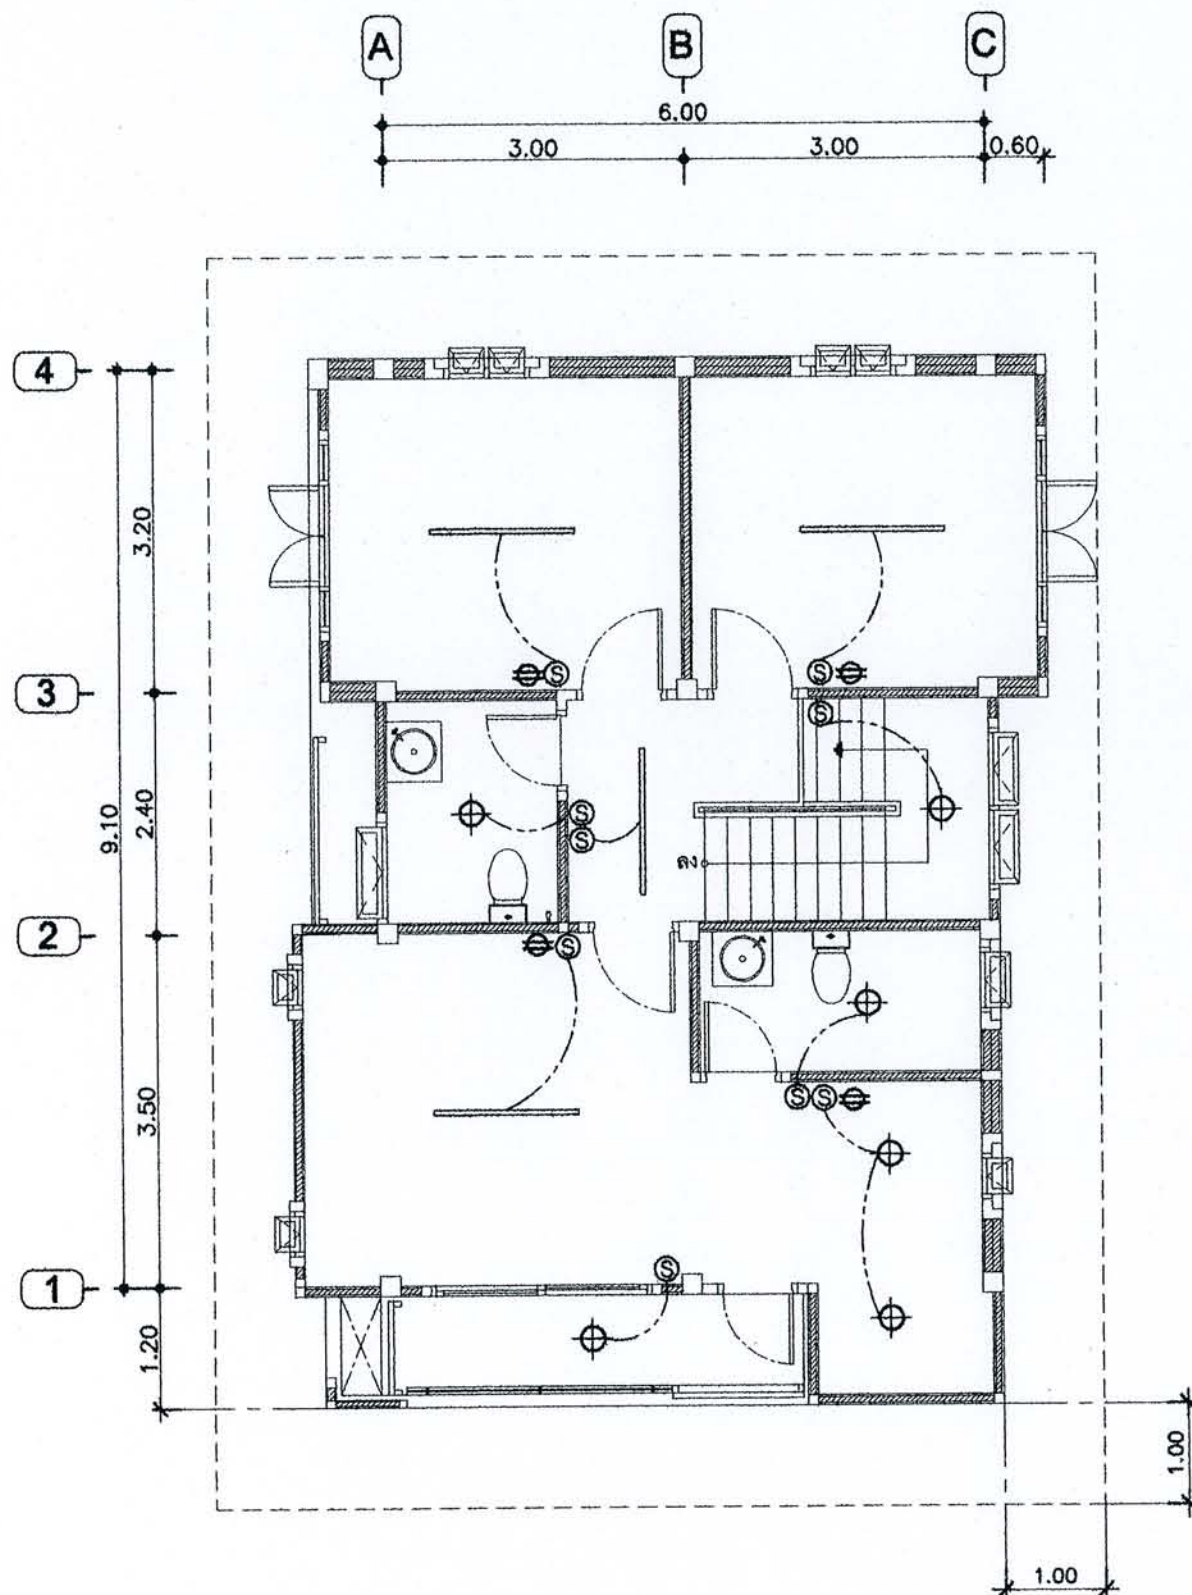


**หมายเหตุ ระดับความสูงฝ้ากำหนดจากความสูงของพื้นห้อง

ผังไฟฟ้าชั้นบน

มาตราส่วน

1 : 75

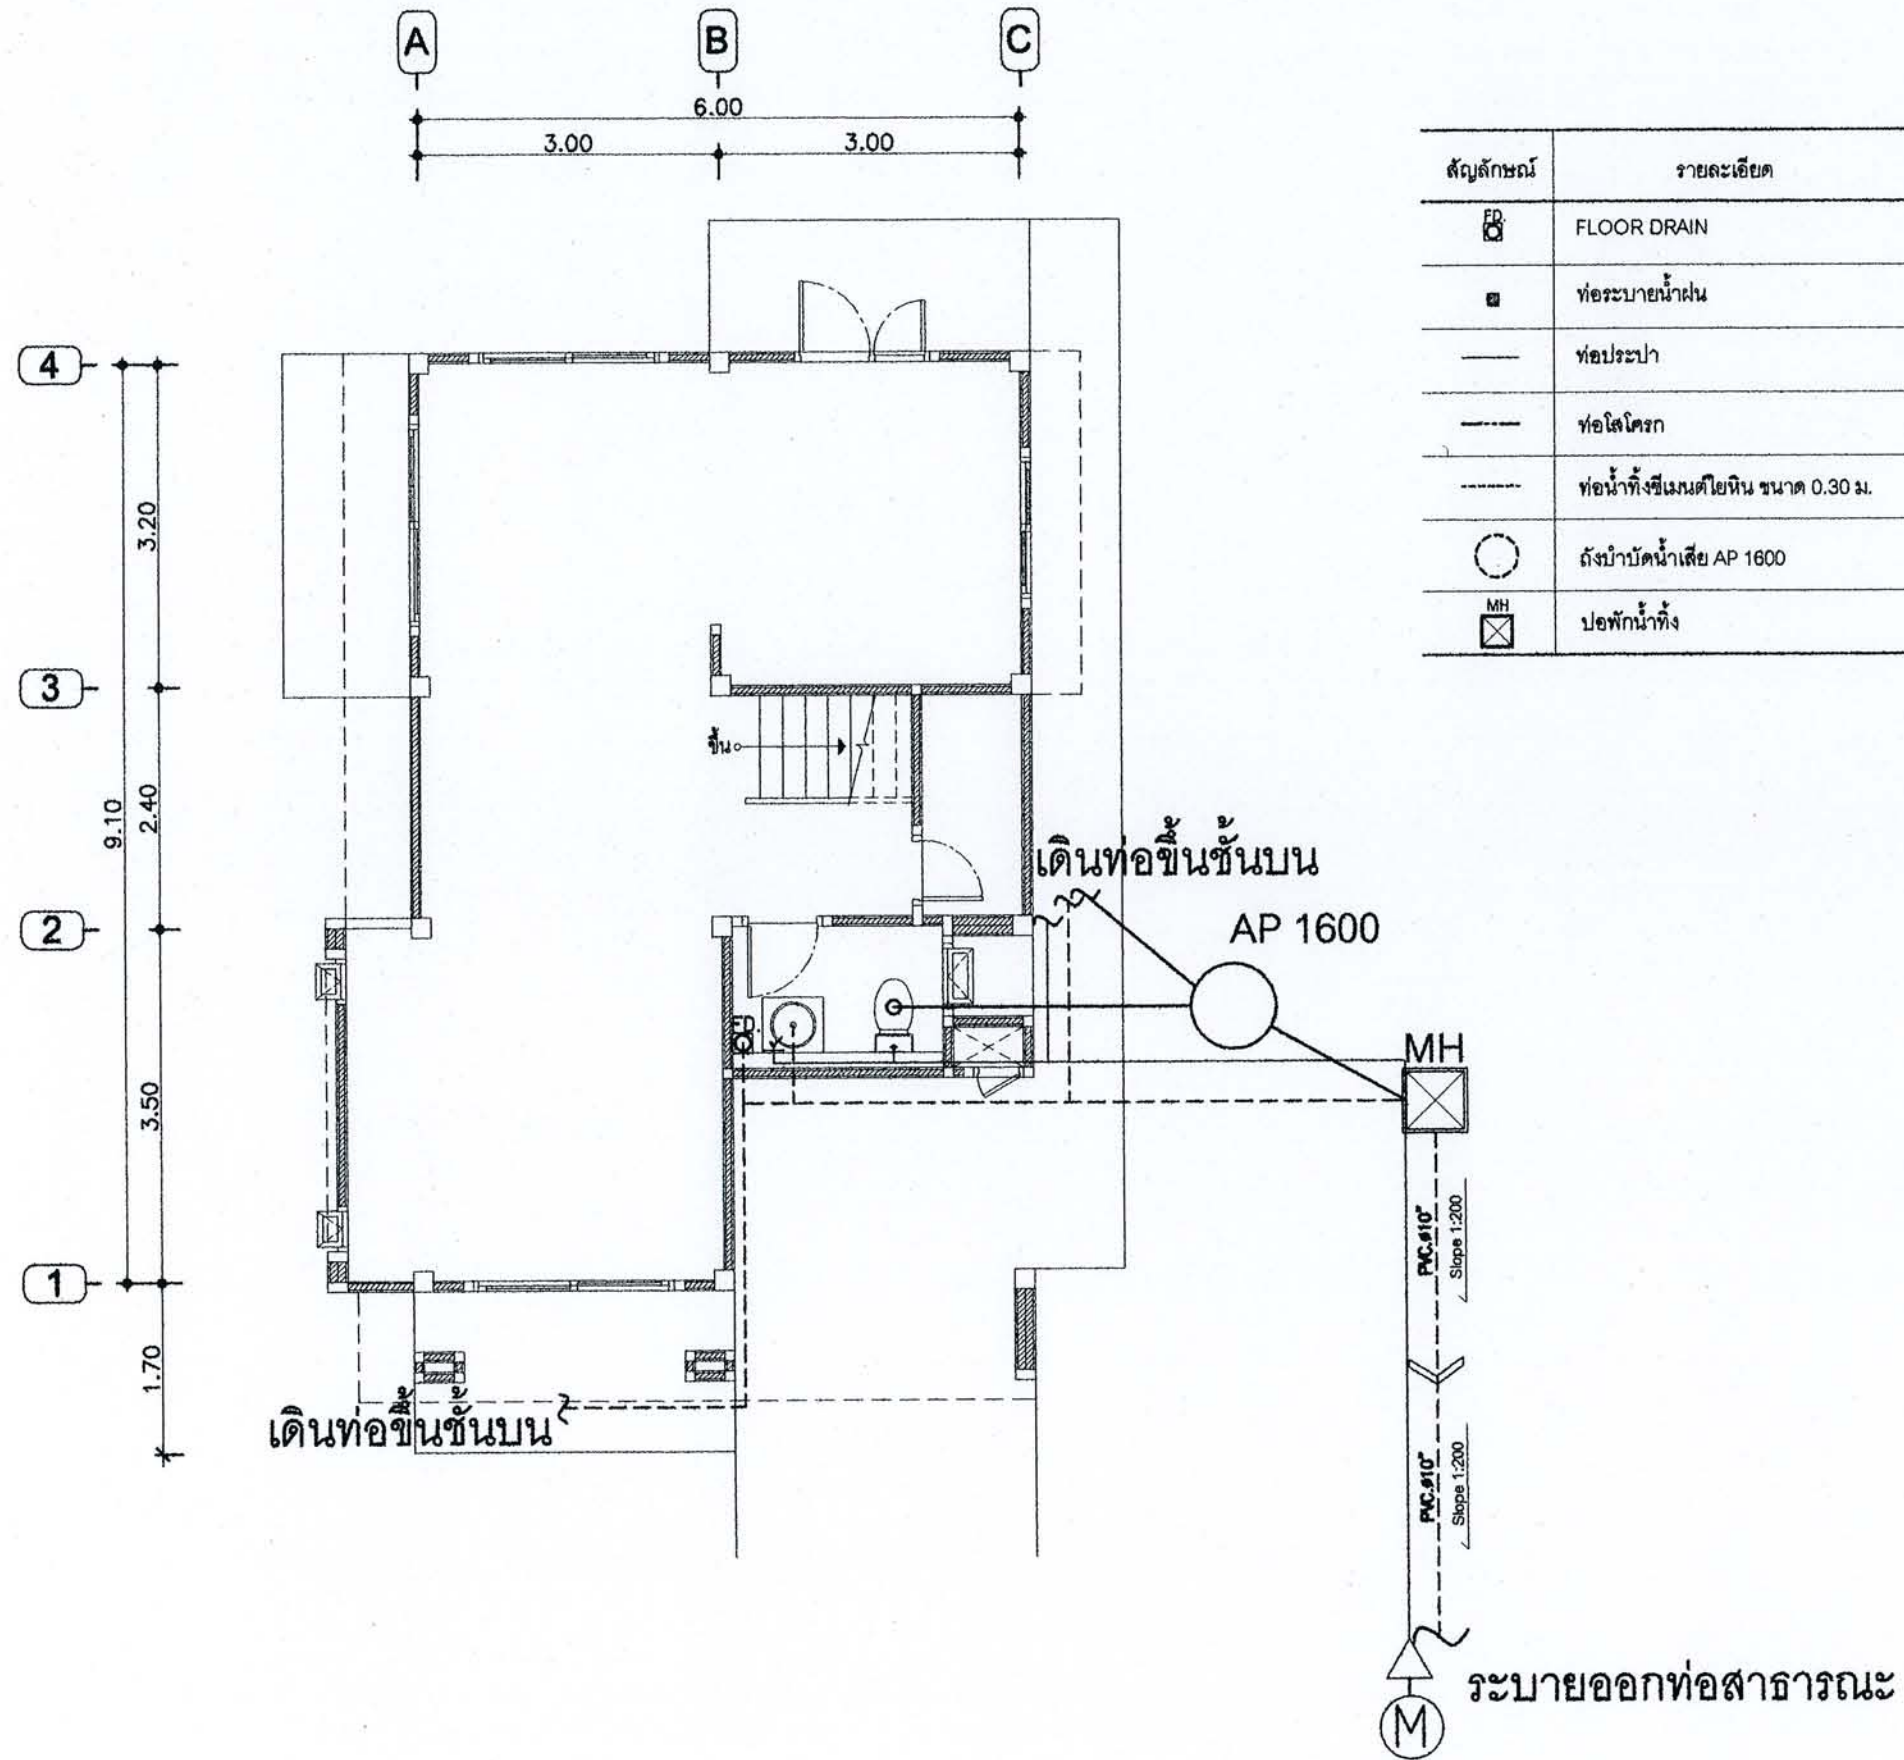

ผังสุขาภิบาลชั้นล่าง

มาตราส่วน

1:75



สำนักงานสาธารณสุข
กรุงเทพมหานคร

โครงการ
แบบบ้านยืมเพื่อประชาชน

ตามนโยบาย

ม.ร.ว.สุขุมพันธุ์ บริพัตร ผู้ว่าฯกทม.
นายแพทย์ เหว่นโพธิ์ รองผู้ว่าฯกทม.
นายธีระชน มโนวิทย์กุล รองผู้ว่าฯกทม.
นายพงศ์ศักดิ์ แสนสุทนต์ ปลัดฯกทม.

ผู้อำนวยการสำนักงาน

นายจุมพล สว่างพล

รองผู้อำนวยการสำนักงาน

นายทวีศักดิ์ เลิศประพันธ์

ผู้อำนวยการสำนักงานออกแบบ

นายจตุรงค์ สอนเนียม

หัวหน้ากลุ่มงานสถาปัตยกรรม

นายสินธุ์ชัย บุญปักษ์

หัวหน้ากลุ่มงานวิศวกรรม

นายธีระบุท คังสรณ์เดียร

สถาปนิก

นายสินธุ์ชัย บุญปักษ์

วิศวกรโครงสร้าง

วิศวกรไฟฟ้า

วิศวกรสุขาภิบาล

นางสาวฉวีมา ชื่นหอม

วิศวกรโยธา

นายช่างเขียนแบบ

นายประจักษ์ ธรรมจักร

แบบ
(024) ธรรมจักร

เจ้าของ

สถานที่

แบบแสดง
แปลนสุขาภิบาลชั้นล่าง

มาตราส่วน 1:75

FILE :

วันที่ มิถุนายน 2553

โครงการบ้านยืม

นายประจักษ์ ธรรมจักร

รายการแก้ไขแบบ

หน้า

4



สำนักงานโยธา
กรุงเทพมหานคร

โครงการ
แบบบ้านยิมเพื่อประชาชน

ตามนโยบาย

น.อ.สุรพันธ์ ปิณฑะ ผู้ว่าฯกทม.
นายพรเทพ ธรรมโศภณ รองผู้ว่าฯกทม.
นายธีระชน มโนวิมลบุตร รองผู้ว่าฯกทม.
นายพงษ์ศักดิ์ แสนลำดัย ปลัดฯกทม.

ผู้อำนวยการสำนักงานโยธา
นายจุมพล คำภาพล
รองผู้อำนวยการสำนักงานโยธา
นายทวีศักดิ์ เดชประพันธ์
ผู้อำนวยการสำนักงานออกแบบ
นายจตุรงค์ สอนเนียม
หัวหน้ากลุ่มงานสถาปัตยกรรม
นายสินธุ์ชัย บุญปักษ์
หัวหน้ากลุ่มงานวิศวกรรม
นายธีระยุทธ คงสวัสดิ์ชัย

สถาปนิก
นายสินธุ์ชัย บุญปักษ์

วิศวกรโครงสร้าง

วิศวกรไฟฟ้า

วิศวกรสุขาภิบาล

นางสาวณณจิรา สมทอง

วิศวกรเครื่องกล

นายช่างเขียนแบบ

นายประยูร อรรถจักร์

แบบ
(024) อรรถจักร์

เจ้าของ

สถานที่

แบบแสดง
แปลนสุขาภิบาลชั้นสอง

มาตราส่วน 1:75

FILE :

วันที่ มิถุนายน 2553


ชื่อเอกสารแบบ

นายประยูร อรรถจักร์

รายการแก้ไขแบบ

หน้า


4

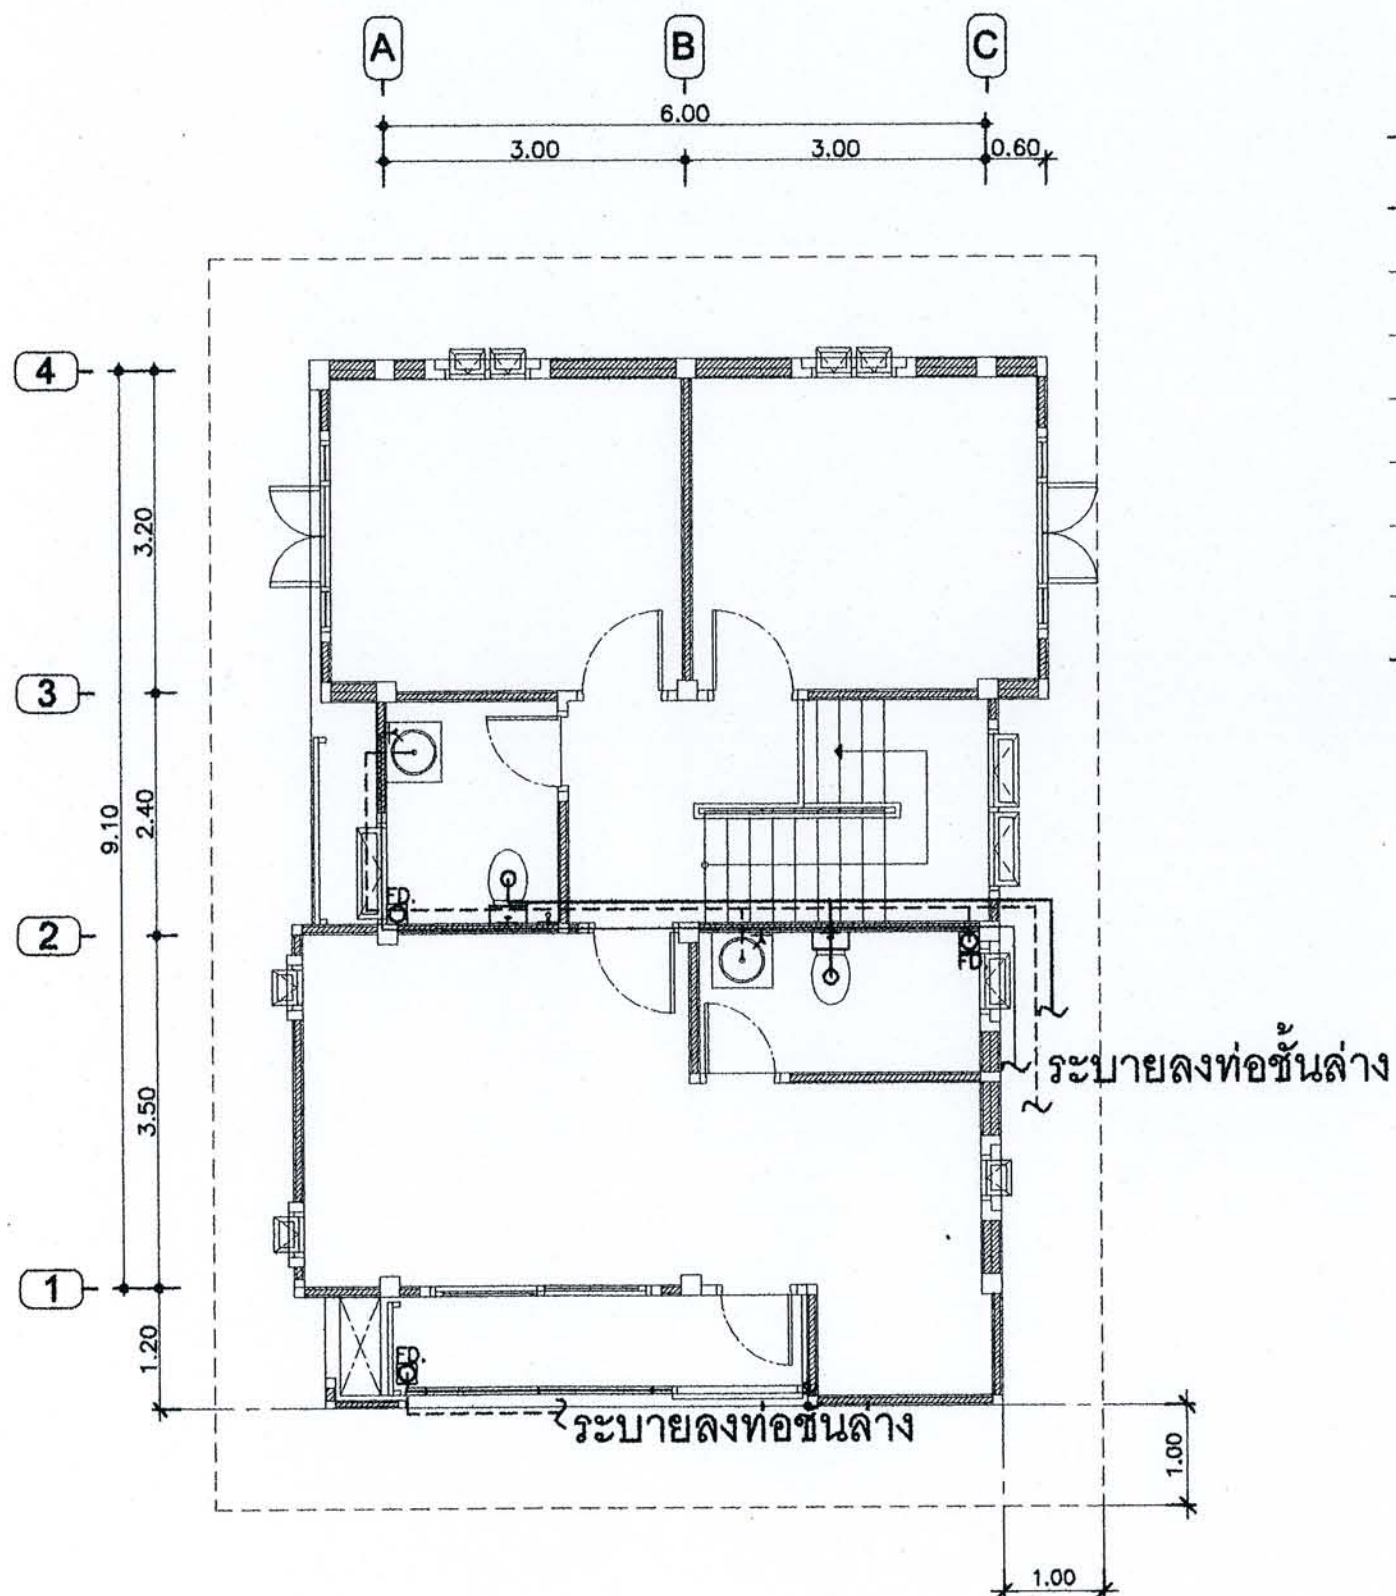

ผังสุขาภิบาลชั้นบน


มาตราส่วน

1:75

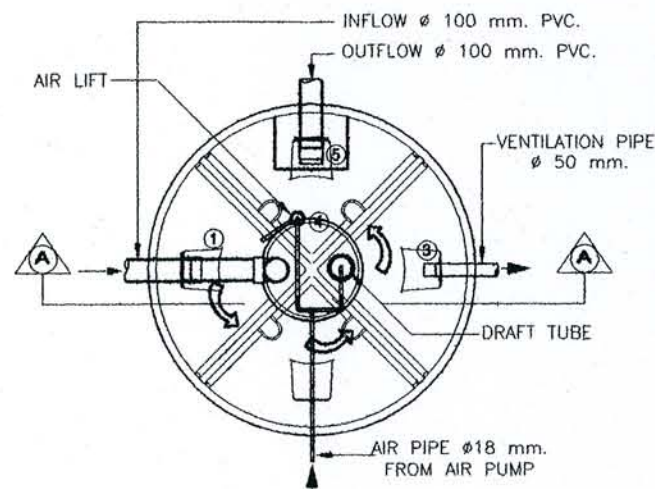


TOP-SECTION


- ① SOLIDS SEPARATION CHAMBER-1
- ② SOLIDS SEPARATION CHAMBER-2
- ③ AEROBIC CHAMBER-1
- ④ AEROBIC CHAMBER-2
- ⑤ SEDIMENTATION CHAMBER

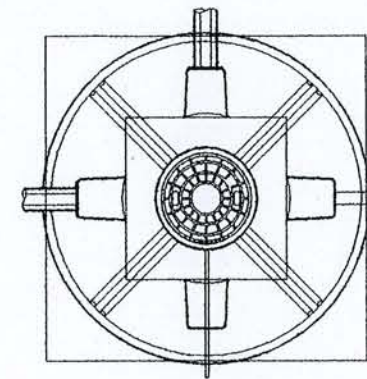


TOP-VIEW

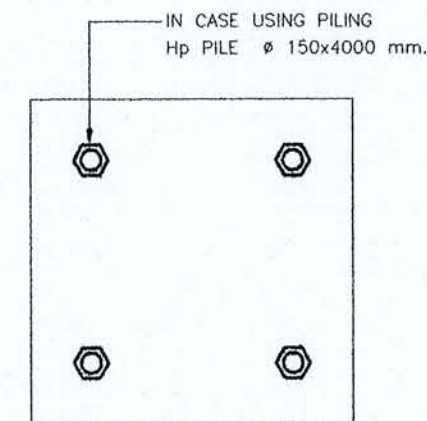

PLAN-PILE

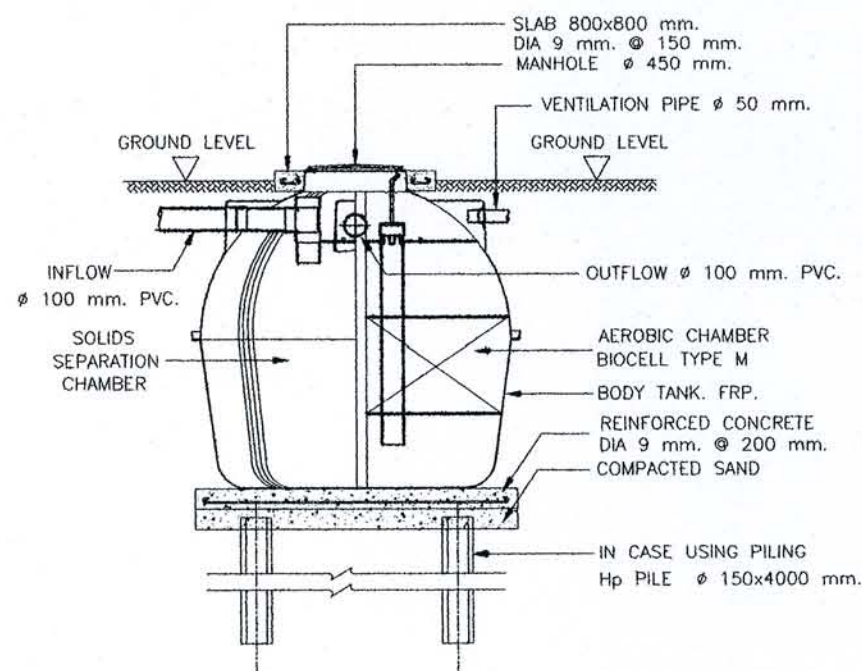

SECTION (A-A)

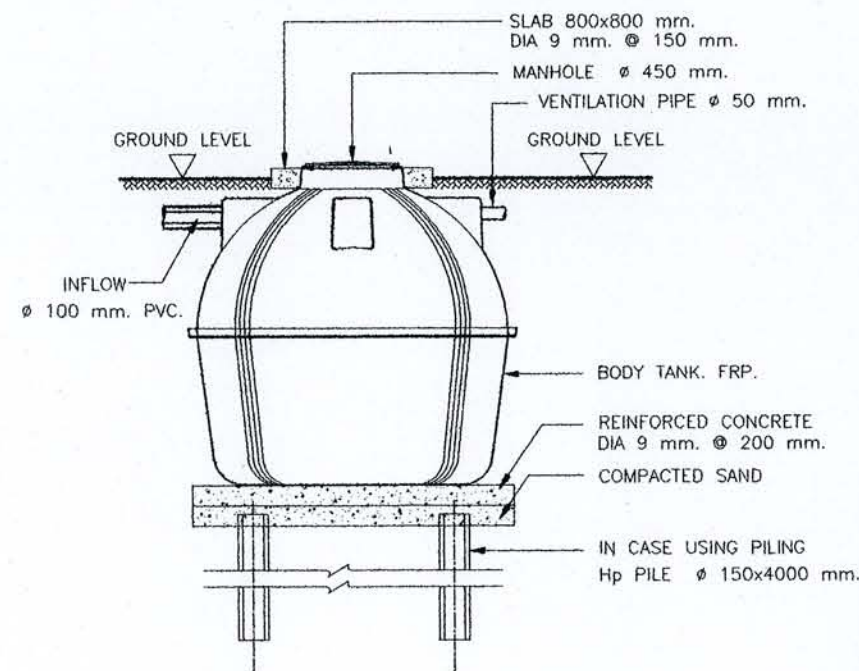

SIDE-VIEW

REMARK
PIPING AND FOUNDATION DESIGN, SHALL BE DETERMINED OR OMITTED
BASED ON ACTUAL SOIL BEARING CAPACITY BY CONSULTING WITH CIVIL
ENGINEER.

INSTALLATION FOR UNDER GARDEN AREA

หมายเหตุ

ระบบบำบัดน้ำเสีย ใช้ถังบำบัดน้ำเสียสำเร็จรูป ขนาดและวิธีการติดตั้งดูตามแบบของบริษัทผู้ผลิตที่เลือกใช้

BIOCELL MEDIA SPECIFICATION	
TYPE	M
SHAPE	EGG SHAPE HOLLOW SHELL
MAXIMUM I.D.; M.M. Ø	45.0
LENGTH ; M.M.	54.0
MINIMUM I.D.; M.M. Ø	30.0
SURFACE AREA ; M2	0.019677
MATERIAL	HDPE
SPECIFIC GRAVITY	0.964
SPECIFIC SURFACE AREA ; M2/M3.	170.72
VOID RATIO ; %	96.59

BIOTECH WASTEWATER TREATMENT TANK SEPTIC AEROBIC FILTER TANK MODEL BO-2200				
SCALE 1:30	STRUCTURAL ENGINEER	PITAKCHON	ENVIRONMENTAL SCIENCE	RAHWAN
DATE 17-08-2000	ENVIRONMENTAL ENGINEER	VICHAI POOKHUM	APPROVED BY	FUKUJI SEKENE
DWG. NO. BO-2200	ELECTRICAL ENGINEER	SOMNUJUK	DRAWN BY	IMIT



สำนักงานนโยบาย
และแผนทรัพยากรธรรมชาติและสิ่งแวดล้อม

โครงการ
แบบบ้านขี้เฒ่าเพื่อประชาชน

ตามนโยบาย

นายสุจินต์ บริหารสถิต ผู้อำนวยการ
นายทศพร เตชะไพฑูริย์ รองผู้อำนวยการ
นายธีระวัฒน์ นิลนันทน์ รองผู้อำนวยการ
นายพงศ์ศักดิ์ เสงี่ยมพงศ์ ปลัดสำนัก

ผู้อำนวยการสำนักงานนโยบาย

นายสุจินต์ บริหารสถิต ผู้อำนวยการ

รองผู้อำนวยการสำนักงานนโยบาย

นายทศพร เตชะไพฑูริย์ รองผู้อำนวยการ

นายธีระวัฒน์ นิลนันทน์ รองผู้อำนวยการ

นายพงศ์ศักดิ์ เสงี่ยมพงศ์ ปลัดสำนัก

นายสุจินต์ บริหารสถิต ผู้อำนวยการ

รองผู้อำนวยการสำนักงานนโยบาย

นายทศพร เตชะไพฑูริย์ รองผู้อำนวยการ



สำนักงานโยธา
กรุงเทพมหานคร

โครงการ
แบบบ้านยืมเพื่อประชาชน

ตามนโยบาย

น.ร.สุจินต์ บัณฑิต ผู้ว่าฯ กทม.
นายพรเทพ เศรษฐ์ รักษาราชการ
นายธีระชน นิ่มนัยสินธุ์ รักษาราชการ
นายพงษ์ศักดิ์ แสนล้านต์ ปลัดฯ กทม.

ผู้อำนวยการสำนักงานโยธา

นายจุมพล สันภาพล

รองผู้อำนวยการสำนักงานโยธา

นายทวีศักดิ์ เลิศประพันธ์

ผู้อำนวยการสำนักงานออกแบบ

นายจตุรงค์ สันติธรรม

หัวหน้ากลุ่มงานสถาปัตยกรรม

นายสินธุ์ชัย บุญปักษ์

หัวหน้ากลุ่มงานวิศวกรรม

นายธีระยุทธ คงสวัสดิ์เกียรติ

สถาปนิก

นายสินธุ์ชัย บุญปักษ์

วิศวกรโครงสร้าง

วิศวกรไฟฟ้า

วิศวกรสุขาภิบาล

นางสาวมณฑิรา สมพอม

วิศวกรเครื่องกล

นายช่างเขียนแบบ

นายประยูร อรรถจักร์

แบบ
(024) อรรถจักร์

เจ้าของ

สถานที่

แบบแสดง

ขยายบ่อพัก

มาตราส่วน 1:20

FILE : วันที่ 2553

หน้า 4

หน้า 4

หน้า 4

หน้า 4

หน้า 4

หน้า 4


หน้า 4

หน้า 4


หน้า 4

หน้า 4


หน้า 4

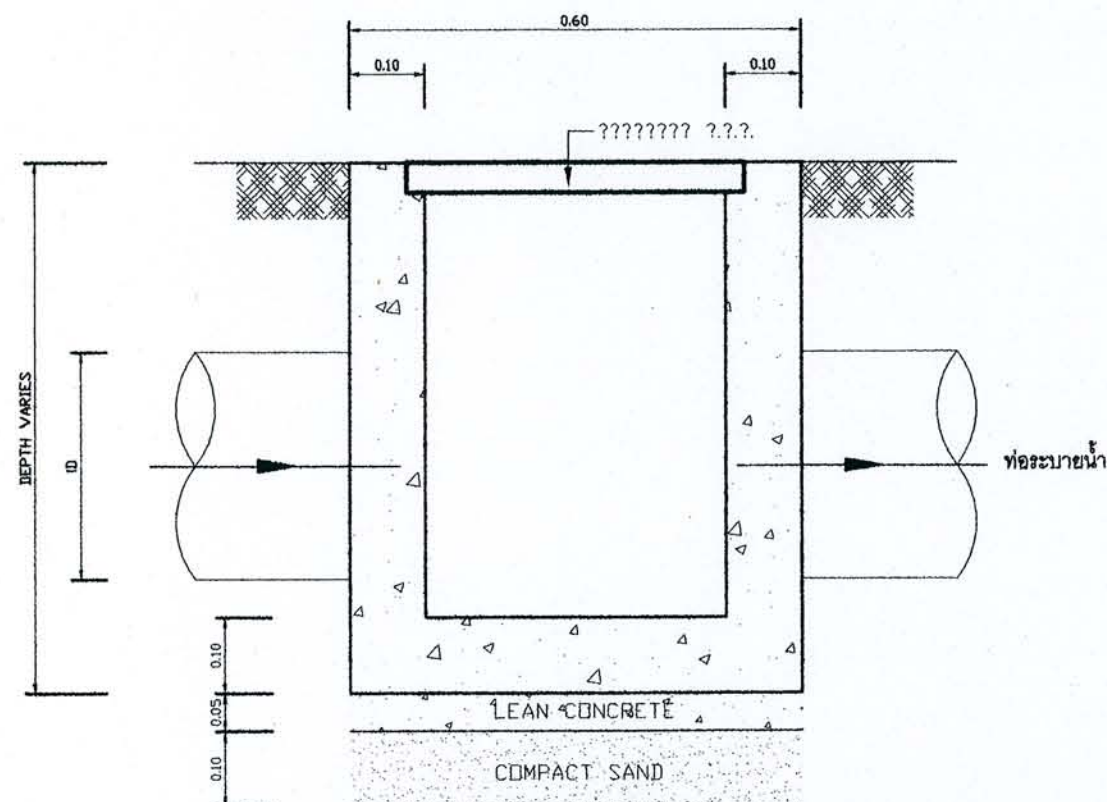


?????? B-B
????????? 1:10

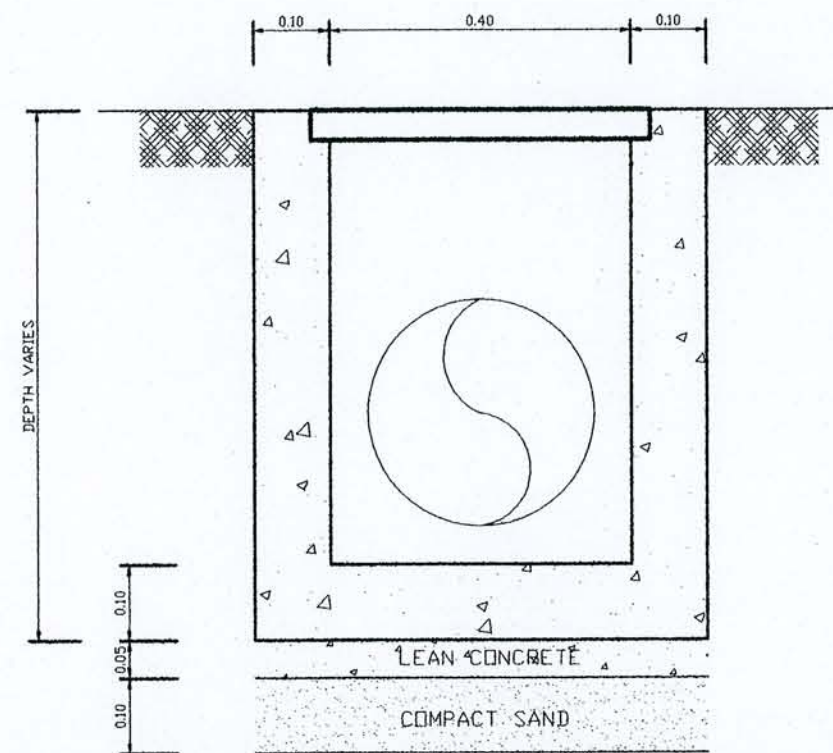

?????? C-C
????????? 1:10

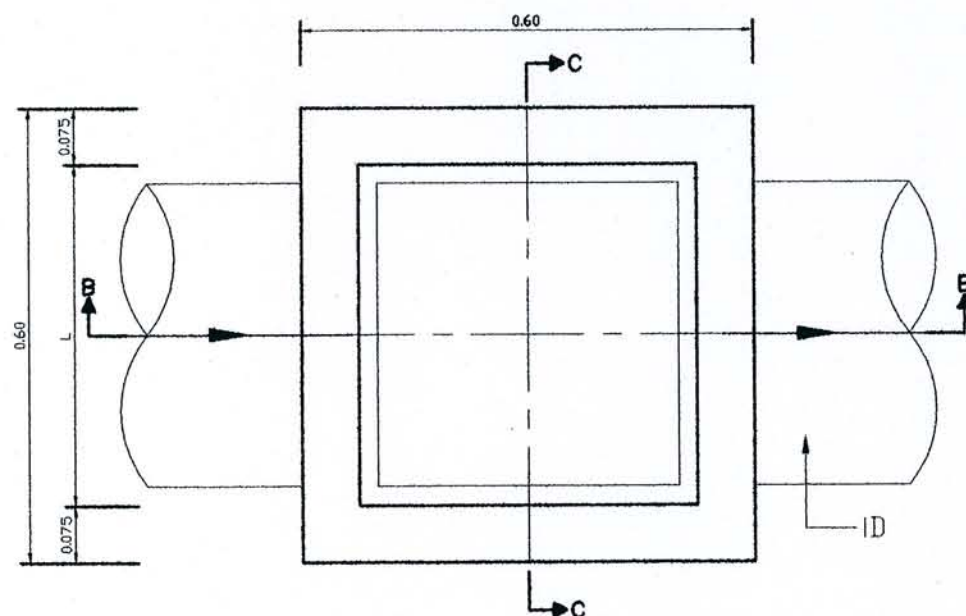

????????????????????
????????? 1:10

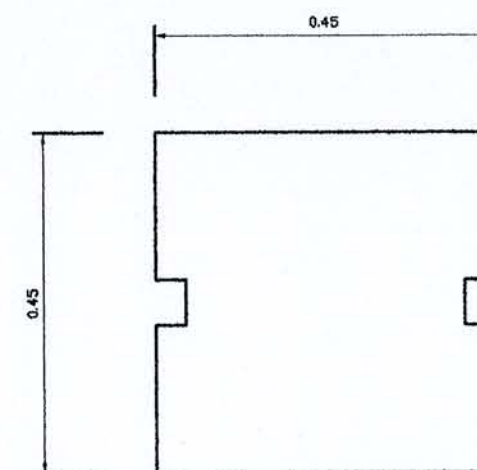

??????????
????????? 1:10