



ตามนโยบายของ
กรมราชวงศ์สุขุมพันธุ์ บริพัตร
ผู้ว่าราชการกรุงเทพมหานคร
โดย สำนักการโยธา



แบบบ้านยืม... เพื่อประชาชน

100 แบบบ้านมาตรฐาน...
สวย ดี โดนใจ...
พร้อมปลูกสร้างได้ทันที

ห้ามพลาด!!! โอกาส...
ยืมรับ... บ้านใหม่
แบบ **บ้านสวย
เลือกได้**
ใน “โครงการแบบบ้านยืม...เพื่อประชาชน”

แบบ 100 แบบบ้าน
มาตรฐาน...
สวย ดี โดนใจ
พร้อมปลูก
สร้างได้ทันที
เพื่อให้เลือก
หลากหลาย
ตอบสนอง
ทุกไลฟ์สไตล์คนเมือง

ปุระพวง

สำนักการโยธา กรุงเทพมหานคร

[illegible]

กรุงเทพมหานคร มีความประสงค์ที่จะออกแบบบ้านพักอาศัย "โครงการแบบบ้านยี่สิบเอ็ดประชาชน" แก่ประชาชนที่ต้องการรับบริการการออกแบบ โดยที่กรุงเทพมหานครมีขีดจำกัดค่าใช้จ่าย ดังนี้

- รายละเอียดประกอบแบบรายการ
 - การบิลด์ระบบ

หากขนาดหรือรูปร่างที่แตกต่างจากที่ระบุไว้ ควรมีการตรวจสอบและพิจารณาปรับผังบริเวณ ให้ตรงกับข้อกำหนดต่างๆ ที่เกี่ยวข้องกับการควบคุมการก่อสร้างอาคาร แต่โดยทั่วไปแล้ว หากที่ดินที่จะปลูกสร้างบ้านนั้น มีขนาดใหญ่มากกว่าที่ระบุในผังบริเวณ ย่อมมีโอกาสที่เชื้อต่อการปฏิบัติตามกฎหมายและสิ่งแวดล้อมที่ดีขึ้น

ผู้รับจ้างจะต้องทำการบิลด์ผังวางระดับมาตรฐานให้ถูกต้องตามที่ปรากฏในผังบริเวณ ก่อนที่จะดำเนินการต่อไป ระดับ ± 0.00 ให้ถือตามระดับถนนด้านหน้าหรือถนนสาธารณะ ทางเข้าของเขตที่ดิน ส่วนการลดระดับหรือเปลี่ยนระดับพื้นภายในอาคาร ให้ยึดถือระดับเมื่อถมแล้วผิวพื้นเรียบร้อยแล้ว ตามที่ระบุในแบบสถาปัตยกรรมเป็นหลัก
 - งานโครงสร้าง

ดูรายละเอียดตามแบบวิศวกรรมโครงสร้าง โดยแบบโครงสร้างที่ปรากฏในแบบฉบับนี้ เป็นการออกแบบเพื่อใช้สำหรับก่อสร้างในเขตกรุงเทพมหานครทั่วไป กรณีที่ไม่ไปก่อสร้างบนพื้นที่ที่มีลักษณะพิเศษ เช่น เขตบางขุนเทียน เขตทุ่งครุ หรือพื้นที่ต่างจังหวัด จะต้องมีการพิจารณาออกแบบโครงสร้างฐานรากใหม่ เพื่อให้ได้ SAFE LOAD ตามที่วิศวกรกำหนด
 - งานสถาปัตยกรรม
 - งานผนังอาคารทั้งหมด ให้ใช้ผนังอิฐก่อส่วสามัญ หรือคอนกรีตมวลเบา หรืออื่นๆ (เจ้าของกำหนด) การก่อผนังภายใน ให้ก่อสูงระดับท้องพื้นชั้นบน โดยผนังทั่วไป ให้ตามแต่จะวางผิวเรียบ ทาสี ส่วนผนังห้องน้ำ ให้ตกแต่งปูกระเบื้องเซรามิค ชนิดผนัง ลายและขนาด (เจ้าของกำหนด)
 - งานพื้น พื้นอาคารเป็น คสล ตามแบบขยายทางวิศวกรรมโครงสร้าง ในกรณีพื้นล่างระบุเป็น แผ่นสำเร็จรูป ให้ปูแผ่นพลาสติก ชนิดหนา ก่อนปูพื้นดังกล่าว ในกรณีพื้นเป็นพื้นคสล หล่อในที่ ด้านล่างให้ถมด้วยทราย เป็นแฉะแบบ ส่วนการตกแต่งผิวพื้น ให้เป็นไปตามสัญลักษณ์แบบสถาปัตยกรรม ทั้งนี้ในส่วนงานบัวพื้น จะต้องทำทุกส่วนที่พื้นนั้นไปจรจบ ให้บัวพื้นไม่สังเคราะห์ ไม่มีส่วนผสมของ Asbestos
 - งานฝ้าเพดาน เป็นโครงค้ำเหล็กสูงสังกะสี บุด้วยแผ่นไฟเบอร์ซีเมนต์ หนาไม่น้อยกว่า ๐.๘ม (ในท้องน้ำใช้ชนิดหนาขึ้น) ฉาบเรียบ ทาสี กรรมวิธีในการติดตั้งตามมาตรฐานบริษัทผู้ผลิต ให้ยึดถือฉนวนกันความร้อน บนฝ้าเพดานห้องชั้นบน หรือใต้โครงสร้าง
 - งานประตู-หน้าต่าง ช่องแสง และกระชาก ระบุแบบให้เป็นไปตามแบบขยาย หรือเจ้าของกำหนด
 - งานประตูหน้าต่าง ให้ใช้กระจกใสเนื้อแข็ง ขนาด 2"x๘" บานประตูสำเร็จรูป ทาสี
 - งานหน้าต่าง ให้ใช้วงกบและกรอบบานไม้เนื้อแข็ง หรือใช้วงกบและกรอบบานอลูมิเนียม เนื้อของอลูมิเนียม (ALUMINIUM EXTRUSION) เป็น ALLOY ชนิด 6063-T5 หรือ 505-T5
 - ลูกฟักกระชากทั่วไป ให้ใช้กระชากโฟลด์ไสหรือกระชากดัดแสง หนาไม่น้อยกว่า ๐.๘ม (เจ้าของกำหนด) ส่วนกระชากงา กระชากผ้า ต้องทำจากกระชากโฟลด์ไสเท่านั้น
 - ให้ติดตั้งมุ้งลวดไฟเบอร์ กรอบอลูมิเนียม ทุกบาน
 - งานห้องน้ำ-ส้วม และสุขภัณฑ์ ระบุแบบให้เป็นไปตามแบบขยาย หรือเจ้าของกำหนด โดยที่ผู้รับจ้างจะต้องประกอบงาน งานสุขภัณฑ์เพื่อทำการติดตั้งเครื่องสุขภัณฑ์ อุปกรณ์ประกอบห้องน้ำและอื่นๆ ผู้รับจ้างต้องตรวจสอบขนาด ตำแหน่ง และระบุรายการของต่างๆ ที่ตรงกันกับฐานและข้อที่ผู้รับจ้างกำหนด พื้นห้องน้ำ-ส้วม ต้องเป็นคสลผสมมัน้ำยากันซึม ทาทั้งด้วยน้ำยากันซึม ก่อนปูกระเบื้องเซรามิค
 - งานทาสี โดยทั่วไป ผู้รับจ้างต้องทำการเตรียมผิววัสดุทุกส่วนที่จะทาสีให้เรียบร้อก่อน จึงจะทาสีได้
 - ส่วนที่เป็นปูน ชิมมัต ให้ทาสีสองพื้นปูนใหม่ 1 เที่ยว ก่อนทาสีจึงทึบหน้าอย่างน้อย 2 เที่ยว ทั้งนี้ ผิวผนังปูน ฝ้าเพดาน ให้ทาคอยล์ ACRYLIC 100% กึ่งเงา หรือเจ้าของกำหนด
 - ส่วนที่เป็นไม้จะต้องอุดโป๊วและขัดสีเรียบด้วยกระดาษทรายขนาด 120 กรวด พื้นไม้ 1 เที่ยว ก่อนทาสีจึงทึบหน้าอย่างน้อย 2 เที่ยว
 - ส่วนที่เป็นเหล็ก หากมีสนิม ให้ขัดสนิมออกให้มากที่สุด รวมทั้งกับความเรียบร้อยของรอยเชื่อม ทาด้วยสีรองพื้นกันสนิม 1 เที่ยว ก่อนทาสีจึง (สีน้ำเงิน) ทึบหน้าอย่างน้อย 2 เที่ยว
 - งานหลังคา

โครงสร้างหลังคา ตามแบบวิศวกรรมโครงสร้าง ในกรณีที่เป็นหลังคากระเบื้อง ให้ใช้กระเบื้องซีเทคโมเนีย การติดตั้งให้เป็นไปตามกรรมวิธีของบริษัทผู้ผลิตอย่างเคร่งครัด ในกรณีที่เป็นหลังคา หรือกันสาดคสล ให้ผสมมัน้ำยากันซึมในโครงสร้าง และทึบระบบกันซึม สำหรับหลังคา หรือชั้มน้ำ สำหรับกันสาด
 - งานบันได

บันไดคอนกรีตเสริมเหล็ก โครงสร้างตามแบบวิศวกรรมโครงสร้าง ฉาบเรียบ ทาสี พื้นบันไดและชานพัก ให้บุด้วยแผ่นไม้จริง เป็นไม้เนื้อแข็ง หนา 1" ขนาดเท่าลูกนอน โดยขึ้นจากขอบลูกตั้ง 1"
 - งานอื่นๆ
 - งานสุขภัณฑ์ ไม่รวมอยู่ในงานก่อสร้างนี้ ยกเว้นเจ้าของงานตกลงเป็นงานเพิ่มเติมเป็นรายการนี้ ทั้งนี้ผู้รับจ้างรับผิดชอบงานเดินท่อระบบสุขาภิบาลและระบบไฟฟ้า เพื่อรองรับการติดตั้งสุขภัณฑ์
 - กรณีเดินท่อบ PVC Class 13.5 เพื่อทำปลั๊กมอด มอด แฉะ รวมอยู่ในงานก่อสร้างนี้
- งานระบบสุขาภิบาล

ผู้รับจ้างต้องเดินท่อระบบสุขาภิบาล ตามแบบ พร้อมติดตั้งสุขภัณฑ์ บ่อบำบัดสำเร็จรูป และอื่นๆที่ระบุในแบบ กรณีที่ท่อเดินท่อบนคาน พื้น หรือโครงสร้าง จะต้องหุ้มด้วย SLEEVE ให้เรียบร้อย ให้ผู้รับจ้างติดตั้ง ถังบำบัดน้ำเสียสำเร็จรูป ปริมาตรไม่น้อยกว่า 1 ลบม และถังเก็บน้ำประปาสำเร็จรูป บนดิน ปริมาตรไม่น้อยกว่า 1 ลบม พร้อมเบร็กวาล์วอัตโนมัติ ขนาด 200 มิลลิเมตร
- งานระบบไฟฟ้า

ผู้รับจ้างต้องติดตั้งและเดินสายระบบไฟฟ้า ระบบแสงสว่าง ตามแบบรายการประกอบแบบทางไฟฟ้า และตามมาตรฐานการไฟฟ้า กรณีที่ท่อเดินท่อบนคาน พื้น หรือโครงสร้าง จะต้องหุ้มด้วย SLEEVE ให้เรียบร้อย

1. การก่อร่างสร้างให้เป็นไปตามแบบ และรายการประกอบแบบ ผู้รับจ้างต้องเขียน ทห/สผ อุปกรณ์ เครื่องมือ เครื่องใช้ ช่างฝีมือที่ดี และแรงงานทั้งหมด ให้เพียงพอ และพร้อมเพื่อปฏิบัติงานก่อสร้างให้ดำเนินงานไปด้วยความรวดเร็ว เขียนบัญชีและใบประวัติการทำงานและตัวเลขงานที่ถูกต้องสมบูรณ์ตามแบบและรายการก่อสร้างทุกประการ โดยมีผลงานที่มีคุณภาพด้วย
2. แบบ และรายการก่อสร้าง ทห/สผให้แนบไปด้วยทั้งนี้เพื่อคำวินิจฉัยของ สถาปนิกหรือวิศวกรผู้ออกแบบ เป็นหลัก หรือระบุในแบบแต่มีระบุในรายการก่อสร้าง หรือระบุในรายการก่อสร้างแต่ไม่ได้ระบุในแบบ ให้ถือเสมือนว่าระบุไว้ทั้งสองที่ หรือมีระบุไว้ในทั้งสองที่ แต่ต้องความเรียบร้อยของงานก่อสร้าง หรือที่ผ่านการดีของงานก่อสร้าง ผู้รับจ้างต้องรับดำเนินการโดยไม่มีค่าใช้จ่ายเพิ่มเติมจากที่กล่าวไว้ หากข้อสงสัยให้สอบถามสถาปนิกหรือ วิศวกรผู้ออกแบบก่อนลงมือดำเนินการก่อสร้างทุกครั้ง
3. วัสดุอุปกรณ์ที่ปรากฏอยู่ในแบบ และ/หรือ รายการก่อสร้างที่ดี หรือมีอยู่ในแบบและ/หรือรายการก่อสร้างที่ดี นั้นเป็นส่วนหนึ่งของเป็นส่วนประกอบรายการก่อสร้างอาคารนี้ให้เป็นไปตามหลักและมาตรฐานรายการก่อสร้างที่ดีนี้ ผู้รับจ้างจะต้องจัดหาความและใช้ในงานก่อสร้างให้ดีขึ้น
4. ผู้รับจ้างจะต้องจัดหาอย่างวัสดุอุปกรณ์ทุกอย่างหรือที่สถาปนิกและวิศวกรและผู้จ้างพิจารณาเห็นว่าชอบ อยู่เหนือมาตรฐานที่ดี วัสดุอุปกรณ์ทุกที่ที่ใช้ในการก่อสร้างนี้จะต้องไม่เป็นของที่มีลักษณะที่อาจก่อให้เกิดว่าเป็นของที่ไม่ใช่เป็นงานหรือเพื่อจากการใช้มาก่อน และต้องเป็นของซึ่งหากผู้ผลิตจะต้องมีคุณภาพดี ไม่มีรอยขาด เสียหาย แตกหัก และจะต้องถูกต้องตรงตามที่ระบุในแบบและรายการก่อสร้าง

รายการสัญลักษณ์ผังและผิวผนัง	
①	ผนังทั่วไป ผนังก่ออิฐก่อลังสามัญหรือคอนกรีตมวลเบา หรืออื่นๆ ฉาบเรียบ ทาสี
②	ผนังท่อน้ำ ผนังก่ออิฐก่อลังสามัญหรือคอนกรีตมวลเบา หรืออื่นๆ บุกระเบื้องเซรามิก ชนิดปูผนัง เกรด A
หมายเหตุ - ชนิดของทั้ง และรายละเอียดในการตกแต่งผิวผนัง เจ้าของงานเป็นผู้ตัดสินใจ โดยให้รับจ้างจัดหาวัสดุห่อหุ้ม และปรึกษาเจ้าของงาน ก่อนดำเนินการ - ให้ผู้รับจ้างติดฉนวนที่ ผนัง ไม่ใช้ Asbestos หรือทาสี	
รายการสัญลักษณ์พื้น	
①	ท-1 พื้นคอนกรีต ปูทับด้วยกระเบื้องเซรามิก ชนิดปูพื้น เกรด A
②	ท-2 พื้นคอนกรีต ปูทับด้วยปาร์เก้ไม้ หรือพื้นไม้สังเคราะห์
③	ท-3 พื้น ค.ส.ล. ผิวขัดมัน
④	ท-4 พื้น ค.ส.ล. ผิวขัดหยาบ
หมายเหตุ - ชนิดของทั้ง และรายละเอียดในการตกแต่งผิวพื้น เจ้าของงานเป็นผู้ตัดสินใจ โดยให้รับจ้างจัดหาวัสดุห่อหุ้ม และปรึกษาเจ้าของงาน ก่อนดำเนินการ - ให้ผู้รับจ้างติดฉนวนที่ พื้น ไม่ใช้ Asbestos หรือทาสี	
รายการสัญลักษณ์ฝ้าเพดาน	
①	ฝ้า-1 ฝ้าเพดานโพลีเอสเตอร์ หนาไม่น้อยกว่า 6 มม. ชนิดขอบลาด ฉาบรอยต่อเรียบ ทาสี
②	ฝ้า-2 ฝ้าเพดานโพลีเอสเตอร์ หนาไม่น้อยกว่า 6 มม. ชนิดขอบลาด ทาสี ฉาบรอยต่อเรียบ ทาสี
หมายเหตุ - เจ้าของ SERVICE แบบสำเร็จรูป บริเวณฝ้าเพดาน ขึ้นบนยึดกับหลังคา ขนาด 0.60x0.80 ม. พื้นหน้าล่างของฝ้าเพดานงาน - ให้ติดตั้งฉนวนกันความร้อน บนฝ้าเพดานข้างชั้นบน หรือใต้โครงสร้าง - ให้ผู้รับจ้างติดตั้งฝ้าเพดาน ไม่ใช้ Asbestos หรือทาสี	





สำนักงานโยธา
กรุงเทพมหานคร

โครงการ
แบบบ้านยิมเพื่อประชาชน

ตามนโยบาย

ม.ร.ว.สุขุมพันธุ์ บริพัตร ผู้ว่าฯกทม.
นายพรเทพ เศรษฐินทรัพย์ รองผู้ว่าฯกทม.
นายธีระชน มโนชัยปิณฑย์ รองผู้ว่าฯกทม.
นายพงษ์ศักดิ์ภูมิพัฒน์ ปลัดฯกทม.

ผู้อำนวยการสำนักงานโยธา

นายจันทพล สันภาพล

รองผู้อำนวยการสำนักงานโยธา

นายทวีศักดิ์ เลิศประพันธ์

ผู้อำนวยการสำนักงานออกแบบ

นายจตุรงค์ สมนิโยม

หัวหน้ากลุ่มงานสถาปัตยกรรม

นายสิริวัชร บัญญัติ

หัวหน้ากลุ่มงานวิศวกรรม

นายธีระยุทธ คงสวัสดิ์โยธ

สถาปนิก

นางสาวสุนทรภรณ์ กาญจนะ

วิศวกรโครงสร้าง

นายวันโสม บัณฑิตโยธ

วิศวกรไฟฟ้า

นายกิตติพงษ์ จิระเดชาก

วิศวกรสุขาภิบาล

นางสาวมณฑิรา ผลหอม

วิศวกรเครื่องกล

นายชาญวิทย์แบบ

นายณัฐพงษ์ ณรงค์บุญชู

แบบ
026 บ้านพุระพง

เจ้าของ

สถานที่

แบบแสดง
ผังพื้นที่ขุด


มาตราส่วน 1:75

FILE : เลขที่ 03

วันที่ 2553 A-03 03

คัดลอก ปรับปรุงแบบ รวมแผ่น 22

รายการแก้ไขแบบ

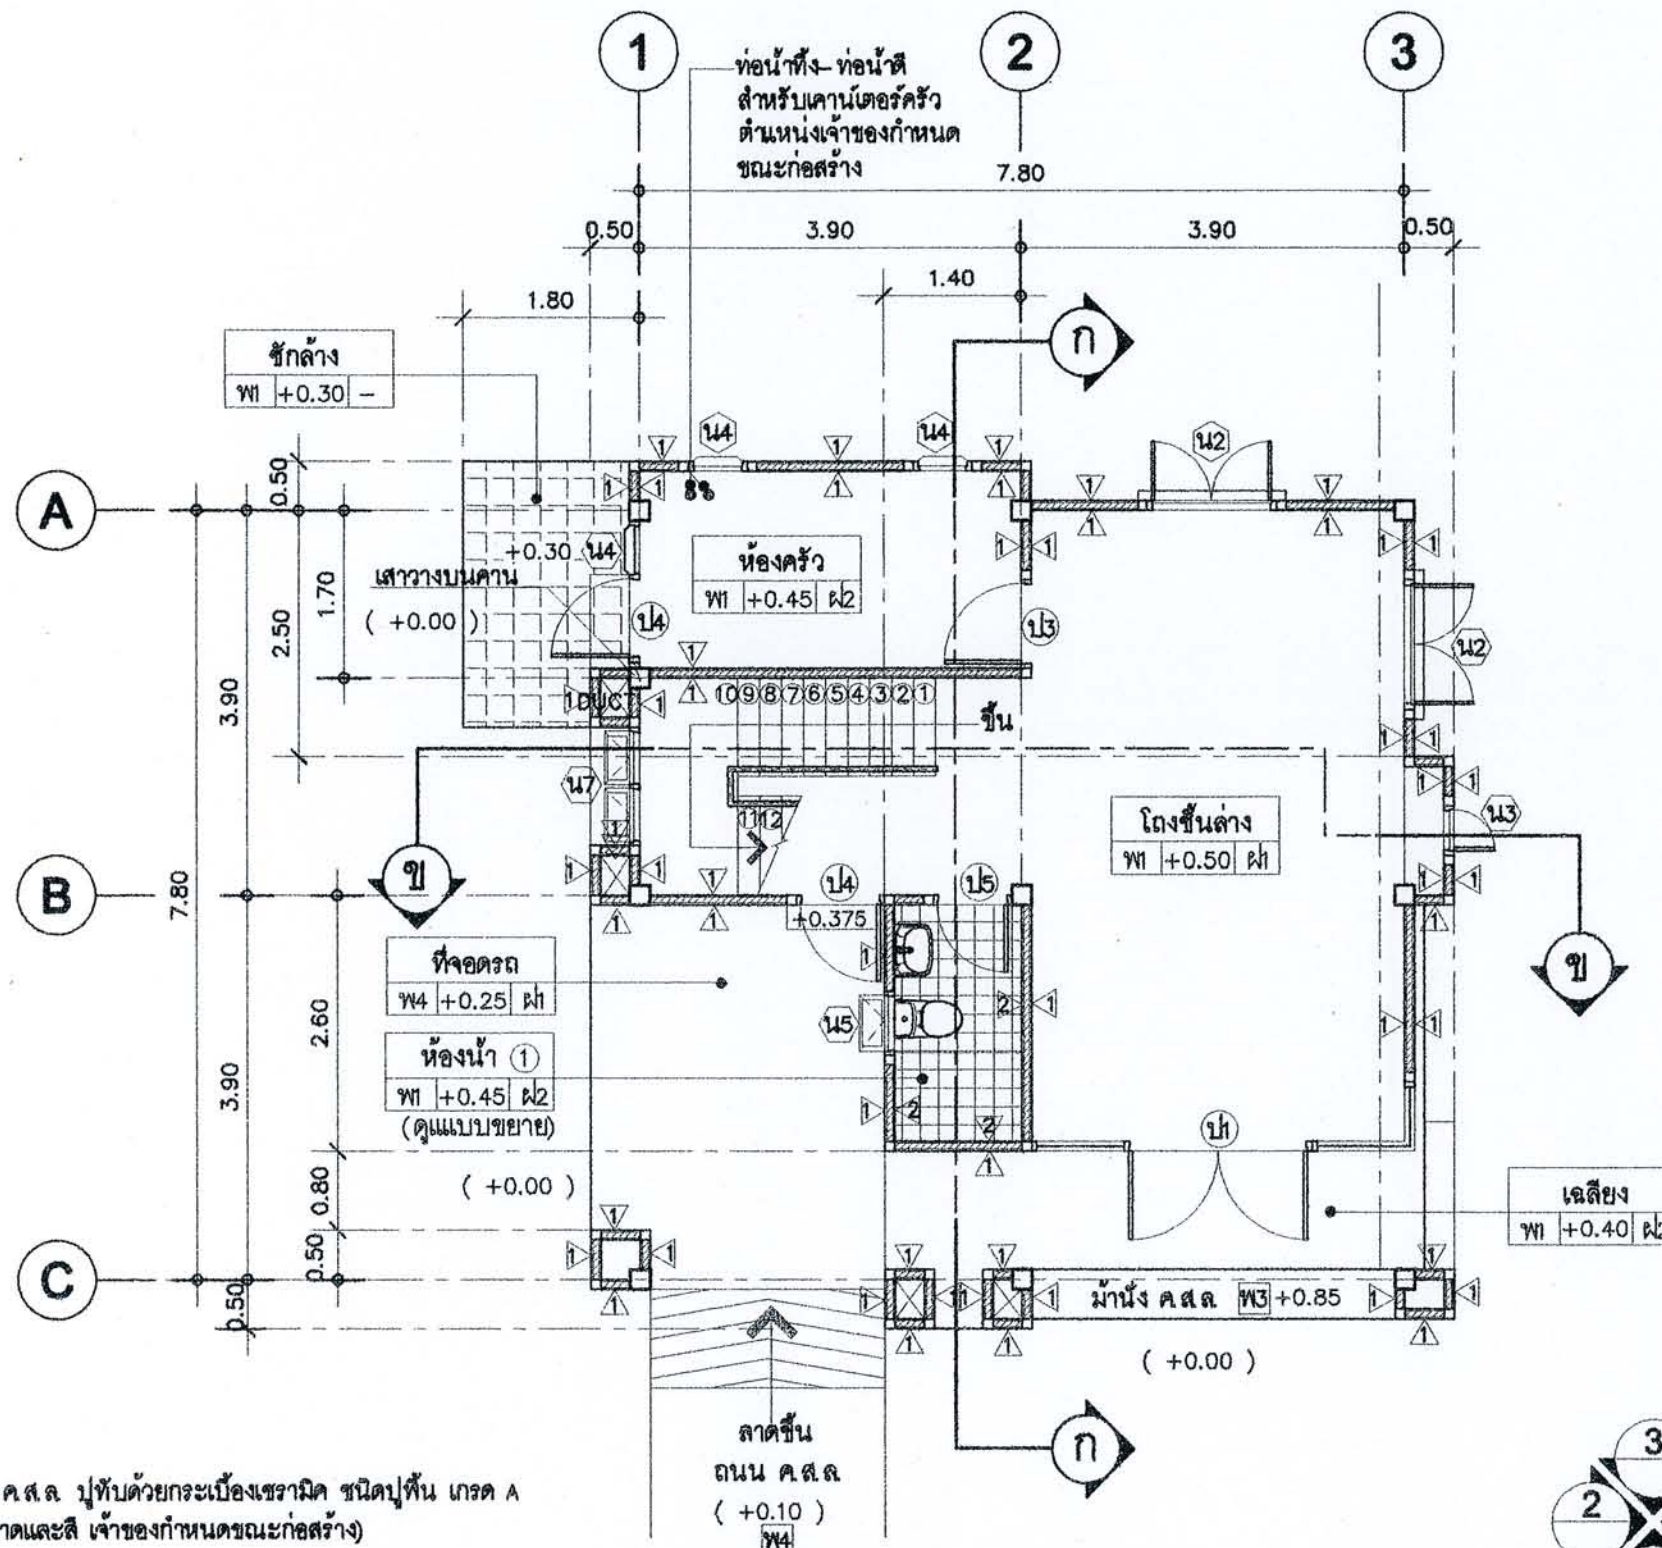

พ1 พื้น ค.ส.ล. ปูทับด้วยกระเบื้องเซรามิค ชนิดปูพื้น เกรด A
(ขนาดและสี เจ้าของกำหนดขณะก่อสร้าง)

พ2 พื้น ค.ส.ล. ปูทับด้วยไม้ปาร์เก้หรือพื้นไม้สังเคราะห์
(ชนิดและขนาด เจ้าของกำหนดขณะก่อสร้าง)

พ3 พื้น ค.ส.ล. ผิวขัดมัน

พ4 พื้น ค.ส.ล. ผิวขัดหยาบ

แปลนพื้นที่ขุด

มาตราส่วน 1:75

ทิศแสดงการมองรูปด้าน



สำนักงานโยธา
กรุงเทพมหานคร

โครงการ
แบบบ้านขึ้นเพื่อประชาชน

ตามนโยบาย

น.ร.สุชนพันธุ์ บริพัตร ผู้ว่าฯกทม.
นายแพทย์ เจริญโพธิ์ รองผู้ว่าฯกทม.
นายธีระชน มโนชัยปิฎก รองผู้ว่าฯกทม.
นายพงศ์ศักดิ์ แสนลำดัย ปลัดฯกทม.

ผู้อำนวยการสำนักงานโยธา

นายจุมพล สันภาพล

รองผู้อำนวยการสำนักงานโยธา

นายทวีศักดิ์ เลิศประพันธ์

ผู้อำนวยการสำนักงานออกแบบ

นายจตุรงค์ สมนิยม

หัวหน้ากลุ่มงานสถาปัตยกรรม

นายสินธุ์ชัย บุญปักษ์

หัวหน้ากลุ่มงานวิศวกรรม

นายธีระยุทธ คงสรค์เดโช

สถาปนิก

นางสาวสุนนมาลย์ กาญจนะ

วิศวกรโครงสร้าง

นายวันโอ บรีคไพฑูริย์

วิศวกรไฟฟ้า

นายกิตติพงษ์ จิระเดชากร

วิศวกรสุขาภิบาล

นางสาวณัฏฐา สรพยอม

วิศวกรเครื่องกล

นายช่างเขียนแบบ

นายอภิรุฬห์ ณรงค์บุญญาสุทธ

แบบ
026 บ้านพุระพง

เจ้าของ

สถานที่

แบบแสดง

ผังพื้นที่ขึ้นบน

มาตราส่วน 1:75


FILE : เลขที่ 04

วันที่ 1 มิถุนายน 2553

คัดลอกปรับปรุงแบบ

รวมแผ่น 22

รายการแก้ไขแบบ

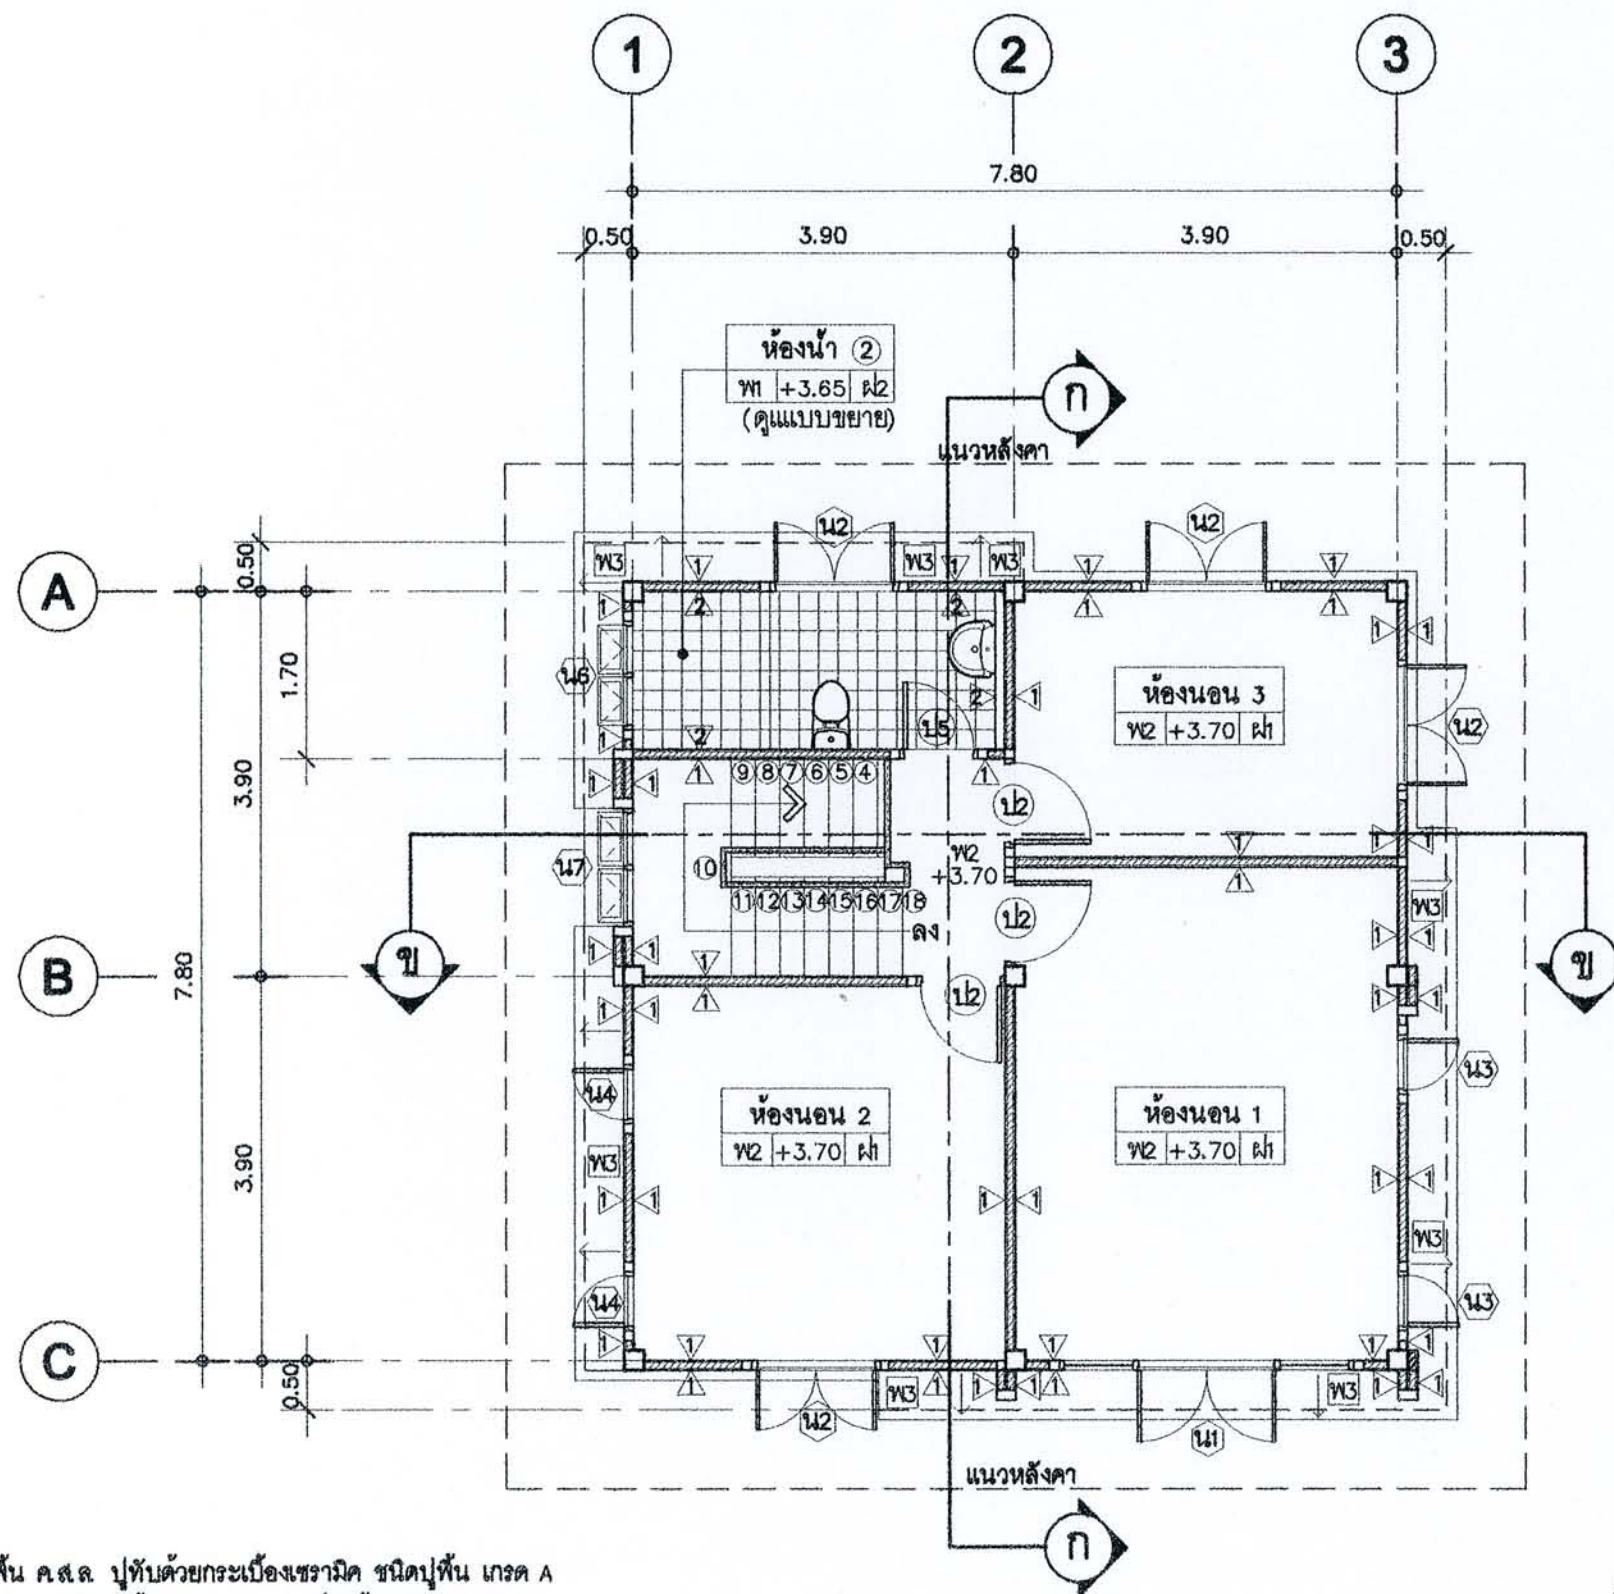

แปลนพื้นที่ขึ้นบน
มาตราส่วน 1:75



- W1 พื้น ค.ส.ล. ปูทับด้วยกระเบื้องเซรามิค ชนิดปูพื้น เกรด A (ขนาดและสี เจ้าของกำหนดขณะก่อสร้าง)
- W2 พื้น ค.ส.ล. ปูทับด้วยไม้ปาร์เก้หรือพื้นไม้สำเร็จรูป (ชนิดและขนาด เจ้าของกำหนดขณะก่อสร้าง)
- W3 พื้น ค.ส.ล. ผิวขัดมัน
- W4 พื้น ค.ส.ล. ผิวขัดหยาบ



สำนักงานโยธา
กรุงเทพมหานคร

โครงการ
แบบบ้านขี้เหล็กประชาชน

ตามนโยบาย

ม.ร.ว.สุขุมพันธุ์ บริพัตร ผู้ว่าฯกทม.
นายพรหม เสงี่ยมพงษ์ รองผู้ว่าฯกทม.
นายธีระชน มโนวิจิตรกุล รองผู้ว่าฯกทม.
นายพงศ์ศักดิ์ สุขสมิทธิ์ ปลัดฯกทม.

ผู้อำนวยการสำนักงานโยธา

นายจุมพล ตันภาพล

รองผู้อำนวยการสำนักงานโยธา

นายทวีศักดิ์ เลิศประพันธ์

ผู้อำนวยการสำนักงานออกแบบ

นายจตุรงค์ ตันเชียม

หัวหน้ากลุ่มงานสถาปัตยกรรม

นายสินธุ์ชัย บุญปักษ์

หัวหน้ากลุ่มงานวิศวกรรม

นายธีระยุทธ คงสวรรค์

สถาปนิก

นางสาวสุนทราภรณ์ กาญจนะ

วิศวกรโครงสร้าง

นายวันโน บัวศรีโพธิ์

วิศวกรไฟฟ้า

นายกิตติพงษ์ จิระเดชาก

วิศวกรสุขาภิบาล

นางสาวณัฏฐิรา ส้มหอม

วิศวกรเครื่องกล

นายช่างเขียนแบบ

นายณัฐพงศ์ ณรงค์บุญญาสุทนต์

แบบ

026 บ้านทุระพง

เจ้าของ

สถานที่

แบบแสดง

ผังหลังคา

มาตราส่วน 1:75

FILE :


วันที่ 2553

คดีเลขที่ 05

คดีเลขที่ 05

รวมแผ่น 22

รายการแนบแบบ

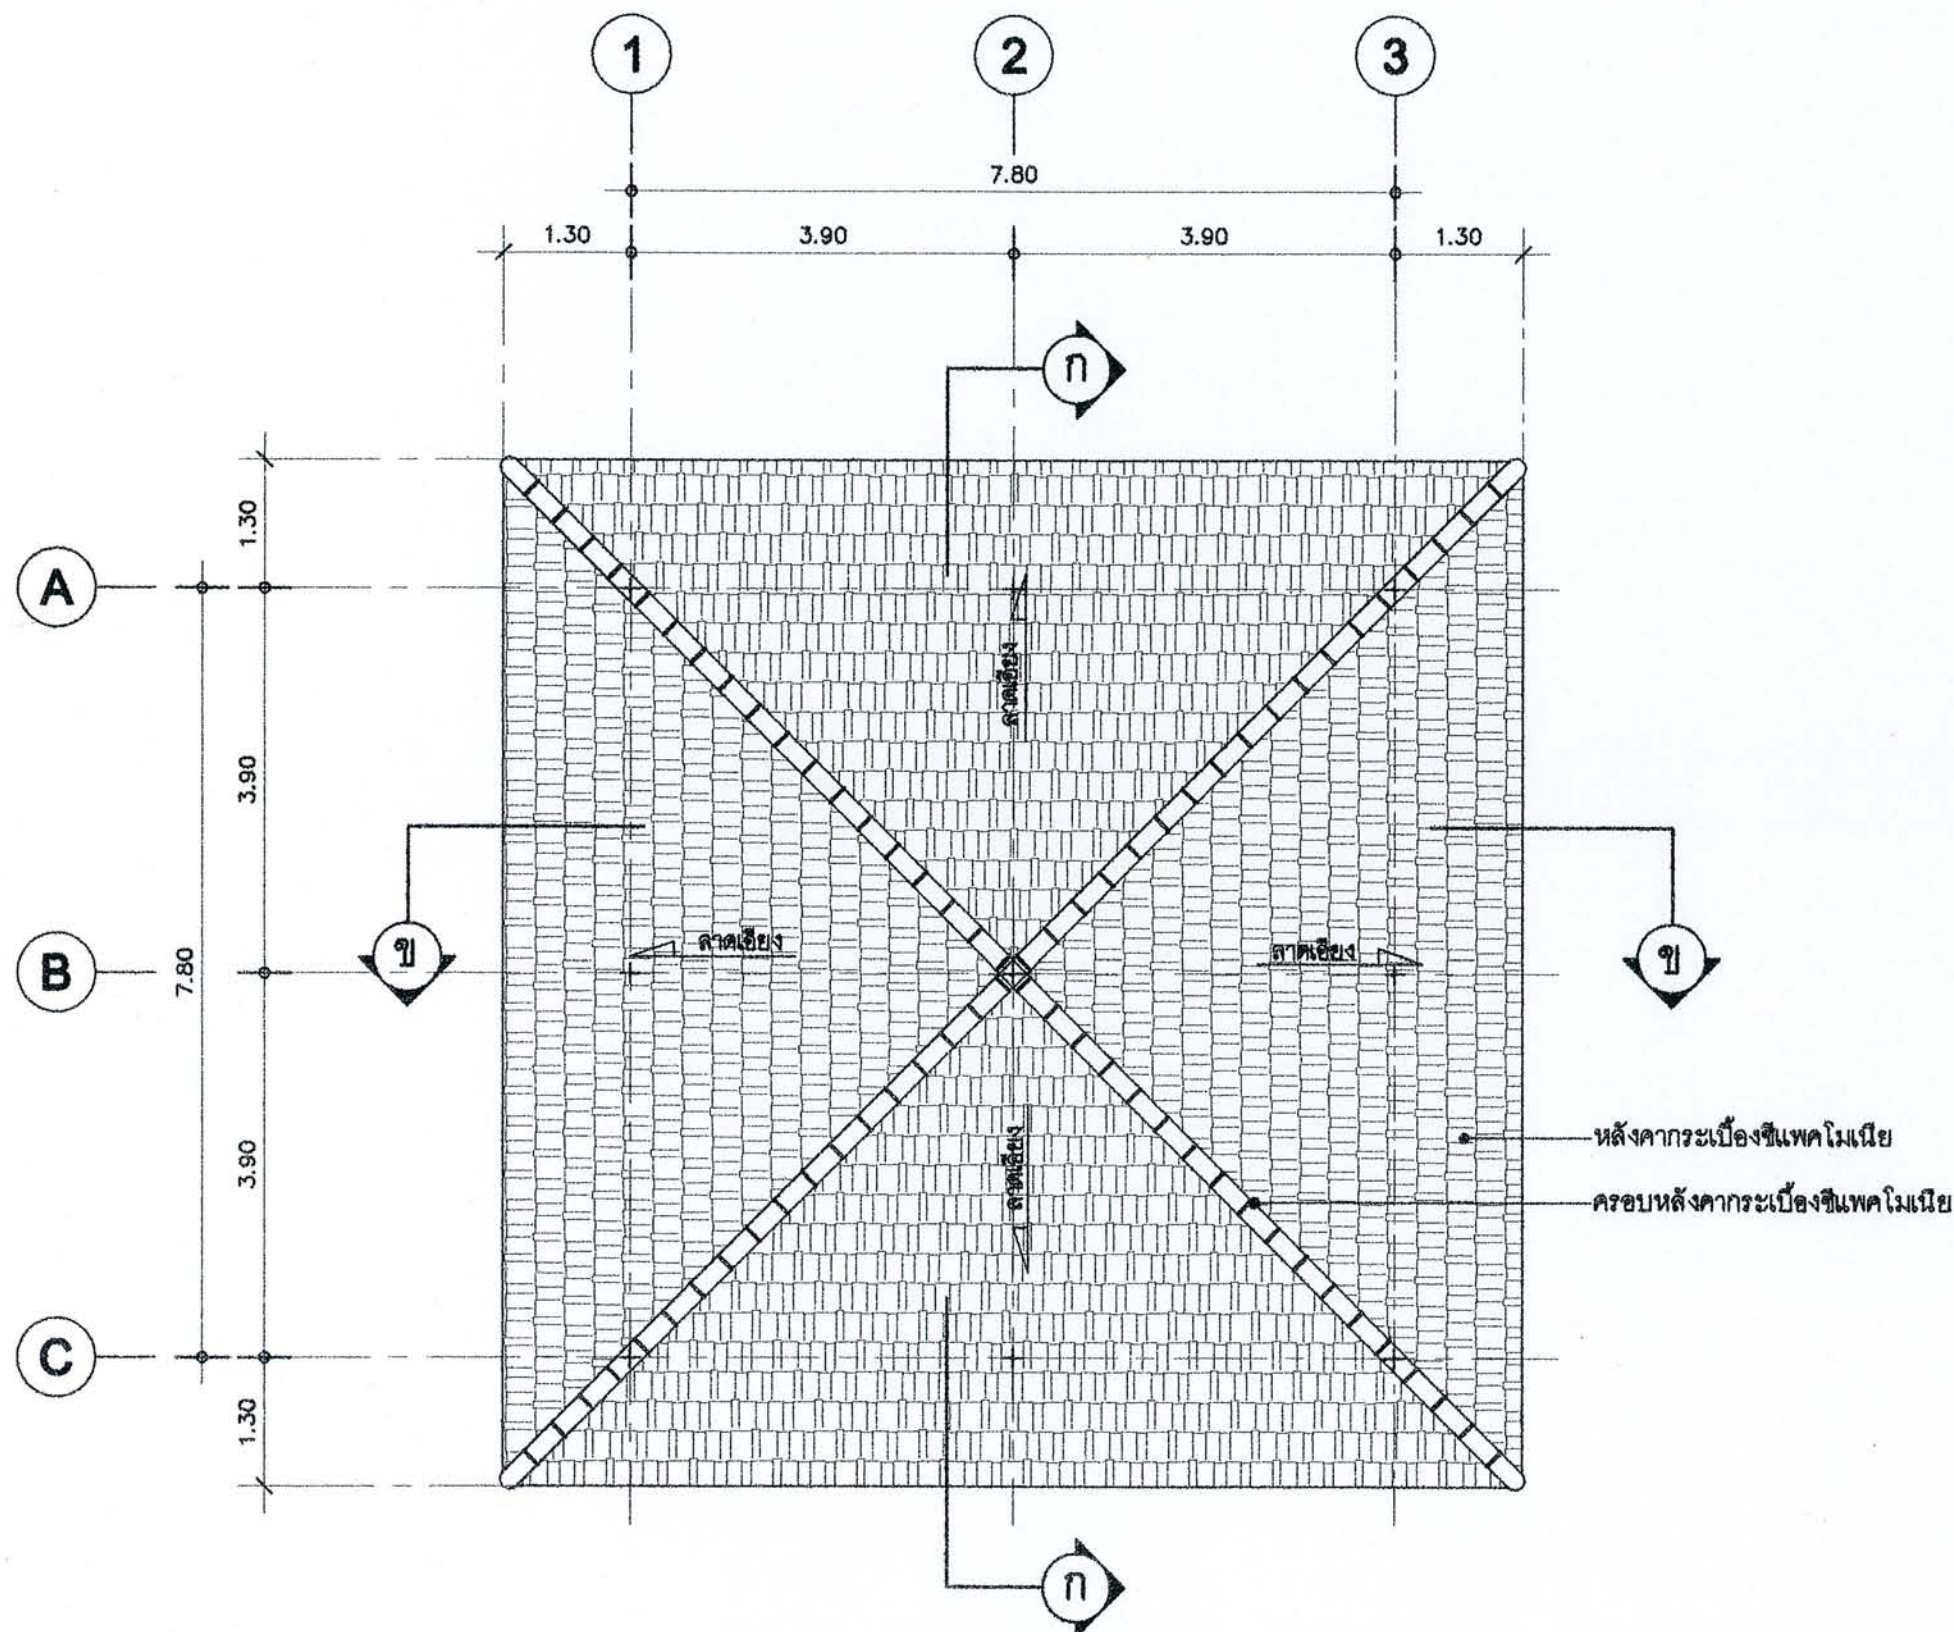

แปลนหลังคา

มาตราส่วน 1:75



สำนักงานโยธา
กรุงเทพมหานคร

โครงการ
แบบบ้านยิมเพื่อประชาชน

ตามนโยบาย

ม.ร.ว.สุขุมพันธุ์ บริพัตร ผู้ว่าฯกทม.
นายแพทย์ เติร์ดโกญจนาถ รองผู้ว่าฯกทม.
นายธีระชน มโนชัยปิฎก รองผู้ว่าฯกทม.
นายพงศ์ศักดิ์ แสนสุริย ปัสดาภรณ์

ผู้อำนวยการสำนักงานโยธา

นายจุมพล สันกาล

รองผู้อำนวยการสำนักงานโยธา

นายทวีศักดิ์ เดชประพันธ์

ผู้อำนวยการสำนักงานออกแบบ

นายจตุรงค์ ตนเอียด

หัวหน้ากลุ่มงานสถาปัตยกรรม

นายสินธุ์ชัย บุญภิรักษ์

หัวหน้ากลุ่มงานวิศวกรรม

นายธีระยุทธ คงสุวรรณเกียรติ

สถาปนิก

นางสาวลัดดาเมธย์ กาญจนะ

วิศวกรโครงสร้าง

นายวันโณ บริศไพฑูริย์

วิศวกรไฟฟ้า

นายกิตติพงษ์ จิระเดชากร

วิศวกรสุขาภิบาล

นางสาวเมธีรา สมหอม

วิศวกรเครื่องกล

นายช่างเขียนแบบ

นายณัฐพงศ์ ณรงค์บุญชูสุรินทร์

แบบ
026 บ้านทุ่งระพ

เจ้าของ

สถานที่

แบบแสดง

รูปด้าน 1

มาตราส่วน 1:75


FILE : เลขที่

วันที่ มิถุนายน 2553 A-06 06

คัดลอกปรับปรุงแบบ


รวมแผ่น 22

รายการแก้ไขแบบ

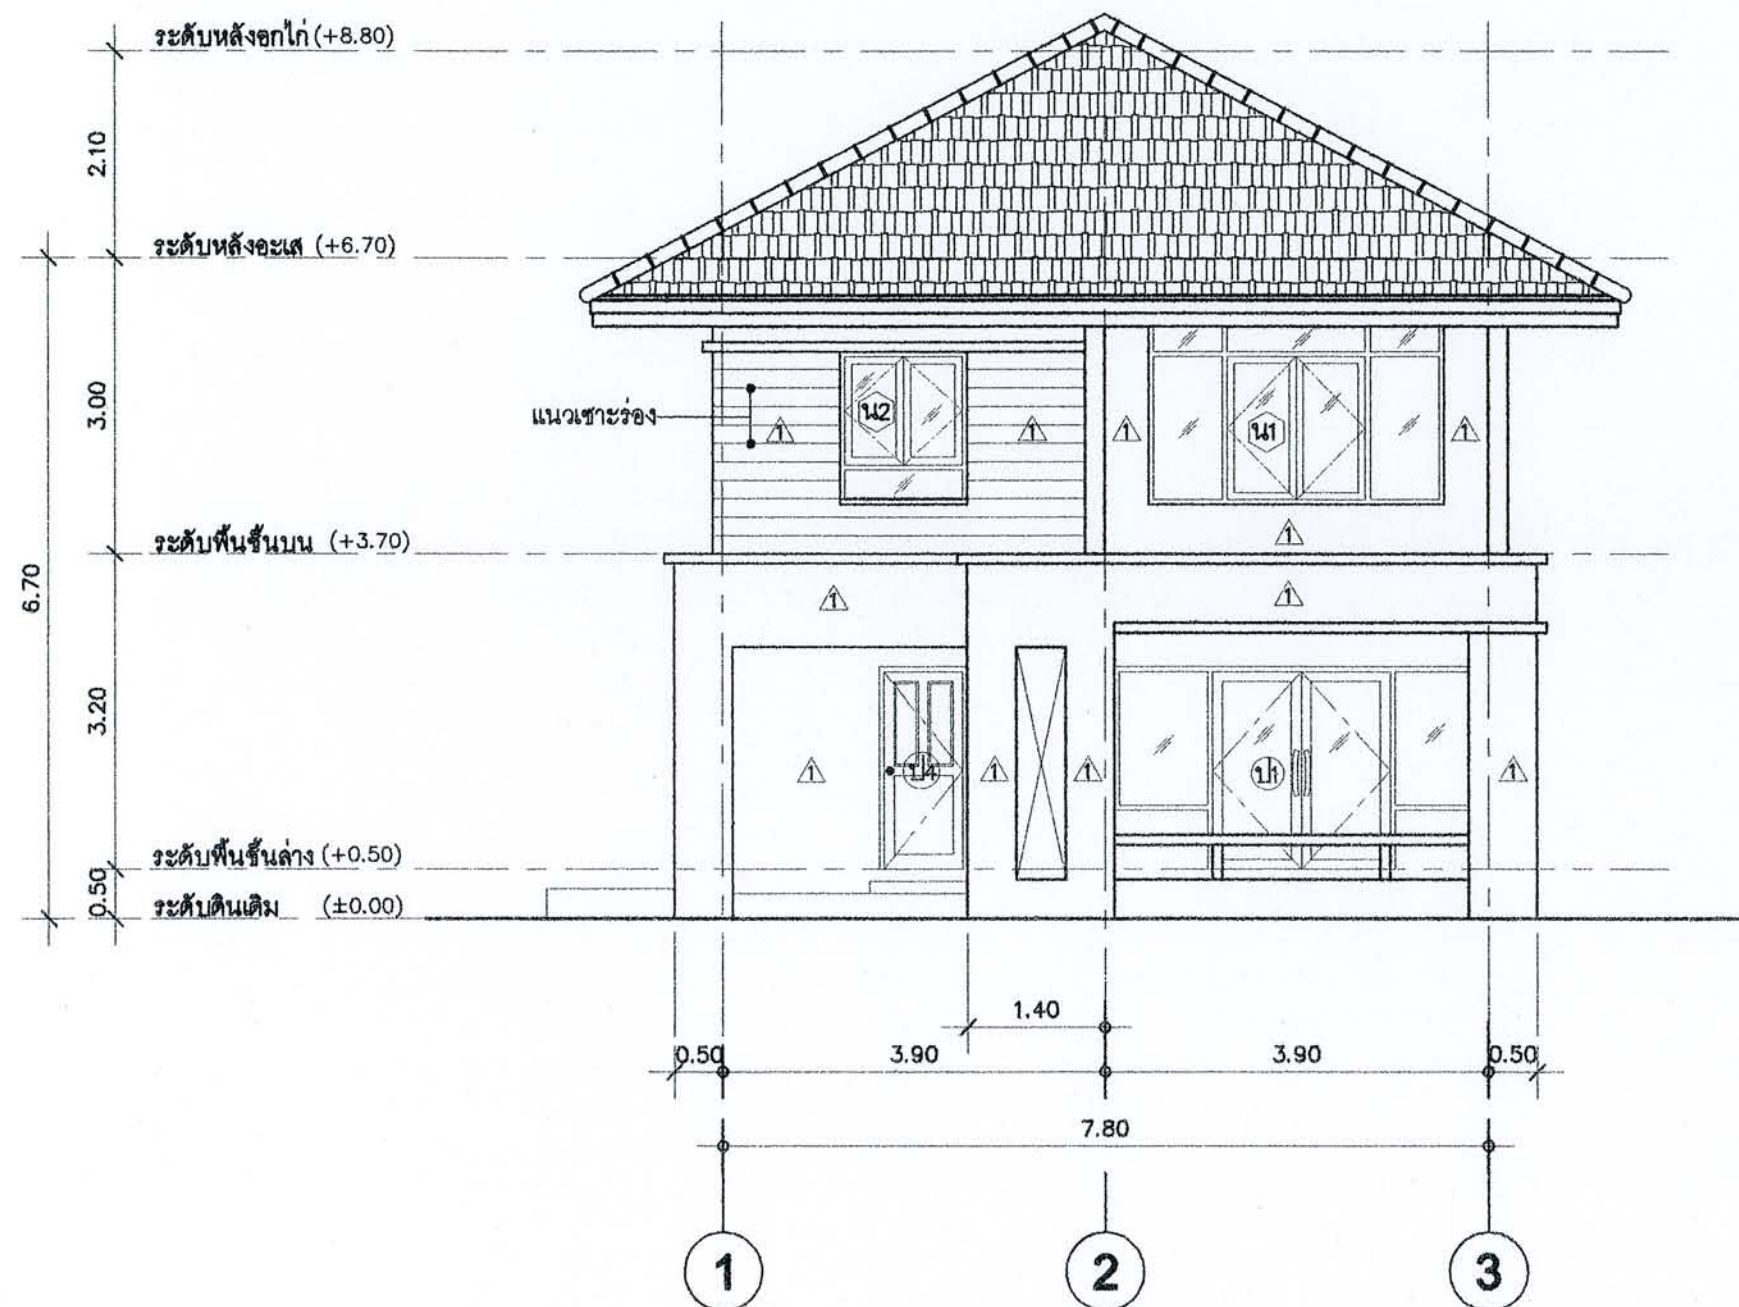

รูปด้าน 1

มาตราส่วน 1:75

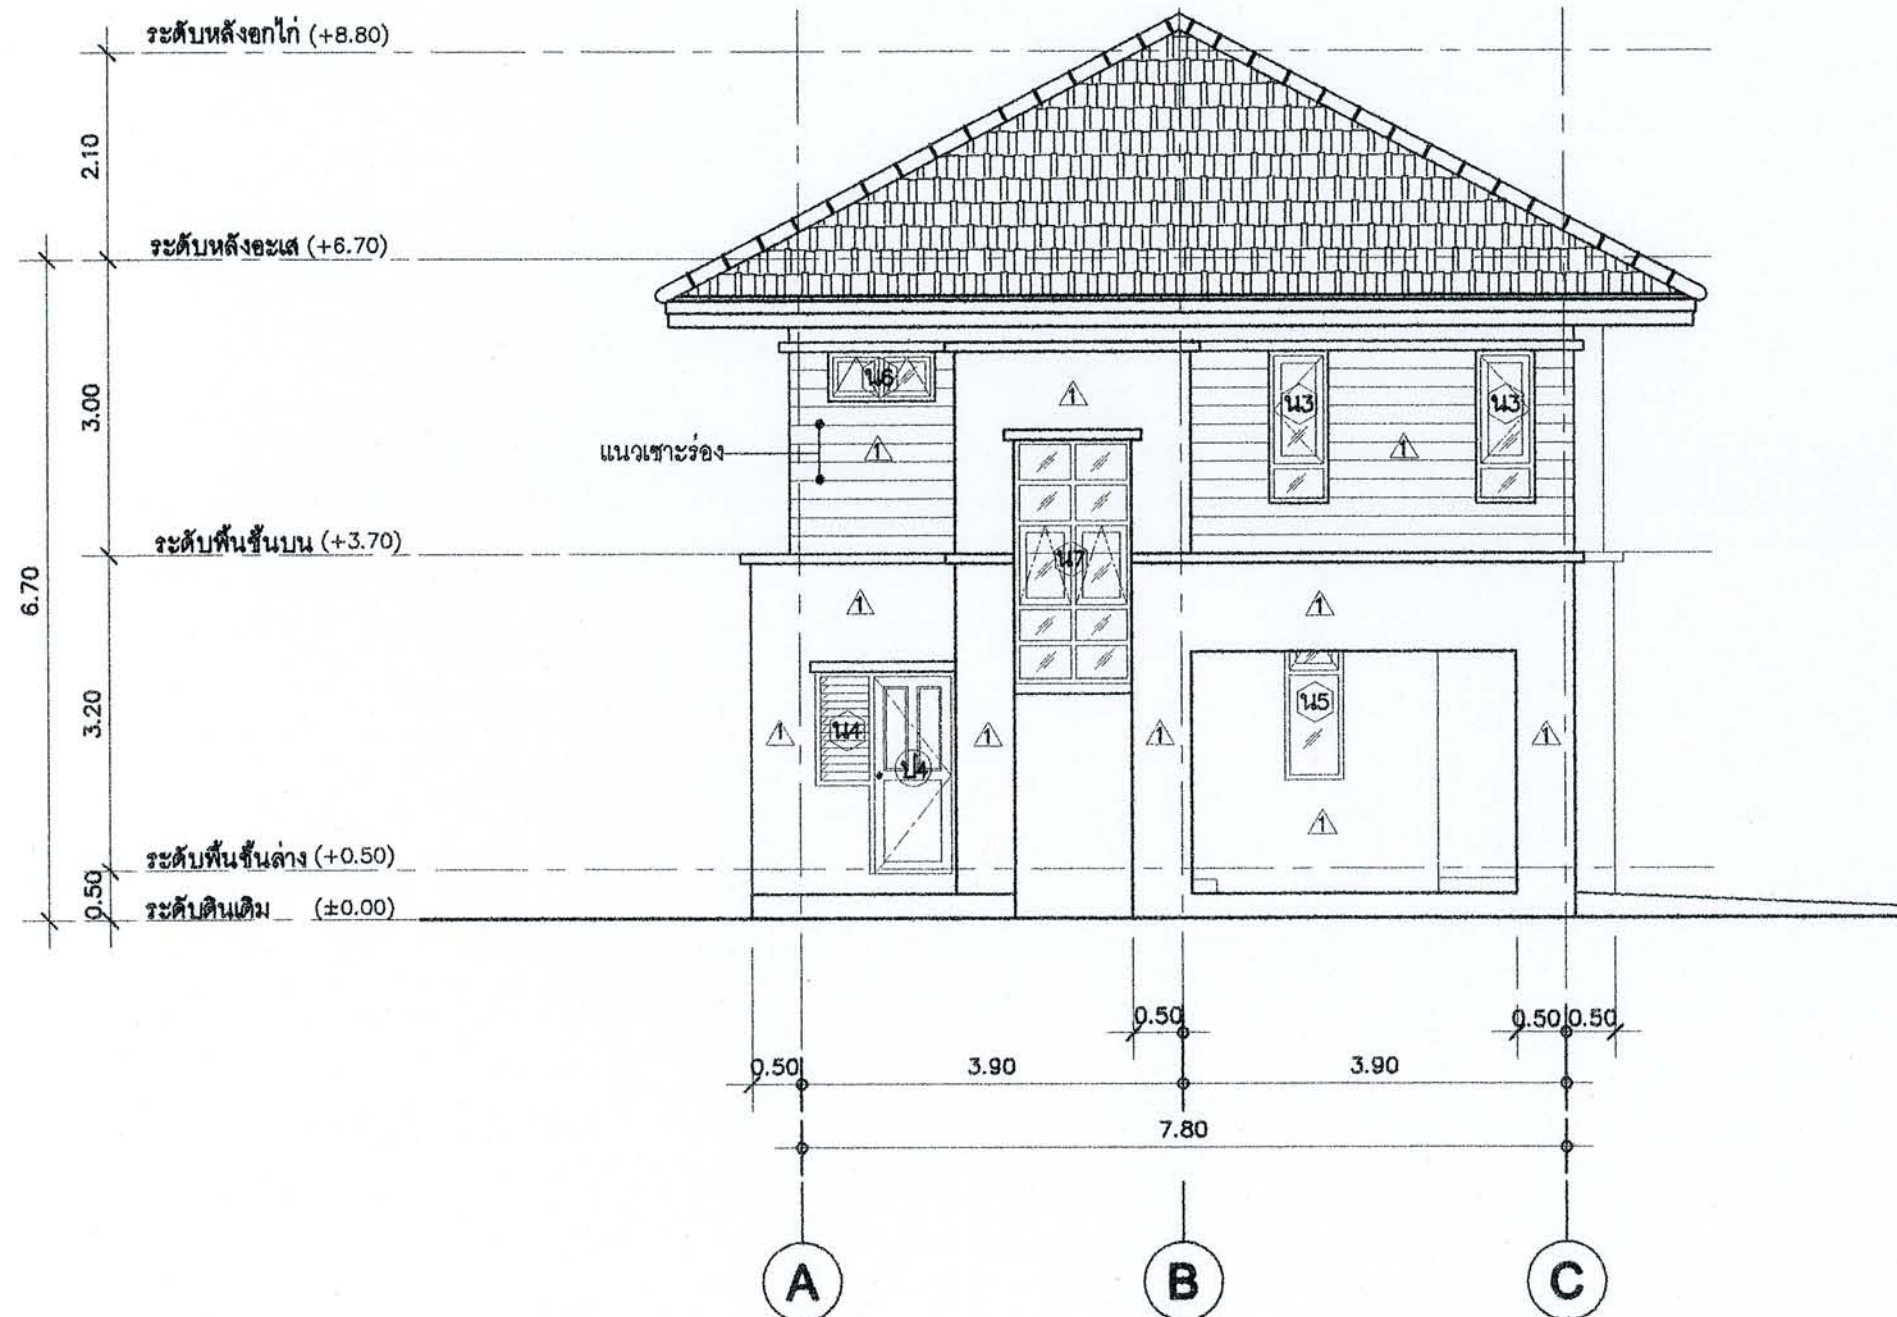

รูปด้าน 2
มาตราส่วน 1:75



สำนักงานโยธา
กรุงเทพมหานคร

โครงการ
แบบบ้านยืมเพื่อประชาชน

ตามนโยบาย

น.ร.สุชนพันธุ์ บริษัท สุวาทิต
นายพทพ เศรษฐ์ ร่องฟ้าทพ
นายธีระชน มโนชัยทพ ร่องฟ้าทพ
นายทศศักดิ์ สมสันต์ ปัสดาทพ

ผู้อำนวยการสำนักงานโยธา
นายจุมพล อภิบาล
รองผู้อำนวยการสำนักงานโยธา
นายวิศักดิ์ เลิศประพันธ์
ผู้อำนวยการสำนักงานออกแบบ
นายจตุรงค์ สอนเนียม
หัวหน้ากลุ่มงานสถาปัตยกรรม
นายสินธุ์ บุญปักษ์
หัวหน้ากลุ่มงานวิศวกรรม
นายธีระยุทธ คงสวัสดิ์ไชย

สถาปนิก
นางสาวสุนนมาลย์ กาญจนะ
วิศวกรโครงสร้าง
นายวิณ โฉม บัวโคกโพธิ์
วิศวกรไฟฟ้า
นายกิตติพงษ์ จิระเดชาก
วิศวกรสุขาภิบาล
นางสาวมณีนีรา สมนาคม
วิศวกรเครื่องกล

นายช่างเขียนแบบ
นายธีรพงศ์ อรรถโอบุญสุทนต์

แบบ
026 บ้านทุ่งระพ

เจ้าของ

สถานที่

แบบแสดง
รูปด้าน 2

มาตราส่วน 1:75


FILE : เลขที่ แผนที่

วันที่ มี.ค. 2553 A-07 07

คัลเลอร์ ปรีบรู๊จแบบ รวมแผ่น

22

รายการแก้ไขแบบ

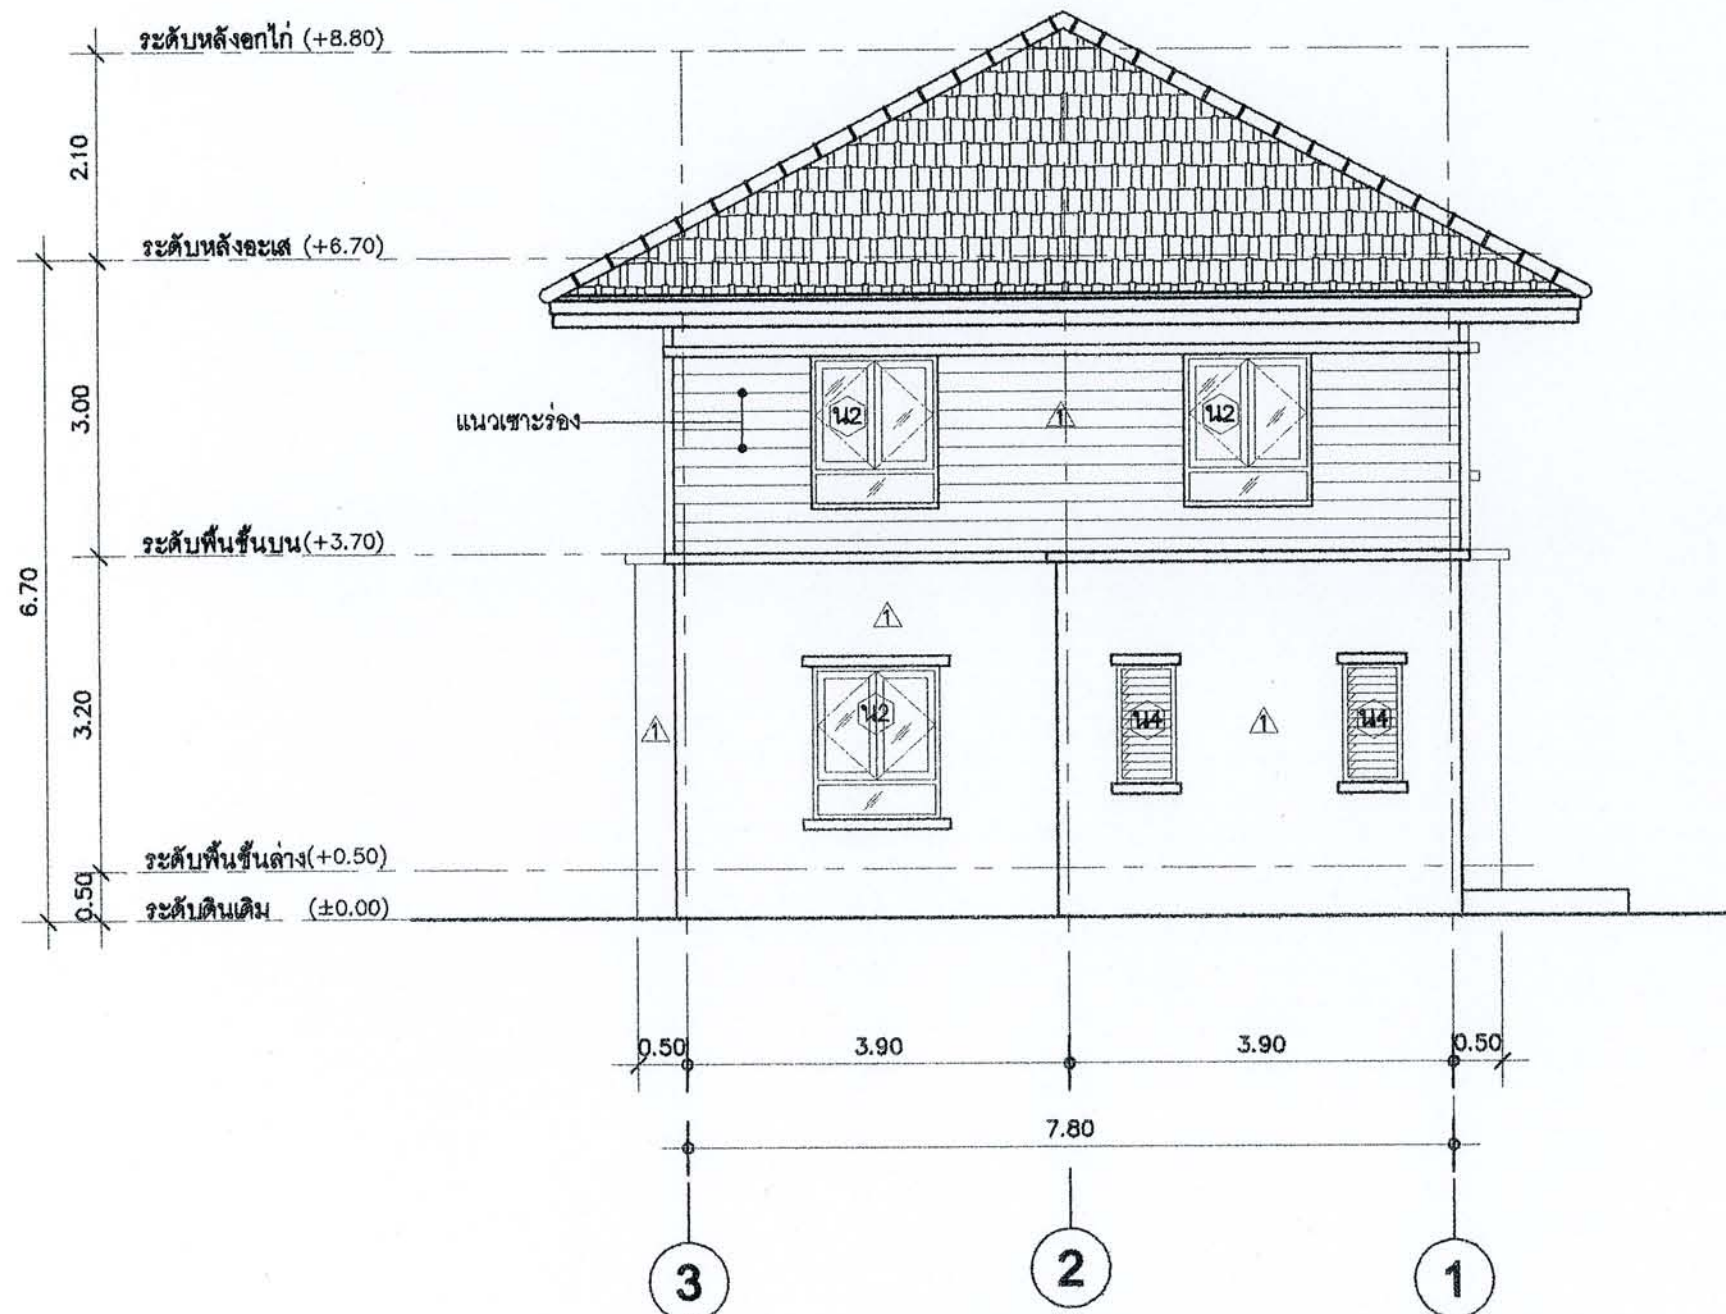

สำนักงานโยธา
กรุงเทพมหานคร

โครงการ
แบบบ้านยี่สิบเพื่อประชาชน

ตามนโยบาย

น.อ.จ.สุเมสันต์ บัณฑิต ผู้ว่าฯกทม.
นายพรเทพ เศรษฐ์ ร่องจั่วฯกทม.
นายธีระชน มโนชัยบุตย์ ร่องจั่วฯกทม.
นายพงษ์ศักดิ์ แสนสันต์ ปลัดฯกทม.

ผู้สนับสนุนโครงการโยธา

นายจุมพล สันภาพล

รองผู้อำนวยการสำนักงานโยธา

นายทวีศักดิ์ เลิศประพันธ์

ผู้อำนวยการสำนักงานออกแบบ

นายจตุรงค์ สมน้อย

หัวหน้ากลุ่มงานสถาปัตยกรรม

นายสินธุ์ชัย บุญยักษ์

หัวหน้ากลุ่มงานวิศวกรรม

นายธีระยุทธ คงสวัสดิ์เสถียร

สถาปนิก

นางสาวสุมนนภณ์ กาญจนะ

วิศวกรโครงสร้าง

นายวัฒน์ โน บัณฑิต

วิศวกรไฟฟ้า

นายกิตติพงษ์ จิระเดชาก

วิศวกรสุขาภิบาล

นางสาวมณจิรา สมน้อม

วิศวกรเครื่องกล

นายช่างเขียนแบบ

นายณัฐพงศ์ ณรงค์บุญชู

แบบ
026 บ้านพุระพง

เจ้าของ

สถานที่

แบบแสดง
รูปด้าน 3

มาตราส่วน 1: 75

FILE : เลขที่ แผนที่

วันที่ 2553 A-08 08

ตรวจสอบแบบ รวมน

22

รายการแก้ไขแบบ



สำนักงานโยธา
กรุงเทพมหานคร

โครงการ
แบบบ้านขี้มเพื่อประชาชน

ตามนโยบาย

ม.ร.ว.สุขุมพันธุ์ บริพัตร ผู้ว่าฯกทม.
นายพรเทพ เศรษฐินกุลย์ รองผู้ว่าฯกทม.
นายธีระชน มโนวิทย์กุลย์ รองผู้ว่าฯกทม.
นายพงศ์ศักดิ์ เตมสันต์ ปลัดฯกทม.

ผู้อำนวยการสำนักงานโยธา

นายจุมพล สันภาพ

รองผู้อำนวยการสำนักงานโยธา

นายทวีศักดิ์ เดชประพันธ์

ผู้อำนวยการสำนักงานออกแบบ

นายจตุรงค์ สมน้อย

หัวหน้ากลุ่มงานสถาปัตยกรรม

นายสินธุ์ชัย บุญปักษ์

หัวหน้ากลุ่มงานวิศวกรรม

นายธีระยุทธ คงสวัสดิ์

สถาปนิก

นางสาวสุนนภรณ์ กาญจนะ

วิศวกรโครงสร้าง

นายวันโน บัวดี

วิศวกรไฟฟ้า

นายกิตติพงษ์ จิระเดชากร

วิศวกรสุขาภิบาล

นางสาวณณชิตา สมหนอง

วิศวกรเครื่องกล

นายช่างเขียนแบบ

นายณัฐพงศ์ ณรงค์บุญญาฤทธิ์

แบบ
026 บ้านพุระพง

เจ้าของ

สถานที่

แบบแสดง

รูปด้าน 4

มาตราส่วน 1: 75


FILE : เลขที่ แผนที่

วันที่ มิถุนายน 2553 A-09 09

คัดลอก ปรับปรุงแบบ รวมแผ่น


22

รายการแก้ไขแบบ

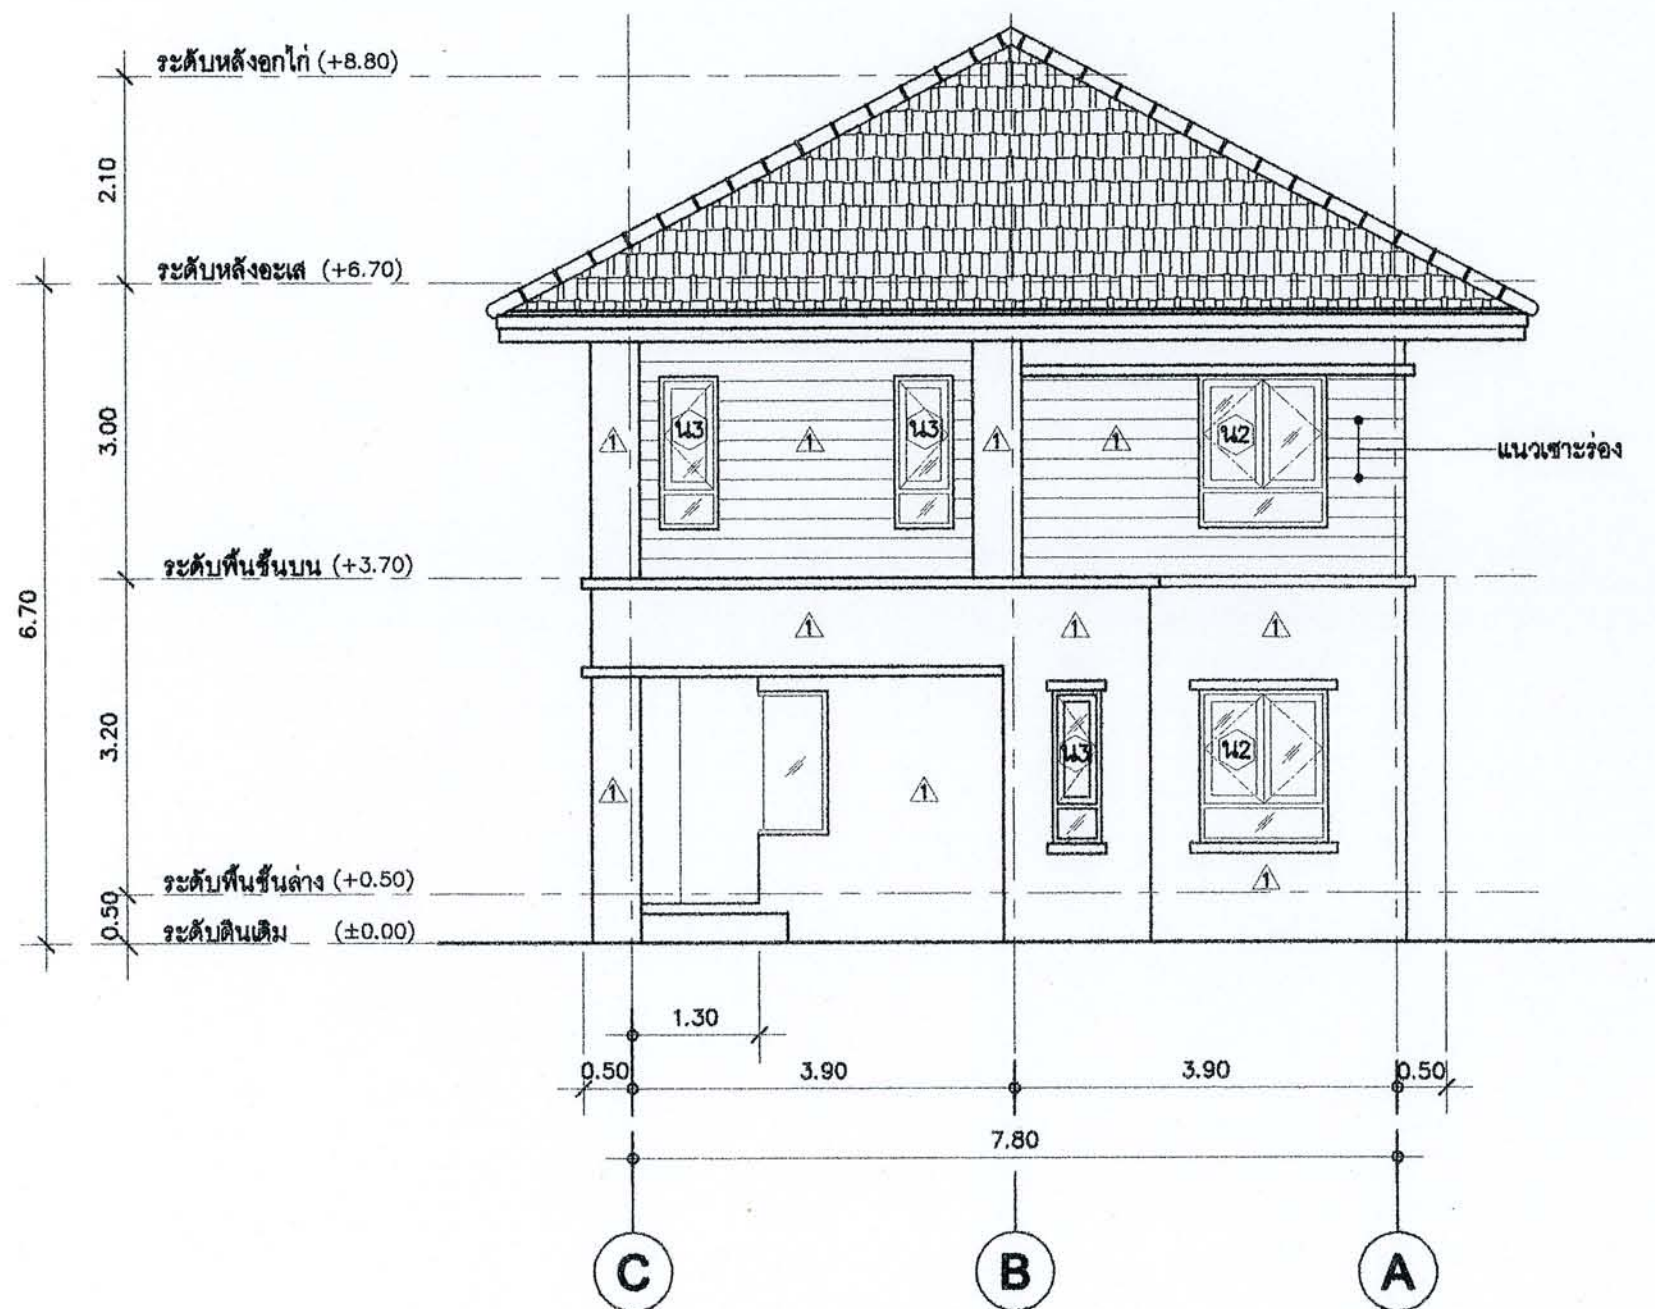

รูปด้าน 4

มาตราส่วน 1: 75

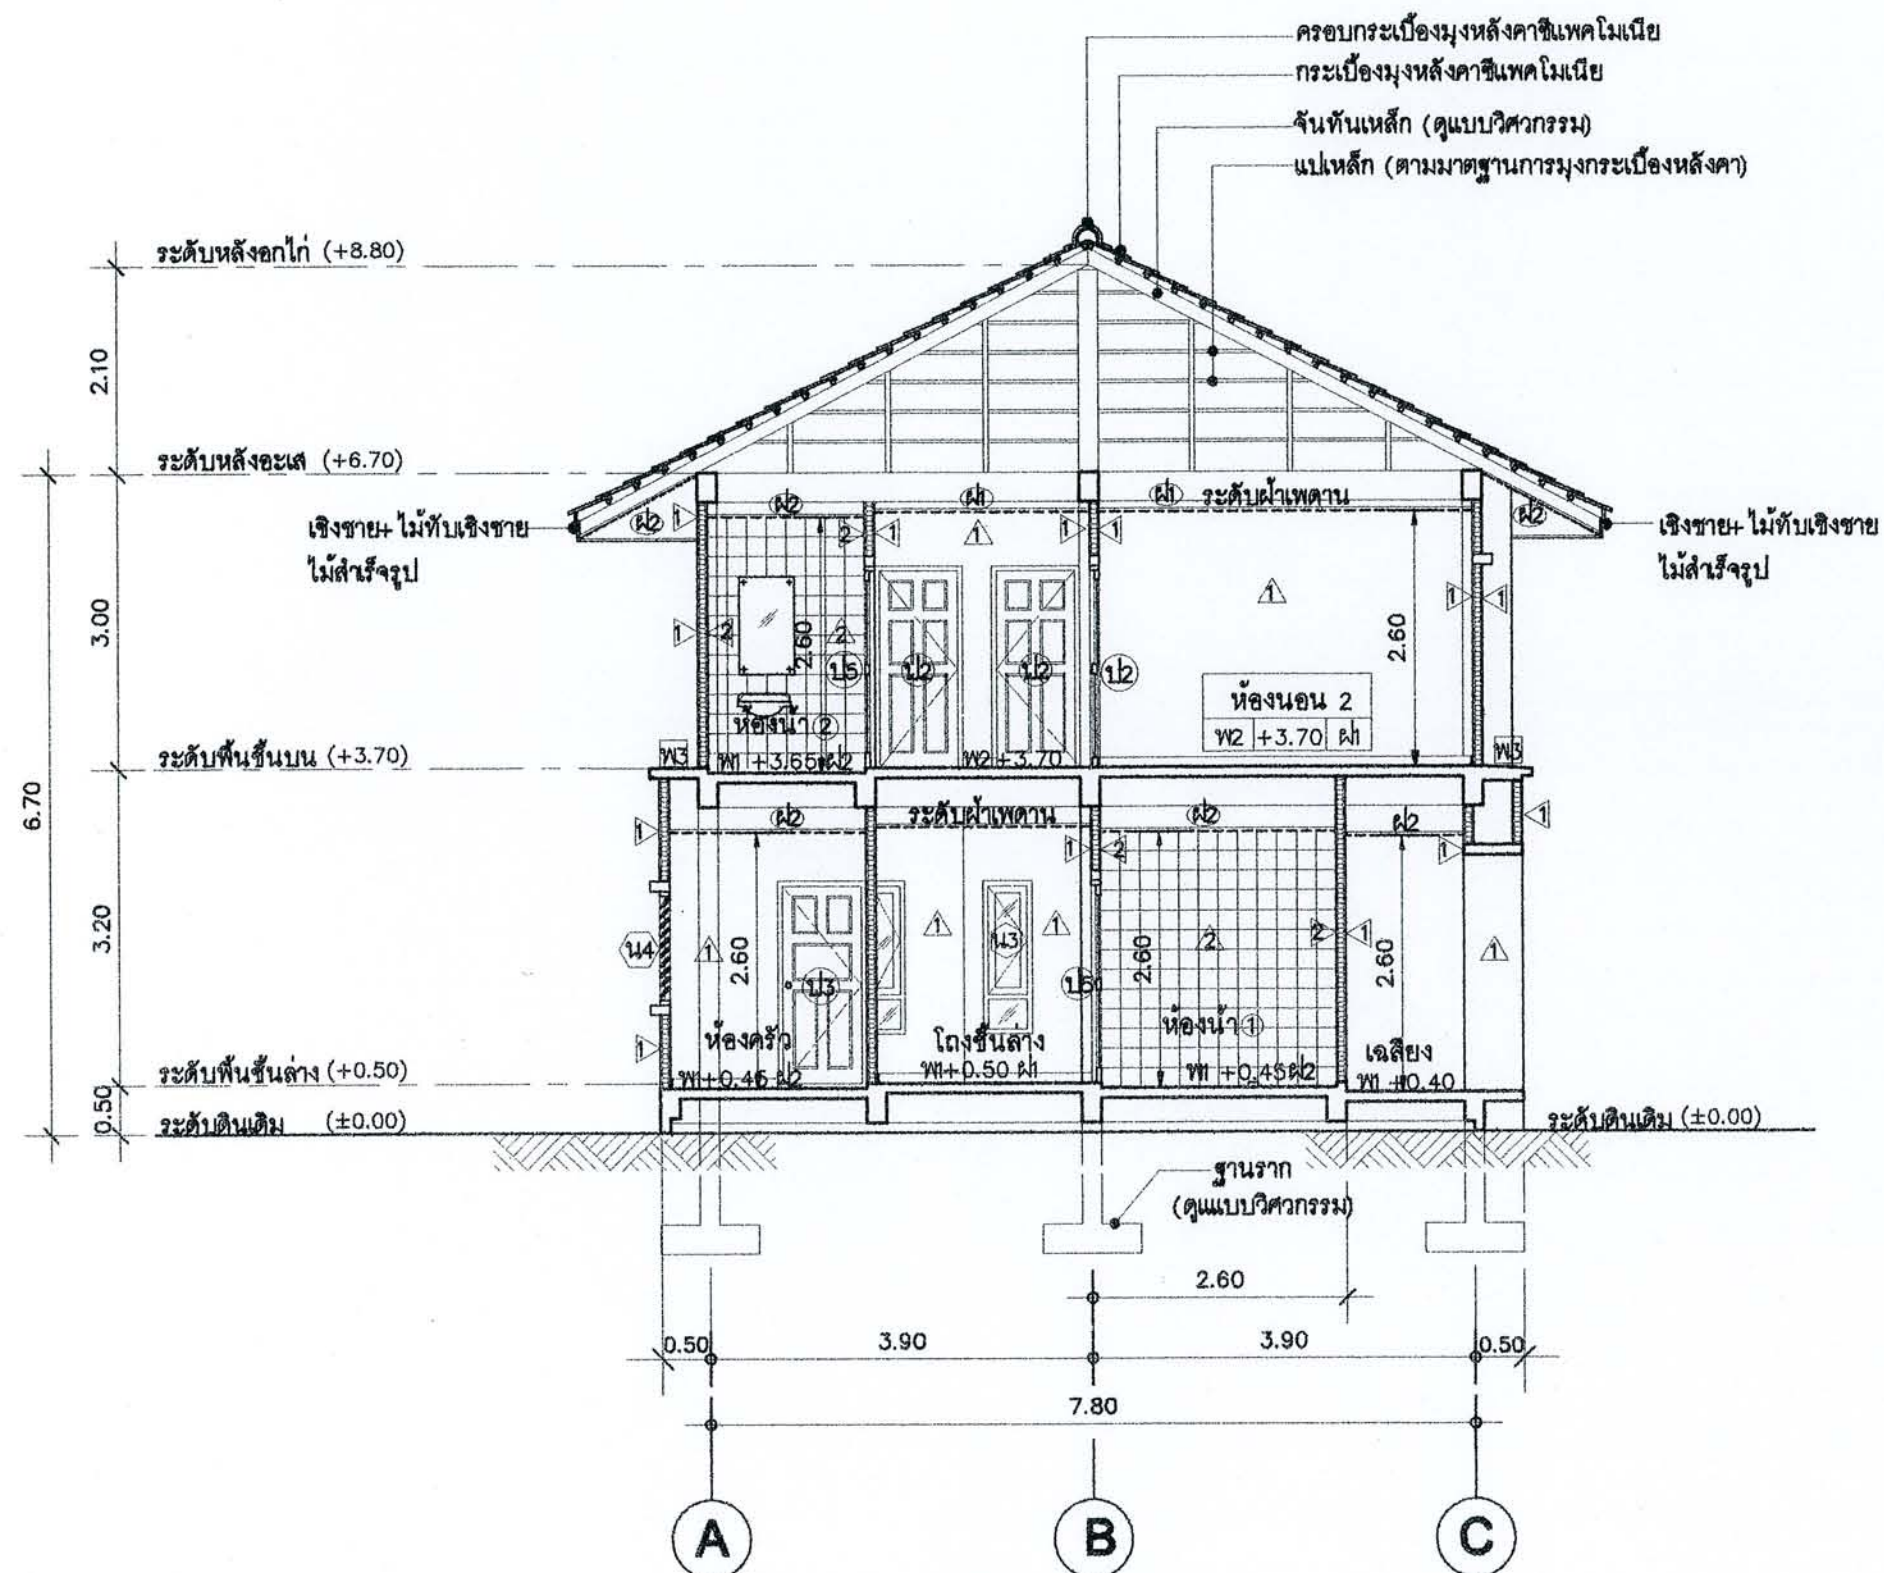

รูปตัด ก-ก
มาตราส่วน 1 : 75



สำนักงานโยธา
กรุงเทพมหานคร

โครงการ
แบบบ้านขึ้นเพื่อประชาชน

ตามนโยบาย

น.ร.สุเมธพันธ์ บริพัตร สุวาทิต
นายแพทย์ เศรษฐกิจ รองผู้อำนวยการ
นายธีระชน นิมิตต์บุตร รองผู้อำนวยการ
นายพงศ์ศักดิ์ แสนสันต์ ปลัดกรุงเทพมหานคร

ผู้อำนวยการสำนักงานโยธา
นายจุมพล สันภาพ
รองผู้อำนวยการสำนักงานโยธา
นายทวีศักดิ์ เลิศประพันธ์
ผู้อำนวยการสำนักงานออกแบบ
นายจตุรงค์ สอนเนียม
หัวหน้ากลุ่มงานสถาปัตยกรรม
นายสินธุ์ชัย บุญปักษ์
หัวหน้ากลุ่มงานวิศวกรรม
นายธีระยุทธ คงสุวรรณ

สถาปนิก
นางสาวสุนนมาลย์ กาญจนะ
วิศวกรโครงสร้าง
นายวันโย บริพัตร
วิศวกรไฟฟ้า
นายกิตติพงษ์ จิระเดชาก
วิศวกรสุขาภิบาล
นางสาวมณฑิรา สมหอม
วิศวกรเครื่องกล

นายช่างเขียนแบบ
นายณัฐพงศ์ ณรงค์บุญชู

แบบ
026 บ้านทุ่งระพ


เจ้าของ
สถานที่

แบบแสดง
รูปตัด ก-ก

มาตราส่วน 1: 75

FILE :
วันที่ มิถุนายน 2553
ครั้งที่ 10
ครั้งที่ 22

รายการแก้ไขแบบ

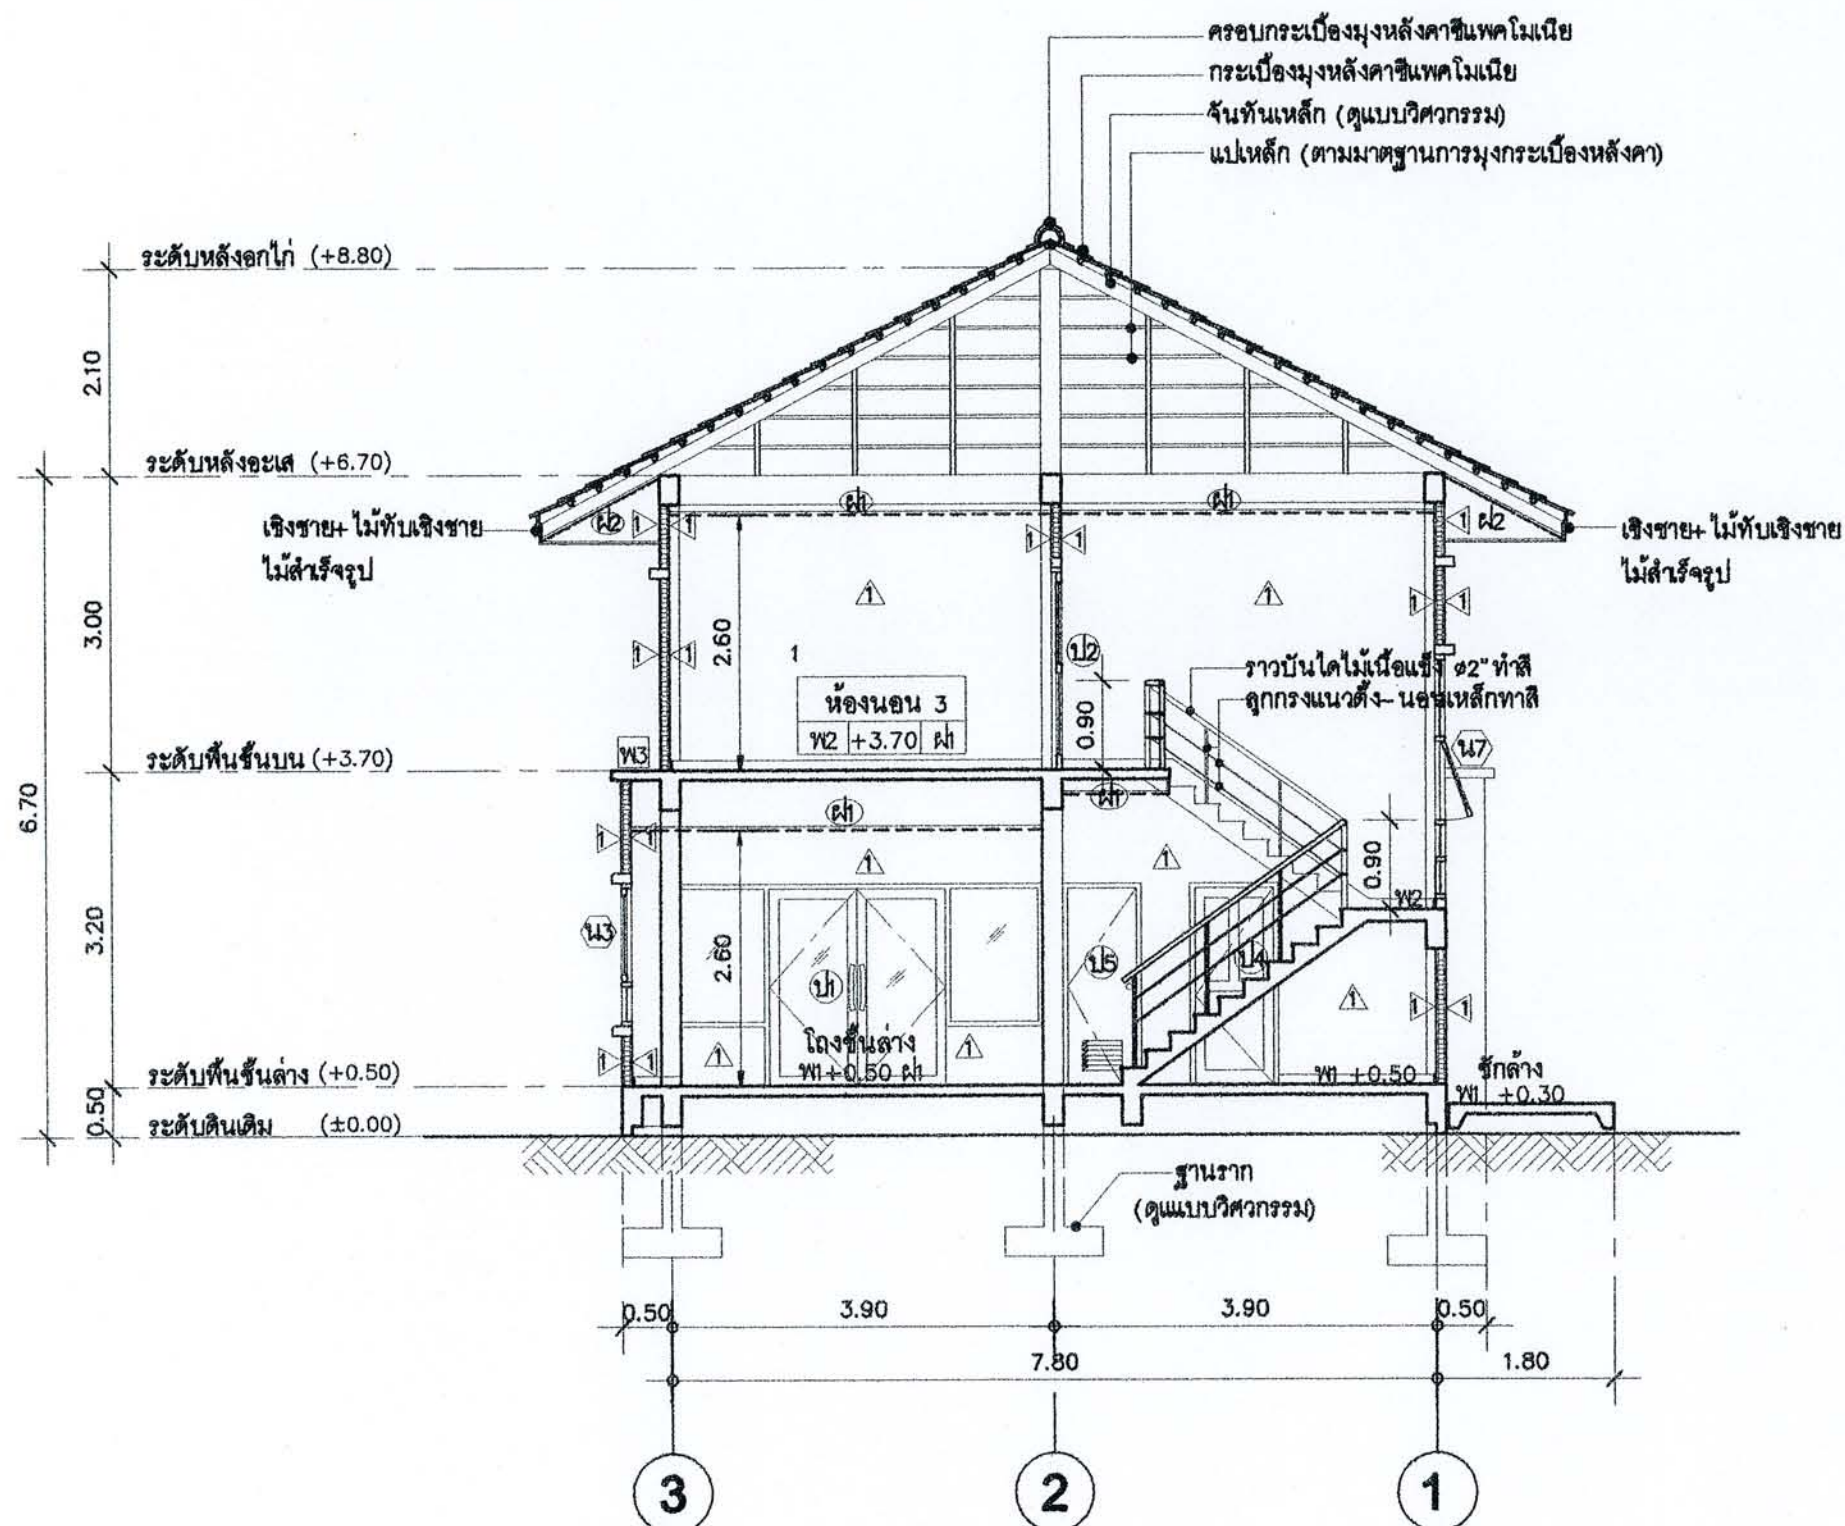

รูปตัด ข-ข
มาตราส่วน 1 : 75



สำนักงานโยธา
กรุงเทพมหานคร

โครงการ
แบบบ้านขึ้นเพื่อประชาชน

ตามนโยบาย

ม.ร.ว.สุขุมพันธุ์ บริพัตร ผู้ว่าฯกทม.
นายแพทย์ เจริญพร รอดูว่ากทม.
นายธีระชน มโนวิทย์ รอดูว่ากทม.
นายพงศ์ศักดิ์ เทมสันต์ ปลัดฯกทม.

ผู้อำนวยการสำนักงานโยธา

นายจุมพล สันภาพ

รองผู้อำนวยการสำนักงานโยธา

นายวิศักดิ์ เลิศประพันธ์

ผู้อำนวยการสำนักงานออกแบบ

นายจตุรงค์ สอนเนียม

หัวหน้ากลุ่มงานสถาปัตยกรรม

นายสินธุ์ชัย บุญปักษ์

หัวหน้ากลุ่มงานวิศวกรรม

นายธีระยุทธ คาสวรรค์ดิษฐ์

สถาปนิก

นางสาวสมนมาลย์ กาญจนะ

วิศวกรโครงสร้าง

นายวันโน บรีทใหญ่ชัย

วิศวกรไฟฟ้า

นายภคิพงษ์ จิระเดชาก

วิศวกรสุขาภิบาล

นางสาวมณจิรา สมน้อม

วิศวกรเครื่องกล

นายช่างเขียนแบบ

นายณัฐพงศ์ ณรงค์บุญญาสุทนต์

แบบ
026 บ้านพระพร

เจ้าของ

สถานที่

แบบแสดง
รูปตัด ข-ข

มาตราส่วน 1:75

FILE : เลขที่ 11

วันที่ 11

วันที่ 11

รวมแผ่น 22

รายการแก้ไขแบบ



สำนักงานโยธา
กรุงเทพมหานคร

โครงการ
แบบบ้านขี้เหล็กประชาชน

ตามนโยบาย

ม.ร.ว.สุขุมพันธุ์ บริพัตร ผู้ว่าฯ กทม.
นายพรเทพ เตชะไพบูลย์ รองผู้ว่าฯ กทม.
นายธีระชน นิมมิทธิ์กุลย์ รองผู้ว่าฯ กทม.
นายพงศ์พิทักษ์ เสน่ห์สันต์ ปลัดฯ กทม.

ผู้อำนวยการสำนักงานโยธา

นายจุมพล สำนากุล

รองผู้อำนวยการสำนักงานโยธา

นายทวีศักดิ์ เลิศประพันธ์

ผู้อำนวยการสำนักงานออกแบบ

นายสุรพงศ์ สอนเนียม

หัวหน้ากองงานสถาปัตยกรรม

นายสันติสุข บุญปักษ์

หัวหน้ากองงานวิศวกรรม

นายธีระยุทธ คงศรีศรีเจริญ

สถาปนิก

นางสาวสุมนมาลย์ กาญจนะ

วิศวกรโครงสร้าง

นายวิวัฒน์ บริรักษ์

วิศวกรไฟฟ้า

นายวิวัฒน์พงษ์ จิระเดชาก

วิศวกรสุขาภิบาล

นางสาวณัฏฐา สัมพร

วิศวกรเครื่องกล

นายช่างเขียนแบบ

นายณัฐพงศ์ ณรงค์บุญชู

แบบ

026 บ้านทุ่งระพ

เจ้าของ

สถานที่

แบบแสดง

แบบขยายประตู

มาตราส่วน 1:50

FILE :


วันที่ 2553

ชื่อโครงการ

รวมแผ่น

22


รายการแก้ไขแบบ

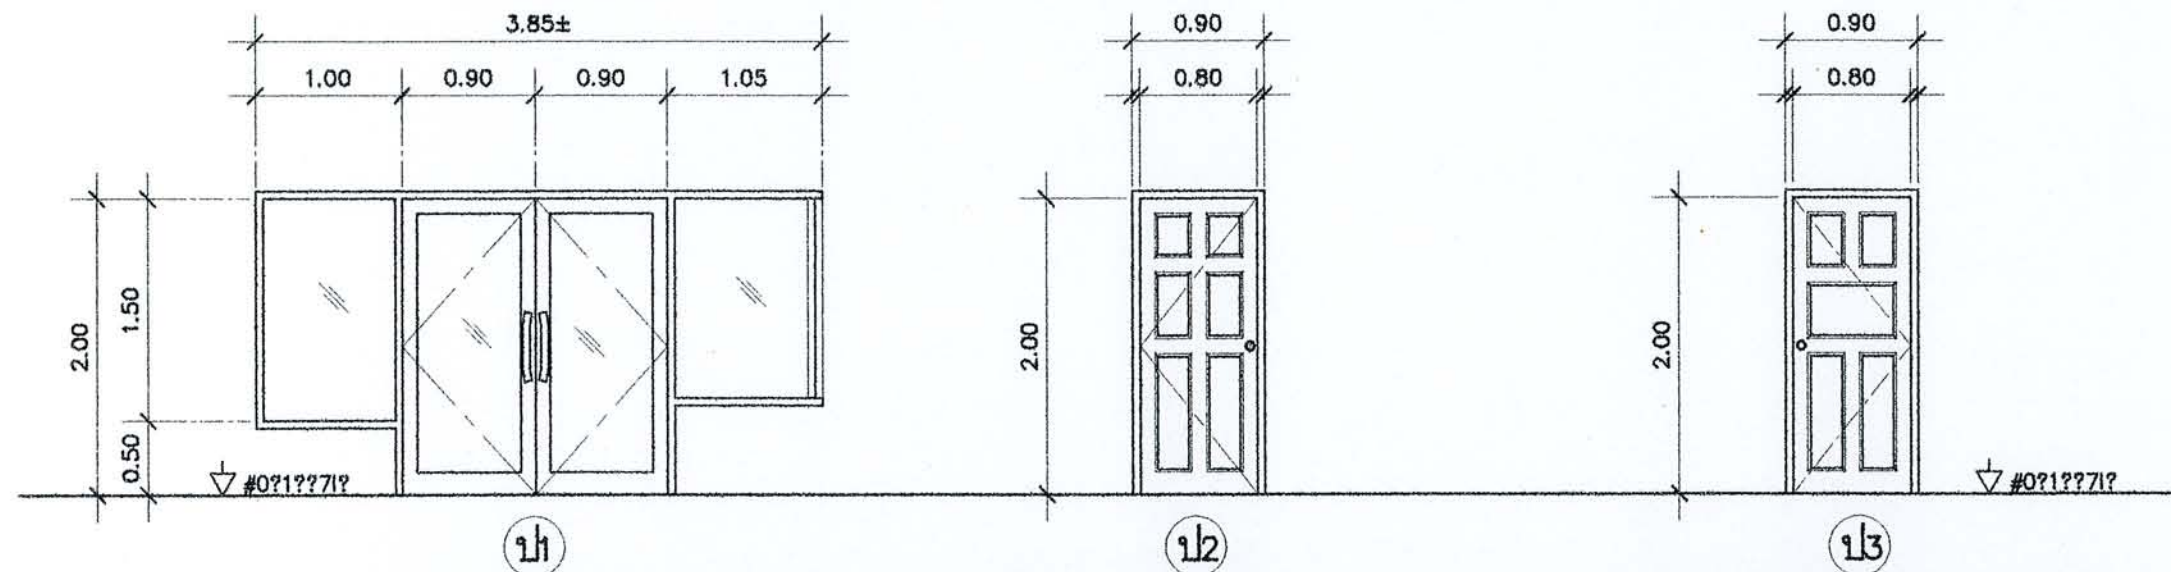

ลักษณะบาน	ประตูบานสวิงคู่ พร้อมช่องแสงกระจกติดตาย
วงกบ	อลูมิเนียมสีธรรมชาติ
กรอบบาน	อลูมิเนียมสีธรรมชาติ
ลูกพับ	?#0??C??1?A??5??5" + ?2 6 II.
อุปกรณ์	?#-117-?1?A%0-8??#?L?#? 8?

ลักษณะบาน	ประตูบานเปิด
วงกบ	ไม้เนื้อแข็ง 2"x4"
กรอบบาน	กรอบบานไม้เนื้อแข็ง 1 1/2"x4"
ลูกพับ	DI11??7I-A?G?+?12??5"? 2 ?12?
อุปกรณ์	?#-117-?1?A%0-8??#?L?#? 8?

ลักษณะบาน	ประตูบานเปิด
วงกบ	ไม้เนื้อแข็ง 2"x4"
กรอบบาน	กรอบบานไม้เนื้อแข็ง 1 1/2"x4"
ลูกพับ	DI11??7I-A?G?+?12??5"? 2 ?12?
อุปกรณ์	?#-117-?1?A%0-8??#?L?#? 8?

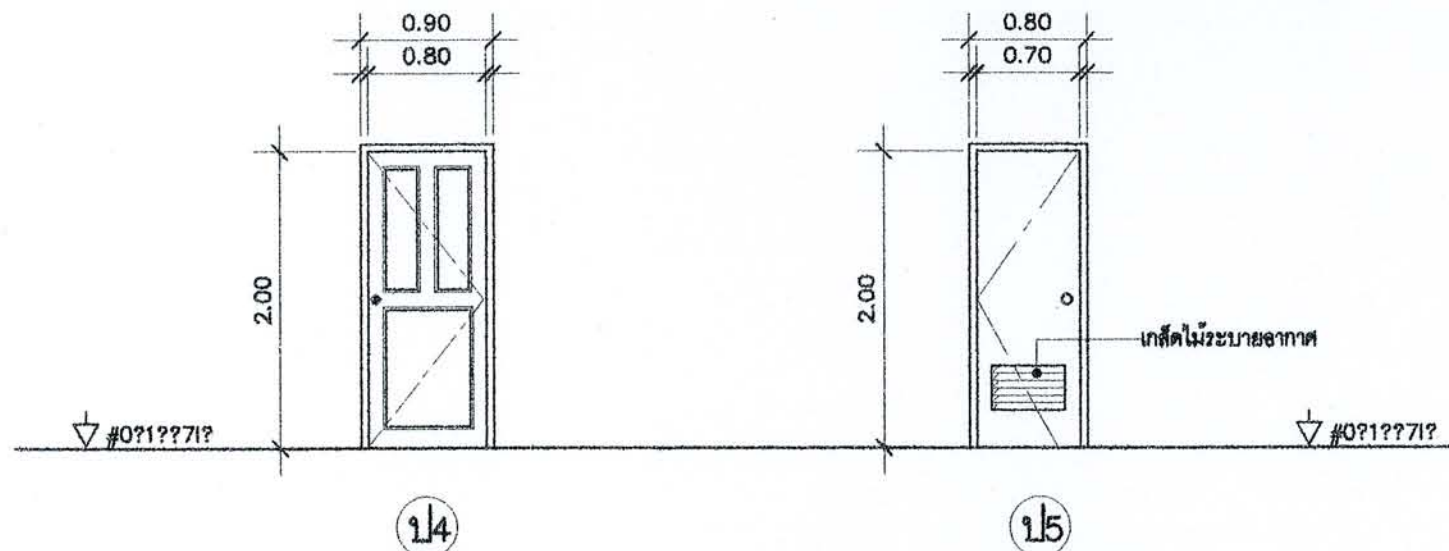

ลักษณะบาน	ประตูบานเปิด
วงกบ	ไม้เนื้อแข็ง 2"x4"
กรอบบาน	กรอบบานไม้เนื้อแข็ง 1 1/2"x4"
ลูกพับ	DI11??7I-A?G?+?12??5"? 2 ?12?
อุปกรณ์	?#-117-?1?A%0-8??#?L?#? 8?

ลักษณะบาน	ประตูบานเปิด
วงกบ	ไม้เนื้อแข็ง 2"x4"
กรอบบาน	กรอบบานไม้เนื้อแข็งกันชื้น ทำสี
ลูกพับ	DI11-1?"2??1?
อุปกรณ์	?#-117-?1?A%0-8??#?L?#? 8?

แบบขยายประตู 1:50



สำนักงานโยธา
กรุงเทพมหานคร

โครงการ
แบบบ้านยี่สิบสี่ห้อง

ตามนโยบาย

ม.ร.ว.สุขุมพันธุ์ บริพัตร ผู้ว่าฯกทม.
นายพรเทพ เกษมทรัพย์ รองผู้ว่าฯกทม.
นายธีระชน มโนวิมลปัดย์ รองผู้ว่าฯกทม.
นายพงศ์ศักดิ์ เศรษฐินต์ ปลัดฯกทม.

ผู้อำนวยการสำนักงานโยธา

นายจุมพล สันกาลาด

รองผู้อำนวยการสำนักงานโยธา

นายทวีศักดิ์ เต็มประพันธ์

ผู้อำนวยการสำนักงานออกแบบ

นายจตุรงค์ สันติธรรม

หัวหน้ากลุ่มงานสถาปัตยกรรม

นายสินธุ์ชัย บุญนิกข

หัวหน้ากลุ่มงานวิศวกรรม

นายธีระยุทธ คงสวัสดิ์เจริญ

สถาปนิก

นางสาวสุมนะภรณ์ กาญจนะ

วิศวกรโครงสร้าง

นายวิวัฒน์ ไบ บรีดโพธิ์

วิศวกรไฟฟ้า

นายกิจติพงษ์ จิระเดชาก

วิศวกรสุขาภิบาล

นางสาวมณจิรา สมน้อม

วิศวกรเครื่องกล

นายช่างเขียนแบบ

นายณัฐพัชร์ ณรงค์บุญญาสุท

แบบ
026 บ้านพระพรหม

เจ้าของ

สถานที่

แบบแสดง
แบบขยายหน้าต่าง

มาตราส่วน 1:50


FILE : เลขที่

วันที่ 13 มิถุนายน 2553 A-13 13

คิดลด ปรับปรุงแบบ รวมแผ่น

22


รายการแก้ไขแบบ

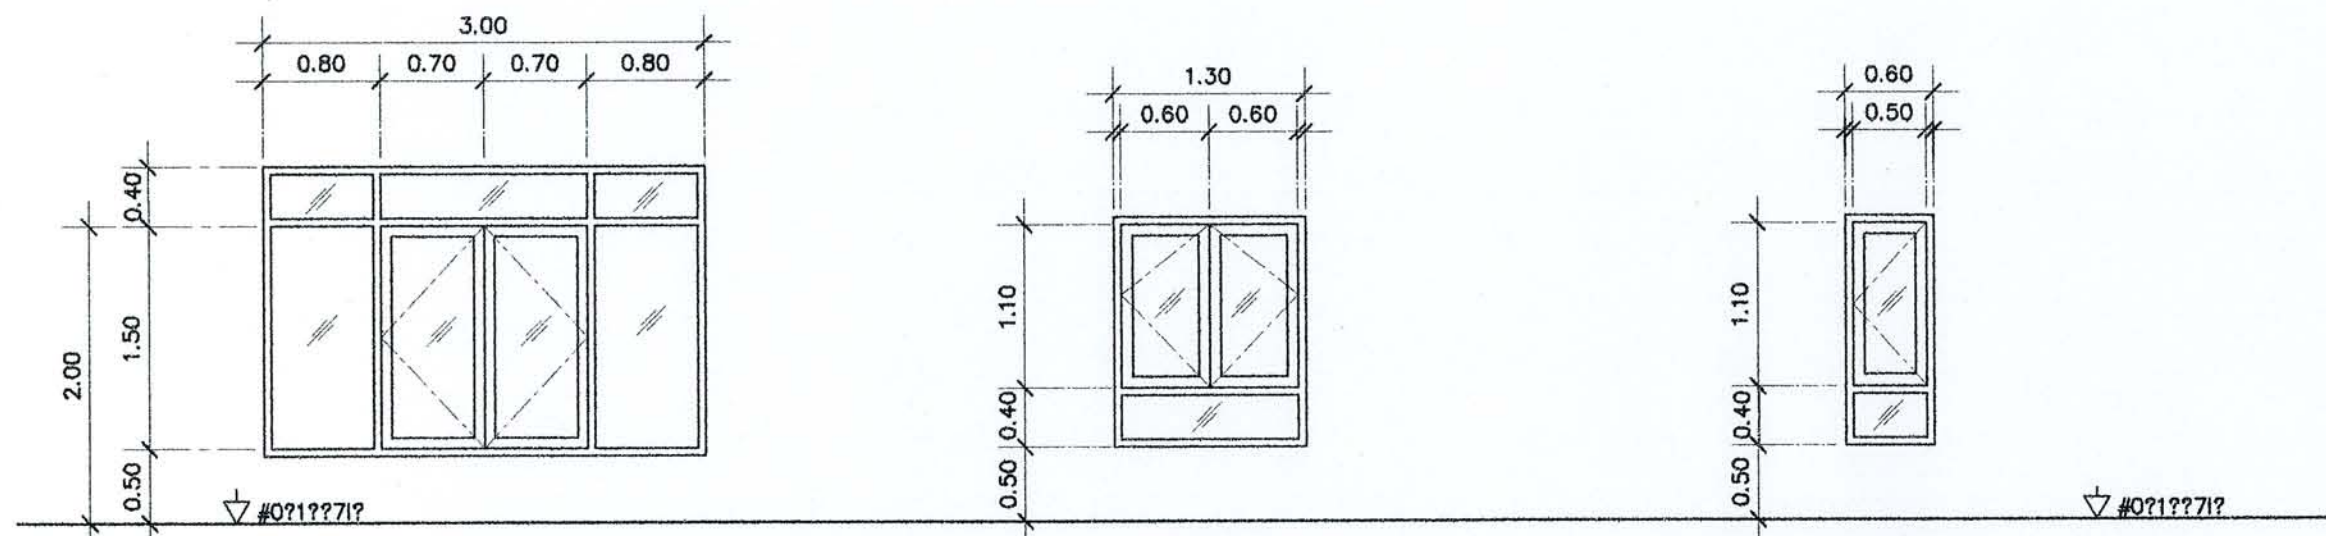

ลักษณะบาน	หน้าต่างบานเปิดคู่ พร้อมช่องแสงกระจกติดตาย
วงกบ	ไม้เนื้อแข็ง 2"x4"
กรอบบาน	กรอบบานไม้เนื้อแข็ง 1"x4"
ลูกพับ	กระจกใส ติดตั้งลิ้นชักหนา 6 มม.
อุปกรณ์	พร้อมมือจับและอุปกรณ์ครบชุด

ลักษณะบาน	หน้าต่างบานเปิดคู่ พร้อมช่องแสงกระจกติดตาย
วงกบ	ไม้เนื้อแข็ง 2"x4"
กรอบบาน	กรอบบานไม้เนื้อแข็ง 1"x4"
ลูกพับ	กระจกใส ติดตั้งลิ้นชักหนา 6 มม.
อุปกรณ์	พร้อมมือจับและอุปกรณ์ครบชุด

ลักษณะบาน	หน้าต่างบานกระทุ้ง พร้อมช่องแสงกระจกติดตาย
วงกบ	ไม้เนื้อแข็ง 2"x4"
กรอบบาน	กรอบบานไม้เนื้อแข็ง 1"x4"
ลูกพับ	กระจกใส ติดตั้งลิ้นชักหนา 6 มม.
อุปกรณ์	พร้อมมือจับและอุปกรณ์ครบชุด

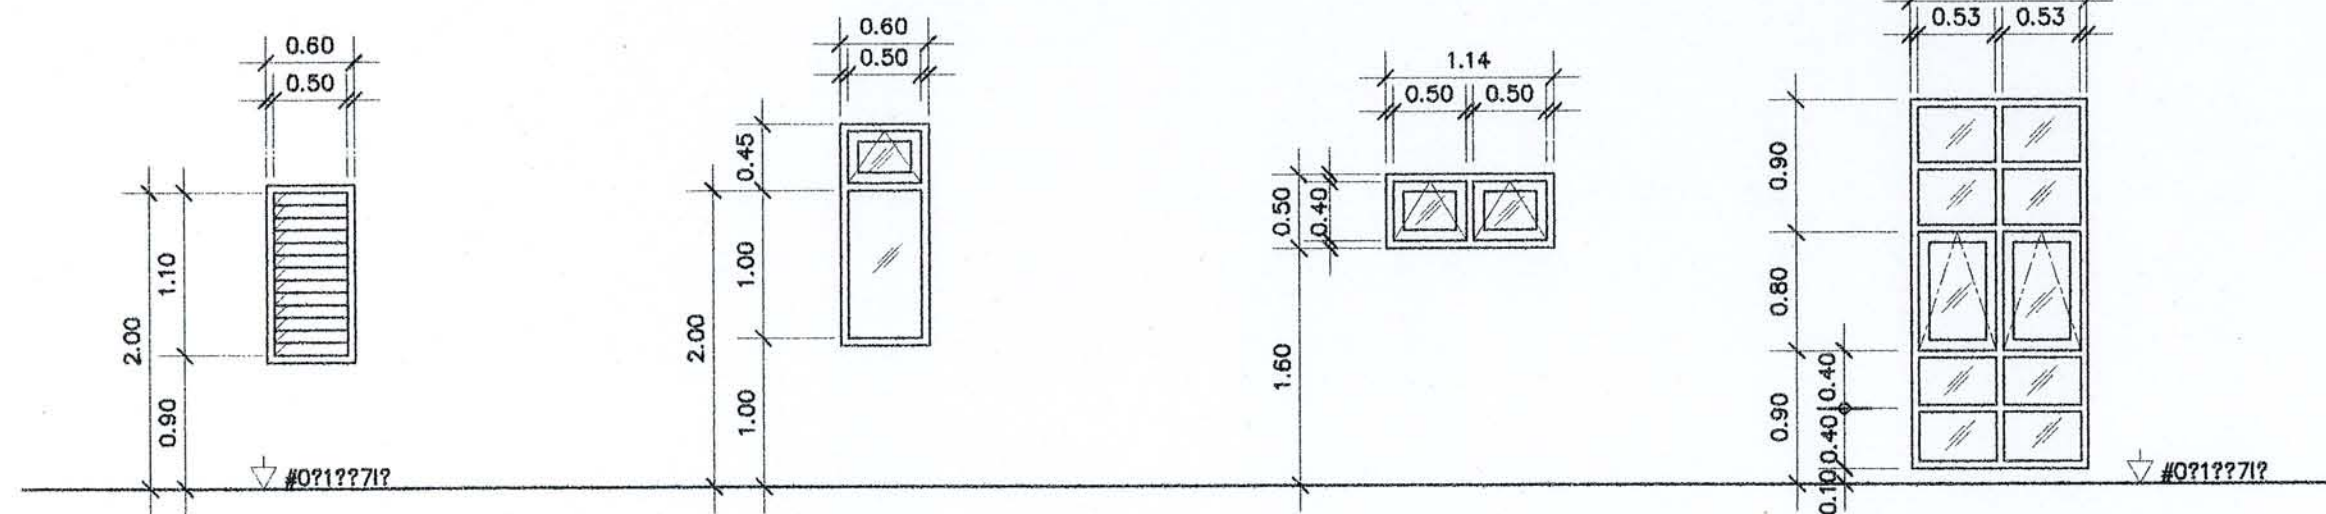

ลักษณะบาน	หน้าต่างบานเกล็ด ปรับมุมได้
วงกบ	วงกบไม้เนื้อแข็ง 2"x4"
กรอบบาน	—
ลูกพับ	กระจกใส หนา 6 มม.
อุปกรณ์	พร้อมมือจับและอุปกรณ์ครบชุด

ลักษณะบาน	หน้าต่างบานกระทุ้ง พร้อมช่องแสงกระจกติดตาย
วงกบ	วงกบไม้เนื้อแข็ง 2"x4"
กรอบบาน	กรอบบานไม้เนื้อแข็ง 1"x4"
ลูกพับ	กระจกใส หนา 6 มม.
อุปกรณ์	พร้อมมือจับและอุปกรณ์ครบชุด

ลักษณะบาน	หน้าต่างบานเกล็ด ปรับมุมได้
วงกบ	วงกบไม้เนื้อแข็ง 2"x4"
กรอบบาน	—
ลูกพับ	กระจกใส หนา 6 มม.
อุปกรณ์	พร้อมมือจับและอุปกรณ์ครบชุด

ลักษณะบาน	หน้าต่างบานเกล็ด ปรับมุมได้
วงกบ	วงกบไม้เนื้อแข็ง 2"x4"
กรอบบาน	—
ลูกพับ	กระจกใส หนา 6 มม.
อุปกรณ์	พร้อมมือจับและอุปกรณ์ครบชุด

แบบขยายหน้าต่าง 1:50



สำนักงานโยธา
กรุงเทพมหานคร

โครงการ
แบบบ้านขึ้นเพื่อประชาชน

ตามนโยบาย

ม.ร.ว.สุขุมพันธุ์ บริพัตร ผู้ว่าฯ กทม.
นายพลเทพ เดชะใหญ่ รองผู้ว่าฯ กทม.
นายธีระชน มโนมัยพิบูลย์ รองผู้ว่าฯ กทม.
นายพงศ์ศักดิ์ เลิศสันต์ ปลัดฯ กทม.

ผู้อำนวยการสำนักงานโยธา

นายจุฬพล ลำภาผล

รองผู้อำนวยการสำนักงานโยธา

นายวิศักดิ์ เดชประพันธ์

ผู้อำนวยการสำนักงานออกแบบ

นายสุรศักดิ์ สมนิธิ

หัวหน้ากลุ่มงานสถาปัตยกรรม

นายสันติชัย บุญปักษ์

หัวหน้ากลุ่มงานวิศวกรรม

นายธีระยุทธ คงสวัสดิ์เสถียร

สถาปนิก

นางสาวสุกสมมาลย์ กาญจนะ

วิศวกรโครงสร้าง

นายวิรัตน์ บัณฑิต

วิศวกรไฟฟ้า

นายกิตติพงษ์ จิระเดชาร

วิศวกรสุขาภิบาล

นางสาวมณีนีรา สมนิธิ

วิศวกรเครื่องกล

นายช่างเขียนแบบ

นายณัฐพงศ์ ณรงค์บุญชู

แบบ
026 บ้านพระพรหม

คำขอ

สถานที่

แบบแสดง

แบบขยายบันได

มาตราส่วน 1:50


FILE : เลขที่ 14

วันที่ 14 มิถุนายน 2553

คัดลอกแบบ


รวมแผ่น 22

รายการแก้ไขแบบ

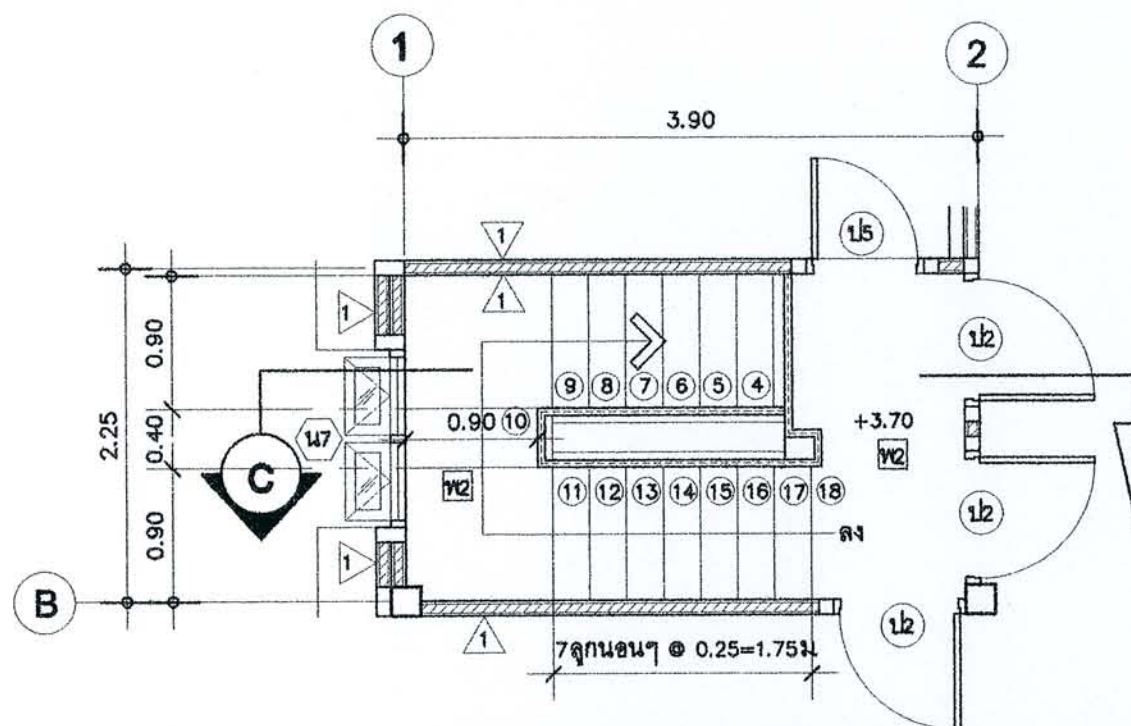


แปลนขยายบันไดชั้นบน

มาตราส่วน 1:50

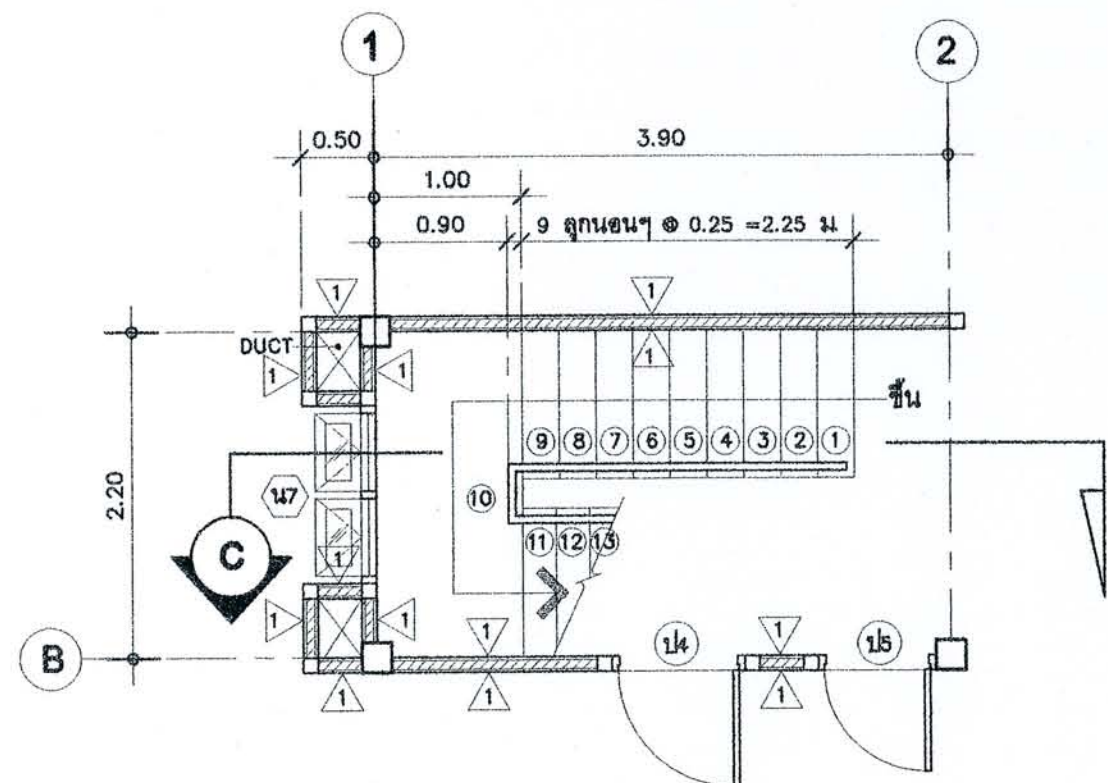

แปลนขยายบันไดชั้นล่าง

มาตราส่วน 1:50

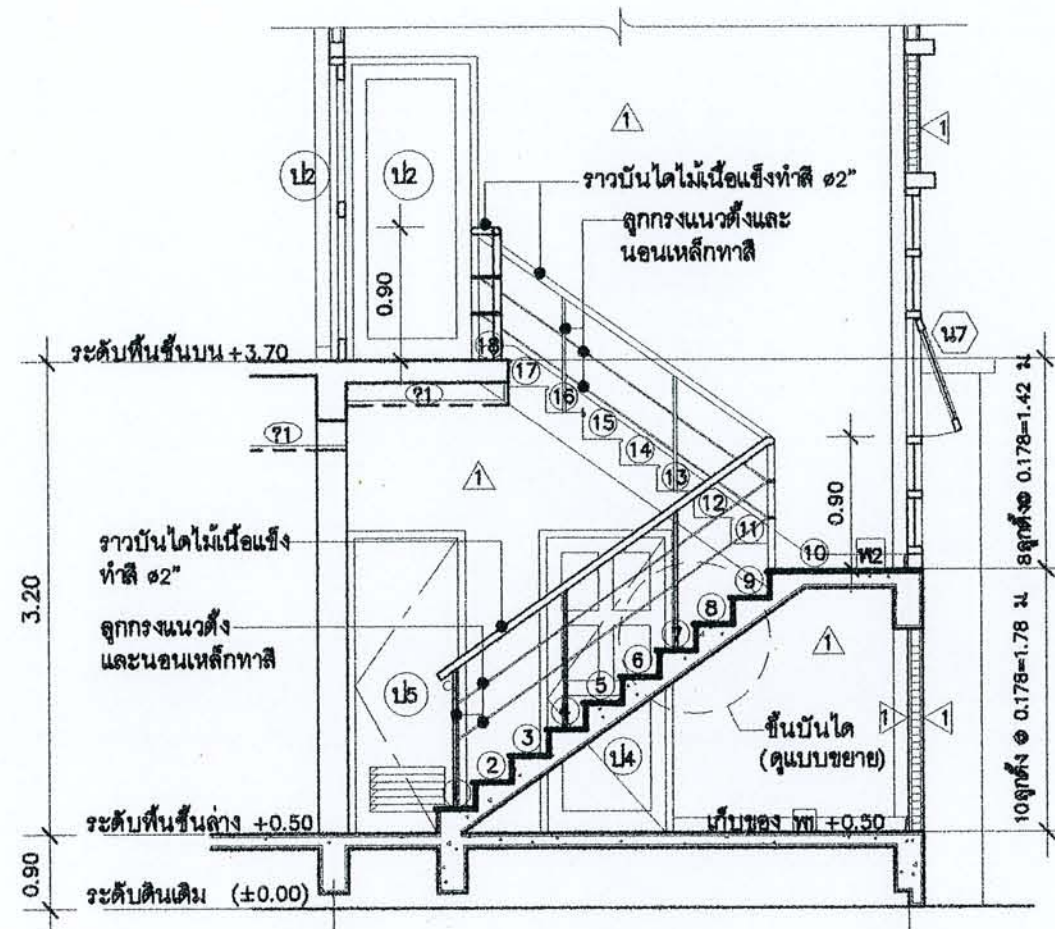


รูปตัด C-C

มาตราส่วน 1:50

ลูกนอนบันไดไม้เนื้อแข็ง
หนา 1" กว้าง 27.5 ซม.

ลูกตั้งไม้เนื้อแข็งหนา 1 1/2"

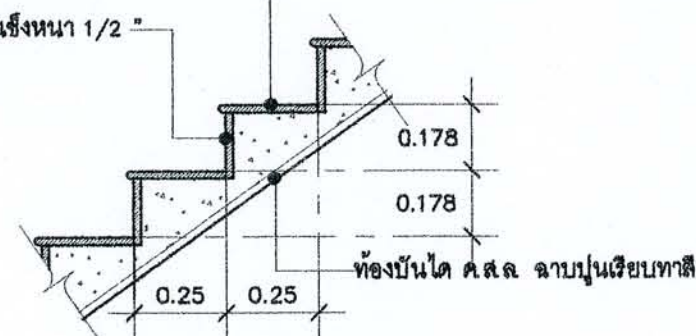

แบบขยายขึ้นบันได

มาตราส่วน 1:20



สำนักงานโยธา
กรุงเทพมหานคร

โครงการ
แบบบ้านขึ้นเพื่อประชาชน

ตามนโยบาย

ม.ร.ว.สุขุมพันธุ์ บริพัตร ผู้ว่าฯ กทม.
นายพรเทพ เศรษฐิน รองผู้ว่าฯ กทม.
นายธีระชน มโนชัยปูลัย รองผู้ว่าฯ กทม.
นายพงศ์ศักดิ์ เทมสันต์ ปลัดฯ กทม.

ผู้อำนวยการสำนักงานโยธา

นายจุมพล ลำภาส

รองผู้อำนวยการสำนักงานโยธา

นายวิศักดิ์ เลิศประพันธ์

ผู้อำนวยการสำนักงานออกแบบ

นายจตุรงค์ สันติธรรม

หัวหน้ากลุ่มงานสถาปัตยกรรม

นายสินธุ์ชัย บุญภิรักษ์

หัวหน้ากลุ่มงานวิศวกรรม

นายธีระยุทธ คงสวัสดิ์เสถียร

สถาปนิก

นางสาวสุมนภรณ์ กาญจนะ

วิศวกรโครงสร้าง

นายวิวัฒน์ บริรักษ์

วิศวกรไฟฟ้า

นายวิฑิตพงษ์ จิระเดชาก

วิศวกรสุขาภิบาล

นางสาวมณฑิรา สมพยอม

วิศวกรเครื่องกล

นายช่างเขียนแบบ

นายณัฐพงศ์ ณรงค์บุญชูชาติ

แบบ

026 บ้านห้วยพะวง

เจ้าของ

สถานที่

แบบแสดง

แบบขยายห้องน้ำ

มาตราส่วน 1:50


FILE : A-15

วันที่ 2553


คัดลอกแบบ

รวมแผ่น 22


รายการแก้ไขแบบ

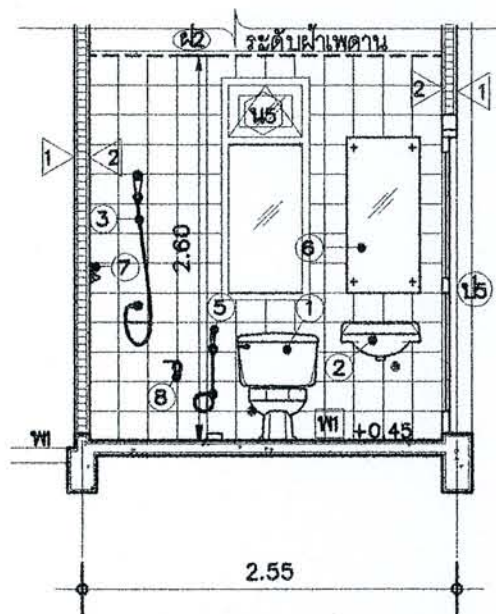


รูปตัด A - A
มาตราส่วน 1 : 50

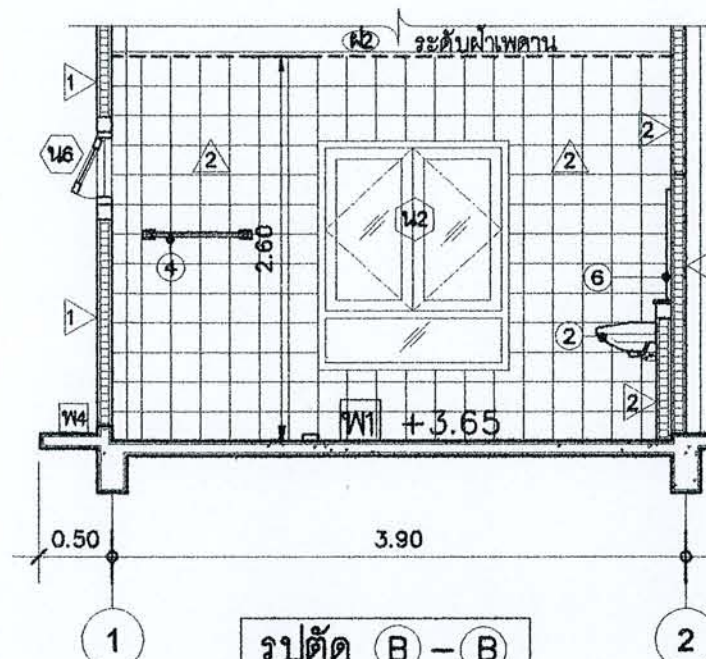

รูปตัด B - B
มาตราส่วน 1 : 50

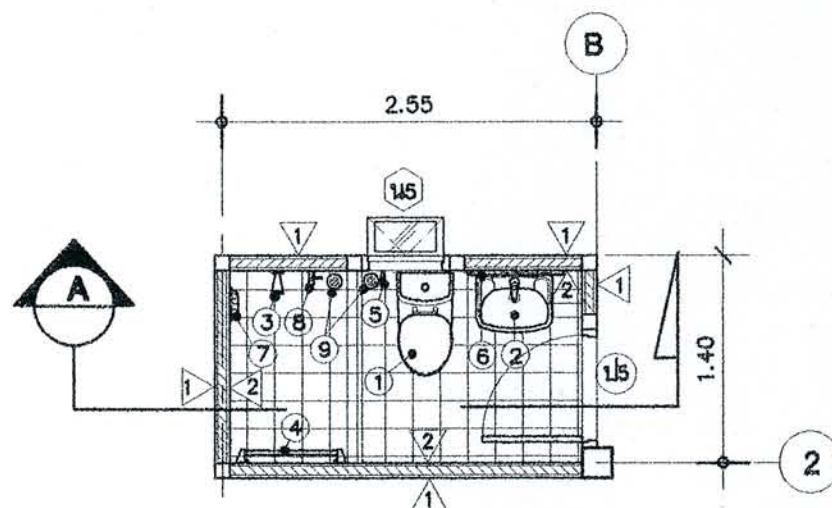

แปลนขยายห้องน้ำ ②
มาตราส่วน 1 : 50

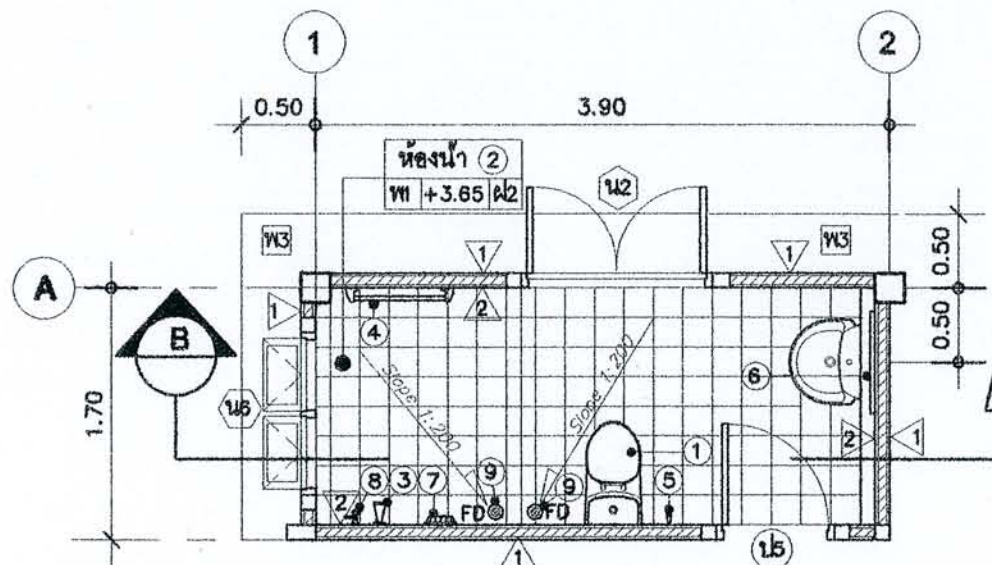

แบบขยายห้องน้ำ ① และ ②
มาตราส่วน 1 : 50

แปลนขยายห้องน้ำ ②
มาตราส่วน 1 : 50

สัญลักษณ์	รายการ
①	ชักโครกแบบนั่งราบ พร้อมอุปกรณ์โครบชุด
②	อ่างล้างหน้าชนิดแขวนผนัง ขนาดไม่เกิน 20"
③	ฝักบัวสายอ่อนอย่างดี
④	ราวแขวนผ้า
⑤	สายชำระ
⑥	กระจกเงาดมผนังอย่างดี กว้างยาวกลมกลืนกับอ่าง
⑦	ที่วางสบู่
⑧	ก๊อมน้ำโครเมี่ยมสูงจากพื้น 0.50 ม.
⑨	ระบายนํ้าทิ้ง

หมายเหตุ ยี่ห้อ , รุ่น กำหนดภายหลัง

รายการประกอบแบบบ้านวิศวกรรมโยธา

1. ซีเมนต์

- 1.1 ส่วนของโครงสร้างคอนกรีตเสริมเหล็กทั้งหมดต้องใช้ PORTLAND CEMENT ประเภทที่ 1 ที่มีคุณสมบัติตามมาตรฐานผลิตภัณฑ์อุตสาหกรรมเท่านั้น
- 1.2 ถ้าไม่ได้ระบุเป็นอย่างอื่น คอนกรีต 1 ลบ.ม. ต้องมีส่วนผสมของซีเมนต์ไม่น้อยกว่า 320 กก.

2. คอนกรีต

- 2.1 คอนกรีตที่ใช้กับโครงสร้างอาคารได้แก่ ฐานราก, เสา, คาน, พื้น, คอนกรีตทับหน้าพื้นสำเร็จรูป, บัง, ค.ส.ล. ฯลฯ ต้องมีกำลังอัดเฉลี่ยไม่น้อยกว่า 210 กก./ตร.ซม. เมื่ออายุ 28 วัน โดยทดสอบจากแท่งคอนกรีตตัวอย่างทรงกระบอก Ø 150 x 300 มม.
- 2.2 ADMIXTURES ที่ใช้ต้องมีคุณสมบัติตาม ASTM หรือ BS

3. งานเหล็ก

- 3.1 คุณสมบัติของเหล็กเส้นเสริมคอนกรีต มีดังนี้

ขนาดเหล็กเสริม มม.	ชั้นคุณภาพ	มาตรฐาน	หมายเหตุ
RB 6 , RB 9	SR - 24	มอก. 20-2527	
DB 12 ขึ้นไป	SD - 30	มอก. 24-2536	

- 3.2 เหล็กรูปพรรณ , เหล็กกล่องสำหรับก่อสร้าง

- 3.2.1 เหล็กรูปพรรณที่จะใช้ต้องมีคุณสมบัติตาม มอก. 1227-2537, มอก.1228-2537 หรือ JIS เหล็กกล่องที่ใช้ต้องมีคุณสมบัติตาม มอก. 107-2533 หรือ JIS และเหล็กรูปพรรณเชื่อมประกอบจะต้องมีคุณสมบัติตาม มอก. 1303-2538
- 3.2.2 เหล็กรูปพรรณทั้งหมดต้องเป็นของใหม่ ไม่เคยใช้งานมาก่อน ตรงไม่บิดเบี้ยว ไม่มีรอยตำหนิไม่พึงประสงค์ ไม่เป็นสนิม หรือน้ำมัน
- 3.2.3 การต่อเหล็กรูปพรรณ ถ้าไม่จำเป็นจริงๆ แล้วห้ามต่อ ในกรณีที่มีการต่อเหล็ก รอยต่อของเหล็กต้องมี กำลังมากกว่าหรือเท่ากับเหล็กที่ไม่มีรอยต่อ การต่อให้ตรงจุดเดียวกัน และการต่อให้เป็นไปตามมาตรฐาน AISC
- 3.2.4 การประกอบเหล็กคานให้ดำเนินการตามมาตรฐาน AISC หรือตามมาตรฐานสำหรับอาคารเหล็กรูปพรรณของ วสท. ที่ 1015-40
- 3.2.5 ผู้รับจ้างจะต้องทำ ค้ำยัน ยึดโครง ให้เพียงพอเพื่อยึดโครงสร้างให้แน่นหนาอยู่ในแนวและตำแหน่งที่ต้องการ
- 3.2.6 องค์อาคารที่วางทาบหรือต่อเชื่อมจะต้องวางให้แนบสนิทเต็มหน้า
- 3.2.7 การเชื่อมต้องทั้งหมดให้ใช้วิธีเชื่อมด้วยไฟฟ้าการ (Electric arc welding) โดยตลอดผิวหน้าที่มีเส้นการเชื่อมให้เป็นไปตามมาตรฐาน AWS ขนาดของรอยเชื่อมต้องไม่น้อยกว่าความหนาของแผ่นเหล็ก
- 3.2.8 ถ้าไม่ได้กำหนดให้เป็นอย่างอื่นรอยต่อระหว่างชิ้นส่วนเหล็กต่างๆให้ใช้วิธี เชื่อมตะเข็บตลอดแนวชน
- 3.2.9 ผิวหน้าที่จะทำการเชื่อม ต้องสะอาดปราศจากสะเก็ดร่อน สนิมกรัน ไขมัน สี หรือสิ่งแปลกปลอมอื่นใด
- 3.2.10 ลวดเชื่อมต้องมีคุณสมบัติตาม มอก. หรือ AWS หรือ AISC
- 3.2.11 ให้ทาสีกันสนิมไม่น้อยกว่า 2 ชั้น คุณภาพเทียบเท่า RUST-OLEAM, JOTAN, SIKKENS


4. ระบบกันซึม

- 4.1 รายละเอียดและคุณสมบัติ

ส่วนของอาคาร	ชนิดและผลิตภัณฑ์	ผลิตภัณฑ์คุณภาพเทียบเท่า
- พื้นห้องน้ำ , กันสาด ค.ส.ล.	น้ำยาเคมีแบบกันซึมชนิดทา	BRUSHBOND ของ FOSROC
รางน้ำ ค.ส.ล. หลังคา ค.ส.ล.		LANKO 225 ?-? DAVCO

5.ทั่วไปและการเตรียมงาน

- 5.1 รายการประกอบแบบอื่นใดที่ไม่ได้กำหนดไว้ให้ถือปฏิบัติตาม " บทกำหนดทั่วไปสำหรับอาคารก่อสร้างอาคารคอนกรีตเสริมเหล็ก " ของ วสท. เป็นเกณฑ์
- 5.2 แบบรายการเหล่านี้ เป็นแบบรายการที่ใช้เป็นแนวทางในการก่อสร้างเท่านั้น หากมีความจำเป็นต้องเพิ่มเติมรายละเอียดเพื่อให้เกิดความมั่นคงแข็งแรงหรือความกลมกลืนมากยิ่งขึ้น หรือหากแบบขัดแย้ง แสดงรายละเอียดไม่ครบถ้วน วิศวกรฝ่ายวิศวกรรมจะเป็นผู้กำหนดให้ หรืออาจผู้รับจ้างดำเนินการออกแบบในส่วนนั้นๆ โดยอาศัยหลักวิชาช่างในขณะก่อสร้างจะต้องมีวิศวกรไม่ต่ำกว่าสามวิศวกรลงนามรับรอง และต้องเสนอต่อฝ่ายวิศวกรรมอาคารเพื่อขออนุมัติ โดยถือเป็นส่วนหนึ่งของแบบรายการนี้ และไม่ว่าการก่อสร้างนี้ผิดไปจากแบบรายการก่อสร้างแต่อย่างใด แต่ทั้งนี้ เนื่องจากงานต้องไม่ลดน้อยกว่าเดิมและผู้รับจ้างจะต้องไม่คิดค่าใช้จ่ายเพิ่ม

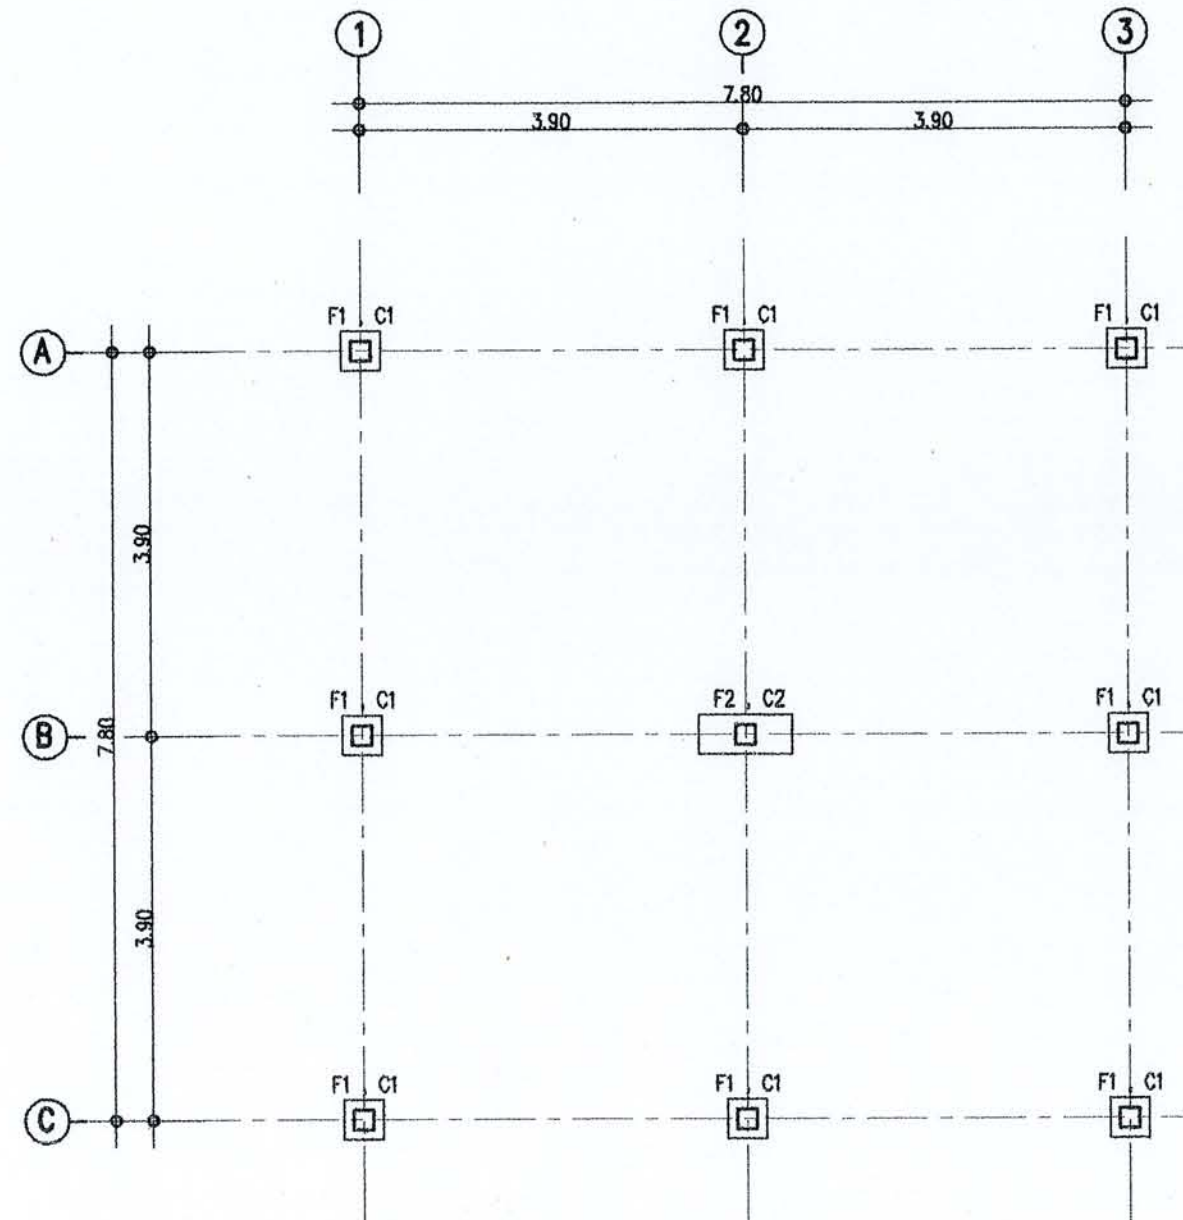

แปลนเสาเข็มและฐานราก

มาตราส่วน 1 : 75



สำนักงานโยธา
กรุงเทพมหานคร

โครงการ
แบบบ้านเข็มเพื่อประชาชน

ตามนโยบาย
น.ร.สุรพันธุ์ บริพัตร ผู้ว่าฯกทม.
นายพรเทพ เศรษฐินฤทัย รองผู้ว่าฯกทม.
นายธีระชน มโนชัยปูลัย รองผู้ว่าฯกทม.
นายพงศ์ศักดิ์ เศรษฐินฤทัย ปลัดฯกทม.

ผู้อำนวยการสำนักงานโยธา
นายชุมพล สันภาพล
รองผู้อำนวยการสำนักงานโยธา
นายทวีศักดิ์ เลิศประพันธ์
ผู้อำนวยการสำนักงานออกแบบ
นายจตุรงค์ สมนิยม
หัวหน้ากองงานสถาปัตยกรรม
นายสันติชัย บุญนิกษ์
หัวหน้ากองงานวิศวกรรม
นายธีระยุทธ คงสวัสดิ์เสถียร

สถาปนิก
นางสาวสุมนะวาลย์ กาญจนะ
วิศวกรโครงสร้าง
นายธินันท์ นริศไพฑูริย์
วิศวกรไฟฟ้า
นายกิตติพงษ์ จิระเดชากะ
วิศวกรสุขาภิบาล
นางสาวมณฑิรา สมทอง
วิศวกรเครื่องกล

นายช่างเขียนแบบ
นายไพบูลย์นุส ประกอบกิจ

แบบ
026 บ้านห้วยพะวง

เจ้าของ
สถานที่

แบบแสดง
รายการประกอบแบบโยธา
แปลนเสาเข็มและฐานราก
มาตราส่วน 1:75

FILE :
วันที่ 16
วันที่ 2553
ครั้งที่ 16
ครั้งที่ 22

รายการแก้ไขแบบ



สำนักงานโยธา
กรุงเทพมหานคร

โครงการ
แบบบ้านยิมเพื่อประชาชน

ตามนโยบาย

น.ร. ๖ สุขุมพันธุ์ บริษัท รจนาทณ
นายพรเทพ เศรษฐินกุล รจนาทณ
นายธีระชน มโนวิทย์กุล รจนาทณ
นายพงศ์ศักดิ์ เกษมสันต์ บริษัท รจนาทณ

ผู้อำนวยการสำนักงานโยธา

นายชุมพล สำนกพล

รองผู้อำนวยการสำนักงานโยธา

นายทวีศักดิ์ เกษมสันต์

ผู้อำนวยการสำนักงานออกแบบ

นายจตุรงค์ สอนเนียม

หัวหน้ากลุ่มงานสถาปัตยกรรม

นายสันติชัย บุญมีรักษ์

หัวหน้ากลุ่มงานวิศวกรรม

นายธีระยุทธ คงทรัพย์เจริญ

สถาปนิก

นางสาวศุมนมาศ กาญจนะ

วิศวกรโครงสร้าง

นายวิวัฒน์ บริษัทไทยยุค

วิศวกรไฟฟ้า

นายธีระพงษ์ จิระธรราก

วิศวกรสุขาภิบาล

นางสาวณิชา สมน้อม

วิศวกรเครื่องกล

นายช่างเขียนแบบ

นางนุญช ปรุภกอบกิจ

แบบ
026 บ้านพุระพง

เจ้าของ

สถานที่

แบบแสดง

แปลนโครงสร้างชั้นล่าง

แปลนโครงสร้างชั้น 2

มาตราส่วน 1:75


FILE : S-02

วันที่ มิถุนายน 2553

คัดลอกแบบ


รวมแผ่น 22

รายการแก้ไขแบบ

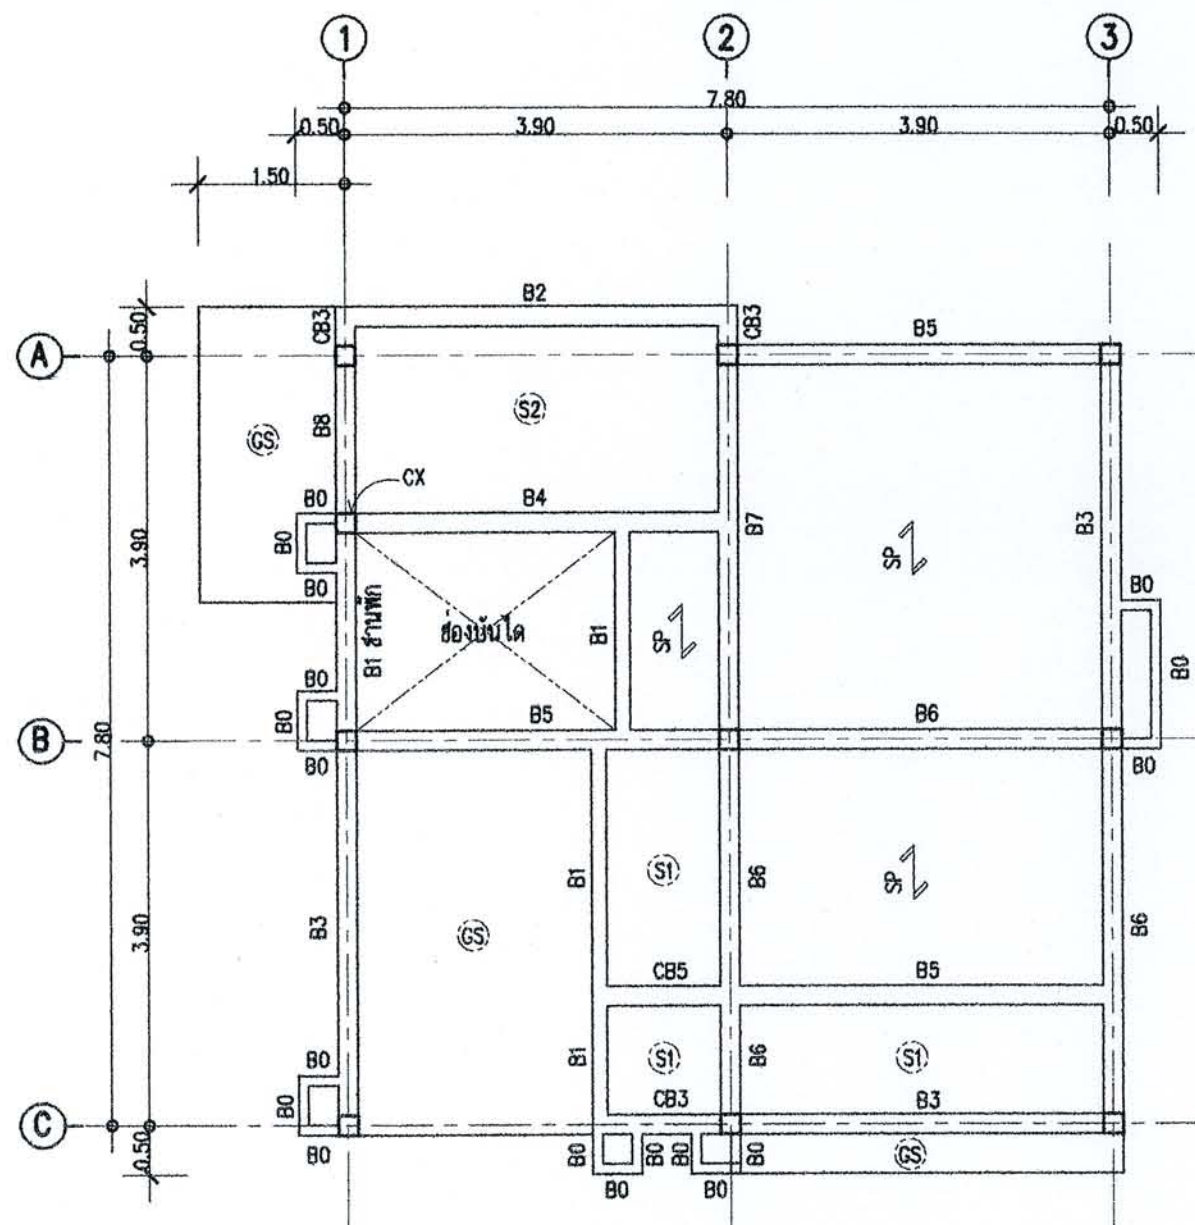

แปลนโครงสร้างชั้นล่าง

มาตราส่วน 1 : 75

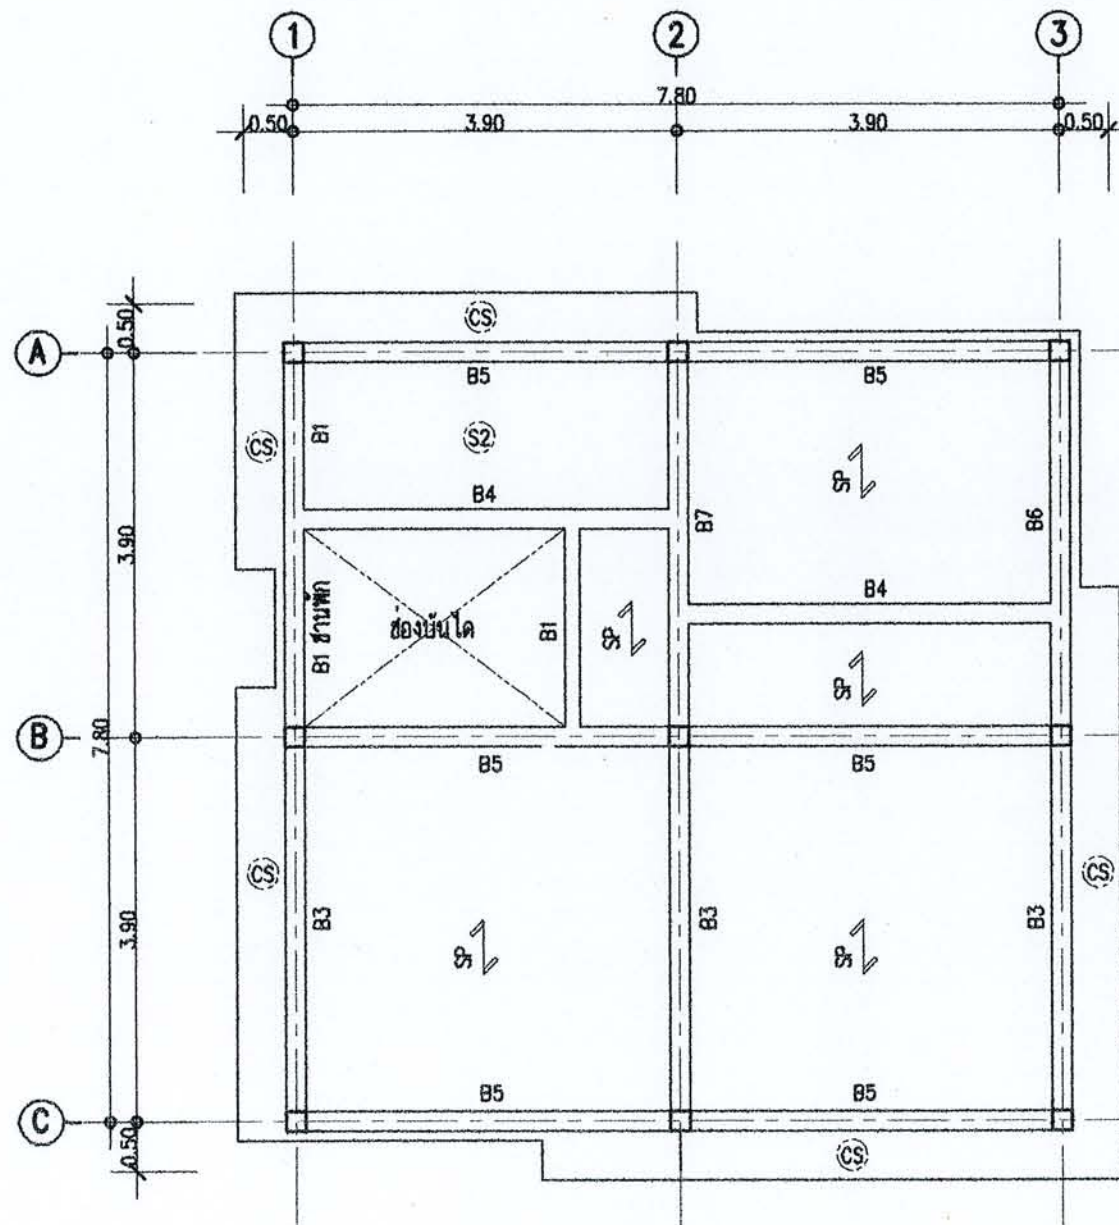

แปลนโครงสร้างชั้น 2

มาตราส่วน 1 : 75



สำนักงานโยธา
กรุงเทพมหานคร

โครงการ
แบบบ้านยี่มเพื่อประชาชน

ตามนโยบาย

ม.ร.ว.สุขุมพันธุ์ บริพัตร ผู้ว่าฯกทม.
นายพรเทพ เกษมไพฑูรย์ รองผู้ว่าฯกทม.
นายธีระชน มโนวิจิตรกุล รองผู้ว่าฯกทม.
นายพงศ์ศักดิ์ สอนันต์ ปลัดฯกทม.

ผู้อำนวยการสำนักงานโยธา

นายชุมพล สันภาพ

รองผู้อำนวยการสำนักงานโยธา

นายอภิศักดิ์ เลิศประพันธ์

ผู้อำนวยการสำนักงานออกแบบ

นายจตุรงค์ สมเยี่ยม

หัวหน้ากลุ่มงานสถาปัตยกรรม

นายสินธุ์ บุญมี

หัวหน้ากลุ่มงานวิศวกรรม

นายธีระยุทธ คงสวัสดิ์

สถาปนิก

นางสาวสุนนมาศ กาญจนะ

วิศวกรโครงสร้าง

นายจิณโณ บริศไพฑูรย์

วิศวกรไฟฟ้า

นายศักดิ์พงษ์ จิระเดชาก

วิศวกรสุขาภิบาล

นางสาวมณฑิรา สมหอม

วิศวกรเครื่องกล

นายช่างเขียนแบบ

นางปัญญนุช ประกอบกิจ

แบบ
026 บ้านพุระพง

เจ้าของ

สถานที่

แบบแสดง
แปลนคานและโครงหลังคา

มาตราส่วน 1:75


FILE : เลขที่

วันที่ 18

ปี 2553

ชุดแบบ 22

รายการแก้ไขแบบ

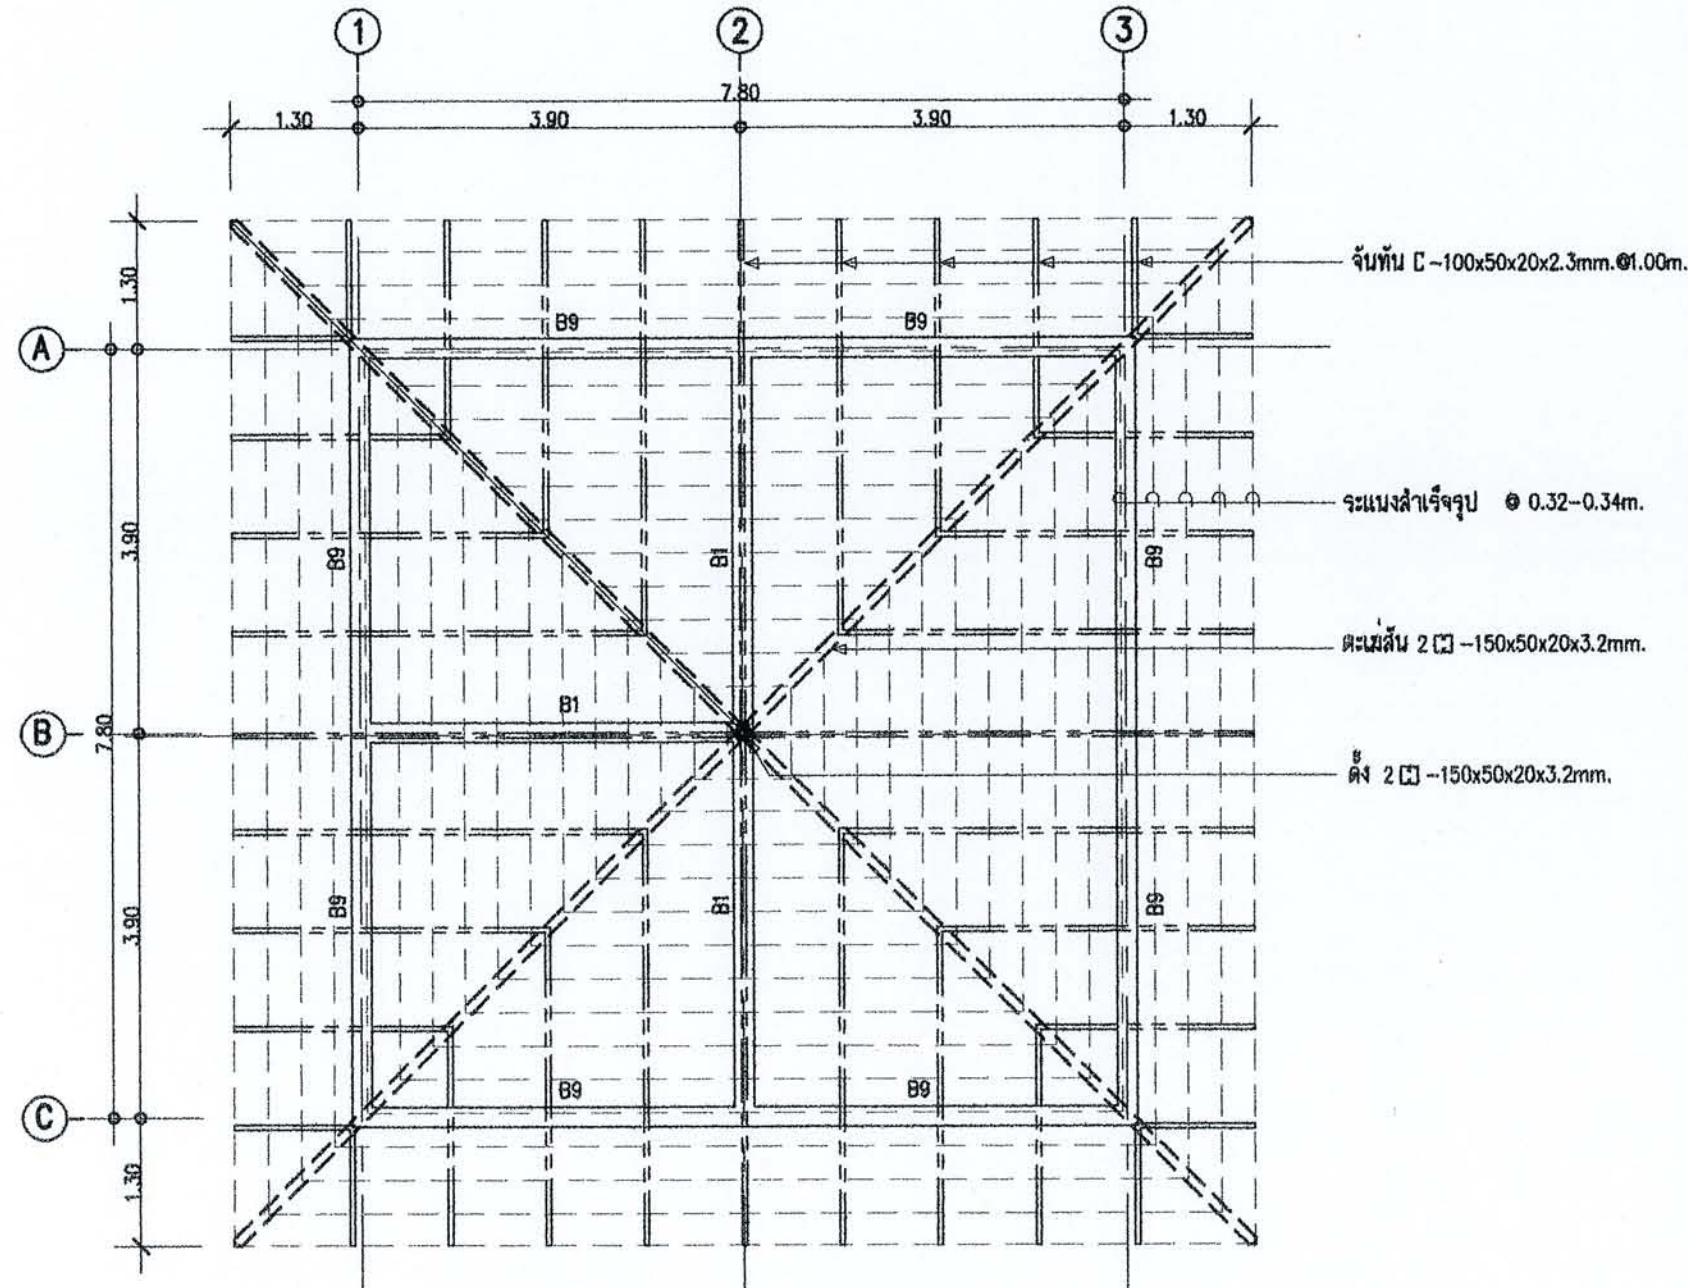

แปลนคานและโครงหลังคา

มาตราส่วน

1 : 75



สำนักงานโยธา
กรุงเทพมหานคร

โครงการ
แบบบ้านขี้ผึ้งประชาชน

ตามนโยบาย

ม.ร.ว.สุขุมพันธุ์ บริพัตร ผู้ว่าฯ กทม.
นายพงษ์เทพ เศรษฐ์โพธิ์ รองผู้ว่าฯ กทม.
นายธีระชน มโนชัยปูลอย รองผู้ว่าฯ กทม.
นายพงศ์ศักดิ์ เสน่ห์สันต์ ปลัดฯ กทม.

ผู้อำนวยการสำนักงานโยธา
นายจุมพล สำนกพล
รองผู้อำนวยการสำนักงานโยธา
นายทวีศักดิ์ เศรษฐ์โพธิ์
ผู้อำนวยการสำนักงานออกแบบ
นายจตุรงค์ สมชัย
หัวหน้ากองงานสถาปัตยกรรม
นายสันติชัย บุญปักษ์
หัวหน้ากองงานวิศวกรรม
นายธีระยุทธ คงระวีเสถียร

สถาปนิก
นางสาวสุนันดา กัญจนะ
วิศวกรโครงสร้าง
นายวิวัฒน์ บัณฑิตโพธิ์
วิศวกรไฟฟ้า
นายดิเรกพงษ์ จิระดาการ
วิศวกรสุขาภิบาล
นางสาวณณชิตา สัมพอม
วิศวกรเครื่องกล

นายช่างเขียนแบบ
นางปณณณัฐ ประกอบกิจ

แบบ
026 บ้านทุระพงษ์

เจ้าของ

สถานที่

แบบขยาย
วิศวกรรมโครงสร้าง 1

มาตราส่วน 1:25


FILE : เลขที่ 19

วันที่ 19 พฤษภาคม 2553


คิดออกใบรับร่างแบบ

รวมแผ่น 22


รายการแก้ไขแบบ

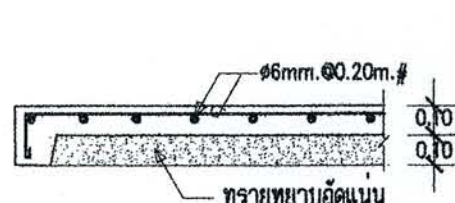


DETAIL GS

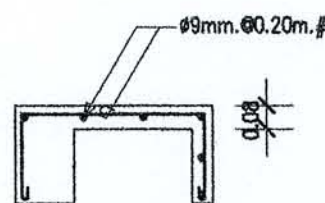


DETAIL CS

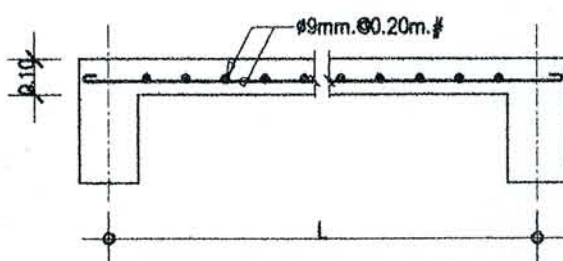


DETAIL S1

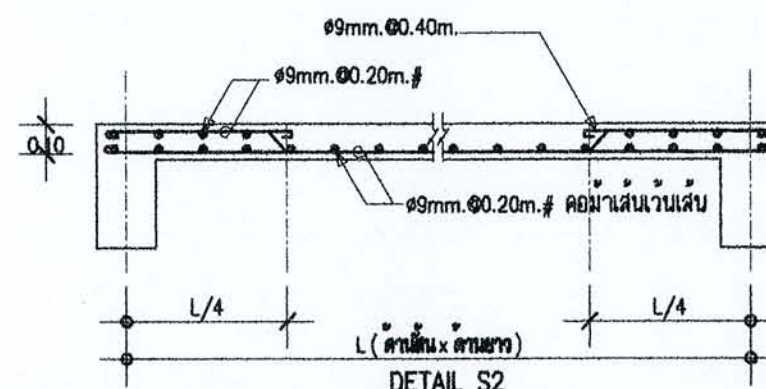


DETAIL S2

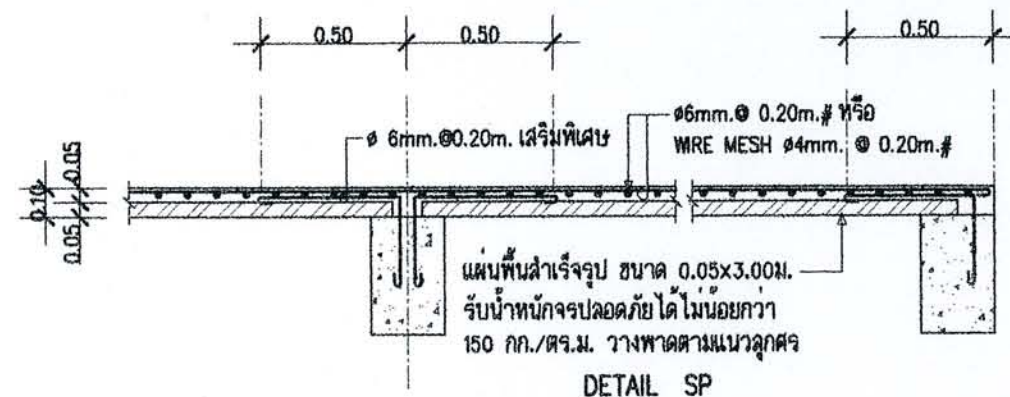


DETAIL SP

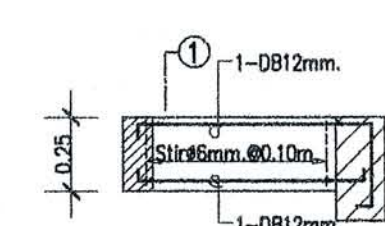


LONG SECTION BO

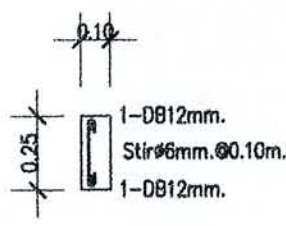


SECTION 1-1 (BO)

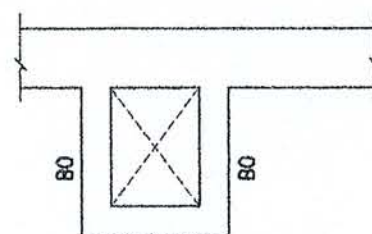


DETAIL DUCT

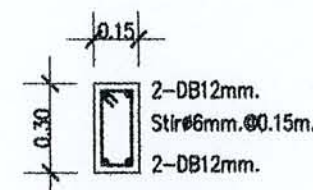


DETAIL B1

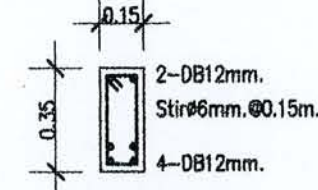


DETAIL B2

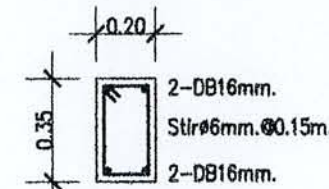


DETAIL B3

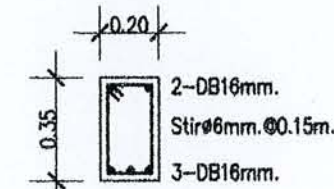


DETAIL B4

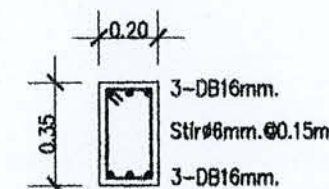


DETAIL B5

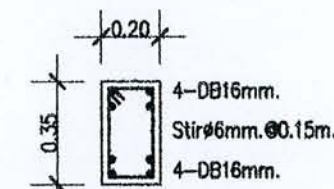


DETAIL B6

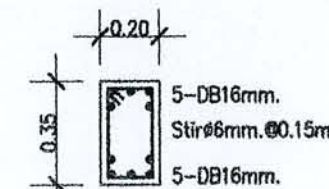


DETAIL B7

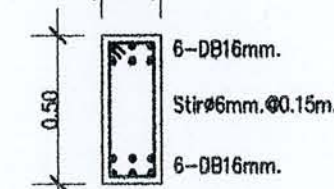


DETAIL B8

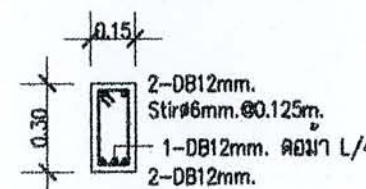

DETAIL B9

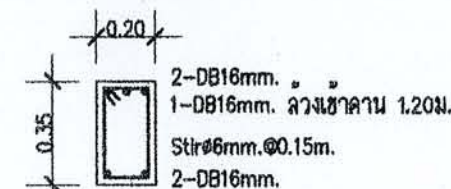

DETAIL CB3

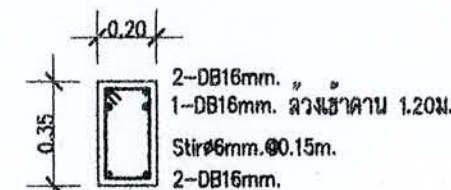

DETAIL CB5



สำนักงานโยธา
กรุงเทพมหานคร

โครงการ
แบบบ้านยี่สิบสี่ห้อง

ตามนโยบาย

ม.ร.ว.สุขุมพันธุ์ บริพัตร ผู้ว่าฯ กทม.
นายพรเทพ เศรษฐินพร รองผู้ว่าฯ กทม.
นายธีระชน มโนชัยปูลัย รองผู้ว่าฯ กทม.
นายพงศ์ศักดิ์ สมสันต์ ปลัดฯ กทม.


ผู้อำนวยการสำนักงานโยธา
นายชุมพล สันกาลาด
รองผู้อำนวยการสำนักงานโยธา
นายทวีศักดิ์ เดชประพันธ์
ผู้อำนวยการสำนักงานออกแบบ
นายจตุรงค์ สันติเยน
หัวหน้ากองงานสถาปัตยกรรม
นายสินธุ์ชัย บุญปักษ์
หัวหน้ากองงานวิศวกรรม
นายธีระยุทธ คงสวัสดิ์เสียว

สถาปนิก
นางสาวสุนันดา ภาณุชนะ
วิศวกรโครงสร้าง
นายวิวัฒน์ บริศัลย์
วิศวกรไฟฟ้า
นายกิตติพงษ์ จิระธรากร
วิศวกรสุขาภิบาล
นางสาวณัฏฐา สมหอม
วิศวกรเครื่องกล
นายชาญชัย ชื่นแบบ
นางปณิษฐา ประกอบกิจ


แบบ
026 บ้านทุ่งระยอง
เจ้าของ
สถานที่

แบบแสดง
แบบขยาย
วิศวกรรมโครงสร้าง 2
มาตราส่วน 1:25
FILE : เลขที่ 20
วันที่ 2553 S-05
จัดพิมพ์แบบ
รวมแผ่น 22

รายการแก้ไขแบบ

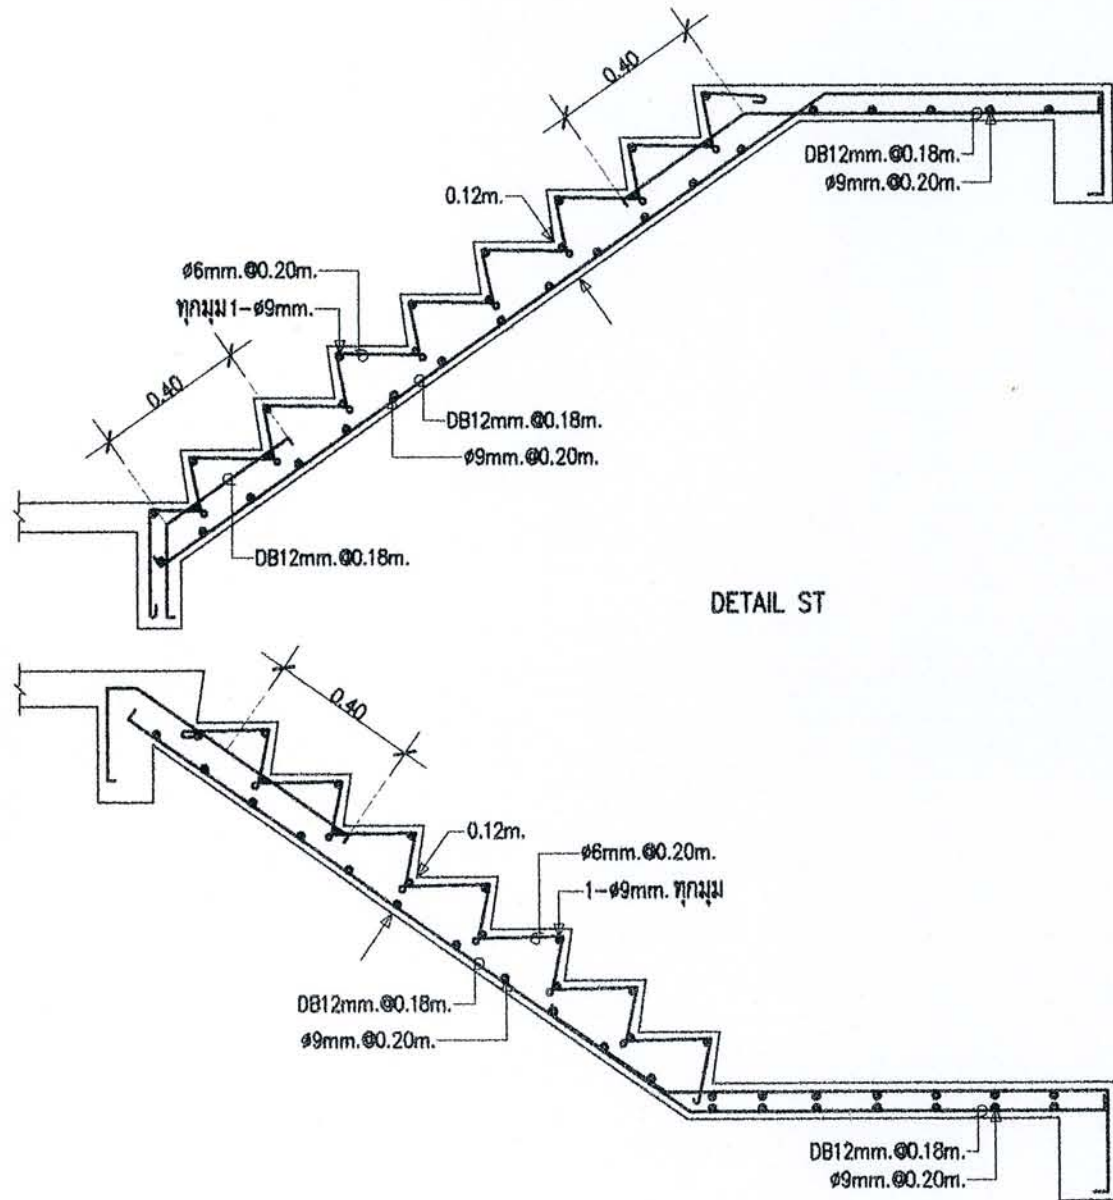


DETAIL ST

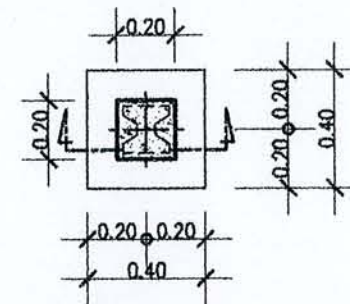


แบบขยาย F1

มาตราส่วน 1 : 25

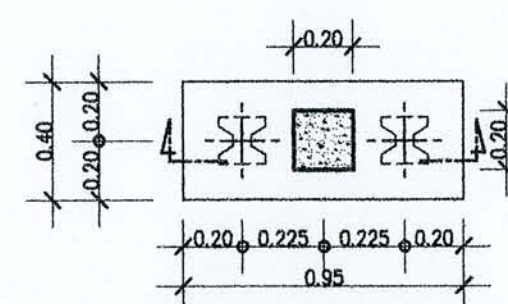


แบบขยาย F2

มาตราส่วน 1 : 25

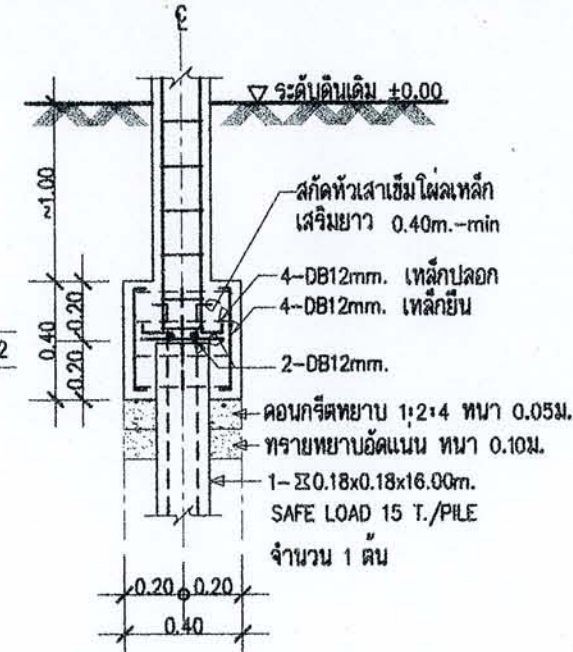

รูปตัด F1

มาตราส่วน 1 : 25

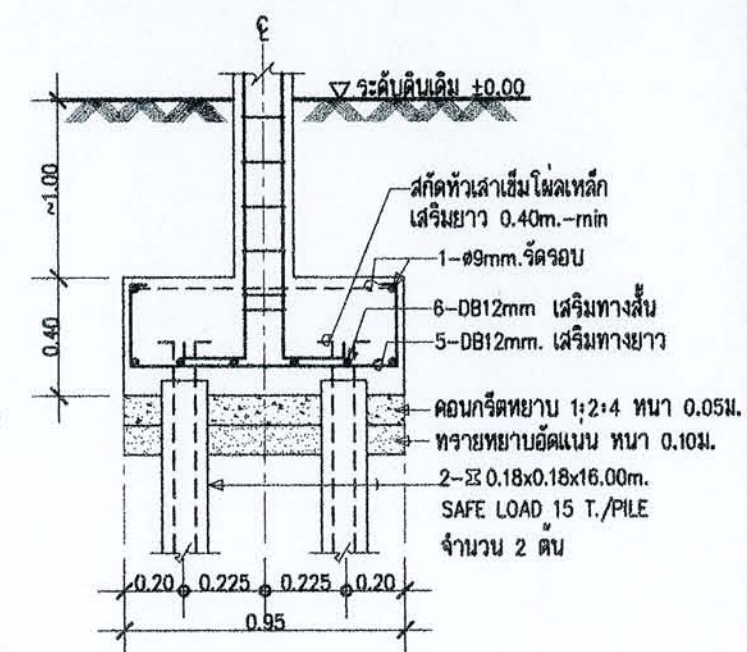

รูปตัด F2

มาตราส่วน 1 : 25

พื้นชั้น 2 - หลังคา	0.20	4-DB12mm. Stir#6mm. @0.15m.	0.20	4-DB12mm. Stir#6mm. @0.15m.
FLOOR COLUMN	C1, CX		C2	
ฐานราก - พื้นชั้น 2	0.20	4-DB12mm. Stir#6mm. @0.15m.	0.20	6-DB12mm. Stir#6mm. @0.15m.
FLOOR COLUMN	C1		C2	



สำนักงานนโยบาย
และแผนพลังงาน

โครงการ
แบบบ้านขึ้นเพื่อประชาชน

ตามนโยบาย

ม.ร.ว.สุขุมพันธุ์ บริพัตร ผู้ว่าฯกทม.
นายพรเทพ เศรษฐกิจ รองผู้ว่าฯกทม.
นายธีระวัฒน์ มโนวิทย์ รองผู้ว่าฯกทม.
นายพงศ์ศักดิ์ เตมียาภรณ์ ปลัดฯกทม.

ผู้อำนวยการสำนักงานนโยบาย
และแผนพลังงาน
นายสุวิทย์ สันติสุข
รองผู้อำนวยการสำนักงานนโยบาย
และแผนพลังงาน
นายสุวิทย์ สันติสุข
หัวหน้ากลุ่มงานสถาปัตยกรรม
นายสุวิทย์ สันติสุข
หัวหน้ากลุ่มงานวิศวกรรม
นายสุวิทย์ สันติสุข
นายธีระวัฒน์ มโนวิทย์

สถาปนิก
นางสาวสุนันดา กัญญา
วิศวกรโครงสร้าง
นายวิวัฒน์ บริพัตร
วิศวกรไฟฟ้า
นายสุวิทย์ สันติสุข
วิศวกรสุขาภิบาล
นางสาวกมลทิพย์ สันติสุข
วิศวกรเครื่องกล

นายช่างเขียนแบบ

แบบ
026 บ้านทุ่งระพี

เจ้าของ

สถานที่

แบบแสดง
รายการประกอบแบบ

DIAGRAM

มาตราส่วน No Scale

FILE : เลขที่ 21
วันที่ 2553 E-01
คัดลอกปรับปรุงแบบ รวม 22

รายการแก้ไขแบบ

รายการประกอบแบบไฟฟ้า

1. ในการติดตั้ง ผู้รับจ้างต้องปฏิบัติตามกฎระเบียบข้อบังคับของการไฟฟ้า

2. วัสดุอุปกรณ์ที่ใช้

2.1 แผงสวิทช์อัตโนมัติเป็นผลิตภัณฑ์ SQUARE-D, ABB, MEM, CLIPSAL, SIEMENS, HAGER

2.2 CIRCUIT BREAKER เป็นผลิตภัณฑ์ SQUARE-D, ABB, MEM, CLIPSAL, SIEMENS, HAGER

2.3 ตัวต่อไฟฟ้า เป็นผลิตภัณฑ์ภายในประเทศที่มีเครื่องหมายการค้า โดยผู้ประกอบประกอบดังนี้


- ท่อร้อยสายเคเบิล มาตรฐาน มอก.236-2533
- ขั้วรับหลอดและขั้วรับสายเคเบิล มาตรฐาน มอก.344-2530
- สายเคเบิล มาตรฐาน มอก.183-2528
- บัสบาร์ มาตรฐาน มอก.23-2521





2.4 สายไฟฟ้าเป็นผลิตภัณฑ์ มาตรฐาน มอก. 11-2531

2.5 สวิทช์และตัวรับไฟฟ้า เป็นผลิตภัณฑ์ NATIONAL, CLIPSAL, BTICINO, ABB


3. หากมีได้กำหนดไว้เป็นอย่างอื่น ชนิดและขนาดของสายไฟฟ้าให้ใช้ดังนี้

- 3.1 สายเมนวงจรย่อย ให้ใช้สายขนาด 2.5 ตารางมิลลิเมตร
- 3.2 สายไฟฟ้าระหว่างตัวต่อ และสายจากสวิทช์เข้าตัวต่อ ให้ใช้สายขนาด 2.5 ตารางมิลลิเมตร
- 3.3 สายวงจรตัวรับไฟฟ้า ให้ใช้สายขนาด 2.5 ตารางมิลลิเมตร
- 3.4 สายดิน ให้ใช้สายขนาดไม่ต่ำกว่า 1.5 ตารางมิลลิเมตร

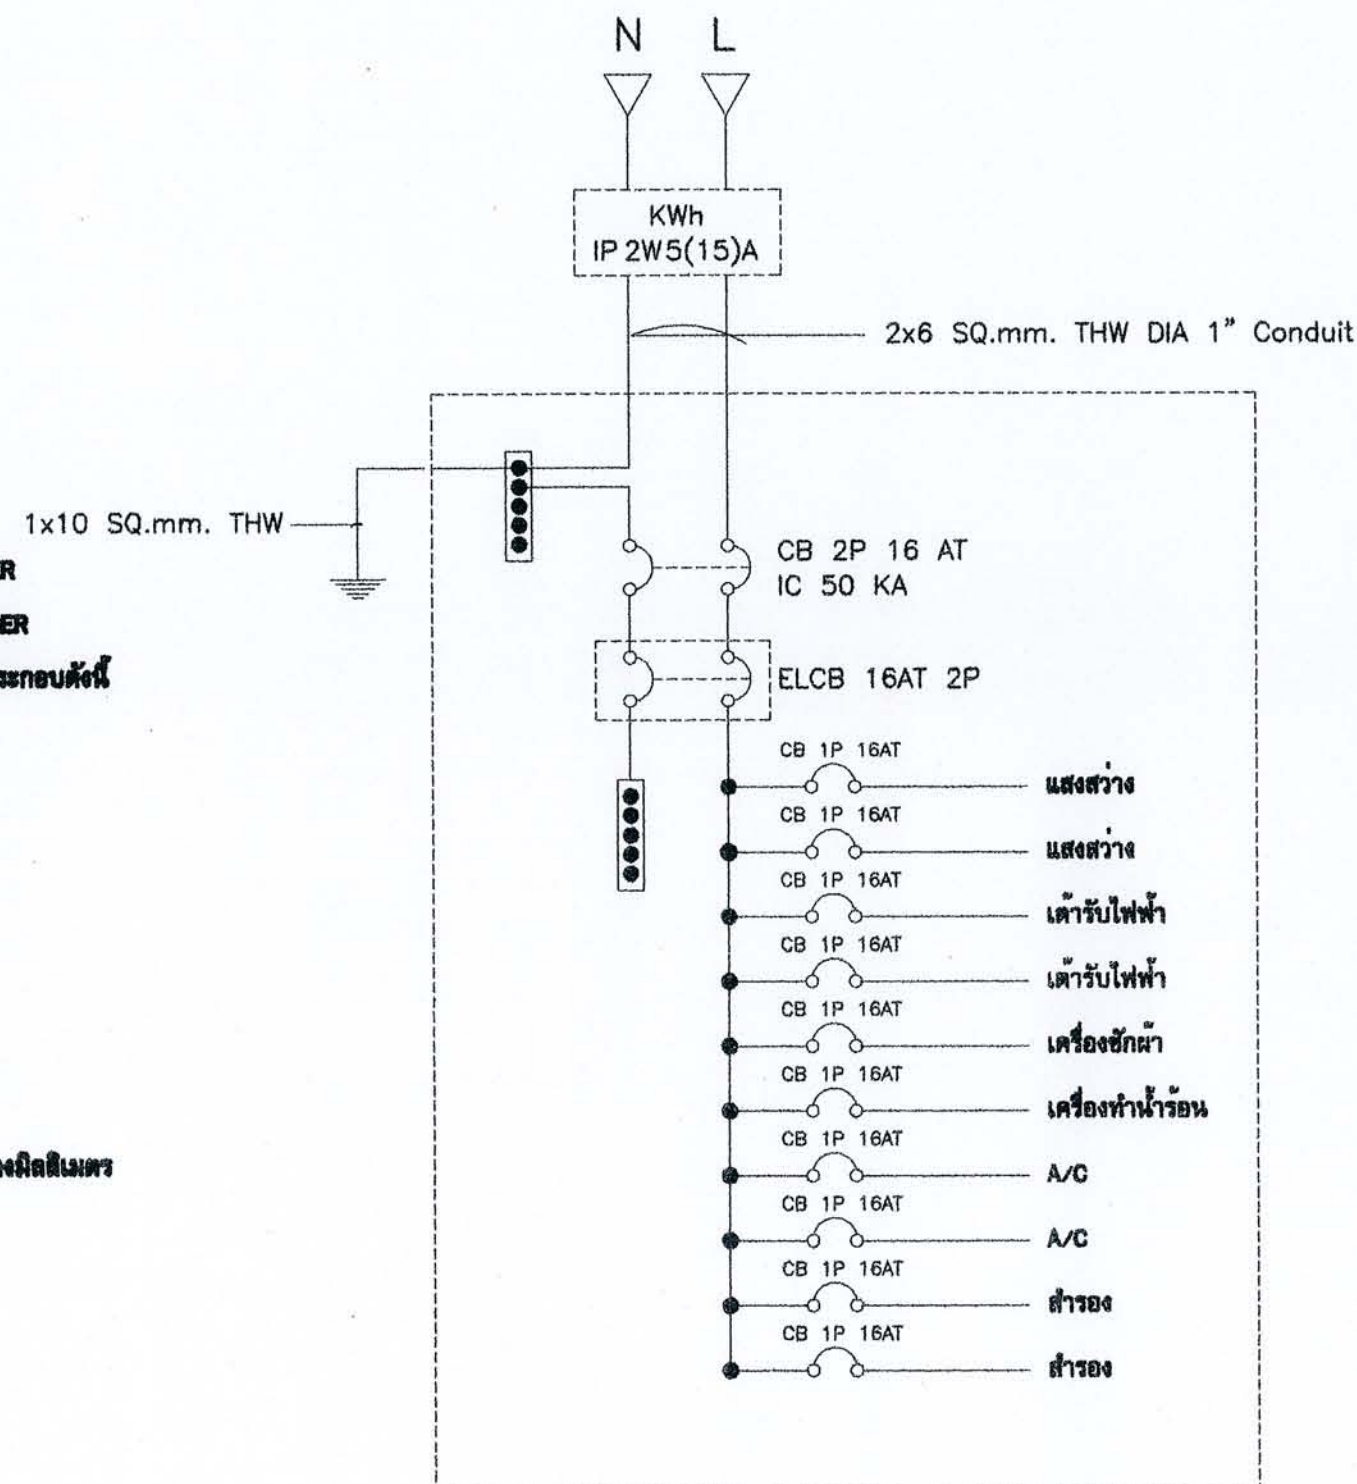


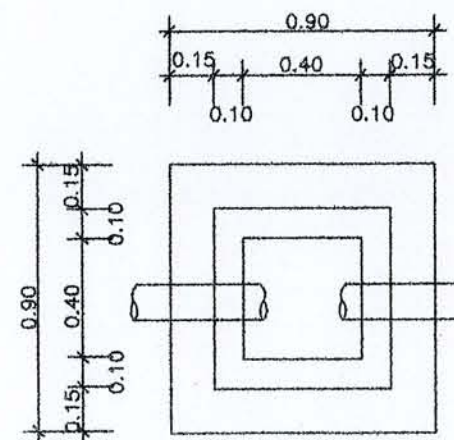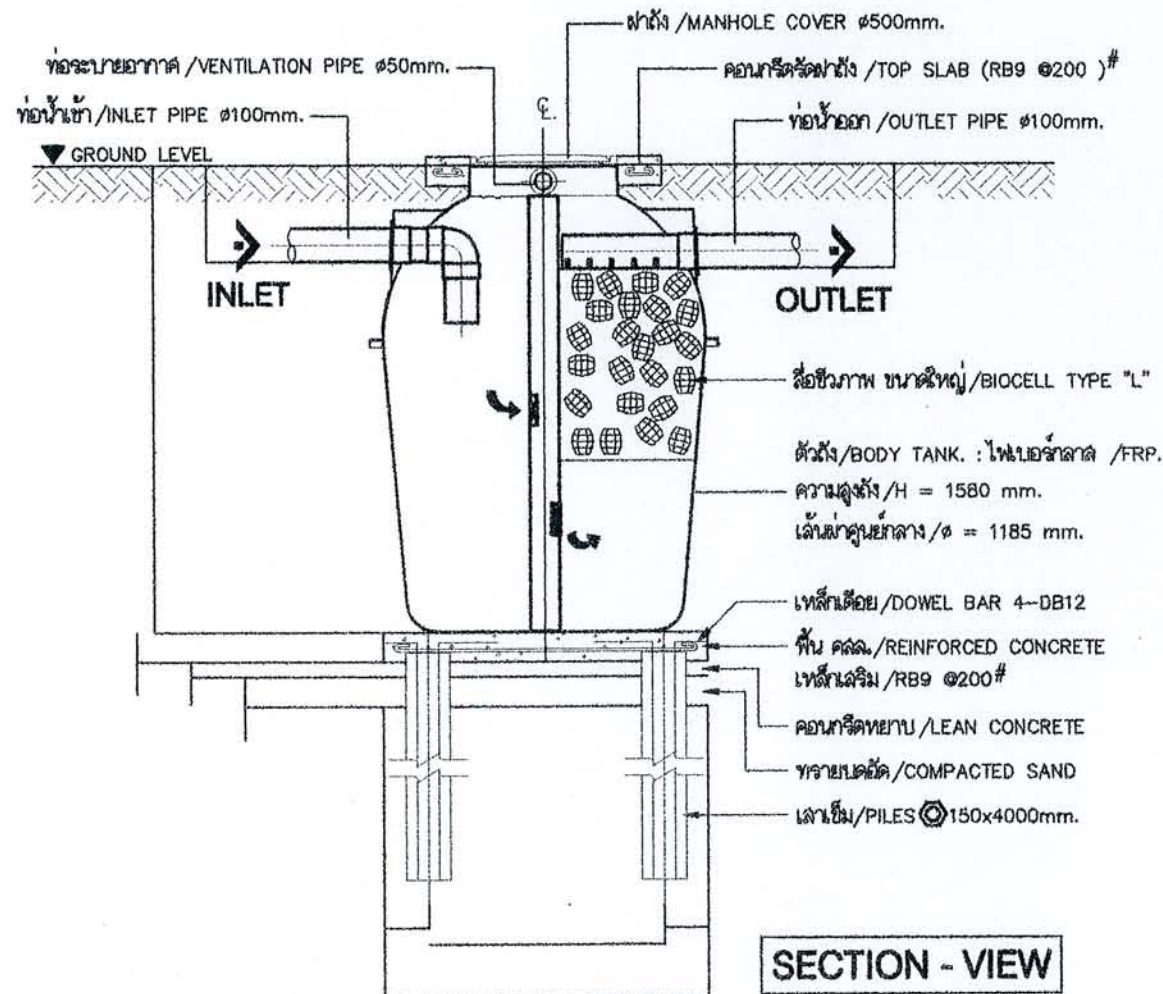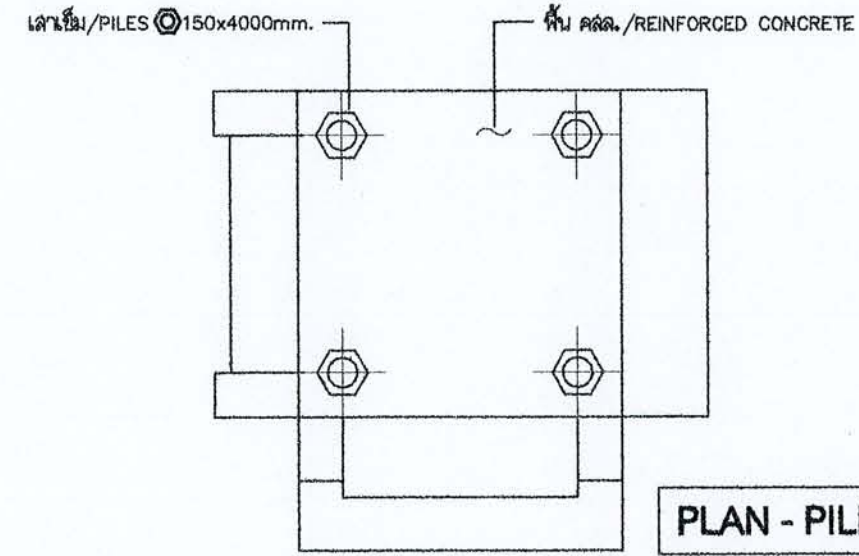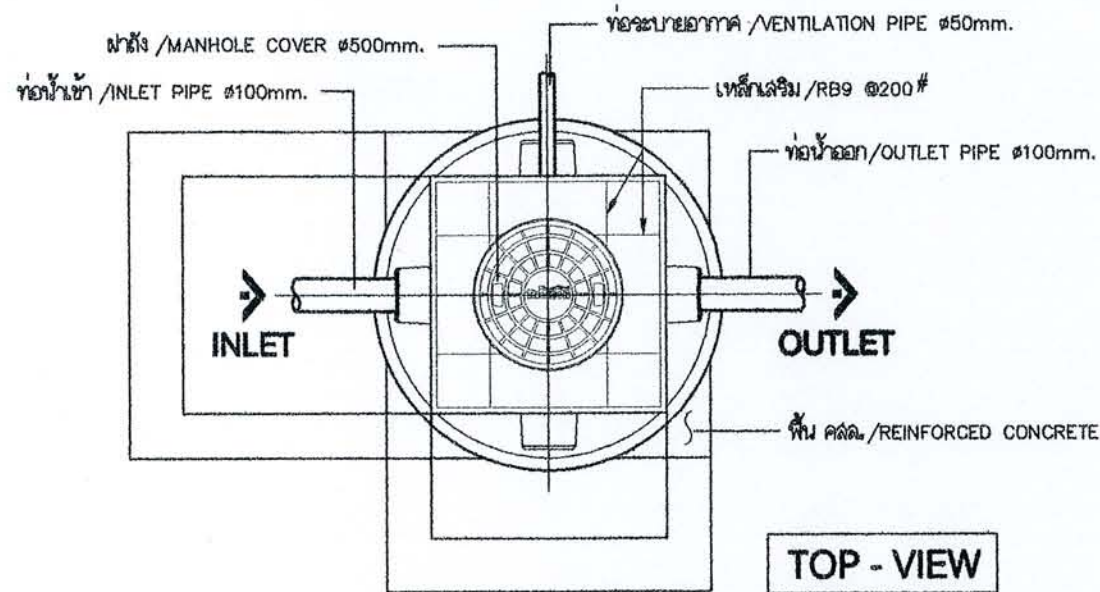


แปลนขยายบ่อพัก

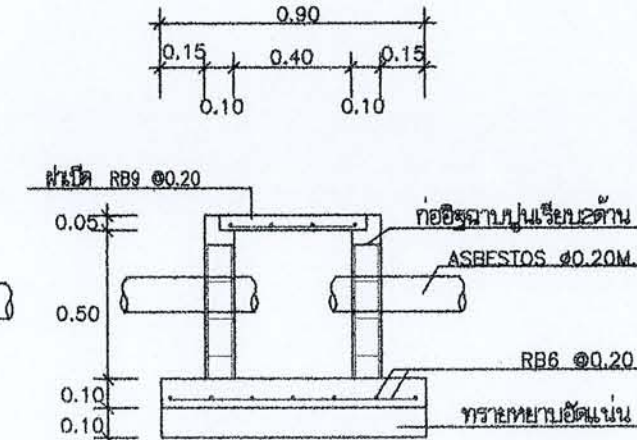

รูปตัดขยายบ่อพัก

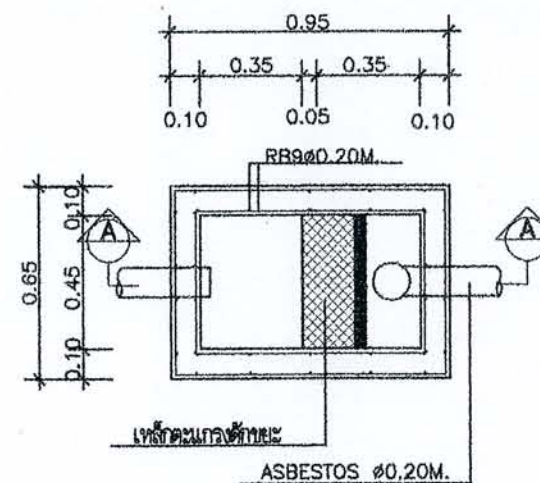

แปลนขยายบ่อพักขยะ

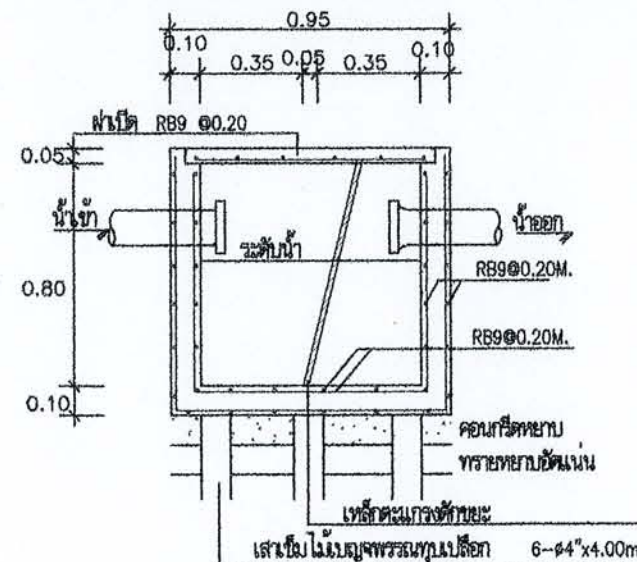

รูปตัดขยายบ่อพักขยะ

REMARK

PILING AND FOUNDATION DESIGN, SHALL BE DETERMINED OR OMITTED BASED ON ACTUAL SOIL BEARING CAPACITY BY CONSULTING WITH CIVIL ENGINEER.

การออกแบบเสาเข็มและฐานรากให้ยึดถือตามผลการการรับน้ำหนักของดินที่หน้างาน ภายใต้การควบคุมและให้คำปรึกษาโดยวิศวกรโครงสร้าง



สำนักงานโยธา
กรุงเทพมหานคร

โครงการ
แบบบ้านขยะเพื่อประชาชน

ตามนโยบาย

ม.ร.ว.สุขุมพันธุ์ บริพัตร ผู้ว่าฯกทม.
นายแพทย์ เจริญพร รอดูจากกทม.
นายธีระชน มโนทิตตกุล รอดูจากกทม.
นายพงศ์ศักดิ์ เต็มศักดิ์ ปลัดฯกทม.

ผู้อำนวยการสำนักงานโยธา
นายสมศักดิ์ สันติ
รองผู้อำนวยการสำนักงานโยธา
นายวิศักดิ์ เต็มพร
ผู้อำนวยการสำนักงานโยธา
นายสมศักดิ์ สันติ
หัวหน้ากลุ่มงานสถาปัตยกรรม
นายสมศักดิ์ สันติ
หัวหน้ากลุ่มงานวิศวกรรม
นายสมศักดิ์ สันติ
นายธีระชน รอดูจากกทม.

สถาปนิก
นางสาวสมนารถย์ กัญจนะ
วิศวกรโครงสร้าง
นายวิวัฒน์ เจริญพร
วิศวกรไฟฟ้า
นายอภิสิทธิ์ จิระนคร
วิศวกรสุขาภิบาล
นางสาวสมนารถย์ กัญจนะ
วิศวกรเครื่องกล

นายช่างเขียนแบบ

แบบ
026 บ้านขยะ

เจ้าของ

สถานที่

แบบแสดง

แบบขยายบ่อน้ำดื่ม
แบบขยายบ่อพัก บ่อคักขยะ

มาตราส่วน No Scale

FILE : เลขที่ 22

วันที่ 2553

ชื่อโครงการ

รวมแบบ

22

รายการแนบ